






Structure of the tagging system

Structure of the component tagging

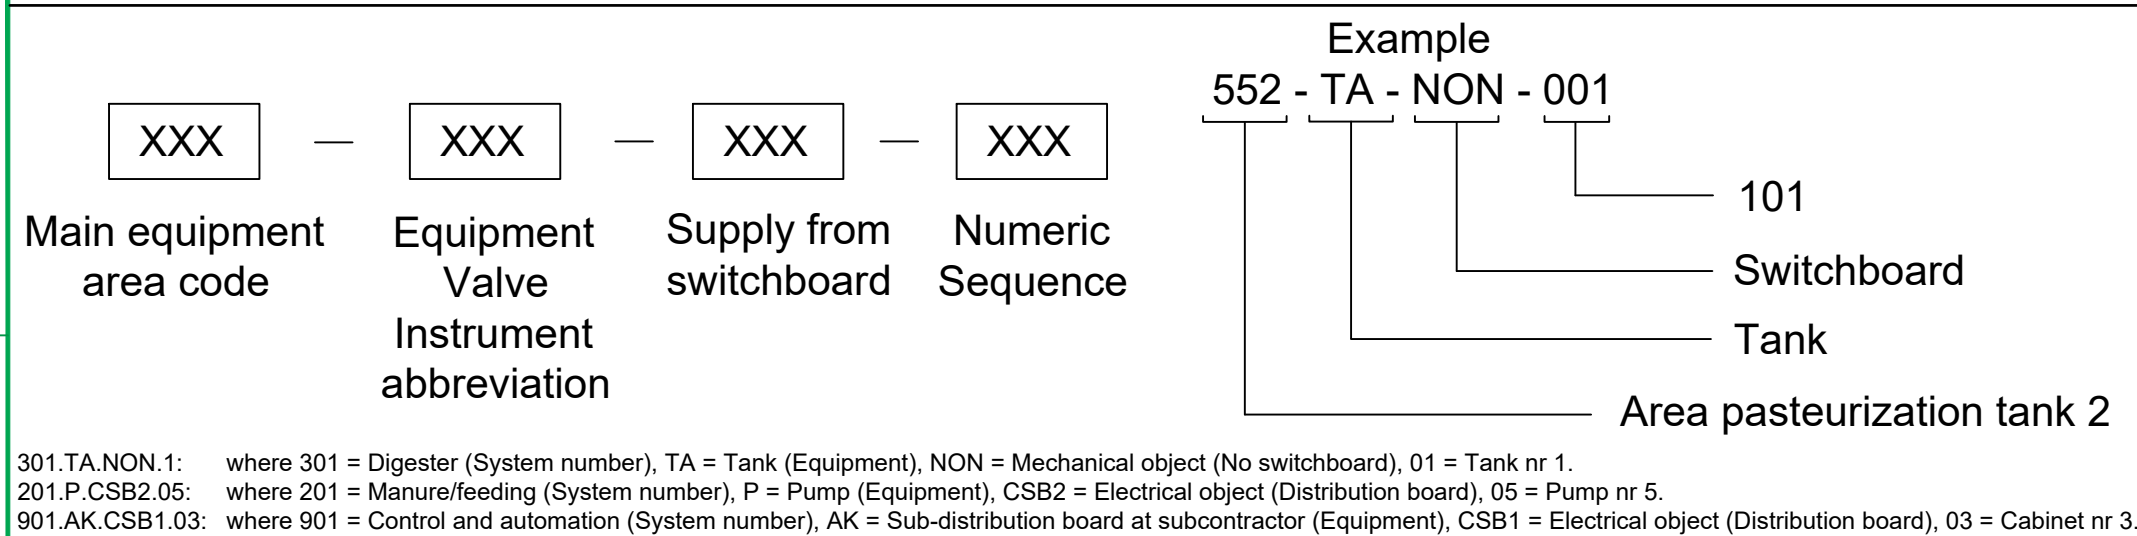

301.TA.NON.1: where 301 = Digester (System number), TA = Tank (Equipment), NON = Mechanical object (No switchboard), 01 = Tank nr 1.
 201.P.CSB2.05: where 201 = Manure/feeding (System number), P = Pump (Equipment), CSB2 = Electrical object (Distribution board), 05 = Pump nr 5.
 901.AK.CSB1.03: where 901 = Control and automation (System number), AK = Sub-distribution board at subcontractor (Equipment), CSB1 = Electrical object (Distribution board), 03 = Cabinet nr 3.

Lines

 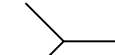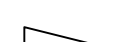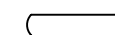Description	Symbol
Subcontractor scope	
Boundary line	
Page connector	
Start pipe - Not linked to page	
End pipe - Not linked to page	
Fald/ Slope	
Insulation	
Electrical Heat tracing	

Building/Area/Tank


Description	Code
Primary digester	PD
Secondary digester	SD
Digester storage	DST
Liquid manure tank	LMT
Liquid biomass tank	LBT
Outlet tank	OT
Blackwater tank	BWT
Tech building	TB
Admin building	ADB
Solid biomass building	SBB
Liquid biomass building	LBB
Plansilo	PS
Pump house	PH
Hygienization tanks	HYG
Flare	FLA
Stack	STA
Odour treatment facility	OD
Upgrade facility	UPG
Liquifaction facility	LIQ
Oil boiler	OB
Wood boiler	WB
Transformer	TR

Media code

Media	Pipe color	RBG color	Code
Heat Return		0,37,245	HR
Heat Supply		255,0,0	HS
Heat Hot Return		255,223,127	HHR
Heat Hot Supply		238,129,129	HHS
Cooling Supply		0,255,183	CS
Cooling Return		126,189,189	CR
Black Water		36,39,132	BW
CIP		253,53,223	CIP
Process Water		170,170,255	PW
Technical Water		69,78,104	TW
Drinking Water		0,0,129	DW
Drinking Water Hot		0,127,255	DWH
Condensate		108,163,208	CW
Steam		255,82,82	ST
Steam Condensate		189,0,0	STC
Liquid Manure (Slurry)		240,130,40	LM
Liquid Biomass (Substrat)		128,0,255	LB
Process Biomass		165,103,82	PB
Hygienized Biomass		169,130,0	HB
Recirculated Biomass		165,103,82	RCB
Ferric Chloride FeCl		145,255,71	FeCl
Ventilation Odour Treatment		199,199,199	VOT
Ventilation Fresh Air		199,199,199	VFA
Compressed Air		64,64,64	CA
Oxygen		0,128,255	O2
Raw Biogas		255,255,0	RB
Return/reject Gas		116,118,4	RG
Nature Gas		0,255,127	NG
Instrument Leader		Green	N/A

Structure of the pipeline tagging system

The pipetag consists of various information about the pipe
Full pipeline tag as shown below

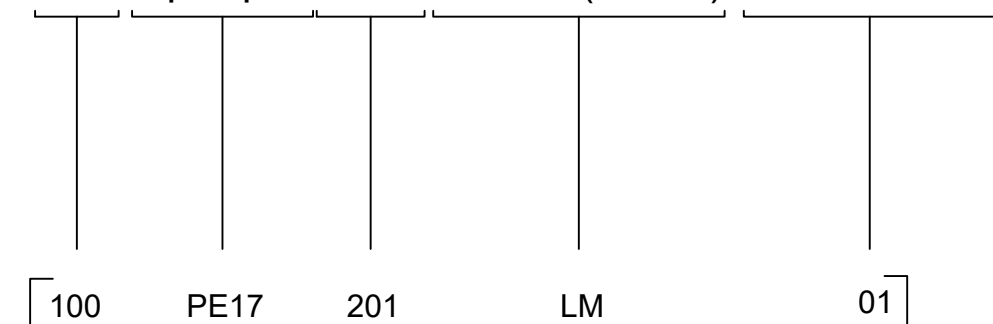

Example

Two (2) digits. Starts with 01
[01]

- Two (2) to four (4) characters (letters)
- [LM - Liquid manure]

Three (3) digits
[201 - Manure feeding in tank 1]

Pipe Spec name
[PE17 - PE100 SDR17]

Pipe size
DN indication for Metric pipes
OD indication for PE-pipe
[This example is OD 100 mm]

The pipe tag will be shown on the P&ID as follows: PipeSpec-Size
Area-Service-Serialnumber

Example of line tag notation on P&ID: PE17-110
201-LM-01

Line color corresponding to table above.
The part below the pipeline is the Unique Line Tag.
Unique Line Tag is generated automatically when creating complete Line Tag.
Unique Line Tag is used by the P3D system when designing pipes in the 3D model and when generating Isometrics.

Rev. Nr.: Rev. Dato: Rev. Description:

Builder: ST1

Project: SLK

Subject: PID Legend
 Rev. 6

Int.: MDC | QC.: CM | APP.: | Date: 15-10-2025




Lundbsy Renewable Solutions A/S, Hjarbakvej 65, 8831 Løgstrup
Tlf.: +45 96 49 43 00 Info@lundbsy.dk
This Drawing is subject to copyright and may not be reproduced without permission from Lundbsy Renewable Solutions A/S.


Project nr.: 1768

Drawing nr.:
PID Legend


FORMAT: **A1**

1	2	3	4	5	6	7	8																																						
Valves		Equipment			Piping	Instruments																																							
Hand valves		Pumps / Compressors / Blowers		Equipment	Piping symbols		Description																																						
Symbols	Code	Description	Symbols	Code	Description	Symbols	Code	Description																																					
	HV	General valve		P	Pump (General)		N/A	Offpage connector	Instruments will be tagged XXX - XX - XXX - XXX Main area code Letter code Switchboard Numeric sequence First letter XX Succeeding letter XX Numeric sequence Description Example Field instrument Instrument with connection to control TI 01 Temperature indication 01 LS 02 Level switch 02 Instruments with succeeding letter T is an analog signal. Instruments with succeeding letter S is a digital signal. <table><tr><th>Instruments</th><th>Abbreviation</th></tr><tr><td>Analyze Indicator</td><td>AI</td></tr><tr><td>Analyse Transmitter</td><td>AT</td></tr><tr><td>Energi Transmitter</td><td>ET</td></tr><tr><td>Flow Indicator</td><td>FI</td></tr><tr><td>Flow Transmitter</td><td>FT</td></tr><tr><td>Flow Switch</td><td>FS</td></tr><tr><td>Flow Transmitter</td><td>FT</td></tr><tr><td>General Switch</td><td>GS</td></tr><tr><td>Level Switch</td><td>LS</td></tr><tr><td>Level Indicator</td><td>LI</td></tr><tr><td>Level Transmitter</td><td>LT</td></tr><tr><td>Pressure Indicator</td><td>PI</td></tr><tr><td>Pressure Switch</td><td>PS</td></tr><tr><td>Pressure Transmitter</td><td>PT</td></tr><tr><td>Thermometer</td><td>TI</td></tr><tr><td>Temperature Transmitter</td><td>TT</td></tr><tr><td>Weight Transmitter</td><td>WT</td></tr></table>	Instruments	Abbreviation	Analyze Indicator	AI	Analyse Transmitter	AT	Energi Transmitter	ET	Flow Indicator	FI	Flow Transmitter	FT	Flow Switch	FS	Flow Transmitter	FT	General Switch	GS	Level Switch	LS	Level Indicator	LI	Level Transmitter	LT	Pressure Indicator	PI	Pressure Switch	PS	Pressure Transmitter	PT	Thermometer	TI	Temperature Transmitter	TT	Weight Transmitter	WT
Instruments	Abbreviation	
Analyze Indicator	AI	
Analyse Transmitter	AT	
Energi Transmitter	ET	
Flow Indicator	FI	
Flow Transmitter	FT	
Flow Switch	FS	
Flow Transmitter	FT	
General Switch	GS	
Level Switch	LS	
Level Indicator	LI	
Level Transmitter	LT	
Pressure Indicator	PI	
Pressure Switch	PS	
Pressure Transmitter	PT	
Thermometer	TI	
Temperature Transmitter	TT	
Weight Transmitter	WT	
	HV	Ball valve		P	Positive displacement pump		N/A	Flange connection																																					
	HV	Butterfly valve		P	Helical rotor pump		N/A	Blind flange																																					
	HV	Globe valve		P	Centrifugal pump		NO	Truck nozzle																																					
	HV	Three way valve		P	Peristaltic pump		NO	Funnel/Drain																																					
	HV	Ground covered valve		MC	Rotacut		AS	Expansion joint																																					
	BV	Balancing valve		MC	Shredder		SN	Strainer																																					
Actuated valves / Regulating valves			Heating and Cooling				N/A	Going into the ground / Coming up from																																					
	MV/RV	Motor ball valve		HX	Heat exchanger - Shell & tube		AJ	Concentric reducer																																					
	MV/RV	Motor butterfly valve		HX	Heat exchanger - plate		AJ	Eccentric reducer																																					
	AV/RV	Pneumatic ball valve		HX	Heat exchanger - double pipe		AX	Sample point																																					
	AV/RV	Pneumatic valve		HX	Heating coil (in tank)		BS	Inline silencer																																					
	AV	Solenoid valve		HS	Heatpump		BU	Electrical heat tracing																																					
Safety valves			Tank equipment				N/A	Going though wall																																					
	SV	Exhaust valve covers		AG	ISO Agitator - Propeller	<table><tr><th>Category</th><th>Numbers</th></tr><tr><td>Manual valves</td><td>001-099</td></tr><tr><td>Manual regulation valves</td><td>101-199</td></tr><tr><td>Pneumatic, electrical, solenoid</td><td>201-299</td></tr><tr><td>-</td><td>301-399</td></tr><tr><td>Check, Non-return valves</td><td>401-499</td></tr><tr><td>Drain, venting valves</td><td>501-599</td></tr><tr><td>Self-regulating valves (thermal/liquid)</td><td>601-699</td></tr><tr><td>Instrument valves</td><td>701-799</td></tr><tr><td>-</td><td>801-899</td></tr><tr><td>Safety valves</td><td>901-999</td></tr></table>			Category	Numbers	Manual valves	001-099	Manual regulation valves	101-199	Pneumatic, electrical, solenoid	201-299	-	301-399	Check, Non-return valves	401-499	Drain, venting valves	501-599	Self-regulating valves (thermal/liquid)	601-699	Instrument valves	701-799	-	801-899	Safety valves	901-999															
Category	Numbers	
Manual valves	001-099	
Manual regulation valves	101-199	
Pneumatic, electrical, solenoid	201-299	
-	301-399	
Check, Non-return valves	401-499	
Drain, venting valves	501-599	
Self-regulating valves (thermal/liquid)	601-699	
Instrument valves	701-799	
-	801-899	
Safety valves	901-999	
	SV	Safety valve		AG	Agitator	
	SV	Breather valve		LA	Light	
Mechanical valves			Filters and Vessels	
	PV	Pressure holding valve		AT	General filter / Forfilter	
	CV	Check valve		AT	General liquid	
	VV	Venting valve		AT	Drier - General	
Miscellaneous additional valve symbols				F	Suction hood	
		Operator lock mechanism		EXP	Expansion tank	
Equipment			Tanks	
	MX	Bio mixer		DT	Digester tank	
	MC	Premix		ST	Storage tank	
	CV	Debris lift unit		DT/ST	Storage tank with cover	
	CV	Screw conveyor		HT	Gas/Hyginisation tank	
	CV	Belt conveyor		TA	Buried tank	
	CRA	Crane	
	CH	ISO Stack - Chimney	
	FL	Flare	
	PD	Pulsation damper	
	SP	Screw press	
Revision clouds	
1		2		3		4		5		6		7		8																															

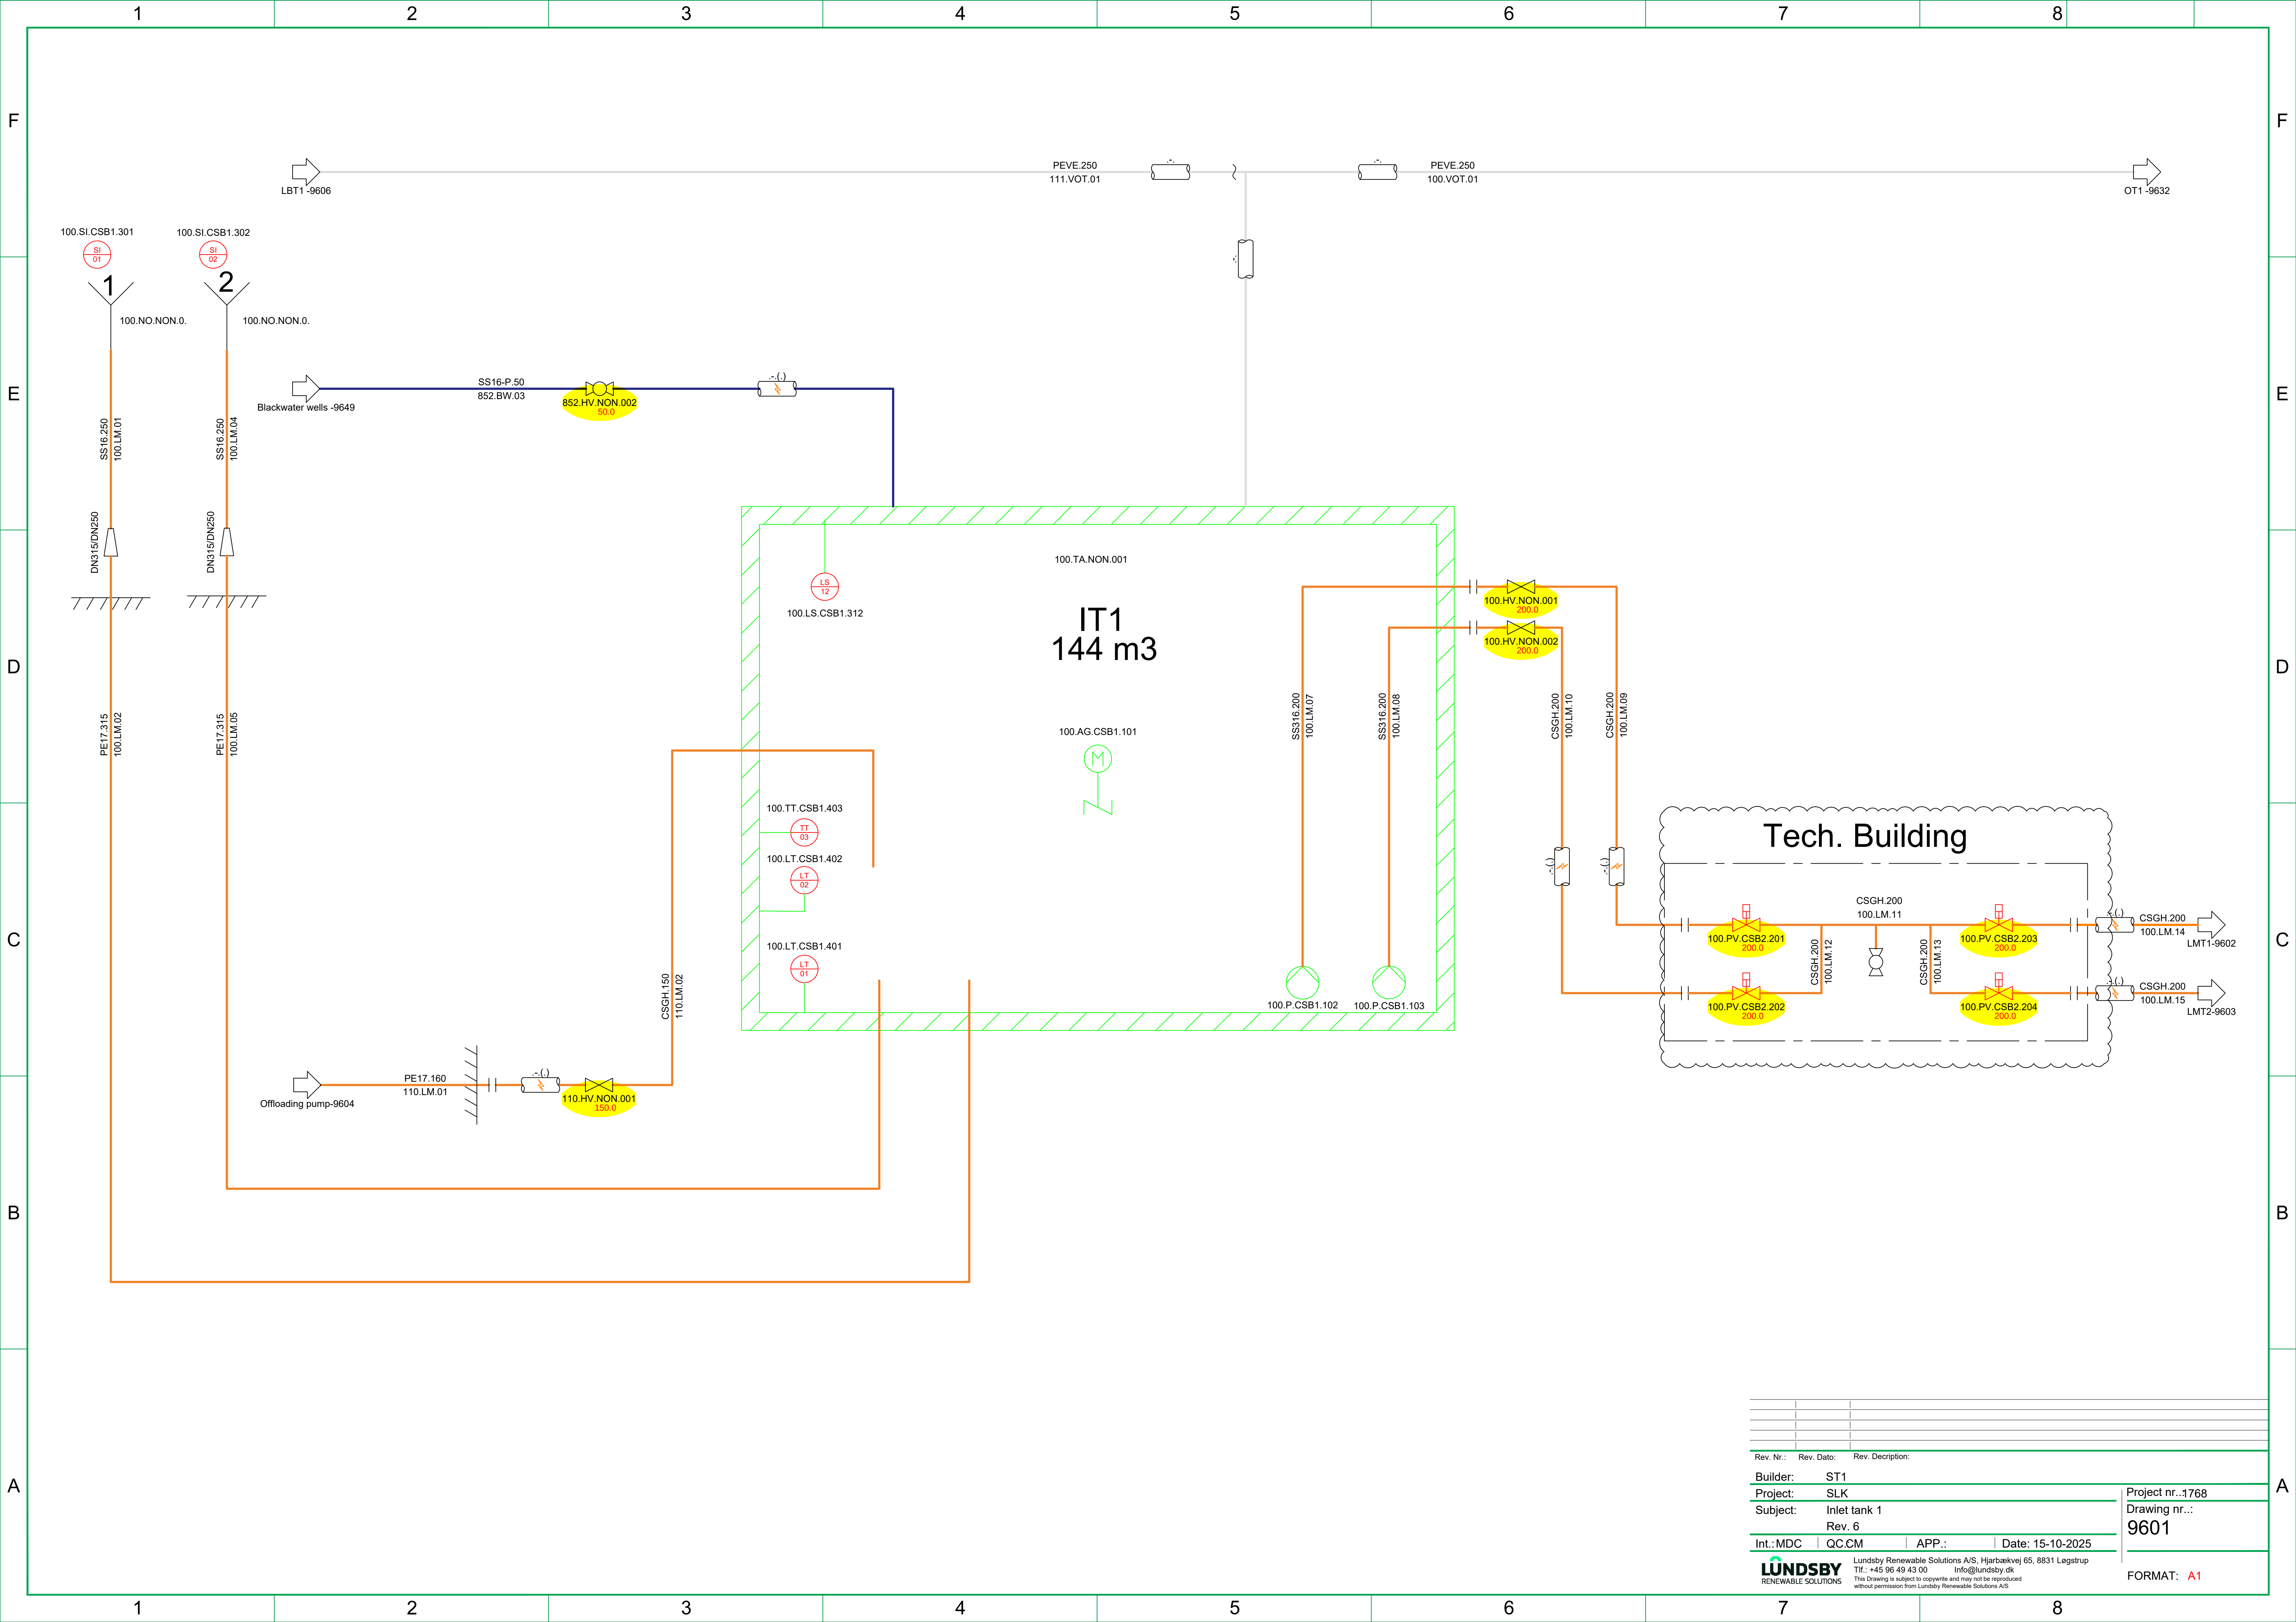


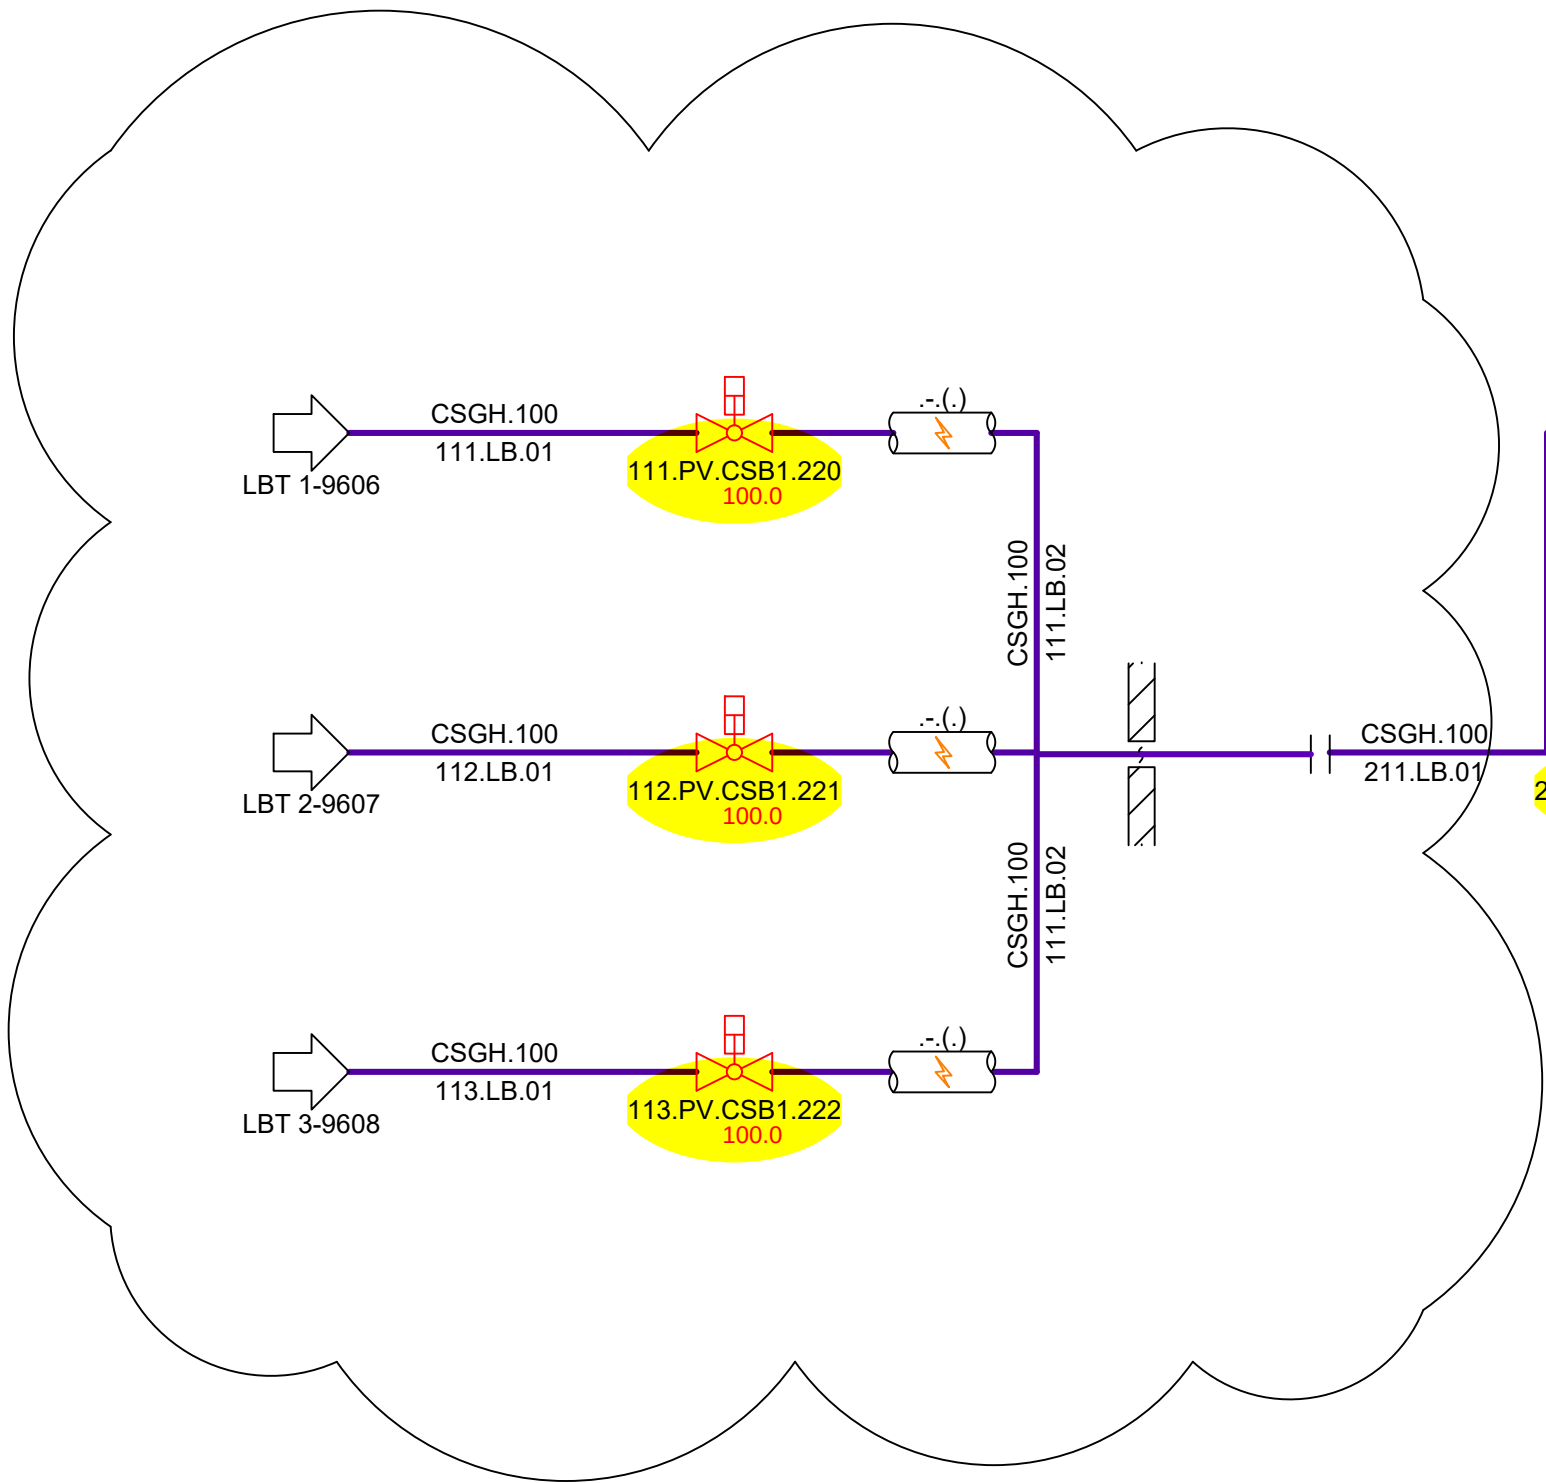


Rev. Nr.:	Rev. Dato:	Rev. Description:
Builder:	ST1	
Project:	SLK	
Subject:	Liquid biomass pump 1	
Rev. 6		
Int.:MDC	QC:CM	APP.:Date: 15-10-2025
LUNDSBY RENEWABLE SOLUTIONS		
Lundsby Renewable Solutions A/S, Hjarbækvej 65, 8831 Løgstrup Tlf.: +45 96 49 43 00 Info@lundsby.dk This Drawing is subject to copyright and may not be reproduced without permission from Lundsby Renewable Solutions A/S		
Project nr.:1768 Drawing nr.: 9605		FORMAT: A1

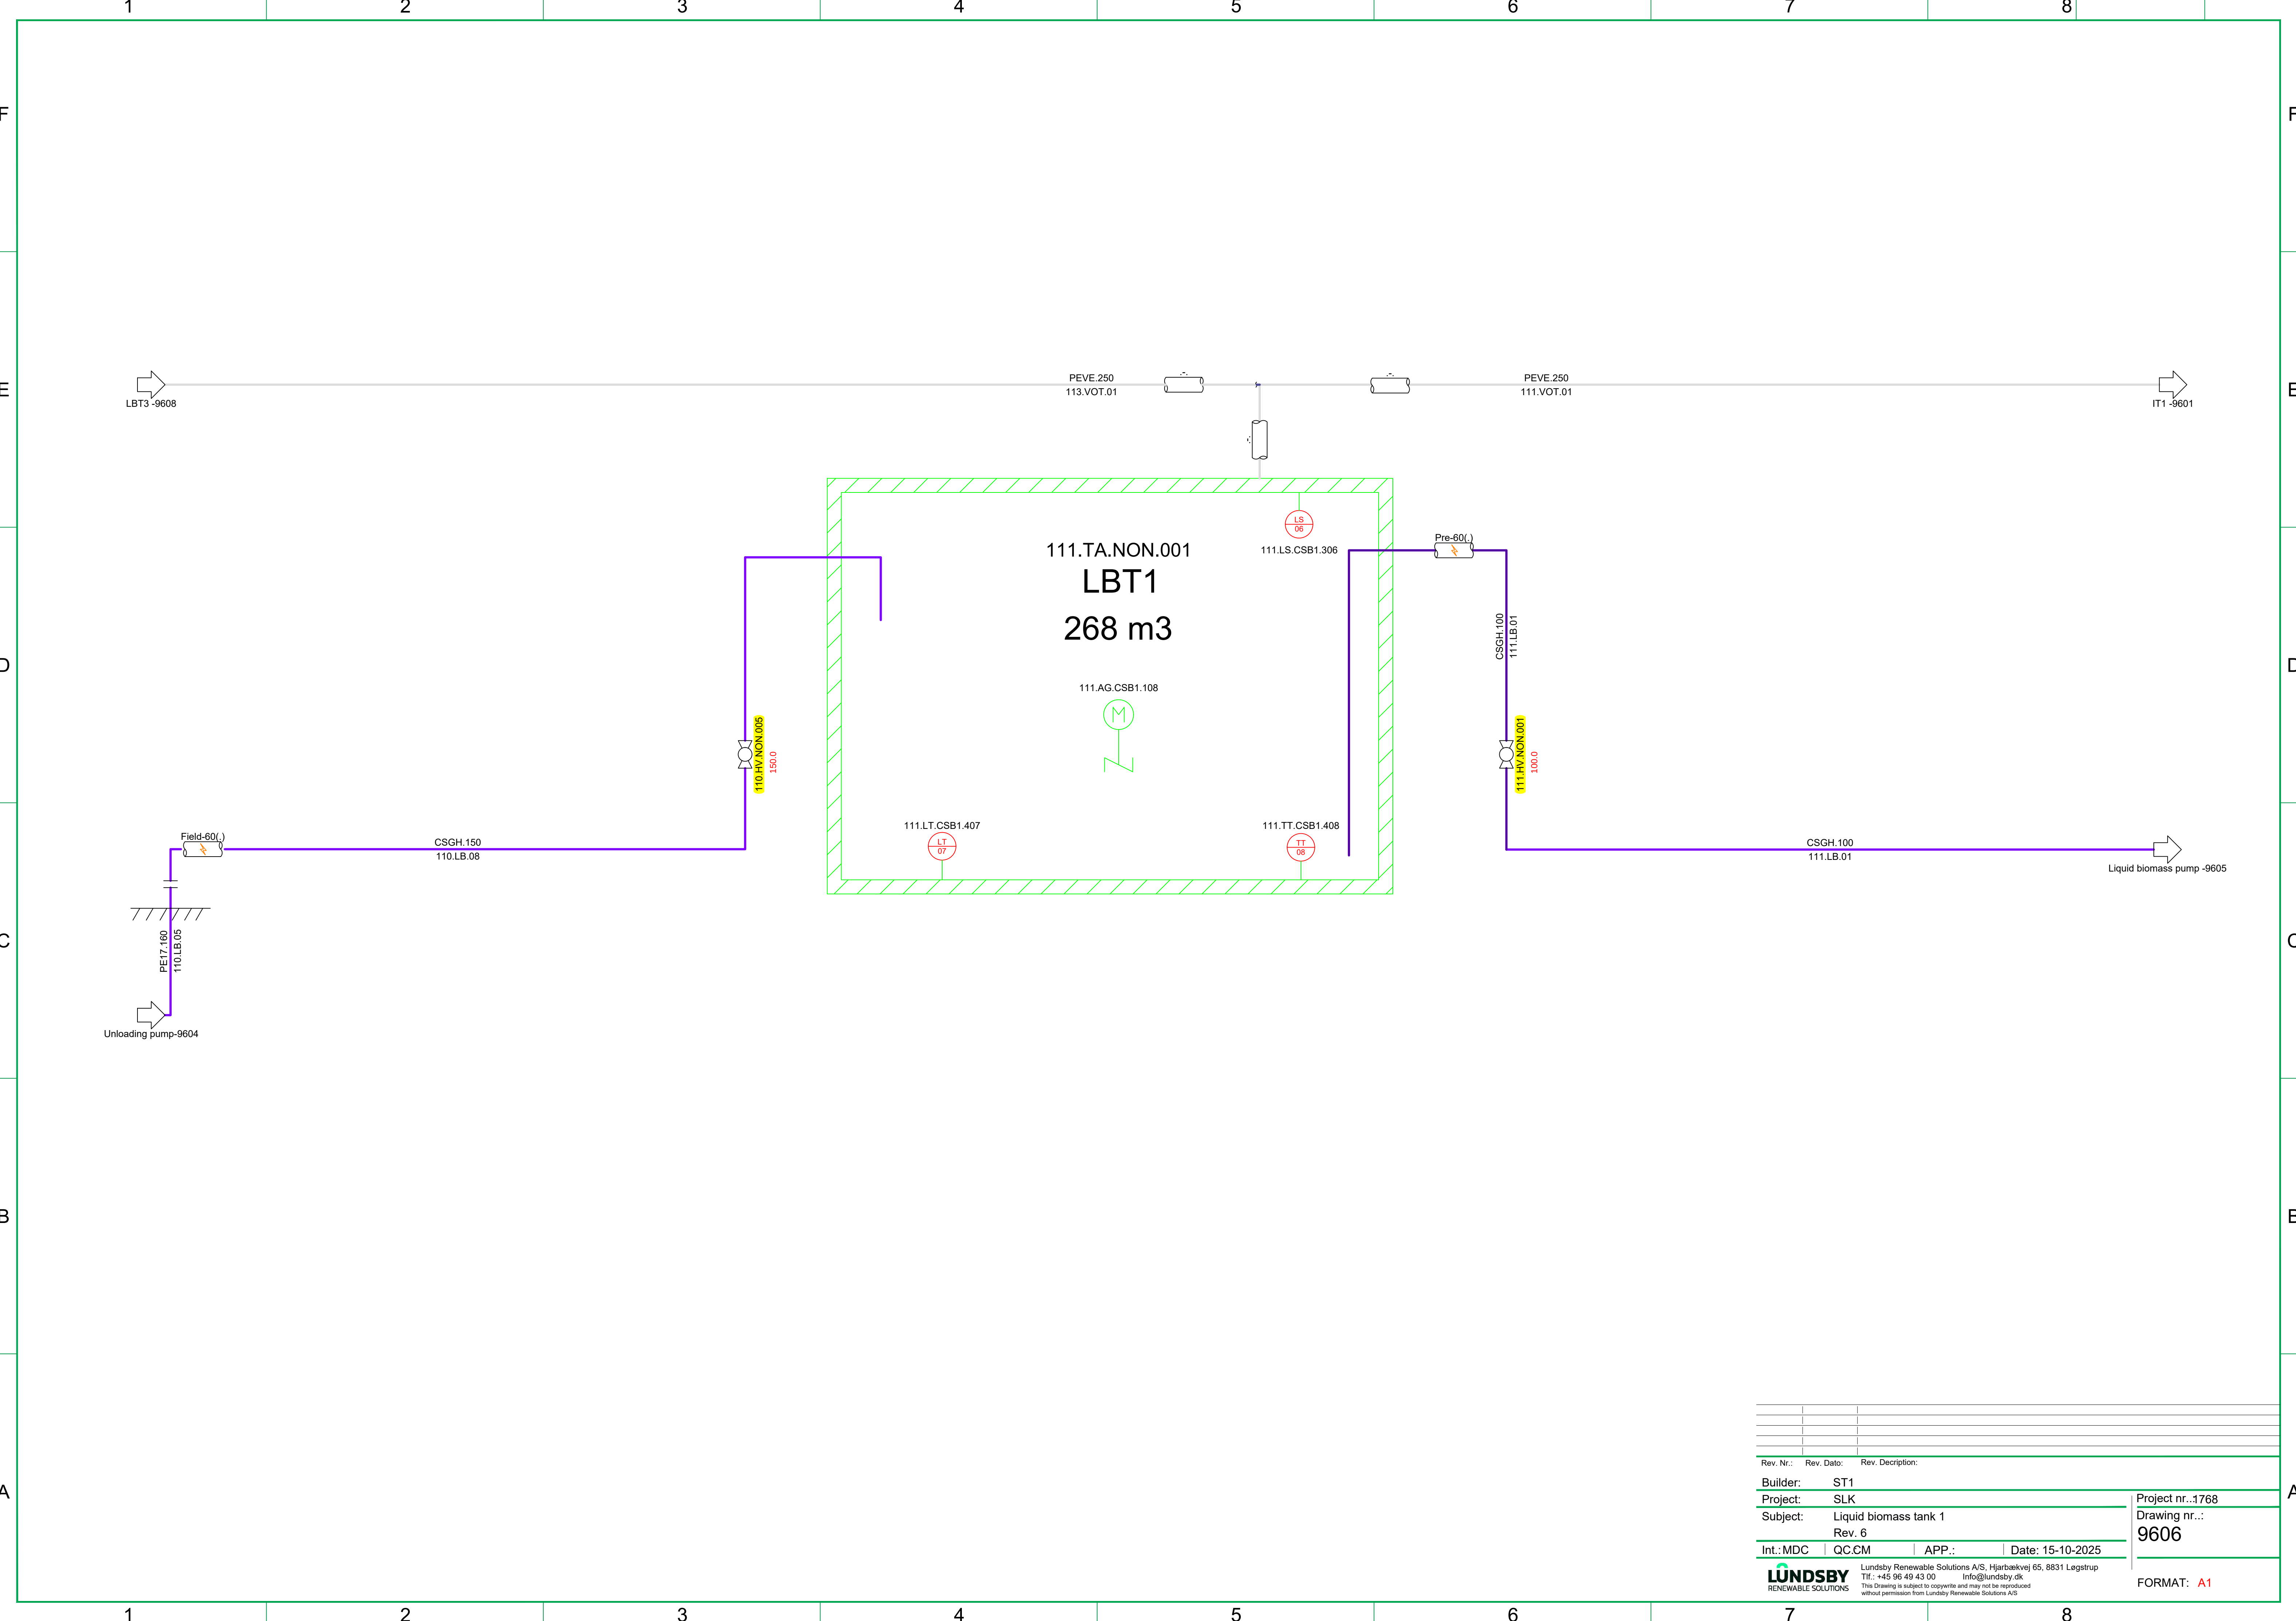


Rev. Nr.:	Rev. Dato:	Rev. Description:	
Builder:	ST1		
Project:	SLK		
Subject:	Liquid biomass tank 1		
	Rev. 6		
Int.:MDC	QC.CM	APP.:	Date: 15-10-2025
LUNDSBY RENEWABLE SOLUTIONS			Lundsby Renewable Solutions A/S, Hjarbækvej 65, 8831 Løgstrup Tlf.: +45 96 49 43 00 Info@lundsby.dk This Drawing is subject to copyright and may not be reproduced without permission from Lundsby Renewable Solutions A/S
			Project nr...1768 Drawing nr...: 9606
			FORMAT: A1

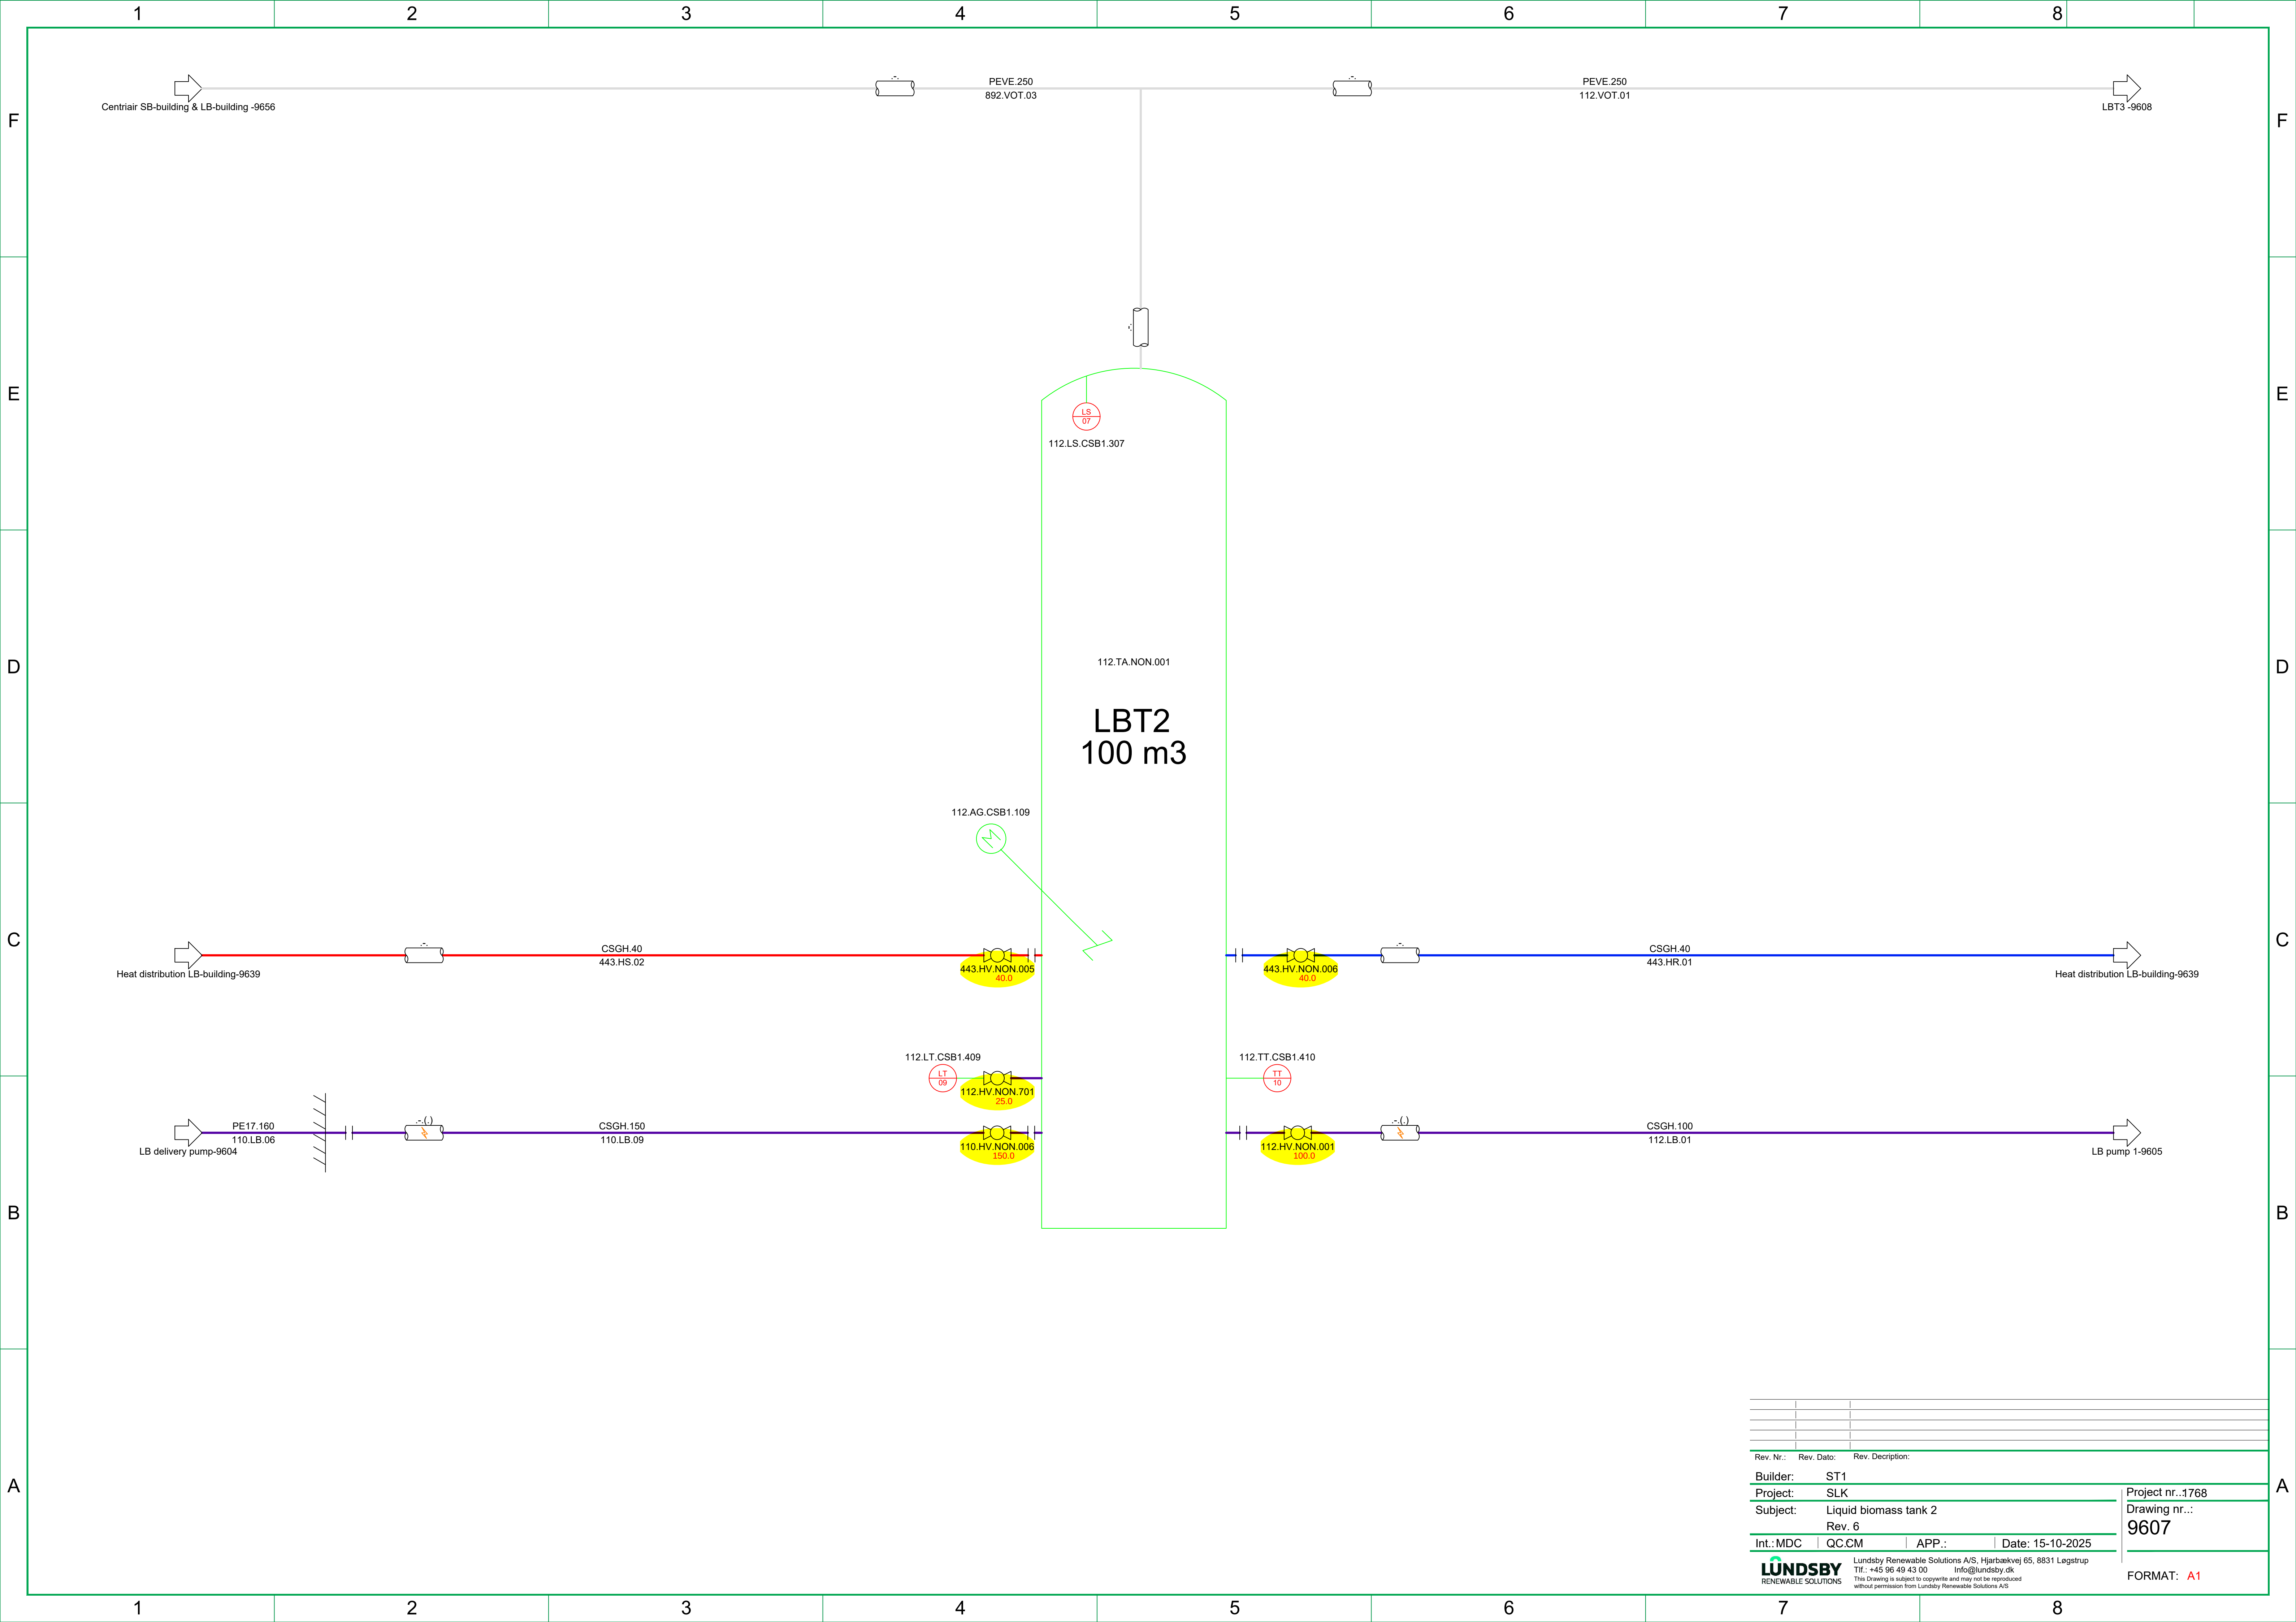


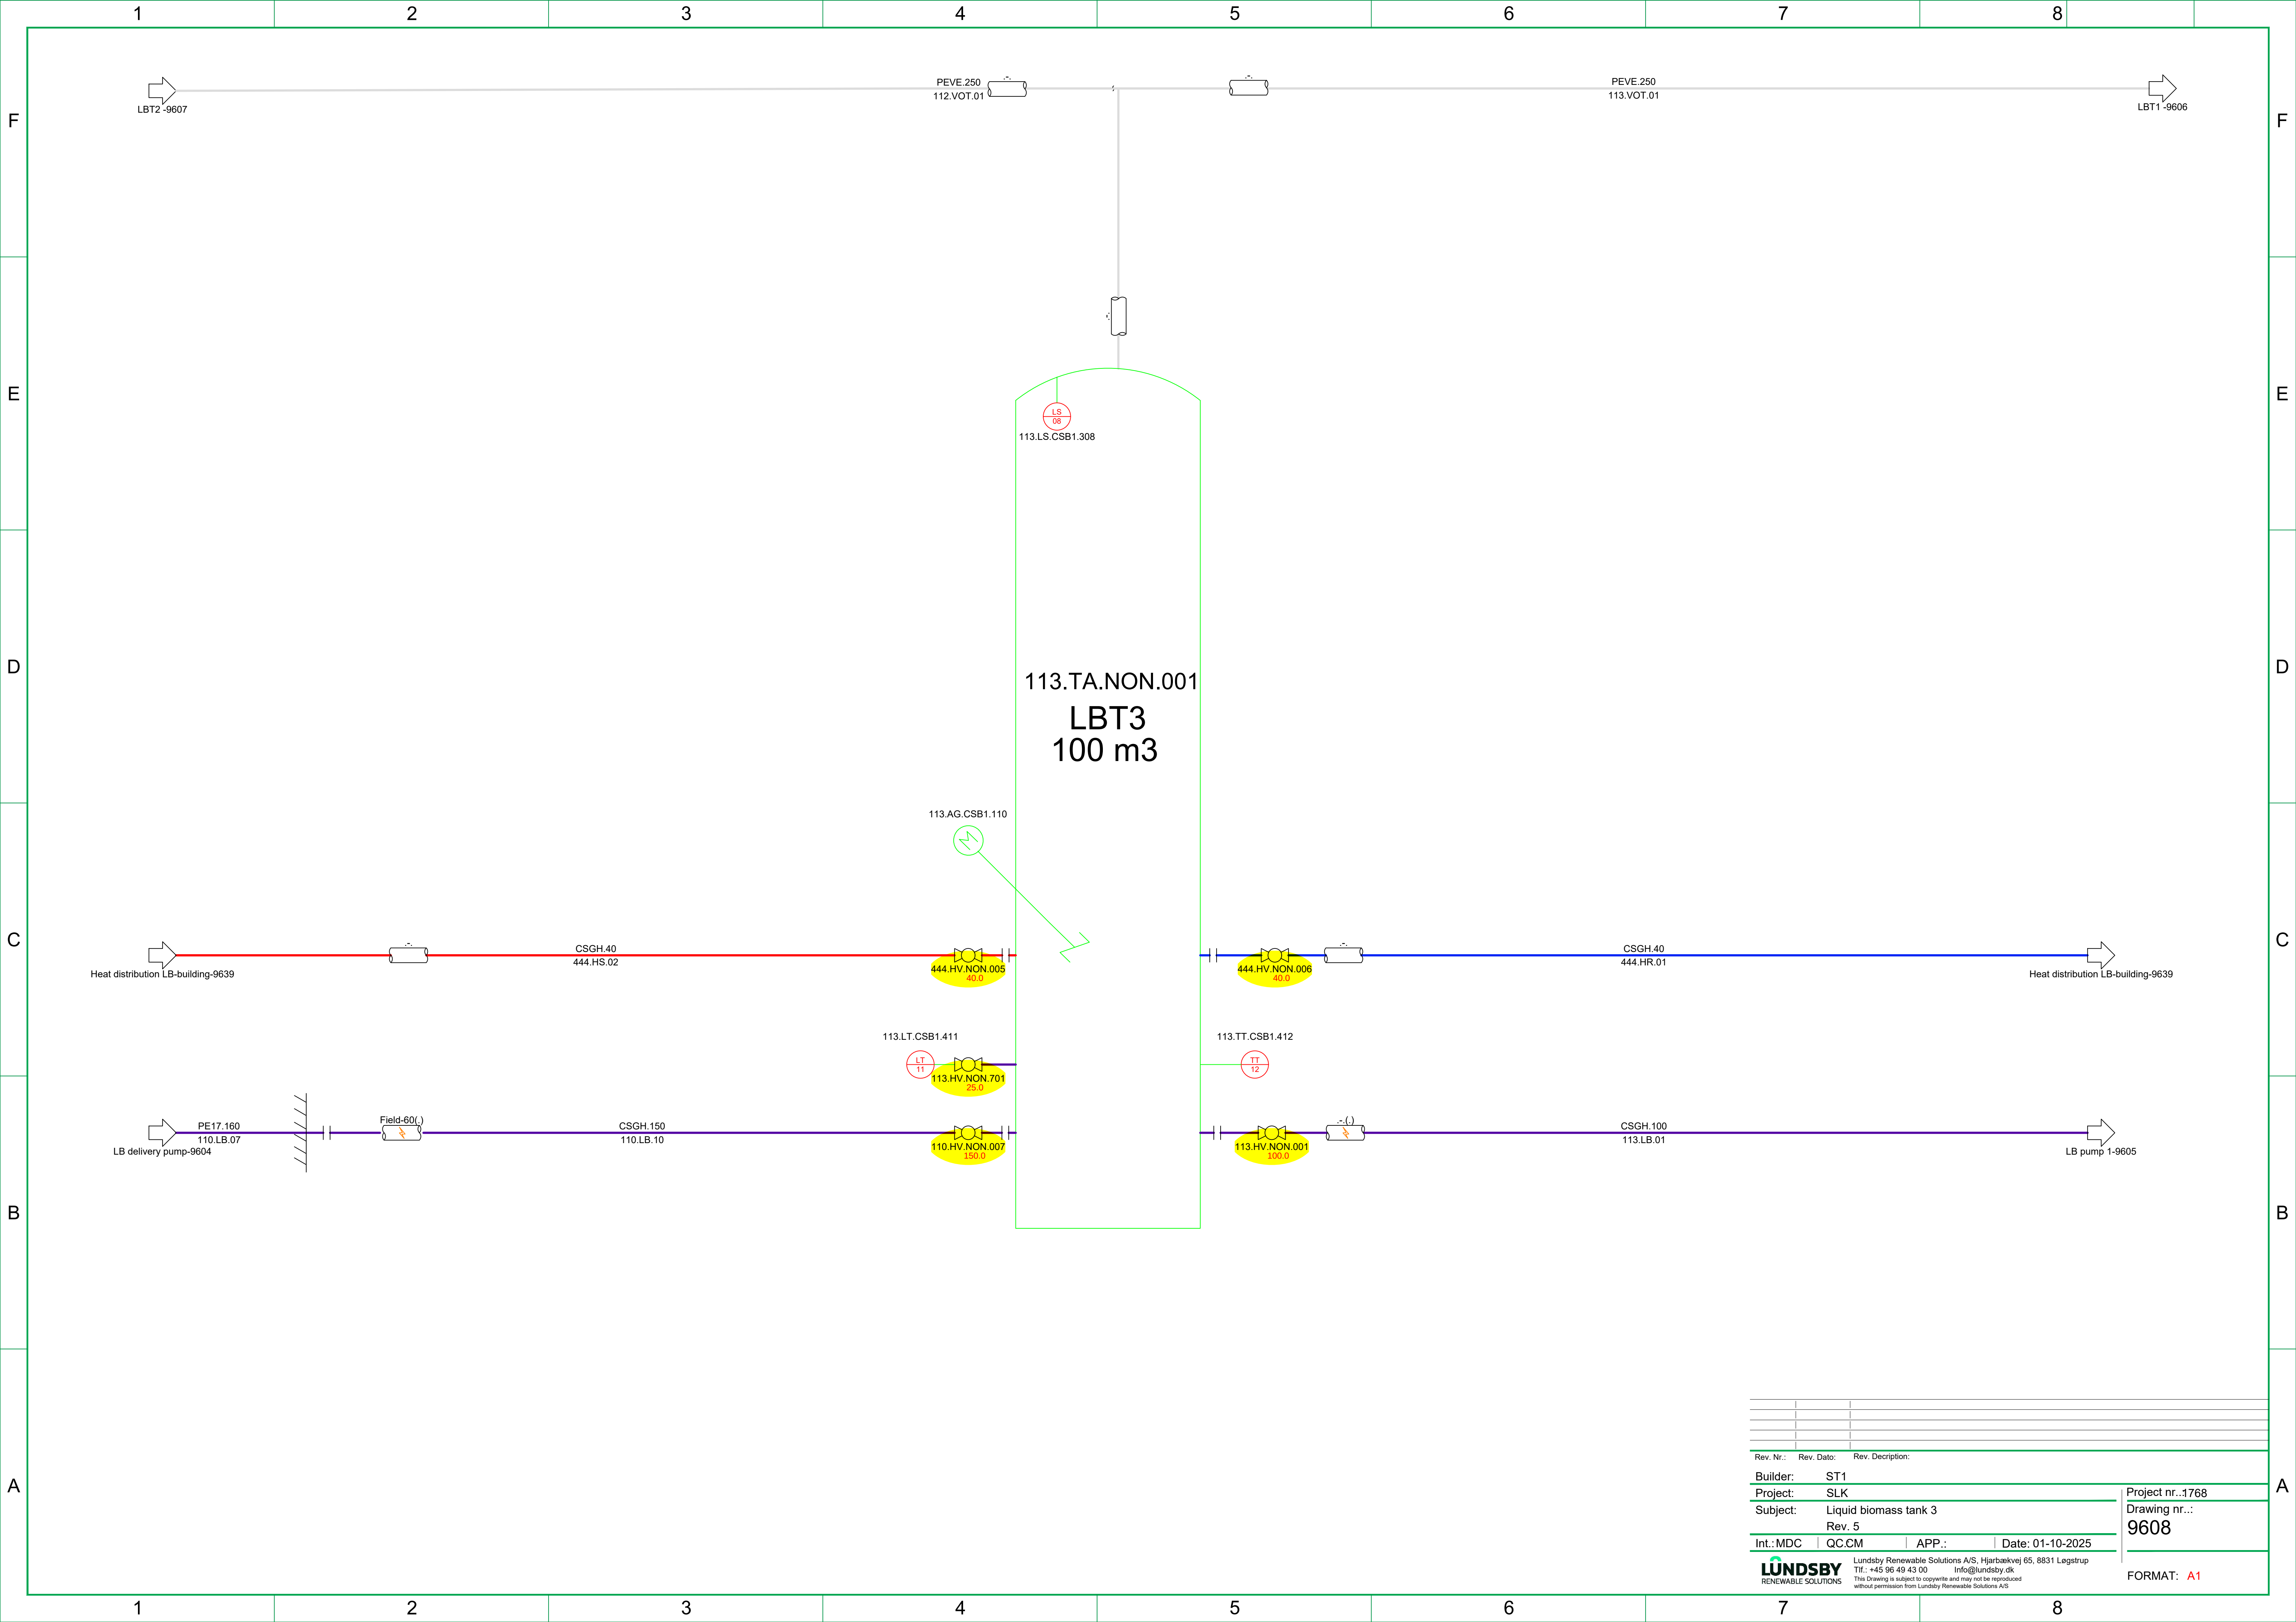

Rev. Nr.:	Rev. Dato:	Rev. Description:		
Builder:	ST1			
Project:	SLK			
Subject:	Liquid biomass tank 3			
	Rev. 5			
Int.:MDC	QC:CM	APP.:	Date: 01-10-2025	
LUNDSBY RENEWABLE SOLUTIONS Lundsby Renewable Solutions A/S, Hjarbækvej 65, 8831 Løgstrup Tlf.: +45 96 49 43 00 Info@lundsby.dk This Drawing is subject to copyright and may not be reproduced without permission from Lundsby Renewable Solutions A/S				
Project nr.:1768			Drawing nr.: 9608	
			FORMAT: A1	

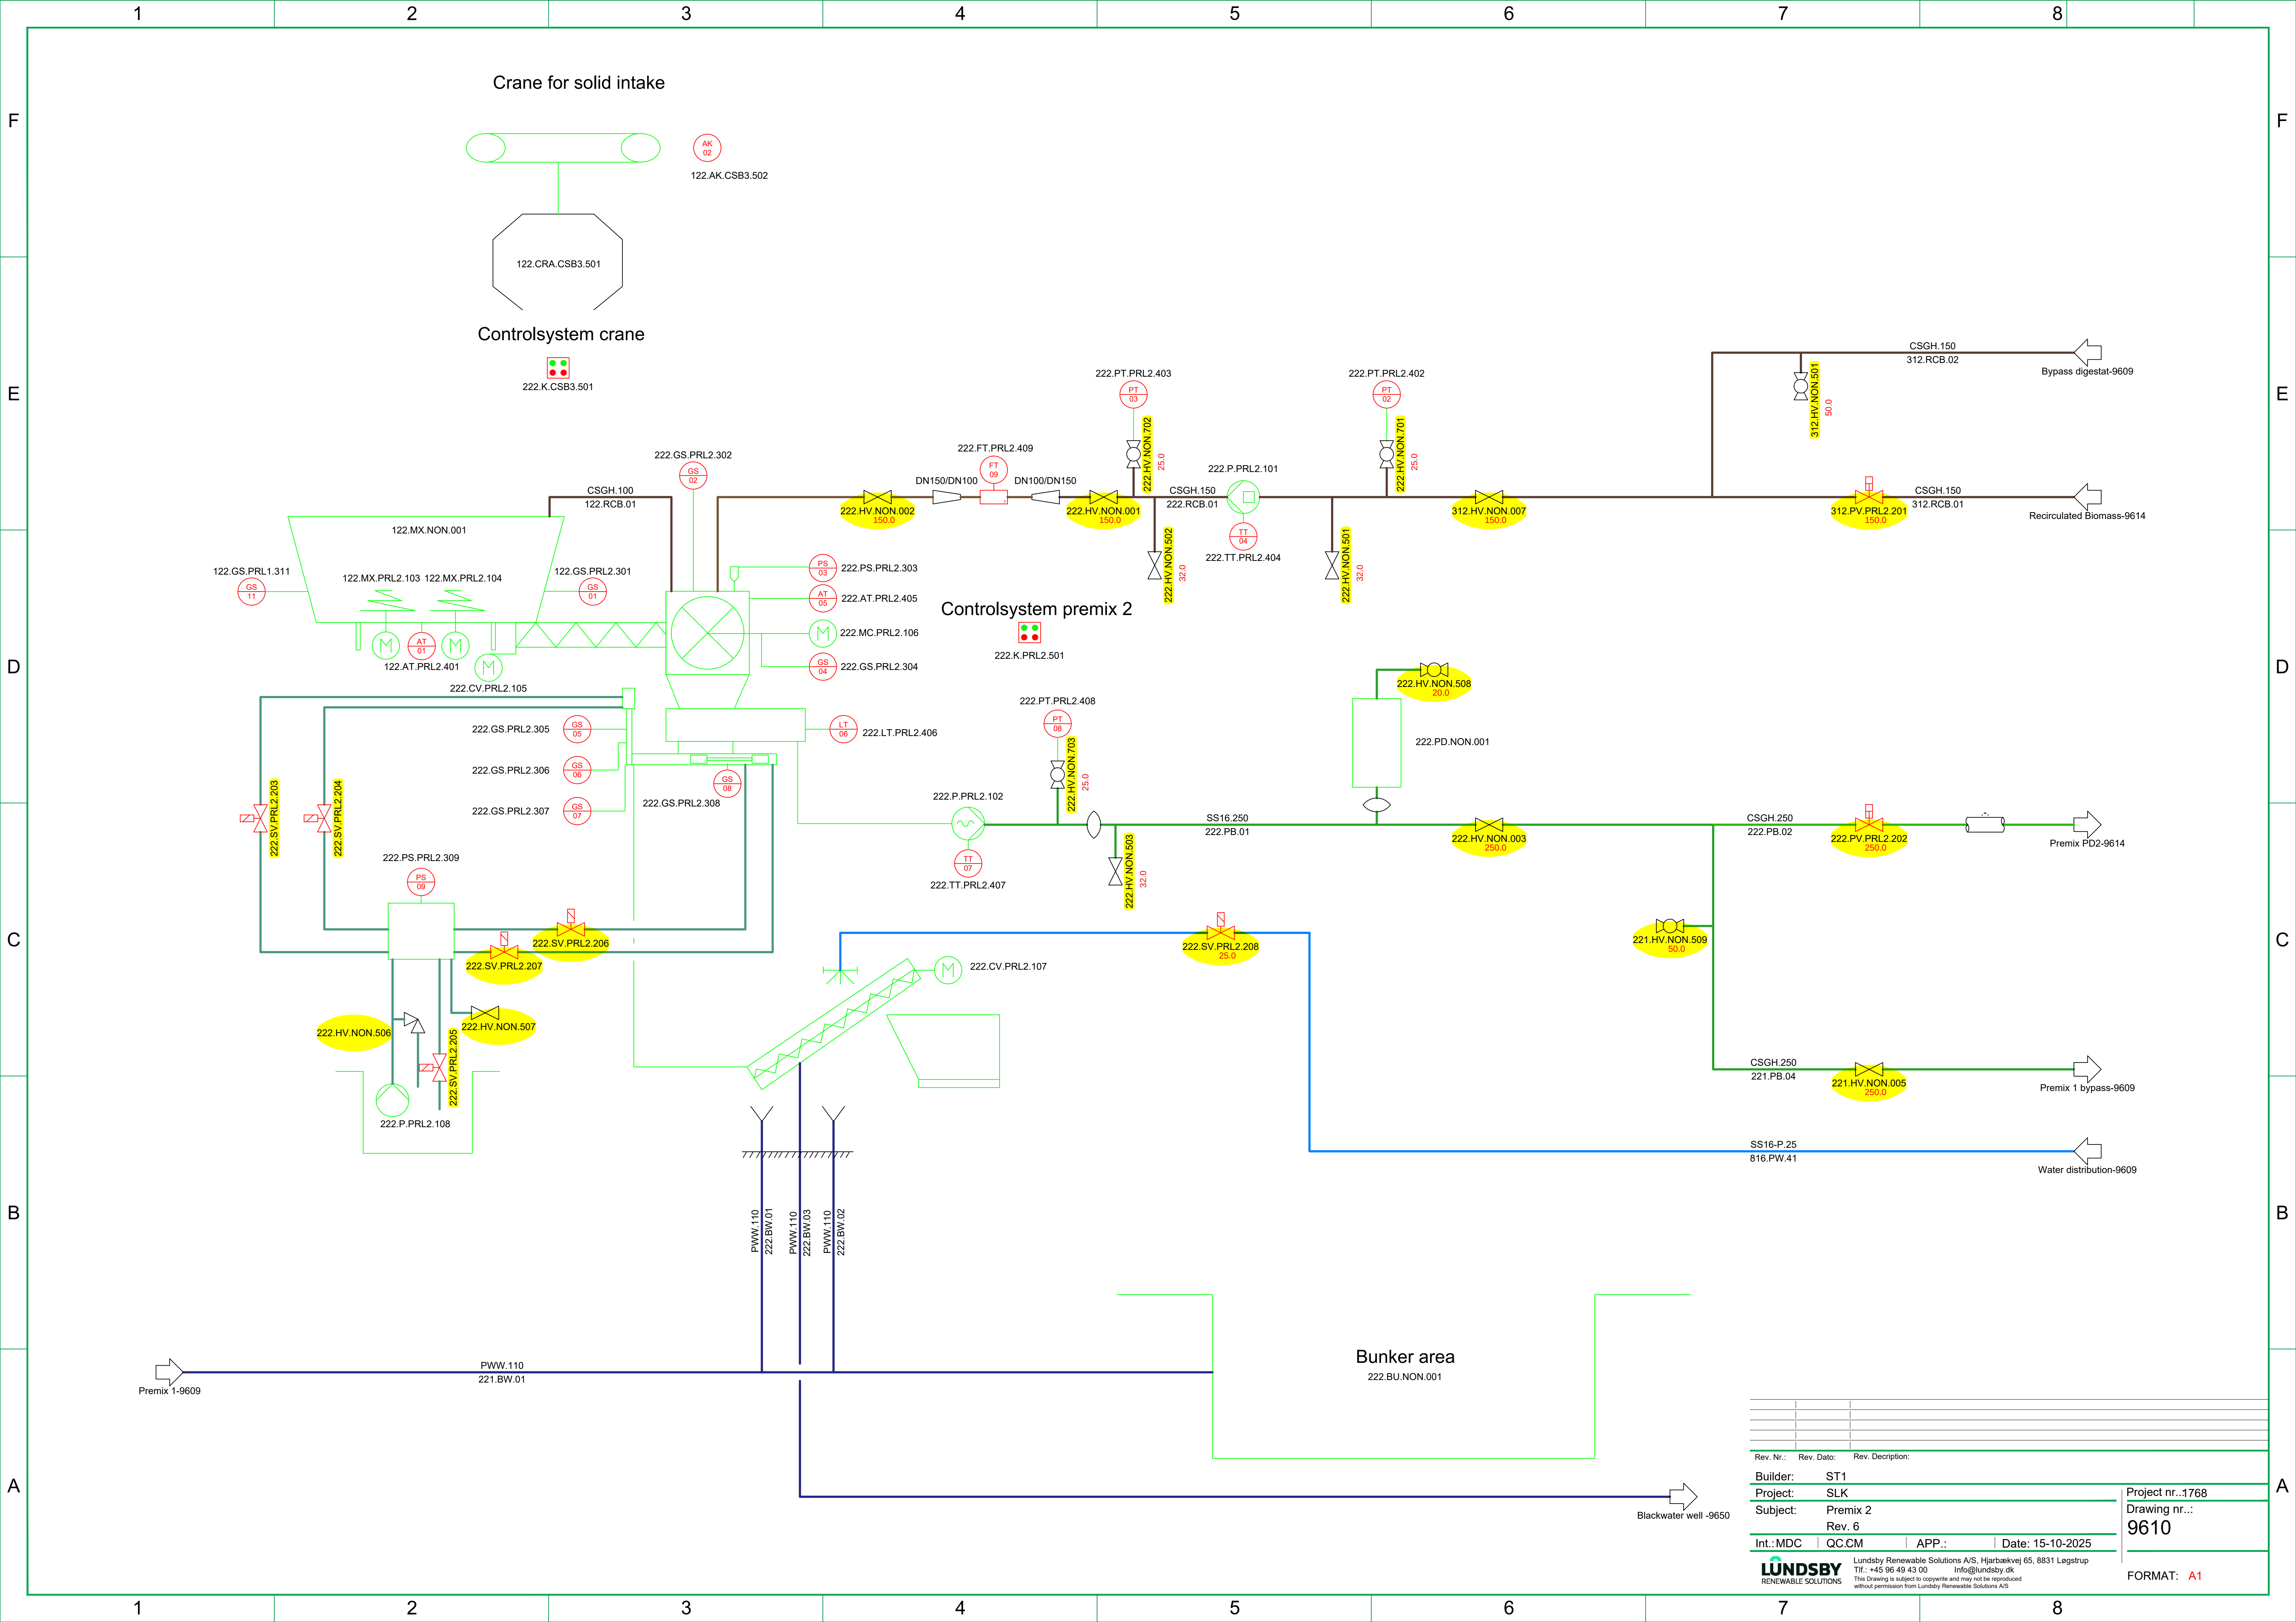


Rev. Nr.:	Rev. Dato:	Rev. Description:
Builder:	ST1	
Project:	SLK	
Subject:	Premix 2	
	Rev. 6	
Int.:MDC	QC.CM	APP.:
		Date: 15-10-2025
LUNDSBY RENEWABLE SOLUTIONS		
Lundsby Renewable Solutions A/S, Hjarbækvej 65, 8831 Løgstrup Tlf.: +45 96 49 43 00 Info@lundsby.dk This drawing is subject to copyright and may not be reproduced without permission from Lundsby Renewable Solutions A/S		
Project nr.:1768 Drawing nr.: 9610		FORMAT: A1

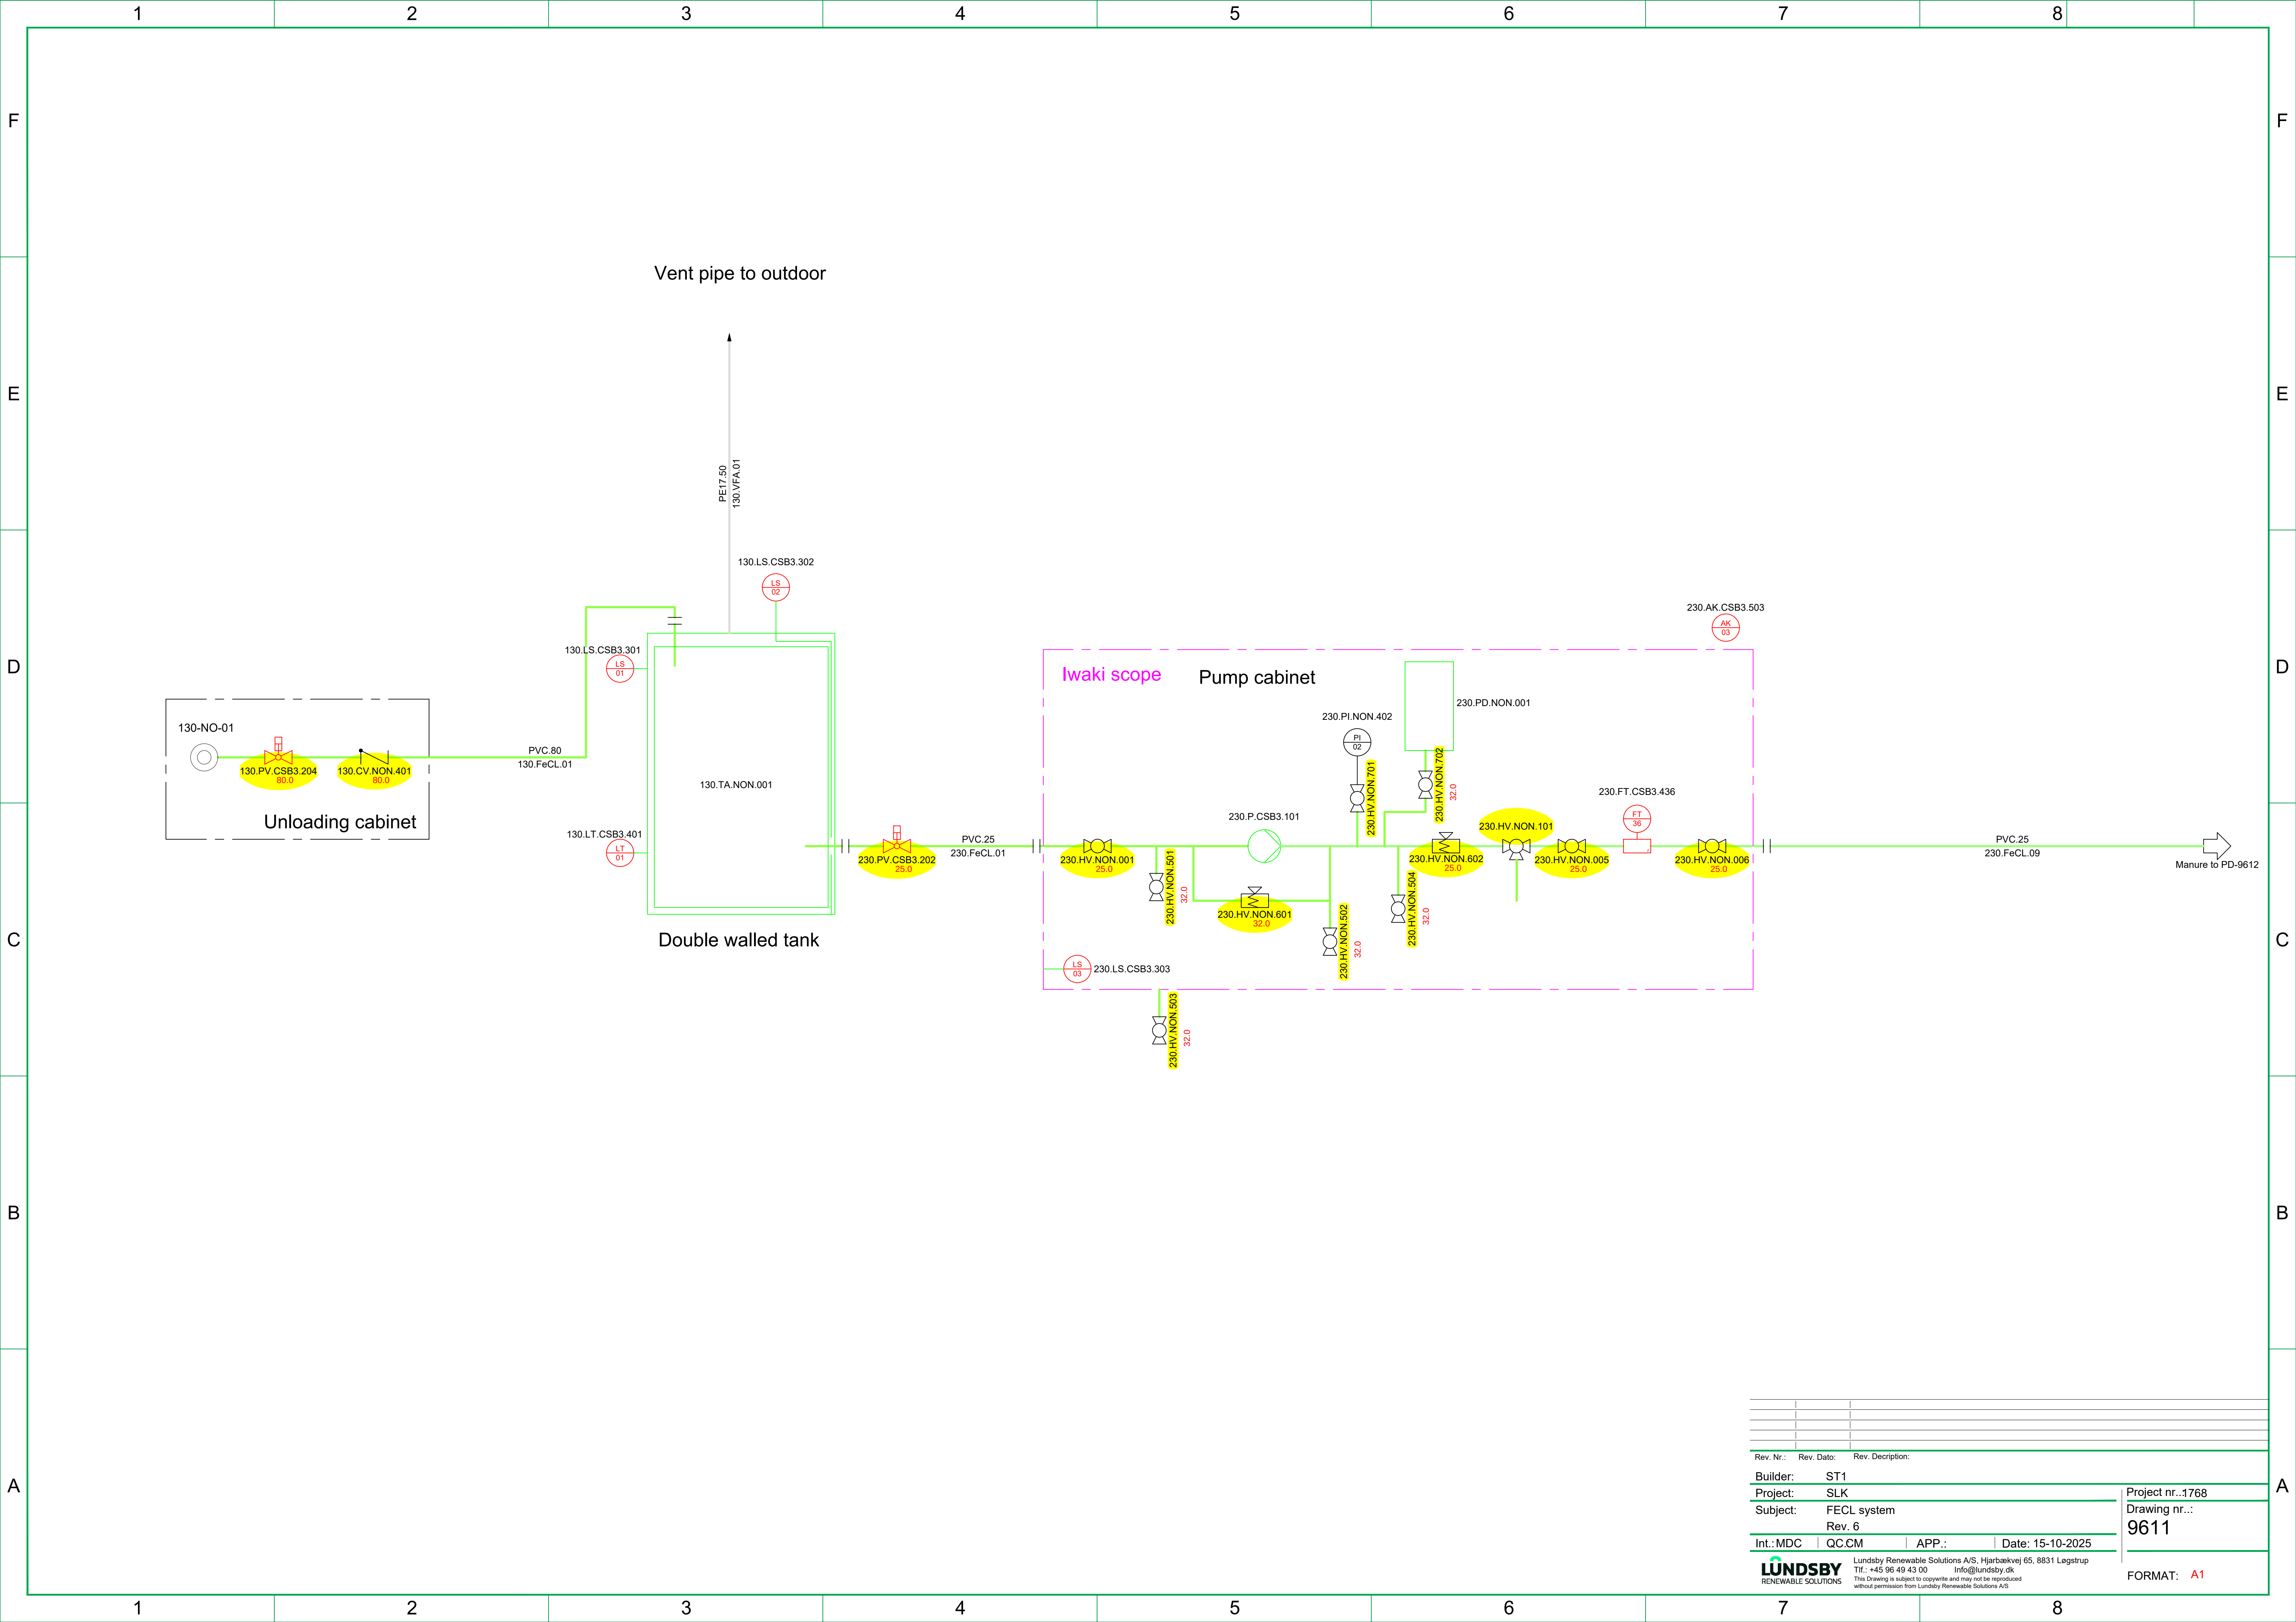


Rev. Nr.:	Rev. Dato:	Rev. Description:	
Builder:	ST1		
Project:	SLK		Project nr...1768
Subject:	FECL system		Drawing nr...: 9611
Rev. 6			
Int.:MDC	QC.CM	APP.:	Date: 15-10-2025
LUNDSBY RENEWABLE SOLUTIONS			Lundsby Renewable Solutions A/S, Hjarbækvej 65, 8831 Løgstrup Tlf.: +45 96 49 43 00 Info@lundsby.dk This Drawing is subject to copyright and may not be reproduced without permission from Lundsby Renewable Solutions A/S
			FORMAT: A1

Pumphouse 2

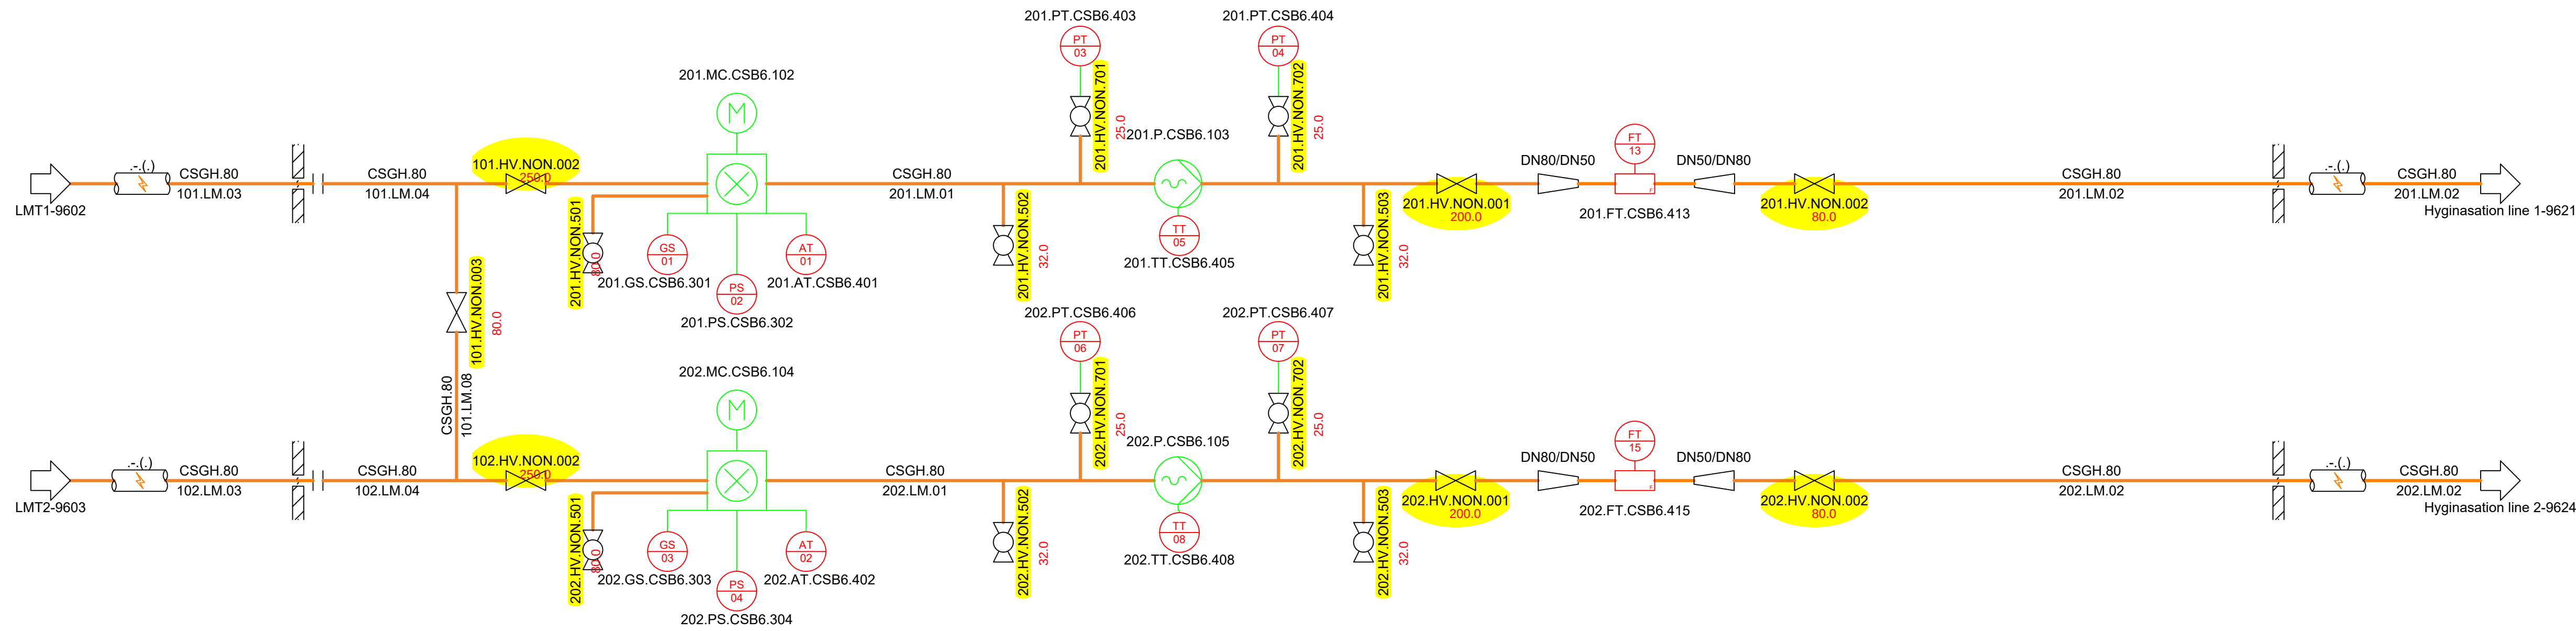



Tech
building

SB-building

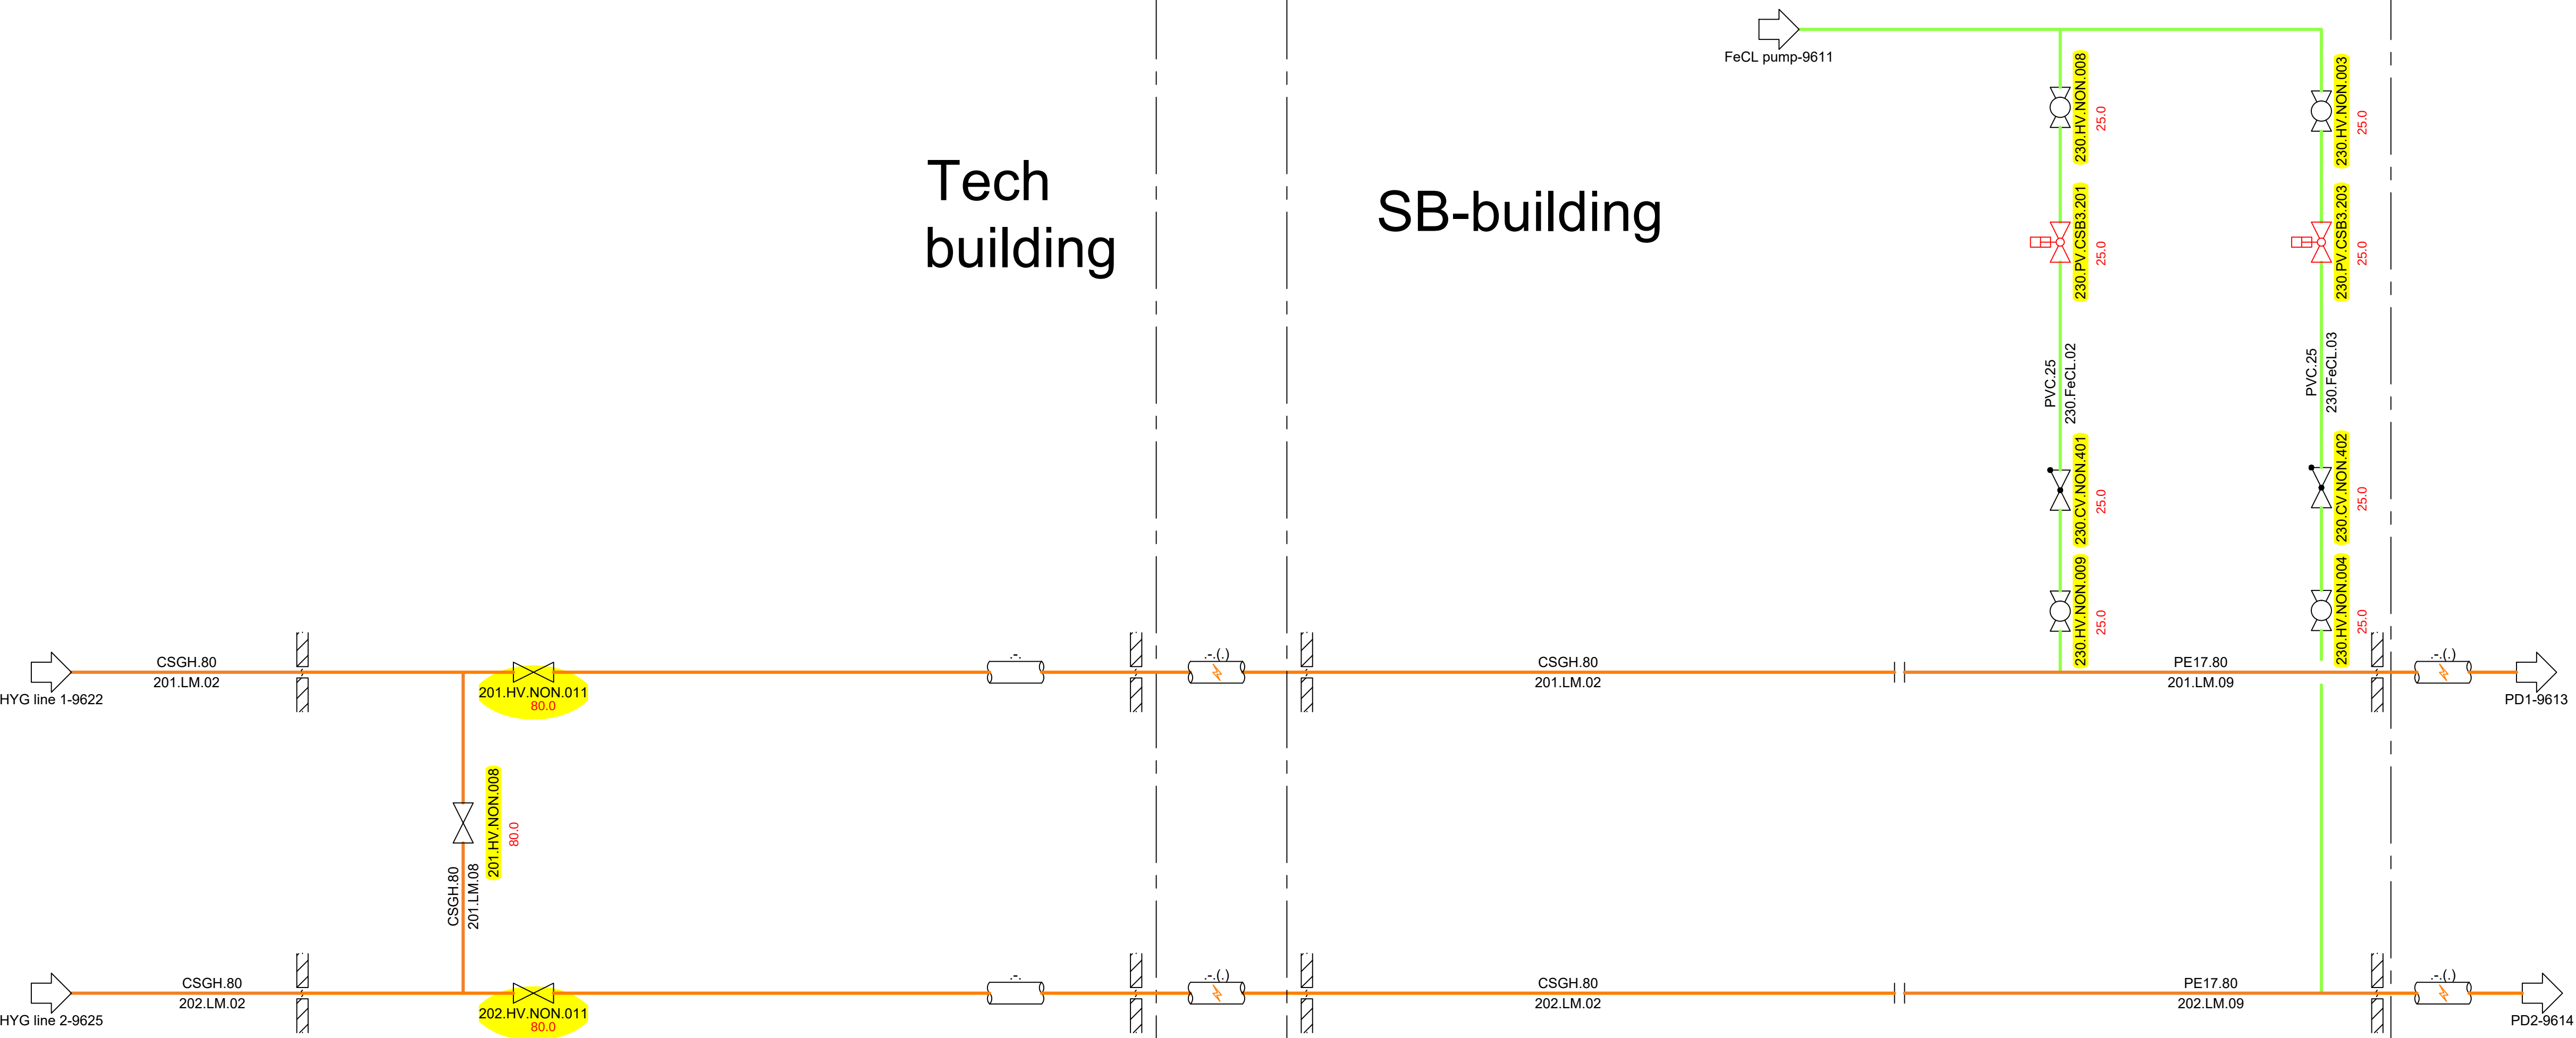


Rev. Nr.:	Rev. Dato:	Rev. Description:
Builder:	ST1	
Project:	SLK	
Subject:	Liquid manure pump	
Rev. 6		
Int.:MDC	QC.CM	APP.:
Date: 15-10-2025		
LUNDSBY RENEWABLE SOLUTIONS		
Lundsby Renewable Solutions A/S, Hjarbækvej 65, 8831 Lægstrup Tlf.: +45 96 49 43 00 Info@lundsby.dk This Drawing is subject to copyright and may not be reproduced without permission from Lundsby Renewable Solutions A/S		
Project nr.:1768 Drawing nr.: 9612		
FORMAT: A1		

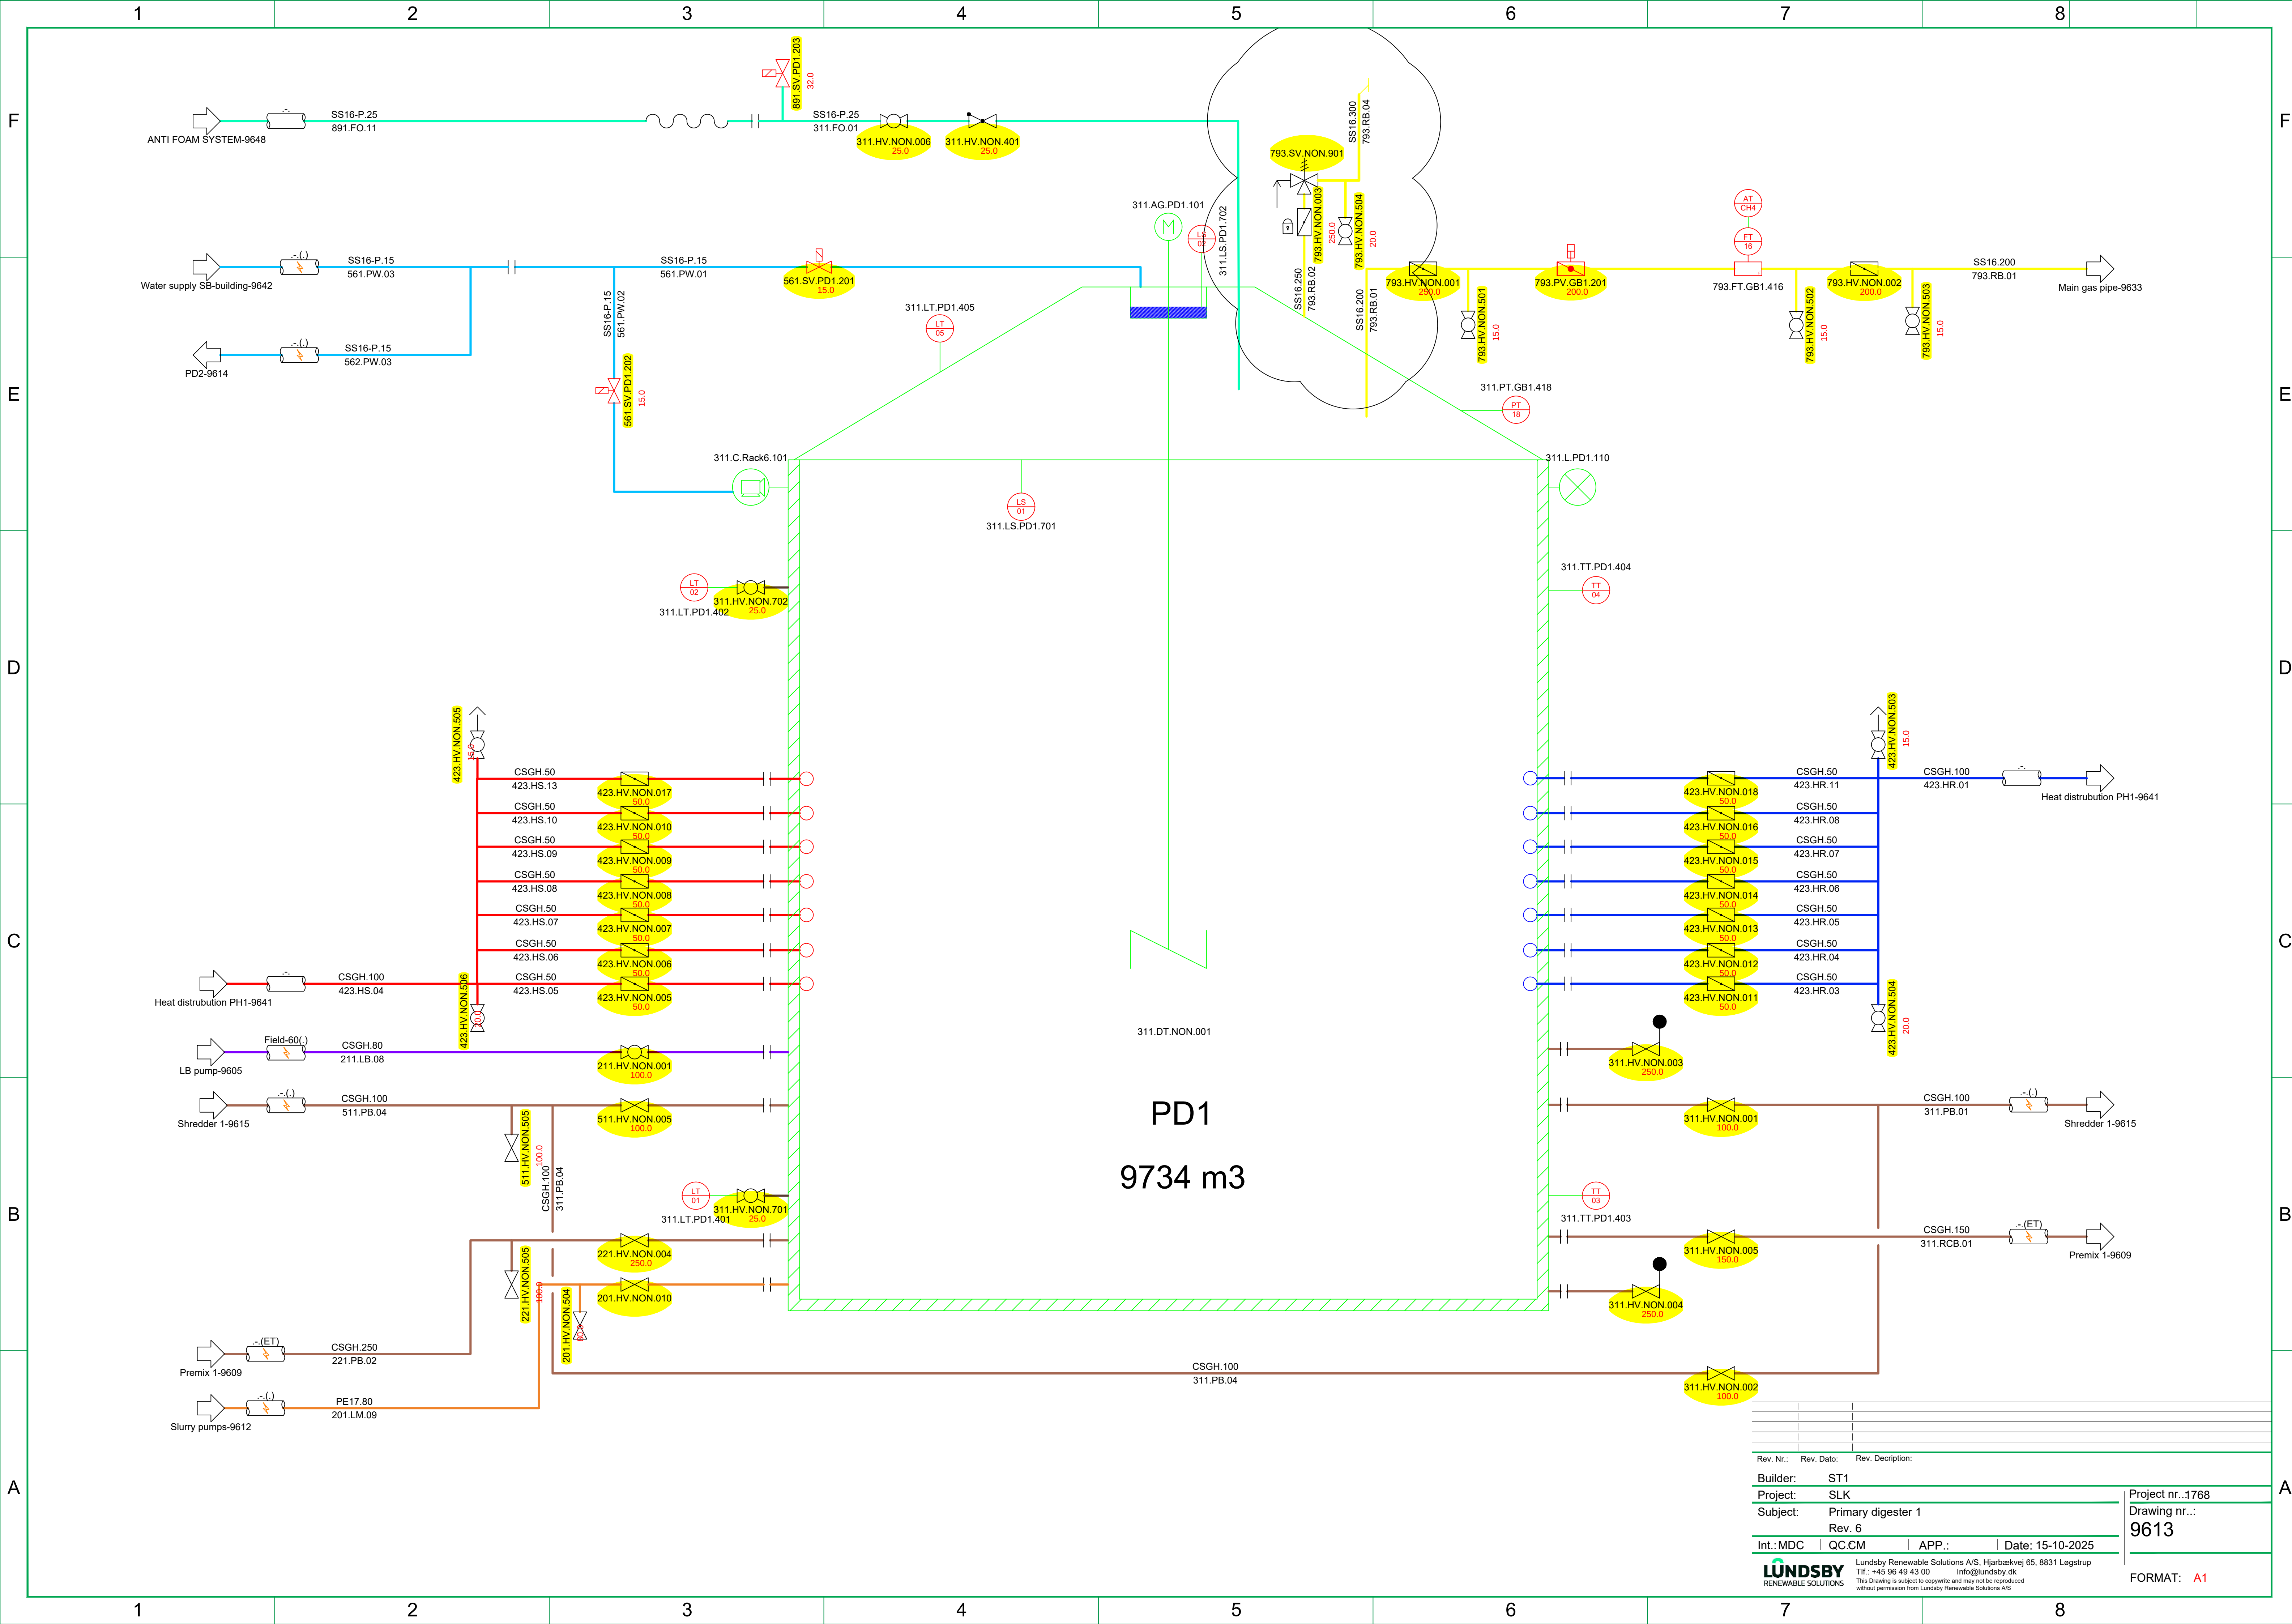


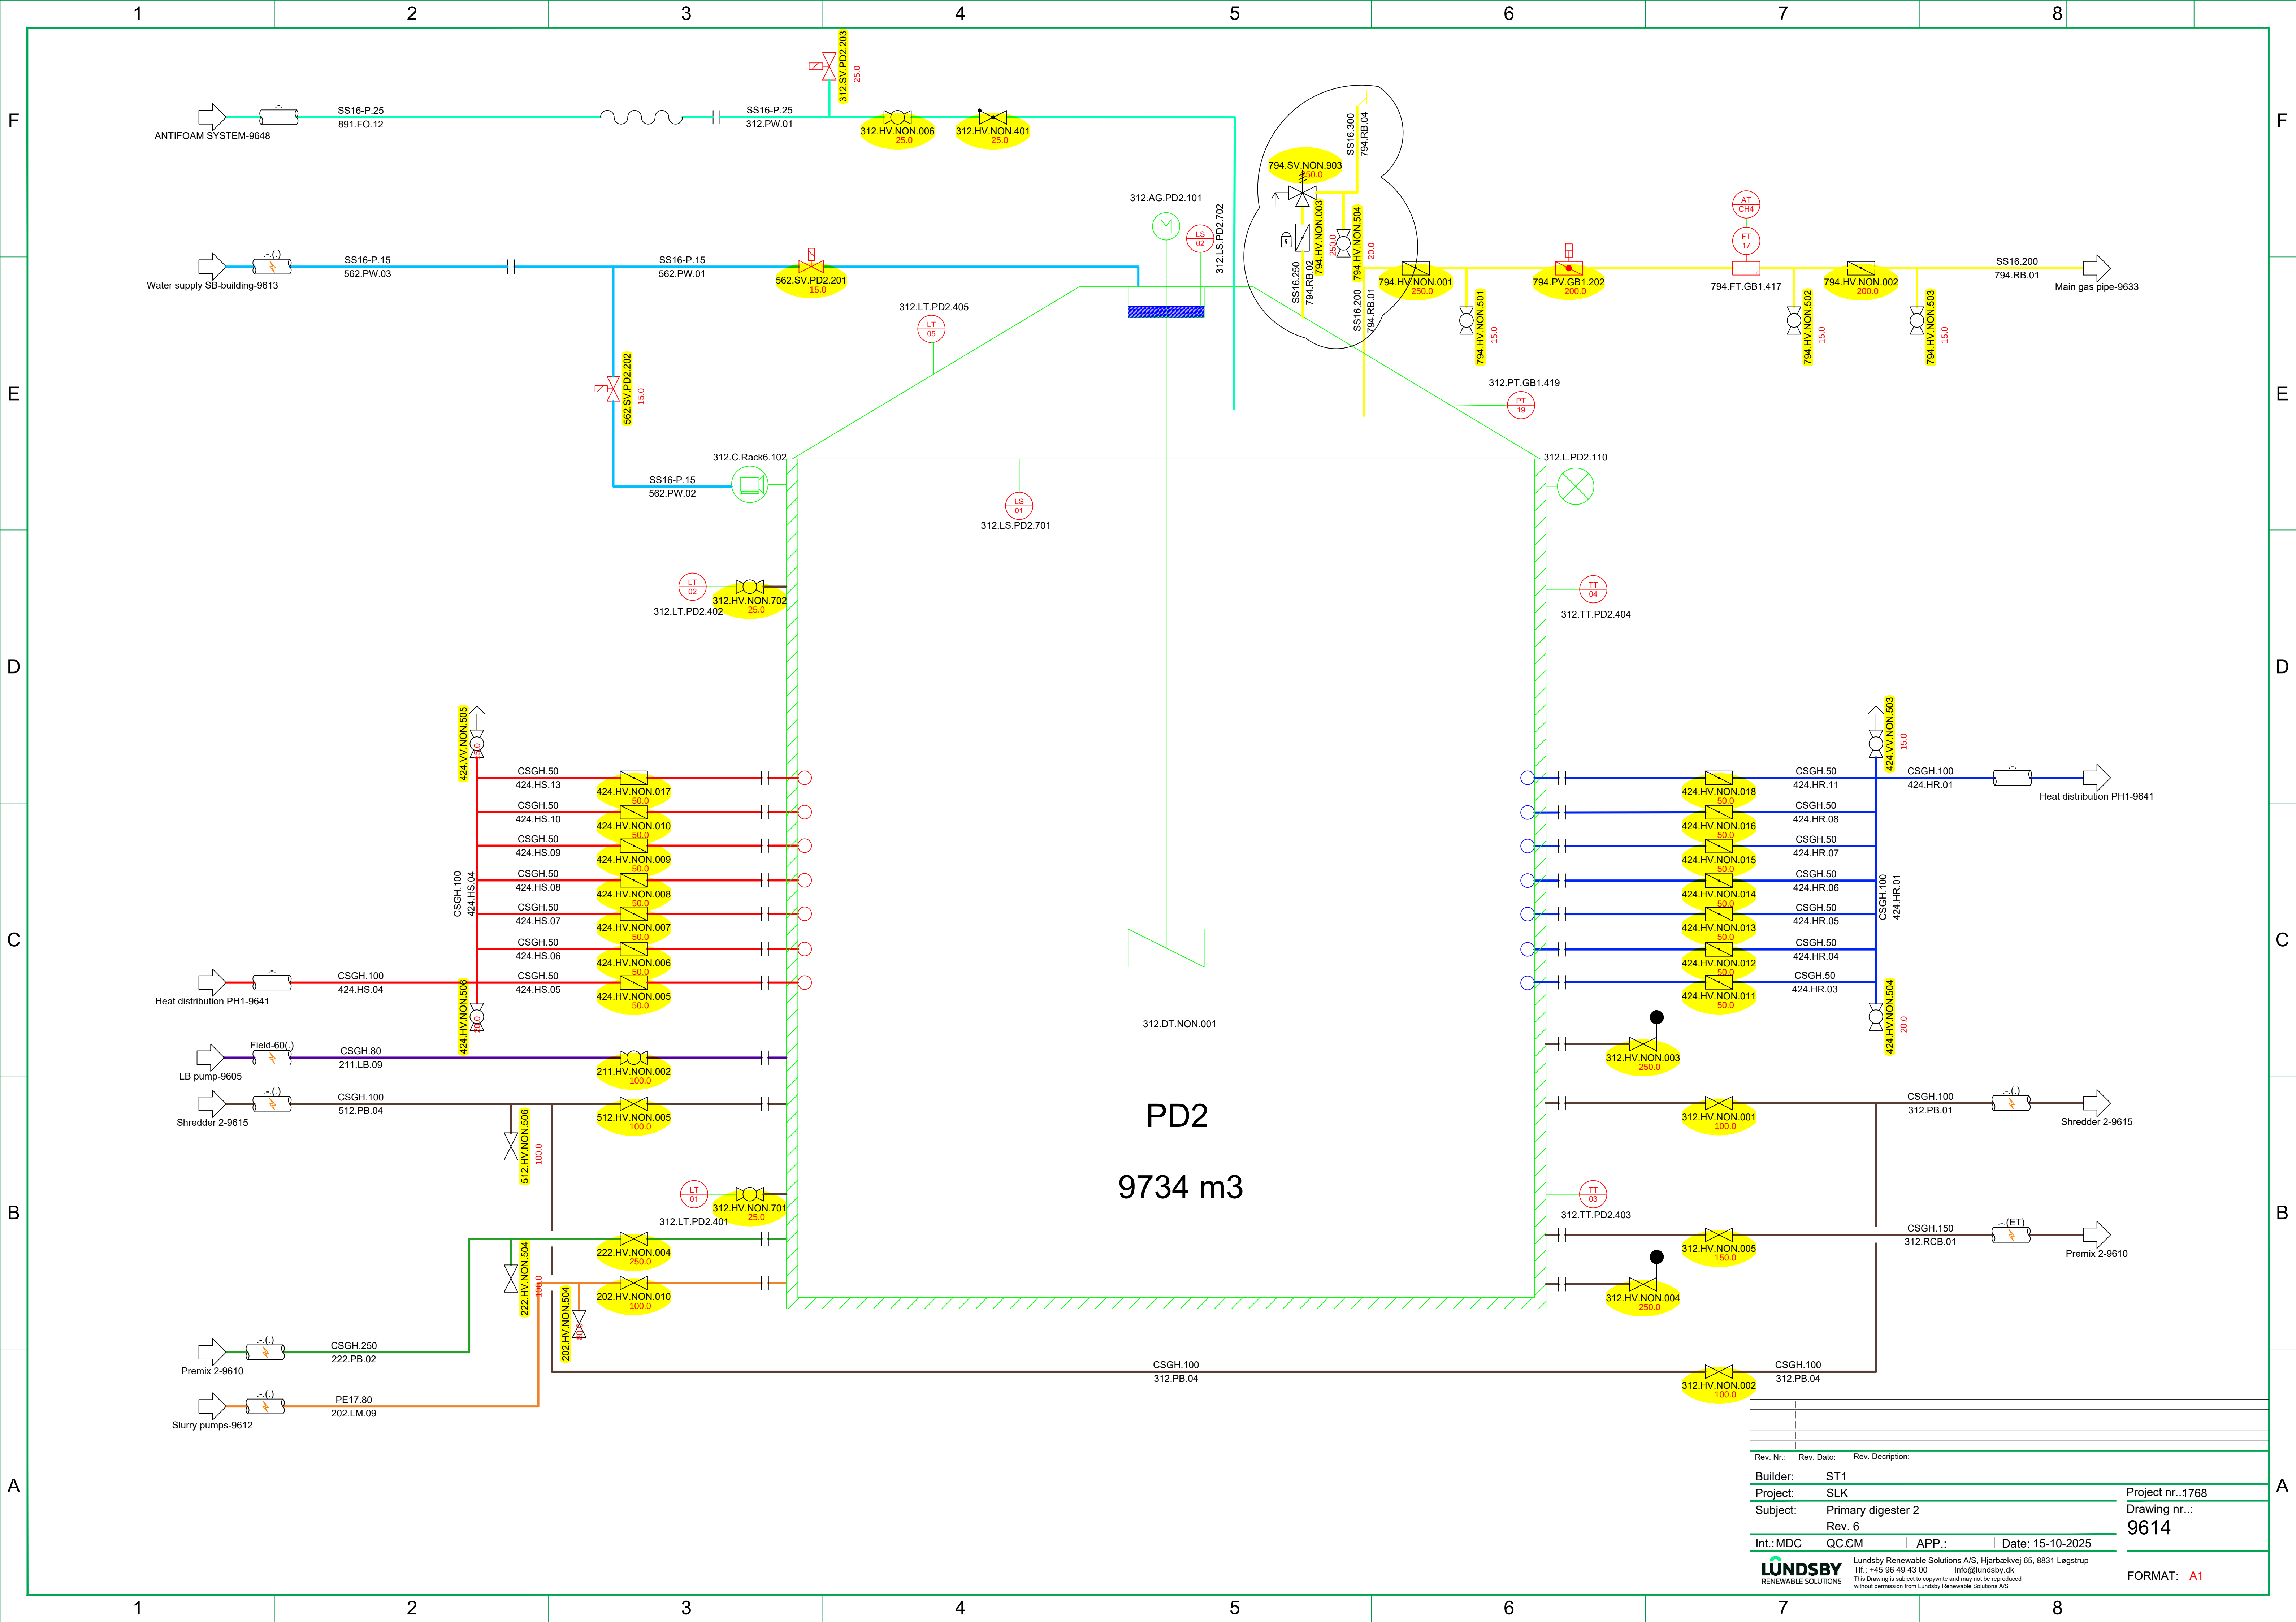

Rev. Nr.:	Rev. Dato:	Rev. Description:	
Builder:	ST1		
Project:	SLK		
Subject:	Primary digester 2		
	Rev. 6		
Int.: MDC	QC.CM	APP.:	Date: 15-10-2025
LUNDSBY RENEWABLE SOLUTIONS			Lundsby Renewable Solutions A/S, Hjarbækvej 65, 8831 Lægstrup Tlf.: +45 96 49 43 00 Info@lundsby.dk This drawing is subject to copyright and may not be reproduced without permission from Lundsby Renewable Solutions A/S
Project nr.: 1768 Drawing nr.: 9614			FORMAT: A1

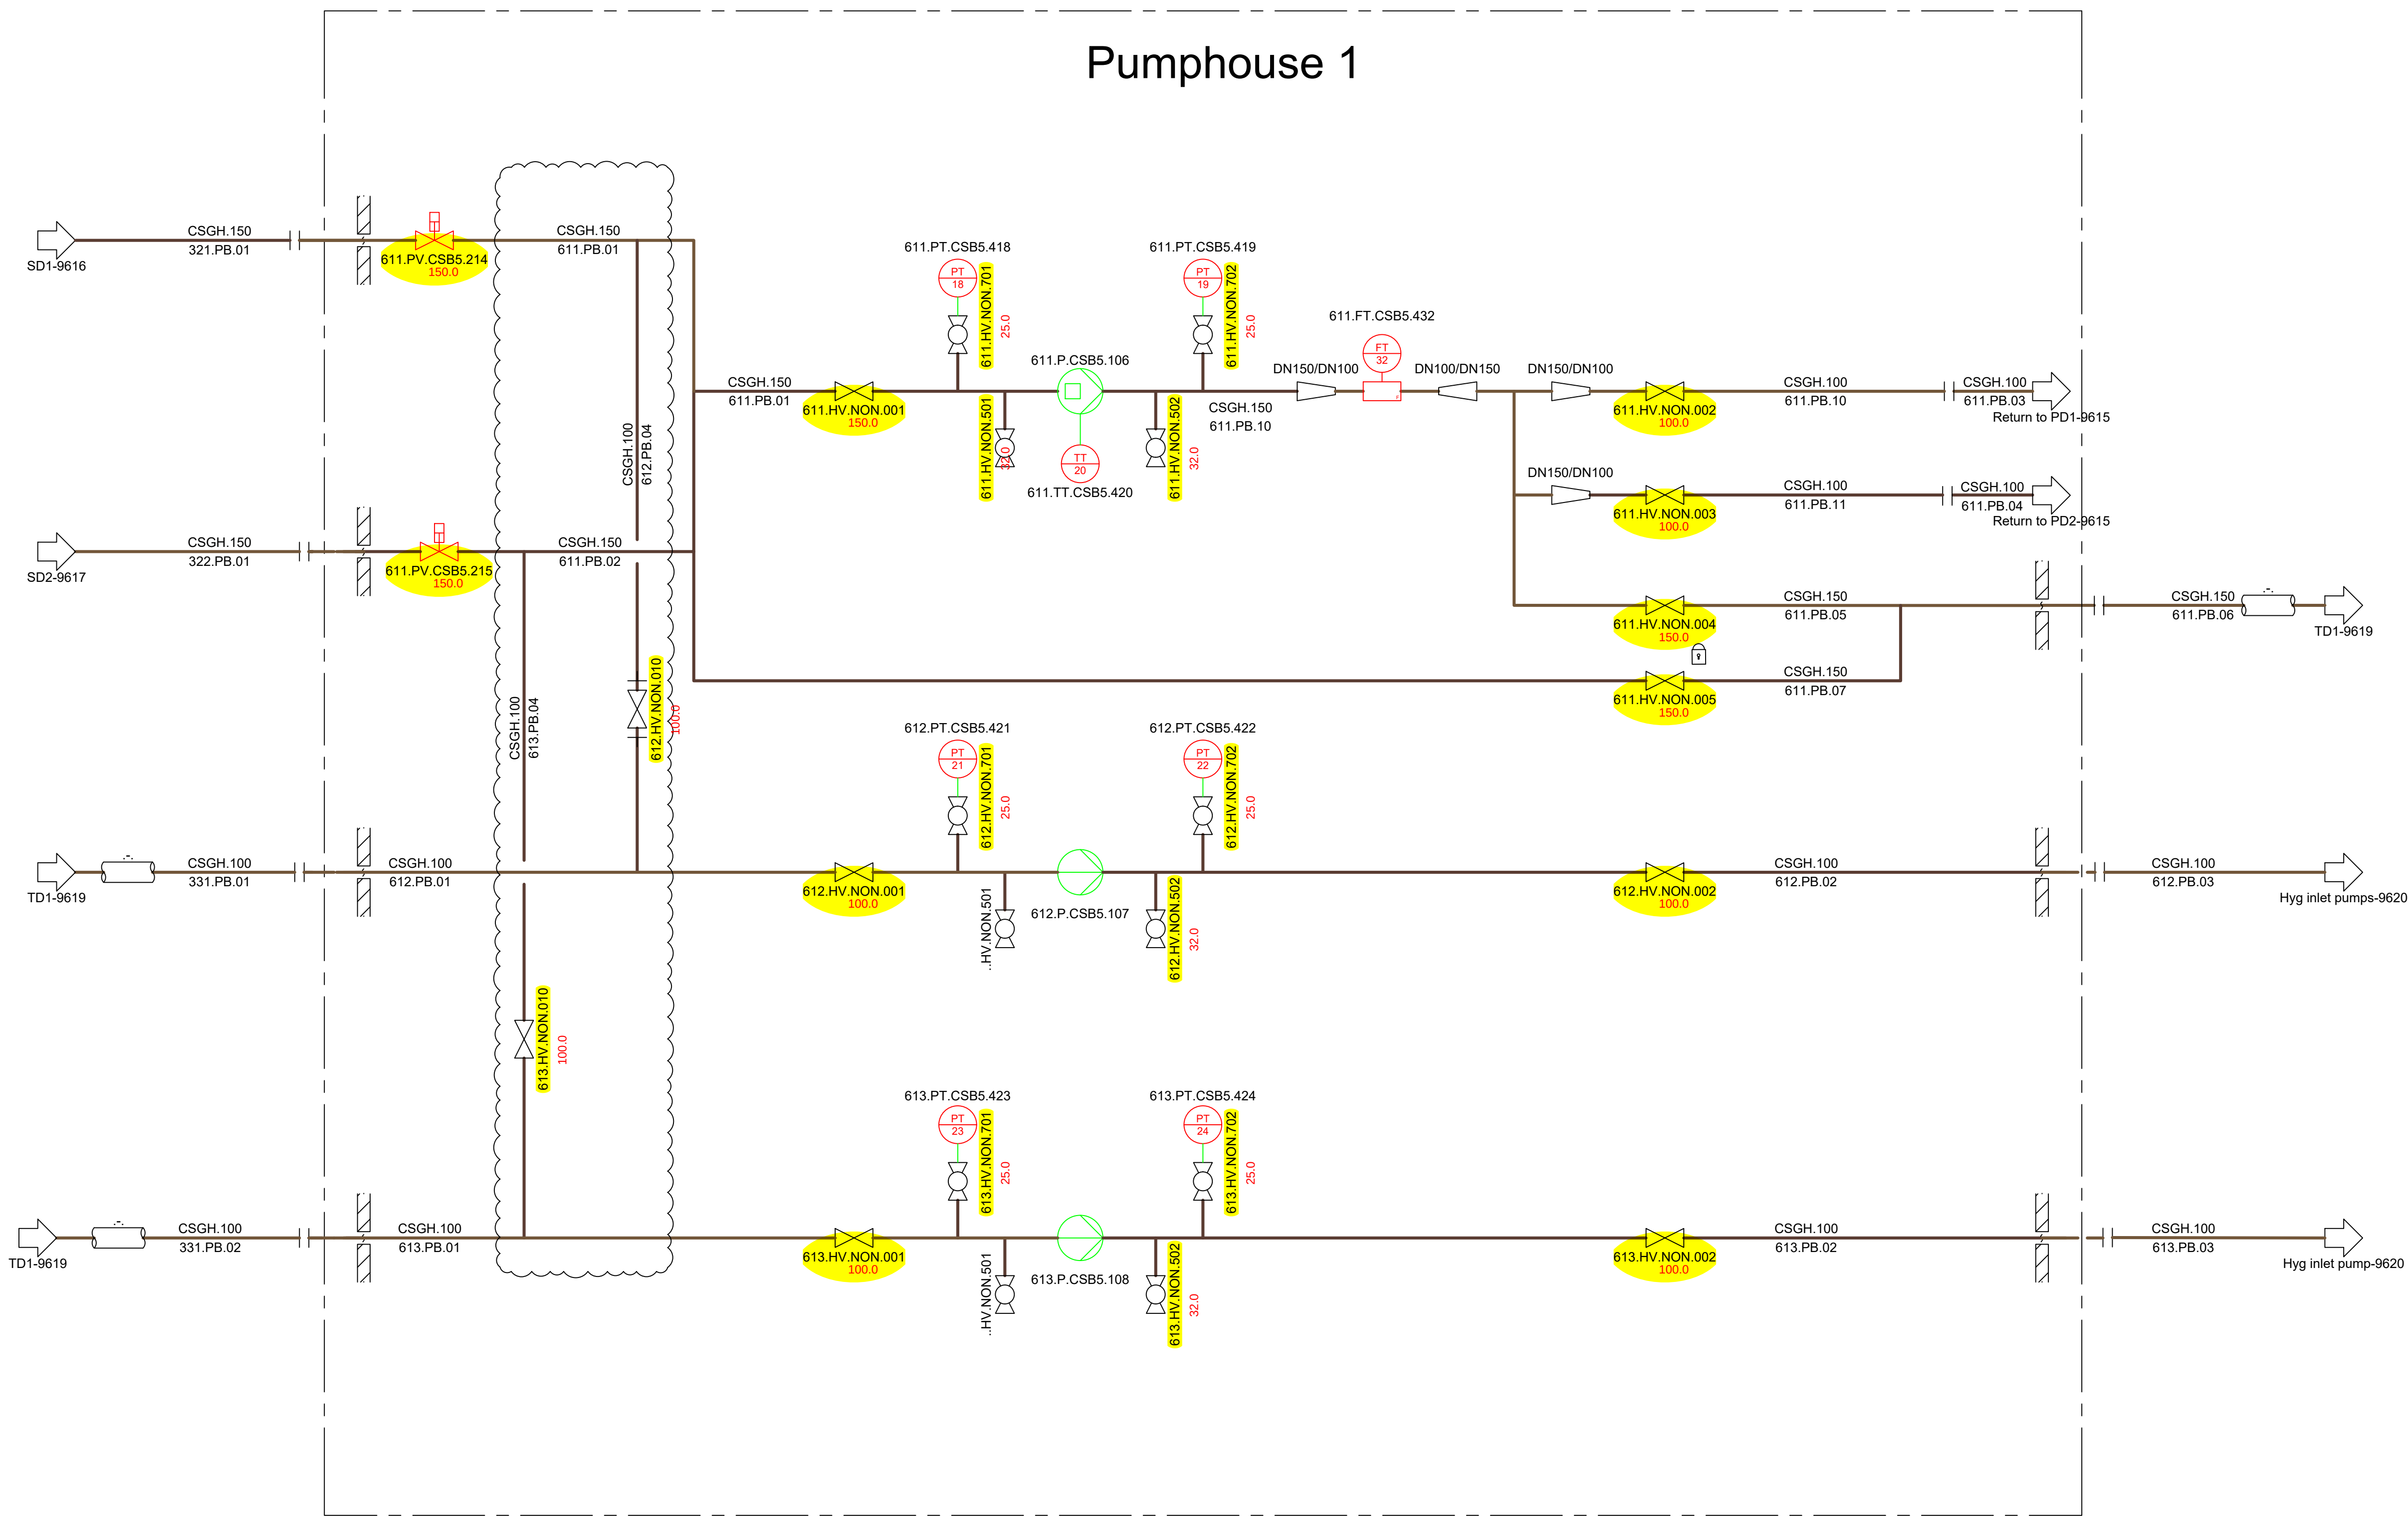


Rev. Nr.:	Rev. Dato:	Rev. Description:	
Builder:	ST1		
Project:	SLK		
Subject:	Procces pumps		
	Rev. 6		
Int.:MDC	QC.CM	APP.:	Date: 15-10-2025
LUNDSBY RENEWABLE SOLUTIONS			Lundsby Renewable Solutions A/S, Hjarbækvej 65, 8831 Løgstrup Tlf.: +45 96 49 43 00 Info@lundsby.dk This Drawing is subject to copyright and may not be reproduced without permission from Lundsby Renewable Solutions A/S
Project nr.:1768 Drawing nr.: 9618			FORMAT: A1

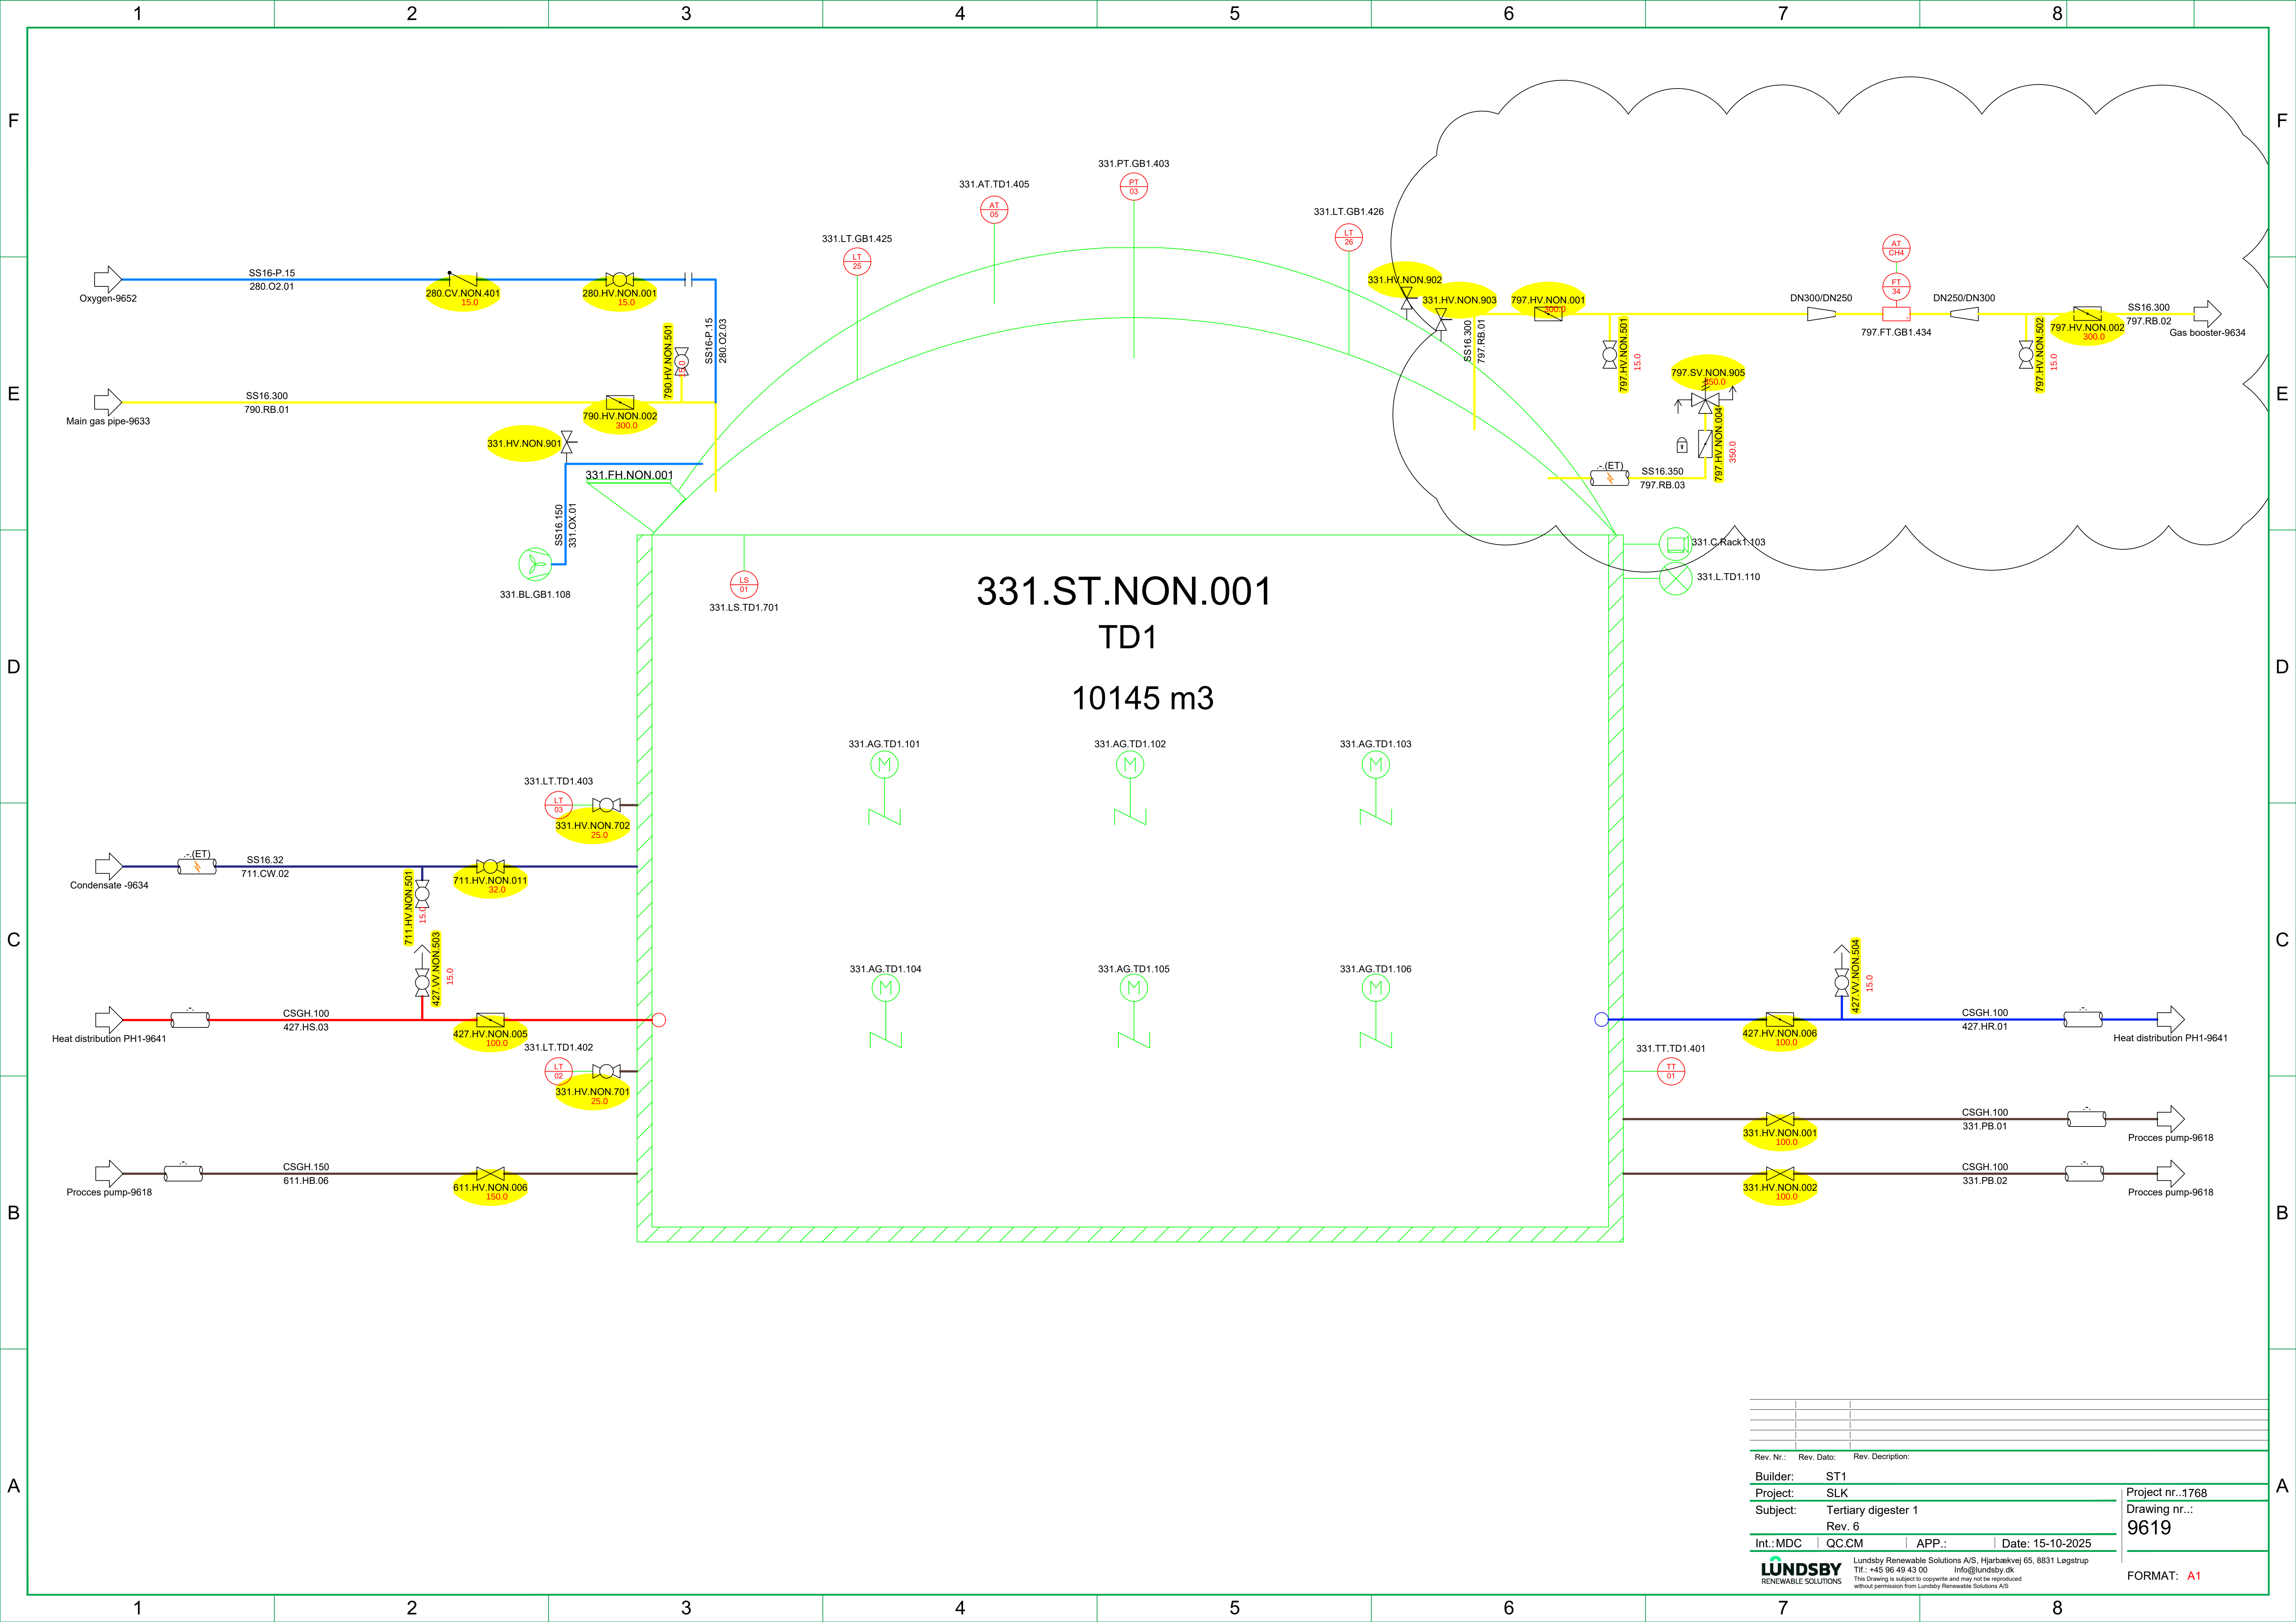


Tech Building


Inlet pumps

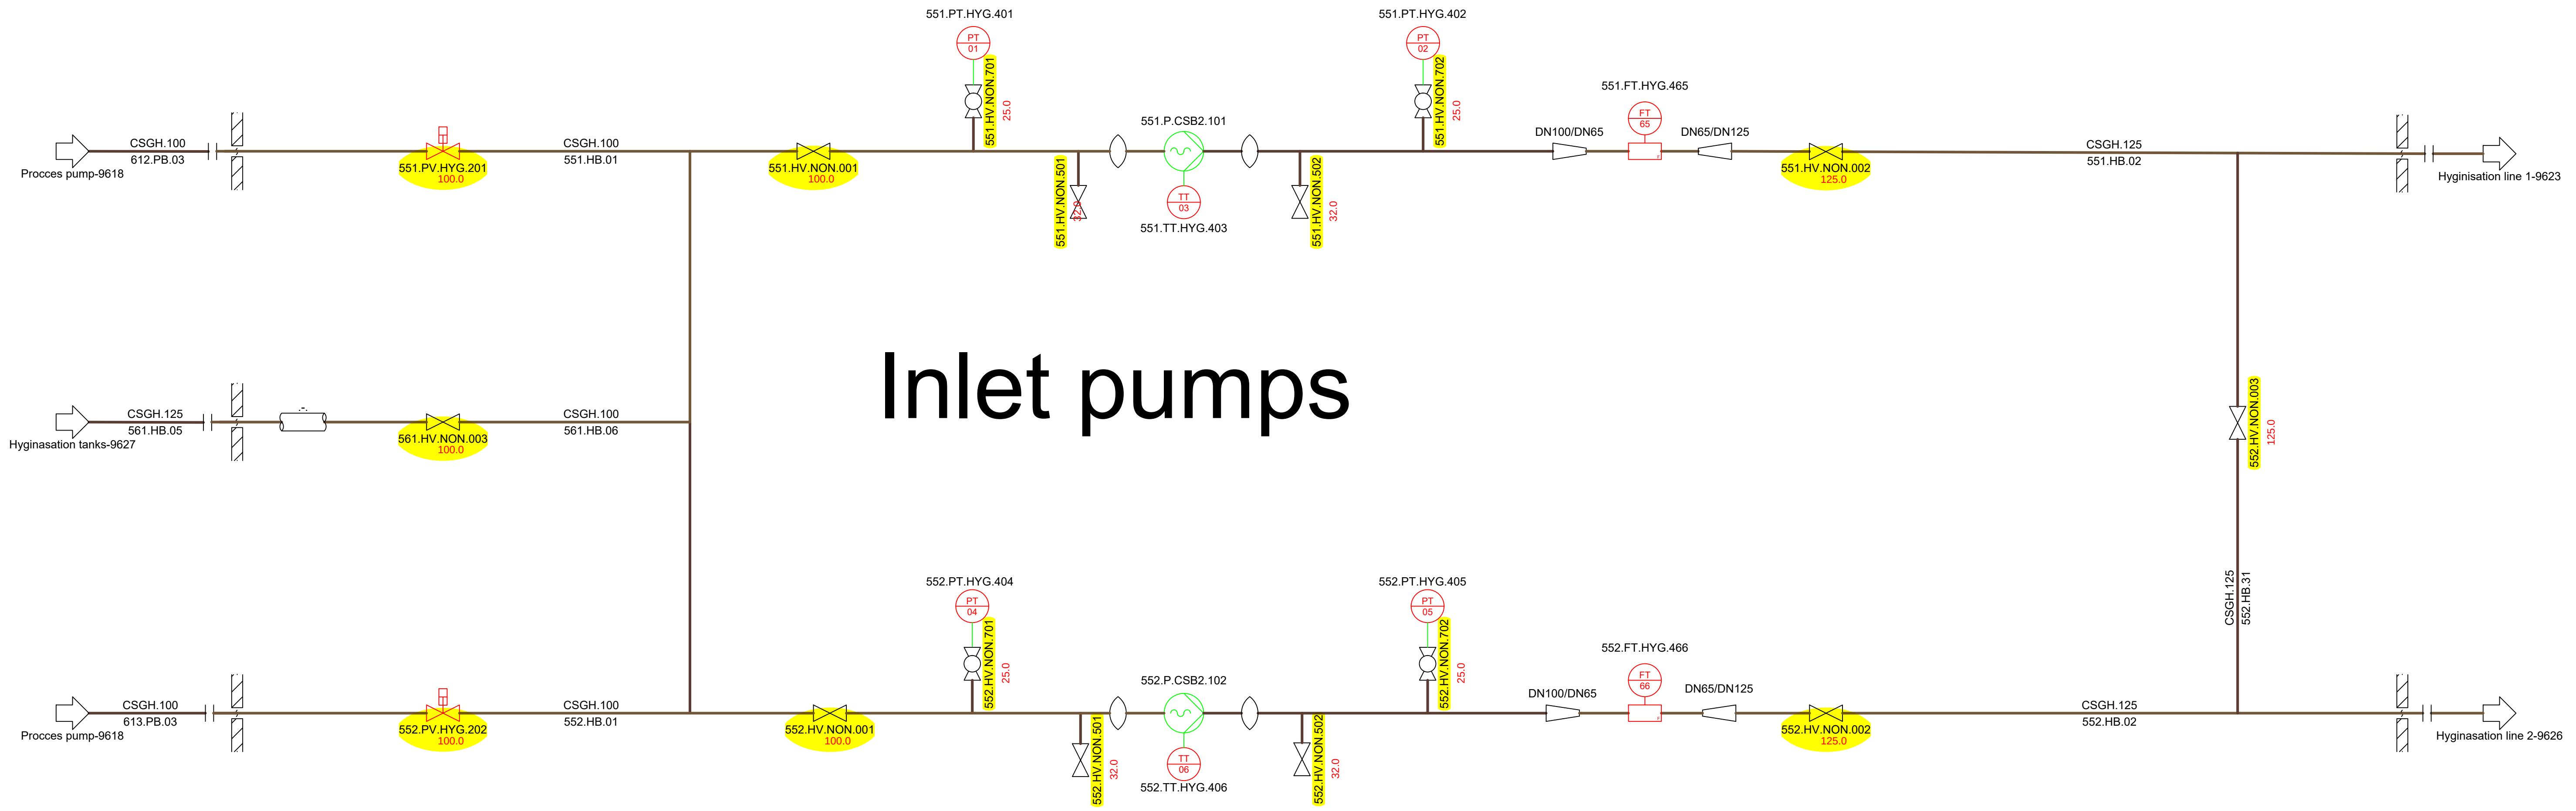



Rev. Nr.:	Rev. Dato:	Rev. Description:	
Builder:	ST1		
Project:	SLK		
Subject:	Hyginisation inlet pumps		
	Rev. 6		
Int.:MDC	QC:CM	APP.:	Date: 15-10-2025
LUNDSBY RENEWABLE SOLUTIONS			Lundsby Renewable Solutions A/S, Hjarbækvej 65, 8831 Løgstrup Tlf.: +45 96 49 43 00 Info@lundsby.dk This Drawing is subject to copyright and may not be reproduced without permission from Lundsby Renewable Solutions A/S
			Project nr.:1768 Drawing nr.: 9620 FORMAT: A1

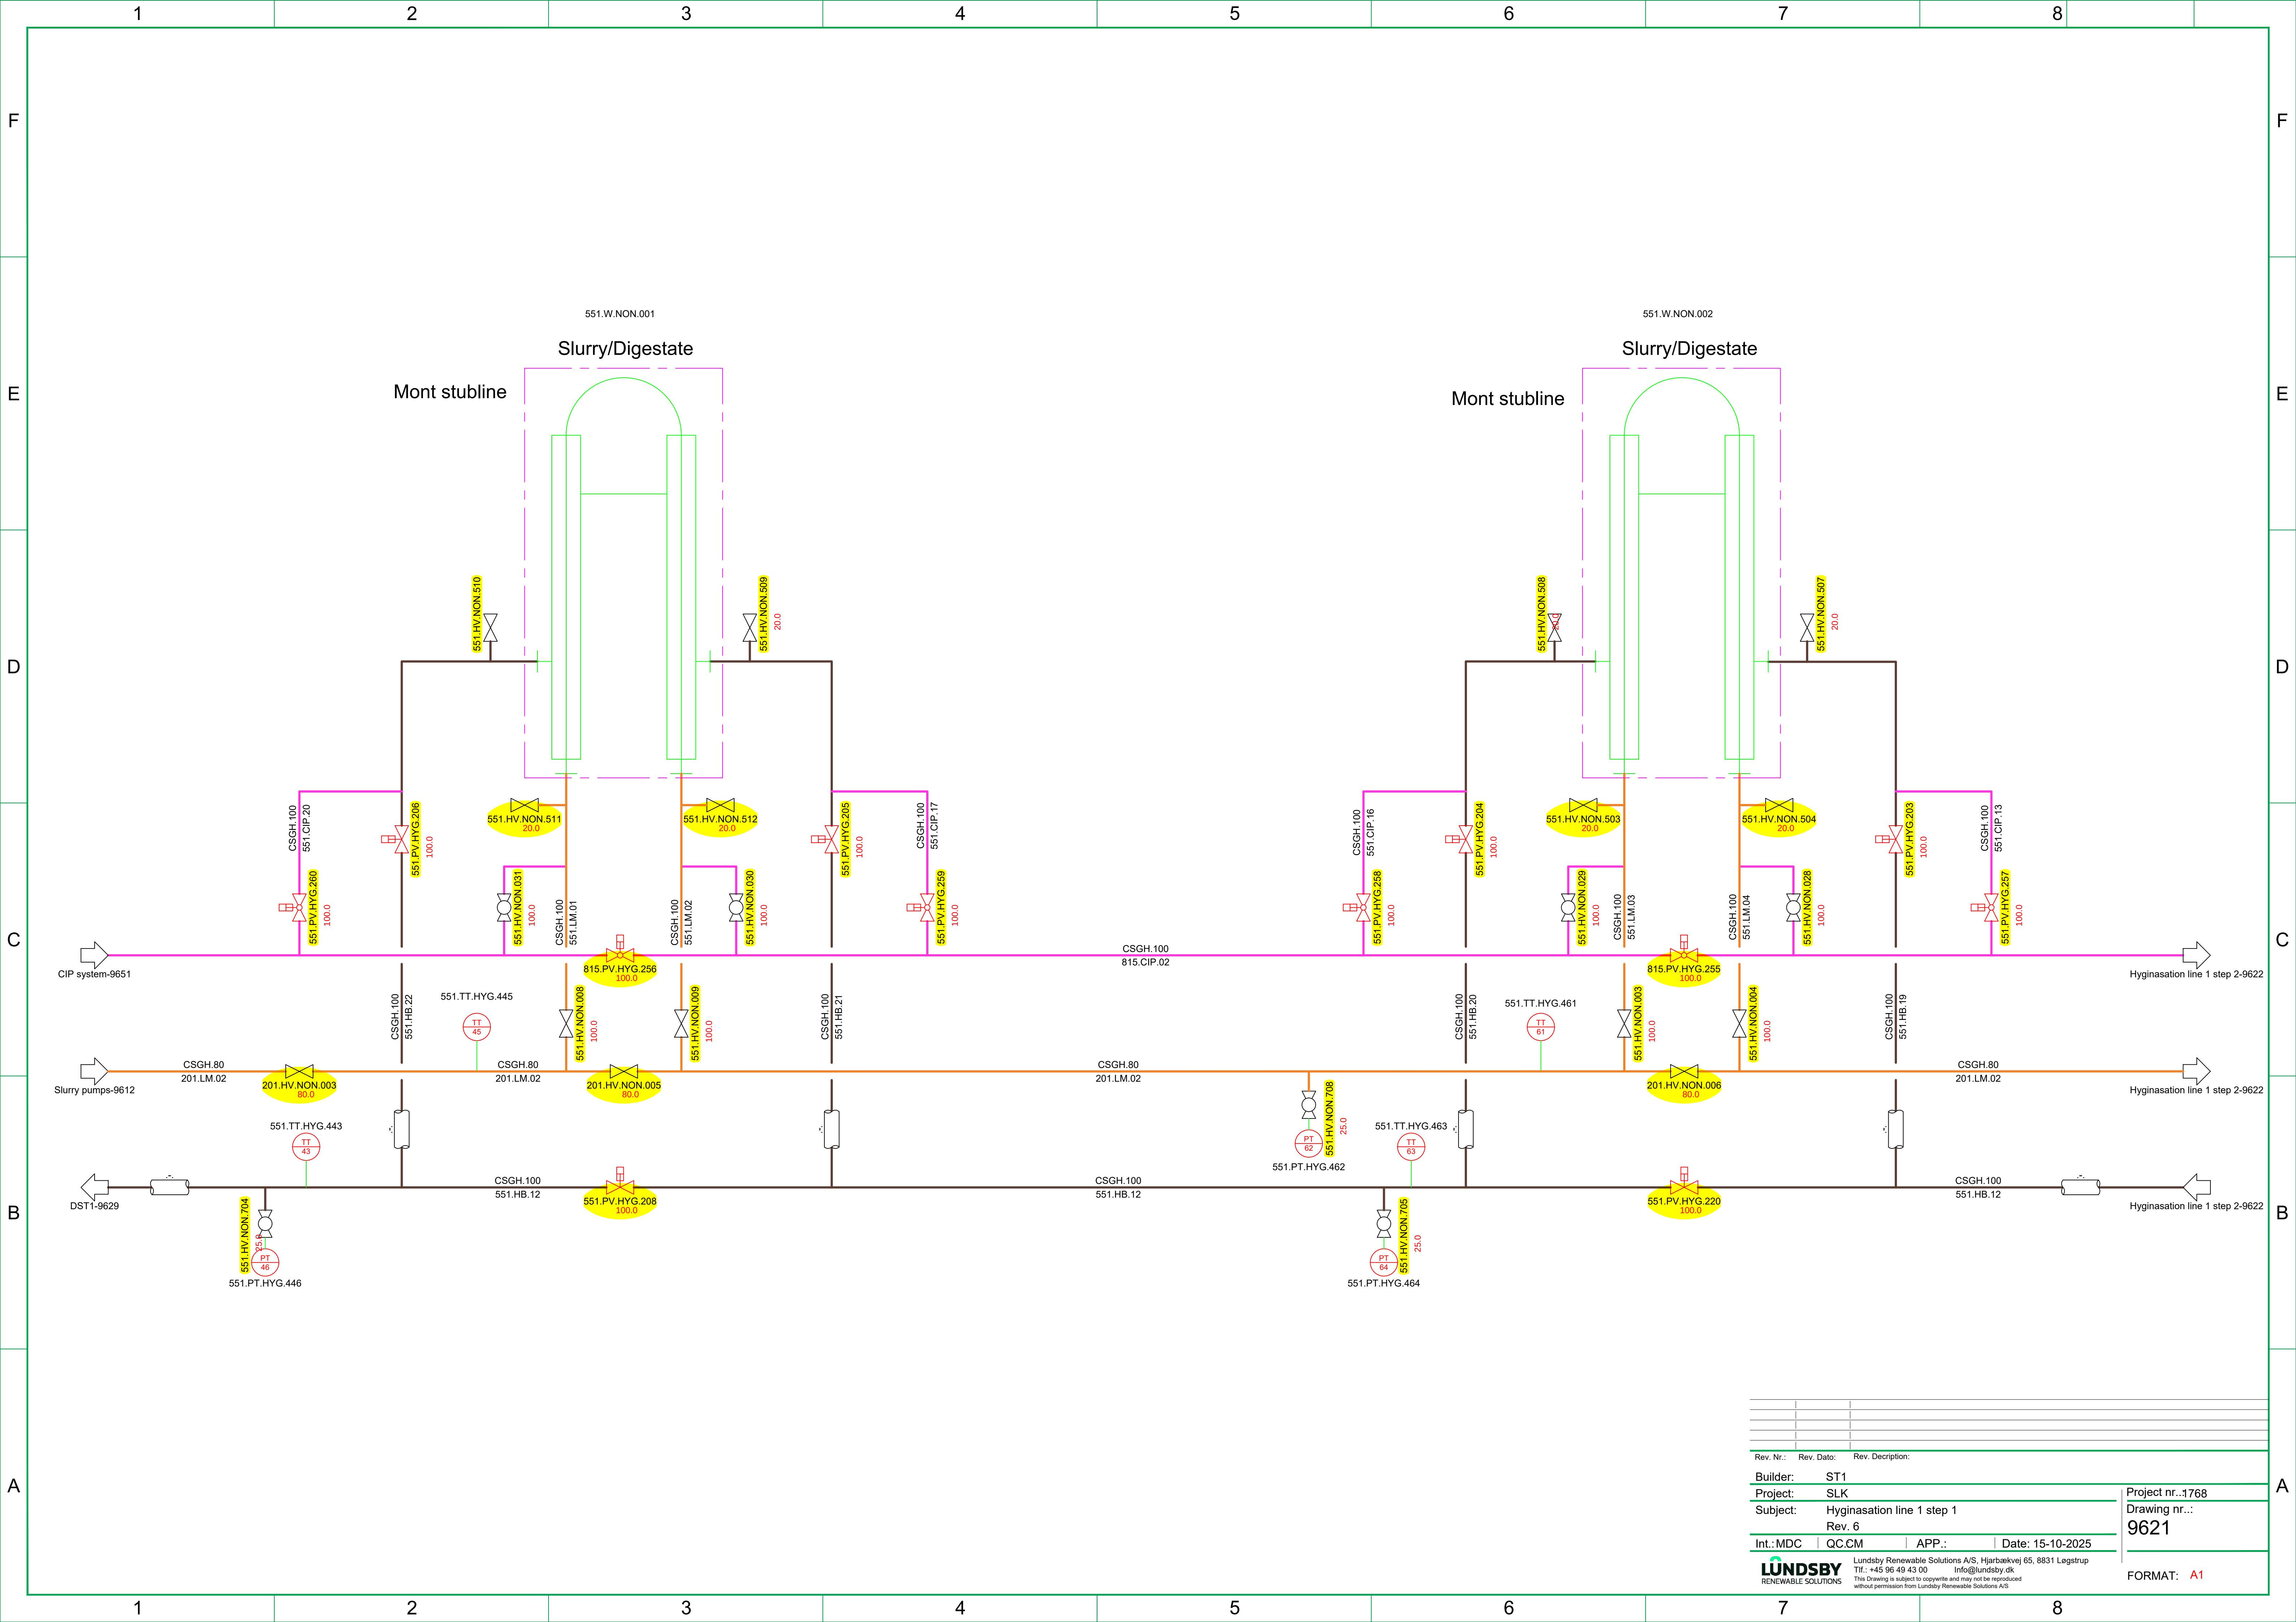



Rev. Nr.:	Rev. Dato:	Rev. Description:
Builder:	ST1	
Project:	SLK	
Subject:	Hyginasation line 1 step 1	
Rev. 6		
Int.: MDC	QC:CM	APP.: Date: 15-10-2025
LUNDSBY RENEWABLE SOLUTIONS		
Lundsby Renewable Solutions A/S, Hjarbækvej 65, 8831 Løgstrup Tlf.: +45 96 49 43 00 Info@lundsby.dk This Drawing is subject to copyright and may not be reproduced without permission from Lundsby Renewable Solutions A/S		
Project nr.: 1768		Drawing nr.: 9621
FORMAT: A1		

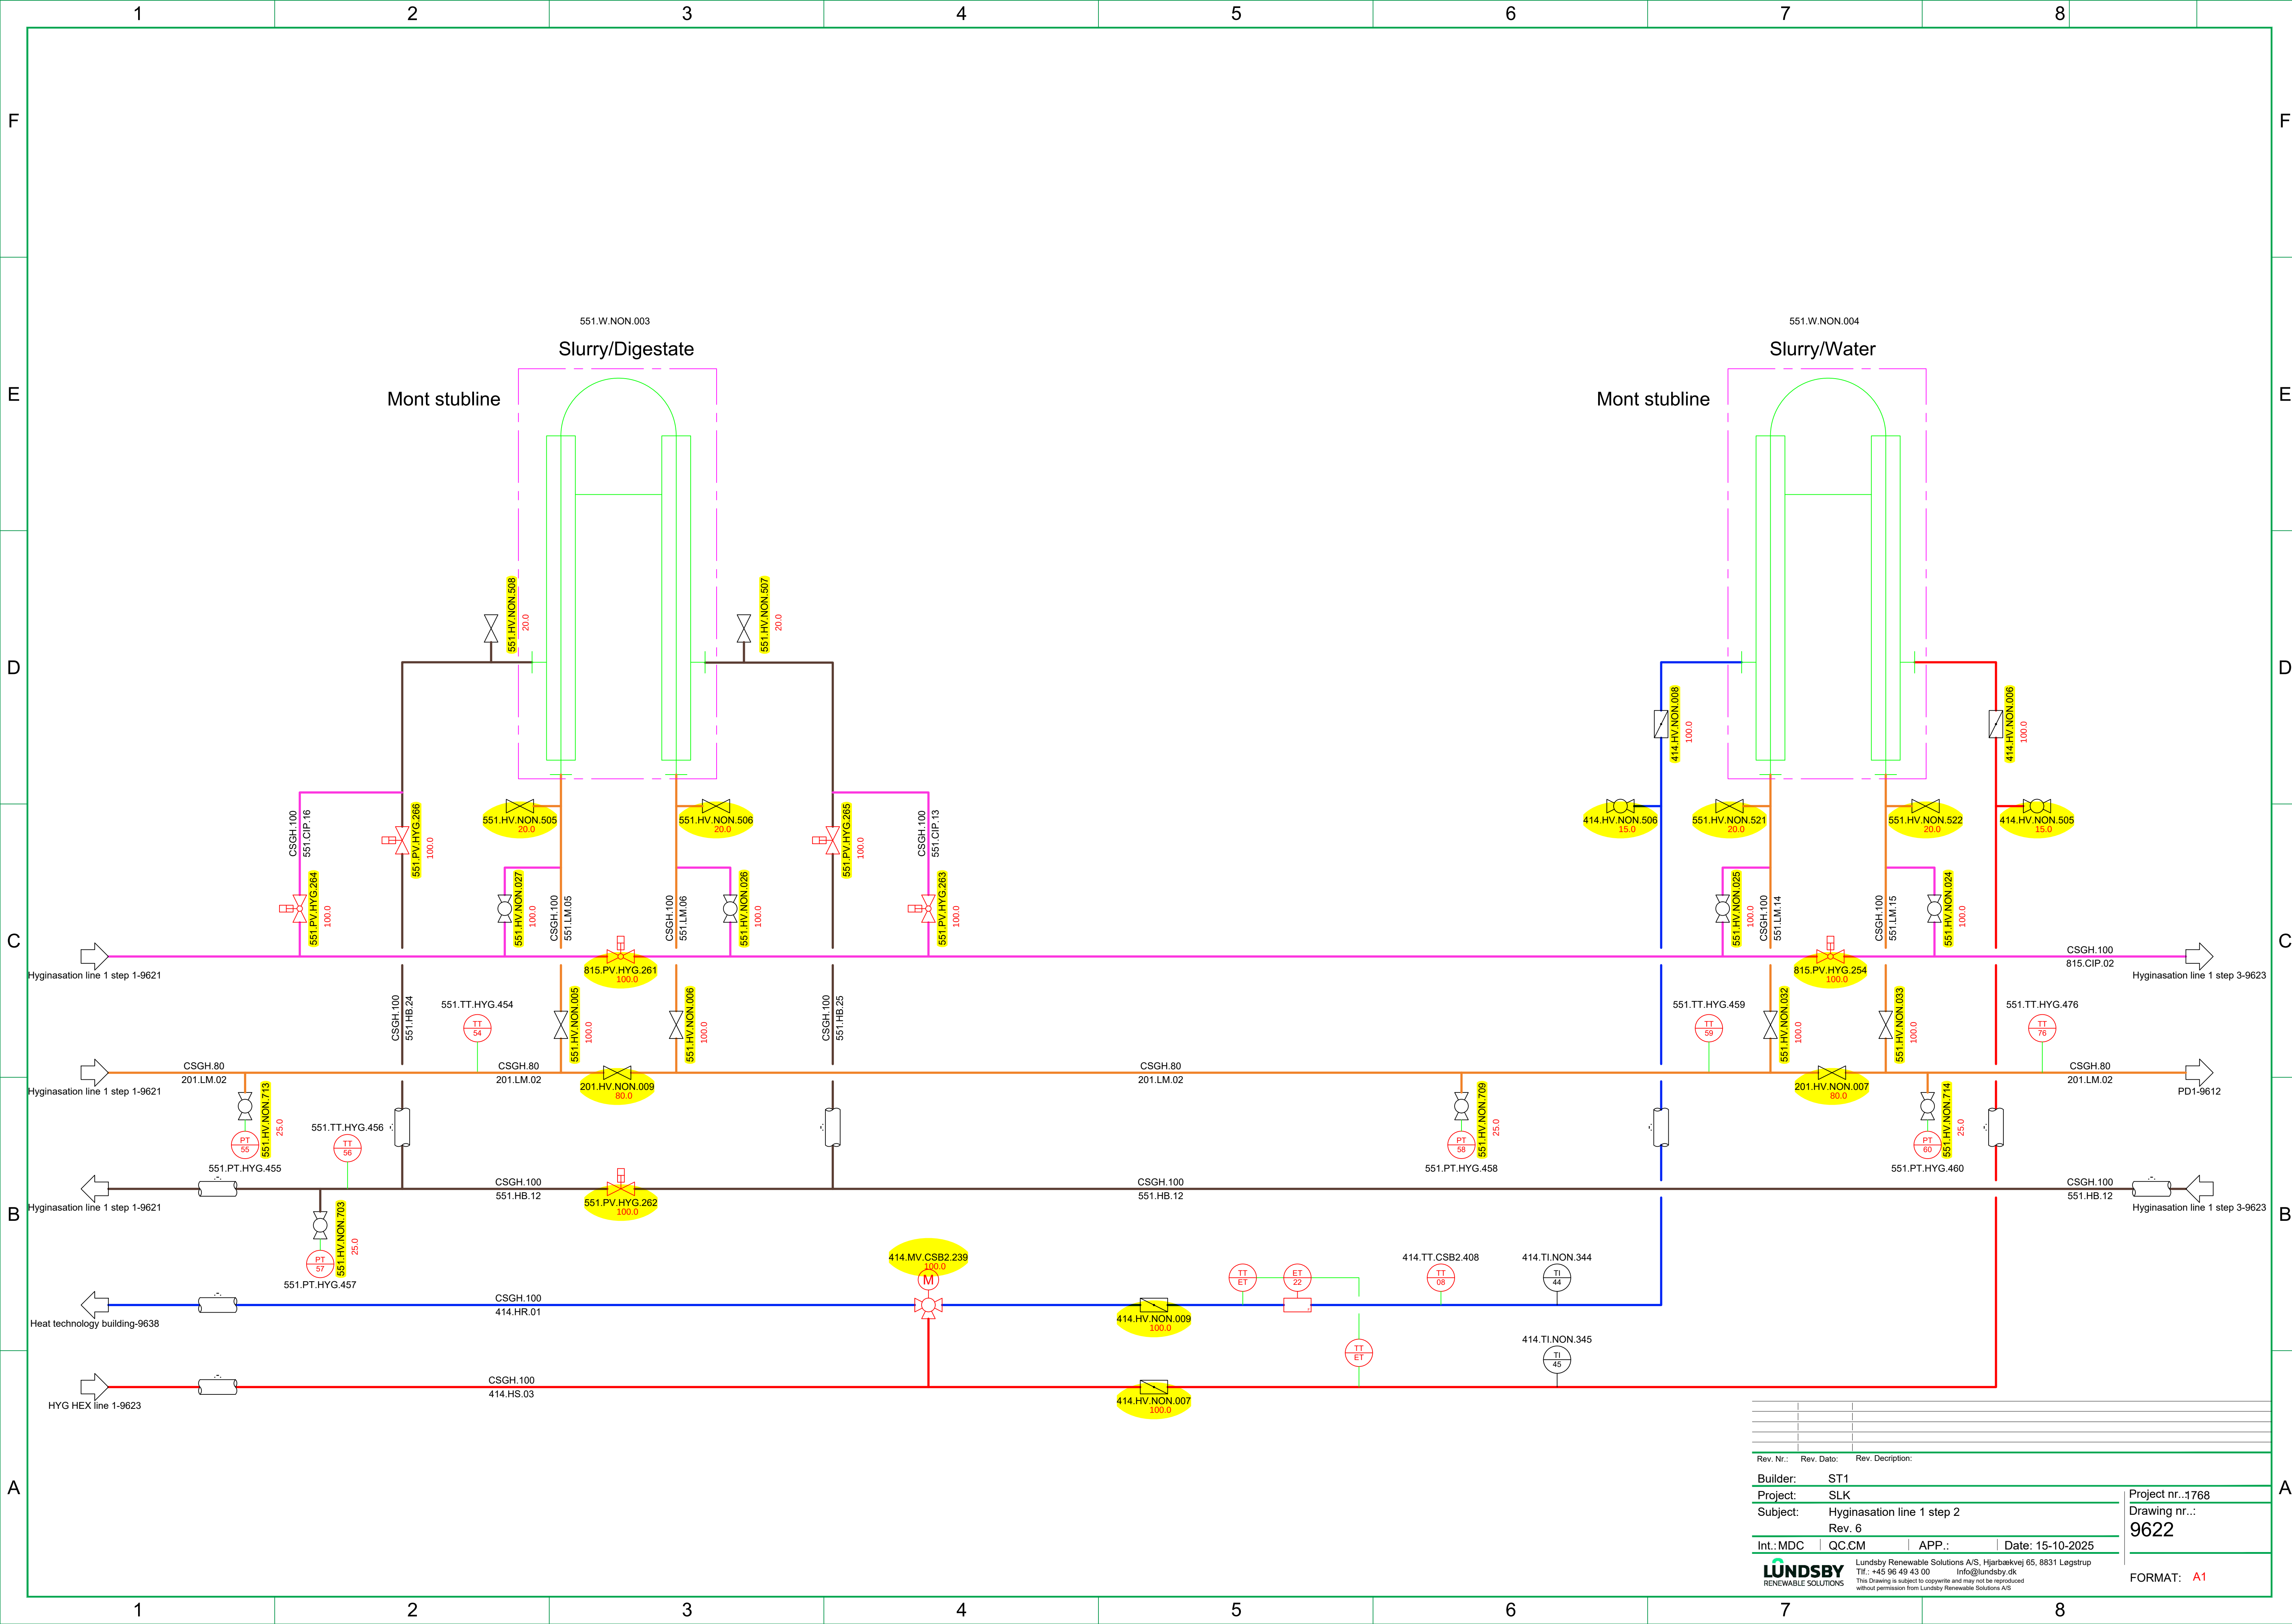


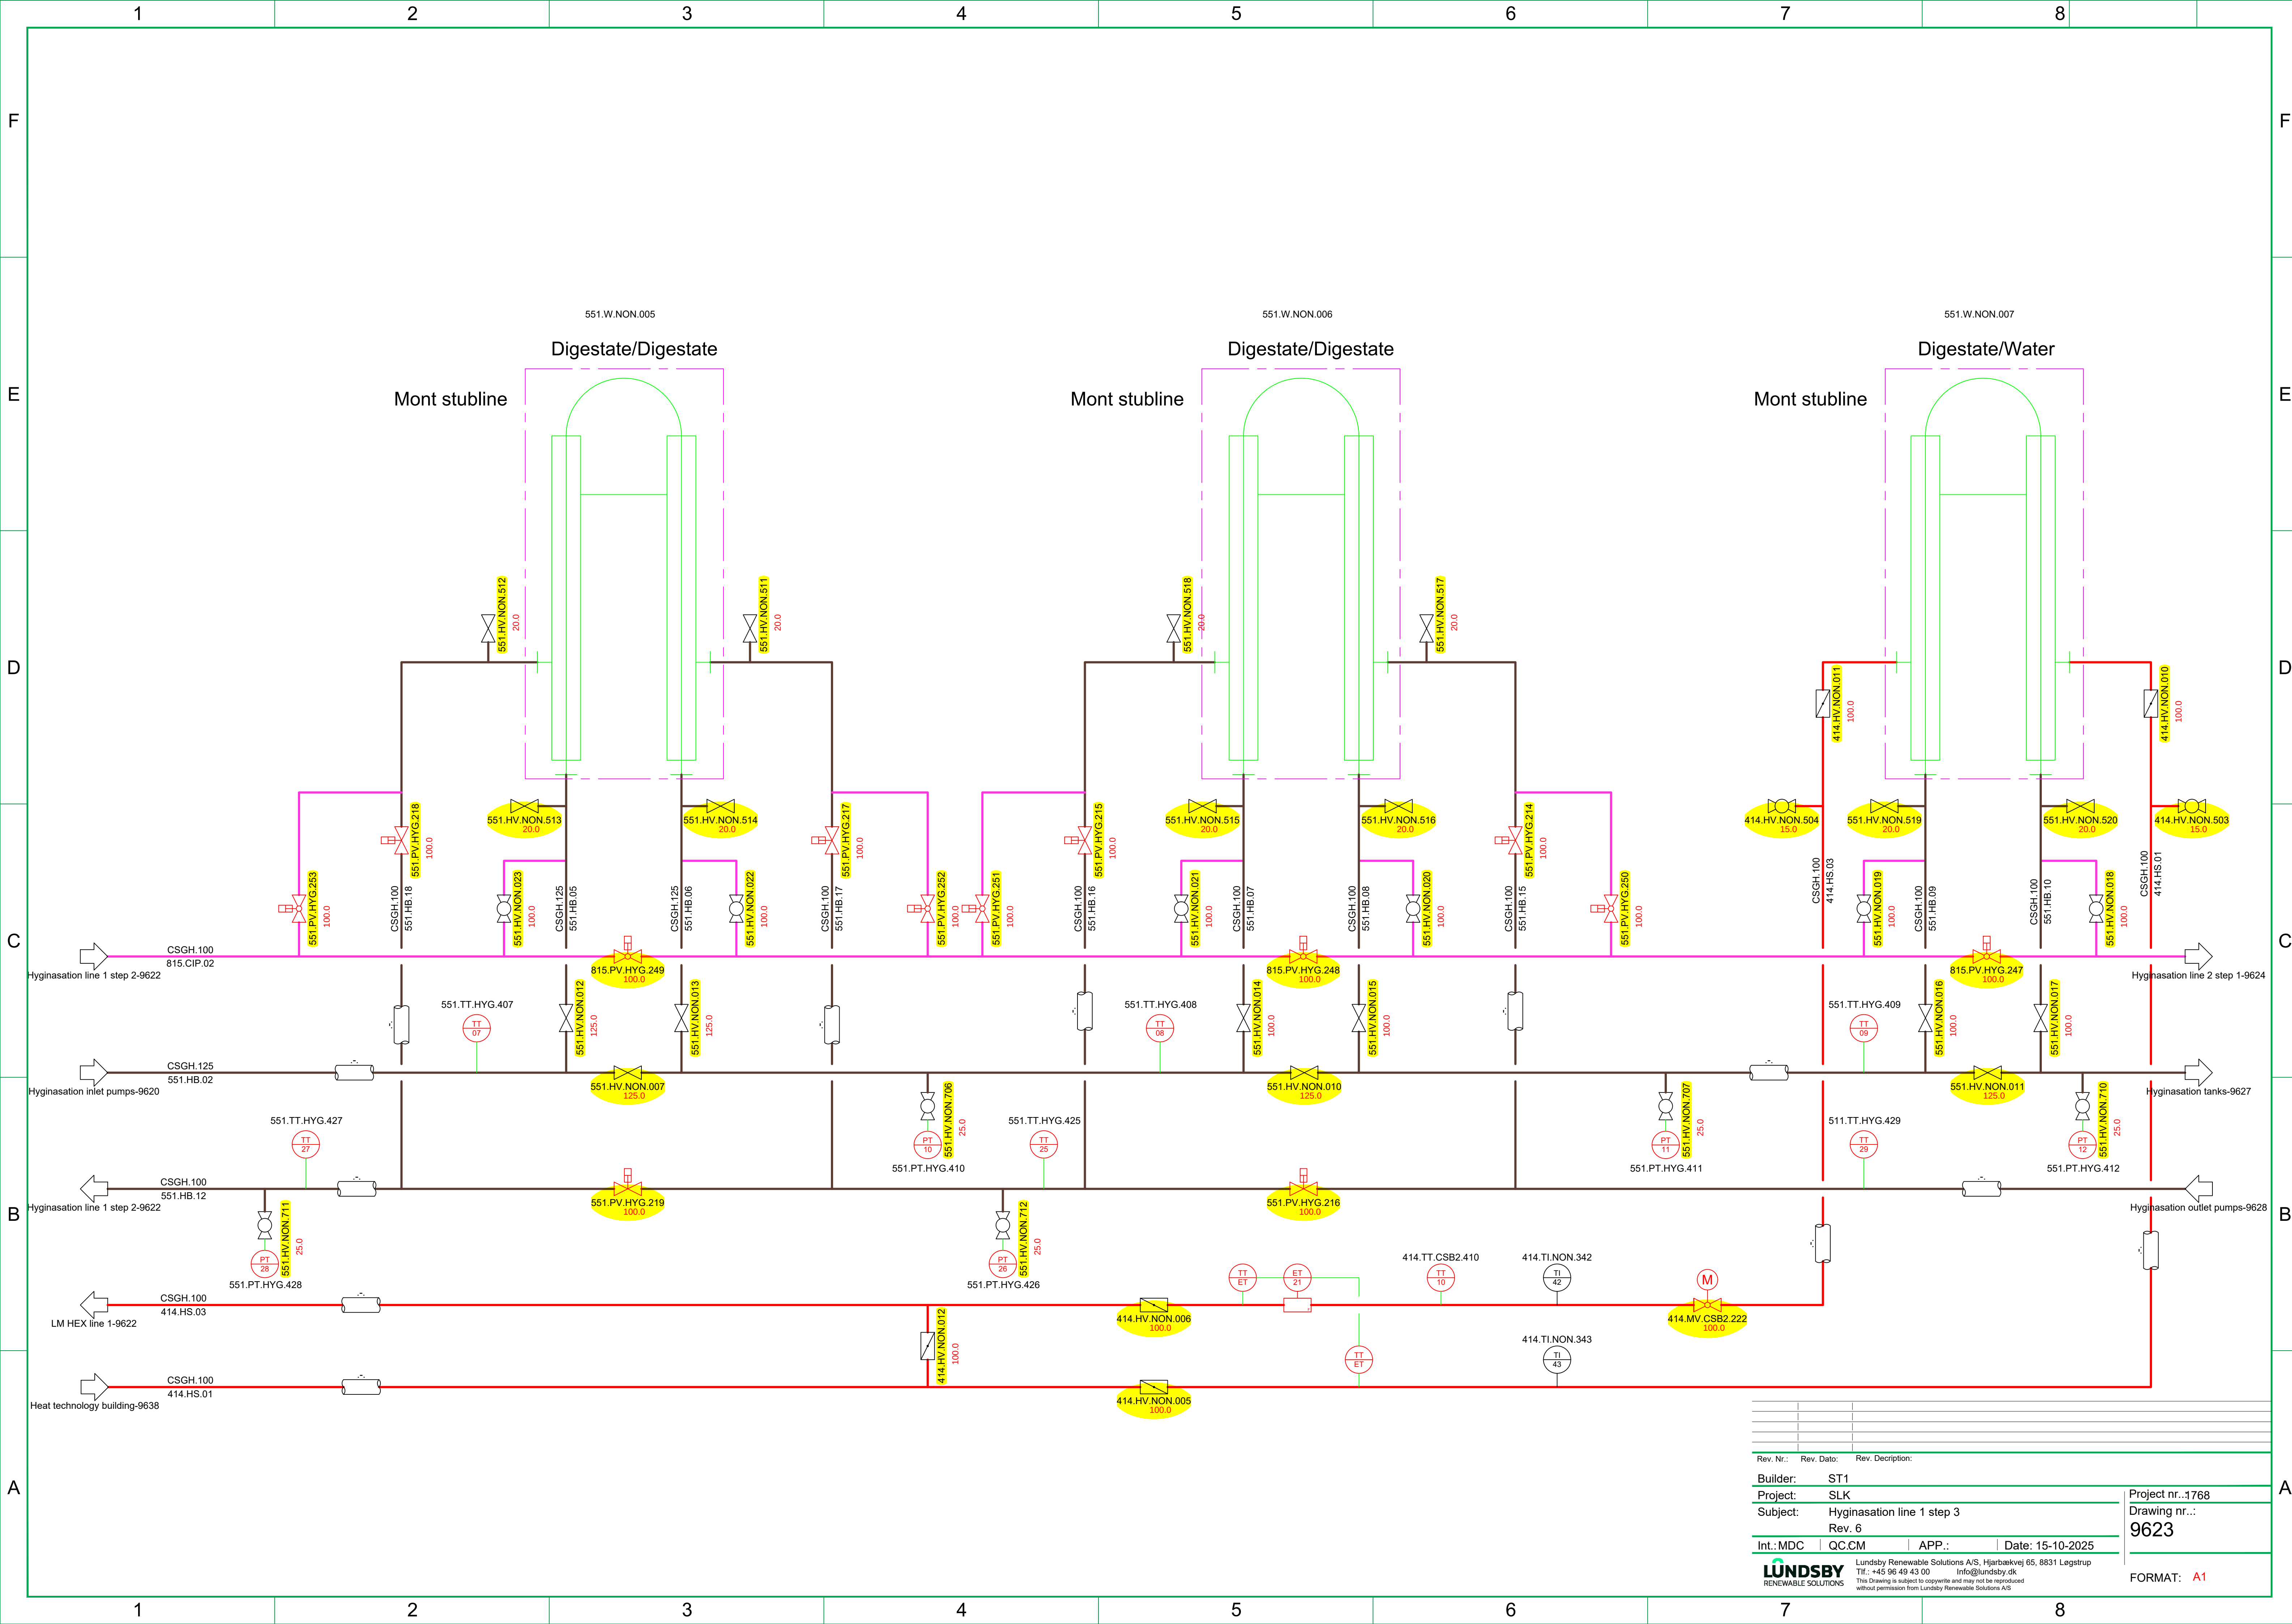

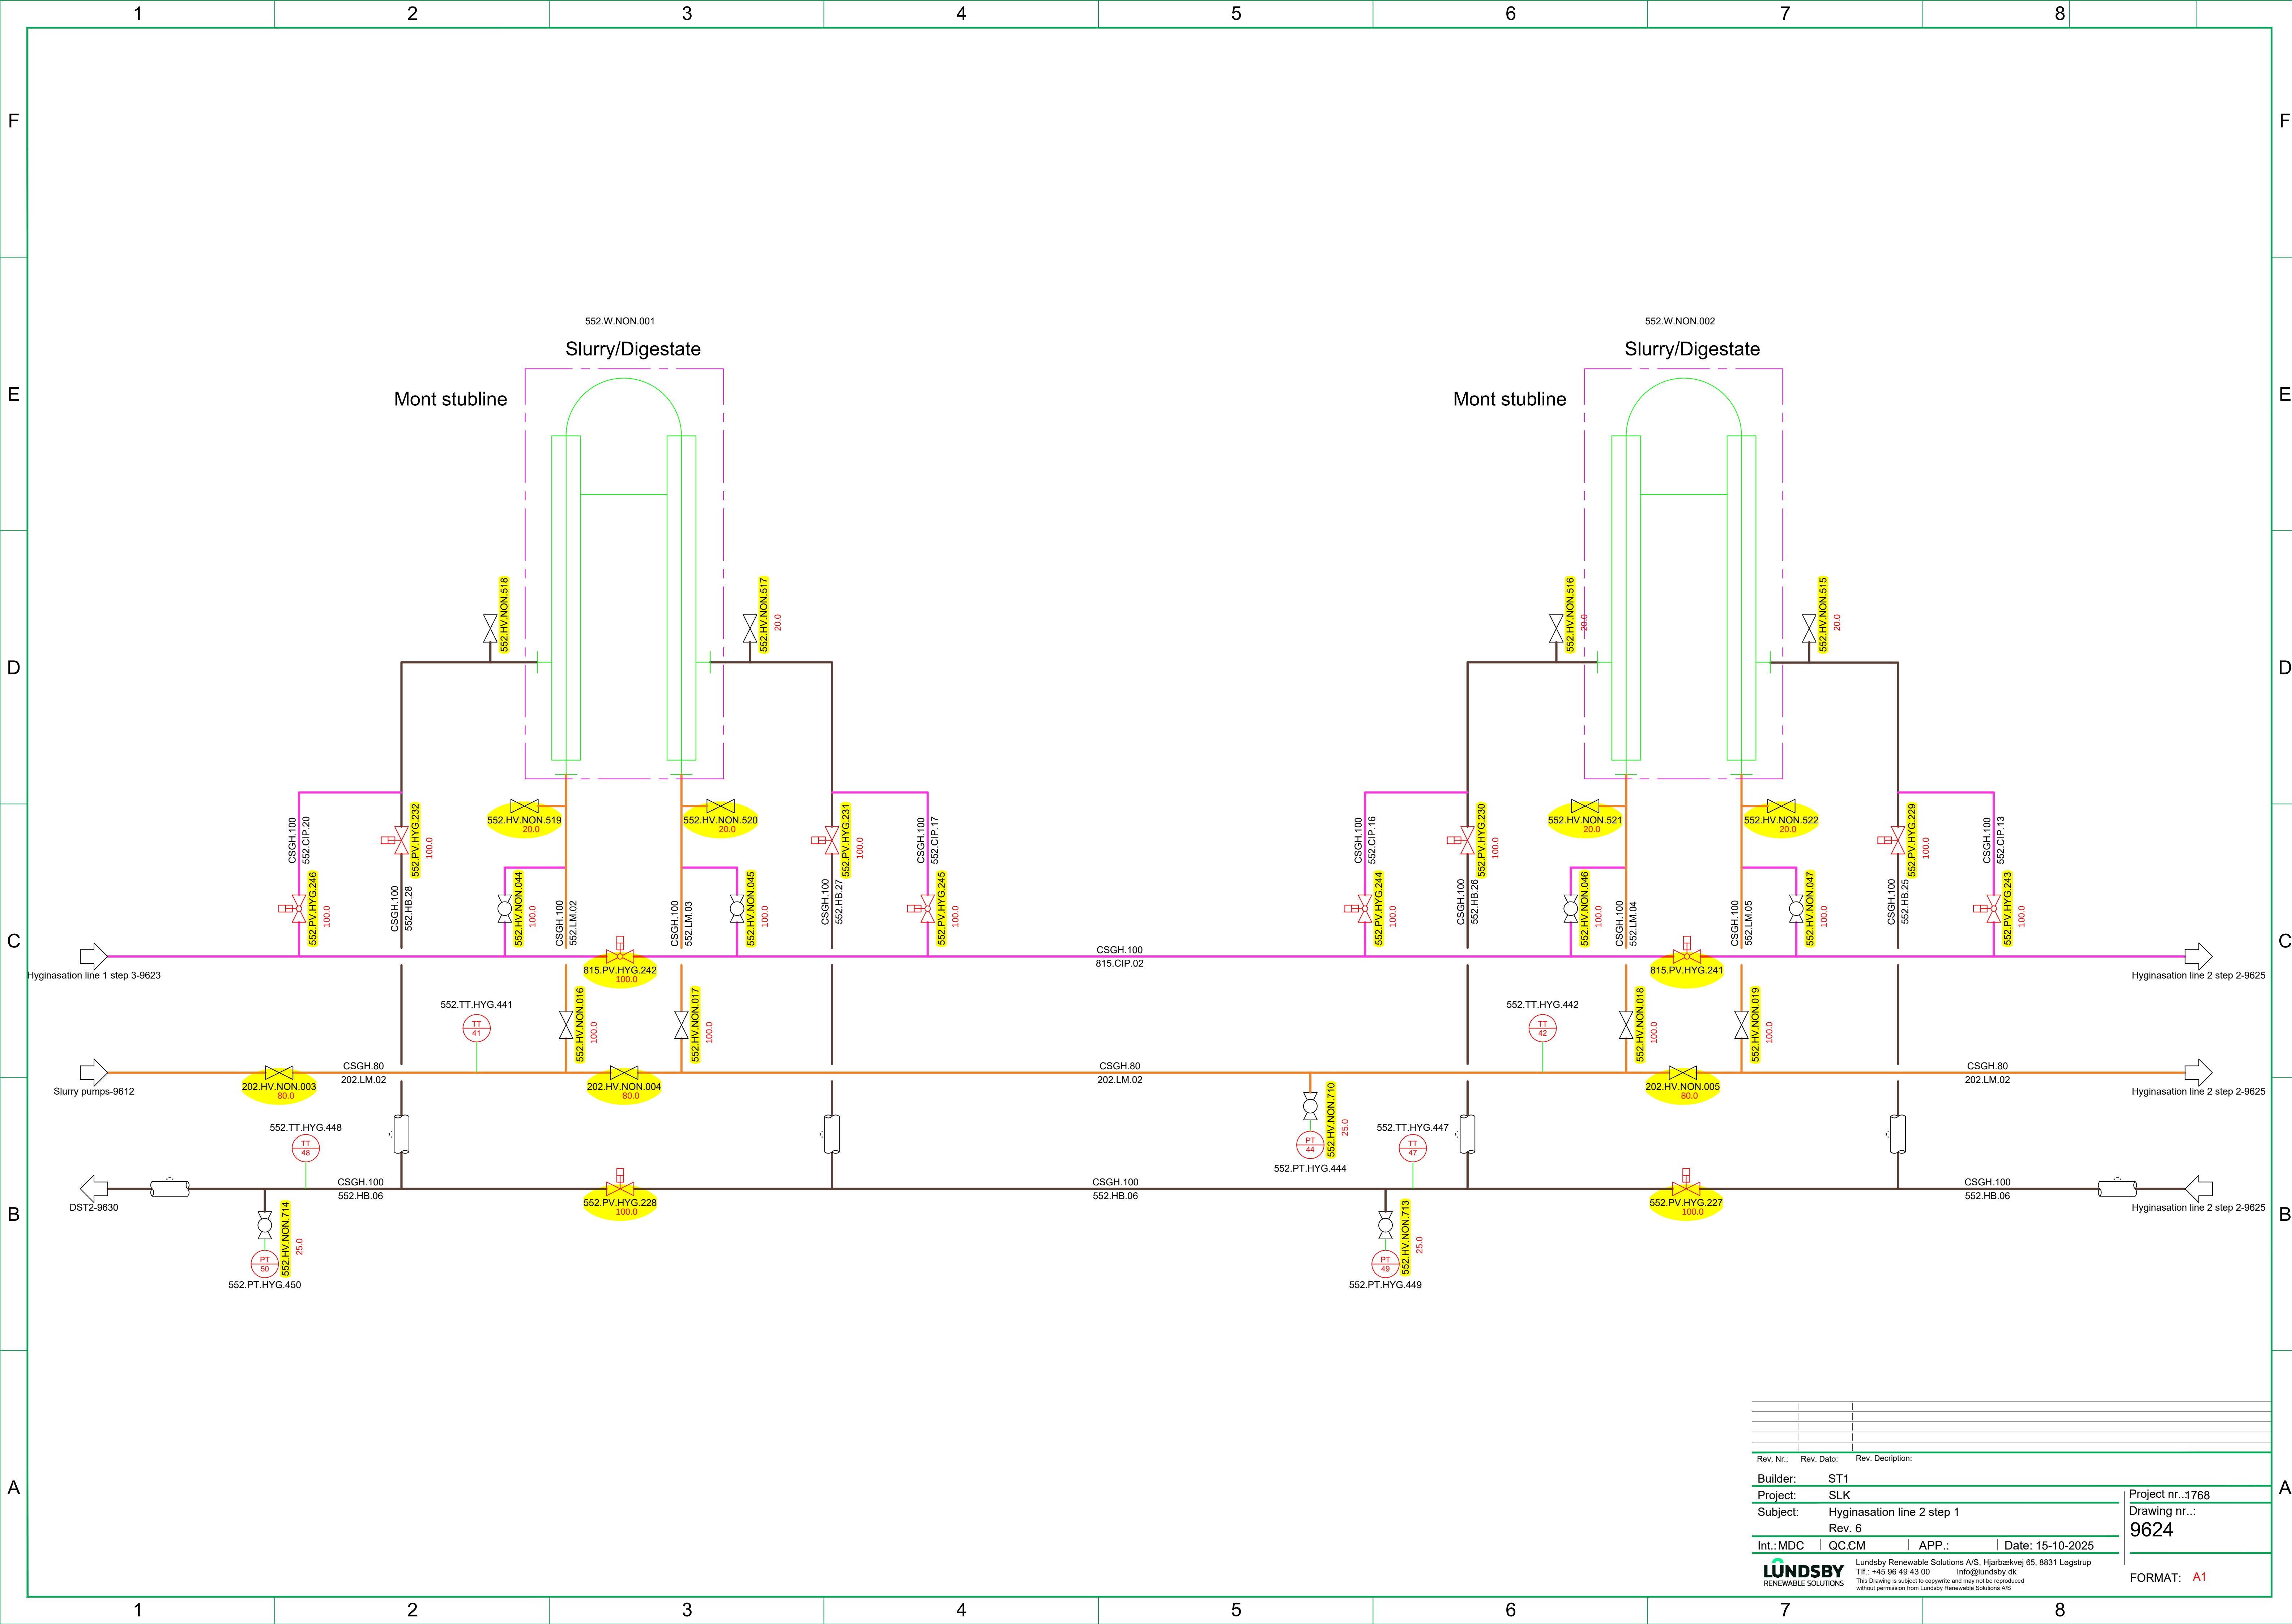

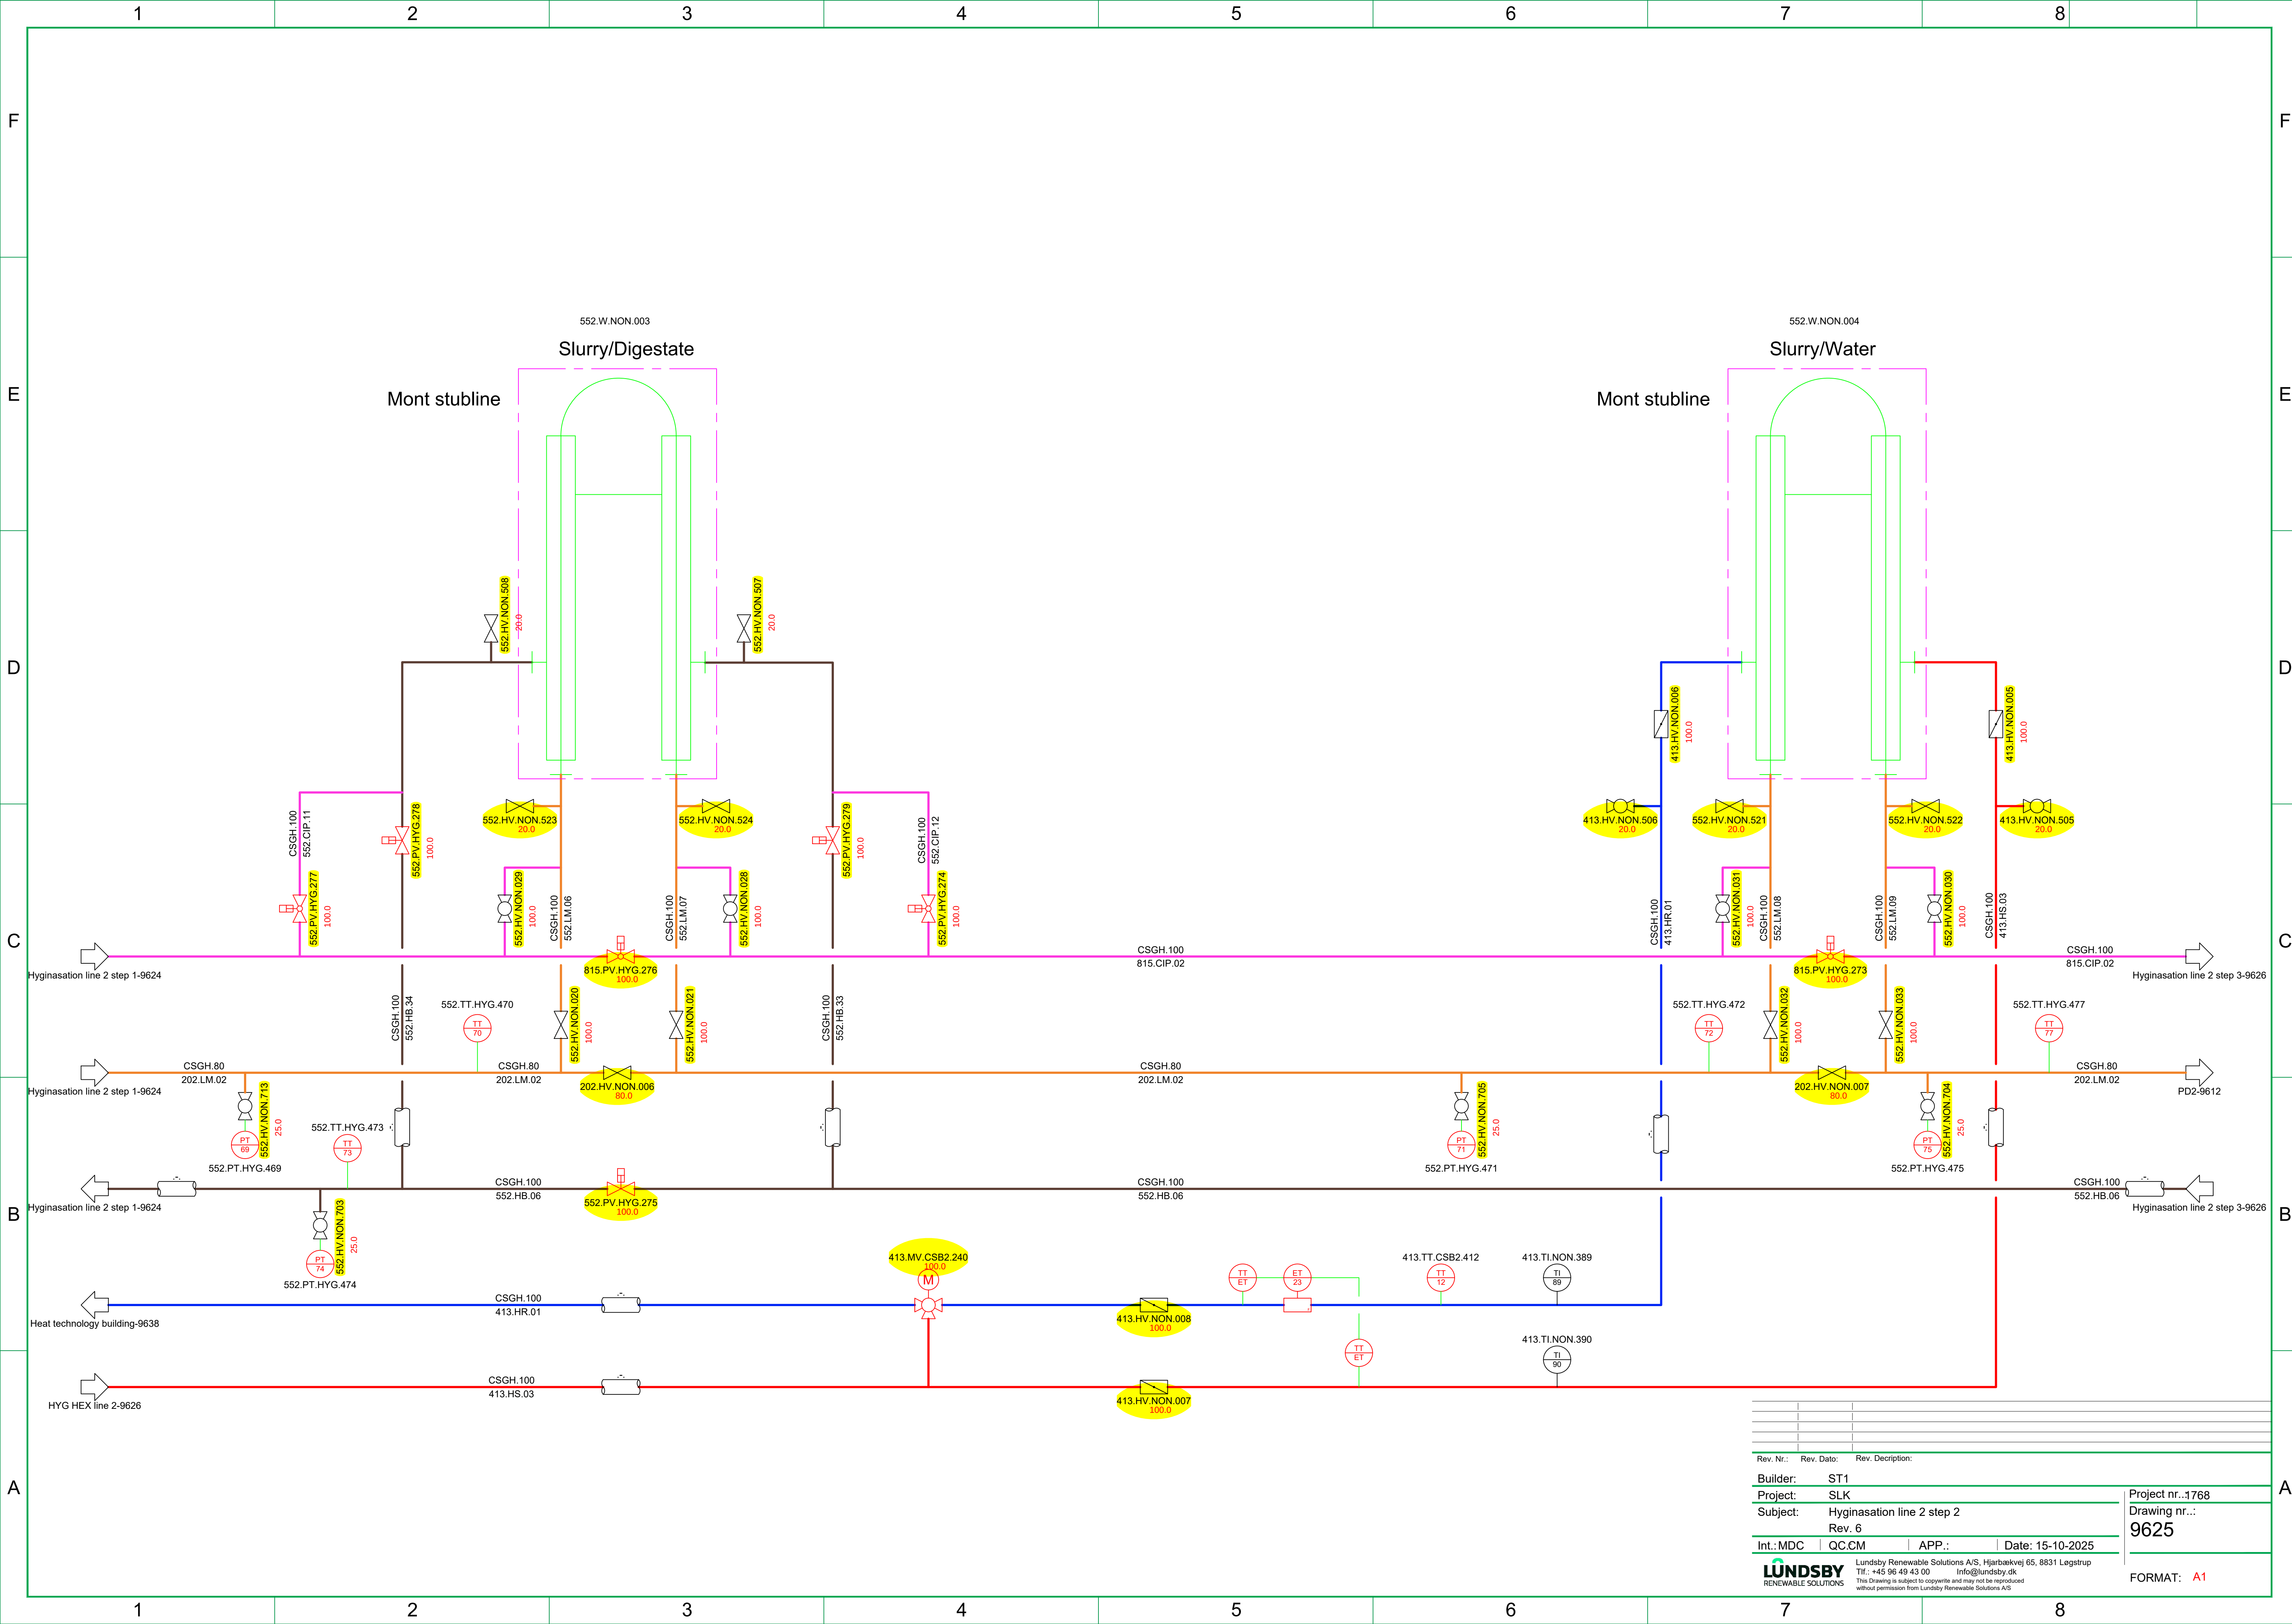

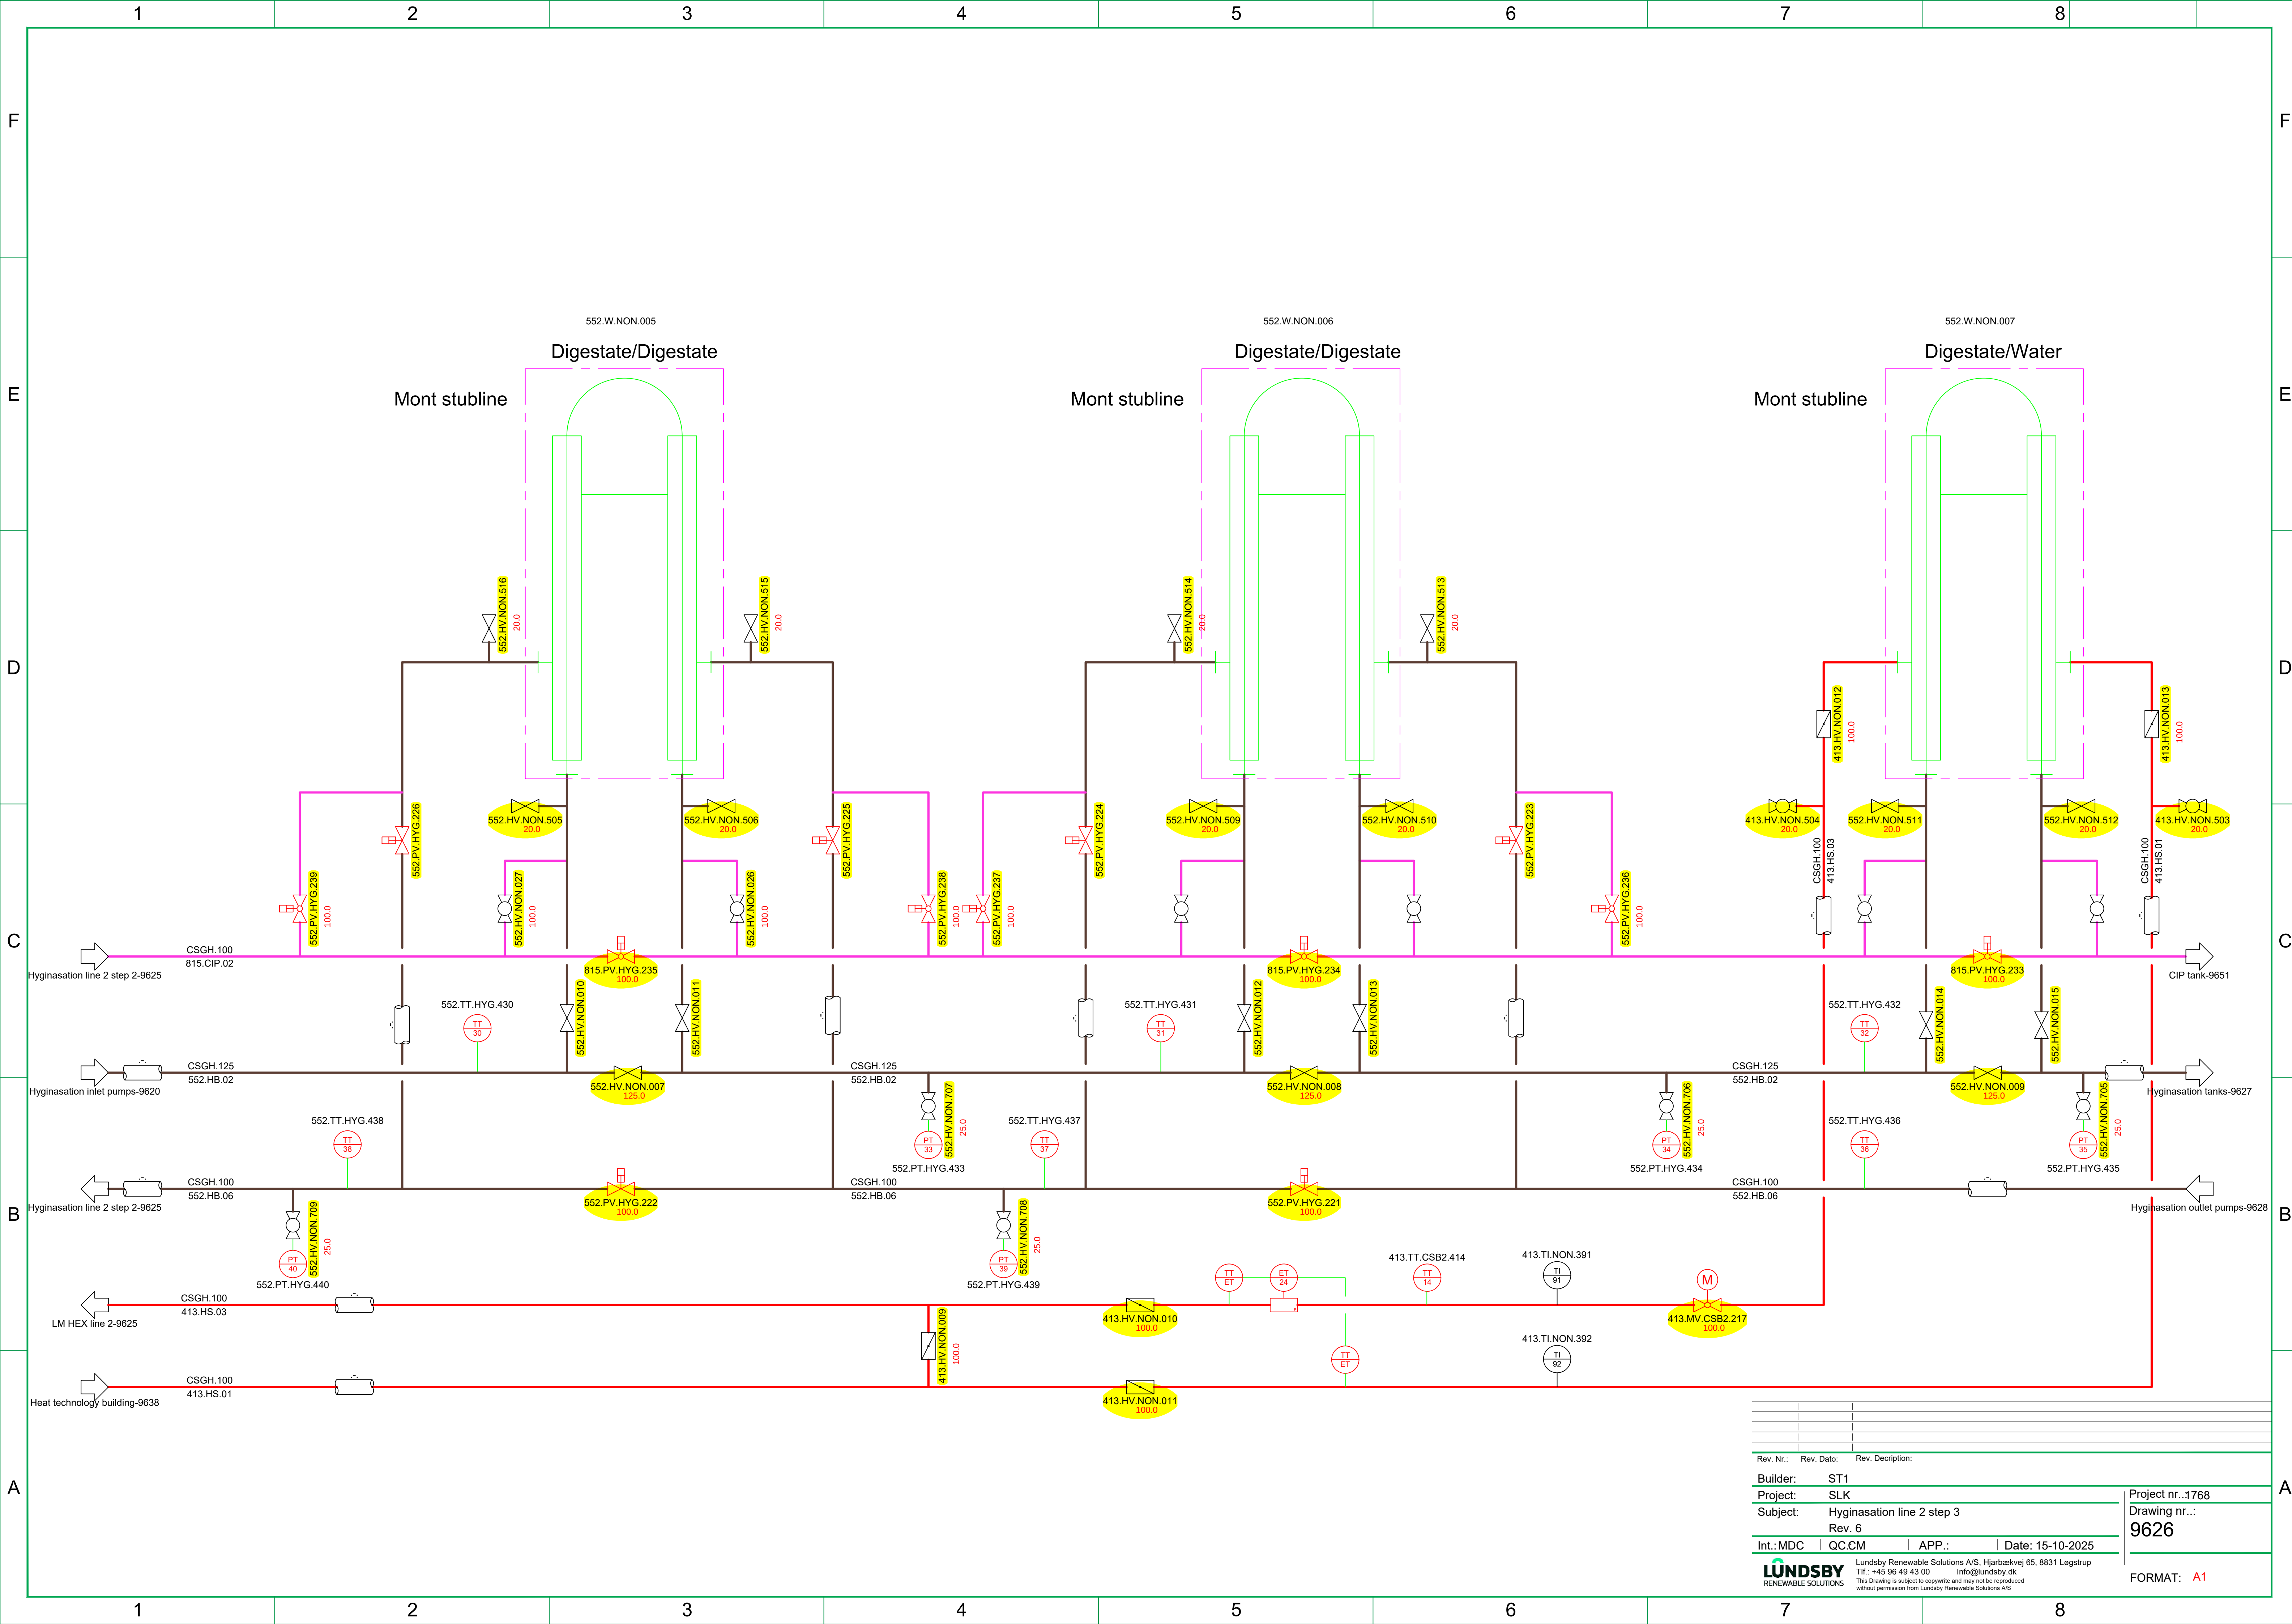


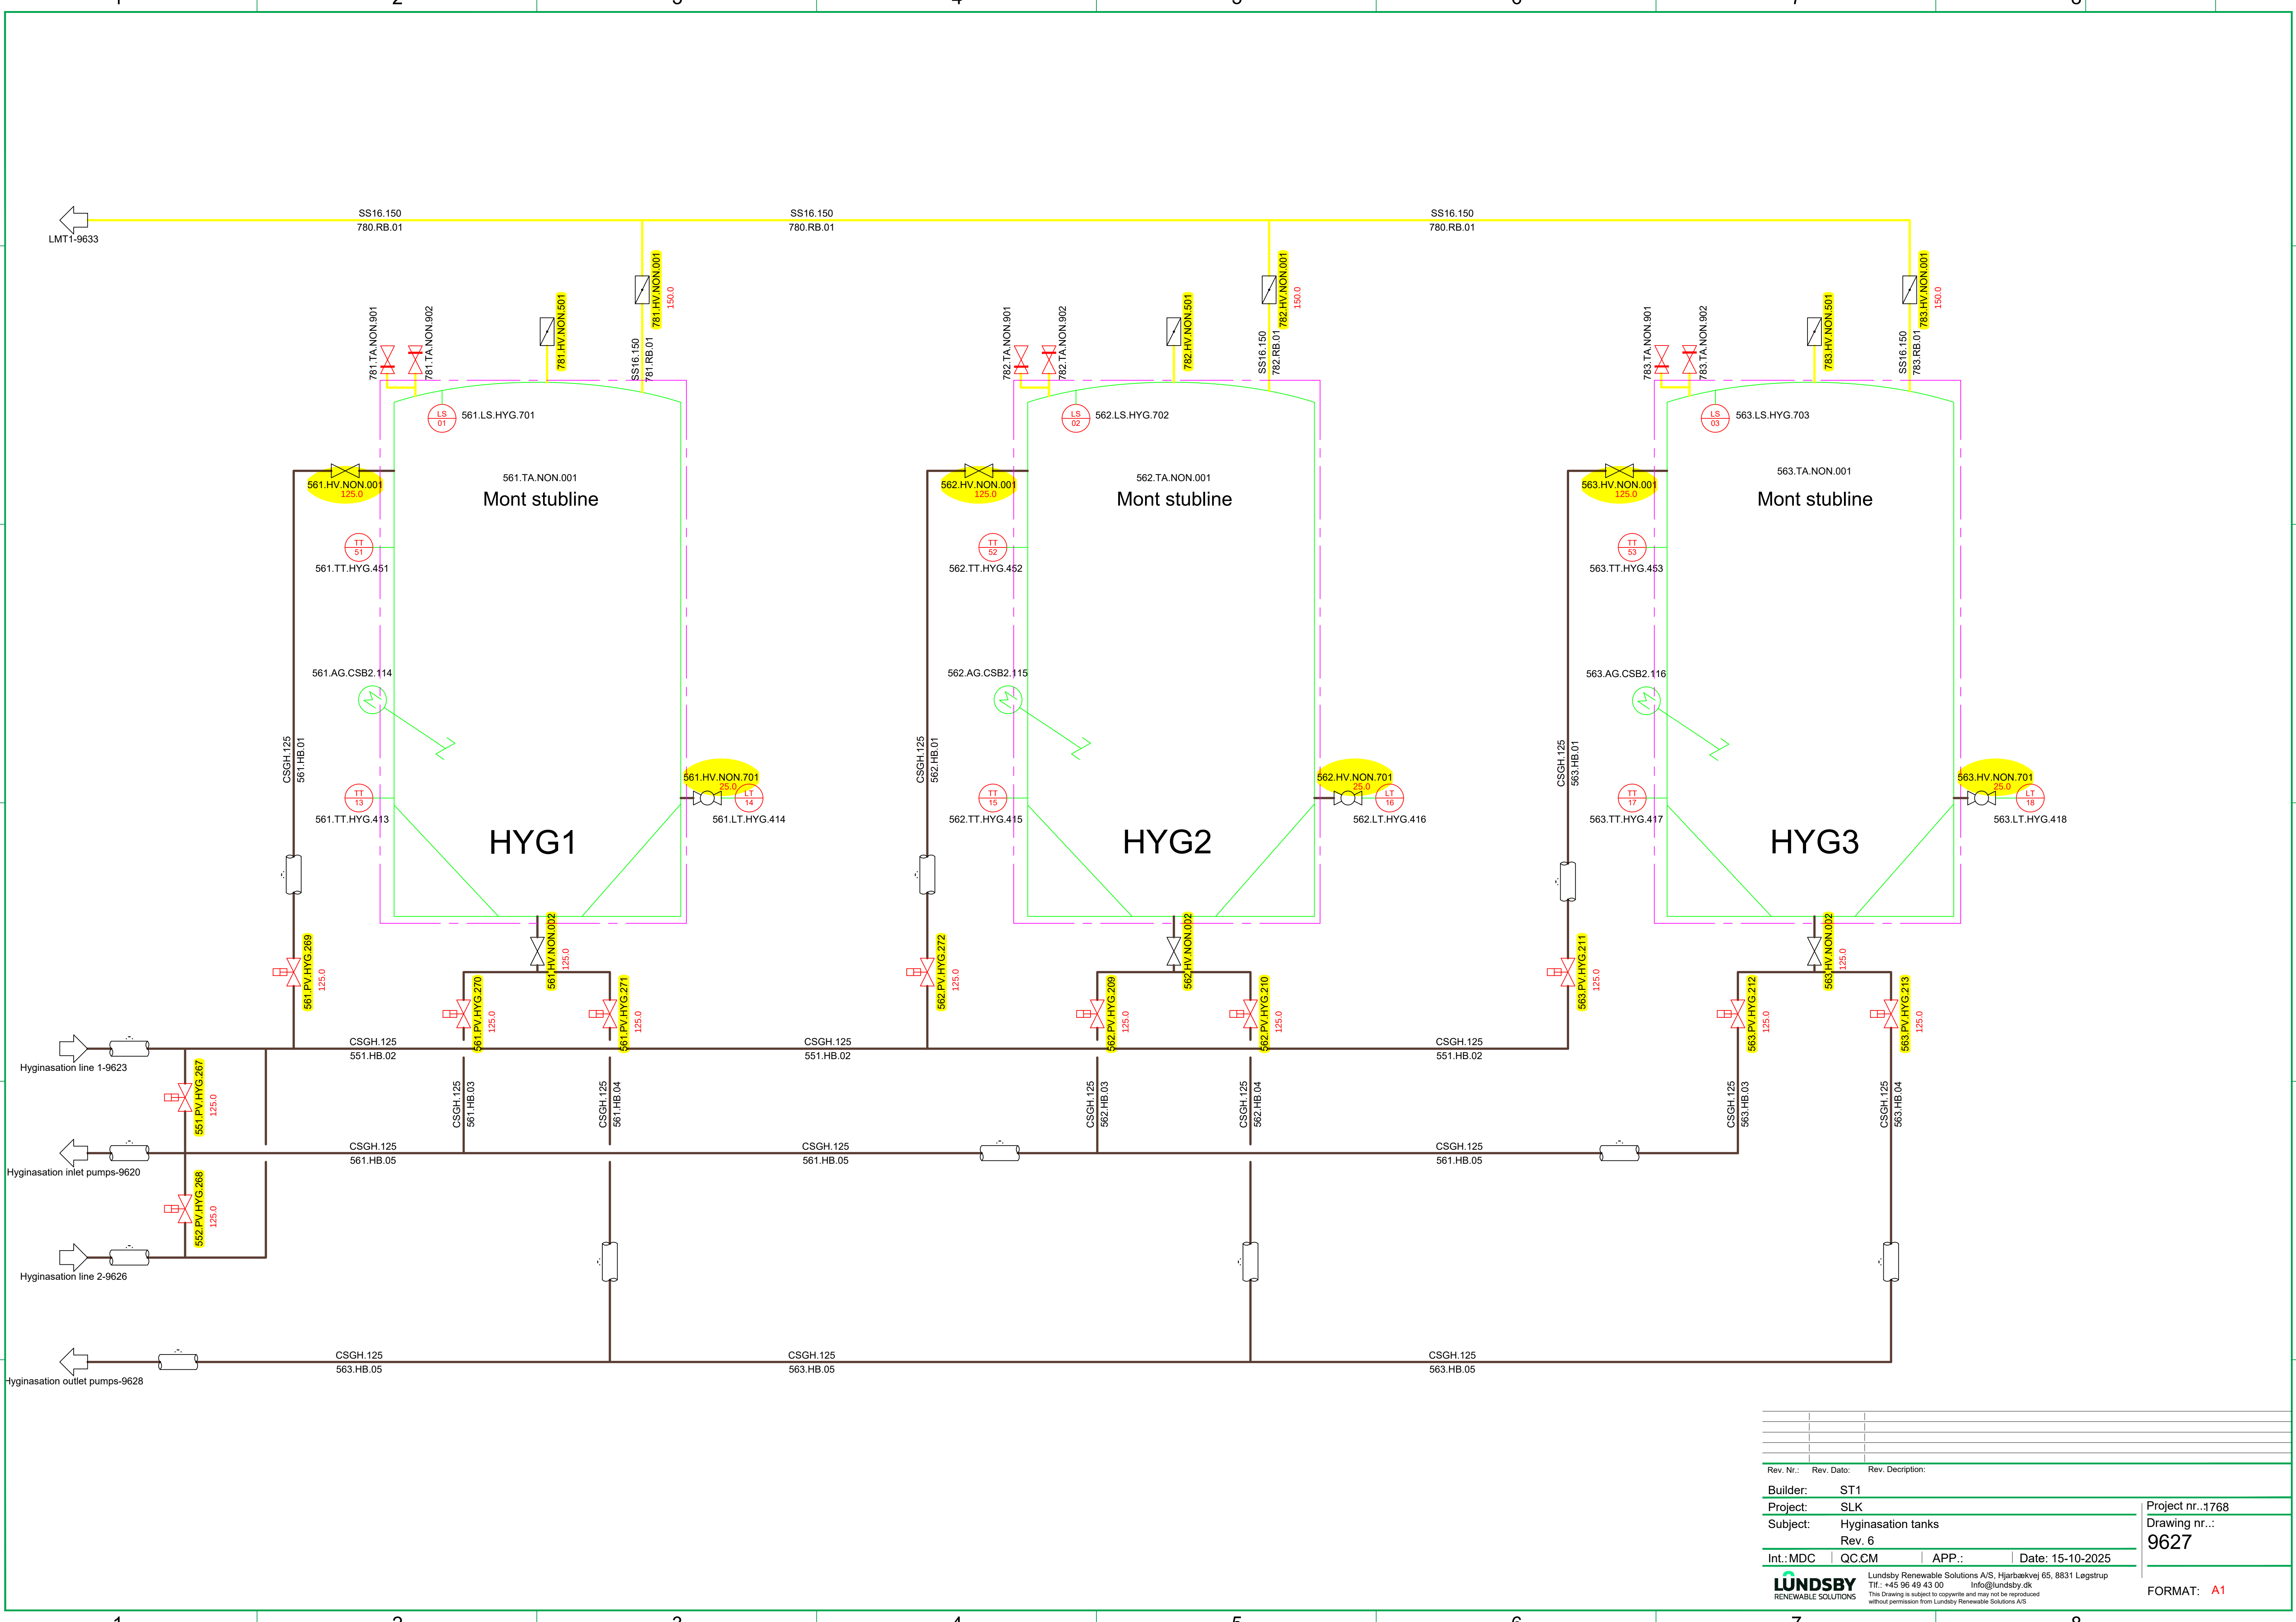


Rev. Nr.:	Rev. Dato:	Rev. Description:	
Builder:	ST1		
Project:	SLK		
Subject:	Hyginasation tanks		
Rev. 6			
Int.: MDC	QC.CM	APP.:	Date: 15-10-2025
LUNDSBY RENEWABLE SOLUTIONS			Lundsby Renewable Solutions A/S, Hjarbrækvej 65, 8831 Løgstrup Tlf.: +45 96 49 43 00 info@lundsby.dk This drawing is subject to copyright and may not be reproduced without permission from Lundsby Renewable Solutions A/S
Project nr.: 1768 Drawing nr.: 9627			FORMAT: A1

Tech Building


Outlet pumps

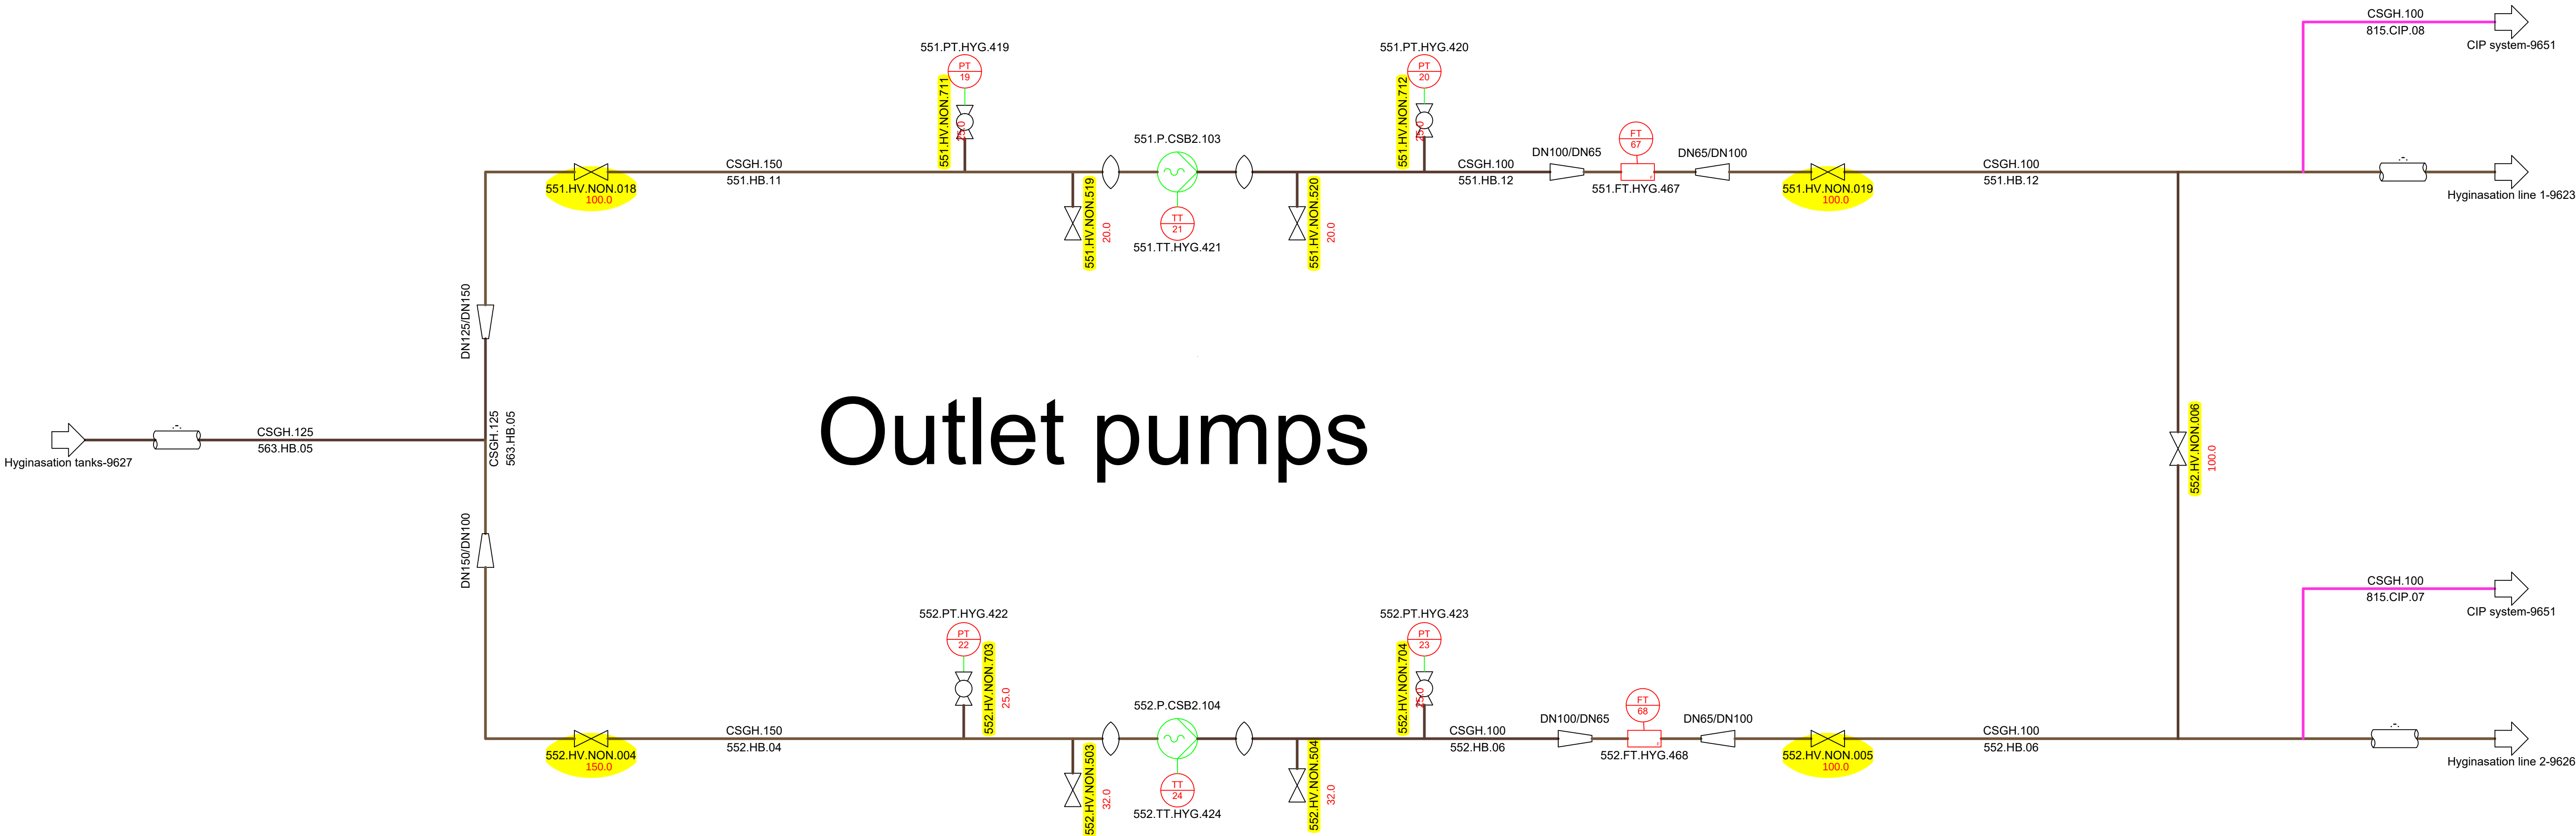


Rev. Nr.:	Rev. Dato:	Rev. Description:	
Builder:	ST1		
Project:	SLK		
Subject:	Hyginasation outlet pumps		
Rev. 6			
Int.:MDC	QC:CM	APP.:	Date: 15-10-2025
LUNDSBY RENEWABLE SOLUTIONS			Lundsby Renewable Solutions A/S, Hjarbrækvej 65, 8831 Lægstrup Tlf.: +45 96 49 43 00 Info@lundsby.dk This Drawing is subject to copyright and may not be reproduced without permission from Lundsby Renewable Solutions A/S
			Project nr.:1768 Drawing nr.: 9628 FORMAT: A1

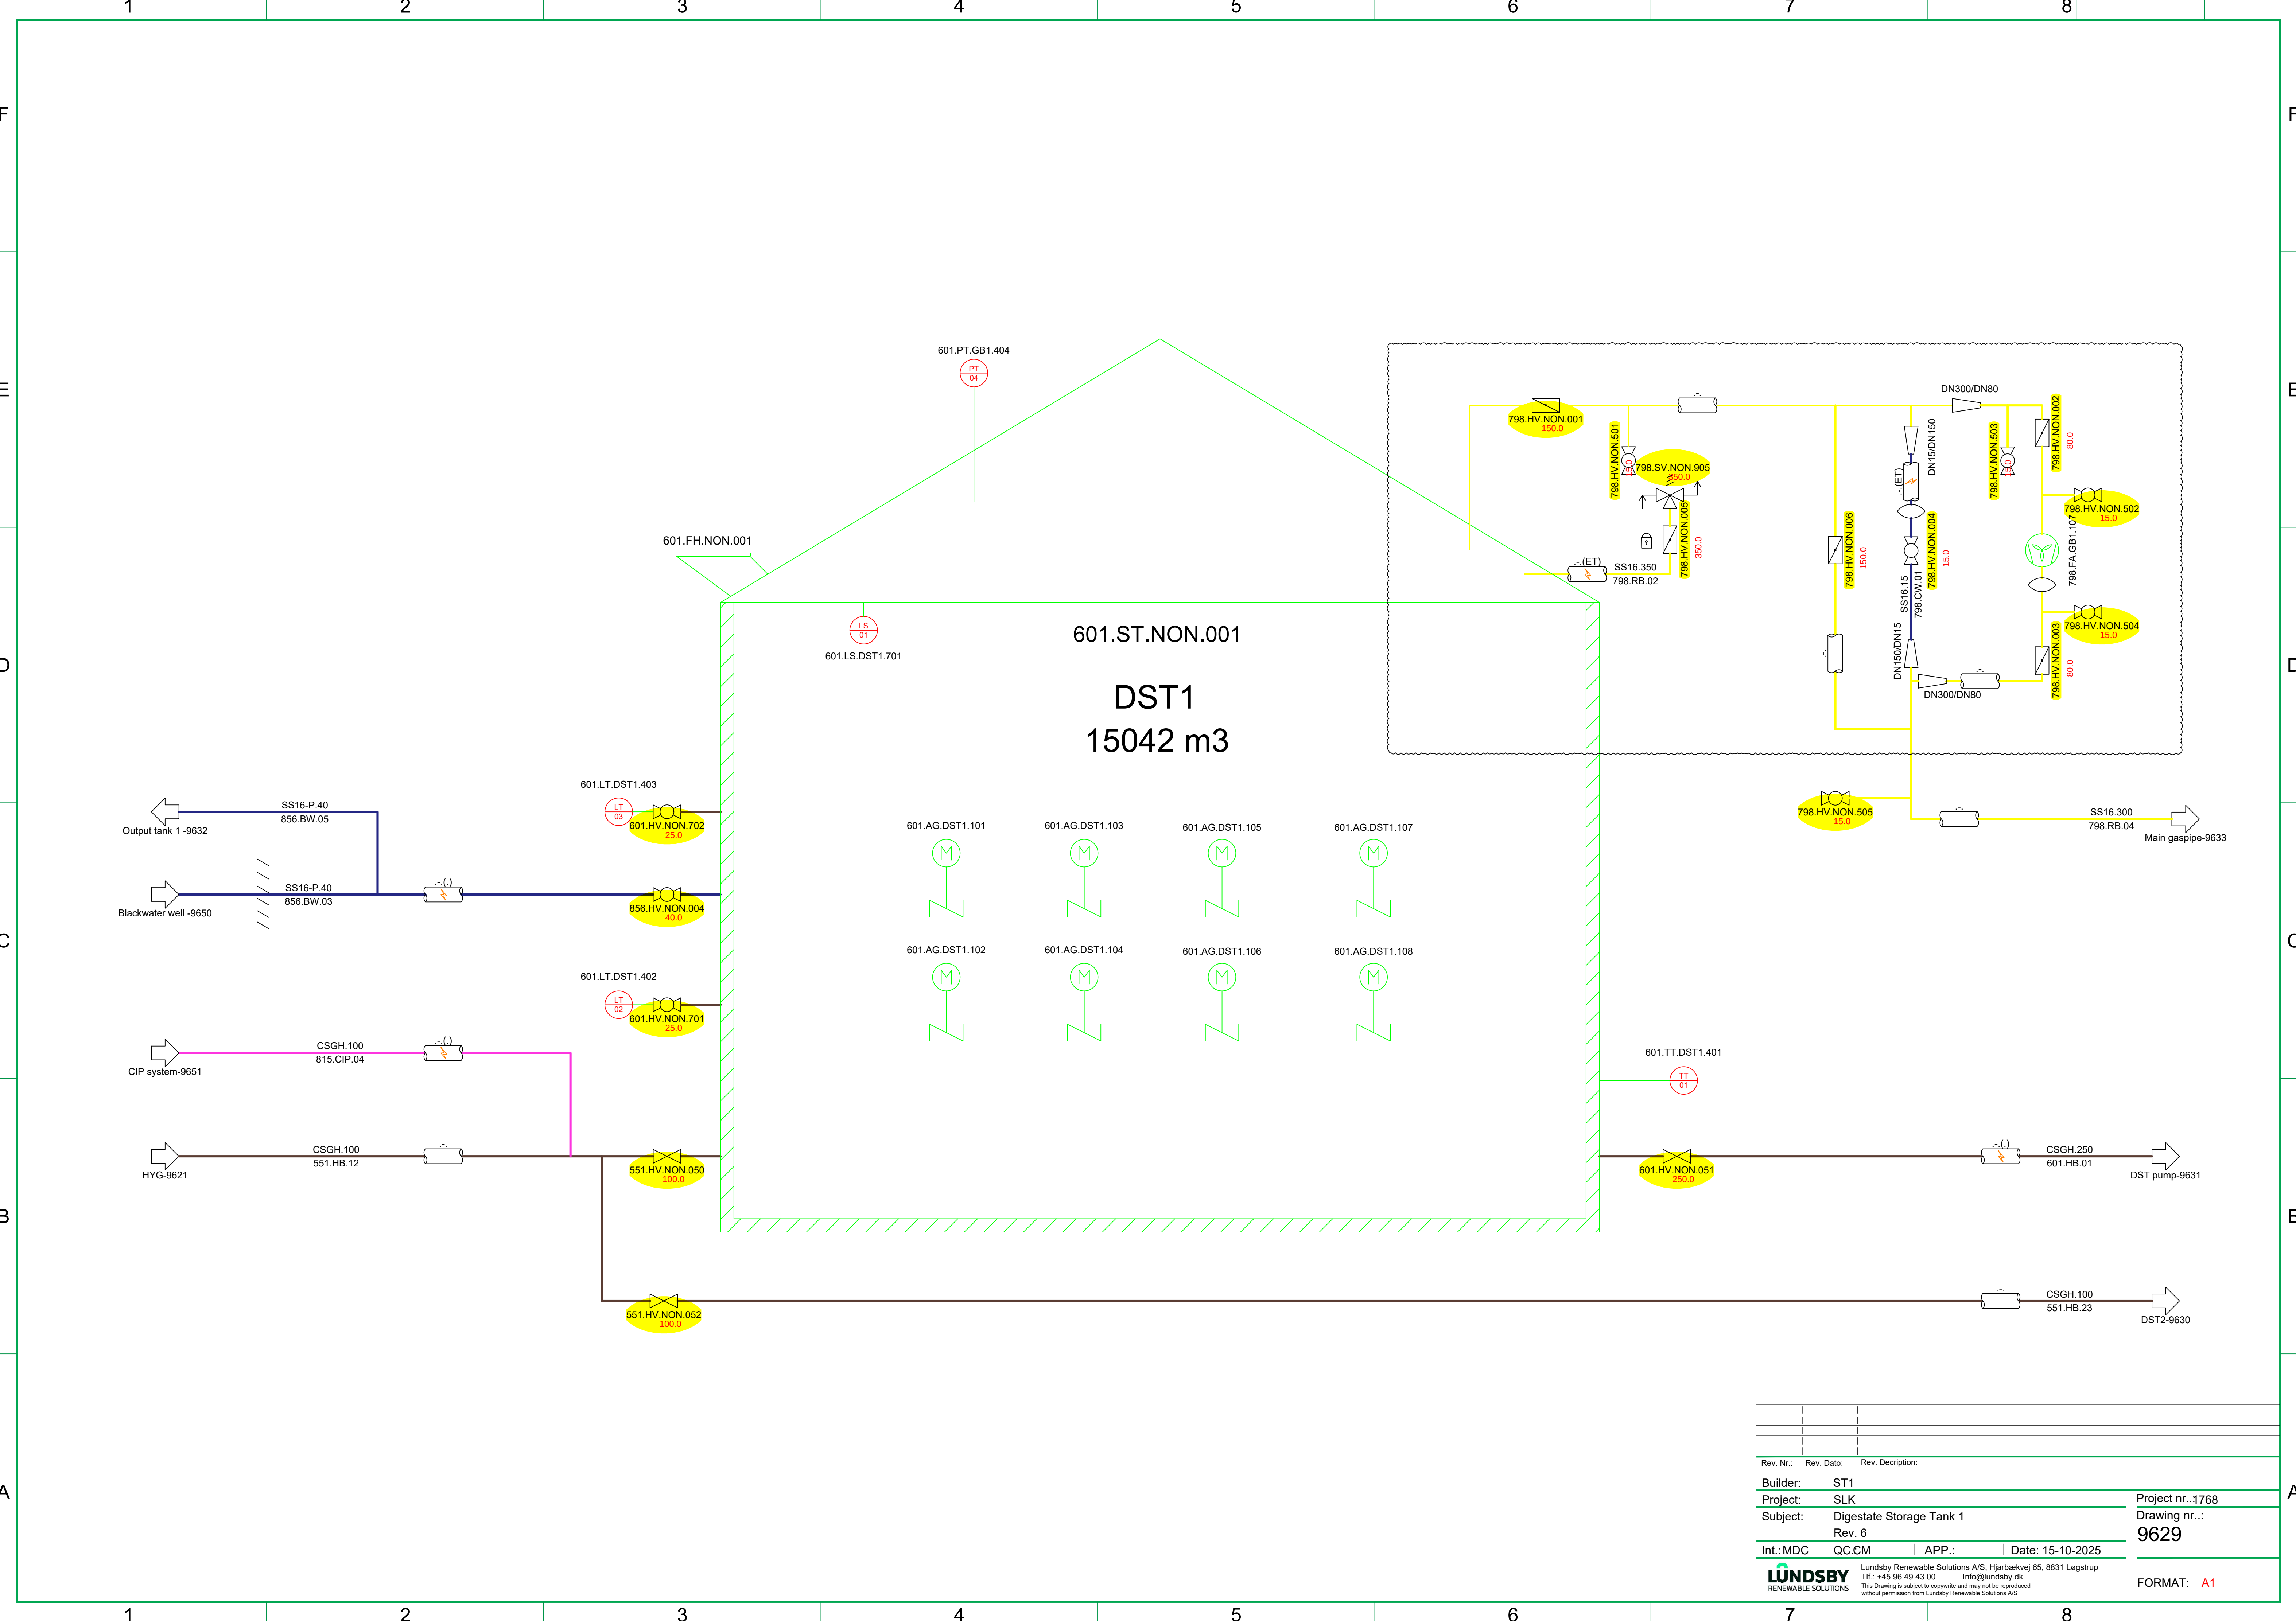


Rev. Nr.:	Rev. Dato:	Rev. Description:	Project nr...1768
Builder:	ST1		Drawing nr...: 9629
Project:	SLK		
Subject:	Digestate Storage Tank 1		
Rev. 6			
Int.:MDC	QC:CM	APP.:	Date: 15-10-2025
LUNDSBY RENEWABLE SOLUTIONS			Format: A1

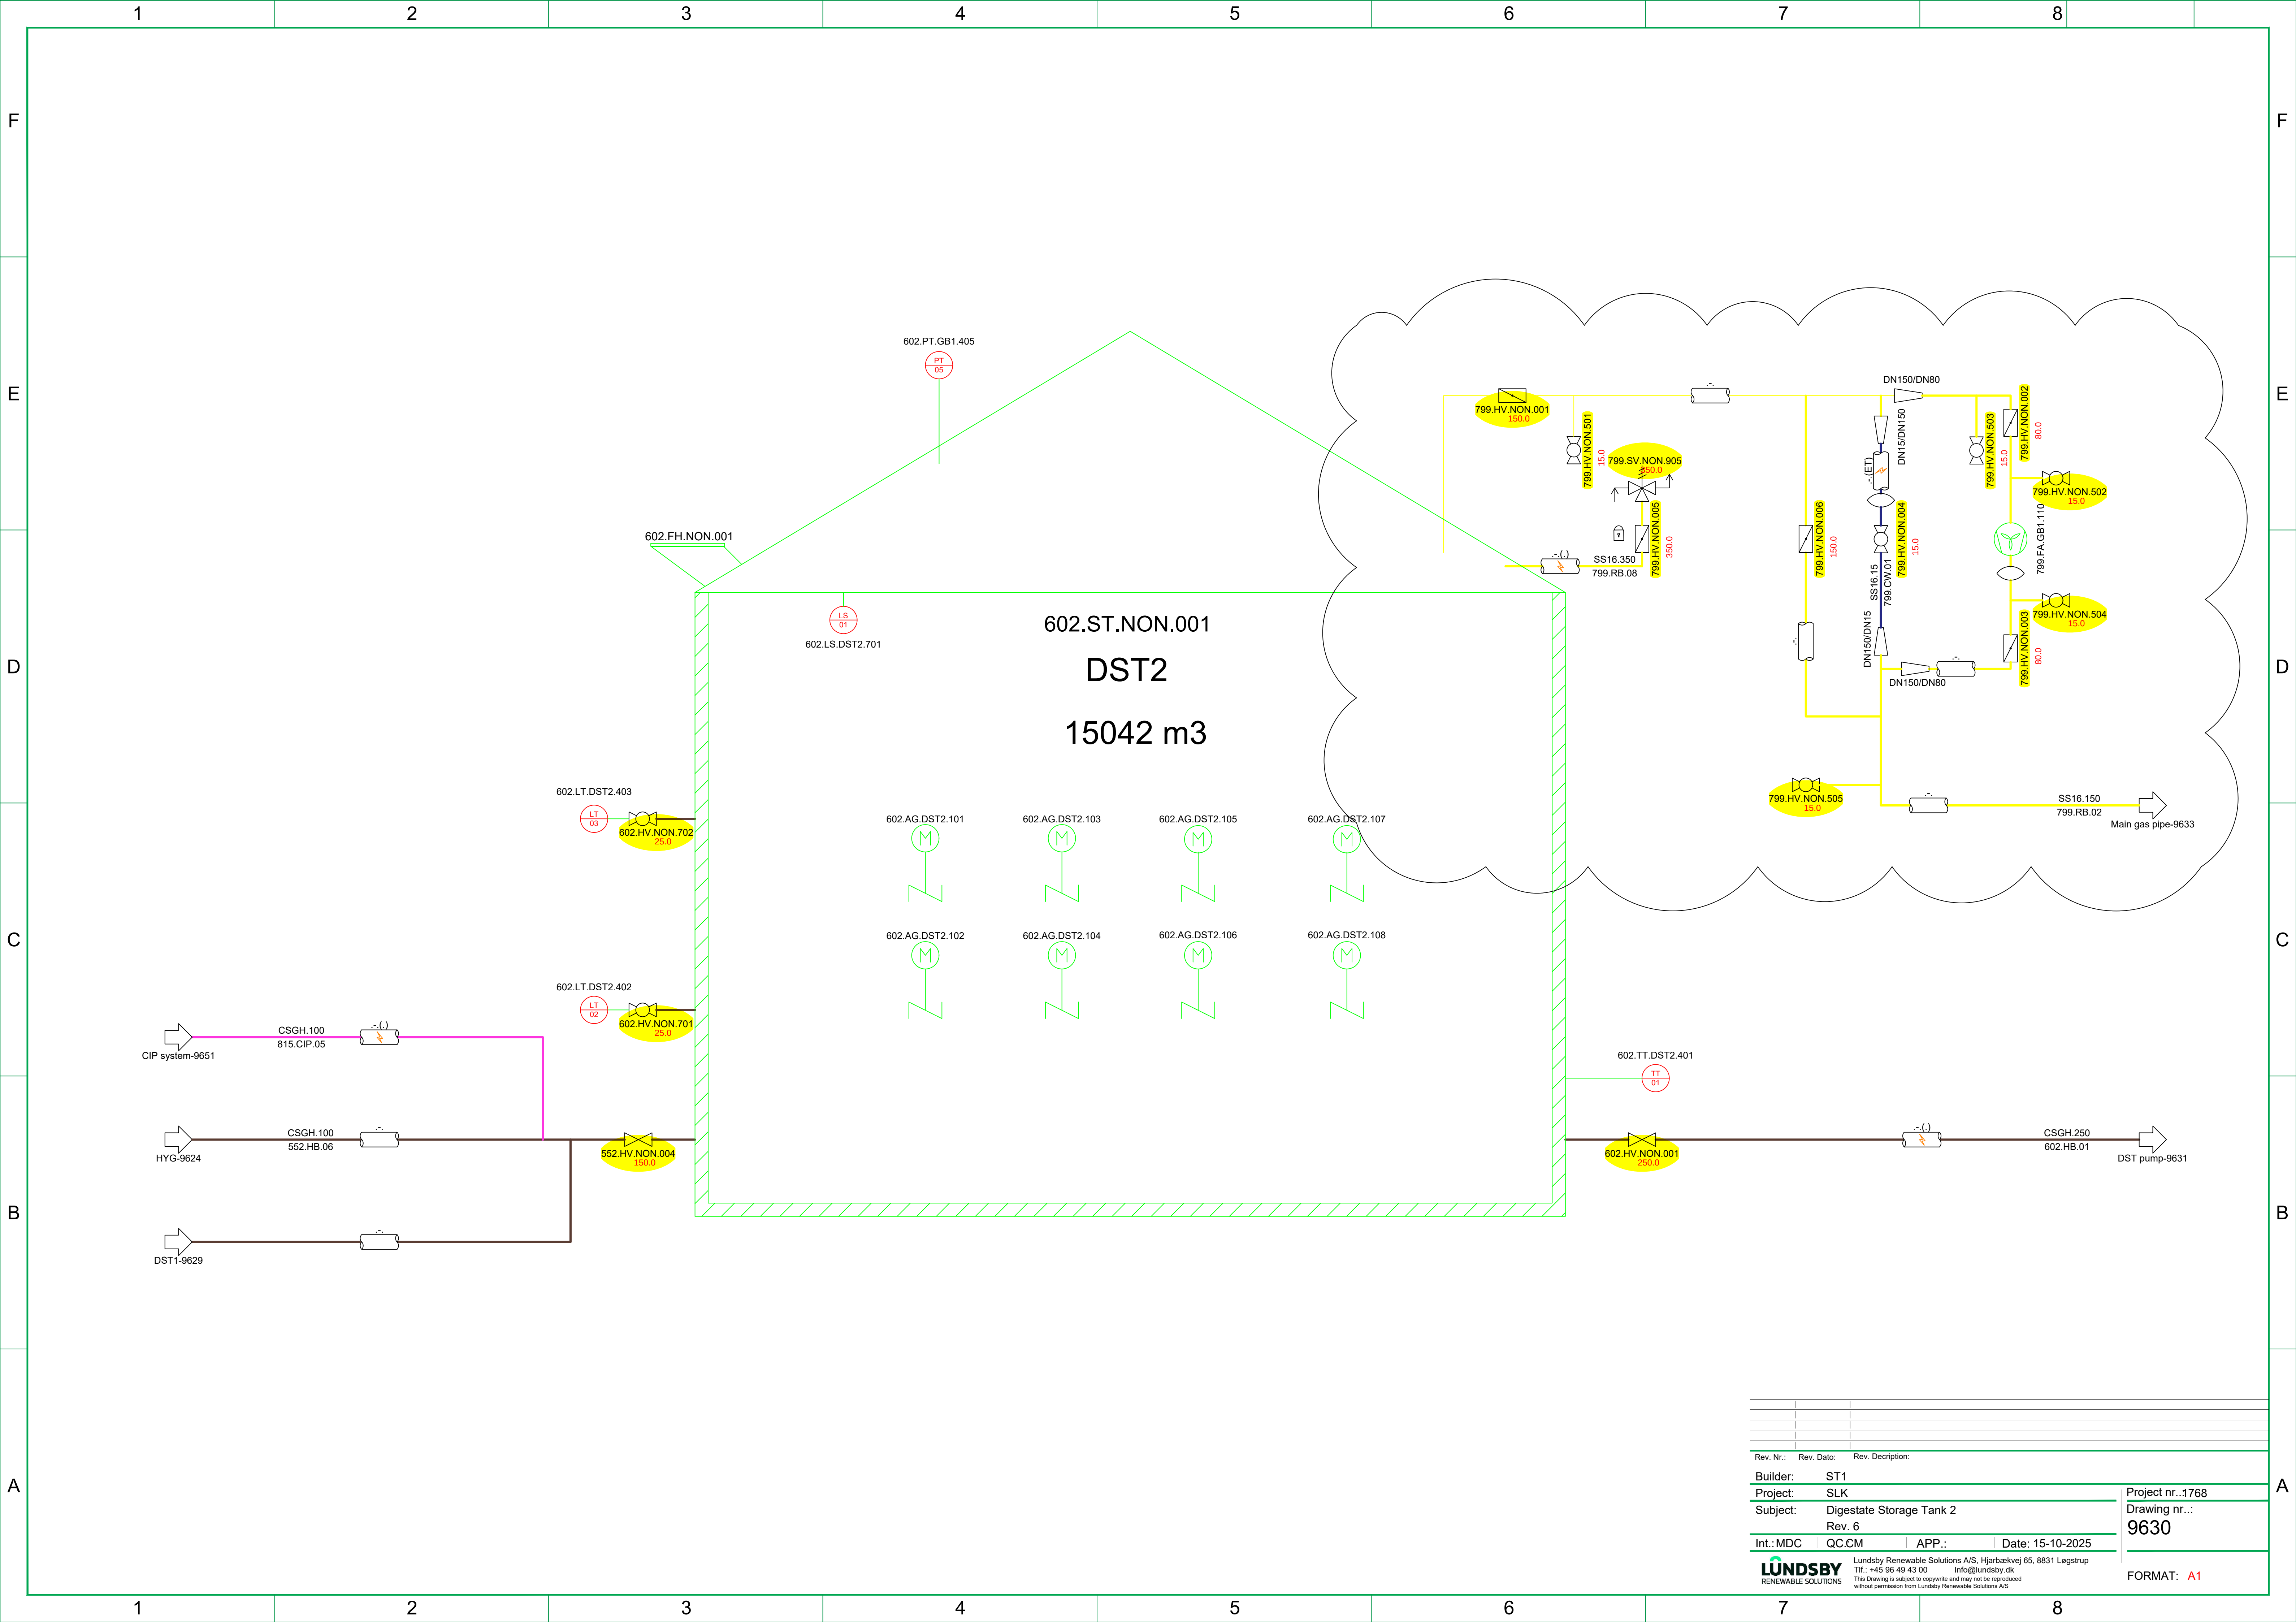

Rev. Nr.:	Rev. Dato:	Rev. Description:
Builder:	ST1	
Project:	SLK	
Subject:	Digestate Storage Tank 2	
Rev. 6		
Int.:MDC	QC:CM	APP.:
Date: 15-10-2025		
LUNDSBY RENEWABLE SOLUTIONS		
Lundsby Renewable Solutions A/S, Hjarbrækvej 65, 8831 Lægstrup Tlf.: +45 96 49 43 00 Info@lundsby.dk This Drawing is subject to copyright and may not be reproduced without permission from Lundsby Renewable Solutions A/S		
Project nr...1768		Drawing nr...: 9630
FORMAT: A1		

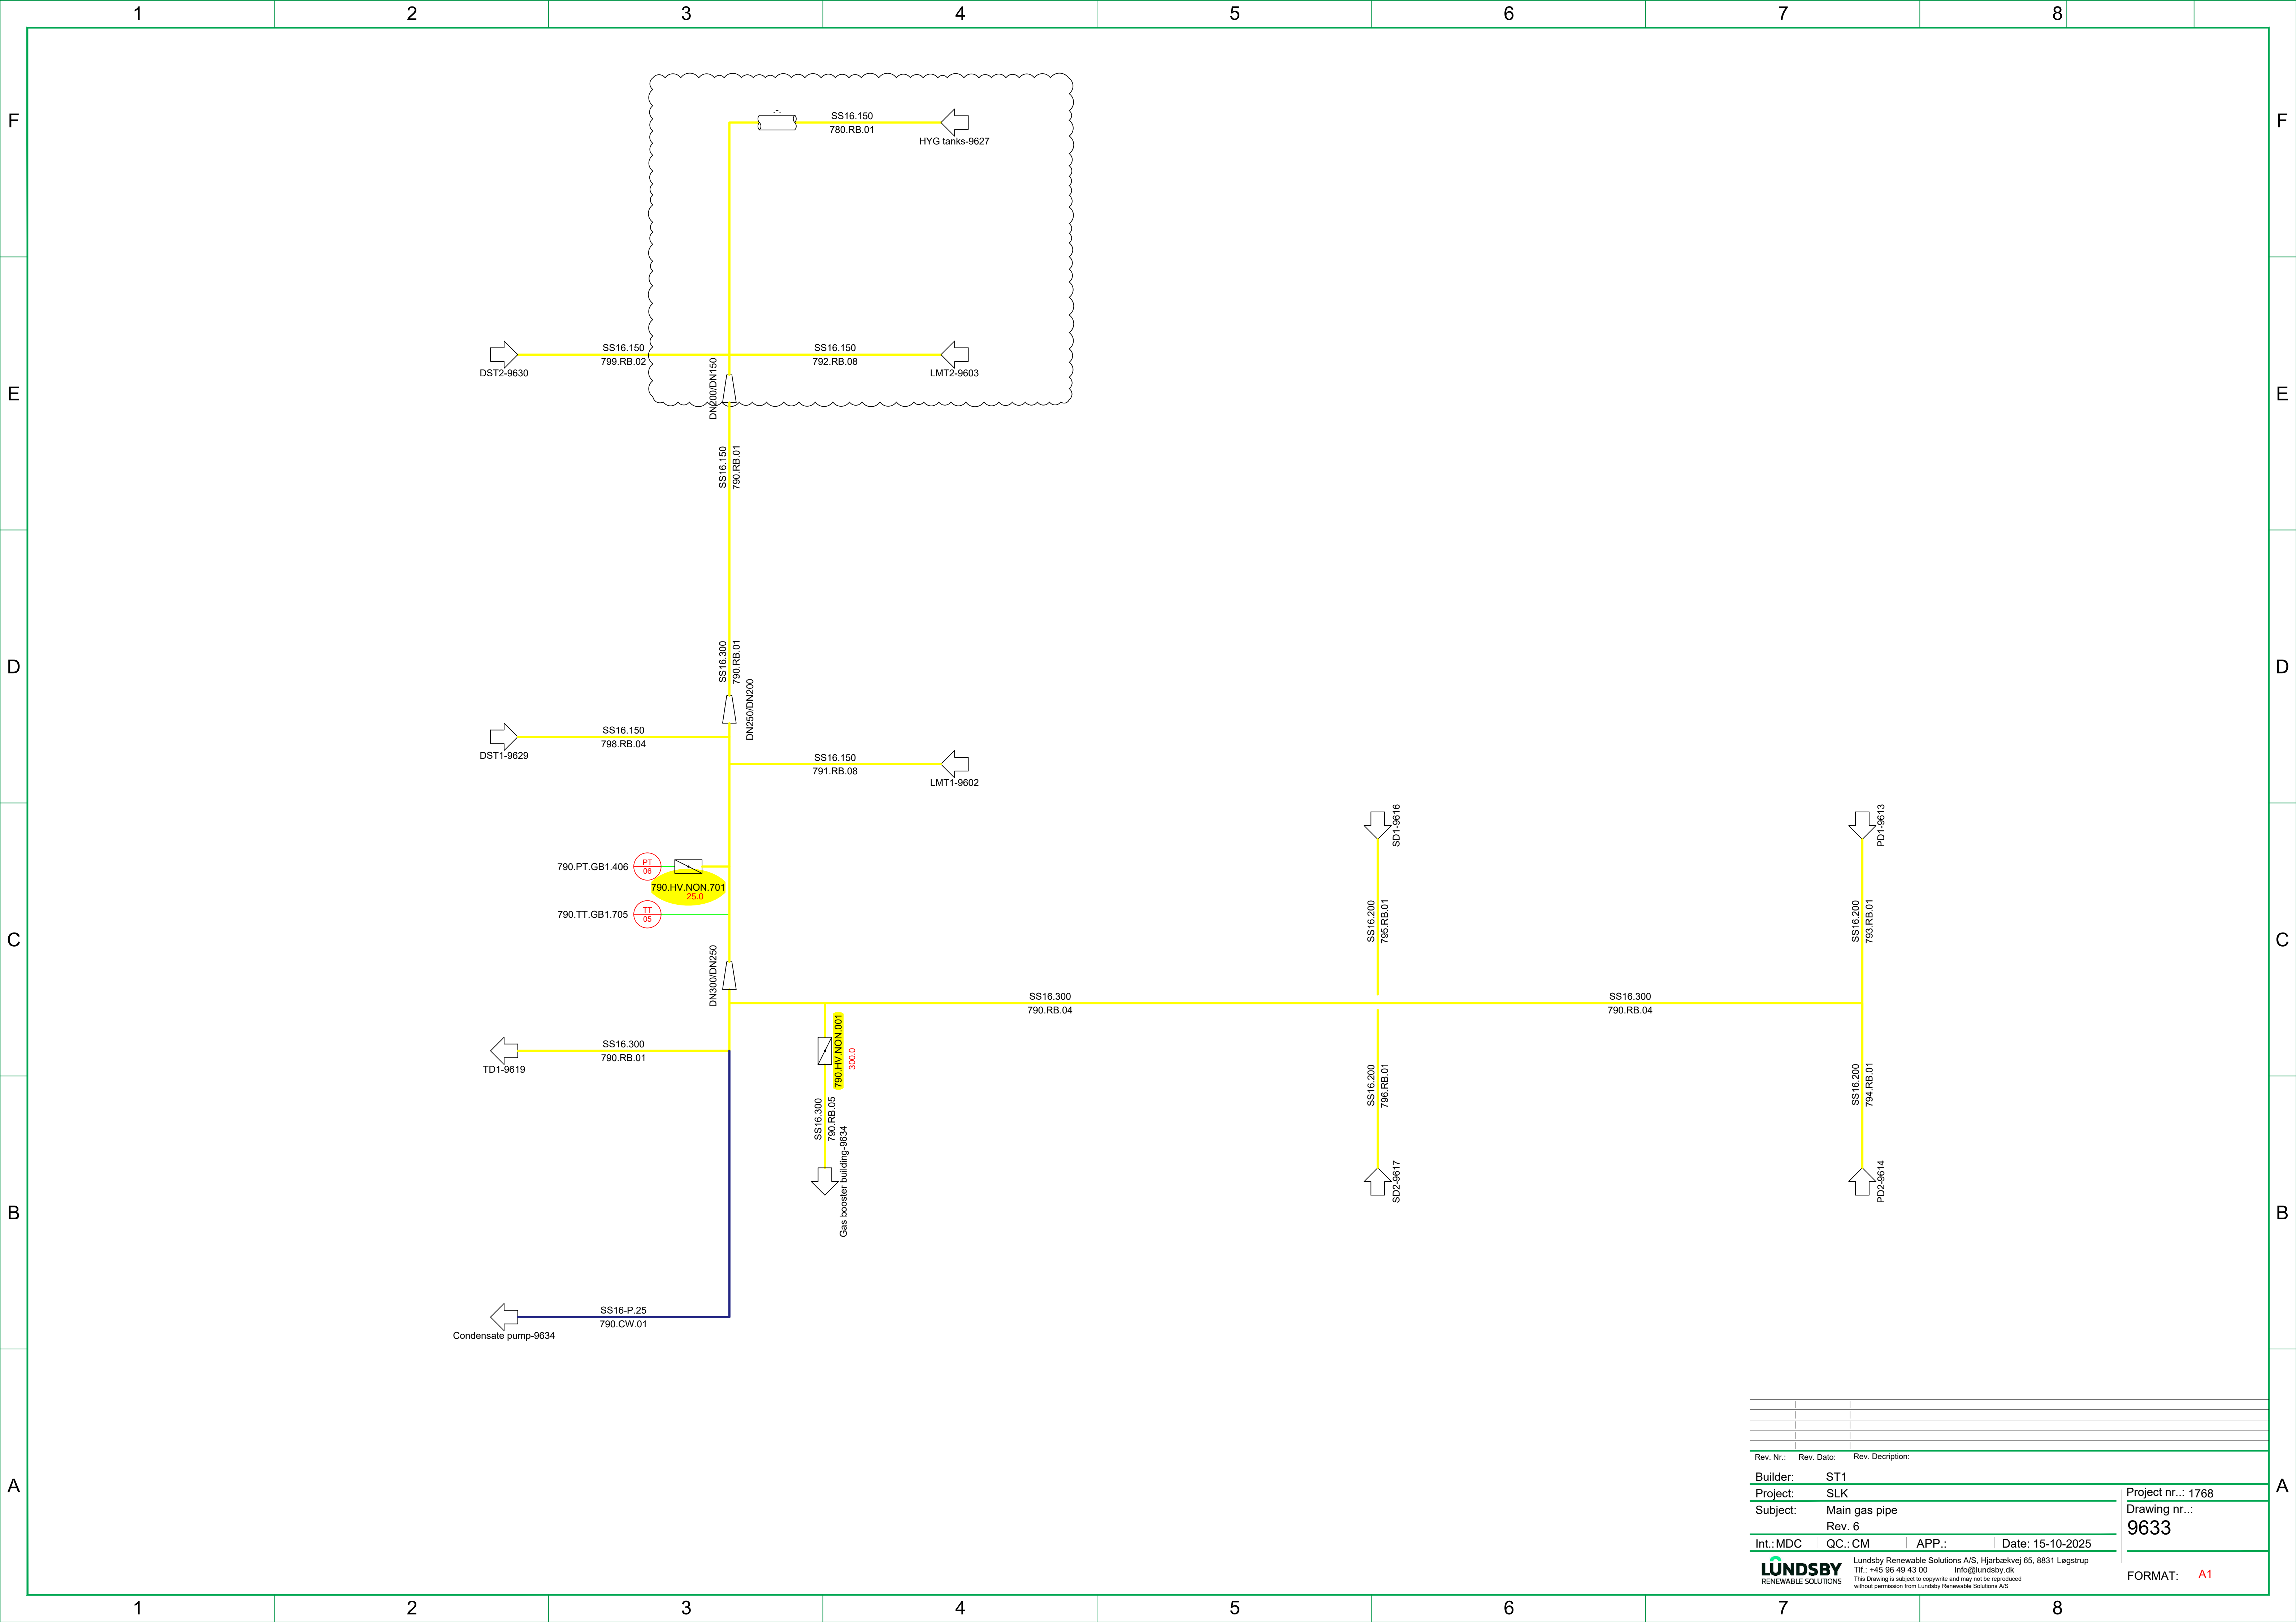


Rev. Nr.:	Rev. Date:	Rev. Description:	
Builder:	ST1		
Project:	SLK		
Subject:	Main gas pipe		
Rev. 6			
Int.:MDC	QC.:CM	APP.:	Date: 15-10-2025
LUNDSBY RENEWABLE SOLUTIONS			Lundsgby Renewable Solutions A/S, Hjarbrækvej 65, 8831 Løgstrup Tlf.: +45 96 49 43 00 Info@lundsgby.dk This Drawing is subject to copyright and may not be reproduced without permission from Lundsgby Renewable Solutions A/S
Project nr.: 1768 Drawing nr.: 9633			FORMAT: A1

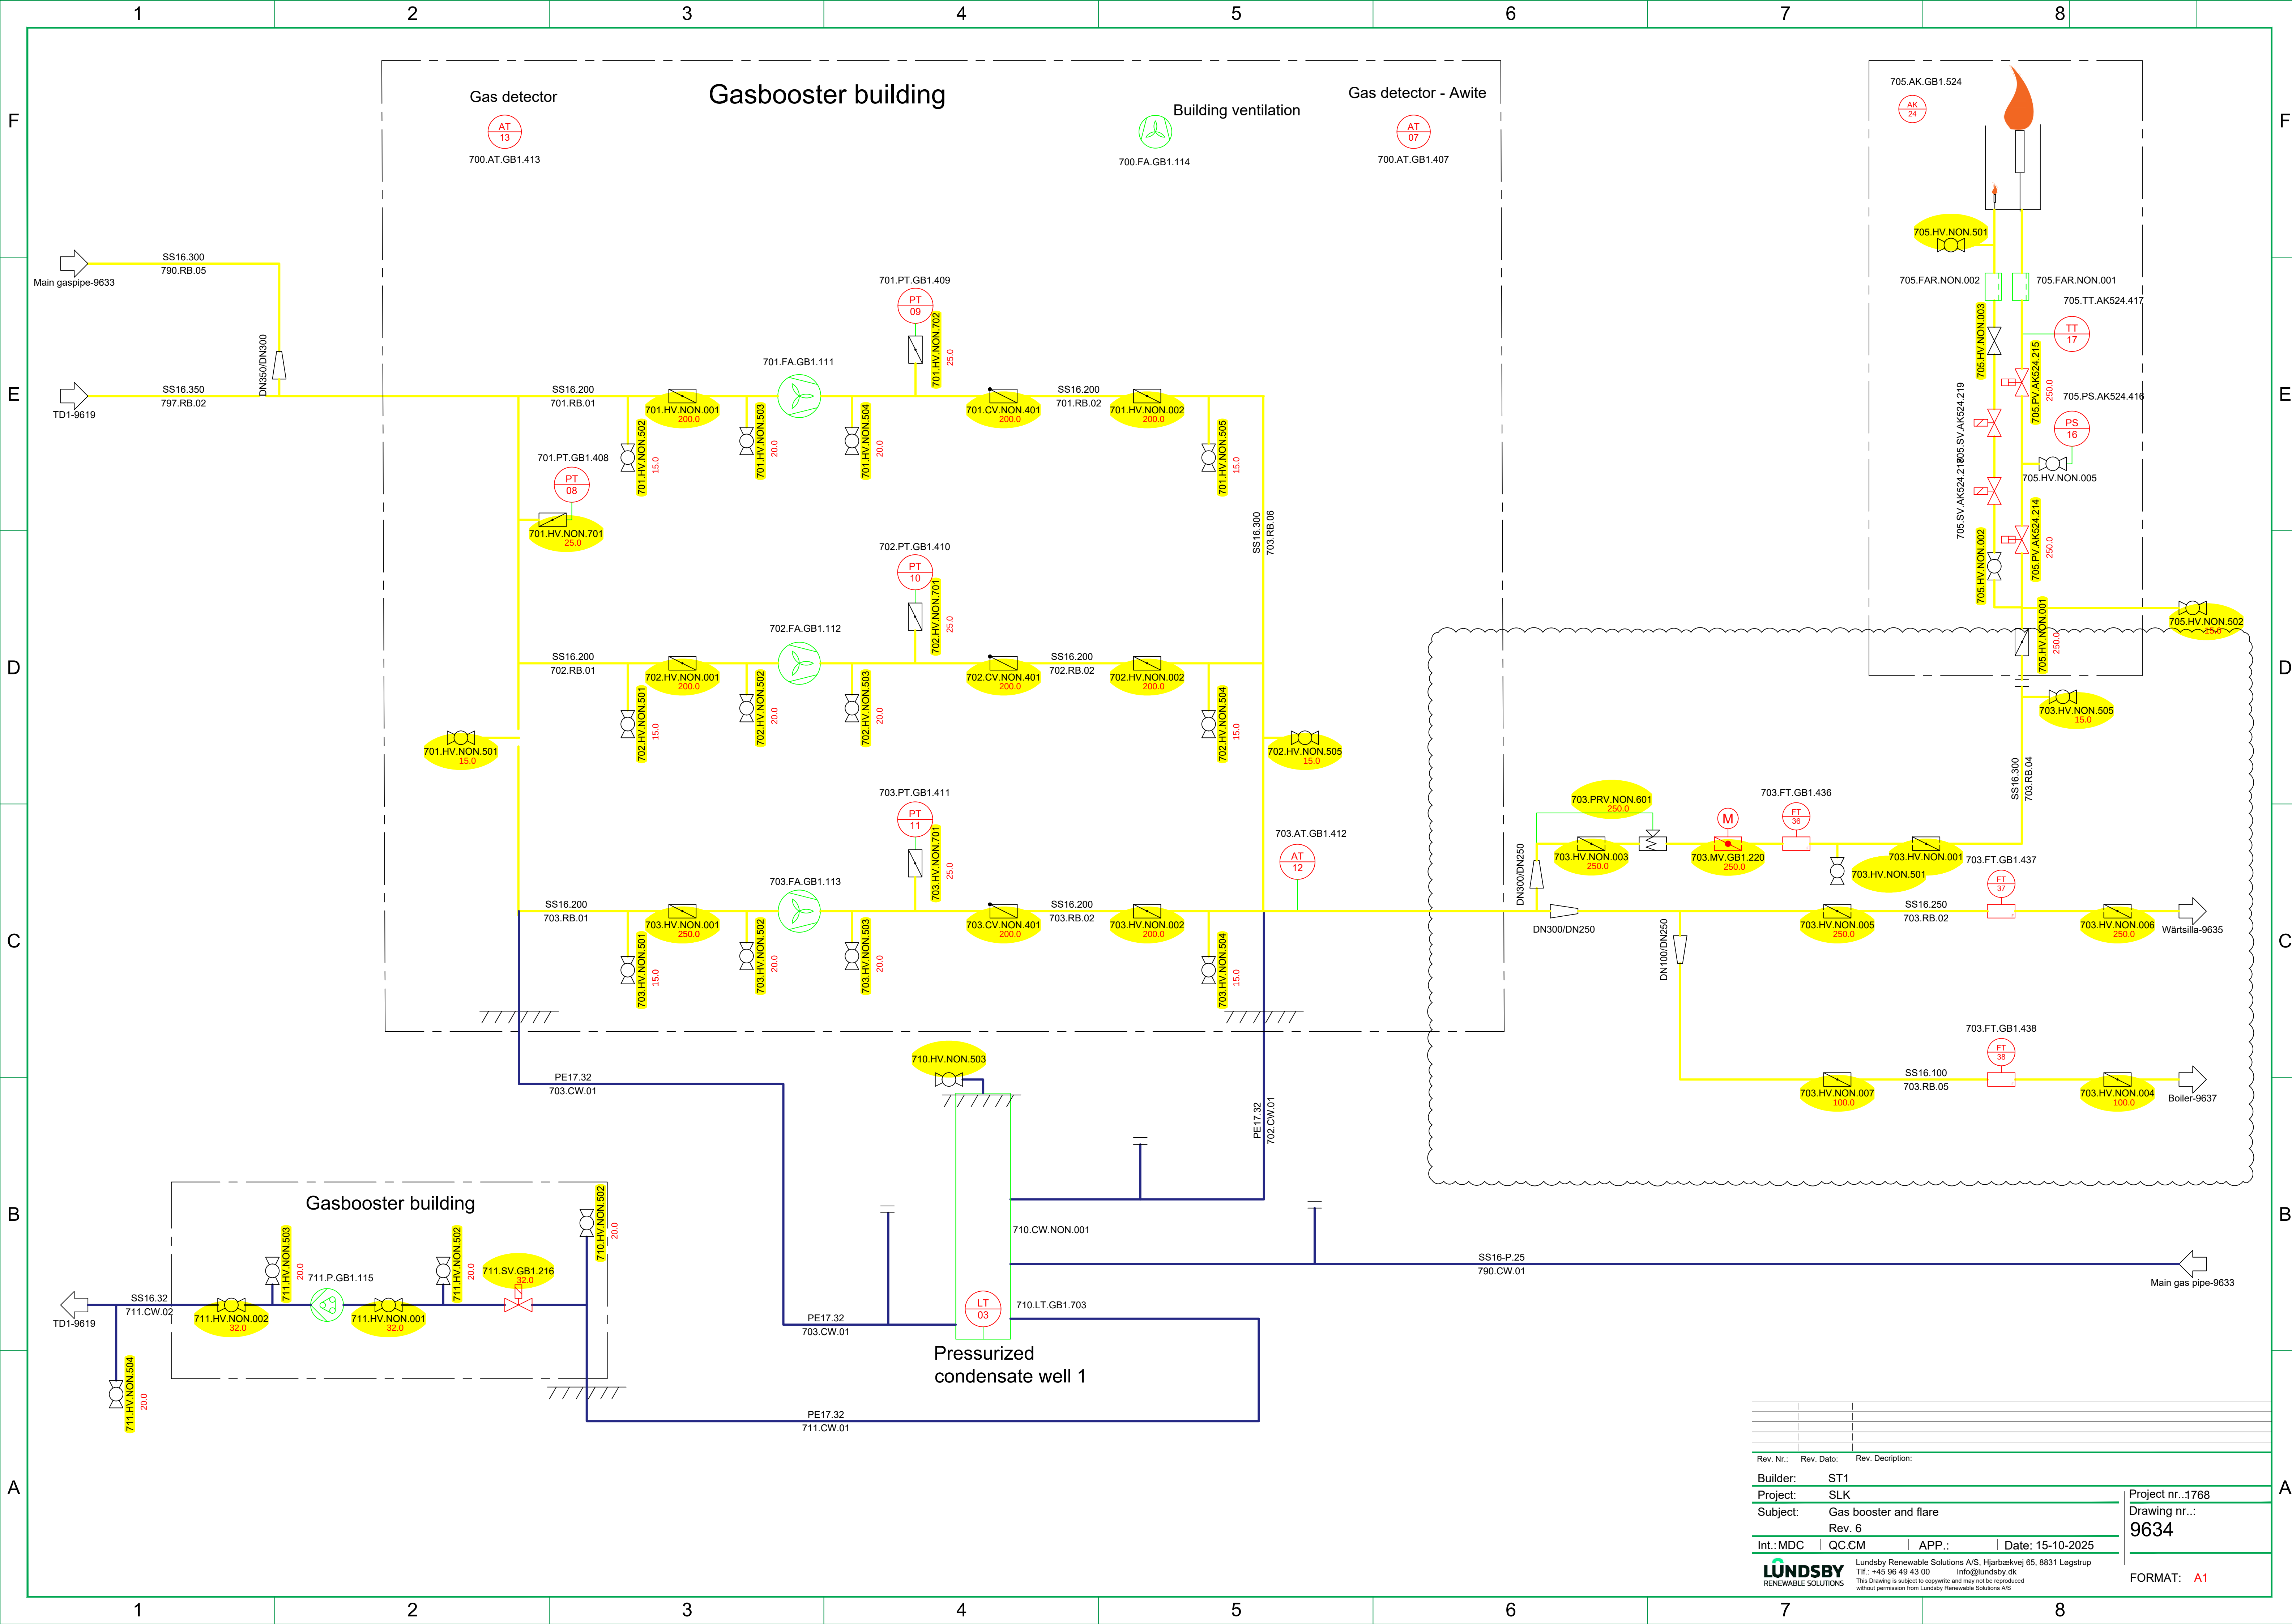


Wärtsillä

730-UPG-01

730-LBG-01

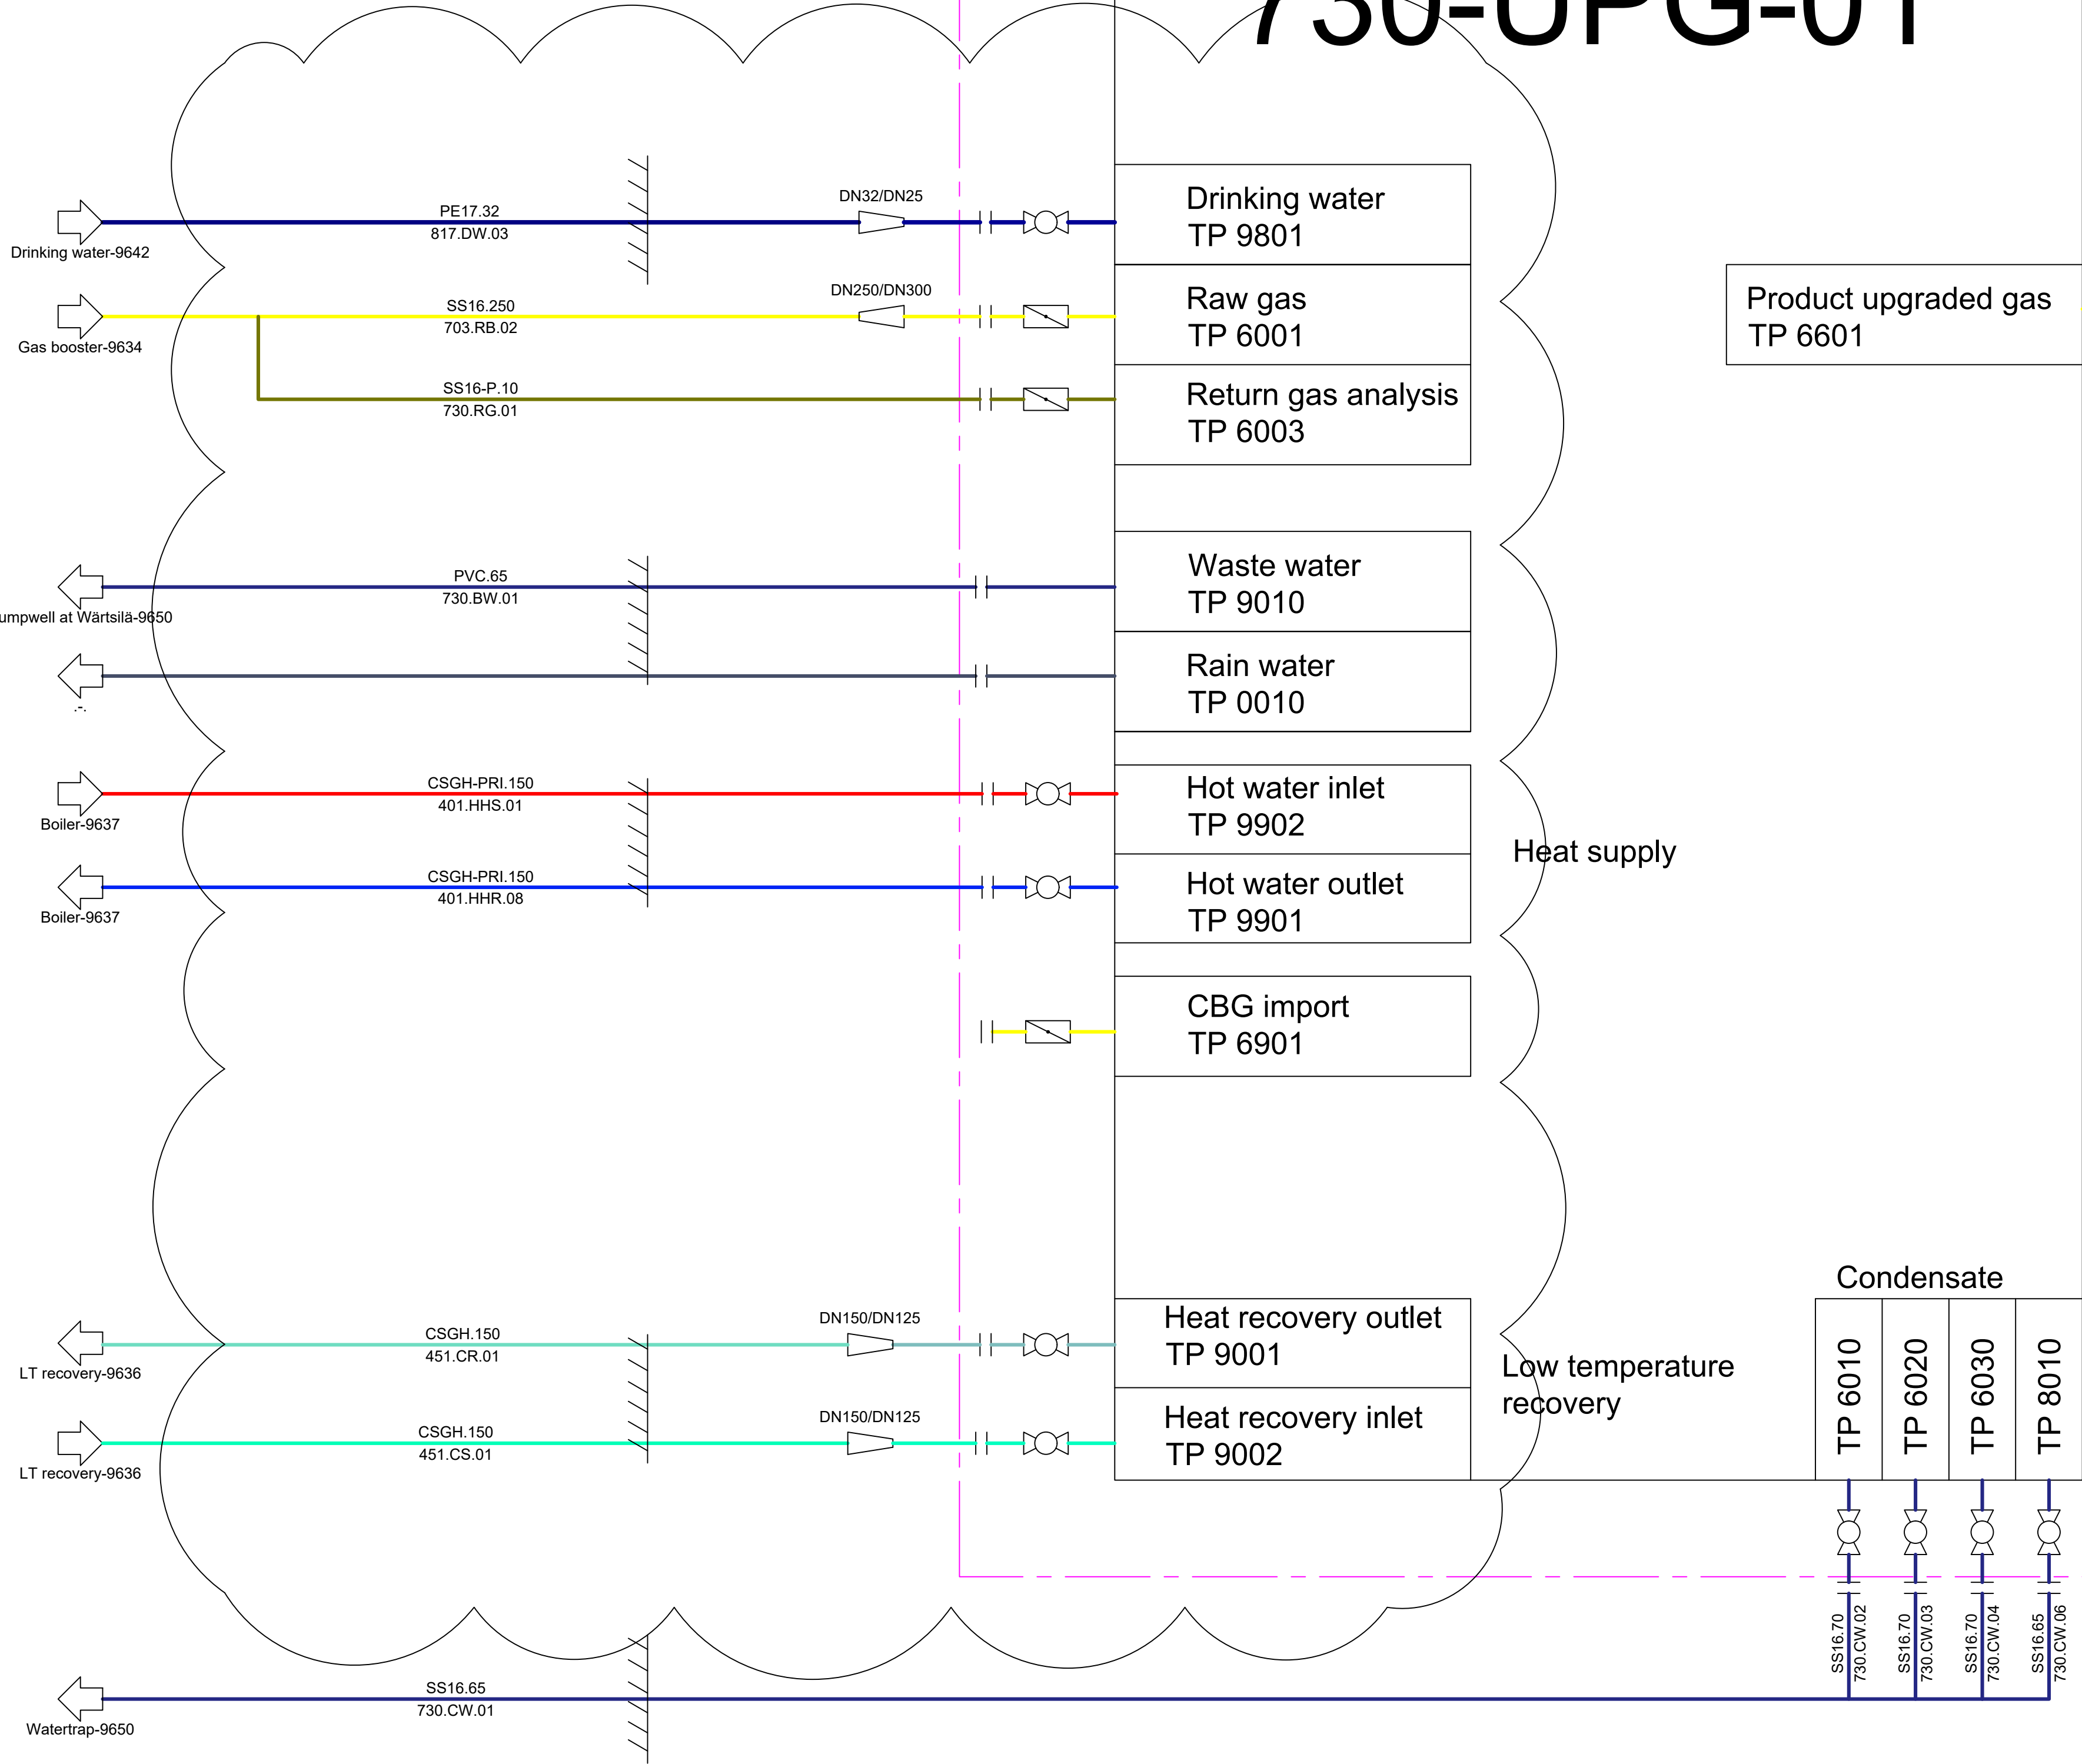


Product upgraded gas
TP 6601

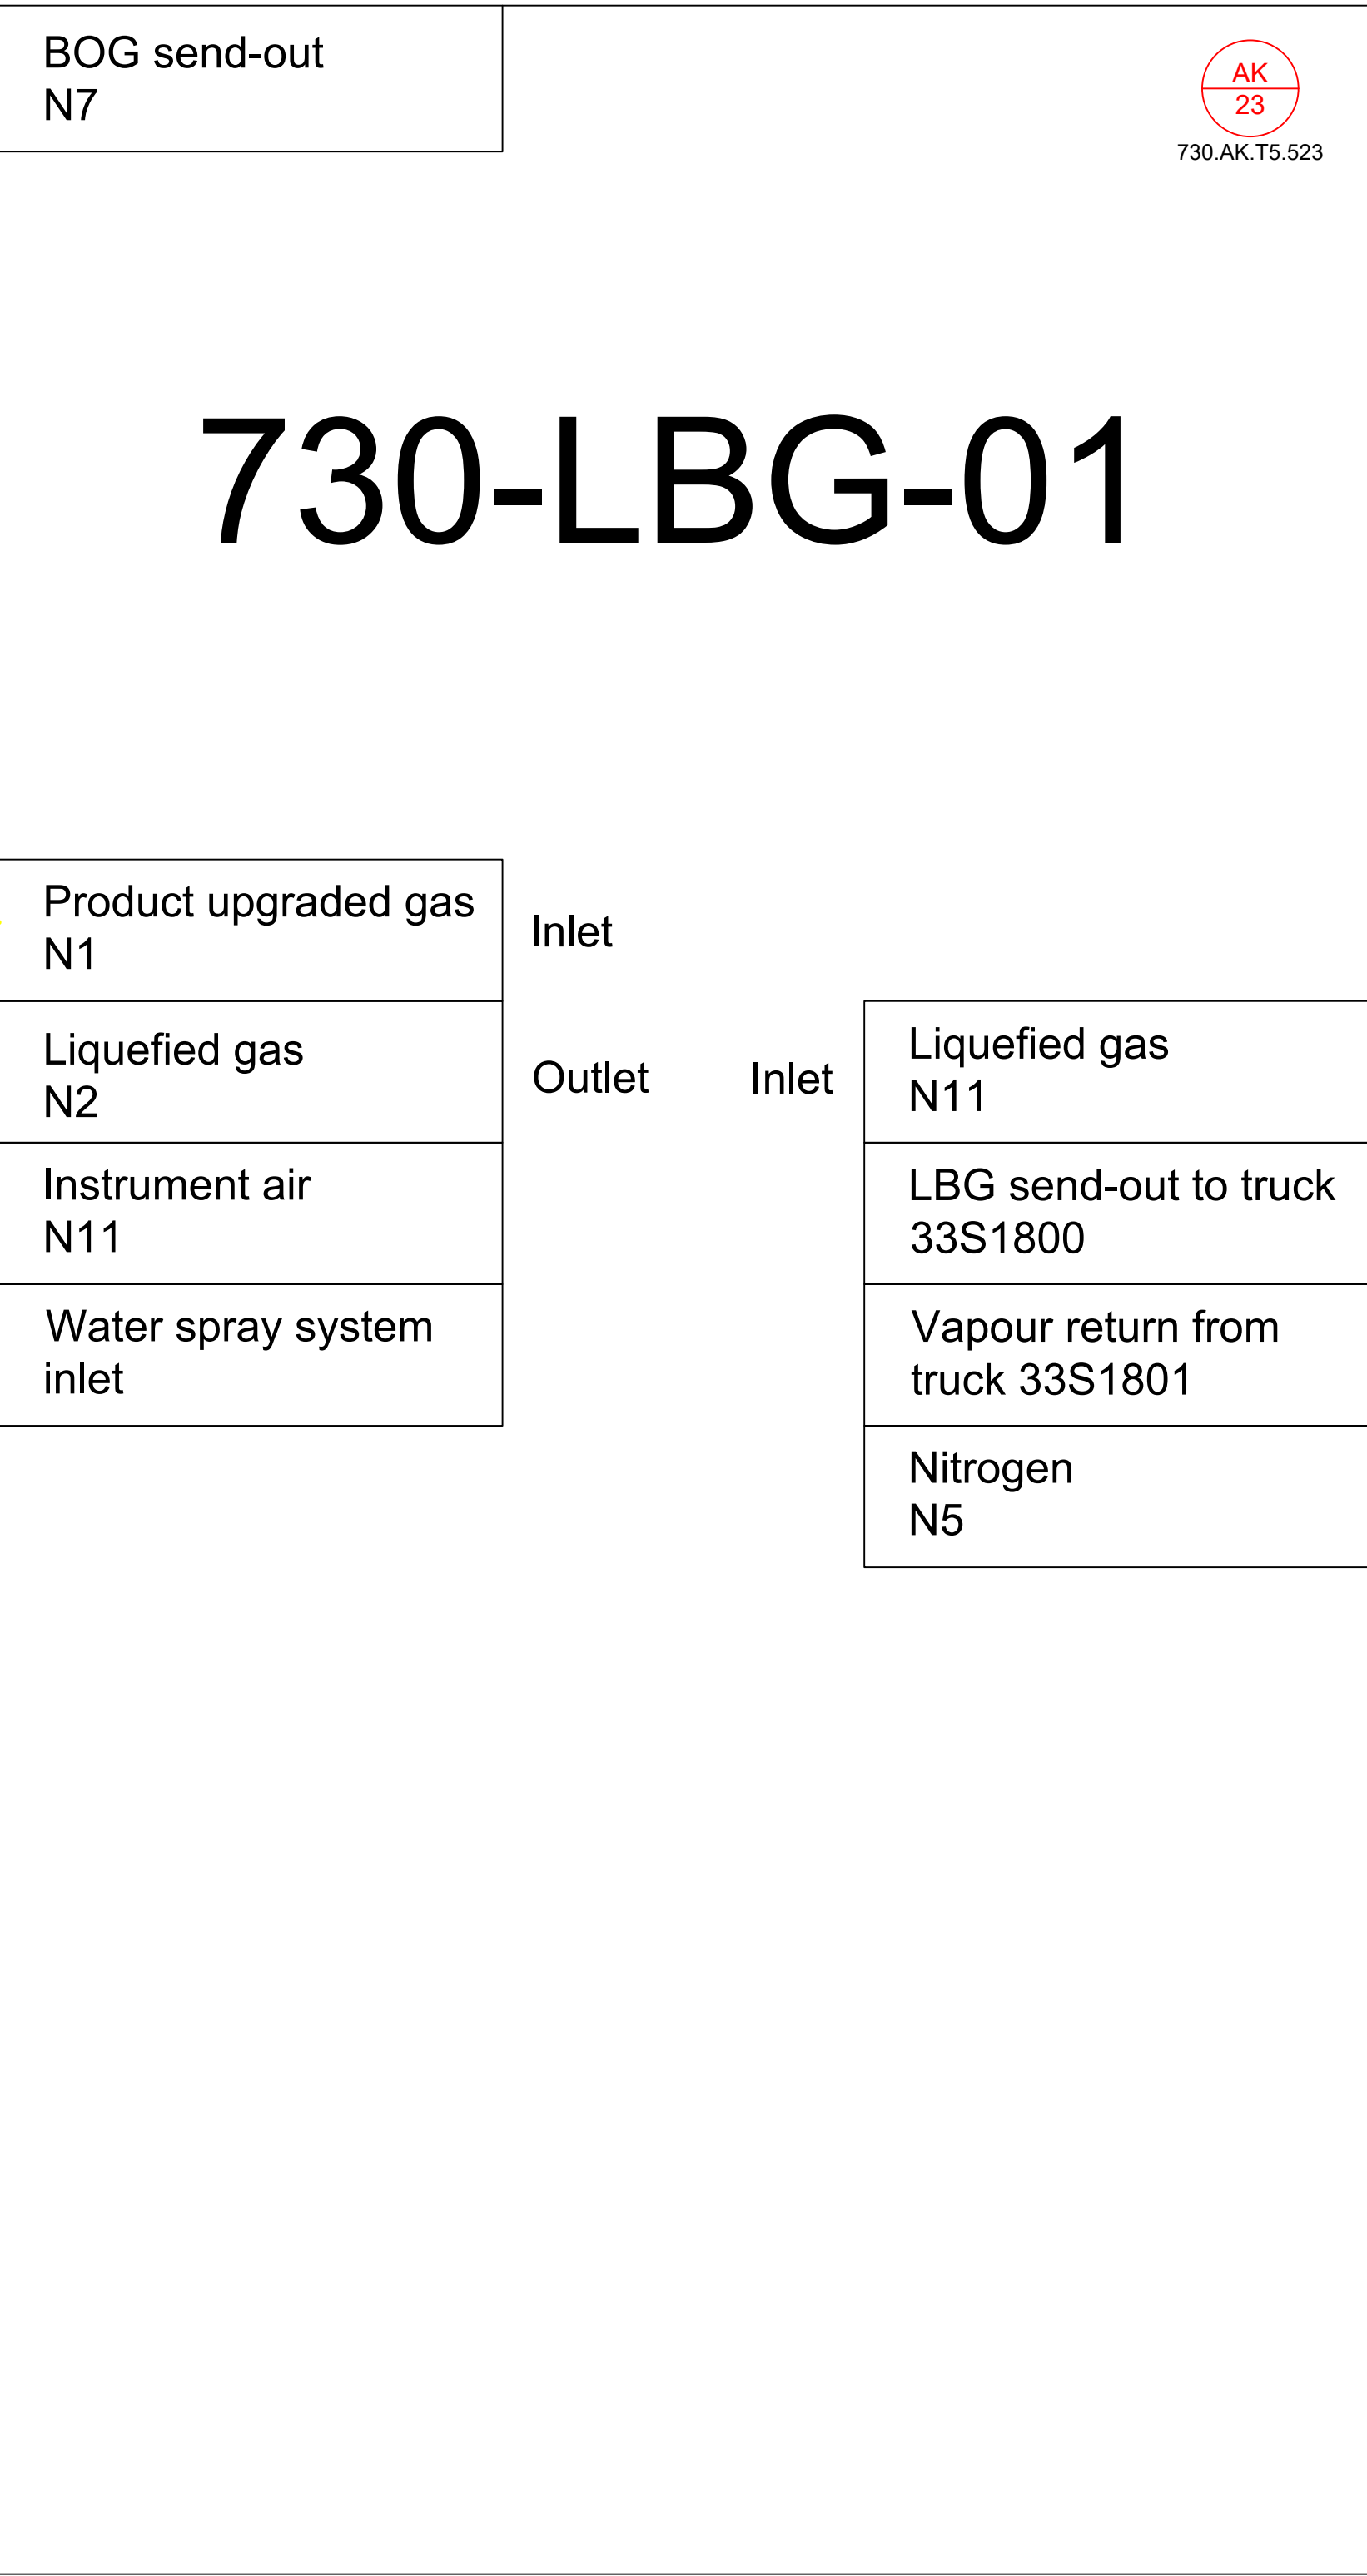


Rev. Nr.:	Rev. Dato:	Rev. Description:
Builder:	ST1	
Project:	SLK	
Subject:	Upgrade	
	Rev. 6	
Int.:MDC	QC.CM	APP.:
		Date: 15-10-2025
LUNDSBY RENEWABLE SOLUTIONS		
Lundsbys Renewable Solutions A/S, Hjarbækvej 65, 8831 Løgstrup Tlf.: +45 96 49 43 00 Info@lundsbys.dk This Drawing is subject to copyright and may not be reproduced without permission from Lundsbys Renewable Solutions A/S		
Project nr...:1768		Drawing nr...: 9635
FORMAT: A1		


Technology building

Heat pump scope

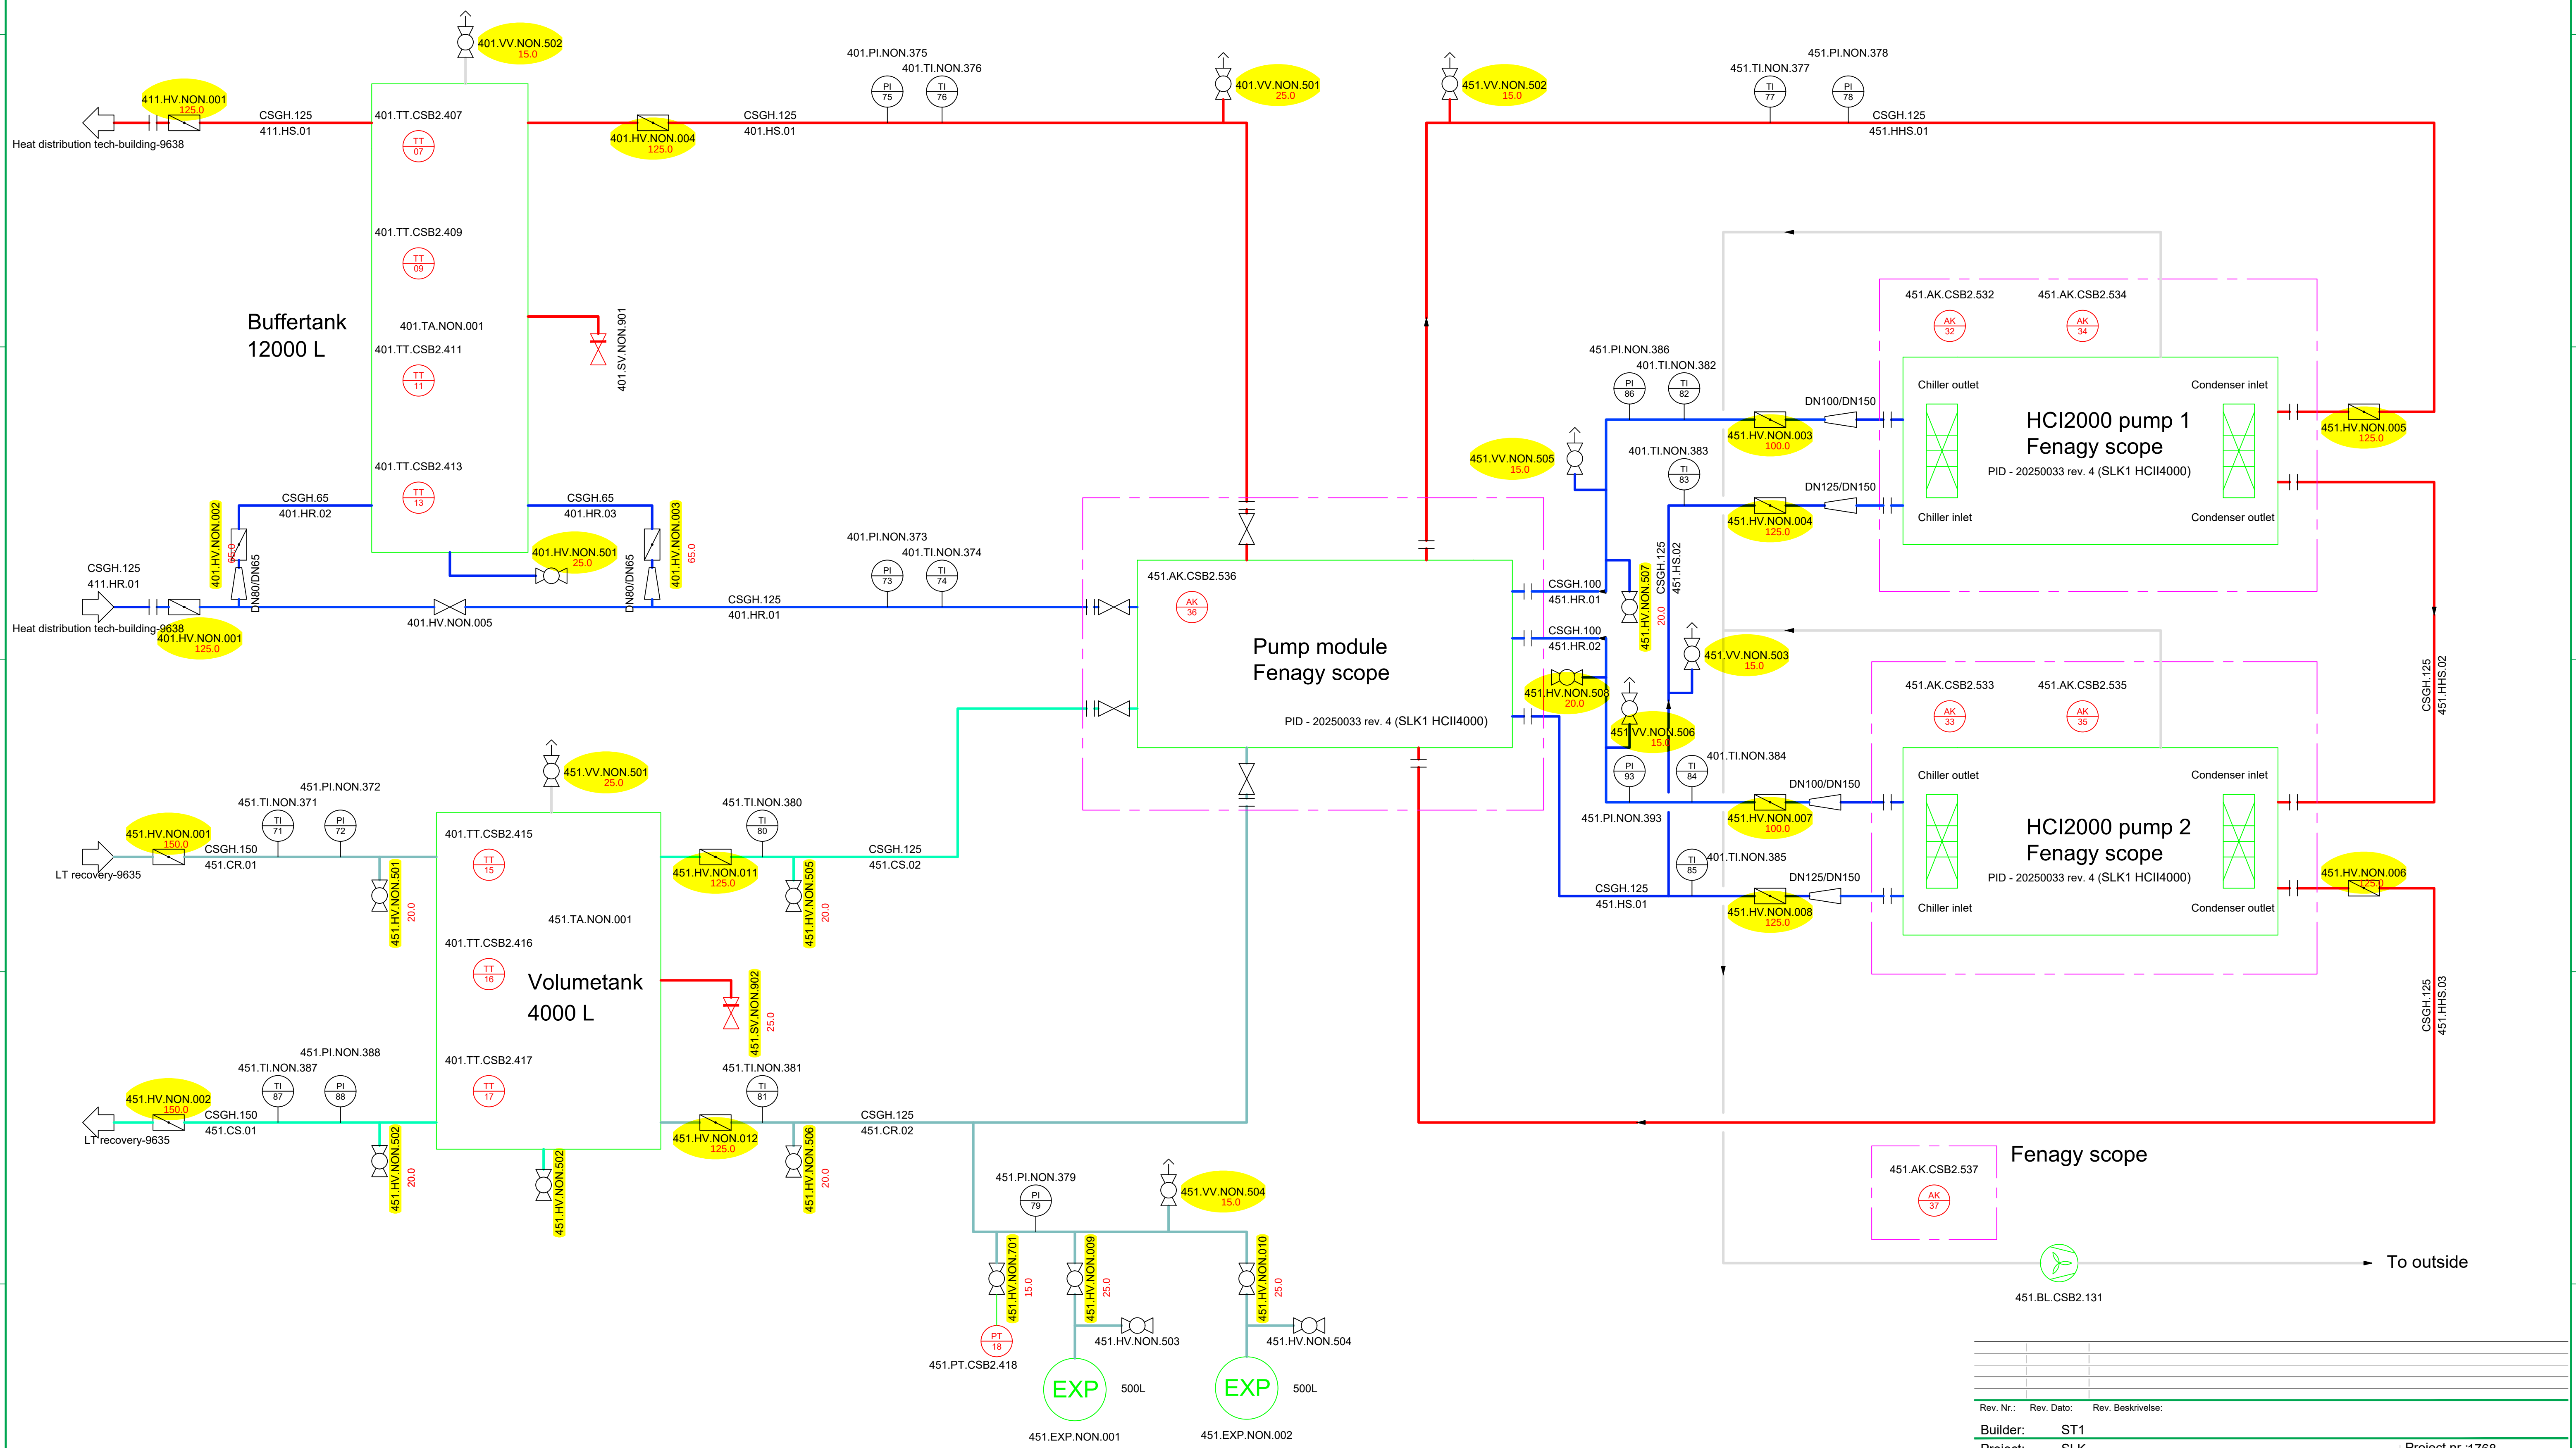

Rev. Nr.:	Rev. Dato:	Rev. Beskrivelse:
Builder:	ST1	
Project:	SLK	
Subject:	Heat pumps	
Rev.:	6	
Int.:MDC	QC: CM	APP.:
Date:	15-10-2025	
LUNDSBY RENEWABLE SOLUTIONS		
Lundsby Biogas A/S, Hjarbækvej 65, 8831 Løgstrup Tlf.: +45 96 49 43 00 info@lundsbybiogas.dk		
Denne tegning er underlagt copywrite op på ikke reproduceres uden tilladelse fra Lundsbybiogas A/S		
Project nr.:1768		
Drawing nr.: 9636		
FORMAT: A1		

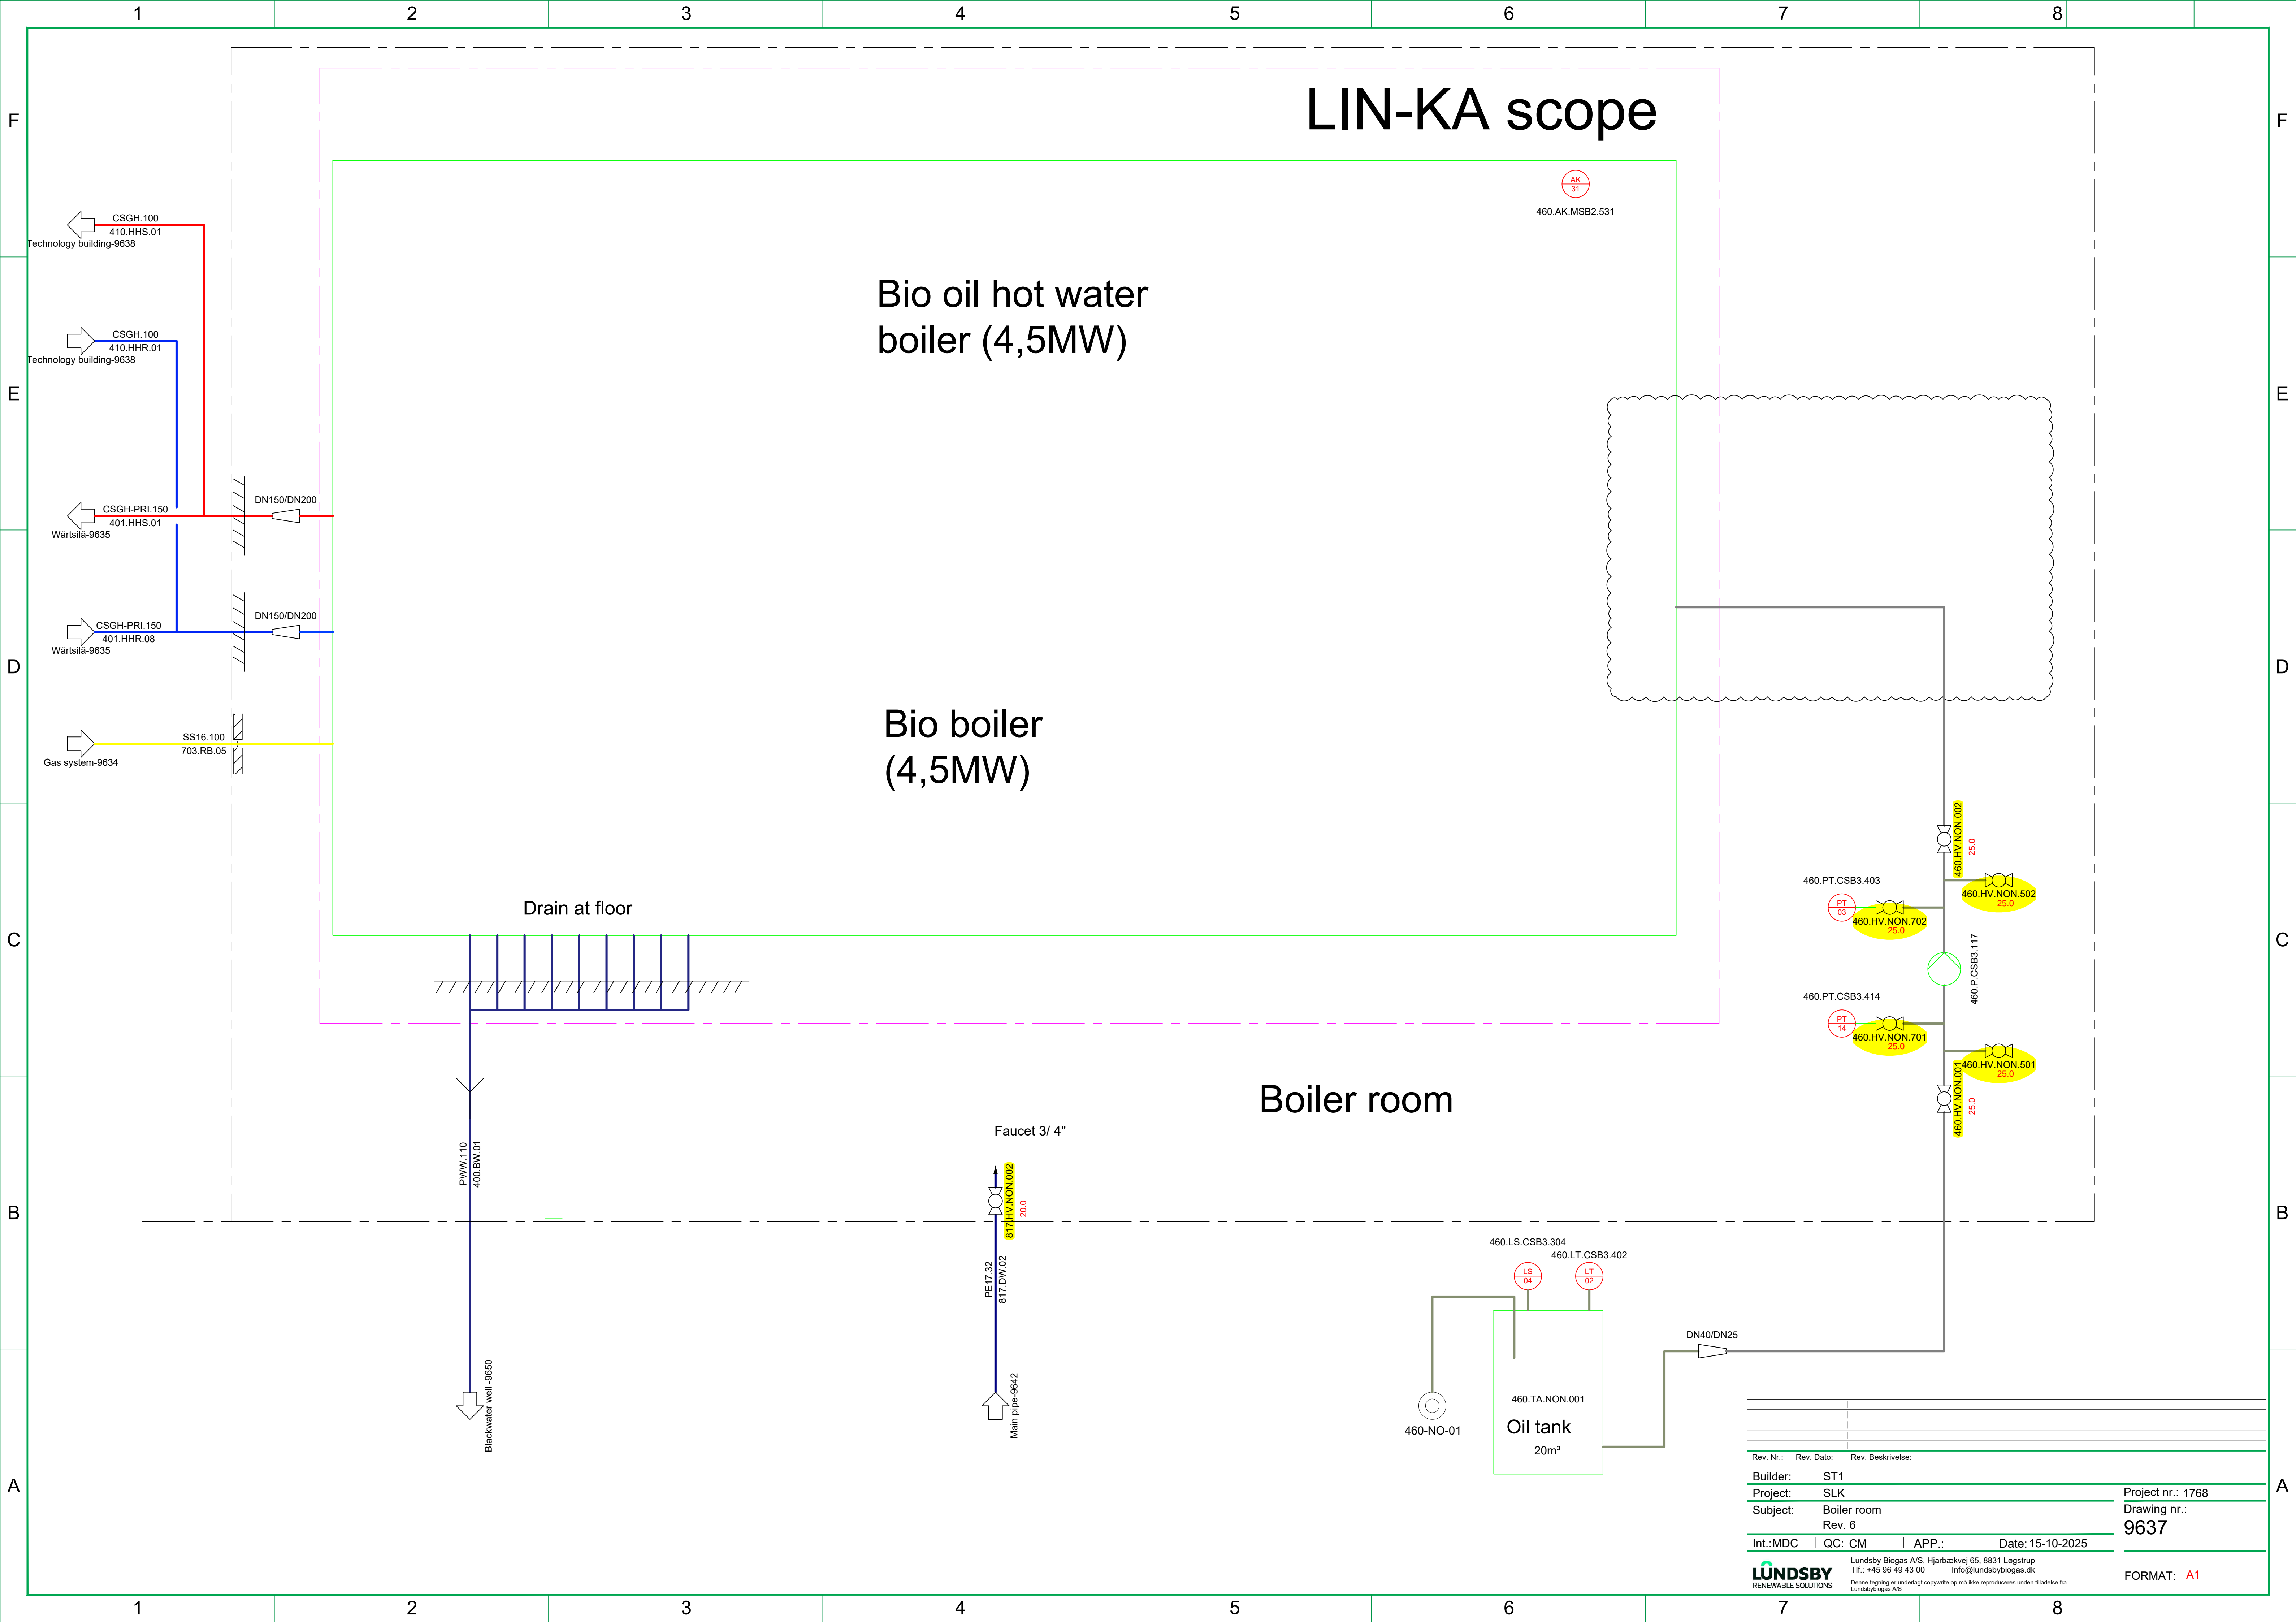

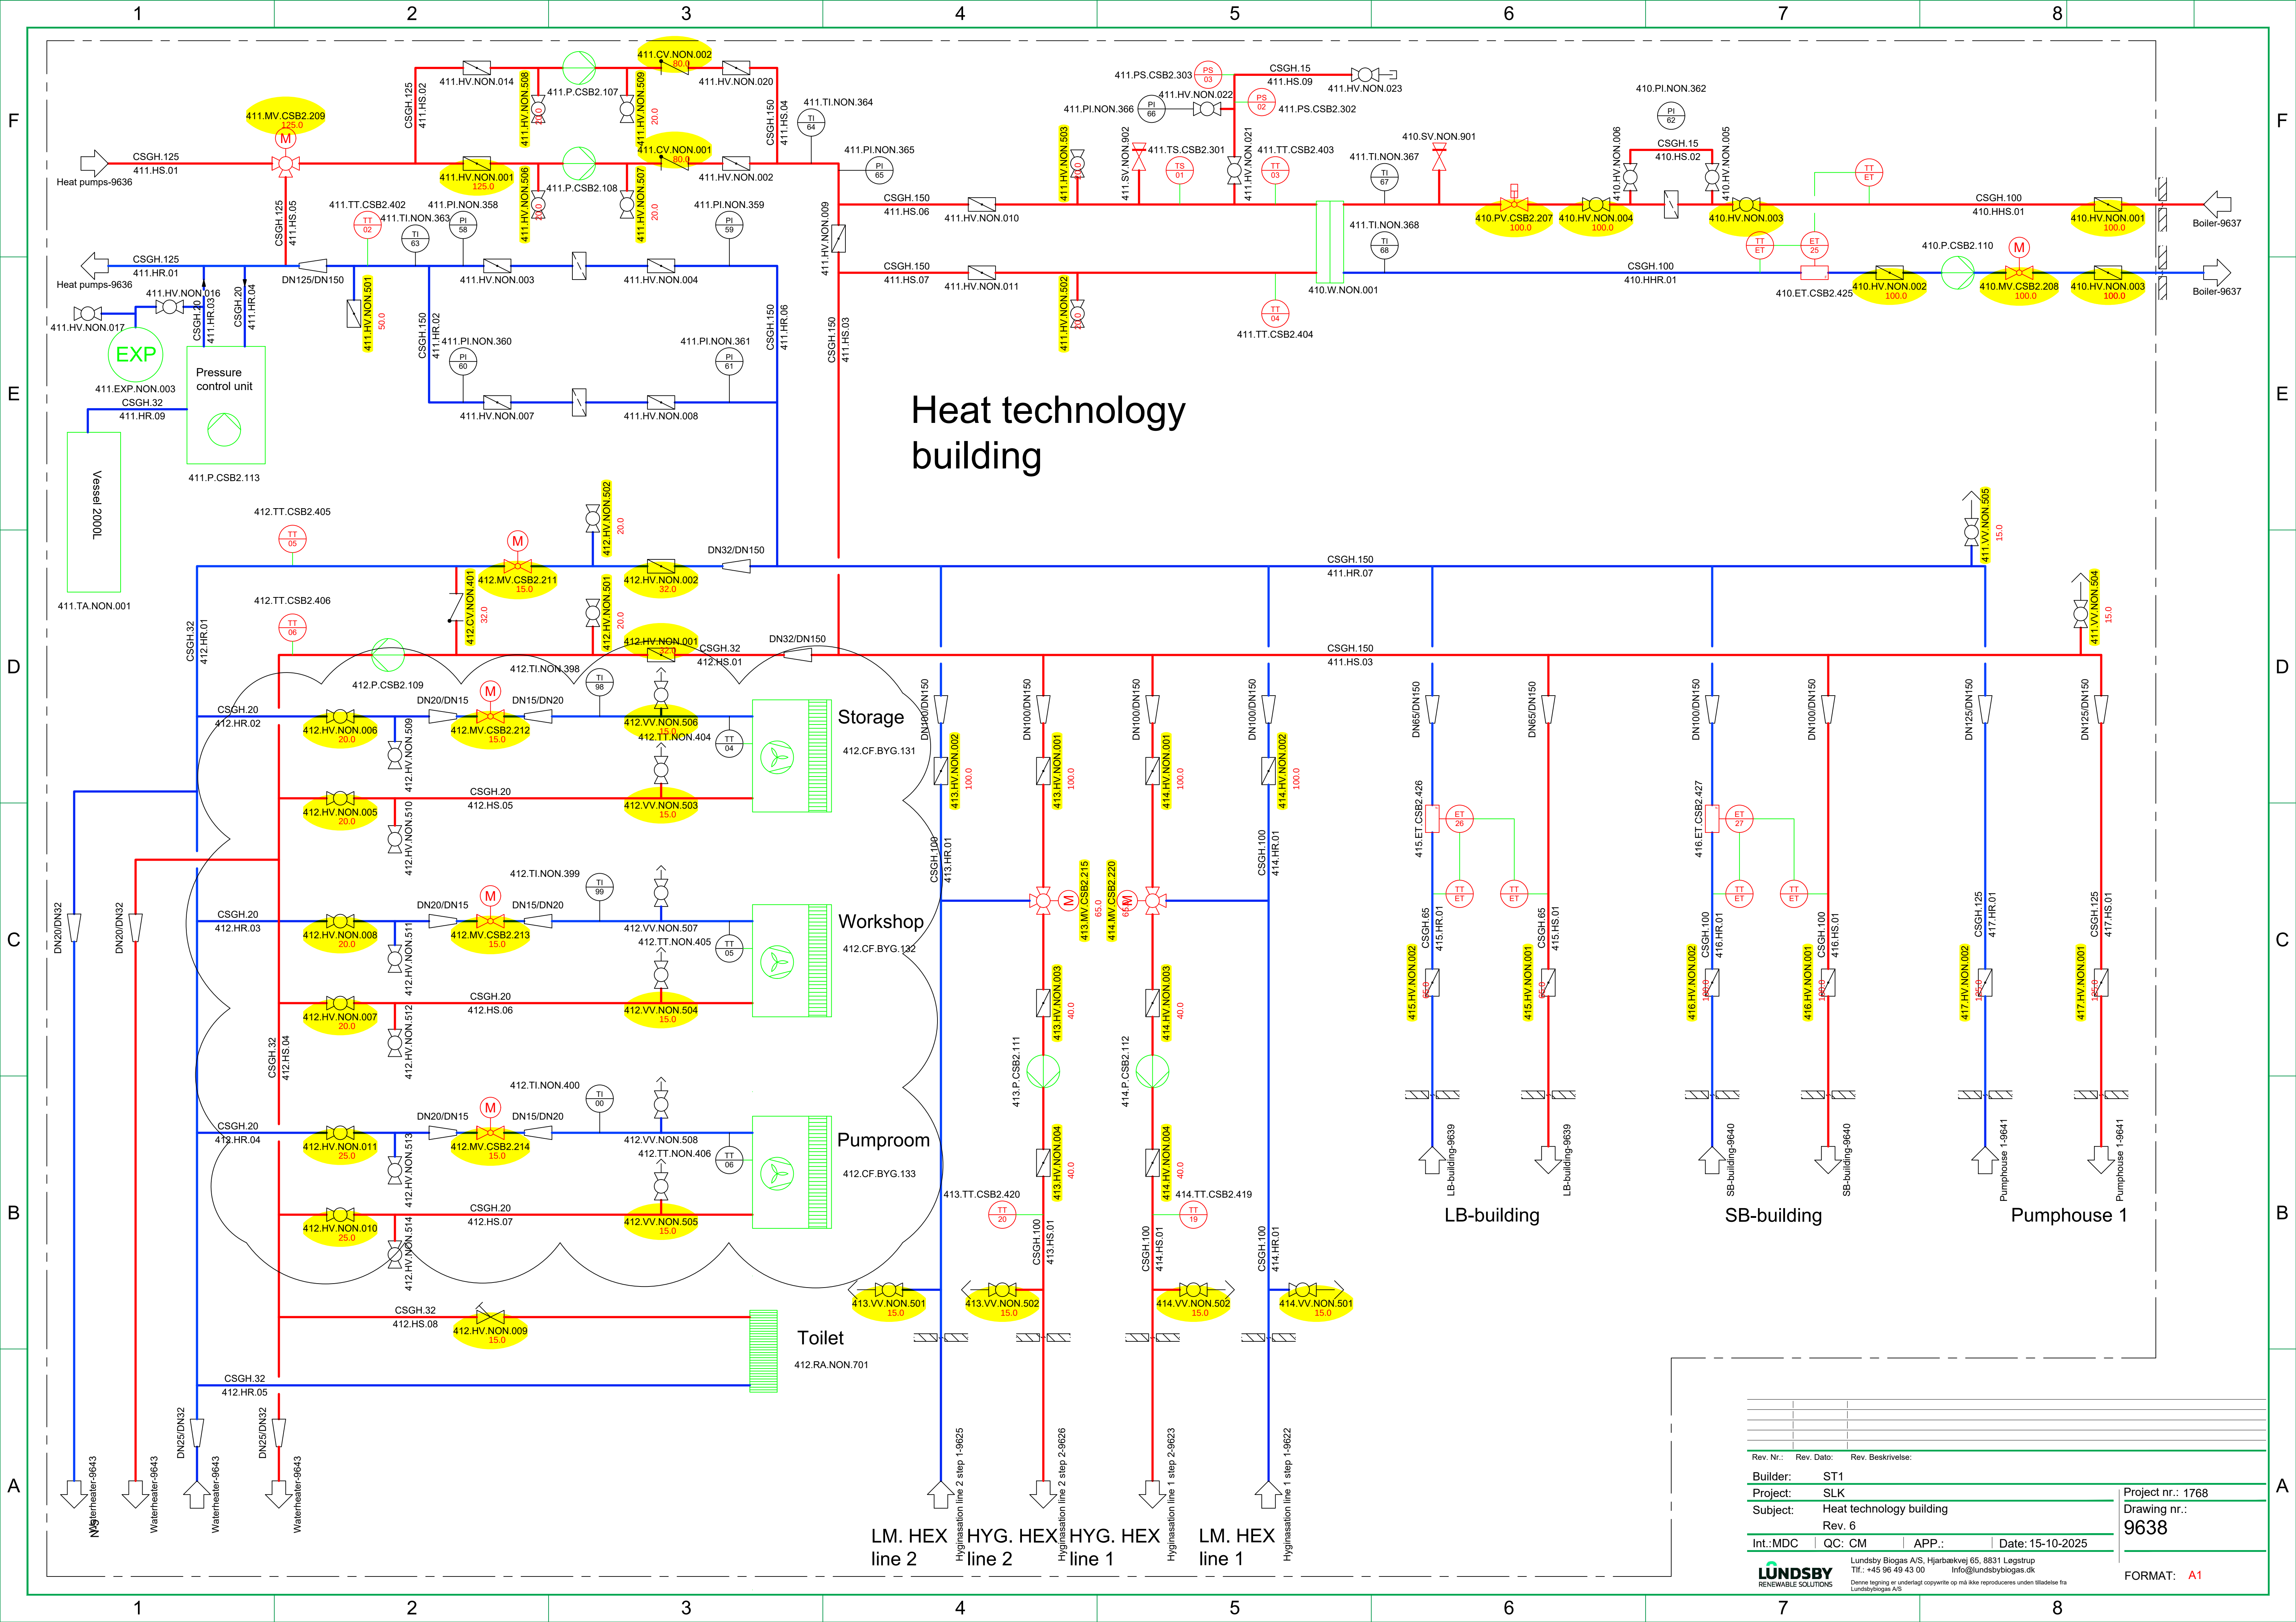

Heat technology building

Storage

Workshop

Pumproom

Toilet

LB-building

SB-building


Pumphouse 1

Rev. Nr.:	Rev. Dato:	Rev. Beskrivelse:
Builder:	ST1	
Project:	SLK	
Subject:	Heat technology building	
Rev. 6		
Int.:MDC	QC: CM	APP.: Date: 15-10-2025
Project nr.: 1768		
Drawing nr.: 9638		
FORMAT: A1		

LUNDSBY
RENEWABLE SOLUTIONS

Lundsby Biogas A/S, Hjarbækvej 65, 8831 Løgstrup
Tlf.: +45 96 49 43 00
info@lundsbybiogas.dk
Denne tegning er underlagt copyright og må ikke reproduceres uden tilladelse fra
Lundsbybiogas A/S

LB-Building

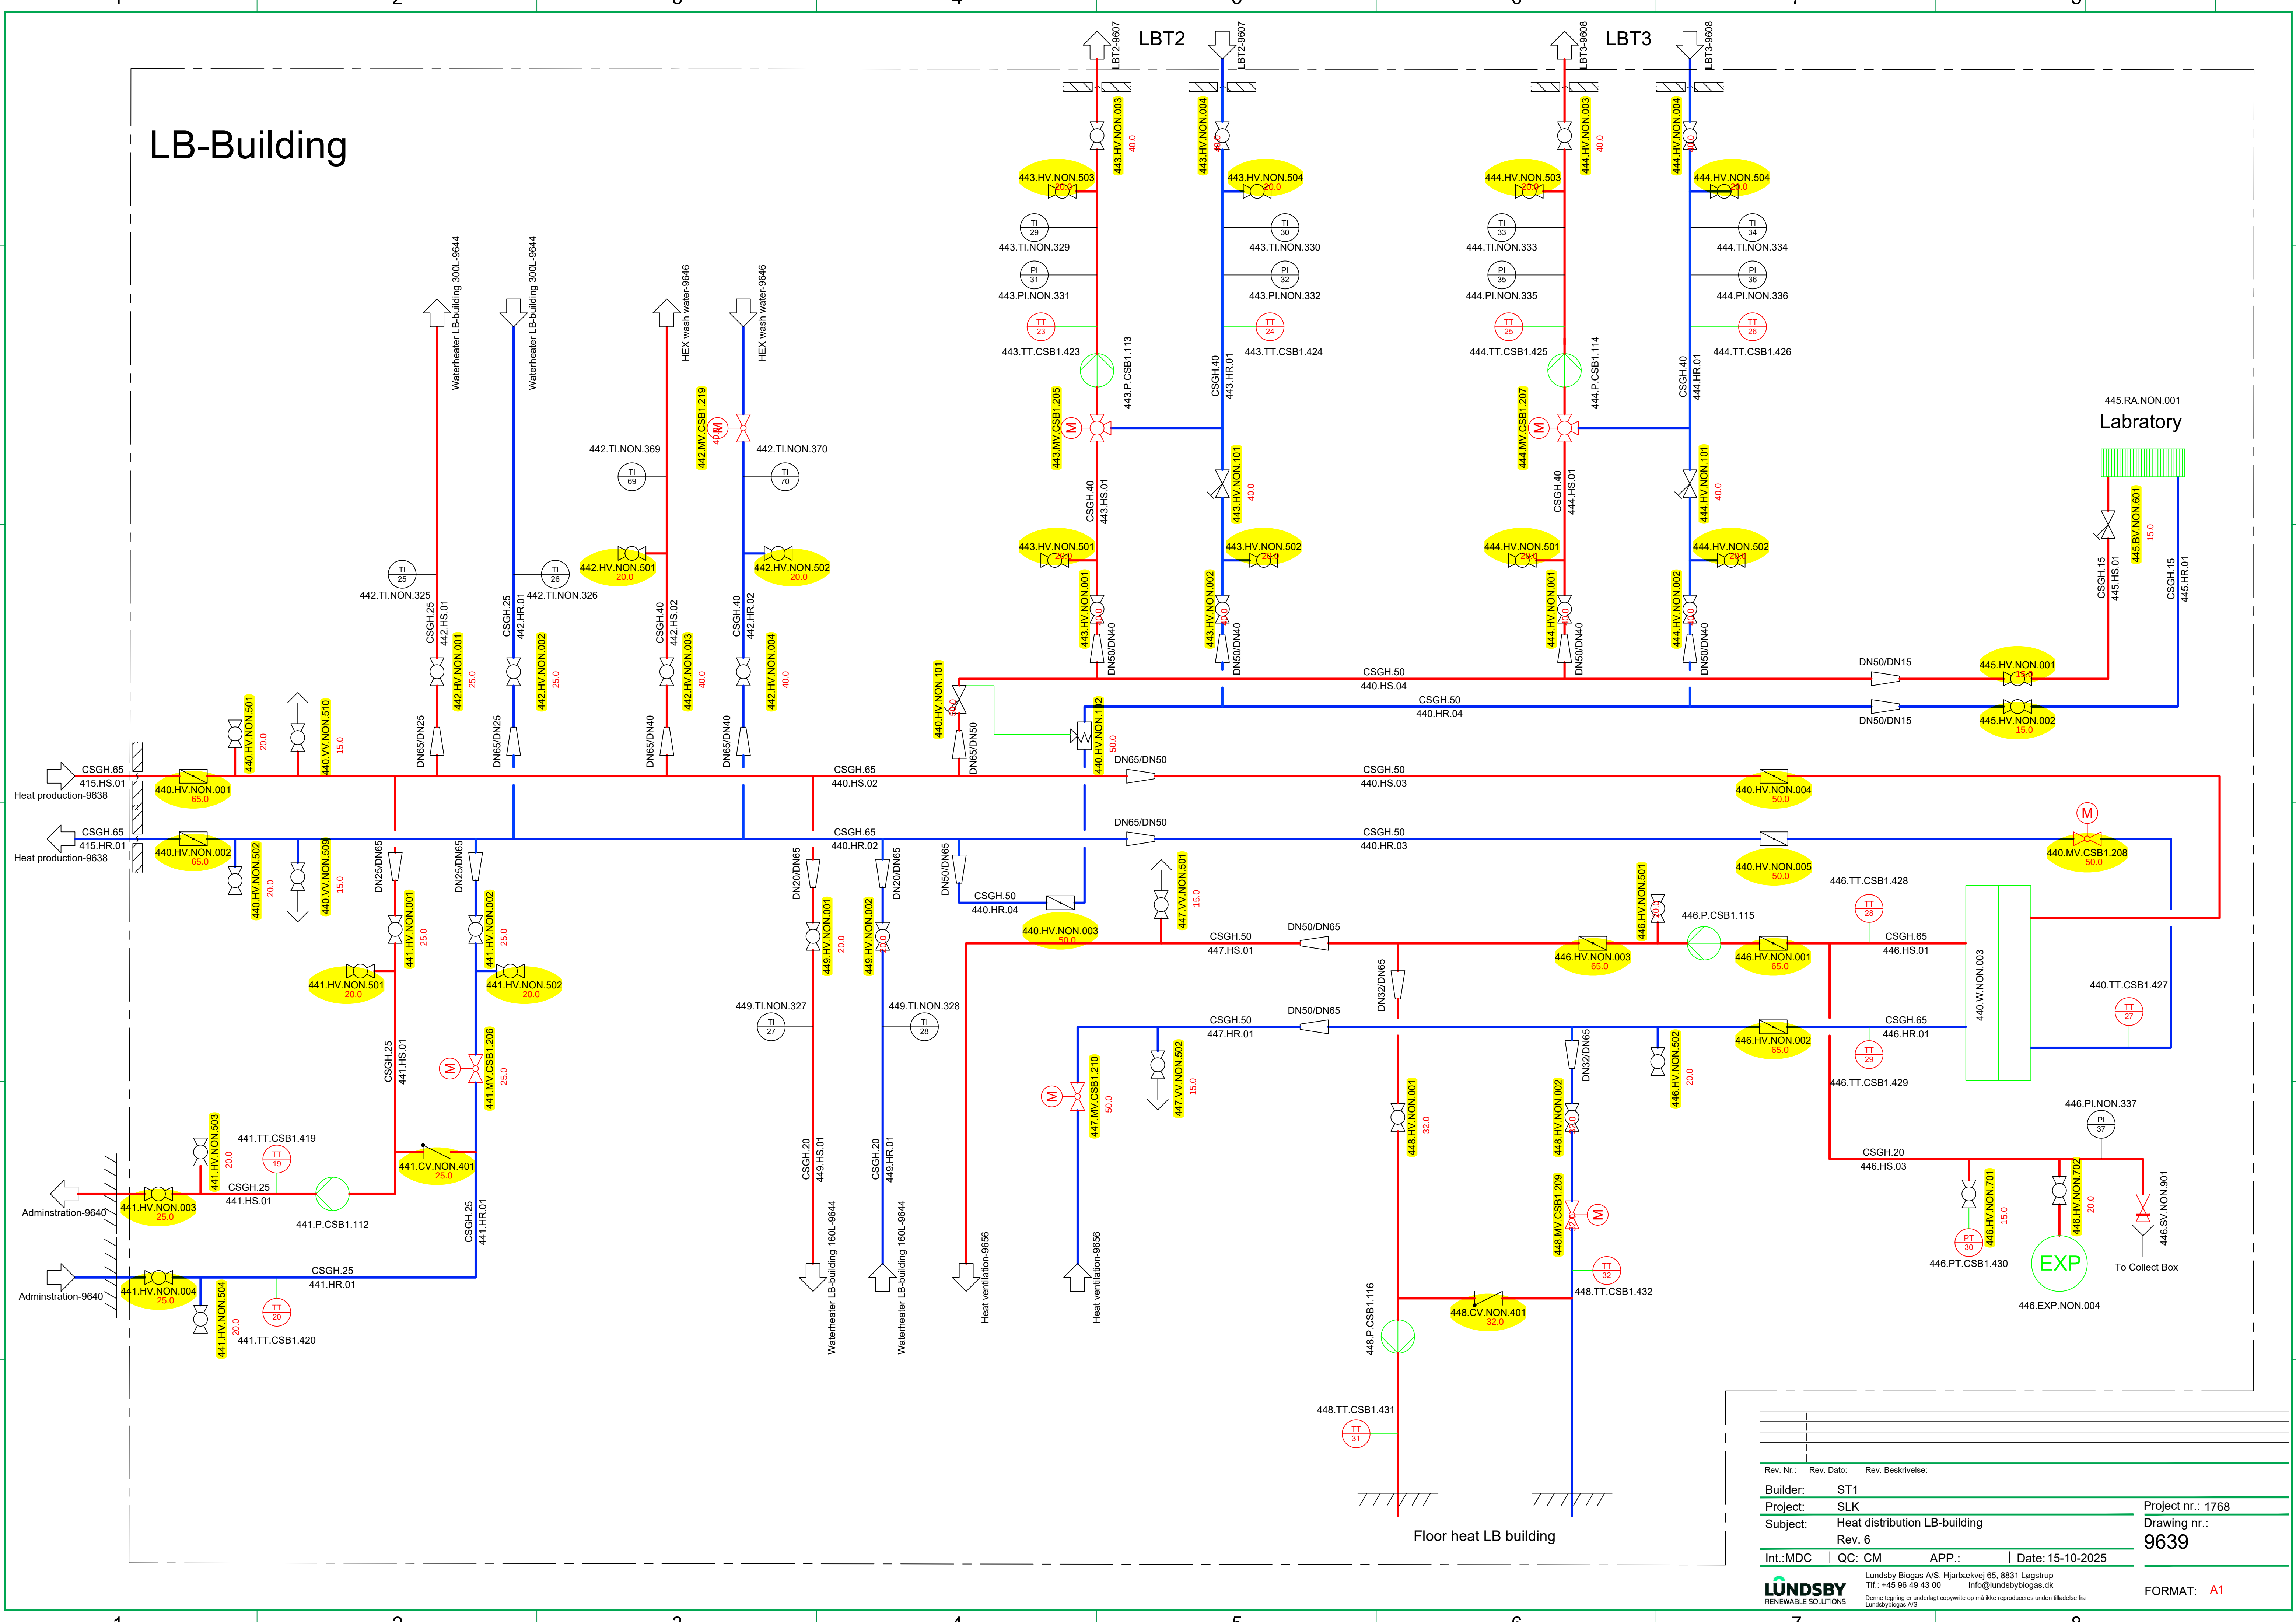

Rev. Nr.:	Rev. Dato:	Rev. Beskrivelse:


Builder:	ST1		
Project:	SLK		
Subject:	Heat distribution LB-building		
Rev. 6			
Int.:MDC	QC: CM	APP.:	Date: 15-10-2025

LUNDSBY
RENEWABLE SOLUTIONS


Lundsby Biogas A/S, Hjarbækvej 65, 8831 Løgstrup
Tlf.: +45 96 49 43 00
info@lundsbybiogas.dk
Denne tegning er underlagt copyright op på ikke reproduceres uden tilladelse fra Lundsbybiogas A/S

Project nr.: 1768
Drawing nr.:
9639
FORMAT: A1

SB-Building

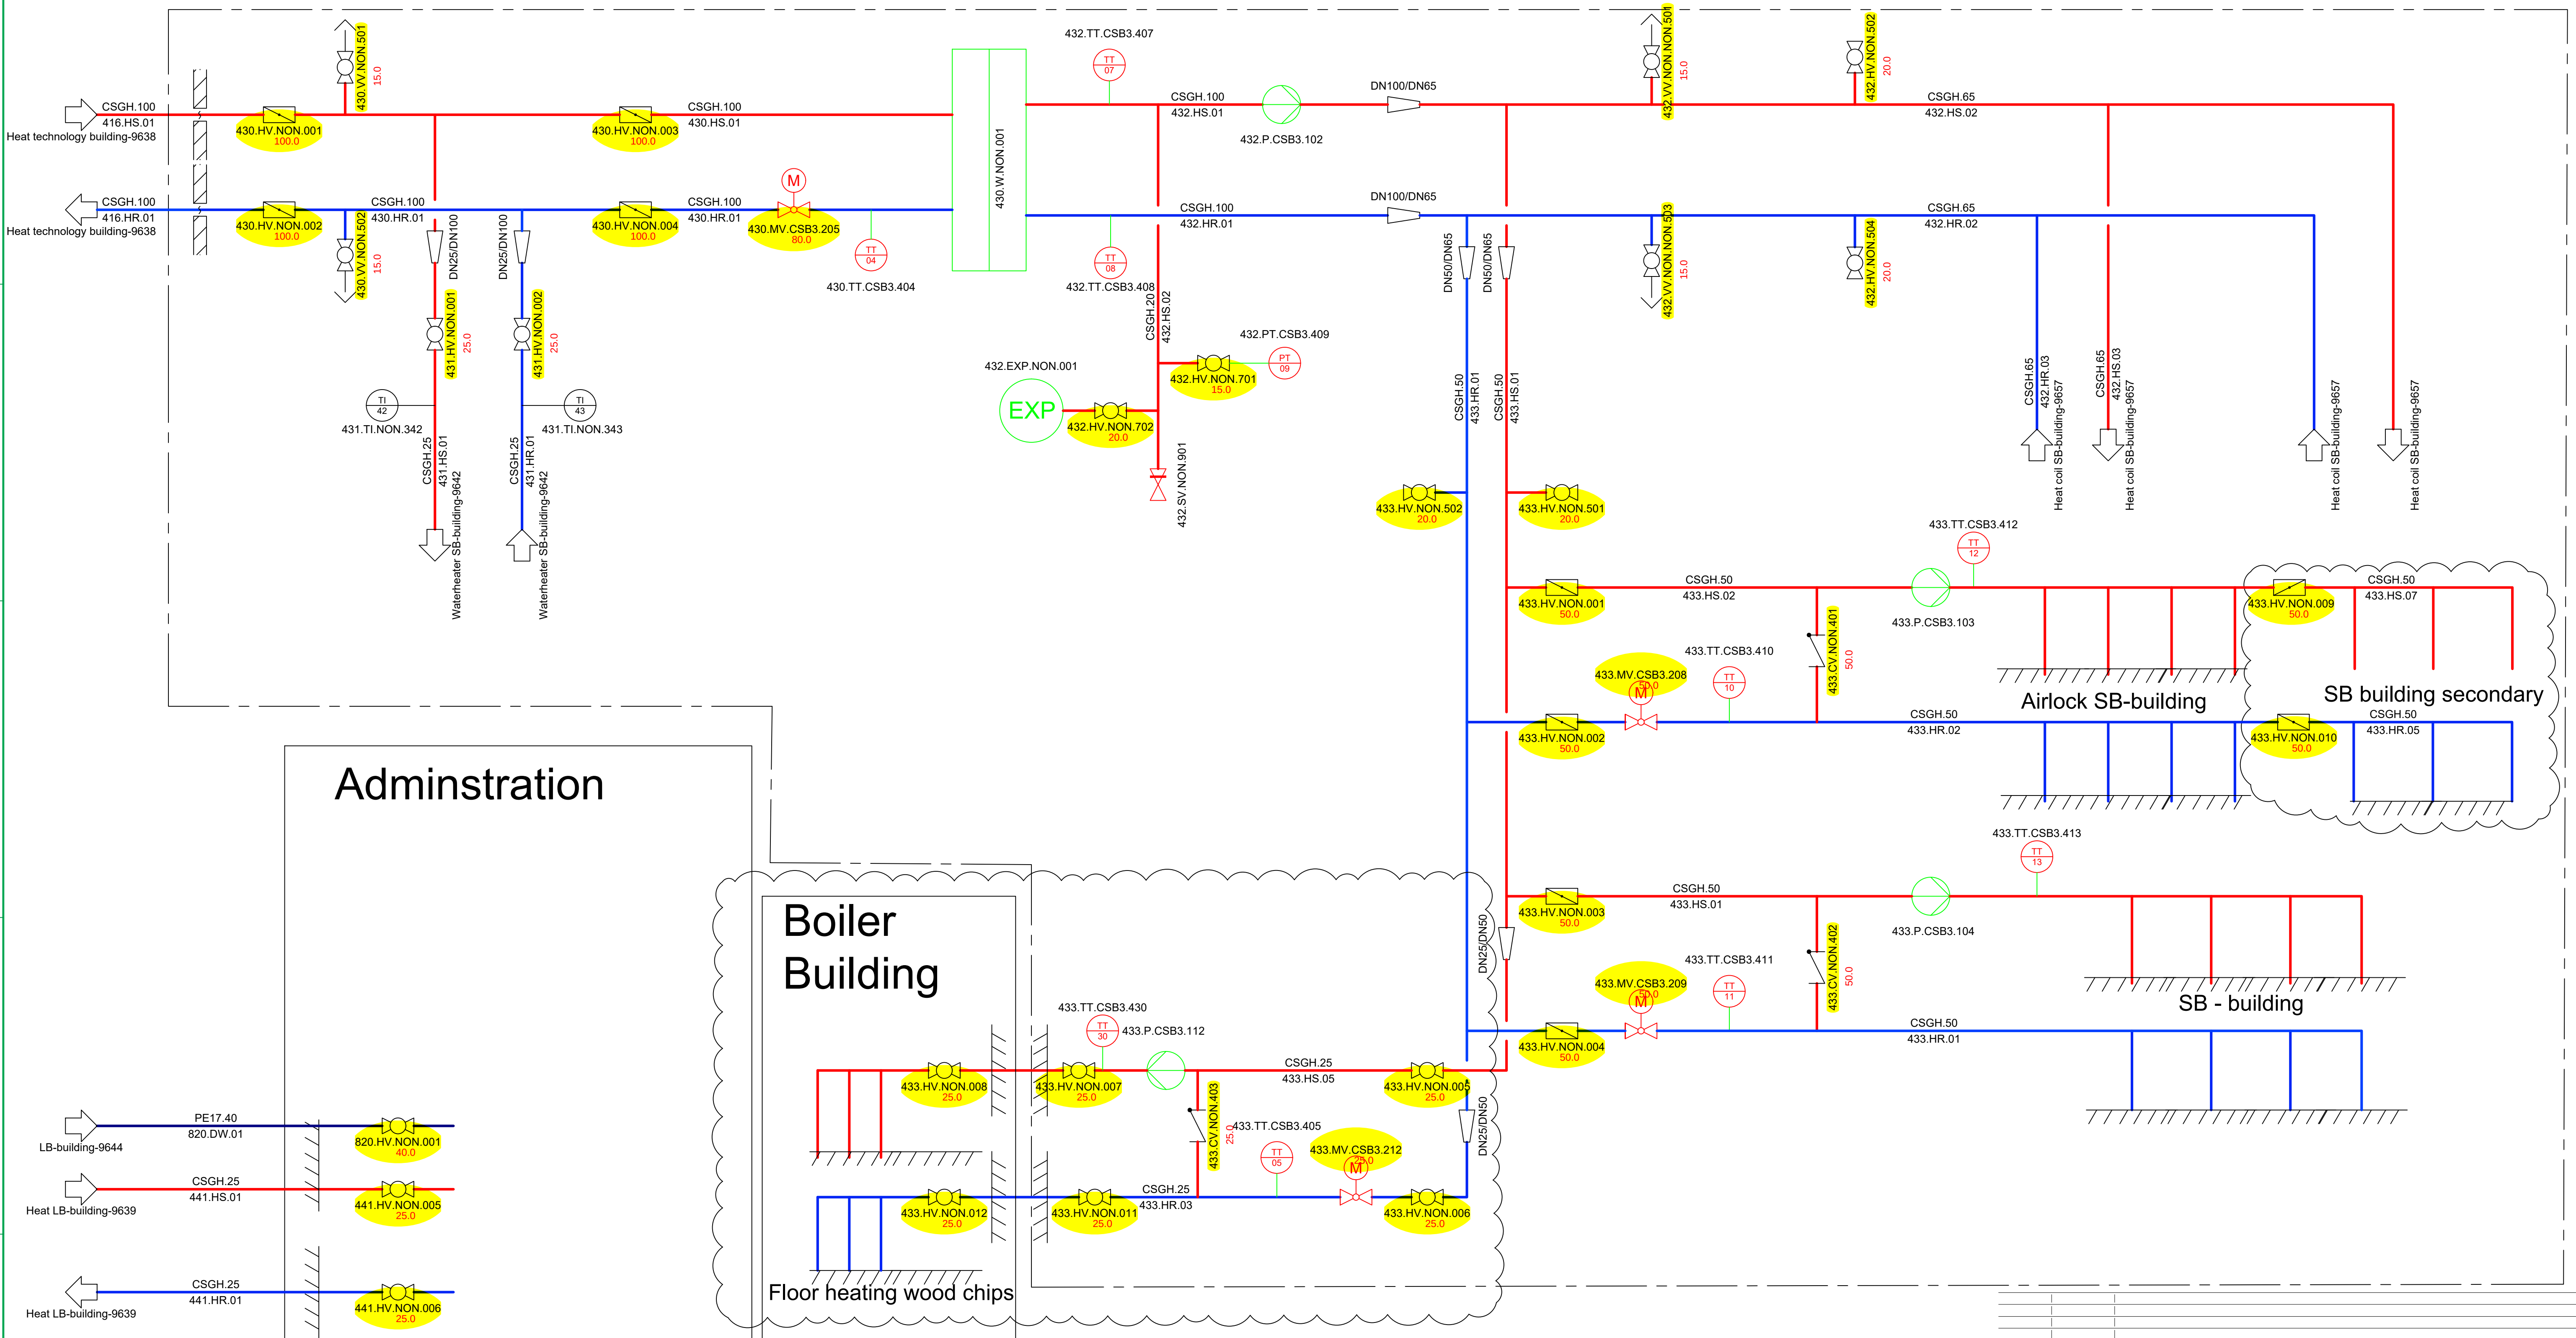


Rev. Nr.:	Rev. Dato:	Rev. Beskrivelse:
Builder:	ST1	
Project:	SLK	Project nr.: 1768
Subject:	Heat distribution SB-building	Drawing nr.:
	Rev. 6	9640
Int.:MDC	QC: CM	APP.: Date: 15-10-2025

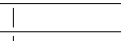


Lundsbey Biogas A/S, Hjarbækvej 65, 8831 Løgstrup
Tlf.: +45 96 49 43 00 Info@lundsbeybiogas.dk
Denne tegning er underlagt copyright og må ikke reproduceres uden tilladelse fra
Lundsbey Biogas A/S

FORMAT: **A1**

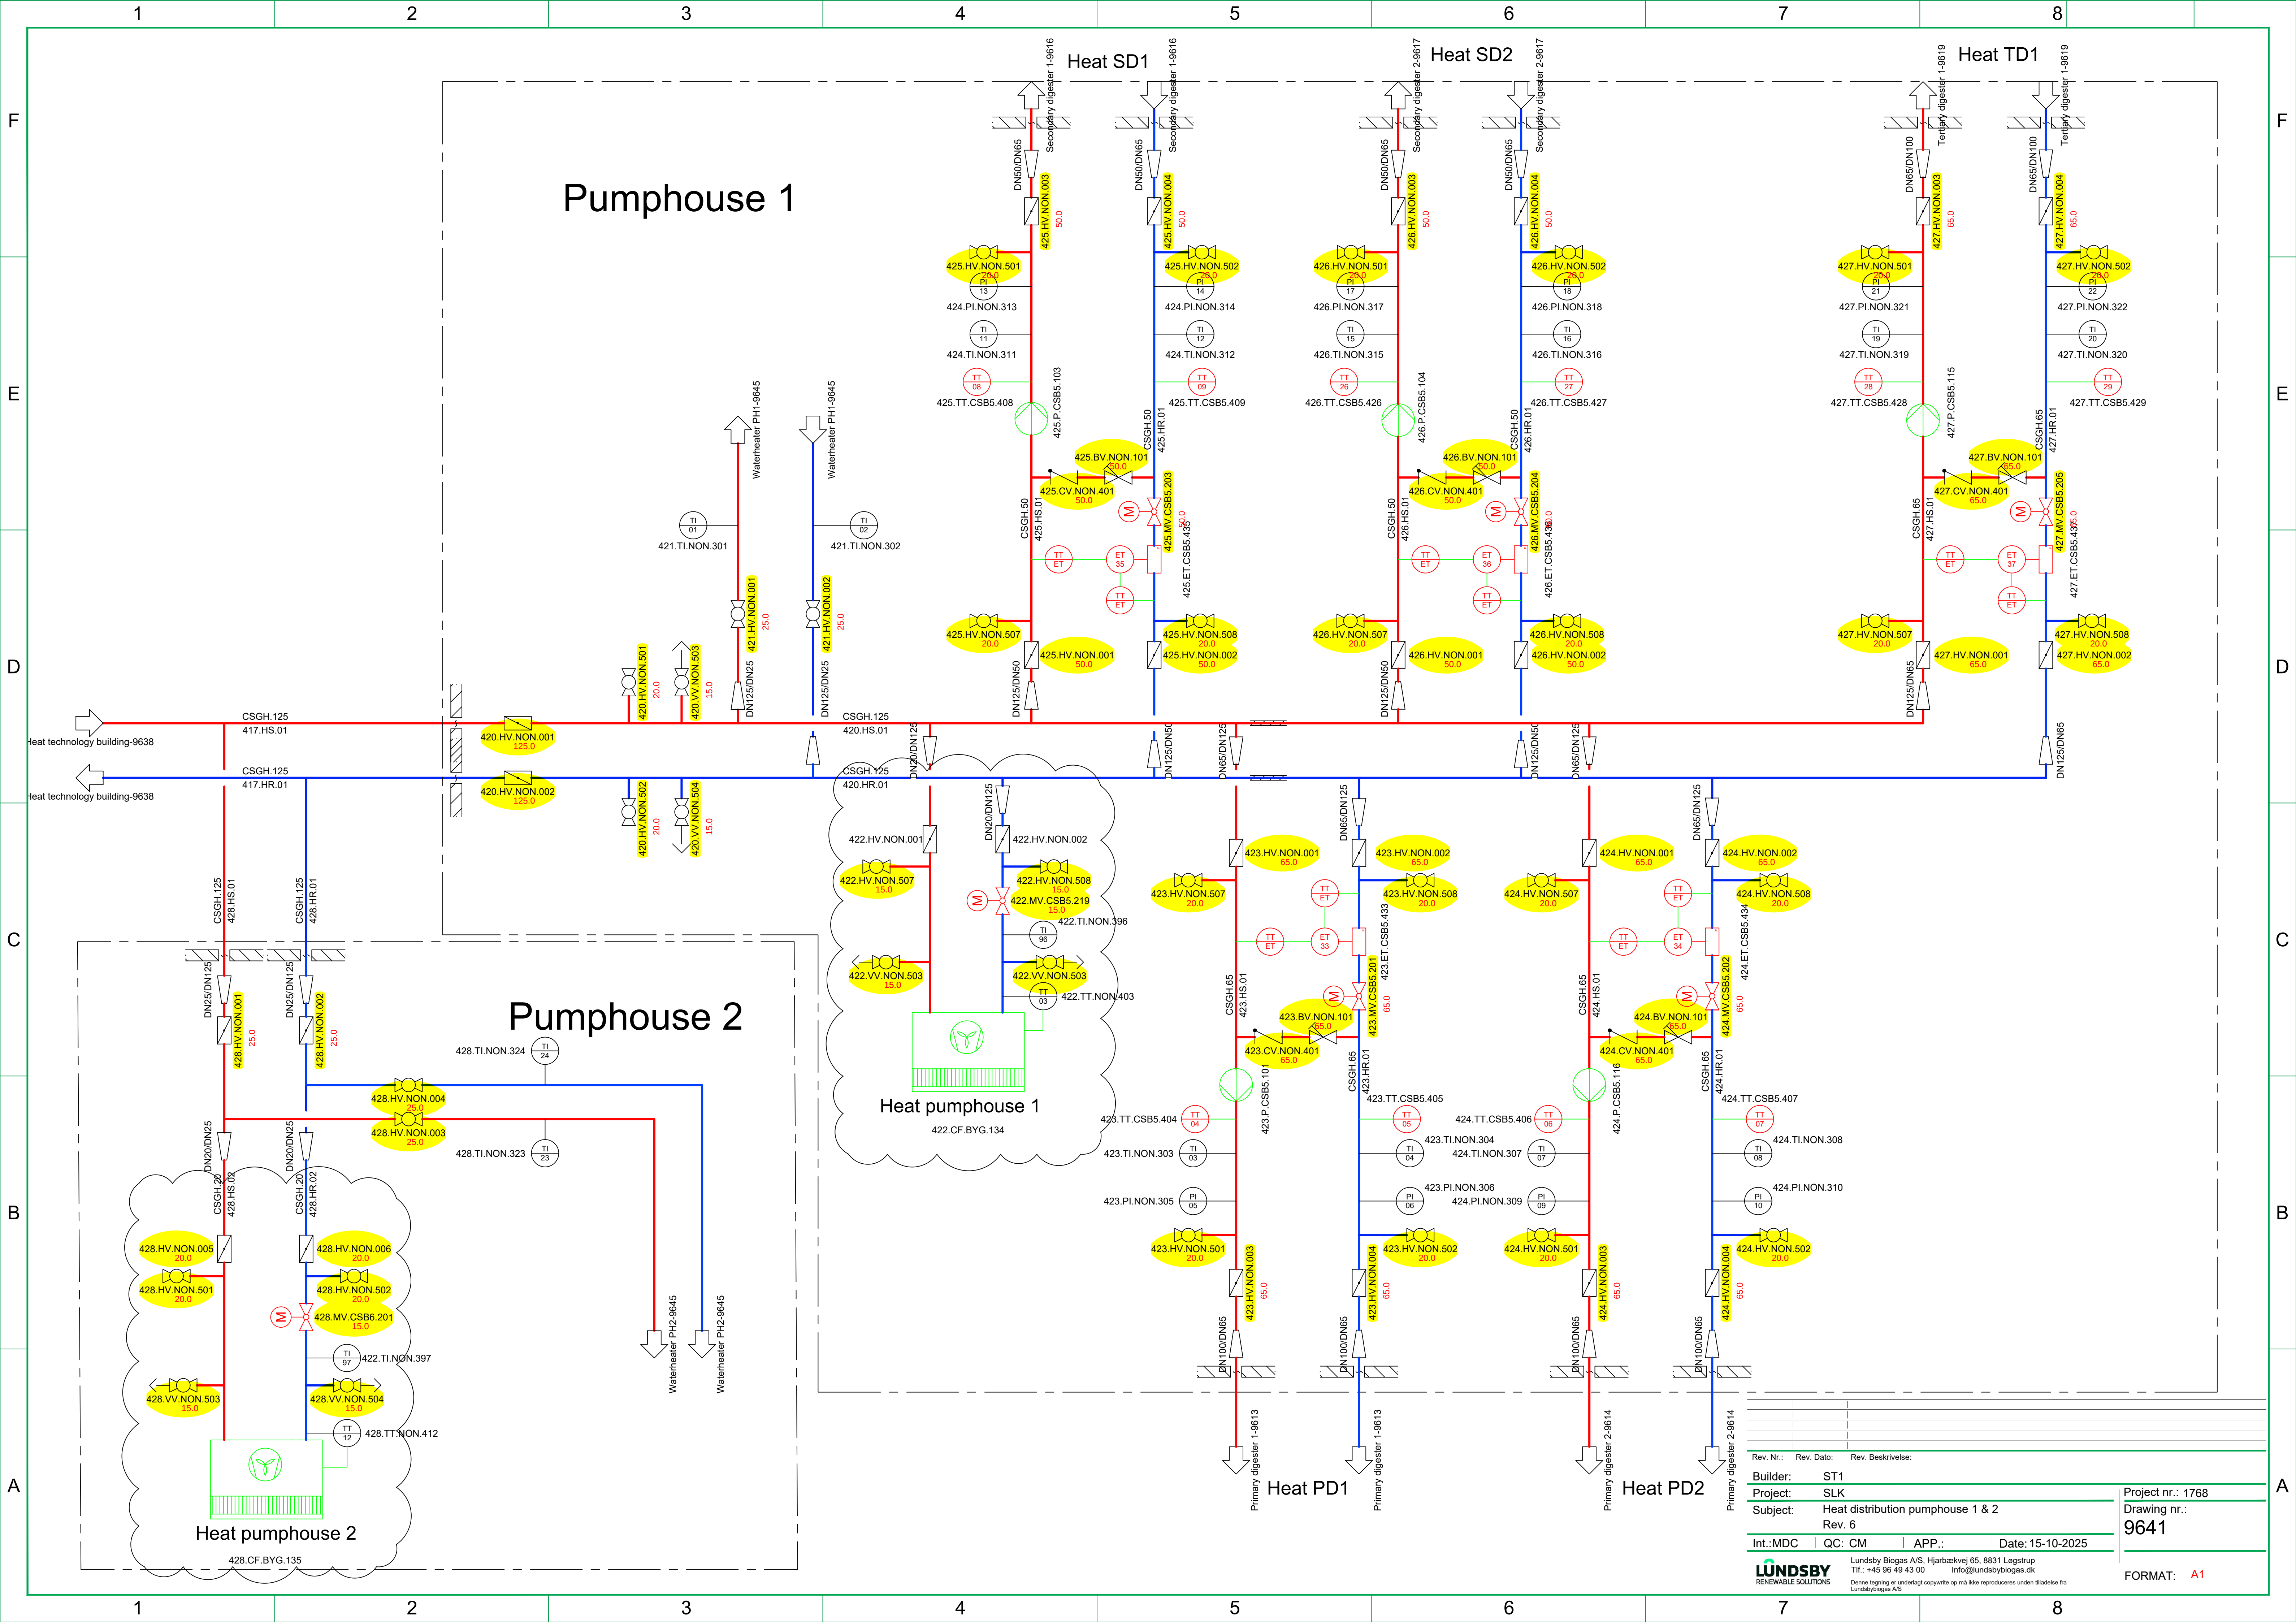


SB-Building

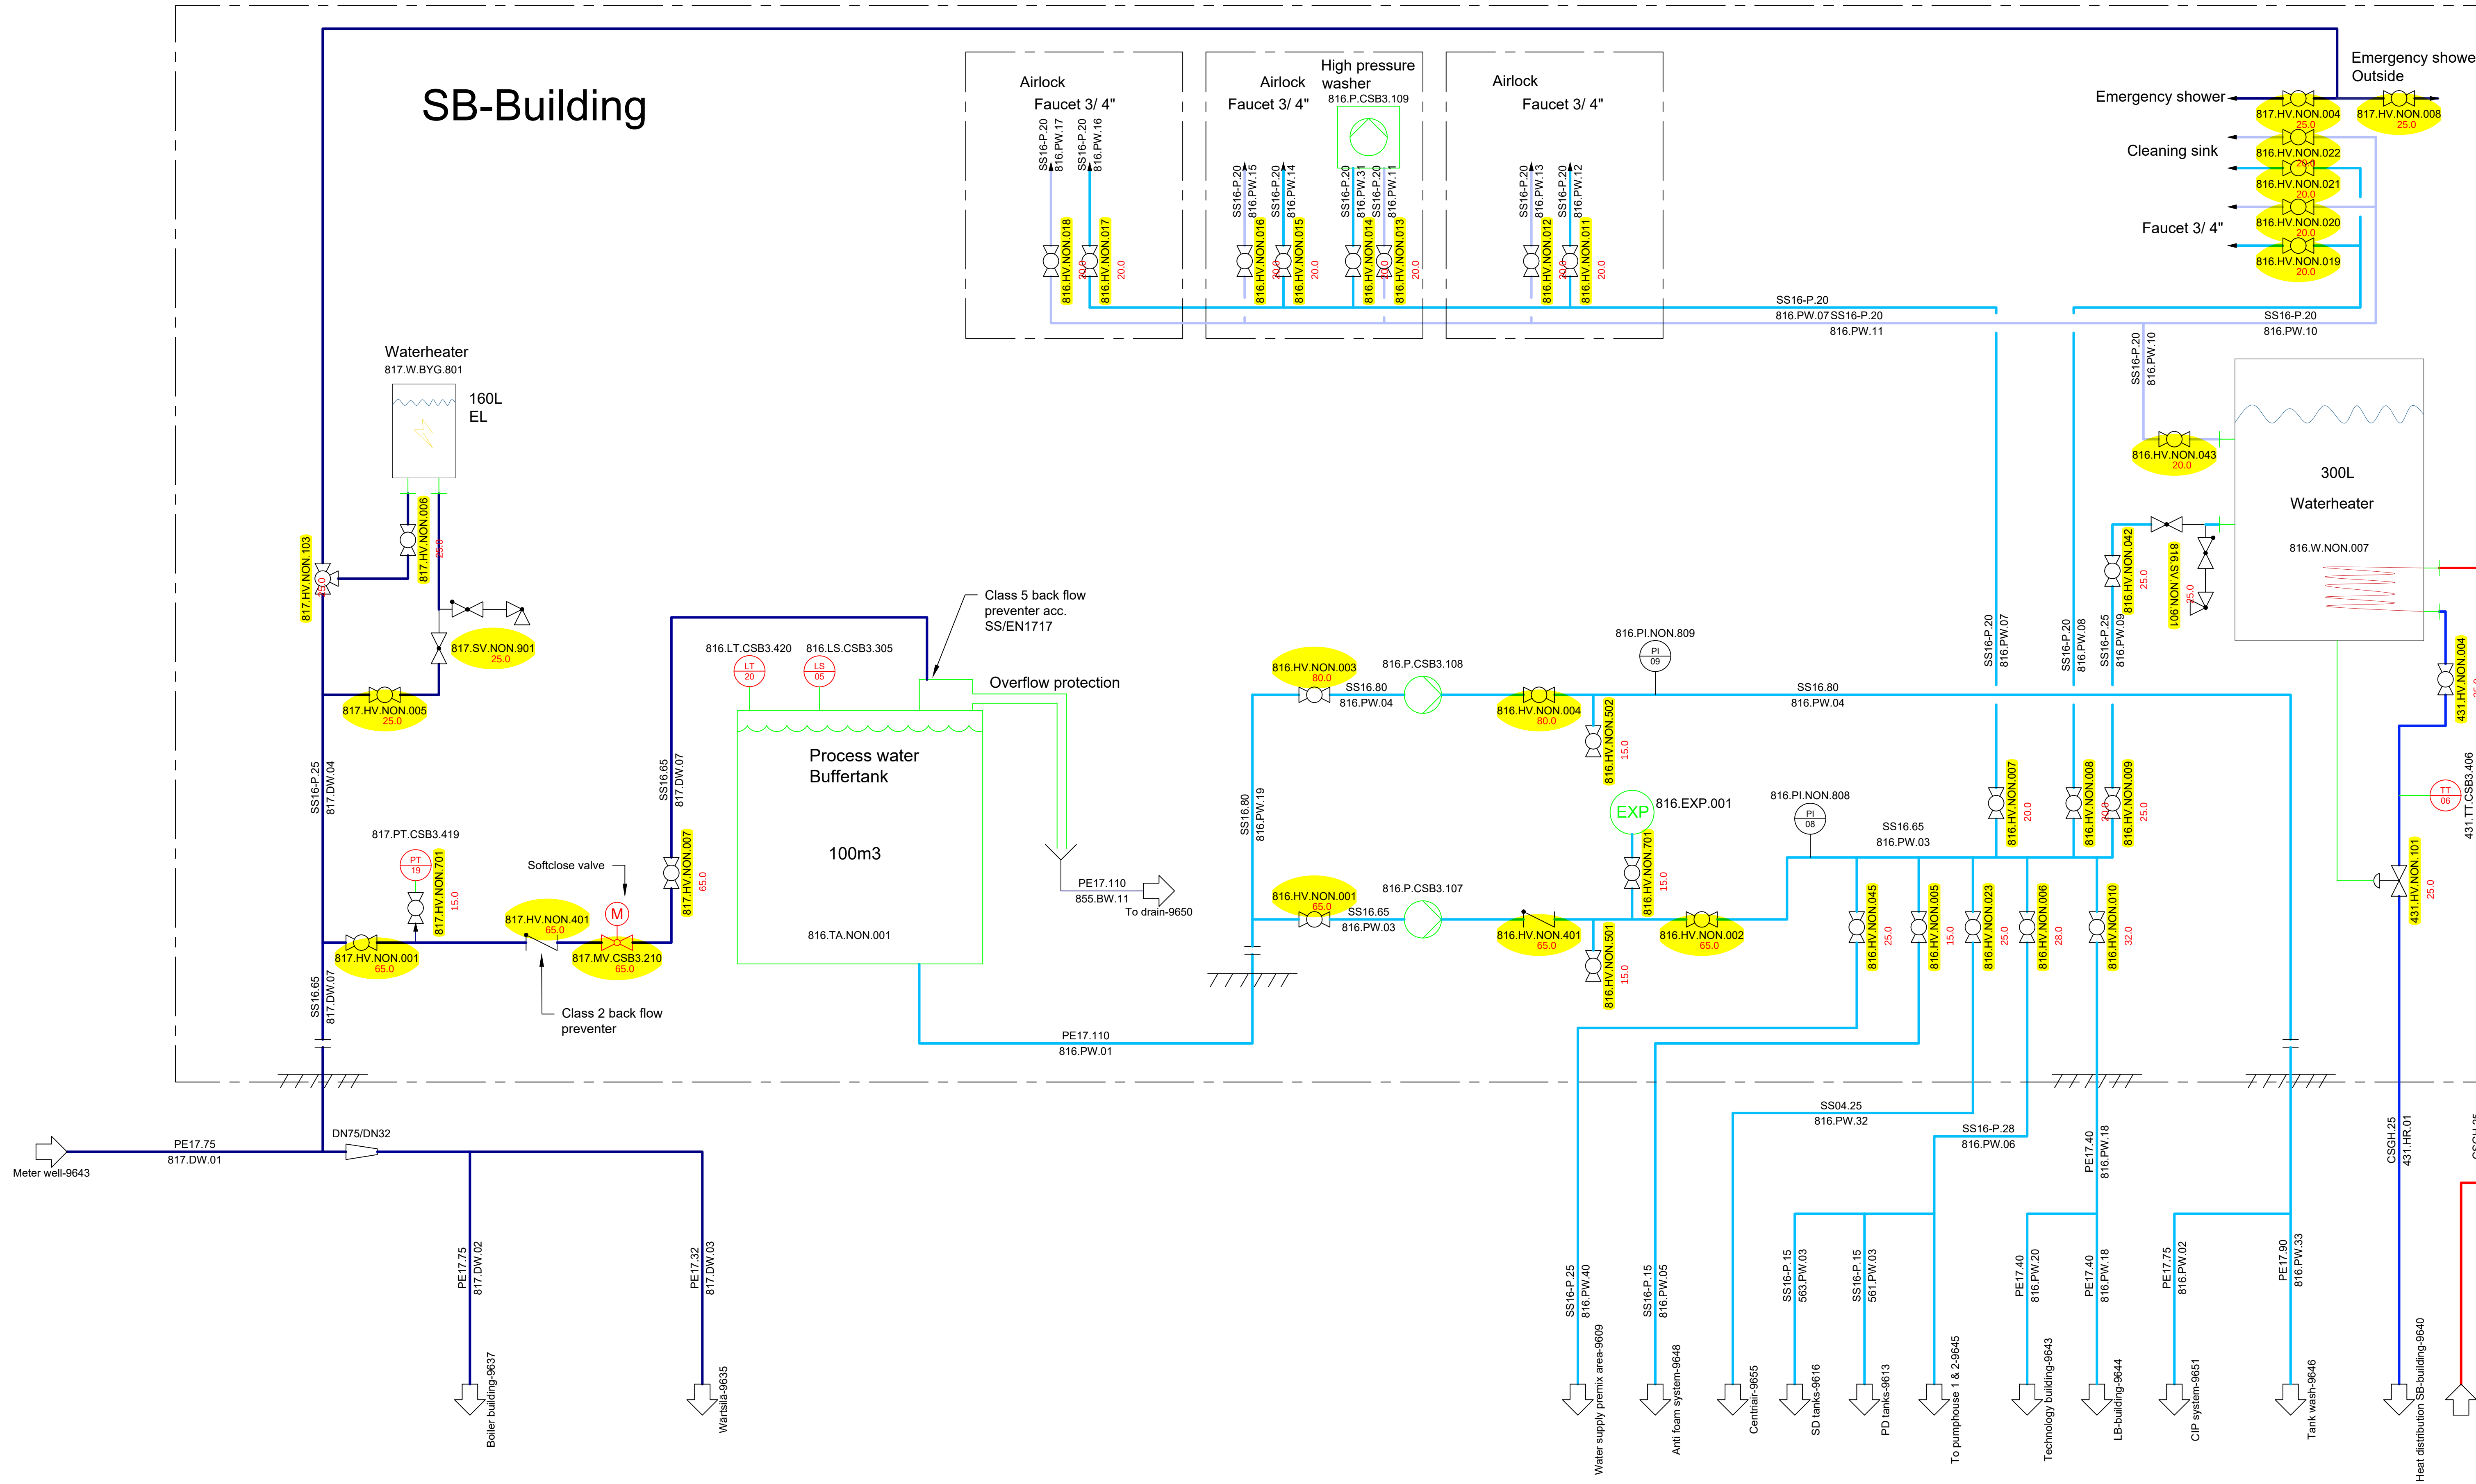


Rev. Nr.:	Rev. Dato:	Rev. Beskrivelse:
Builder:	ST1	
Project:	SLK	
Subject:	Water distribution SB-building	
Rev. 6		
Int.:MDC	QC:CM	APP.: Date: 15-10-2025
LUNDSBY RENEWABLE SOLUTIONS		
Lundsby Biogas A/S, Hjarbækvej 65, 8831 Løgstrup Tlf.: +45 96 49 43 00 info@lundsbybiogas.dk		
Denne tegning er underlagt copyright op på ikke reproduceres uden tilladelse fra Lundsbybiogas A/S		
Project nr.: 1768 Drawing nr.: 9642		FORMAT: A1

Technology building

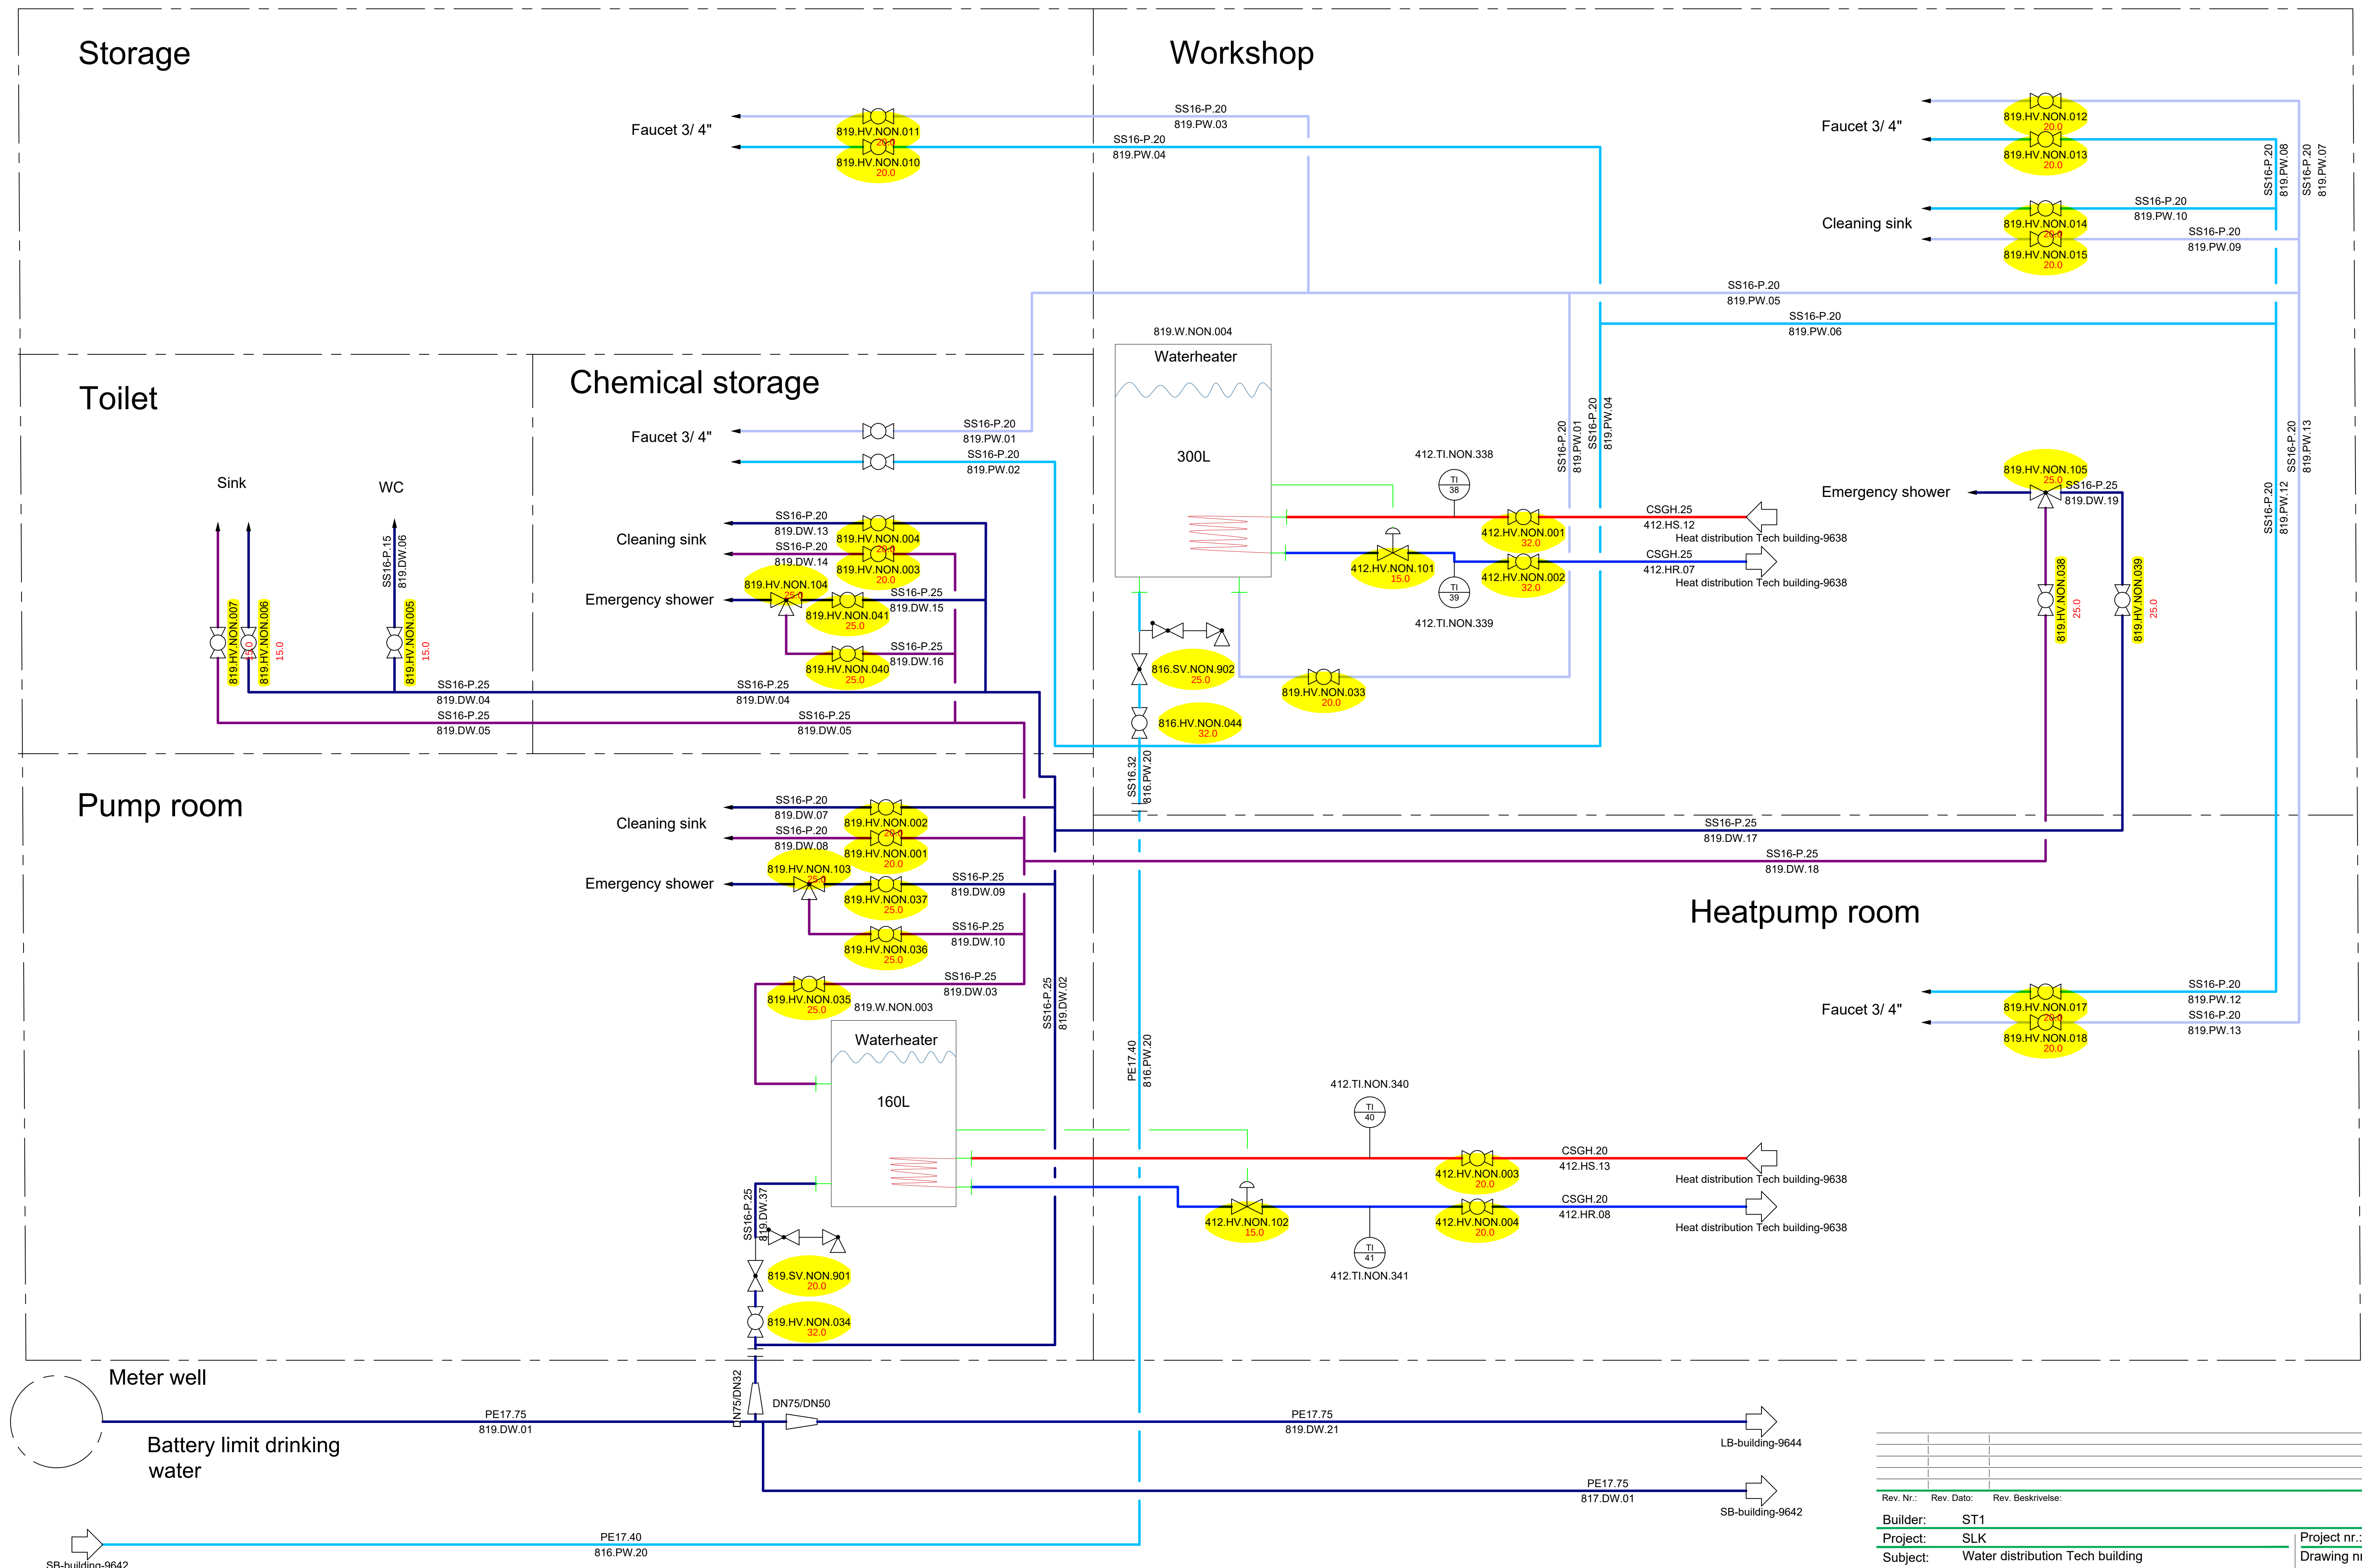[illegible]

LB-building

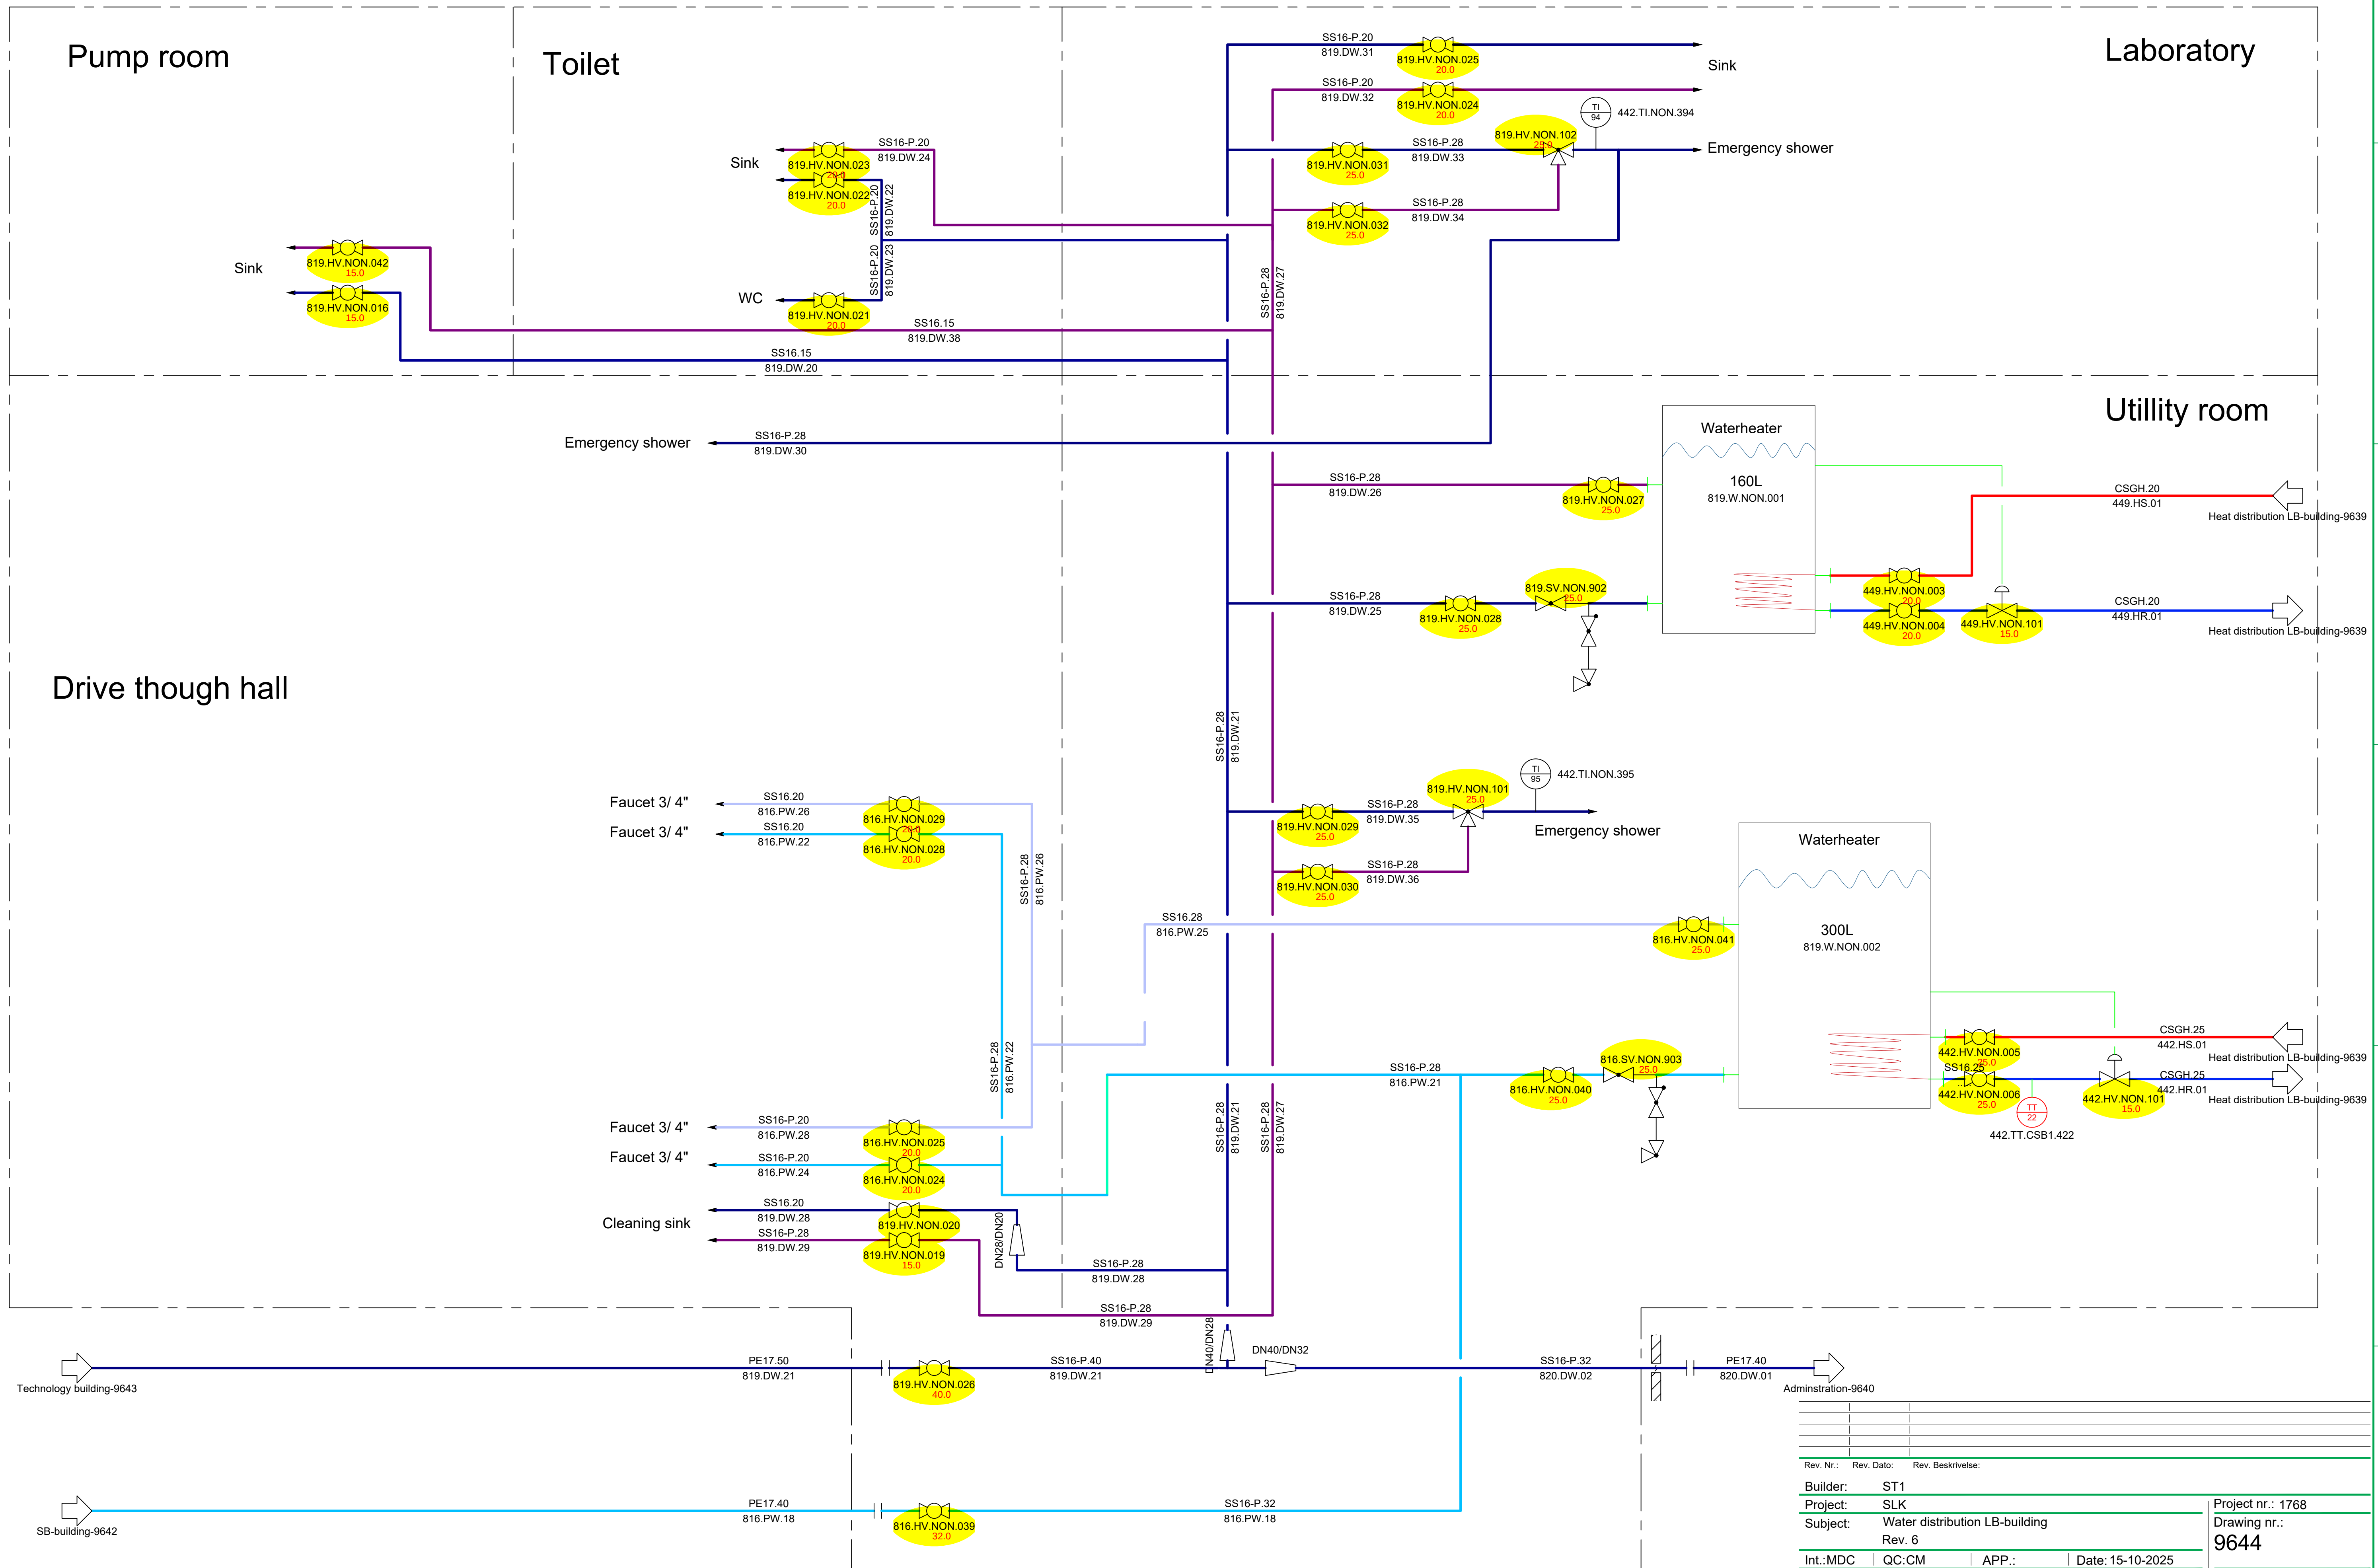

Rev. Nr.: Rev. Dato: Rev. Beskrivelse:

Builder: ST1

Project: SLK

Subject: Water distribution LB-building
 Rev. 6

Int.:MDC QC:CM APP.: Date: 15-10-2025

Project nr.: 1768

Drawing nr.:
9644

LUNDSBY
RENEWABLE SOLUTIONS


Lundsby Biogas A/S, Hjarbækvej 65, 8831 Løgstrup
Tlf.: +45 96 49 43 00 Info@lundsbybiogas.dk

Denne tegning er underlagt copywrite og må ikke reproducere uden tilladelse fra Lundsby Biogas A/S


FORMAT: **A1**

FORMAT: A1


Pumphouse 1

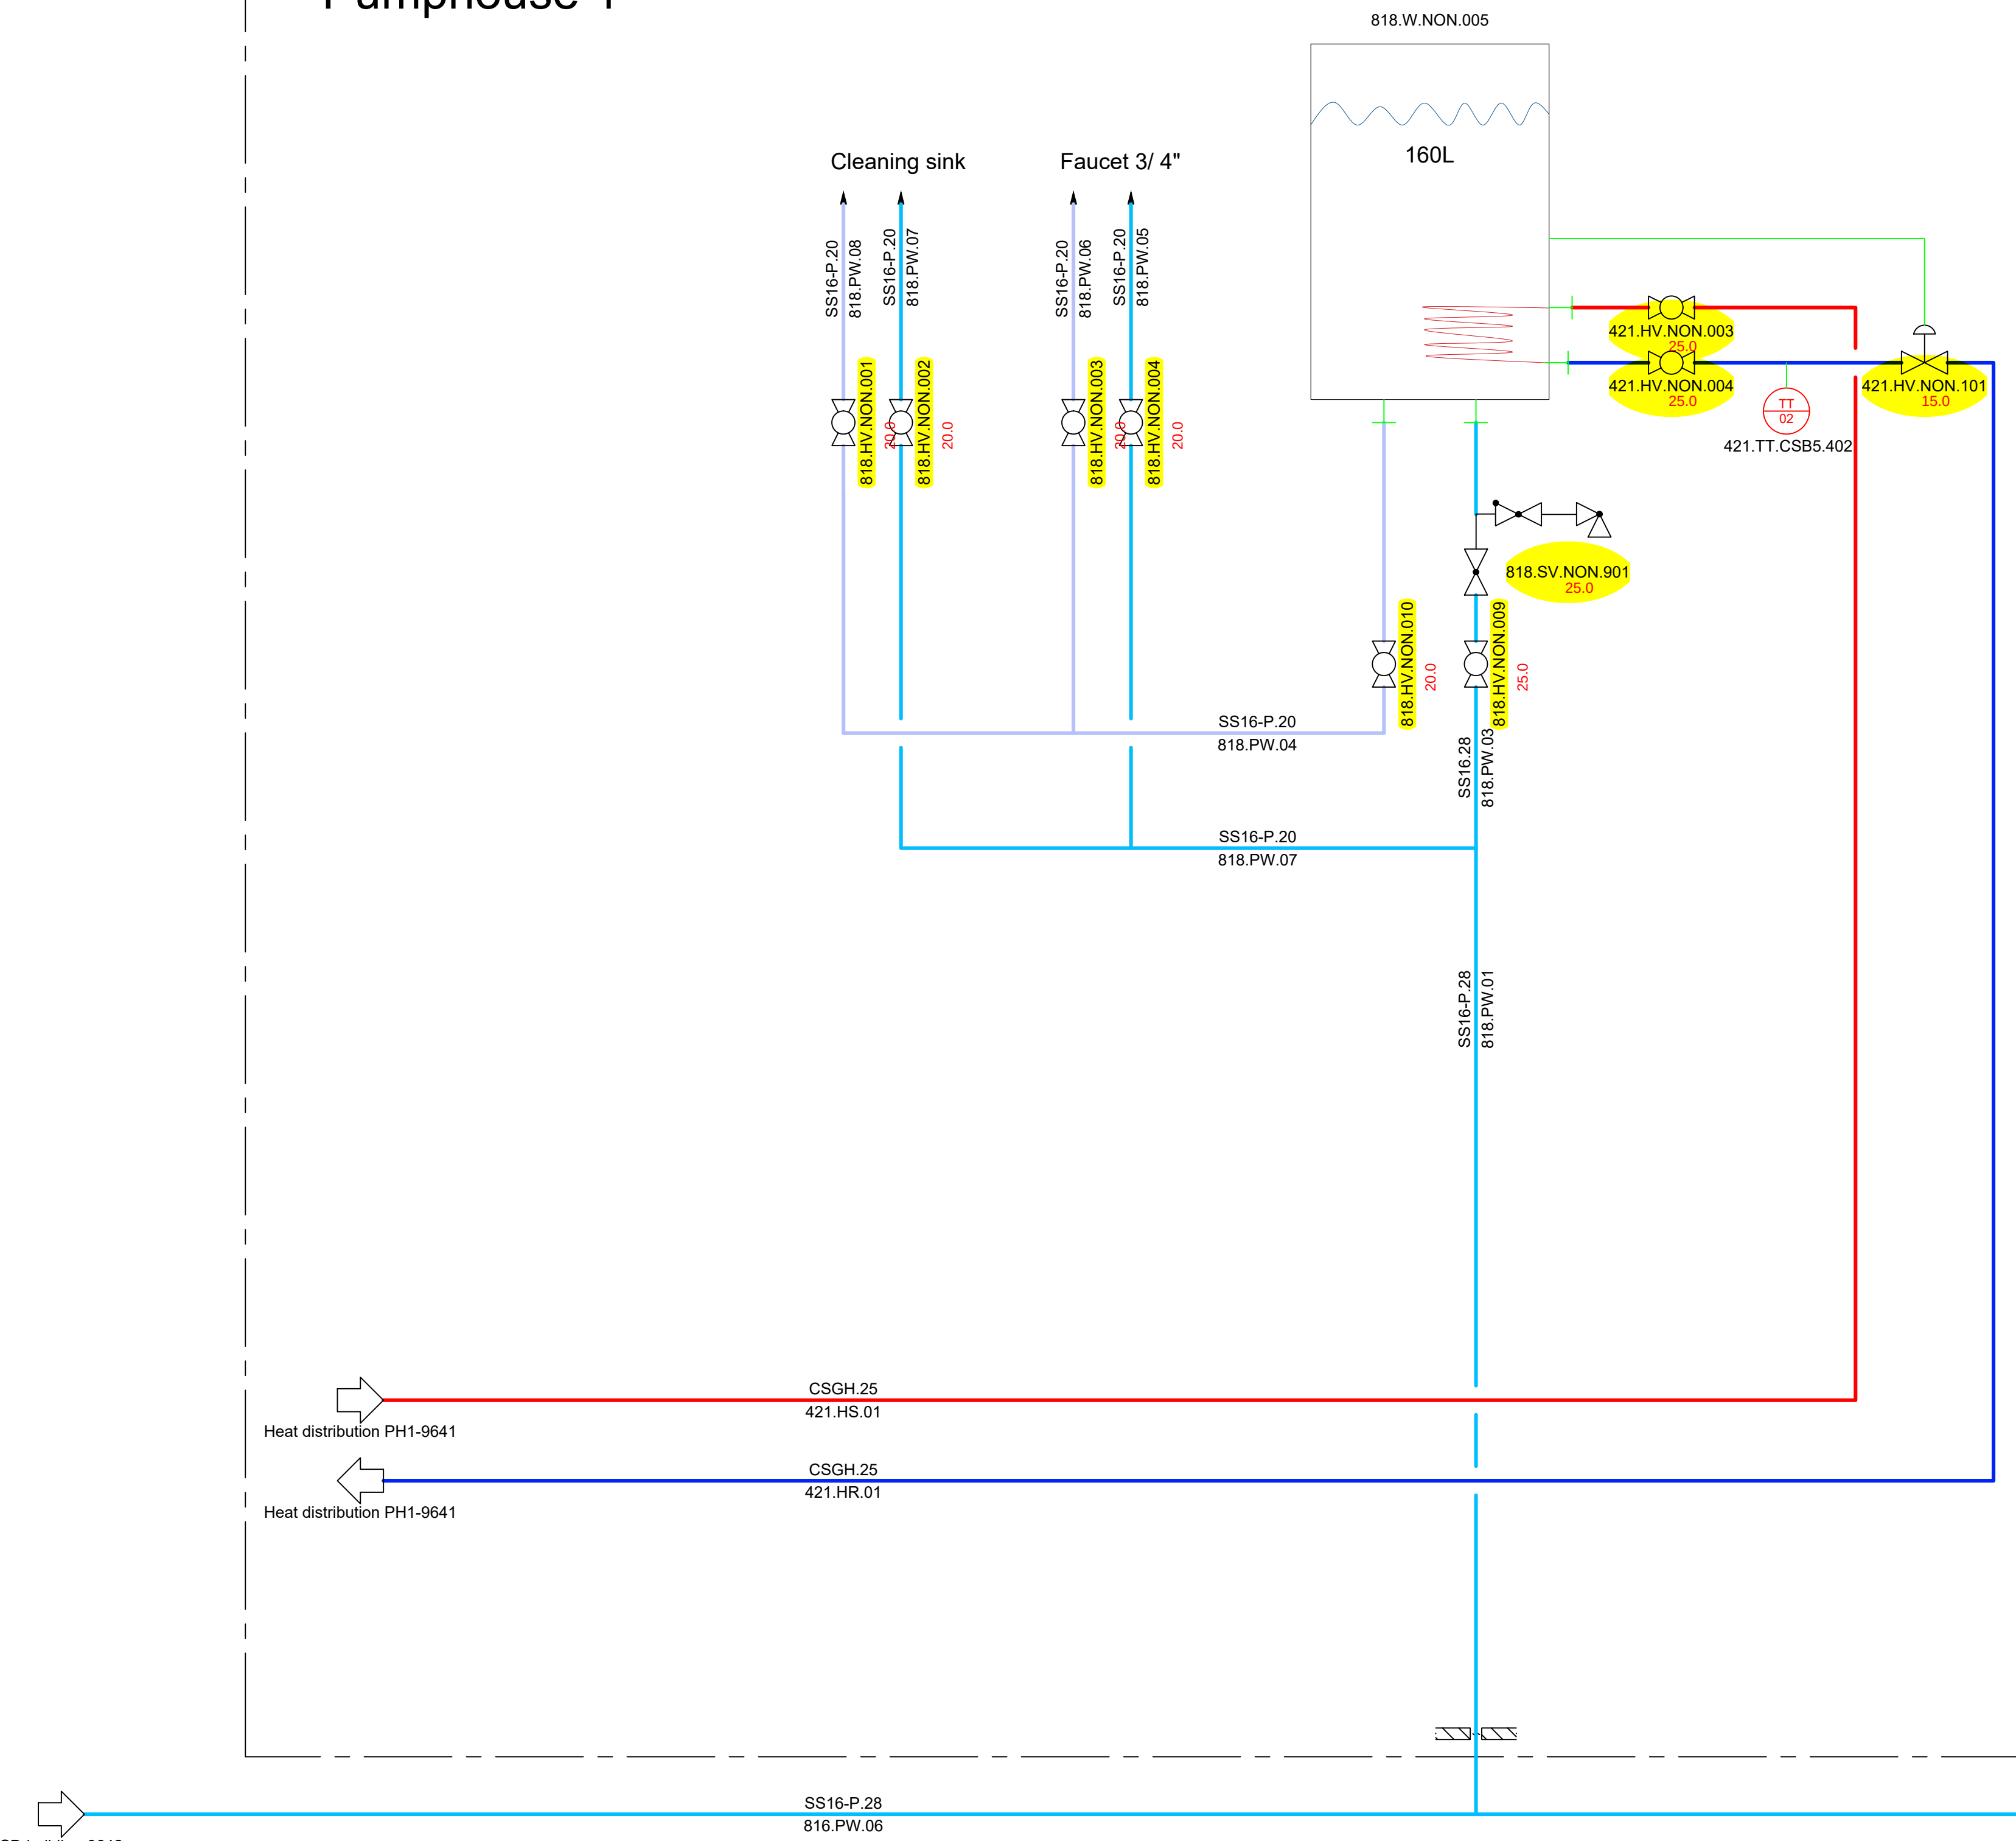


Pumphouse 2

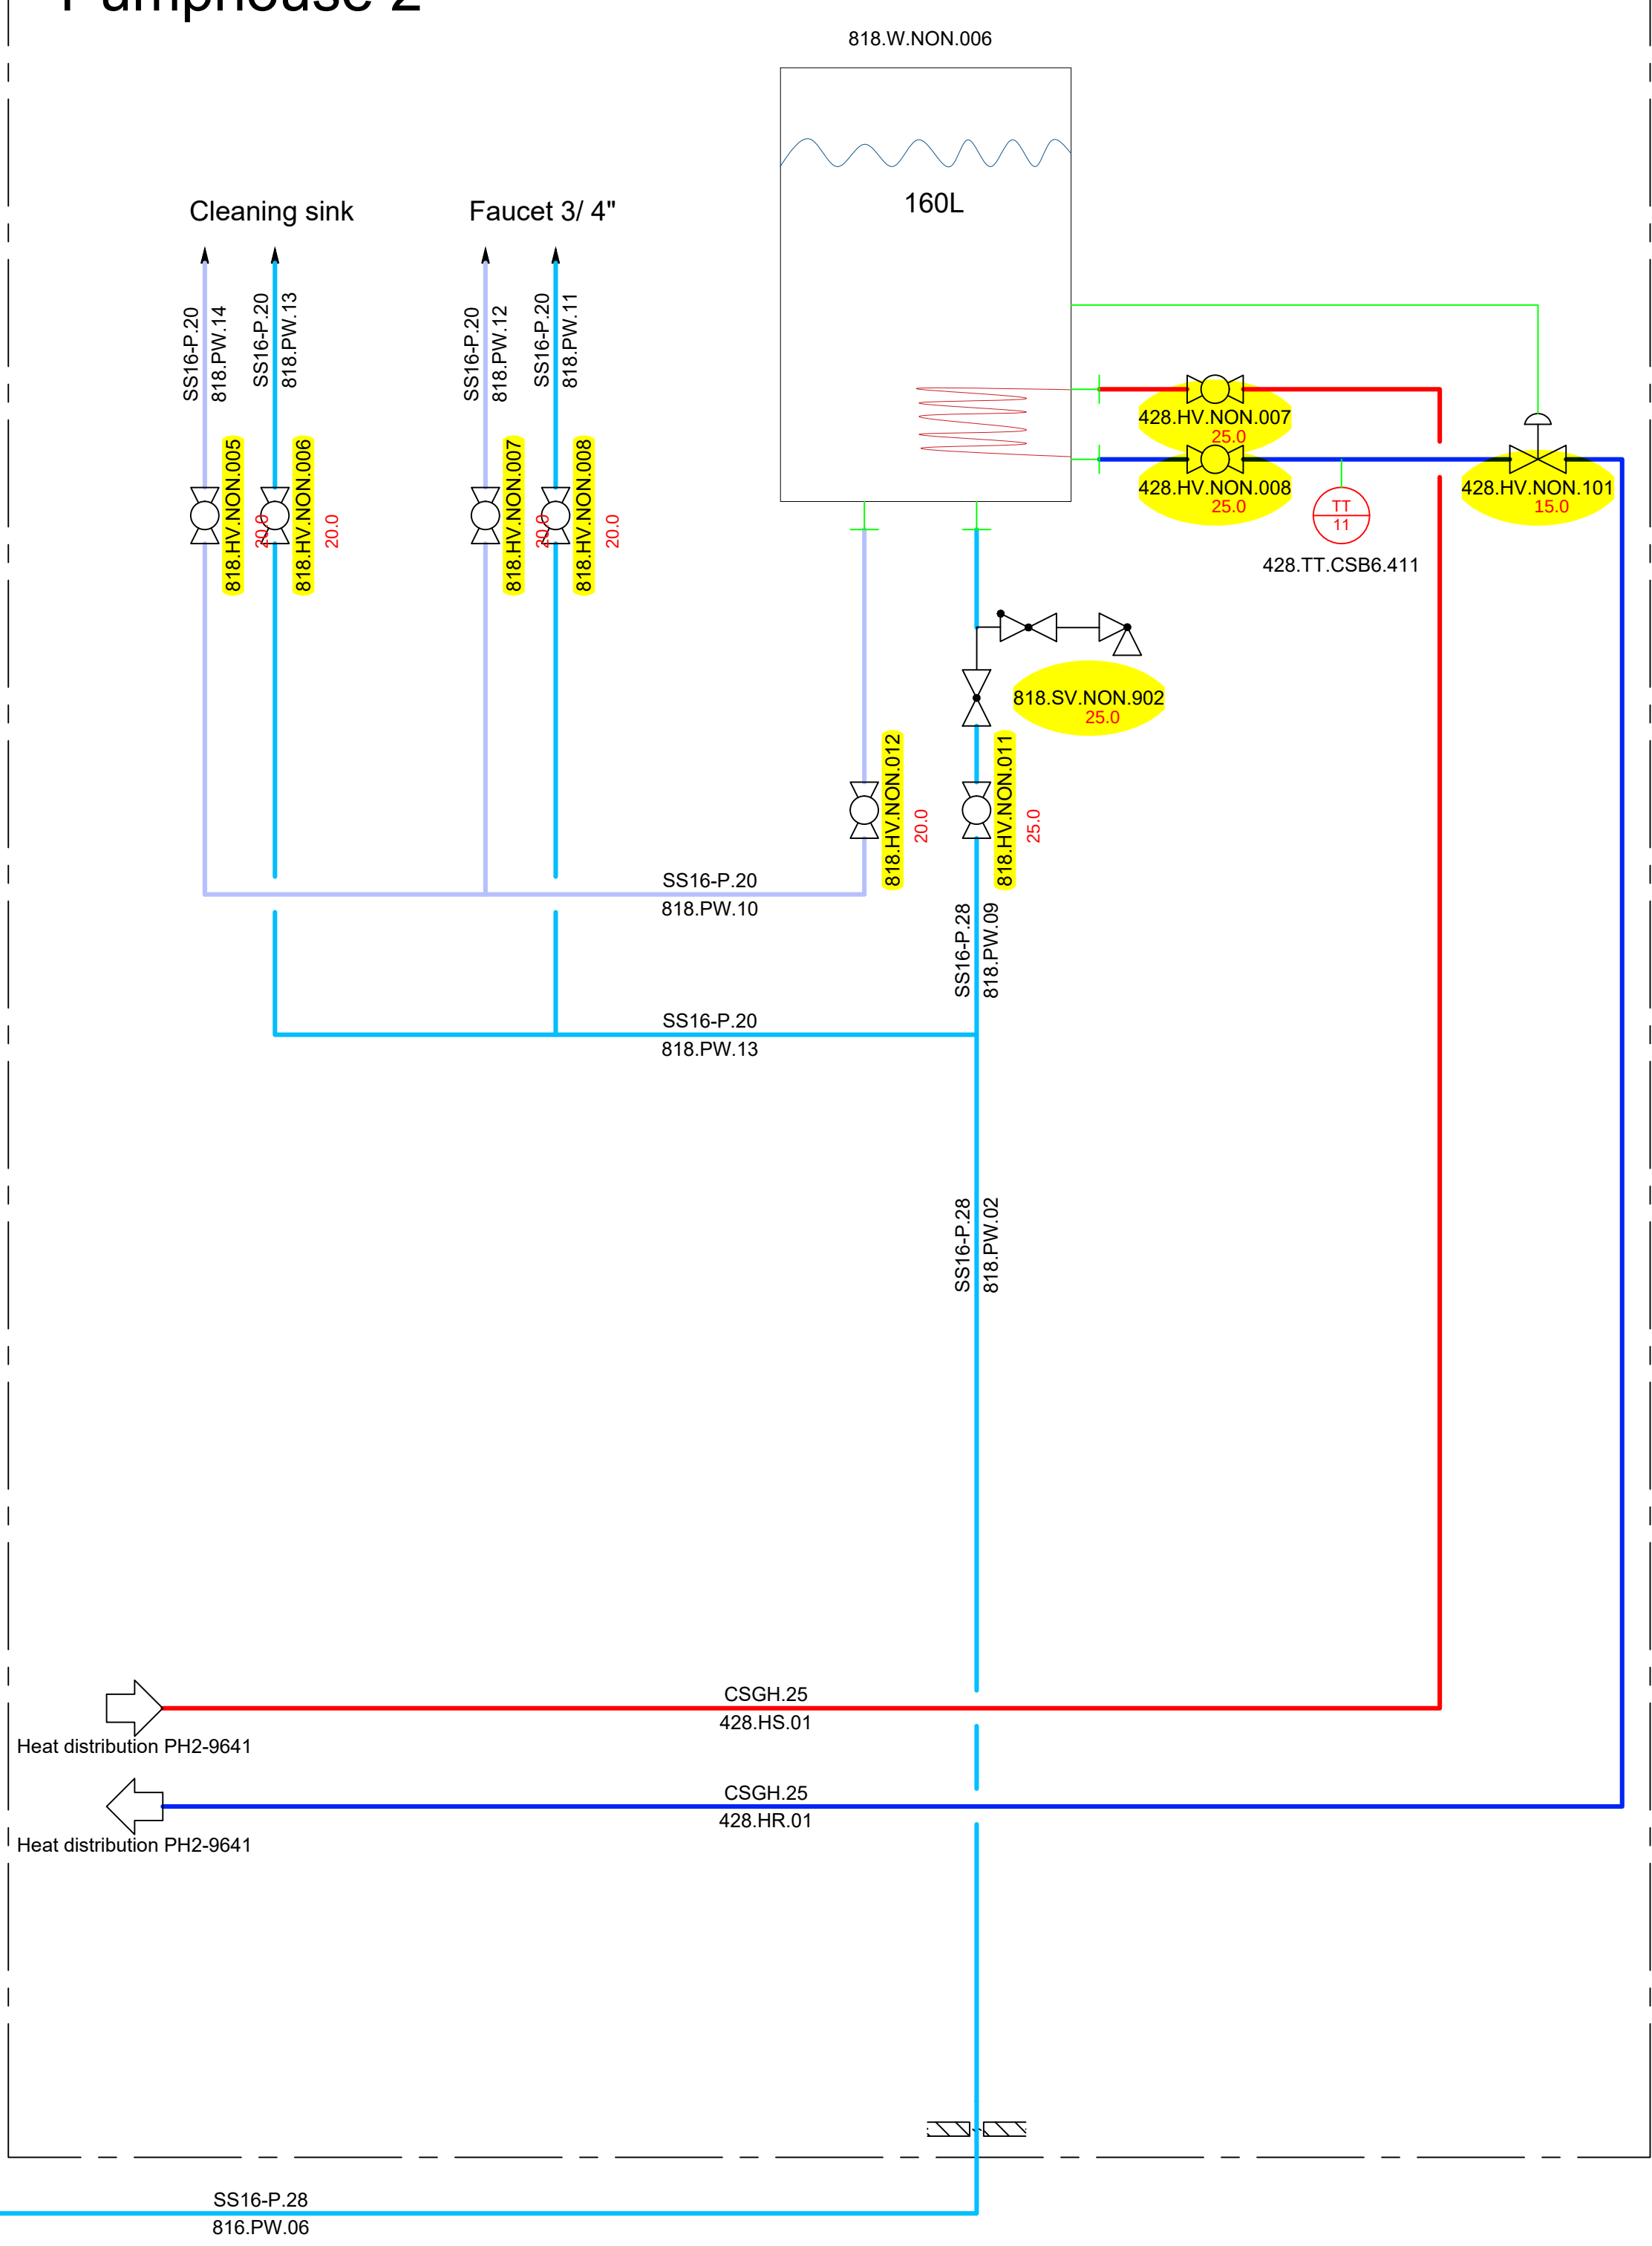


Rev. Nr.:	Rev. Dato:	Rev. Beskrivelse:
Builder:	ST1	
Project:	SLK	
Subject:	Water distribution pumphouse 1 & 2	
Int.:MDC	QC:CM	APP.:
Date:	15-10-2025	
Project nr.:	1768	
Drawing nr.:	9645	
FORMAT:	A1	

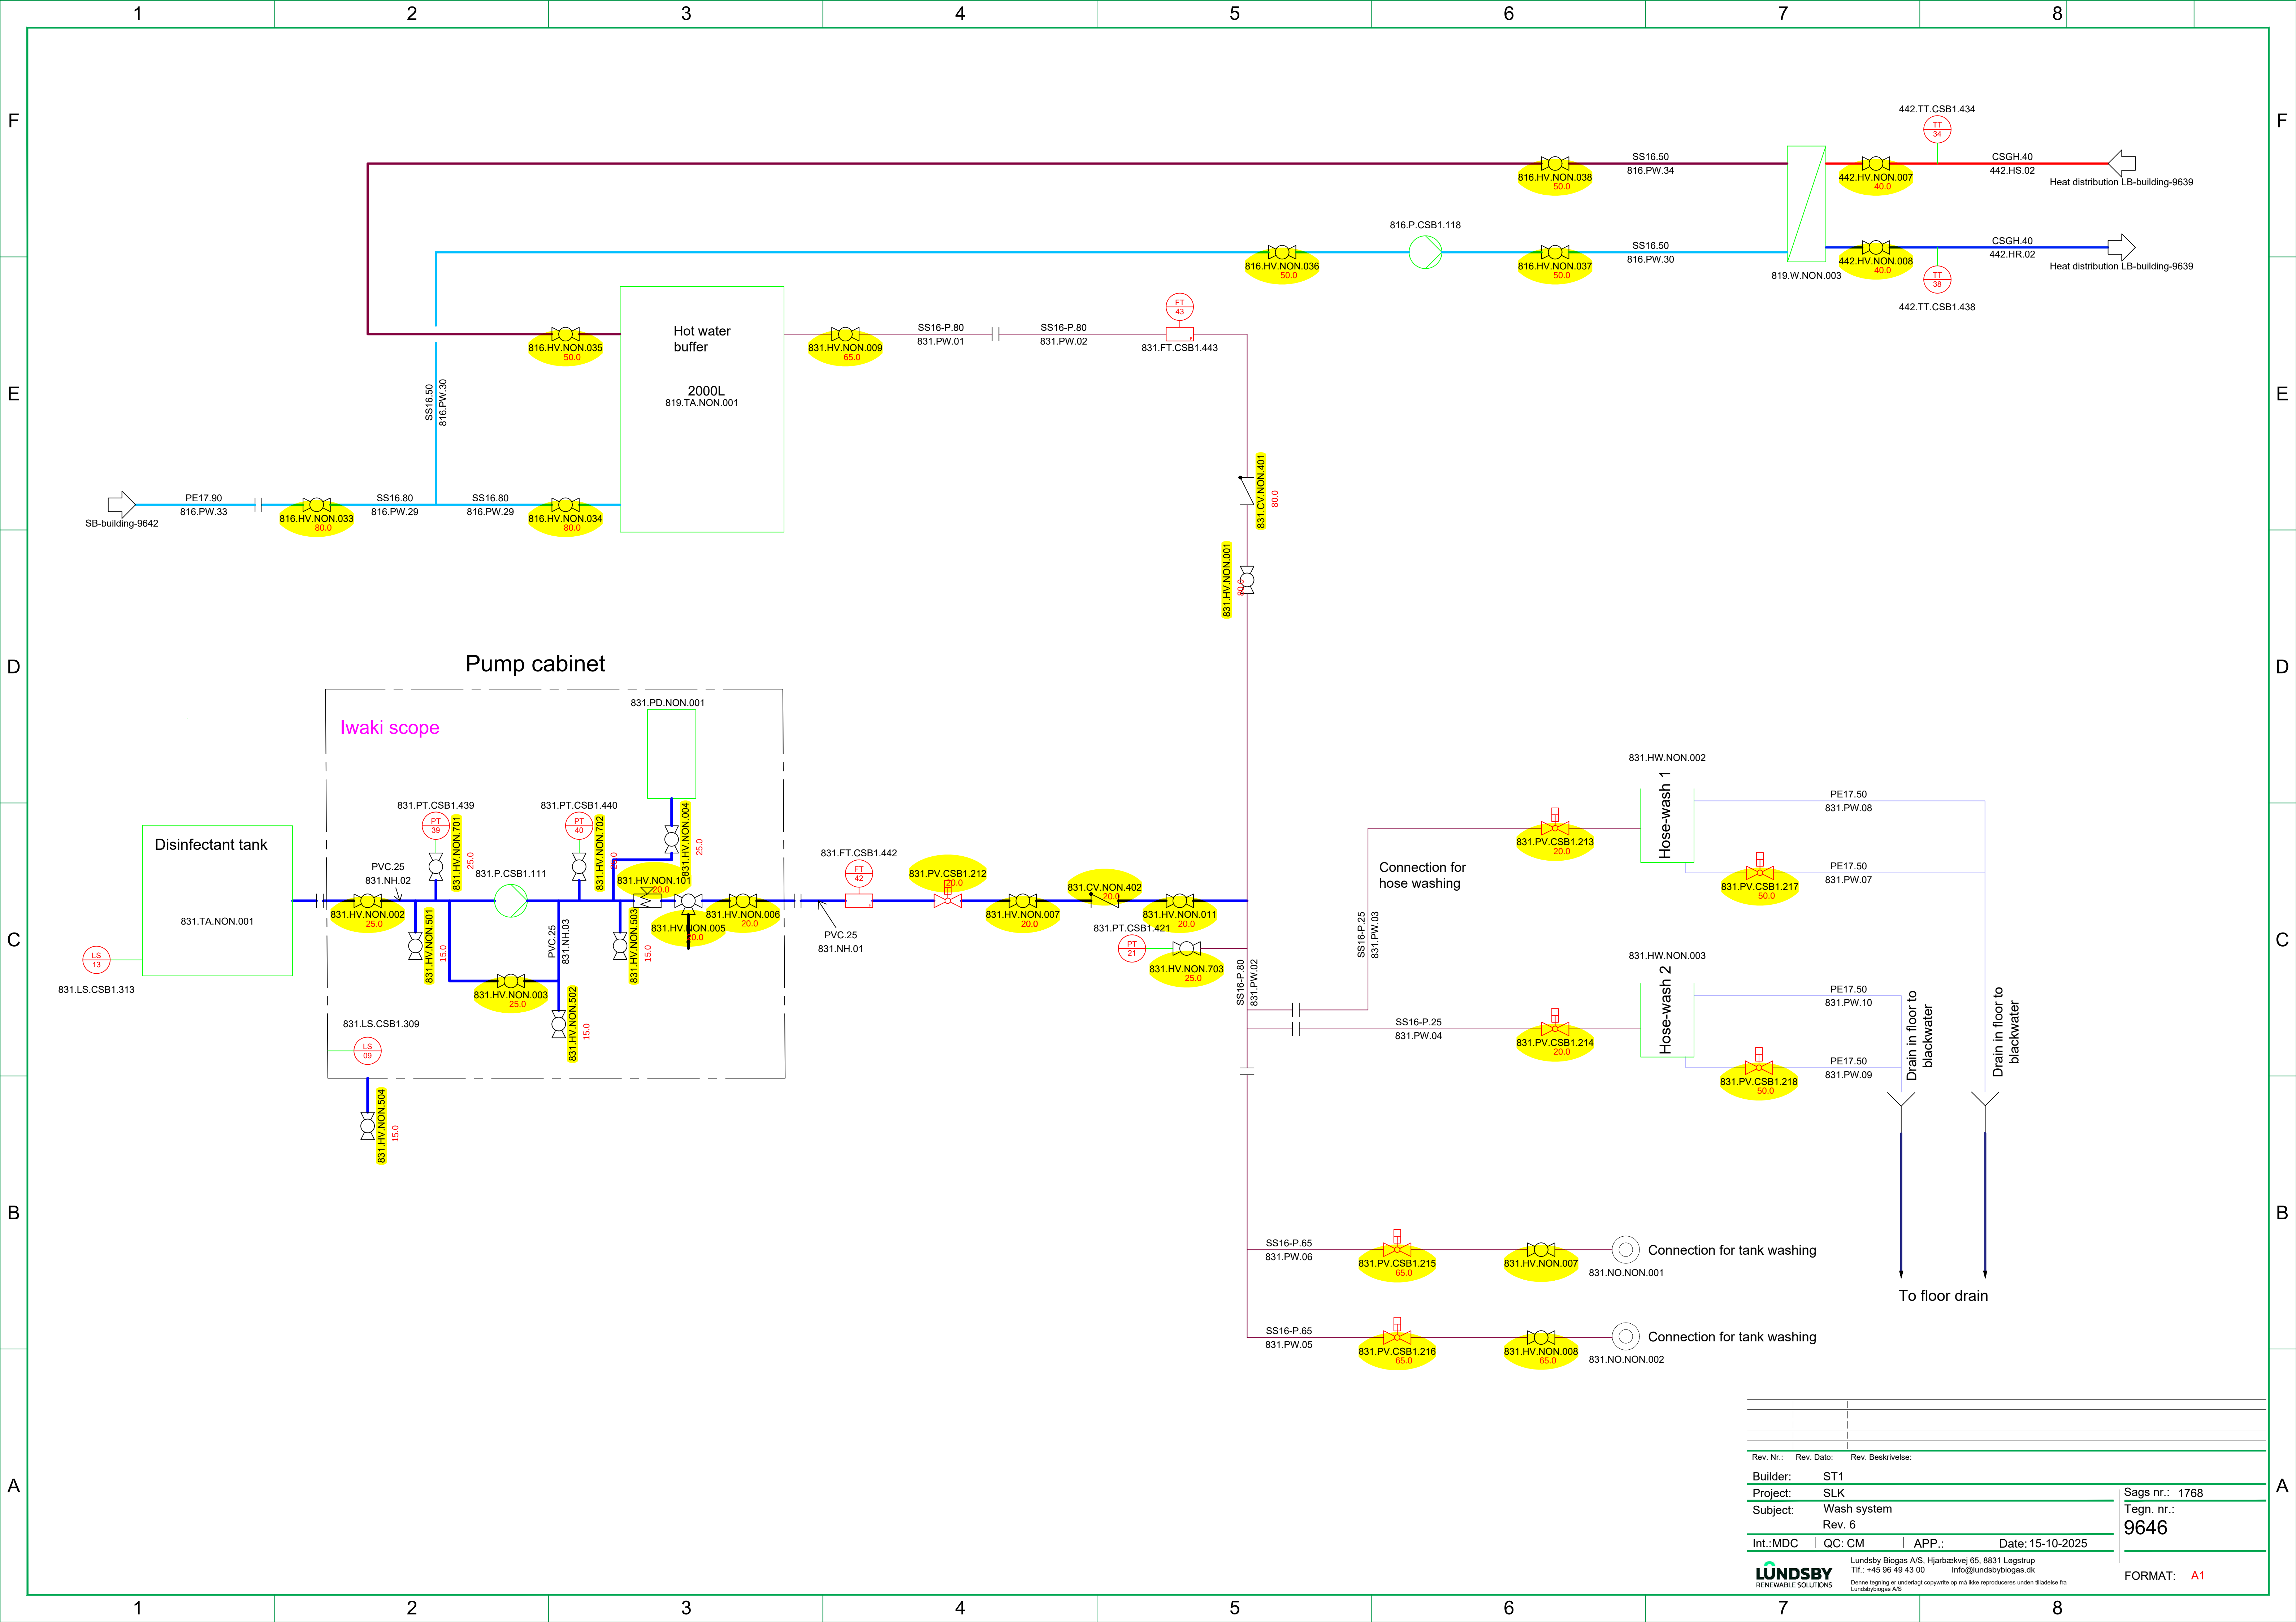


Rev. Nr.:	Rev. Dato:	Rev. Beskrivelse:	
Builder:	ST1		
Project:	SLK		
Subject:	Wash system		
Rev. 6			
Int.:MDC	QC: CM	APP.:	Date: 15-10-2025
LUNDSBY RENEWABLE SOLUTIONS			Lundsby Biogas A/S, Hjarbækvej 65, 8831 Løgstrup Tlf.: +45 96 49 43 00 info@lundsbybiogas.dk Denne tegning er underlagt copyright op på ikke reproduceres uden tilladelse fra Lundsbybiogas A/S
			Sags nr.: 1768 Tegn. nr.: 9646 FORMAT: A1

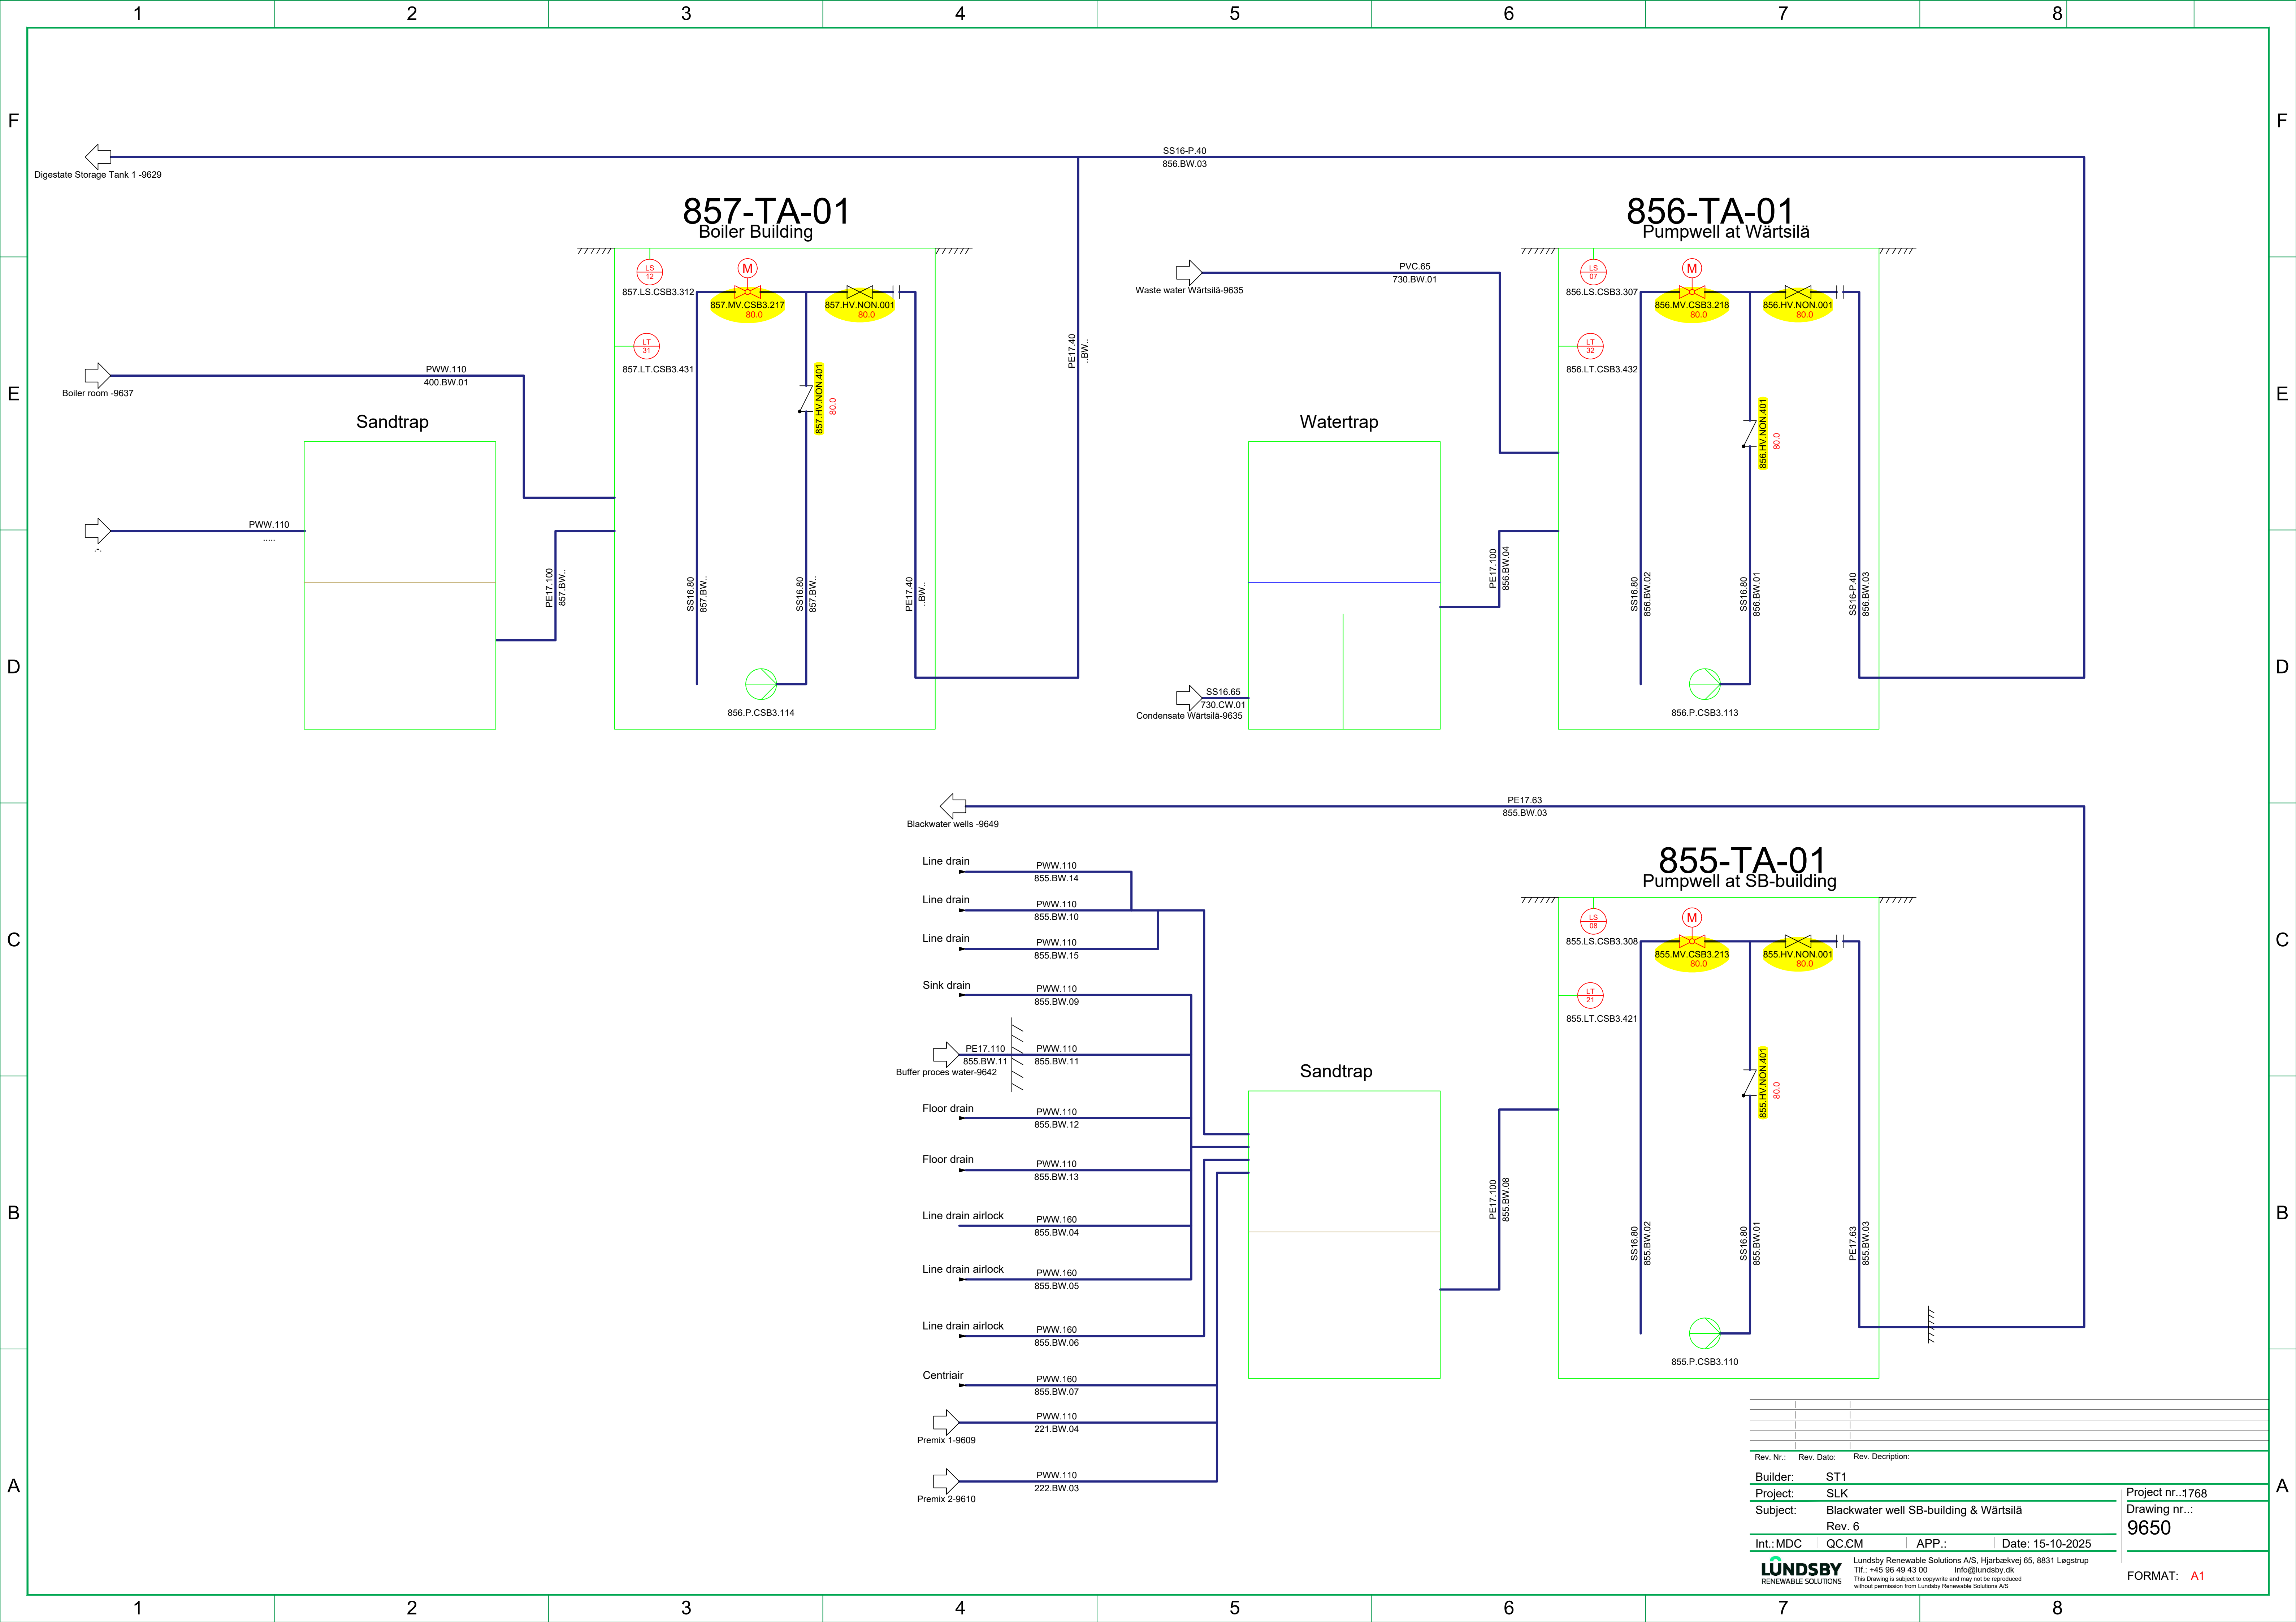

Pumphouse 1
JA Trykluft scope

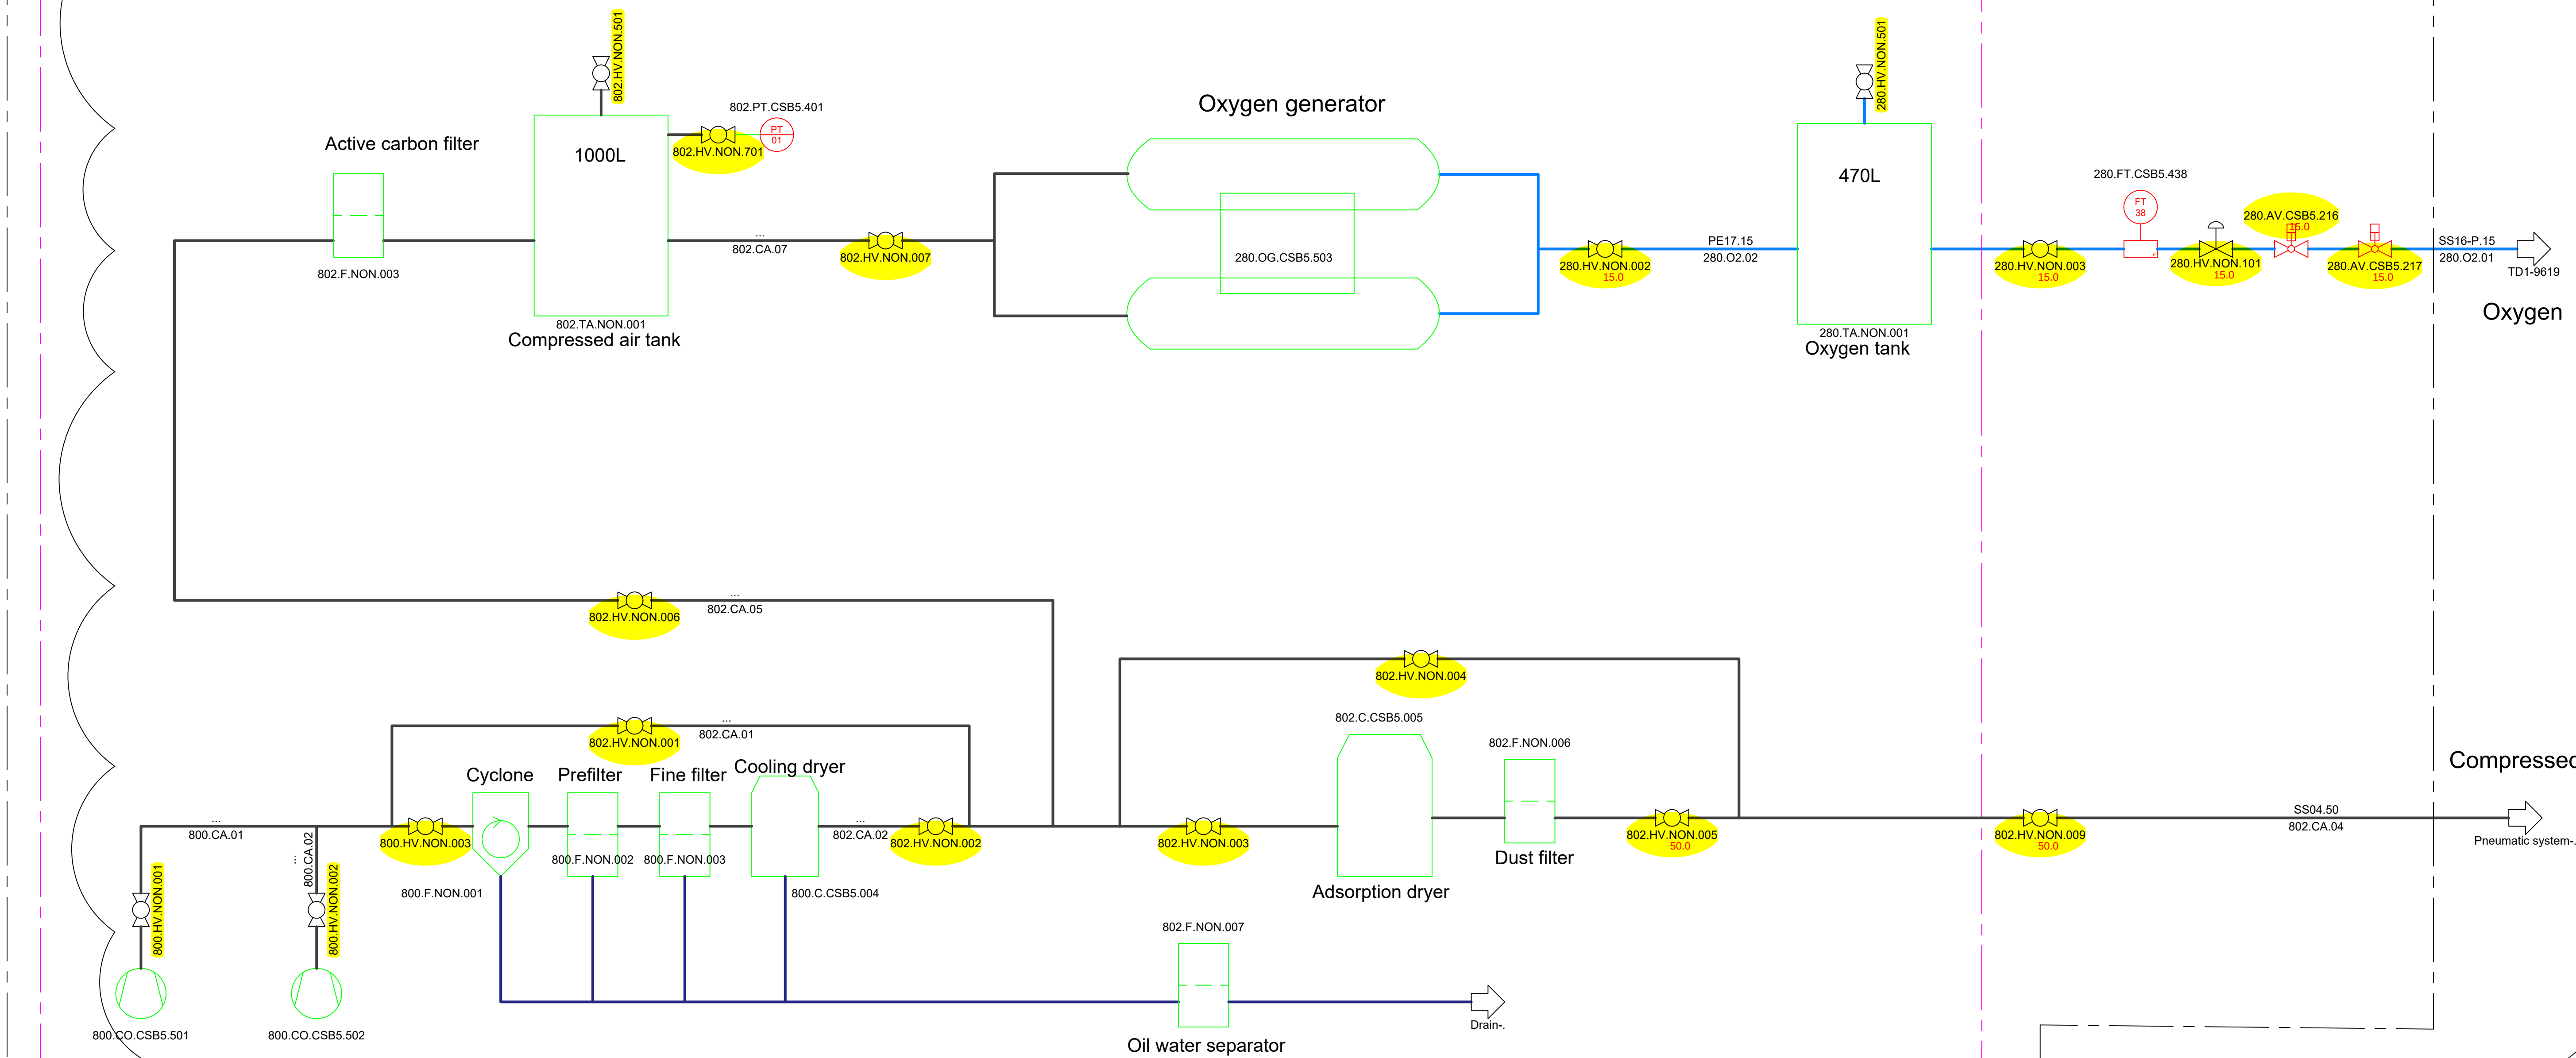


Rev. Nr.:	Rev. Dato:	Rev. Description:	
Builder:	ST1		
Project:	SLK		
Subject:	Compressed air & Oxygen		
Rev. 6			
Int.:MDC	QC.CM	APP.:	Date: 15-10-2025
LUNDSBY RENEWABLE SOLUTIONS			Lundsby Renewable Solutions A/S, Hjarbækvej 65, 8831 Legstrup Tlf.: +45 96 49 43 00 Info@lundsby.dk This drawing is subject to copyright and may not be reproduced without permission from Lundsby Renewable Solutions A/S
Project nr.:1768 Drawing nr.: 9652			FORMAT: A1

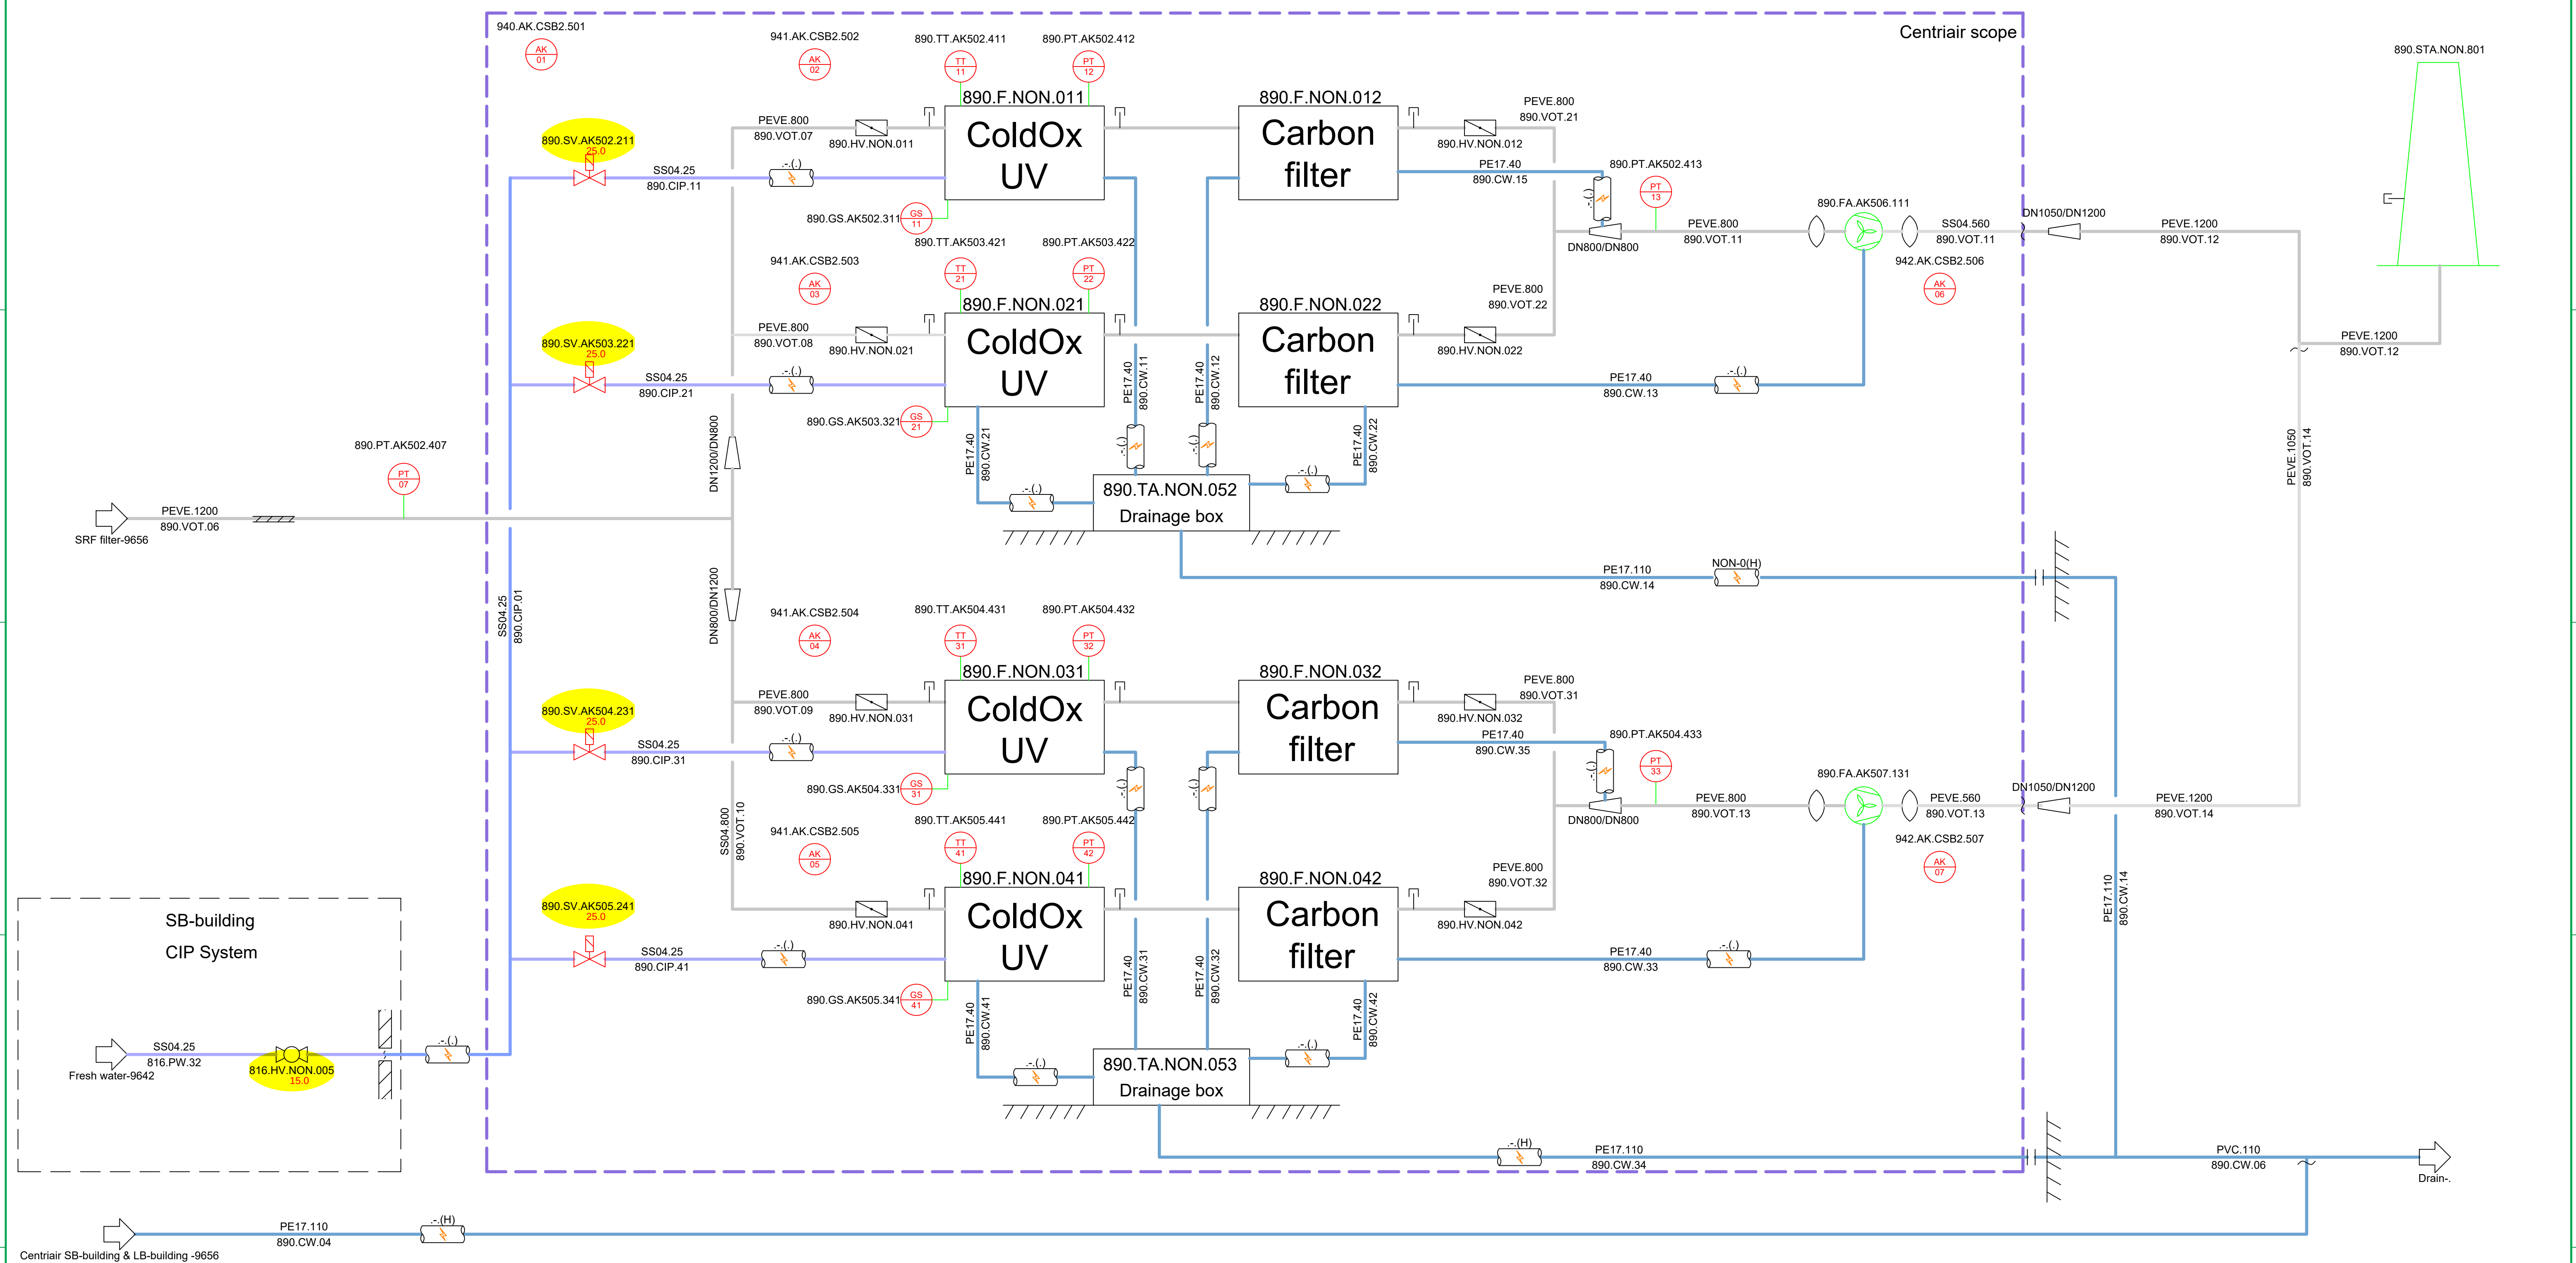


Rev. Nr.:	Rev. Dato:	Rev. Description:
Builder:	ST1	
Project:	SLK	
Subject:	Centriair ColdOx system	
Rev. 6		
Int.: MDC	QC:CM	APP.: Date: 15-10-2025
LUNDSBY RENEWABLE SOLUTIONS		
Lundsby Renewable Solutions A/S, Hjarbækvej 65, 8831 Løgstrup Tlf.: +45 96 49 43 00 info@lundsby.dk This drawing is subject to copyright and may not be reproduced without permission from Lundsby Renewable Solutions A/S		
Project nr.: 1768 Drawing nr.: 9655		FORMAT: A1


LB-building

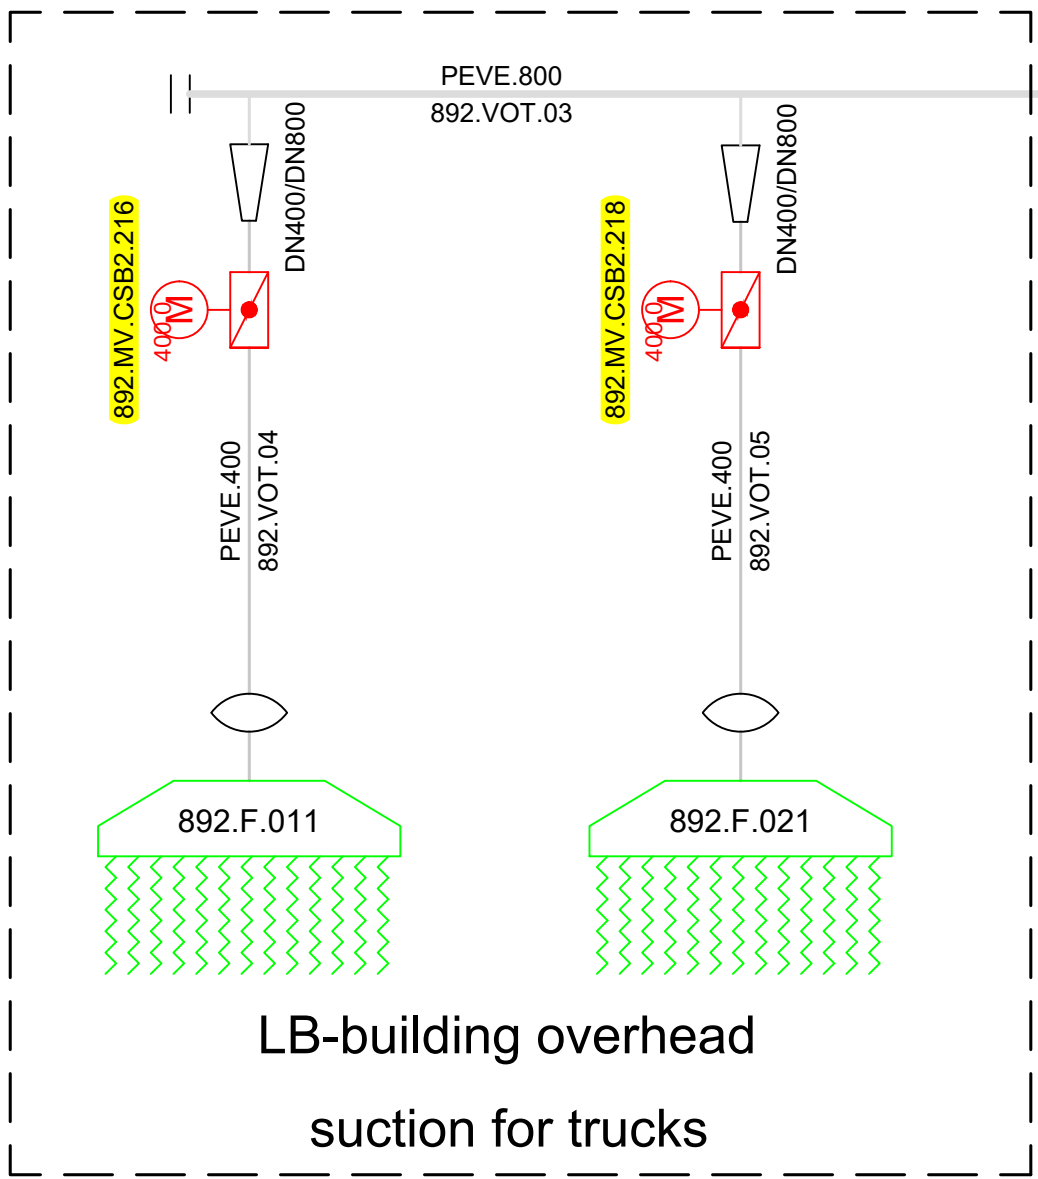


Centriair scope

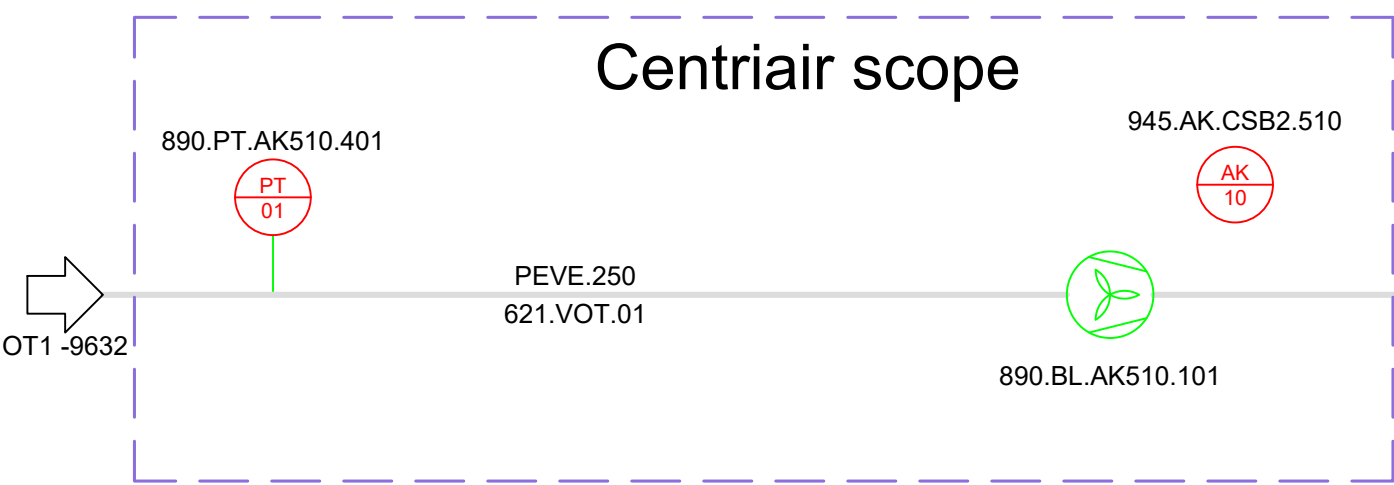

Centriair scope

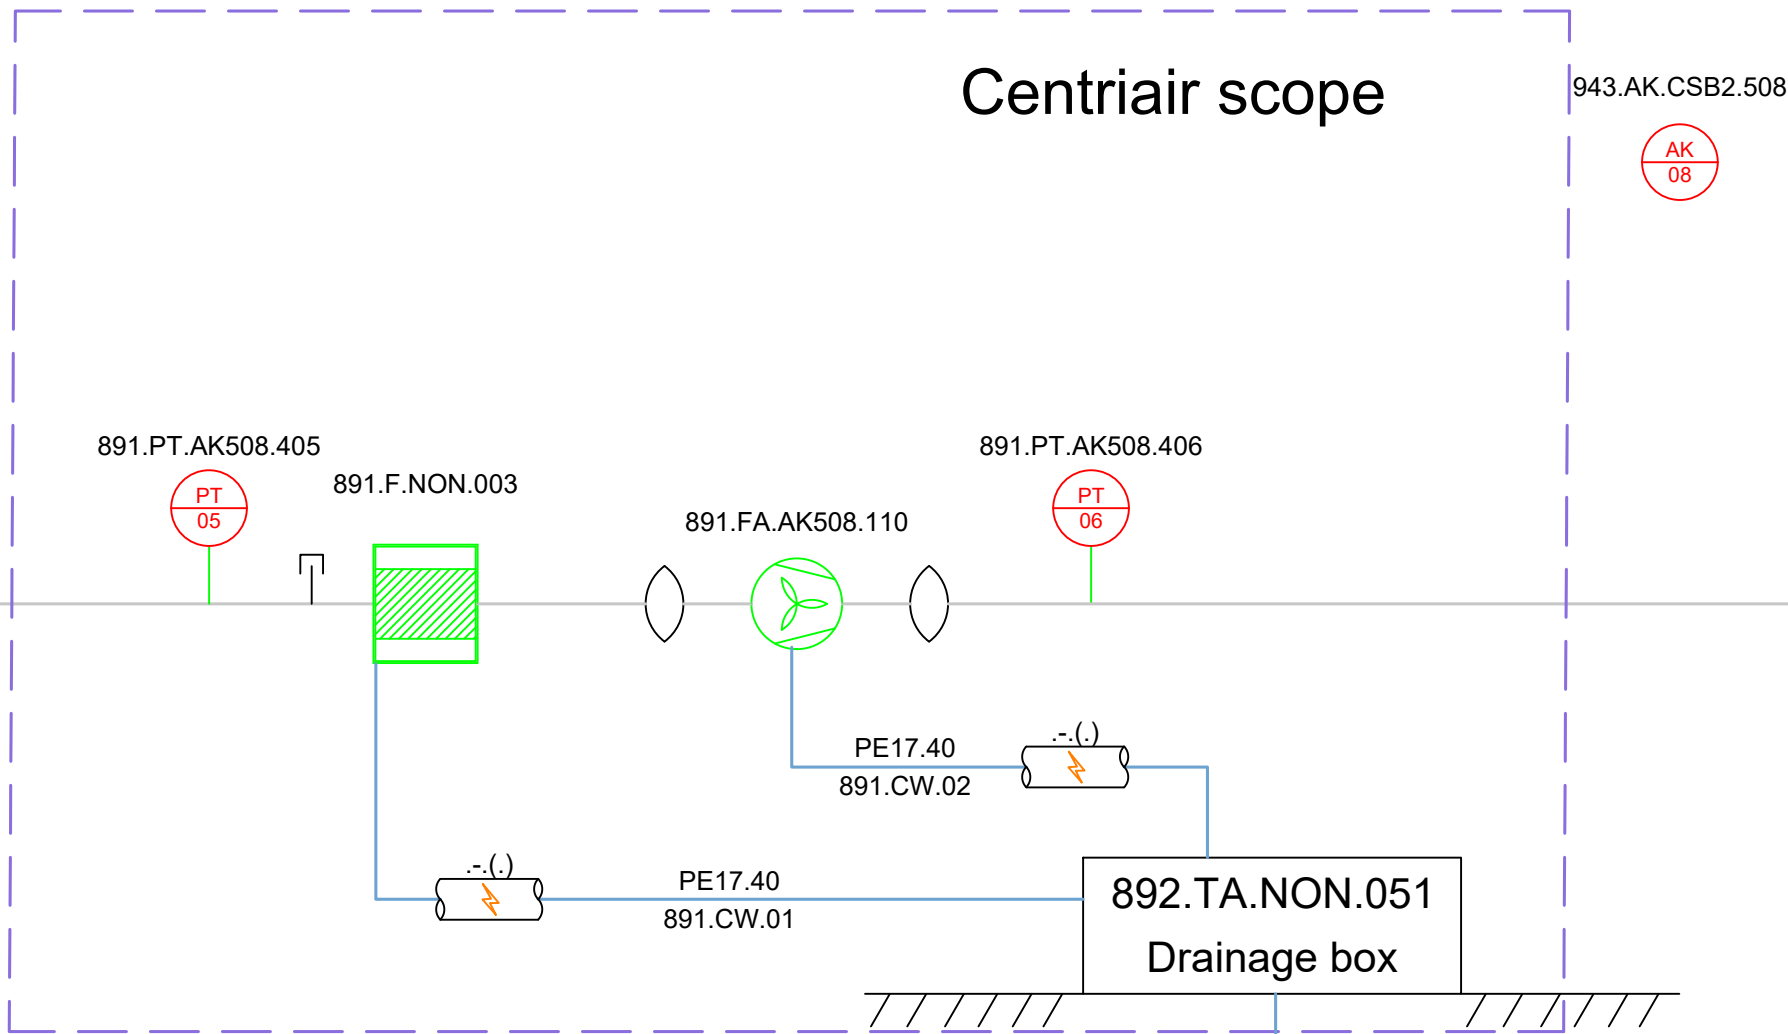

Rev. Nr.:	Rev. Dato:	Rev. Description:
Builder:	ST1	
Project:	SLK	
Subject:	Centriair SB-building & LB-building	
Rev. 6		
Int.:MDC	QC:CM	APP.:
Date: 15-10-2025		
LUNDSBY RENEWABLE SOLUTIONS		
Lundsby Renewable Solutions A/S, Hjarbækvej 65, 8831 Lægstrup Tlf.: +45 96 49 43 00 Info@lundsby.dk This Drawing is subject to copyright and may not be reproduced without permission from Lundsby Renewable Solutions A/S		
Project nr.:1768 Drawing nr.: 9656		FORMAT: A1

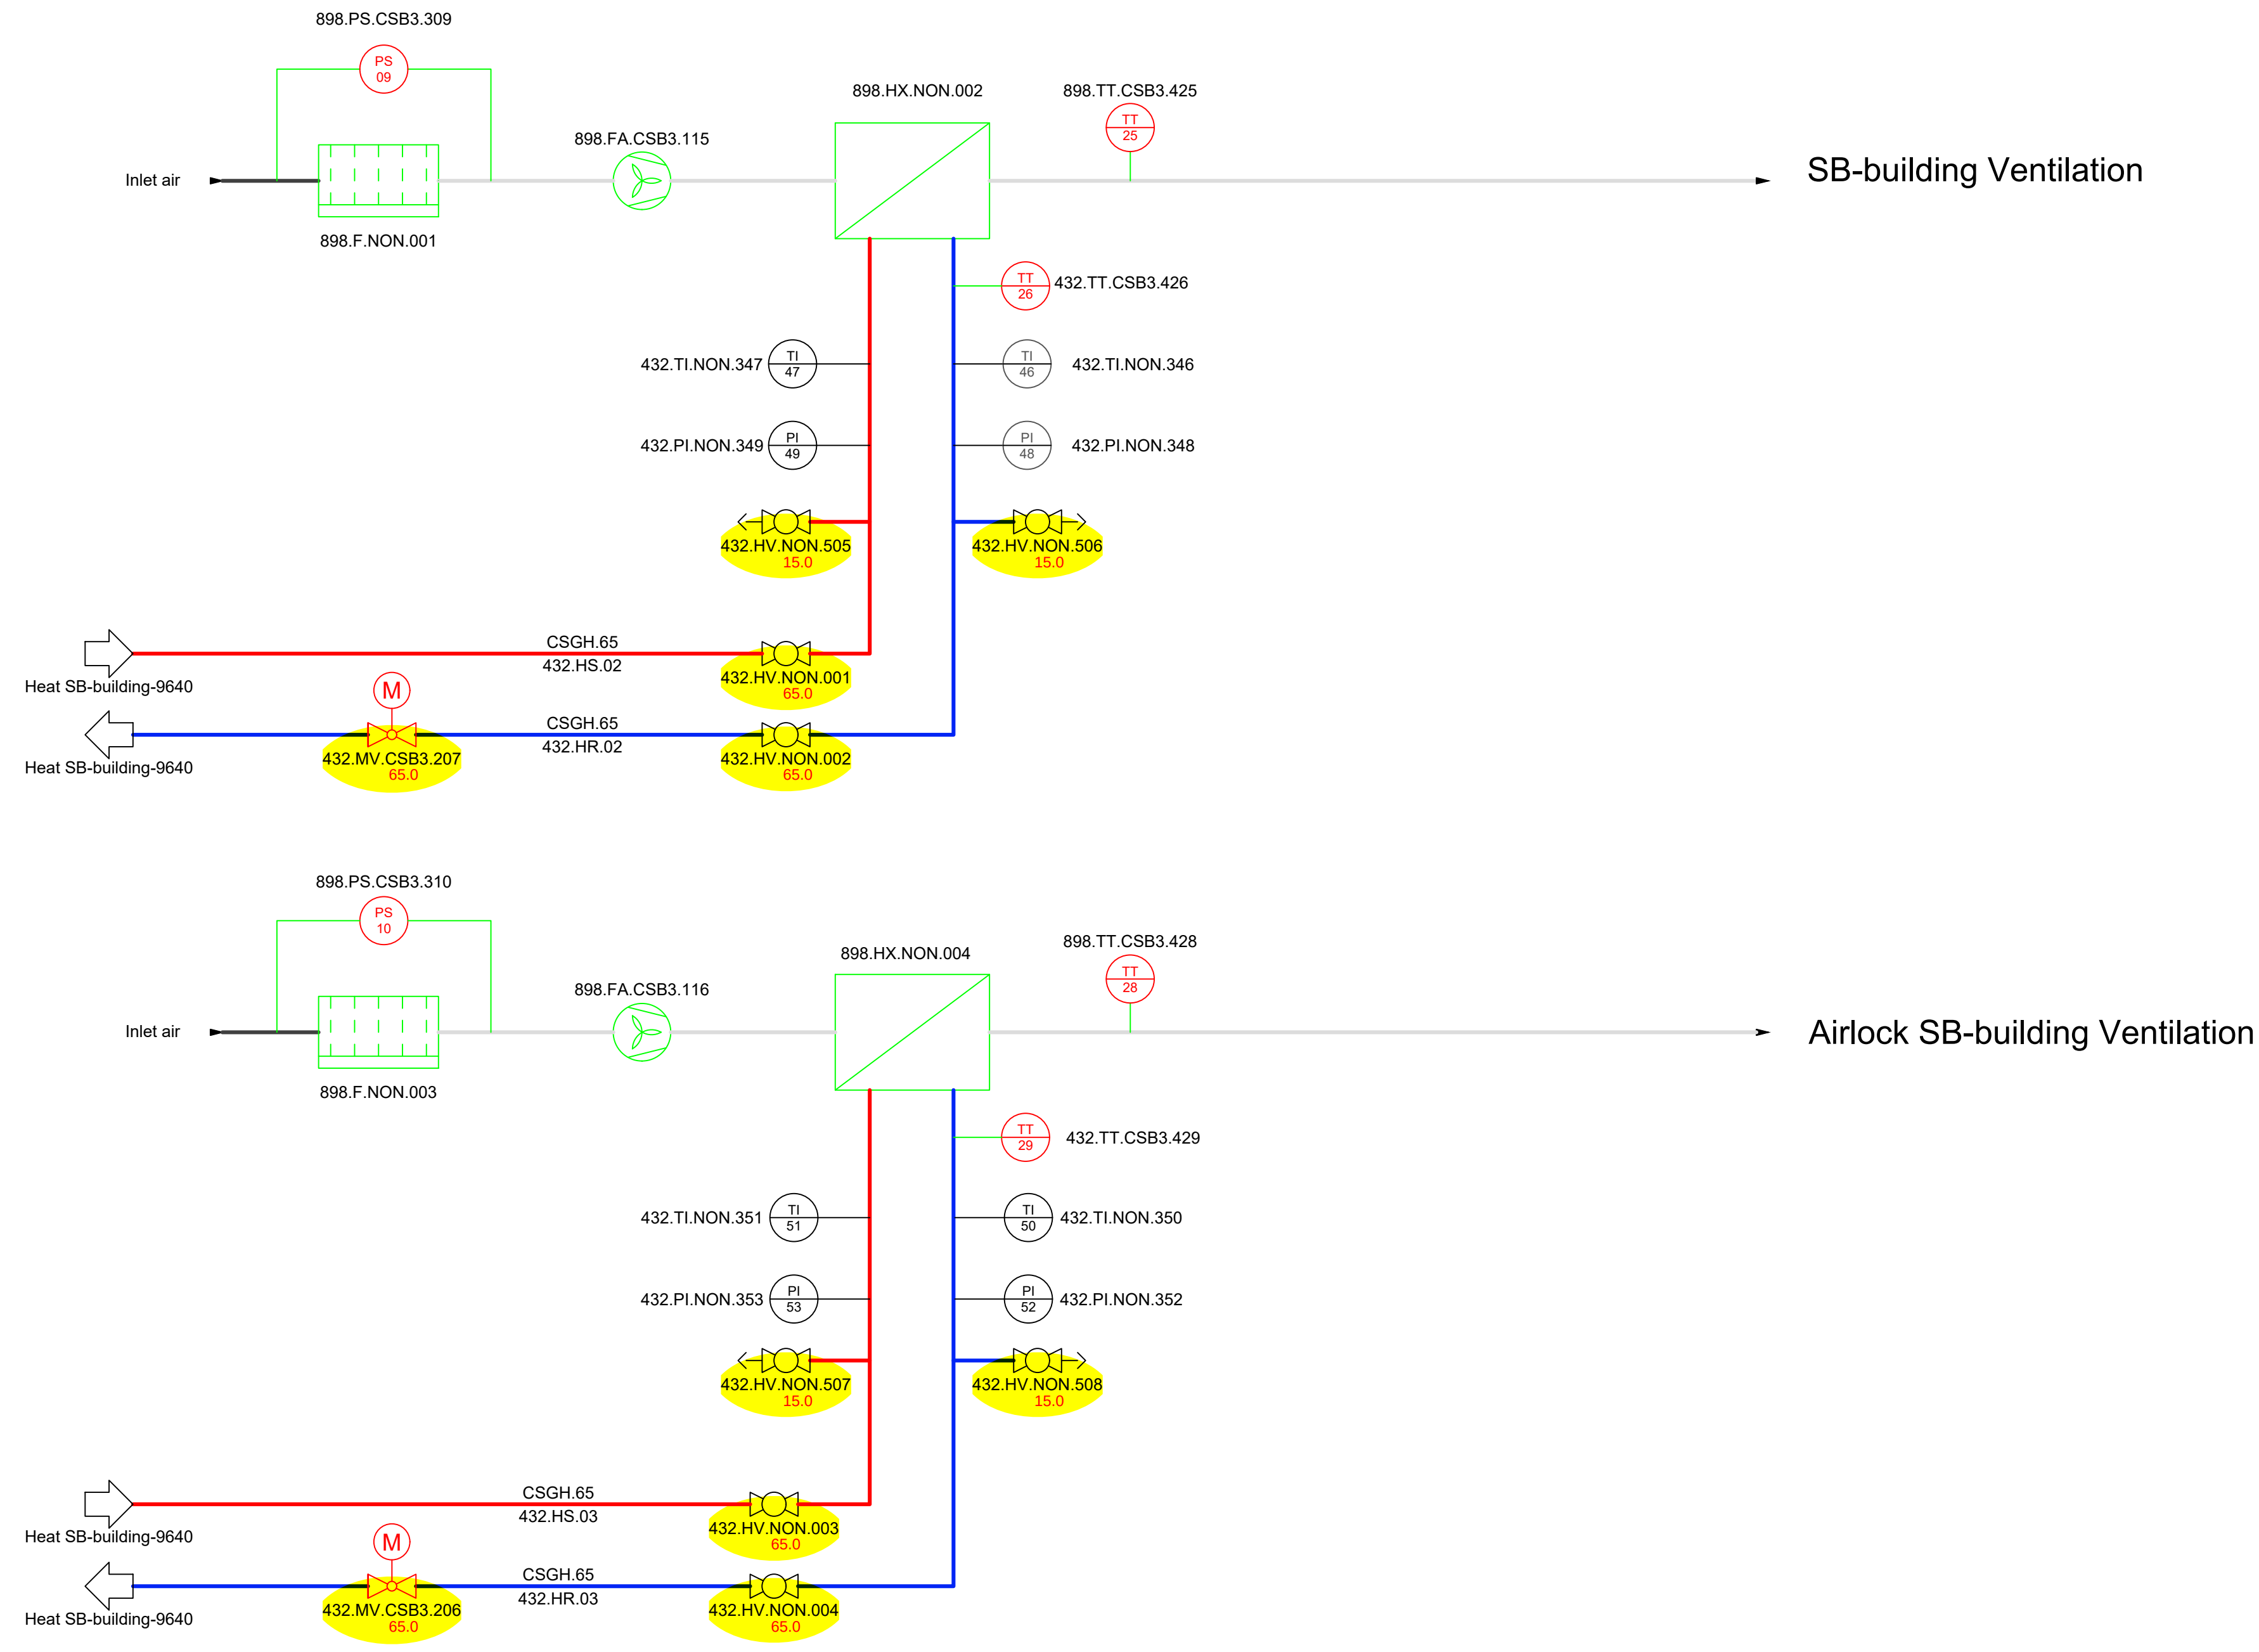

Rev. Nr.:	Rev. Dato:	Rev. Description:	
Builder:	ST1		
Project:	SLK		
Subject:	Ventilation SB-building		
Rev. 6			
Int.:MDC	QC.:CM	APP.:	Date: 15-10-2025
LUNDSBY RENEWABLE SOLUTIONS			Lundsby Renewable Solutions A/S, Hjarbækvej 65, 8831 Løgstrup Tlf.: +45 96 49 43 00 Info@lundsby.dk This Drawing is subject to copyright and may not be reproduced without permission from Lundsby Renewable Solutions A/S
Project nr.: 1768 Drawing nr.: 9657			FORMAT: A1