




1	2	3	4	5	6	7	8	
Structure of the tagging system	
Structure of the component tagging			Lines		Bulding/Area/Tank		Media code	
XXX — XXX — XXX — XXX Main equipment area codeEquipment ValveInstrument abbreviationSupply from switchboardNumeric Sequence Example 552 - TA - NON - 001 101 Switchboard Tank Area pasteurization tank 2 301.TA.NON.1: where 301 = Digester (System number), TA = Tank (Equipment), NON = Mechanical object (No switchboard), 01 = Tank nr 1. 201.P.CSB2.05: where 201 = Manure/feeding (System number), P = Pump (Equipment), CSB2 = Electrical object (Distribution board), 05 = Pump nr 5. 901.AK.CSB1.03: where 901 = Control and automation (System number), AK = Sub-distribution board at subcontractor (Equipment), CSB1 = Electrical object (Distribution board), 03 = Cabinet nr 3.			Description Symbol Subcontractor scope Boundary line Page connector Start pipe - Not linked to page End pipe - Not linked to page Fald/ Slope Insulation Electrical Heat tracing		Description Code Primary digester Secondary digester Digester storage Liquid manure tank Liquid biomass tank Outlet tank Blackwater tank Tech building Admin building Solid biomass building Liquid biomass building Plansilo Pump house Hygienization tanks Flare Stack Odour treatment facility Upgrade facility Liquifaction facility Oil boiler Wood boiler Transformer		Media Pipe color RBG color Code Heat Return Heat Supply Heat Hot Return Heat Hot Supply Cooling Supply Cooling Return Black Water CIP Process Water Technical Water Drinking Water Drinking Water Hot Condensate Steam Steam Condensate Liquid Manure (Slurry) Liquid Biomass (Substrat) Process Biomass Hygienized Biomass Recirculated Biomass Ferric Chloride FeCl Ventilation Odour Treatment Ventilation Fresh Air Compressed Air Oxygen Raw Biogas Return/reject Gas Nature Gas	
<table><tr><th>System:</th><th colspan="2">System number:</th></tr><tr><td>Reception</td><td>100-199</td><td></td></tr><tr><td>Manure tank</td><td></td><td>100-109</td></tr><tr><td>Fat/Liquid Substrate tank</td><td></td><td>110-119</td></tr><tr><td>Dry Dosificator tank</td><td></td><td>120-129</td></tr><tr><td>FeCl tank</td><td></td><td>130-139</td></tr><tr><td>Glycerol tank</td><td></td><td>140-149</td></tr><tr><td>Cereals silo</td><td></td><td>160-169</td></tr><tr><td>Water tank</td><td></td><td>170-179</td></tr><tr><td>LPG tank</td><td></td><td>180-189</td></tr><tr><td>Beets and root crops</td><td></td><td>190-191</td></tr><tr><td>Feeding in</td><td>200-299</td><td></td></tr><tr><td>Manure feeding</td><td></td><td>200-209</td></tr><tr><td>Fat/Liquid Substrate feeding</td><td></td><td>210-219</td></tr><tr><td>Dry Dosificator</td><td></td><td>220-229</td></tr><tr><td>FeCl feeding</td><td></td><td>230-239</td></tr><tr><td>Glycerol feeding</td><td></td><td>240-249</td></tr><tr><td>Pasteurization before digester</td><td></td><td>250</td></tr><tr><td>Cereal feeding</td><td></td><td>260</td></tr><tr><td>Water feeding</td><td></td><td>270</td></tr><tr><td>Oxygen/air dozing</td><td></td><td>280</td></tr><tr><td>Mixing tank</td><td></td><td>290</td></tr><tr><td>Digester</td><td>300-399</td><td></td></tr><tr><td>Primary Digester</td><td></td><td>300-309</td></tr><tr><td>Secondary Digester</td><td></td><td>310-319</td></tr><tr><td>Tertiary Digester</td><td></td><td>320-329</td></tr><tr><td>Line X</td><td></td><td>3X0</td></tr><tr><td>Heating system</td><td>400-499</td><td></td></tr><tr><td>Heating system</td><td></td><td>400-449</td></tr><tr><td>Cooling system</td><td></td><td>450-459</td></tr><tr><td>Feeding out</td><td>500-599</td><td></td></tr><tr><td>Pump</td><td></td><td>500 - 509</td></tr><tr><td>Pasteurization after digester</td><td></td><td>550</td></tr><tr><td>Biofertilizer tank</td><td>600-699</td><td></td></tr><tr><td>Biofertilizer tank 1</td><td></td><td>601</td></tr><tr><td>Biofertilizer tank 2</td><td></td><td>602</td></tr><tr><td>Separation</td><td></td><td>610 - 619</td></tr><tr><td>Gas treatment</td><td>700-799</td><td></td></tr><tr><td>Components on general gas pipe</td><td></td><td>700</td></tr><tr><td>Condensate pit</td><td></td><td>710</td></tr><tr><td>Flare</td><td></td><td>720</td></tr><tr><td>Upgrading unit/CHP/boiler</td><td></td><td>730</td></tr><tr><td>Stripper air combustion</td><td></td><td>740</td></tr><tr><td>RTO</td><td></td><td>750</td></tr><tr><td>High pressure compressor station</td><td></td><td>760</td></tr><tr><td>LNG plant</td><td></td><td>770</td></tr><tr><td>Propane dosing</td><td></td><td>780</td></tr><tr><td>Support system</td><td>800-899</td><td></td></tr><tr><td>Instrument air</td><td></td><td>800</td></tr><tr><td>Hydraulic system</td><td></td><td>805</td></tr><tr><td>Water</td><td></td><td>810</td></tr><tr><td>Backflow protection system</td><td></td><td>815</td></tr><tr><td>Heat tracing cable</td><td></td><td>820</td></tr><tr><td>Car wash</td><td></td><td>830</td></tr><tr><td>Building/container</td><td></td><td>840</td></tr><tr><td>Pumpwell</td><td></td><td>850</td></tr><tr><td>Oil separator</td><td></td><td>860</td></tr><tr><td></td><td></td><td>870</td></tr><tr><td>Dosing equipment</td><td></td><td>880</td></tr><tr><td>Odour cntro/ventilation system</td><td></td><td>890</td></tr><tr><td>Electrical and Control</td><td>900-999</td><td></td></tr><tr><td>Control and automation</td><td></td><td>900-949*</td></tr><tr><td>Server and IT</td><td></td><td>950*</td></tr><tr><td>Electrical power high voltage (>1000V)</td><td></td><td>980-989*</td></tr><tr><td>Electrical power low voltage</td><td></td><td>990-999*</td></tr></table>			System:	System number:		Reception	100-199		Manure tank		100-109	Fat/Liquid Substrate tank		110-119	Dry Dosificator tank		120-129	FeCl tank		130-139	Glycerol tank		140-149	Cereals silo		160-169	Water tank		170-179	LPG tank		180-189	Beets and root crops		190-191	Feeding in	200-299		Manure feeding		200-209	Fat/Liquid Substrate feeding		210-219	Dry Dosificator		220-229	FeCl feeding		230-239	Glycerol feeding		240-249	Pasteurization before digester		250	Cereal feeding		260	Water feeding		270	Oxygen/air dozing		280	Mixing tank		290	Digester	300-399		Primary Digester		300-309	Secondary Digester		310-319	Tertiary Digester		320-329	Line X		3X0	Heating system	400-499		Heating system		400-449	Cooling system		450-459	Feeding out	500-599		Pump		500 - 509	Pasteurization after digester		550	Biofertilizer tank	600-699		Biofertilizer tank 1		601	Biofertilizer tank 2		602	Separation		610 - 619	Gas treatment	700-799		Components on general gas pipe		700	Condensate pit		710	Flare		720	Upgrading unit/CHP/boiler		730	Stripper air combustion		740	RTO		750	High pressure compressor station		760	LNG plant		770	Propane dosing		780	Support system	800-899		Instrument air		800	Hydraulic system		805	Water		810	Backflow protection system		815	Heat tracing cable		820	Car wash		830	Building/container		840	Pumpwell		850	Oil separator		860			870	Dosing equipment		880	Odour cntro/ventilation system		890	Electrical and Control	900-999		Control and automation		900-949*	Server and IT		950*	Electrical power high voltage (>1000V)		980-989*	Electrical power low voltage		990-999*	<table><tr><th>Pipe Spec list</th><th>Code</th></tr><tr><td>Carbon steel P235TR1</td><td>CSTR</td></tr><tr><td>Carbon steel P235GH</td><td>CSGH</td></tr><tr><td>Preinsulated Carbon steel P235GH</td><td>CSGH-PRI</td></tr><tr><td>Stainless steel pipes 1.4304</td><td>SS16 / SS16-P</td></tr><tr><td>PE100 SDR17</td><td>PE17</td></tr><tr><td>Preinsulated PE100 SDR17</td><td>PE17-PRI</td></tr><tr><td>PE100 SDR11</td><td>PE11</td></tr><tr><td>PE pipes for ventilation</td><td>PEVE</td></tr><tr><td>PE Drain Pipes</td><td>PWW</td></tr><tr><td>Electrical Conduit And Piping</td><td>ELCP</td></tr><tr><td>Ventilation Steel</td><td>VENTS</td></tr><tr><td>Ventilation Plastic</td><td>VENTP</td></tr><tr><td>?</td><td>Unknown</td></tr></table>		Pipe Spec list	Code	Carbon steel P235TR1	CSTR	Carbon steel P235GH	CSGH	Preinsulated Carbon steel P235GH	CSGH-PRI	Stainless steel pipes 1.4304	SS16 / SS16-P	PE100 SDR17	PE17	Preinsulated PE100 SDR17	PE17-PRI	PE100 SDR11	PE11	PE pipes for ventilation	PEVE	PE Drain Pipes	PWW	Electrical Conduit And Piping	ELCP	Ventilation Steel	VENTS	Ventilation Plastic	VENTP	?	Unknown
System:	System number:	
Reception	100-199	
Manure tank		100-109	
Fat/Liquid Substrate tank		110-119	
Dry Dosificator tank		120-129	
FeCl tank		130-139	
Glycerol tank		140-149	
Cereals silo		160-169	
Water tank		170-179	
LPG tank		180-189	
Beets and root crops		190-191	
Feeding in	200-299	
Manure feeding		200-209	
Fat/Liquid Substrate feeding		210-219	
Dry Dosificator		220-229	
FeCl feeding		230-239	
Glycerol feeding		240-249	
Pasteurization before digester		250	
Cereal feeding		260	
Water feeding		270	
Oxygen/air dozing		280	
Mixing tank		290	
Digester	300-399	
Primary Digester		300-309	
Secondary Digester		310-319	
Tertiary Digester		320-329	
Line X		3X0	
Heating system	400-499	
Heating system		400-449	
Cooling system		450-459	
Feeding out	500-599	
Pump		500 - 509	
Pasteurization after digester		550	
Biofertilizer tank	600-699	
Biofertilizer tank 1		601	
Biofertilizer tank 2		602	
Separation		610 - 619	
Gas treatment	700-799	
Components on general gas pipe		700	
Condensate pit		710	
Flare		720	
Upgrading unit/CHP/boiler		730	
Stripper air combustion		740	
RTO		750	
High pressure compressor station		760	
LNG plant		770	
Propane dosing		780	
Support system	800-899	
Instrument air		800	
Hydraulic system		805	
Water		810	
Backflow protection system		815	
Heat tracing cable		820	
Car wash		830	
Building/container		840	
Pumpwell		850	
Oil separator		860	
		870	
Dosing equipment		880	
Odour cntro/ventilation system		890	
Electrical and Control	900-999	
Control and automation		900-949*	
Server and IT		950*	
Electrical power high voltage (>1000V)		980-989*	
Electrical power low voltage		990-999*	
Pipe Spec list	Code	
Carbon steel P235TR1	CSTR	
Carbon steel P235GH	CSGH	
Preinsulated Carbon steel P235GH	CSGH-PRI	
Stainless steel pipes 1.4304	SS16 / SS16-P	
PE100 SDR17	PE17	
Preinsulated PE100 SDR17	PE17-PRI	
PE100 SDR11	PE11	
PE pipes for ventilation	PEVE	
PE Drain Pipes	PWW	
Electrical Conduit And Piping	ELCP	
Ventilation Steel	VENTS	
Ventilation Plastic	VENTP	
?	Unknown	
Structure of the pipeline tagging system	
The pipetag consists of various information about the pipe Full pipeline tag as shown below Size-PipeSpec-Area-Service (Medie)-Serial number [100 PE17 201 LM 01] Example Two (2) digits. Starts with 01 [01] Two (2) to four (4) characters (letters) [LM - Liquid manure] Three (3) digits [201 - Manure feeding in tank 1] Pipe Spec name [PE17 - PE100 SDR17] Pipe size DN indication for Metric pipes OD indication for PE-pipe [This example is OD 100 mm]	
The pipe tag will be shown on the P&ID as follows: PipeSpec-Size Area-Service-Serialnumber Example of line tag notation on P&ID: PE17-110 201-LM-01 Line color corresponding to table above. The part below the pipeline is the Unique Line Tag. Unique Line Tag is generated automatically when creating complete Line Tag. Unique Line Tag is used by the P3D system when designing pipes in the 3D model and when generating Isometrics.	
<table><tr><td>Rev. Nr.:</td><td>Rev. Date:</td><td>Rev. Description:</td></tr><tr><td>Builder:</td><td>ST1</td><td></td></tr><tr><td>Project:</td><td>SLK</td><td></td></tr><tr><td>Subject:</td><td>PID Legend</td><td></td></tr><tr><td></td><td>Rev. 6</td><td></td></tr><tr><td>Int.:MDC</td><td>QC.:CM</td><td>APP.: Date: 15-10-2025</td></tr><tr><td colspan="3"> LUNDSBY RENEWABLE SOLUTIONS Lundsby Renewable Solutions A/S, Hjarbækvej 65, 8831 Legstrup Tlf.: +45 96 49 43 00 Info@lundsby.dk This Drawing is subject to copyright and may not be reproduced without permission from Lundsby Renewable Solutions A/S </td></tr><tr><td colspan="3">Project nr.:1768 Drawing nr.: PID Legend</td></tr><tr><td colspan="3">FORMAT: A1</td></tr></table>								Rev. Nr.:	Rev. Date:	Rev. Description:	Builder:	ST1		Project:	SLK		Subject:	PID Legend			Rev. 6		Int.:MDC	QC.:CM	APP.: Date: 15-10-2025	LUNDSBY RENEWABLE SOLUTIONS Lundsby Renewable Solutions A/S, Hjarbækvej 65, 8831 Legstrup Tlf.: +45 96 49 43 00 Info@lundsby.dk This Drawing is subject to copyright and may not be reproduced without permission from Lundsby Renewable Solutions A/S			Project nr.:1768 Drawing nr.: PID Legend			FORMAT: A1	
Rev. Nr.:	Rev. Date:	Rev. Description:	
Builder:	ST1	
Project:	SLK	
Subject:	PID Legend	
	Rev. 6	
Int.:MDC	QC.:CM	APP.: Date: 15-10-2025	
LUNDSBY RENEWABLE SOLUTIONS Lundsby Renewable Solutions A/S, Hjarbækvej 65, 8831 Legstrup Tlf.: +45 96 49 43 00 Info@lundsby.dk This Drawing is subject to copyright and may not be reproduced without permission from Lundsby Renewable Solutions A/S	
Project nr.:1768 Drawing nr.: PID Legend	
FORMAT: A1	
1	2	3	4	5	6	7	8	

1	2	3	4	5	6	7	8																																						
Valves			Equipment			Piping		Instruments																																					
Hand valves			Pumps / Compressors / Blowers			Piping symbols		Description																																					
Symbols	Code	Description	Symbols	Code	Description	Symbols	Code	Description																																					
	HV	General valve		P	Pump (General)		N/A	Offpage connector	Instruments will be tagged XXX - XX - XXX - XXX Main area code Letter code Switchboard Numeric sequence First letter XX Succeeding letter XX Numeric sequence																																				
	HV	Ball valve		P	Positive displacement pump		N/A	Flange connection																																					
	HV	Butterfly valve		P	Helical rotor pump		N/A	Blind flange																																					
	HV	Globe valve		P	Centrifugal pump		NO	Truck nozzle																																					
	HV	Three way valve		P	Peristaltic pump		NO	Funnel/Drain																																					
	HV	Ground covered valve		MC	Rotacut		AS	Expansion joint																																					
	BV	Balancing valve		MC	Shredder		SN	Strainer																																					
Actuated valves / Regulating valves			Heating and Cooling				N/A	Going into the ground / Coming up from	Instruments with succeeding letter T is an analog signal. Instruments with succeeding letter S is a digital signal. <table><tr><th>Instruments</th><th>Abbreviation</th></tr><tr><td>Analyze Indicator</td><td>AI</td></tr><tr><td>Analyse Transmitter</td><td>AT</td></tr><tr><td>Energi Transmitter</td><td>ET</td></tr><tr><td>Flow Indicator</td><td>FI</td></tr><tr><td>Flow Transmitter</td><td>FT</td></tr><tr><td>Flow Switch</td><td>FS</td></tr><tr><td>Flow Transmitter</td><td>FT</td></tr><tr><td>General Switch</td><td>GS</td></tr><tr><td>Level Switch</td><td>LS</td></tr><tr><td>Level Indicator</td><td>LI</td></tr><tr><td>Level Transmitter</td><td>LT</td></tr><tr><td>Pressure Indicator</td><td>PI</td></tr><tr><td>Pressure Switch</td><td>PS</td></tr><tr><td>Pressure Transmitter</td><td>PT</td></tr><tr><td>Thermometer</td><td>TI</td></tr><tr><td>Temperature Transmitter</td><td>TT</td></tr><tr><td>Weight Transmitter</td><td>WT</td></tr></table>	Instruments	Abbreviation	Analyze Indicator	AI	Analyse Transmitter	AT	Energi Transmitter	ET	Flow Indicator	FI	Flow Transmitter	FT	Flow Switch	FS	Flow Transmitter	FT	General Switch	GS	Level Switch	LS	Level Indicator	LI	Level Transmitter	LT	Pressure Indicator	PI	Pressure Switch	PS	Pressure Transmitter	PT	Thermometer	TI	Temperature Transmitter	TT	Weight Transmitter	WT
Instruments	Abbreviation	
Analyze Indicator	AI	
Analyse Transmitter	AT	
Energi Transmitter	ET	
Flow Indicator	FI	
Flow Transmitter	FT	
Flow Switch	FS	
Flow Transmitter	FT	
General Switch	GS	
Level Switch	LS	
Level Indicator	LI	
Level Transmitter	LT	
Pressure Indicator	PI	
Pressure Switch	PS	
Pressure Transmitter	PT	
Thermometer	TI	
Temperature Transmitter	TT	
Weight Transmitter	WT	
	MV/RV	Motor ball valve		HX	Heat exchanger - Shell & tube		AJ	Concentric reducer																																					
	MV/RV	Motor butterfly valve		HX	Heat exchanger - plate		AJ	Eccentric reducer																																					
	AV/RV	Pneumatic ball valve		HX	Heat exchanger - double pipe		AX	Sample point																																					
	AV/RV	Pneumatic valve		HX	Heating coil (in tank)		BS	Inline silencer																																					
	AV	Solenoid valve		HS	Heatpump		BU	Electrical heat tracing																																					
Safety valves			Tank equipment				N/A	Going though wall	<table><tr><th>Category</th><th>Numbers</th></tr><tr><td>Manual valves</td><td>001-099</td></tr><tr><td>Manual regulation valves</td><td>101-199</td></tr><tr><td>Pneumatic, electrical, solenoid</td><td>201-299</td></tr><tr><td>-</td><td>301-399</td></tr><tr><td>Check, Non-return valves</td><td>401-499</td></tr><tr><td>Drain, venting valves</td><td>501-599</td></tr><tr><td>Self-regulating valves (thermal/pressure)</td><td>601-699</td></tr><tr><td>Instrument valves</td><td>701-799</td></tr><tr><td>-</td><td>801-899</td></tr><tr><td>Safety valves</td><td>901-999</td></tr></table>	Category	Numbers	Manual valves	001-099	Manual regulation valves	101-199	Pneumatic, electrical, solenoid	201-299	-	301-399	Check, Non-return valves	401-499	Drain, venting valves	501-599	Self-regulating valves (thermal/pressure)	601-699	Instrument valves	701-799	-	801-899	Safety valves	901-999														
Category	Numbers	
Manual valves	001-099	
Manual regulation valves	101-199	
Pneumatic, electrical, solenoid	201-299	
-	301-399	
Check, Non-return valves	401-499	
Drain, venting valves	501-599	
Self-regulating valves (thermal/pressure)	601-699	
Instrument valves	701-799	
-	801-899	
Safety valves	901-999	
	SV	Exhaust valve covers		AG	ISO Agitator - Propeller		DT	Digester tank																																					
	SV	Safety valve		AG	Agitator		ST	Storage tank																																					
	SV	Breather valve		LA	Light		DT/ST	Storage tank with cover																																					
Mechanical valves			Filters and Vessels				HT	Gas/Hyginisation tank																																					
	PV	Pressure holding valve		AT	General filter / Forfilter		TA	Buried tank																																					
	CV	Check valve		AT	General liquid	Revision clouds																																							
	VV	Venting valve		AT	Drier - General	
Miscellaneous additional valve symbols				F	Suction hood	
		Operator lock mechanism		EXP	Expansion tank	

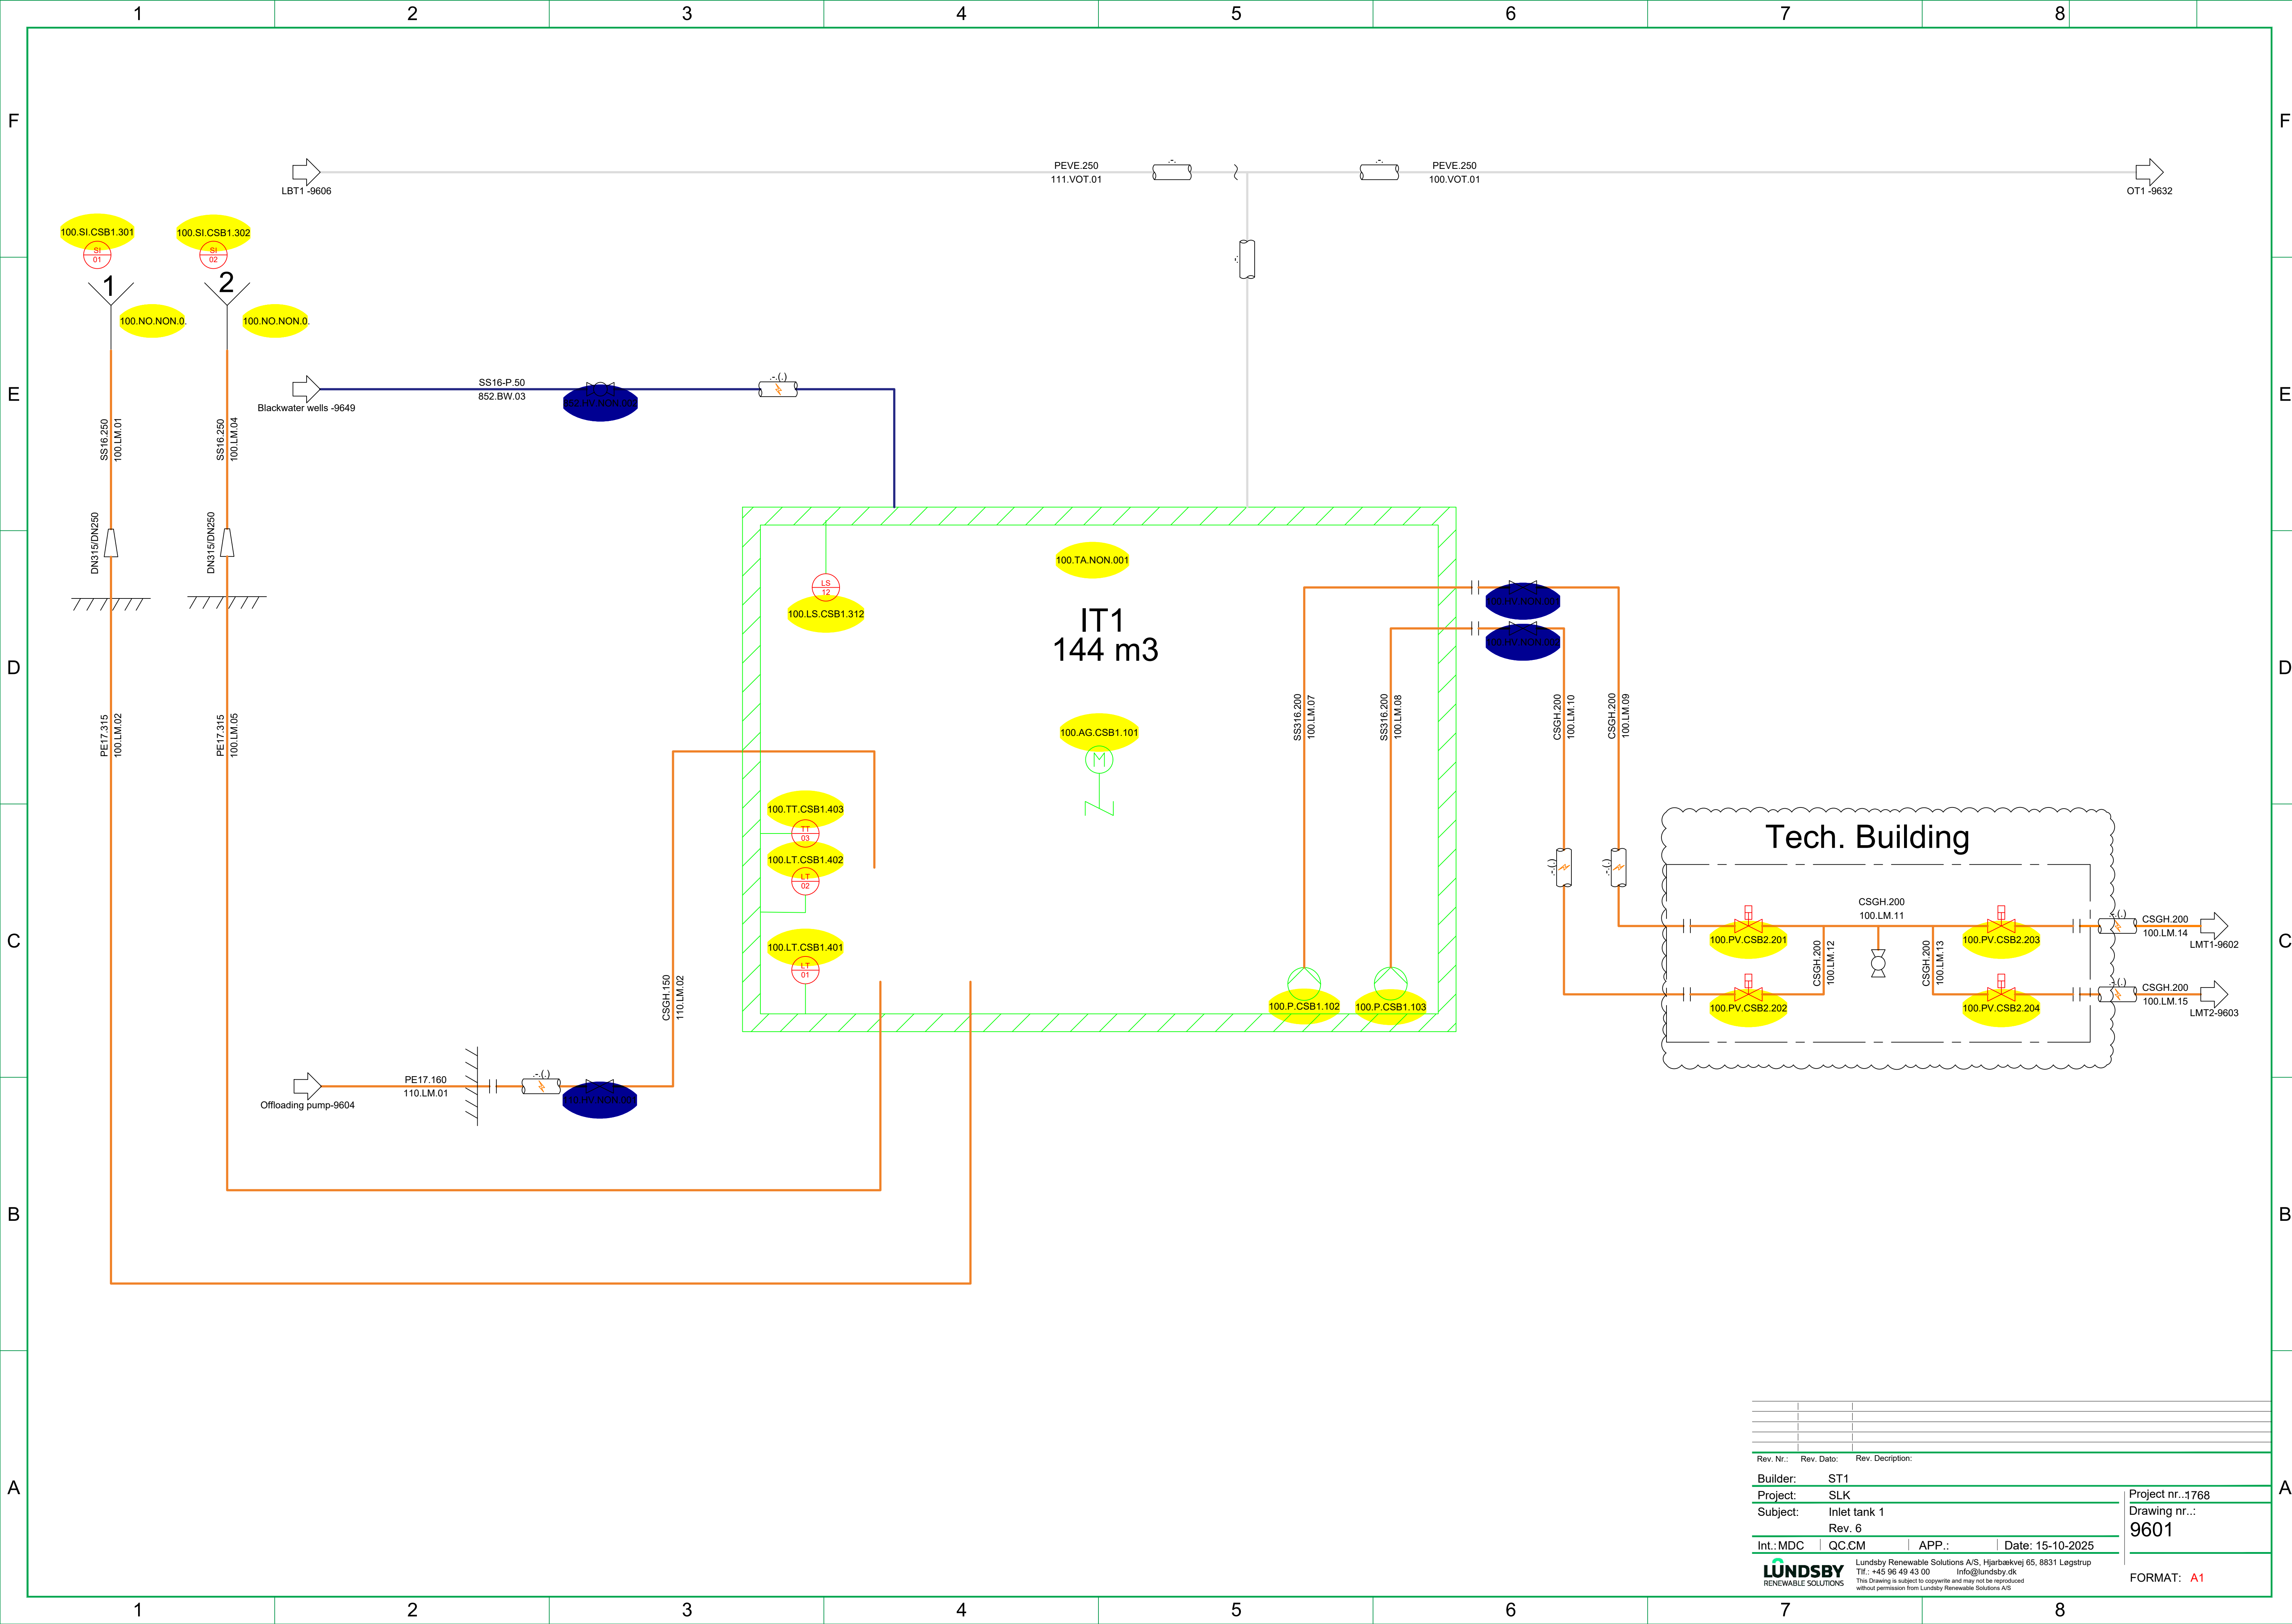


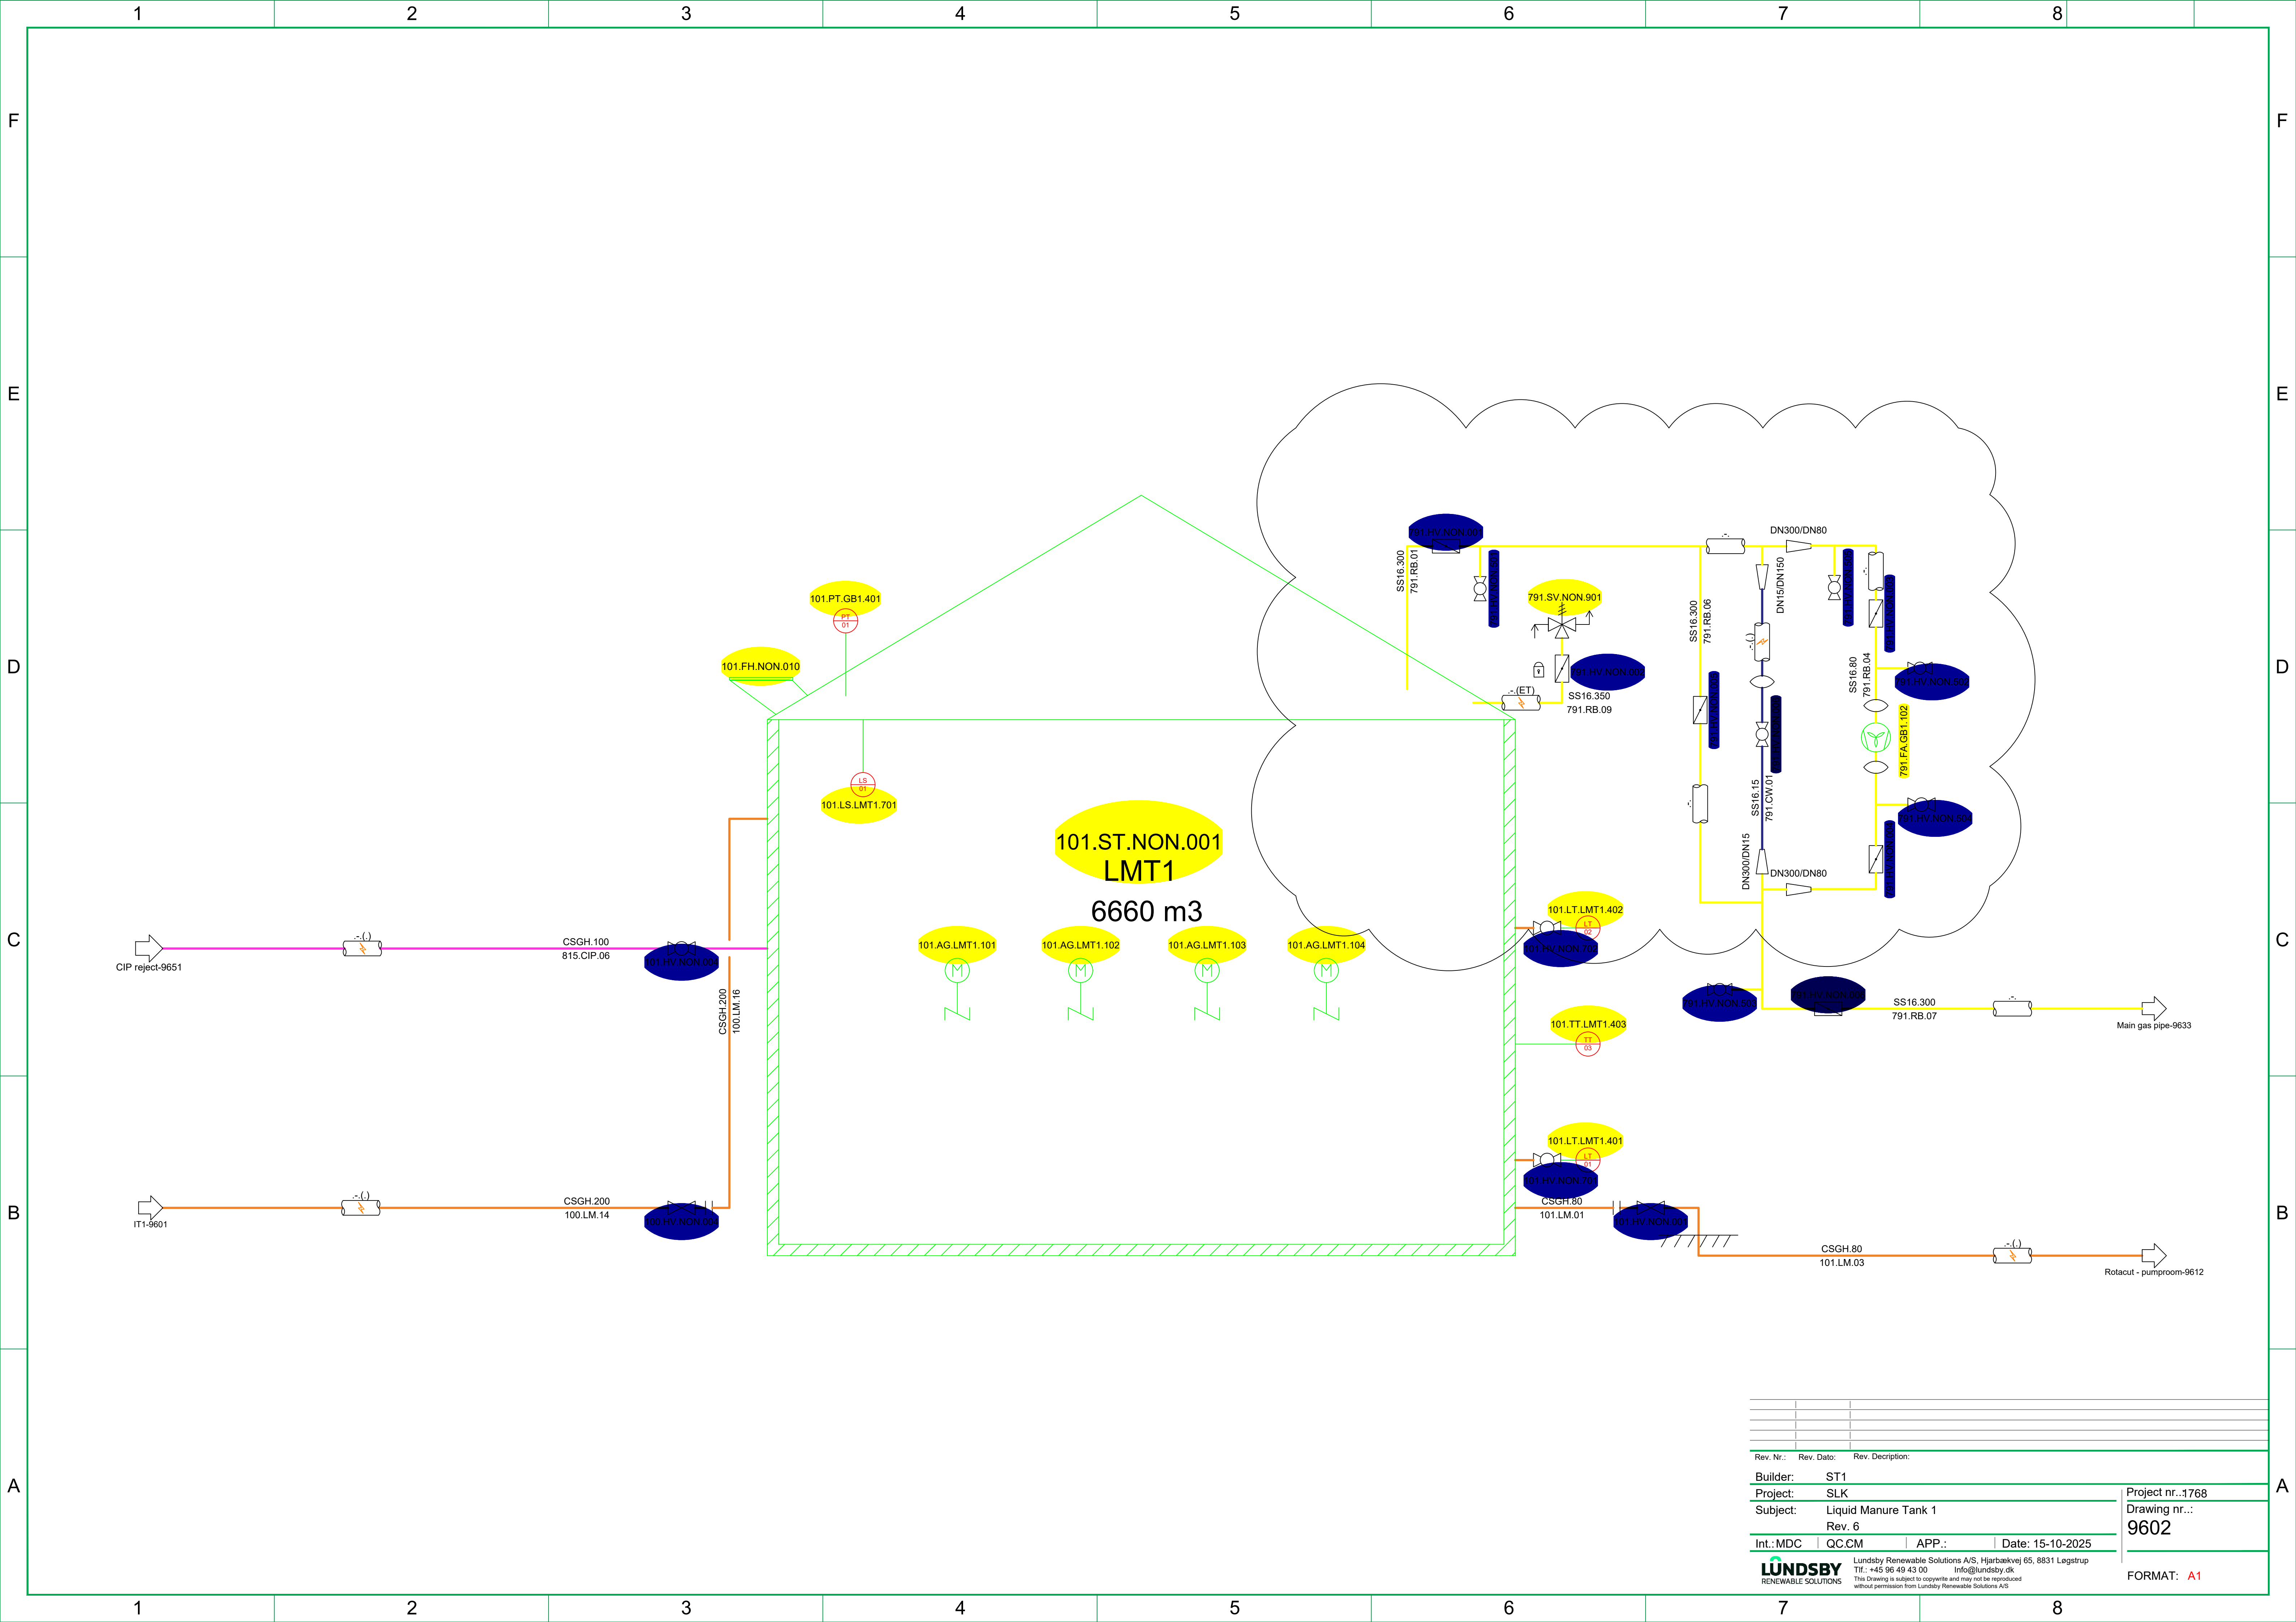

Rev. Nr.:	Rev. Dato:	Rev. Description:
Builder:	ST1	
Project:	SLK	
Subject:	Liquid Manure Tank 1	
Rev. 6		
Int.:MDC	QC:CM	APP.:
Date: 15-10-2025		
LUNDSBY RENEWABLE SOLUTIONS		
Lundsby Renewable Solutions A/S, Hjarbrækvej 65, 8831 Lægstrup Tlf.: +45 96 49 43 00 Info@lundsby.dk This Drawing is subject to copyright and may not be reproduced without permission from Lundsby Renewable Solutions A/S		
Project nr.:1768		Drawing nr.: 9602
FORMAT: A1		

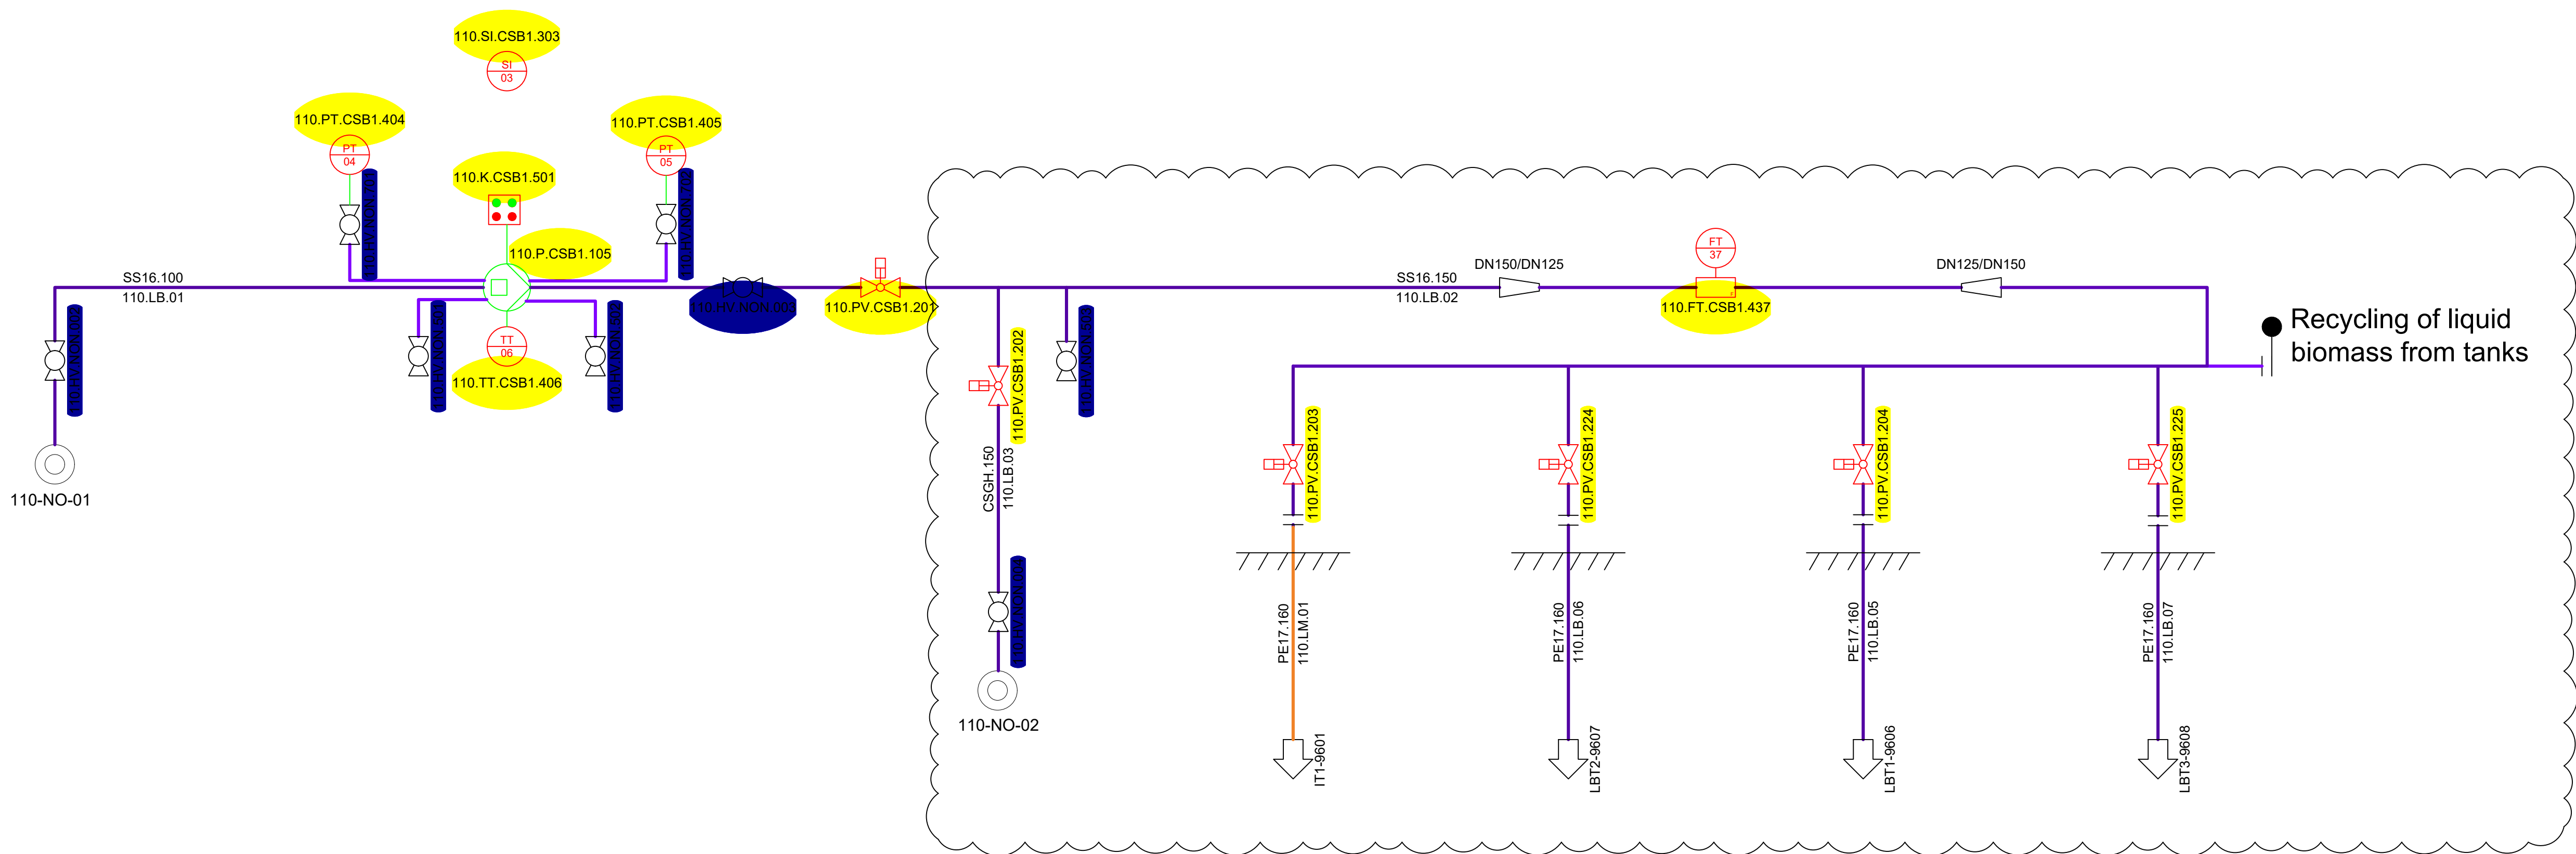

Rev. Nr.:	Rev. Dato:	Rev. Description:	
Builder:	ST1		
Project:	SLK		
Subject:	Liquid biomass delivery pump		
Rev. 6			
Int.:MDC	QC.CM	APP.:	Date: 15-10-2025
LUNDSBY RENEWABLE SOLUTIONS			Lundsby Renewable Solutions A/S, Hjarbækvej 65, 8831 Løgstrup Tlf.: +45 96 49 43 00 Info@lundsby.dk This Drawing is subject to copyright and may not be reproduced without permission from Lundsby Renewable Solutions A/S
Project nr.:1768 Drawing nr.: 9604			FORMAT: A1

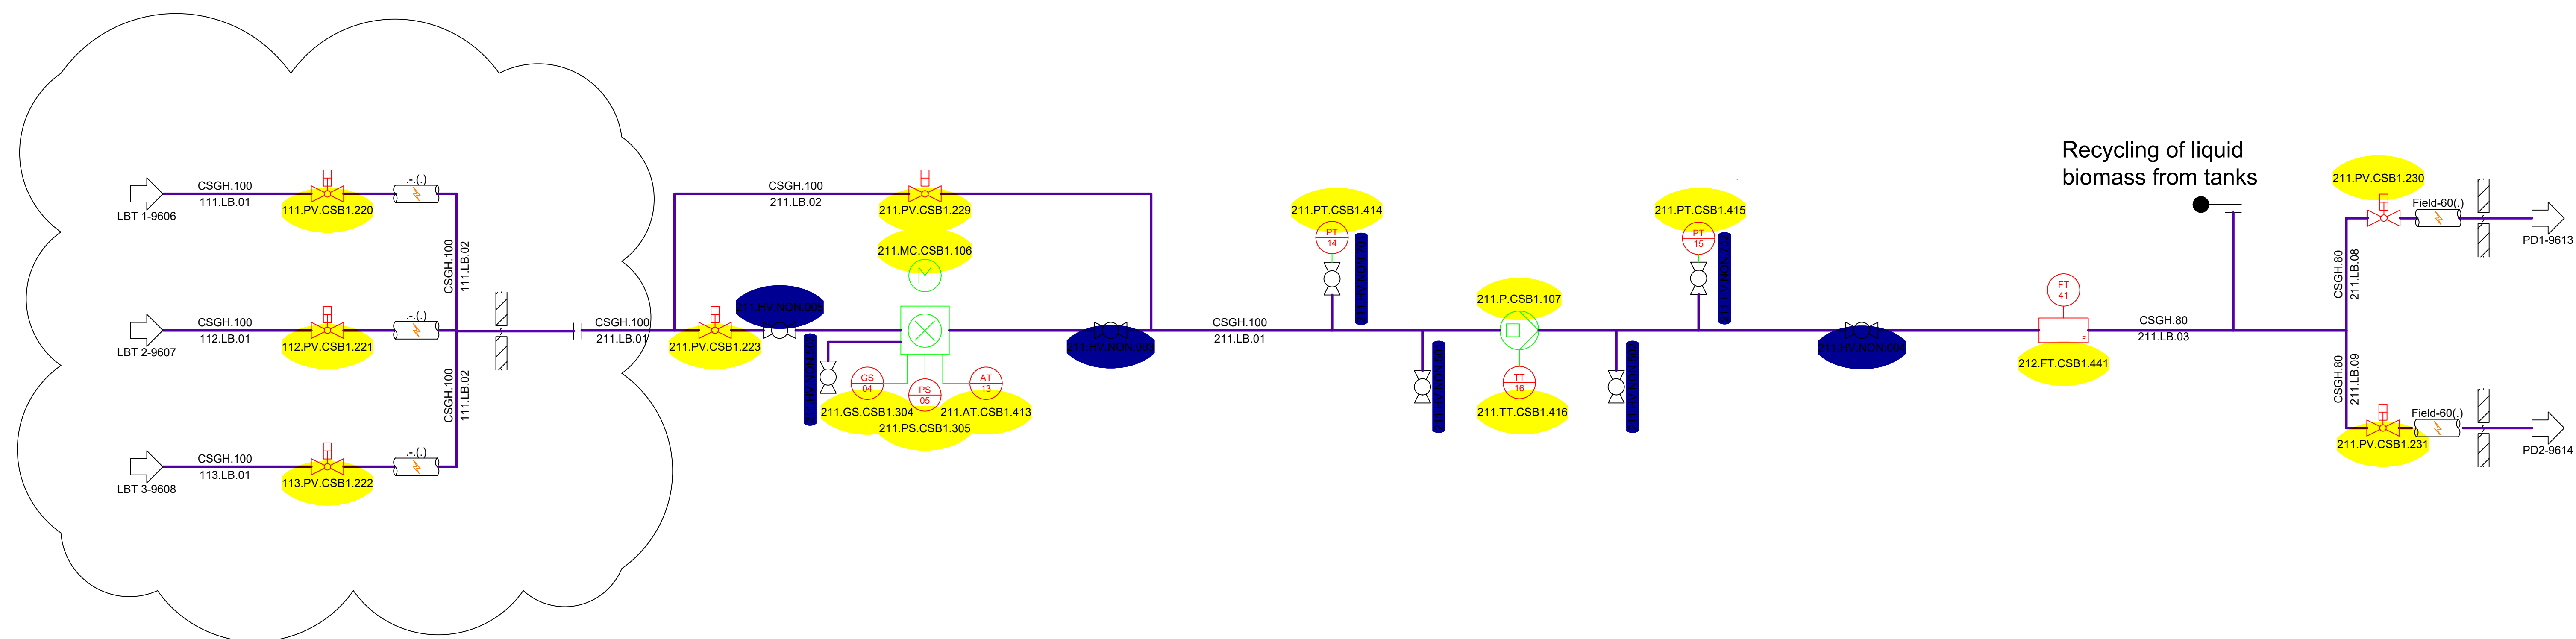

Rev. Nr.:	Rev. Dato:	Rev. Description:
-----------	------------	-------------------

Builder:	ST1
Project:	SLK
Subject:	Liquid biomass pump 1
	Rev. 6

Int.: MDC	QC.CM	APP.:	Date: 15-10-2025
-----------	-------	-------	------------------




Lundsby Renewable Solutions A/S, Hjarbakvej 65, 8831 Lægstrup
Tlf.: +45 96 49 43 00 Info@lundsby.dk
This Drawing is subject to copyright and may not be reproduced
without express written consent from LundSBY Renewable Solutions A/S.


Project nr...1768

Drawing nr.:
9605


FORMAT: **A1**

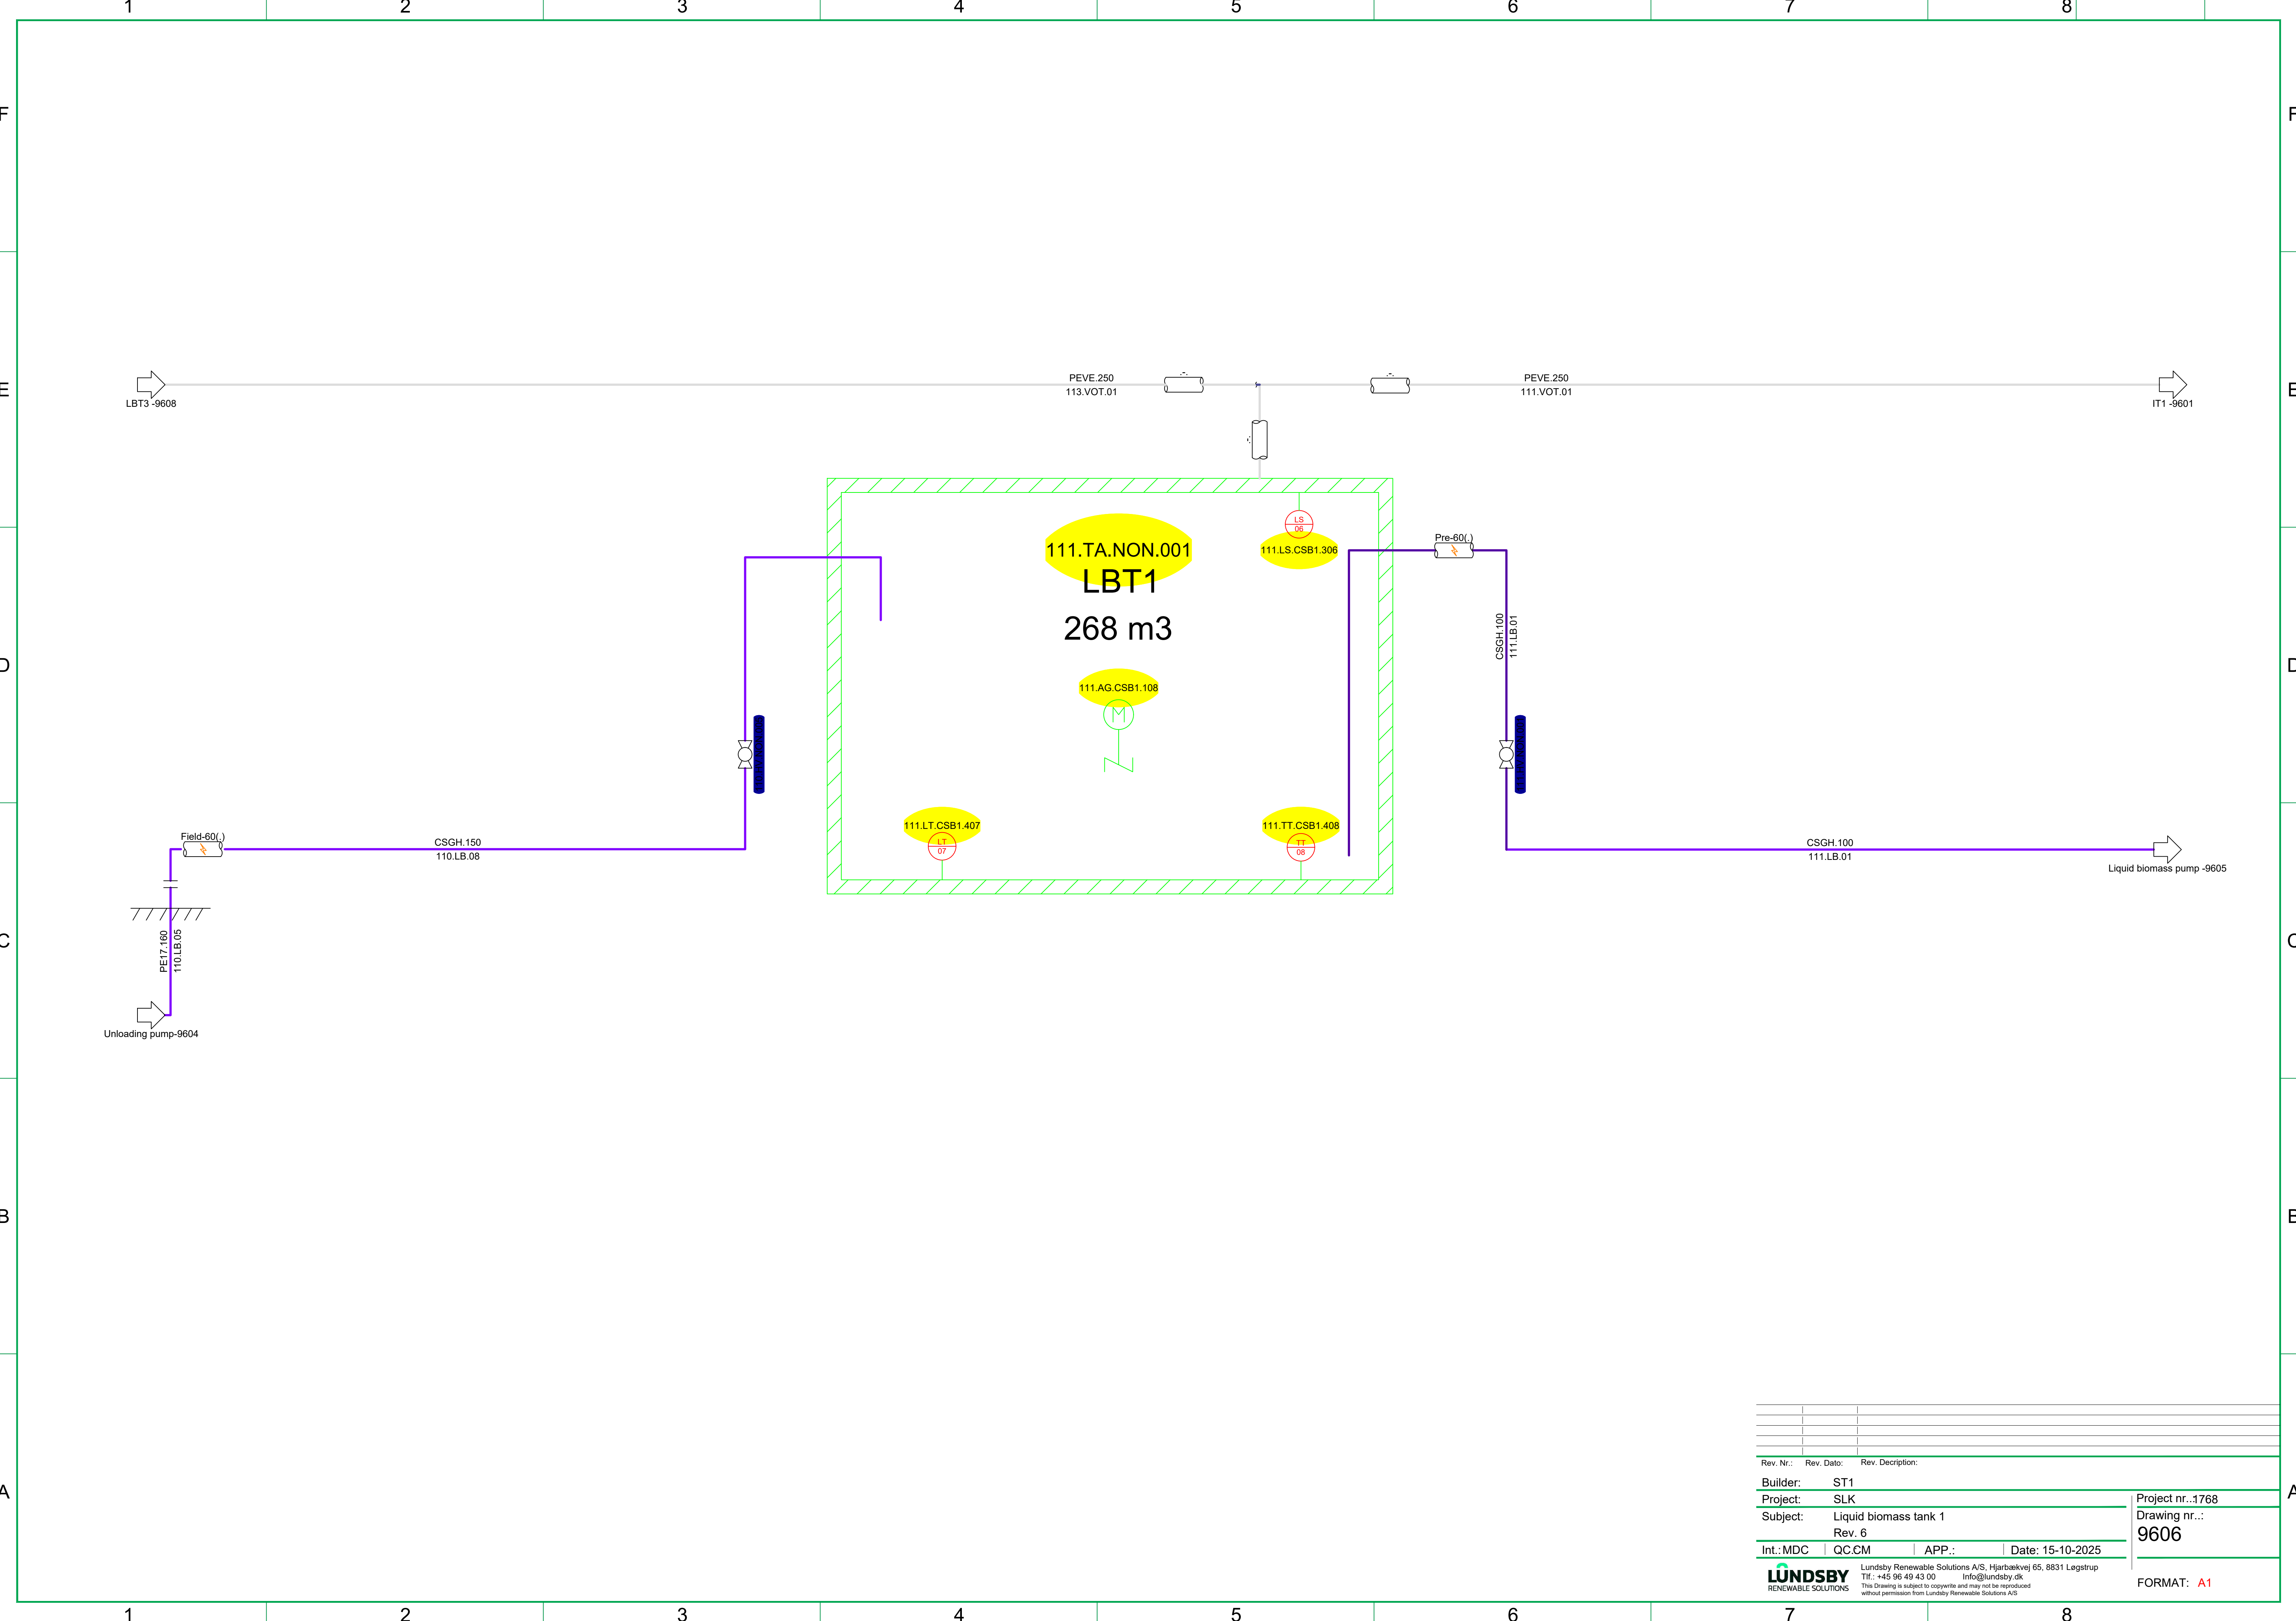


Rev. Nr.:	Rev. Dato:	Rev. Description:	
Builder:	ST1		
Project:	SLK		
Subject:	Liquid biomass tank 1		
	Rev. 6		
Int.:MDC	QC.CM	APP.:	Date: 15-10-2025
LUNDSBY RENEWABLE SOLUTIONS			Lundsby Renewable Solutions A/S, Hjarbækvej 65, 8831 Løgstrup Tlf.: +45 96 49 43 00 Info@lundsby.dk This Drawing is subject to copyright and may not be reproduced without permission from Lundsby Renewable Solutions A/S
			Project nr...1768 Drawing nr...: 9606
			FORMAT: A1

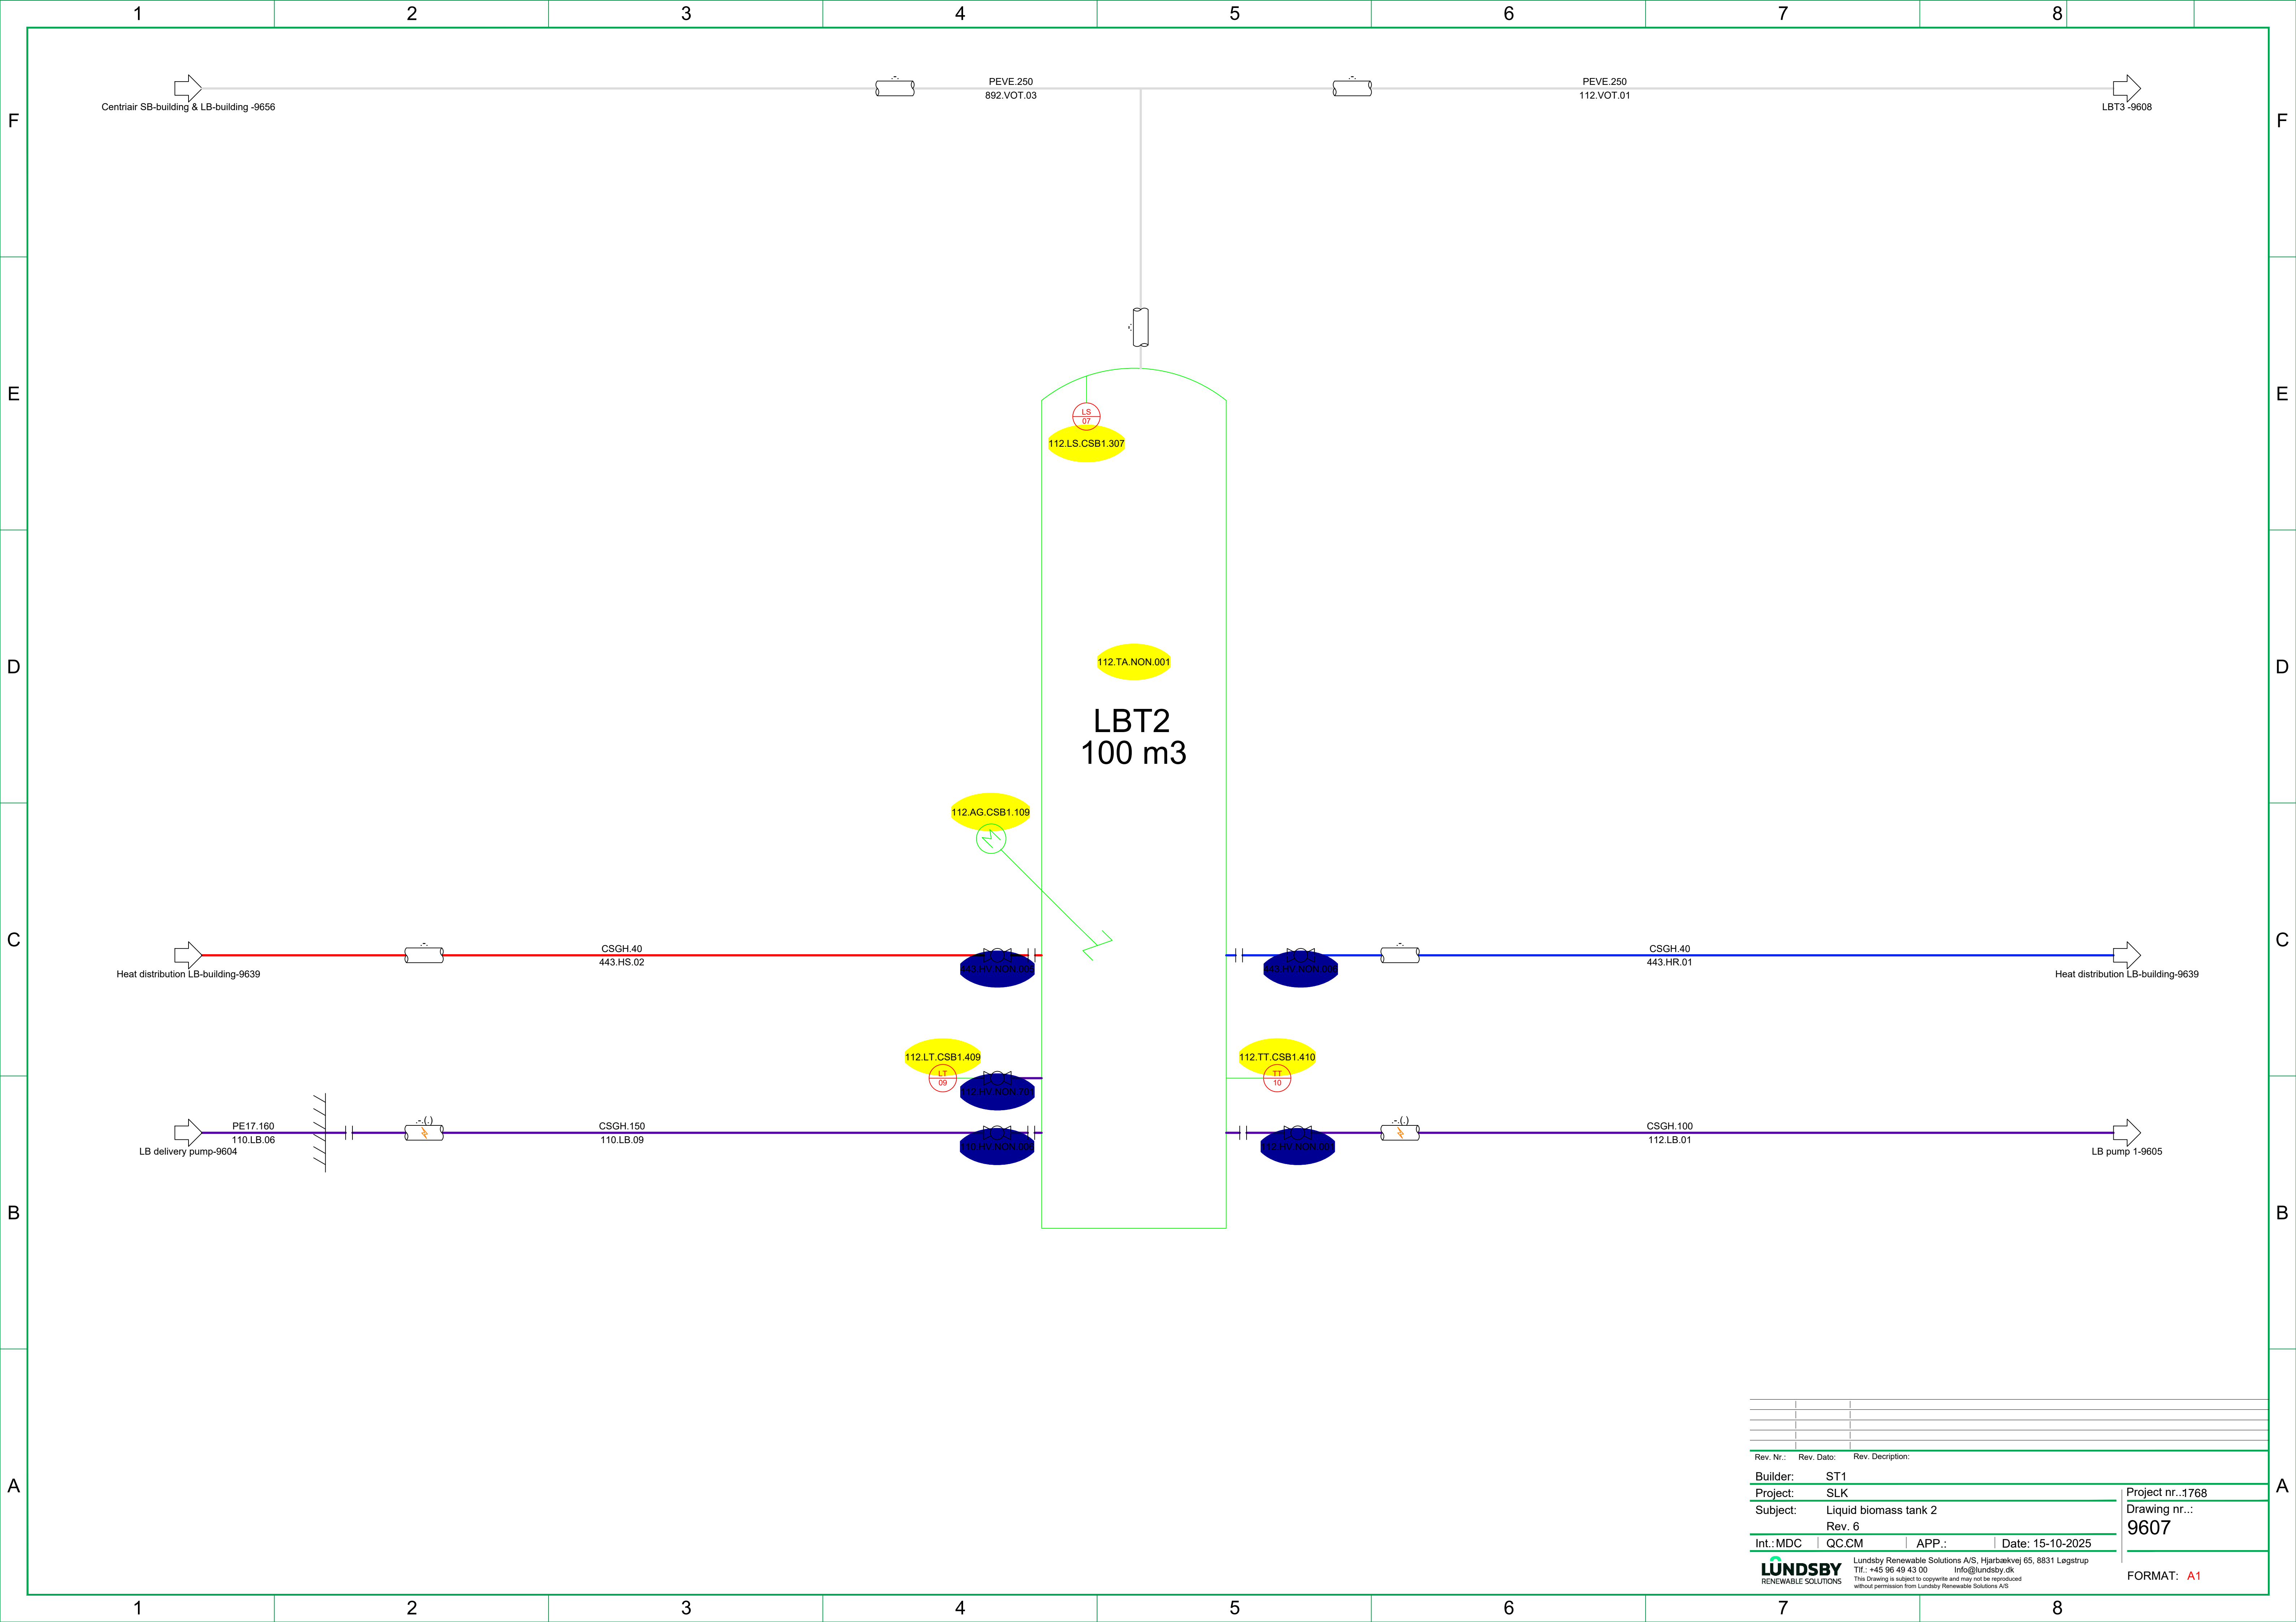


Rev. Nr.:	Rev. Dato:	Rev. Description:	
Builder:	ST1		
Project:	SLK		
Subject:	Liquid biomass tank 2		
	Rev. 6		
Int.:MDC	QC:CM	APP.:	Date: 15-10-2025
LUNDSBY RENEWABLE SOLUTIONS			Lundsby Renewable Solutions A/S, Hjarbækvej 65, 8831 Løgstrup Tlf.: +45 96 49 43 00 Info@lundsby.dk This Drawing is subject to copyright and may not be reproduced without permission from Lundsby Renewable Solutions A/S
			Project nr...1768 Drawing nr...: 9607 FORMAT: A1

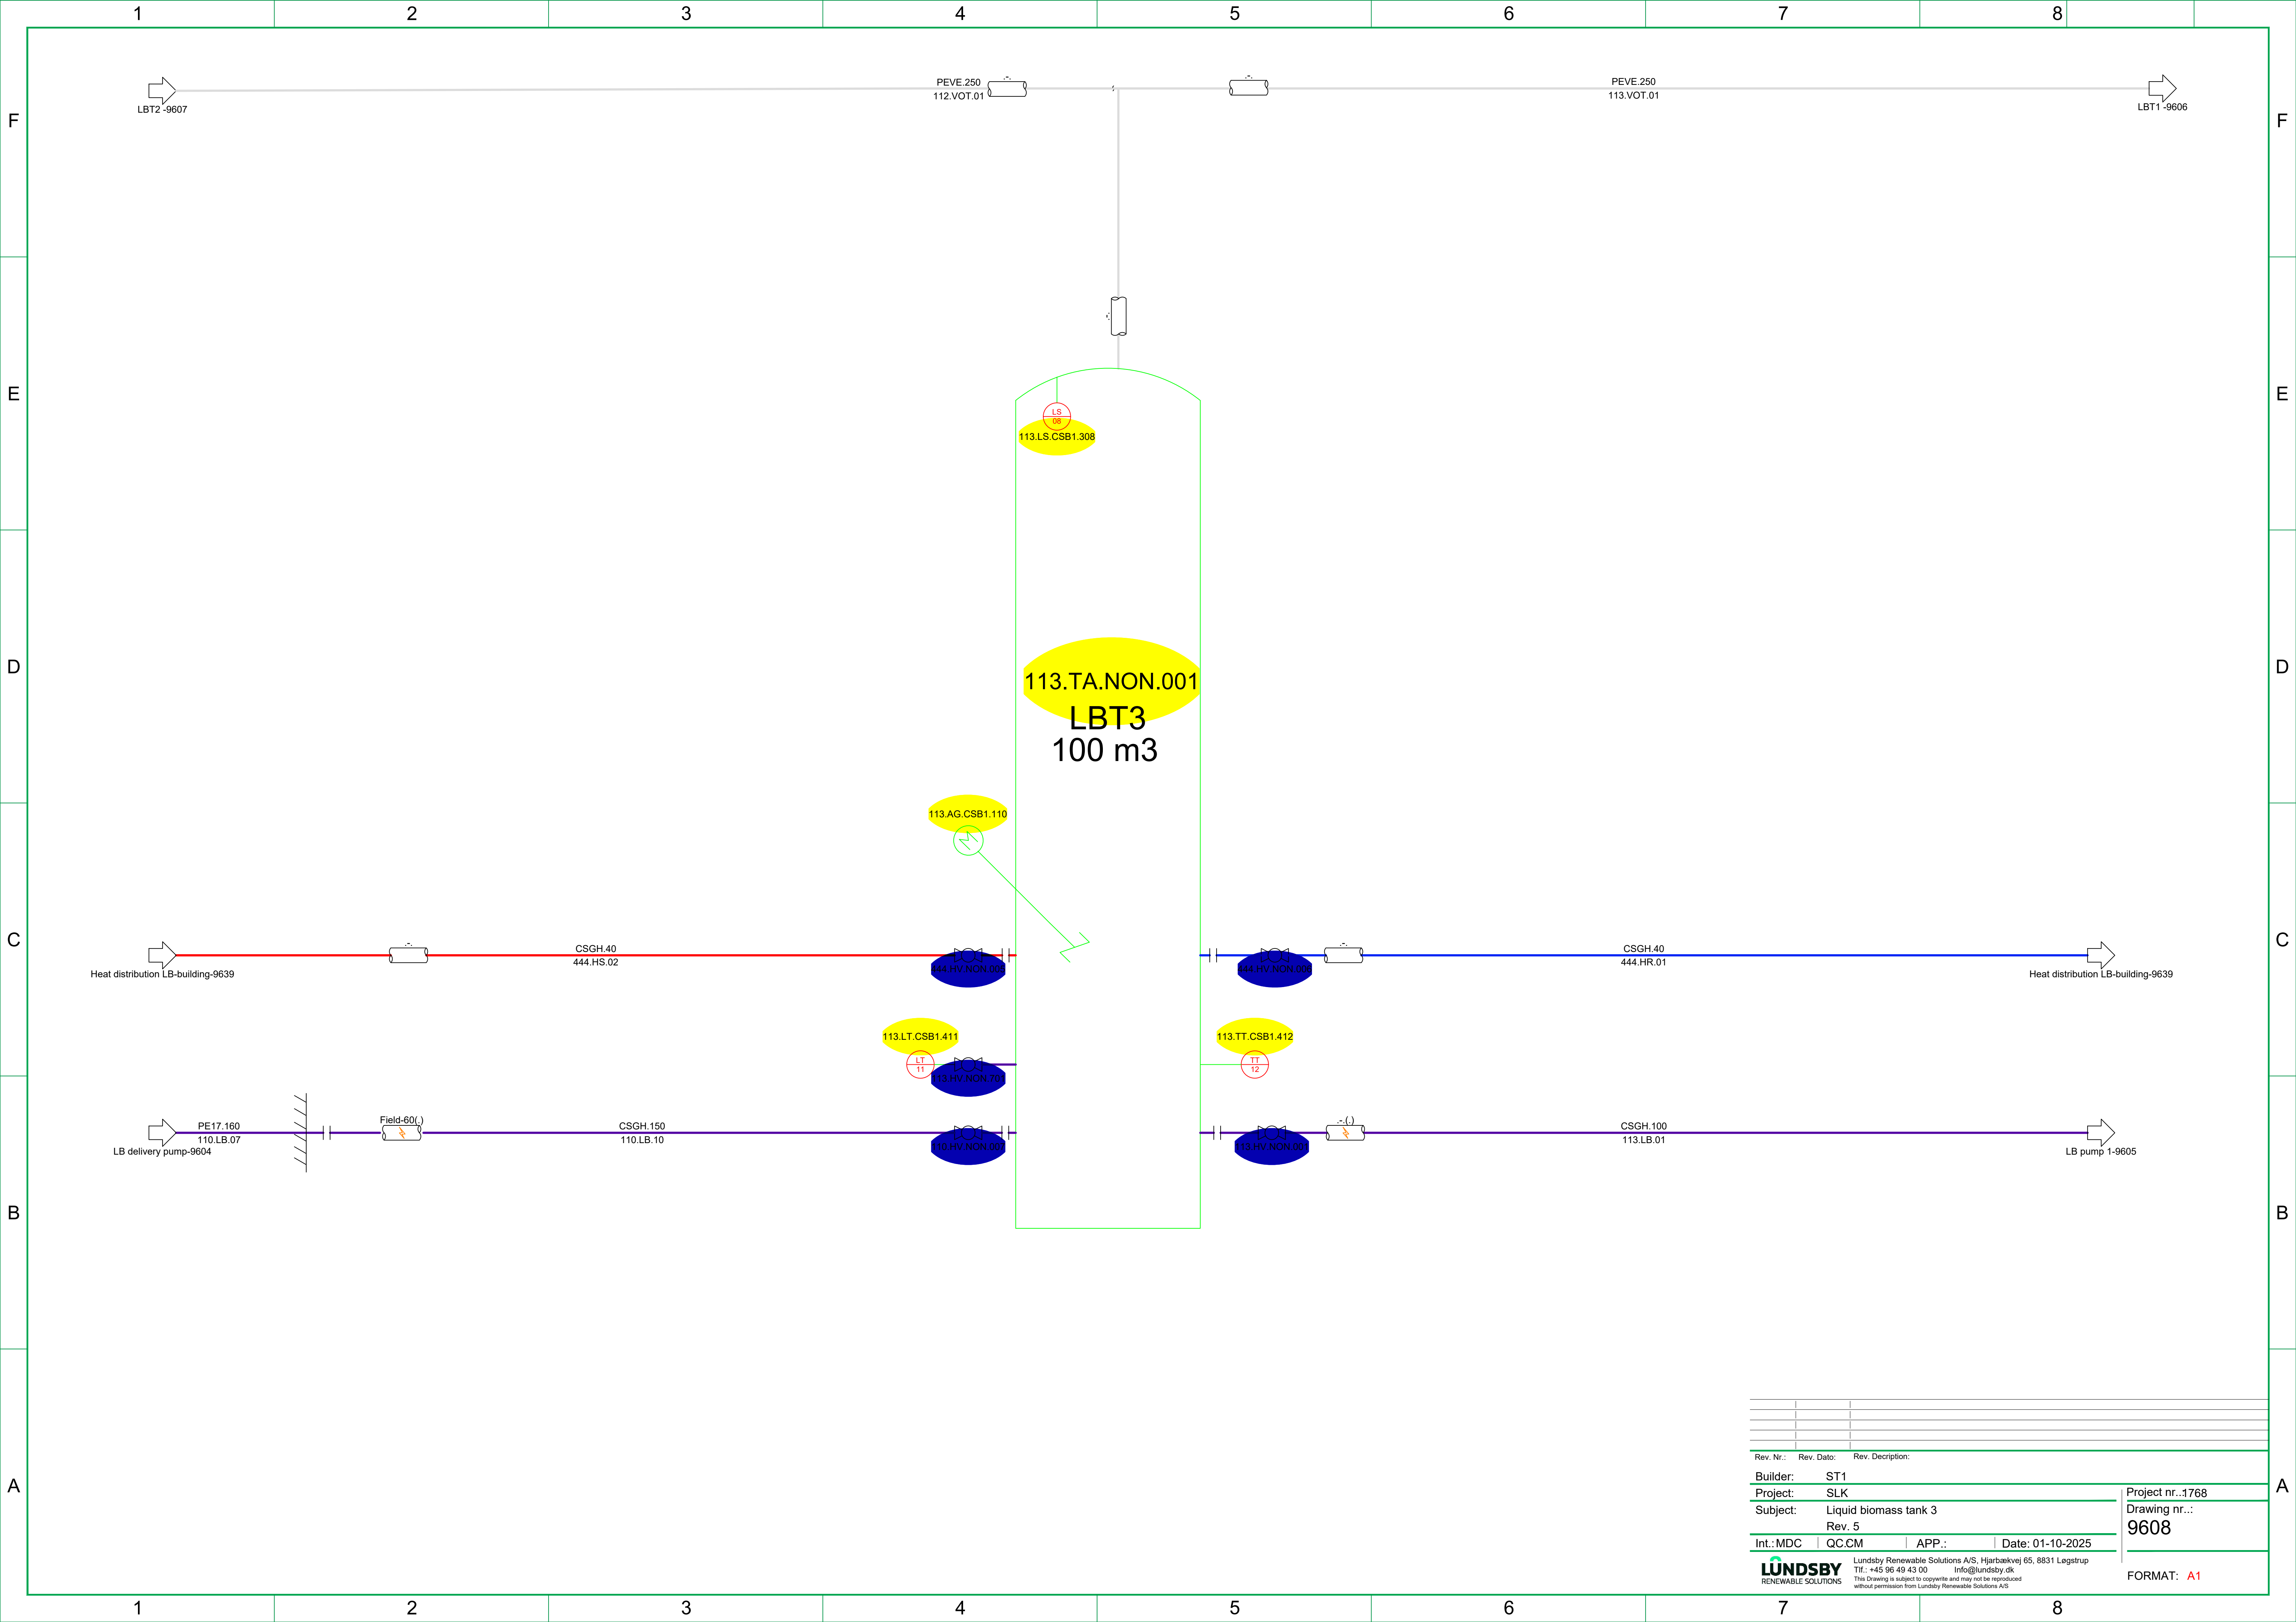

Rev. Nr.:	Rev. Dato:	Rev. Description:	Project nr.:1768
Builder:	ST1		Drawing nr.: 9608
Project:	SLK		
Subject:	Liquid biomass tank 3		
	Rev. 5		
Int.:MDC	QC:CM	APP.:	Date: 01-10-2025
LUNDSBY RENEWABLE SOLUTIONS		Lundsby Renewable Solutions A/S, Hjarbækvej 65, 8831 Løgstrup Tlf.: +45 96 49 43 00 Info@lundsby.dk This Drawing is subject to copyright and may not be reproduced without permission from Lundsby Renewable Solutions A/S	
		FORMAT: A1	

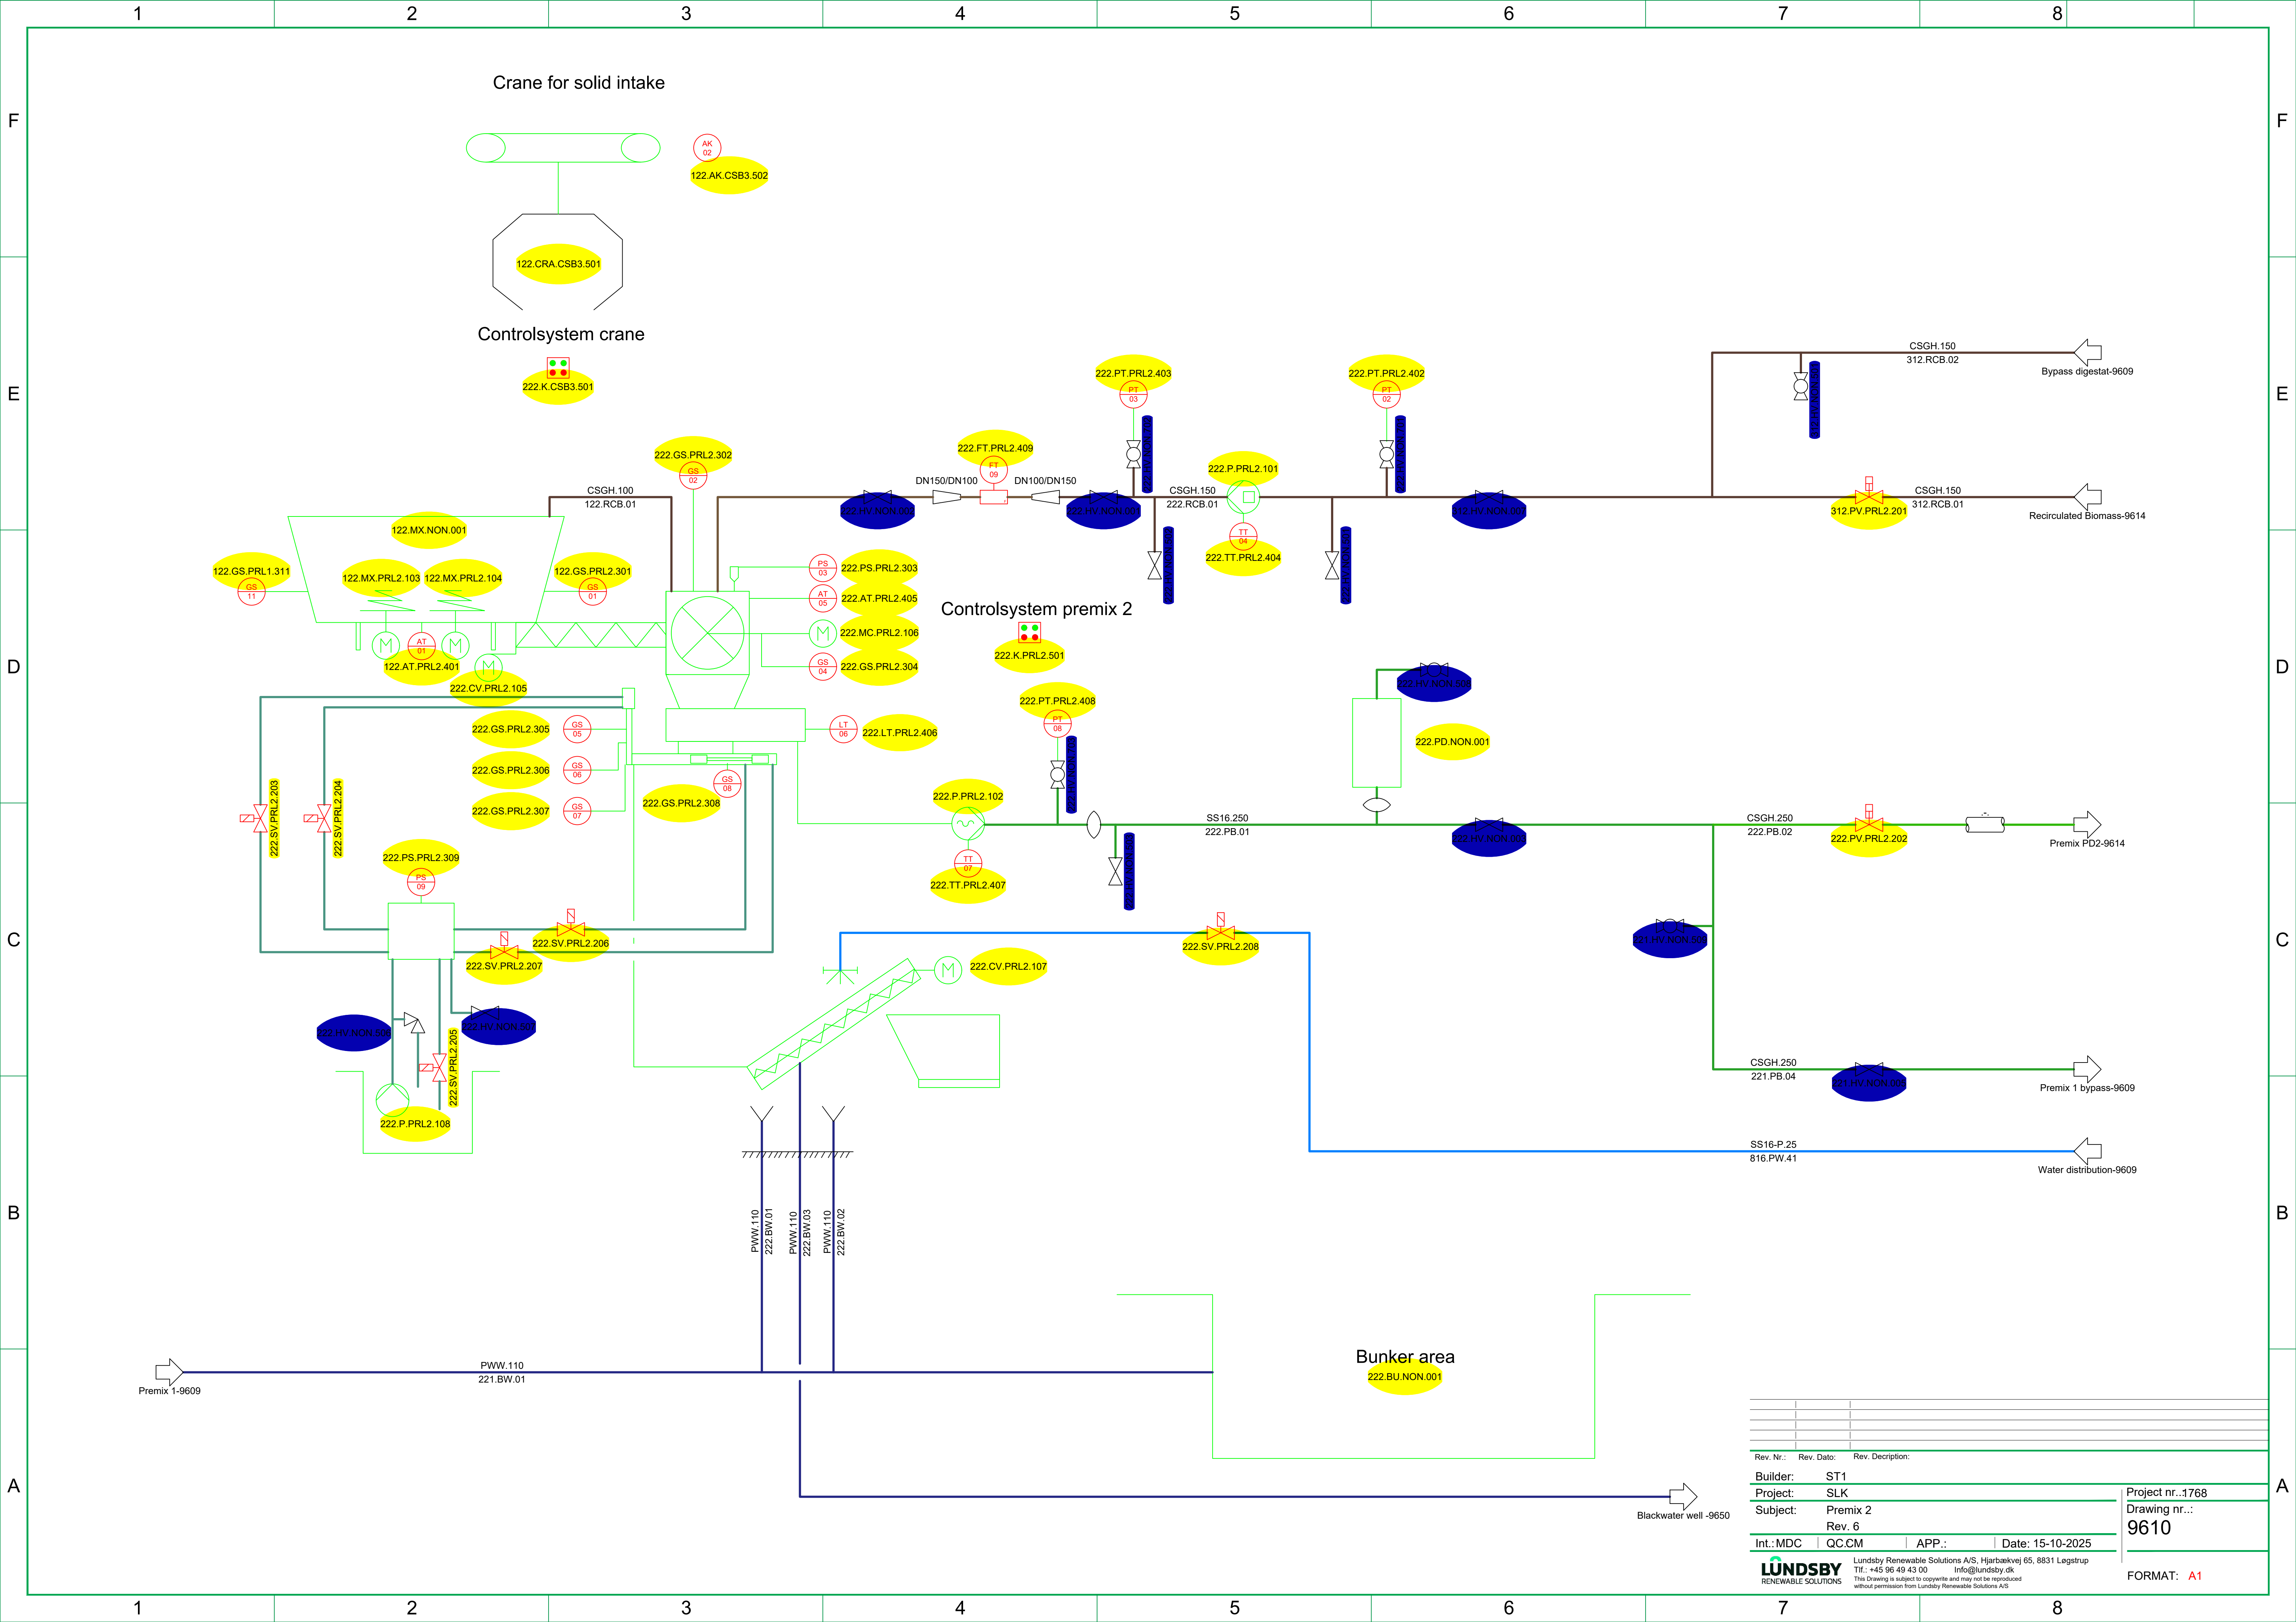


Rev. Nr.:	Rev. Dato:	Rev. Description:
Builder:	ST1	
Project:	SLK	
Subject:	Premix 2	
	Rev. 6	
Int.:MDC	QC:CM	APP.:
		Date: 15-10-2025
LUNDSBY RENEWABLE SOLUTIONS		
Lundsby Renewable Solutions A/S, Hjarbækvej 65, 8831 Løgstrup Tlf.: +45 96 49 43 00 Info@lundsby.dk This Drawing is subject to copyright and may not be reproduced without permission from Lundsby Renewable Solutions A/S		
Project nr.:1768 Drawing nr.: 9610		FORMAT: A1

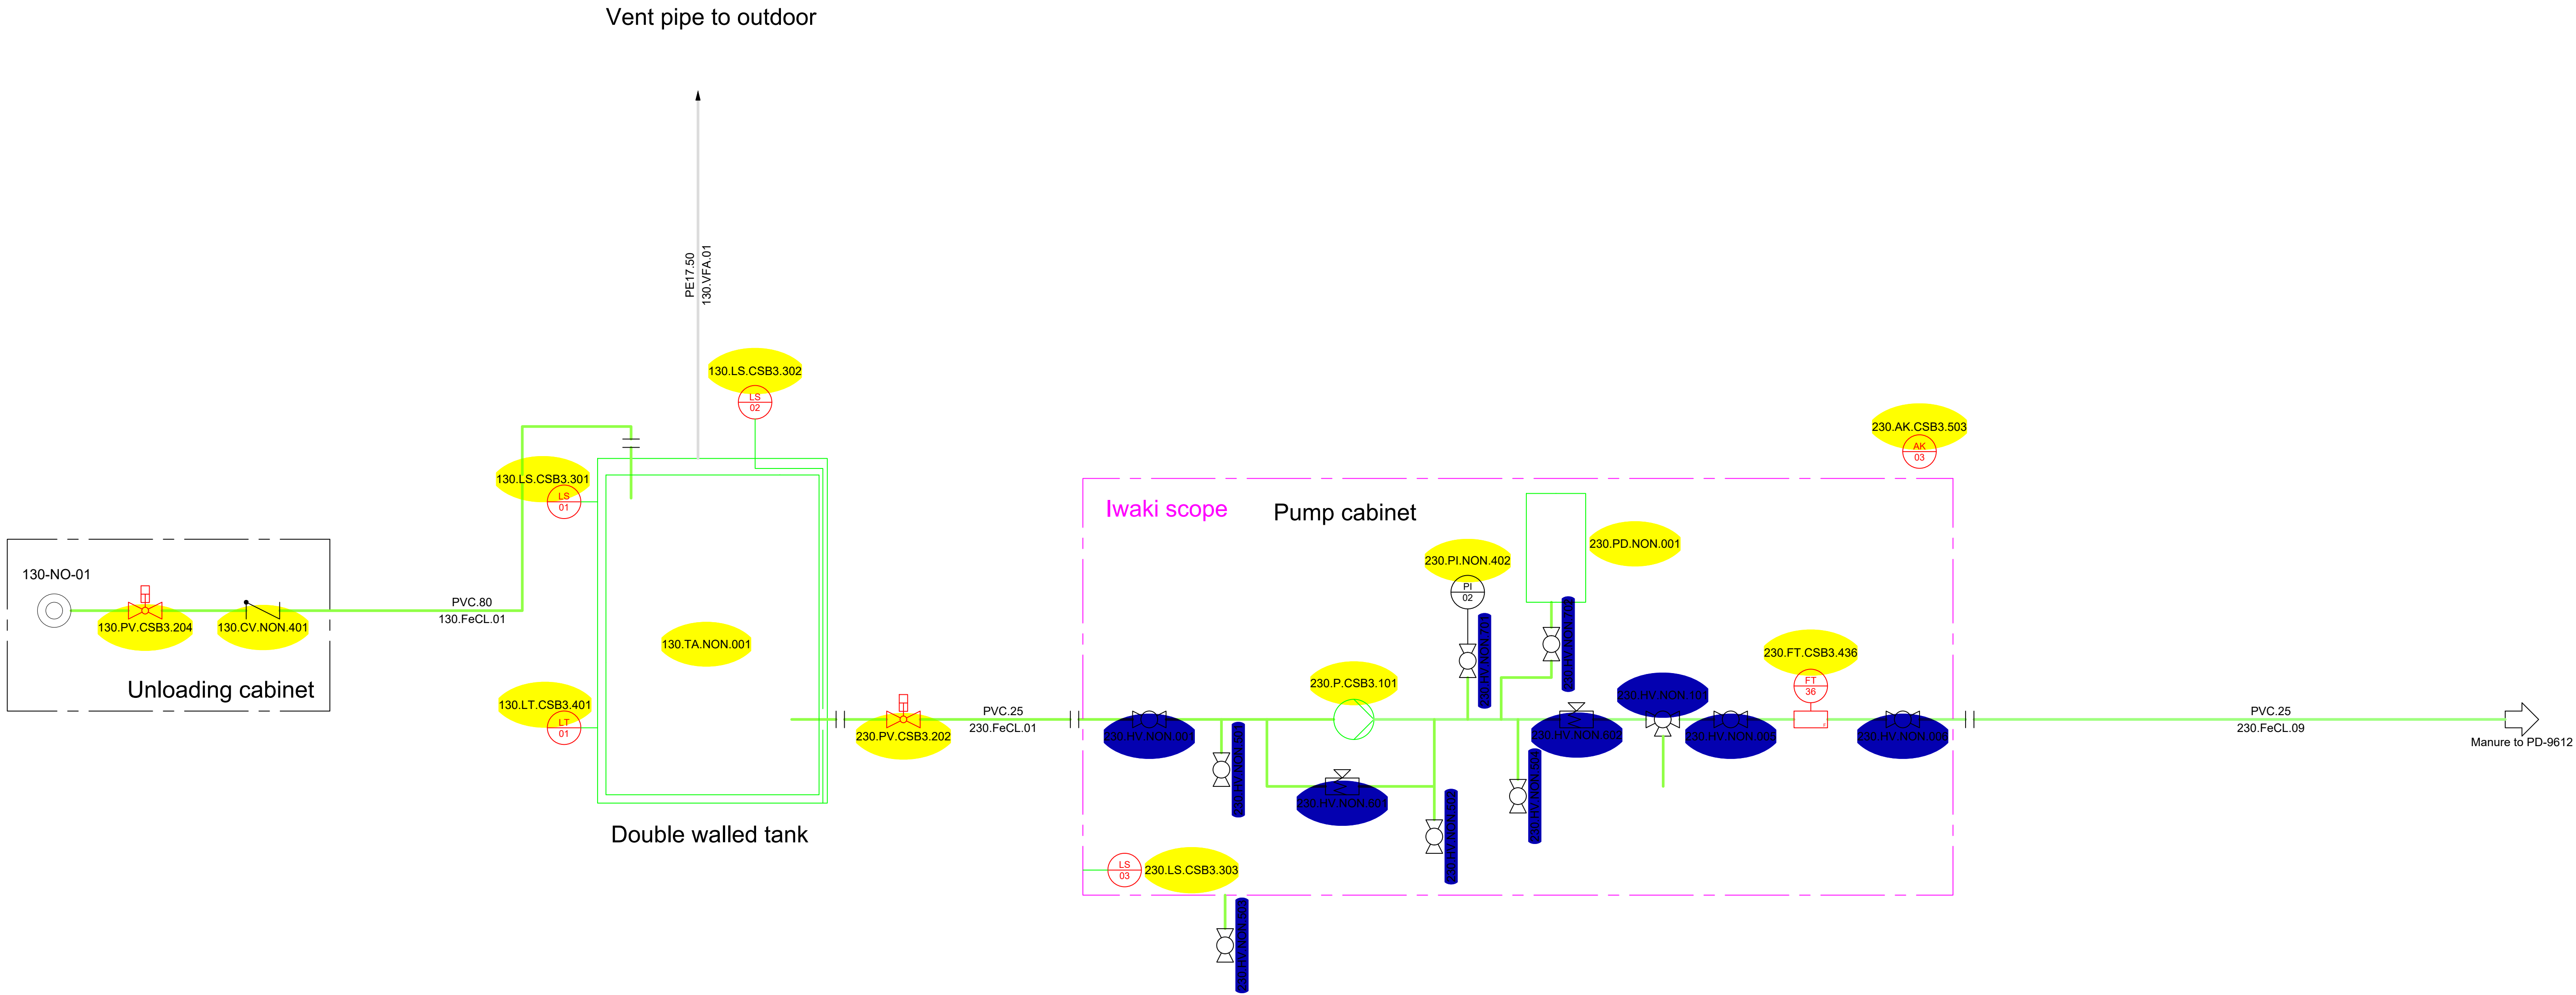


Rev. Nr.: Rev. Dato: Rev. Description:					
Builder:		ST1			
Project:		SLK			
Subject:		FECL system			
		Rev. 6			
Int.: MDC		QC.CM	APP.:	Date: 15-10-2025	
 LUNDSBY RENEWABLE SOLUTIONS Lundsby Renewable Solutions A/S, Hjarbækvej 65, 8831 Løgstrup Tlf.: +45 96 49 43 00 Info@lundsby.dk This Drawing is subject to copyright and may not be reproduced without permission from Lundsby Renewable Solutions A/S					
				Project nr.:1768	
				Drawing nr...:	
				9611	
				FORMAT: A1	

Pumphouse 2

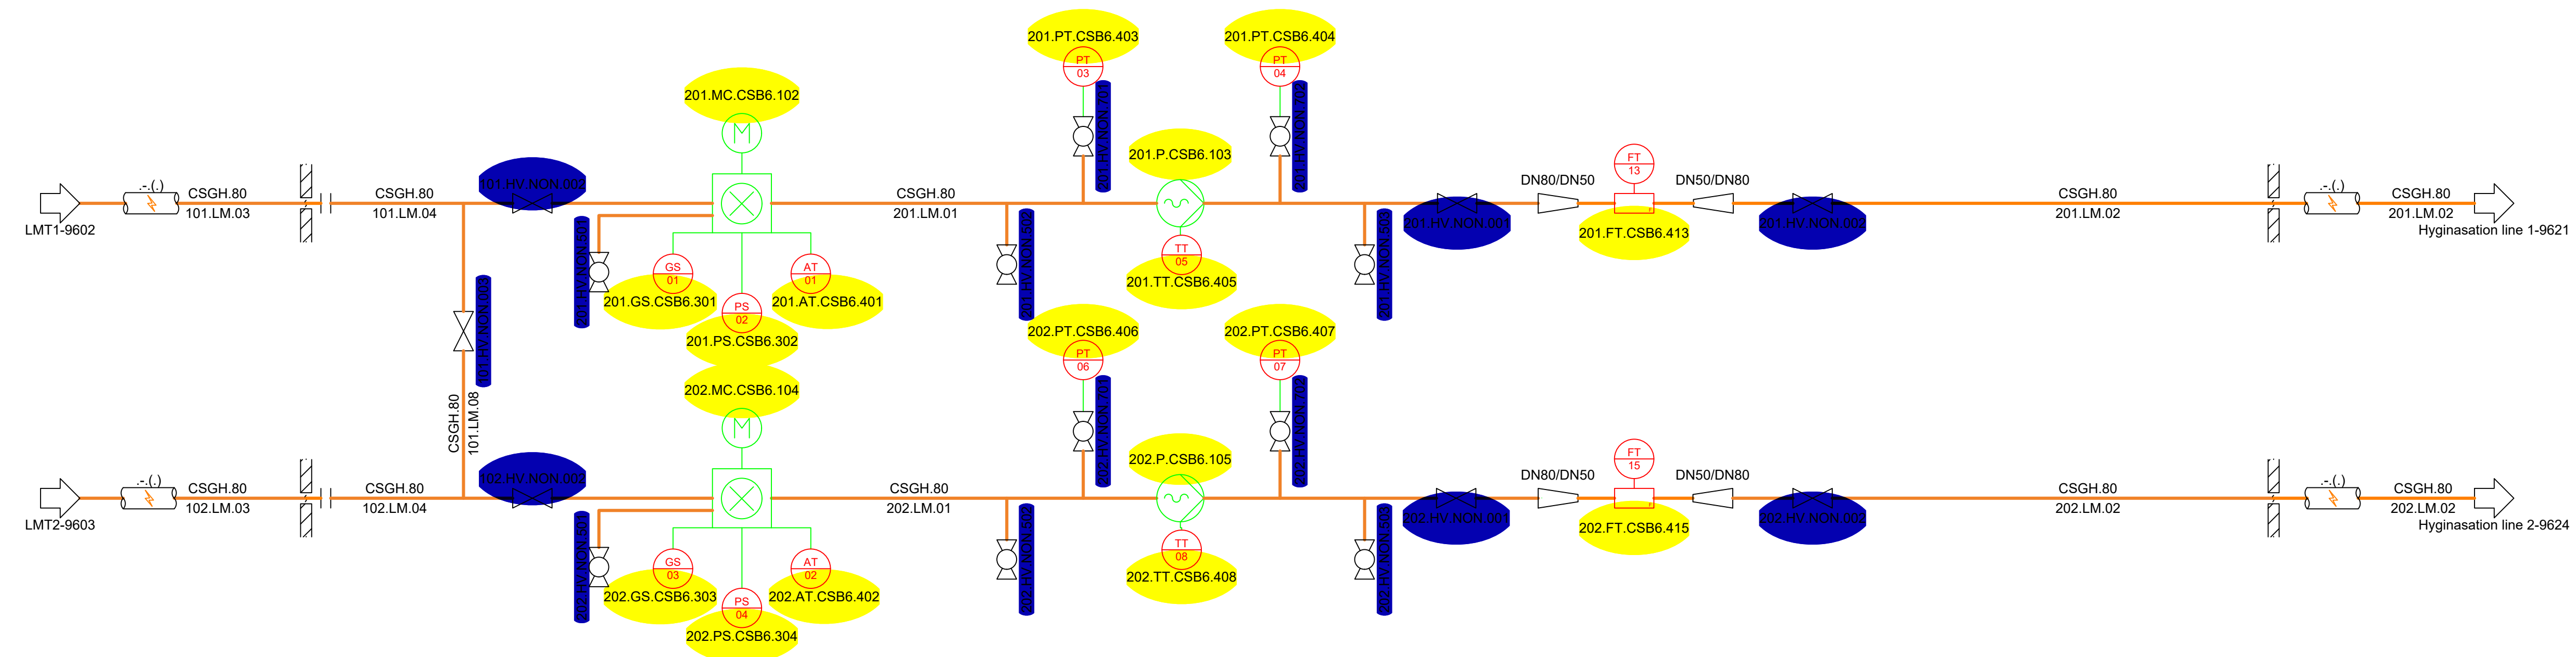


Tech
building


SB-building

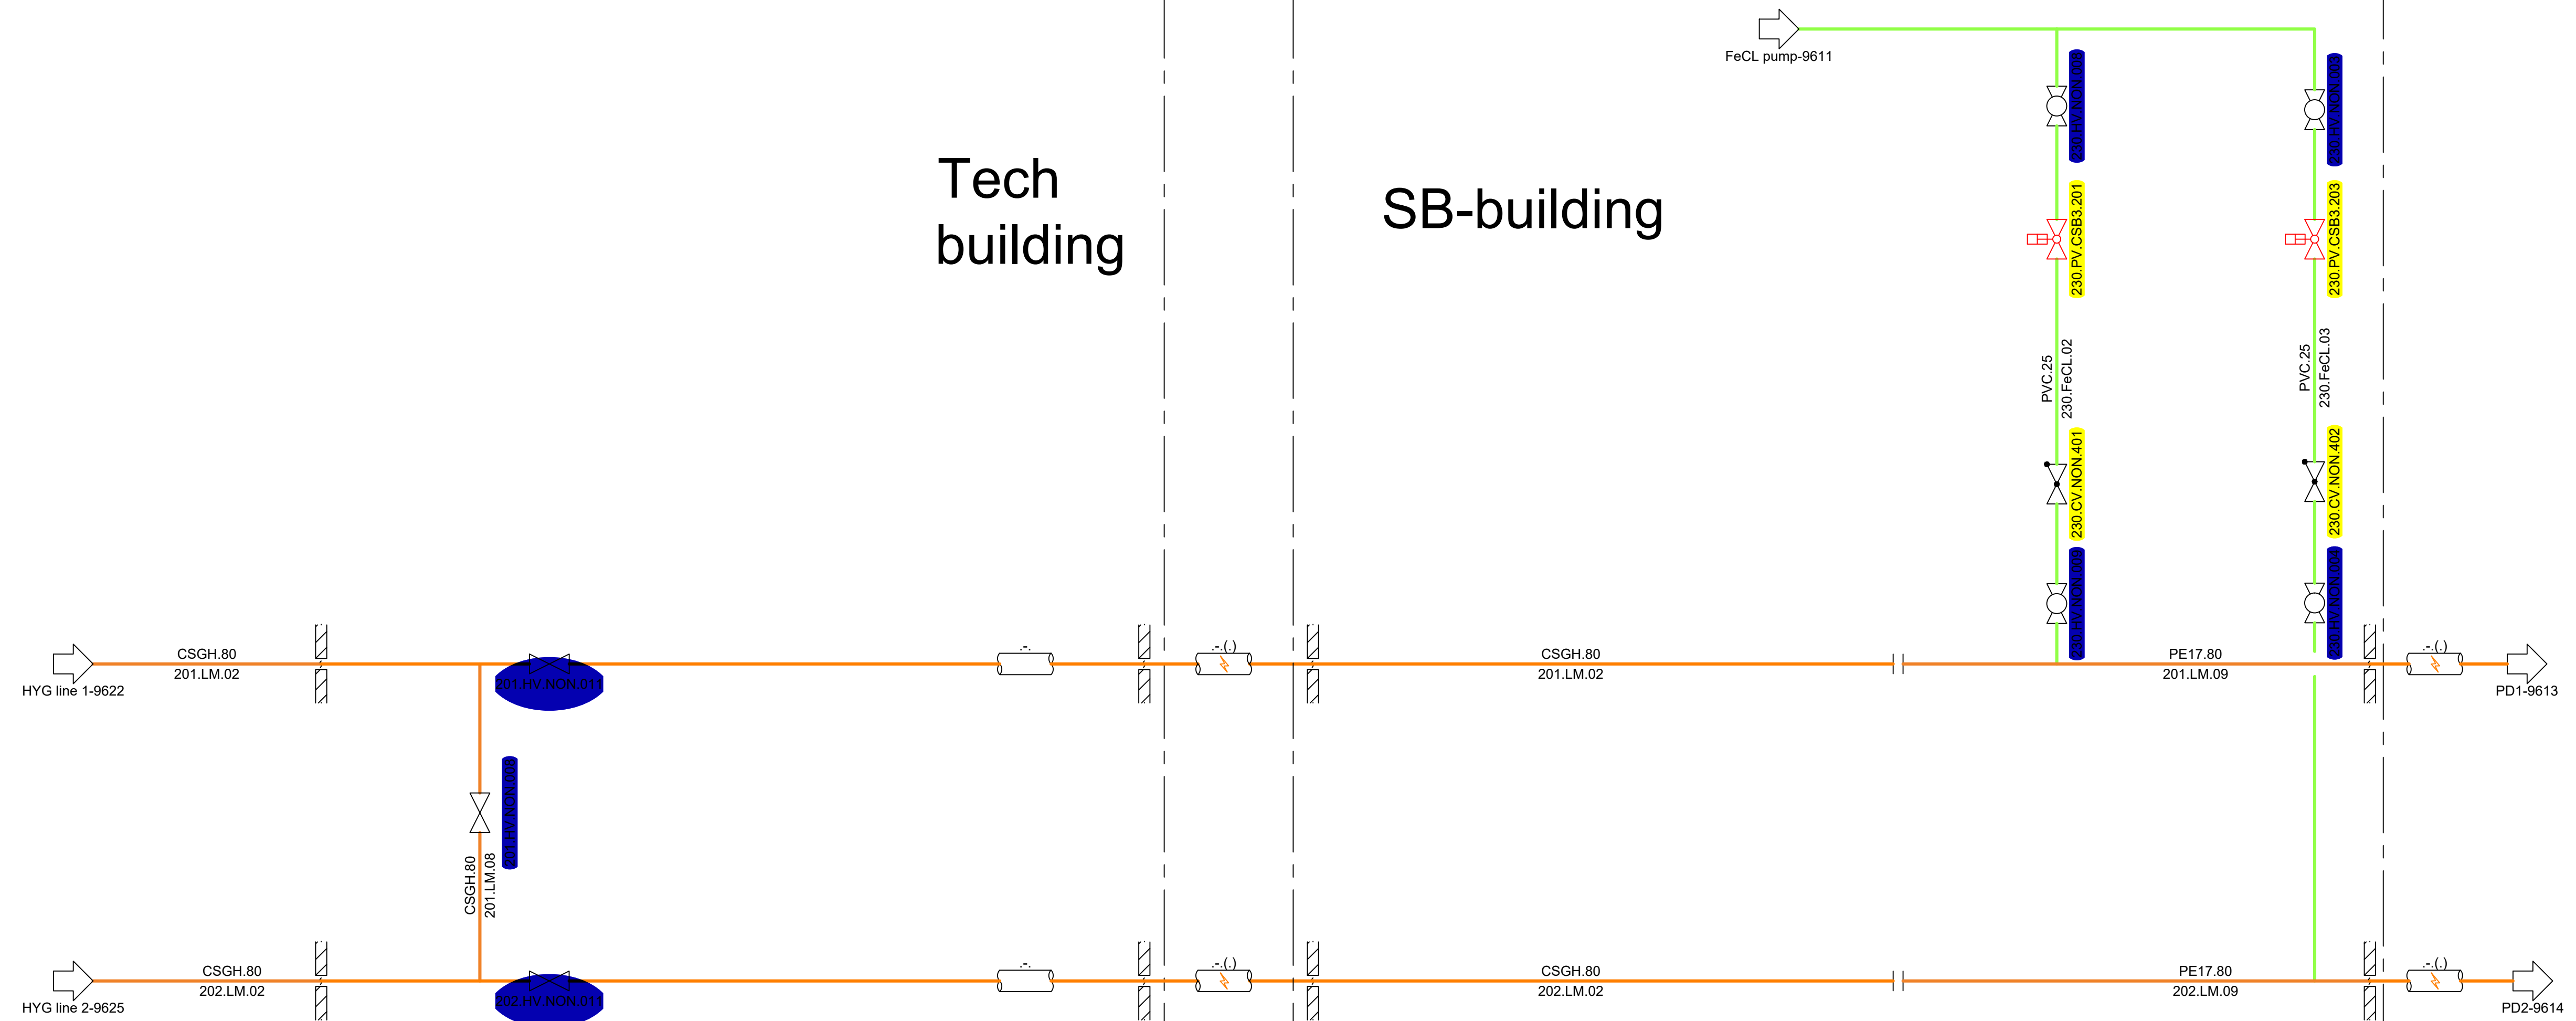


Rev. Nr.:	Rev. Dato:	Rev. Description:	
Builder:	ST1		
Project:	SLK		
Subject:	Liquid manure pump		
Rev. 6			
Int.: MDC	QC: CM	APP.:	Date: 15-10-2025
LUNDSBY RENEWABLE SOLUTIONS			Lundsby Renewable Solutions A/S, Hjarbækvej 65, 8831 Løgstrup Tlf.: +45 96 49 43 00 Info@lundsby.dk This Drawing is subject to copyright and may not be reproduced without permission from Lundsby Renewable Solutions A/S
Project nr.: 1768 Drawing nr.: 9612			FORMAT: A1

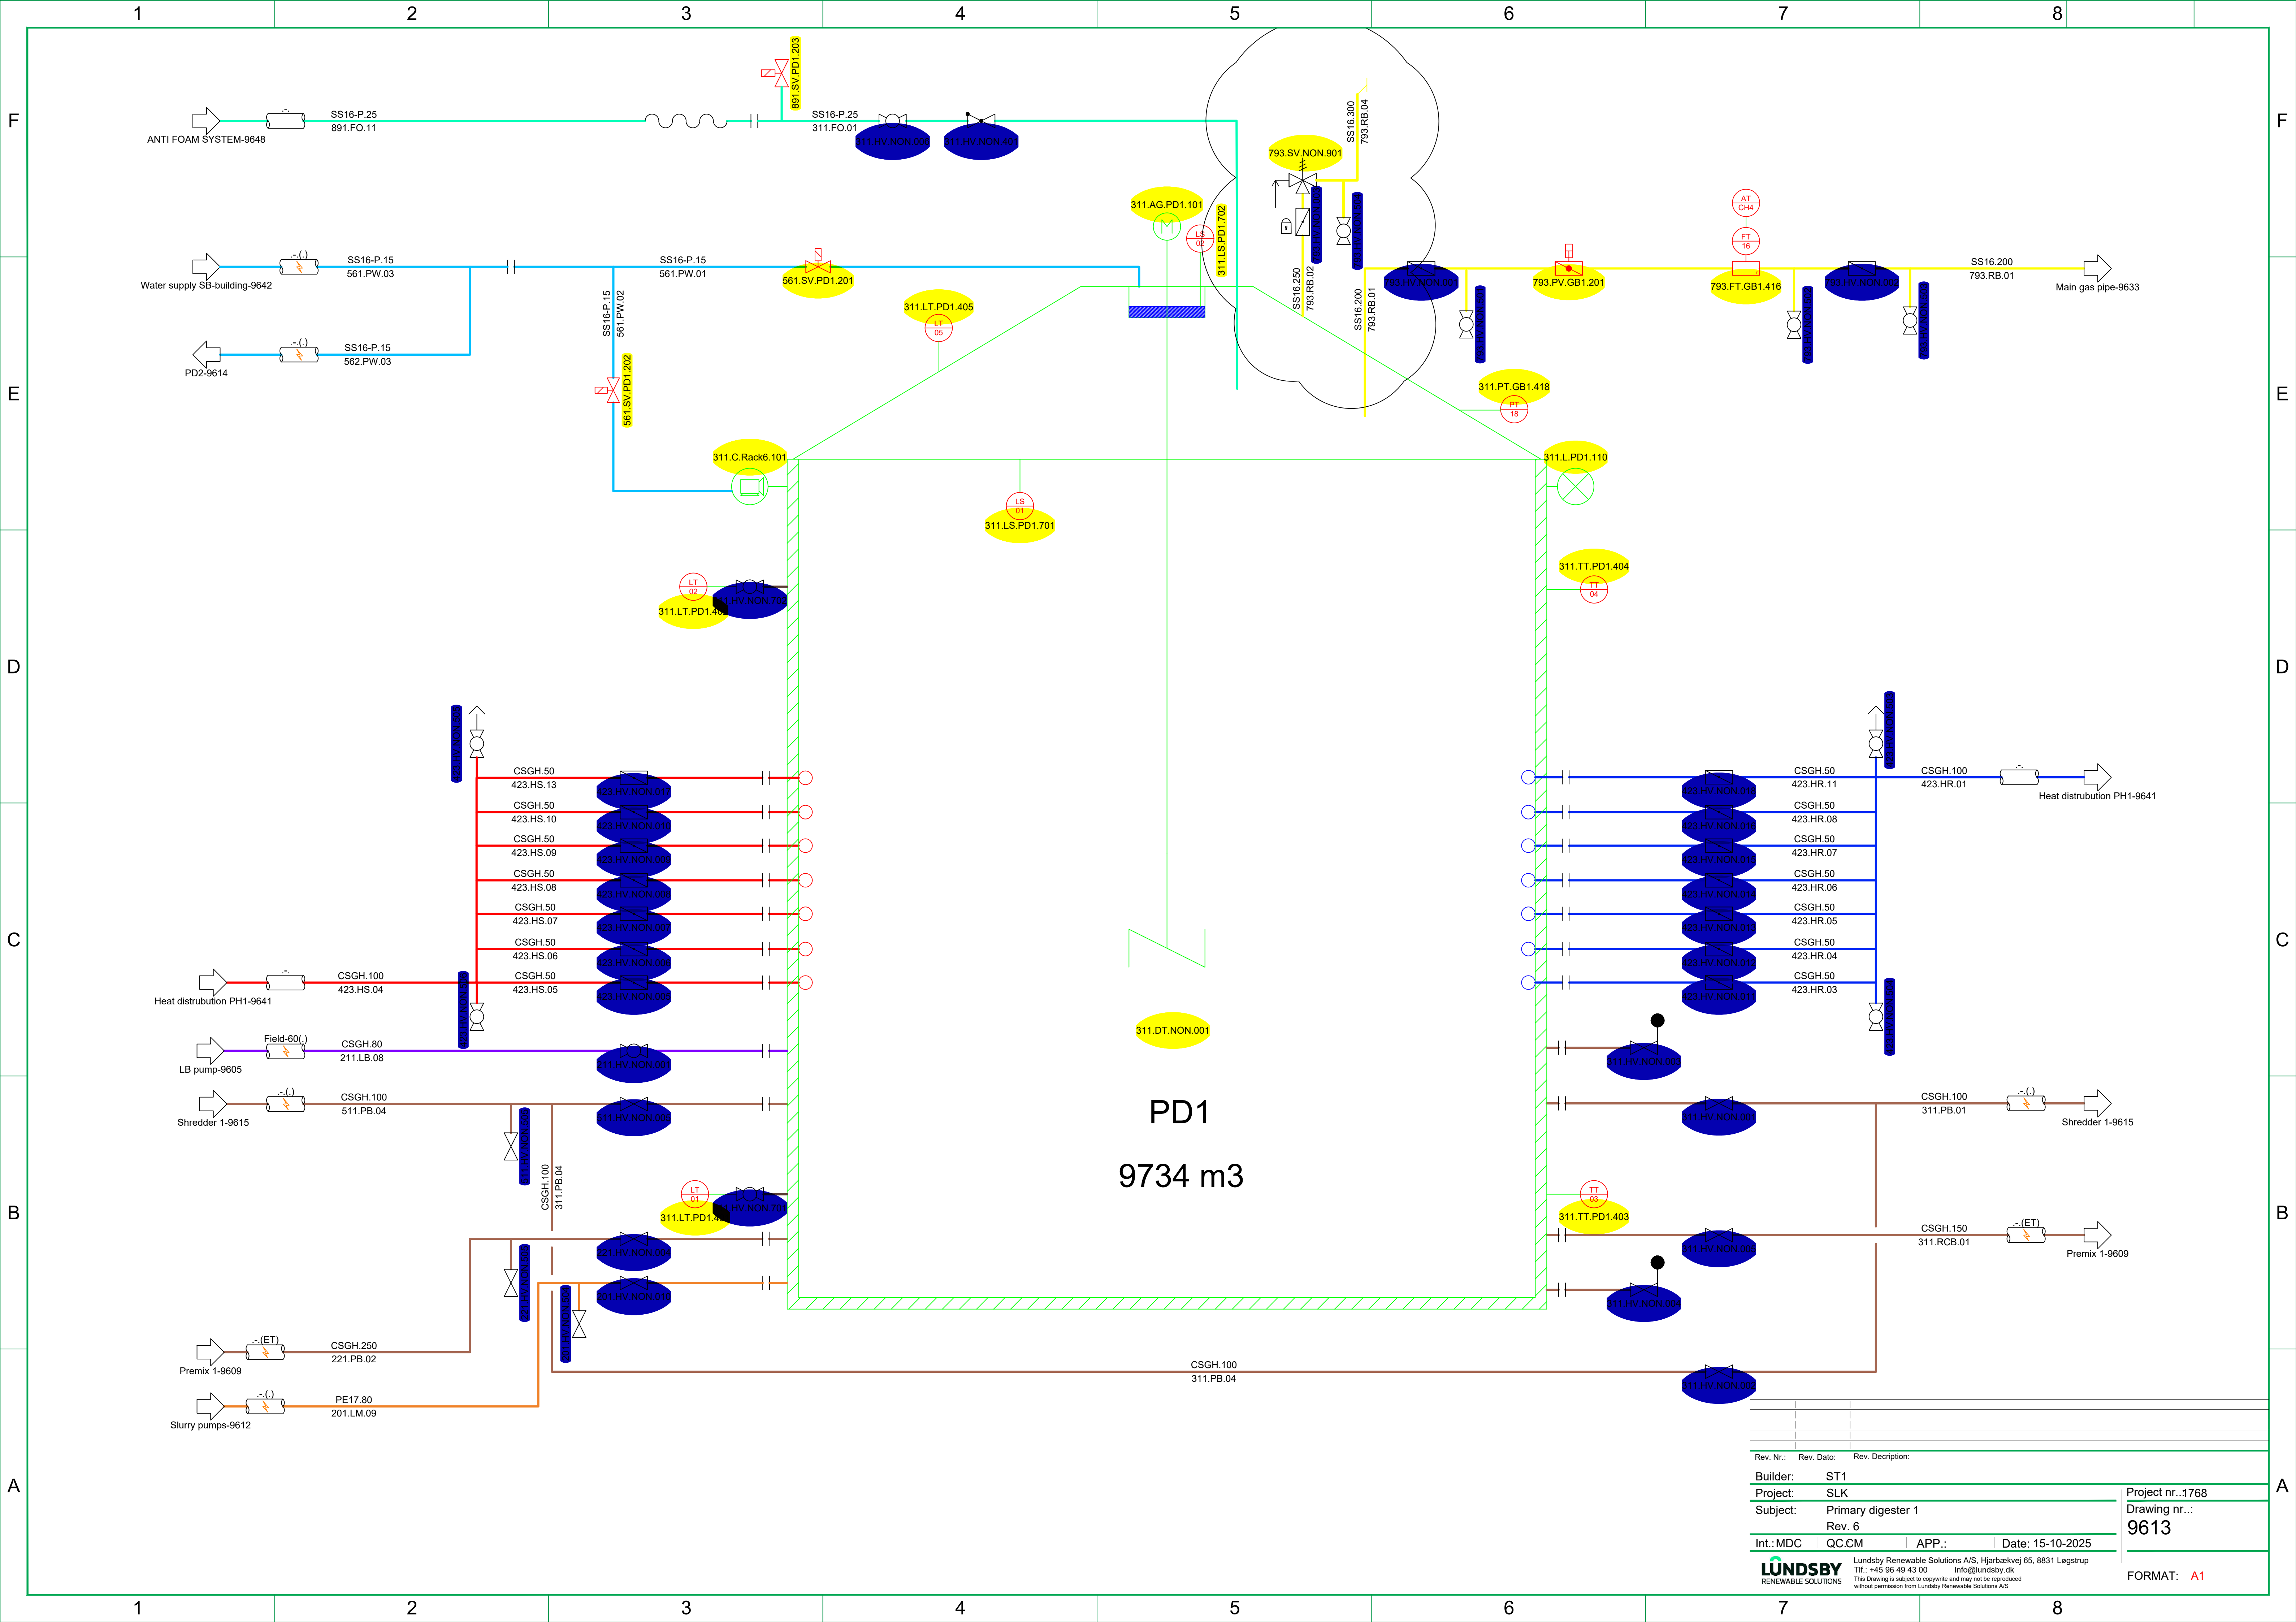



Rev. Nr.:	Rev. Dato:	Rev. Description:
Builder:	ST1	
Project:	SLK	
Subject:	Primary digester 1	
Rev. 6		
Int.:MDC	QC:CM	APP.:
Date: 15-10-2025		
LUNDSBY RENEWABLE SOLUTIONS		
Lundsgby Renewable Solutions A/S, Hjarbrækvej 65, 8831 Lægstrup Tlf.: +45 96 49 43 00 Info@lundsgby.dk This drawing is subject to copyright and may not be reproduced without permission from Lundsgby Renewable Solutions A/S		
Project nr.:1768 Drawing nr.: 9613		FORMAT: A1

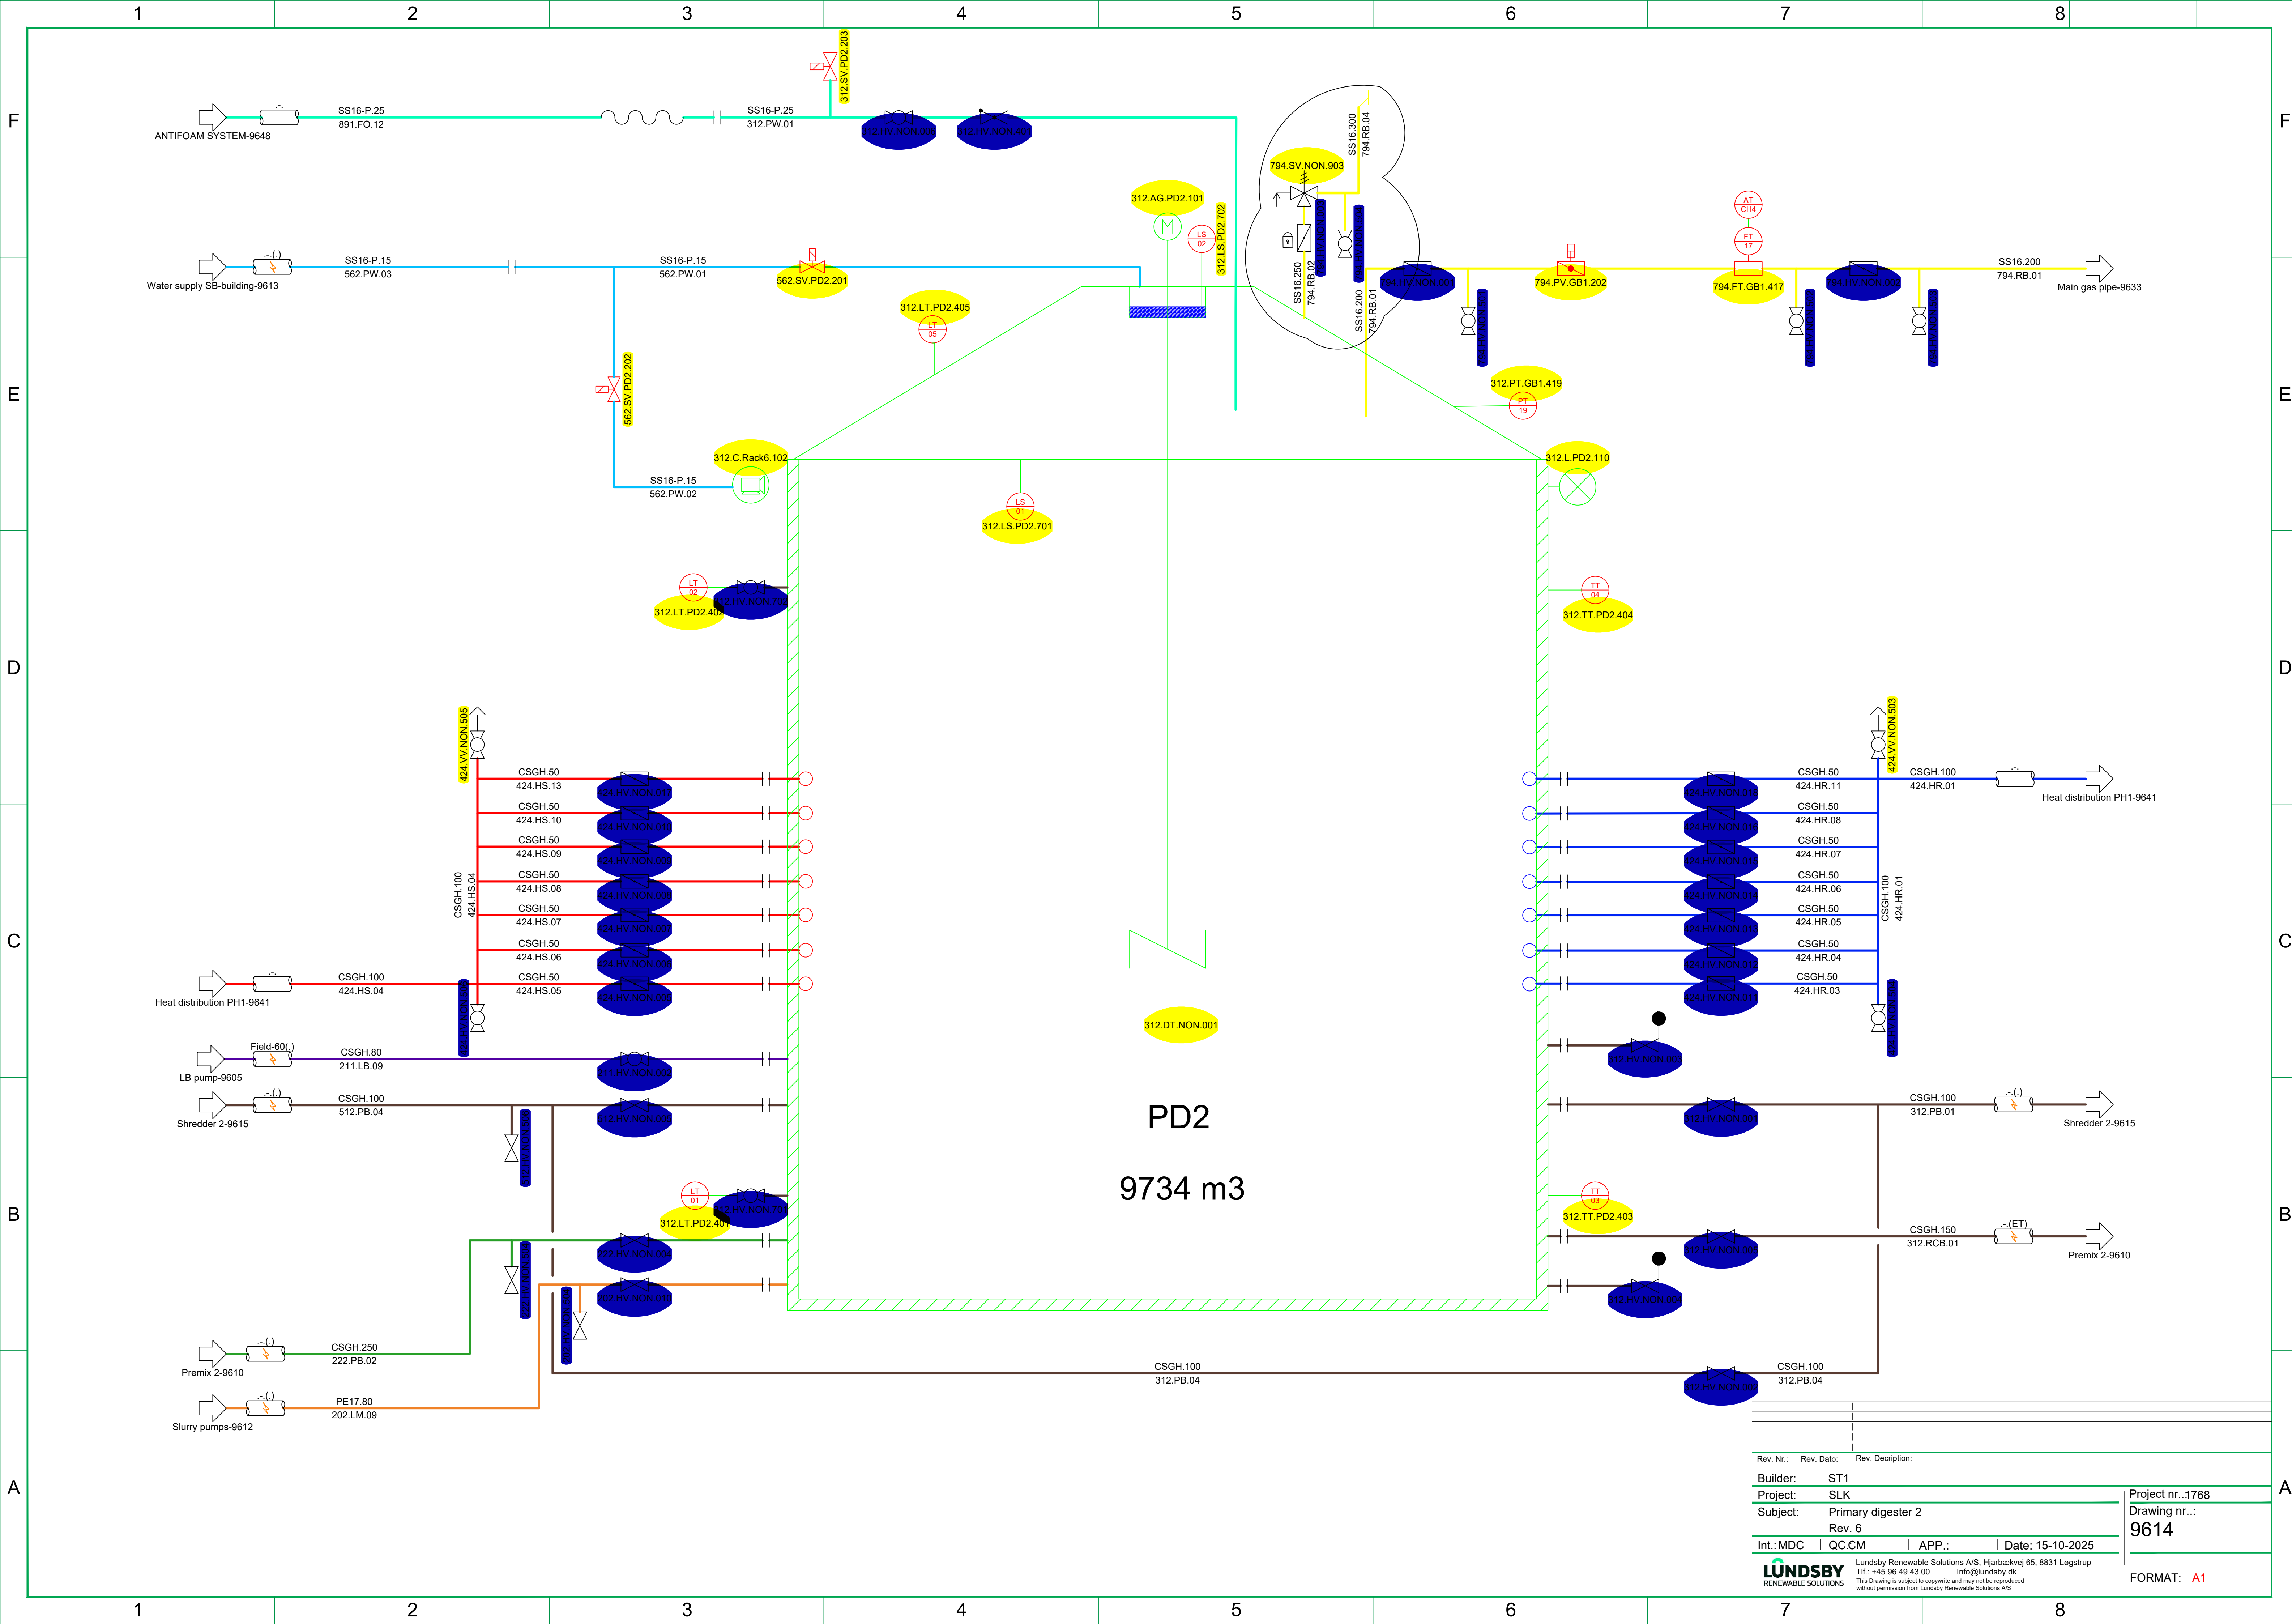

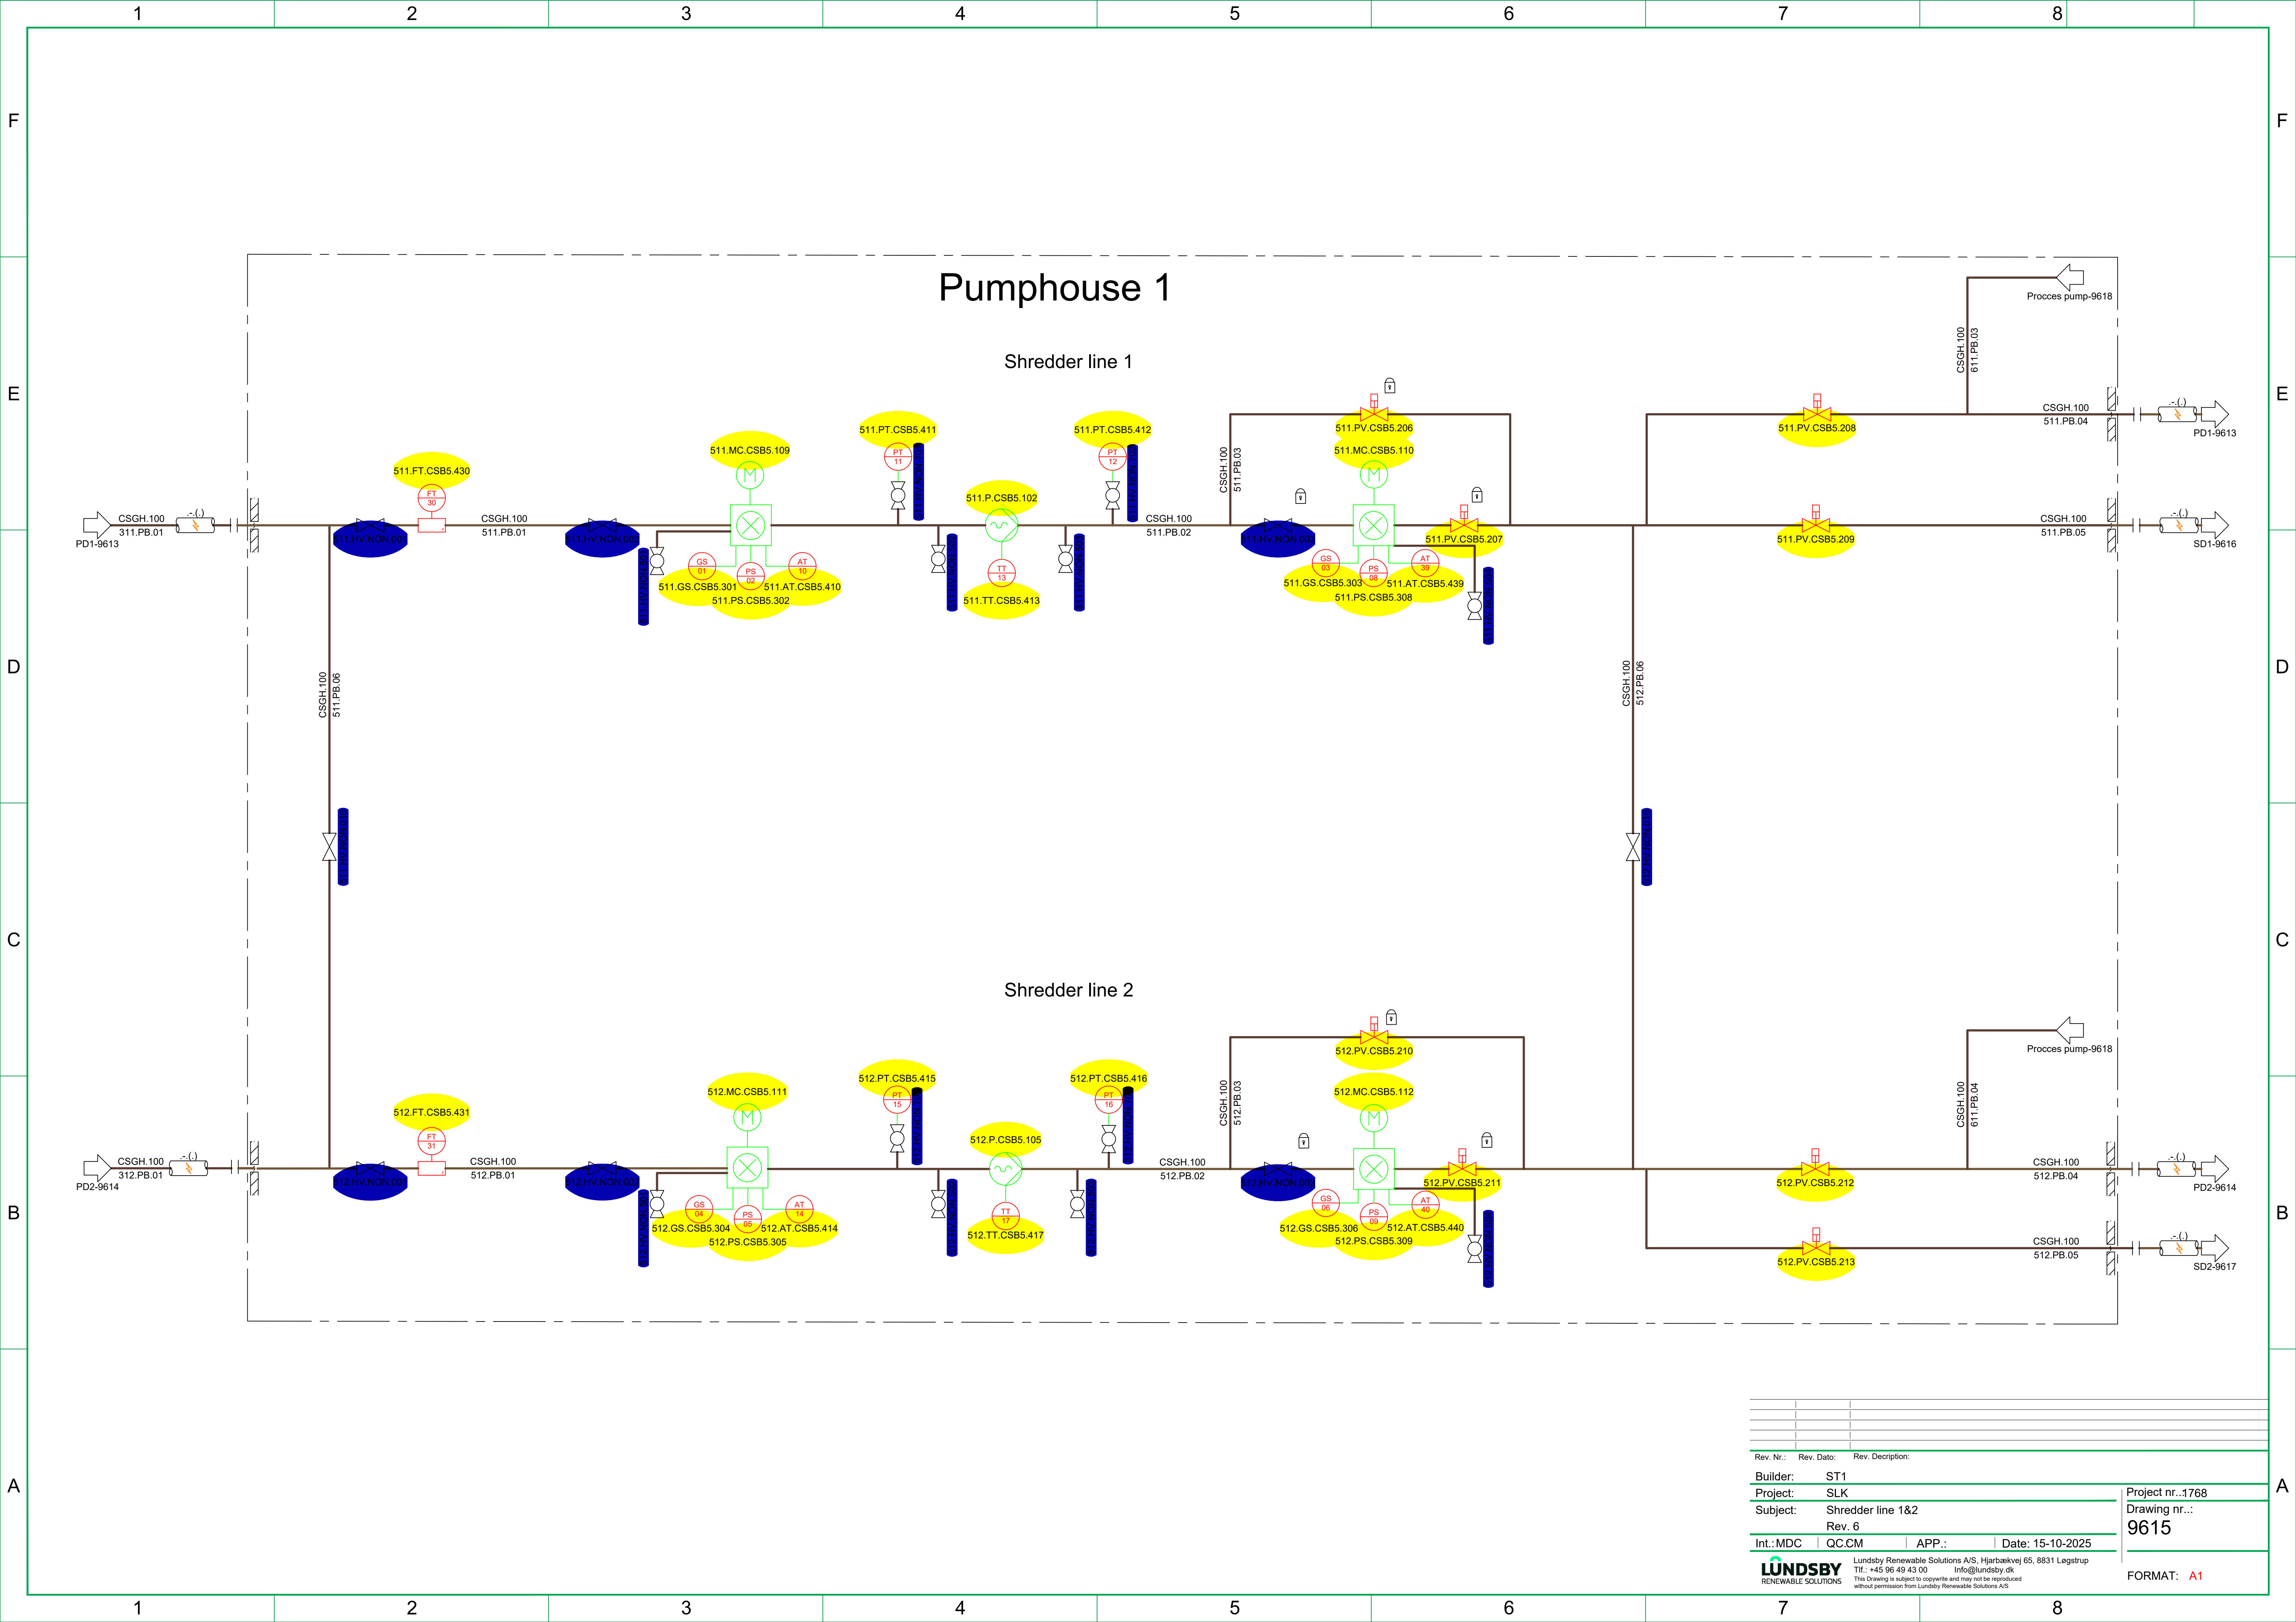


Rev. Nr.:	Rev. Dato:	Rev. Description:
Builder:	ST1	
Project:	SLK	
Subject:	Shredder line 1&2	
Rev. 6		
Int.:MDC	QC:CM	APP.:Date: 15-10-2025
LUNDSBY RENEWABLE SOLUTIONS		
Lundsby Renewable Solutions A/S, Hjarbrækvej 65, 8831 Lægstrup Tlf.: +45 96 49 43 00 Info@lundsby.dk This Drawing is subject to copyright and may not be reproduced without permission from Lundsby Renewable Solutions A/S		
Project nr.:1768 Drawing nr.: 9615		FORMAT: A1

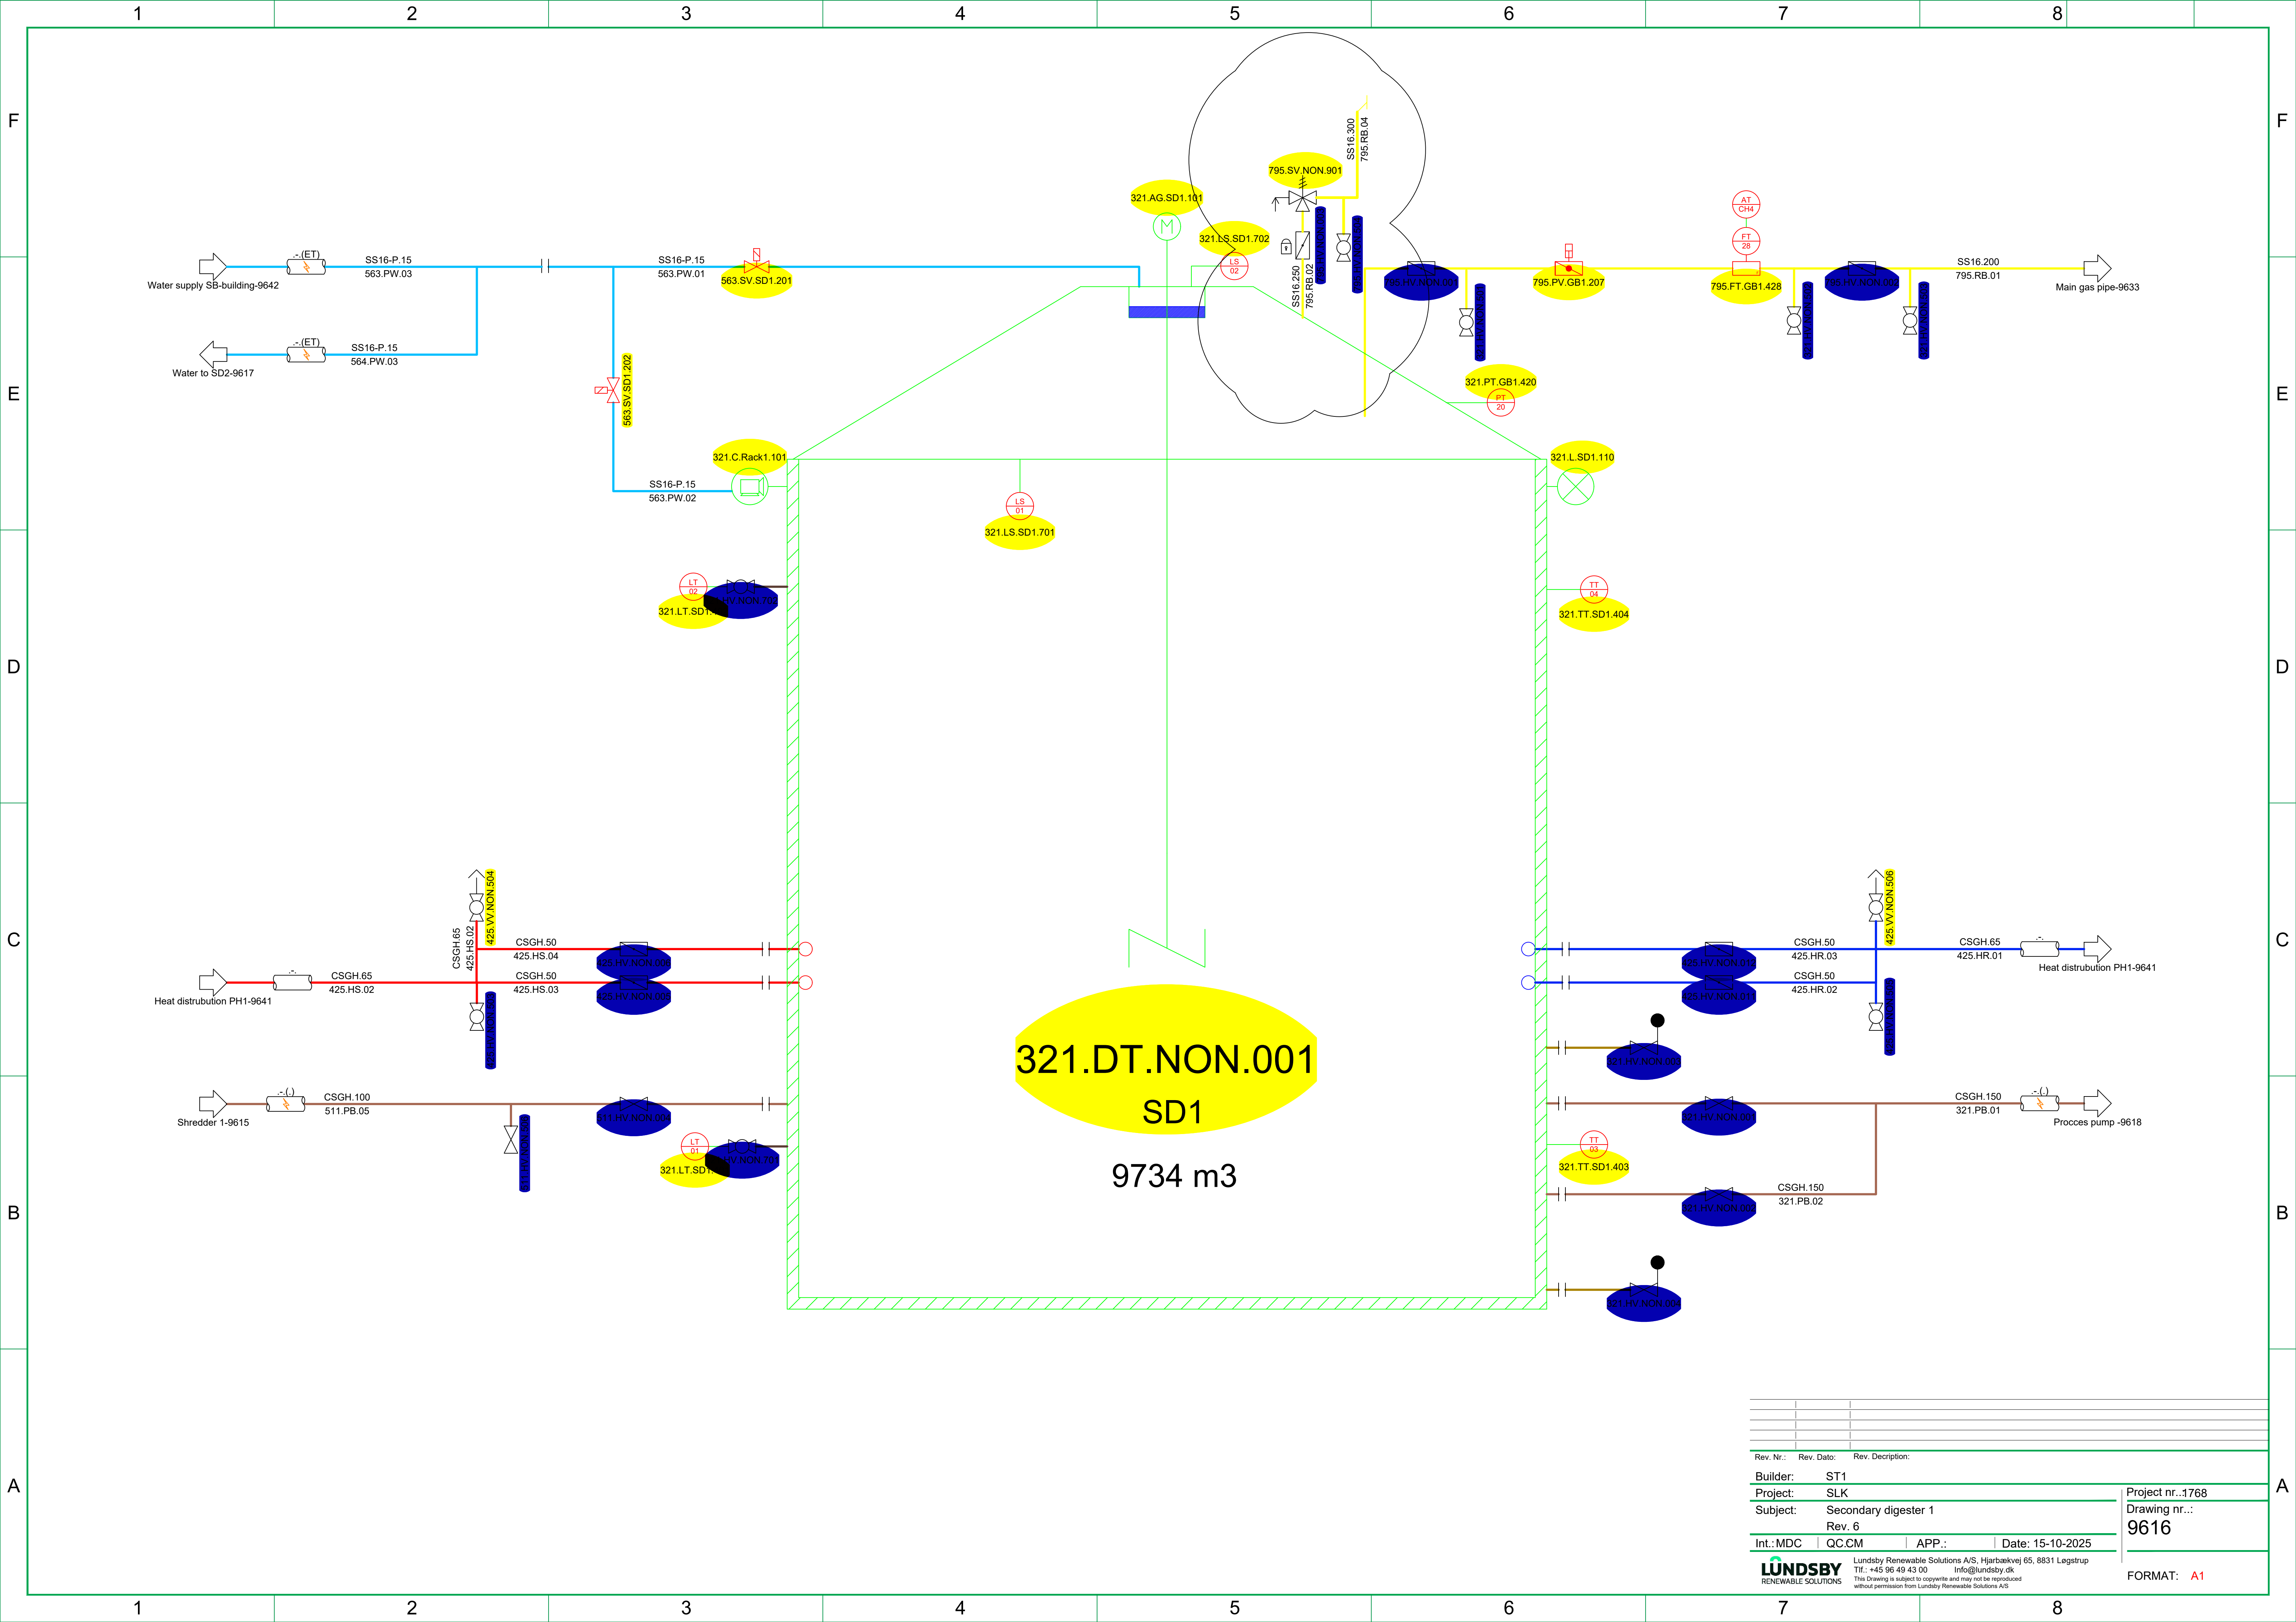

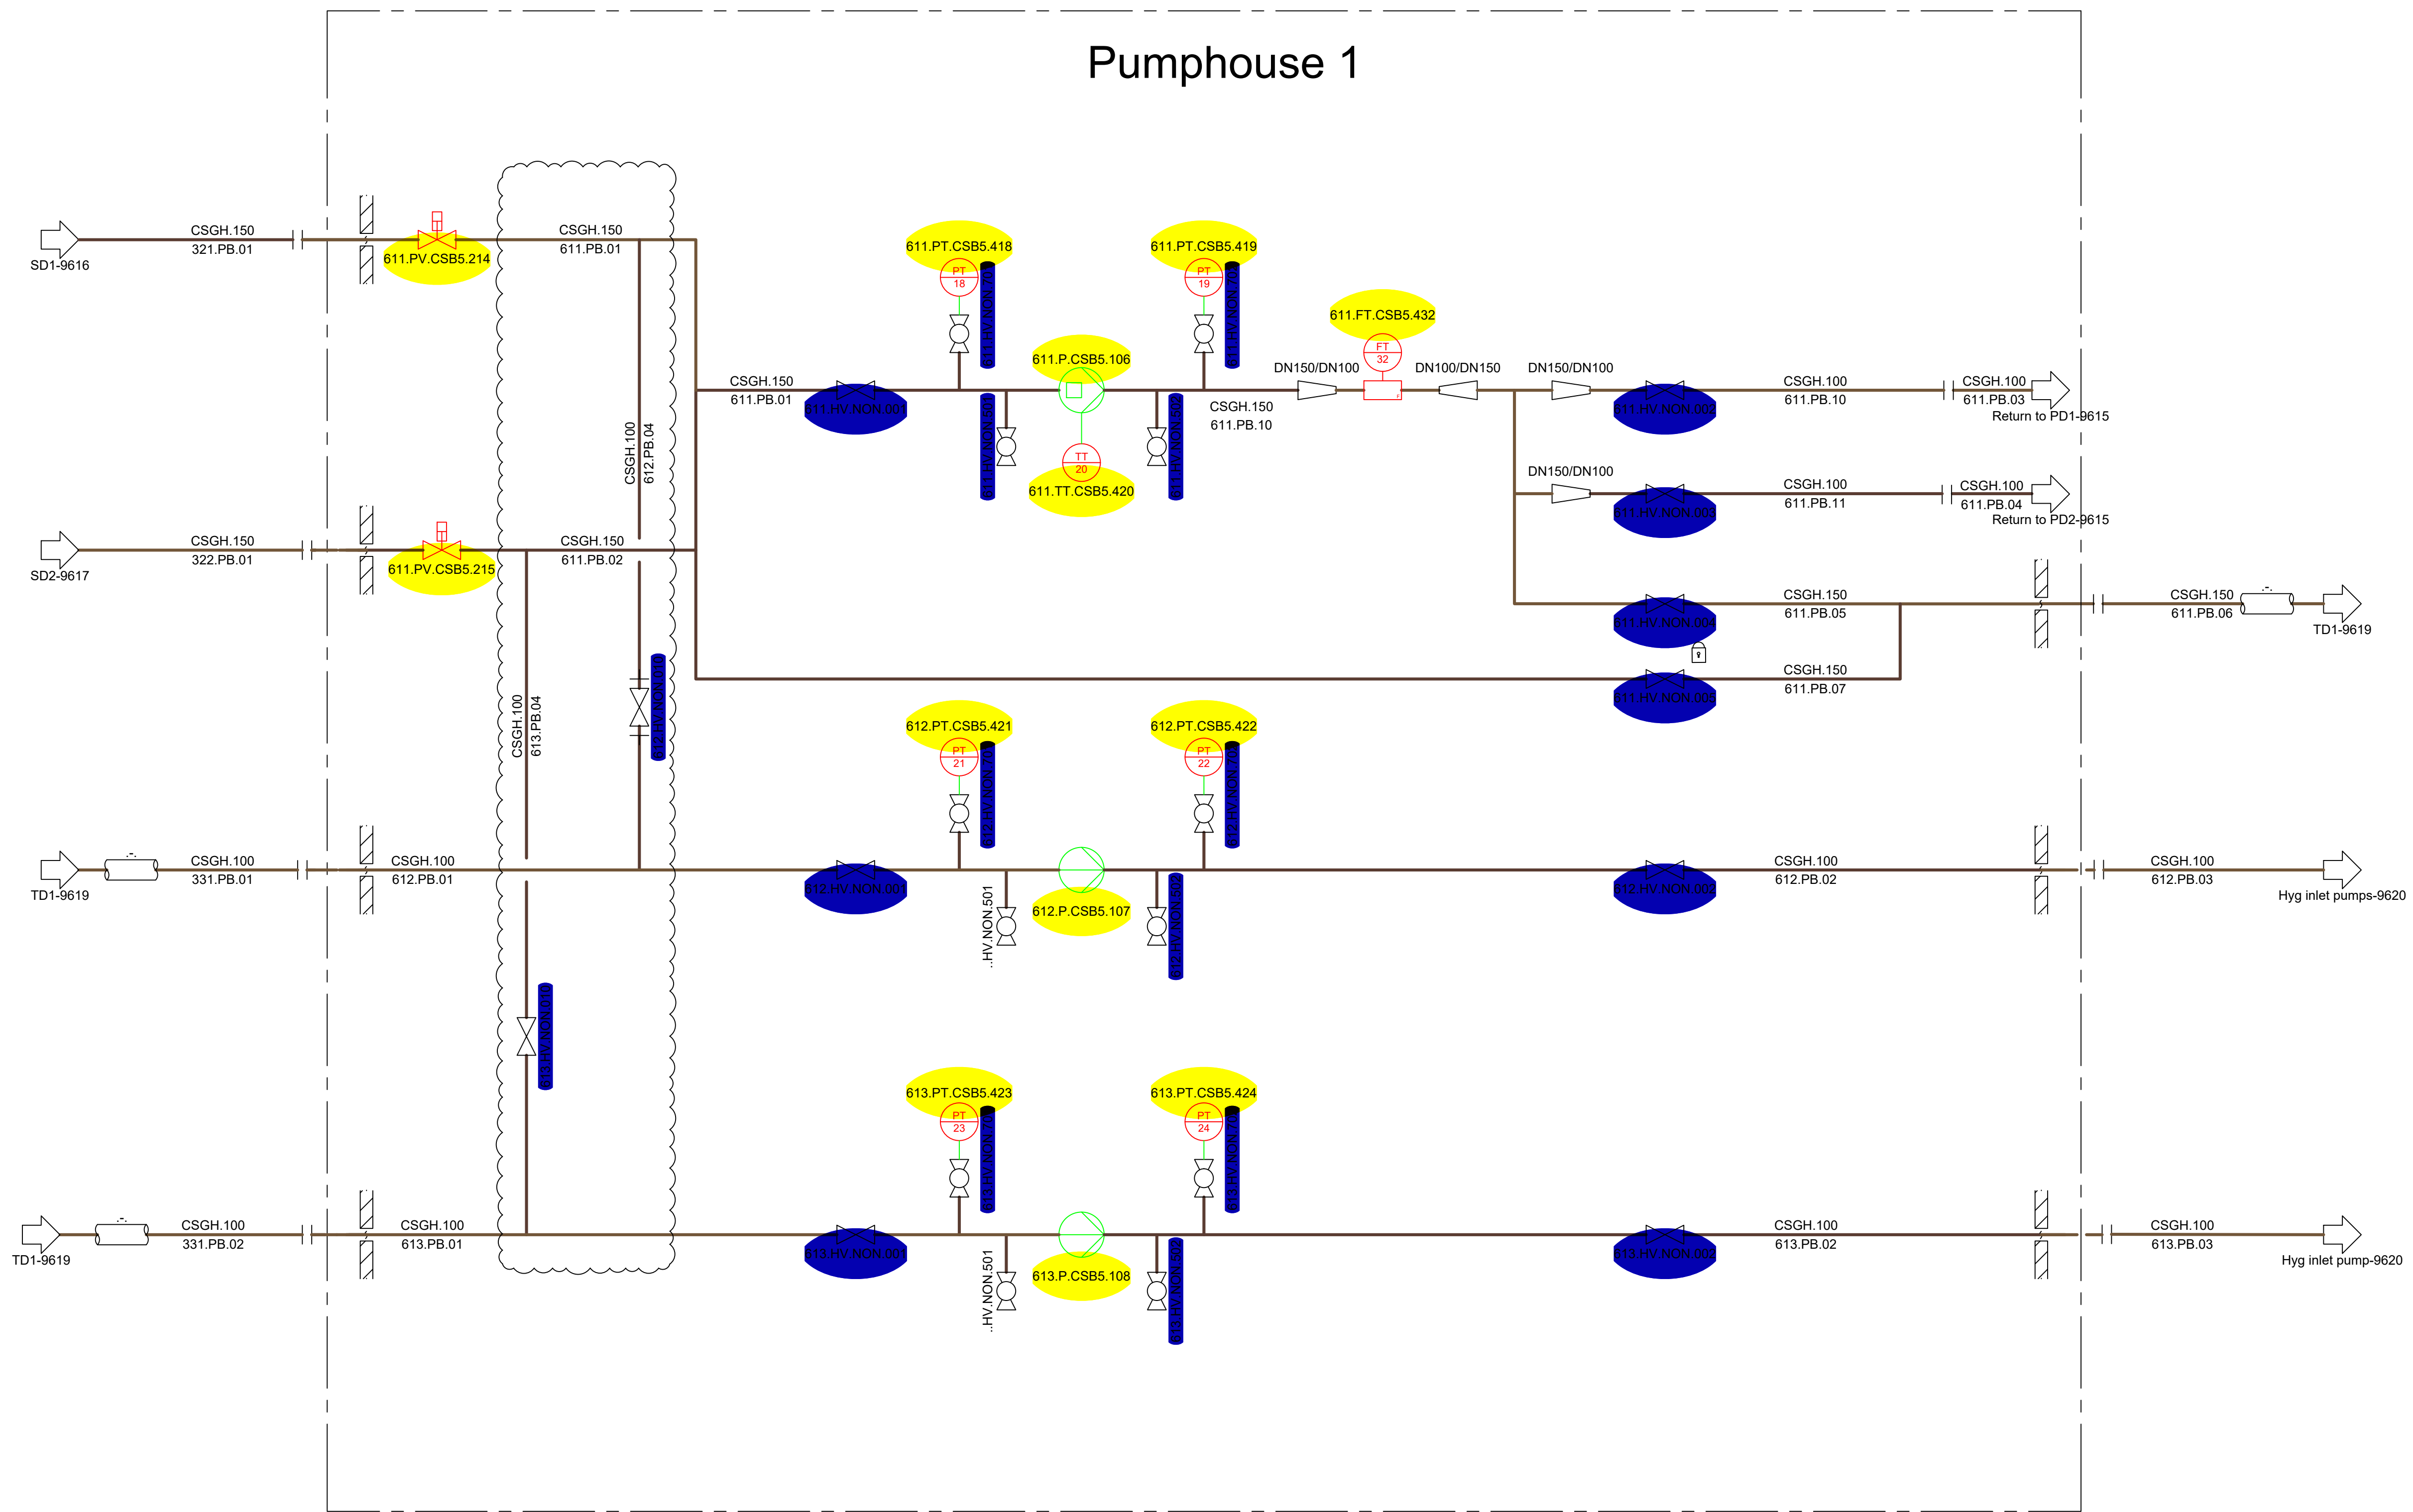


Rev. Nr.:	Rev. Dato:	Rev. Description:	
Builder:	ST1		
Project:	SLK		
Subject:	Procces pumps		
	Rev. 6		
Int.:MDC	QC:CM	APP.:	Date: 15-10-2025
LUNDSBY RENEWABLE SOLUTIONS			Lundsby Renewable Solutions A/S, Hjarbækvej 65, 8831 Løgstrup Tlf.: +45 96 49 43 00 Info@lundsby.dk This Drawing is subject to copyright and may not be reproduced without permission from Lundsby Renewable Solutions A/S
Project nr.:1768 Drawing nr.: 9618			FORMAT: A1

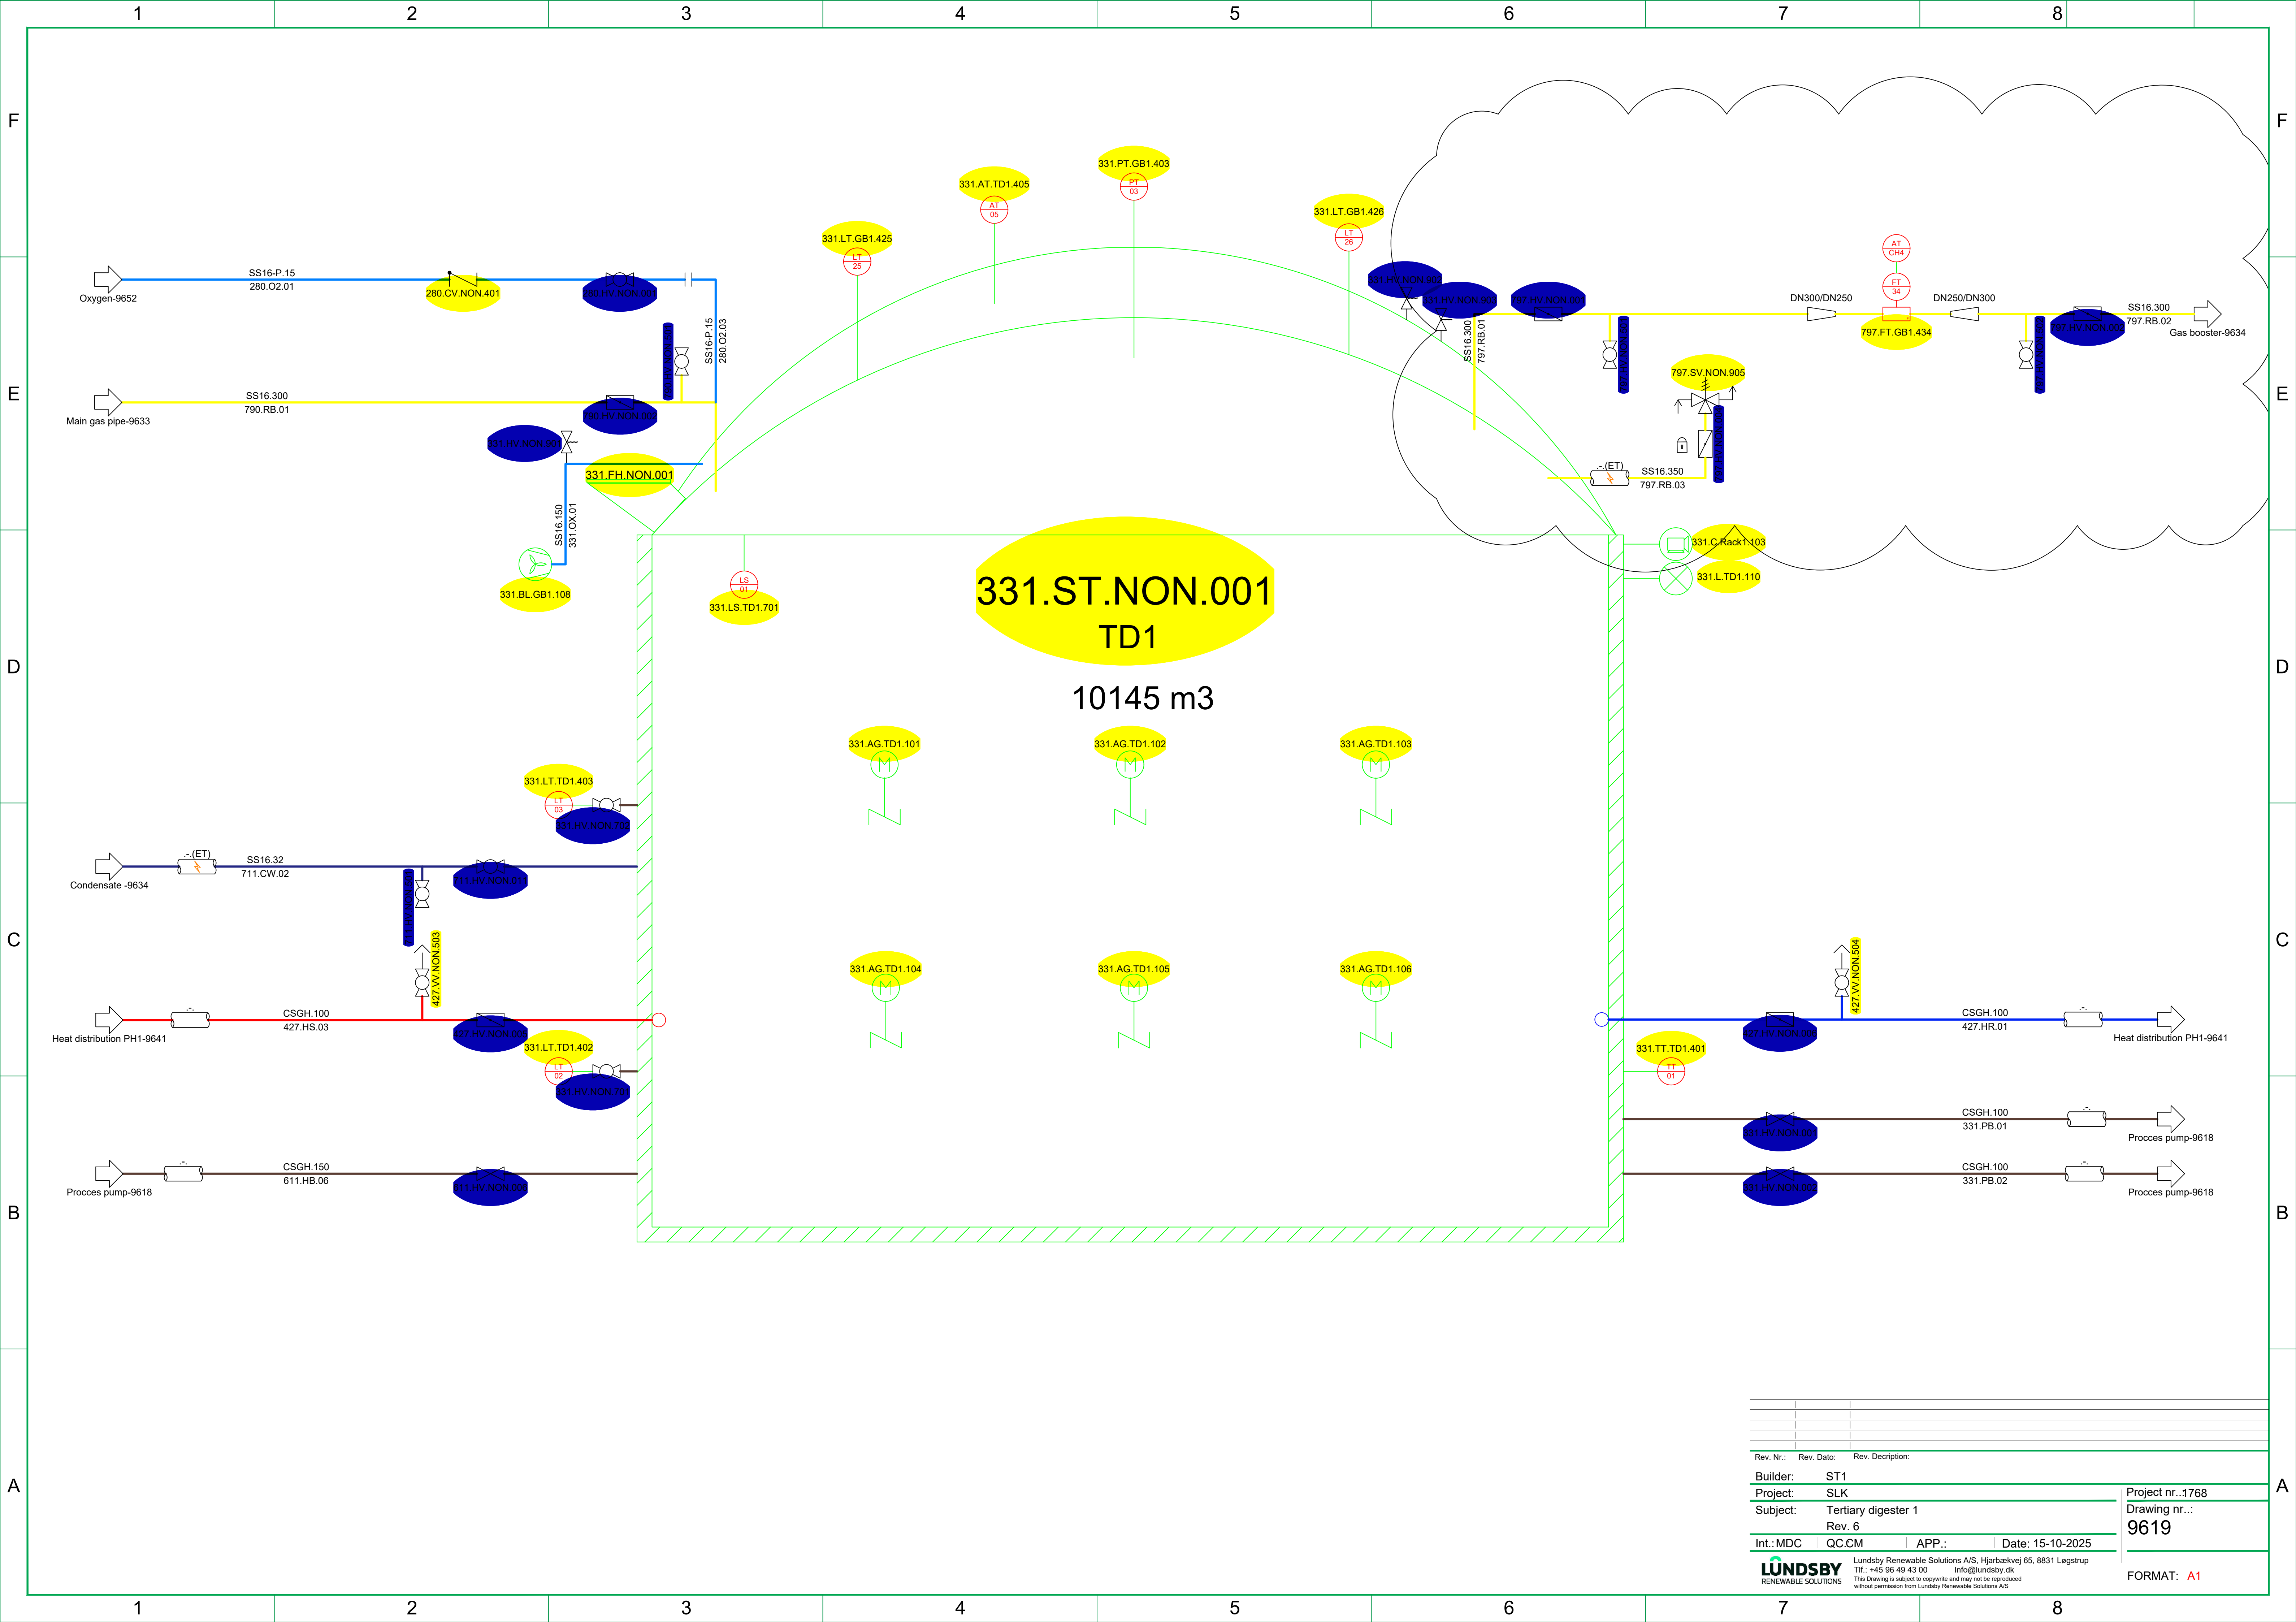


Rev. Nr.:	Rev. Dato:	Rev. Description:			
Builder:	ST1				
Project:	SLK				
Subject:	Tertiary digester 1				
	Rev. 6				
Int.:MDC	QC:CM	APP.:	Date: 15-10-2025		
		Lundsby Renewable Solutions A/S, Hjarbækvej 65, 8831 Lægstrup Tlf.: +45 96 49 43 00 Info@lundsby.dk This Drawing is subject to copyright and may not be reproduced without permission from Lundsby Renewable Solutions A/S			
		Project nr.:1768		Drawing nr.: 9619	
		FORMAT: A1			

Tech Building


Inlet pumps

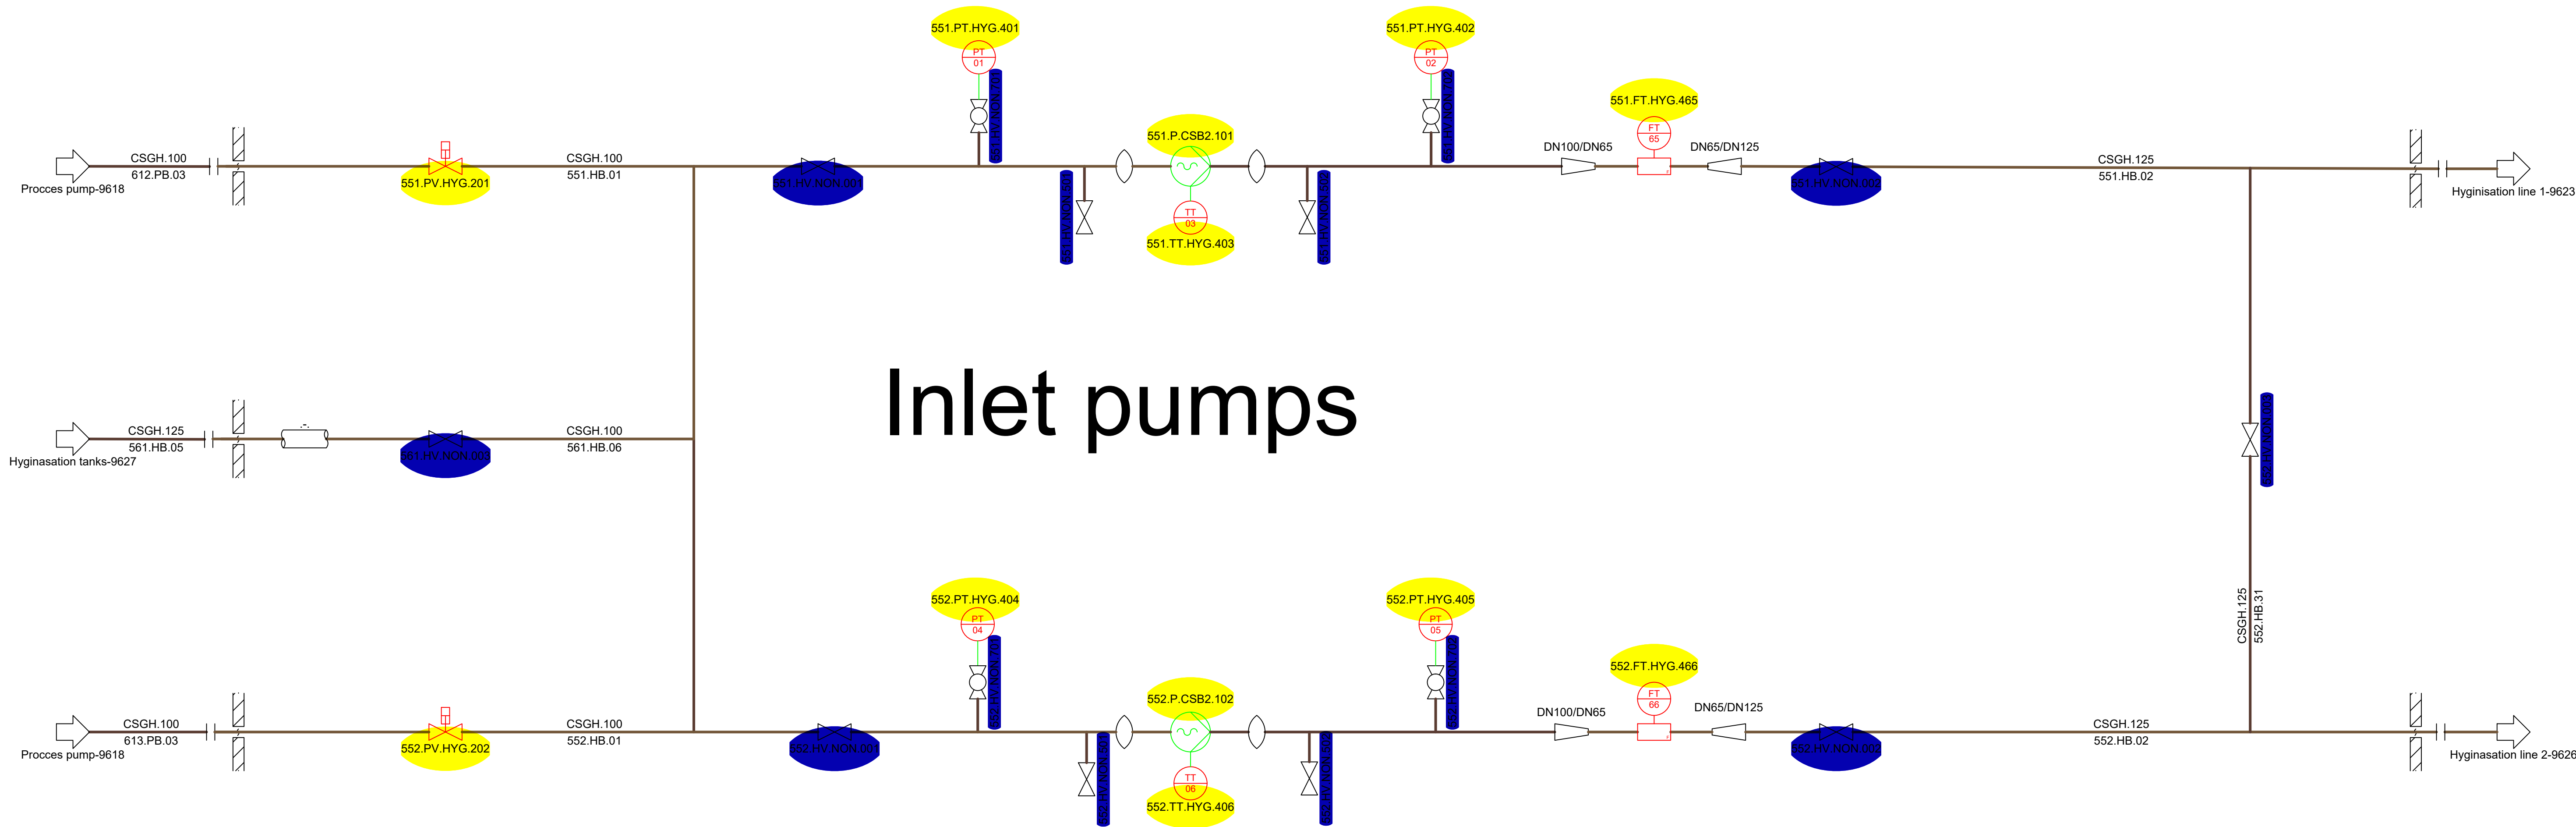



Rev. Nr.:	Rev. Dato:	Rev. Description:	
Builder:	ST1		
Project:	SLK		
Subject:	Hyginisation inlet pumps		
	Rev. 6		
Int.:MDC	QC:CM	APP.:	Date: 15-10-2025
LUNDSBY RENEWABLE SOLUTIONS			Lundsby Renewable Solutions A/S, Hjarbækvej 65, 8831 Løgstrup Tlf.: +45 96 49 43 00 Info@lundsby.dk This Drawing is subject to copyright and may not be reproduced without permission from Lundsby Renewable Solutions A/S
			Project nr.:1768 Drawing nr.: 9620 FORMAT: A1

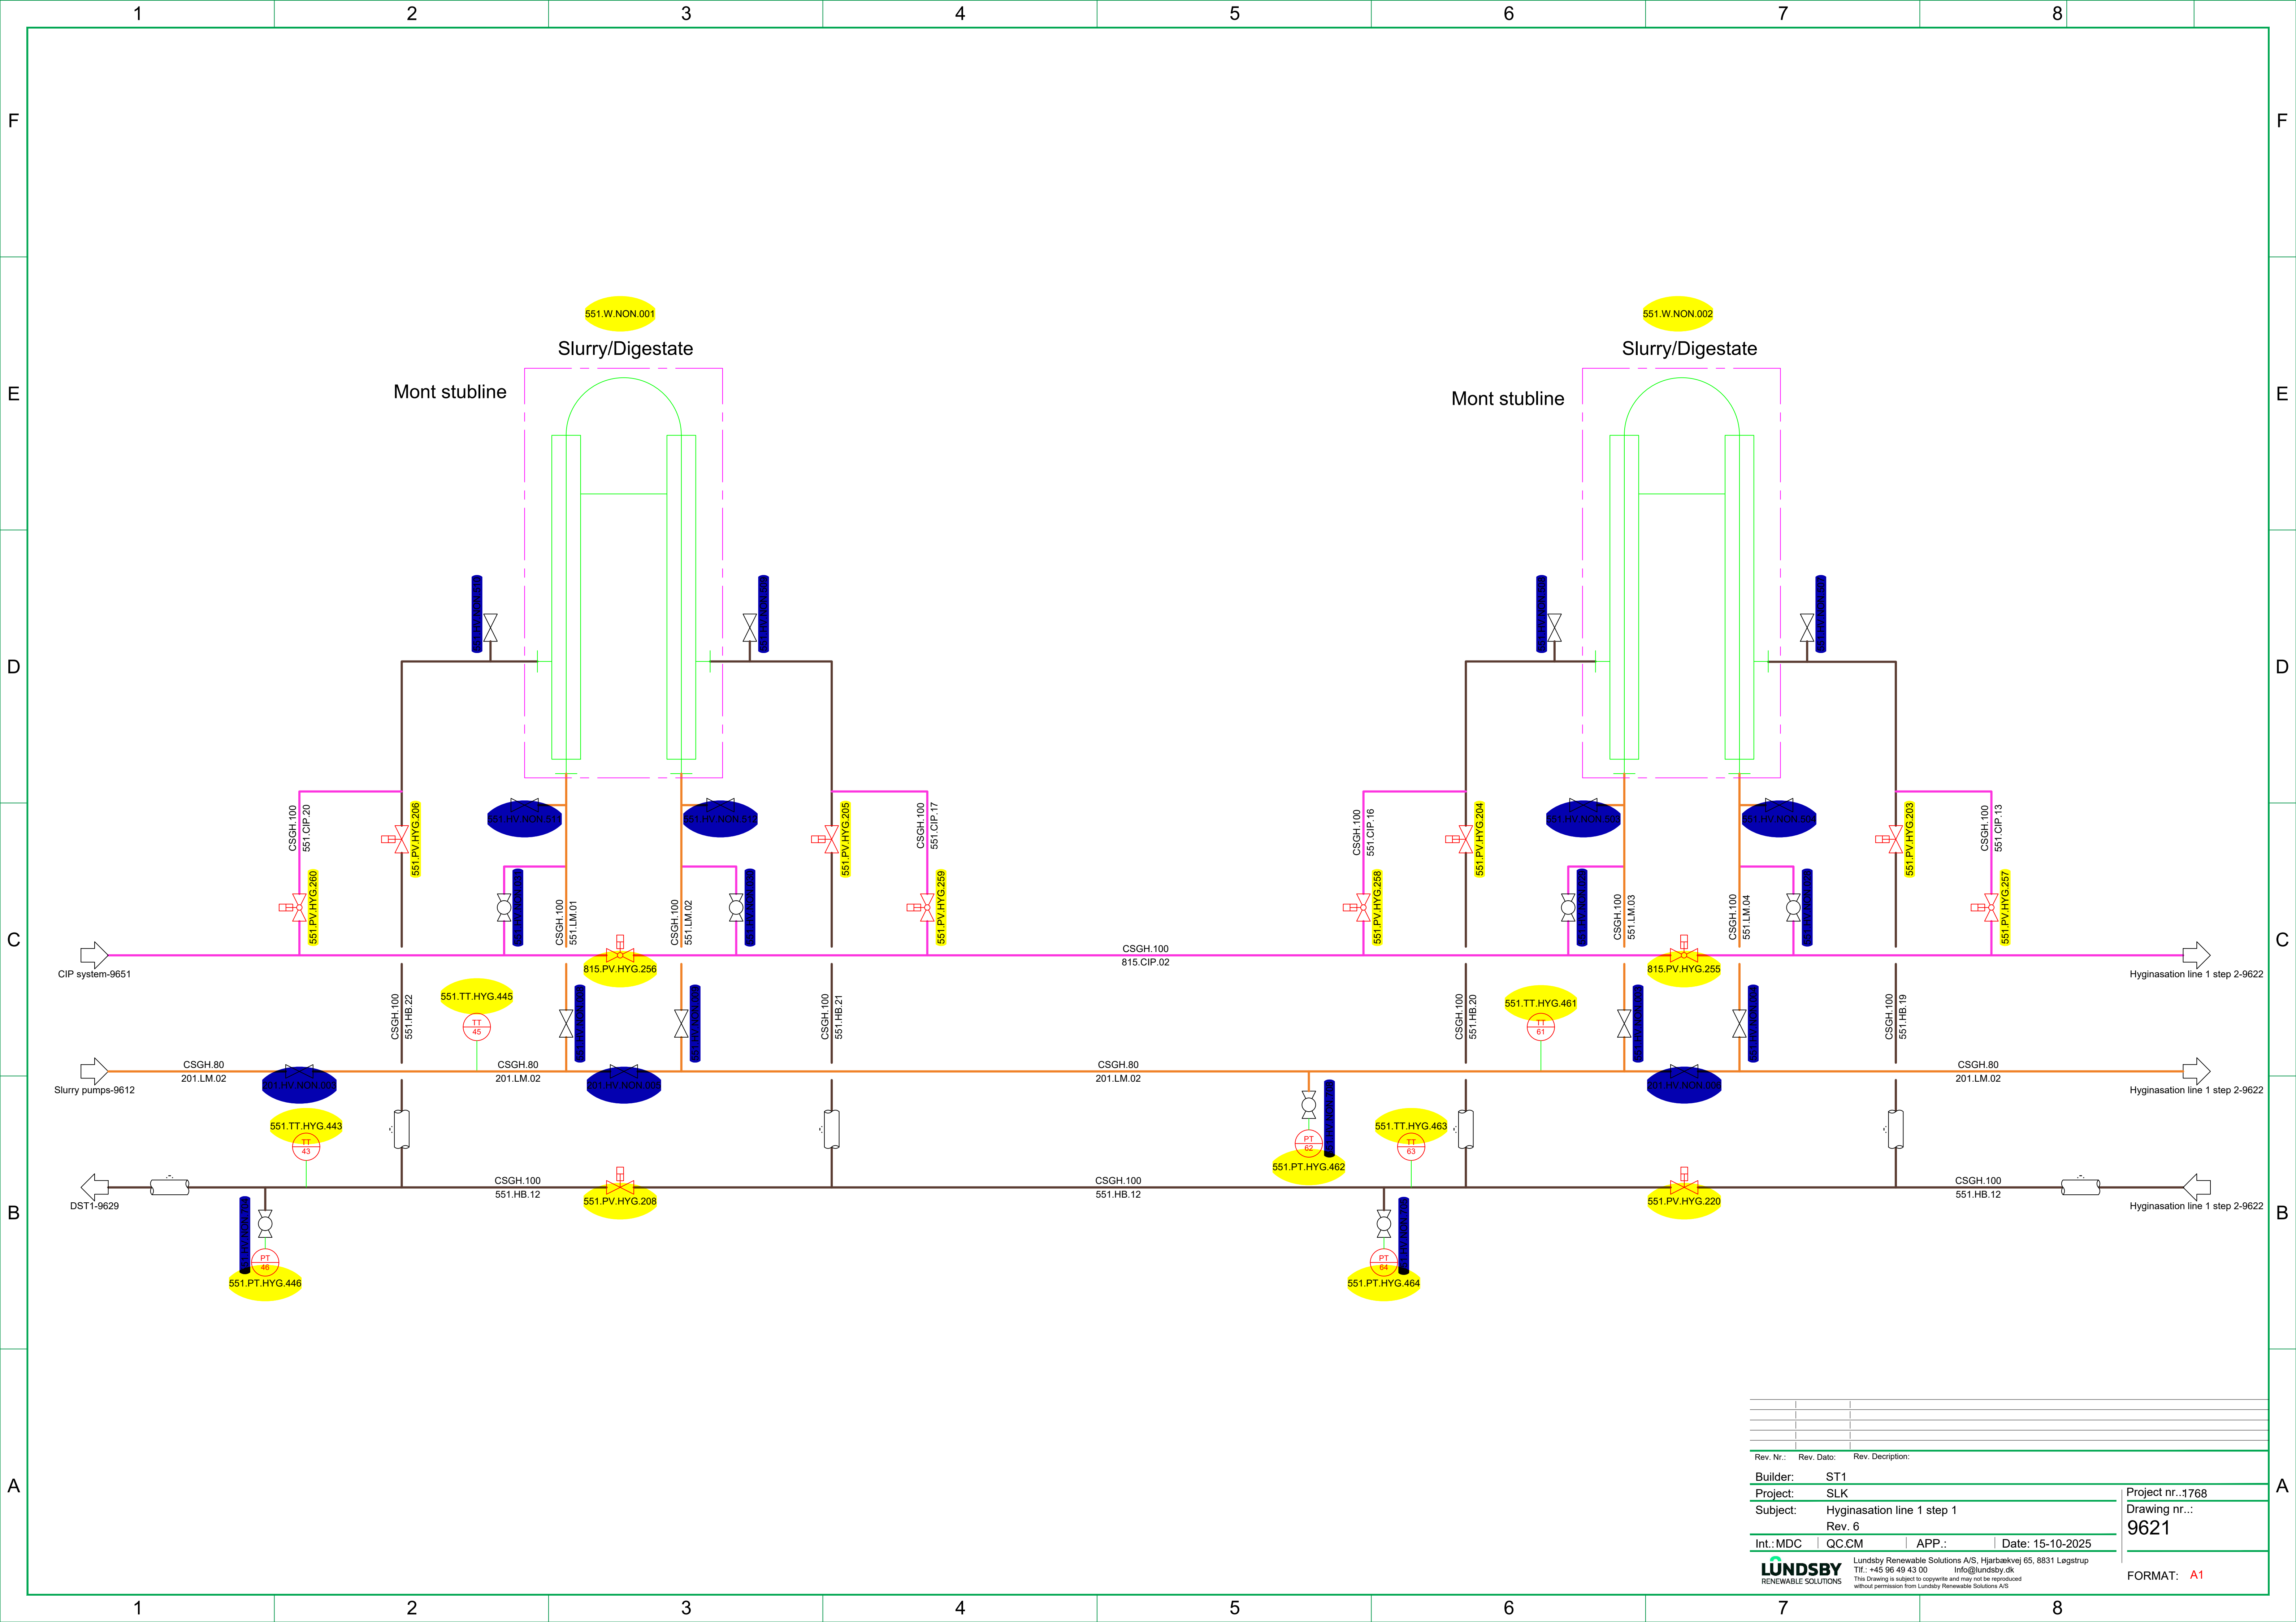


Rev. Nr.:	Rev. Dato:	Rev. Description:
Builder:	ST1	
Project:	SLK	
Subject:	Hyginasation line 1 step 1	
Rev. 6		
Int.:MDC	QC:CM	APP.:
Date: 15-10-2025		
LUNDSBY RENEWABLE SOLUTIONS		
Lundsby Renewable Solutions A/S, Hjarbækvej 65, 8831 Løgstrup Tlf.: +45 96 49 43 00 Info@lundsby.dk This Drawing is subject to copyright and may not be reproduced without permission from Lundsby Renewable Solutions A/S		
Project nr.:1768 Drawing nr.: 9621		FORMAT: A1

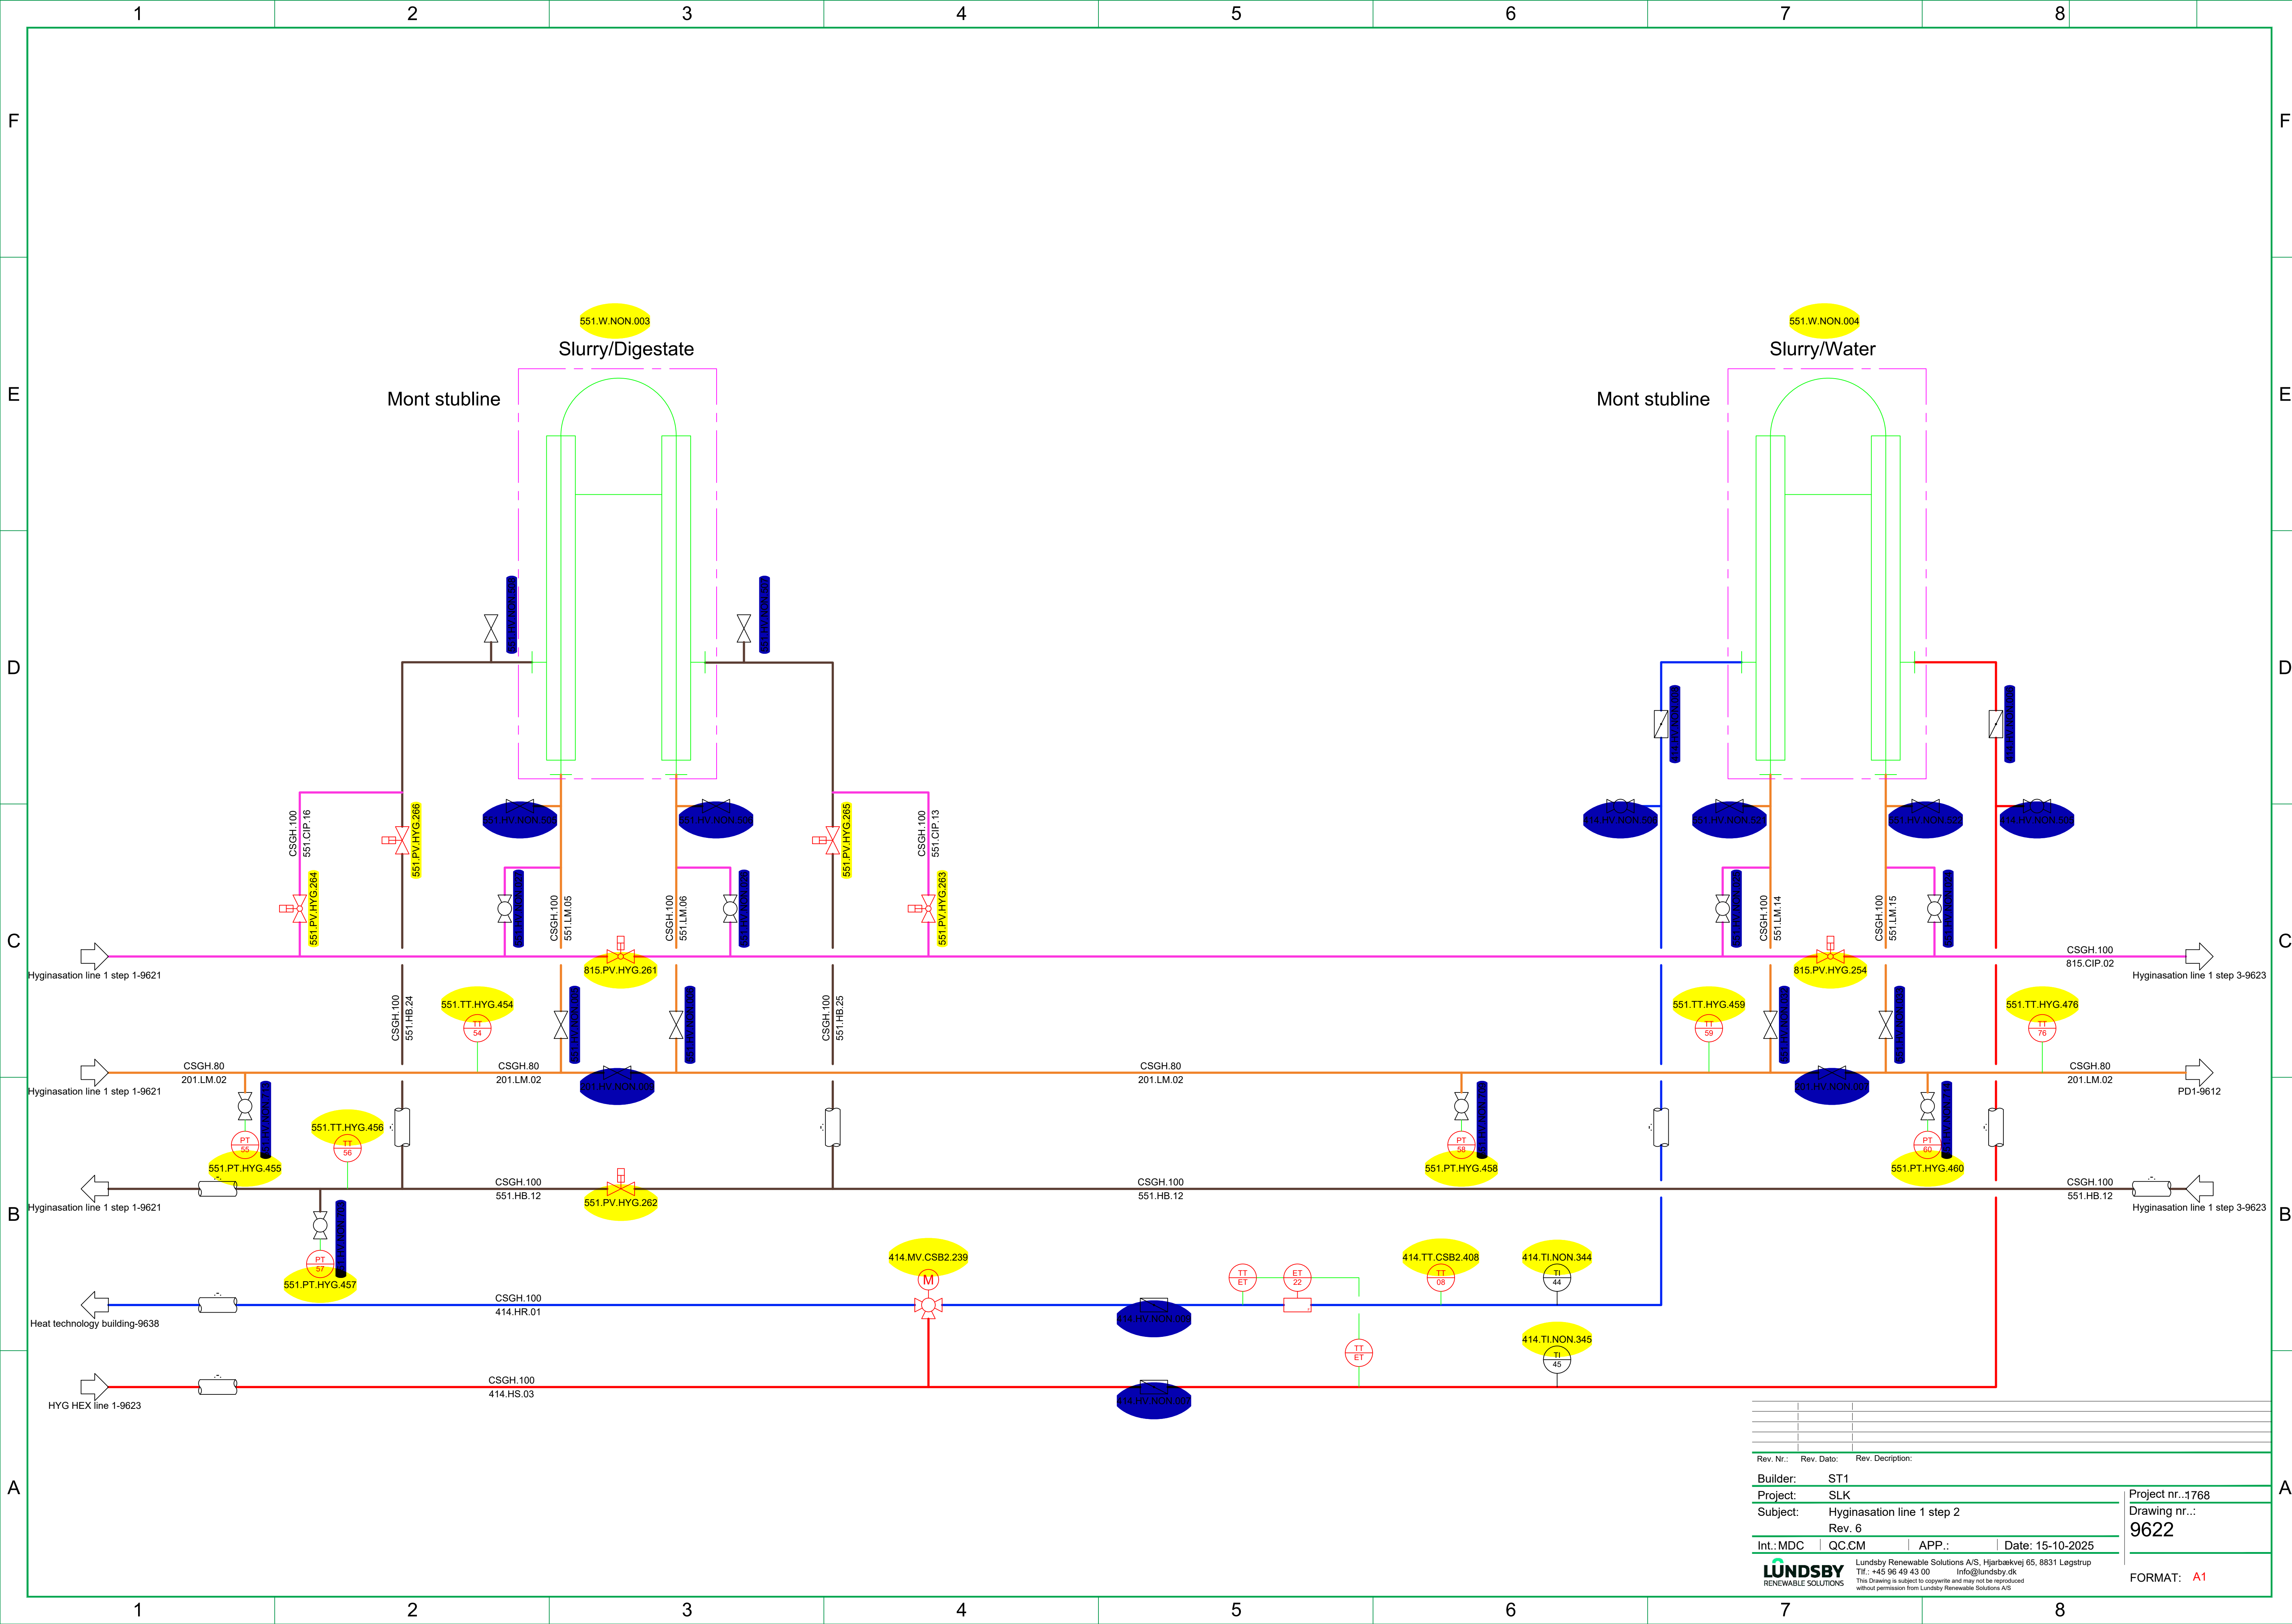

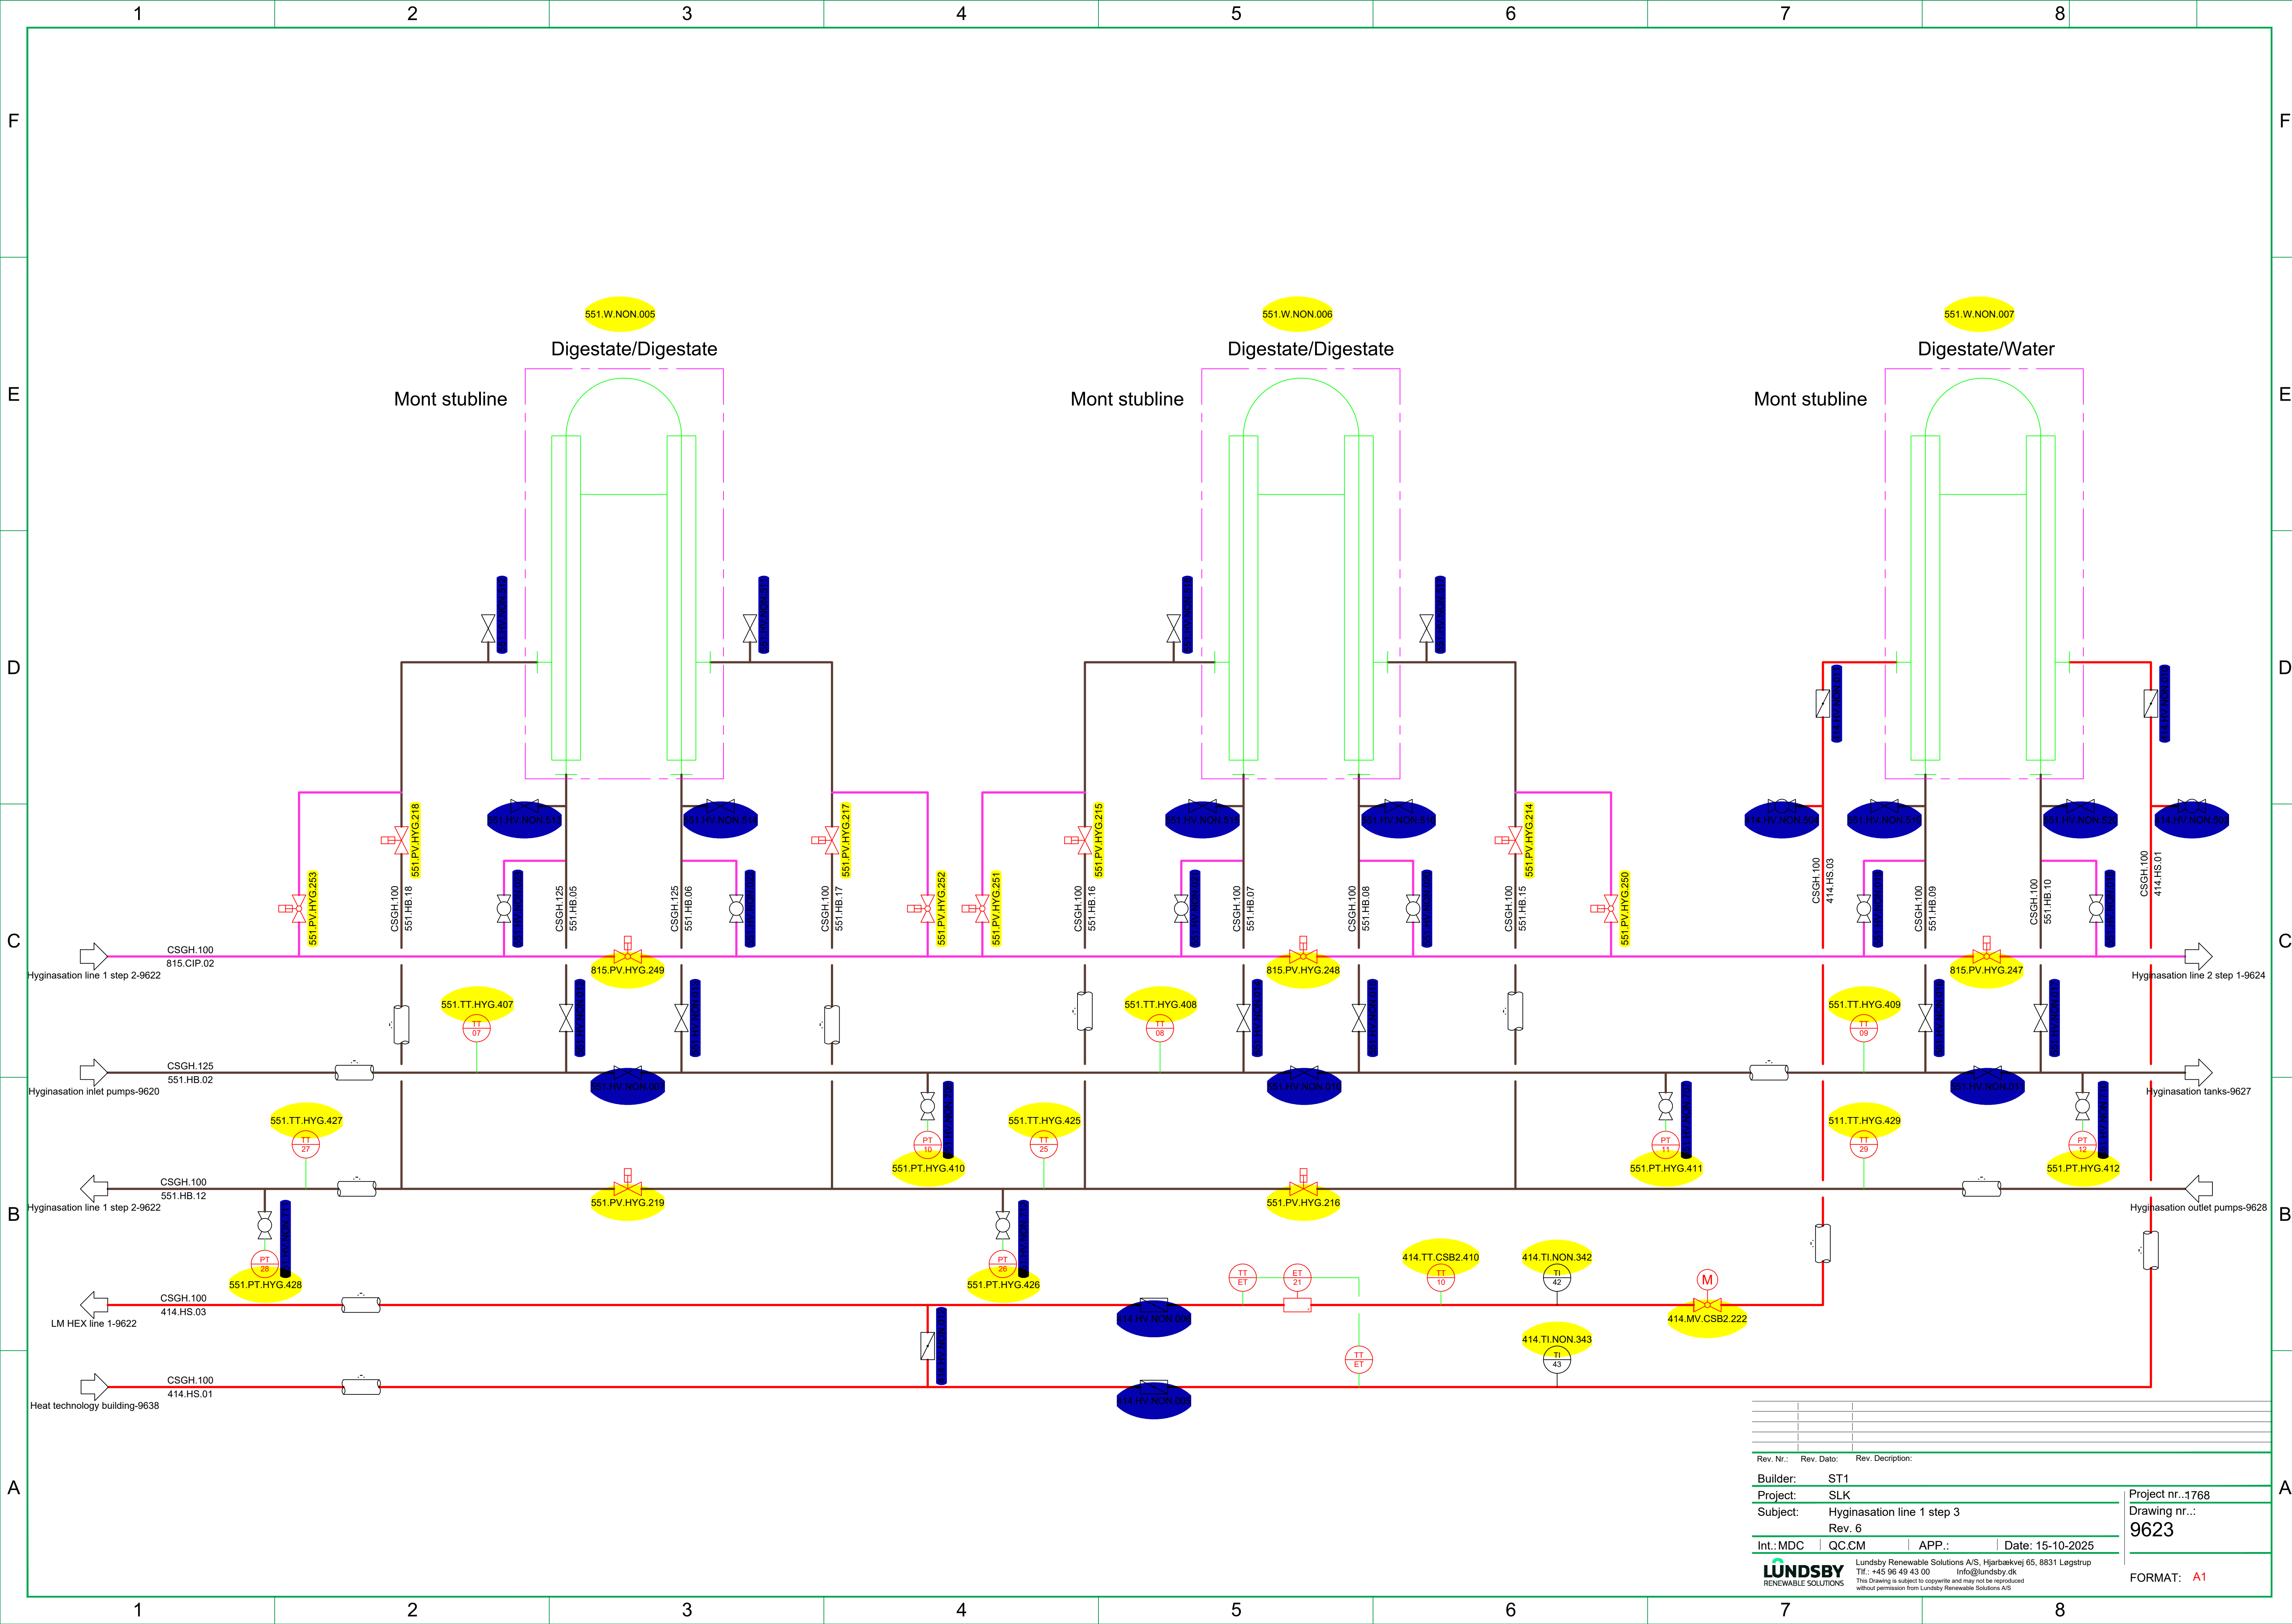


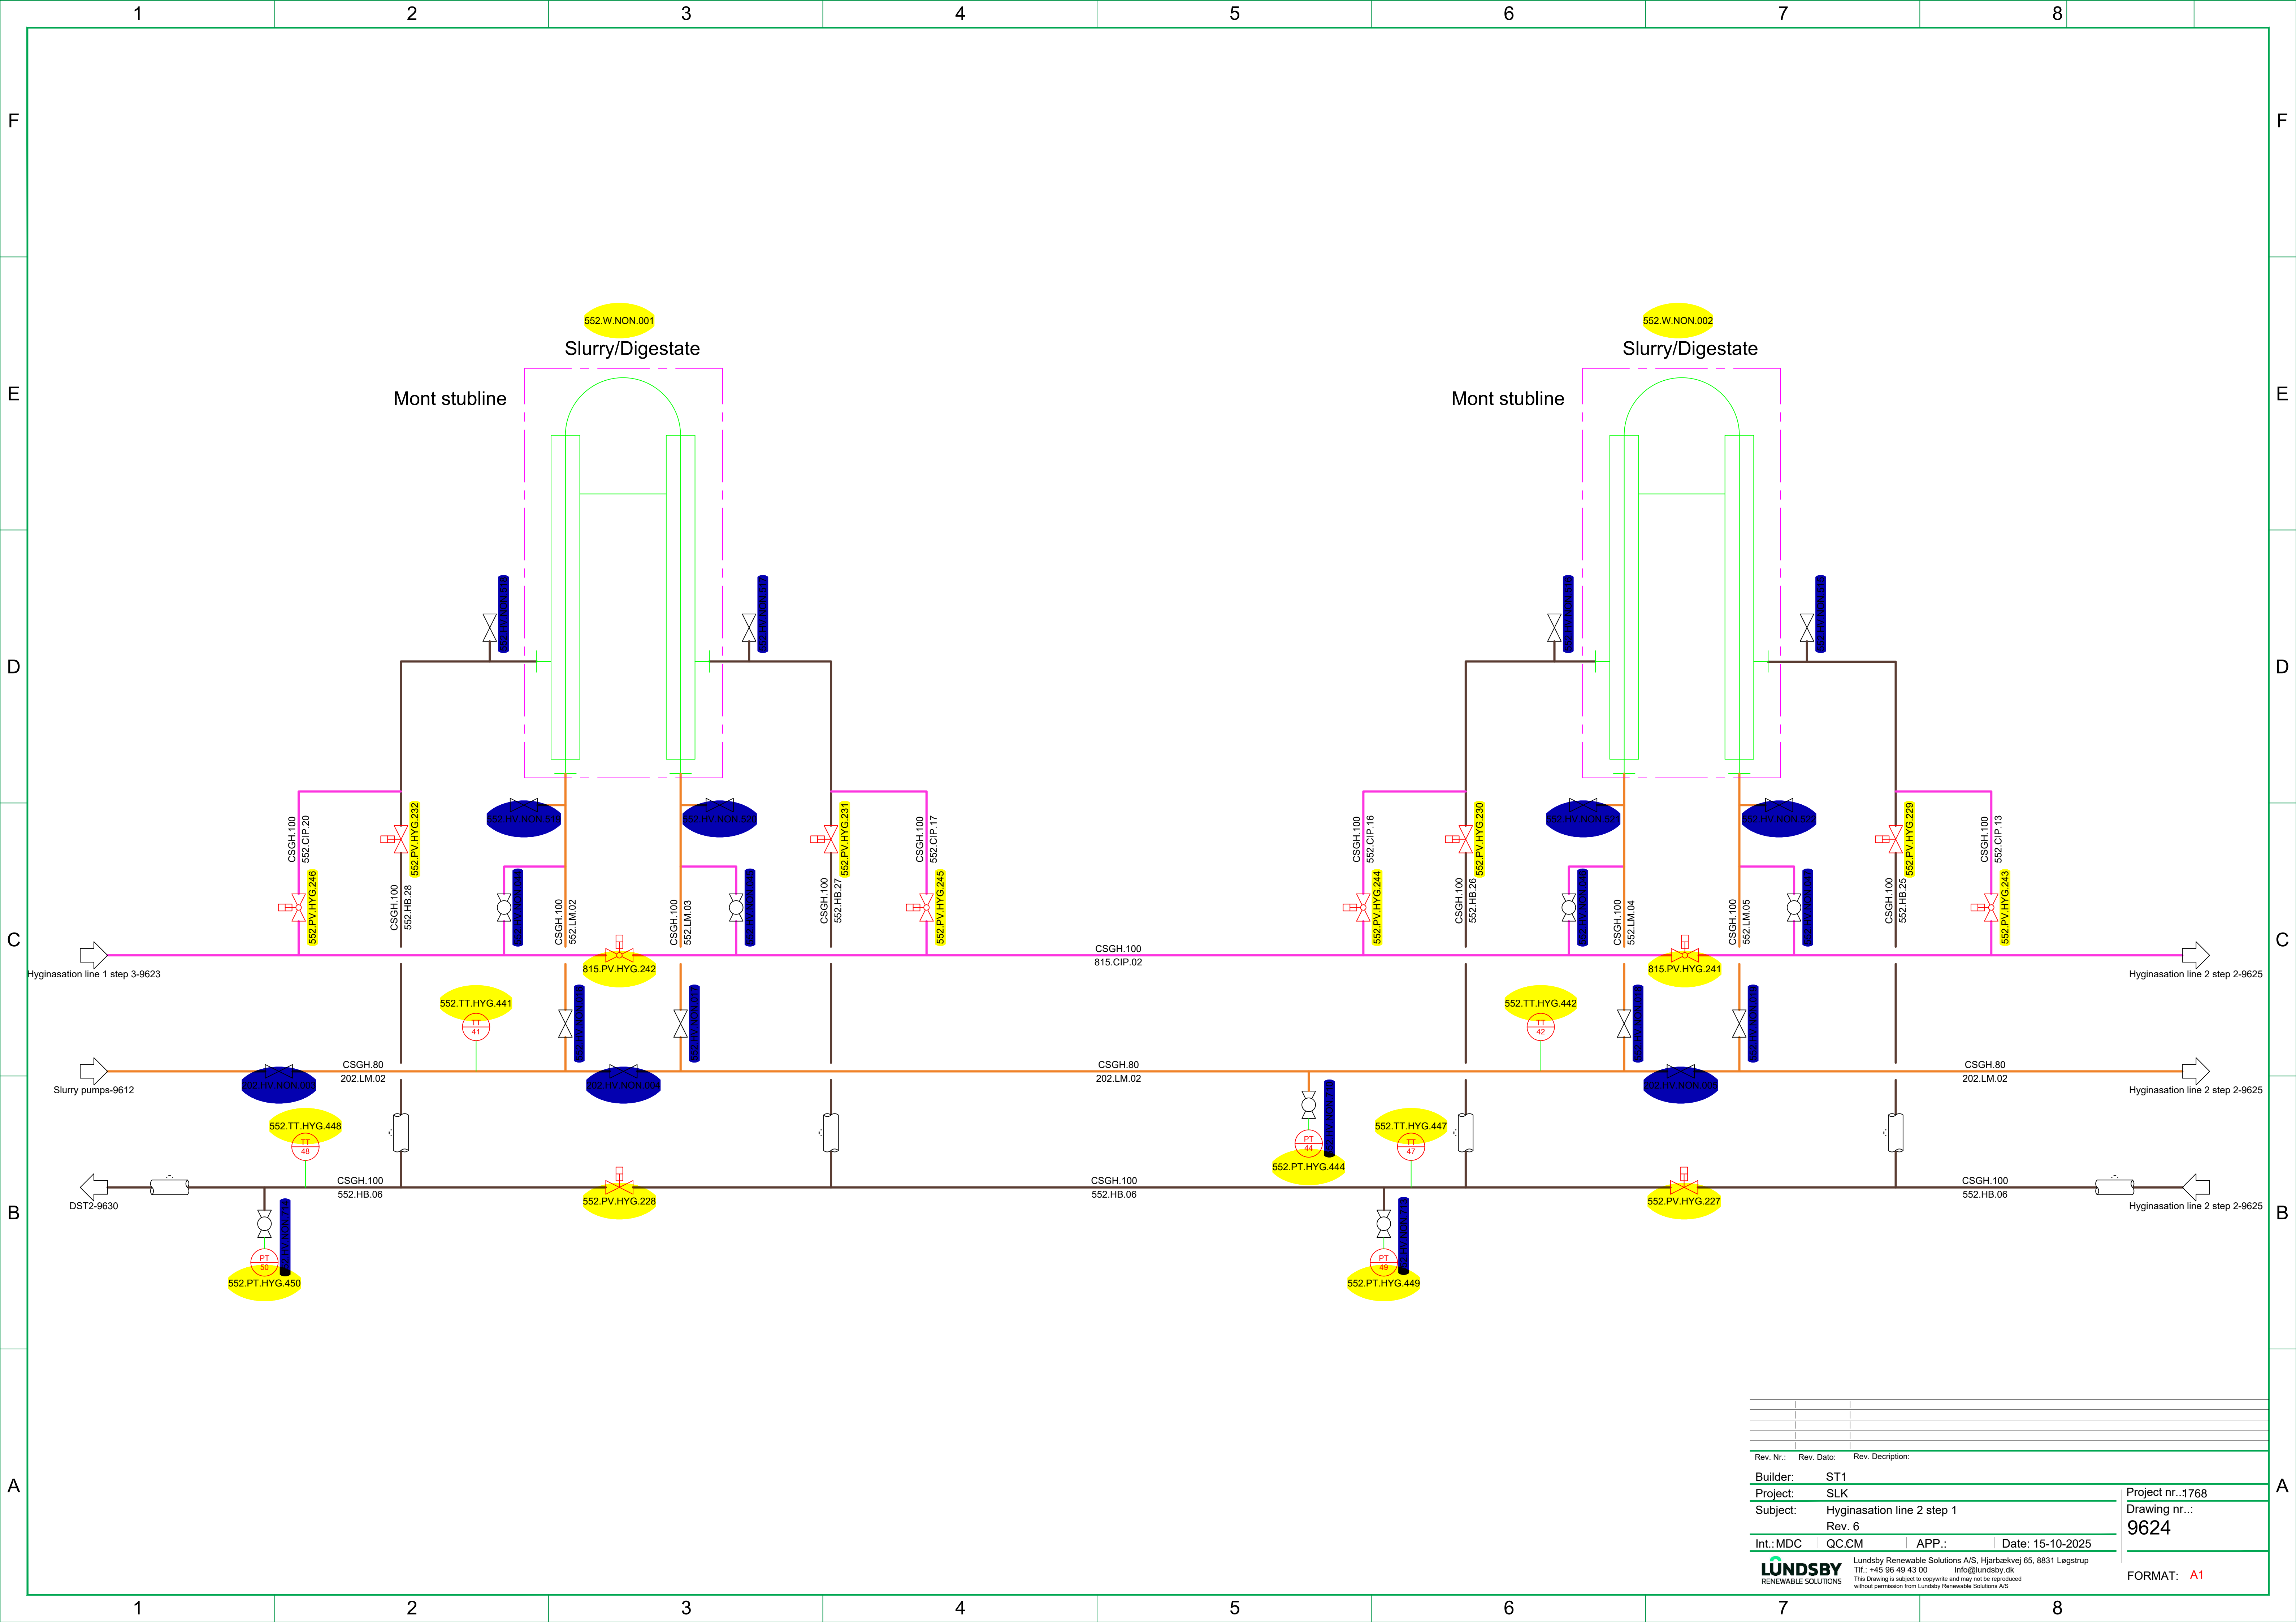


Rev. Nr.:	Rev. Dato:	Rev. Description:
Builder:	ST1	
Project:	SLK	
Subject:	Hyginasation line 2 step 1	
	Rev. 6	
Int.:MDC	QC:CM	APP.:
		Date: 15-10-2025
LUNDSBY RENEWABLE SOLUTIONS		
Lundsby Renewable Solutions A/S, Hjarbækvej 65, 8831 Løgstrup Tlf.: +45 96 49 43 00 Info@lundsby.dk This Drawing is subject to copyright and may not be reproduced without permission from Lundsby Renewable Solutions A/S		
Project nr.:1768 Drawing nr.: 9624		FORMAT: A1

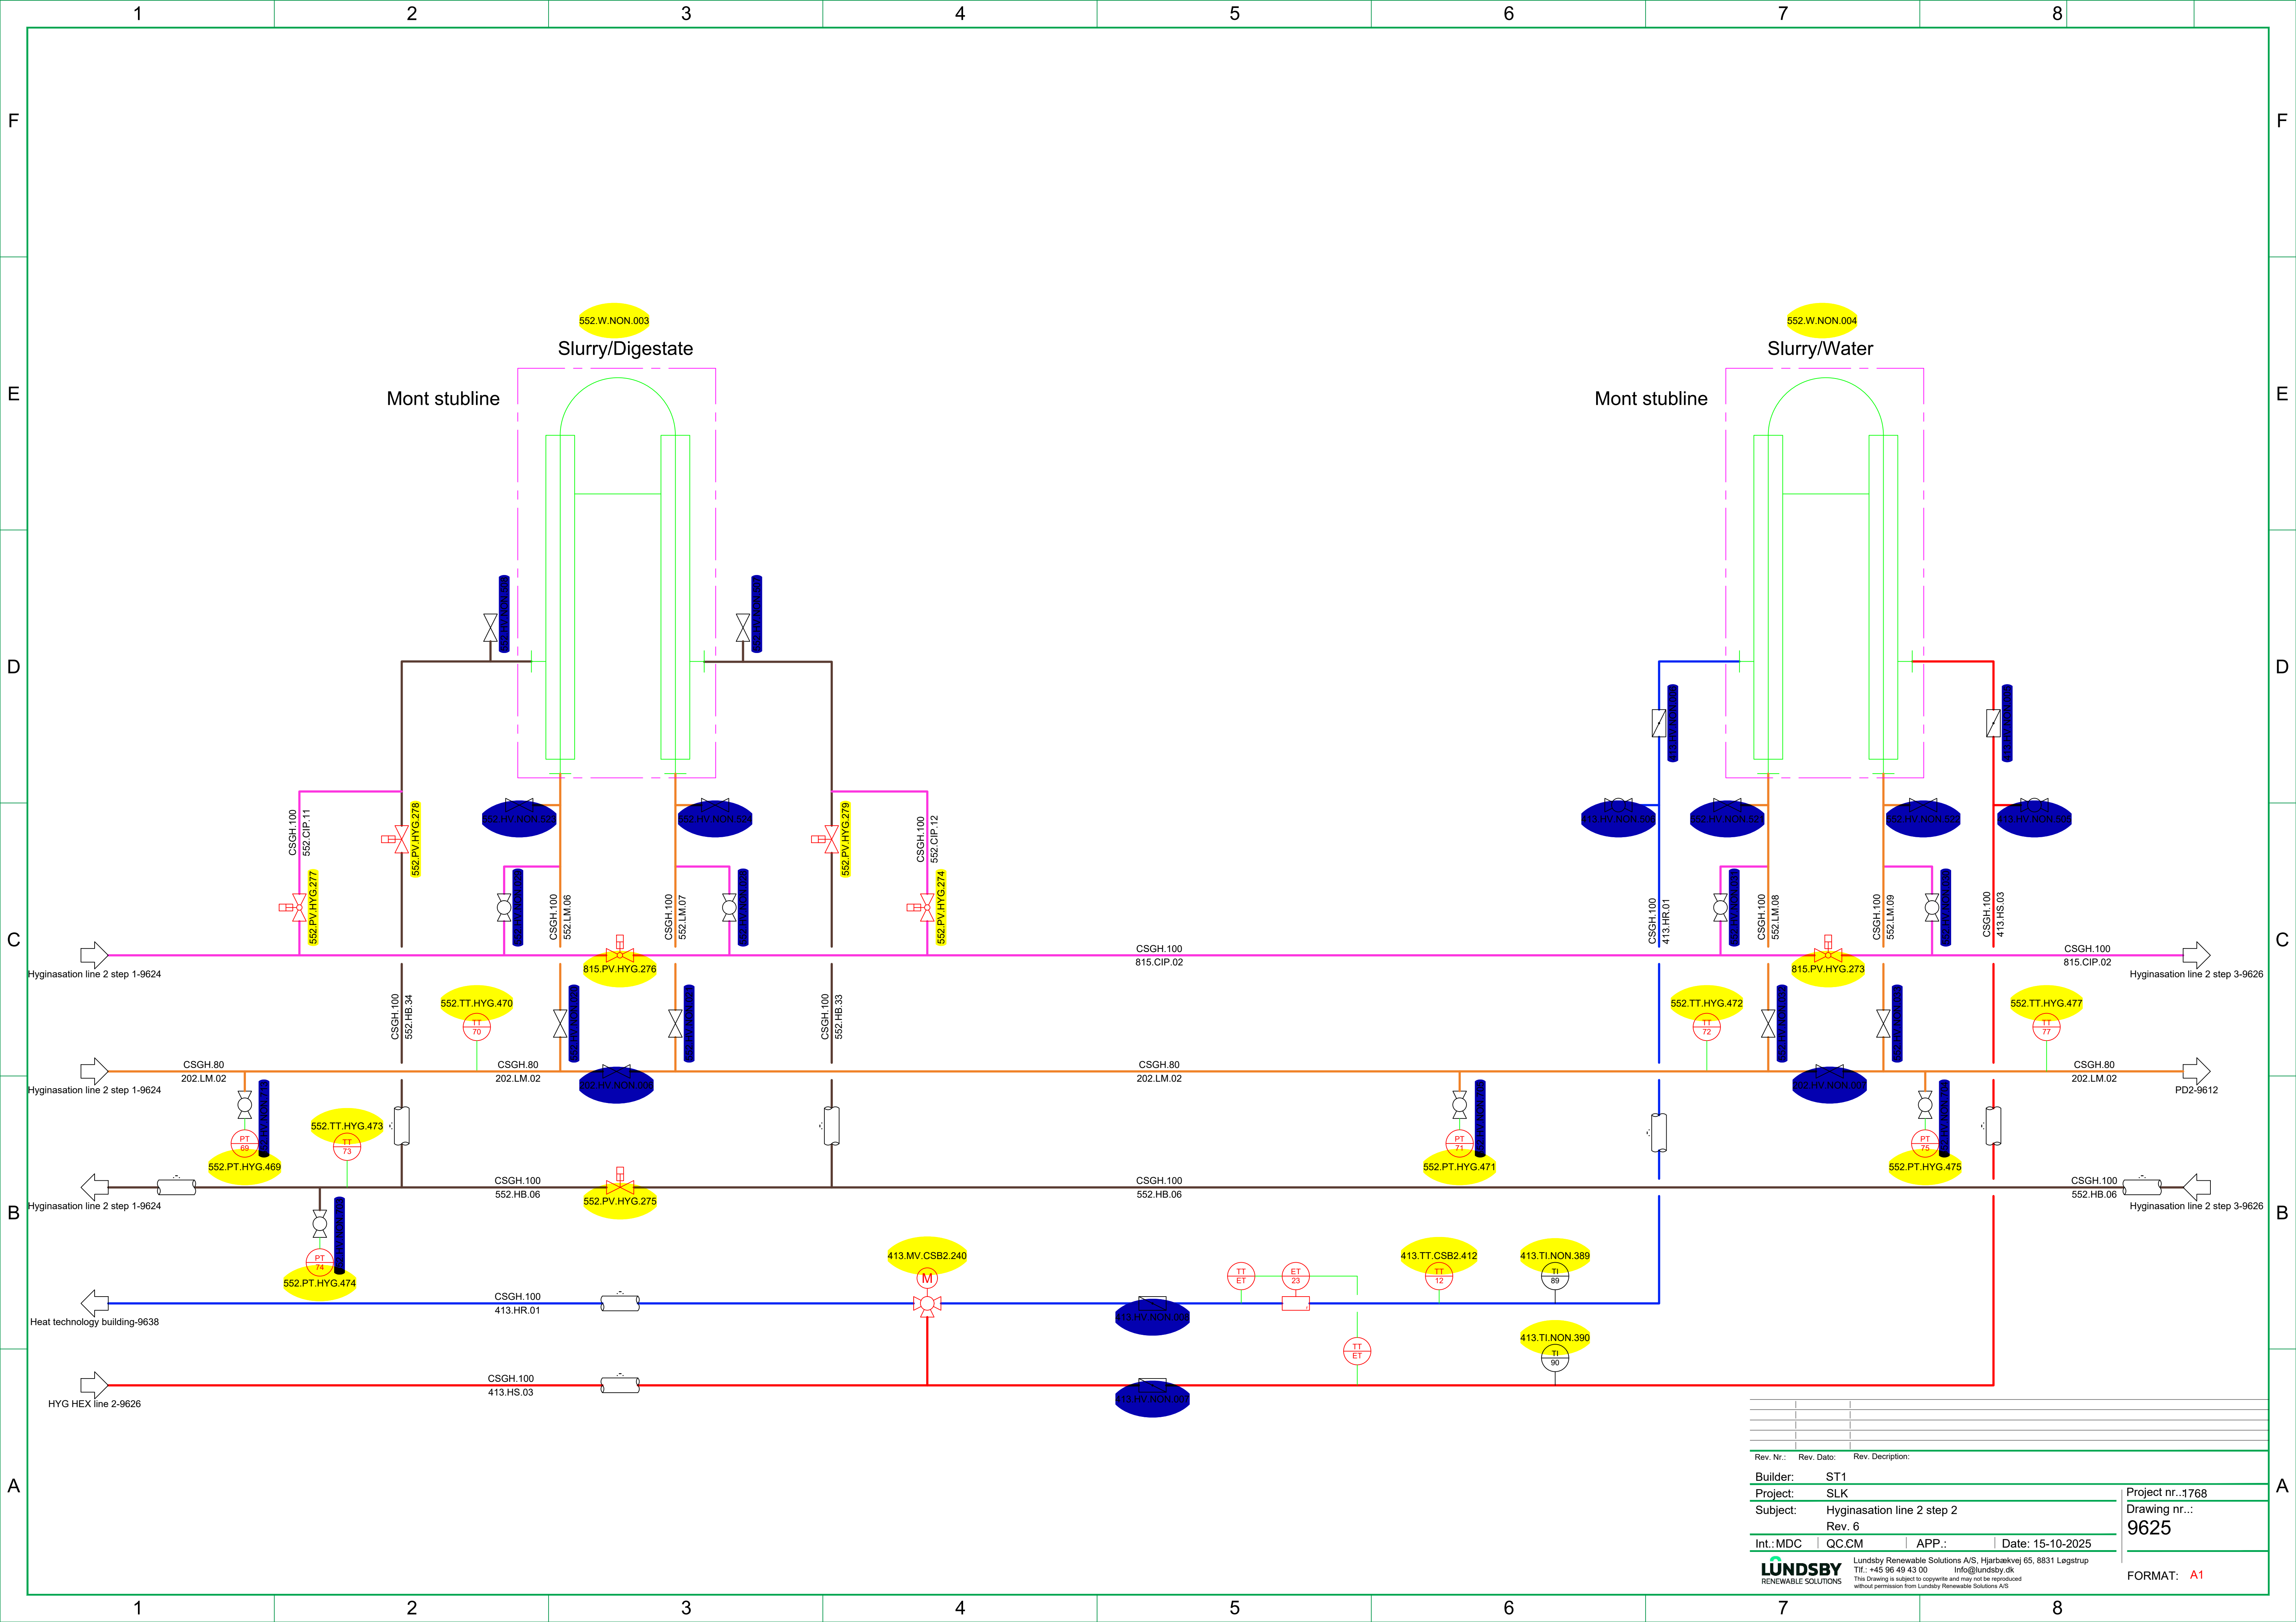

Rev. Nr.:	Rev. Dato:	Rev. Description:
Builder:	ST1	
Project:	SLK	
Subject:	Hyginasation line 2 step 2	
Rev. 6		
Int.:MDC	QC:CM	APP.:
Date:	15-10-2025	
LUNDSBY RENEWABLE SOLUTIONS		
Lundsby Renewable Solutions A/S, Hjarbækvej 65, 8831 Lægstrup Tlf.: +45 96 49 43 00 Info@lundsby.dk This drawing is subject to copyright and may not be reproduced without permission from Lundsby Renewable Solutions A/S		
Project nr.:1768 Drawing nr.: 9625		FORMAT: A1

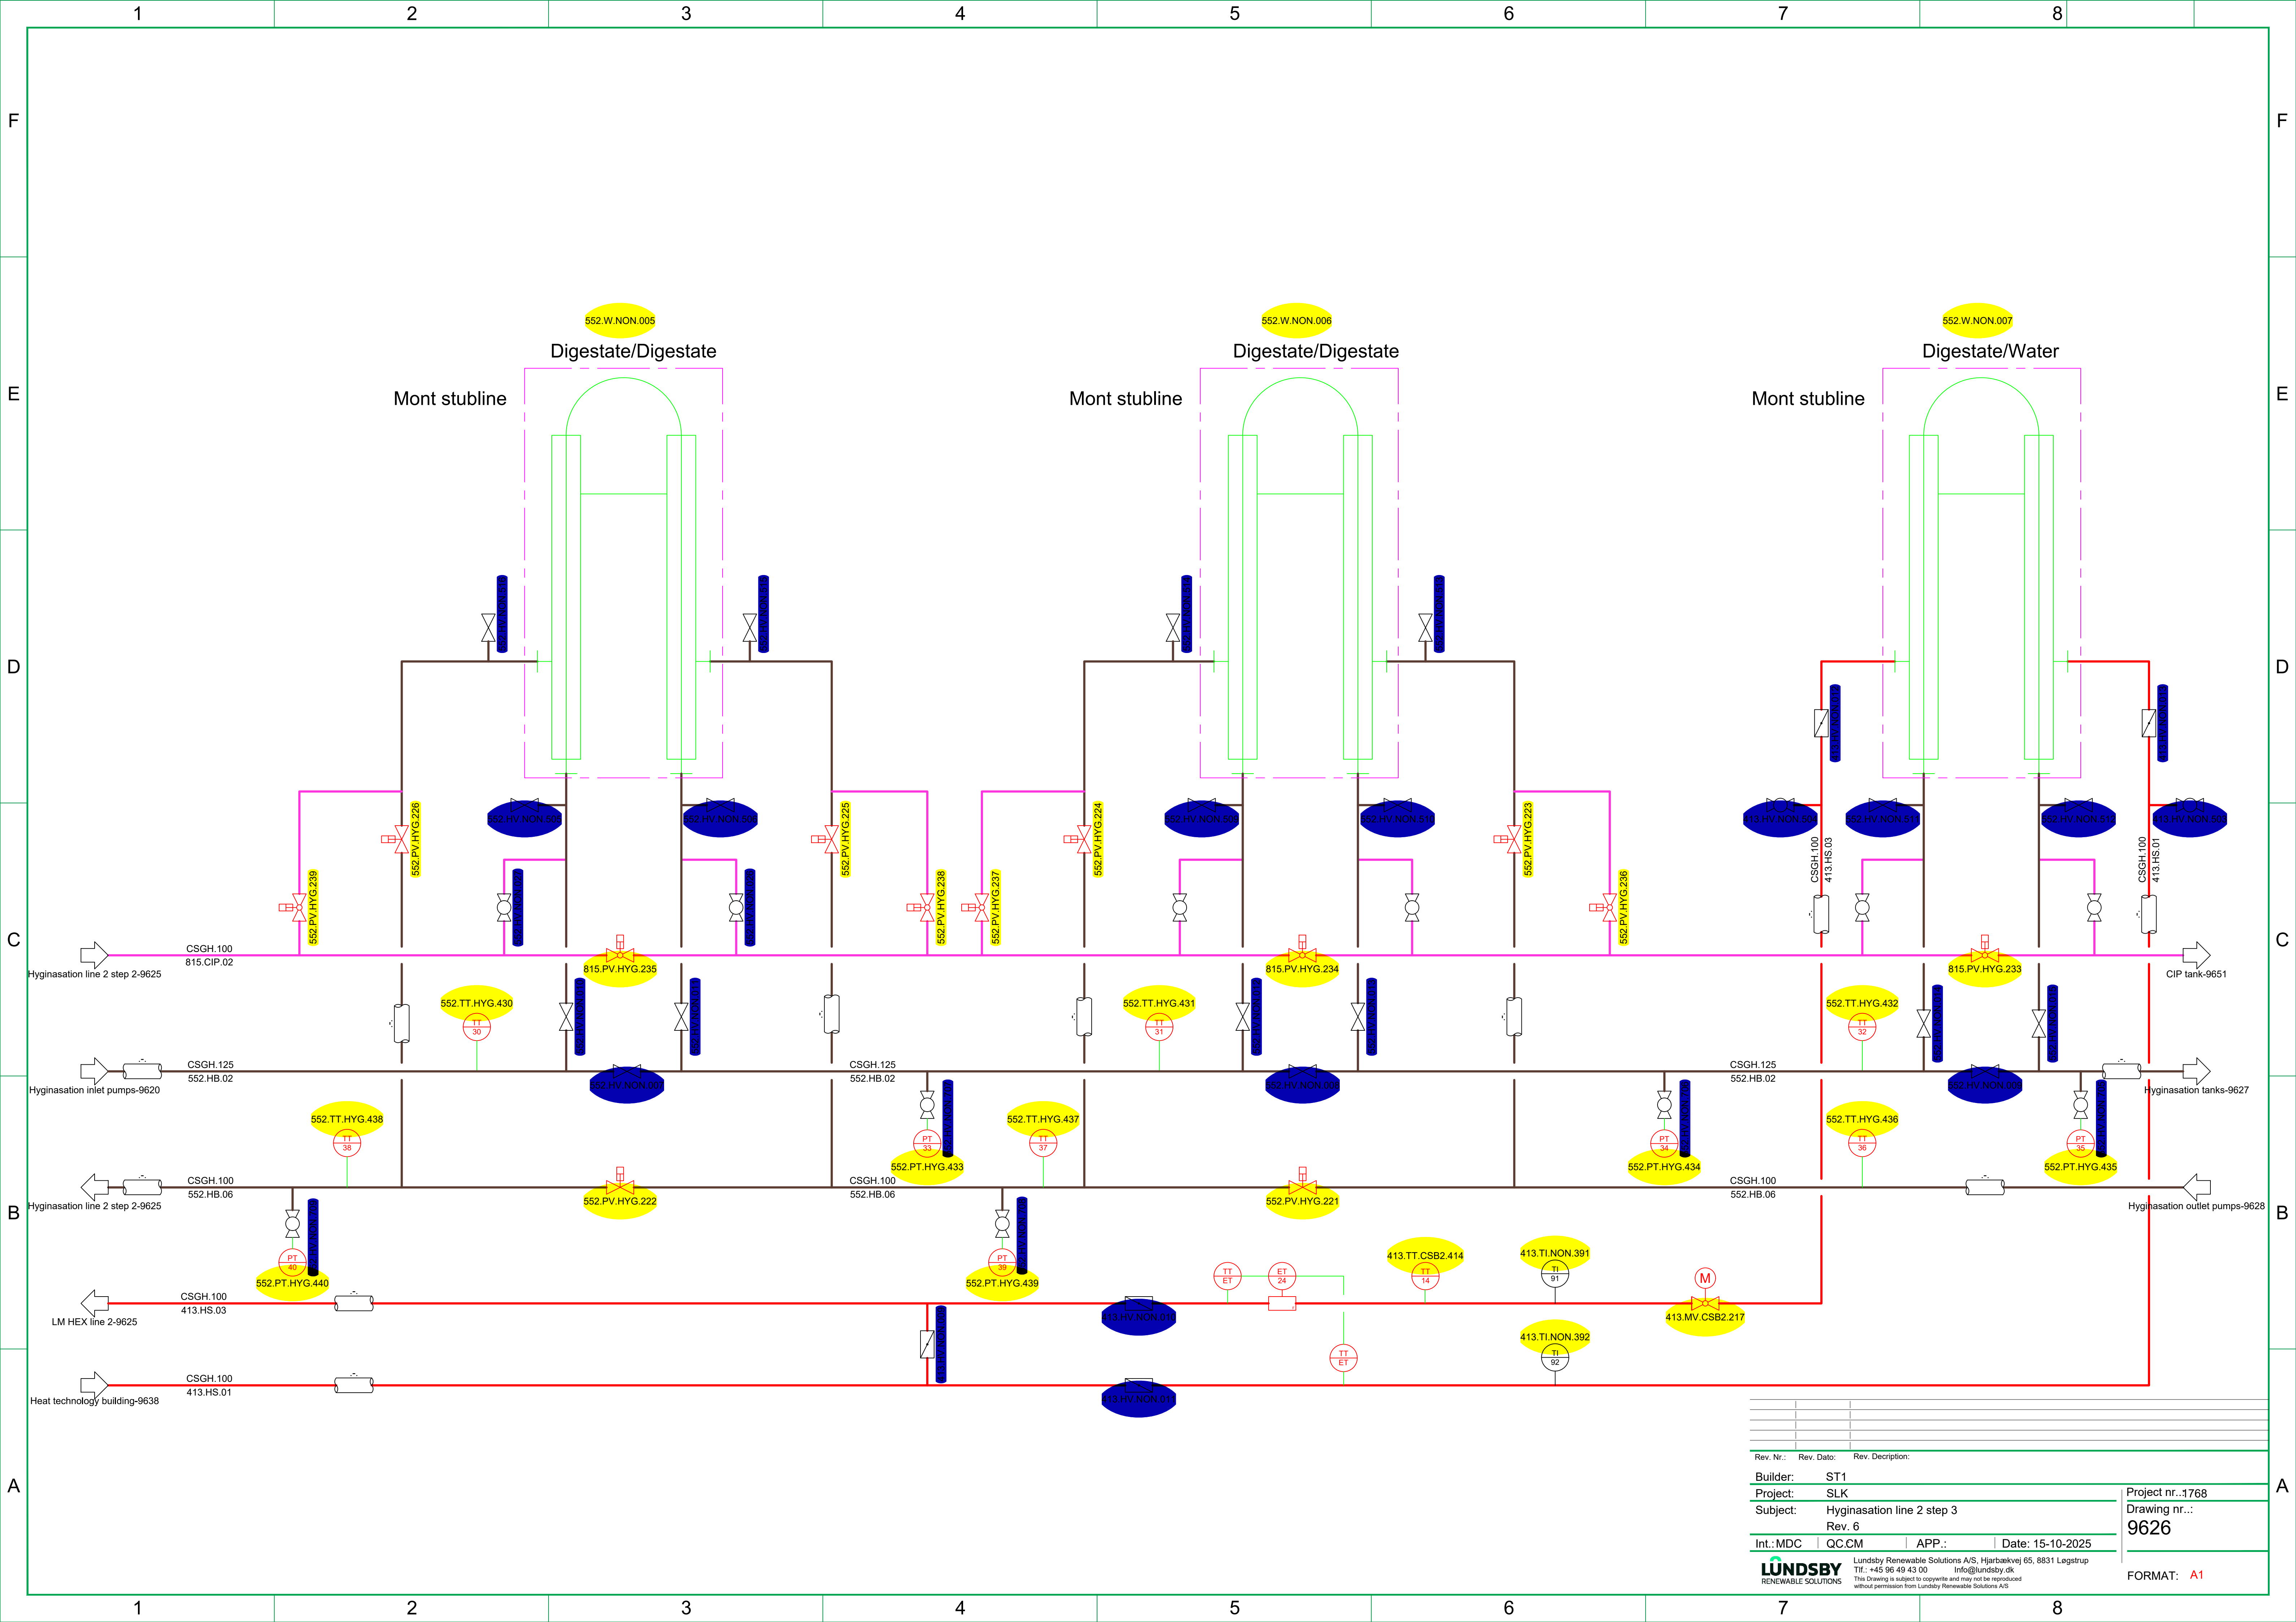


Rev. Nr.:	Rev. Dato:	Rev. Description:
Builder:	ST1	
Project:	SLK	
Subject:	Hyginasation line 2 step 3	
Rev. 6		
Int.: MDC	QC: CM	APP.: Date: 15-10-2025
LUNDSBY RENEWABLE SOLUTIONS		
Lundsby Renewable Solutions A/S, Hjarbrækvej 65, 8831 Lægstrup Tlf.: +45 96 49 43 00 Info@lundsby.dk This Drawing is subject to copyright and may not be reproduced without permission from Lundsby Renewable Solutions A/S		
Project nr.: 1768 Drawing nr.: 9626		FORMAT: A1

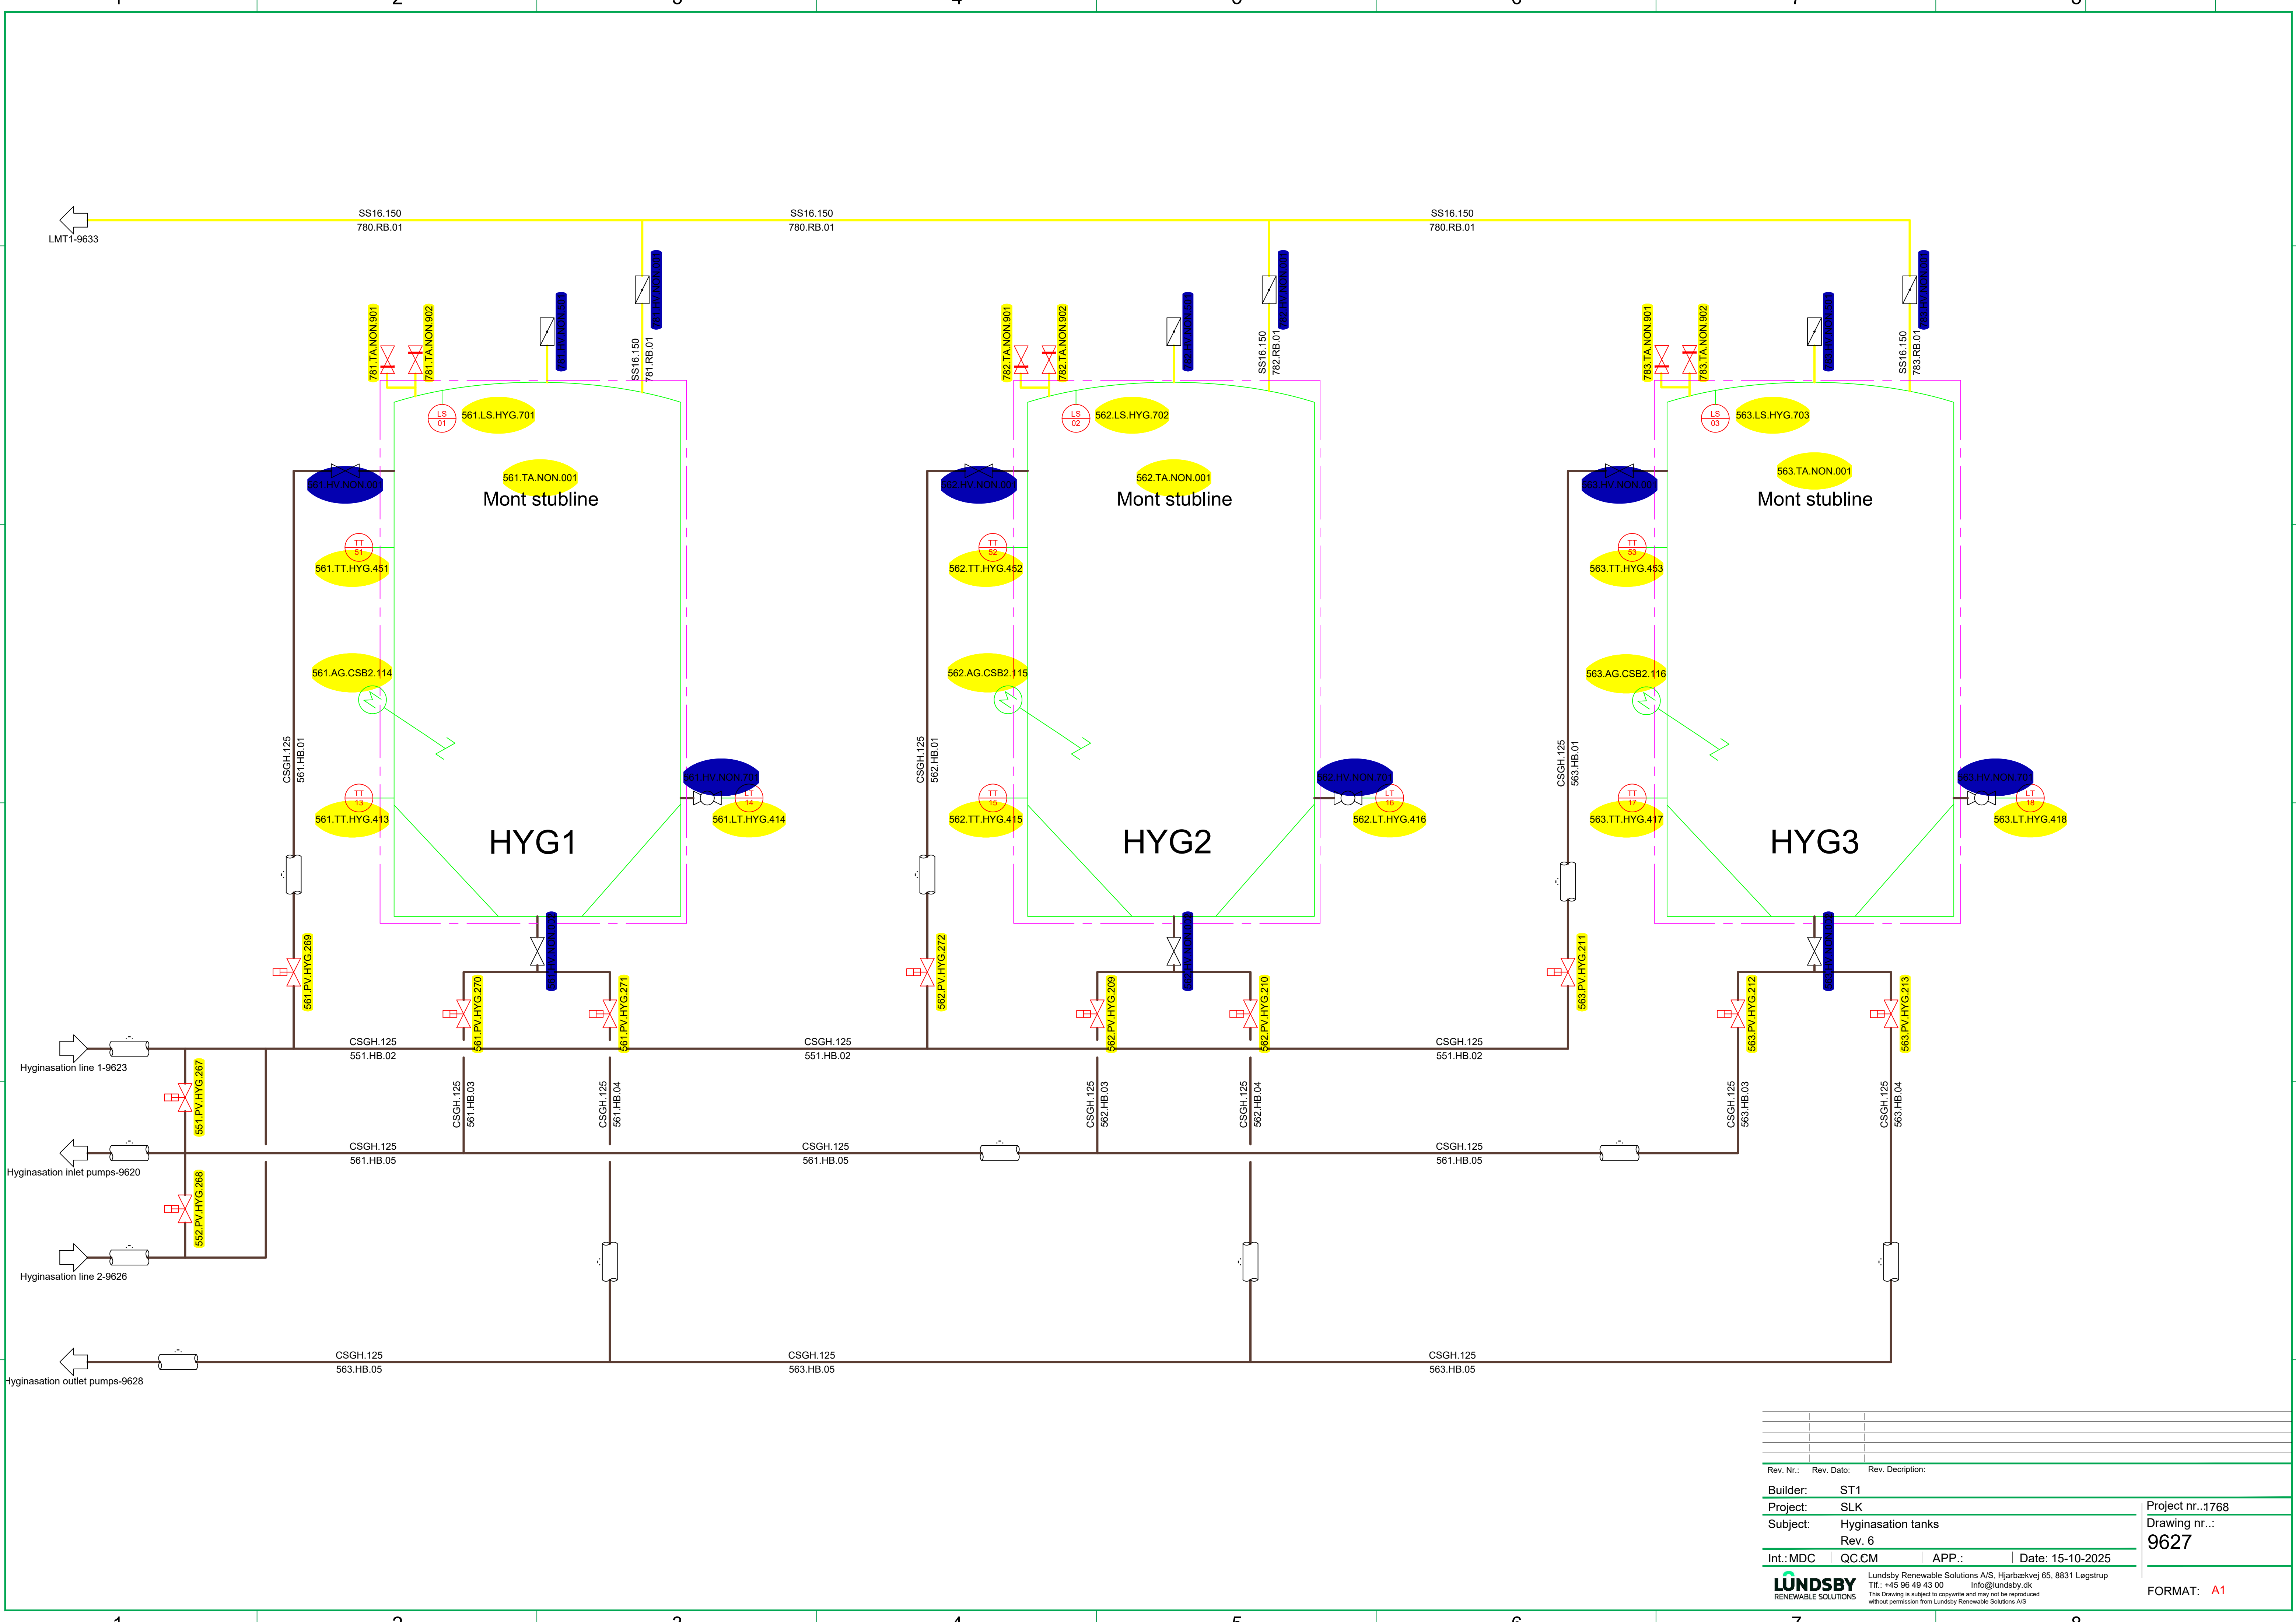

Rev. Nr.:	Rev. Dato:	Rev. Description:	
Builder:	ST1		
Project:	SLK		
Subject:	Hyginasation tanks		
	Rev. 6		
Int.:MDC	QC.CM	APP.:	Date: 15-10-2025
LUNDSBY RENEWABLE SOLUTIONS			Lundsby Renewable Solutions A/S, Hjarbrækvej 65, 8831 Løgstrup Tlf.: +45 96 49 43 00 info@lundsby.dk This Drawing is subject to copyright and may not be reproduced without permission from Lundsby Renewable Solutions A/S
			Project nr.:1768 Drawing nr.: 9627
			FORMAT: A1

Tech Building

Outlet pumps

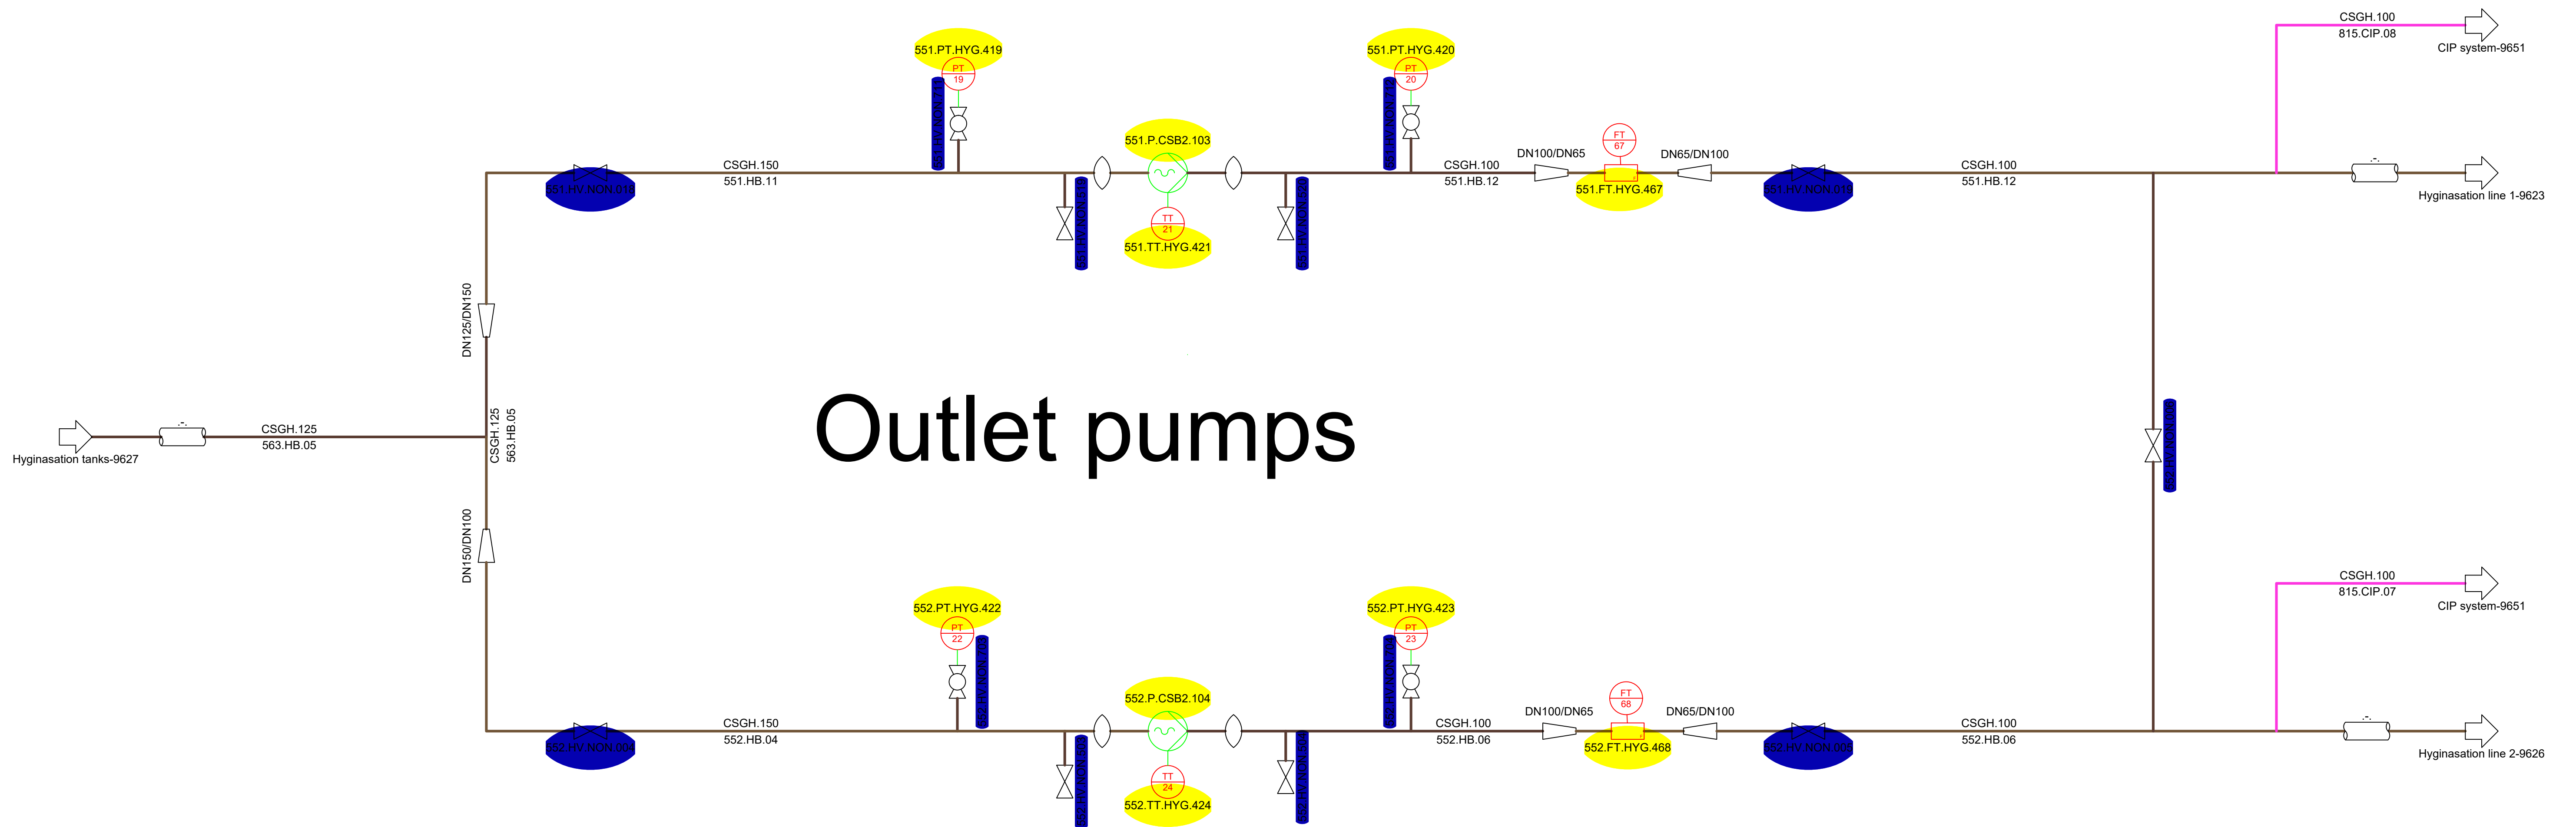

Rev. Nr.: _____
Rev. Dato: _____
Rev. Description: _____

BUILDER: ST1

PJECT: SLK

SUBJECT: Hyginasation outlet pumps

 Rev. 6

Project nr...1768


Drawing nr.:
9628

Intr.: MDC | QC.CM | APP..
Date: 15-10-2025


Lundsby Renewable Solutions A/S, Hjarbækvej 65, 8831 Legstrup
Tlf.: +45 96 49 43 00 info@lundsby.dk

This Drawing is subject to copyright and may not be reproduced without permission from Lundsbys Renewable Solution as.


FORMAT: A1

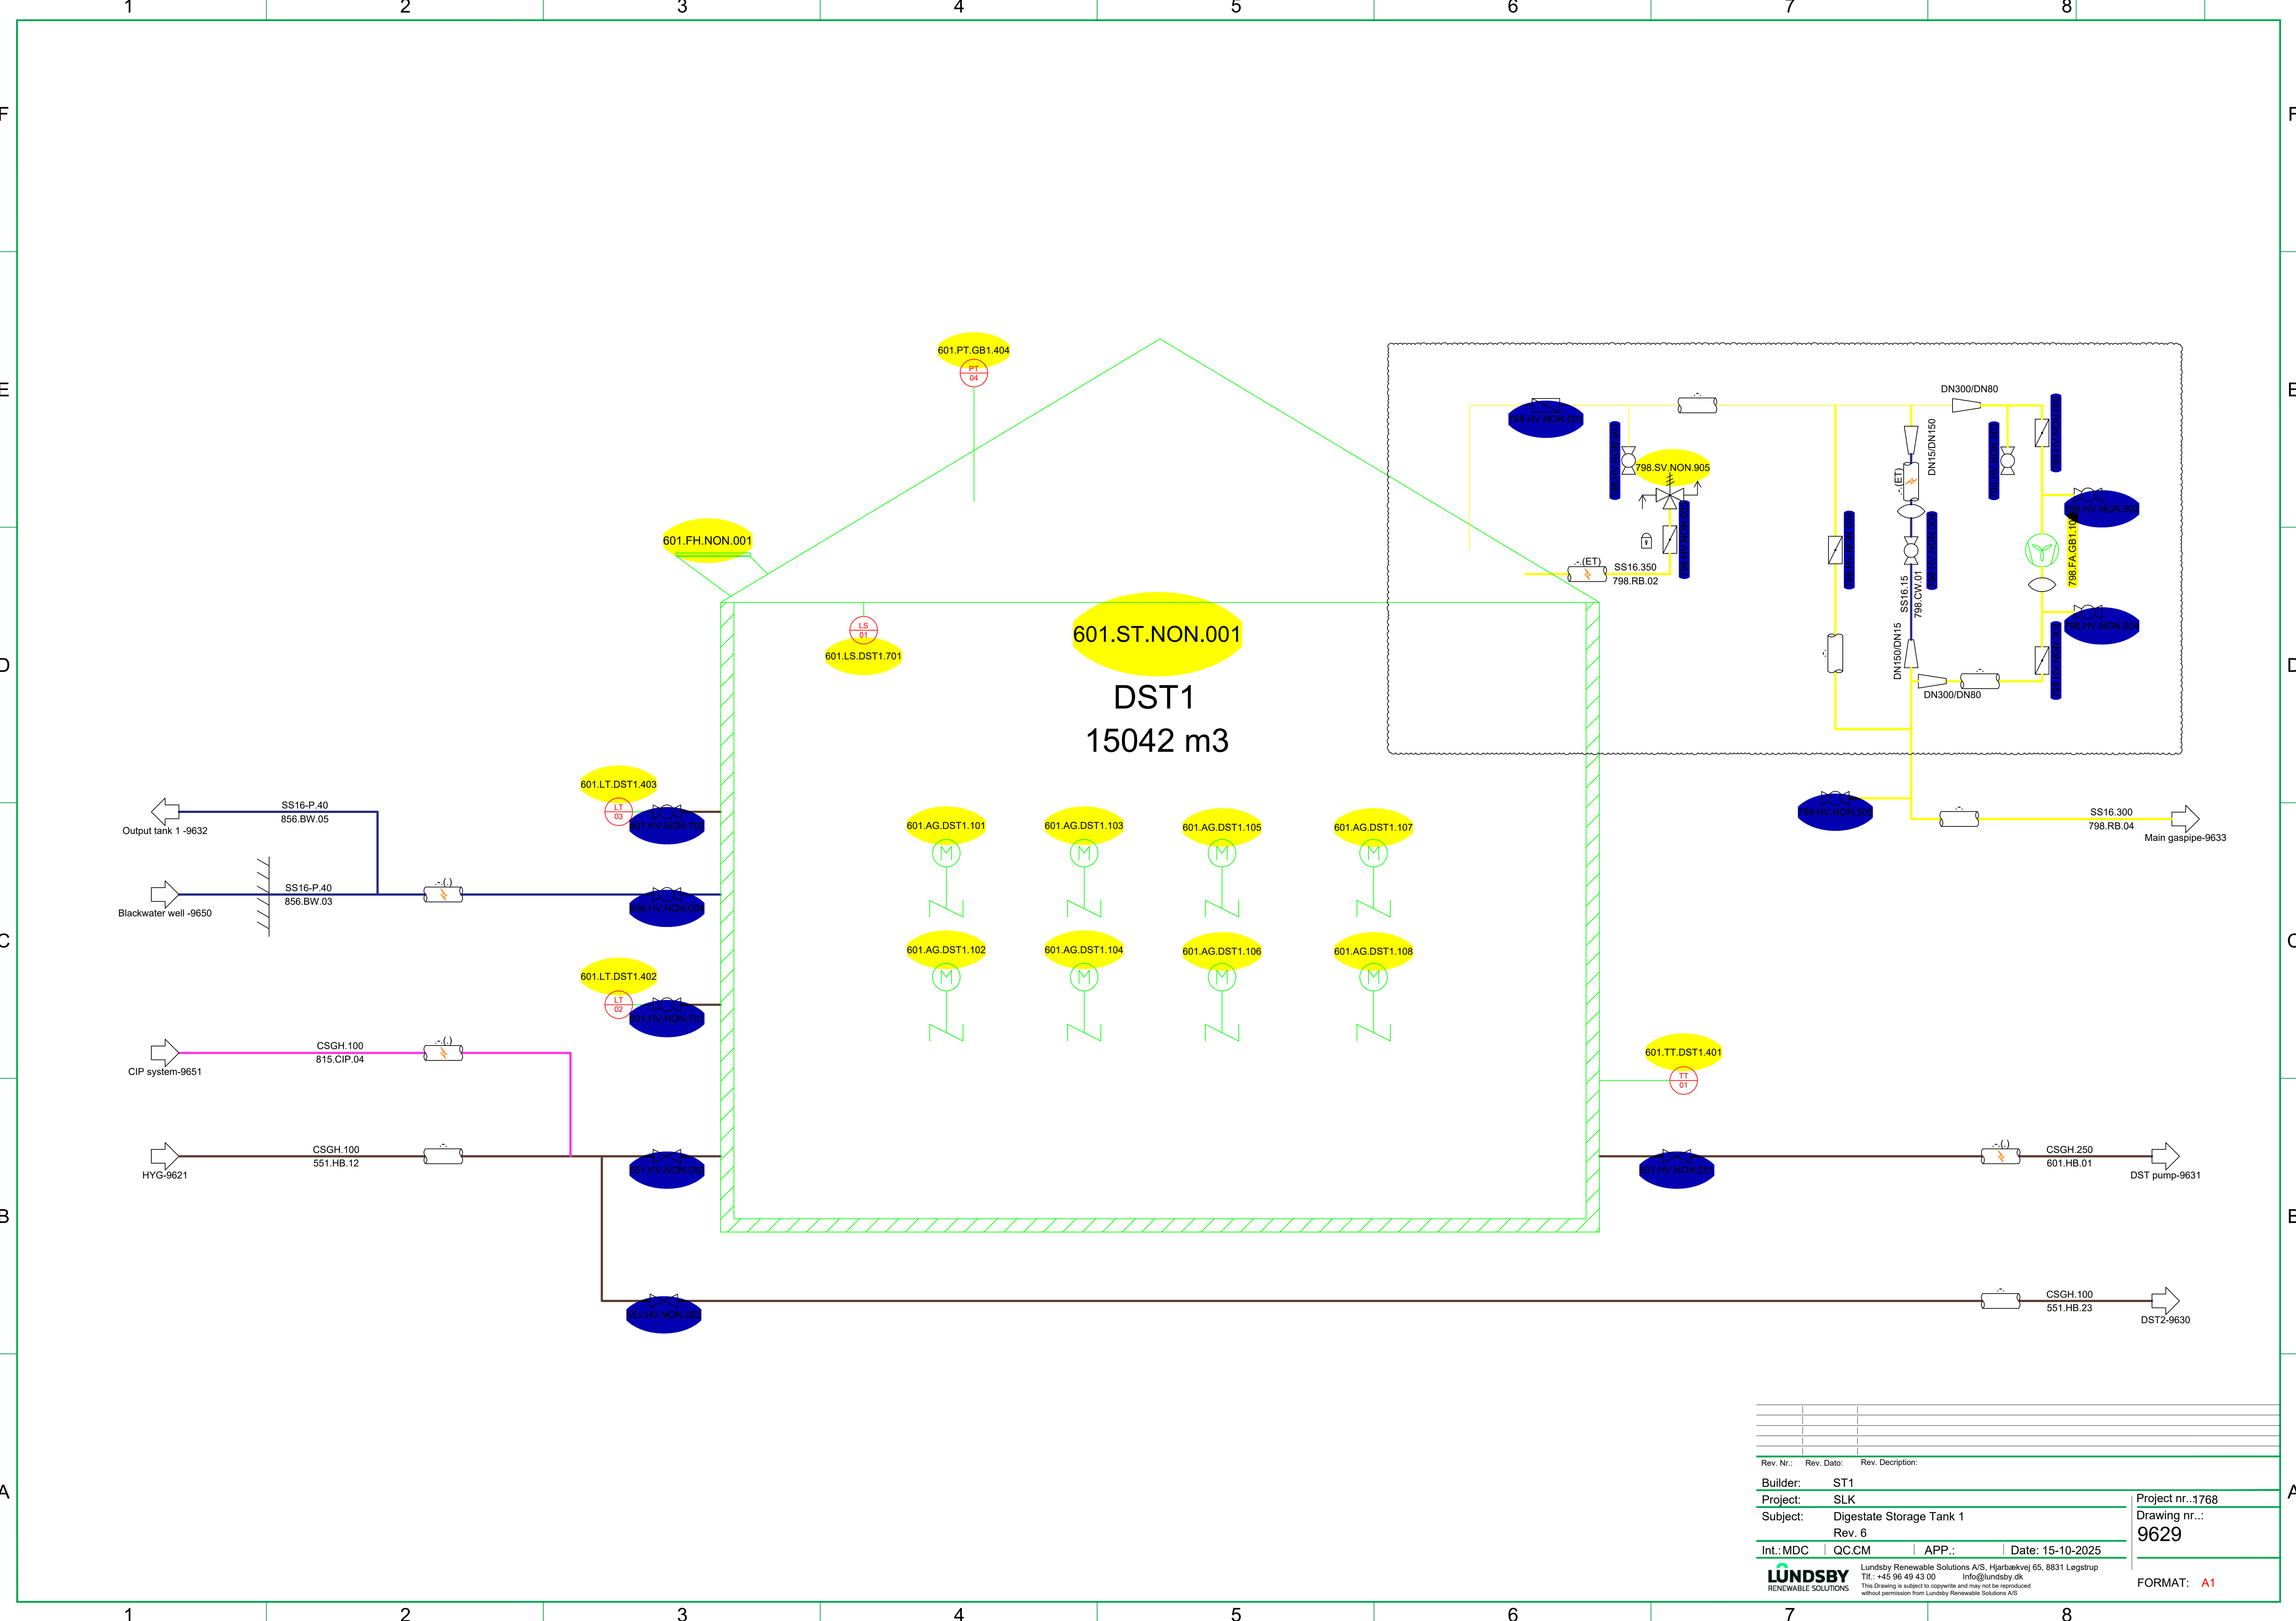


Rev. Nr.:	Rev. Dato:	Rev. Description:	
Builder:	ST1		
Project:	SLK		
Subject:	Digestate Storage Tank 1		
	Rev. 6		
Int.:MDC	QC:CM	APP.:	Date: 15-10-2025
LUNDSBY RENEWABLE SOLUTIONS			Lundsby Renewable Solutions A/S, Hjarbækvej 65, 8831 Løgstrup Tlf.: +45 96 49 43 00 Info@lundsby.dk This drawing is subject to copyright and may not be reproduced without permission from Lundsby Renewable Solutions A/S
Project nr.:1768 Drawing nr.: 9629			FORMAT: A1

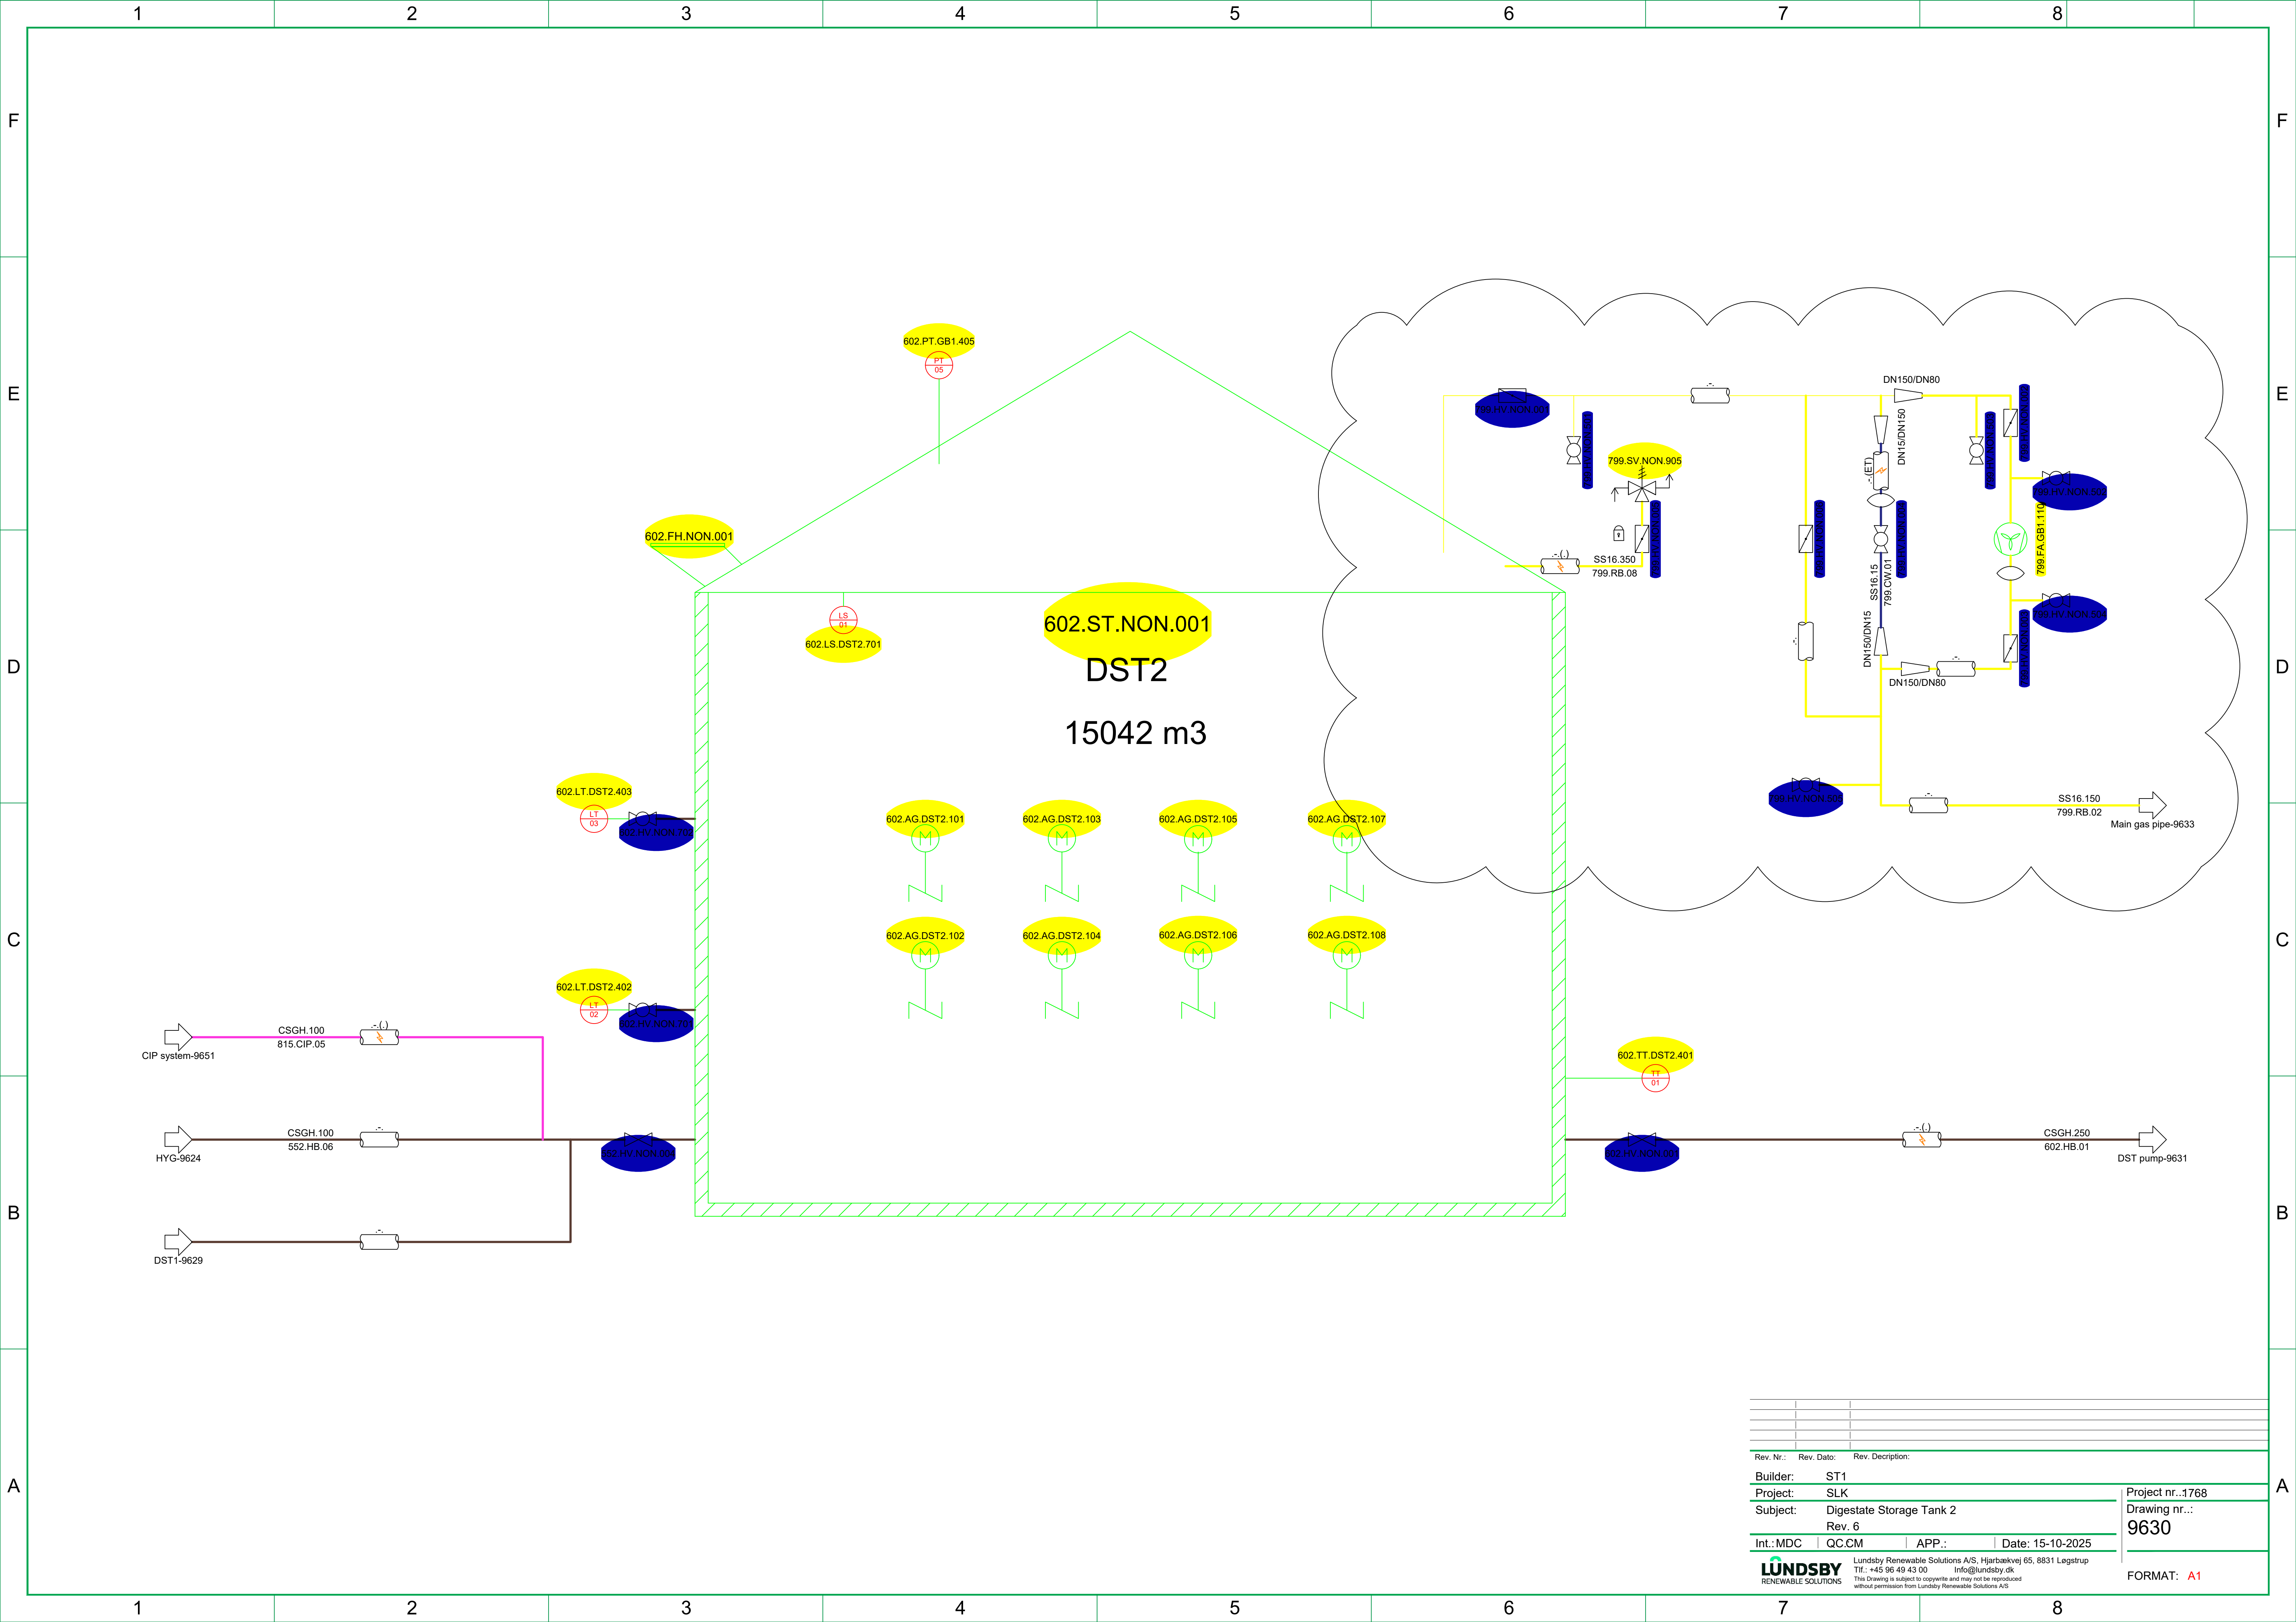


Rev. Nr.:	Rev. Dato:	Rev. Description:	
Builder:	ST1		
Project:	SLK		
Subject:	Digestate Storage Tank 2		
	Rev. 6		
Int.:MDC	QC:CM	APP.:	Date: 15-10-2025
LUNDSBY RENEWABLE SOLUTIONS			Lundsby Renewable Solutions A/S, Hjarbrækvej 65, 8831 Løgstrup Tlf.: +45 96 49 43 00 Info@lundsby.dk This Drawing is subject to copyright and may not be reproduced without permission from Lundsby Renewable Solutions A/S
Project nr.:1768 Drawing nr.: 9630			FORMAT: A1

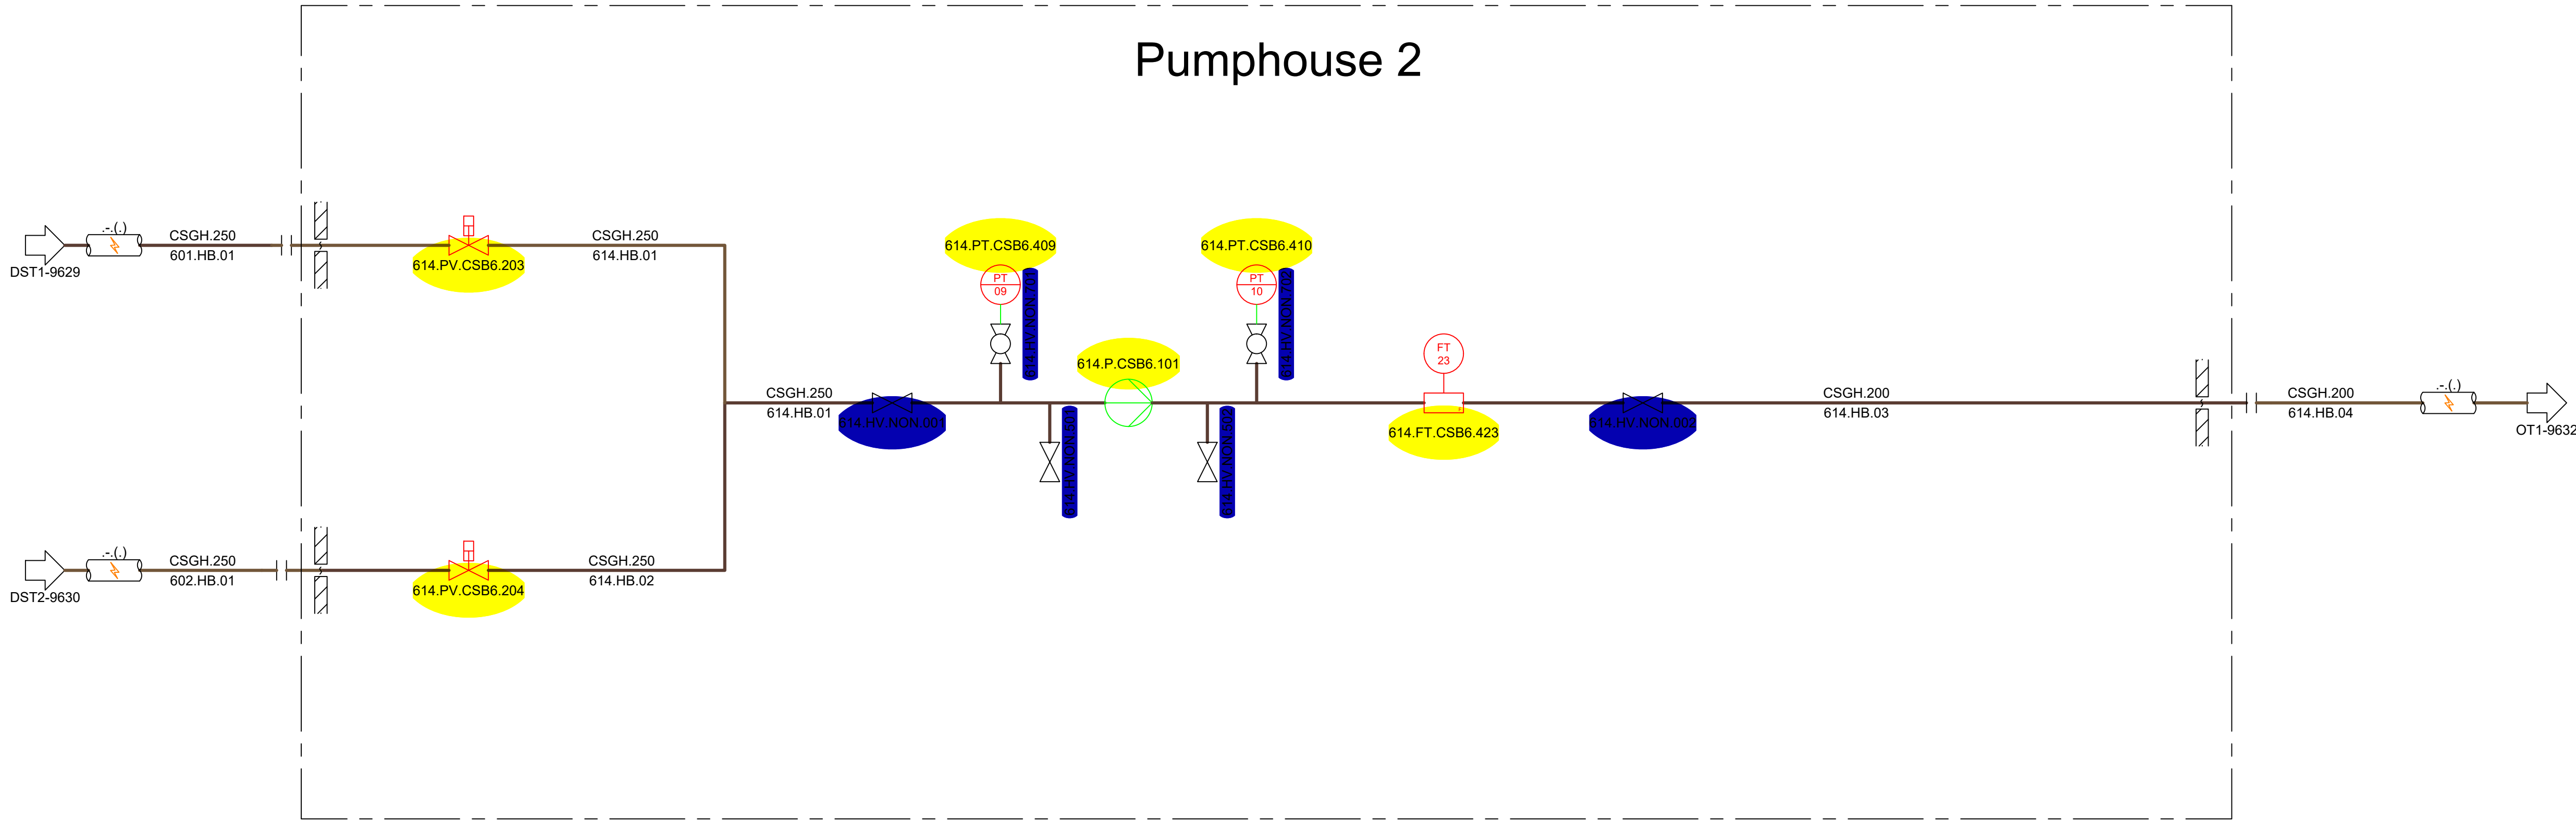


Rev. Nr.:	Rev. Dato:	Rev. Description:	
Builder:	ST1		
Project:	SLK		
Subject:	DST pump		
	Rev. 6		
Int.:MDC	QC:CM	APP.:	Date: 15-10-2025
LUNDSBY RENEWABLE SOLUTIONS			Lundsby Renewable Solutions A/S, Hjarbækvej 65, 8831 Løgstrup Tlf.: +45 96 49 43 00 Info@lundsby.dk This Drawing is subject to copyright and may not be reproduced without permission from Lundsby Renewable Solutions A/S
			Project nr.:1768 Drawing nr.: 9631 FORMAT: A1

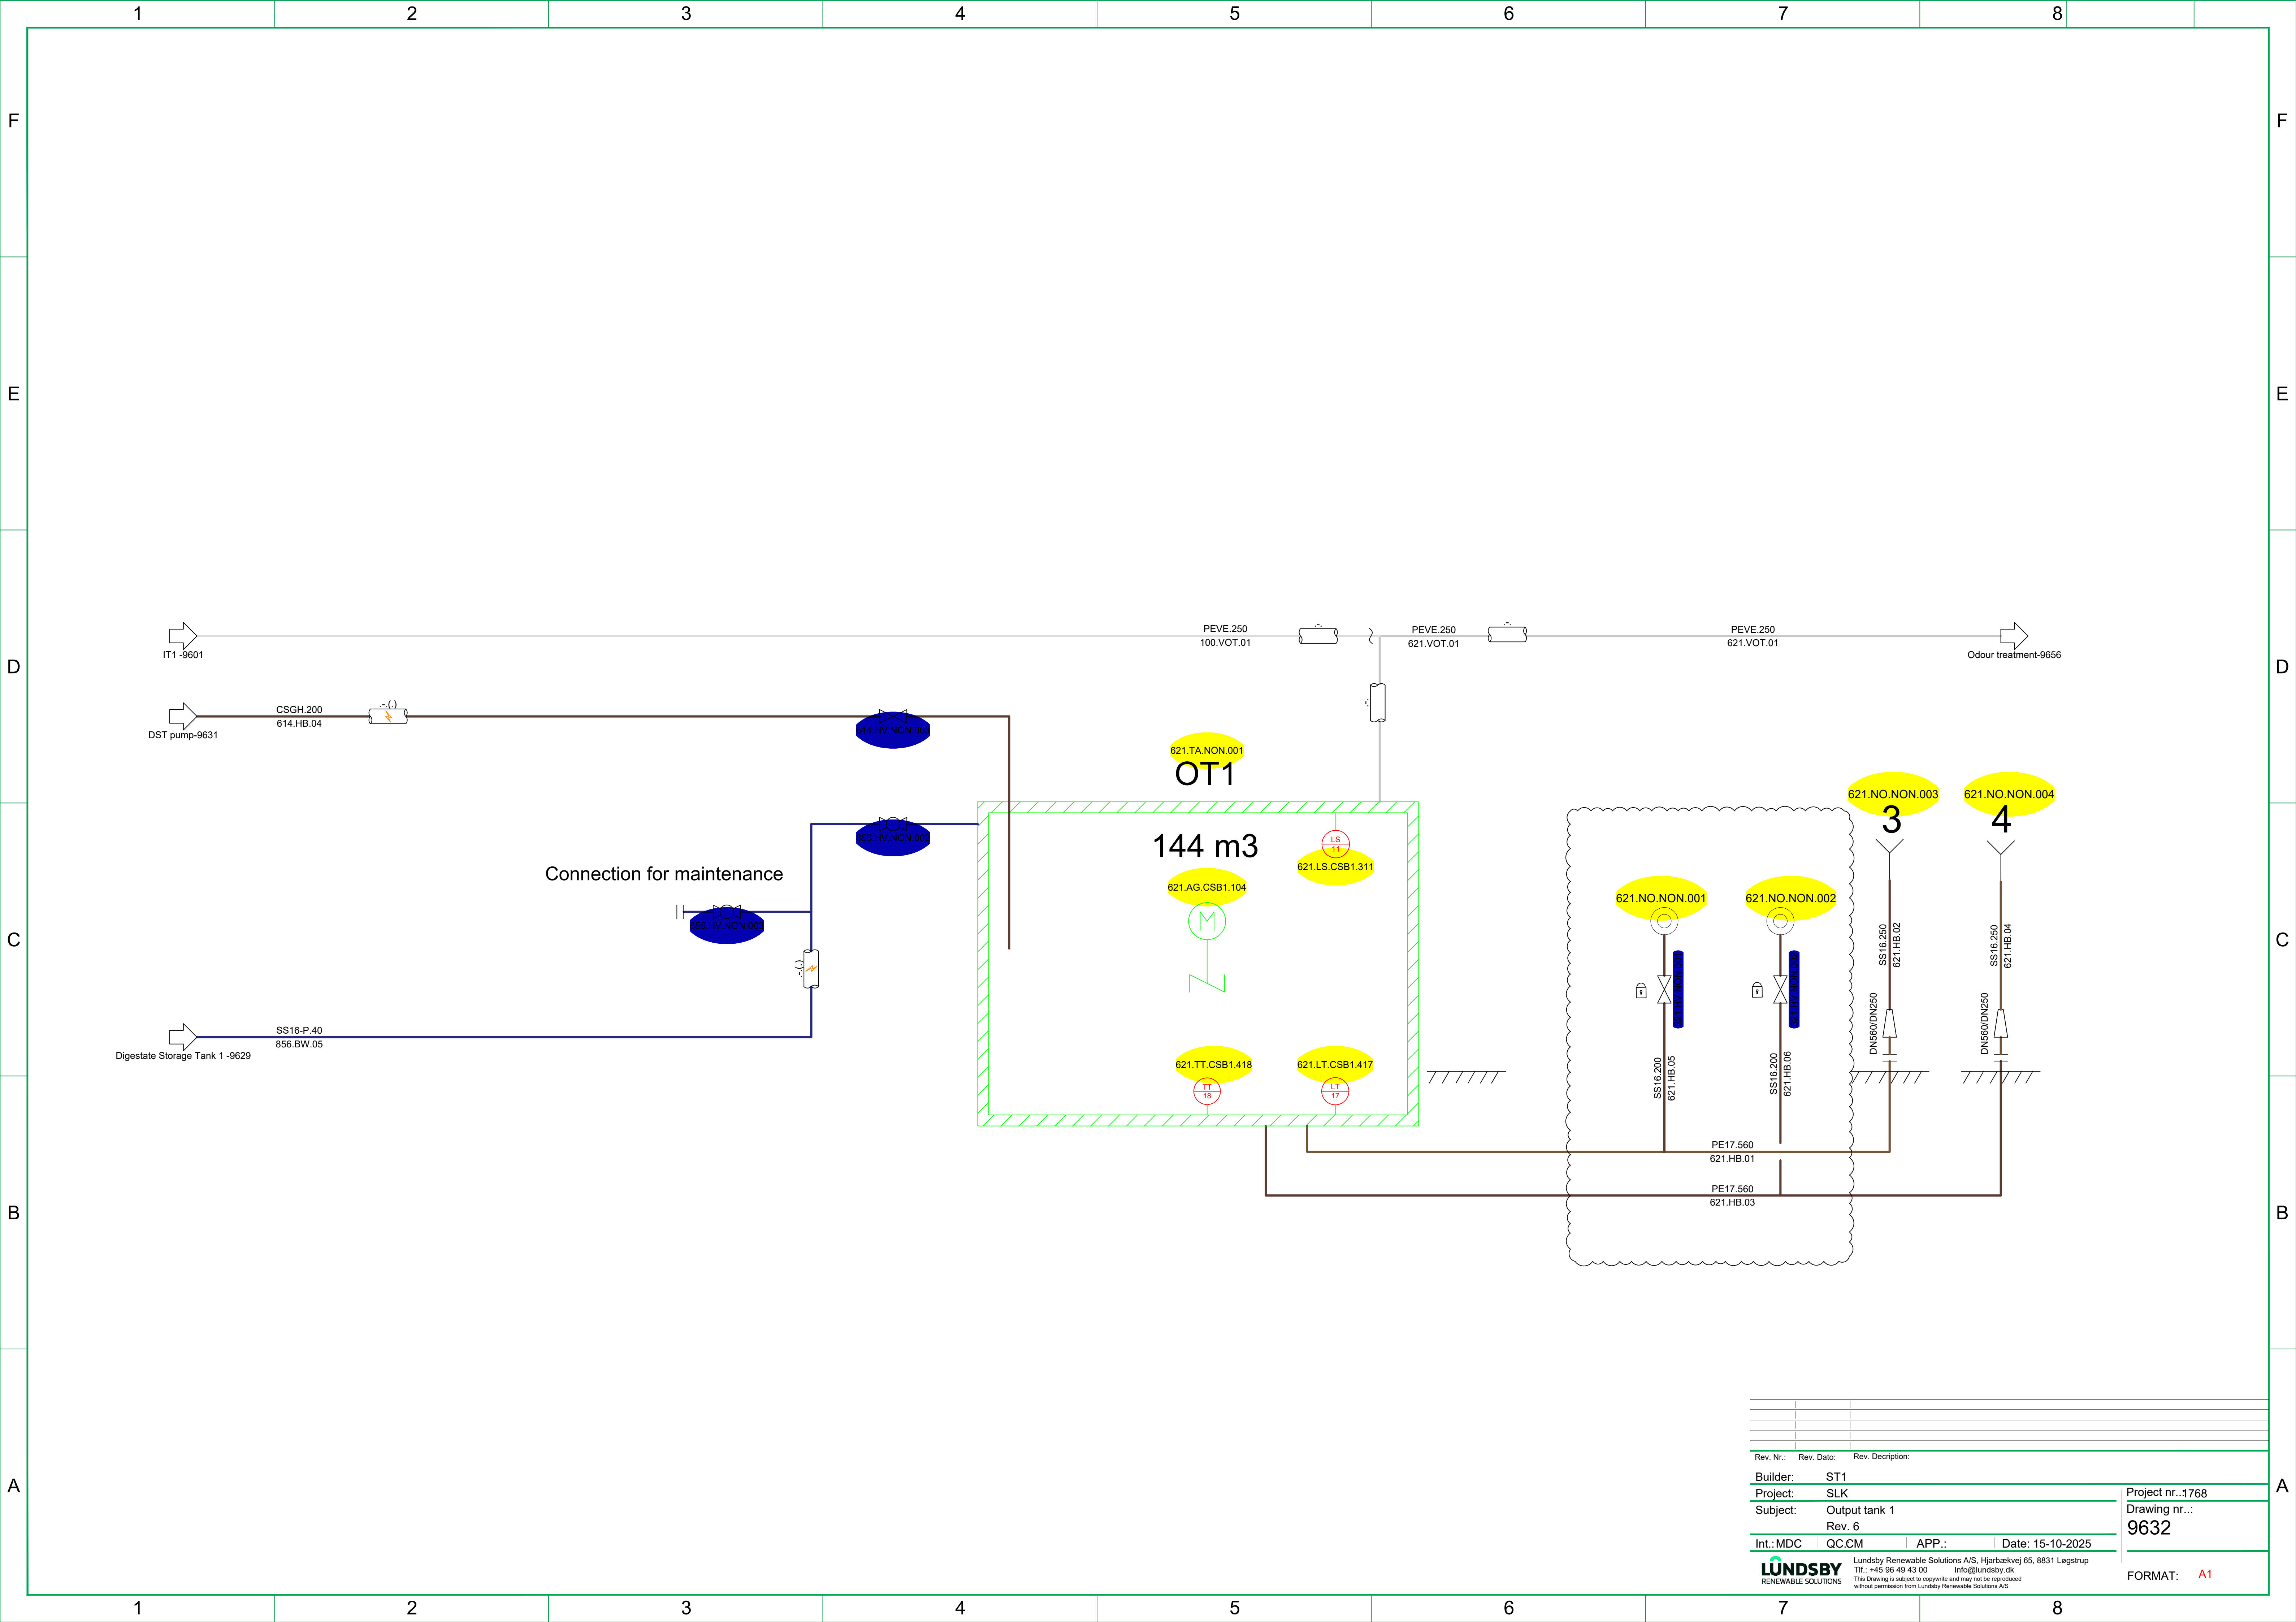

Rev. Nr.:	Rev. Dato:	Rev. Description:	Project nr...1768
Builder:	ST1		Drawing nr...: 9632
Project:	SLK		
Subject:	Output tank 1		
Rev. 6			
Int.:MDC	QC:CM	APP.:	Date: 15-10-2025
LUNDSBYRENEWABLE SOLUTIONS Lundsgby Renewable Solutions A/S, Hjarbrækvej 65, 8831 Løgstrop Tlf.: +45 96 49 43 00 Info@lundsgby.dk This Drawing is subject to copyright and may not be reproduced without permission from Lundsgby Renewable Solutions A/S			
FORMAT: A1			

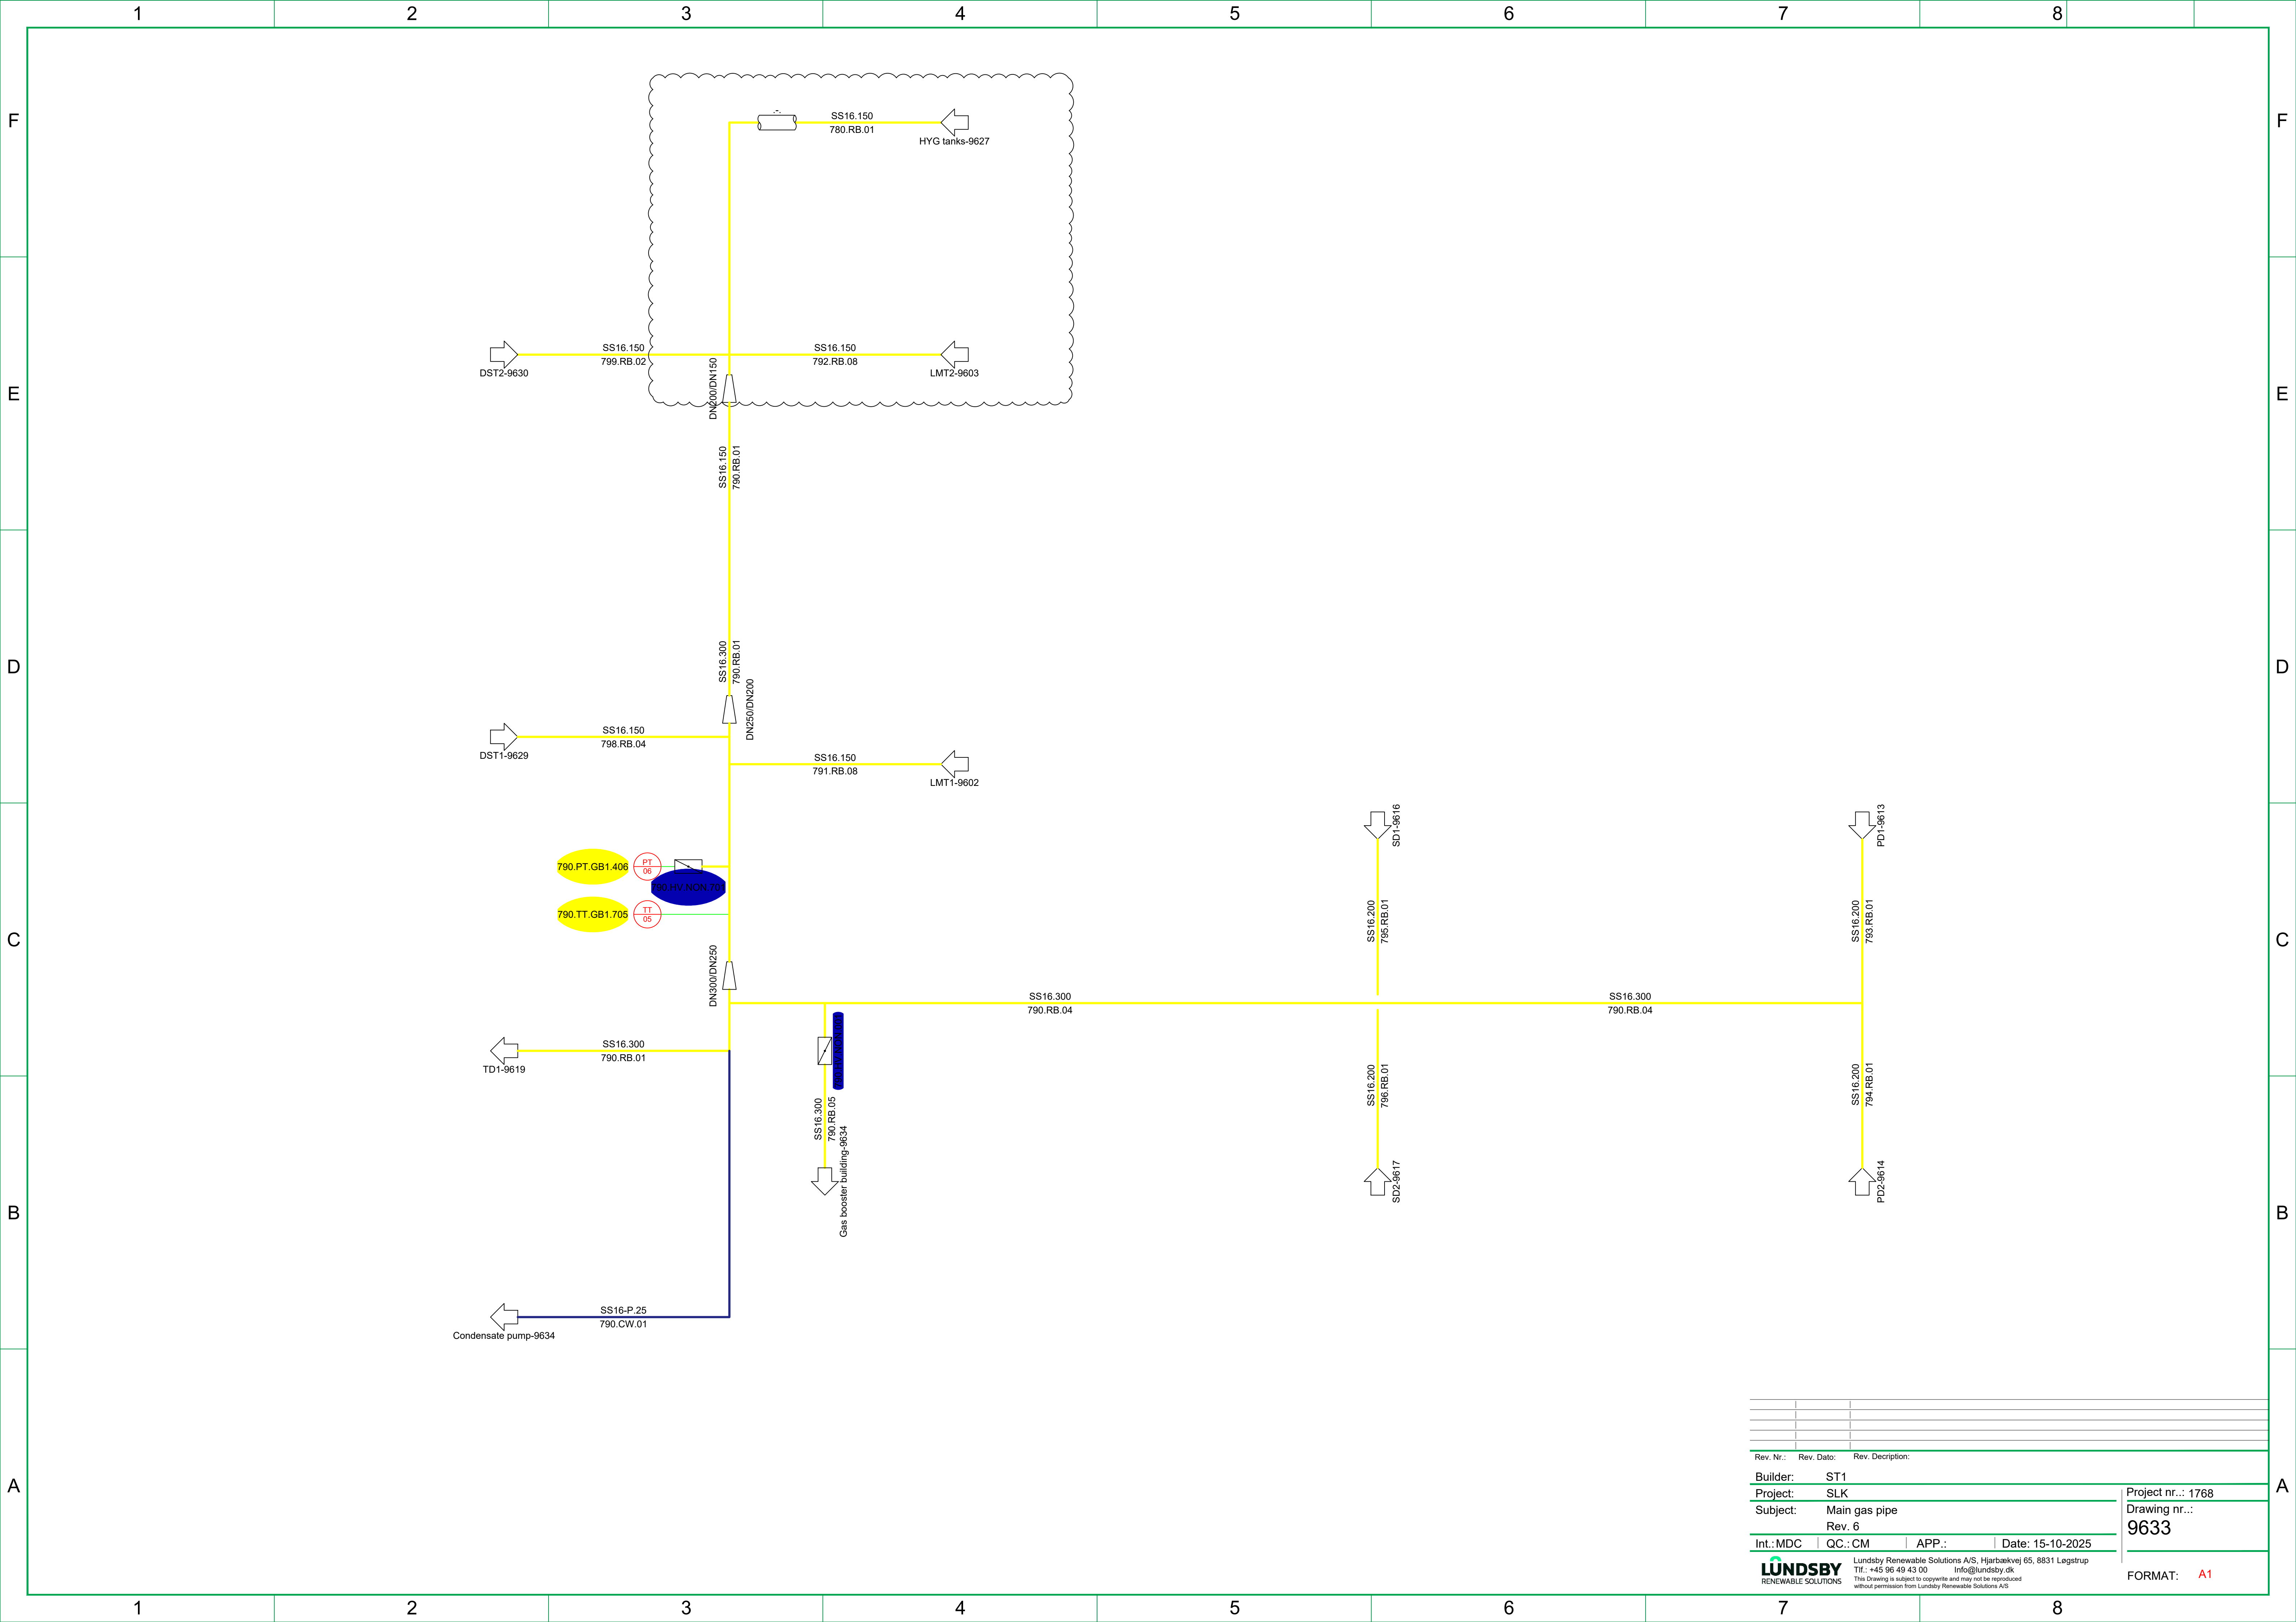


Rev. Nr.:	Rev. Dato:	Rev. Description:	
Builder:	ST1		
Project:	SLK		
Subject:	Main gas pipe		
Rev. 6			
Int.:MDC	QC.:CM	APP.:	Date: 15-10-2025
LUNDSBY RENEWABLE SOLUTIONS			Lundsgby Renewable Solutions A/S, Hjarbrækvej 65, 8831 Løgstrup Tlf.: +45 96 49 43 00 Info@lundsgby.dk This Drawing is subject to copyright and may not be reproduced without permission from Lundsgby Renewable Solutions A/S
Project nr.: 1768 Drawing nr.: 9633			FORMAT: A1

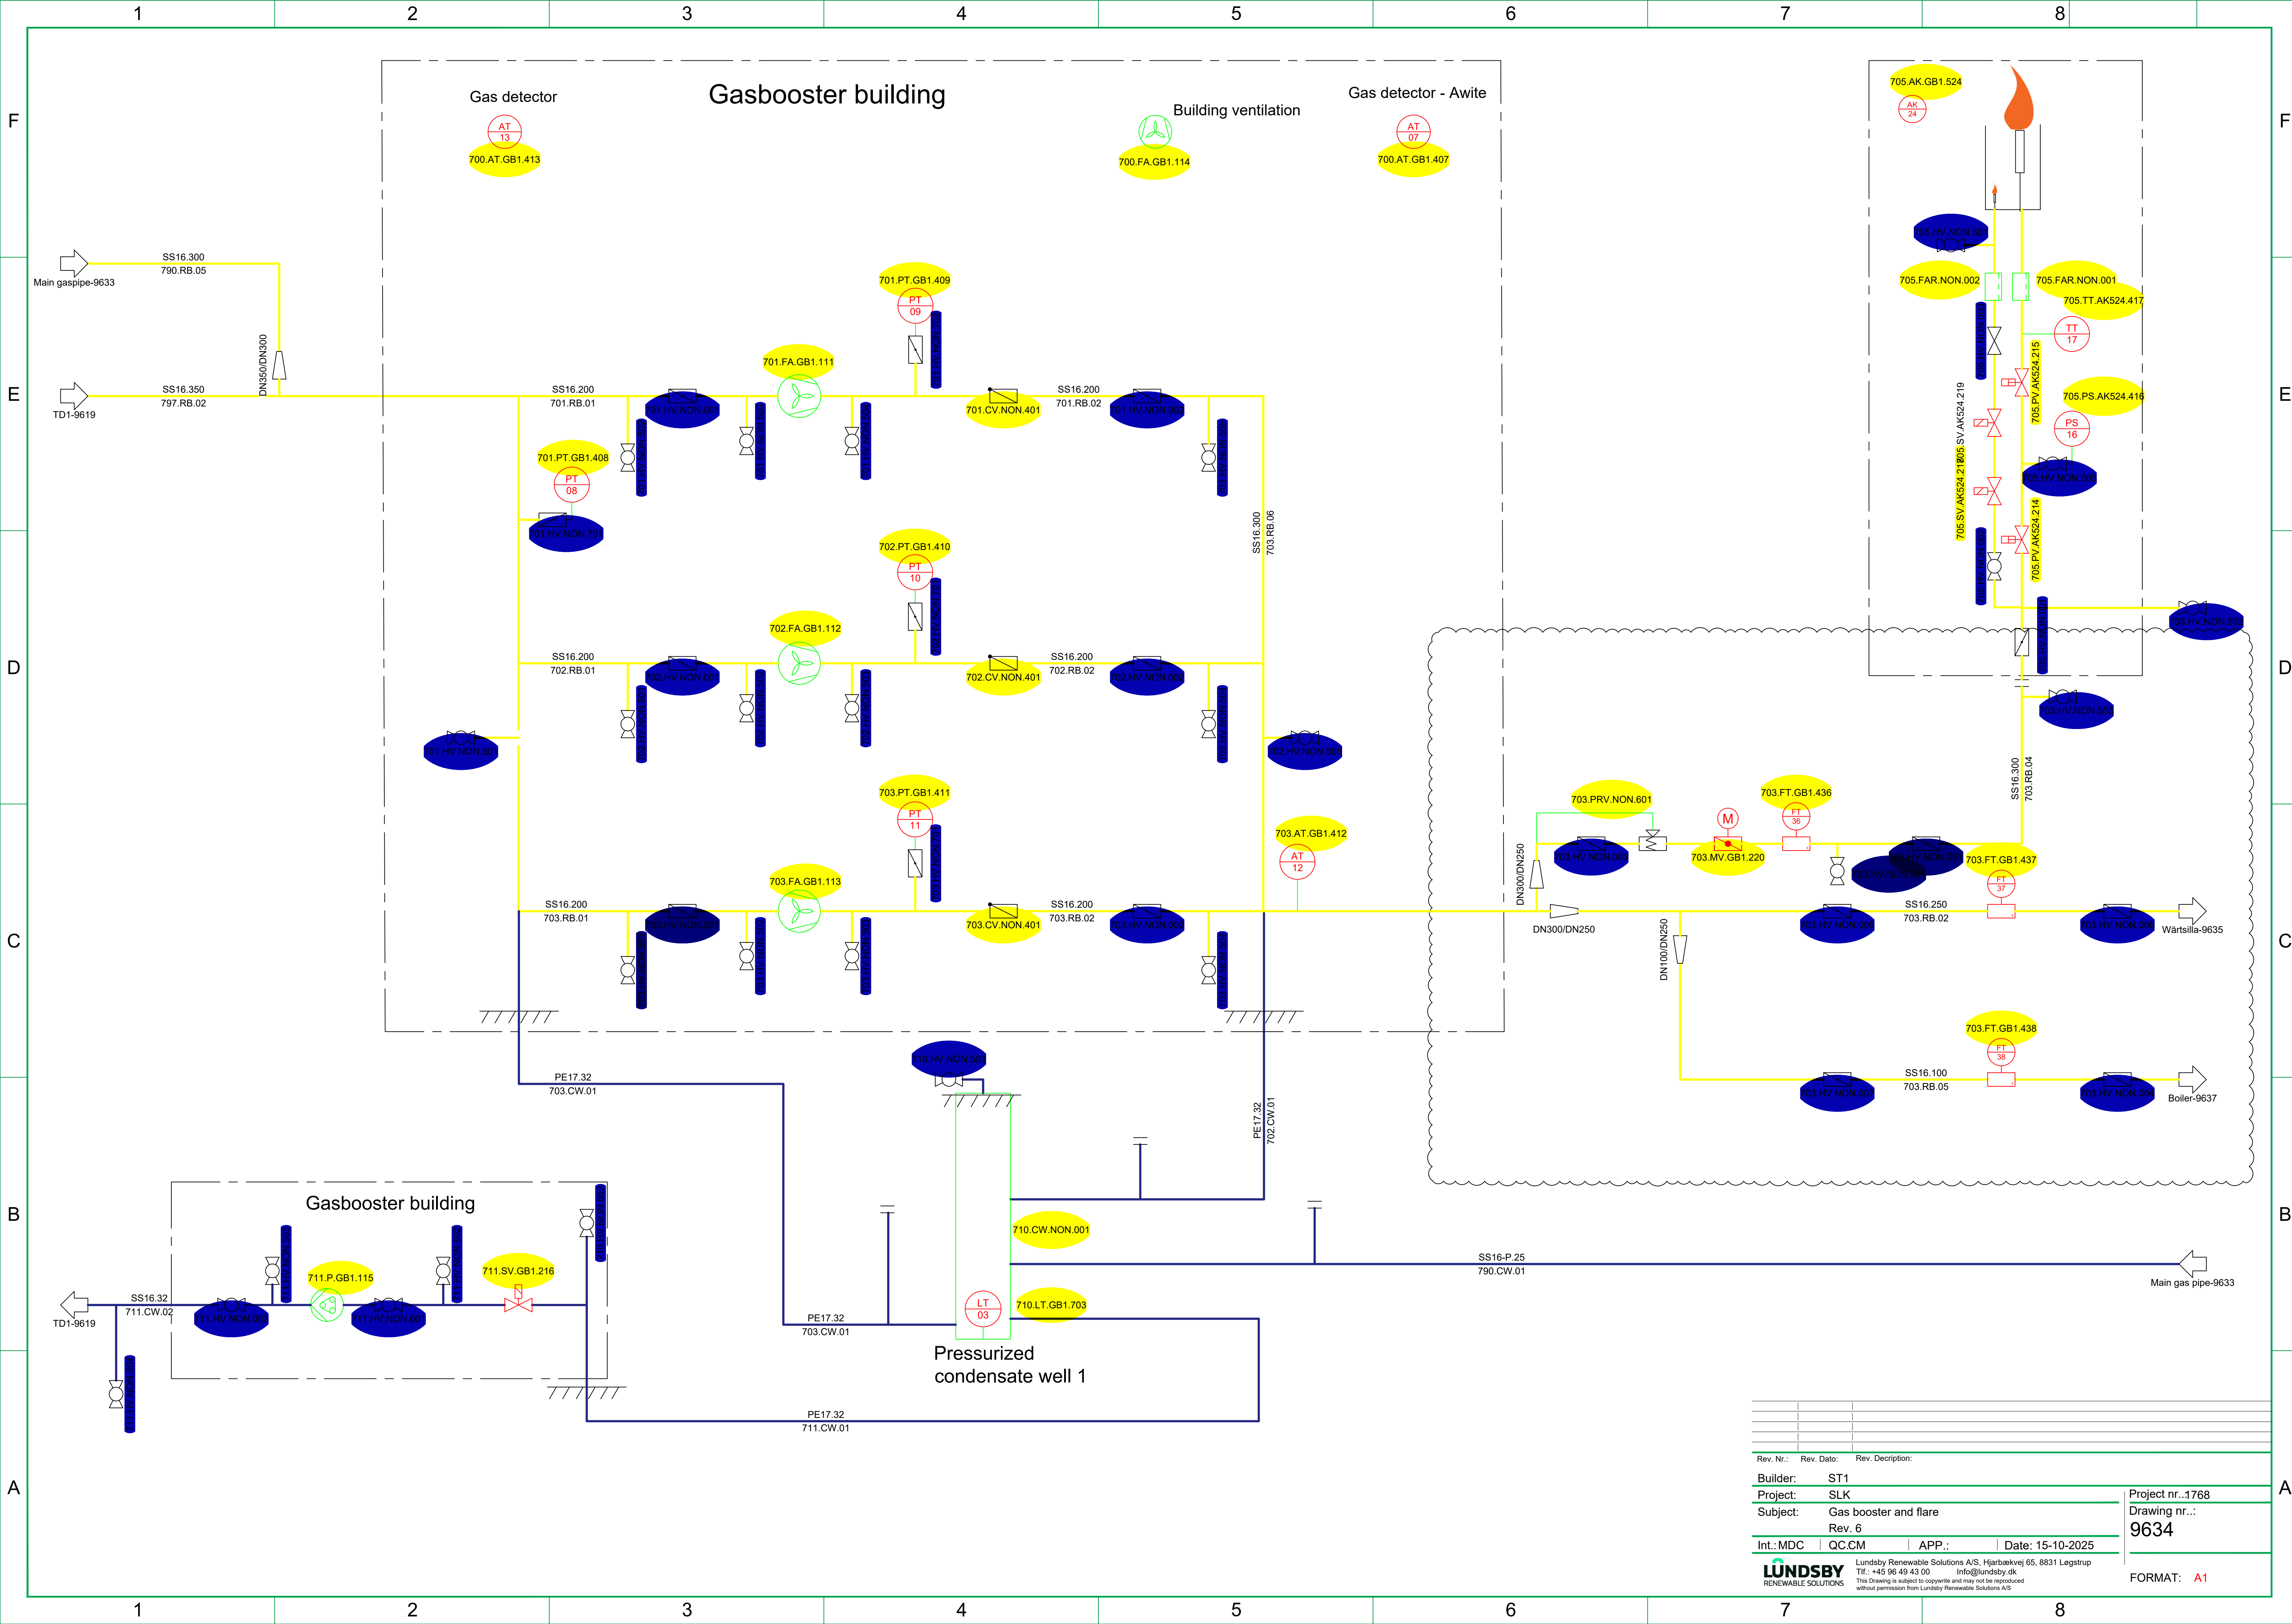


Wärtsillä

730-UPG-01

730-LBG-01

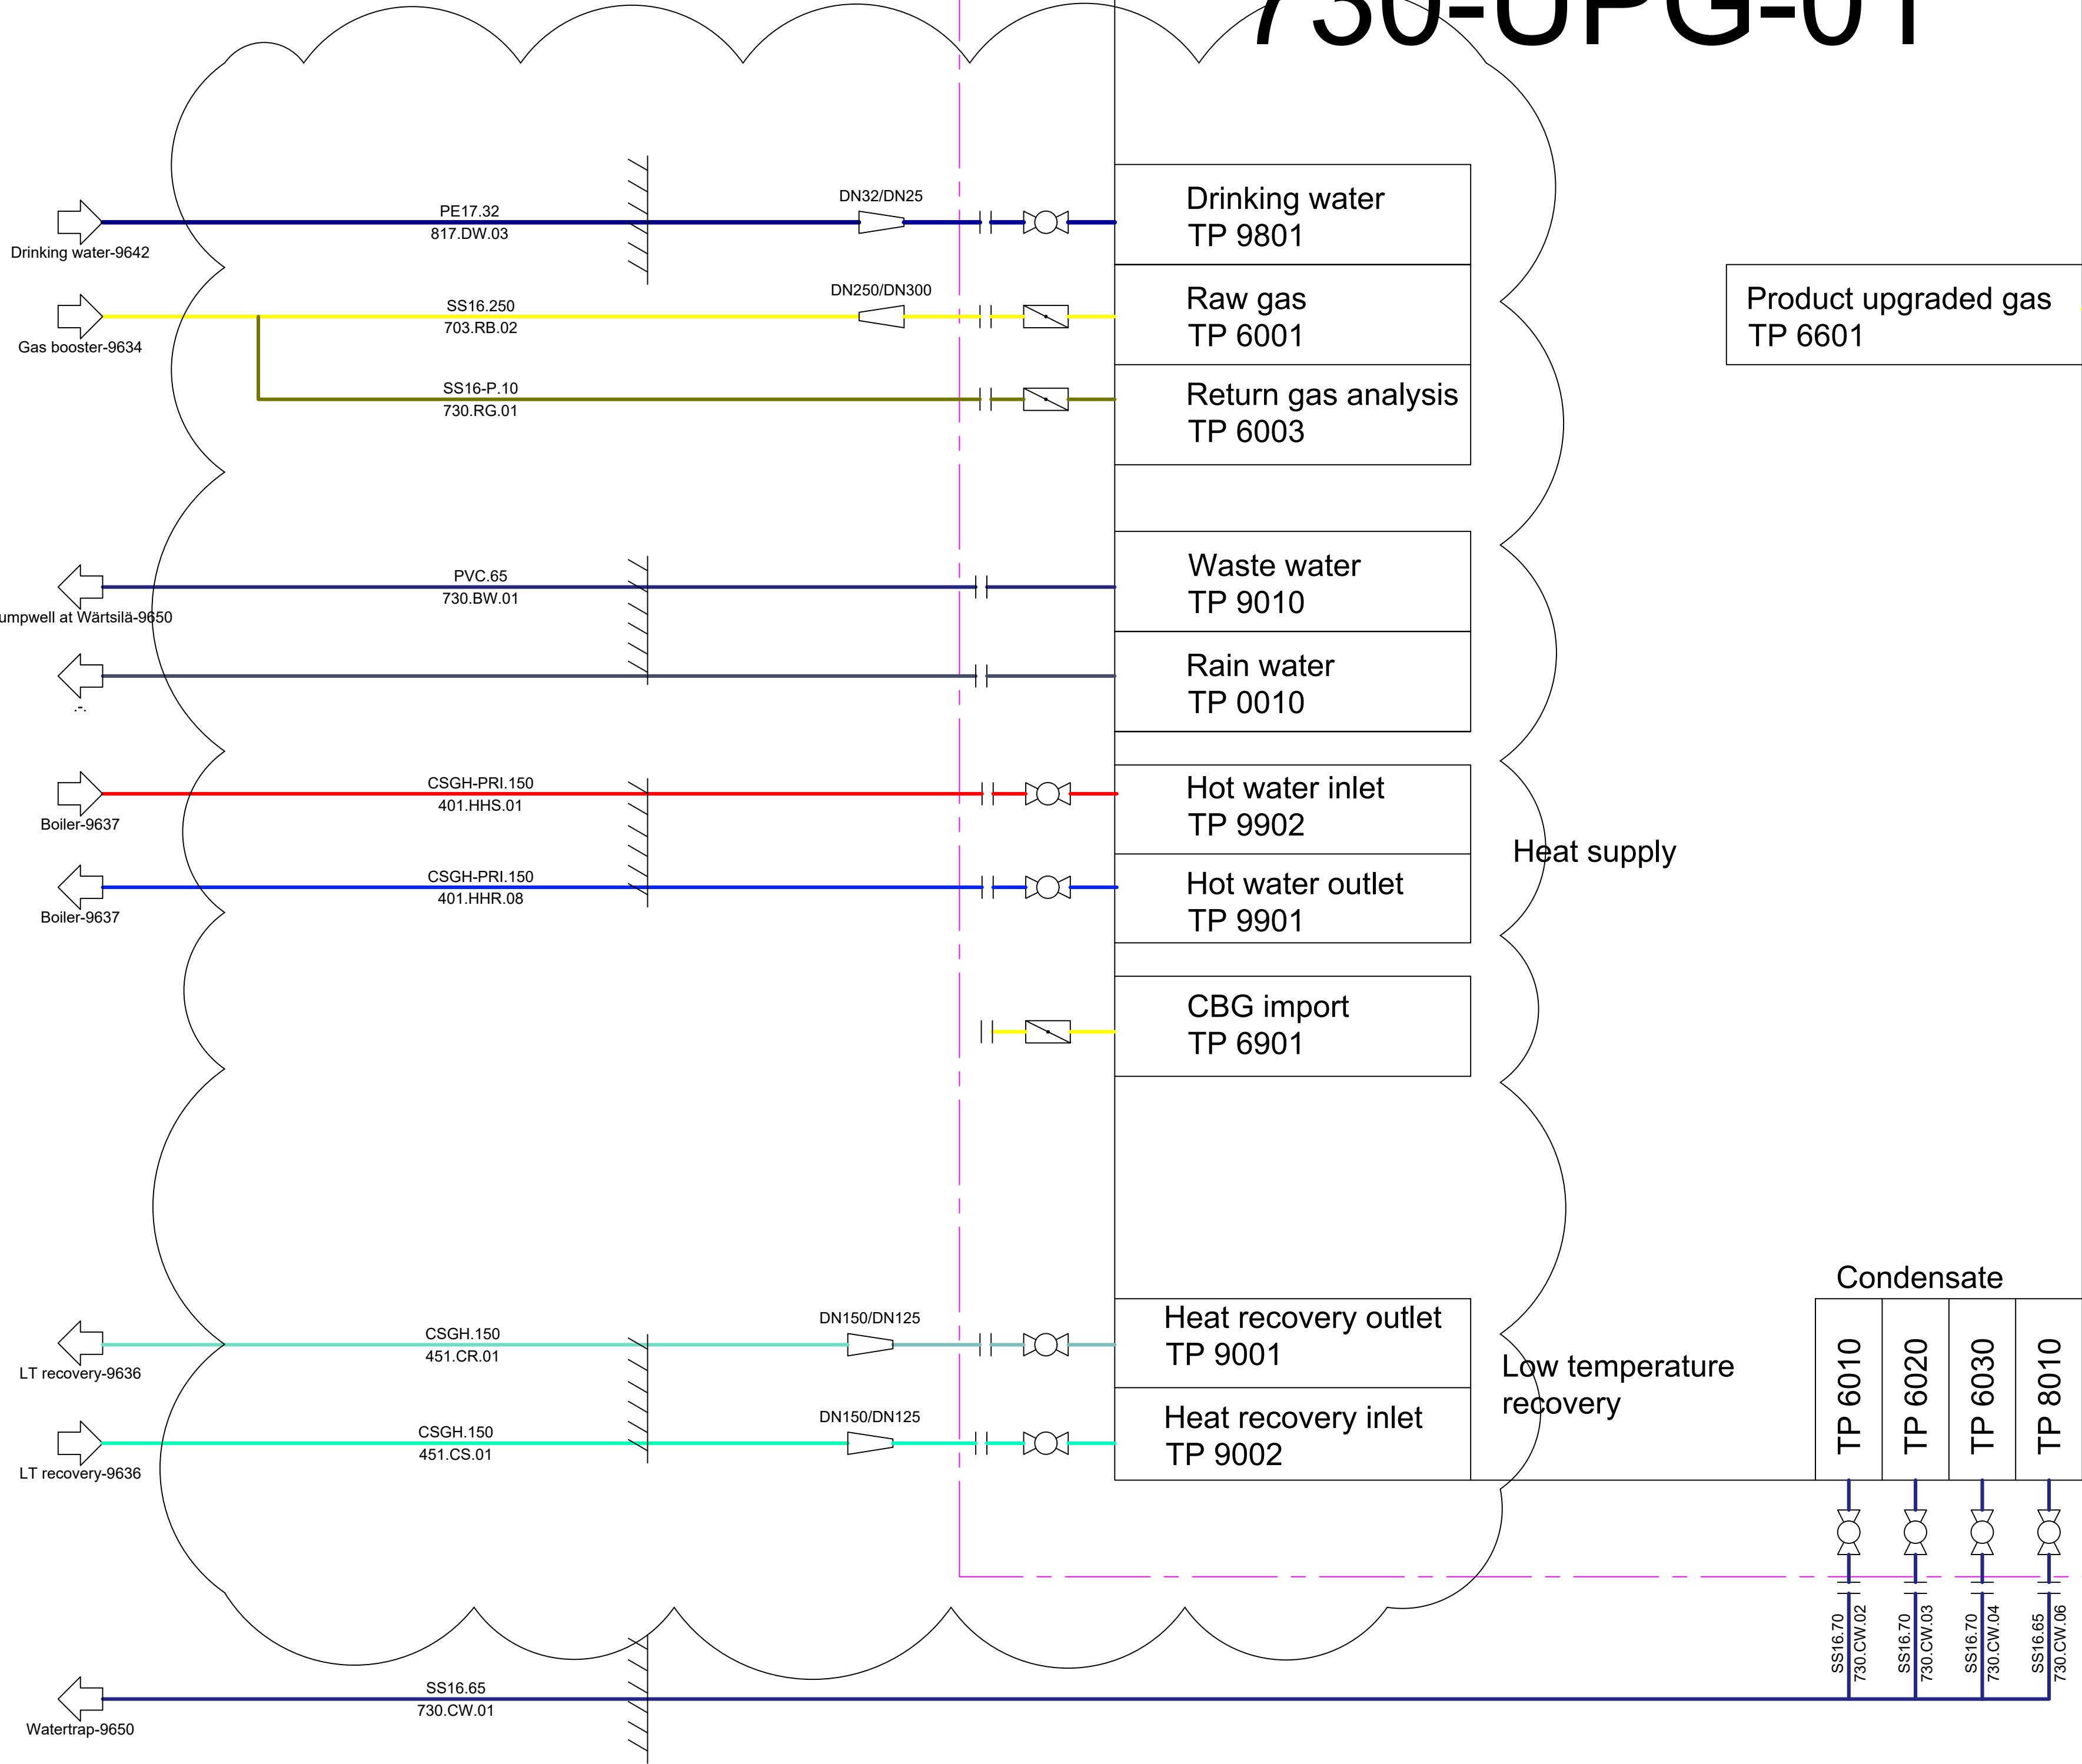


Product upgraded gas
TP 6601

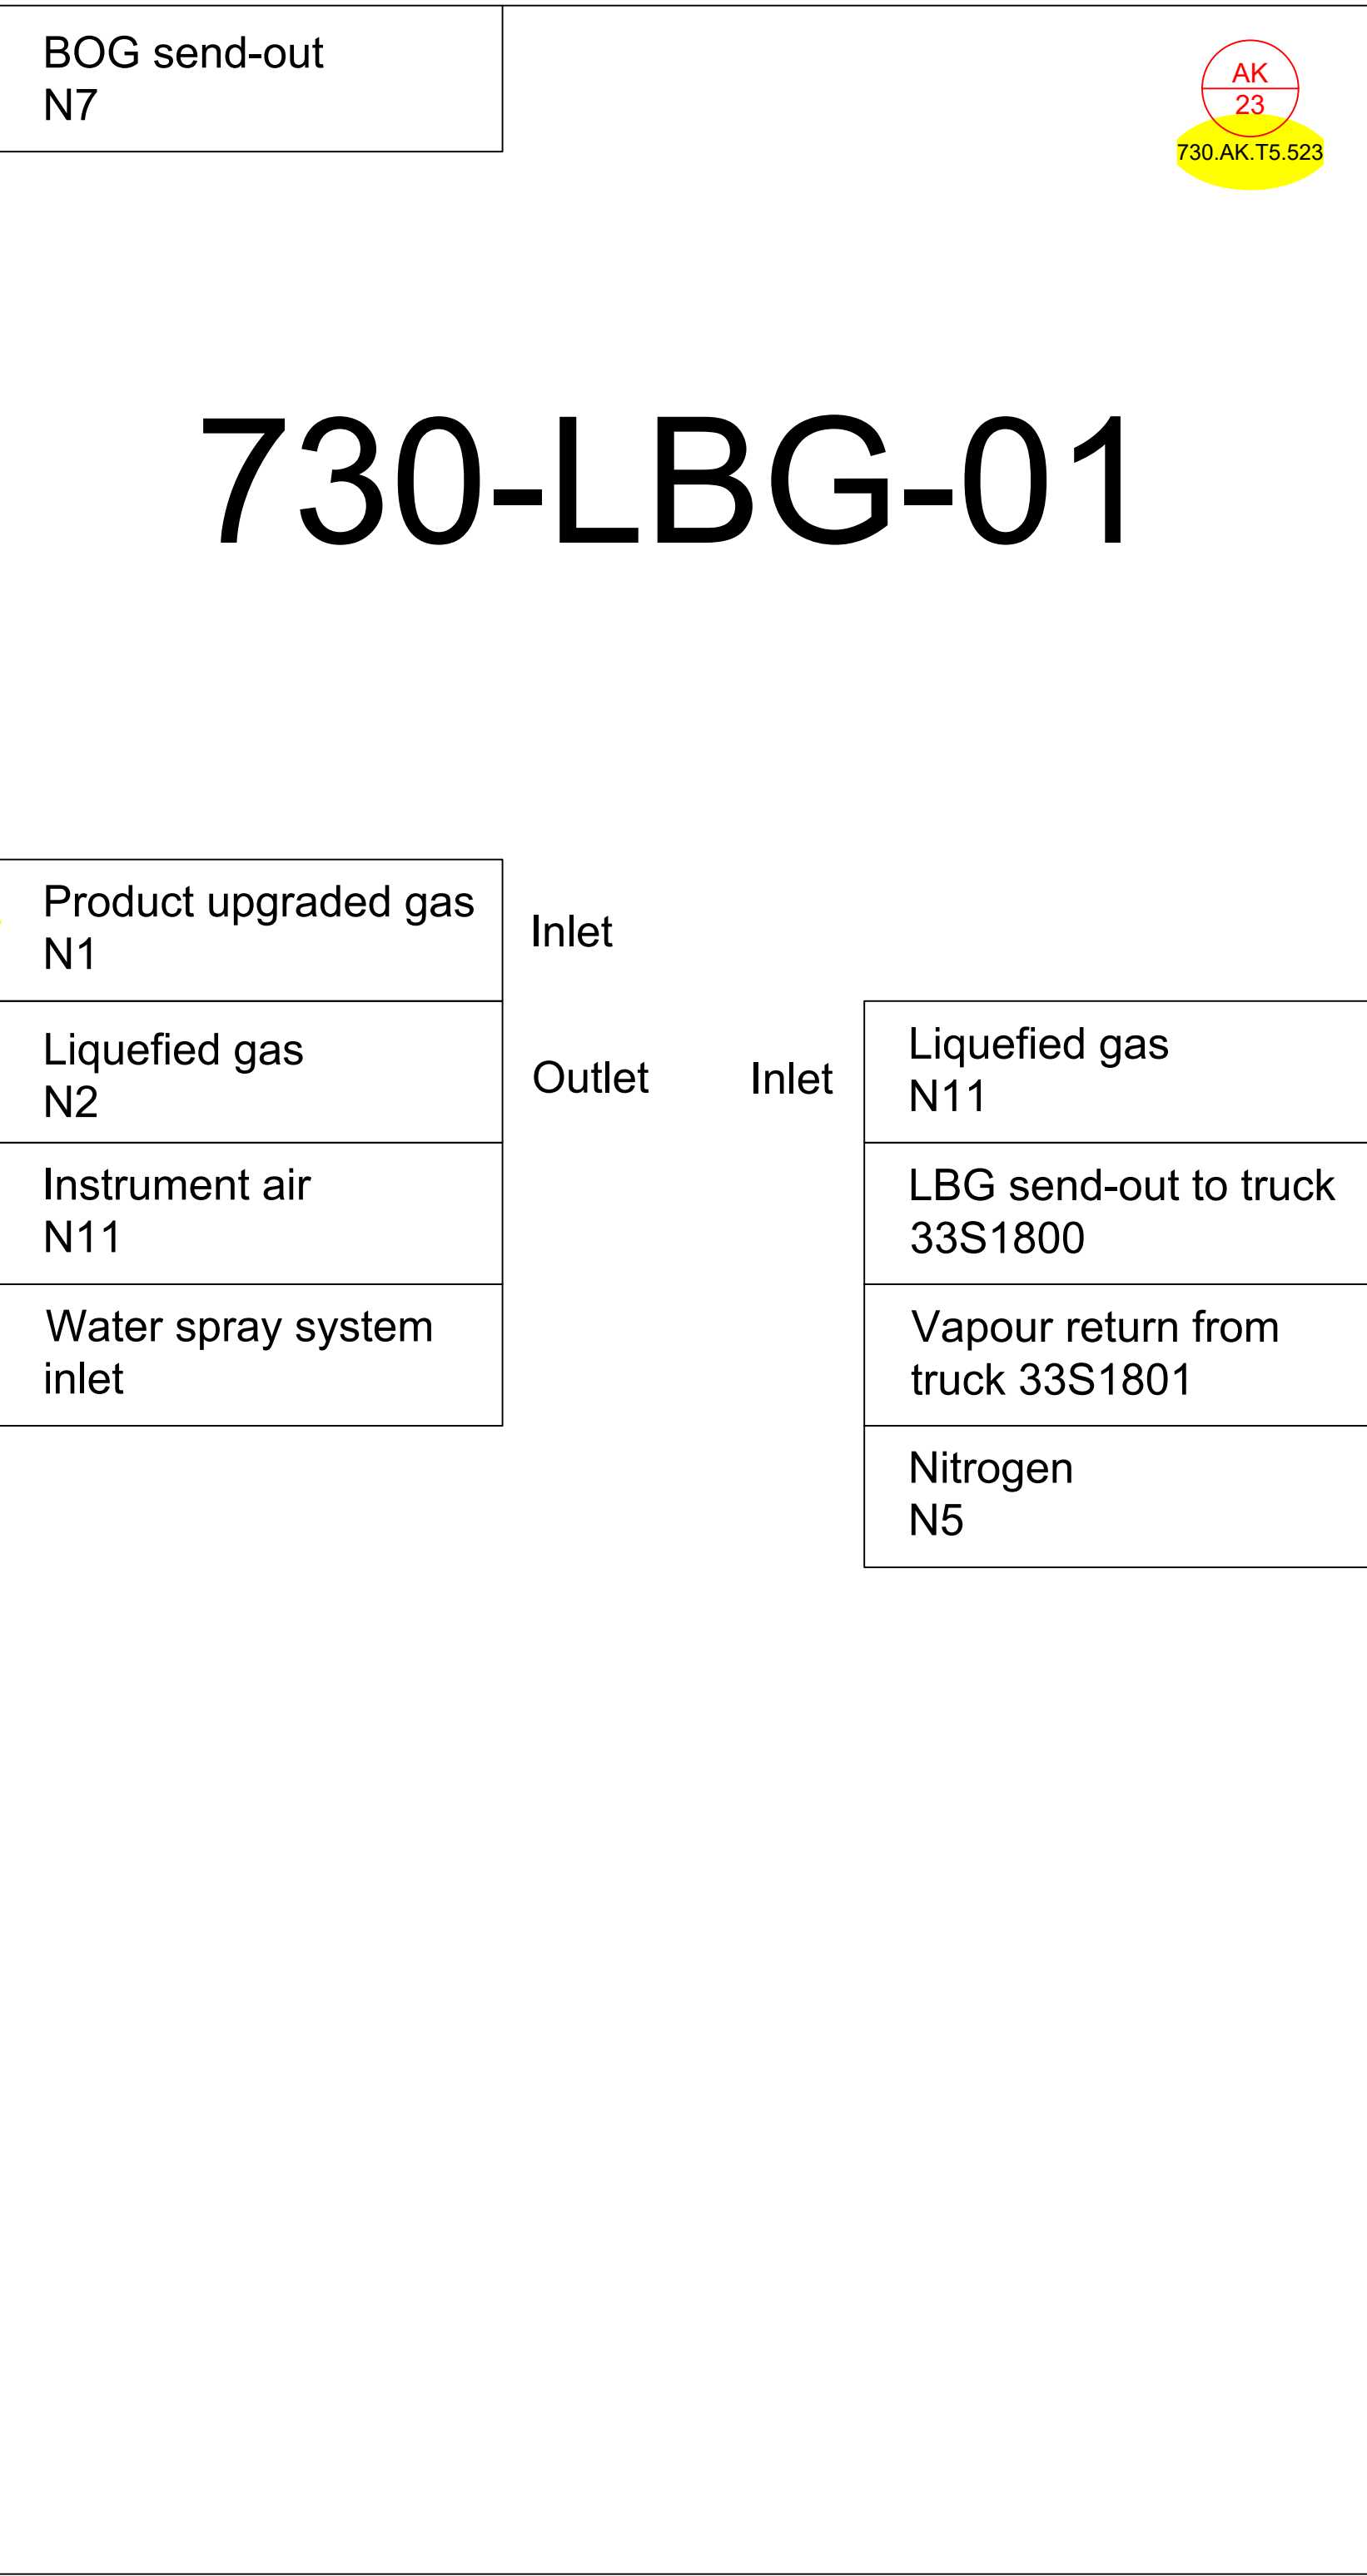


Rev. Nr.:	Rev. Dato:	Rev. Description:
Builder:	ST1	
Project:	SLK	
Subject:	Upgrade	
	Rev. 6	
Int.:MDC	QC.CM	APP.:
		Date: 15-10-2025
LUNDSBY RENEWABLE SOLUTIONS		
Lundsgby Renewable Solutions A/S, Hjarbrækvej 65, 8831 Lægstrup Tlf.: +45 96 49 43 00 Info@lundsgby.dk This Drawing is subject to copyright and may not be reproduced without permission from Lundsgby Renewable Solutions A/S		
Project nr...:1768 Drawing nr...: 9635		FORMAT: A1

Technology building

Heat pump scope

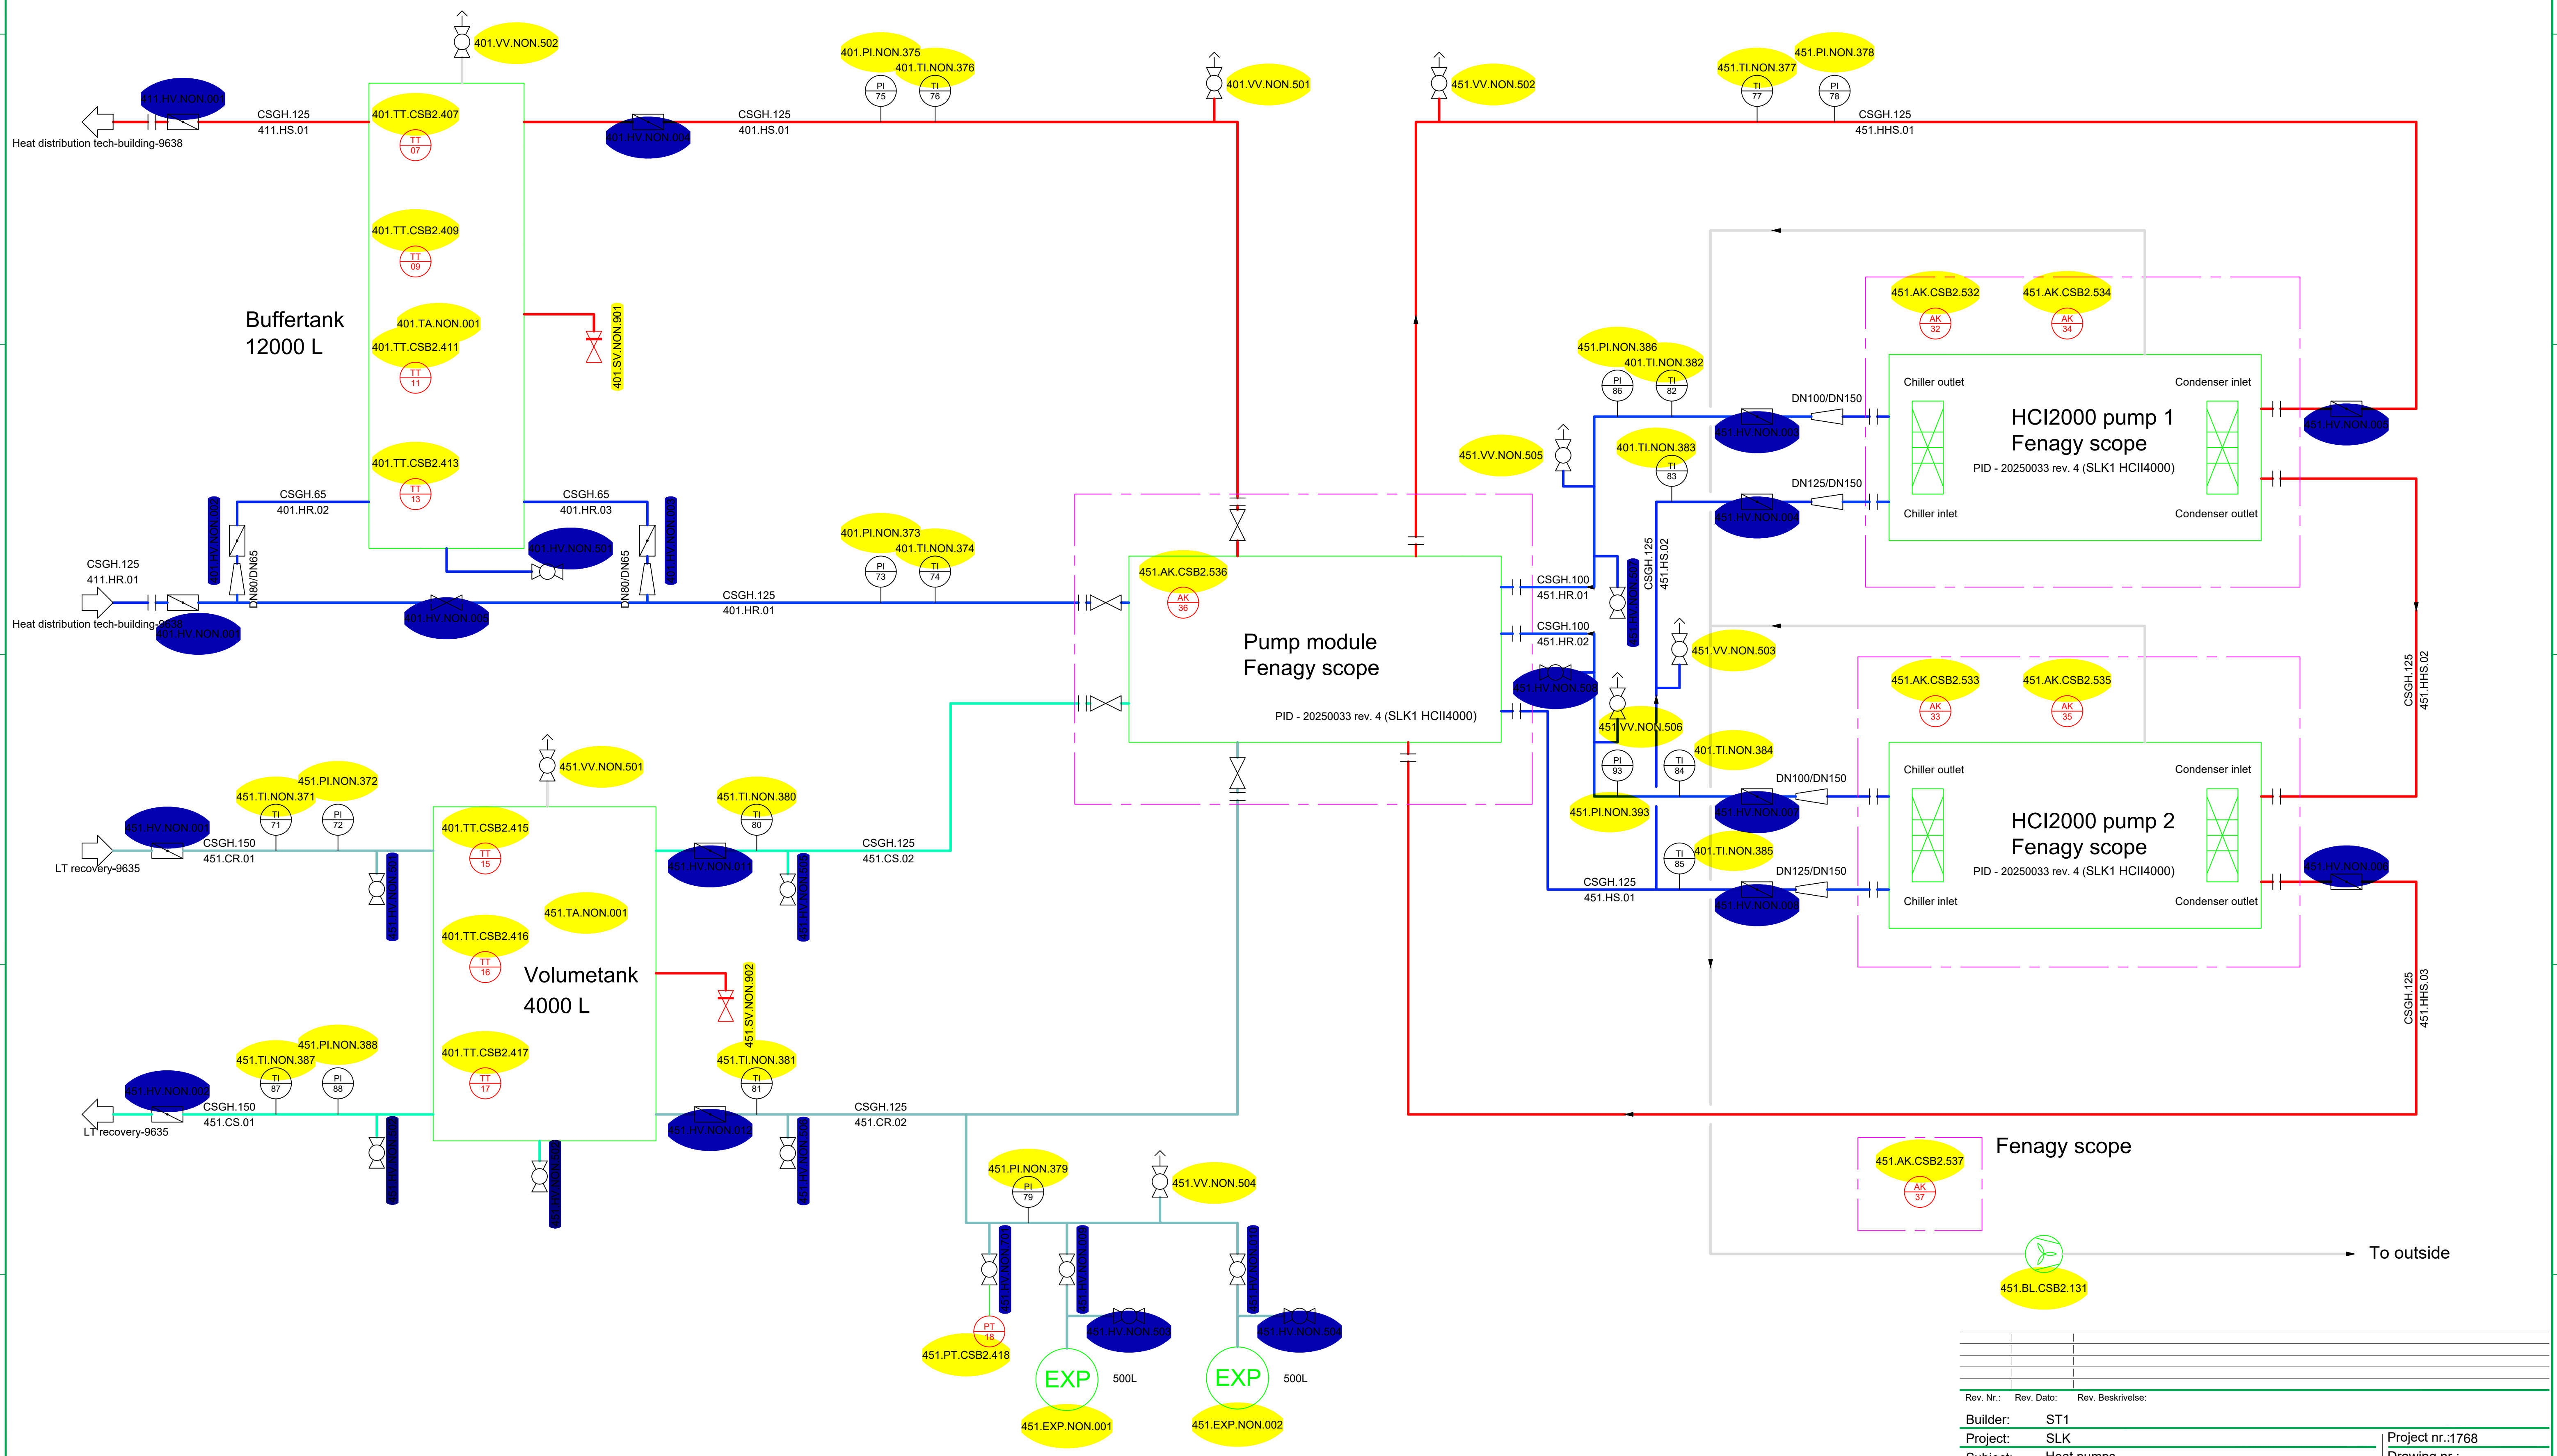

Rev. Nr.:	Rev. Dato:	Rev. Beskrivelse:	
Builder:	ST1		
Project:	SLK		
Subject:	Heat pumps		
Rev.:	6		
Int.:MDC	QC:CM	APP.:	Date: 15-10-2025
LUNDSBY RENEWABLE SOLUTIONS			Lundsby Biogas A/S, Hjarbækvej 65, 8831 Løgstrup Tlf.: +45 96 49 43 00 info@lundsbybiogas.dk Denne tegning er underlagt copyright og må ikke reproduceres uden tilladelse fra Lundsbybiogas A/S
Project nr.:1768 Drawing nr.: 9636			FORMAT: A1

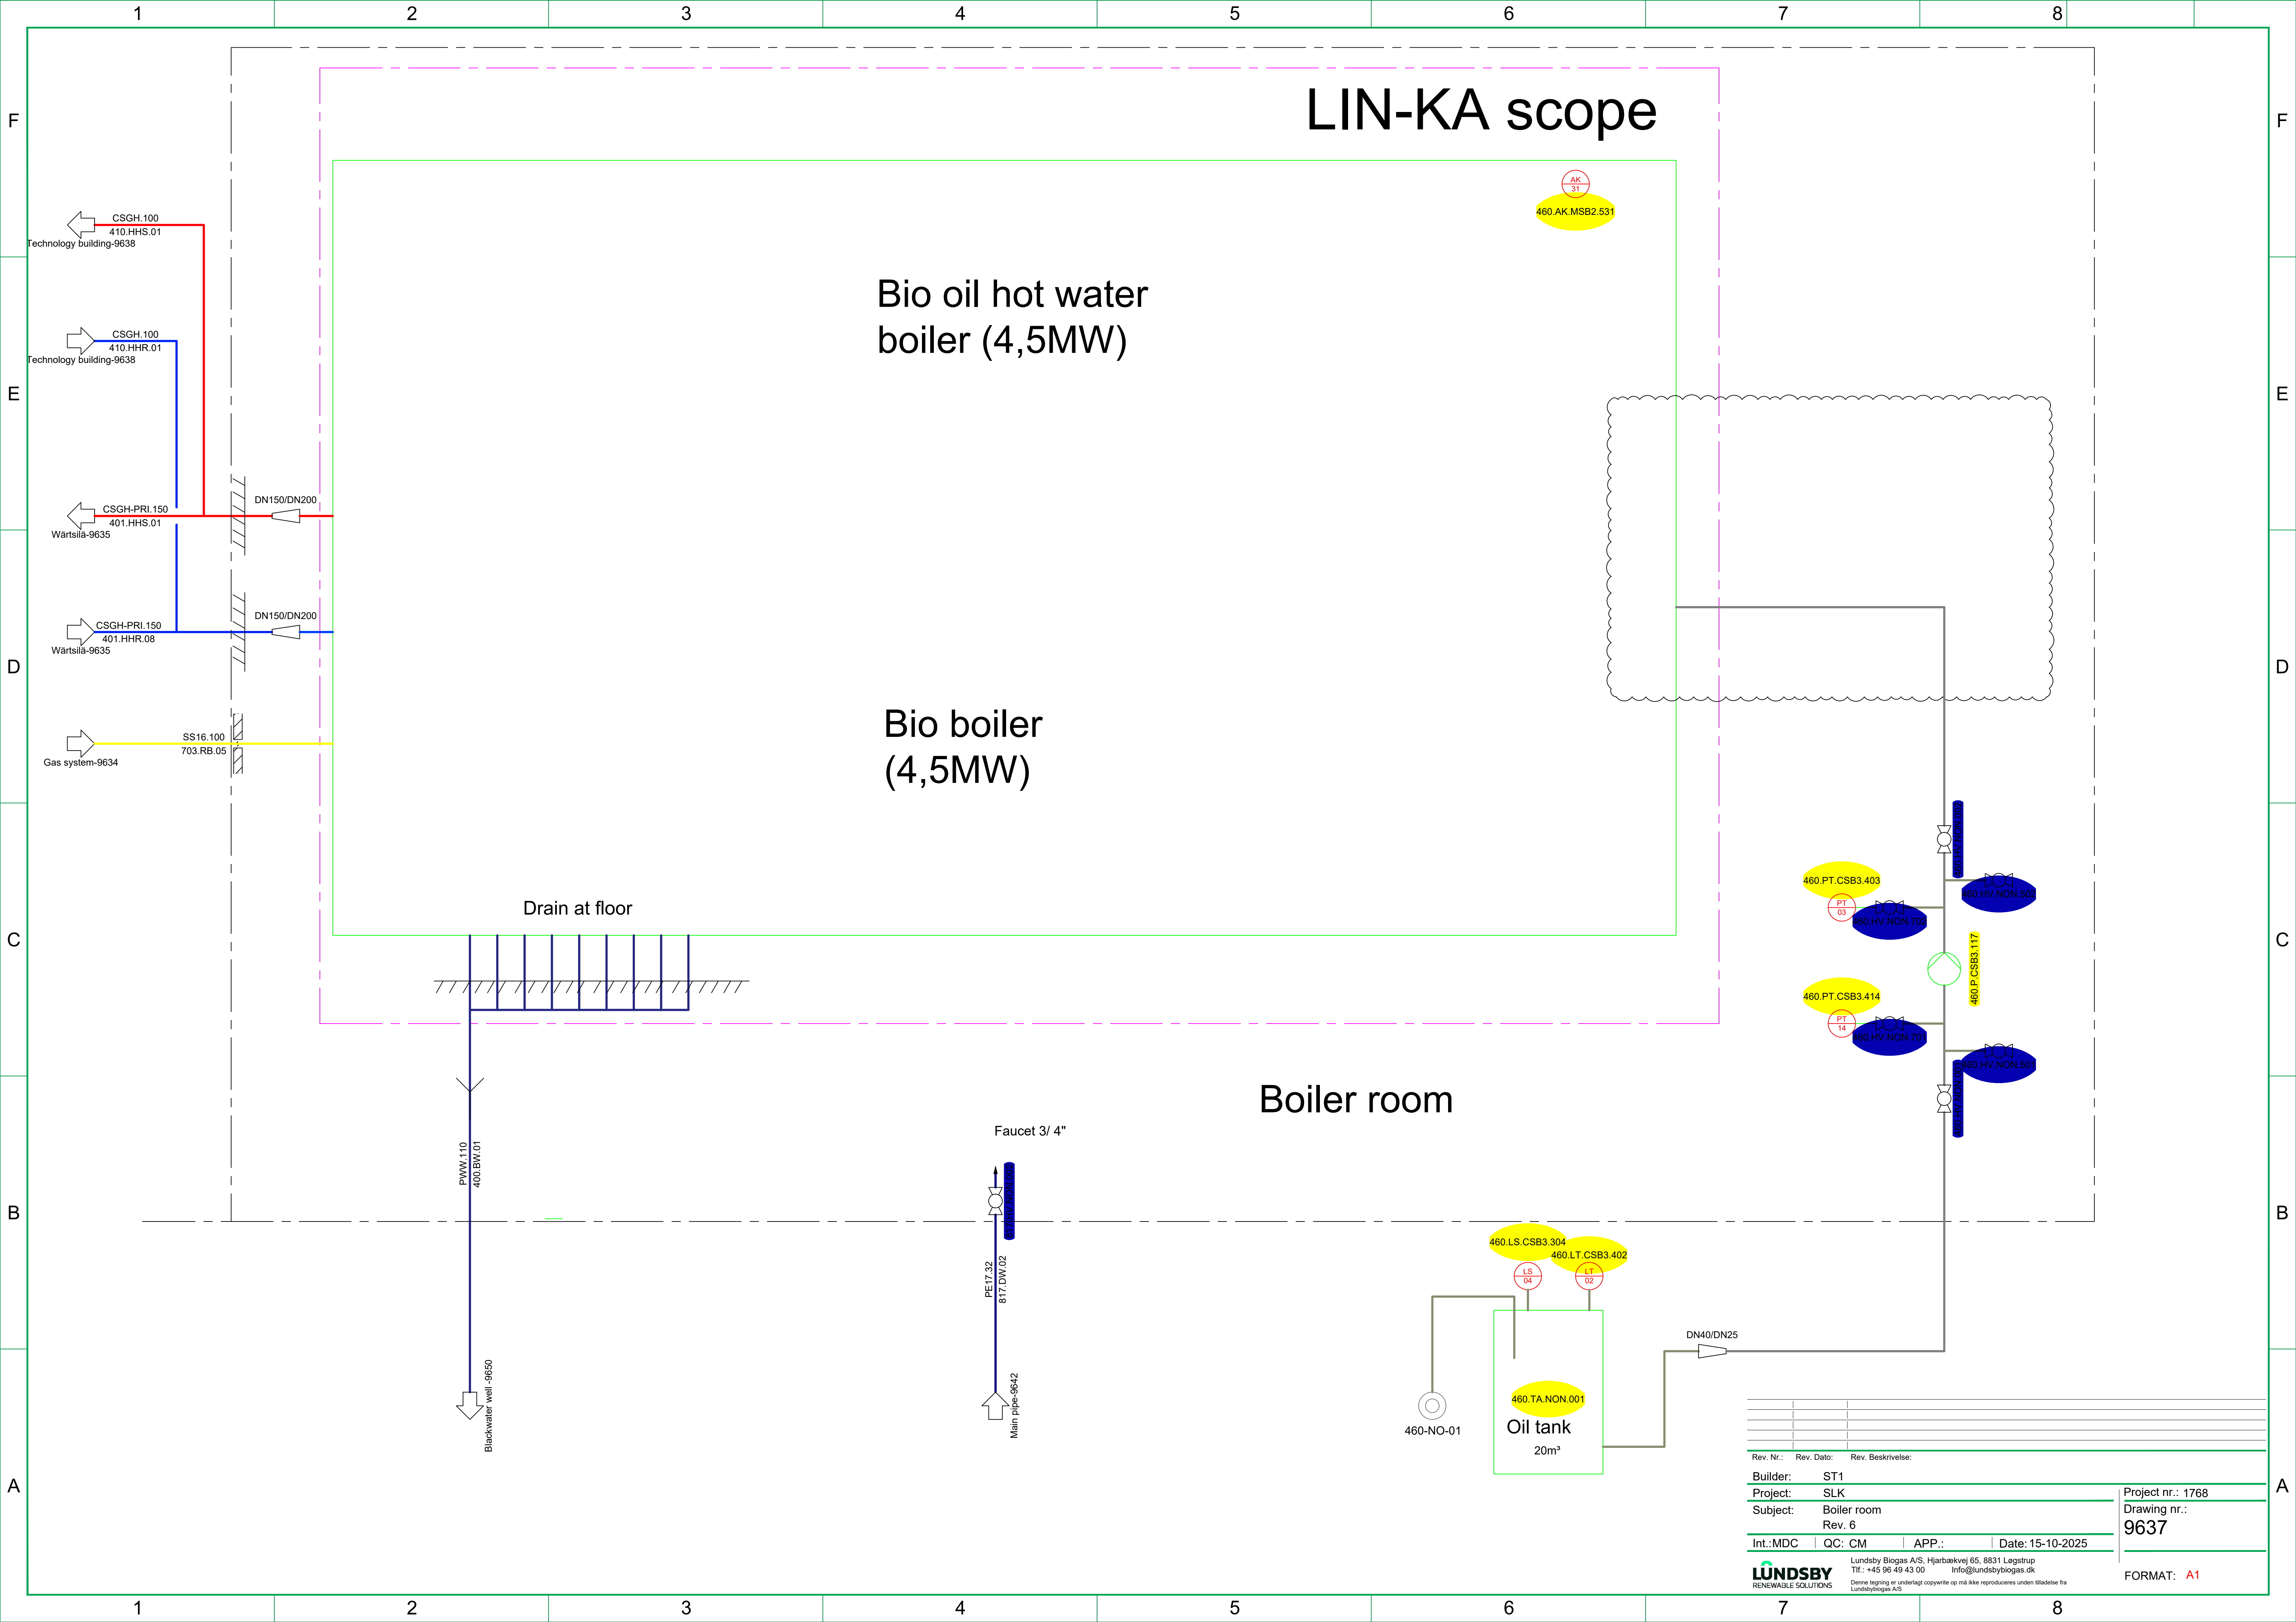

LIN-KA scope

Bio oil hot water boiler (4,5MW)

Bio boiler (4,5MW)


Boiler room

Drain at floor

Faucet 3/ 4"


Oil tank
20m³

Rev. Nr.:	Rev. Dato:	Rev. Beskrivelse:	
Builder:	ST1		
Project:	SLK		
Subject:	Boiler room		
Rev. 6			
Int.:MDC	QC: CM	APP.:	Date: 15-10-2025
LUNDSBY RENEWABLE SOLUTIONS			Lundsby Biogas A/S, Hjarbækvej 65, 8831 Løgstrup Tlf.: +45 96 49 43 00 Info@lundsbybiogas.dk Denne tegning er underlagt copyright og må ikke reproducere uden tilladelse fra Lundsbybiogas A/S
			Project nr.: 1768 Drawing nr.: 9637 FORMAT: A1

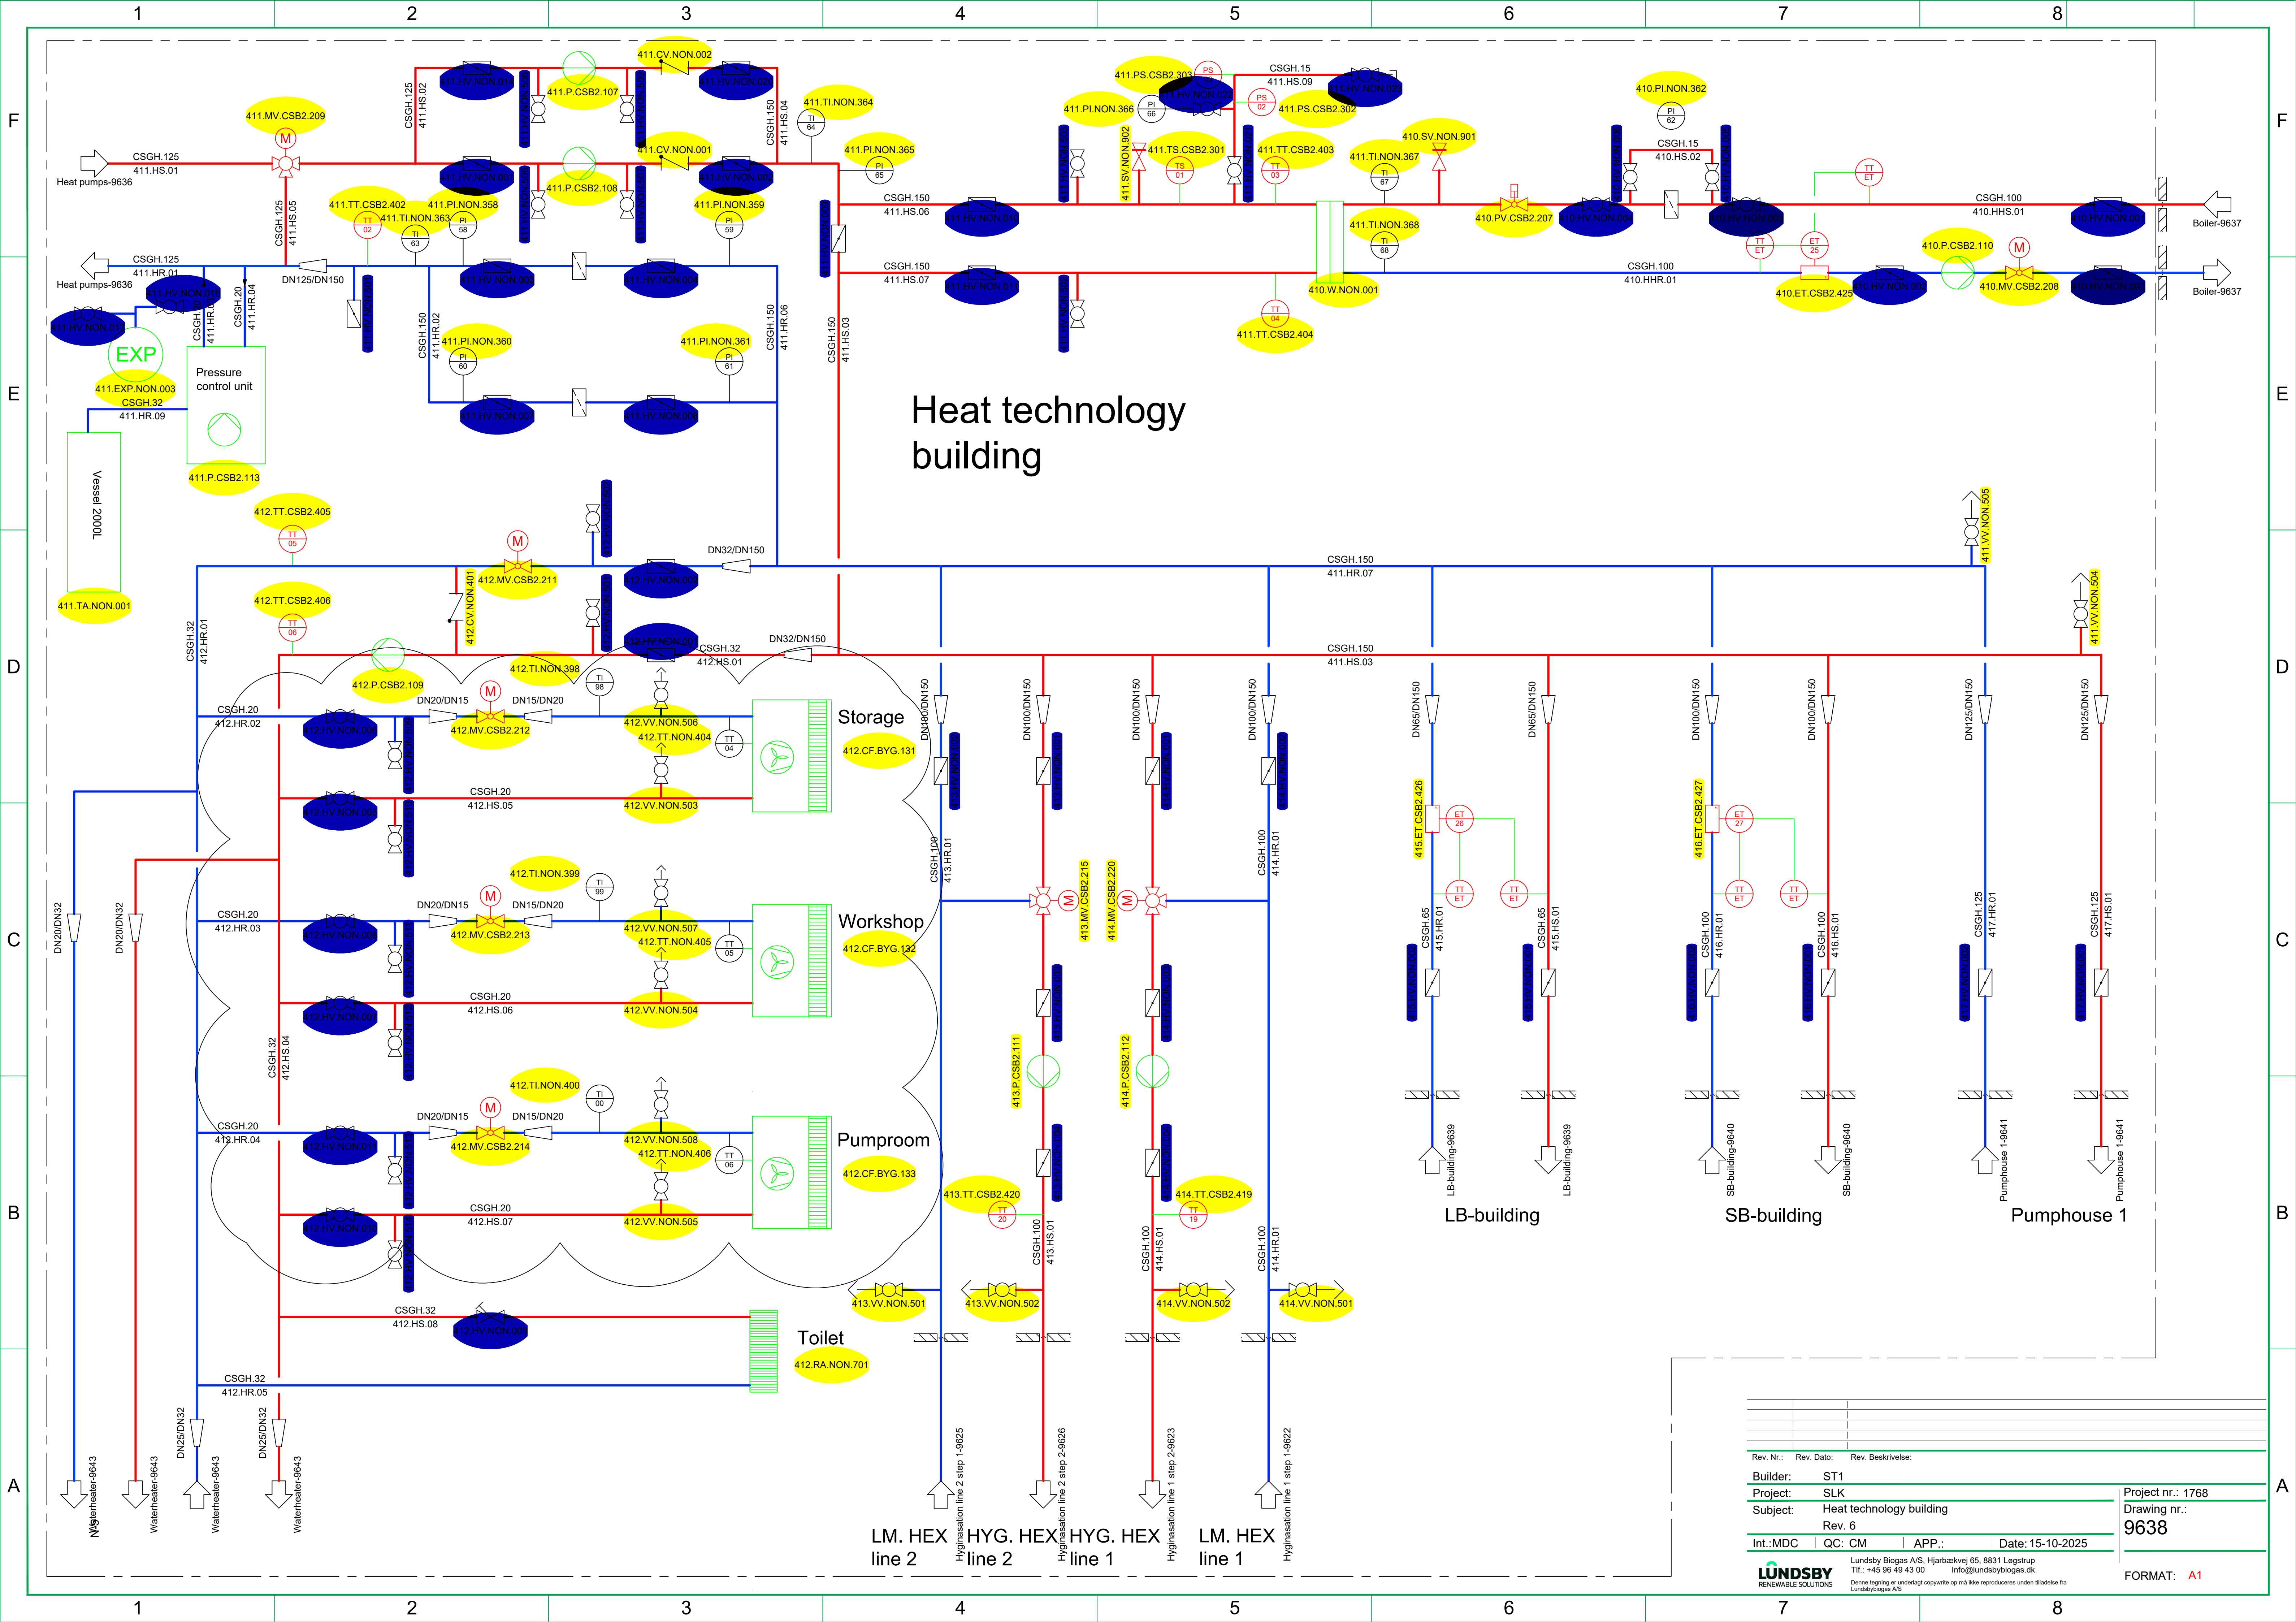


Rev. Nr.:	Rev. Dato:	Rev. Beskrivelse:
Builder:	ST1	
Project:	SLK	
Subject:	Heat technology building	
Rev. 6		
Int.:MDC	QC: CM	APP.: Date: 15-10-2025
LUNDSBY RENEWABLE SOLUTIONS		
Lundsby Biogas A/S, Hjarbækvej 65, 8831 Løgstrup Tlf.: +45 96 49 43 00 info@lundsbybiogas.dk		
Denne tegning er underlagt copyright og må ikke reproducere uden tilladelse fra Lundsbybiogas A/S		
Project nr.: 1768		FORMAT: A1
Drawing nr.: 9638		


LB-Building

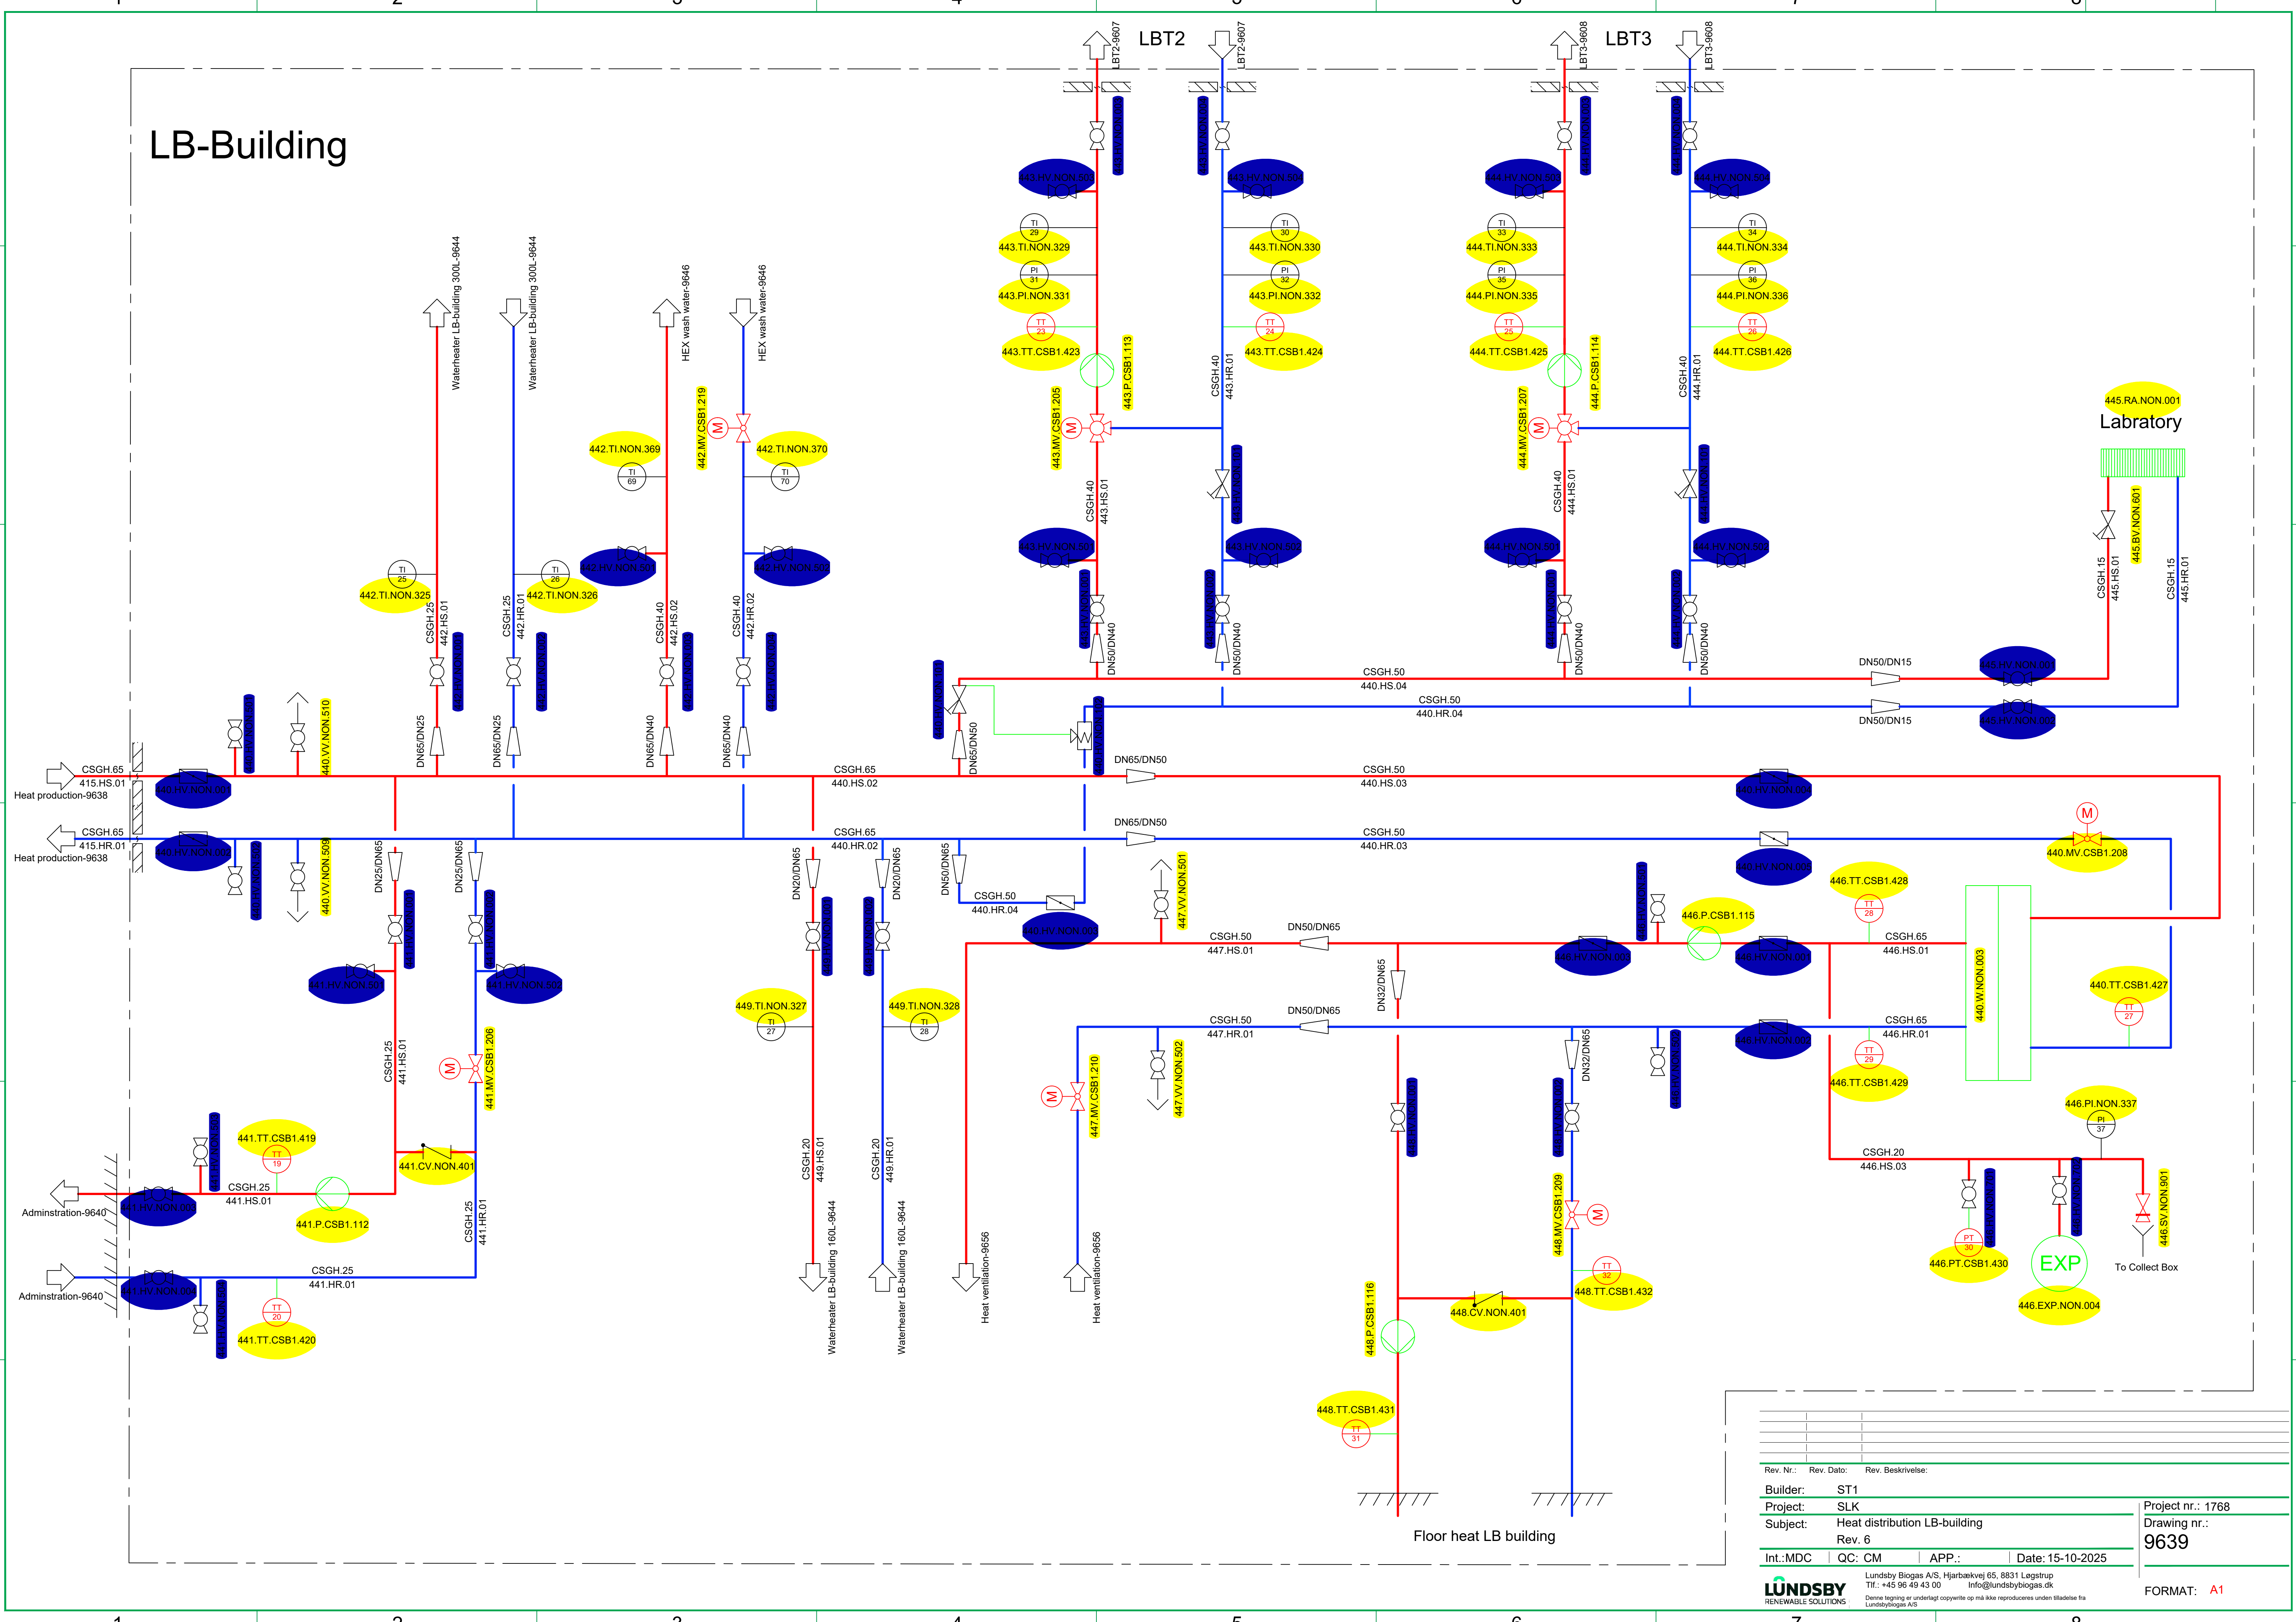

Rev. Nr.:	Rev. Dato:	Rev. Beskrivelse:
Builder:	ST1	
Project:	SLK	
Subject:	Heat distribution LB-building	
Rev. 6		
Int.:MDC	QC: CM	APP.: Date: 15-10-2025
LUNDSBY RENEWABLE SOLUTIONS		
Lundsby Biogas A/S, Hjarbækvej 65, 8831 Løgstrup Tlf.: +45 96 49 43 00 info@lundsbybiogas.dk Denne tegning er underlagt copyright op på ikke reproduceres uden tilladelse fra Lundsbybiogas A/S		
Project nr.: 1768		Drawing nr.: 9639
FORMAT: A1		

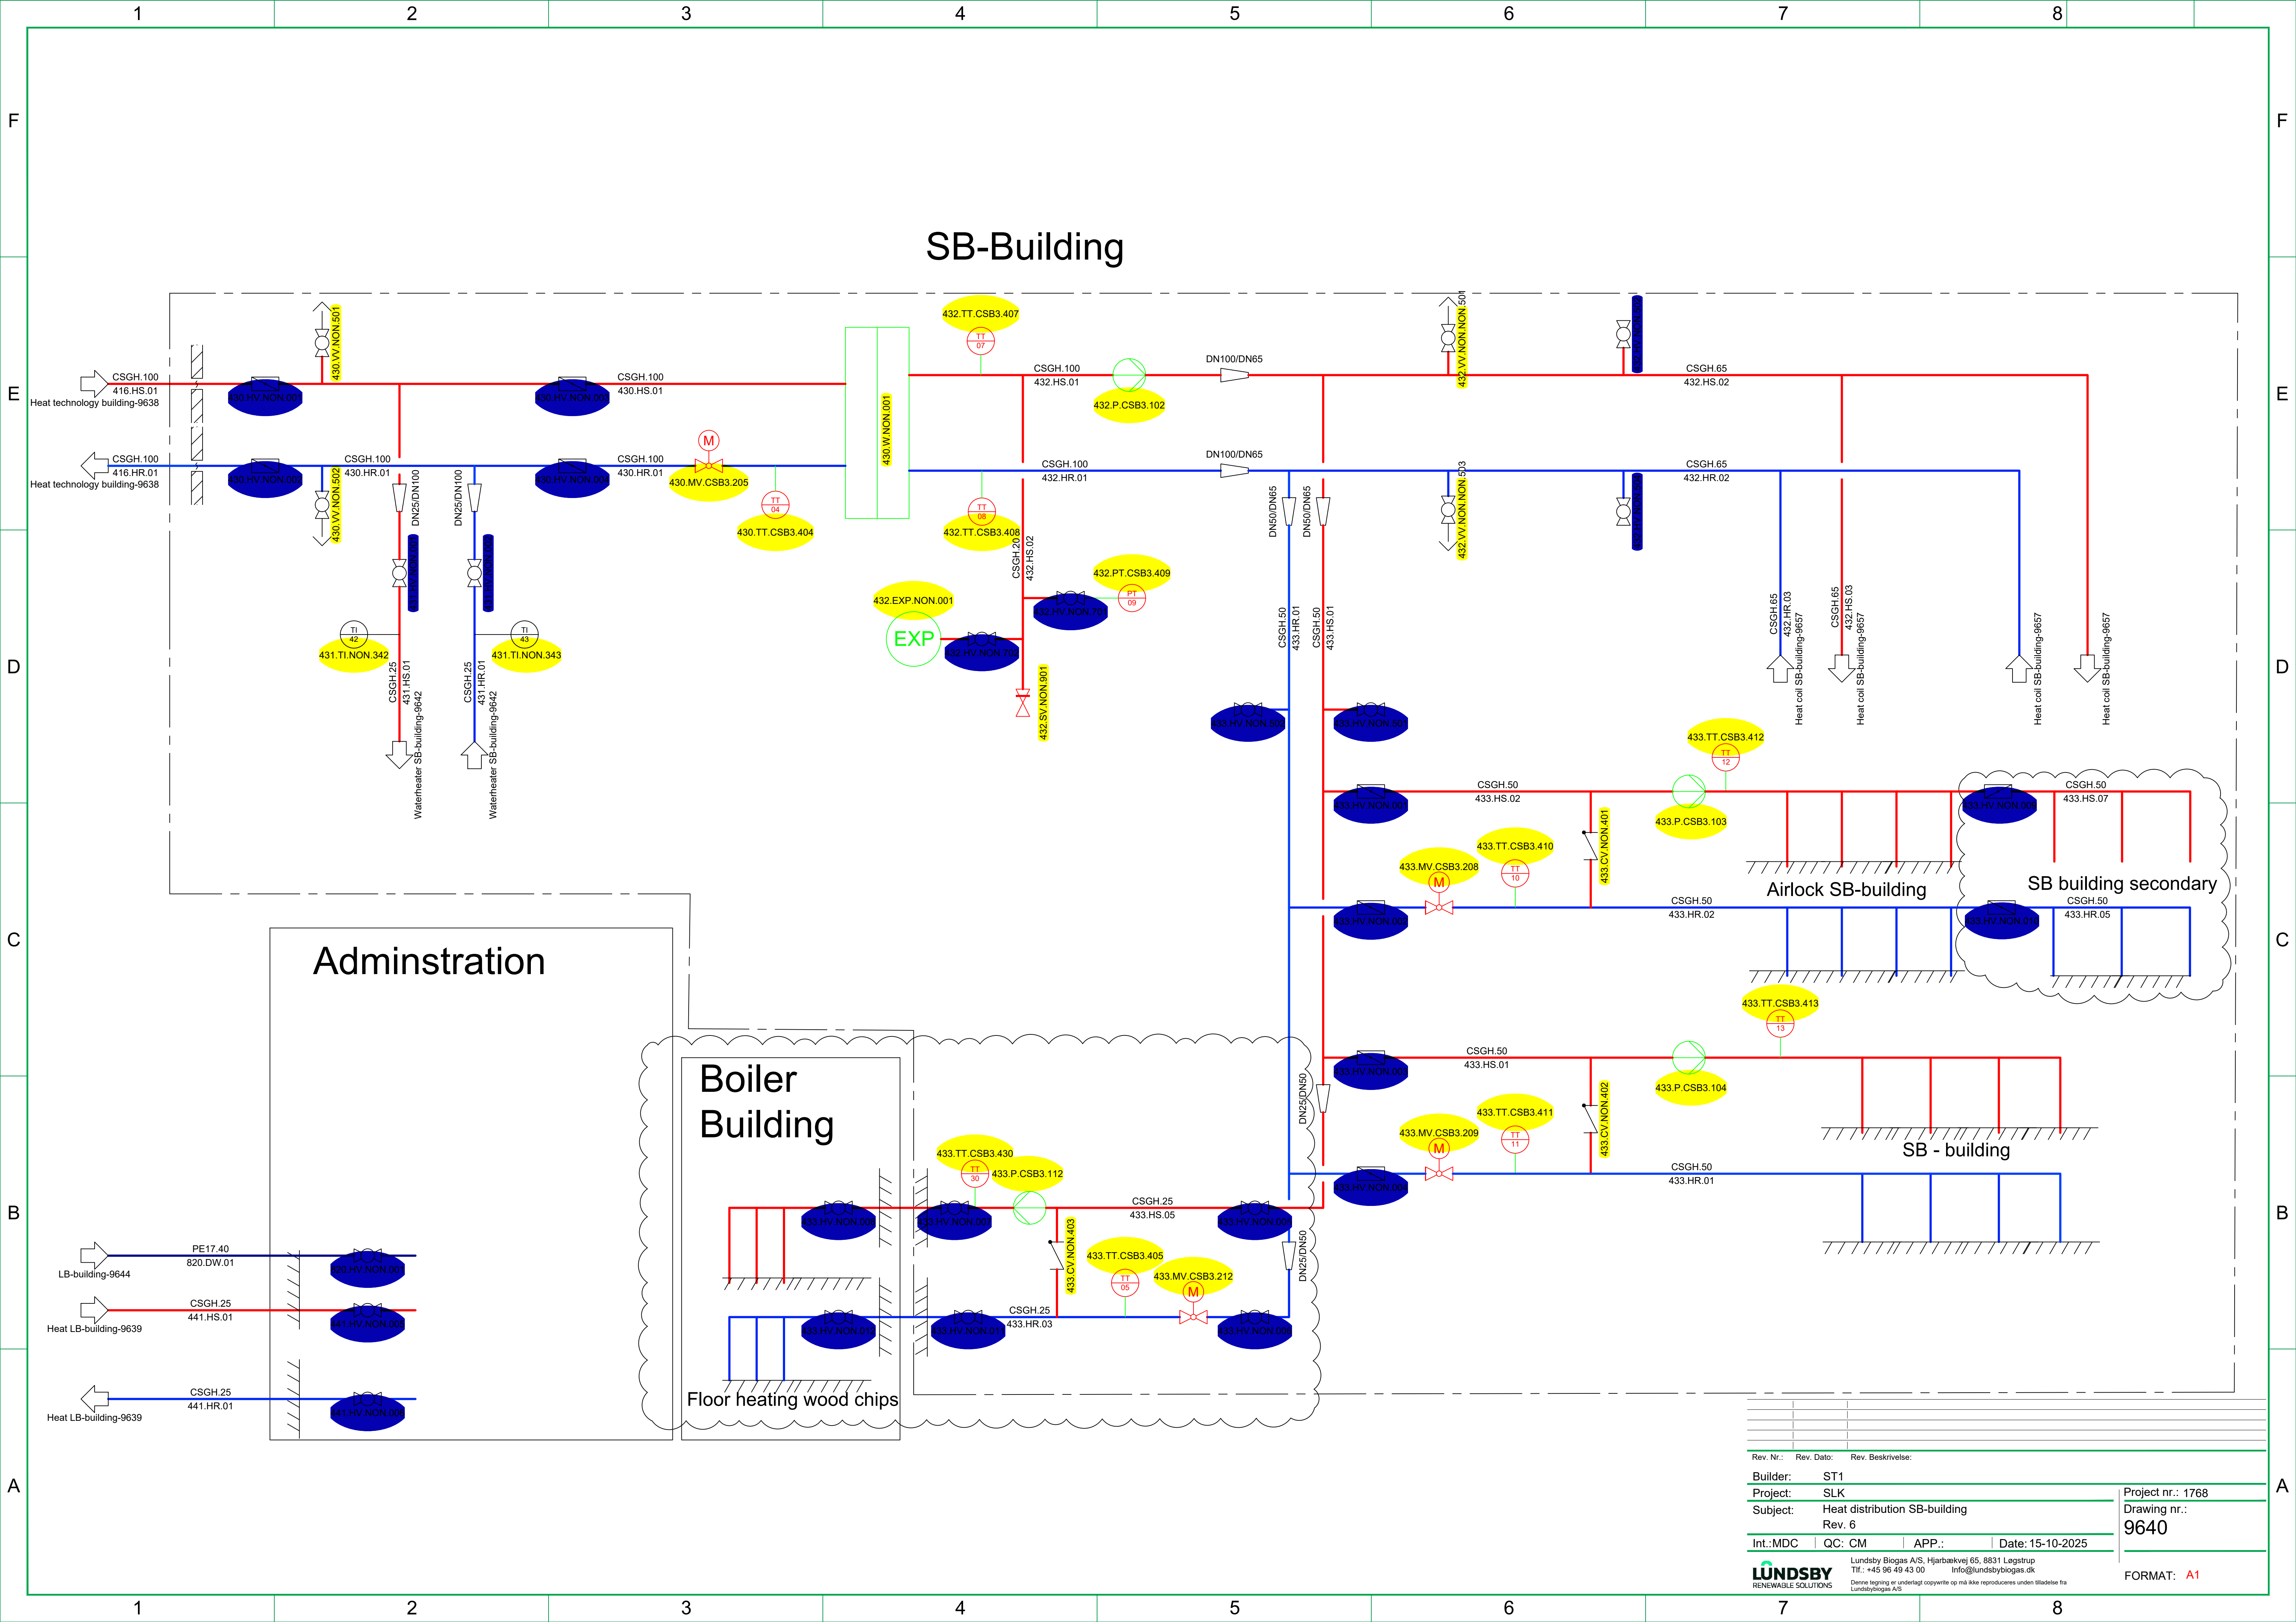

Rev. Nr.:	Rev. Dato:	Rev. Beskrivelse:	
Builder:	ST1		
Project:	SLK		
Subject:	Heat distribution SB-building		
Rev. 6			
Int.:MDC	QC: CM	APP.:	Date: 15-10-2025
LUNDSBY RENEWABLE SOLUTIONS			Lundsby Biogas A/S, Hjarbækvej 65, 8831 Løgstrup Tlf.: +45 96 49 43 00 info@lundsbybiogas.dk Denne tegning er underlagt copyright og må ikke reproduceres uden tilladelse fra Lundsbybiogas A/S
			Project nr.: 1768 Drawing nr.: 9640 FORMAT: A1

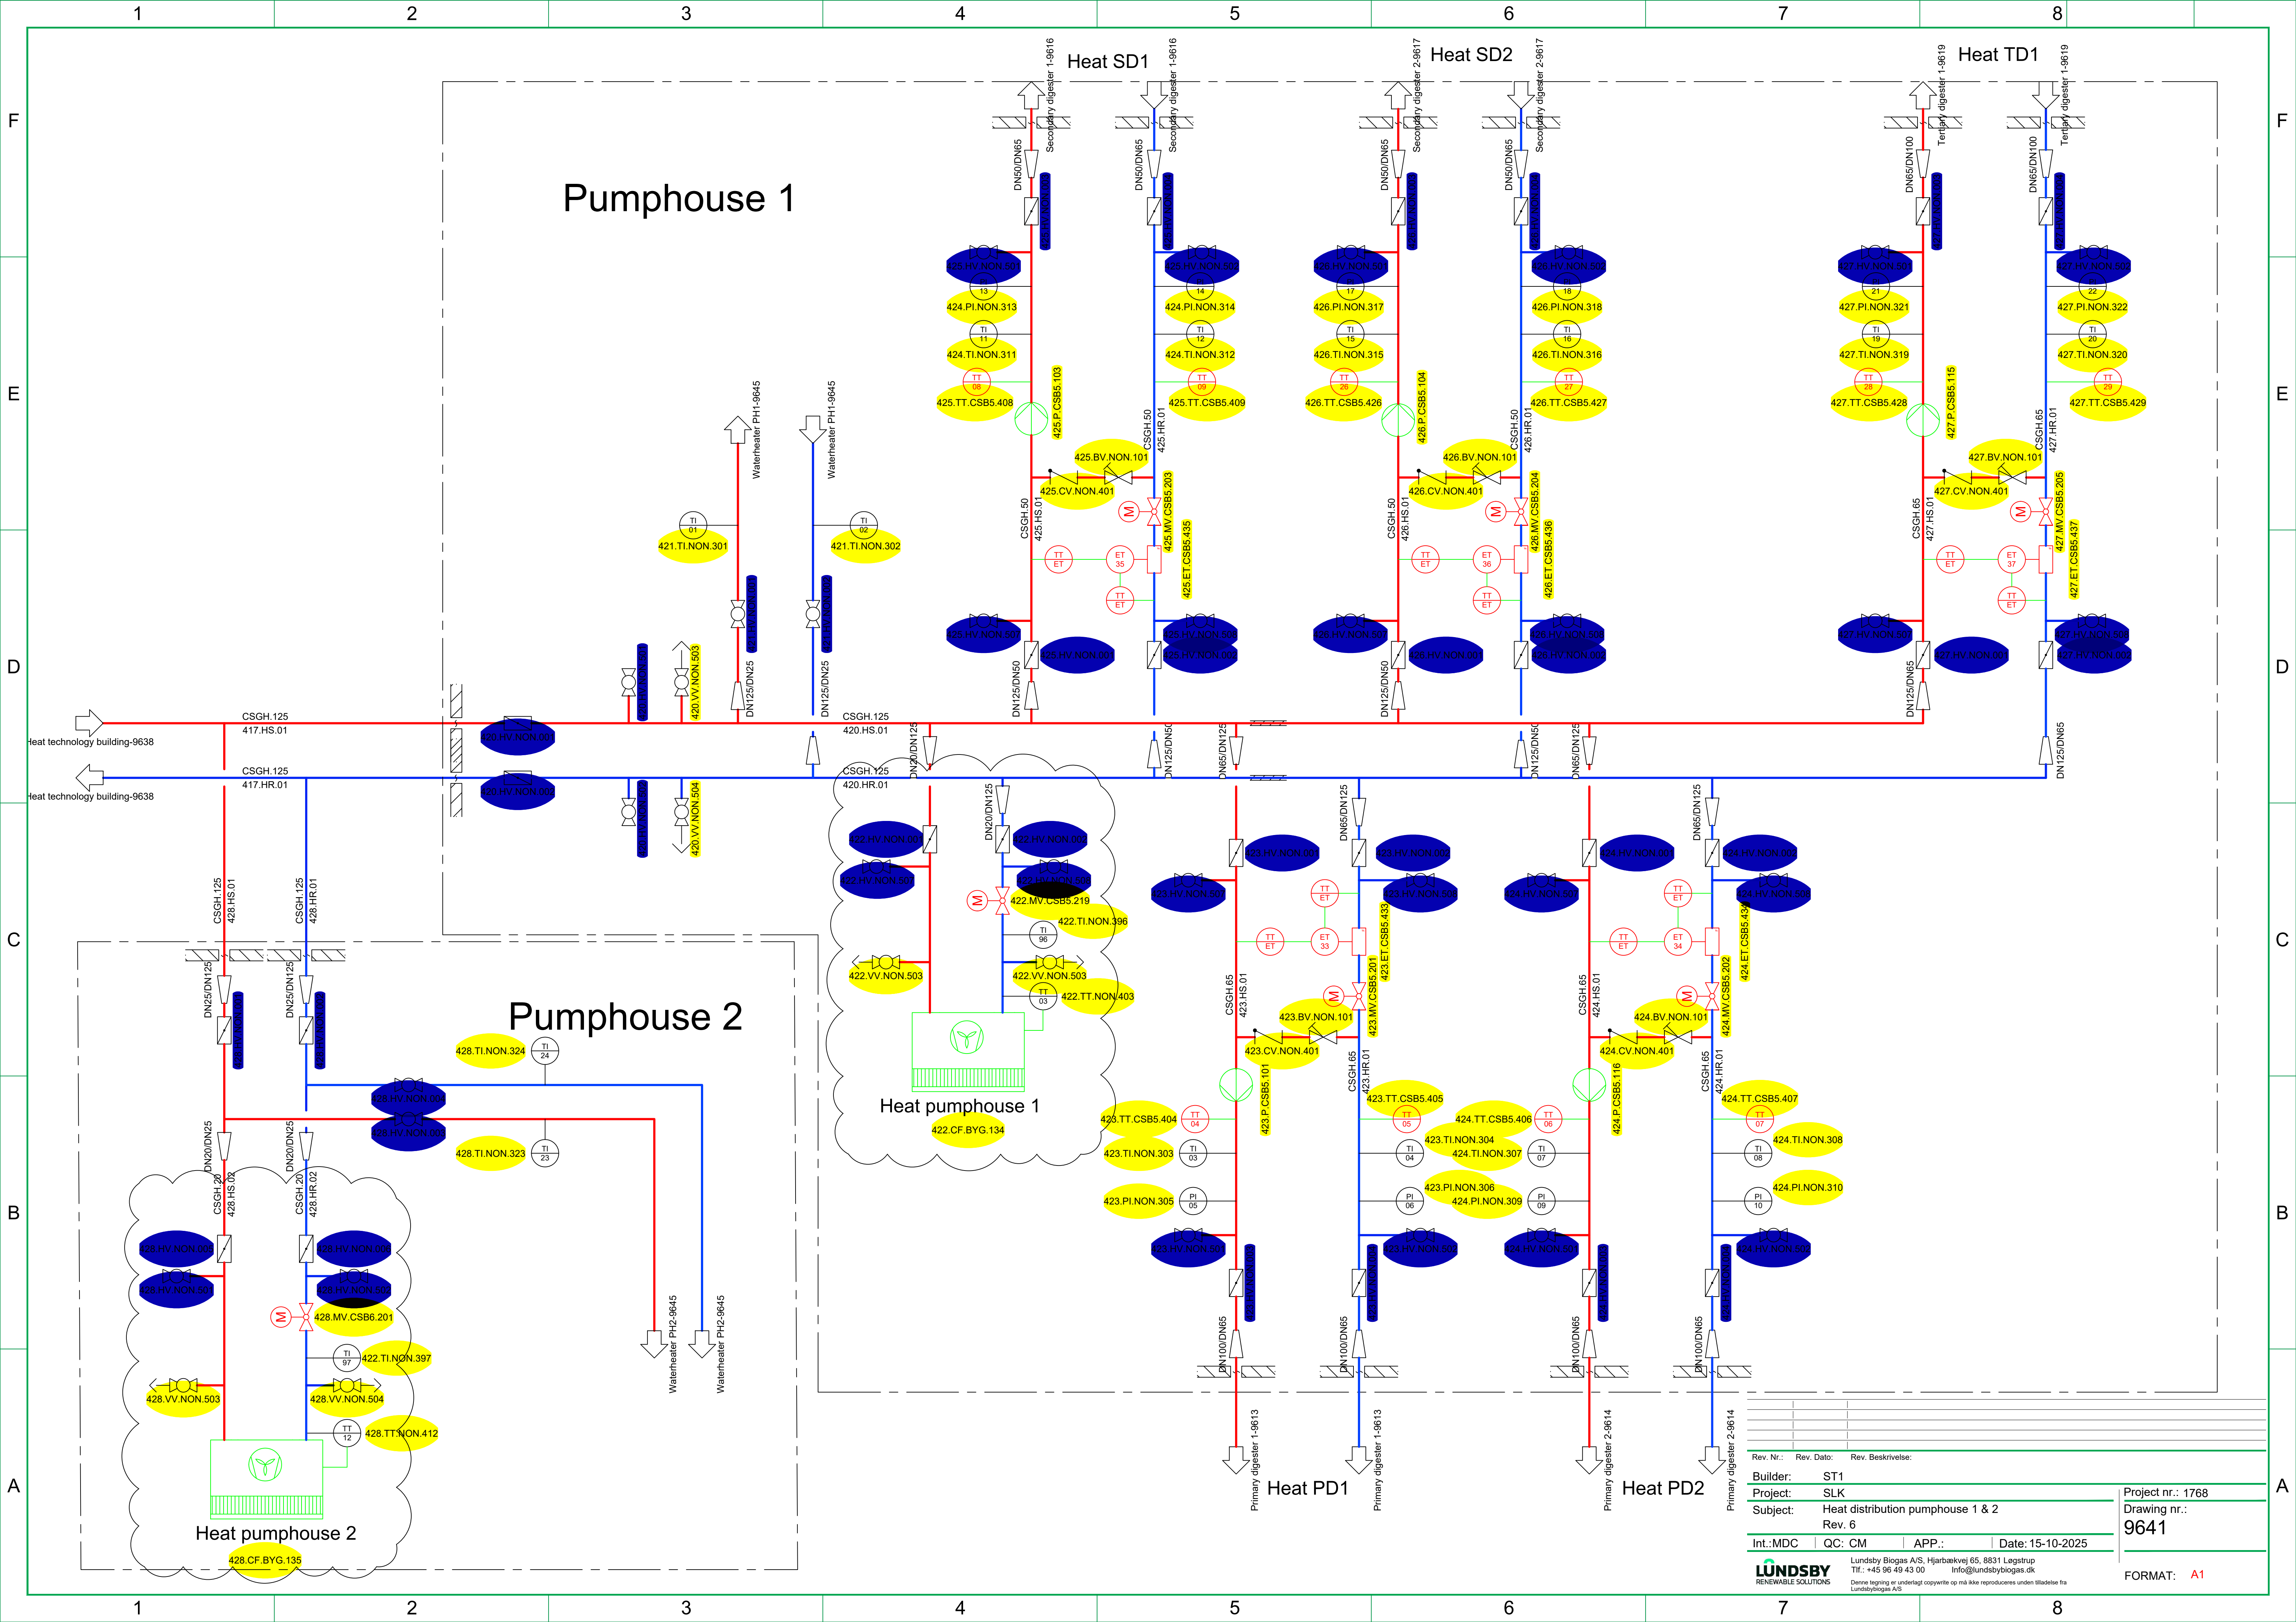


Rev. Nr.:	Rev. Dato:	Rev. Beskrivelse:
Builder:	ST1	
Project:	SLK	
Subject:	Heat distribution pumphouse 1 & 2	
Int.:MDC	QC: CM	APP.:
Date:	15-10-2025	
Project nr.:	1768	
Drawing nr.:	9641	
FORMAT:	A1	

LUNDSBY
RENEWABLE SOLUTIONS


Lundsby Biogas A/S, Hjarbækvej 65, 8831 Løgstrup
Tlf.: +45 96 49 43 00
info@lundsbybiogas.dk
Denne tegning er underlagt copyright op på ikke reproduceres uden tilladelse fra
Lundsbybiogas A/S

SB-Building

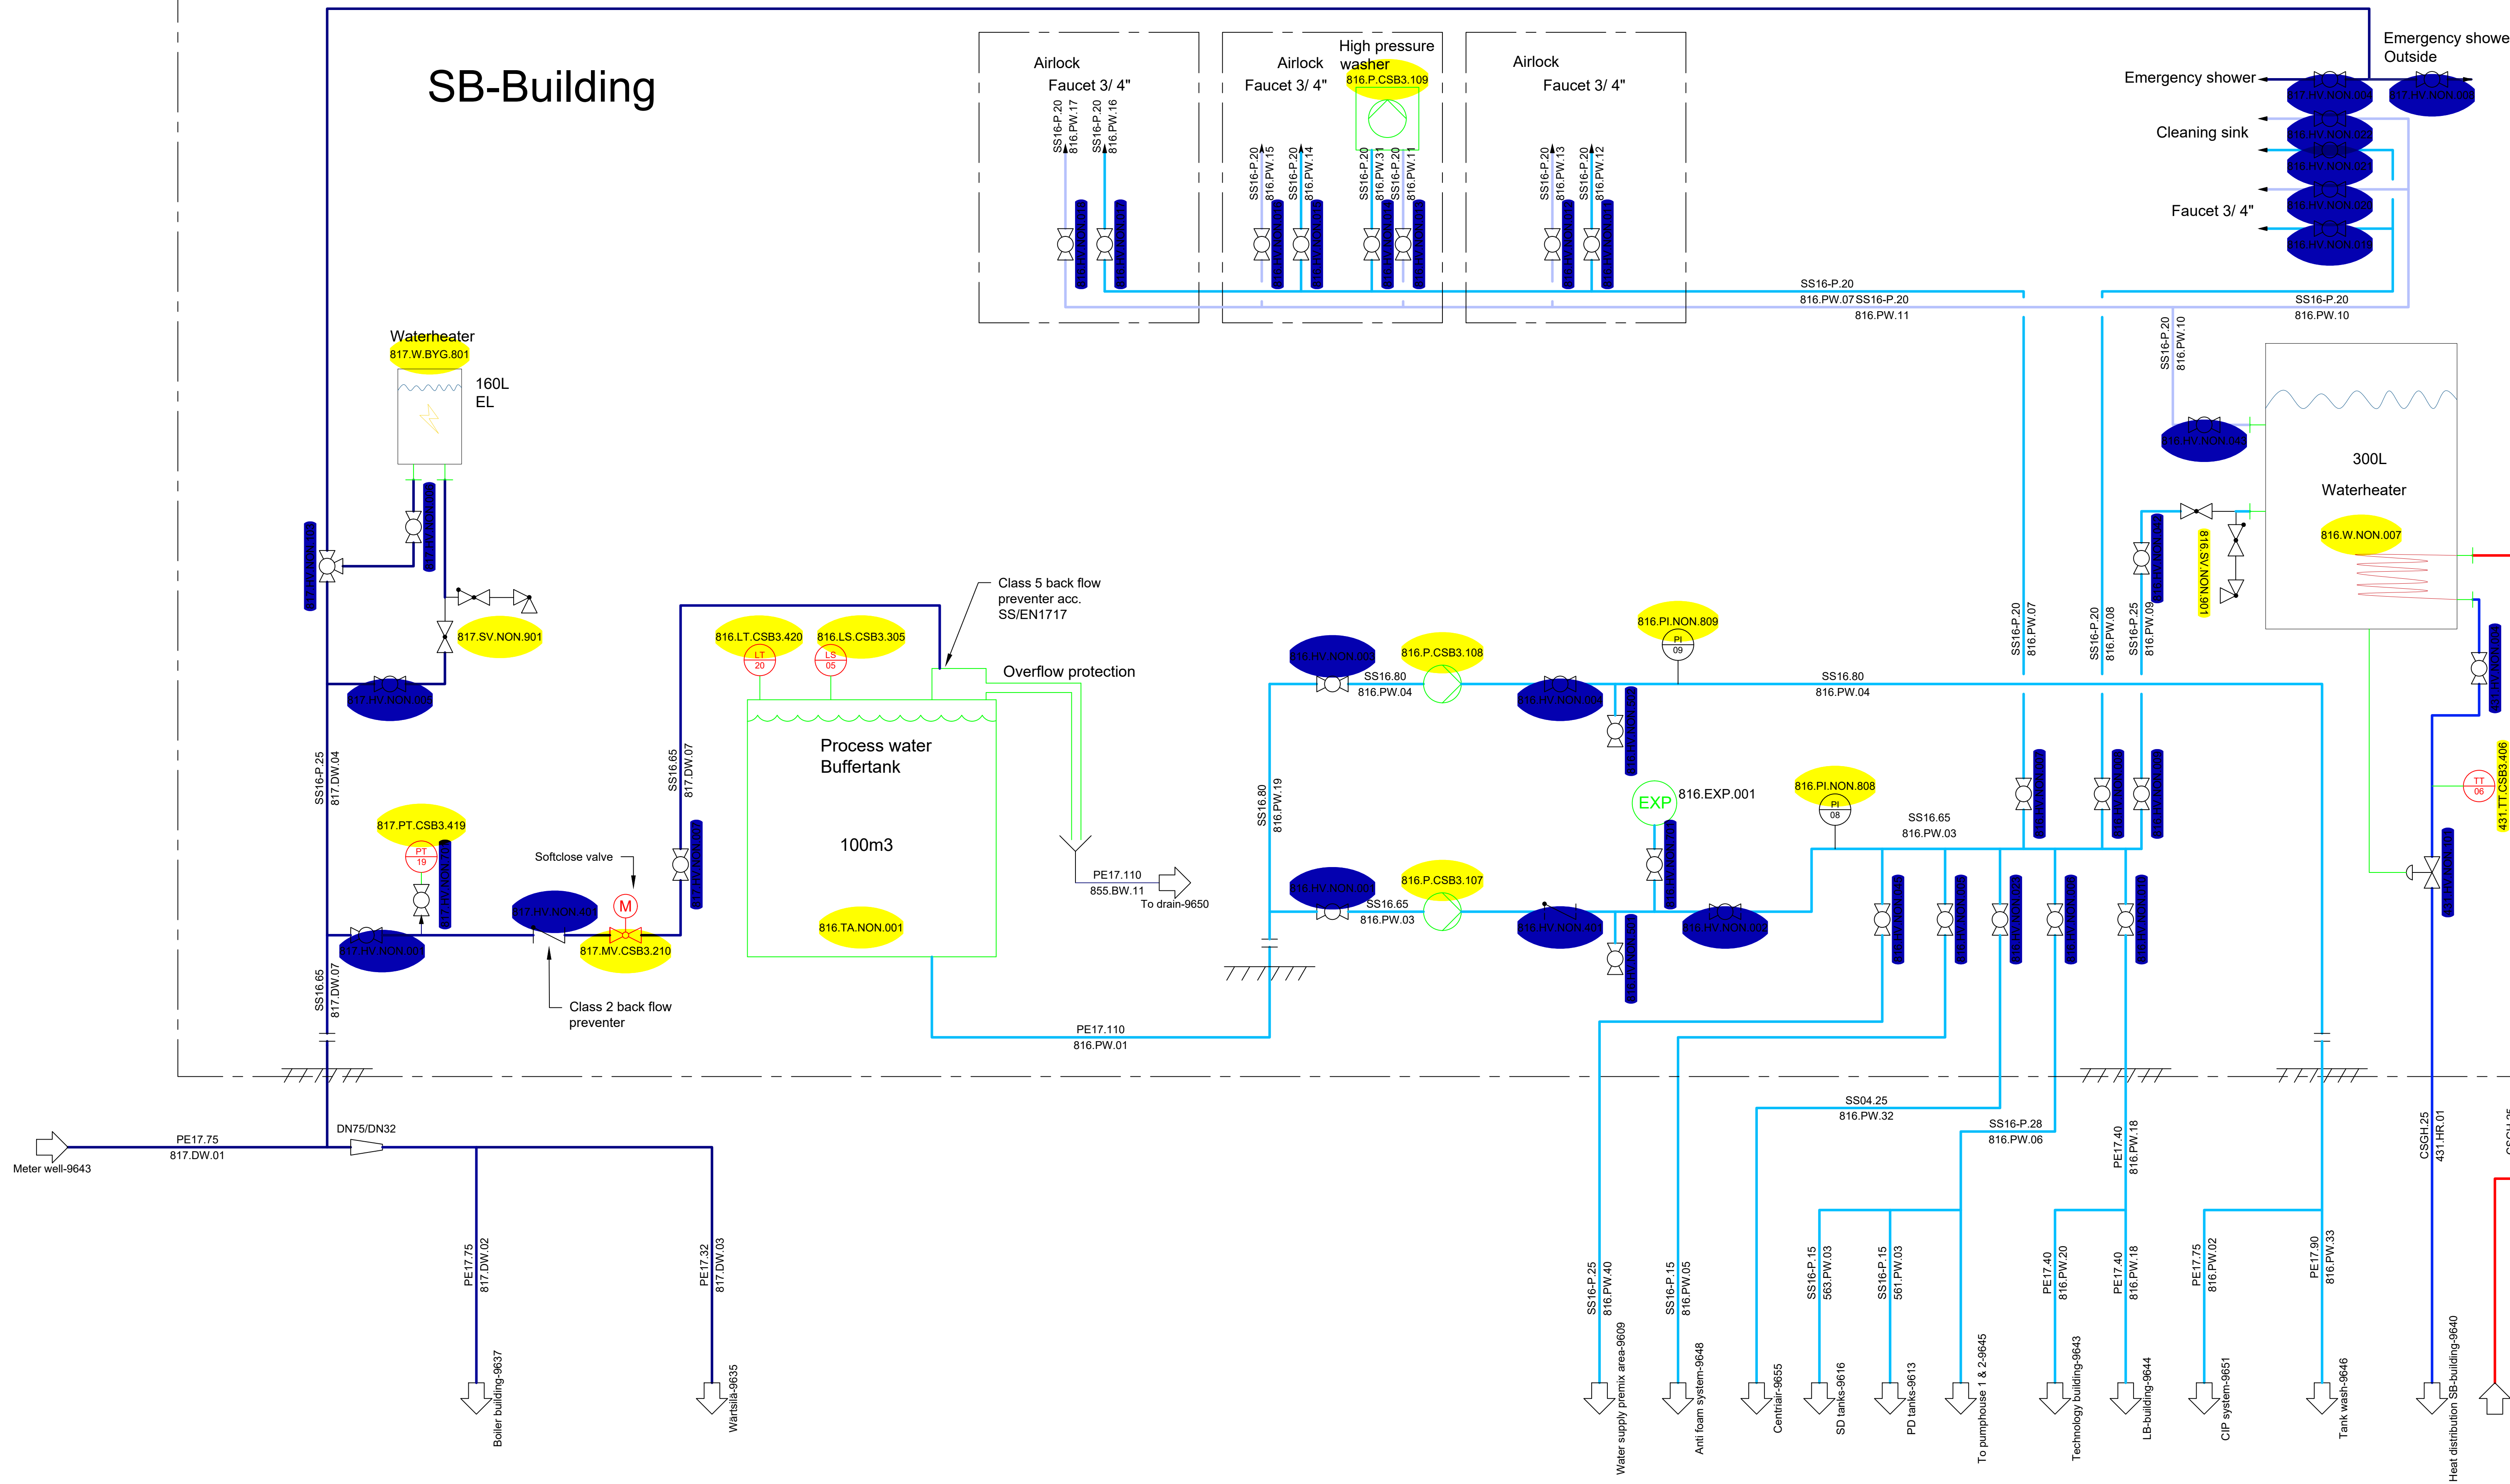


Rev. Nr.:	Rev. Dato:	Rev. Beskrivelse:
Builder:	ST1	
Project:	SLK	
Subject:	Water distribution SB-building	
Rev. 6		
Int.:MDC	QC:CM	APP.:
		Date: 15-10-2025
LUNDSBY RENEWABLE SOLUTIONS		
Lundsby Biogas A/S, Hjarbækvej 65, 8831 Løgstrup Tlf.: +45 96 49 43 00 info@lundsbybiogas.dk		
Denne tegning er underlagt copyright op på ikke reproduceres uden tilladelse fra Lundsbybiogas A/S		
Project nr.: 1768		
Drawing nr.: 9642		
FORMAT: A1		

Technology building

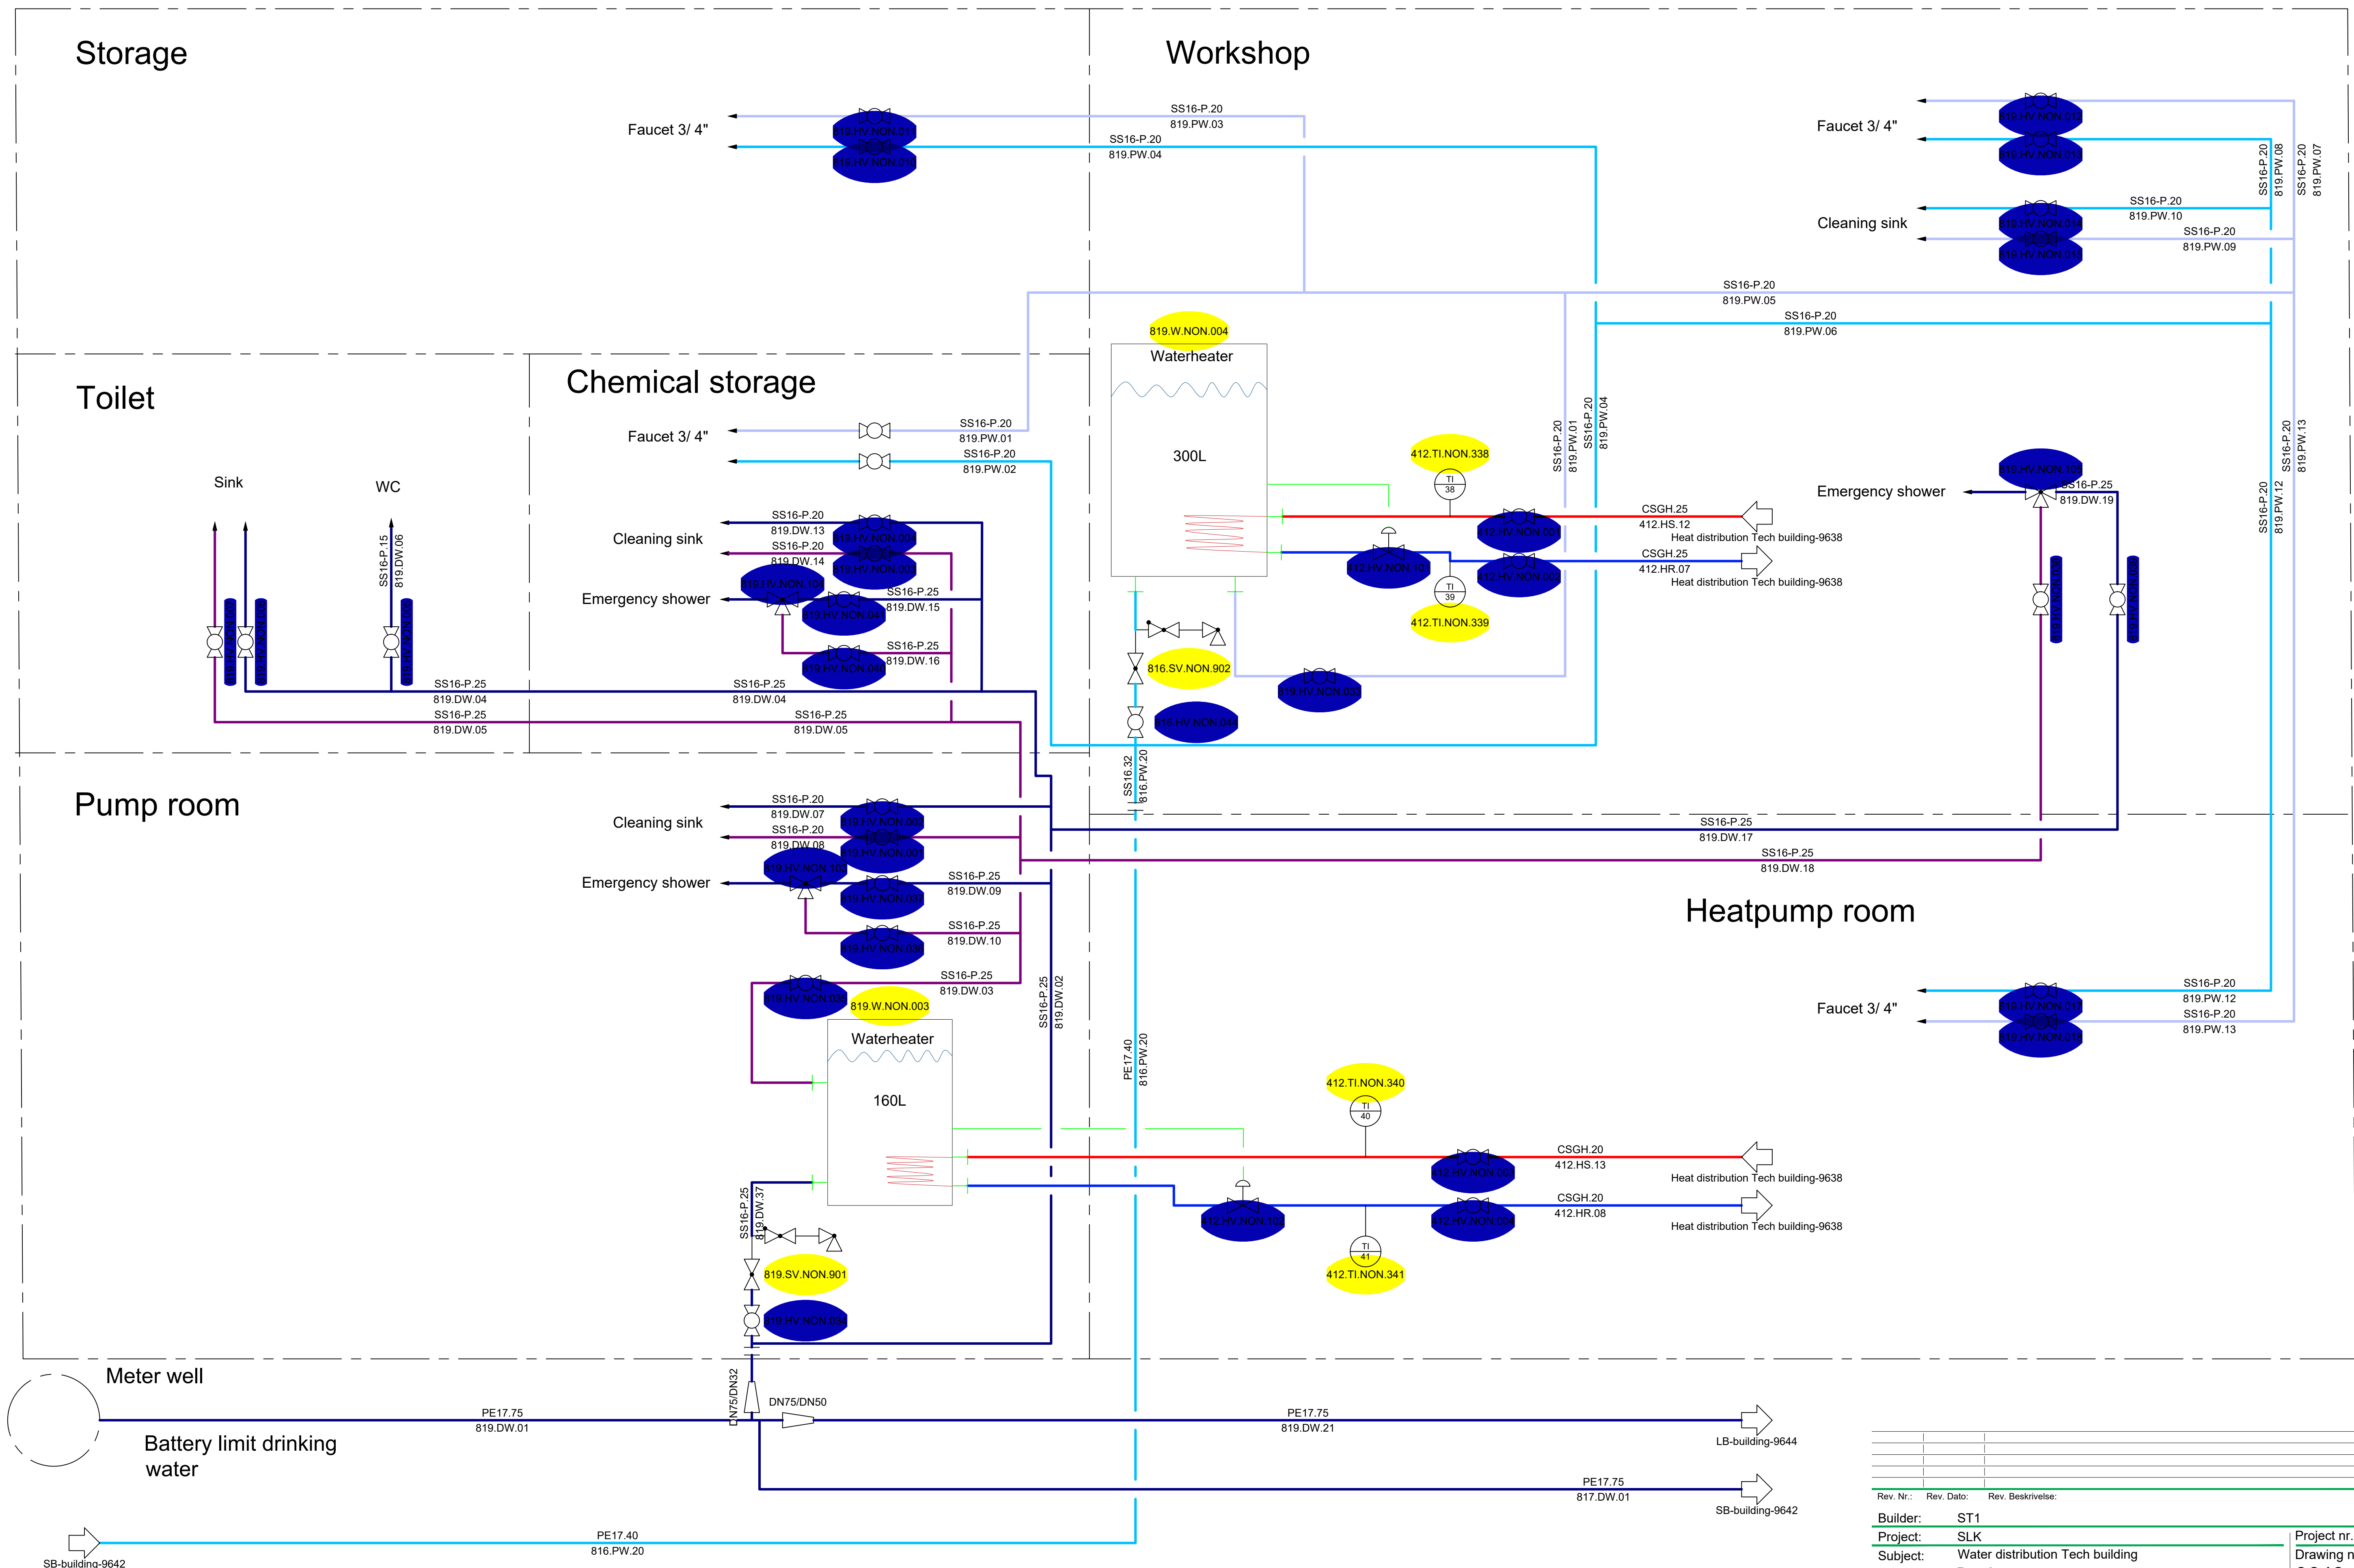


Rev. Nr.:	Rev. Dato:	Rev. Beskrivelse:
Builder:	ST1	
Project:	SLK	
Subject:	Water distribution Tech building	
Rev. 6		
Int.:MDC	QC:CM	APP.:
		Date: 15-10-2025
LUNDSBY RENEWABLE SOLUTIONS		
Lundsby Biogas A/S, Hjarbækvej 65, 8831 Løgstrup Tlf.: +45 96 49 43 00 info@lundsbybiogas.dk Denne tegning er underlagt copyright og må ikke reproduceres uden tilladelse fra Lundsbybiogas A/S		
Project nr.: 1768 Drawing nr.: 9643		FORMAT: A1

LB-building

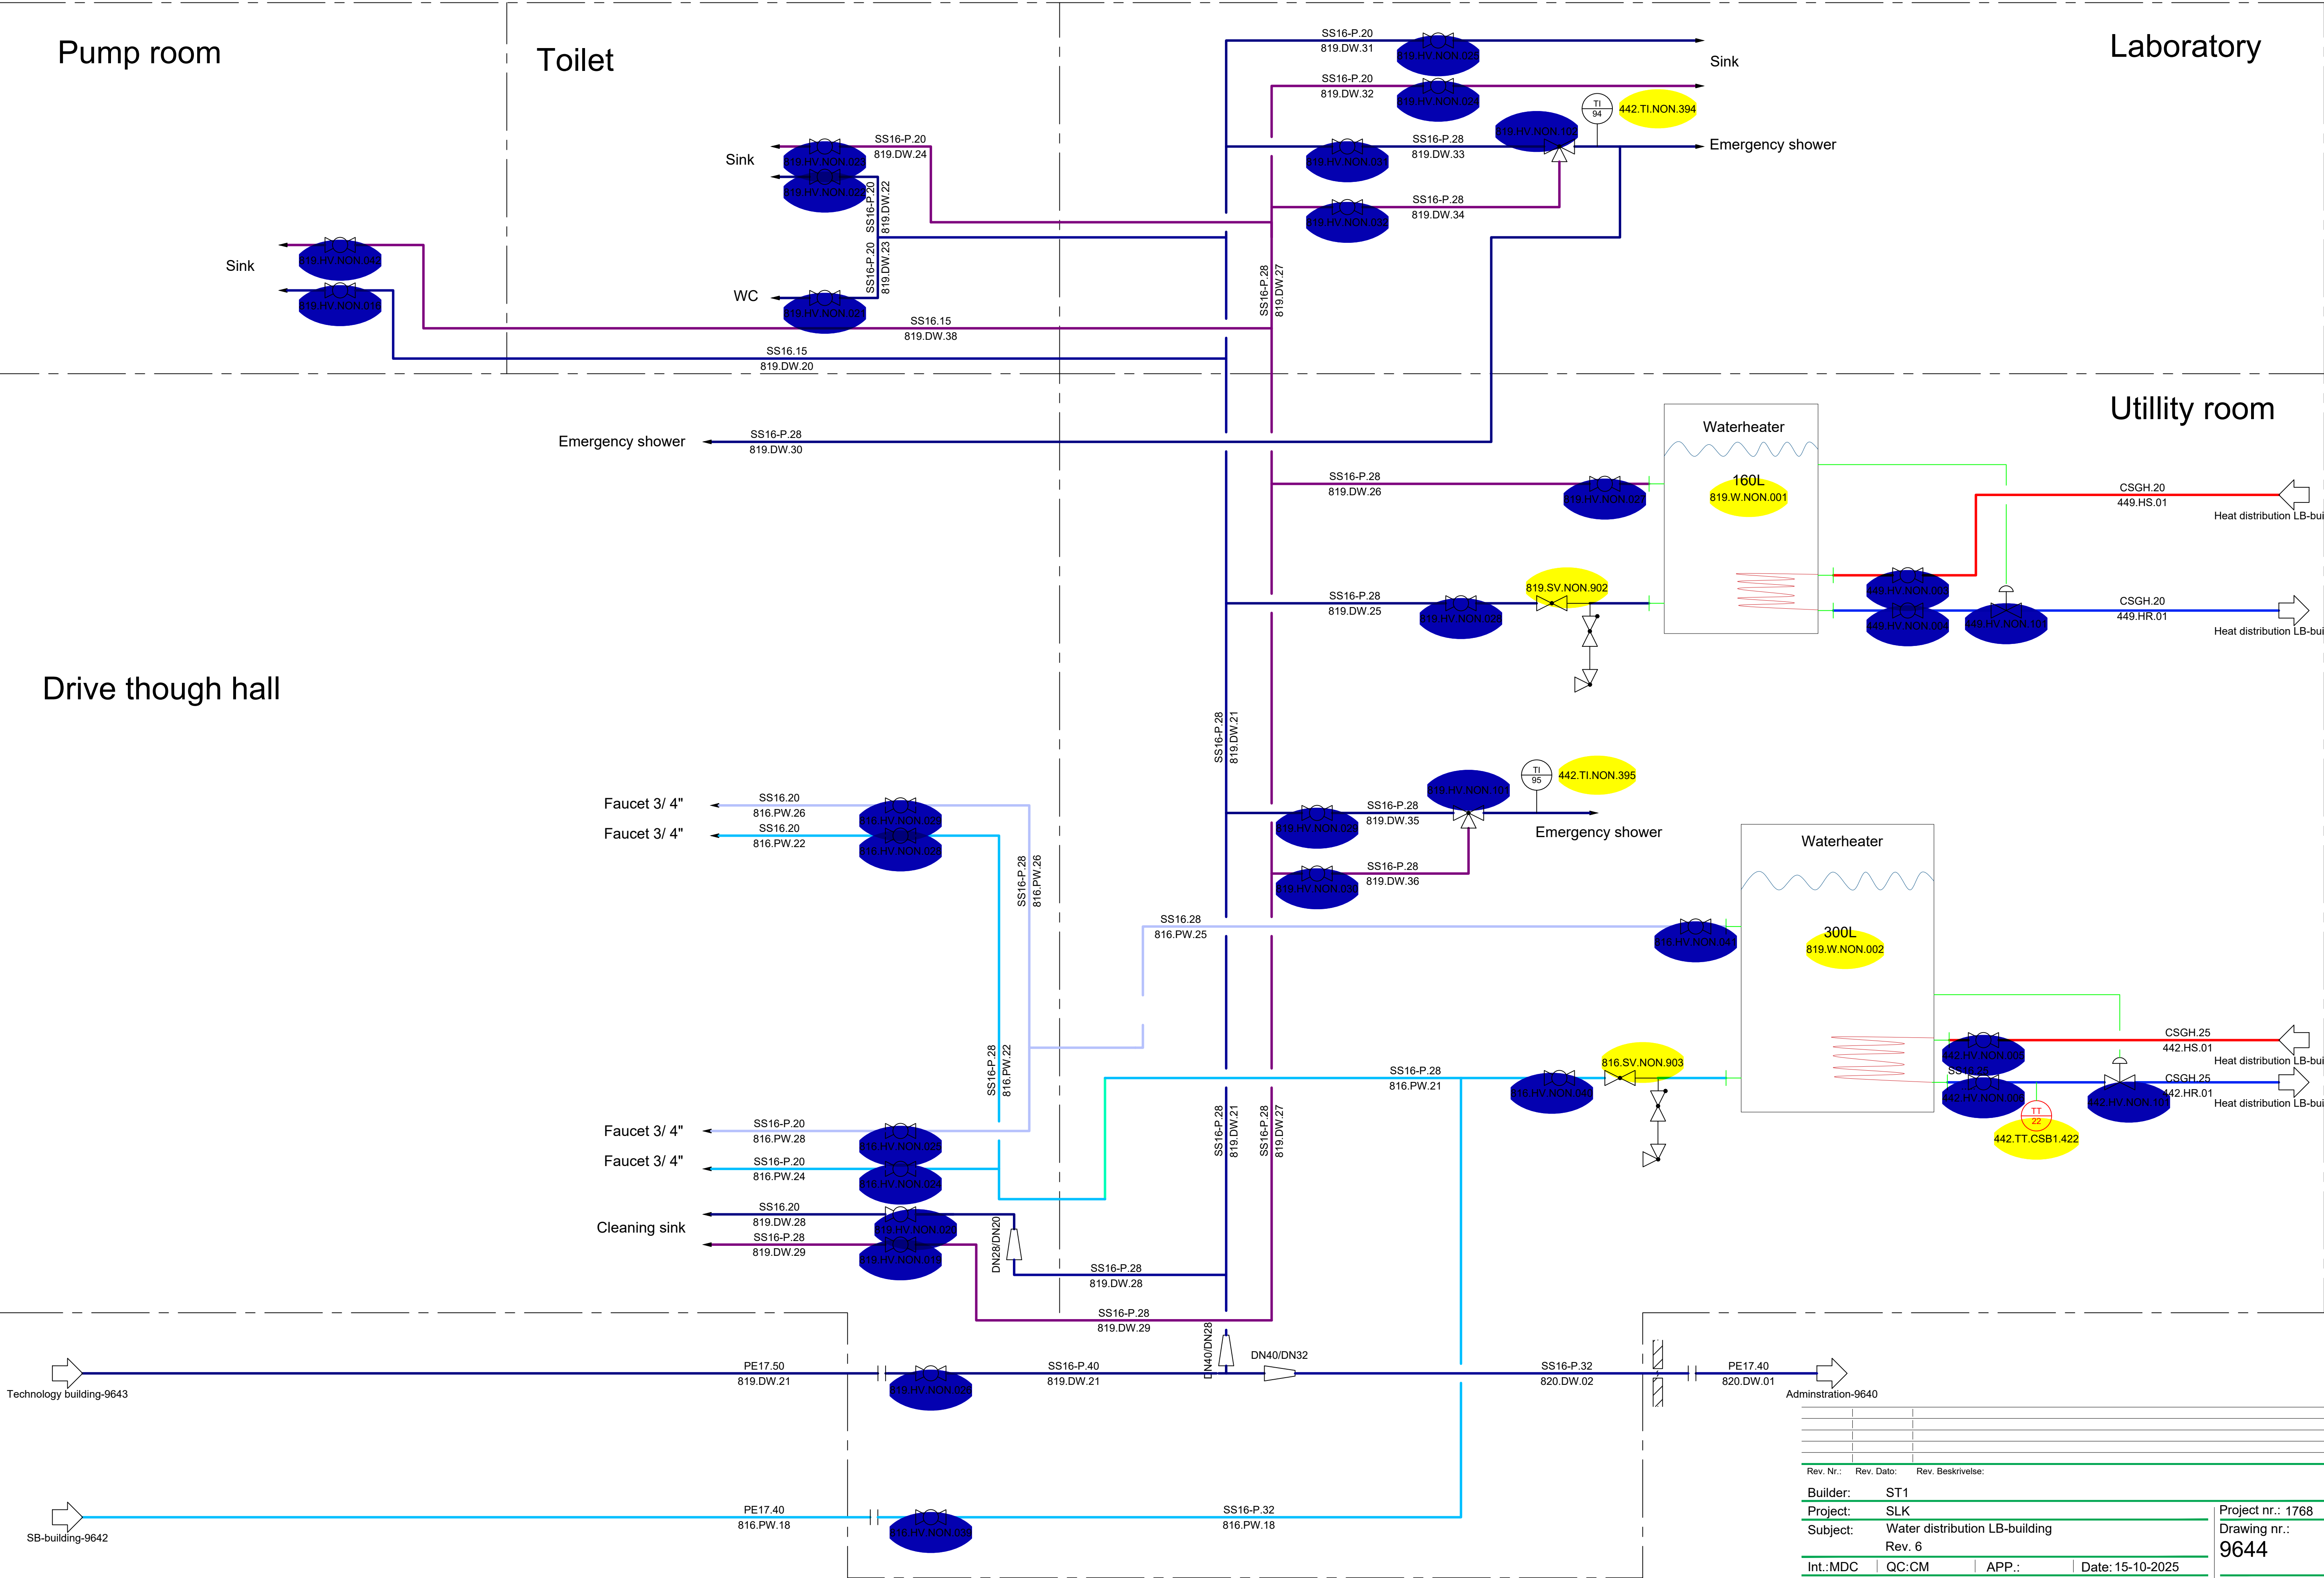


Rev. Nr.:	Rev. Dato:	Rev. Beskrivelse:
Builder:	ST1	
Project:	SLK	
Subject:	Water distribution LB-building	
Rev. 6		
Int.:MDC	QC:CM	APP.:
		Date: 15-10-2025
LUNDSBY RENEWABLE SOLUTIONS		
Lundsby Biogas A/S, Hjarbækvej 65, 8831 Løgstrup Tlf.: +45 96 49 43 00 info@lundsbybiogas.dk Denne tegning er underlagt copyright og må ikke reproduceres uden tilladelse fra Lundsbybiogas A/S		
Project nr.: 1768 Drawing nr.: 9644		FORMAT: A1


Pumphouse 1

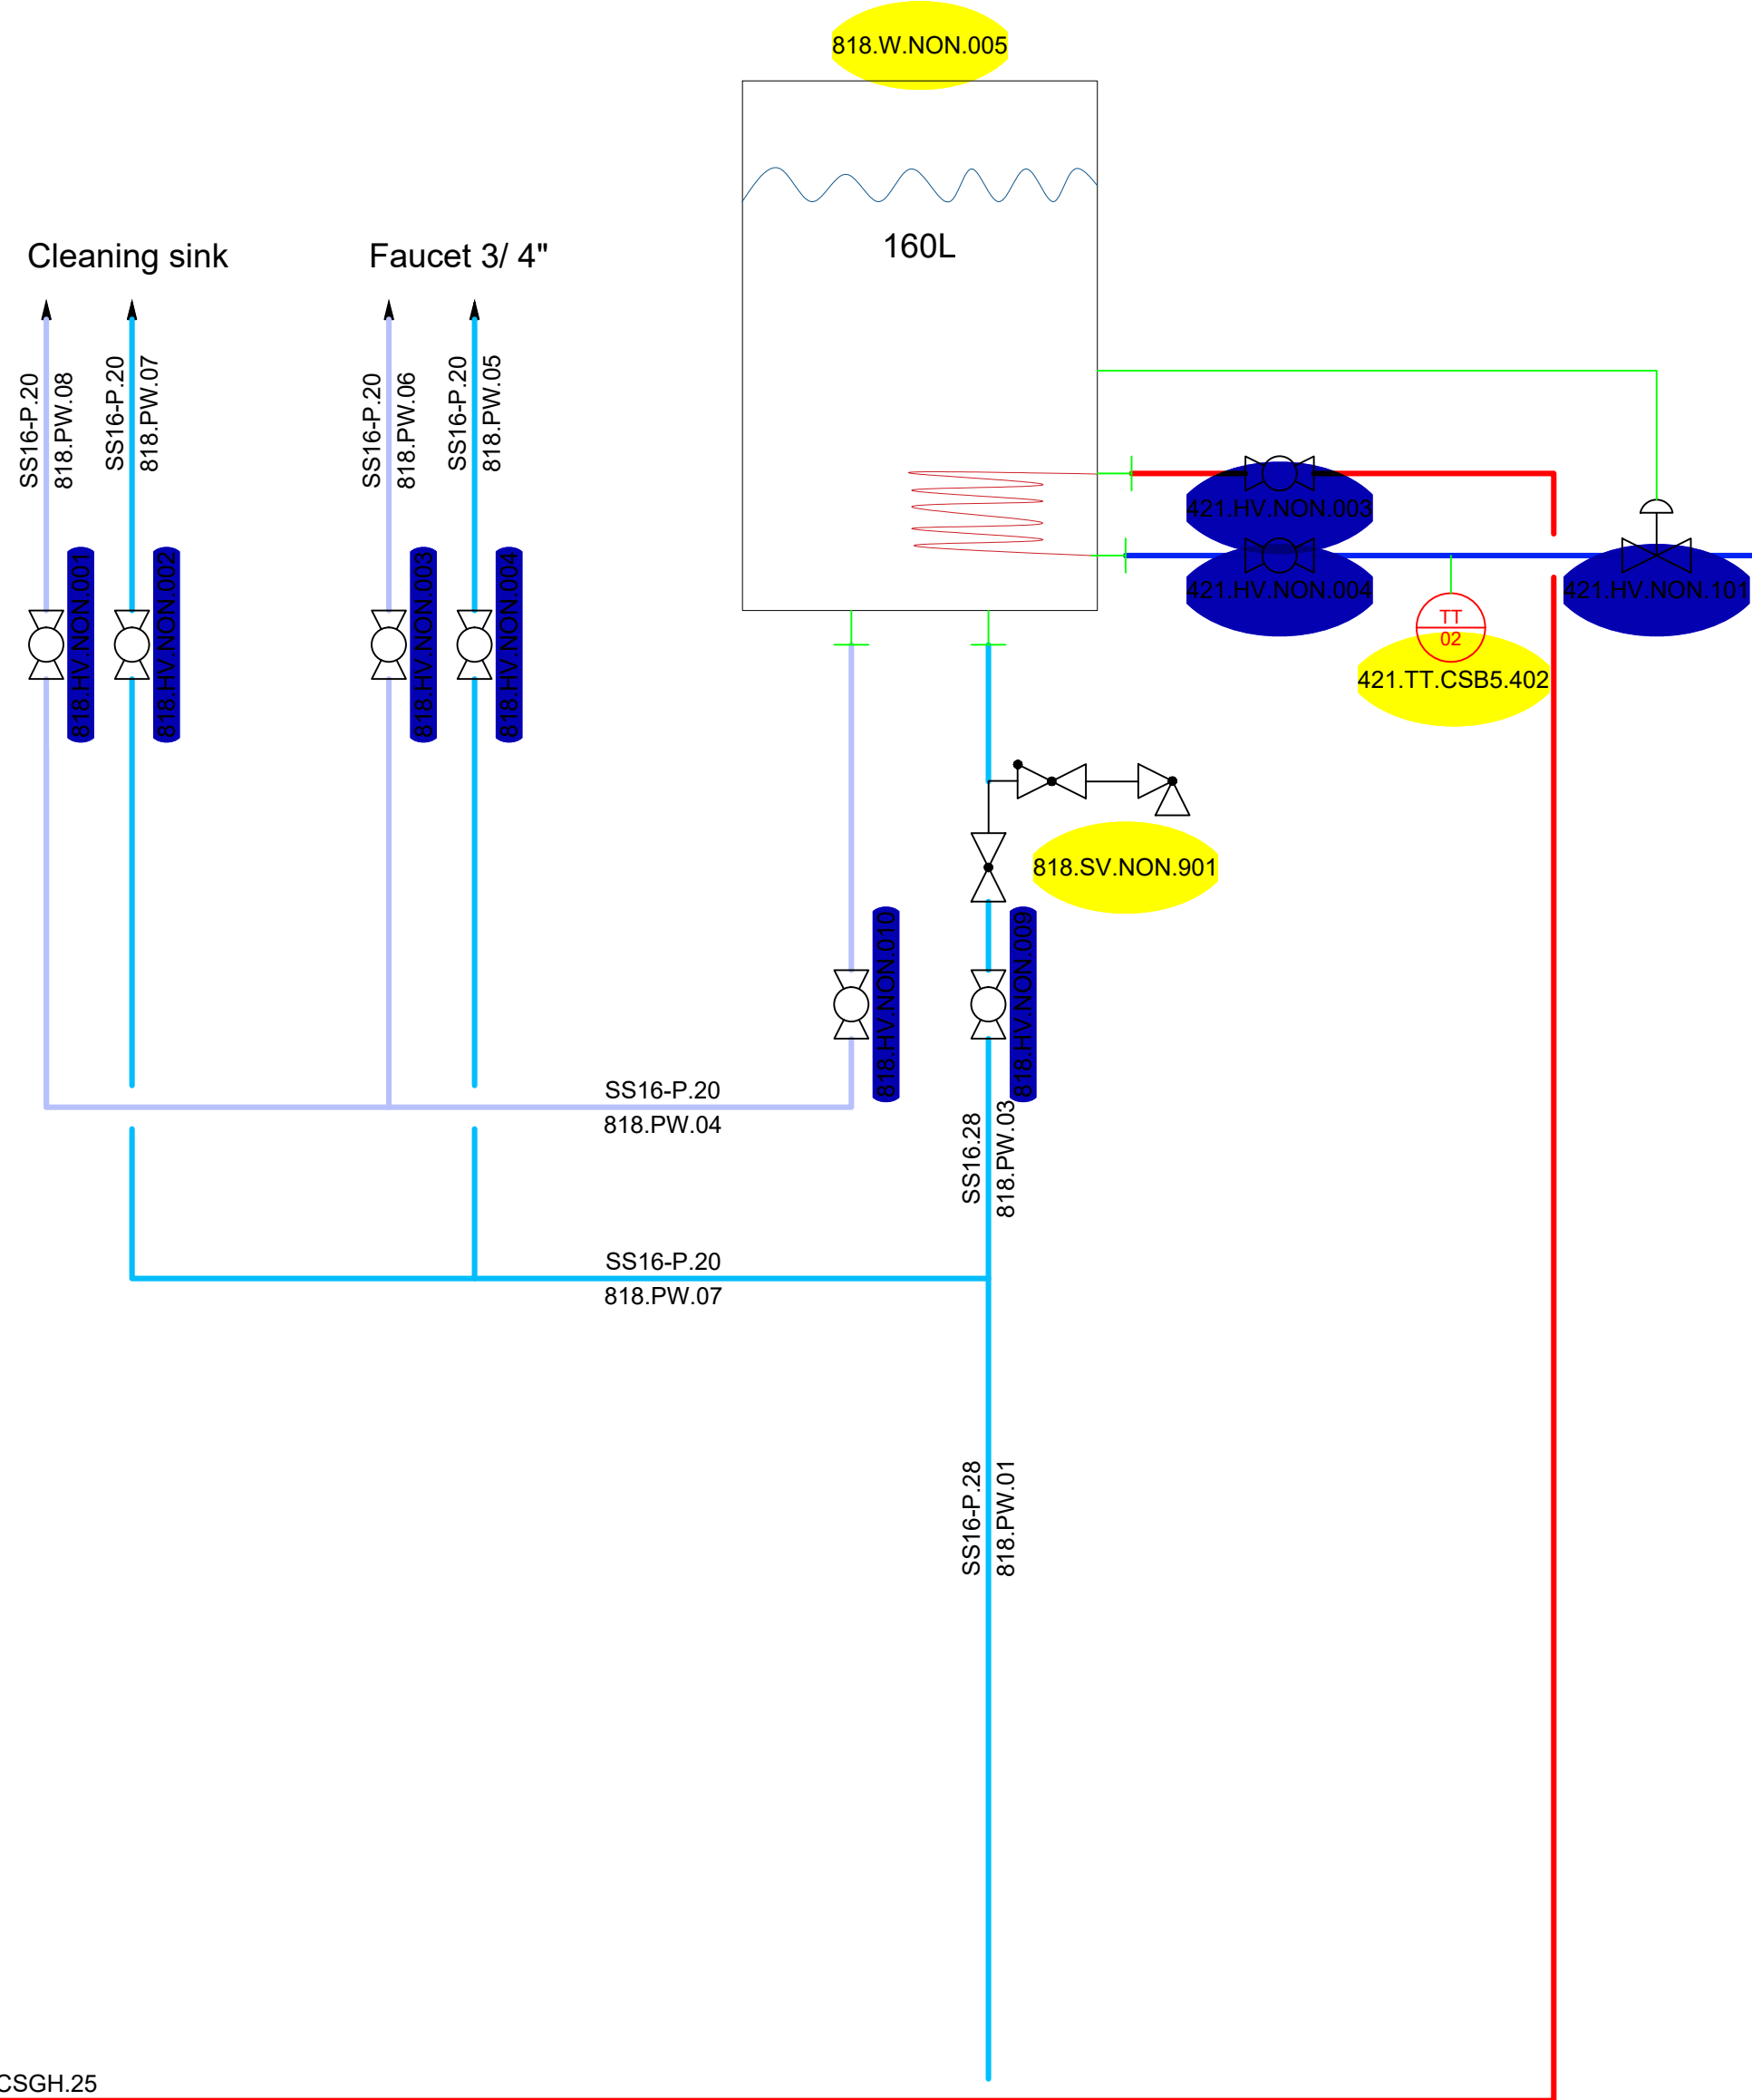


Pumphouse 2

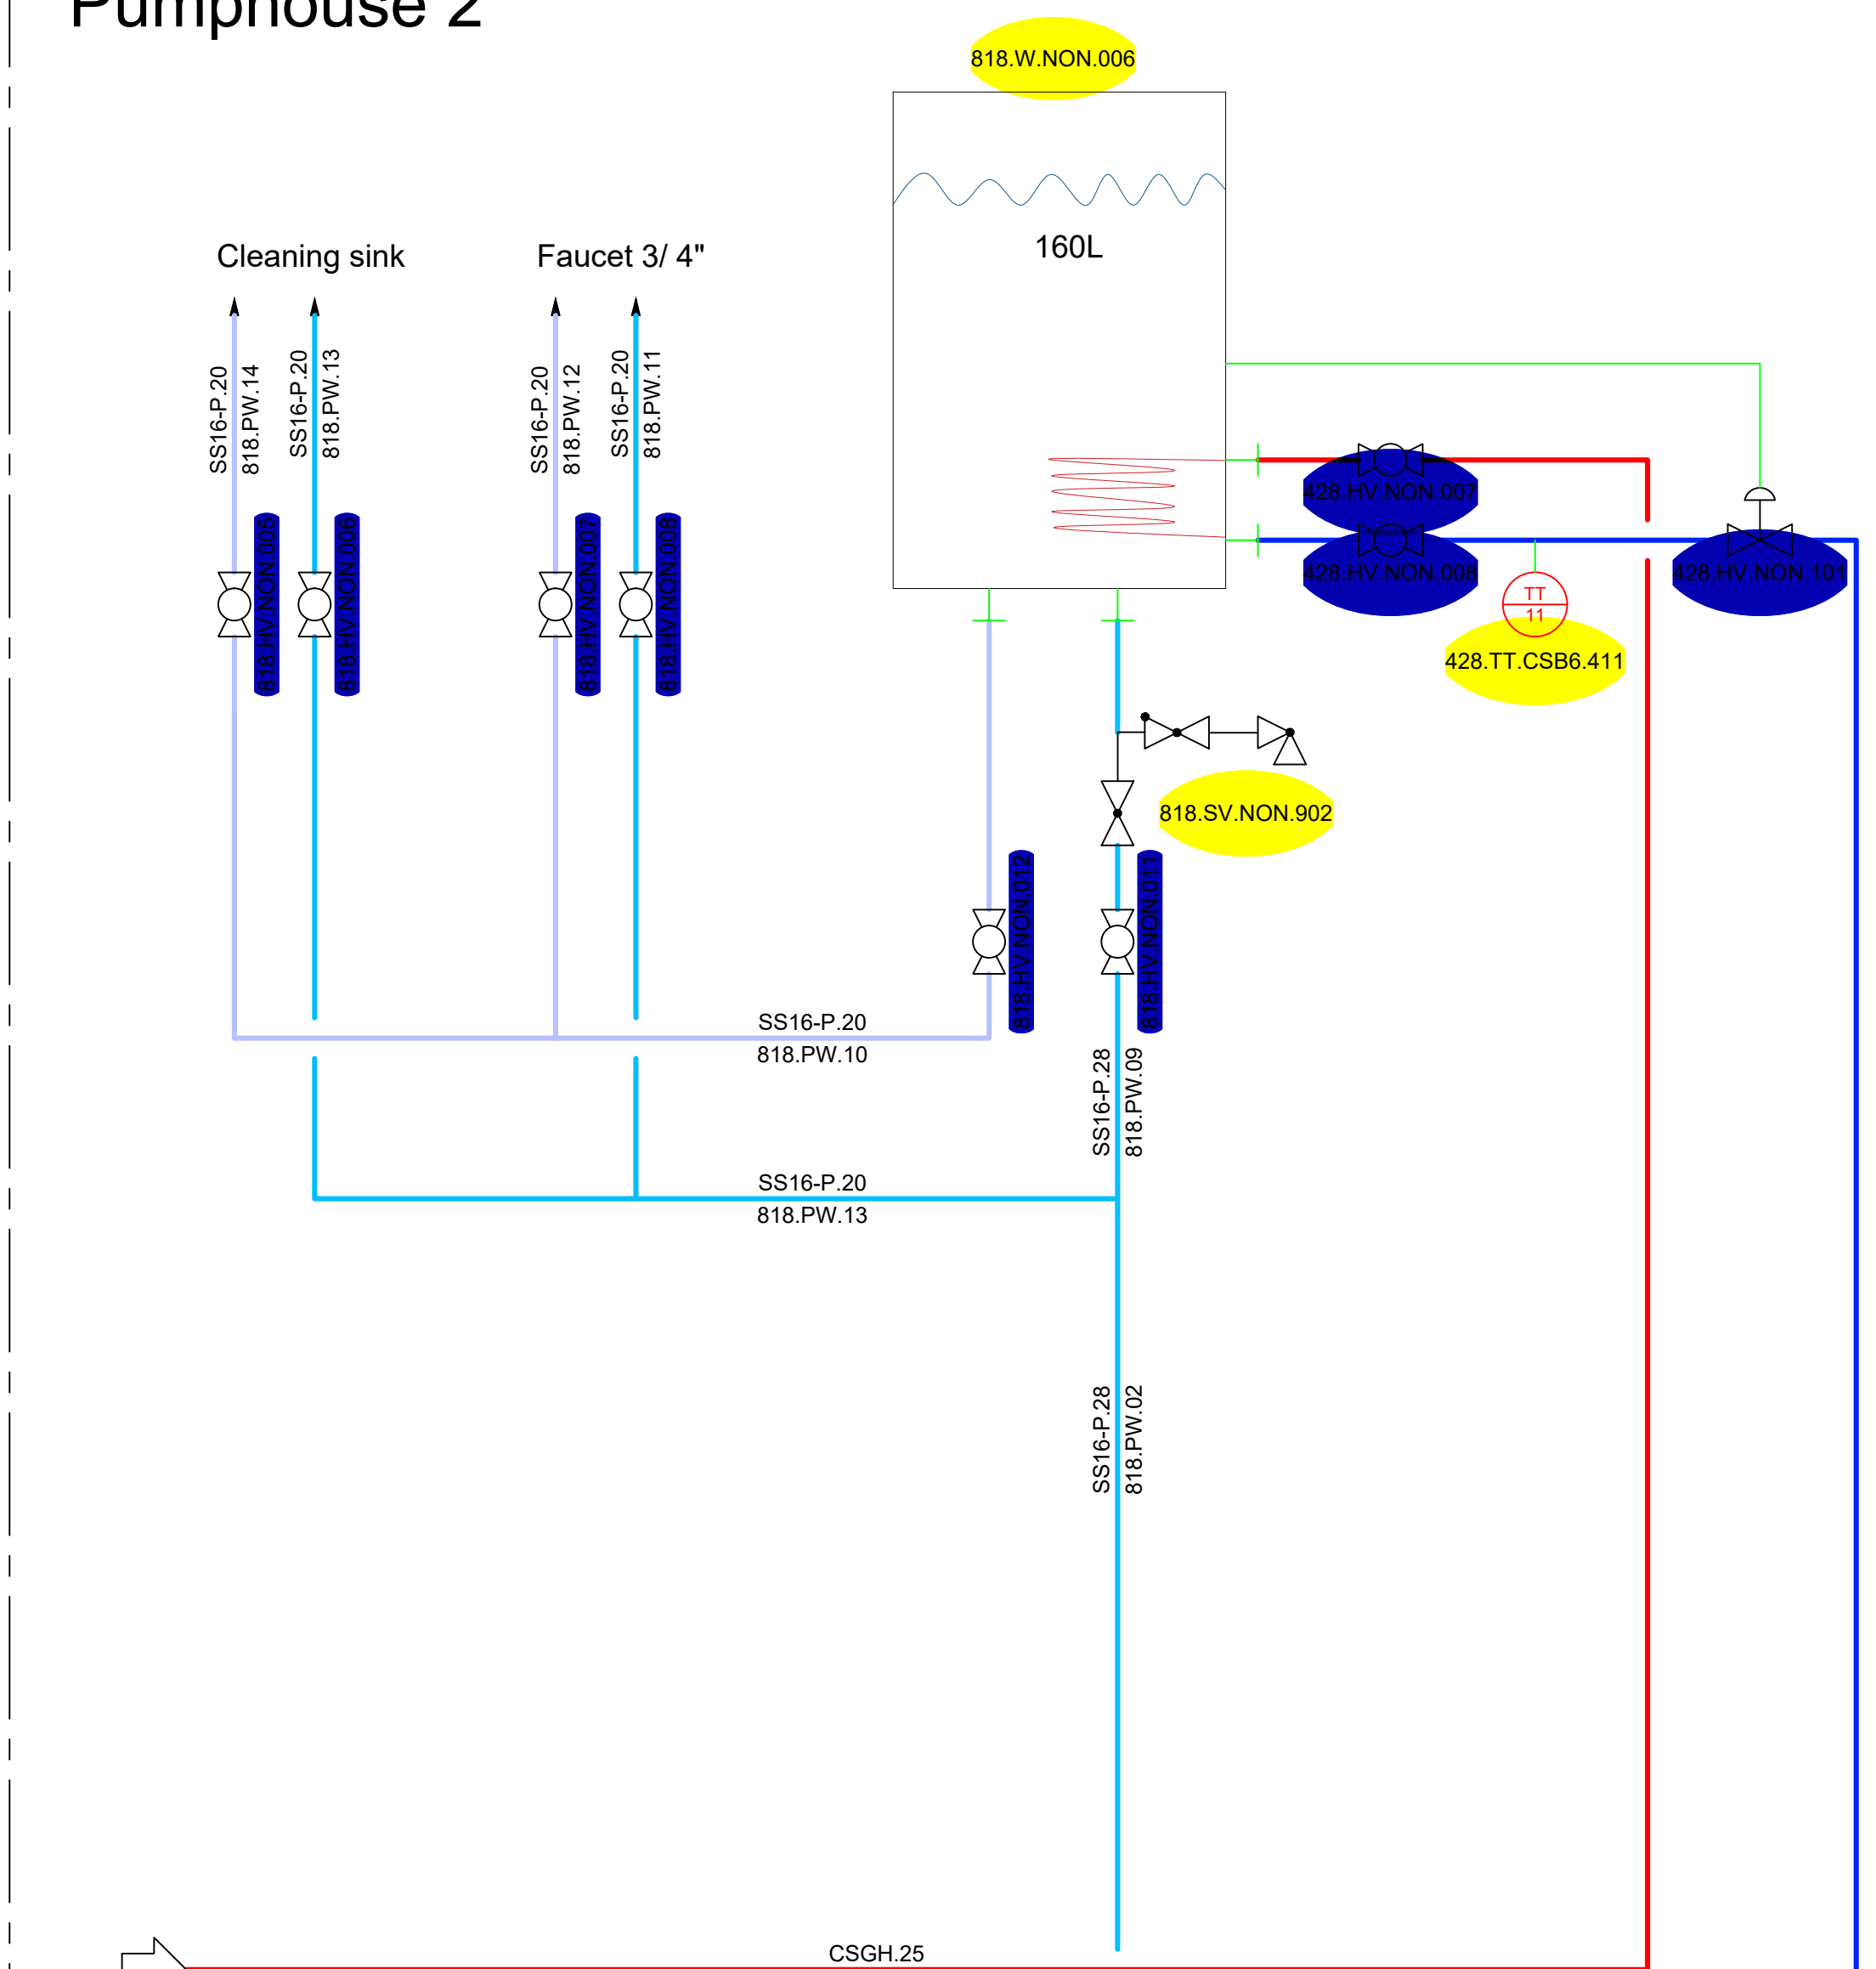


Rev. Nr.:	Rev. Dato:	Rev. Beskrivelse:
Builder:	ST1	
Project:	SLK	
Subject:	Water distribution pumphouse 1 & 2	
Int.:MDC	QC:CM	APP.: Date: 15-10-2025
LUNDSBY RENEWABLE SOLUTIONS		
Lundsby Biogas A/S, Hjarbækvej 65, 8831 Løgstrup Tlf.: +45 96 49 43 00 info@lundsbybiogas.dk Denne tegning er underlagt copyright op på ikke reproduceres uden tilladelse fra Lundsbybiogas A/S		
Project nr.: 1768 Drawing nr.: 9645		FORMAT: A1

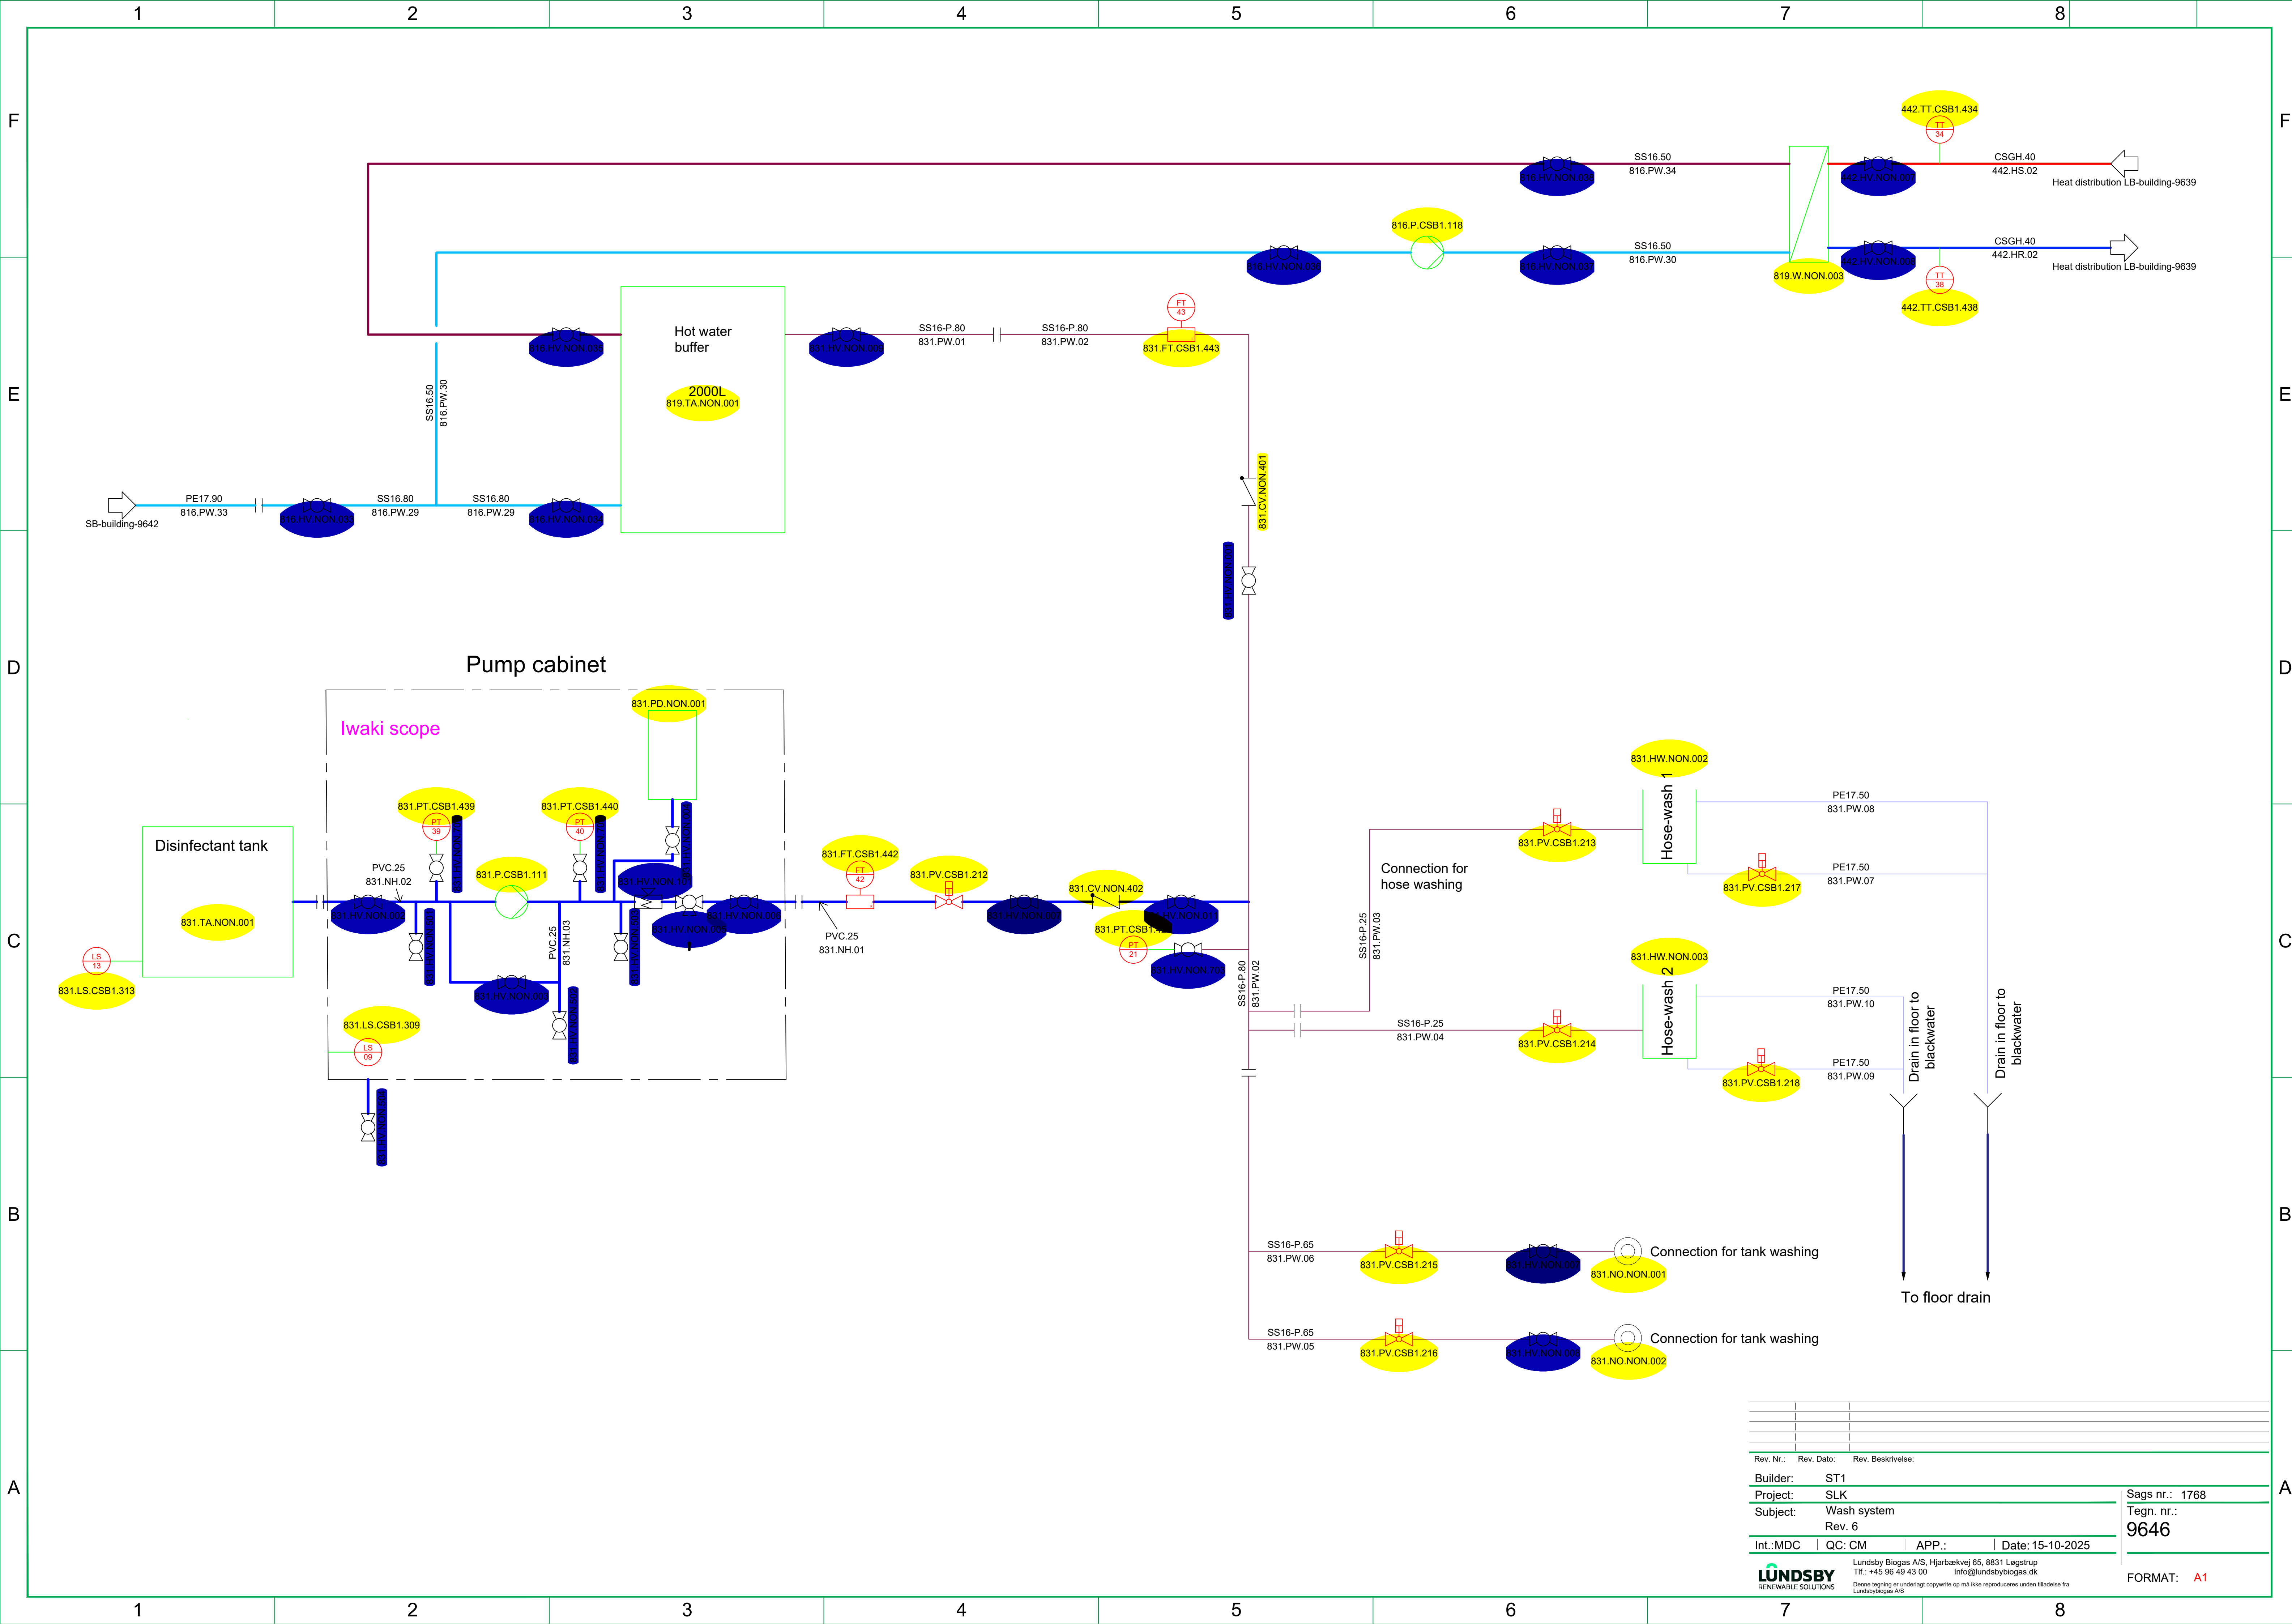

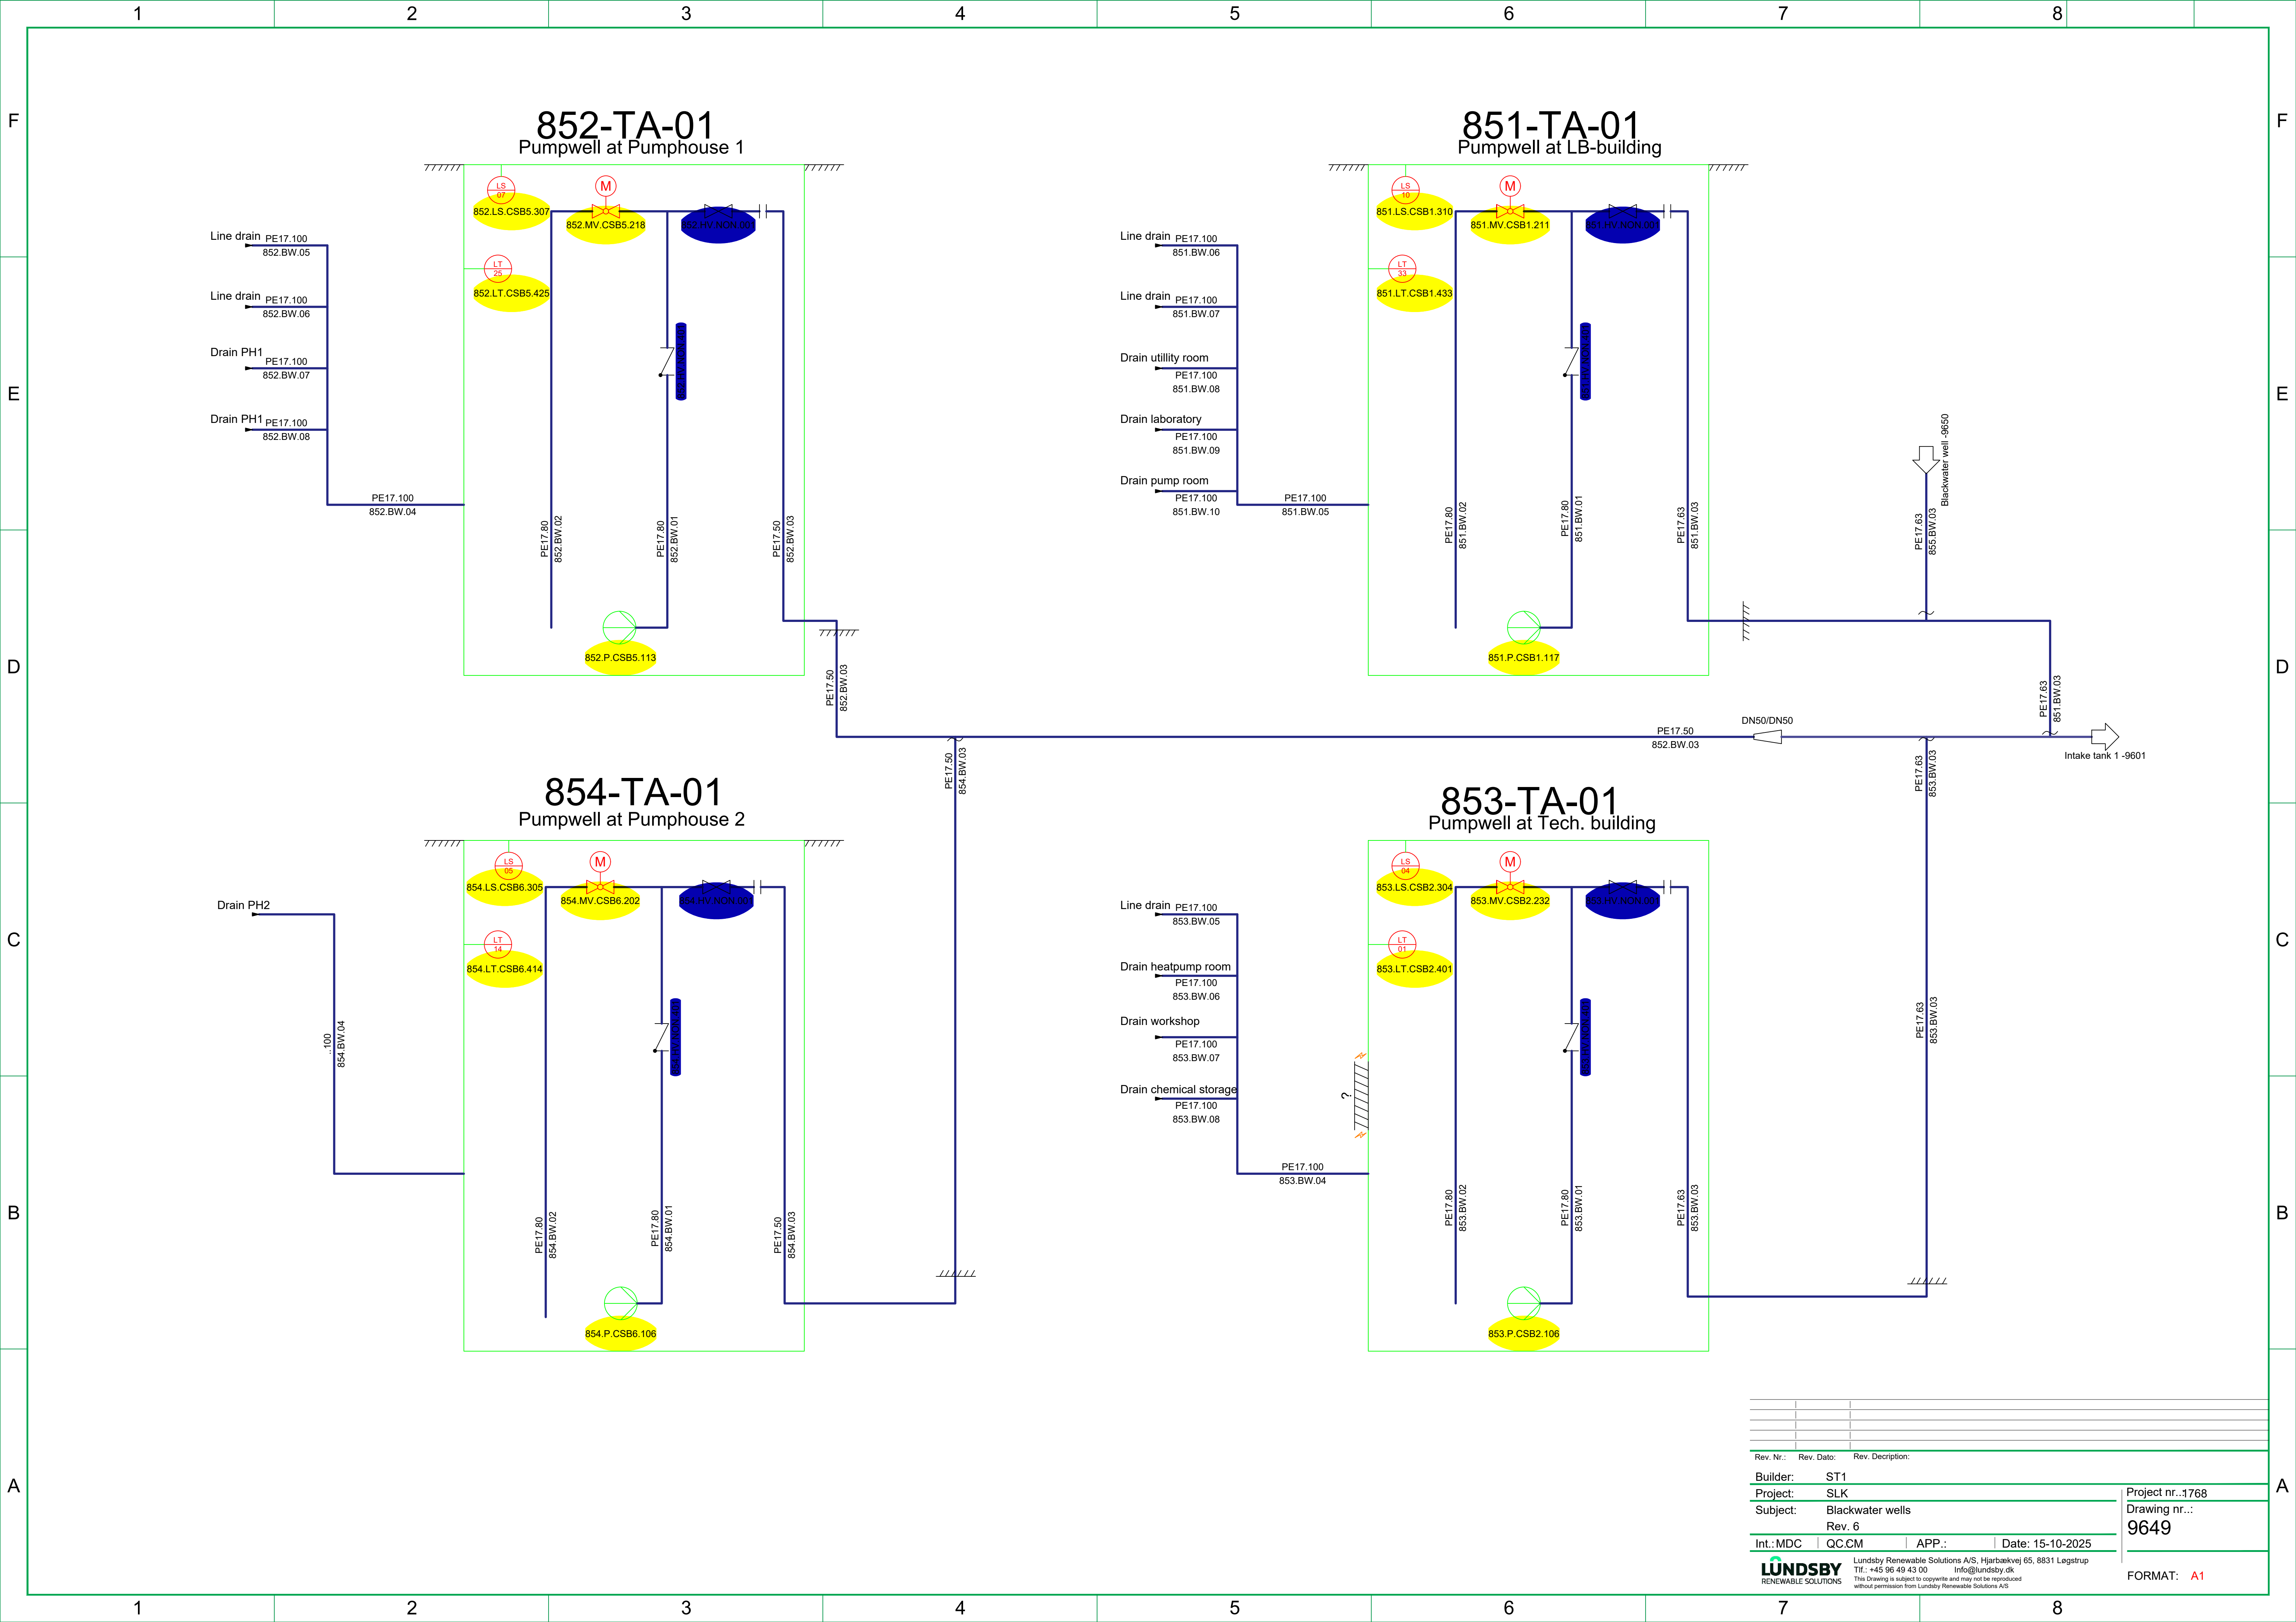


Rev. Nr.:	Rev. Dato:	Rev. Description:
Builder:	ST1	
Project:	SLK	
Subject:	Blackwater wells	
Rev. 6		
Int.:MDC	QC:CM	APP.:Date: 15-10-2025
LUNDSBYRENEWABLE SOLUTIONS Lundsby Renewable Solutions A/S, Hjarbrækvej 65, 8831 Løgstrup Tlf.: +45 96 49 43 00 Info@lundsby.dk This Drawing is subject to copyright and may not be reproduced without permission from Lundsby Renewable Solutions A/S		
Project nr.:1768		Drawing nr.:9649
FORMAT: A1		

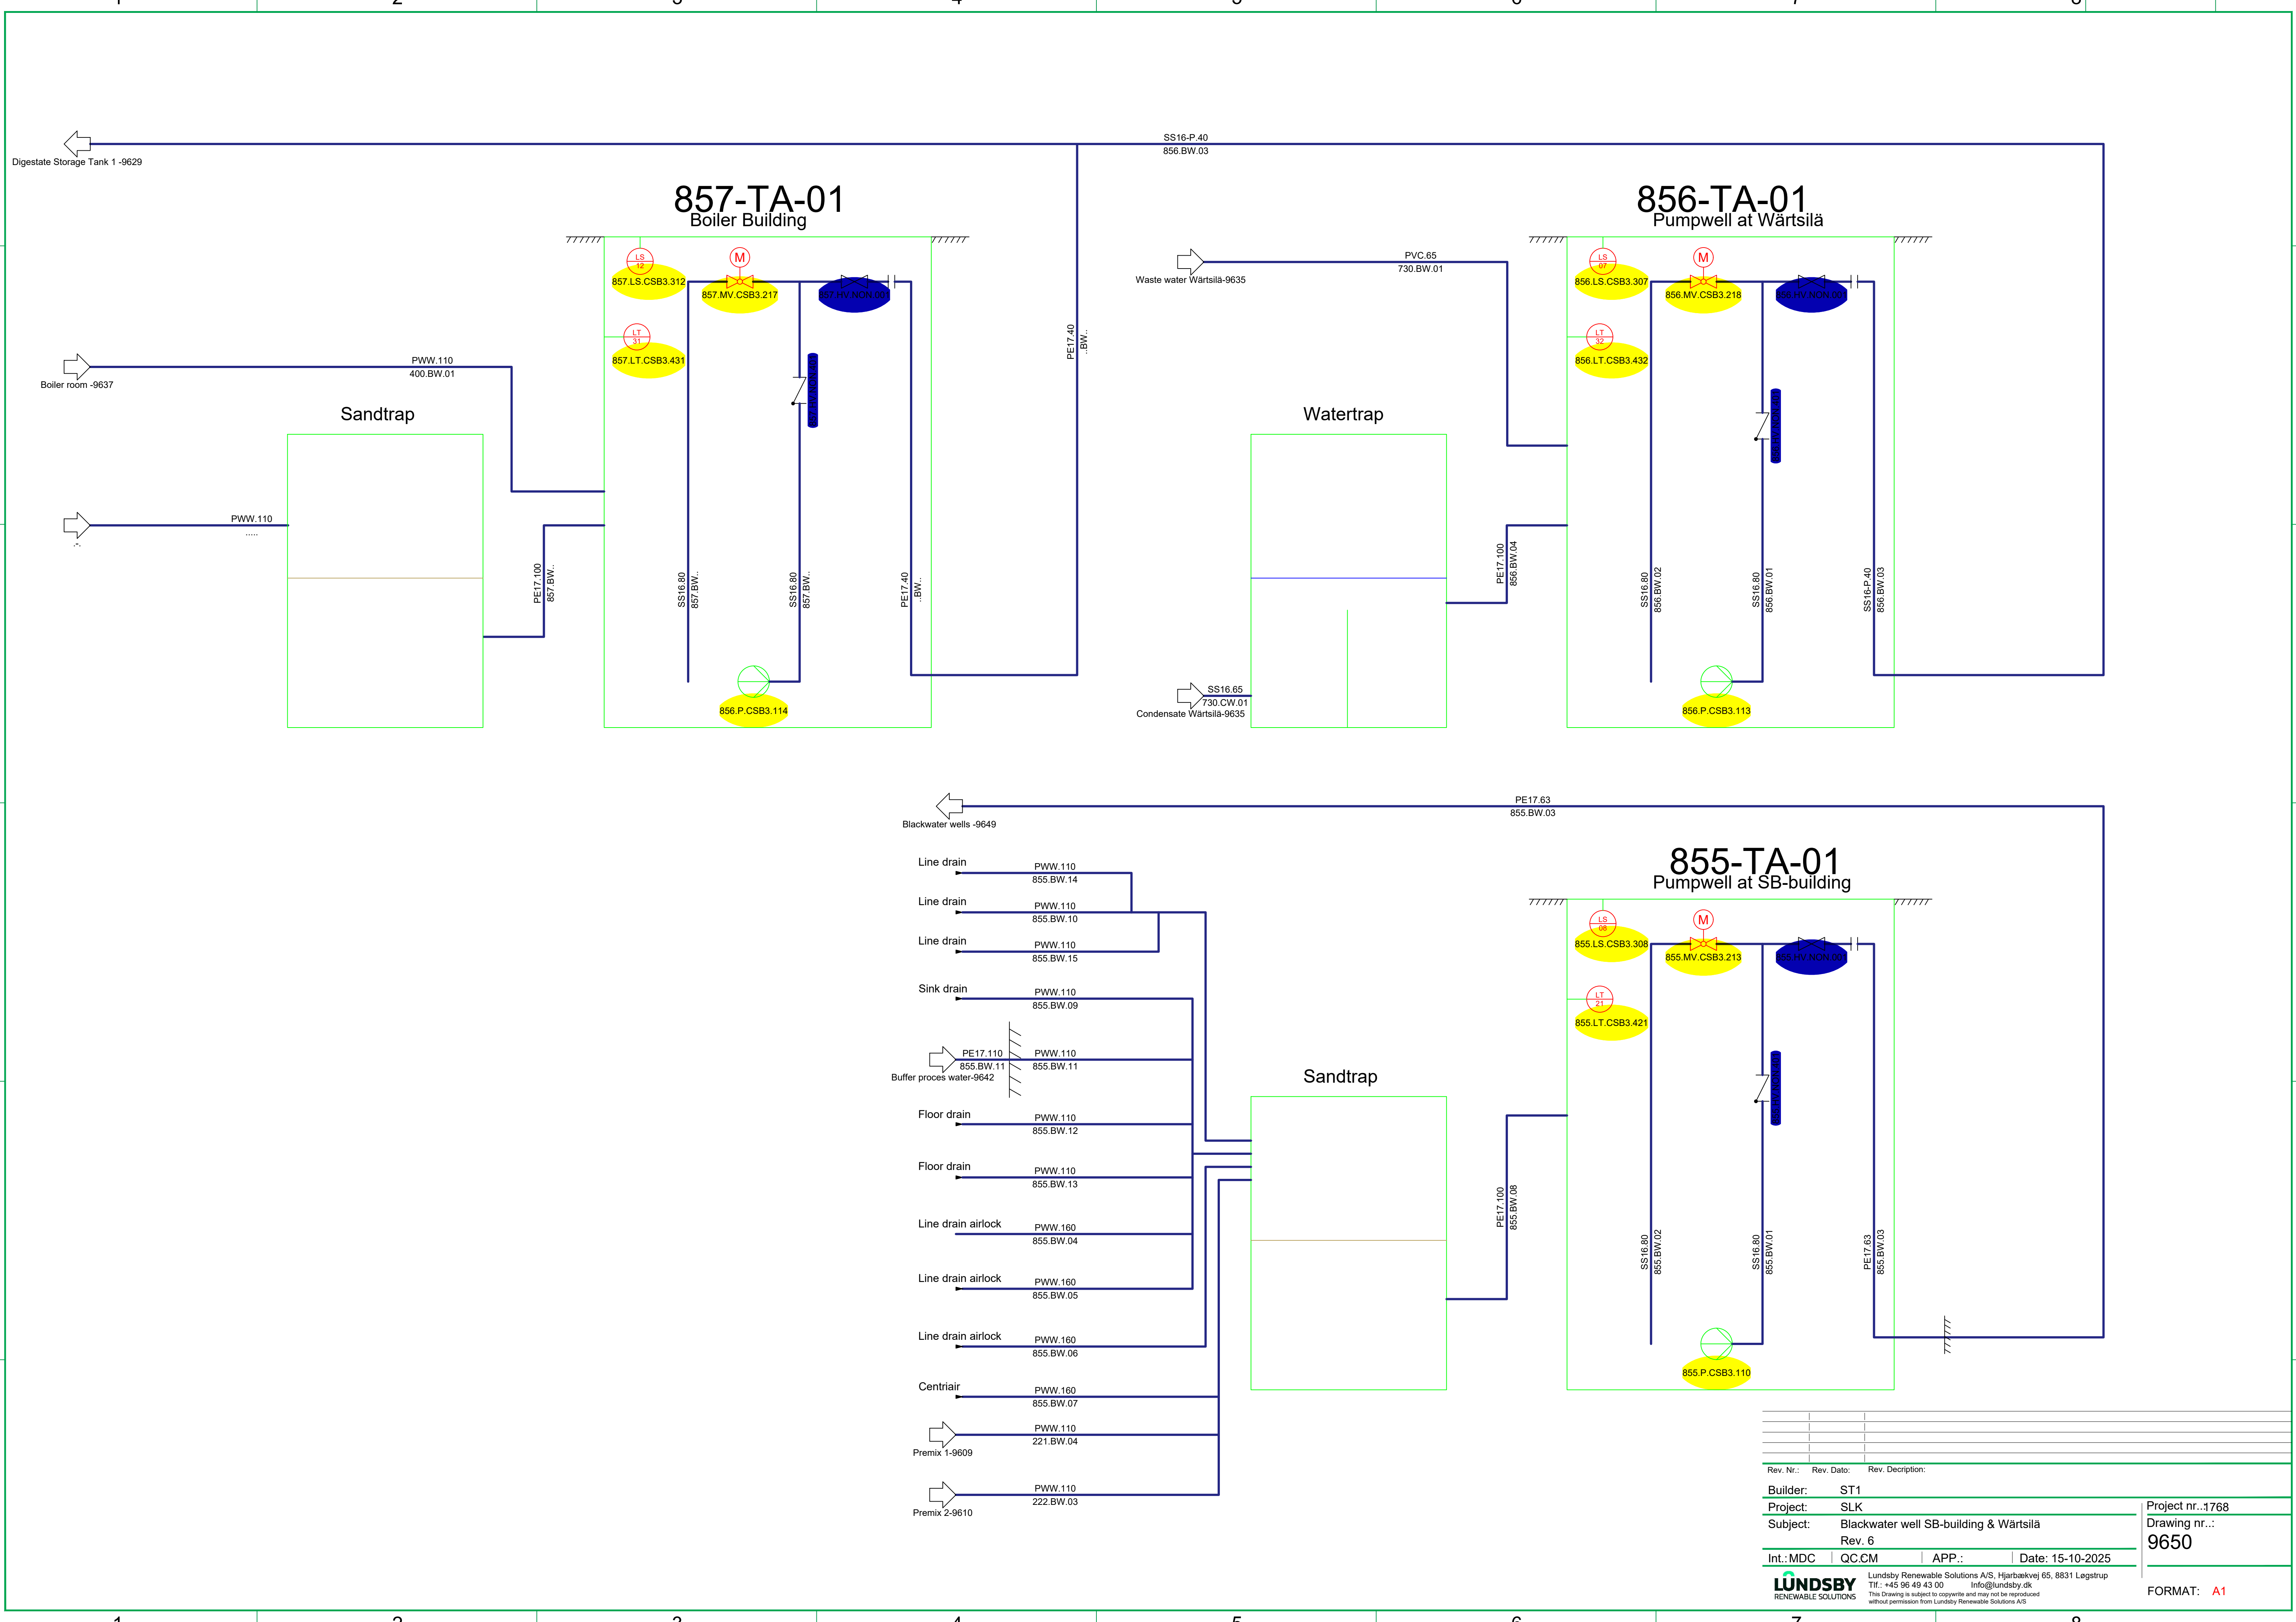


- Line drain PWW.110 855.BW.14
- Line drain PWW.110 855.BW.10
- Line drain PWW.110 855.BW.15
- Sink drain PWW.110 855.BW.09
- PE17.110 855.BW.11 PWW.110 855.BW.11
- Buffer proces water-9642
- Floor drain PWW.110 855.BW.12
- Floor drain PWW.110 855.BW.13
- Line drain airlock PWW.160 855.BW.04
- Line drain airlock PWW.160 855.BW.05
- Line drain airlock PWW.160 855.BW.06
- Centriair PWW.160 855.BW.07
- Premix 1-9609 PWW.110 221.BW.04
- Premix 2-9610 PWW.110 222.BW.03

Rev. Nr.:	Rev. Dato:	Rev. Description:
Builder:	ST1	
Project:	SLK	
Subject:	Blackwater well SB-building & Wärtsilä	
	Rev. 6	
Int.:MDC	QC:CM	APP.: Date: 15-10-2025
LUNDSBYRENEWABLE SOLUTIONS Lundsby Renewable Solutions A/S, Hjarbækvej 65, 8831 Lægstrup Tlf.: +45 96 49 43 00 info@lundsby.dk This Drawing is subject to copyright and may not be reproduced without permission from Lundsby Renewable Solutions A/S		
Project nr...1768		Drawing nr...: 9650
FORMAT: A1		

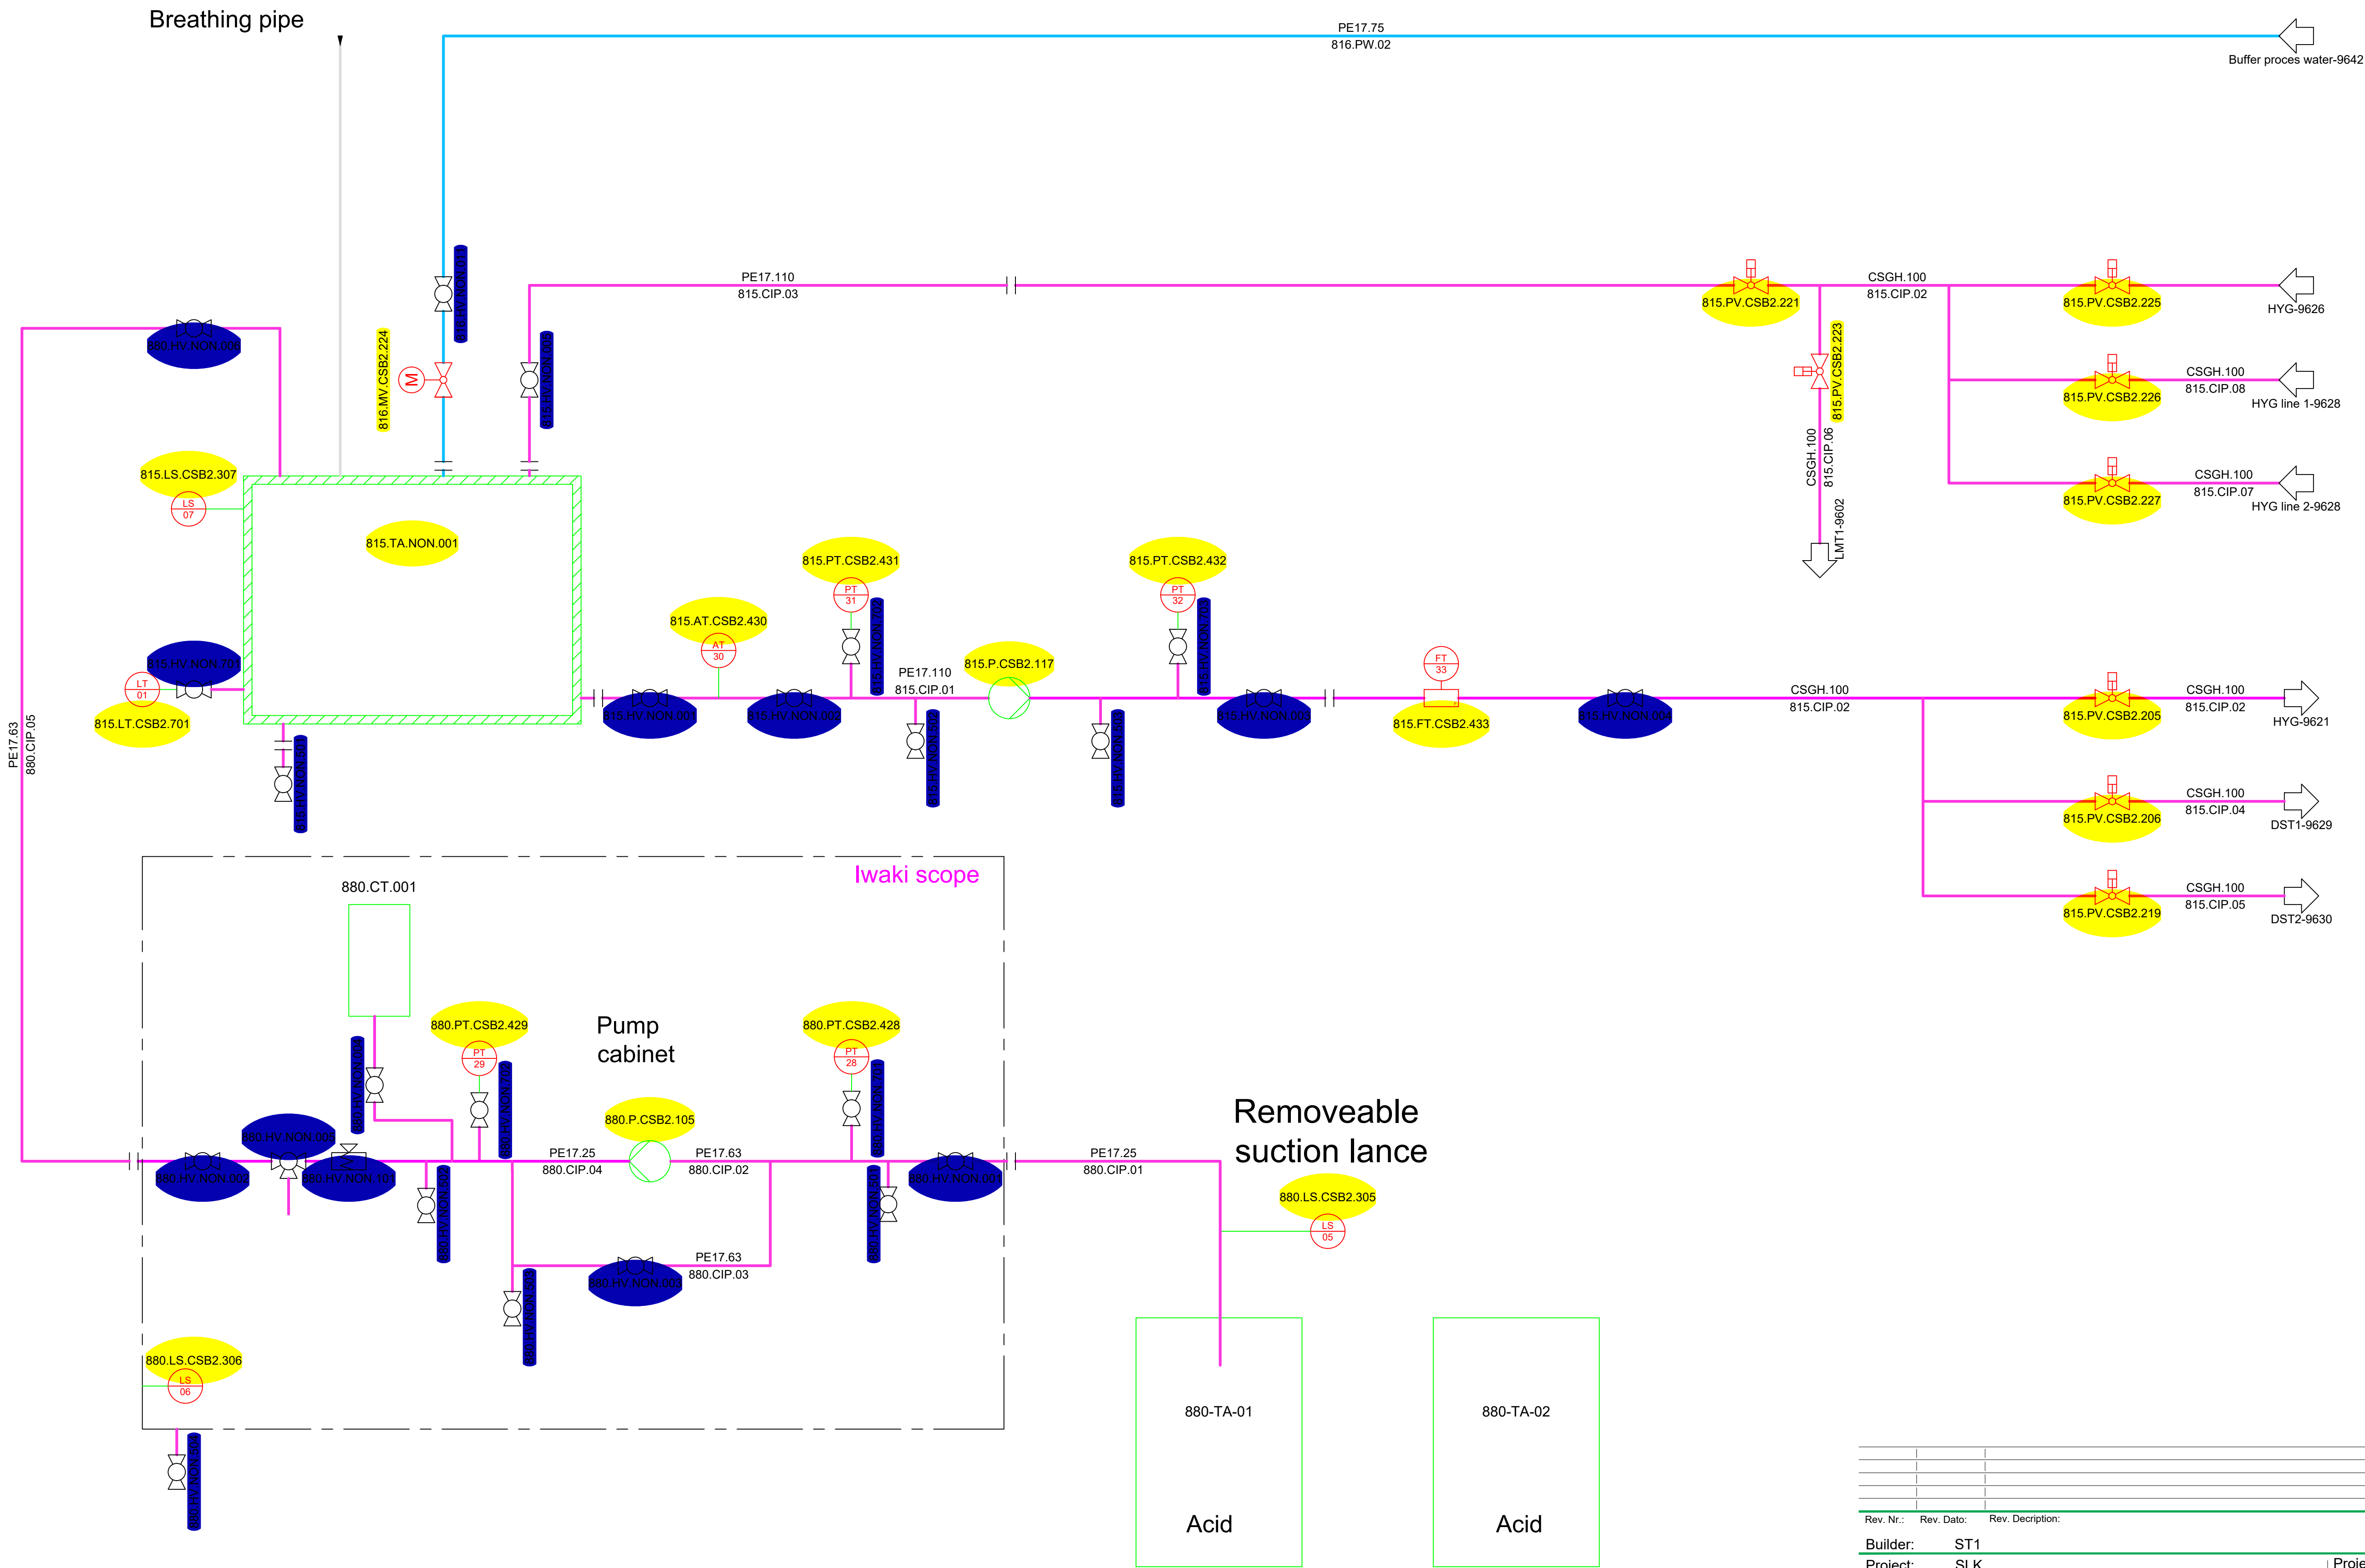


Rev. Nr.:	Rev. Dato:	Rev. Description:	
Builder:	ST1		
Project:	SLK		
Subject:	CIP facility		
	Rev. 6		
Int.:MDC	QC.CM	APP.:	Date: 15-10-2025
LUNDSBY RENEWABLE SOLUTIONS			Lundsby Renewable Solutions A/S, Hjarbrækvej 65, 8831 Legstrup Tlf.: +45 96 49 43 00 Info@lundsby.dk This Drawing is subject to copyright and may not be reproduced without permission from Lundsby Renewable Solutions A/S
Project nr...1768 Drawing nr... 9651			FORMAT: A1


Pumphouse 1
JA Trykluft scope

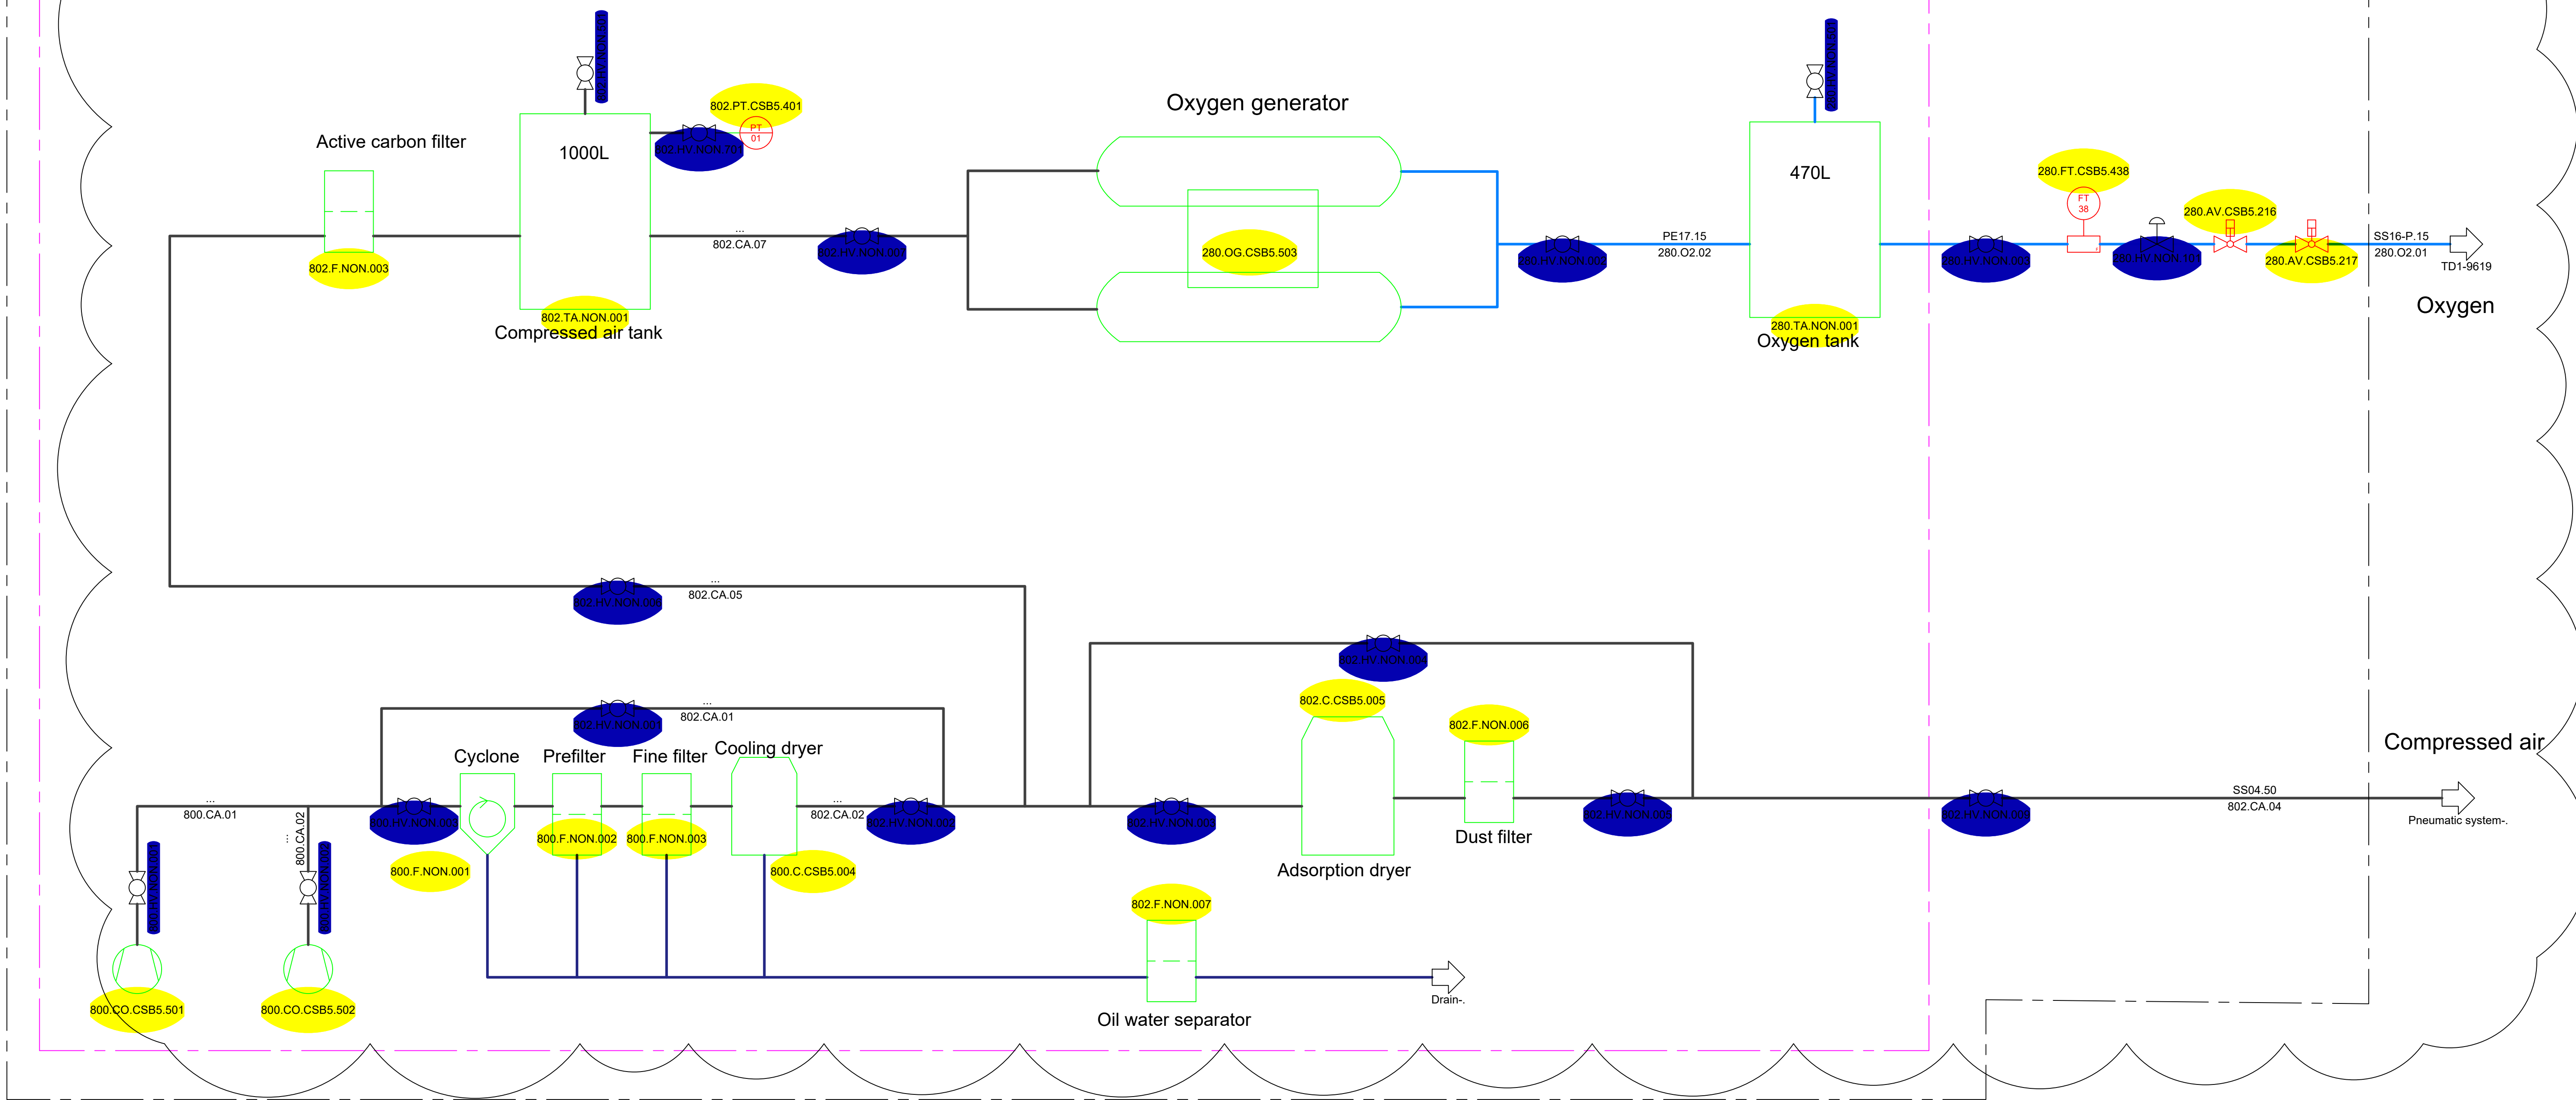


Rev. Nr.:	Rev. Dato:	Rev. Description:
Builder:	ST1	
Project:	SLK	
Subject:	Compressed air & Oxygen	
Rev. 6		
Int.:MDC	QC:CM	APP.:
Date: 15-10-2025		
LUNDSBY RENEWABLE SOLUTIONS		
Lundsby Renewable Solutions A/S, Hjarbækvej 65, 8831 Lægstrup Tlf.: +45 96 49 43 00 Info@lundsby.dk This drawing is subject to copyright and may not be reproduced without permission from Lundsby Renewable Solutions A/S		
Project nr.:1768 Drawing nr.: 9652		FORMAT: A1

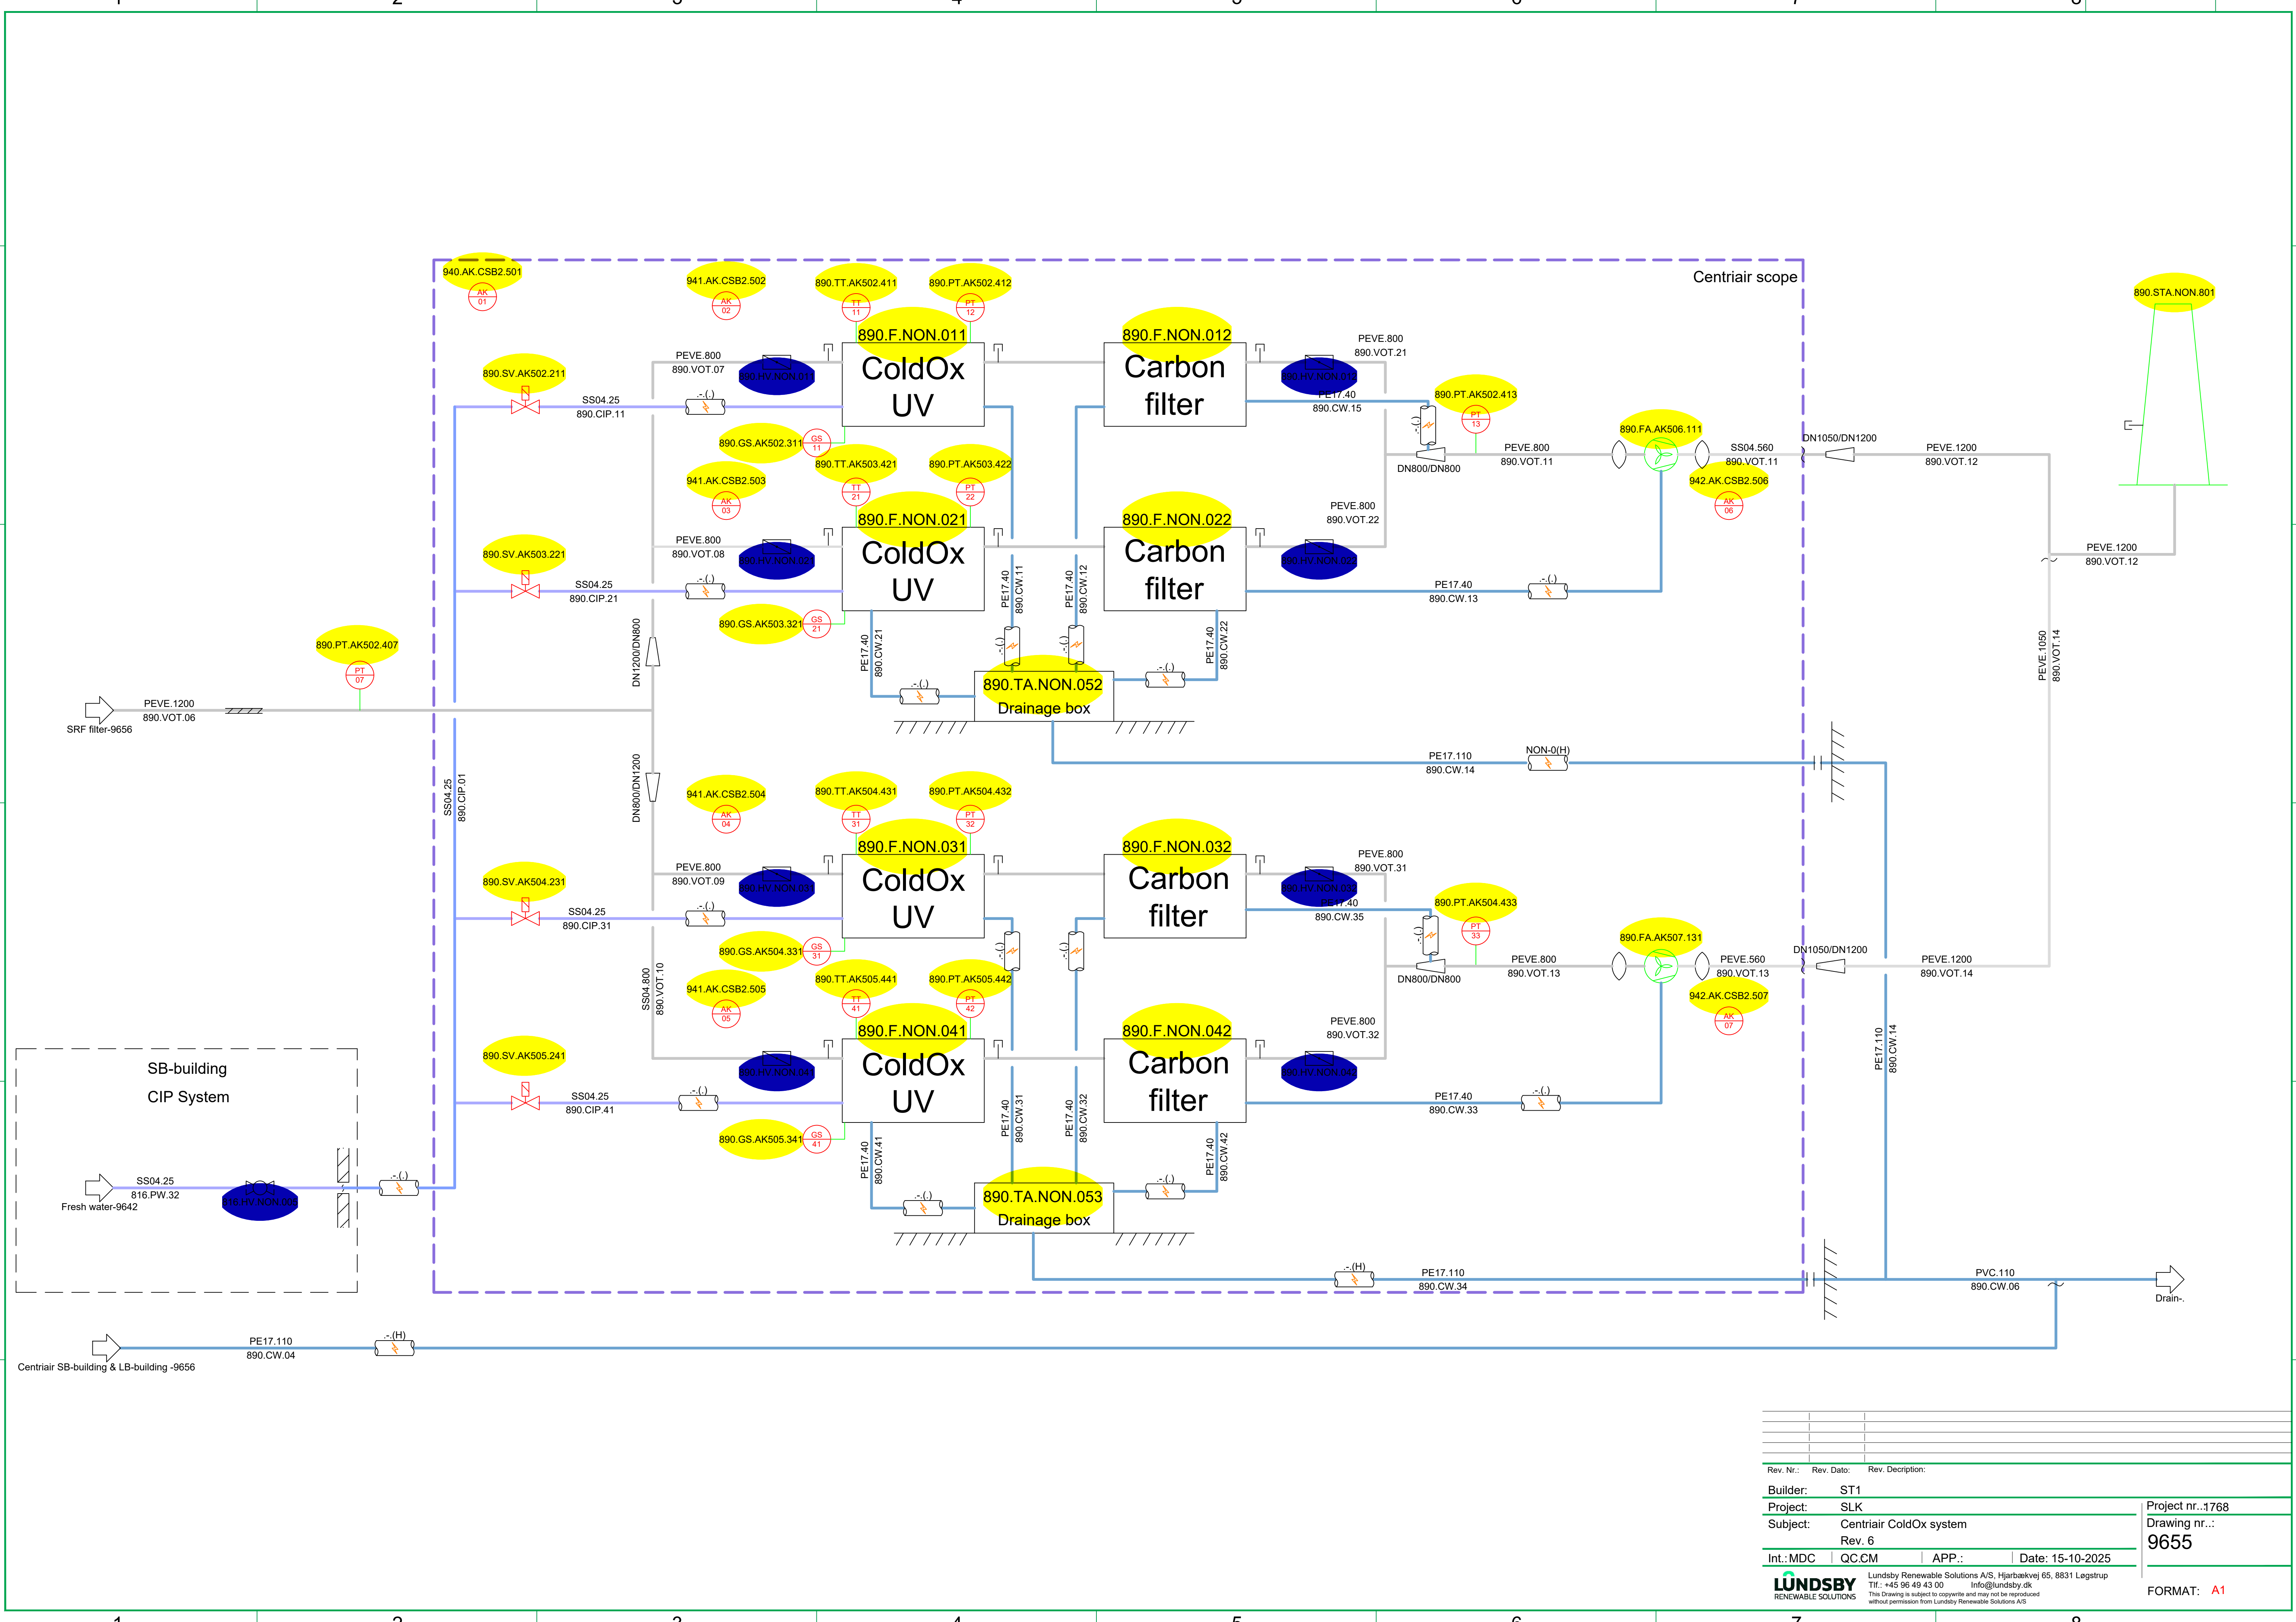

Rev. Nr.:	Rev. Dato:	Rev. Description:
Builder:	ST1	
Project:	SLK	
Subject:	Centriair ColdOx system	
Rev. 6		
Int.:MDC	QC:CM	APP.:
Date:	15-10-2025	
LUNDSBY RENEWABLE SOLUTIONS		
Lundsby Renewable Solutions A/S, Hjarbækvej 65, 8831 Løgstrup Tlf.: +45 96 49 43 00 Info@lundsby.dk This drawing is subject to copyright and may not be reproduced without permission from Lundsby Renewable Solutions A/S		
Project nr.:1768 Drawing nr.: 9655		FORMAT: A1

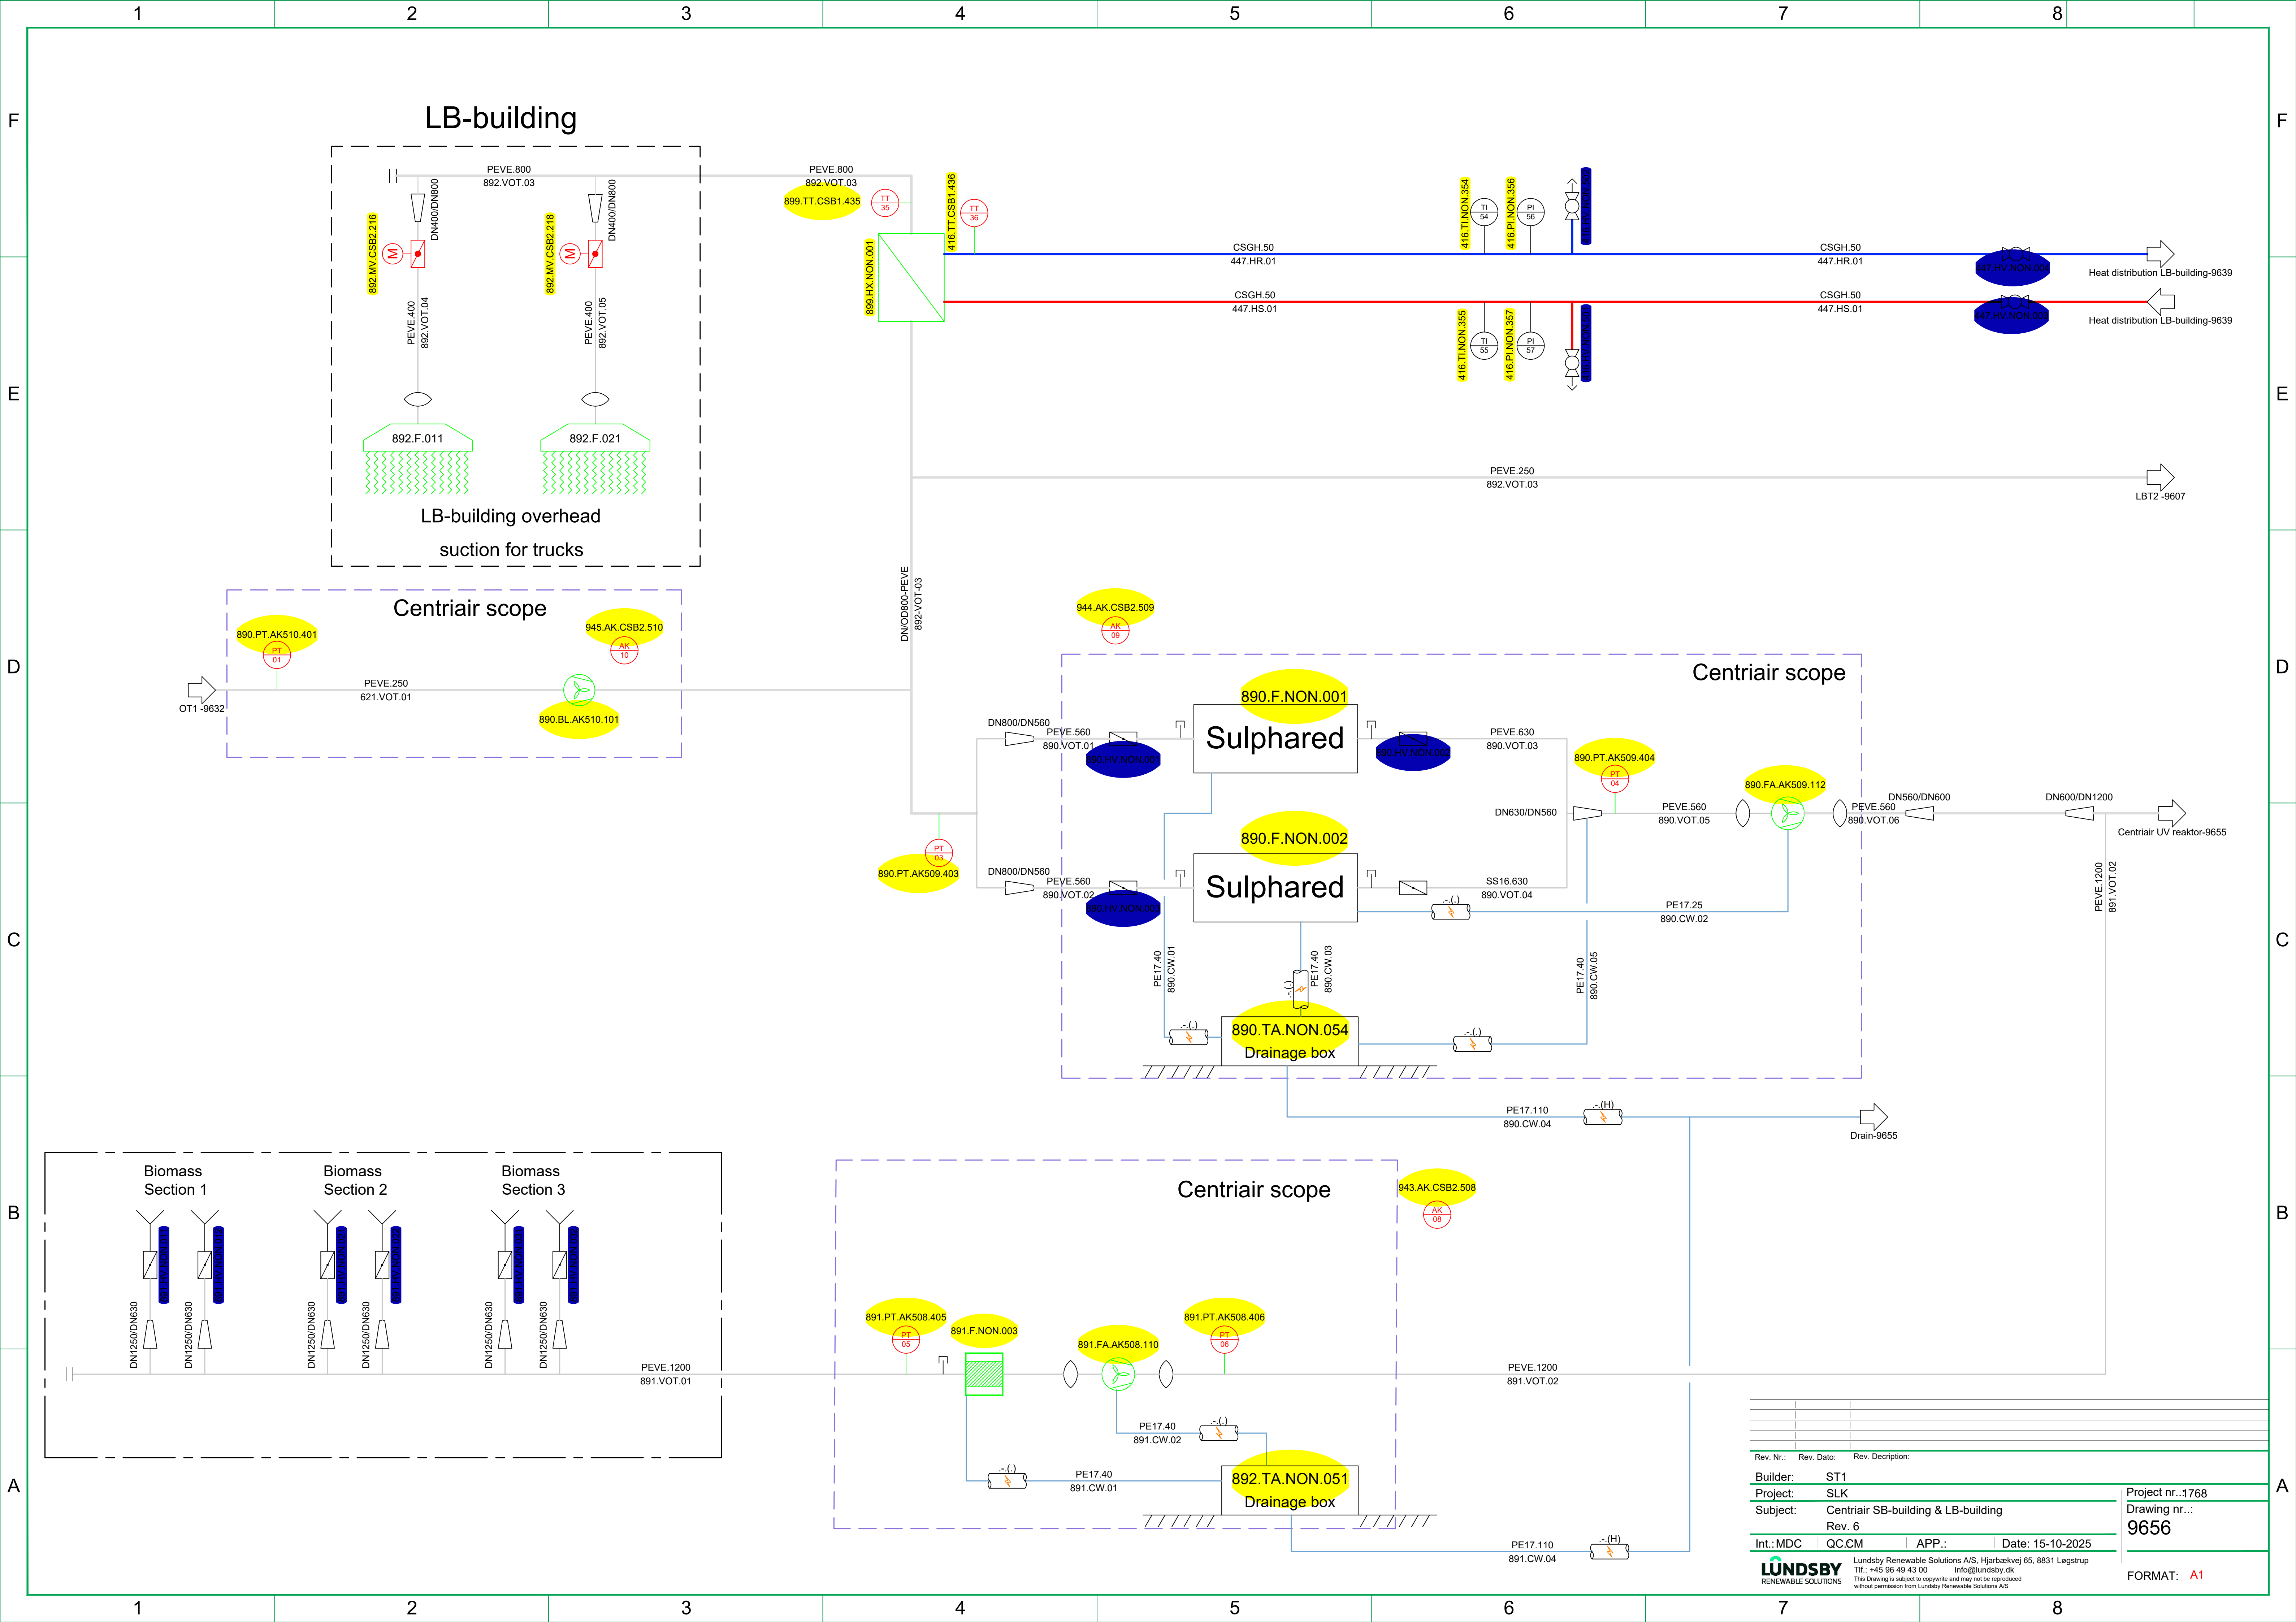

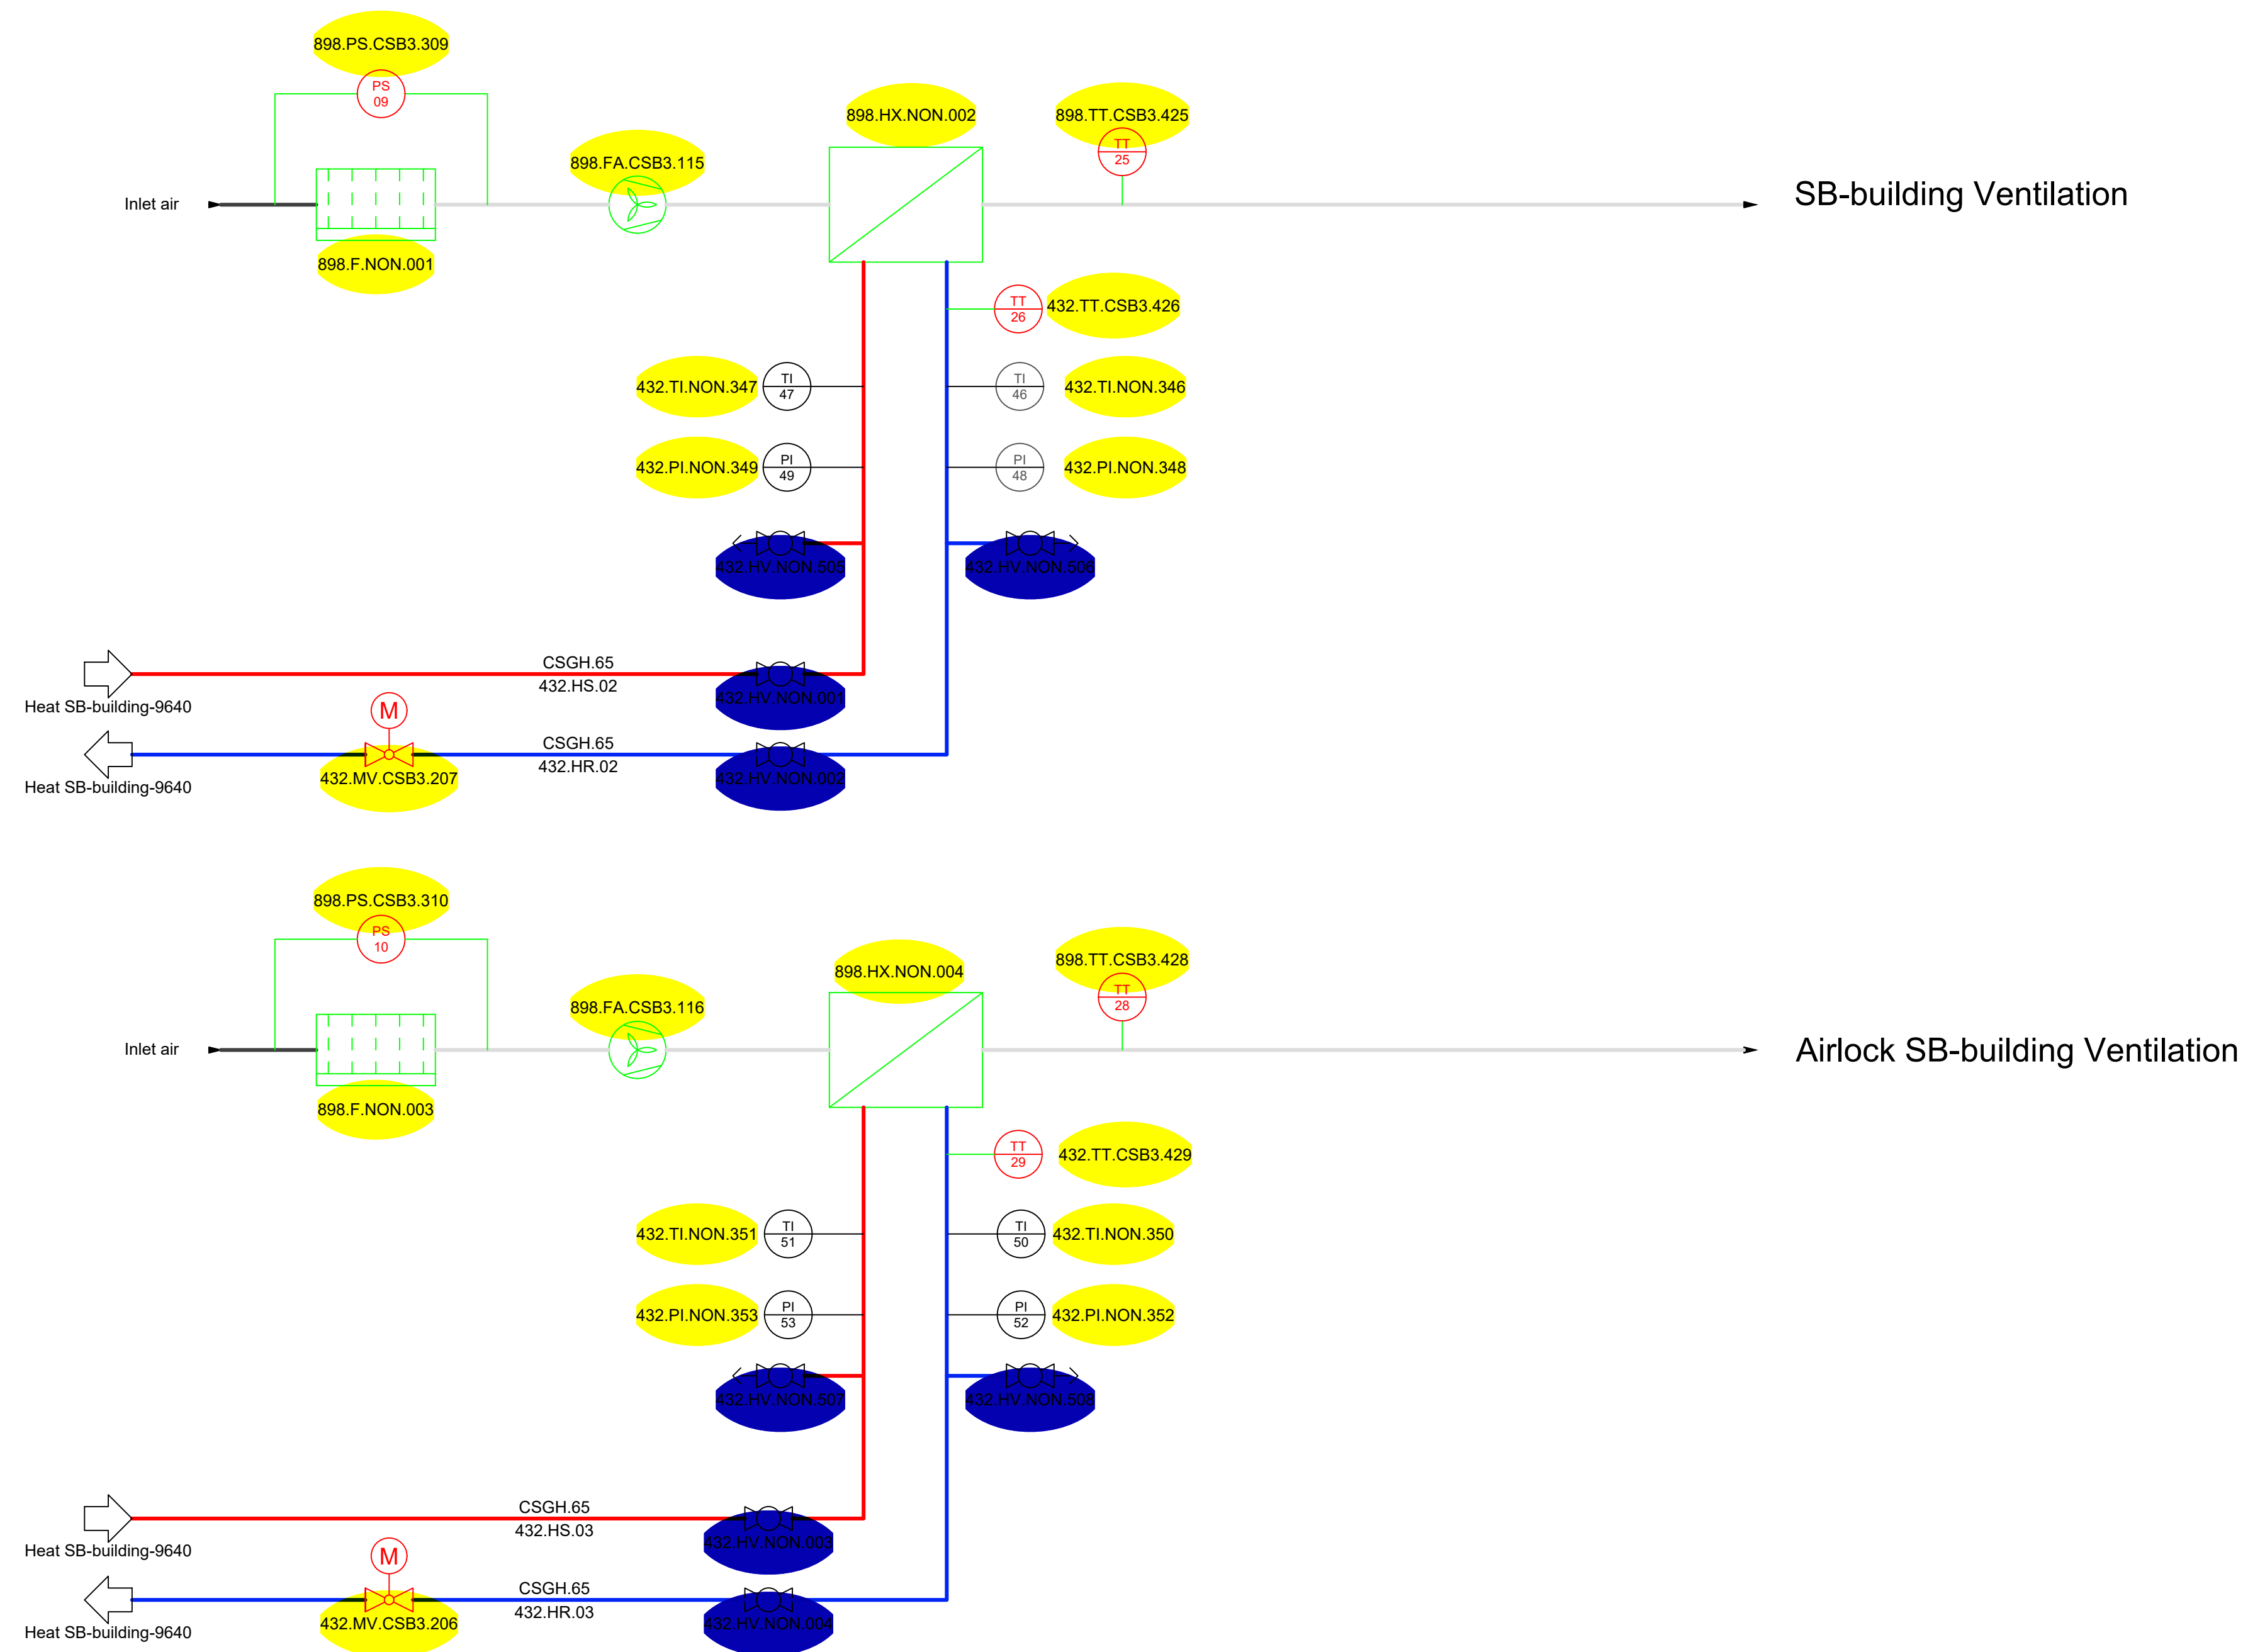

Rev. Nr.:	Rev. Dato:	Rev. Description:	
Builder:	ST1		
Project:	SLK		
Subject:	Ventilation SB-building		
Rev. 6			
Int.:MDC	QC.:CM	APP.:	Date: 15-10-2025
LUNDSBY RENEWABLE SOLUTIONS			Lundsby Renewable Solutions A/S, Hjarbækvej 65, 8831 Løgstrup Tlf.: +45 96 49 43 00 Info@lundsby.dk This Drawing is subject to copyright and may not be reproduced without permission from Lundsby Renewable Solutions A/S
Project nr.: 1768 Drawing nr.: 9657			FORMAT: A1