



1	2	3	4	5	6	7	8	
Structure of the tagging system	
Structure of the component tagging			Lines		Bulding/Area/Tank		Media code	
XXX — XXX — XXX — XXX Main equipment area code Equipment Valve Supply from switchboard Numeric Sequence Example 552 - TA - NON - 001 101 Switchboard Tank Area pasteurization tank 2 301.TA.NON.1: where 301 = Digester (System number), TA = Tank (Equipment), NON = Mechanical object (No switchboard), 01 = Tank nr 1. 201.P.CSB2.05: where 201 = Manure/feeding (System number), P = Pump (Equipment), CSB2 = Electrical object (Distribution board), 05 = Pump nr 5. 901.AK.CSB1.03: where 901 = Control and automation (System number), AK = Sub-distribution board at subcontractor (Equipment), CSB1 = Electrical object (Distribution board), 03 = Cabinet nr 3.			Description Symbol Subcontractor scope Boundary line Page connector Start pipe - Not linked to page End pipe - Not linked to page Fald/ Slope Insulation Electrical Heat tracing		Description Code Primary digester Secondary digester Digester storage Liquid manure tank Liquid biomass tank Outlet tank Blackwater tank Tech building Admin building Solid biomass building Liquid biomass building Plansilo Pump house Hygienization tanks Flare Stack Odour treatment facility Upgrade facility Liquifaction facility Oil boiler Wood boiler Transformer		Media Pipe color RBG color Code Heat Return Heat Supply Heat Hot Return Heat Hot Supply Cooling Supply Cooling Return Black Water CIP Process Water Technical Water Drinking Water Drinking Water Hot Condensate Steam Steam Condensate Liquid Manure (Slurry) Liquid Biomass (Substrat) Process Biomass Hygienized Biomass Recirculated Biomass Ferric Chloride FeCl Ventilation Odour Treatment Ventilation Fresh Air Compressed Air Oxygen Raw Biogas Return/reject Gas Nature Gas	
<table><tr><th>System:</th><th colspan="2">System number:</th></tr><tr><td>Reception</td><td>100-199</td><td></td></tr><tr><td>Manure tank</td><td></td><td>100-109</td></tr><tr><td>Fat/Liquid Substrate tank</td><td></td><td>110-119</td></tr><tr><td>Dry Dosificator tank</td><td></td><td>120-129</td></tr><tr><td>FeCl tank</td><td></td><td>130-139</td></tr><tr><td>Glycerol tank</td><td></td><td>140-149</td></tr><tr><td>Cereals silo</td><td></td><td>160-169</td></tr><tr><td>Water tank</td><td></td><td>170-179</td></tr><tr><td>LPG tank</td><td></td><td>180-189</td></tr><tr><td>Beets and root crops</td><td></td><td>190-191</td></tr><tr><td>Feeding in</td><td>200-299</td><td></td></tr><tr><td>Manure feeding</td><td></td><td>200-209</td></tr><tr><td>Fat/Liquid Substrate feeding</td><td></td><td>210-219</td></tr><tr><td>Dry Dosificator</td><td></td><td>220-229</td></tr><tr><td>FeCl feeding</td><td></td><td>230-239</td></tr><tr><td>Glycerol feeding</td><td></td><td>240-249</td></tr><tr><td>Pasteurization before digester</td><td></td><td>250</td></tr><tr><td>Cereal feeding</td><td></td><td>260</td></tr><tr><td>Water feeding</td><td></td><td>270</td></tr><tr><td>Oxygen/air dozing</td><td></td><td>280</td></tr><tr><td>Mixing tank</td><td></td><td>290</td></tr><tr><td>Digester</td><td>300-399</td><td></td></tr><tr><td>Primary Digester</td><td></td><td>300-309</td></tr><tr><td>Secondary Digester</td><td></td><td>310-319</td></tr><tr><td>Tertiary Digester</td><td></td><td>320-329</td></tr><tr><td>Line X</td><td></td><td>3X0</td></tr><tr><td>Heating system</td><td>400-499</td><td></td></tr><tr><td>Heating system</td><td></td><td>400-449</td></tr><tr><td>Cooling system</td><td></td><td>450-459</td></tr><tr><td>Feeding out</td><td>500-599</td><td></td></tr><tr><td>Pump</td><td></td><td>500 - 509</td></tr><tr><td>Pasteurization after digester</td><td></td><td>550</td></tr><tr><td>Biofertilizer tank</td><td>600-699</td><td></td></tr><tr><td>Biofertilizer tank 1</td><td></td><td>601</td></tr><tr><td>Biofertilizer tank 2</td><td></td><td>602</td></tr><tr><td>Separation</td><td></td><td>610 - 619</td></tr><tr><td>Gas treatment</td><td>700-799</td><td></td></tr><tr><td>Components on general gas pipe</td><td></td><td>700</td></tr><tr><td>Condensate pit</td><td></td><td>710</td></tr><tr><td>Flare</td><td></td><td>720</td></tr><tr><td>Upgrading unit/CHP/boiler</td><td></td><td>730</td></tr><tr><td>Stripper air combustion</td><td></td><td>740</td></tr><tr><td>RTO</td><td></td><td>750</td></tr><tr><td>High pressure compressor station</td><td></td><td>760</td></tr><tr><td>LNG plant</td><td></td><td>770</td></tr><tr><td>Propane dosing</td><td></td><td>780</td></tr><tr><td>Support system</td><td>800-899</td><td></td></tr><tr><td>Instrument air</td><td></td><td>800</td></tr><tr><td>Hydraulic system</td><td></td><td>805</td></tr><tr><td>Water</td><td></td><td>810</td></tr><tr><td>Backflow protection system</td><td></td><td>815</td></tr><tr><td>Heat tracing cable</td><td></td><td>820</td></tr><tr><td>Car wash</td><td></td><td>830</td></tr><tr><td>Building/container</td><td></td><td>840</td></tr><tr><td>Pumpwell</td><td></td><td>850</td></tr><tr><td>Oil separator</td><td></td><td>860</td></tr><tr><td></td><td></td><td>870</td></tr><tr><td>Dosing equipment</td><td></td><td>880</td></tr><tr><td>Odour cntro/ventilation system</td><td></td><td>890</td></tr><tr><td>Electrical and Control</td><td>900-999</td><td></td></tr><tr><td>Control and automation</td><td></td><td>900-949*</td></tr><tr><td>Server and IT</td><td></td><td>950*</td></tr><tr><td>Electrical power high voltage (>1000V)</td><td></td><td>980-989*</td></tr><tr><td>Electrical power low voltage</td><td></td><td>990-999*</td></tr></table>			System:	System number:		Reception	100-199		Manure tank		100-109	Fat/Liquid Substrate tank		110-119	Dry Dosificator tank		120-129	FeCl tank		130-139	Glycerol tank		140-149	Cereals silo		160-169	Water tank		170-179	LPG tank		180-189	Beets and root crops		190-191	Feeding in	200-299		Manure feeding		200-209	Fat/Liquid Substrate feeding		210-219	Dry Dosificator		220-229	FeCl feeding		230-239	Glycerol feeding		240-249	Pasteurization before digester		250	Cereal feeding		260	Water feeding		270	Oxygen/air dozing		280	Mixing tank		290	Digester	300-399		Primary Digester		300-309	Secondary Digester		310-319	Tertiary Digester		320-329	Line X		3X0	Heating system	400-499		Heating system		400-449	Cooling system		450-459	Feeding out	500-599		Pump		500 - 509	Pasteurization after digester		550	Biofertilizer tank	600-699		Biofertilizer tank 1		601	Biofertilizer tank 2		602	Separation		610 - 619	Gas treatment	700-799		Components on general gas pipe		700	Condensate pit		710	Flare		720	Upgrading unit/CHP/boiler		730	Stripper air combustion		740	RTO		750	High pressure compressor station		760	LNG plant		770	Propane dosing		780	Support system	800-899		Instrument air		800	Hydraulic system		805	Water		810	Backflow protection system		815	Heat tracing cable		820	Car wash		830	Building/container		840	Pumpwell		850	Oil separator		860			870	Dosing equipment		880	Odour cntro/ventilation system		890	Electrical and Control	900-999		Control and automation		900-949*	Server and IT		950*	Electrical power high voltage (>1000V)		980-989*	Electrical power low voltage		990-999*	<table><tr><th>Pipe Spec list</th><th>Code</th></tr><tr><td>Carbon steel P235TR1</td><td>CTSR</td></tr><tr><td>Carbon steel P235GH</td><td>CSGH</td></tr><tr><td>Preinsulated Carbon steel P235GH</td><td>CSGH-PRI</td></tr><tr><td>Stainless steel pipes 1.4304</td><td>SS16 / SS16-P</td></tr><tr><td>PE100 SDR17</td><td>PE17</td></tr><tr><td>Preinsulated PE100 SDR17</td><td>PE17-PRI</td></tr><tr><td>PE100 SDR11</td><td>PE11</td></tr><tr><td>PE pipes for ventilation</td><td>PEVE</td></tr><tr><td>PE Drain Pipes</td><td>PWW</td></tr><tr><td>Electrical Conduit And Piping</td><td>ELCP</td></tr><tr><td>Ventilation Steel</td><td>VENTS</td></tr><tr><td>Ventilation Plastic</td><td>VENTP</td></tr><tr><td>?</td><td>Unknown</td></tr></table>		Pipe Spec list	Code	Carbon steel P235TR1	CTSR	Carbon steel P235GH	CSGH	Preinsulated Carbon steel P235GH	CSGH-PRI	Stainless steel pipes 1.4304	SS16 / SS16-P	PE100 SDR17	PE17	Preinsulated PE100 SDR17	PE17-PRI	PE100 SDR11	PE11	PE pipes for ventilation	PEVE	PE Drain Pipes	PWW	Electrical Conduit And Piping	ELCP	Ventilation Steel	VENTS	Ventilation Plastic	VENTP	?	Unknown	Structure of the pipeline tagging system		
System:	System number:	
Reception	100-199	
Manure tank		100-109	
Fat/Liquid Substrate tank		110-119	
Dry Dosificator tank		120-129	
FeCl tank		130-139	
Glycerol tank		140-149	
Cereals silo		160-169	
Water tank		170-179	
LPG tank		180-189	
Beets and root crops		190-191	
Feeding in	200-299	
Manure feeding		200-209	
Fat/Liquid Substrate feeding		210-219	
Dry Dosificator		220-229	
FeCl feeding		230-239	
Glycerol feeding		240-249	
Pasteurization before digester		250	
Cereal feeding		260	
Water feeding		270	
Oxygen/air dozing		280	
Mixing tank		290	
Digester	300-399	
Primary Digester		300-309	
Secondary Digester		310-319	
Tertiary Digester		320-329	
Line X		3X0	
Heating system	400-499	
Heating system		400-449	
Cooling system		450-459	
Feeding out	500-599	
Pump		500 - 509	
Pasteurization after digester		550	
Biofertilizer tank	600-699	
Biofertilizer tank 1		601	
Biofertilizer tank 2		602	
Separation		610 - 619	
Gas treatment	700-799	
Components on general gas pipe		700	
Condensate pit		710	
Flare		720	
Upgrading unit/CHP/boiler		730	
Stripper air combustion		740	
RTO		750	
High pressure compressor station		760	
LNG plant		770	
Propane dosing		780	
Support system	800-899	
Instrument air		800	
Hydraulic system		805	
Water		810	
Backflow protection system		815	
Heat tracing cable		820	
Car wash		830	
Building/container		840	
Pumpwell		850	
Oil separator		860	
		870	
Dosing equipment		880	
Odour cntro/ventilation system		890	
Electrical and Control	900-999	
Control and automation		900-949*	
Server and IT		950*	
Electrical power high voltage (>1000V)		980-989*	
Electrical power low voltage		990-999*	
Pipe Spec list	Code	
Carbon steel P235TR1	CTSR	
Carbon steel P235GH	CSGH	
Preinsulated Carbon steel P235GH	CSGH-PRI	
Stainless steel pipes 1.4304	SS16 / SS16-P	
PE100 SDR17	PE17	
Preinsulated PE100 SDR17	PE17-PRI	
PE100 SDR11	PE11	
PE pipes for ventilation	PEVE	
PE Drain Pipes	PWW	
Electrical Conduit And Piping	ELCP	
Ventilation Steel	VENTS	
Ventilation Plastic	VENTP	
?	Unknown	
The pipetag consists of various information about the pipe Full pipeline tag as shown below Size-PipeSpec-Area-Service (Medie)-Serial number [100 PE17 201 LM 01] Example Two (2) digits. Starts with 01 [01] Two (2) to four (4) characters (letters) [LM - Liquid manure] Three (3) digits [201 - Manure feeding in tank 1] Pipe Spec name [PE17 - PE100 SDR17] Pipe size DN indication for Metric pipes OD indication for PE-pipe [This example is OD 100 mm]			The pipe tag will be shown on the P&ID as follows: PipeSpec-Size Area-Service-Serialnumber Example of line tag notation on P&ID: PE17-110 201-LM-01 Line color corresponding to table above. The part below the pipeline is the Unique Line Tag. Unique Line Tag is generated automatically when creating complete Line Tag. Unique Line Tag is used by the P3D system when designing pipes in the 3D model and when generating Isometrics.	
Rev. Nr.: Rev. Date: Rev. Description: Builder: ST1 Project: SLK Subject: PID Legend Rev. 6 Int.:MDC QC.:CM APP.: Date: 15-10-2025 LUNDSBY RENEWABLE SOLUTIONS Lundsby Renewable Solutions A/S, Hjarbækvej 65, 8831 Legstrup Tlf.: +45 96 49 43 00 Info@lundsby.dk This Drawing is subject to copyright and may not be reproduced without permission from Lundsby Renewable Solutions A/S Project nr.:1768 Drawing nr.: PID Legend FORMAT: A1	
1	2	3	4	5	6	7	8	


1		2		3		4		5		6		7		8																																				
Valves			Equipment						Piping			Instruments																																						
Hand valves			Pumps / Compressors / Blowers			Equipment			Piping symbols			Description																																						
Symbols	Code	Description	Symbols	Code	Description	Symbols	Code	Description	Symbols	Code	Description	Instruments will be tagged																																						
	HV	General valve		P	Pump (General)		MX	Bio mixer		N/A	Offpage connector	XXX - XX - XXX - XXX Main area code Letter code Switchboard Numeric sequence First letter XX Succeeding letter XX Numeric sequence																																						
	HV	Ball valve		P	Positive displacement pump		MC	Premix		N/A	Flange connection	DescriptionExample																																						
	HV	Butterfly valve		P	Helical rotor pump		CV	Debris lift unit		N/A	Blind flange				Temperature indication																																			
	HV	Globe valve		P	Centrifugal pump		CV	Screw conveyor		NO	Truck nozzle																																							
	HV	Three way valve		P	Peristaltic pump		CV	Belt conveyor		NO	Funnel/Drain				Level switch																																			
	HV	Ground covered valve		MC	Rotacut		CRA	Crane		AS	Expansion joint																																							
	BV	Balancing valve		MC	Shredder		CH	ISO Stack - Chimney		SN	Strainer	Instruments with succeeding letter T is an analog signal. Instruments with succeeding letter S is a digital signal.																																						
Actuated valves / Regulating valves			Heating and Cooling									<table><tr><th>Instruments</th><th>Abbreviation</th></tr><tr><td>Analyze Indicator</td><td>AI</td></tr><tr><td>Analyse Transmitter</td><td>AT</td></tr><tr><td>Energi Transmitter</td><td>ET</td></tr><tr><td>Flow Indicator</td><td>FI</td></tr><tr><td>Flow Transmitter</td><td>FT</td></tr><tr><td>Flow Switch</td><td>FS</td></tr><tr><td>Flow Transmitter</td><td>FT</td></tr><tr><td>General Switch</td><td>GS</td></tr><tr><td>Level Switch</td><td>LS</td></tr><tr><td>Level Indicator</td><td>LI</td></tr><tr><td>Level Transmitter</td><td>LT</td></tr><tr><td>Pressure Indicator</td><td>PI</td></tr><tr><td>Pressure Switch</td><td>PS</td></tr><tr><td>Pressure Transmitter</td><td>PT</td></tr><tr><td>Thermometer</td><td>TI</td></tr><tr><td>Temperature Transmitter</td><td>TT</td></tr><tr><td>Weight Transmitter</td><td>WT</td></tr></table>			Instruments	Abbreviation	Analyze Indicator	AI	Analyse Transmitter	AT	Energi Transmitter	ET	Flow Indicator	FI	Flow Transmitter	FT	Flow Switch	FS	Flow Transmitter	FT	General Switch	GS	Level Switch	LS	Level Indicator	LI	Level Transmitter	LT	Pressure Indicator	PI	Pressure Switch	PS	Pressure Transmitter	PT	Thermometer	TI	Temperature Transmitter	TT	Weight Transmitter	WT
Instruments	Abbreviation	
Analyze Indicator	AI	
Analyse Transmitter	AT	
Energi Transmitter	ET	
Flow Indicator	FI	
Flow Transmitter	FT	
Flow Switch	FS	
Flow Transmitter	FT	
General Switch	GS	
Level Switch	LS	
Level Indicator	LI	
Level Transmitter	LT	
Pressure Indicator	PI	
Pressure Switch	PS	
Pressure Transmitter	PT	
Thermometer	TI	
Temperature Transmitter	TT	
Weight Transmitter	WT	
	MV/RV	Motor ball valve		HX	Heat exchanger - Shell & tube		DT	Digester tank		N/A	Going into the ground / Coming up from																																							
	MV/RV	Motor butterfly valve		HX	Heat exchanger - plate		ST	Storage tank		AJ	Concentric reducer																																							
	AV/RV	Pneumatic ball valve		HX	Heat exchanger - double pipe		DT/ST	Storage tank with cover		AJ	Eccentric reducer																																							
	AV/RV	Pneumatic valve		HX	Heating coil (in tank)		HT	Gas/Hyginisation tank		AX	Sample point																																							
	AV	Solenoid valve		HS	Heatpump		TA	Buried tank		BS	Inline silencer																																							
Safety valves			Tank equipment			Tanks				BU	Electrical heat tracing																																							
	SV	Exhaust valve covers		AG	ISO Agitator - Propeller					N/A	Going though wall																																							
	SV	Safety valve		AG	Agitator				<table><tr><th>Category</th><th>Numbers</th></tr><tr><td>Manual valves</td><td>001-099</td></tr><tr><td>Manual regulation valves</td><td>101-199</td></tr><tr><td>Pneumatic, electrical, solenoid</td><td>201-299</td></tr><tr><td>-</td><td>301-399</td></tr><tr><td>Check, Non-return valves</td><td>401-499</td></tr><tr><td>Drain, venting valves</td><td>501-599</td></tr><tr><td>Self-regulating valves (thermal/pressure)</td><td>601-699</td></tr><tr><td>Instrument valves</td><td>701-799</td></tr><tr><td>-</td><td>801-899</td></tr><tr><td>Safety valves</td><td>901-999</td></tr></table>				Category	Numbers	Manual valves	001-099	Manual regulation valves	101-199	Pneumatic, electrical, solenoid	201-299	-	301-399	Check, Non-return valves	401-499	Drain, venting valves	501-599	Self-regulating valves (thermal/pressure)	601-699	Instrument valves	701-799	-	801-899	Safety valves	901-999																
Category	Numbers	
Manual valves	001-099	
Manual regulation valves	101-199	
Pneumatic, electrical, solenoid	201-299	
-	301-399	
Check, Non-return valves	401-499	
Drain, venting valves	501-599	
Self-regulating valves (thermal/pressure)	601-699	
Instrument valves	701-799	
-	801-899	
Safety valves	901-999	
	SV	Breather valve		LA	Light	
Mechanical valves				CA	Camera	
	PV	Pressure holding valve		FH	Foam hatch	
	CV	Check valve	Filters and Vessels	
	VV	Venting valve		AT	General filter / Forfilter	
Miscellaneous additional valve symbols				AT	General liquid	
				AT	Drier - General	
Operator lock mechanism				F	Suction hood	
				EXP	Expansion tank	
1		2		3		4		5		6		7		8																																				
									Revision clouds			<table><tr><td>Rev. Nr.:</td><td>Rev. Dato:</td><td>Rev. Beskrivelse:</td></tr><tr><td>Builder:</td><td>ST1</td><td></td></tr><tr><td>Project:</td><td>SLK</td><td></td></tr><tr><td>Subject:</td><td>PID legend 2</td><td></td></tr><tr><td>Rev. 6</td><td></td><td></td></tr><tr><td>Int.:MDC</td><td>QC: CM</td><td>APP.: Date: 15-10-2025</td></tr></table> LUNDSBY RENEWABLE SOLUTIONS Lundsby Biogas A/S, Hjarbækvej 65, 8831 Løgstrup Tlf.: +45 96 49 43 00 Info@lundsbybiogas.dk Denne tegning er underlagt copyright og må ikke reproduceres uden tilladelse fra Lundsby Biogas A/S			Rev. Nr.:	Rev. Dato:	Rev. Beskrivelse:	Builder:	ST1		Project:	SLK		Subject:	PID legend 2		Rev. 6			Int.:MDC	QC: CM	APP.: Date: 15-10-2025	Project nr.: 1768 Drawing nr.: PID legend 2 FORMAT: A1																	
Rev. Nr.:	Rev. Dato:	Rev. Beskrivelse:	
Builder:	ST1	
Project:	SLK	
Subject:	PID legend 2	
Rev. 6	
Int.:MDC	QC: CM	APP.: Date: 15-10-2025	

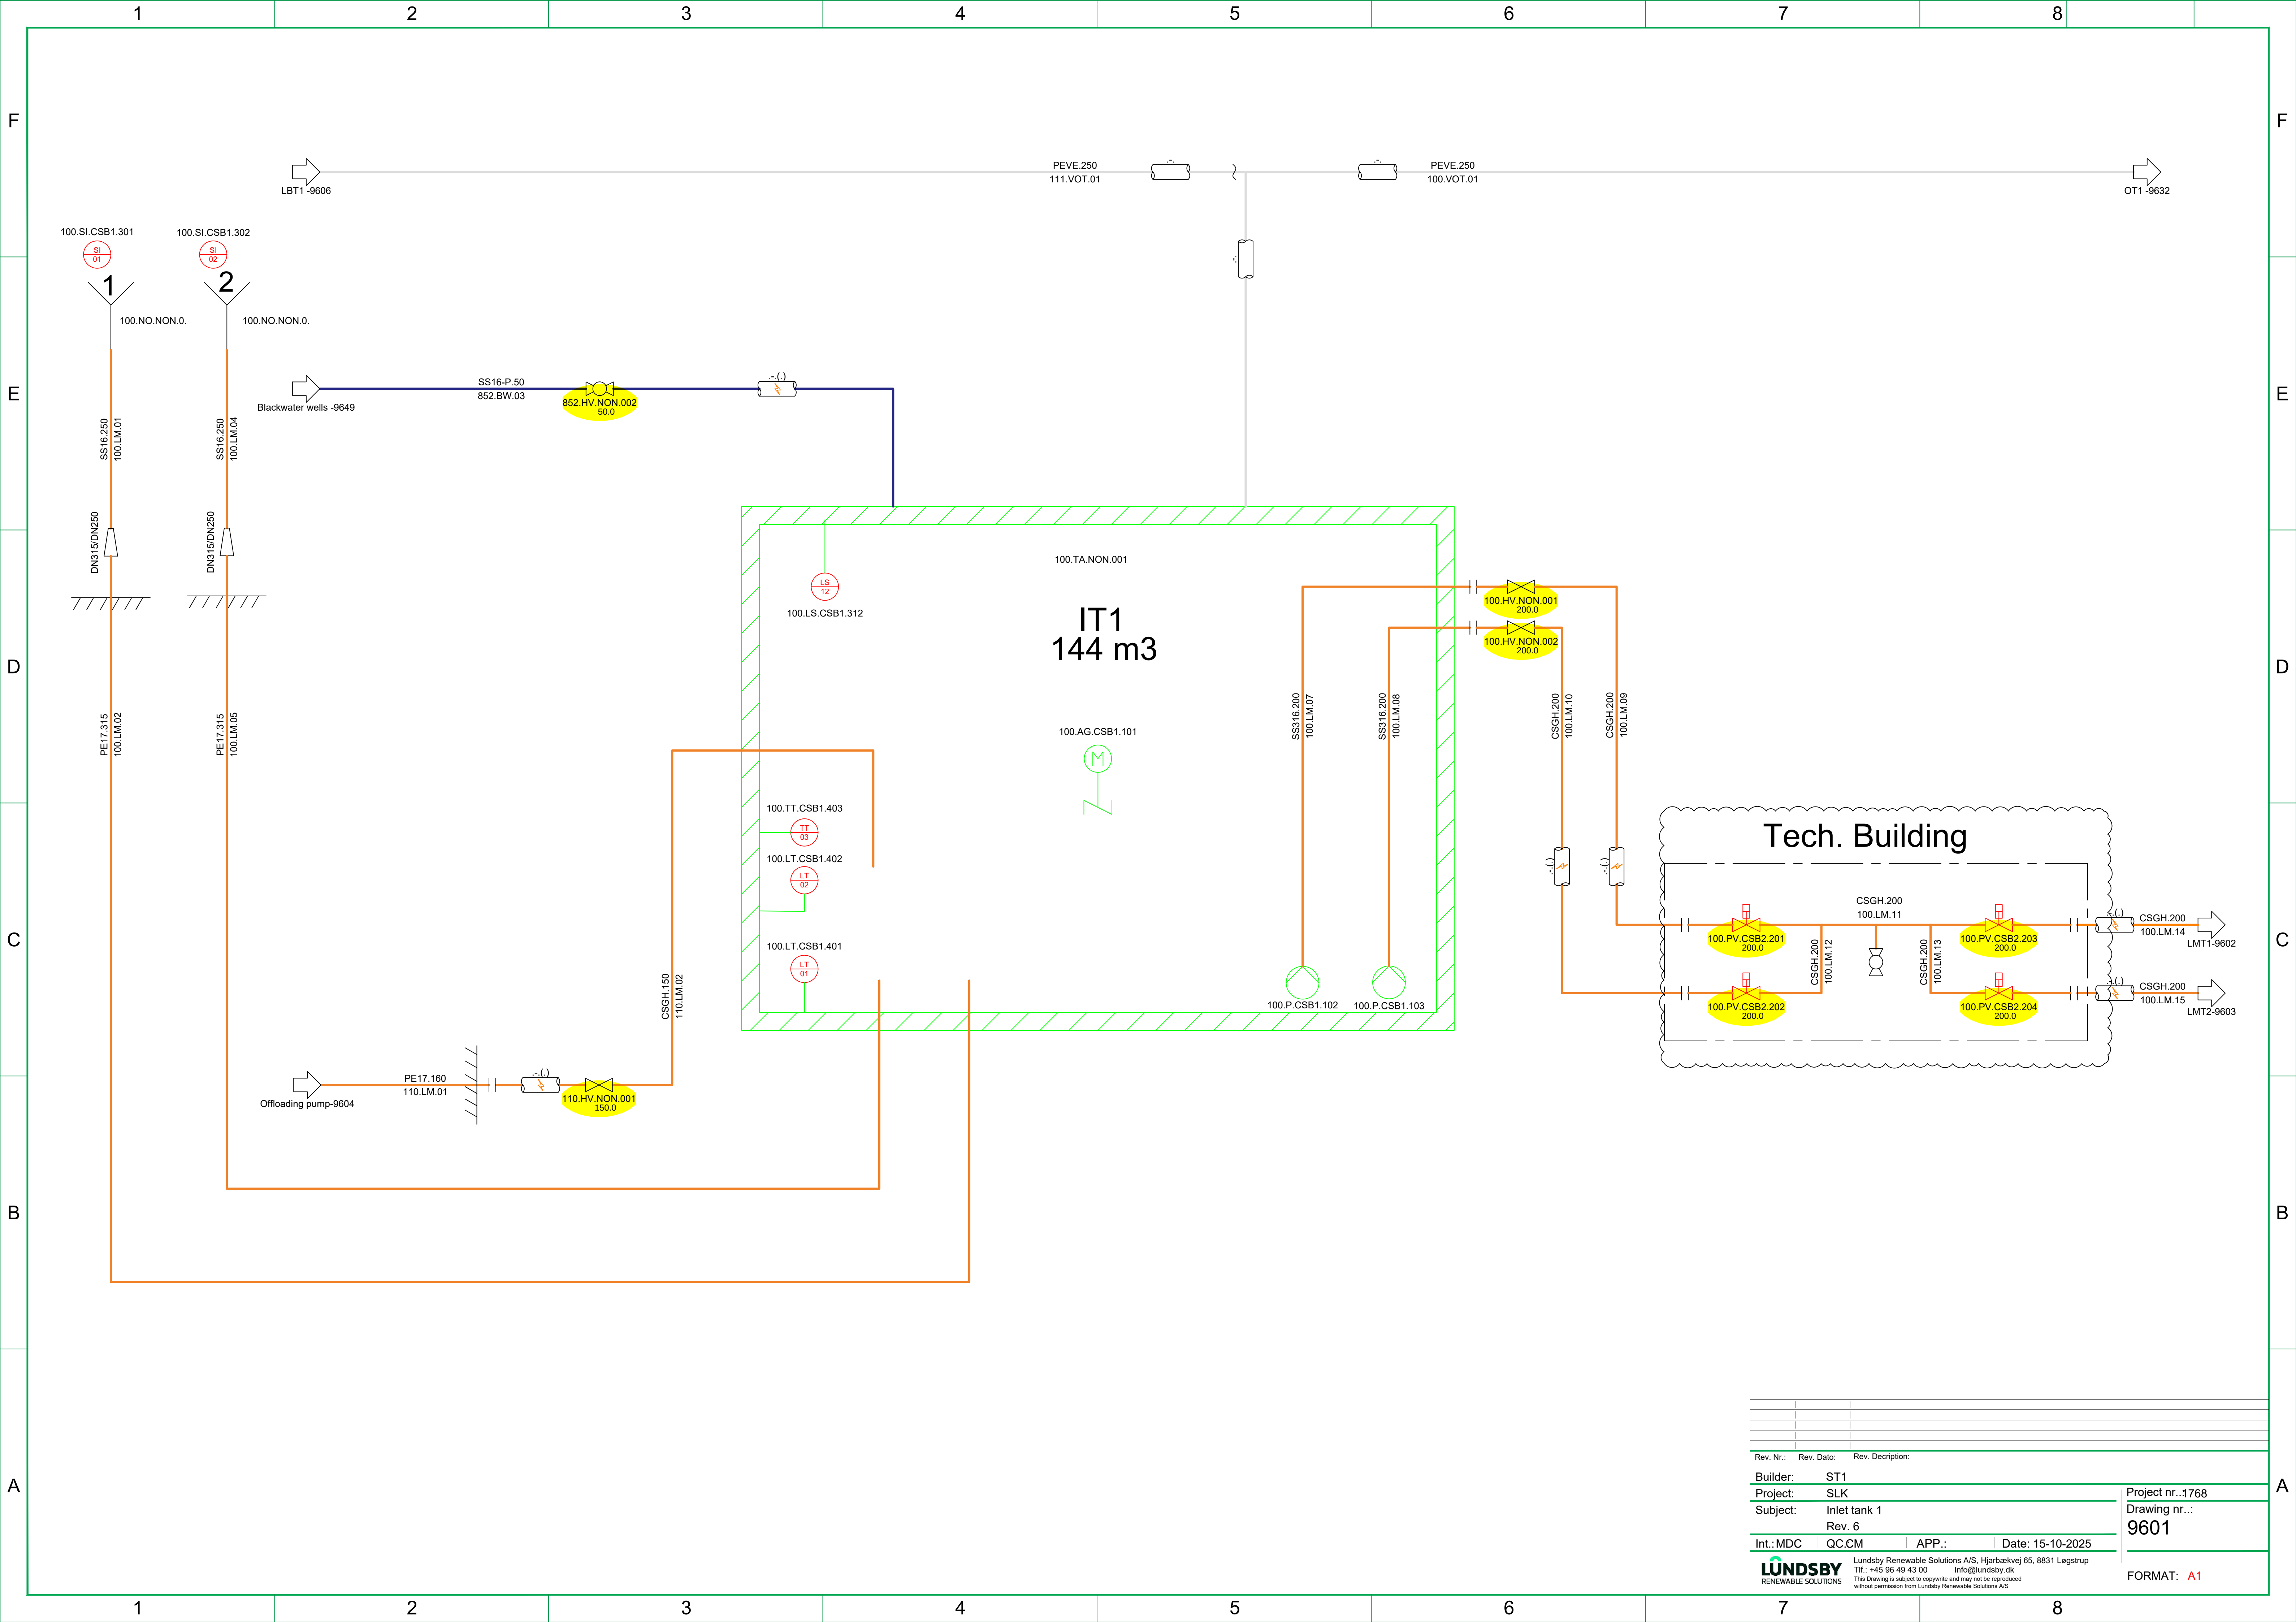


Rev. Nr.:	Rev. Dato:	Rev. Description:
Builder:	ST1	
Project:	SLK	
Subject:	Inlet tank 1	
	Rev. 6	
Int.:MDC	QC:CM	APP.:
		Date: 15-10-2025
LUNDSBY RENEWABLE SOLUTIONS		
Lundsby Renewable Solutions A/S, Hjarbækvej 65, 8831 Løgstrup Tlf.: +45 96 49 43 00 info@lundsby.dk This drawing is subject to copyright and may not be reproduced without permission from Lundsby Renewable Solutions A/S		
Project nr.:1768 Drawing nr.: 9601		FORMAT: A1

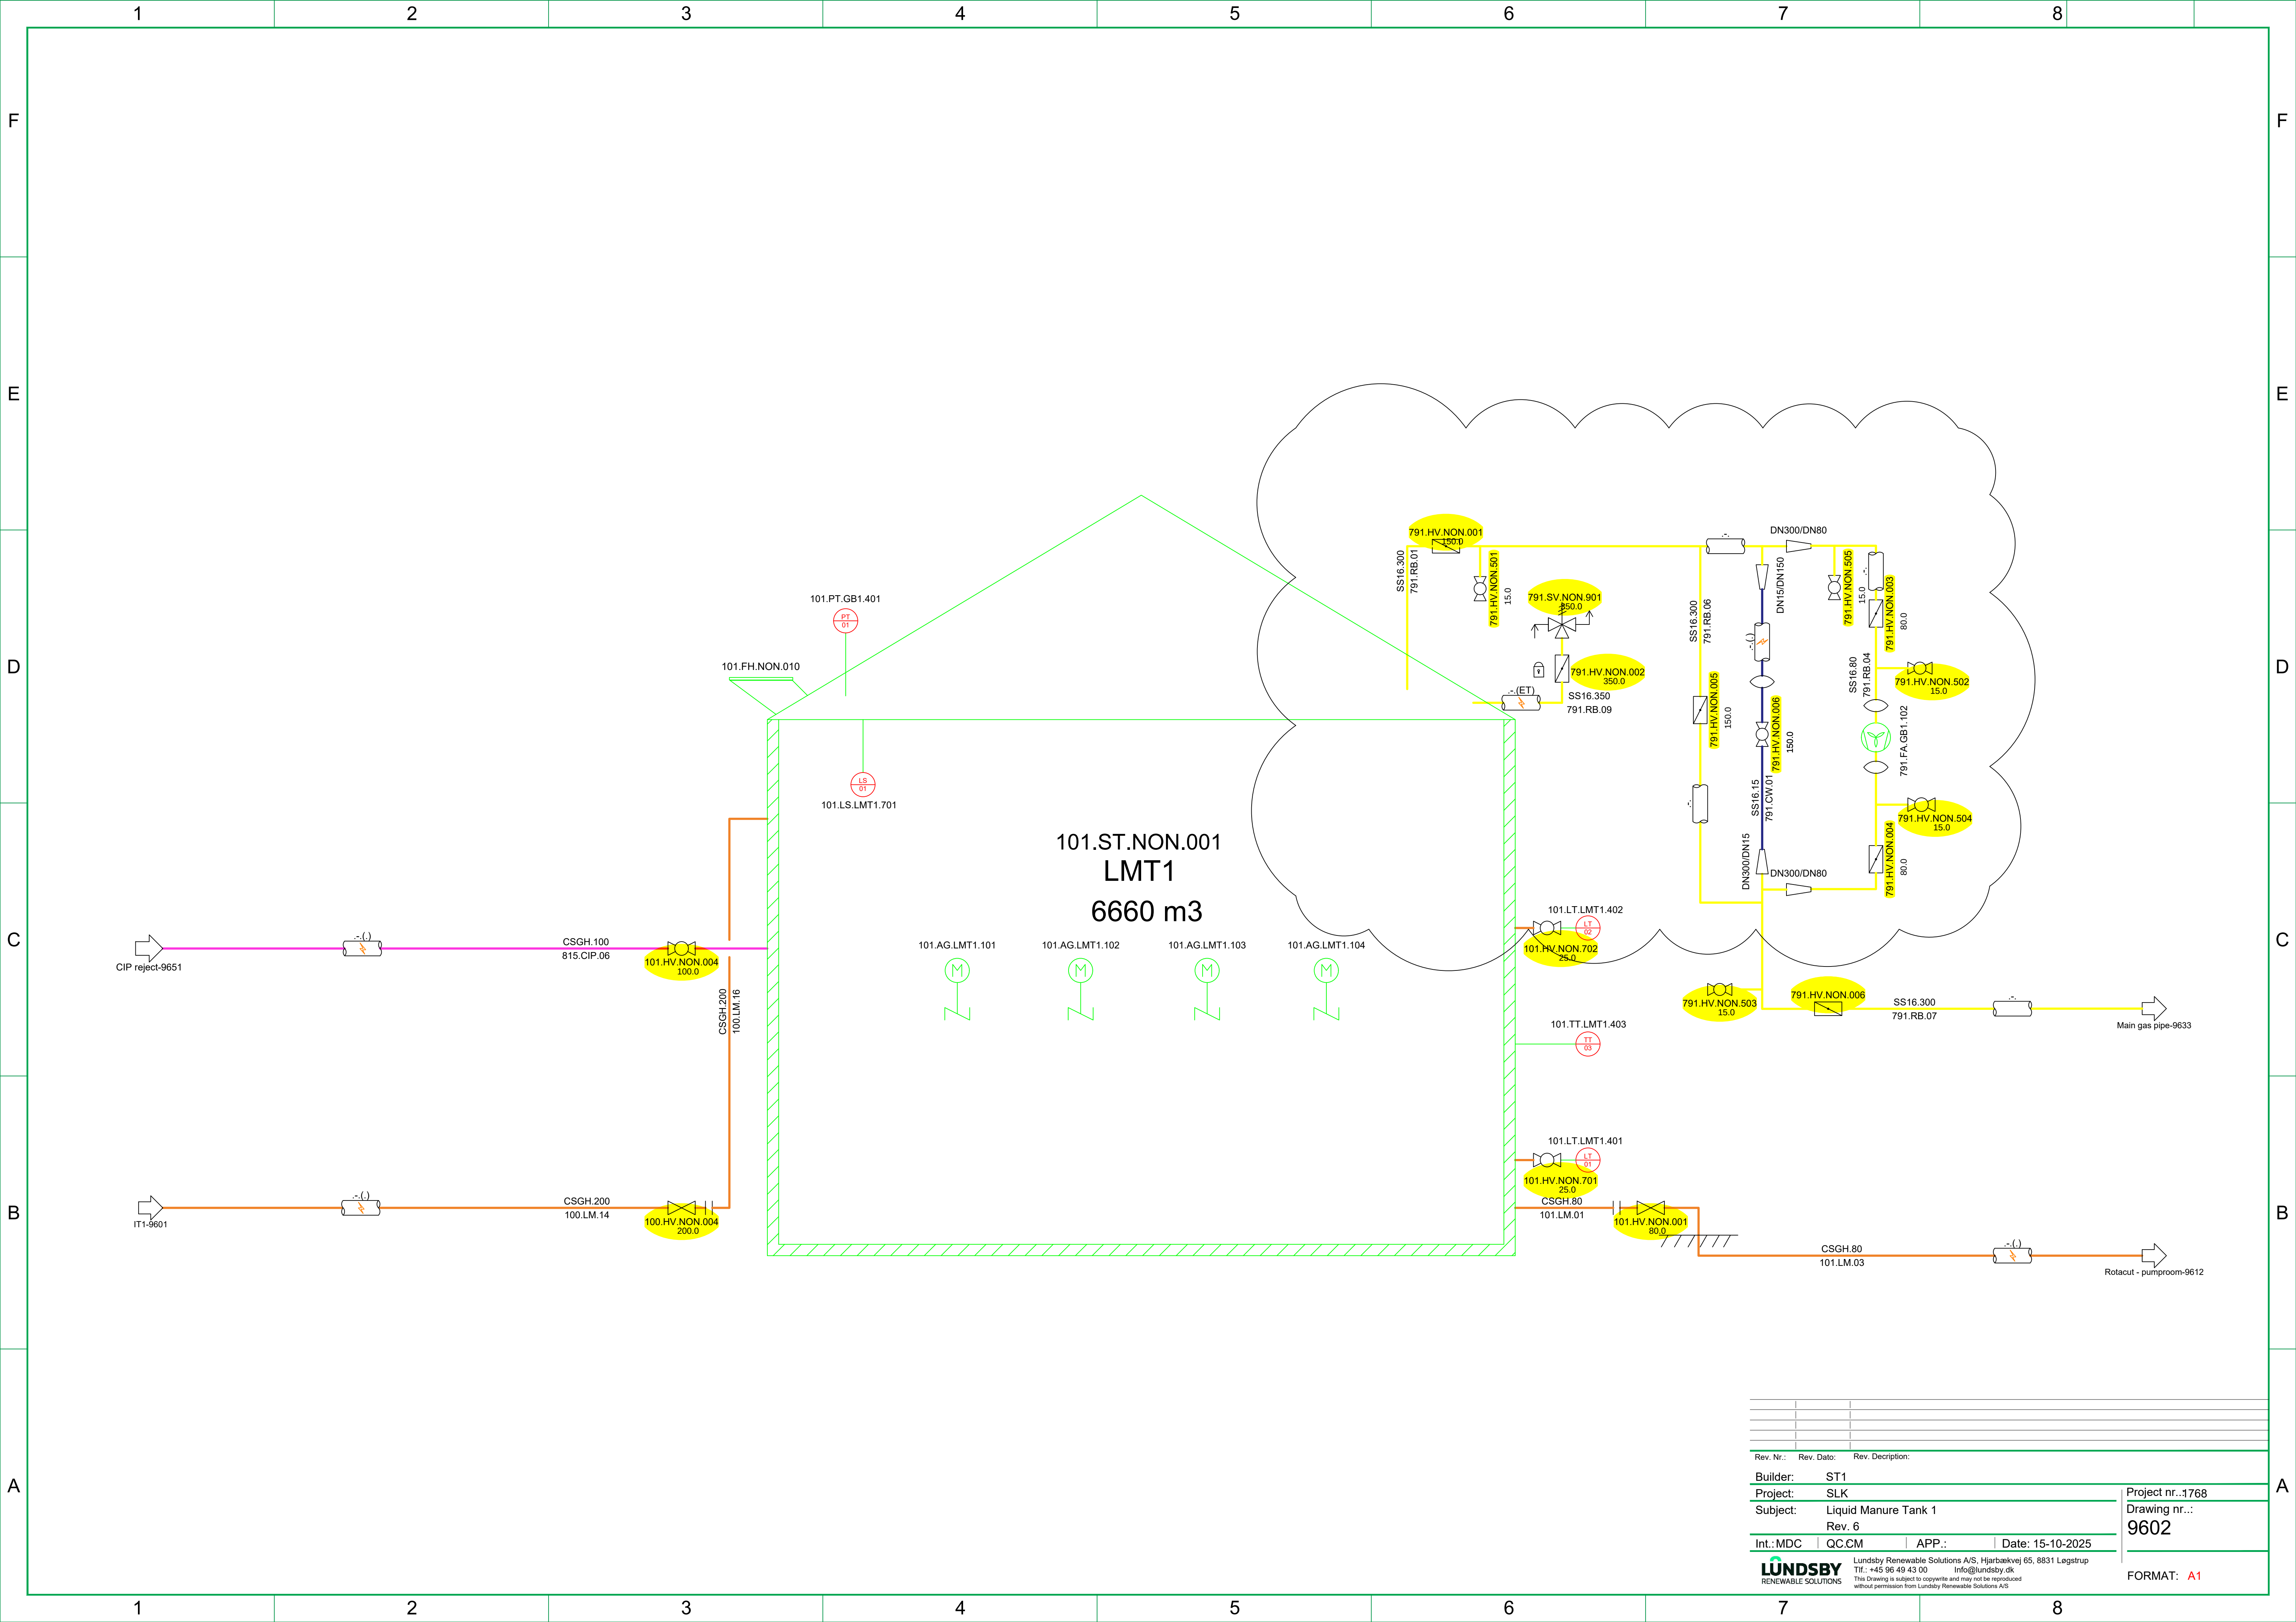


	</
--	--	----

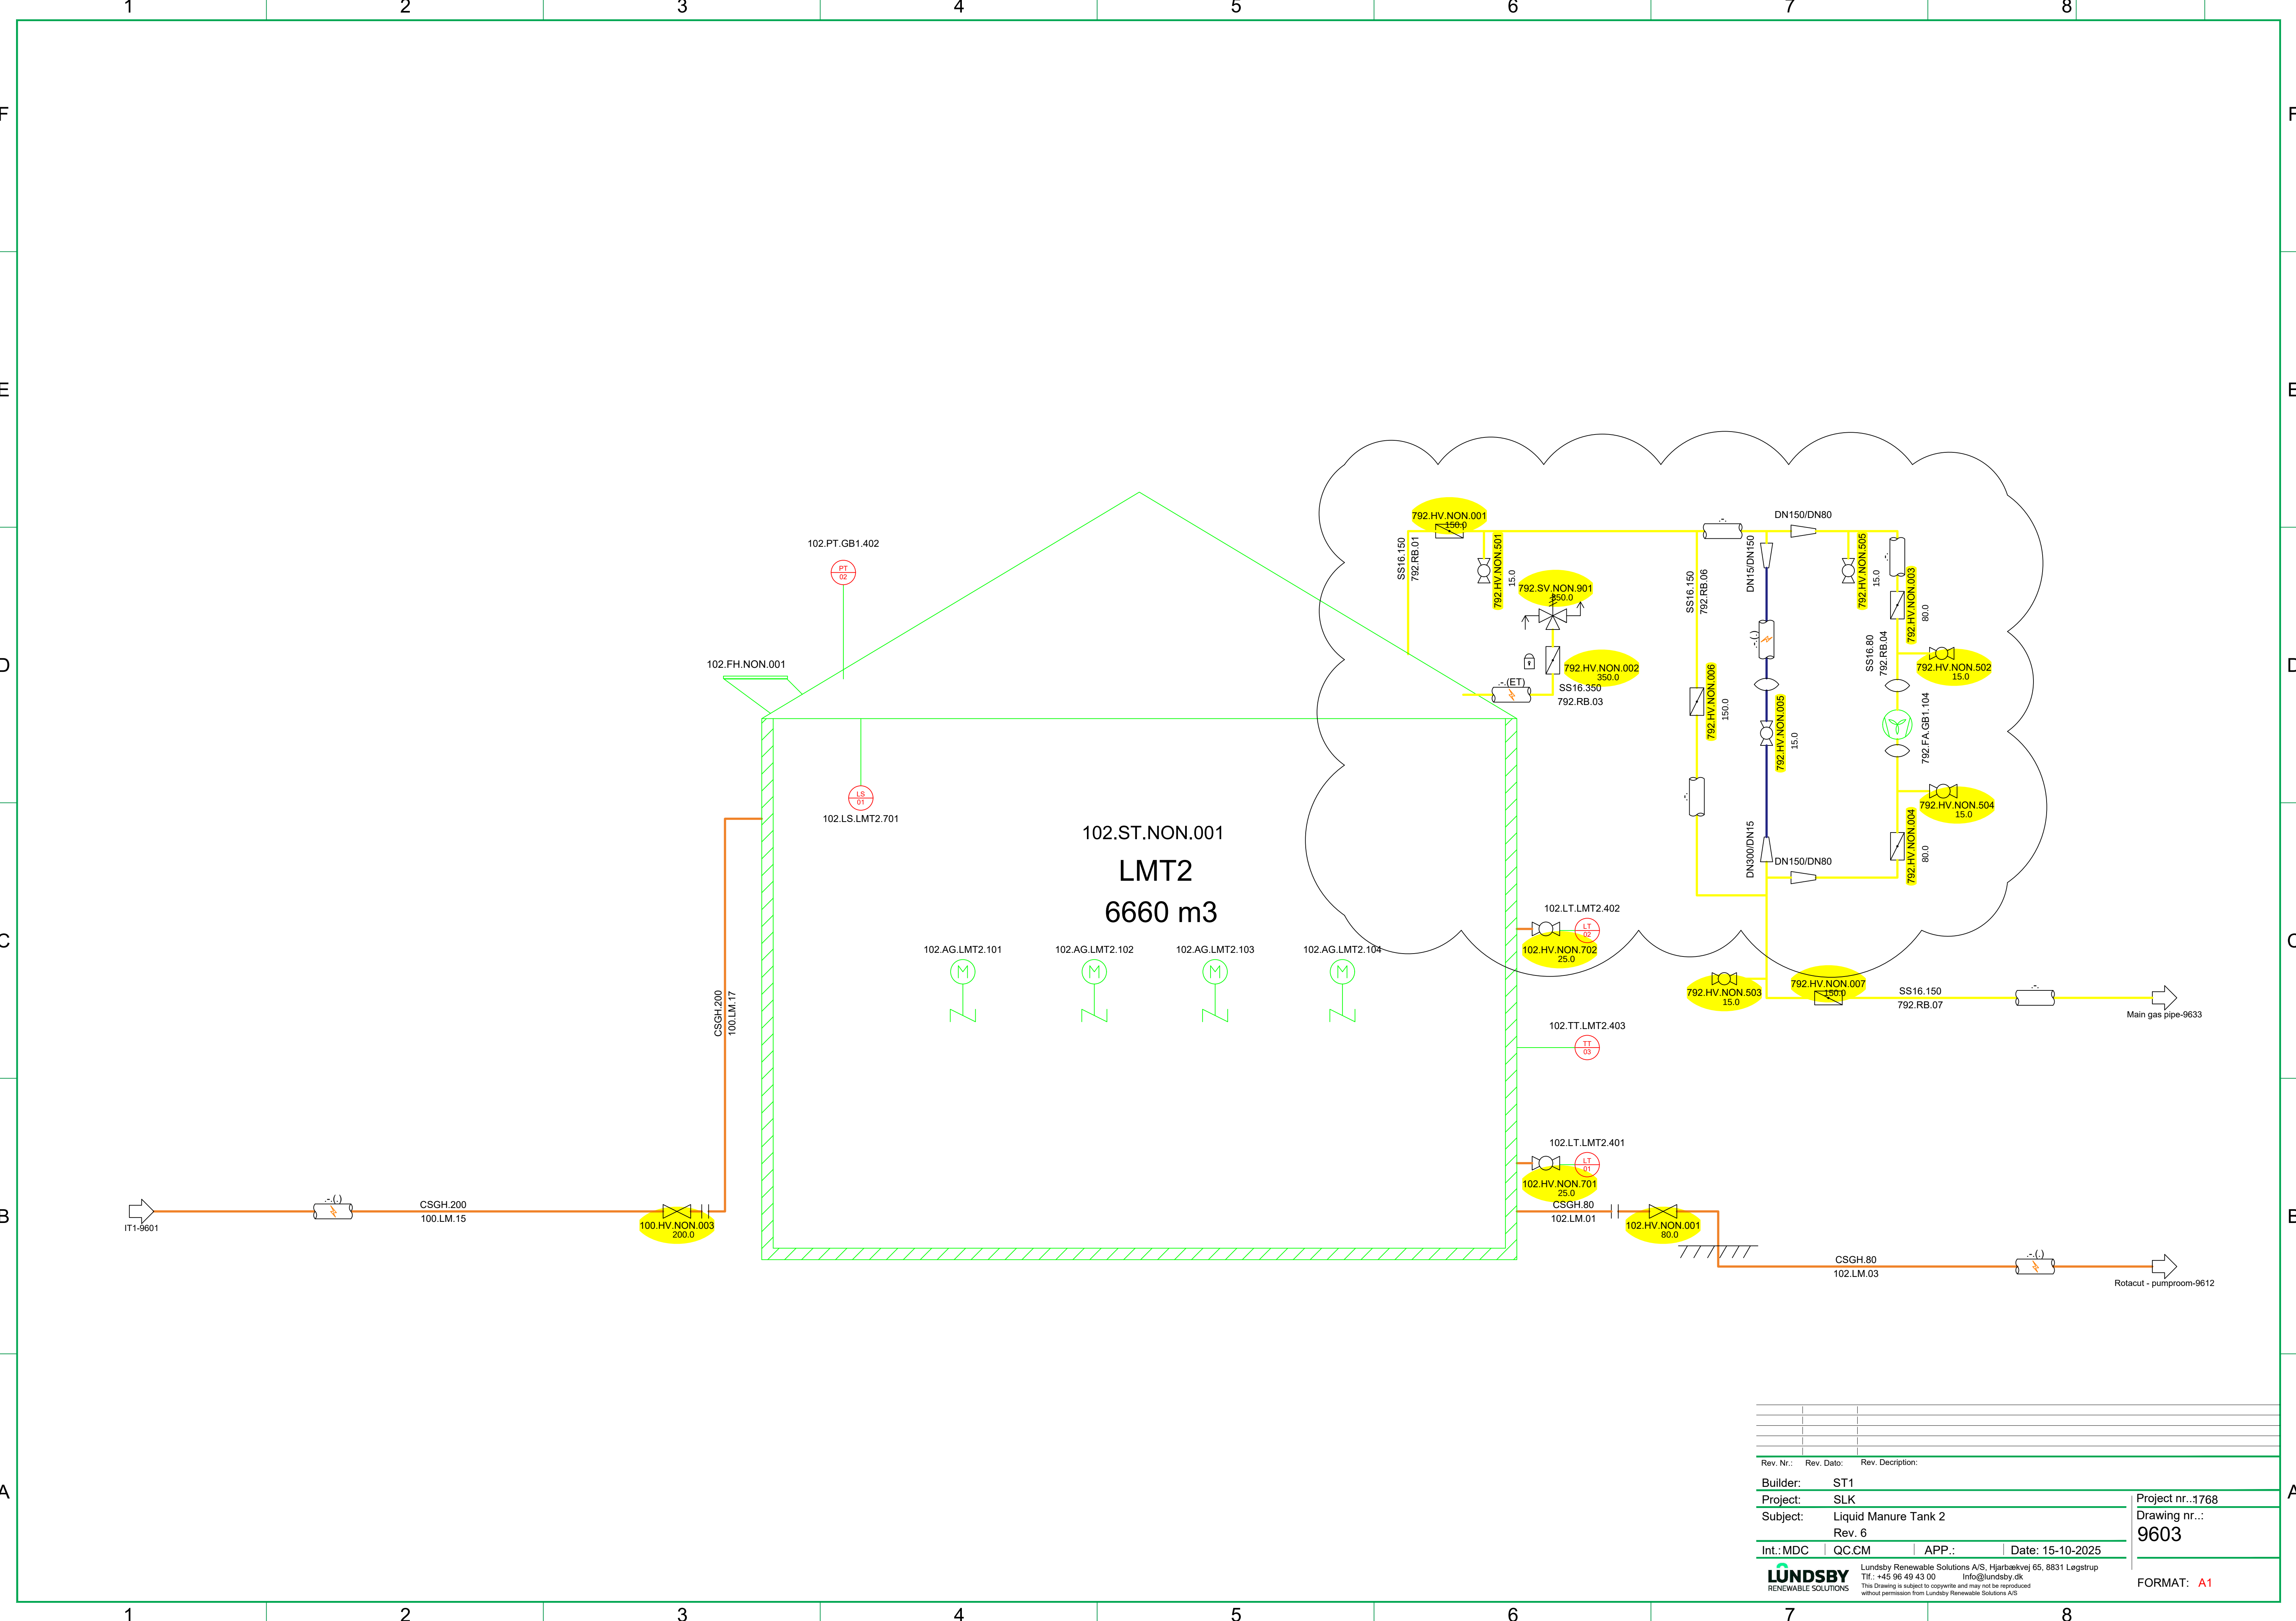


Rev. Nr.:	Rev. Dato:	Rev. Description:	
Builder:	ST1		
Project:	SLK		
Subject:	Liquid Manure Tank 2		
Rev. 6			
Int.:MDC	QC:CM	APP.:	Date: 15-10-2025
LUNDSBY RENEWABLE SOLUTIONS			Lundsby Renewable Solutions A/S, Hjarbækvej 65, 8831 Løgstrup Tlf.: +45 96 49 43 00 Info@lundsby.dk This Drawing is subject to copyright and may not be reproduced without permission from Lundsby Renewable Solutions A/S
Project nr.:1768 Drawing nr.: 9603			FORMAT: A1

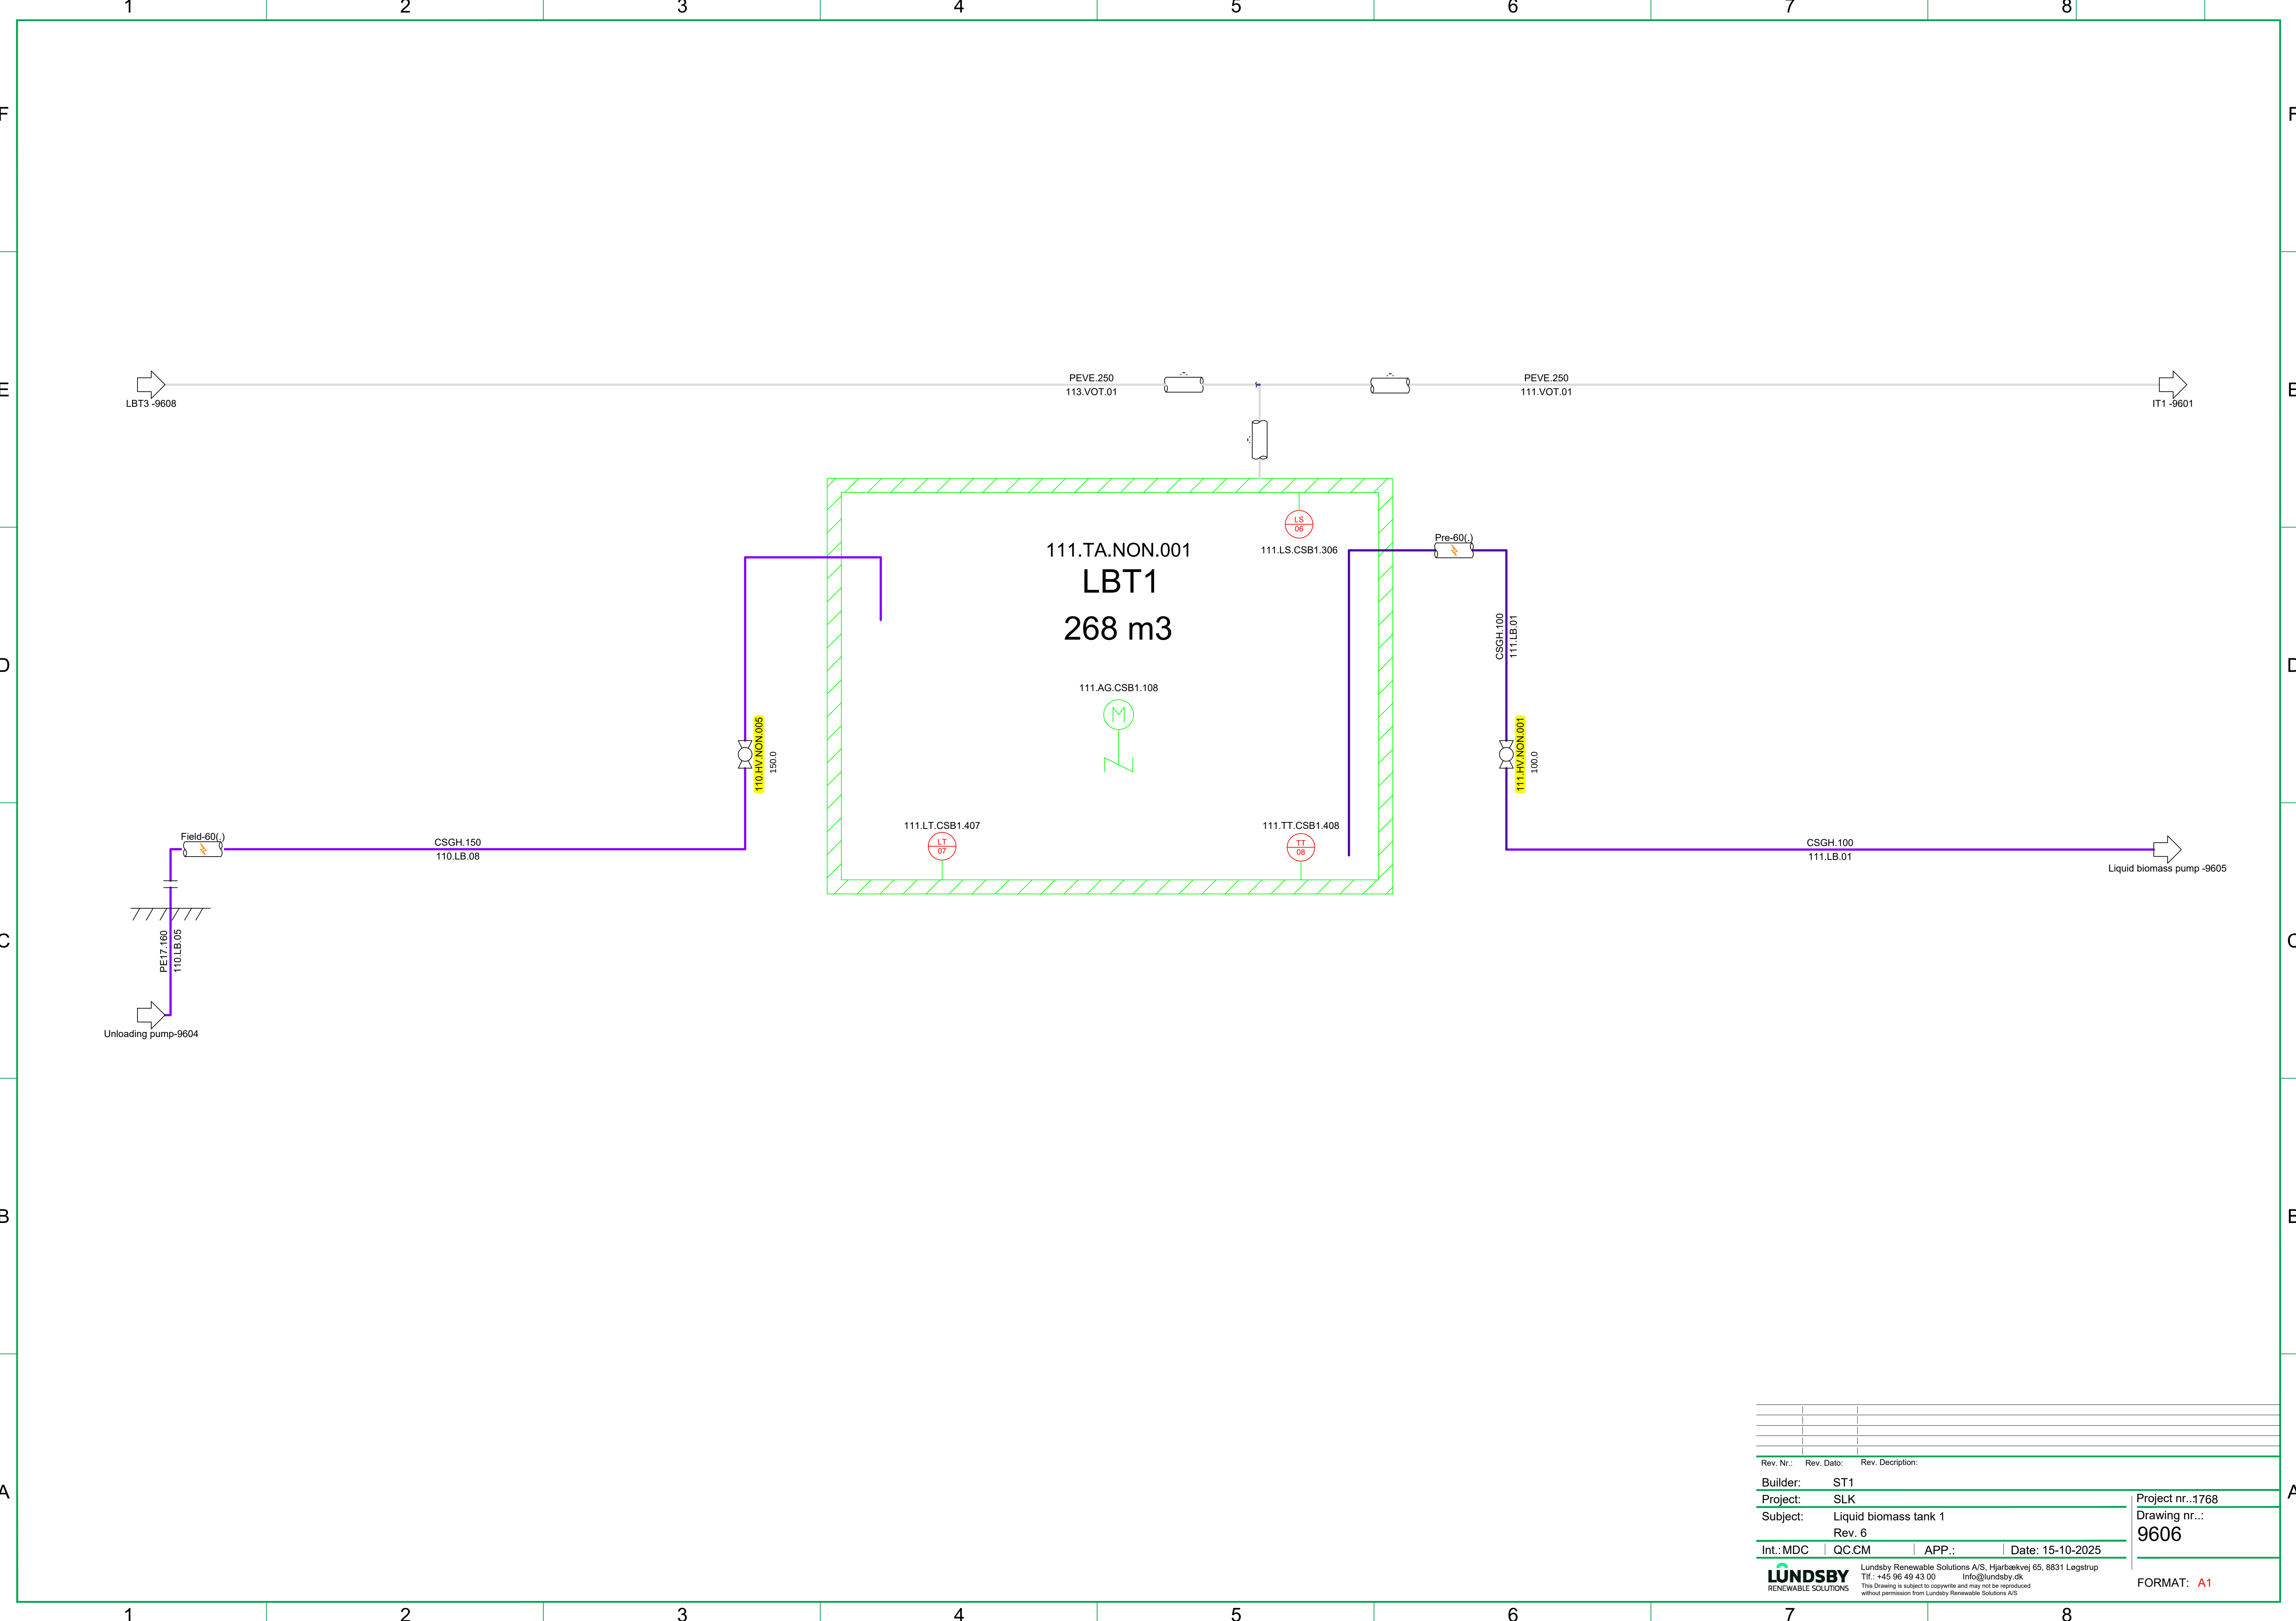


Rev. Nr.:	Rev. Dato:	Rev. Description:	
Builder:	ST1		
Project:	SLK		
Subject:	Liquid biomass tank 1		
	Rev. 6		
Int.:MDC	QC.CM	APP.:	Date: 15-10-2025
LUNDSBY RENEWABLE SOLUTIONS			Lundsby Renewable Solutions A/S, Hjarbækvej 65, 8831 Løgstrup Tlf.: +45 96 49 43 00 Info@lundsby.dk This Drawing is subject to copyright and may not be reproduced without permission from Lundsby Renewable Solutions A/S
			Project nr...1768 Drawing nr...: 9606
			FORMAT: A1

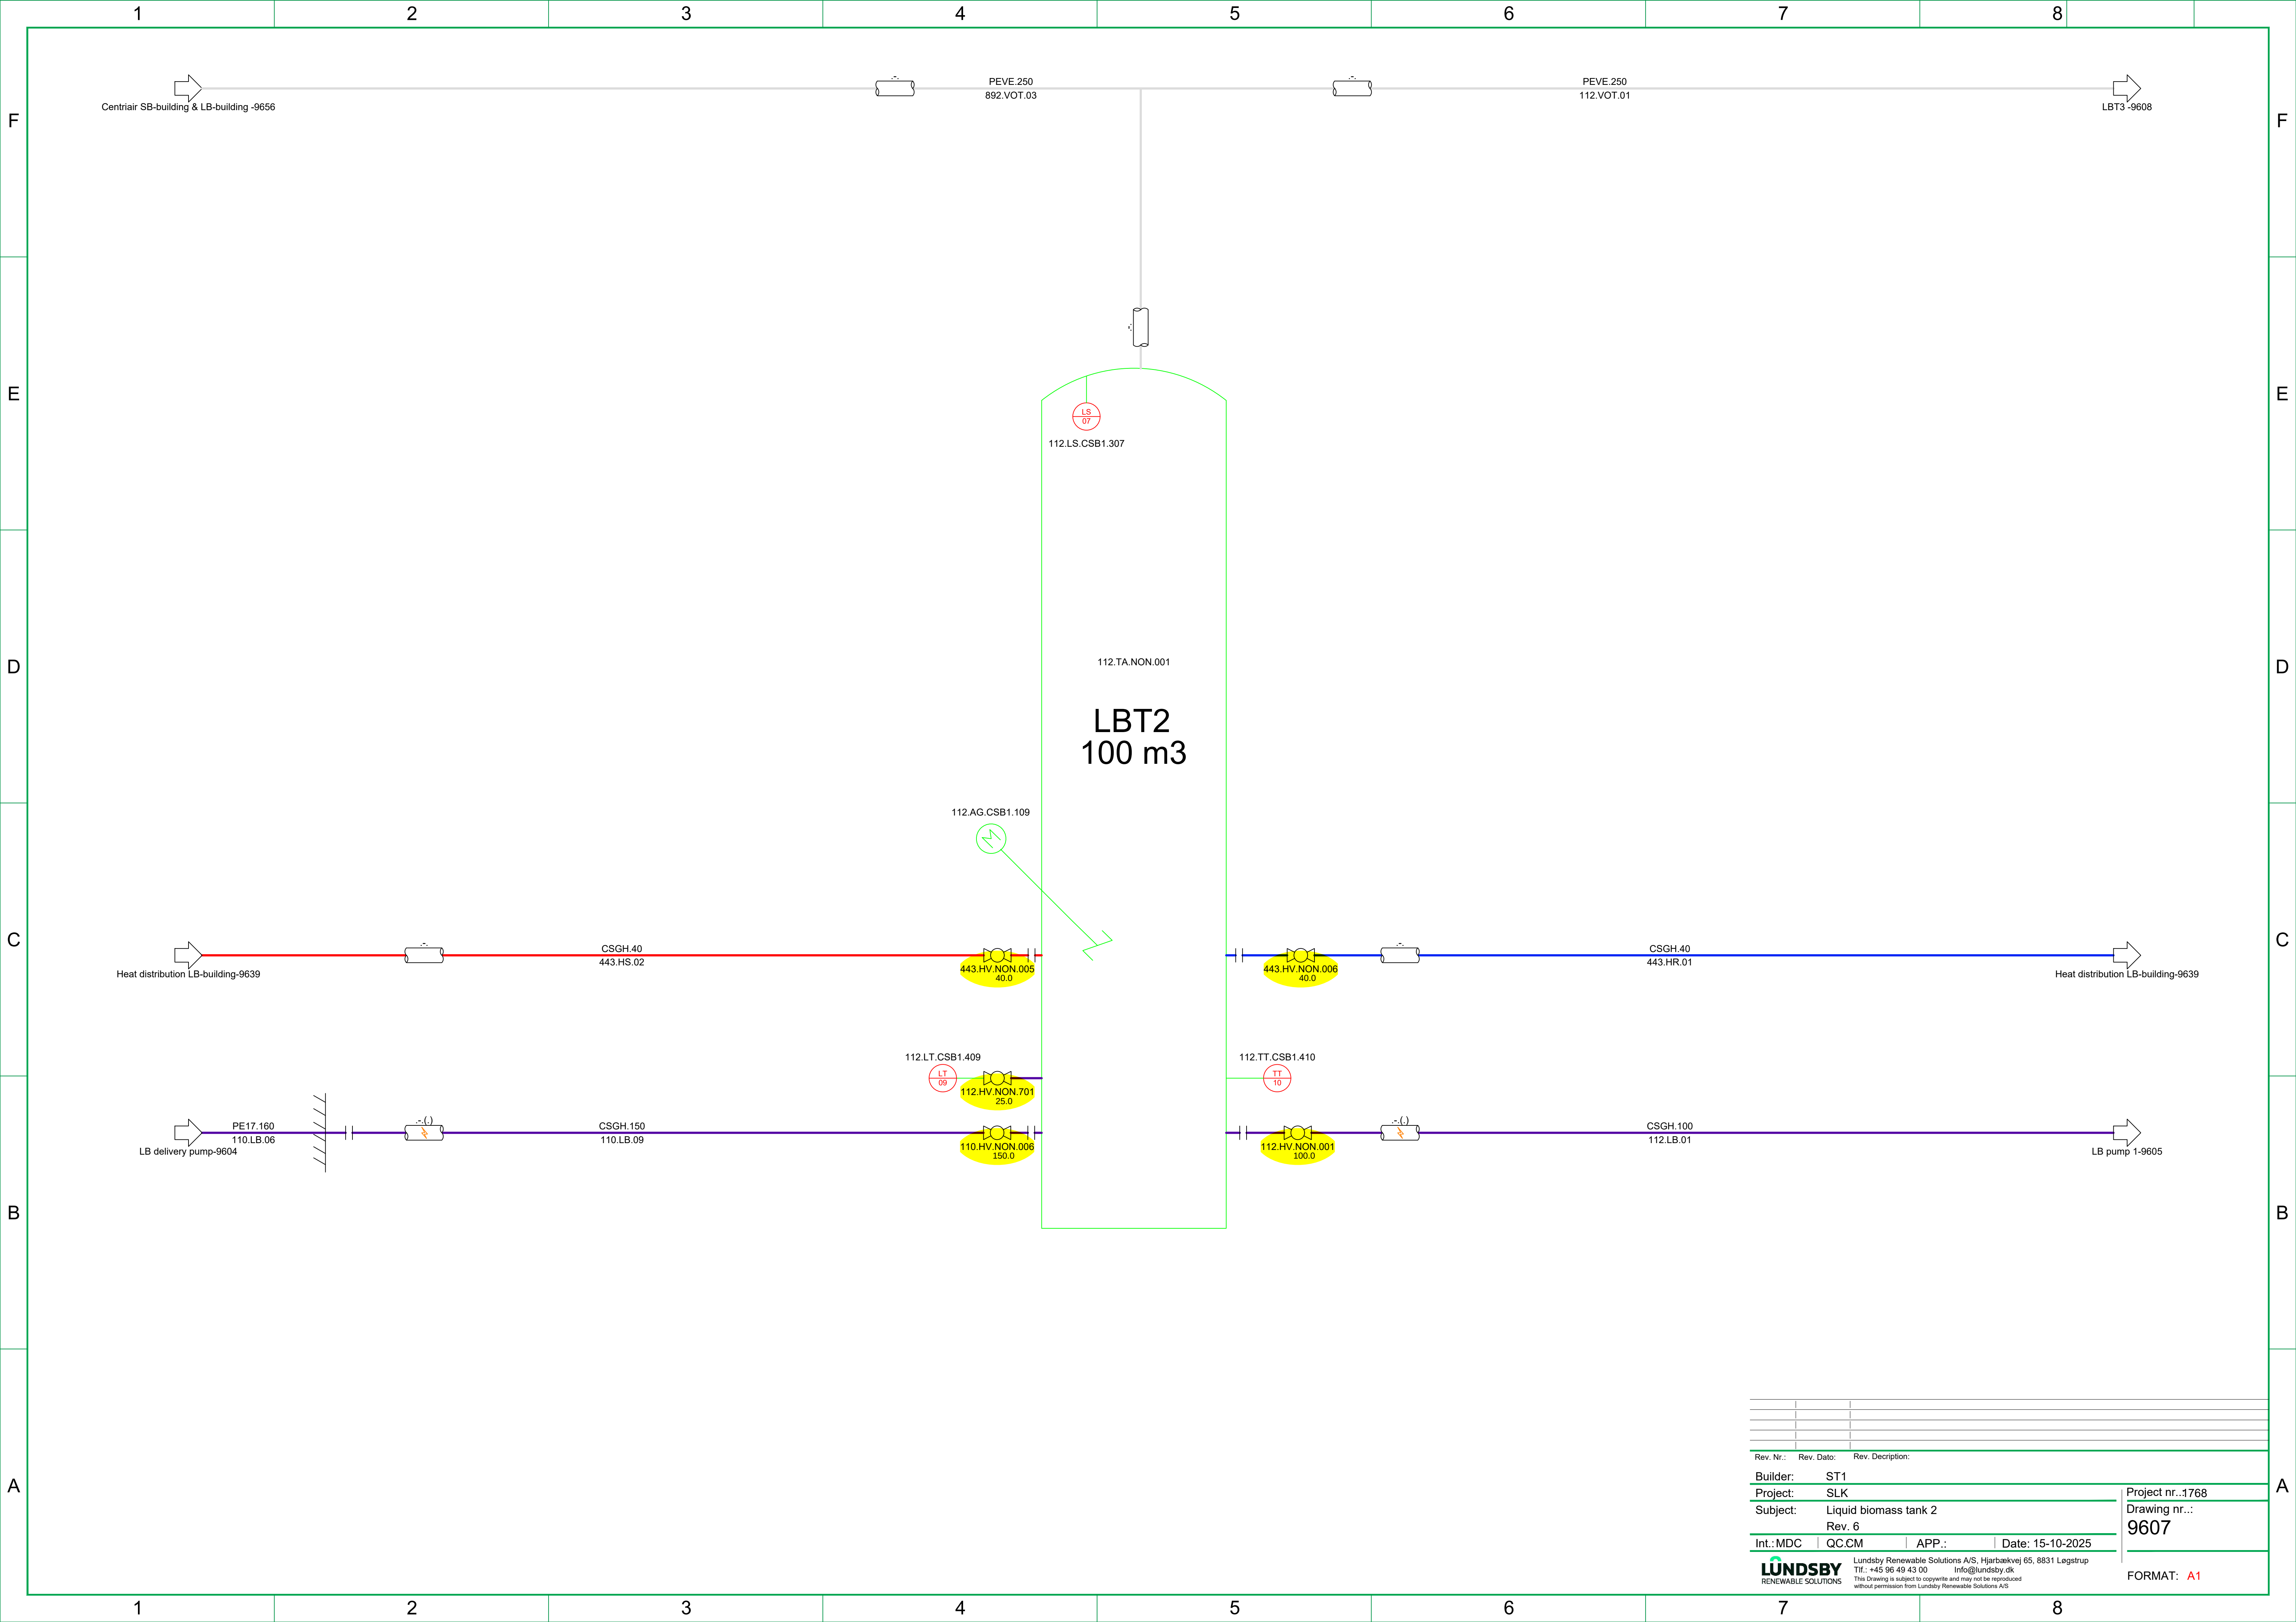


Rev. Nr.:	Rev. Dato:	Rev. Description:
Builder:	ST1	
Project:	SLK	
Subject:	Liquid biomass tank 2	
Rev. 6		
Int.:MDC	QC:CM	APP.:
Date: 15-10-2025		
LUNDSBY RENEWABLE SOLUTIONS		
Lundsby Renewable Solutions A/S, Hjarbækvej 65, 8831 Løgstrup Tlf.: +45 96 49 43 00 Info@lundsby.dk This Drawing is subject to copyright and may not be reproduced without permission from Lundsby Renewable Solutions A/S		
Project nr...1768 Drawing nr...: 9607		FORMAT: A1

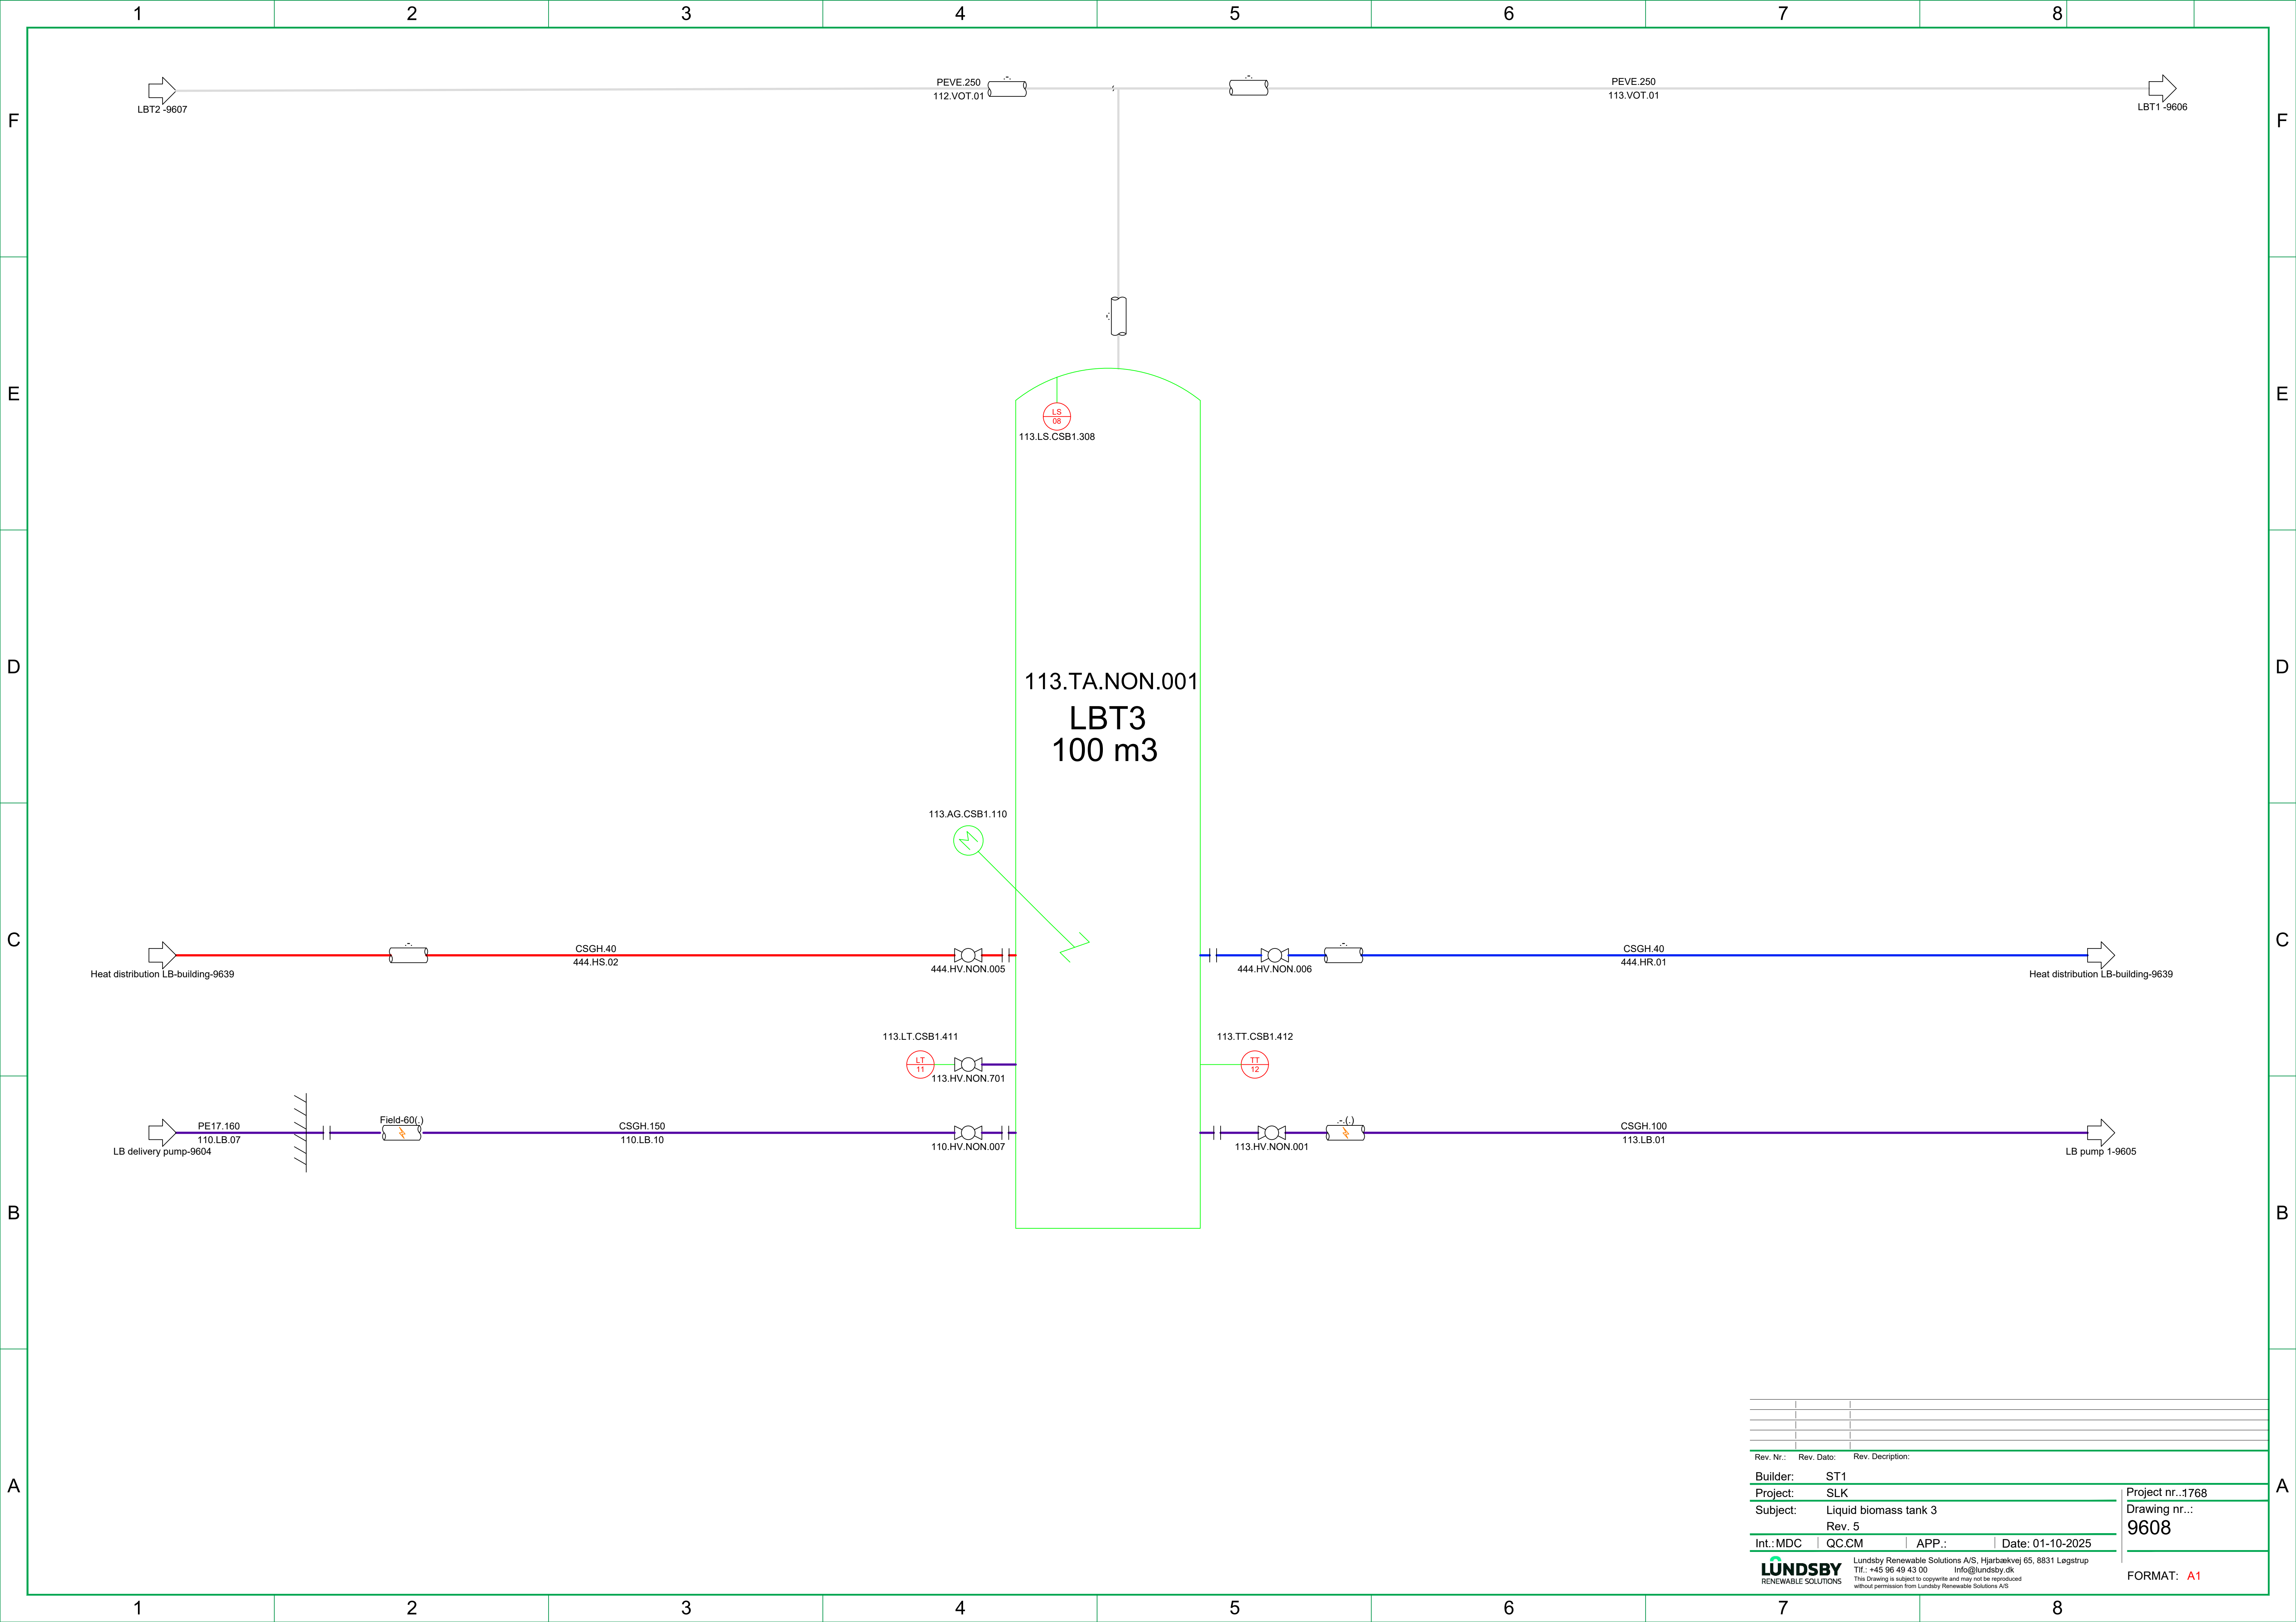


Rev. Nr.:	Rev. Dato:	Rev. Description:		
Builder:	ST1			
Project:	SLK			
Subject:	Liquid biomass tank 3			
	Rev. 5			
Int.:MDC	QC:CM	APP.:	Date: 01-10-2025	
LUNDSBY RENEWABLE SOLUTIONS Lundsby Renewable Solutions A/S, Hjarbækvej 65, 8831 Løgstrup Tlf.: +45 96 49 43 00 Info@lundsby.dk This Drawing is subject to copyright and may not be reproduced without permission from Lundsby Renewable Solutions A/S				
Project nr...1768			Drawing nr...: 9608	
			FORMAT: A1	

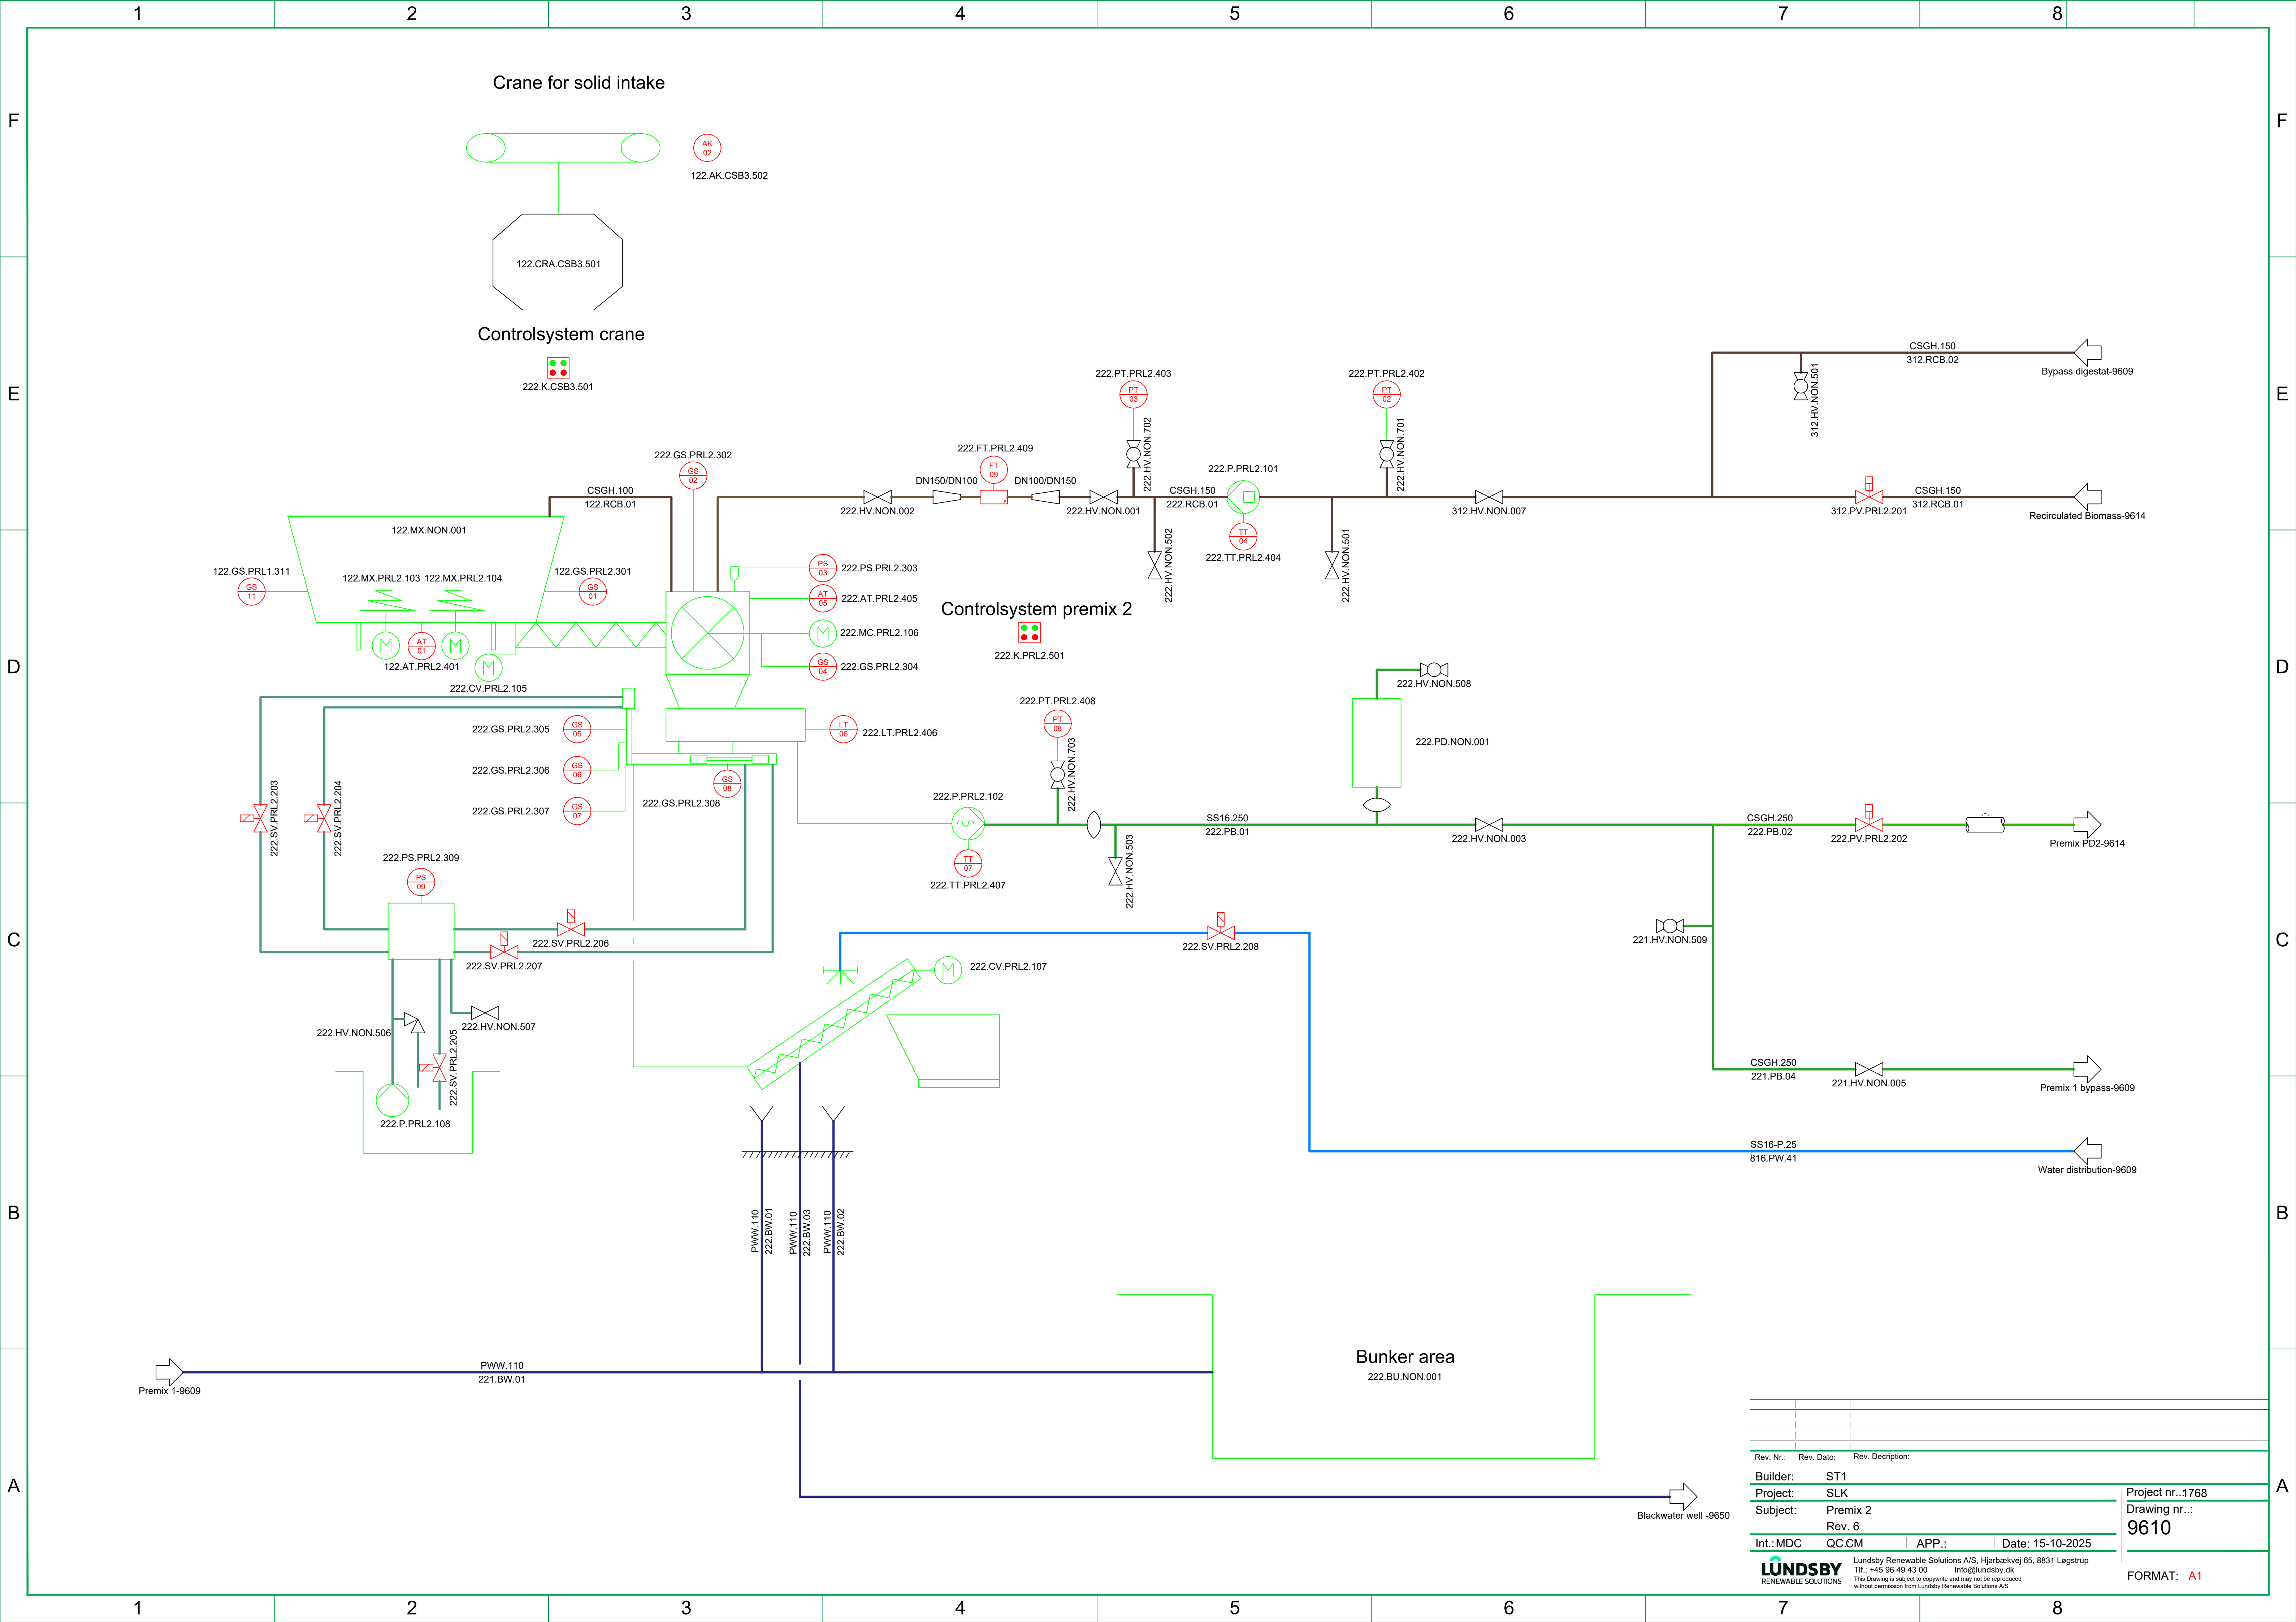

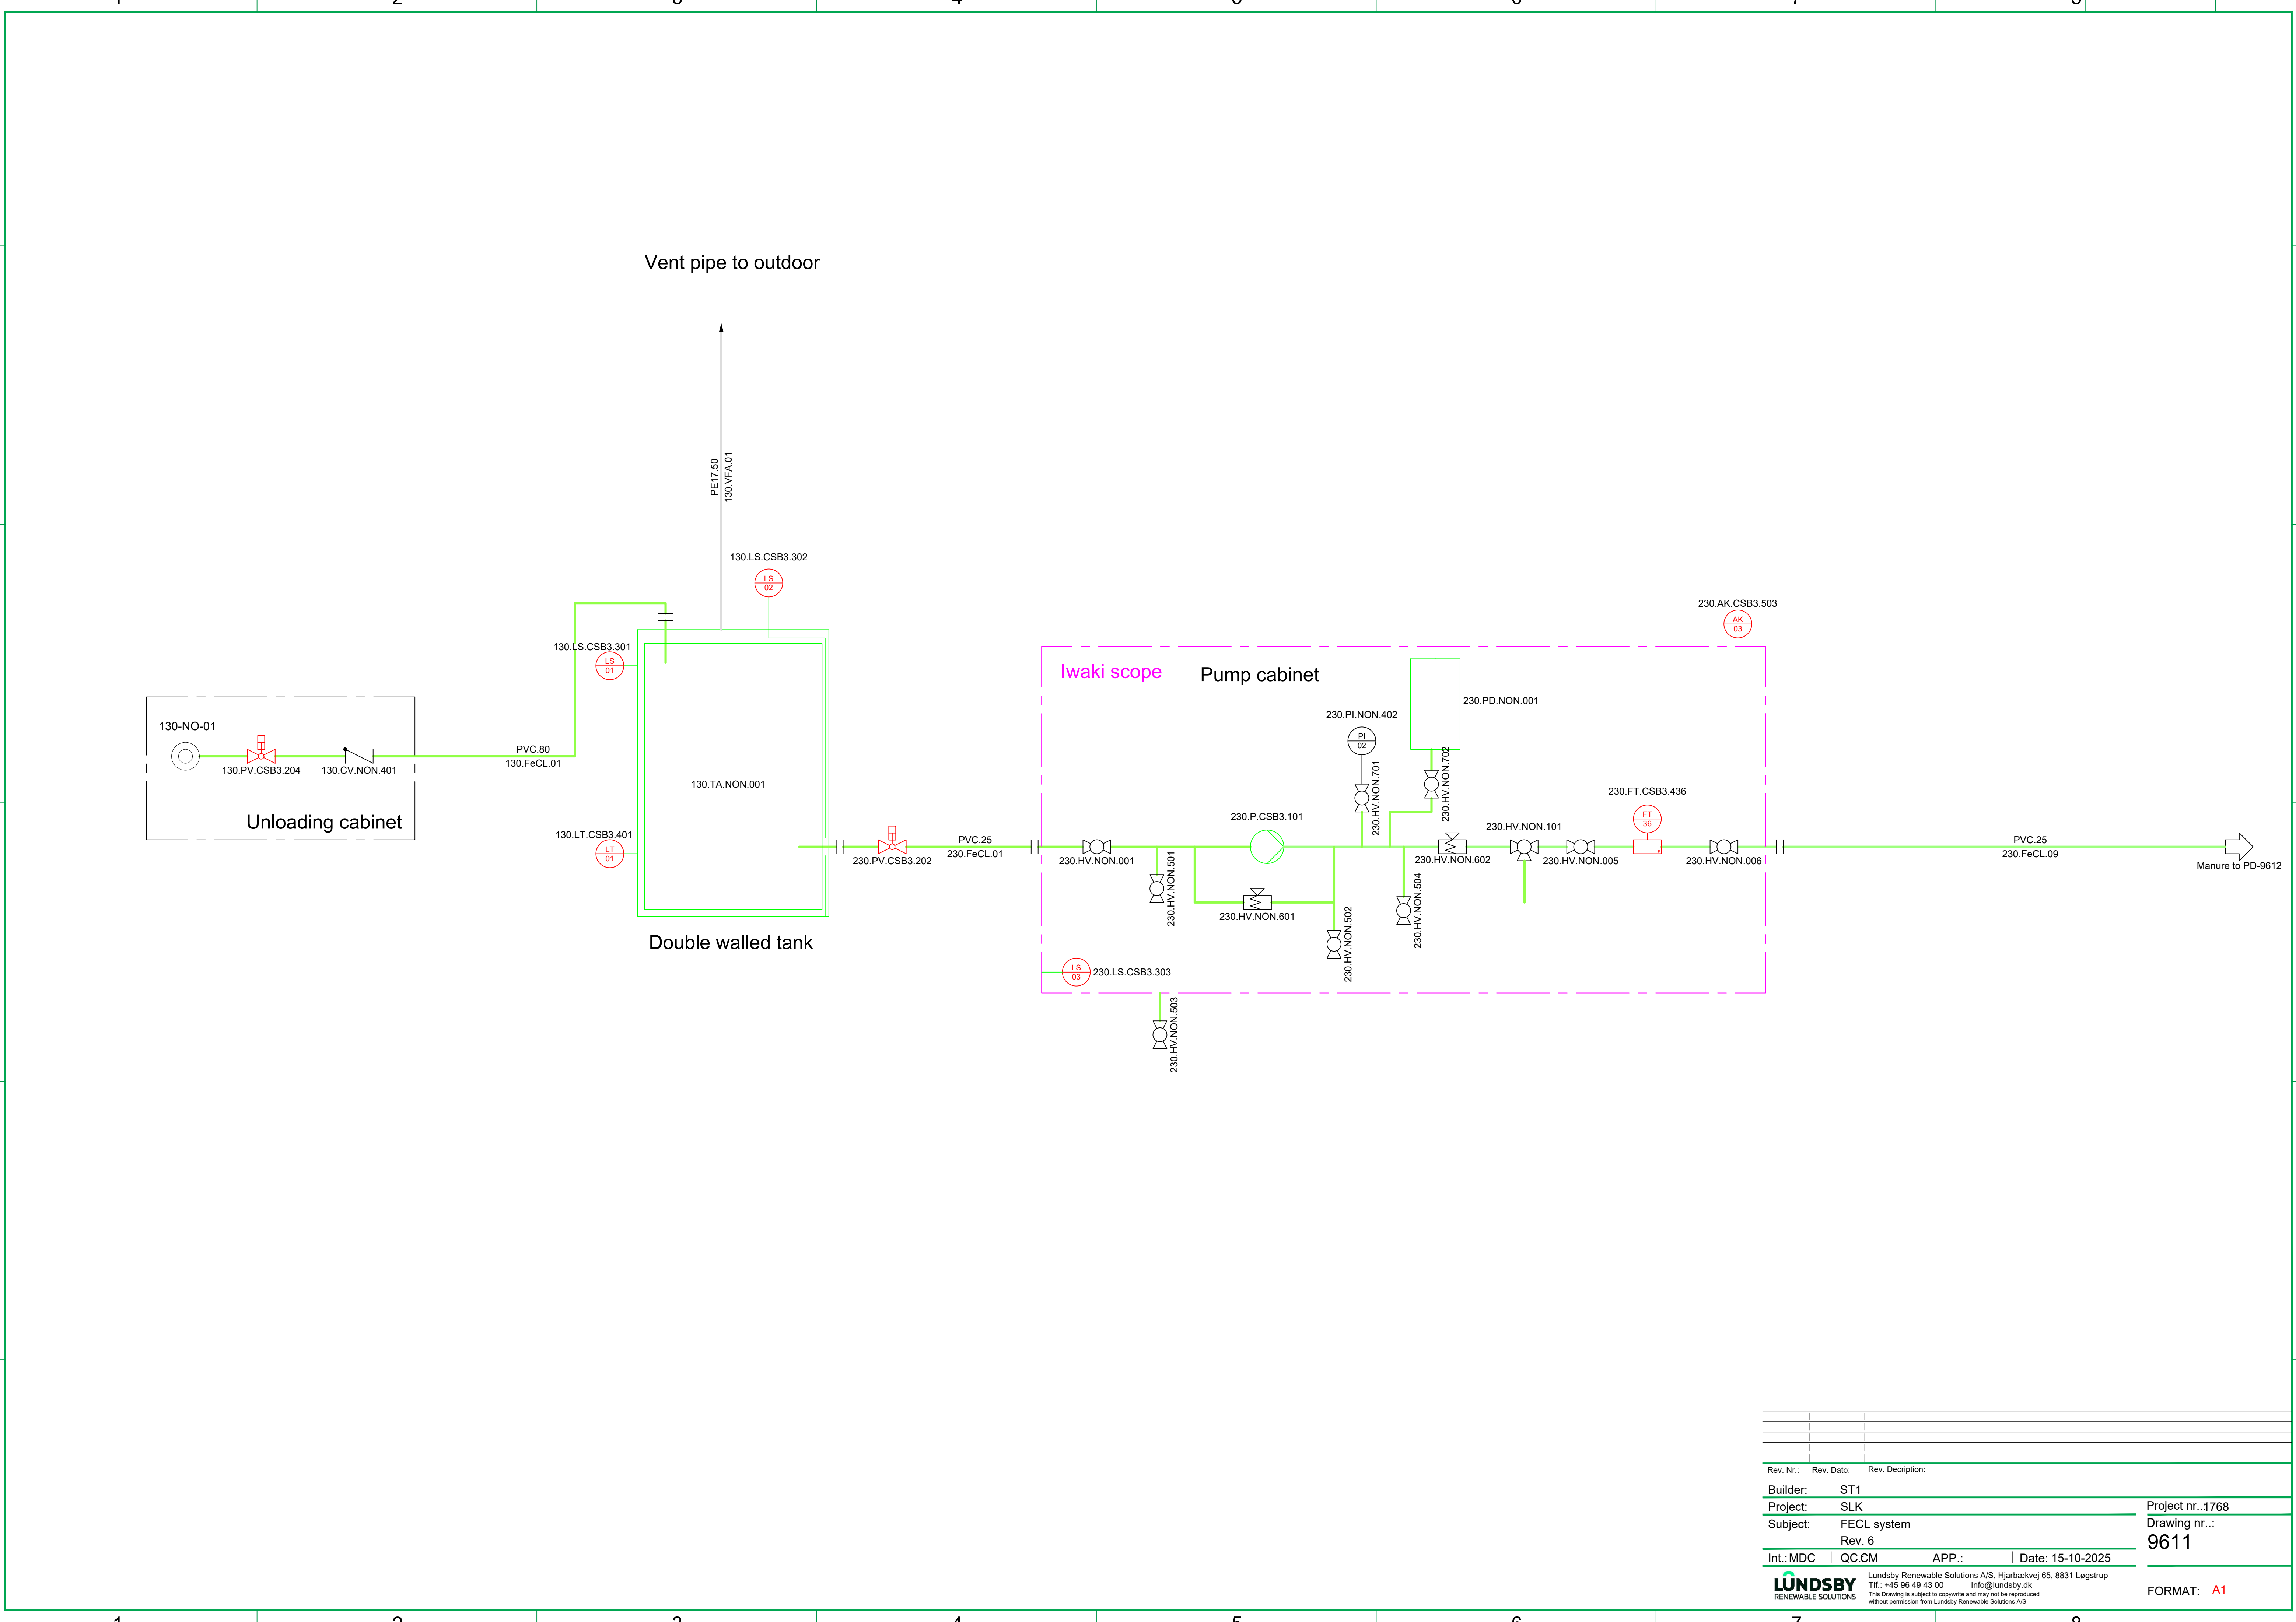


	</
--	--	----

Pumphouse 2

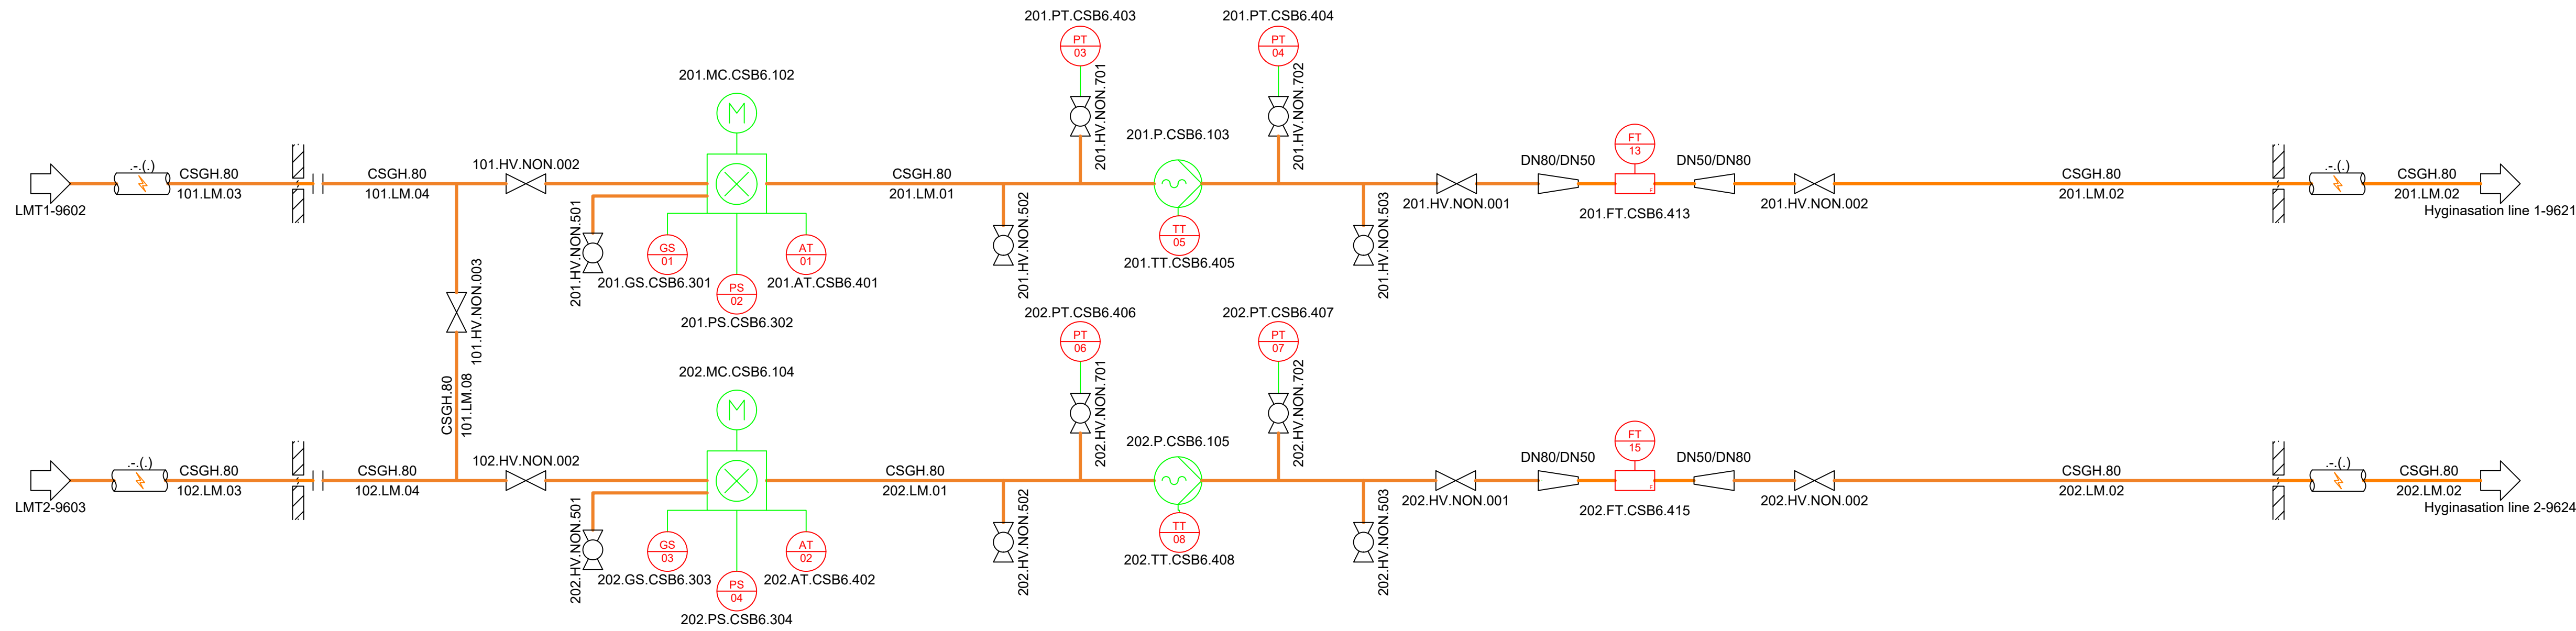


Tech
building


SB-building

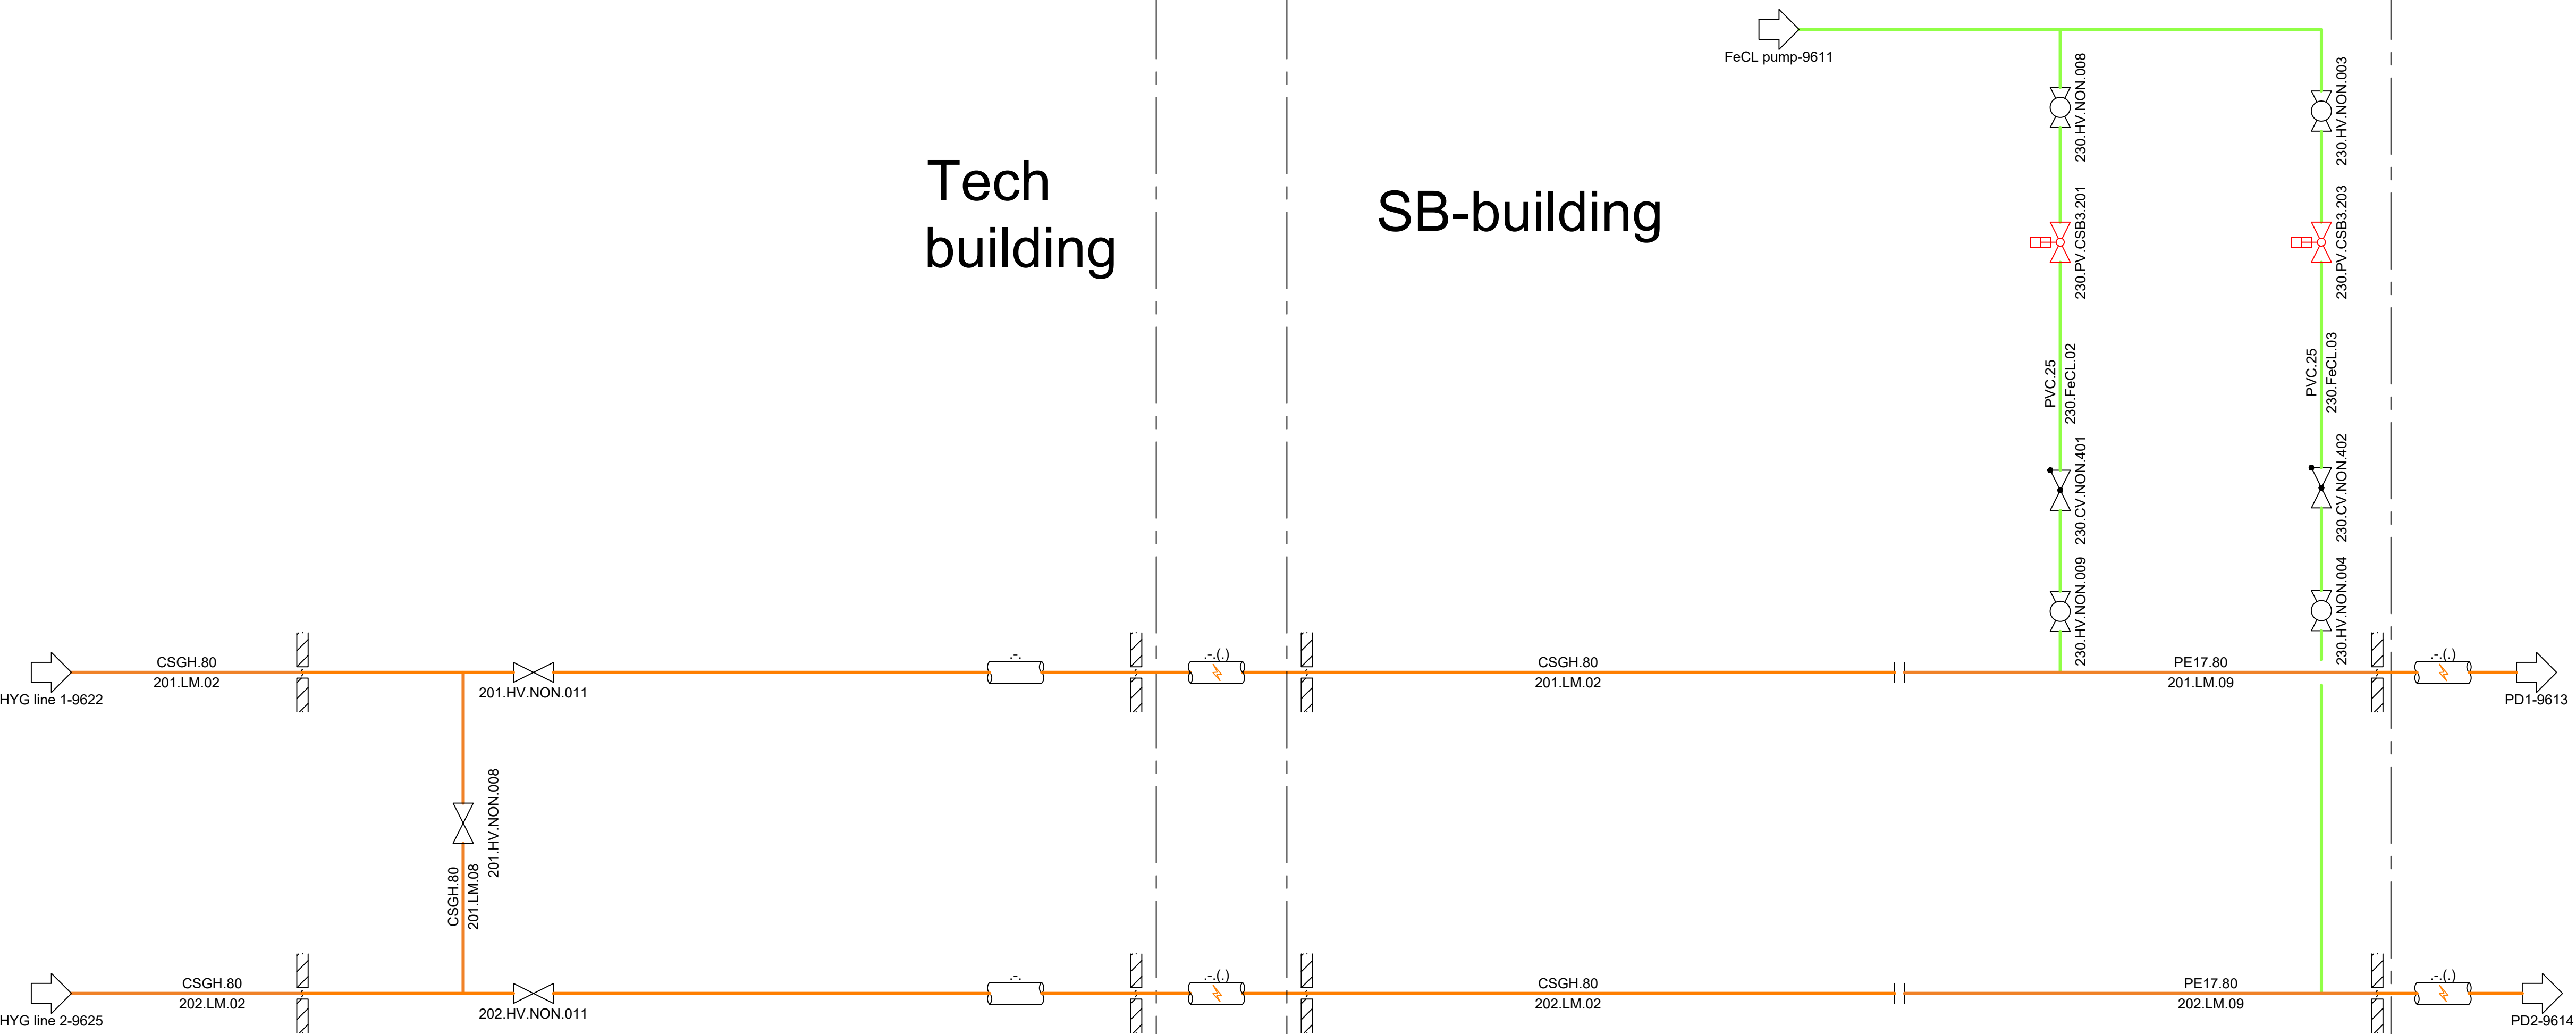


Rev. Nr.:	Rev. Dato:	Rev. Description:
Builder:	ST1	
Project:	SLK	
Subject:	Liquid manure pump	
Rev. 6		
Int.: MDC	QC.CM	APP.:
Date: 15-10-2025		
LUNDSBY RENEWABLE SOLUTIONS		
Lundsby Renewable Solutions A/S, Hjarbækvej 65, 8831 Løgstrup Tlf.: +45 96 49 43 00 info@lundsby.dk This Drawing is subject to copyright and may not be reproduced without permission from Lundsby Renewable Solutions A/S		
Project nr.: 1768 Drawing nr.: 9612		FORMAT: A1

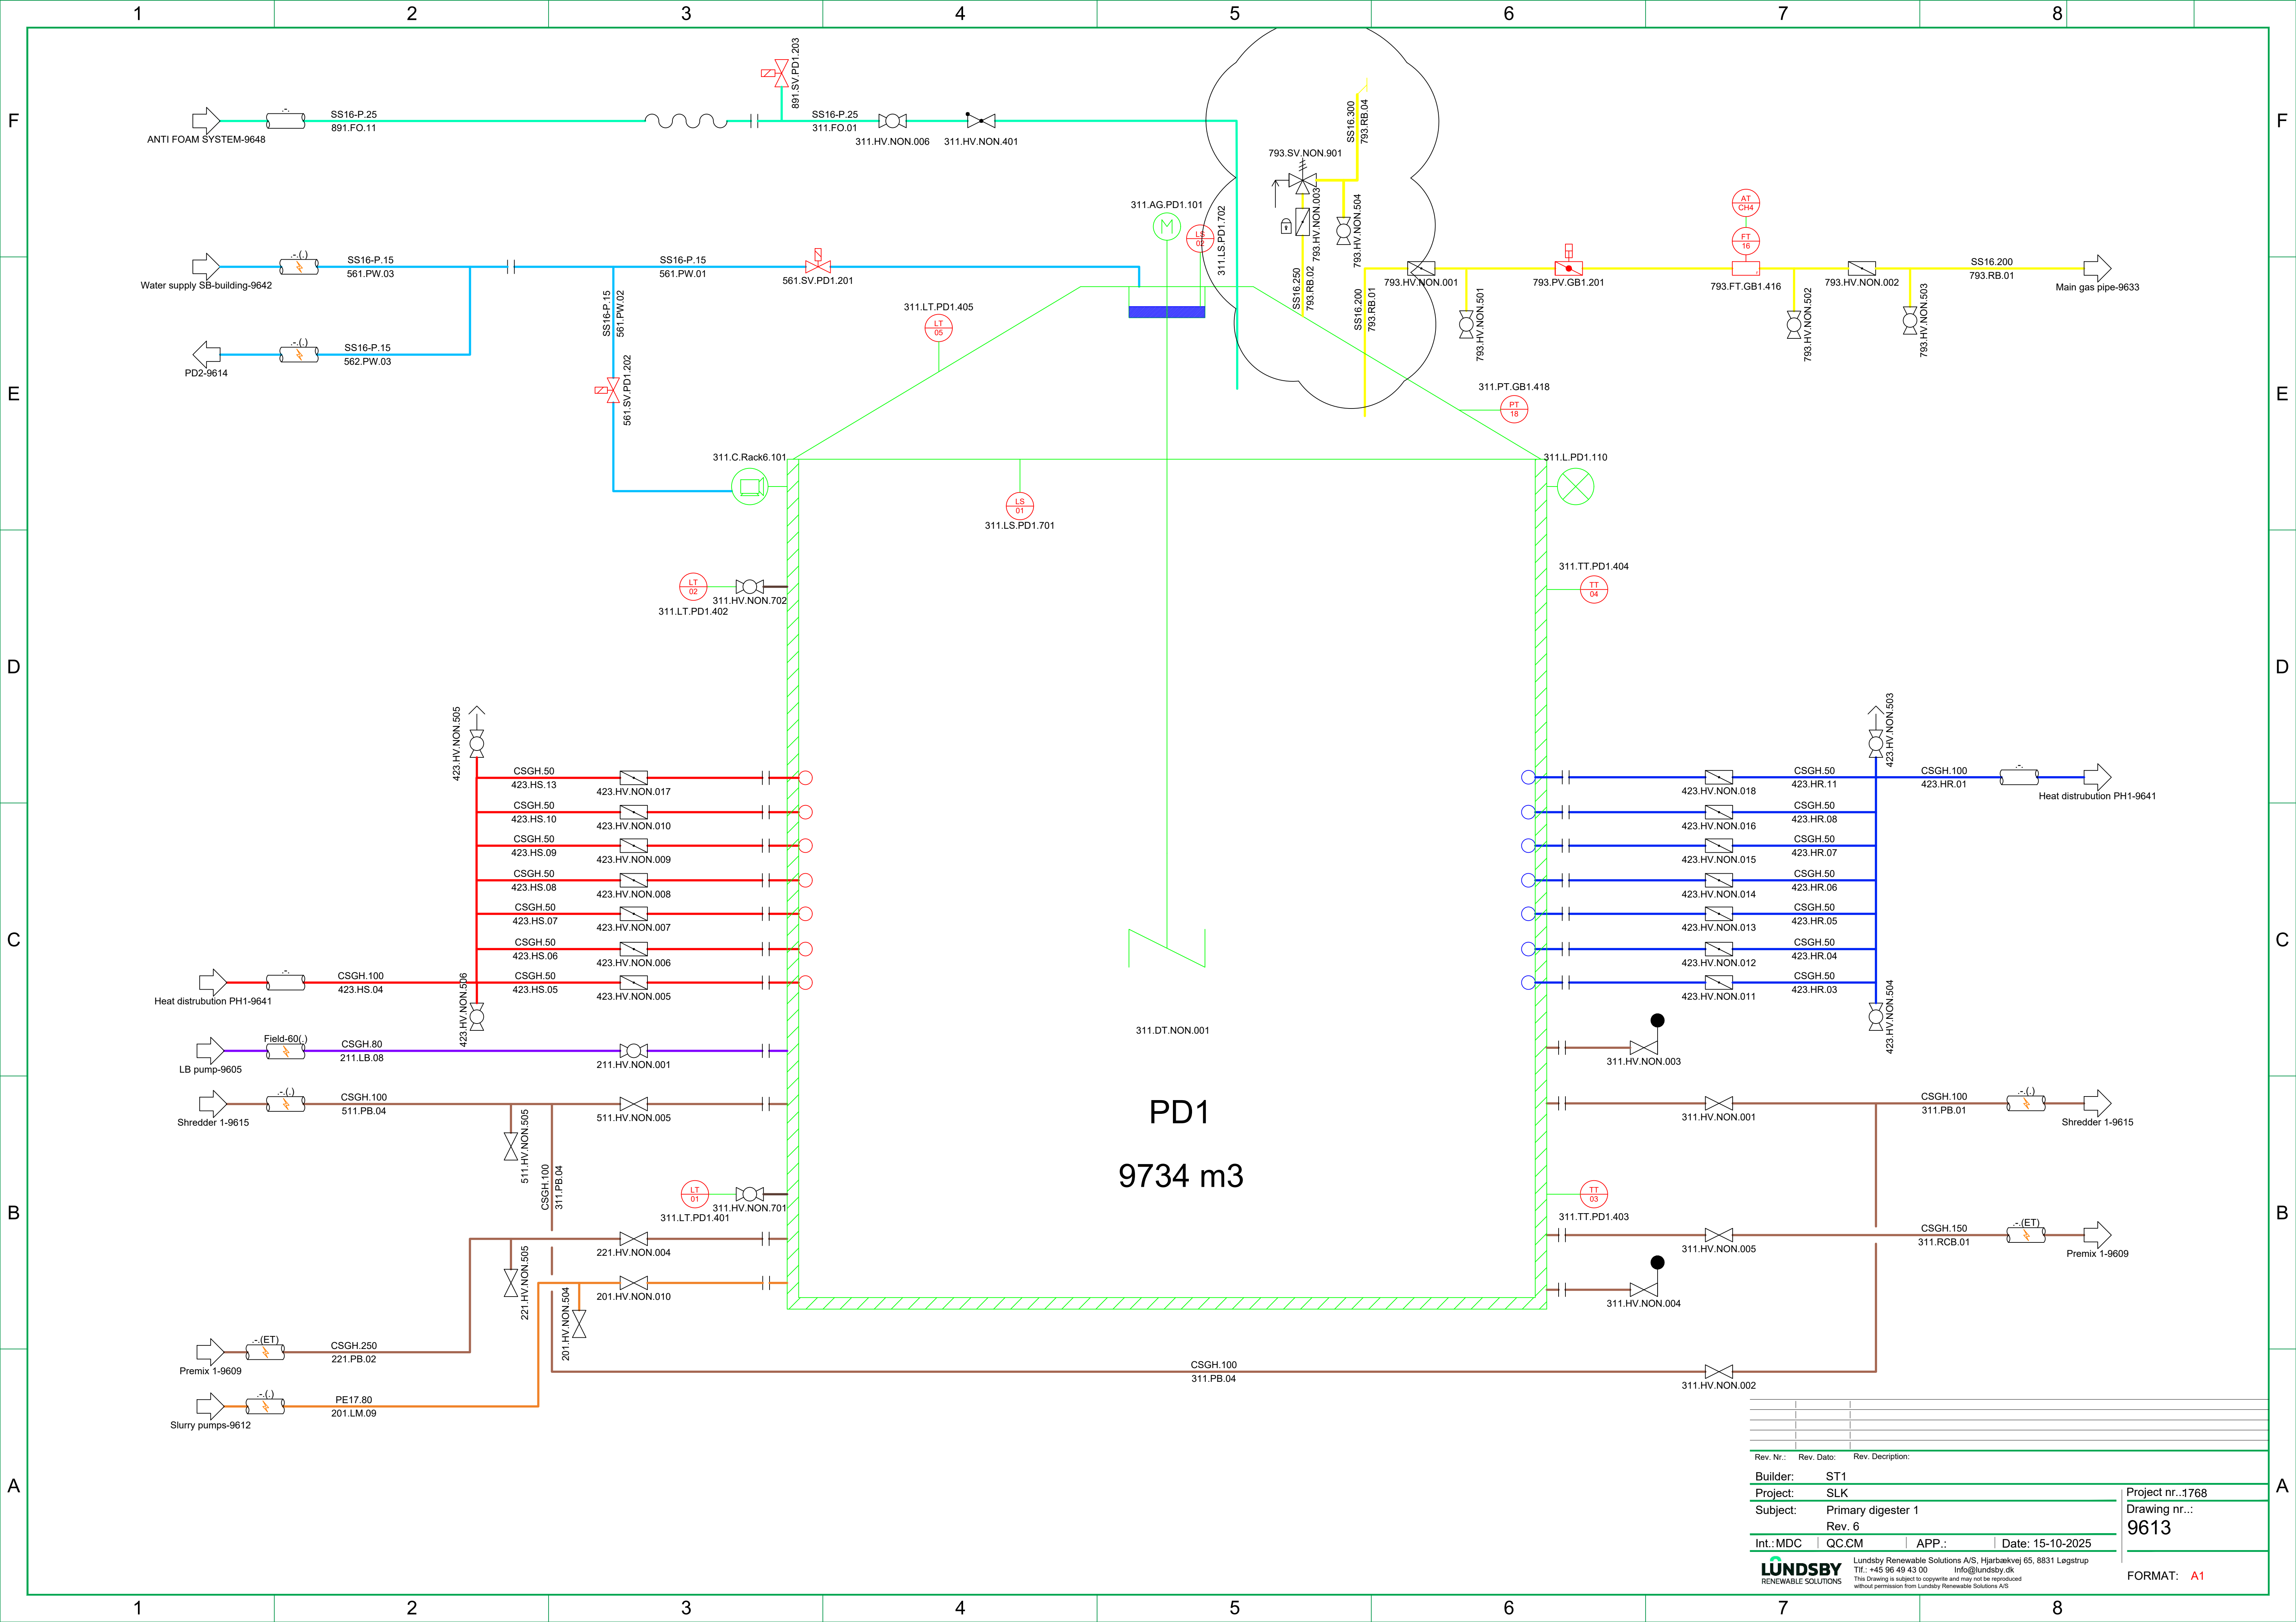


Rev. Nr.:	Rev. Dato:	Rev. Description:
Builder:	ST1	
Project:	SLK	
Subject:	Primary digester 1	
Rev. 6		
Int.:MDC	QC:CM	APP.:
Date: 15-10-2025		
LUNDSBY RENEWABLE SOLUTIONS		
Lundsby Renewable Solutions A/S, Hjarbækvej 65, 8831 Legstrup Tlf.: +45 96 49 43 00 Info@lundsby.dk This drawing is subject to copyright and may not be reproduced without permission from Lundsby Renewable Solutions A/S		
Project nr.:1768 Drawing nr.: 9613		FORMAT: A1

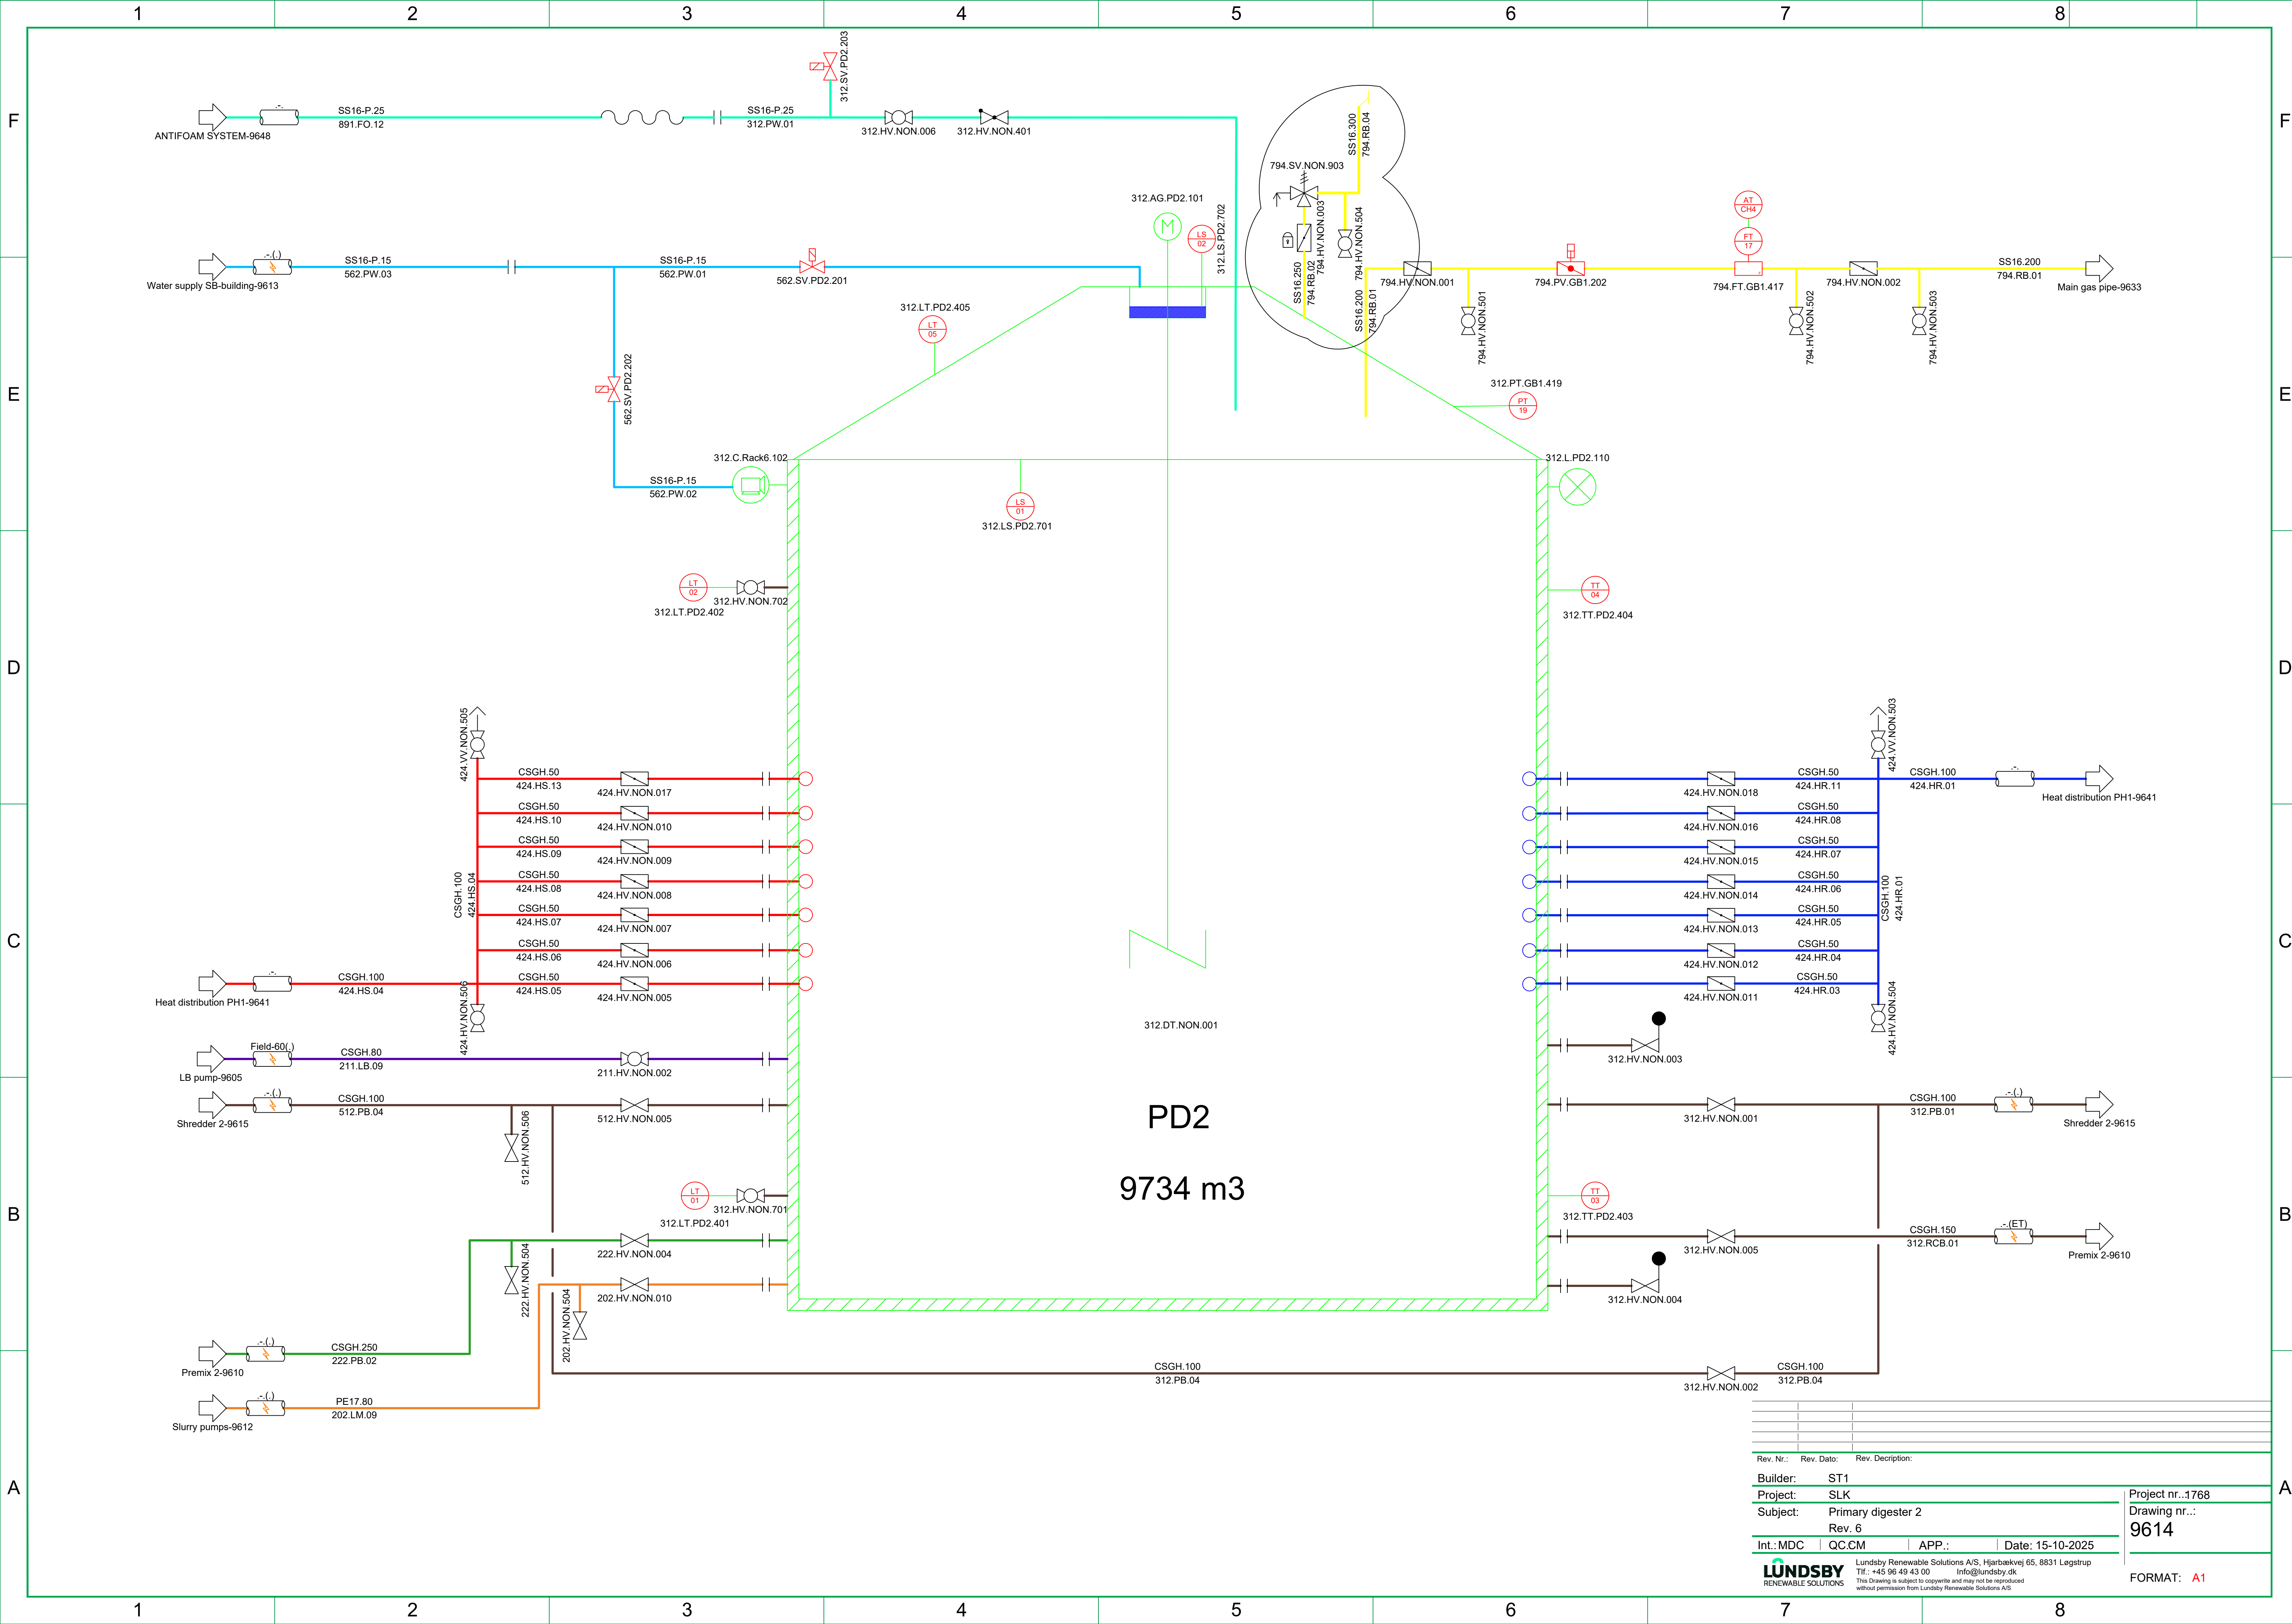


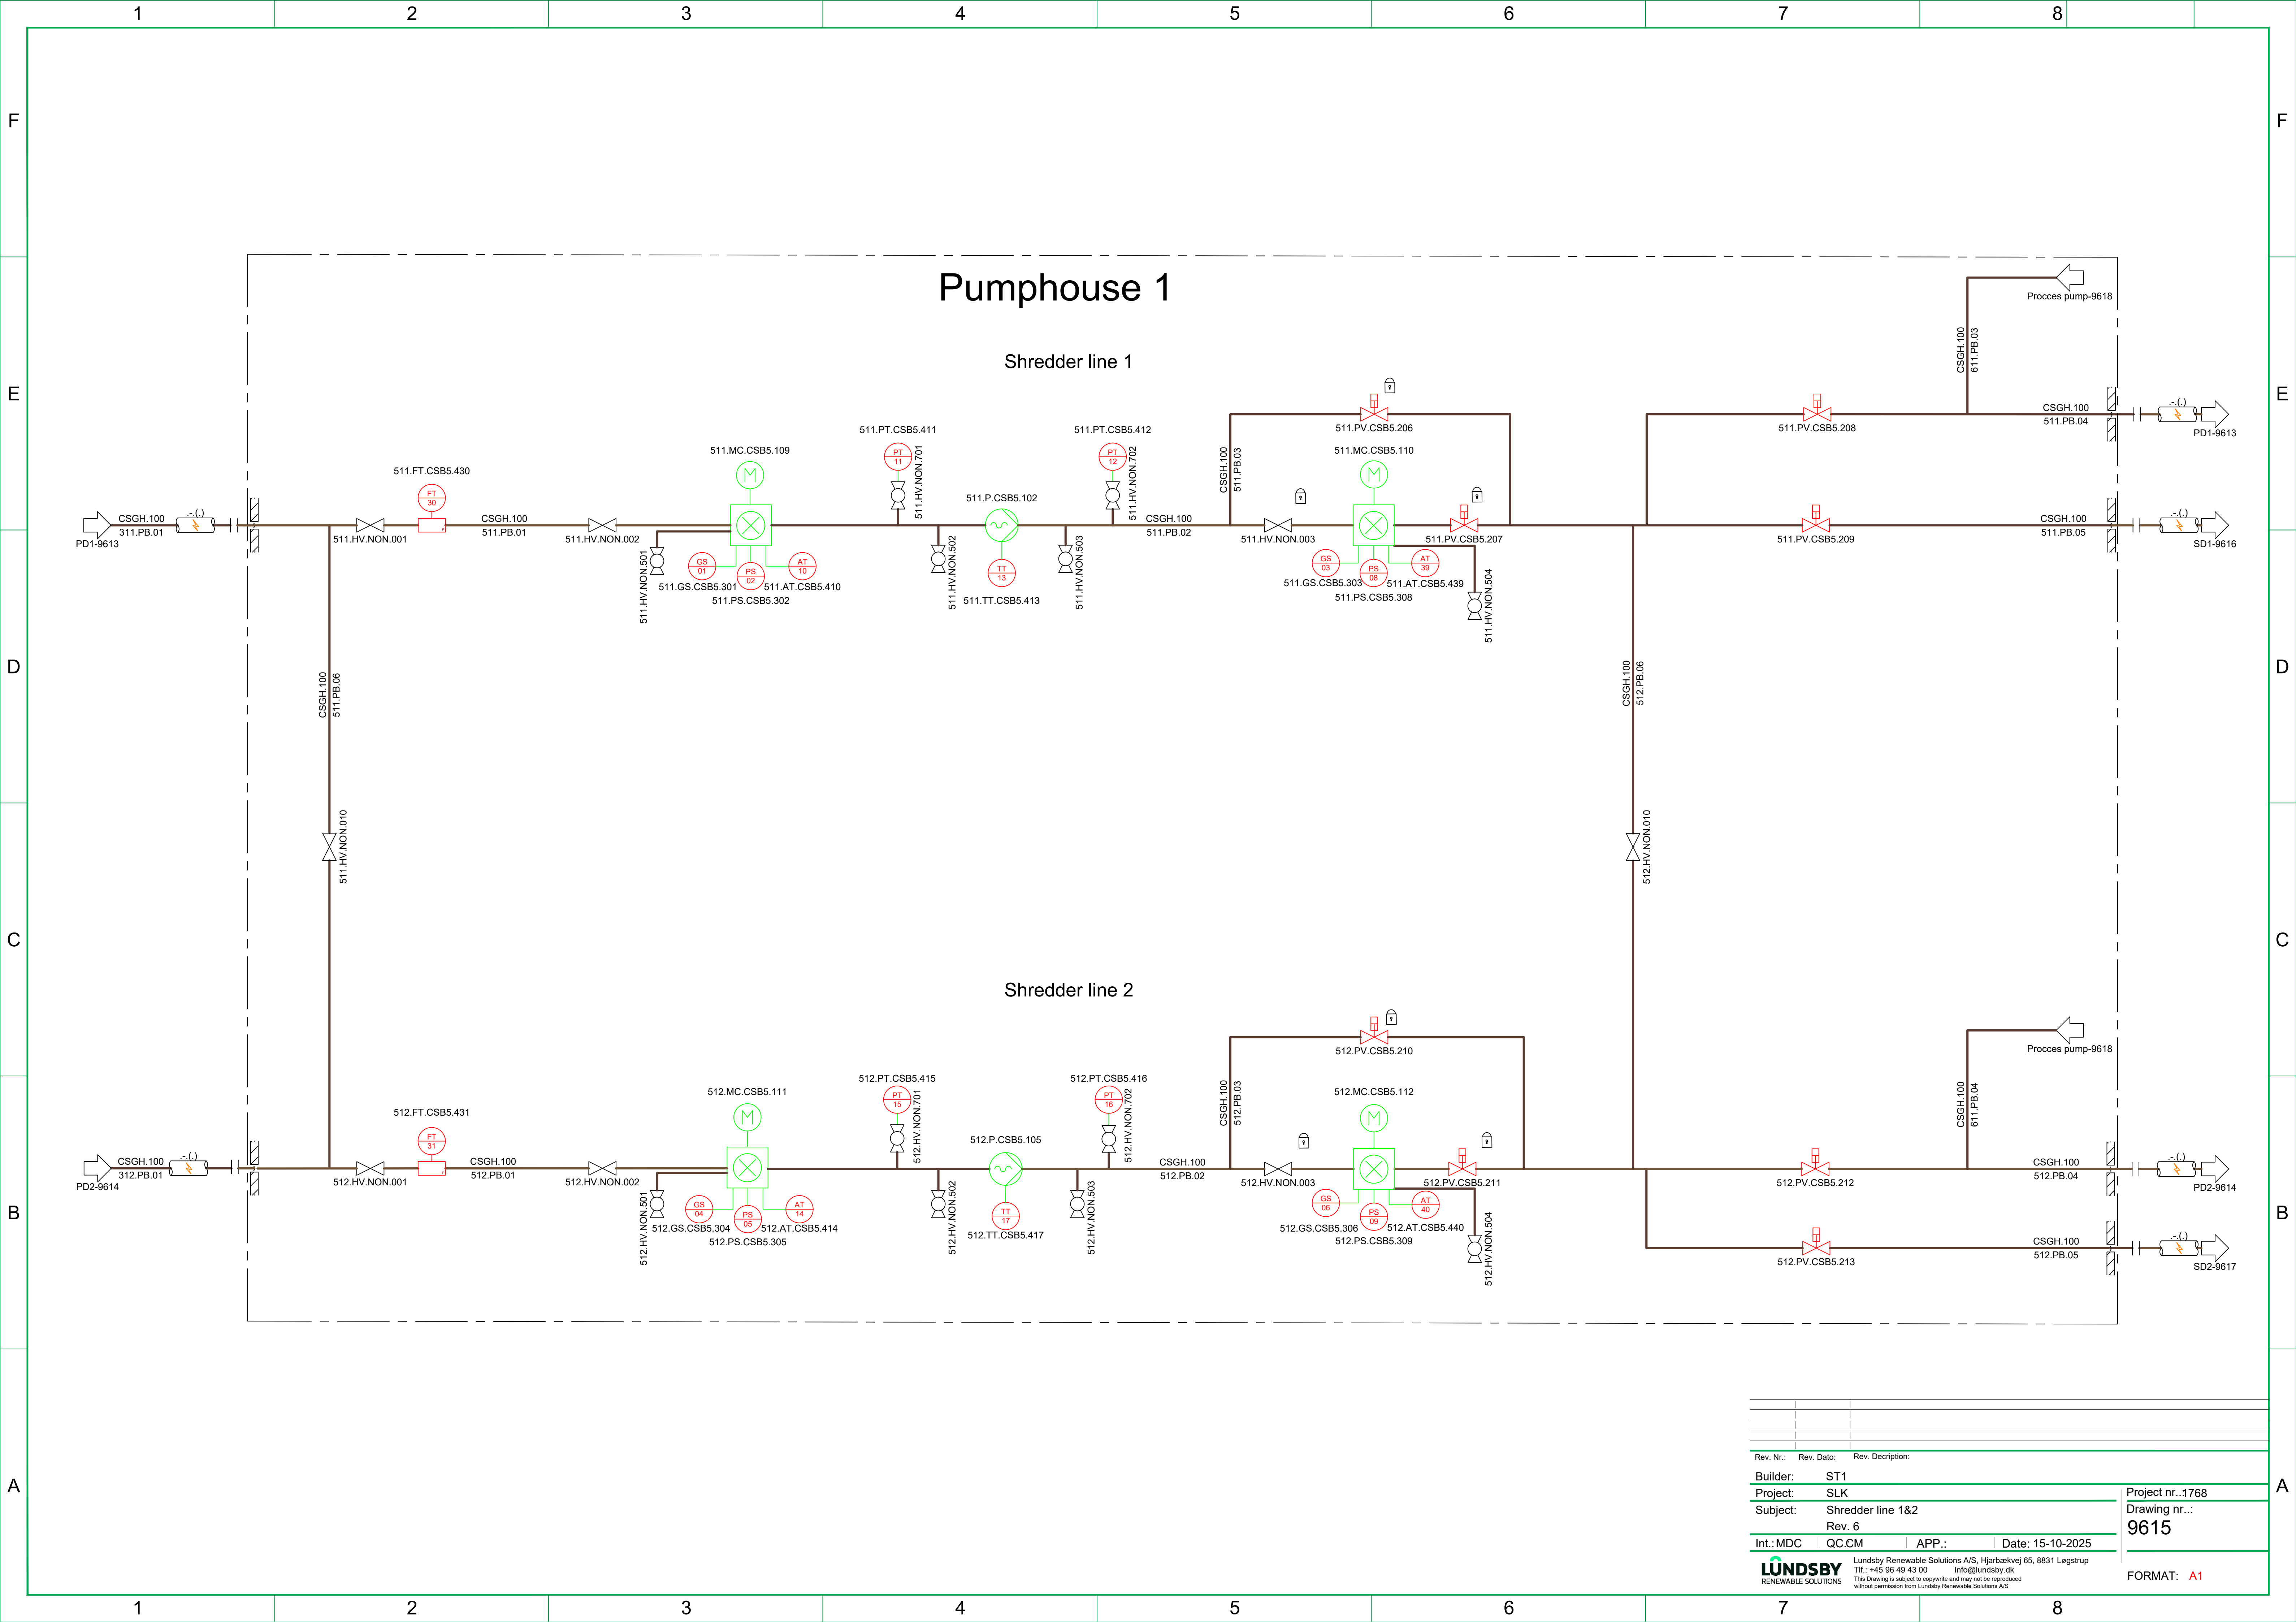


Rev. Nr.:	Rev. Dato:	Rev. Description:
Builder:	ST1	
Project:	SLK	
Subject:	Shredder line 1&2	
	Rev. 6	
Int.:MDC	QC:CM	APP.:Date: 15-10-2025
LUNDSBY RENEWABLE SOLUTIONS		
Lundsby Renewable Solutions A/S, Hjarbækvej 65, 8831 Løgstrup Tlf.: +45 96 49 43 00 Info@lundsby.dk This Drawing is subject to copyright and may not be reproduced without permission from Lundsby Renewable Solutions A/S		
Project nr.:1768 Drawing nr.: 9615		FORMAT: A1

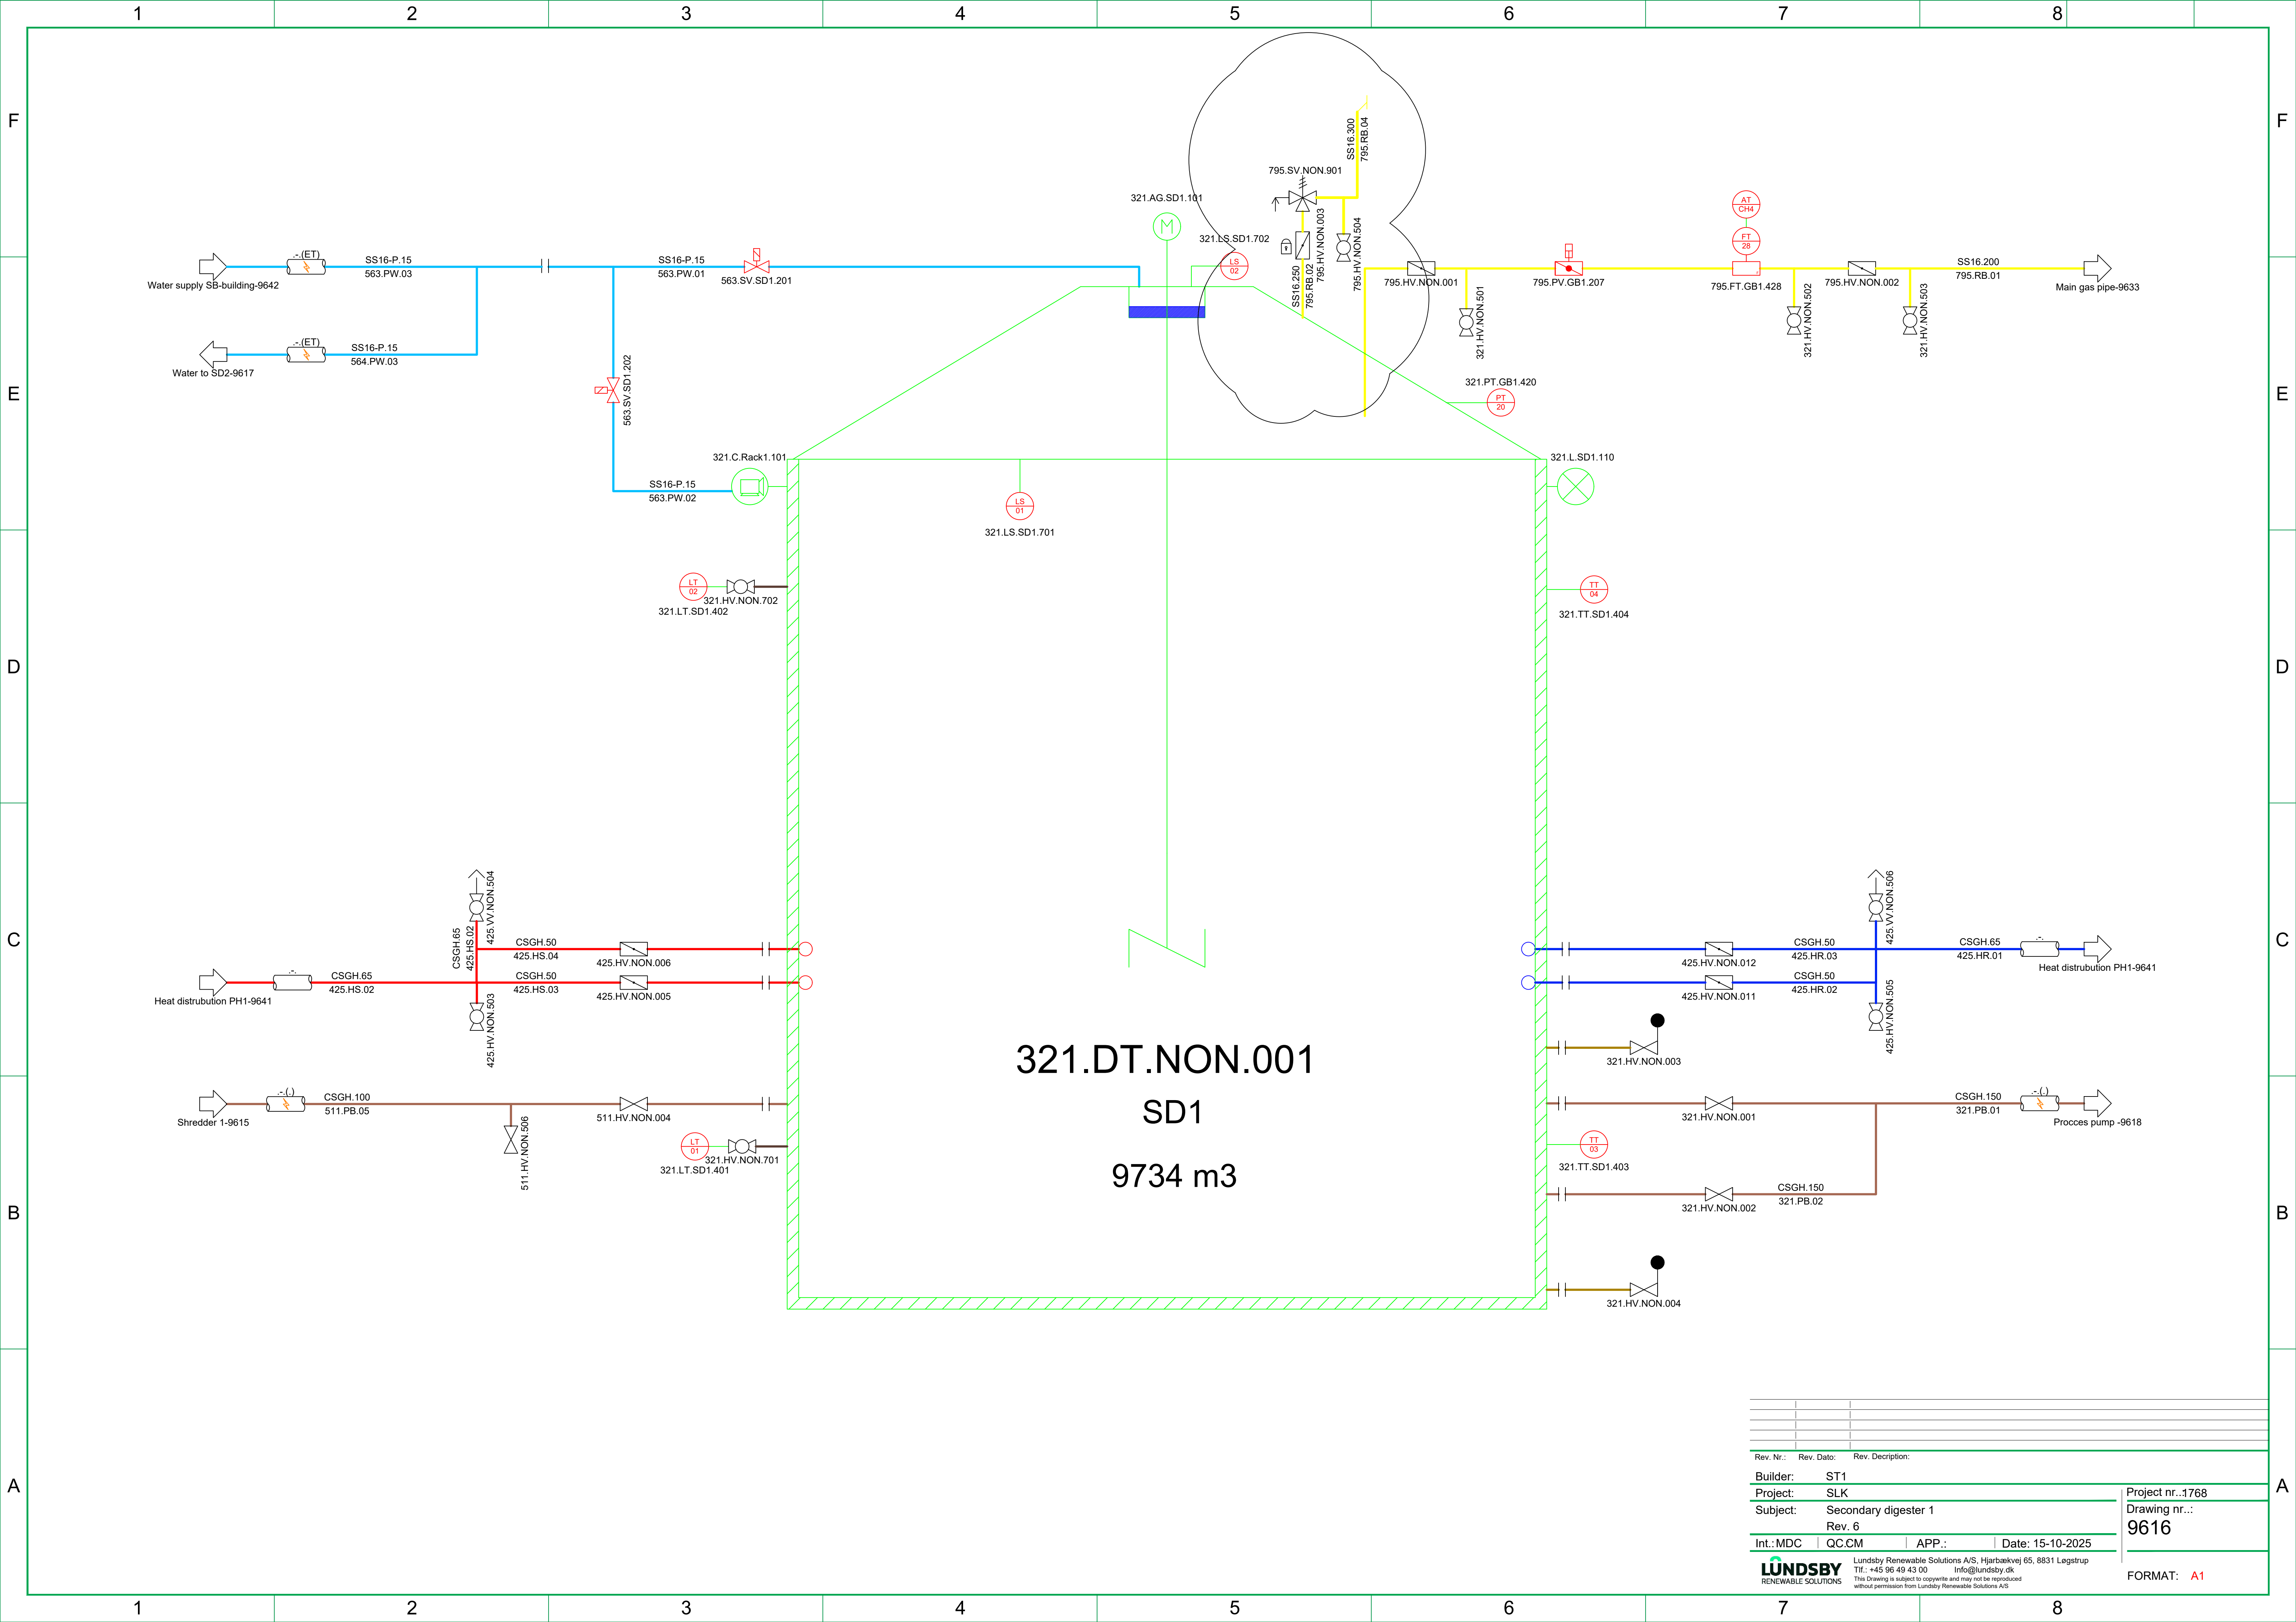

Rev. Nr.:	Rev. Dato:	Rev. Description:	
Builder:	ST1		
Project:	SLK		
Subject:	Secondary digester 1		
Rev. 6			
Int.:MDC	QC.CM	APP.:	Date: 15-10-2025
LUNDSBY RENEWABLE SOLUTIONS			Lundsby Renewable Solutions A/S, Hjarbækvej 65, 8831 Løgstrup Tlf.: +45 96 49 43 00 Info@lundsby.dk This Drawing is subject to copyright and may not be reproduced without permission from Lundsby Renewable Solutions A/S
Project nr.:1768 Drawing nr.: 9616			FORMAT: A1

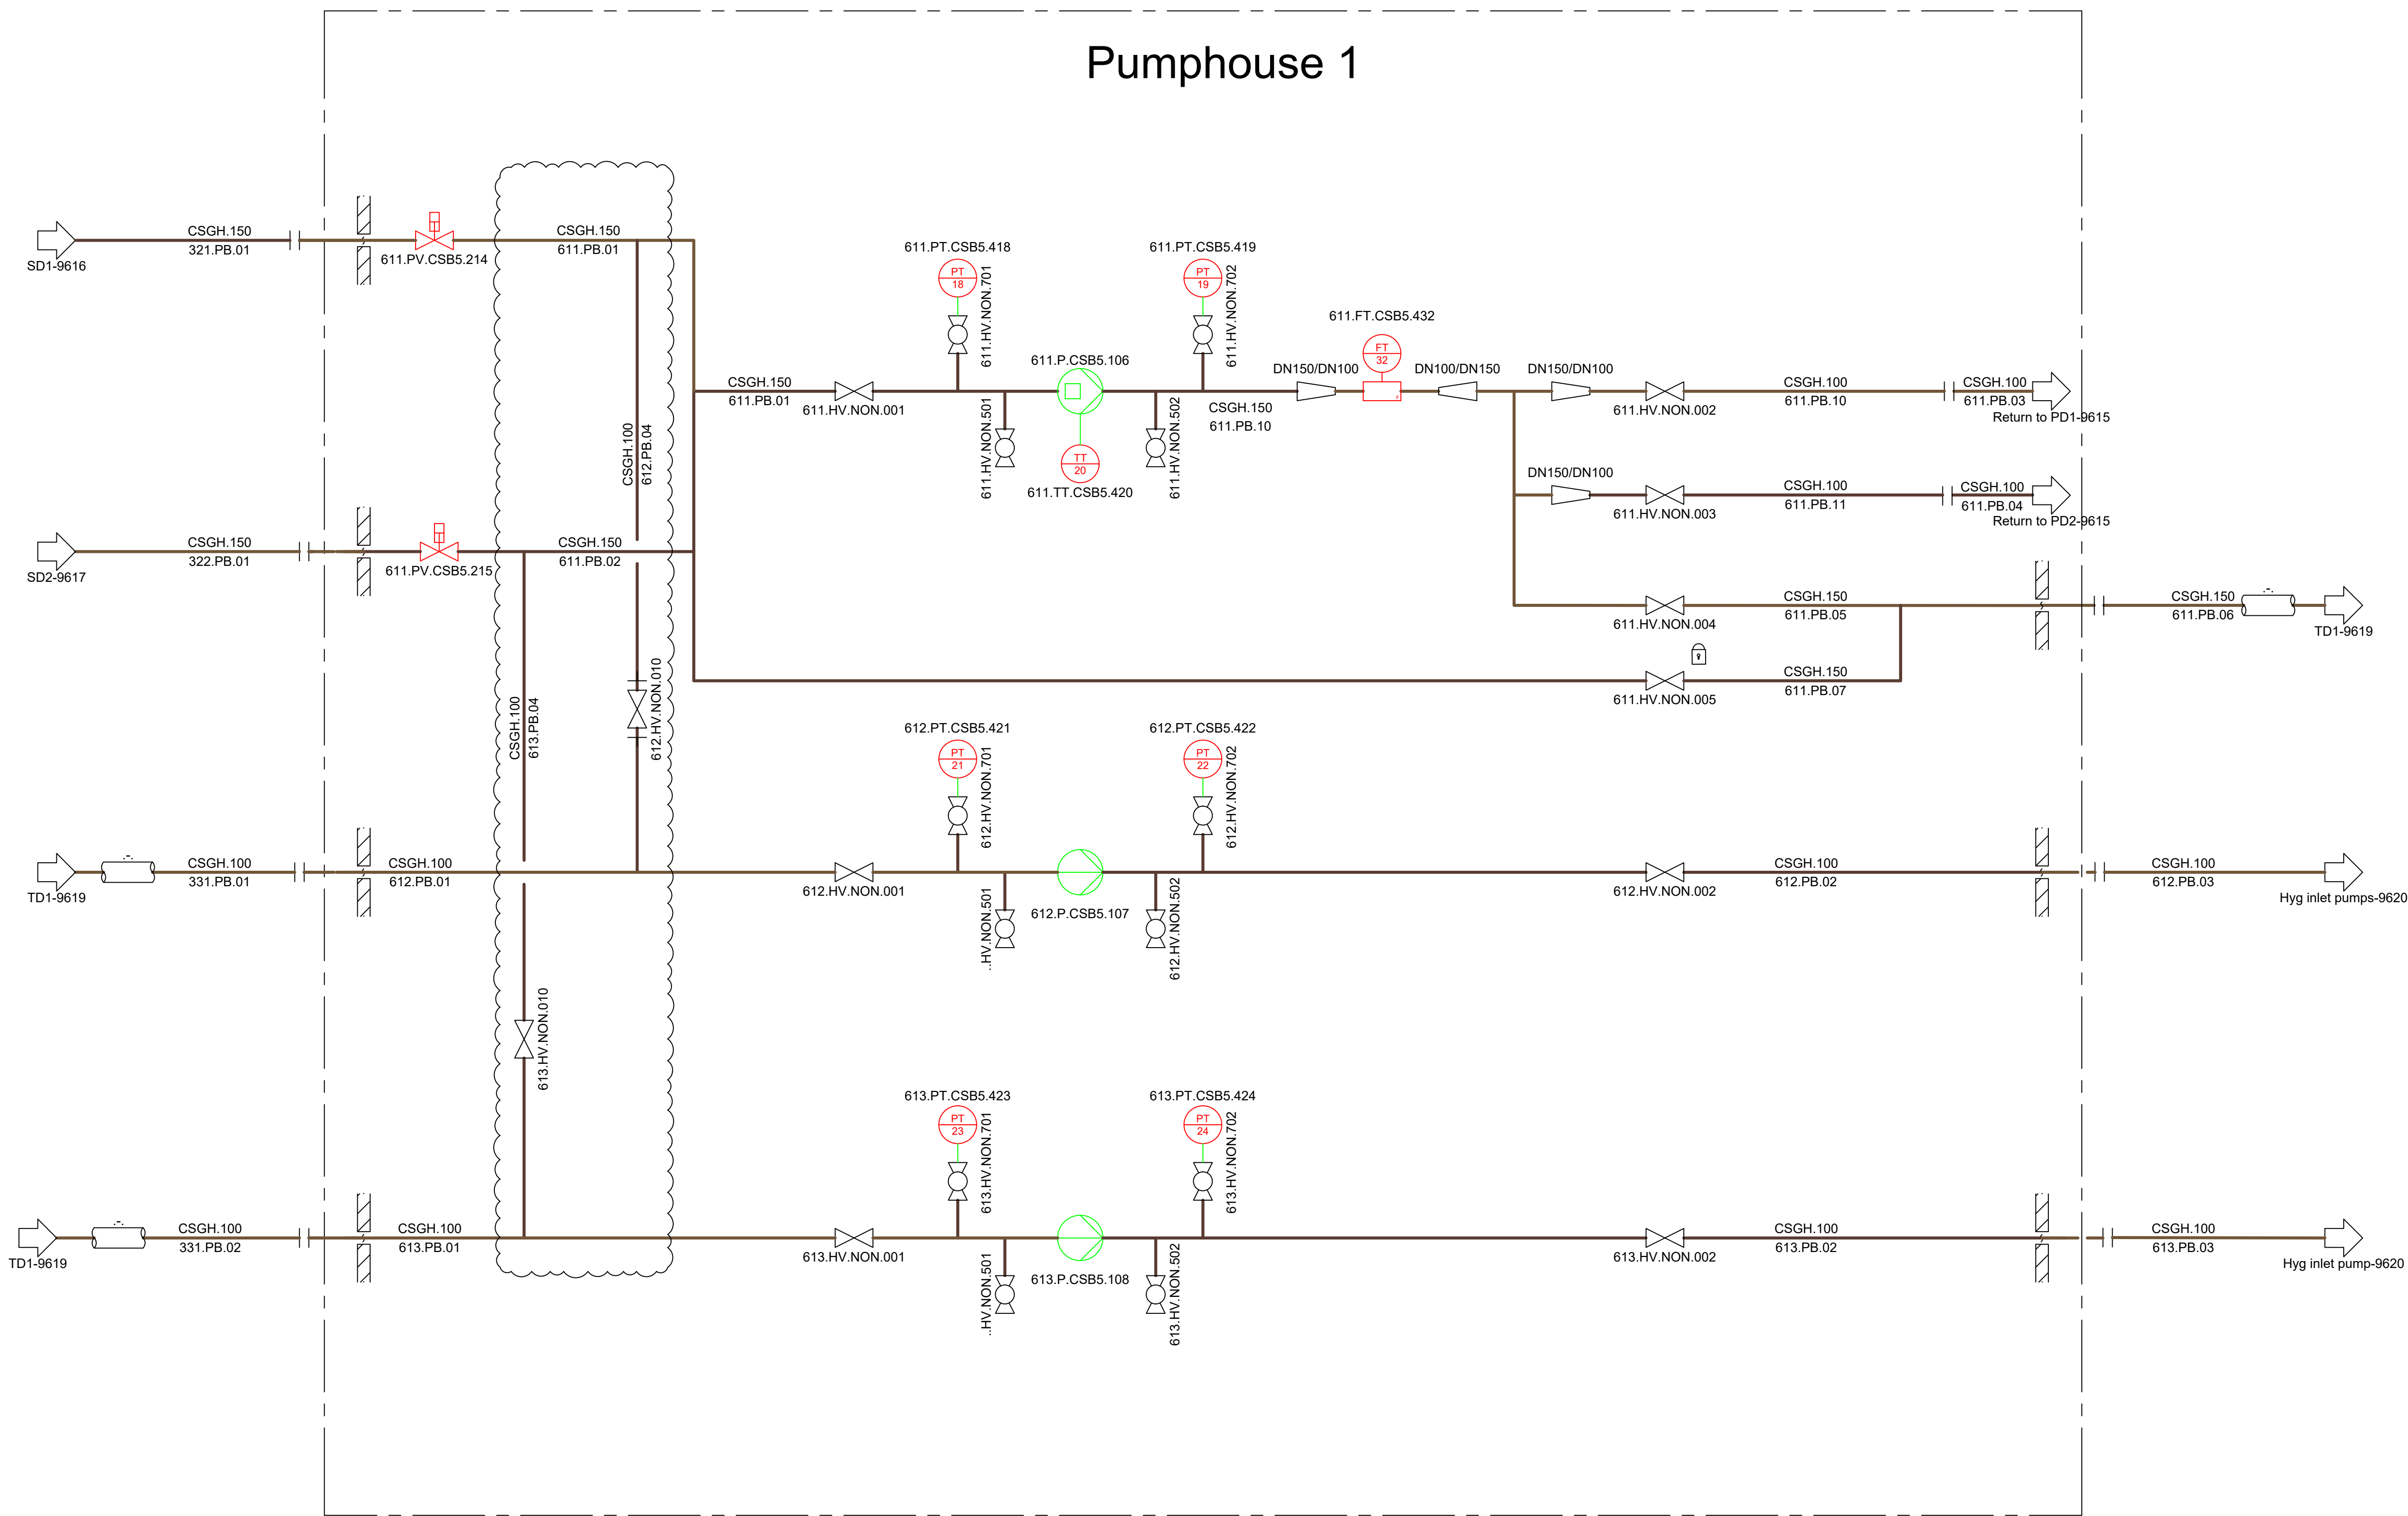


Rev. Nr.:		Rev. Dato:	Rev. Description:
Builder:		ST1	
Project:		SLK	
Subject:		Procces pumps	
		Rev. 6	
Int.: MDC		QC.CM	APP.: Date: 15-10-2025
LUNDSBY RENEWABLE SOLUTIONS		Lundsby Renewable Solutions A/S, Hjarbækvej 65, 8831 Løgstrup Tlf.: +45 96 49 43 00 Info@lundsby.dk This Drawing is subject to copyright and may not be reproduced without permission from Lundsby Renewable Solutions A/S	
Project nr.: 1768		Drawing nr.: 9618	
FORMAT:		A1	

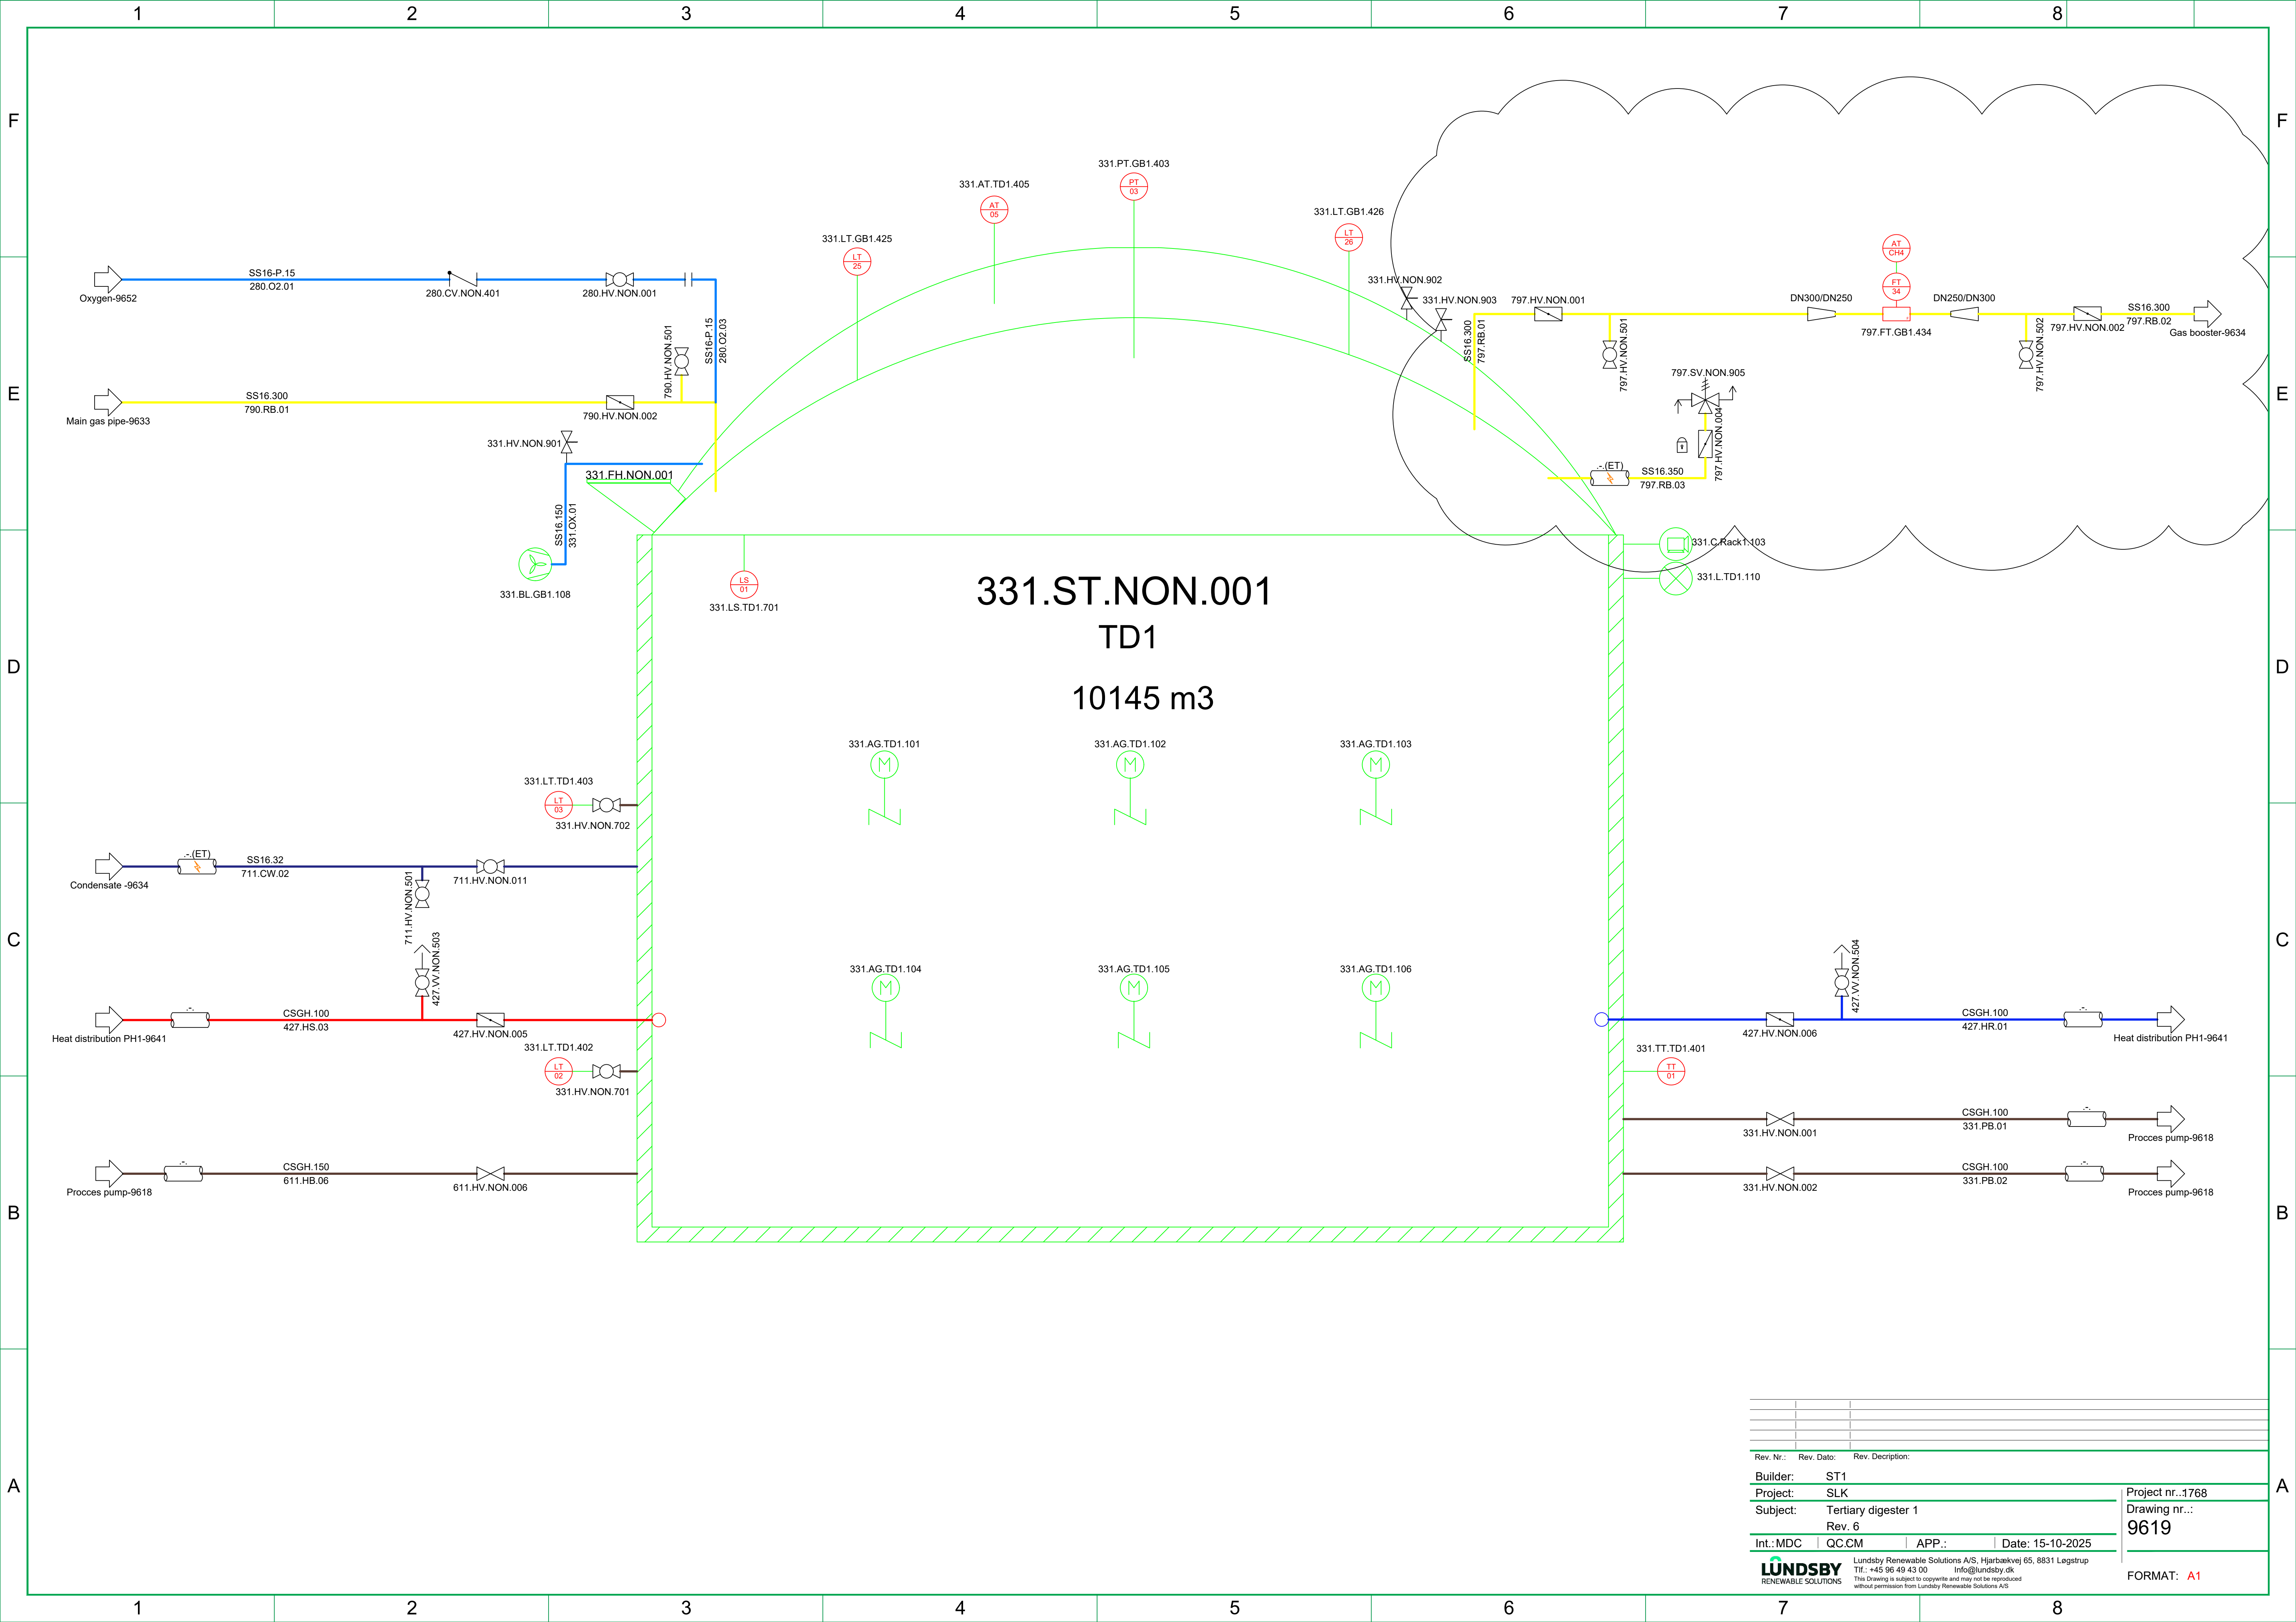


Tech Building


Inlet pumps

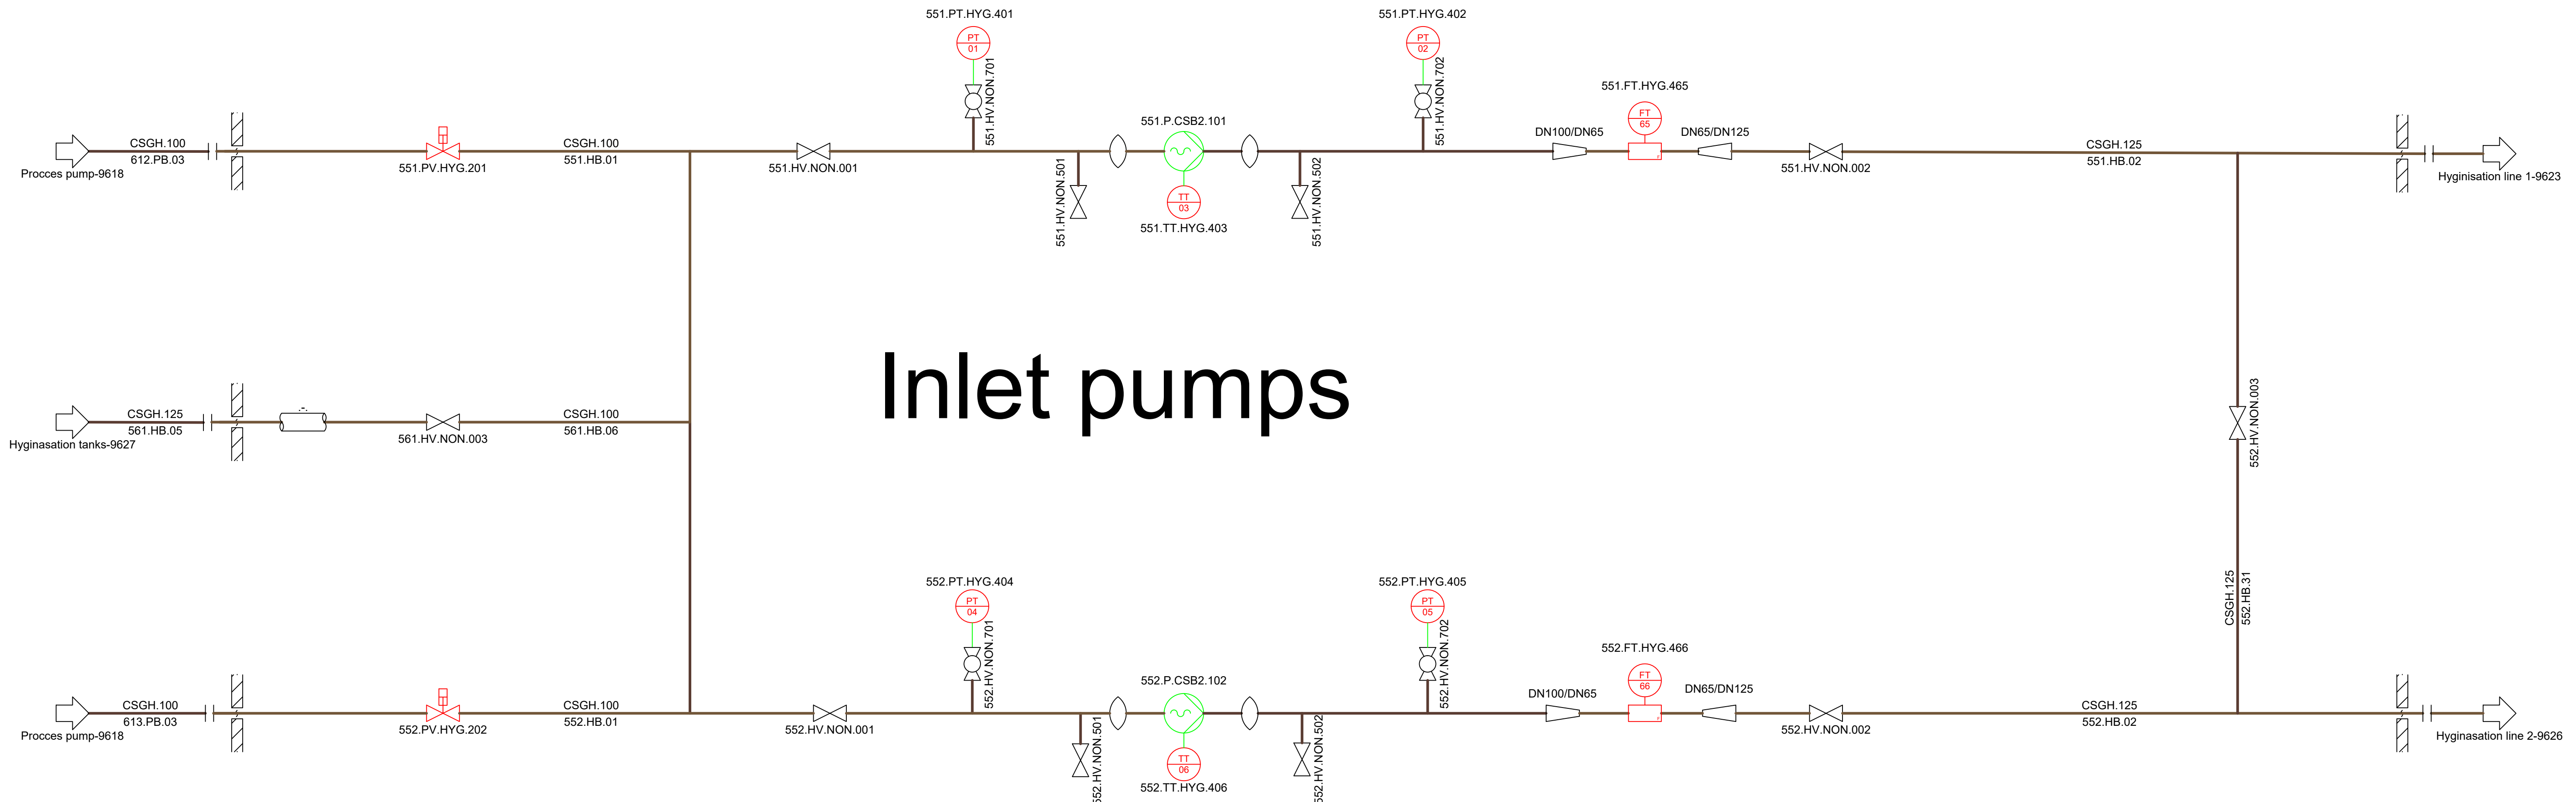


Rev. Nr.:	Rev. Dato:	Rev. Description:			
Builder:	ST1				
Project:	SLK				
Subject:	Hyginisation inlet pumps				
	Rev. 6				
Int.: MDC	QC:CM	APP.:	Date: 15-10-2025		
		Lundsby Renewable Solutions A/S, Hjarbækvej 65, 8831 Løgstrup Tlf.: +45 96 49 43 00 Info@lundsby.dk This Drawing is subject to copyright and may not be reproduced without permission from Lundsby Renewable Solutions A/S			
		Project nr.:1768		Drawing nr.: 9620	
		FORMAT: A1			

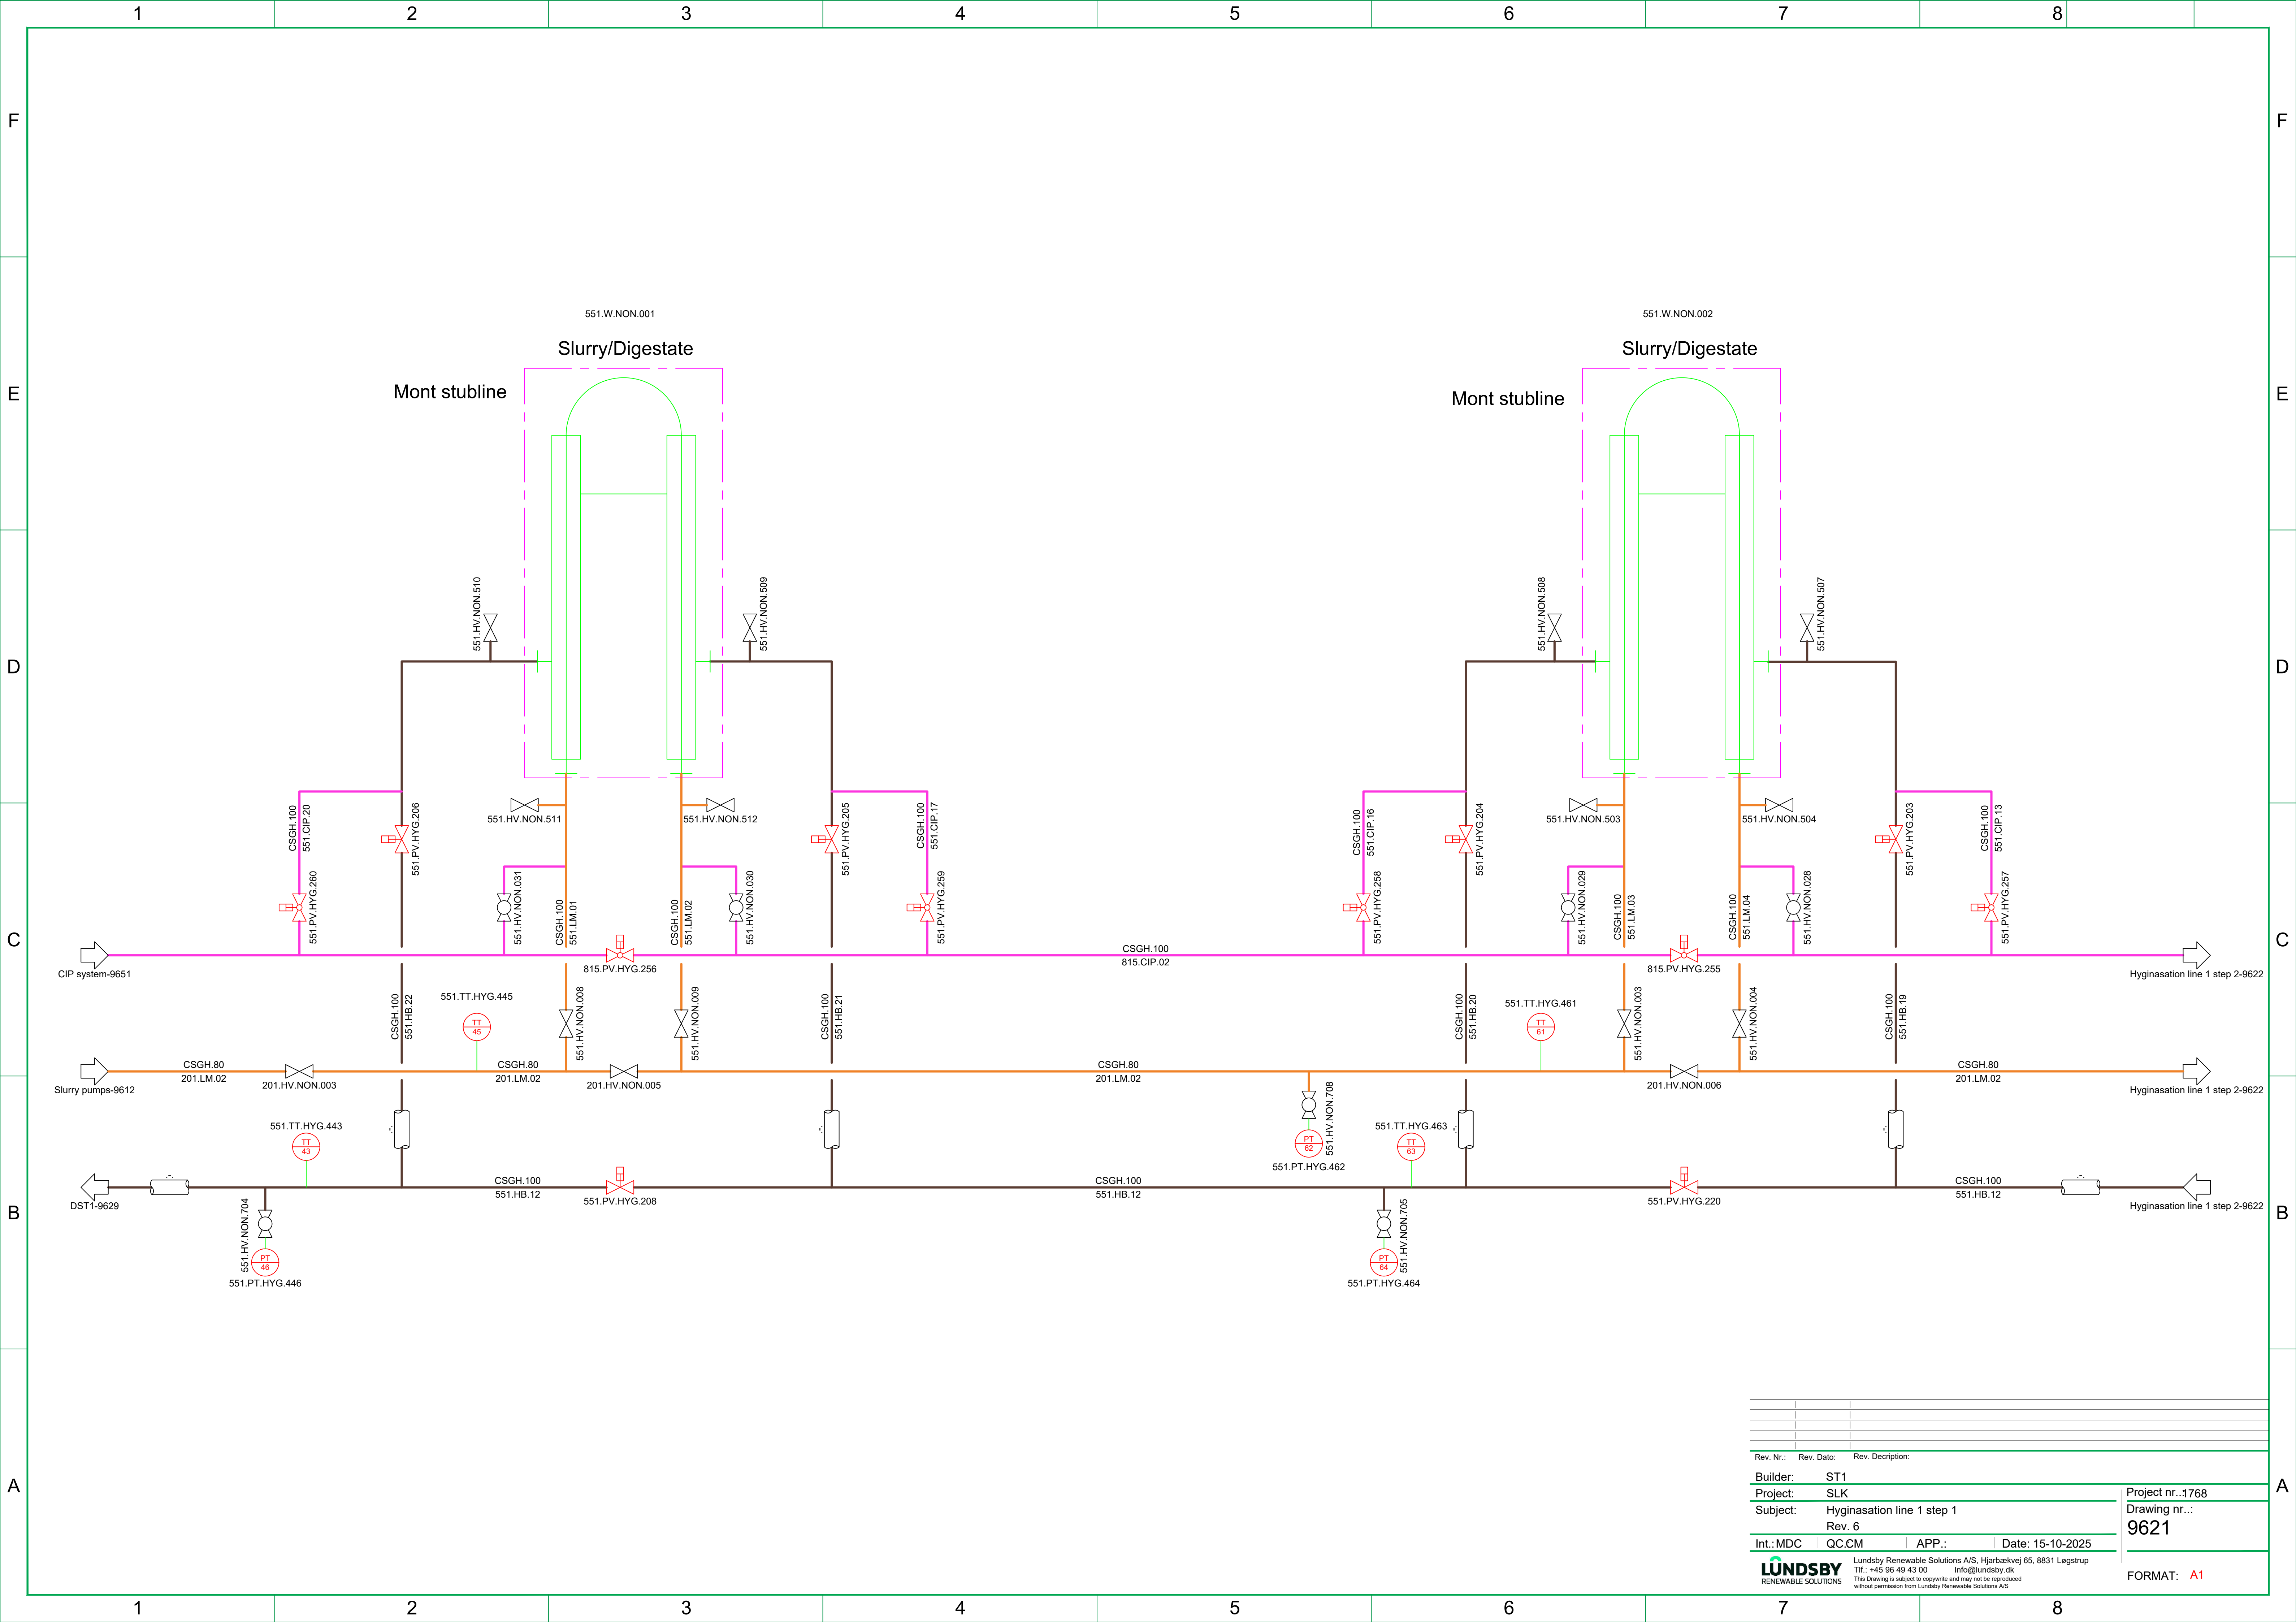


Rev. Nr.:	Rev. Dato:	Rev. Description:
Builder:	ST1	
Project:	SLK	
Subject:	Hyginasation line 1 step 1	
Rev. 6		
Int.: MDC	QC.CM	APP.:
Date: 15-10-2025		
LUNDSBY RENEWABLE SOLUTIONS		
Lundsby Renewable Solutions A/S, Hjarbækvej 65, 8831 Løgstrup Tlf.: +45 96 49 43 00 Info@lundsby.dk This Drawing is subject to copyright and may not be reproduced without permission from Lundsby Renewable Solutions A/S		
Project nr.: 1768		Drawing nr.: 9621
FORMAT: A1		

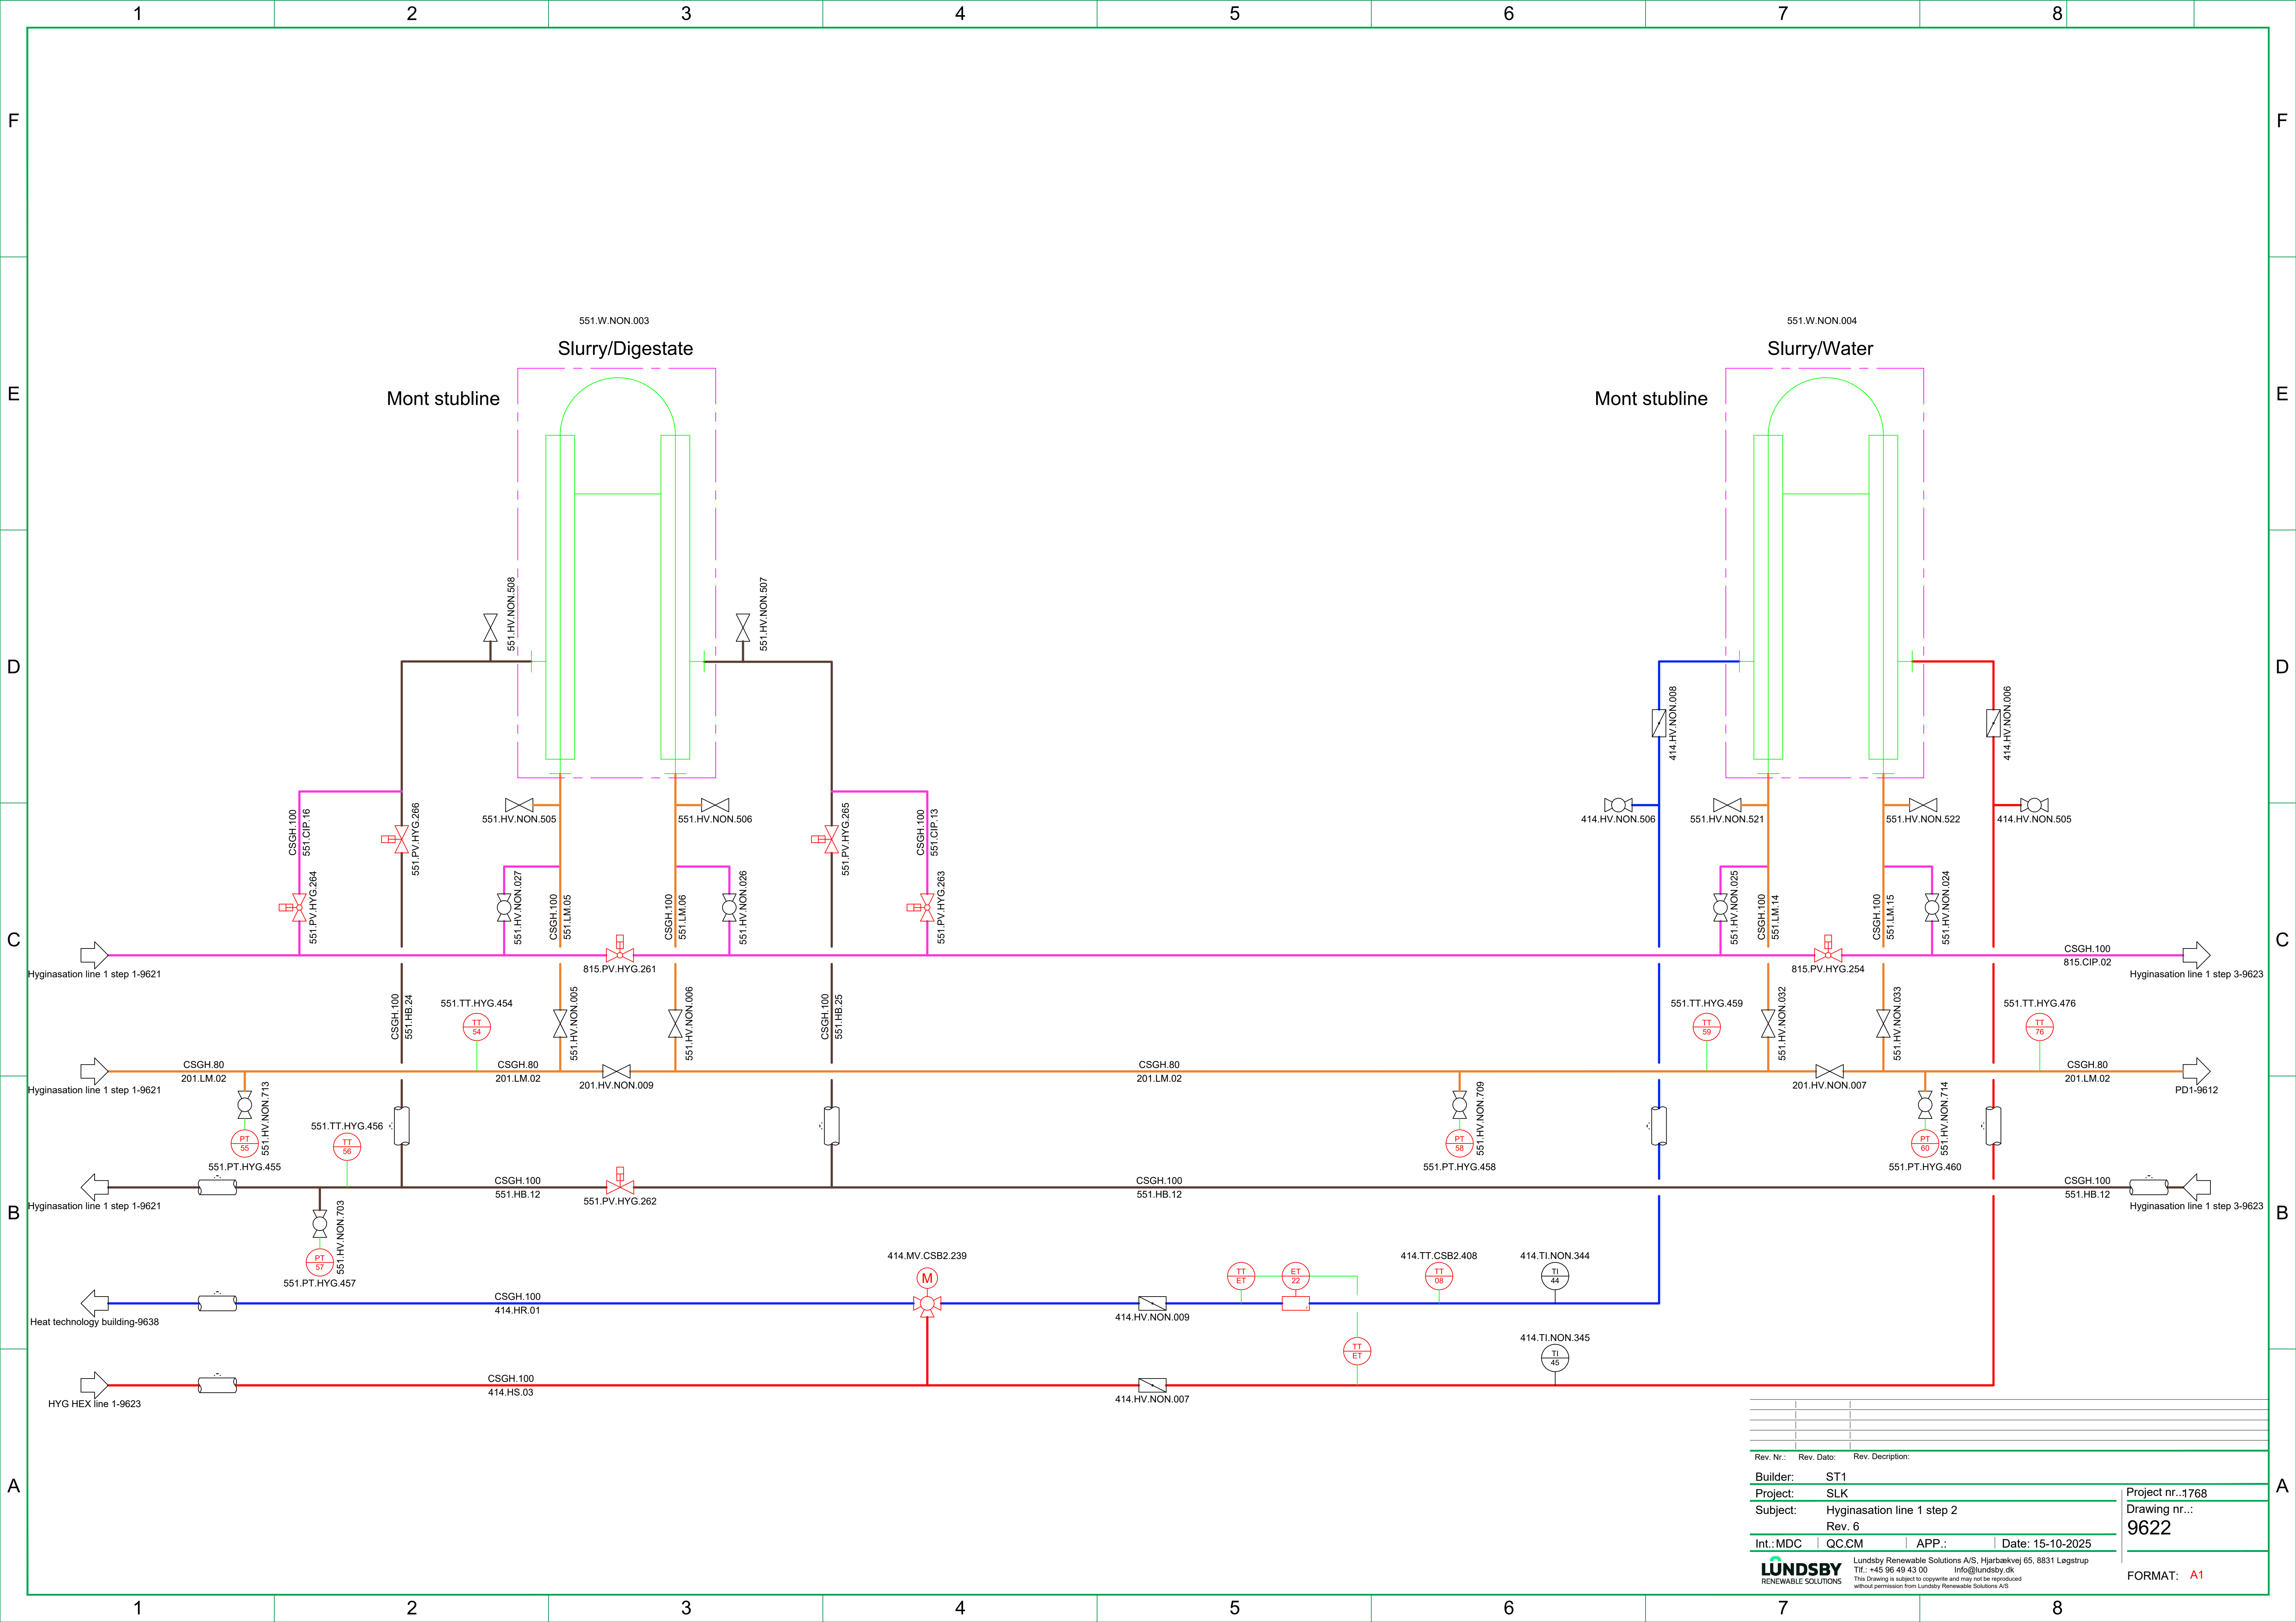



Rev. Nr.:	Rev. Dato:	Rev. Description:
Builder:	ST1	
Project:	SLK	
Subject:	Hyginasation line 1 step 2	
	Rev. 6	
Int.:MDC	QC:CM	APP.:Date: 15-10-2025
LUNDSBYRENEWABLE SOLUTIONS Lundsby Renewable Solutions A/S, Hjarbrækvej 65, 8831 Lægstrup Tlf.: +45 96 49 43 00 Info@lundsby.dk This Drawing is subject to copyright and may not be reproduced without permission from Lundsby Renewable Solutions A/S		
Project nr.:1768		Drawing nr.:9622
FORMAT: A1		

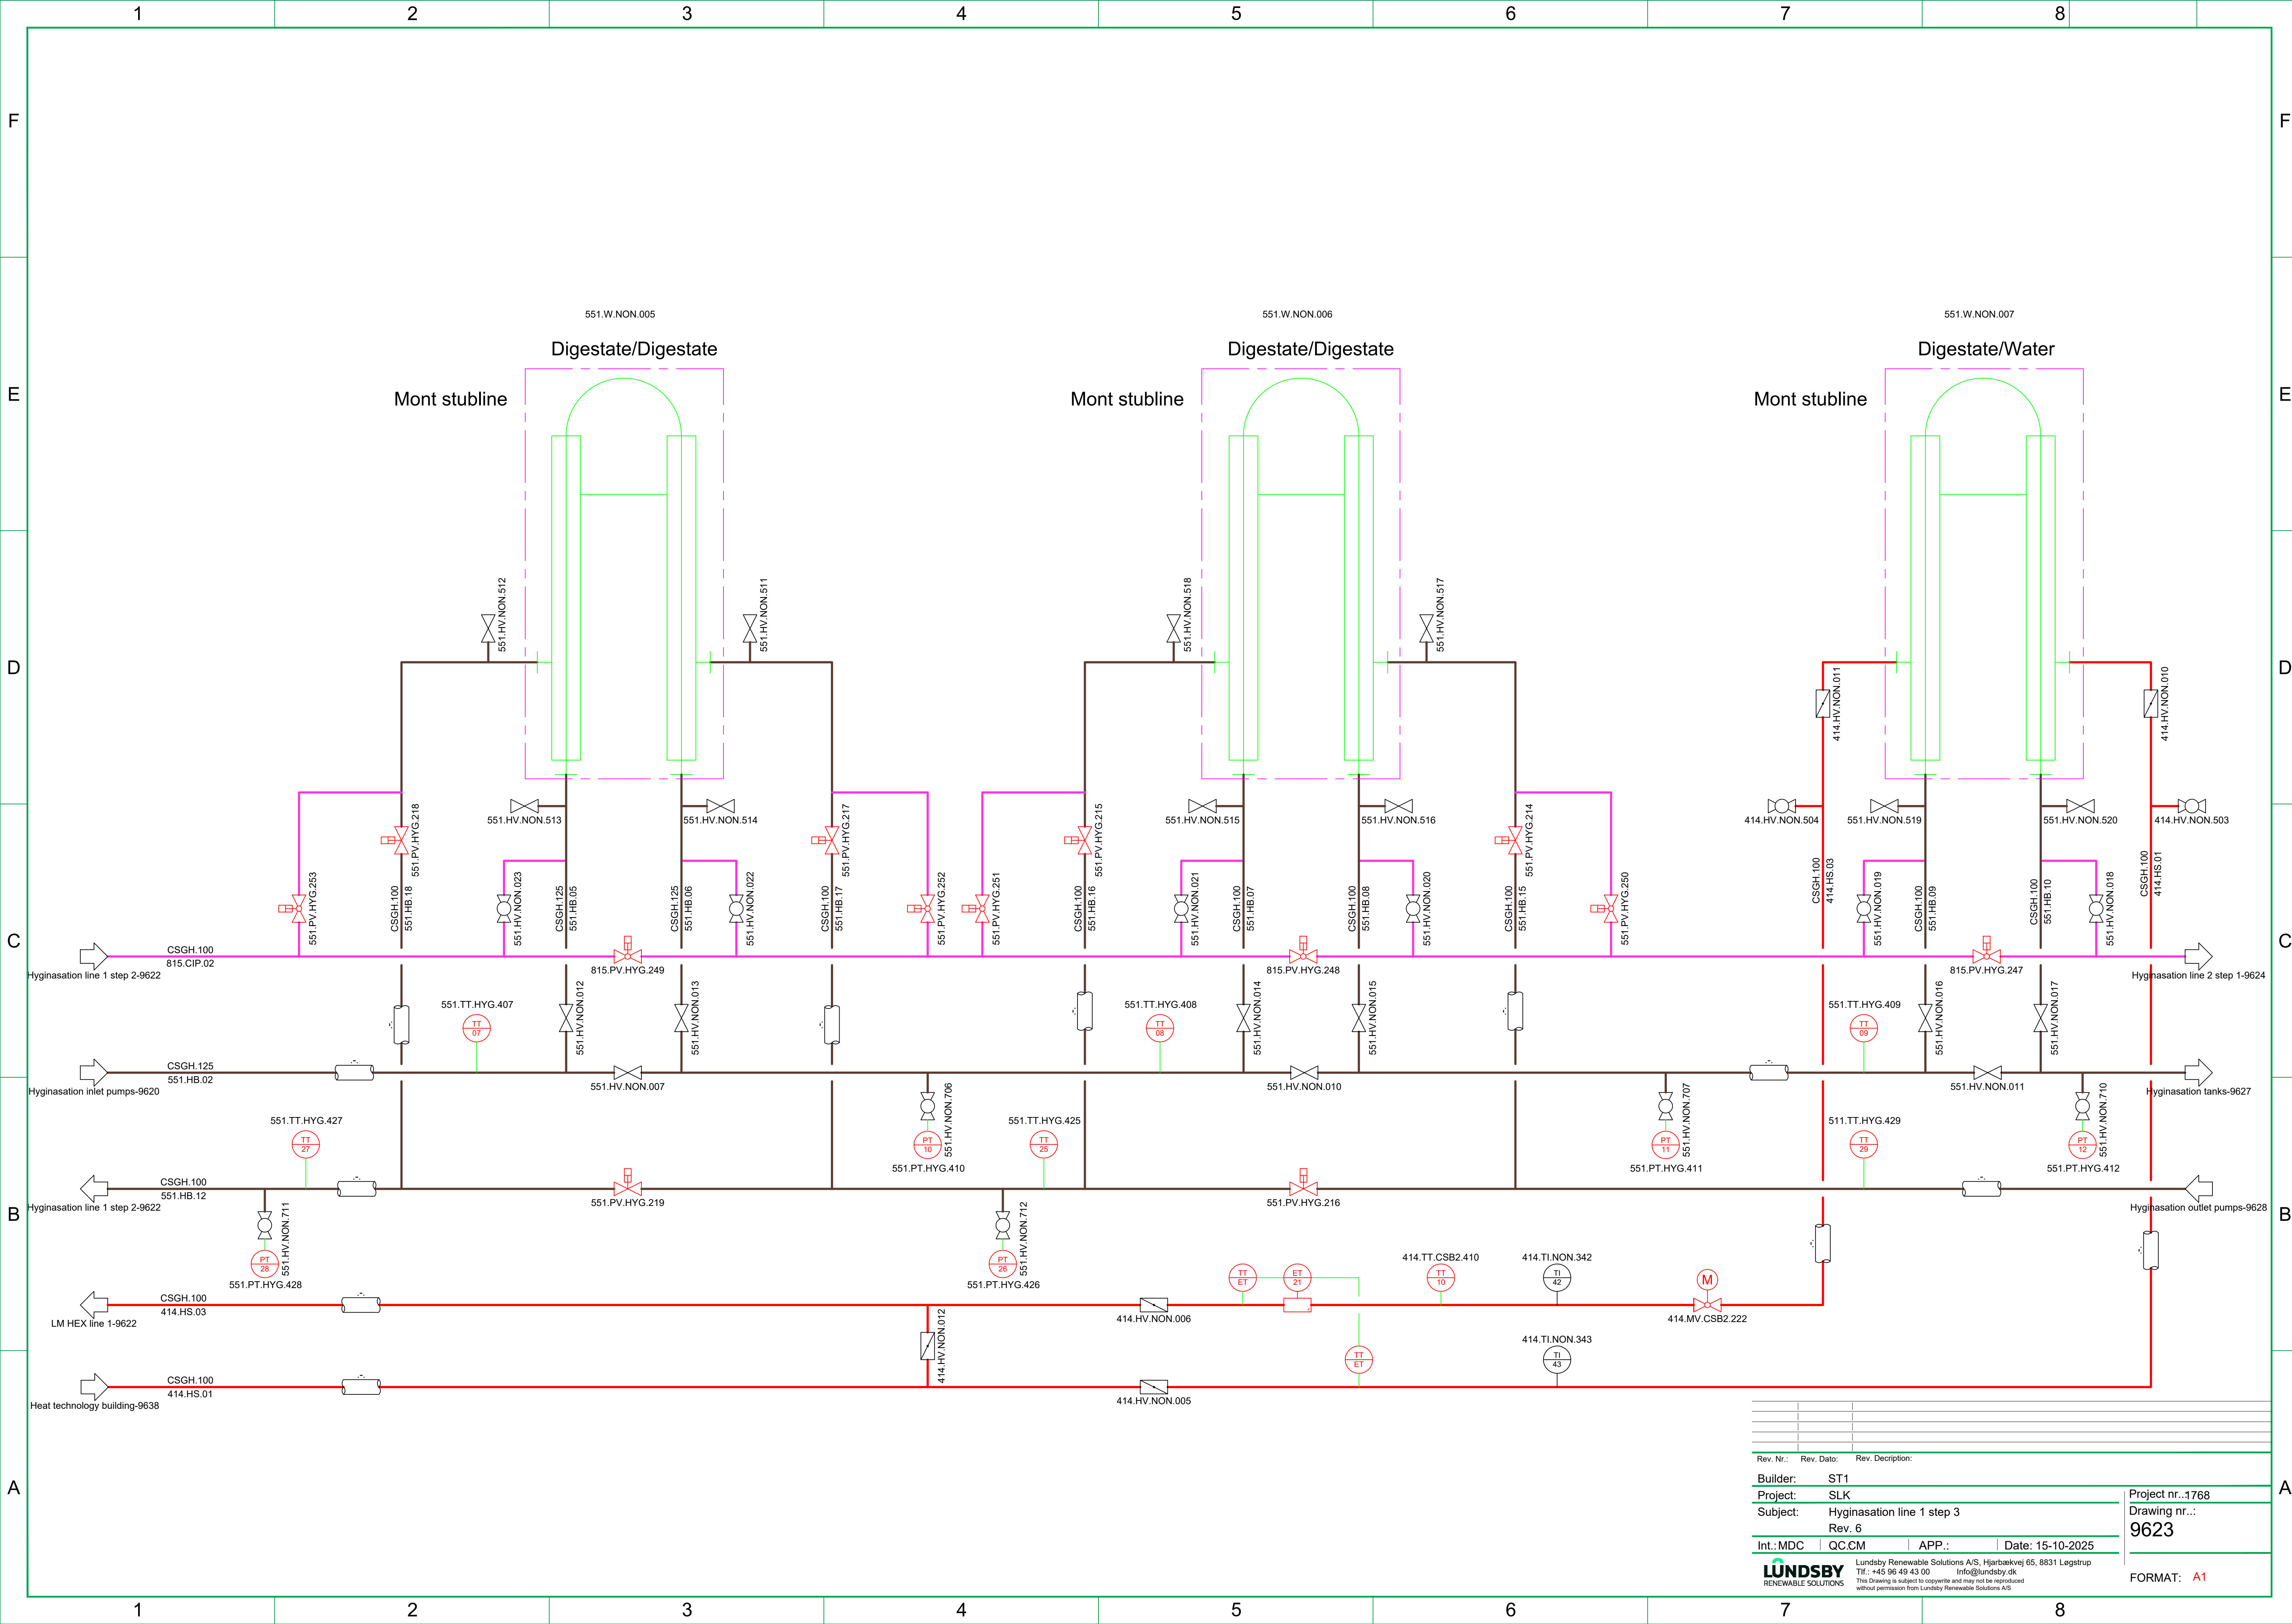


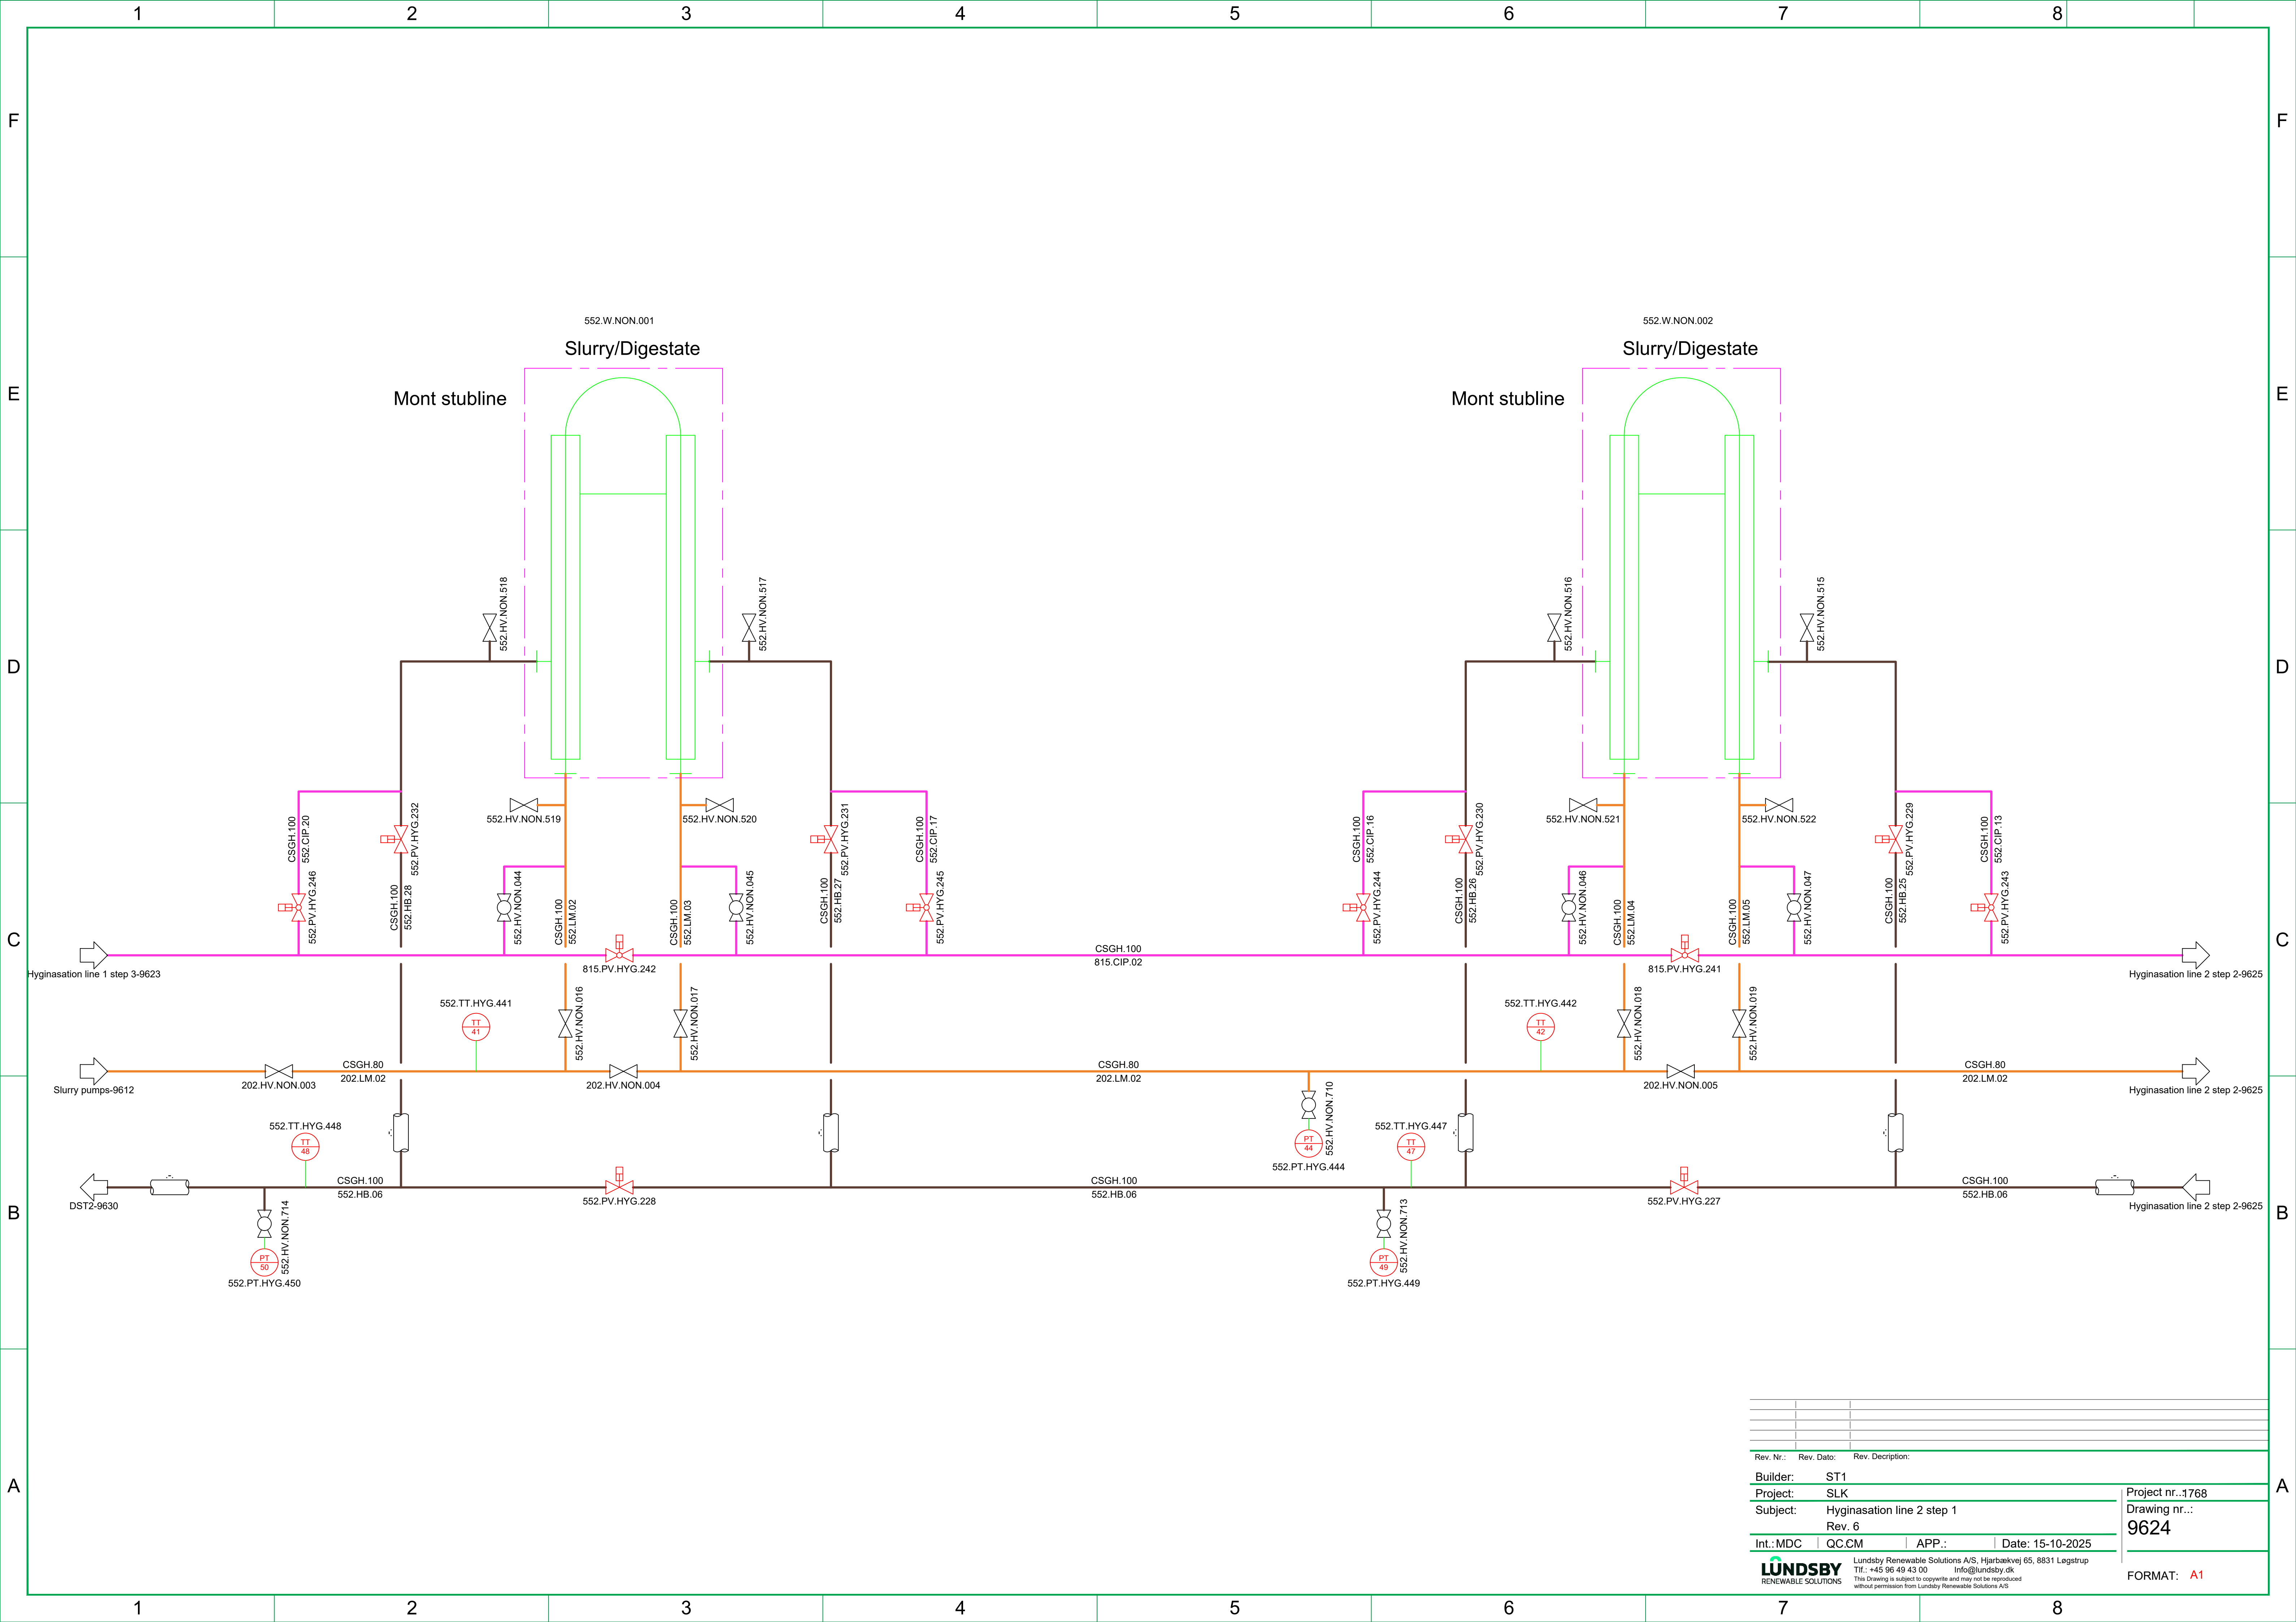

Rev. Nr.:	Rev. Dato:	Rev. Description:
Builder:	ST1	
Project:	SLK	
Subject:	Hyginasation line 2 step 1	
Rev. 6		
Int.:MDC	QC:CM	APP.:
Date: 15-10-2025		
LUNDSBY RENEWABLE SOLUTIONS		
Lundsby Renewable Solutions A/S, Hjarbækvej 65, 8831 Løgstrup Tlf.: +45 96 49 43 00 Info@lundsby.dk This Drawing is subject to copyright and may not be reproduced without permission from Lundsby Renewable Solutions A/S		
Project nr.:1768 Drawing nr.: 9624		FORMAT: A1

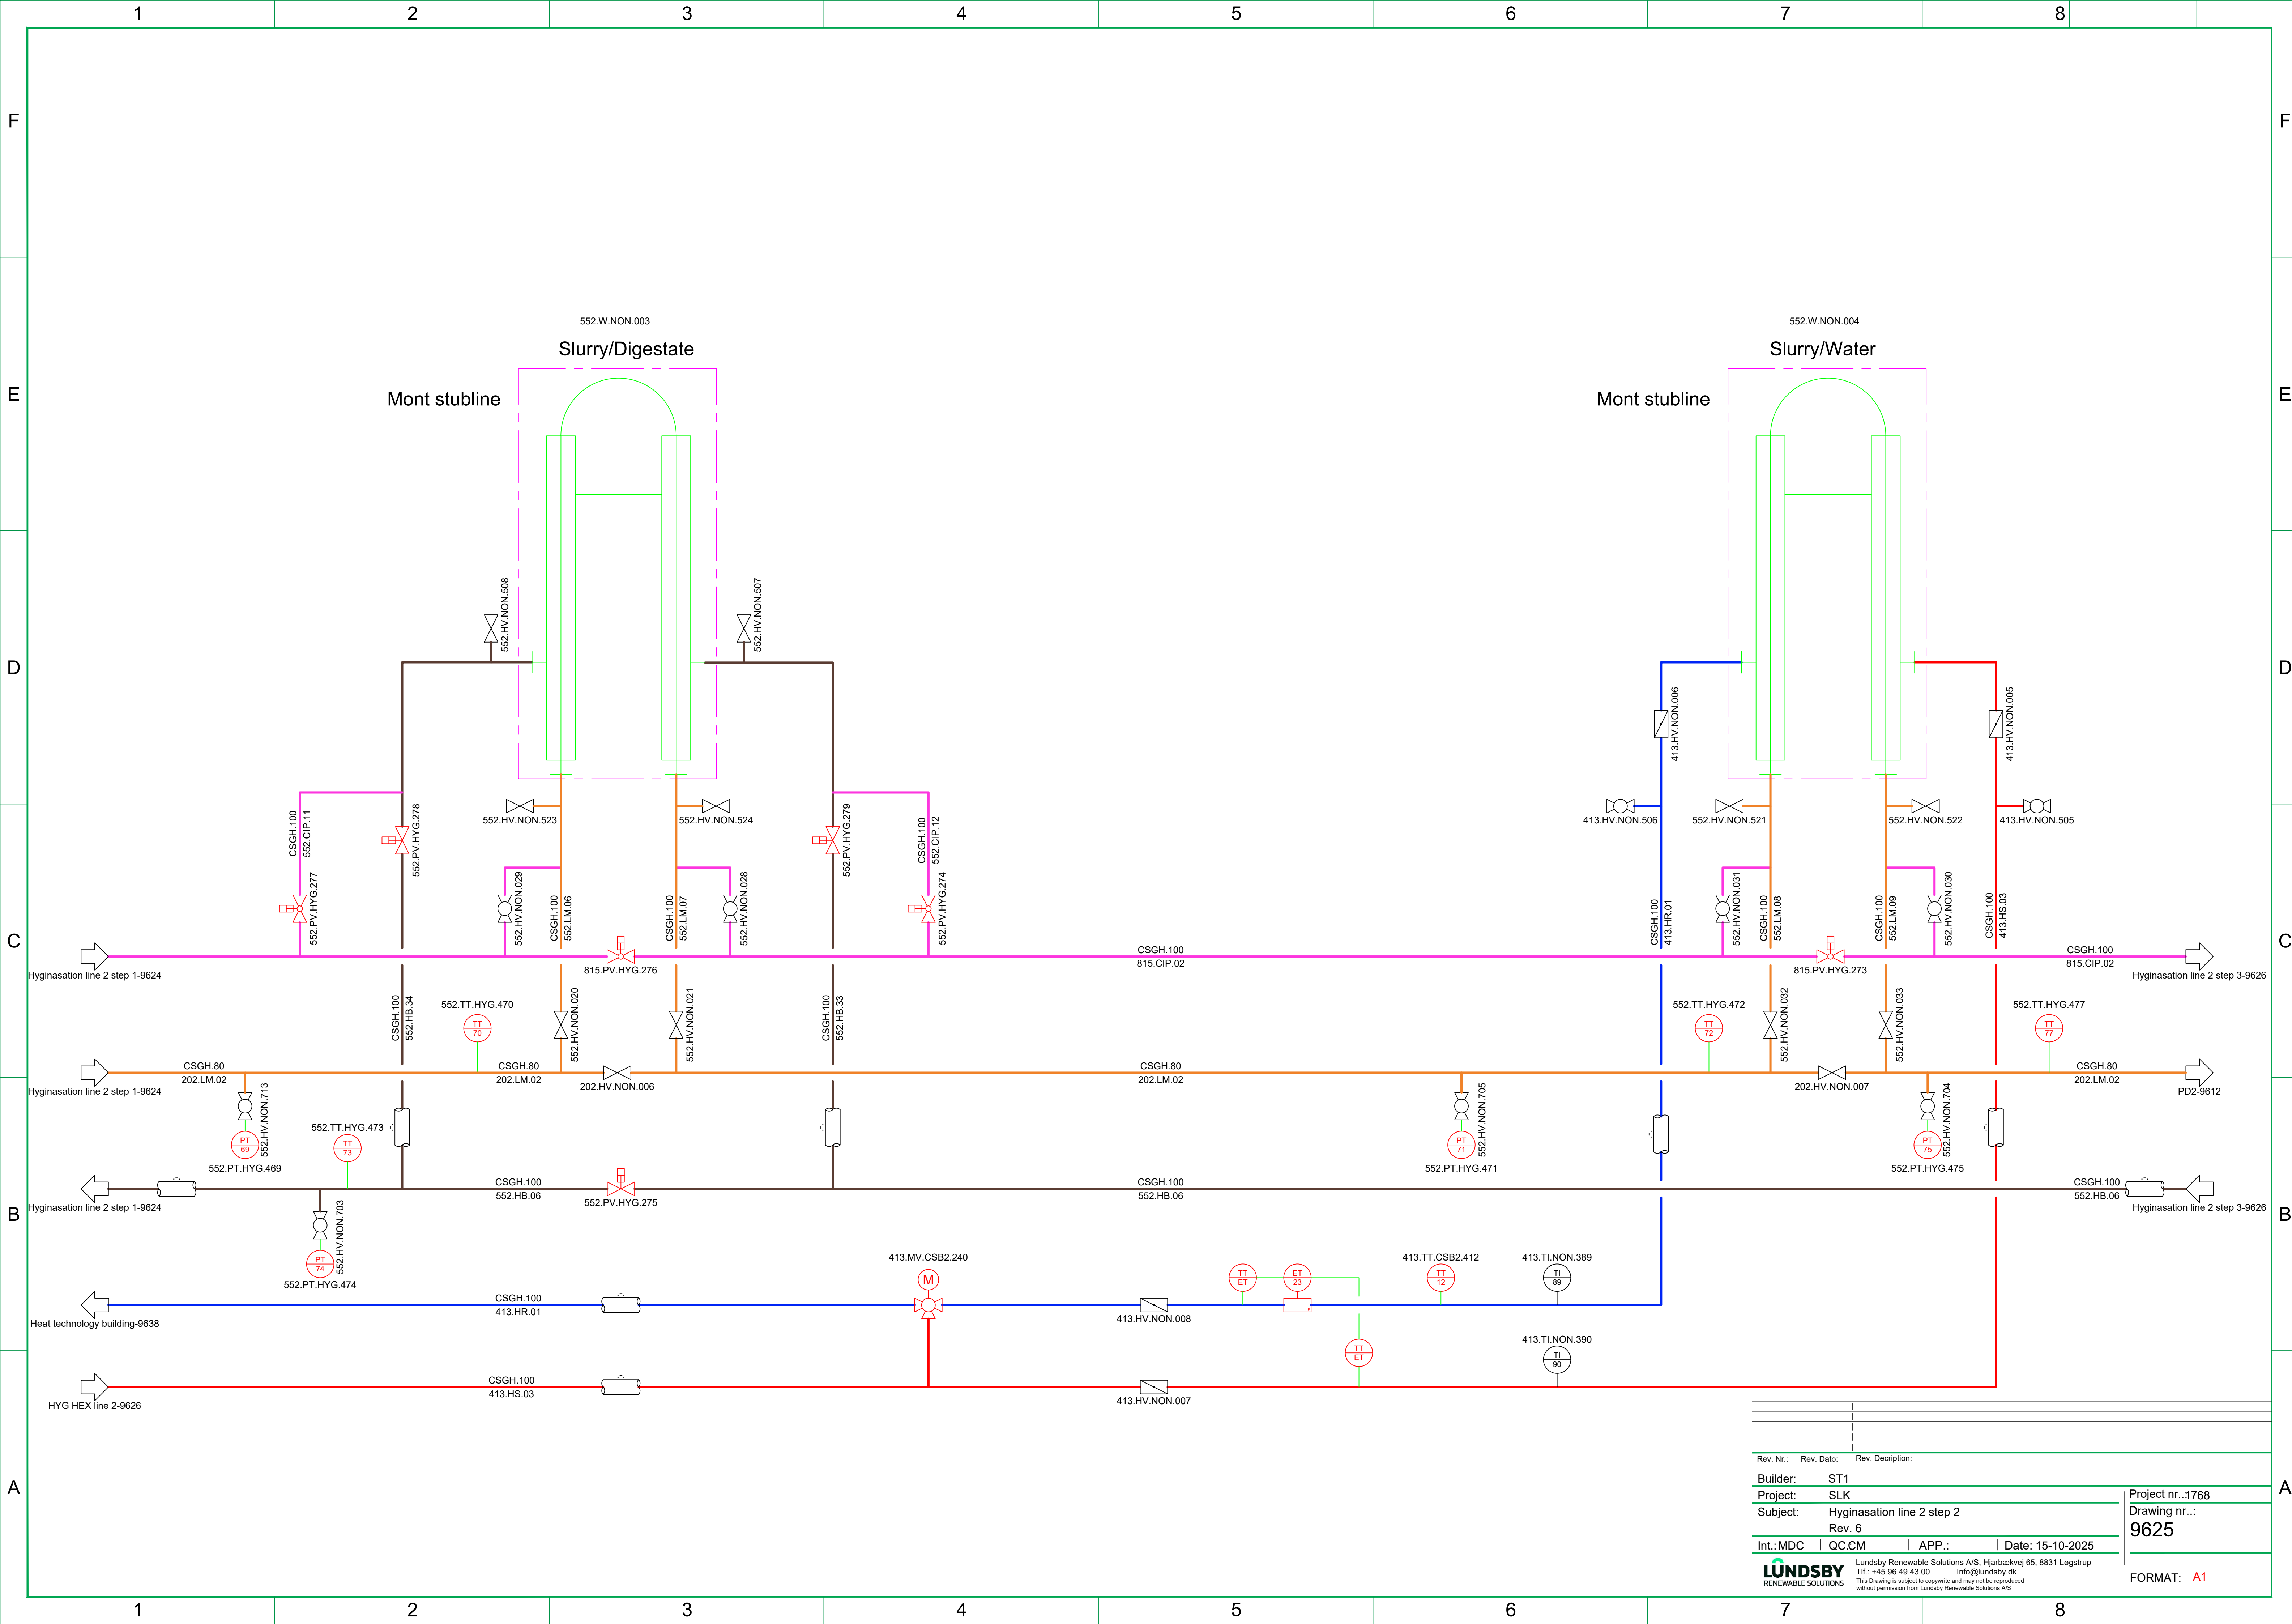

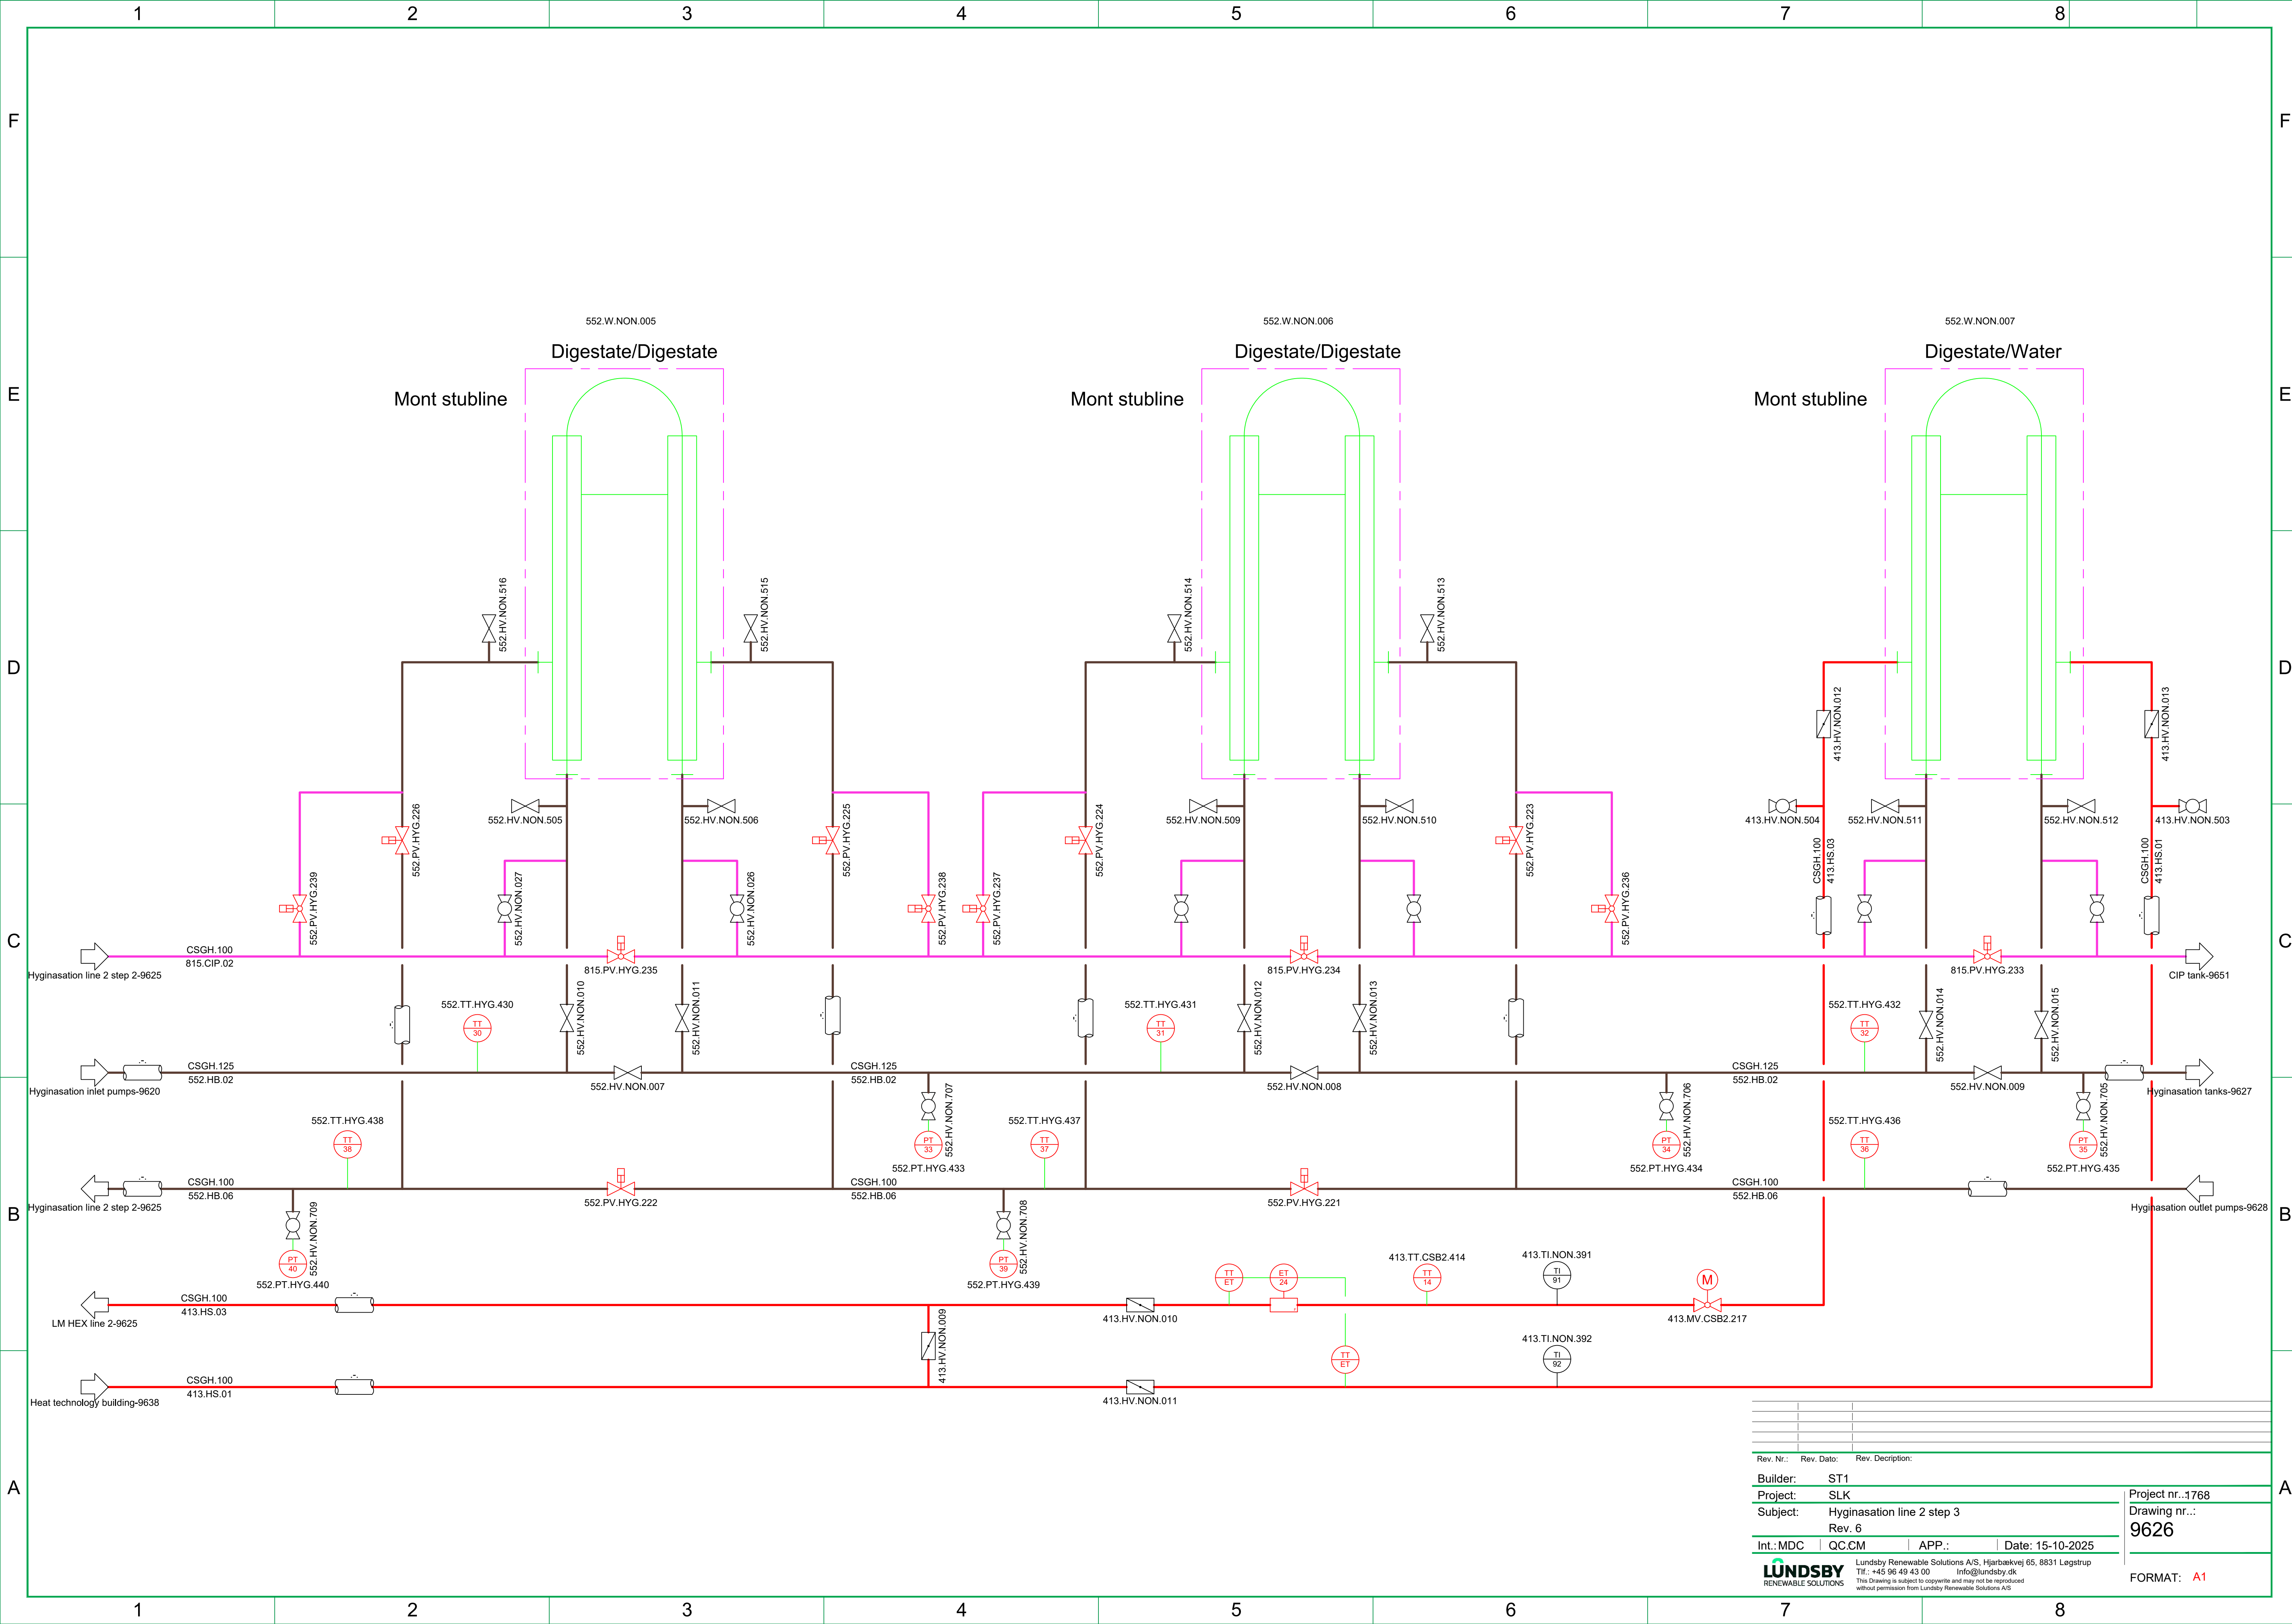


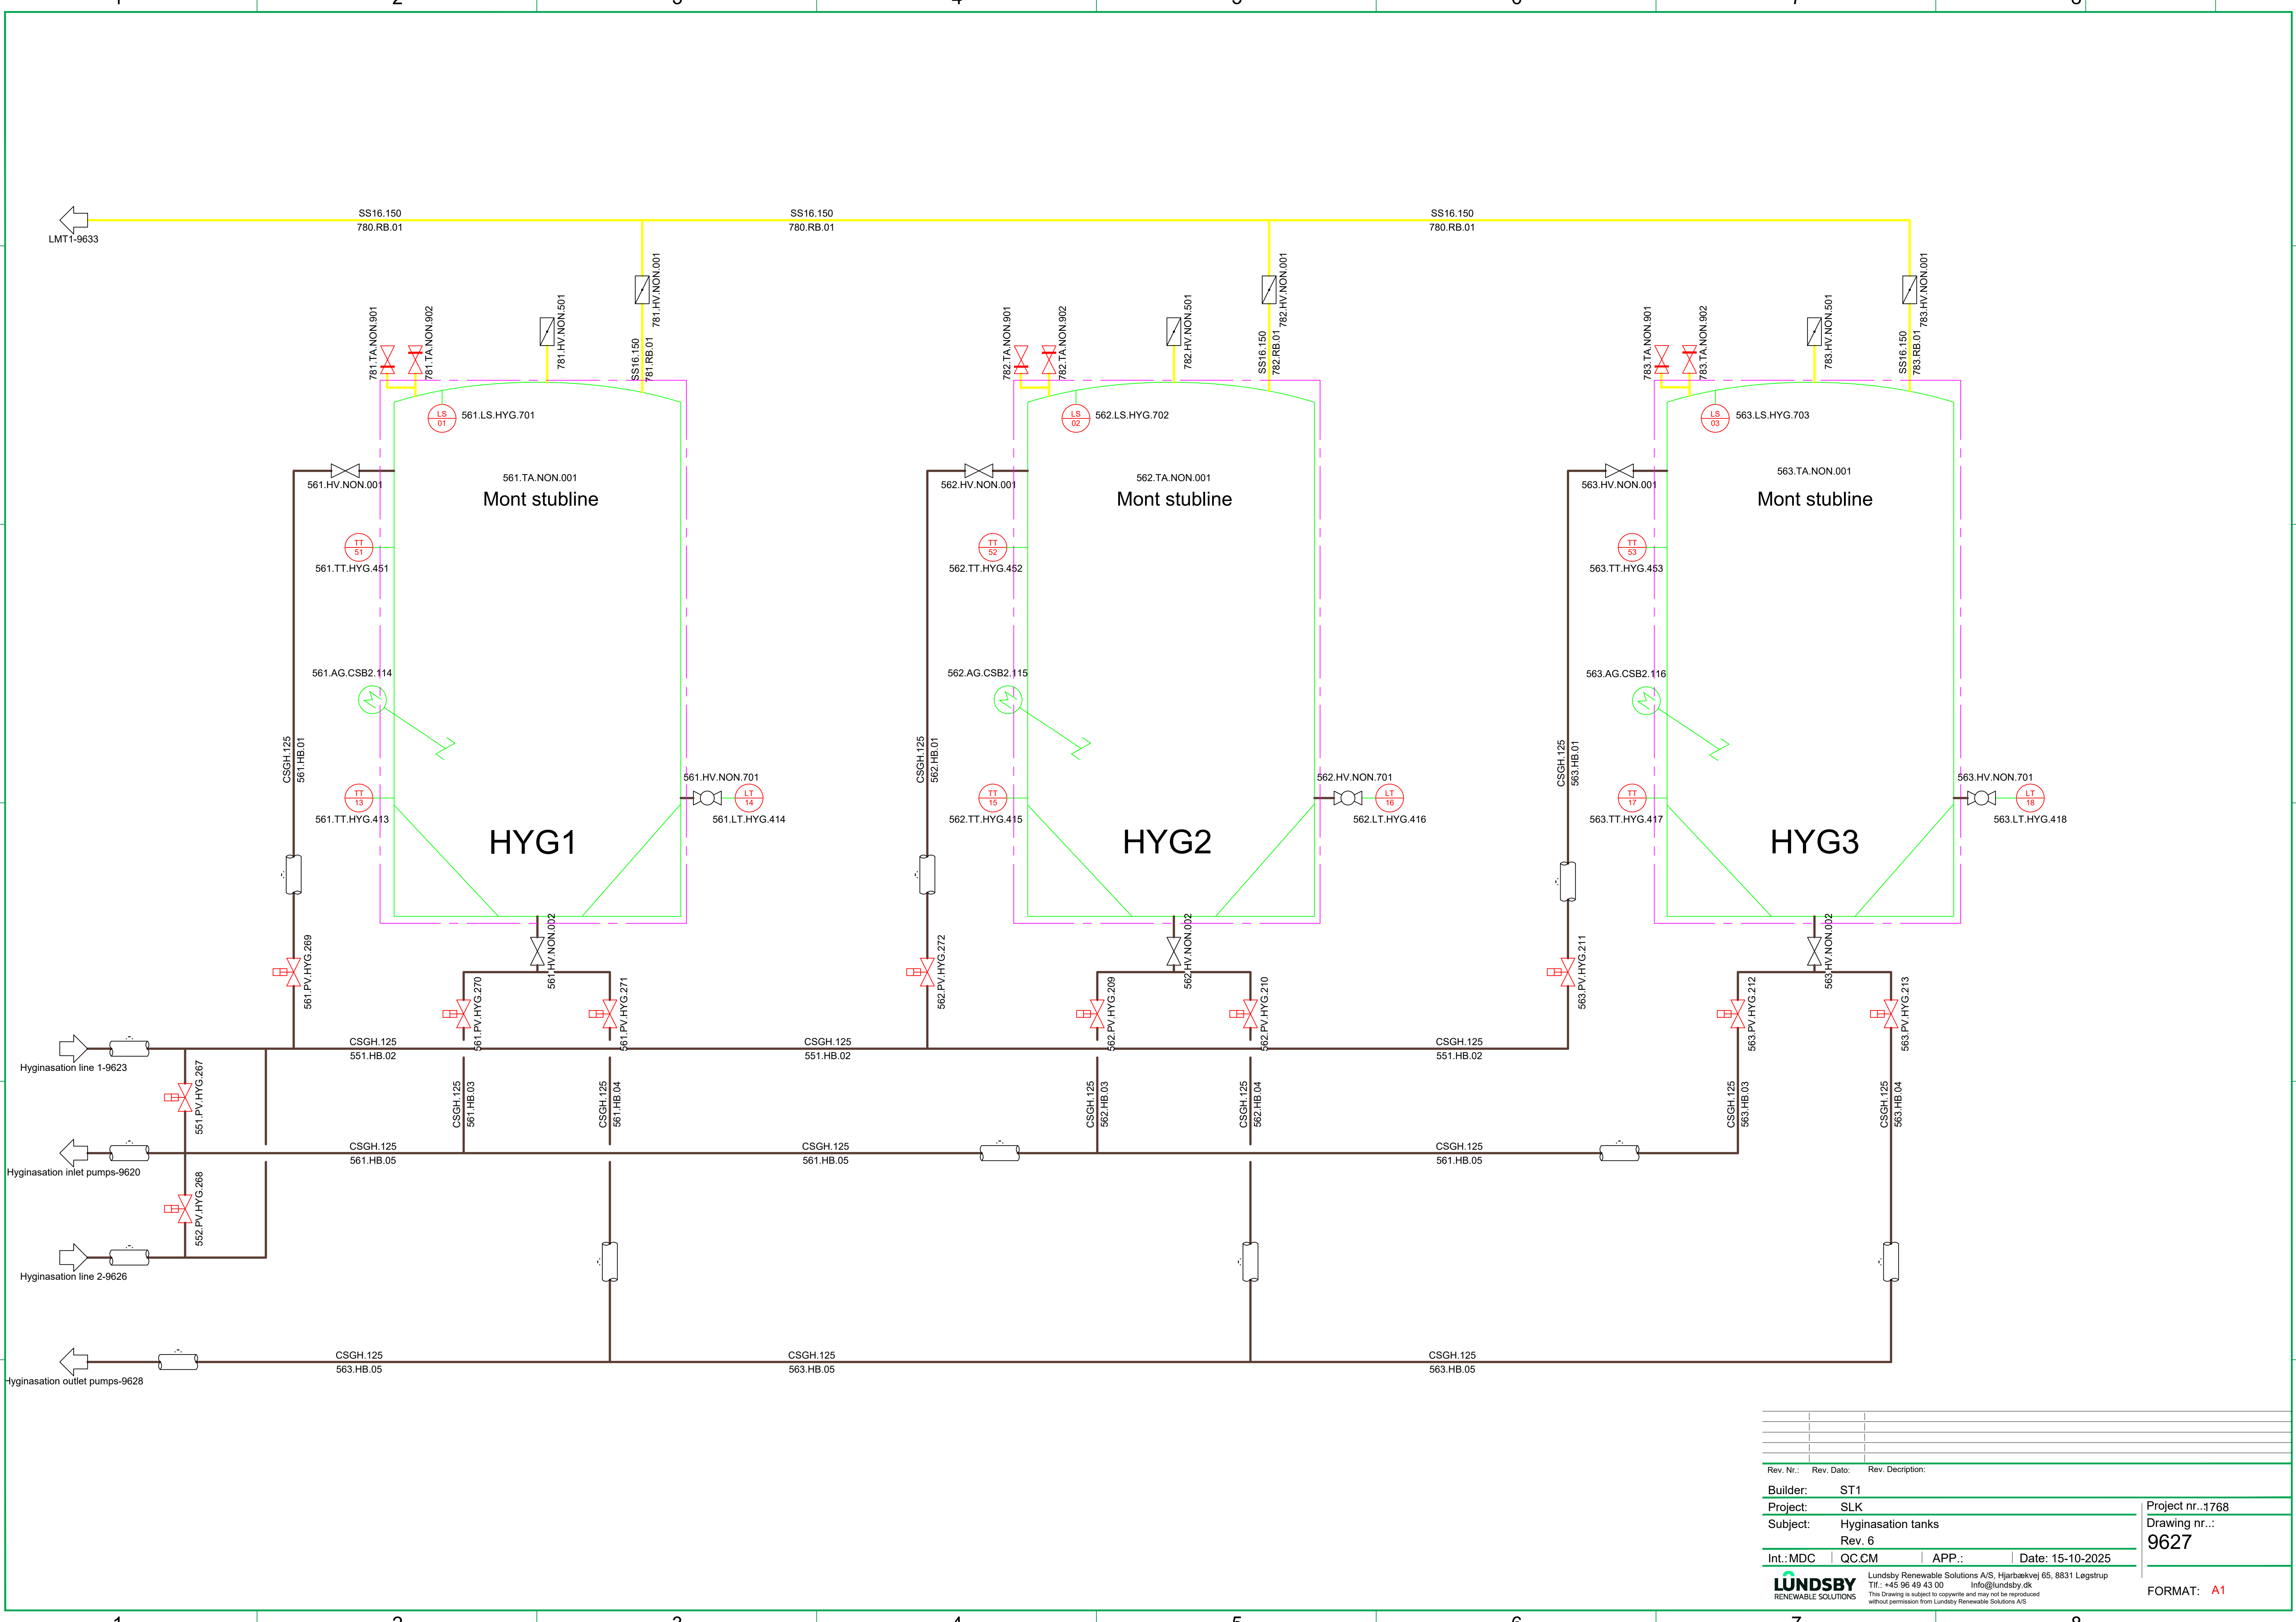


Rev. Nr.:	Rev. Dato:	Rev. Description:
Builder:	ST1	
Project:	SLK	
Subject:	Hyginasation tanks	
Rev. 6		
Int.: MDC	QC.CM	APP.:
Date: 15-10-2025		
LUNDSBY RENEWABLE SOLUTIONS		
Lundsby Renewable Solutions A/S, Hjarbækvej 65, 8831 Løgstrup Tlf.: +45 96 49 43 00 Info@lundsby.dk This Drawing is subject to copyright and may not be reproduced without permission from Lundsby Renewable Solutions A/S		
Project nr.: 1768		
Drawing nr.: 9627		
FORMAT: A1		


Tech Building

Outlet pumps

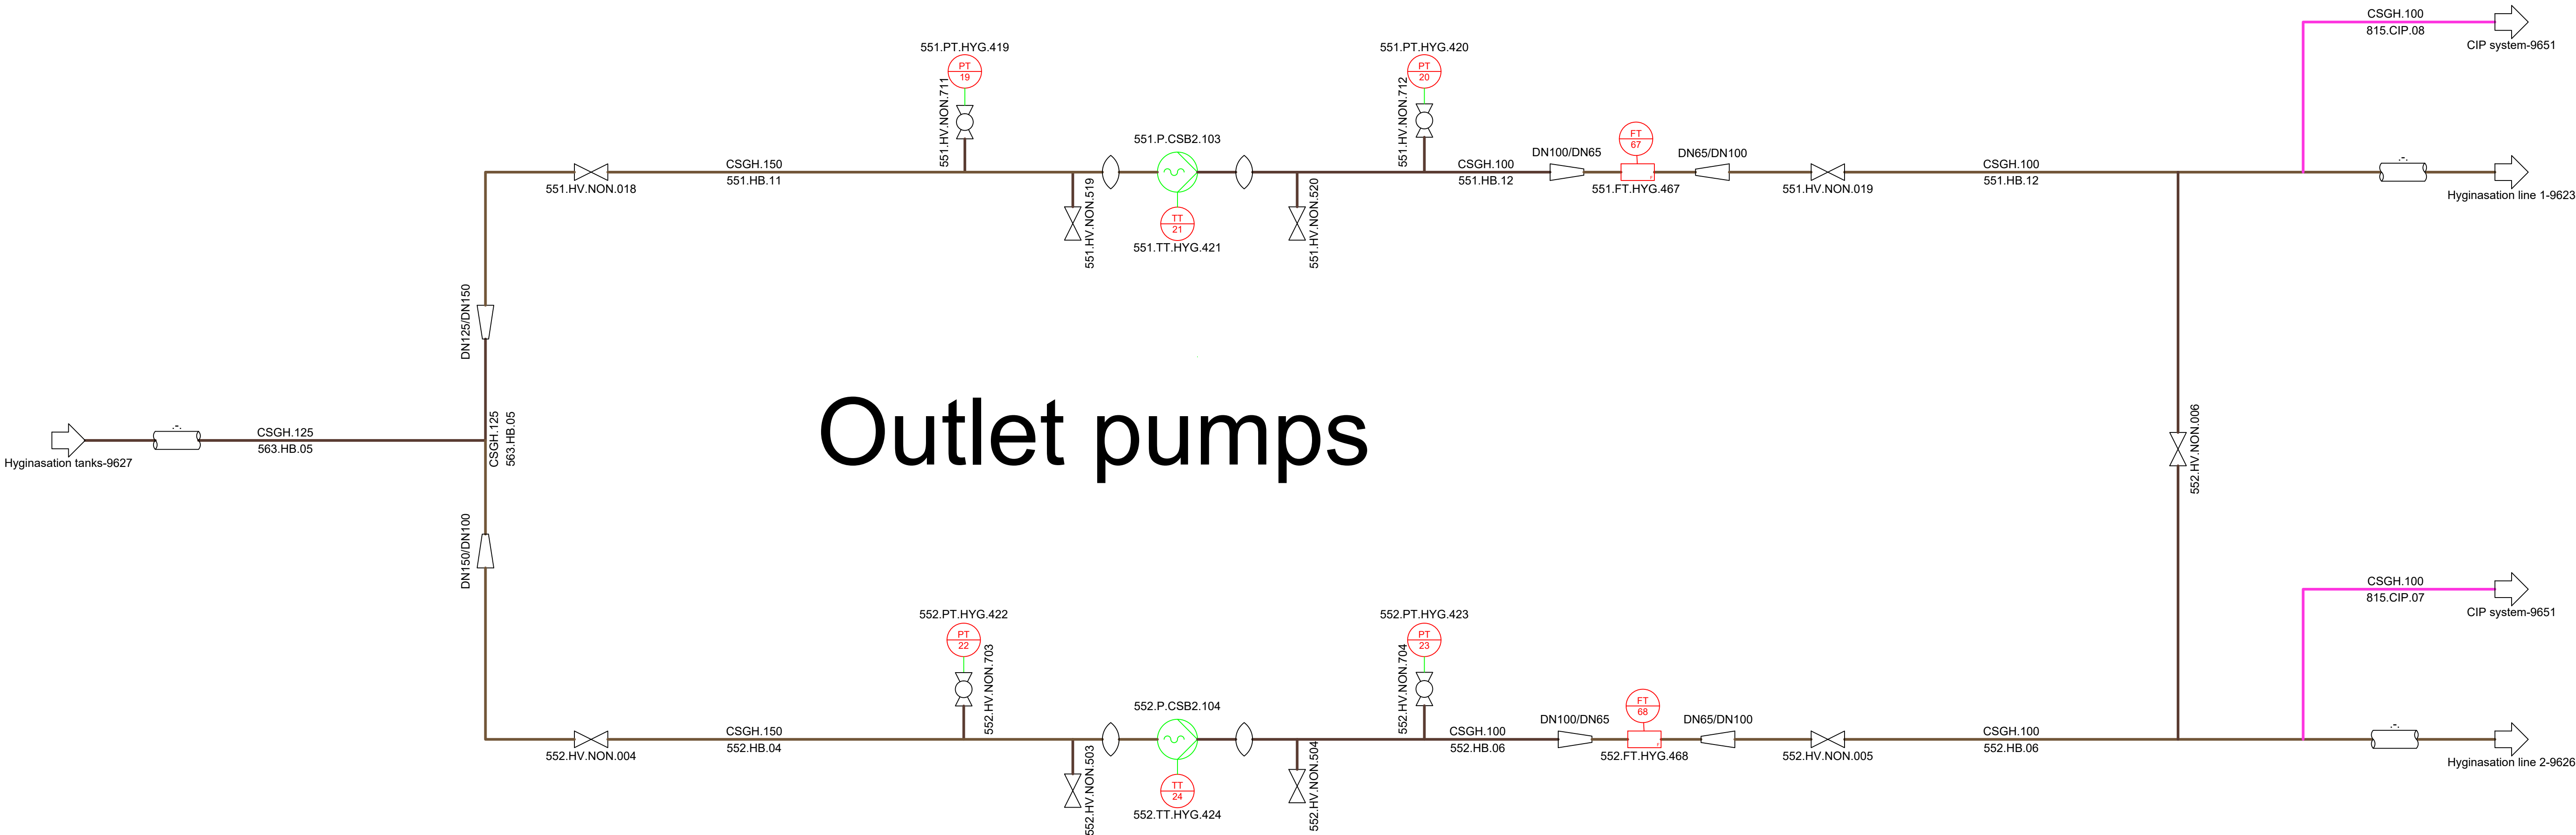


Rev. Nr.:	Rev. Dato:	Rev. Description:	
Builder:	ST1		
Project:	SLK		
Subject:	Hyginasation outlet pumps		
Rev. 6			
Int.:MDC	QC:CM	APP.:	Date: 15-10-2025
LUNDSBY RENEWABLE SOLUTIONS			Lundsby Renewable Solutions A/S, Hjarbrækvej 65, 8831 Løgstrup Tlf.: +45 96 49 43 00 Info@lundsby.dk This Drawing is subject to copyright and may not be reproduced without permission from Lundsby Renewable Solutions A/S
			Project nr.:1768 Drawing nr.: 9628 FORMAT: A1

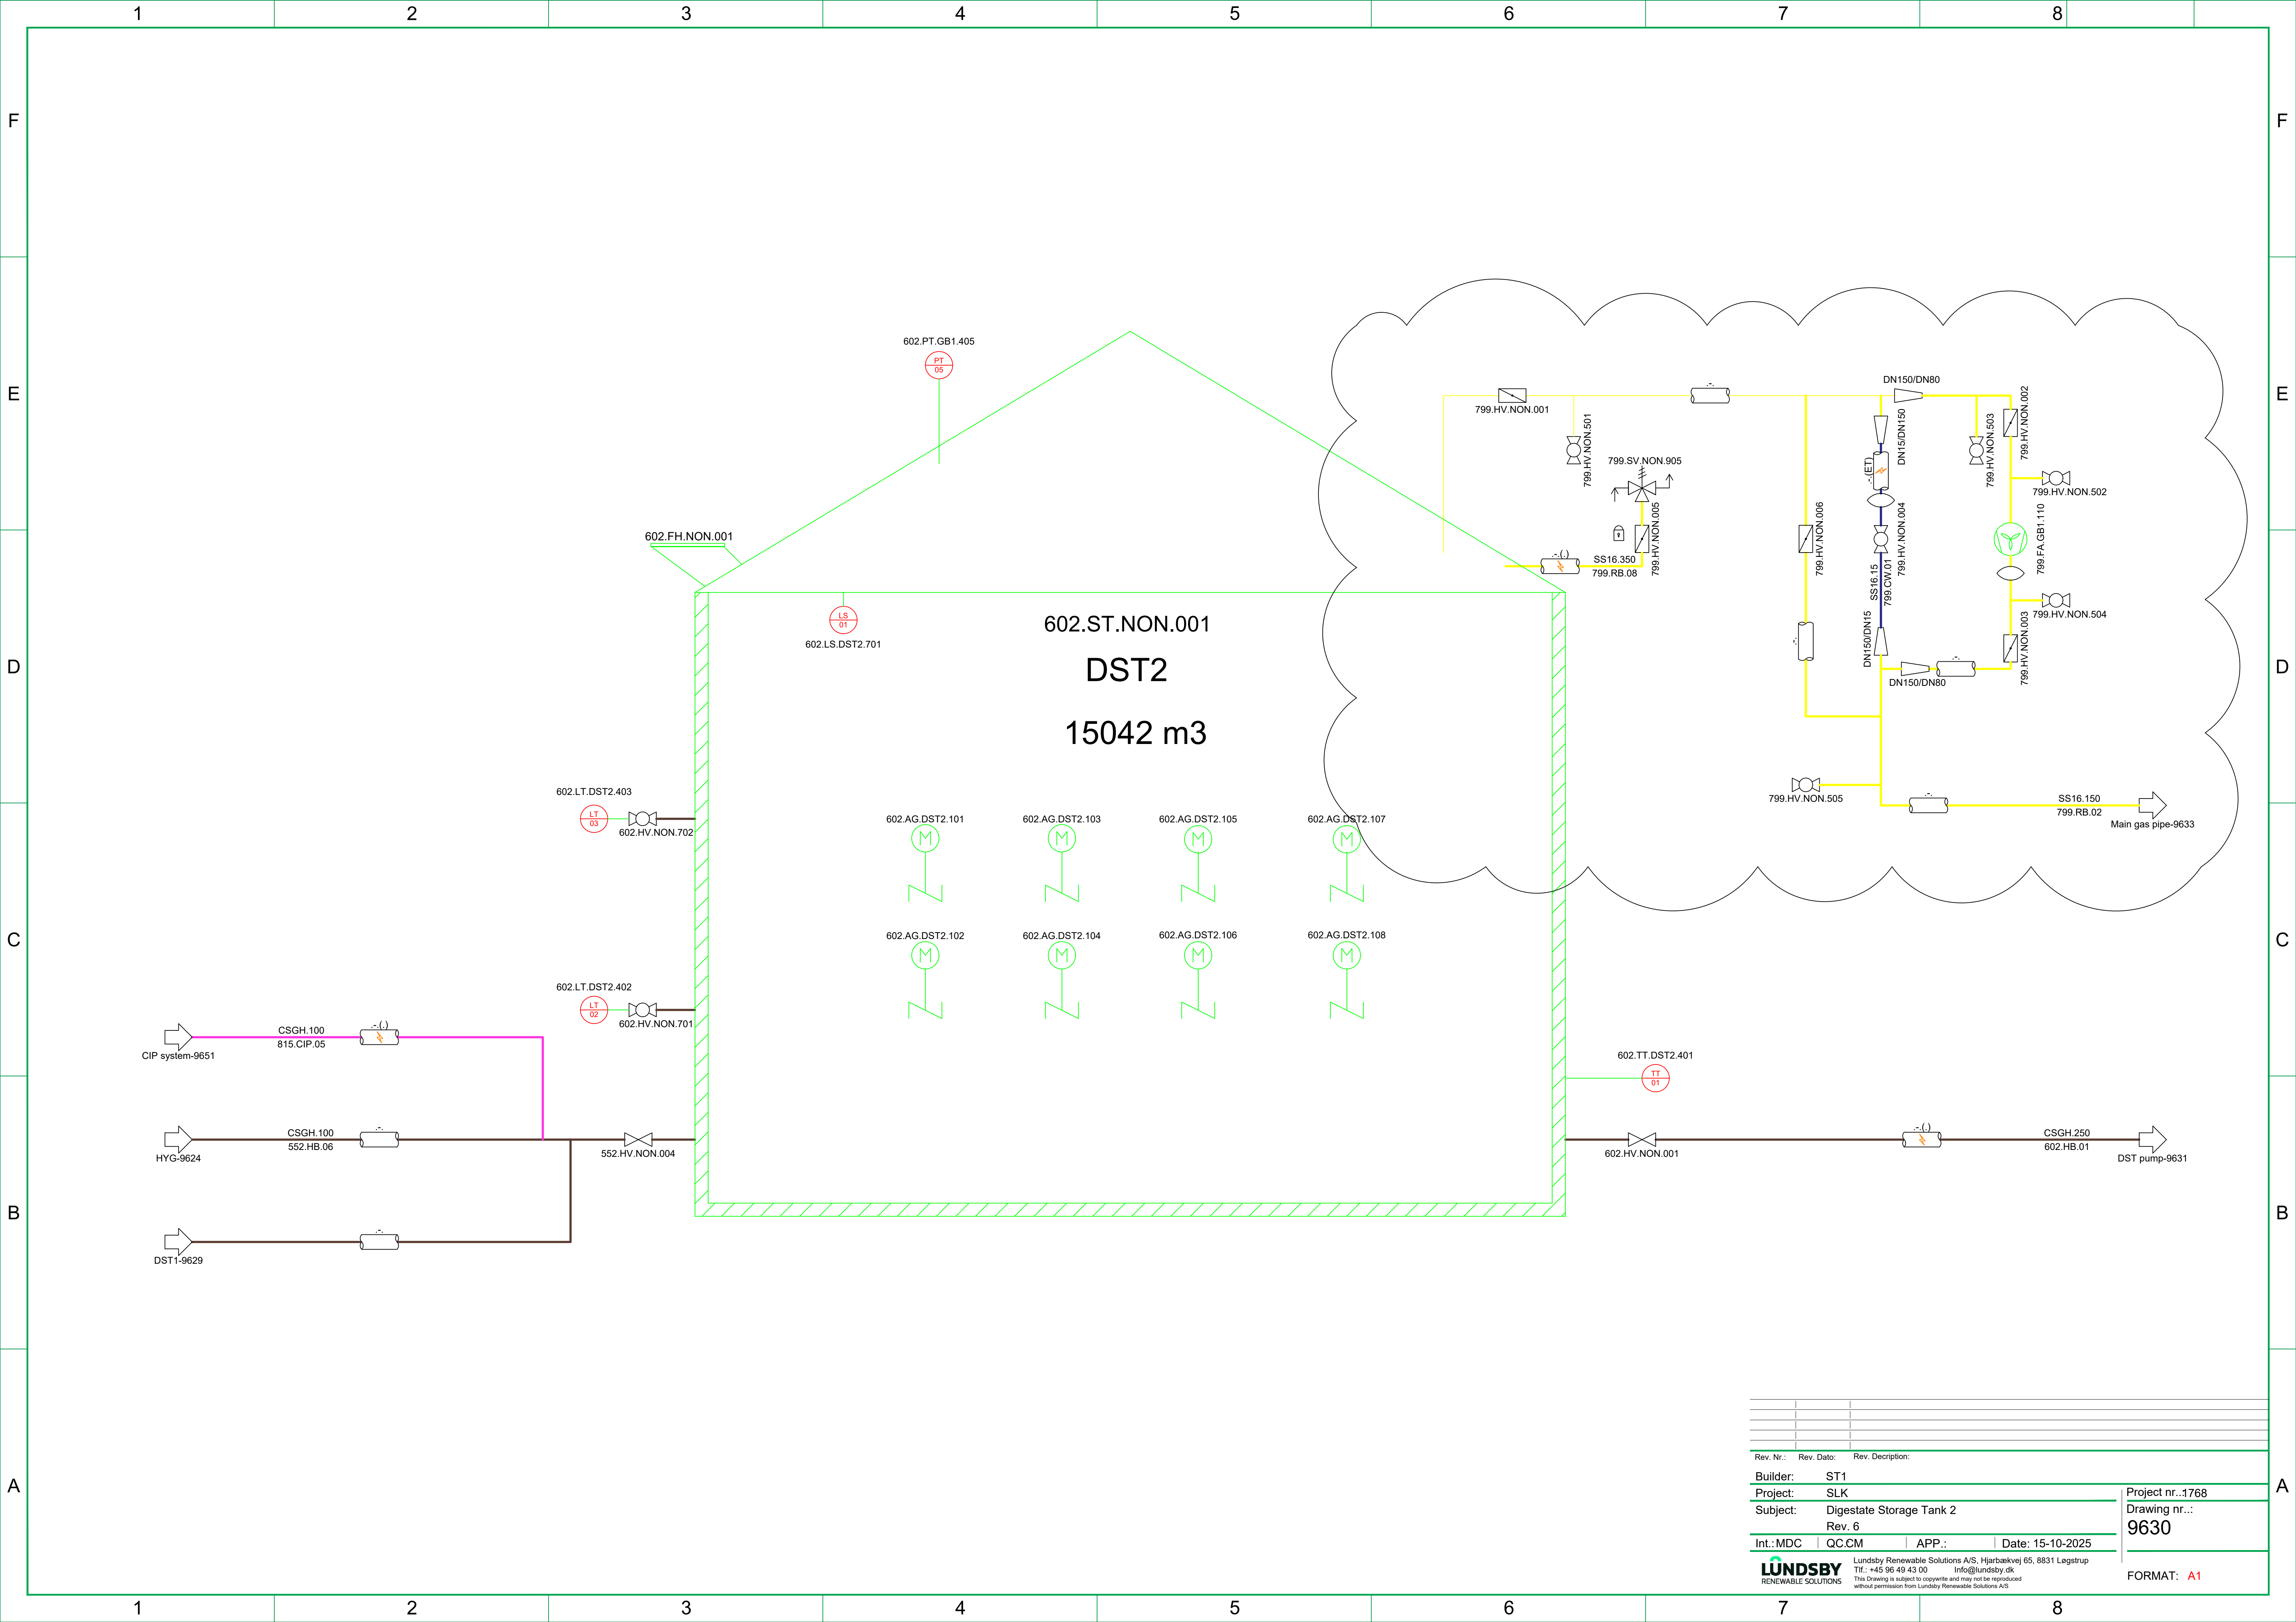


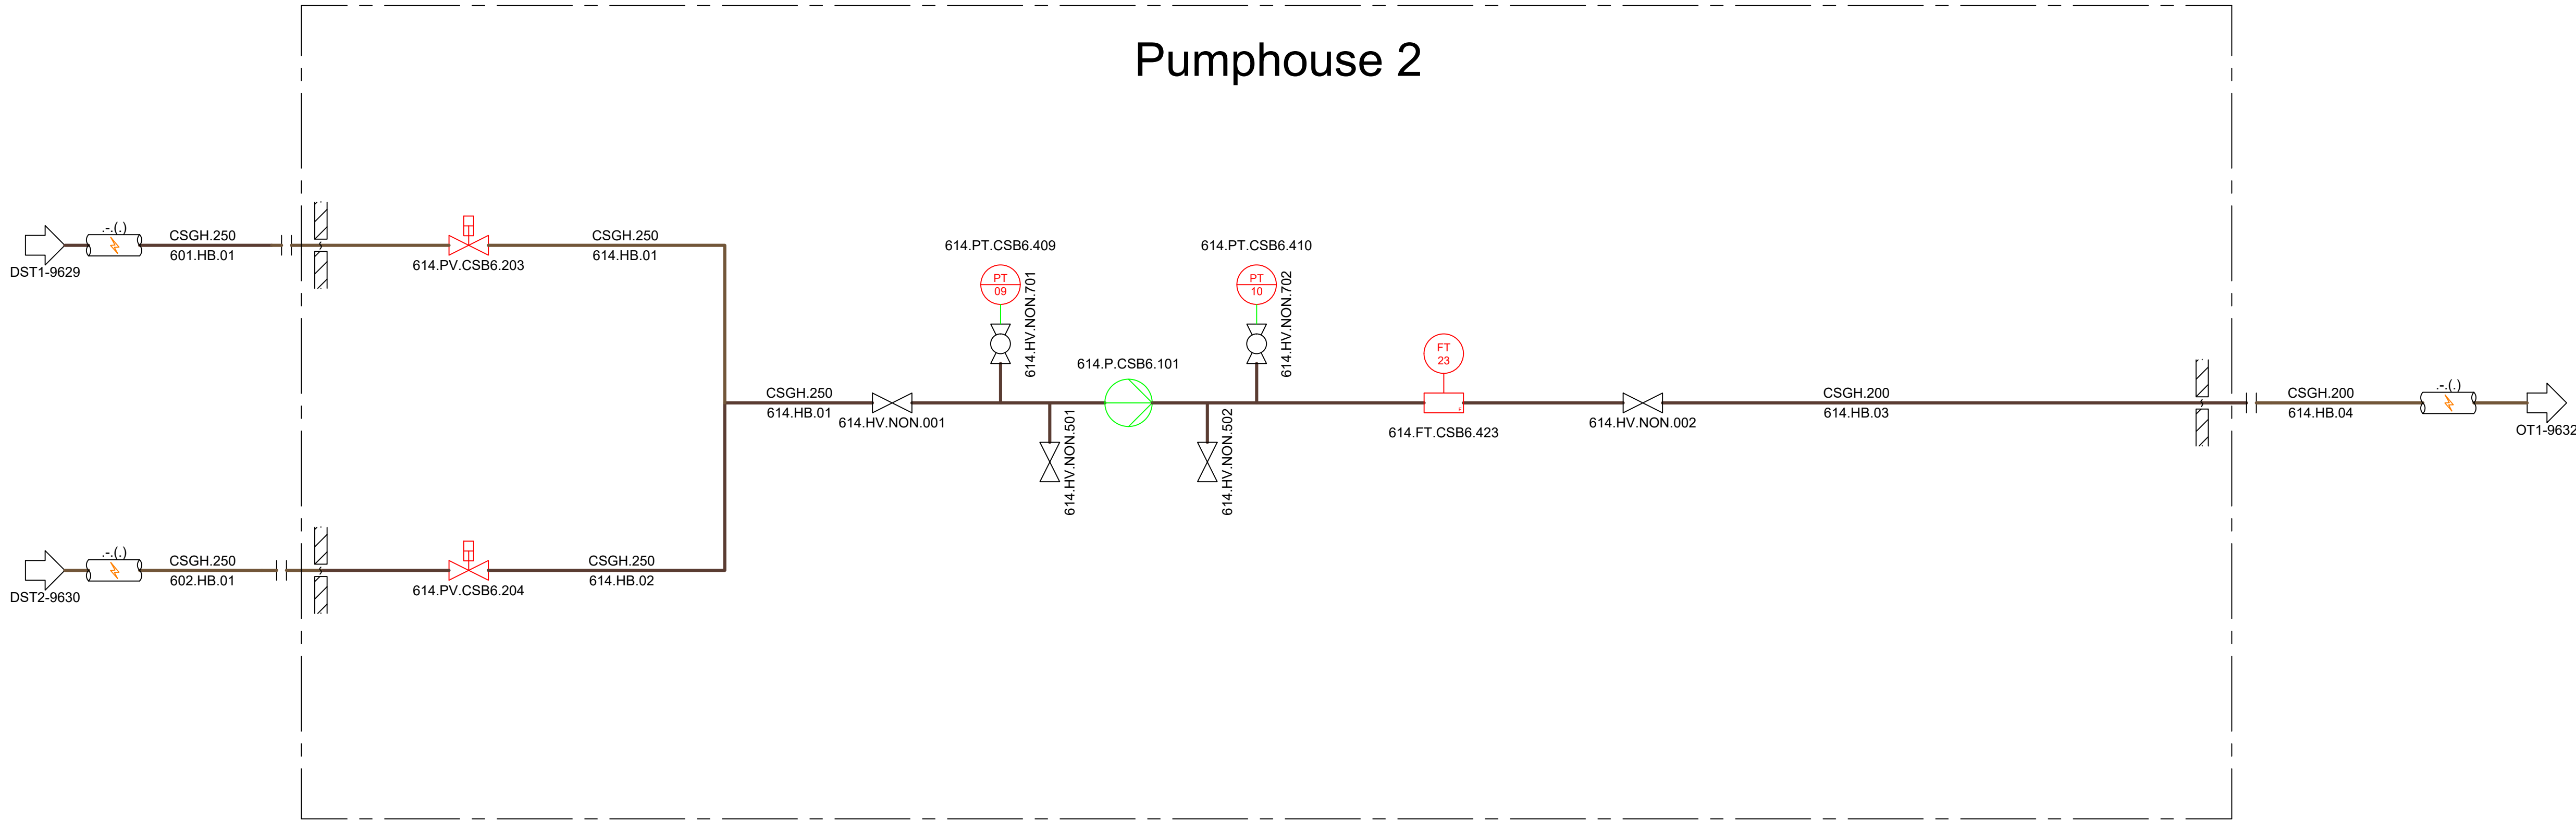

Rev. Nr.:	Rev. Dato:	Rev. Description:	Project nr...1768
Builder:	ST1		Drawing nr...:
Project:	SLK		9631
Subject:	DST pump		
	Rev. 6		
Int.:MDC	QC:CM	APP.:	Date: 15-10-2025
LUNDSBY RENEWABLE SOLUTIONS		Lundsby Renewable Solutions A/S, Hjarbækvej 65, 8831 Løgstrup Tlf.: +45 96 49 43 00 Info@lundsby.dk This Drawing is subject to copyright and may not be reproduced without permission from Lundsby Renewable Solutions A/S	
		FORMAT: A1	

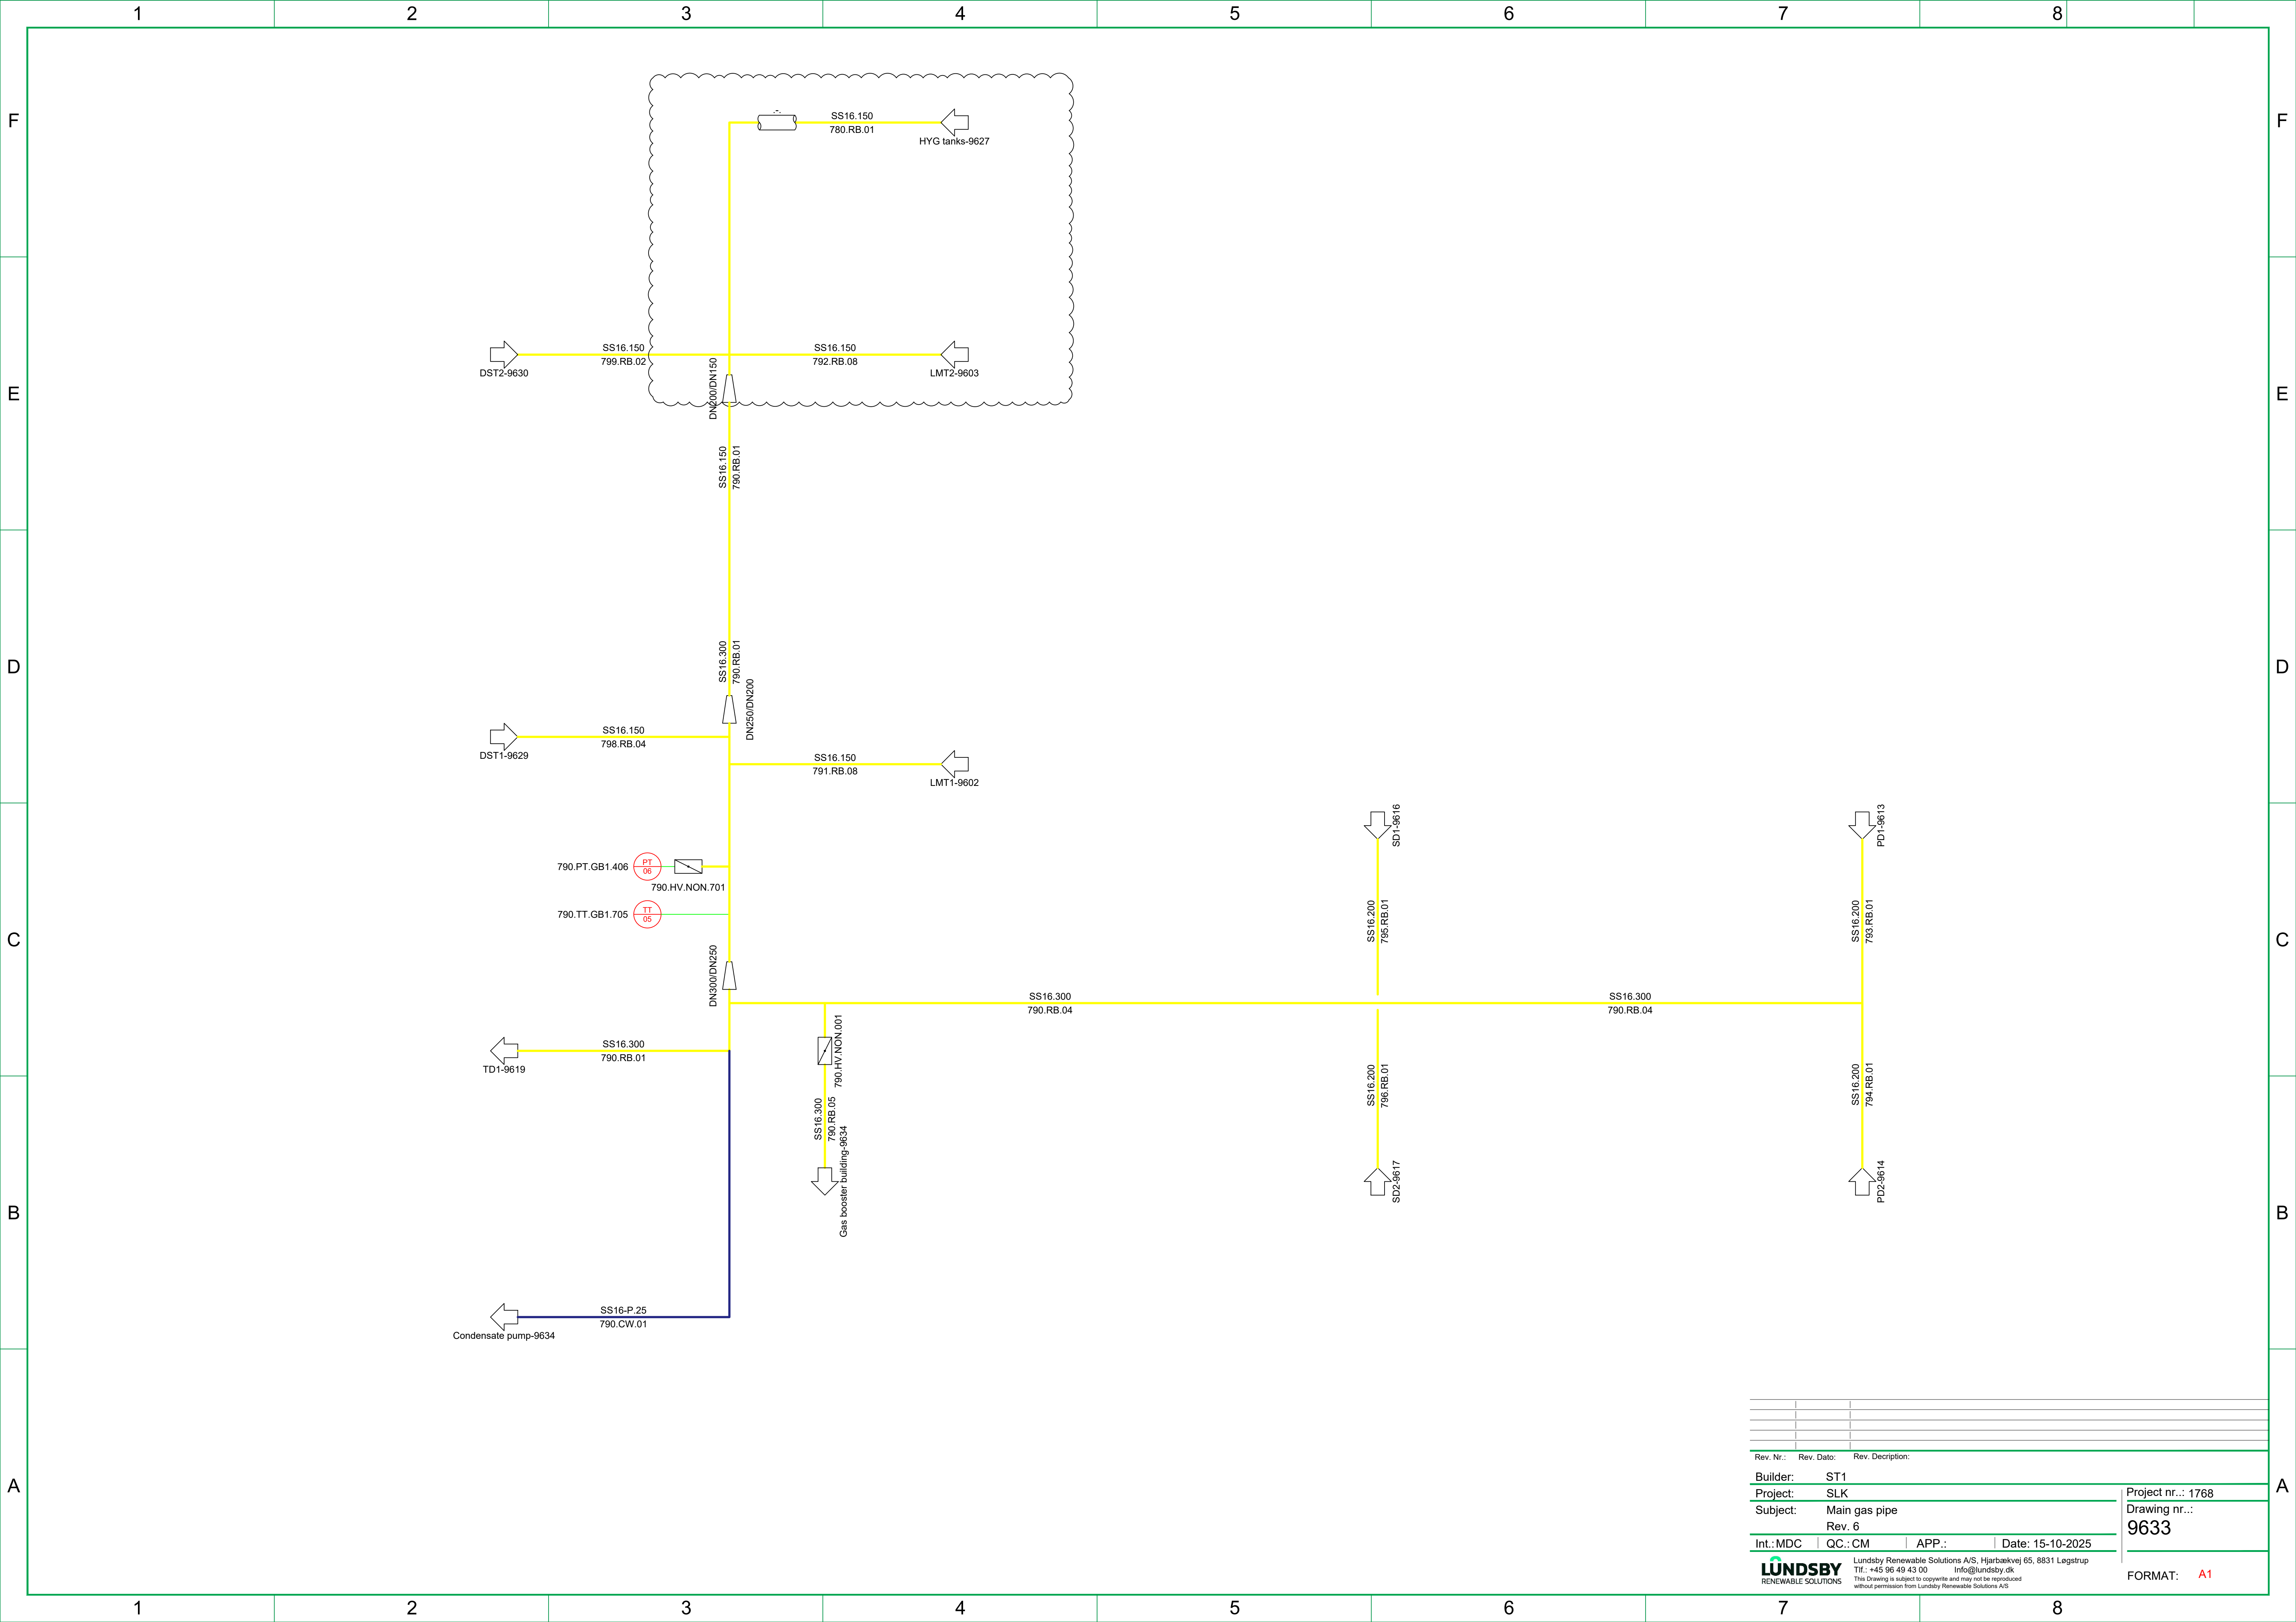


Rev. Nr.:	Rev. Dato:	Rev. Description:	
Builder:	ST1		
Project:	SLK		
Subject:	Main gas pipe		
Rev. 6			
Int.:MDC	QC.:CM	APP.:	Date: 15-10-2025
LUNDSBY RENEWABLE SOLUTIONS			Lundsgby Renewable Solutions A/S, Hjarbrækvej 65, 8831 Løgstrup Tlf.: +45 96 49 43 00 Info@lundsgby.dk This Drawing is subject to copyright and may not be reproduced without permission from Lundsgby Renewable Solutions A/S
Project nr.: 1768 Drawing nr.: 9633			FORMAT: A1

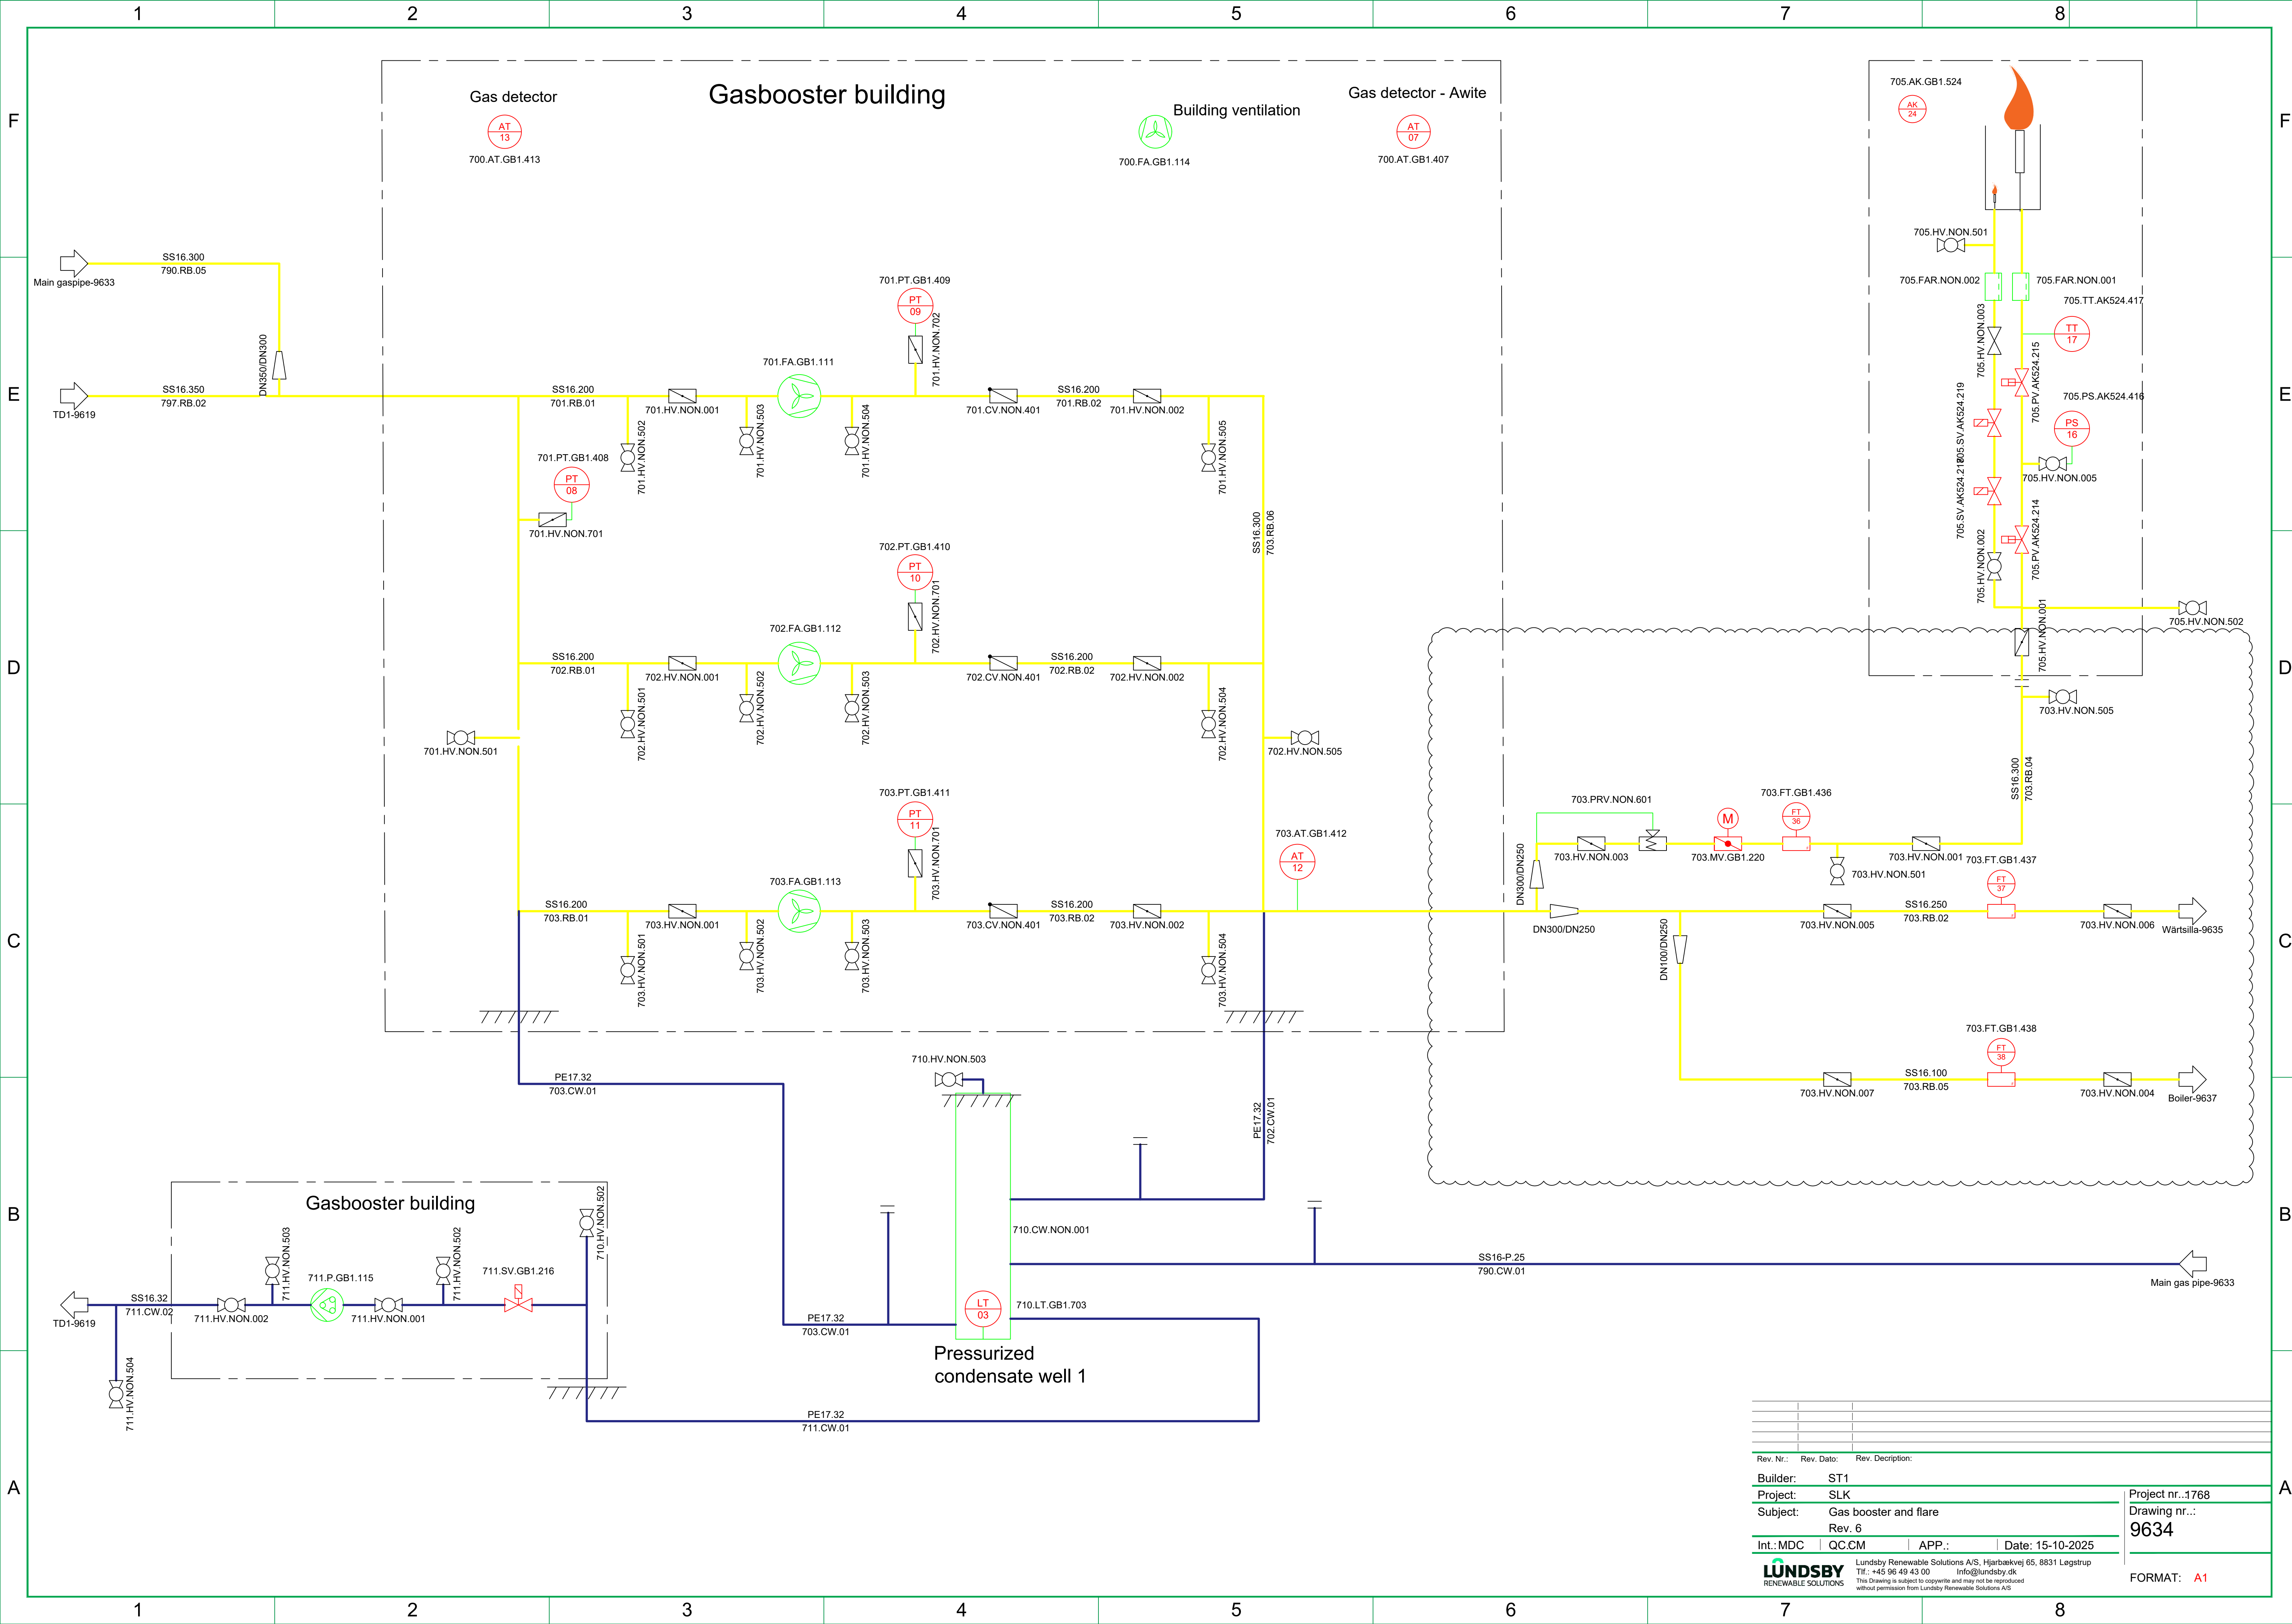

Wärtsillä

730-UPG-01


730-LBG-01

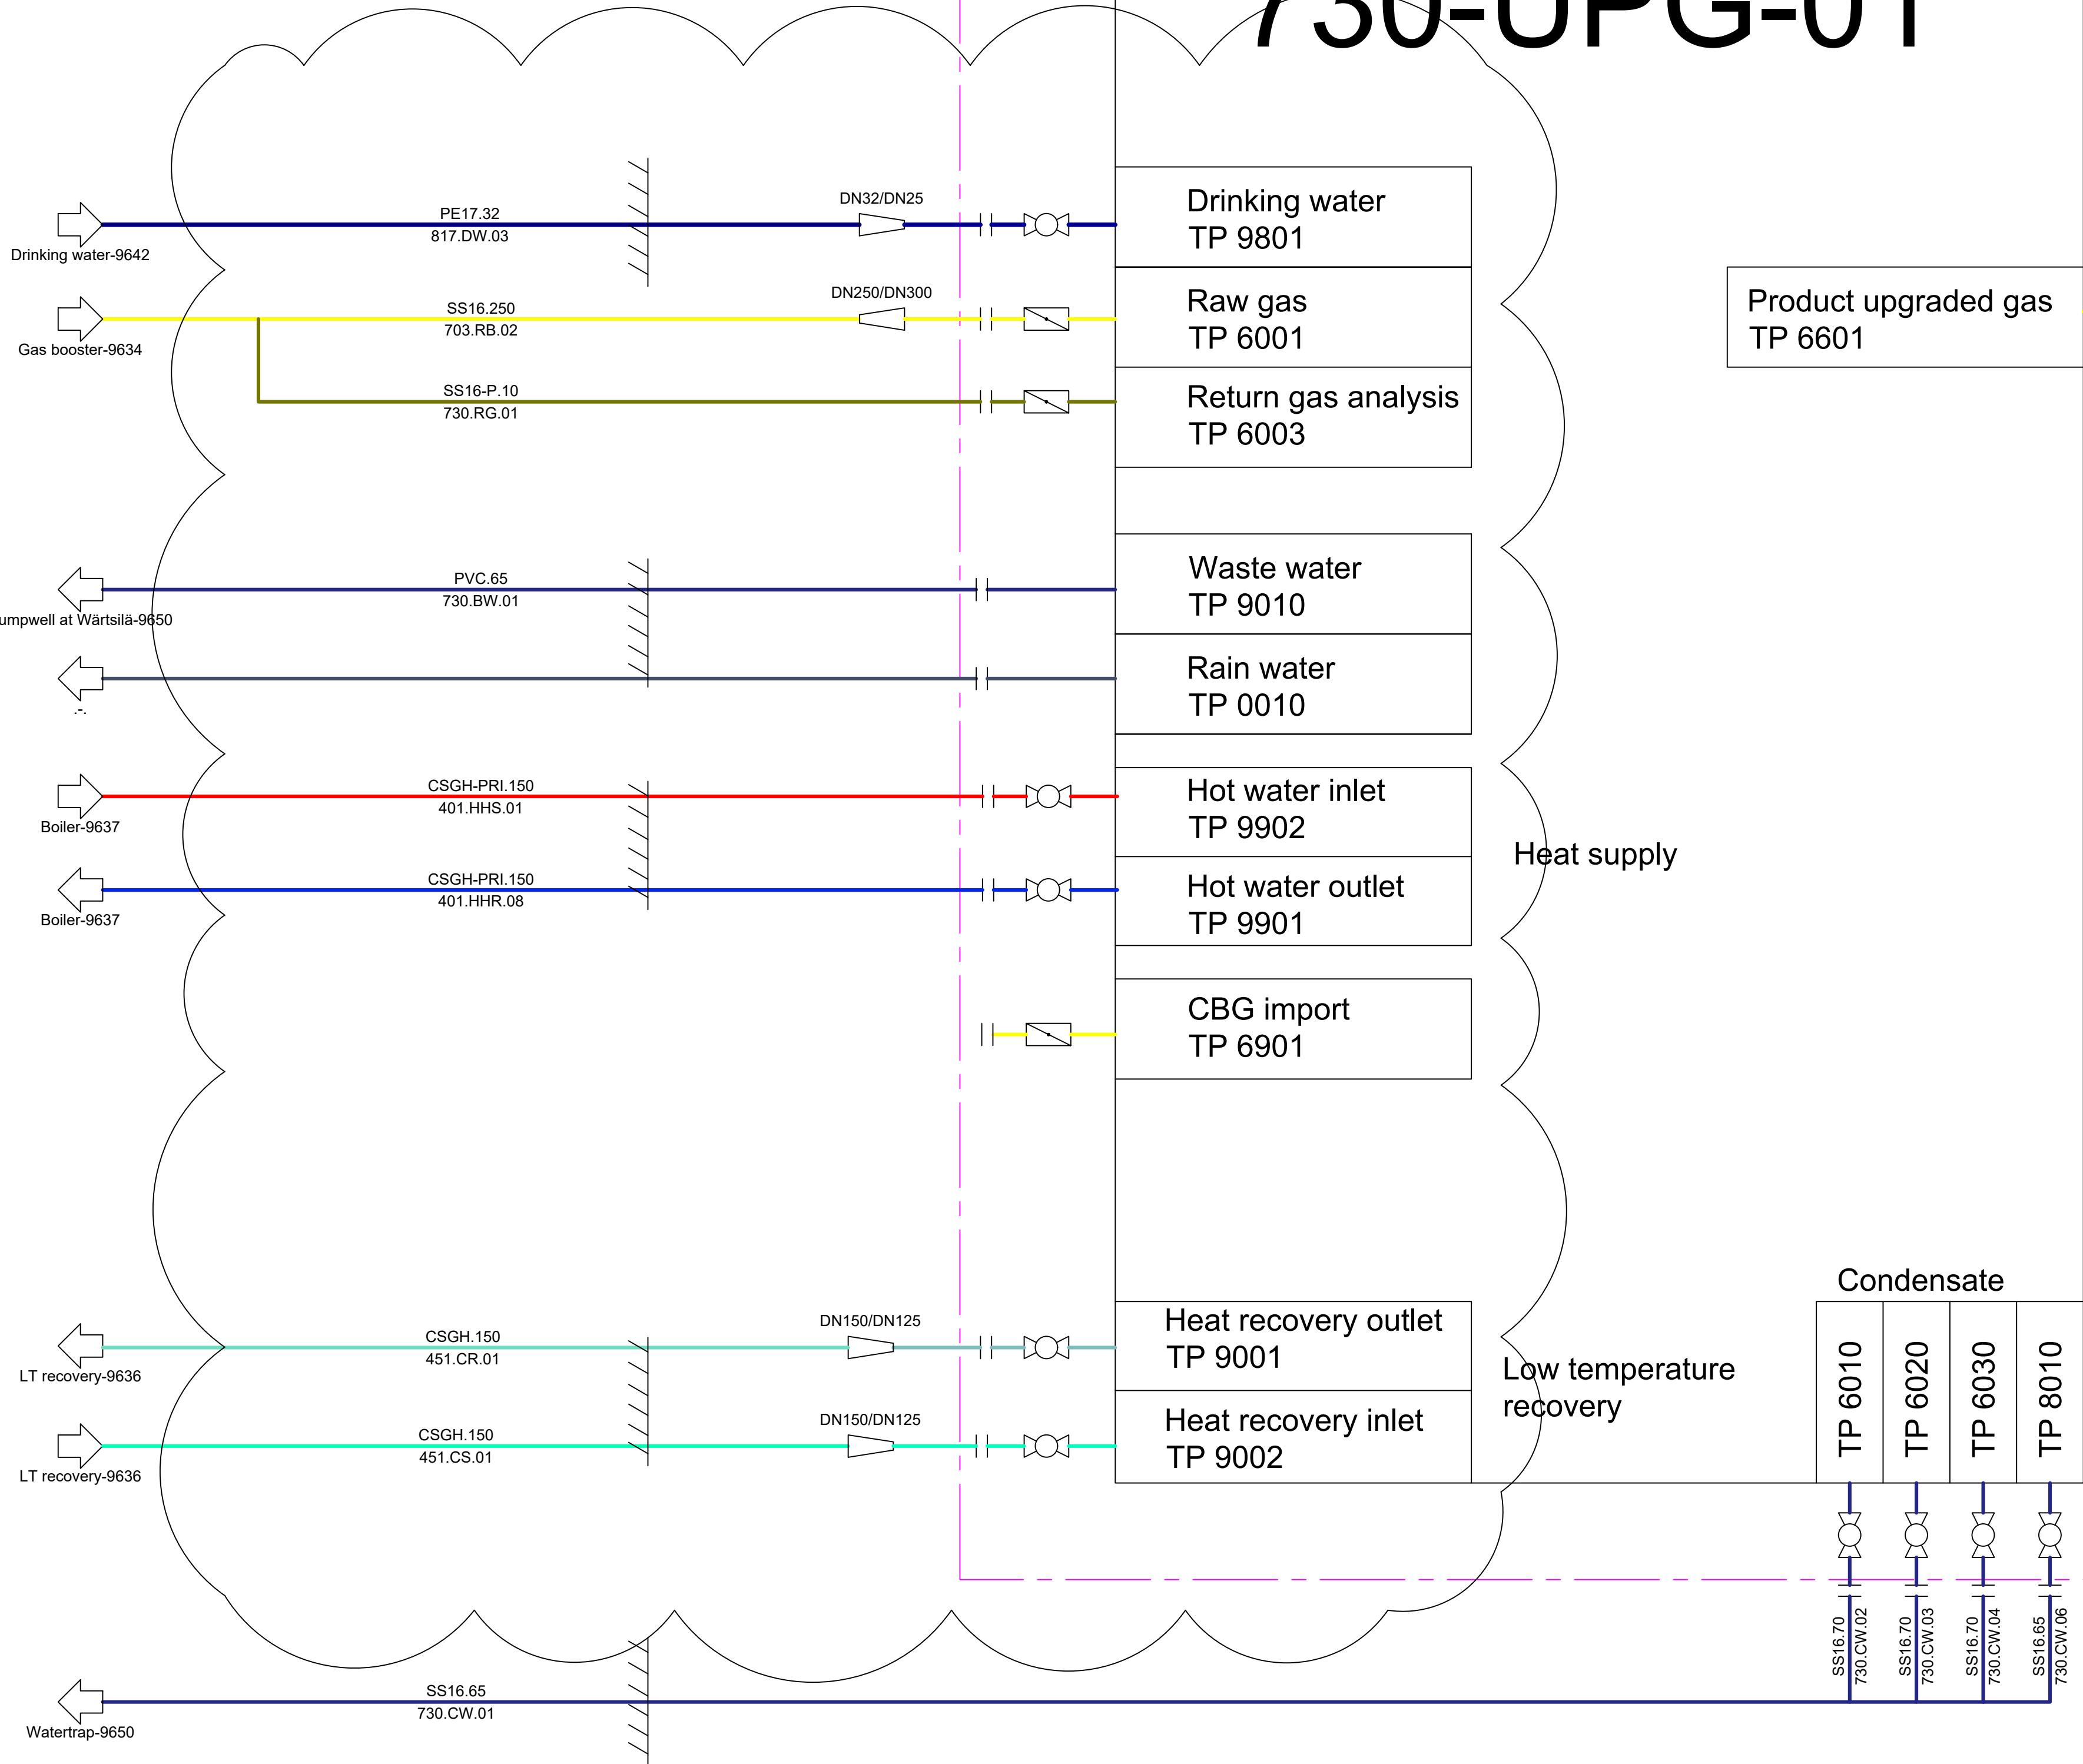

AK
22
730.AK.T4.522

AK
23
730.AK.T5.523


Product upgraded gas
TP 6601

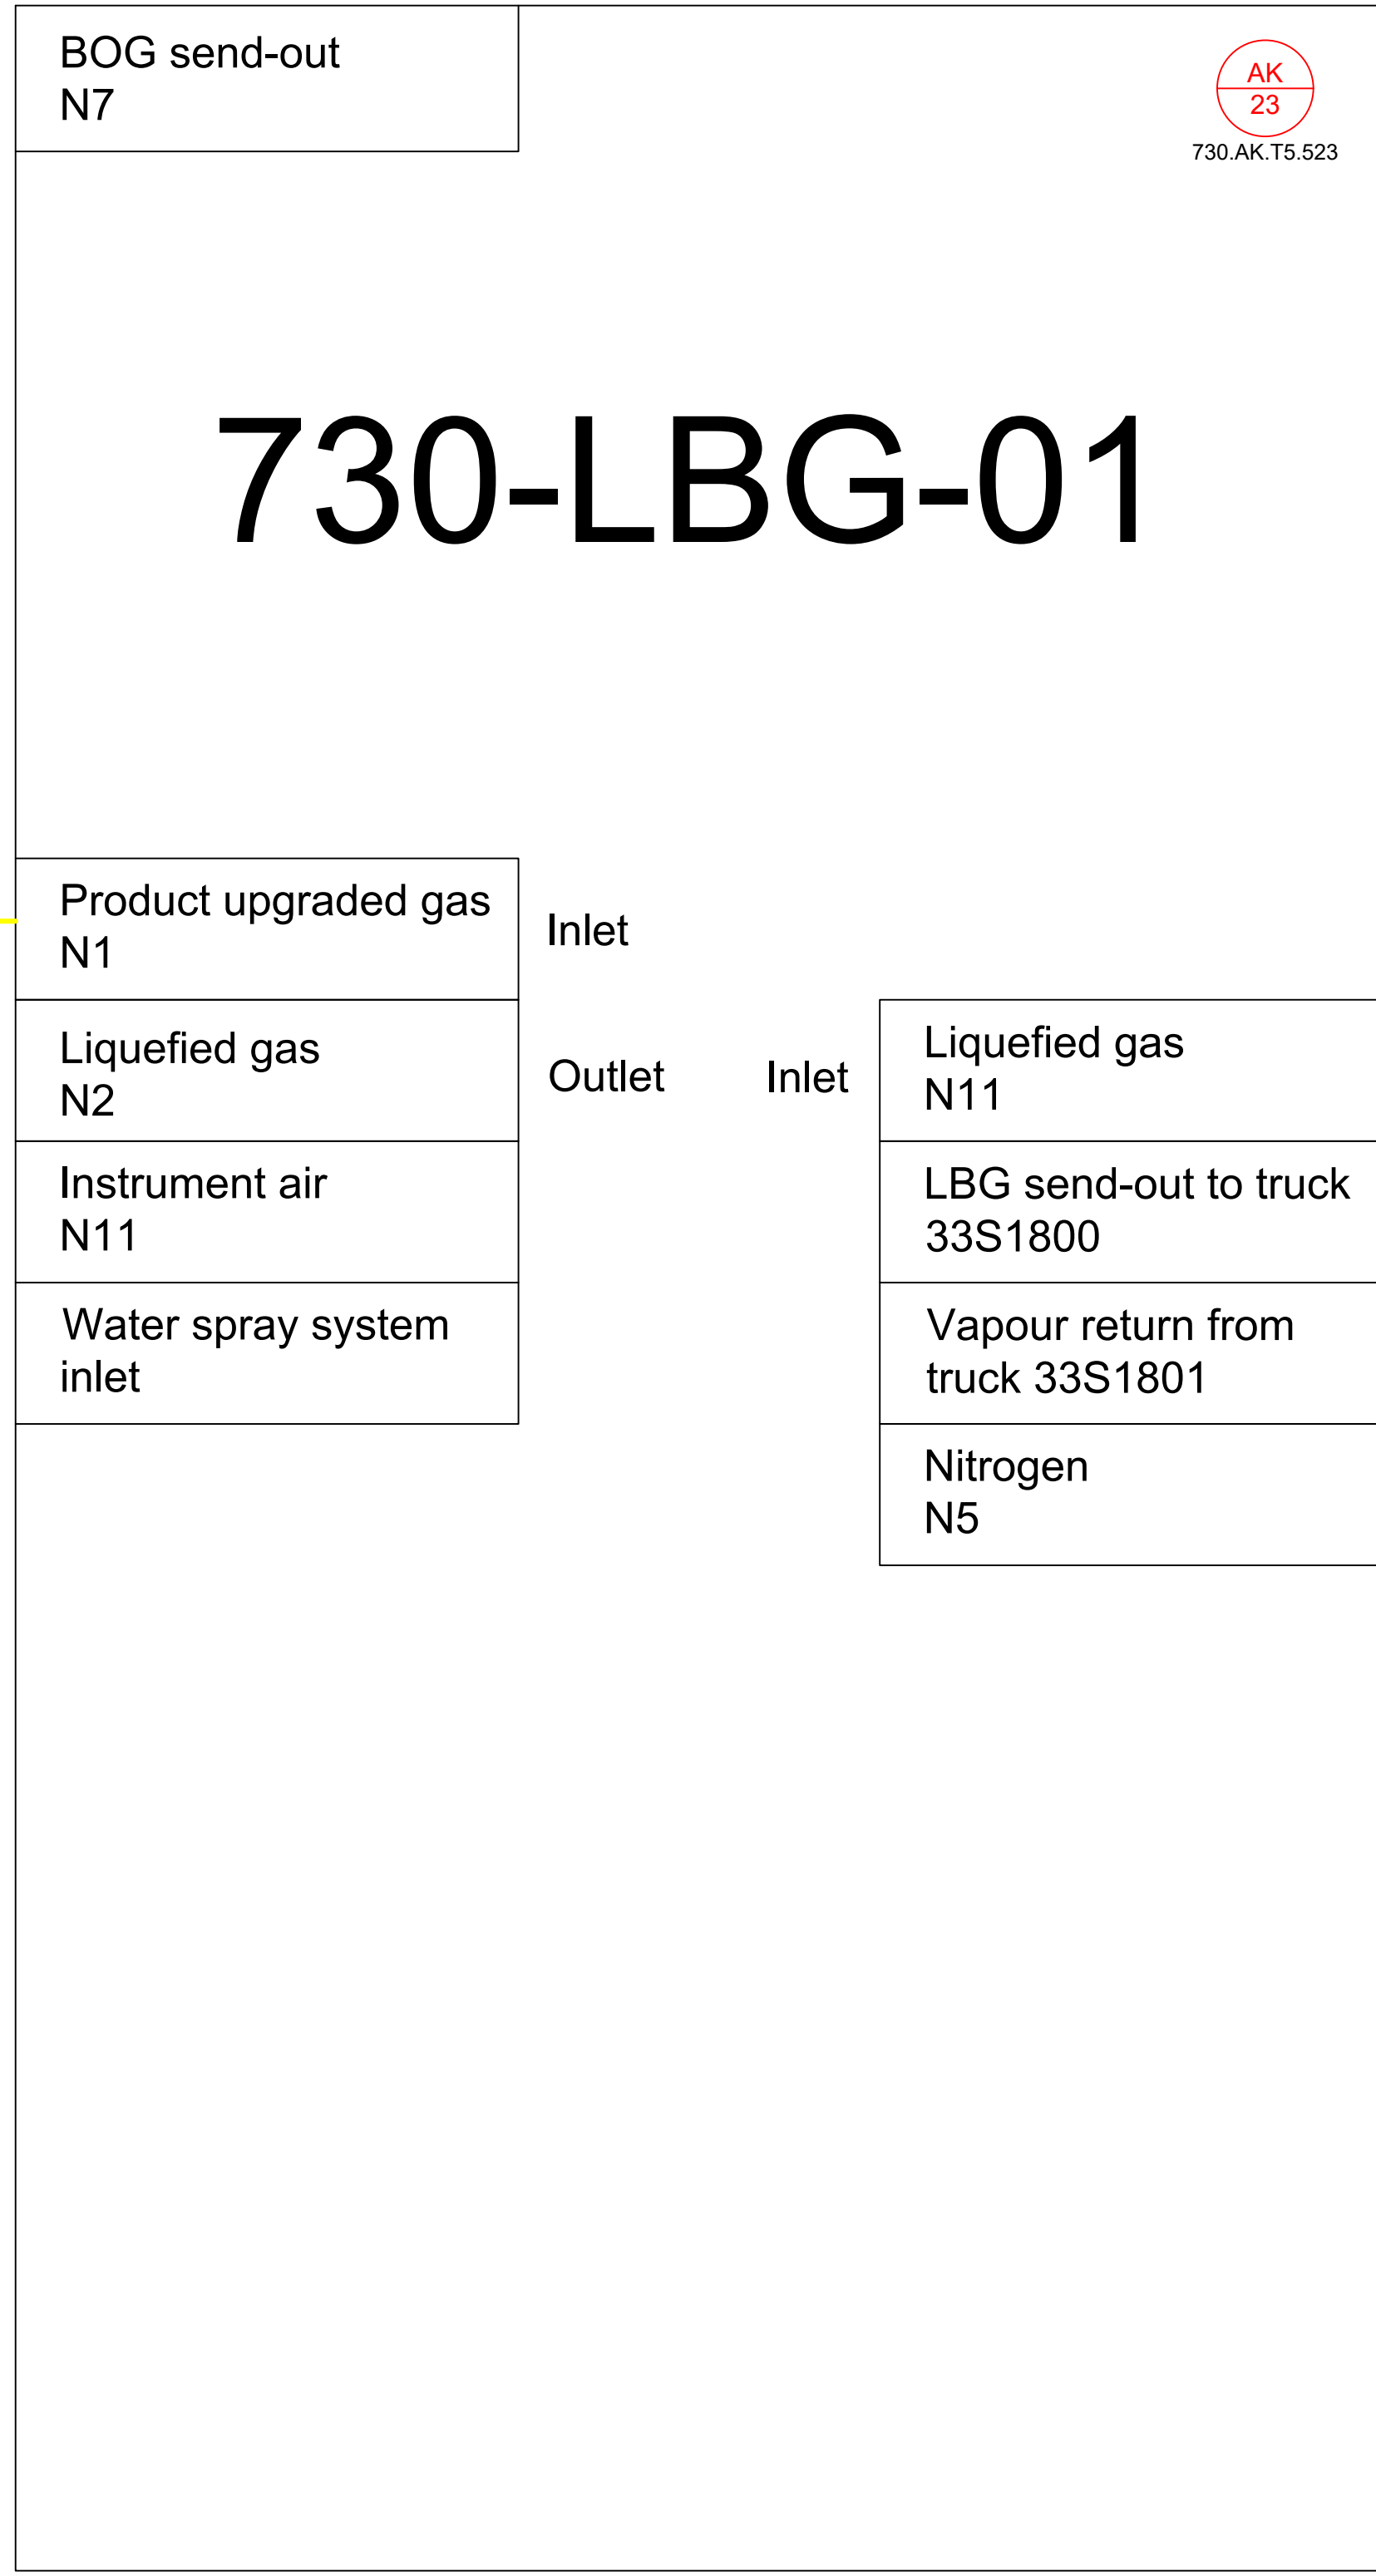


Rev. Nr.:	Rev. Dato:	Rev. Description:
Builder:	ST1	
Project:	SLK	
Subject:	Upgrade	
	Rev. 6	
Int.:MDC	QC.CM	APP.:
		Date: 15-10-2025
LUNDSBY RENEWABLE SOLUTIONS		
Lundby Renewable Solutions A/S, Hjarbækvej 65, 8831 Løgstrup Tlf.: +45 96 49 43 00 Info@lundby.dk This Drawing is subject to copyright and may not be reproduced without permission from Lundby Renewable Solutions A/S		
Project nr...:1768 Drawing nr...: 9635		FORMAT: A1

Technology building

Heat pump scope

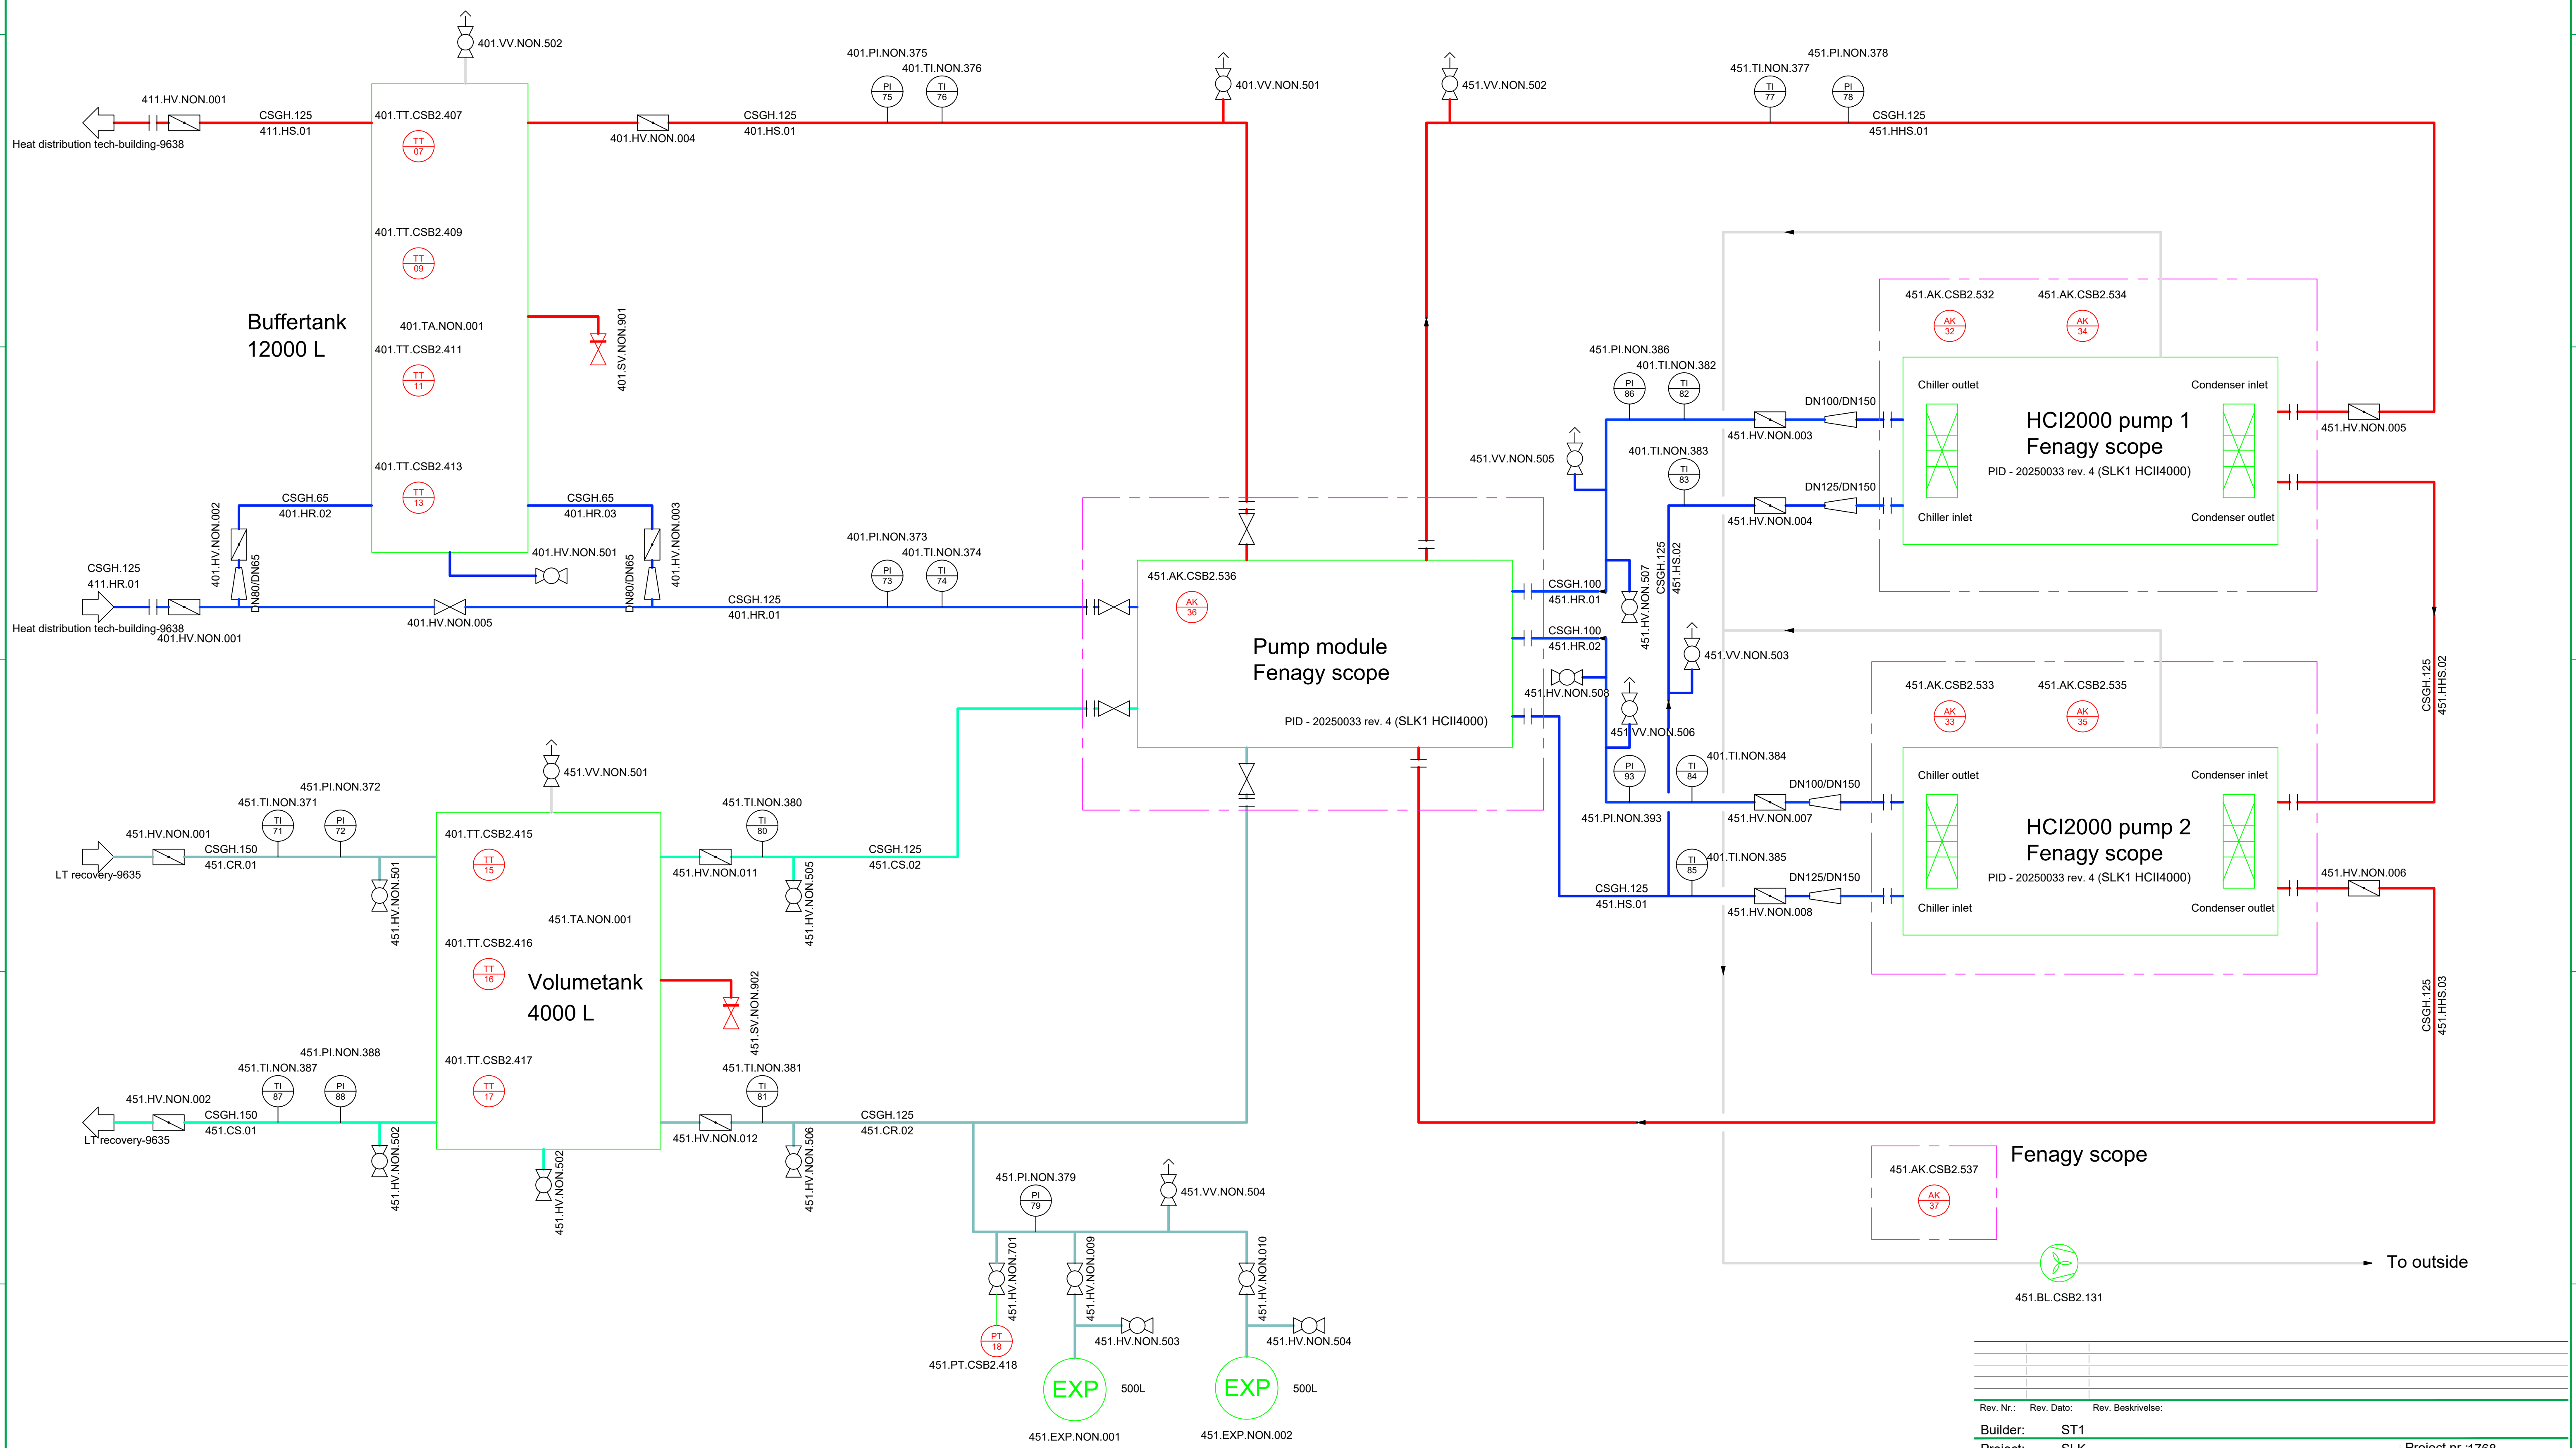

Rev. Nr.:	Rev. Dato:	Rev. Beskrivelse:	
Builder:	ST1		
Project:	SLK		
Subject:	Heat pumps		
Rev.:	6		
Int.:MDC	QC: CM	APP.:	Date: 15-10-2025
LUNDSBY RENEWABLE SOLUTIONS			Lundsby Biogas A/S, Hjarbækvej 65, 8831 Løgstrup Tlf.: +45 96 49 43 00 info@lundsbybiogas.dk Denne tegning er underlagt copyright og må ikke reproduceres uden tilladelse fra Lundsbybiogas A/S
Project nr.:1768 Drawing nr.: 9636			FORMAT: A1

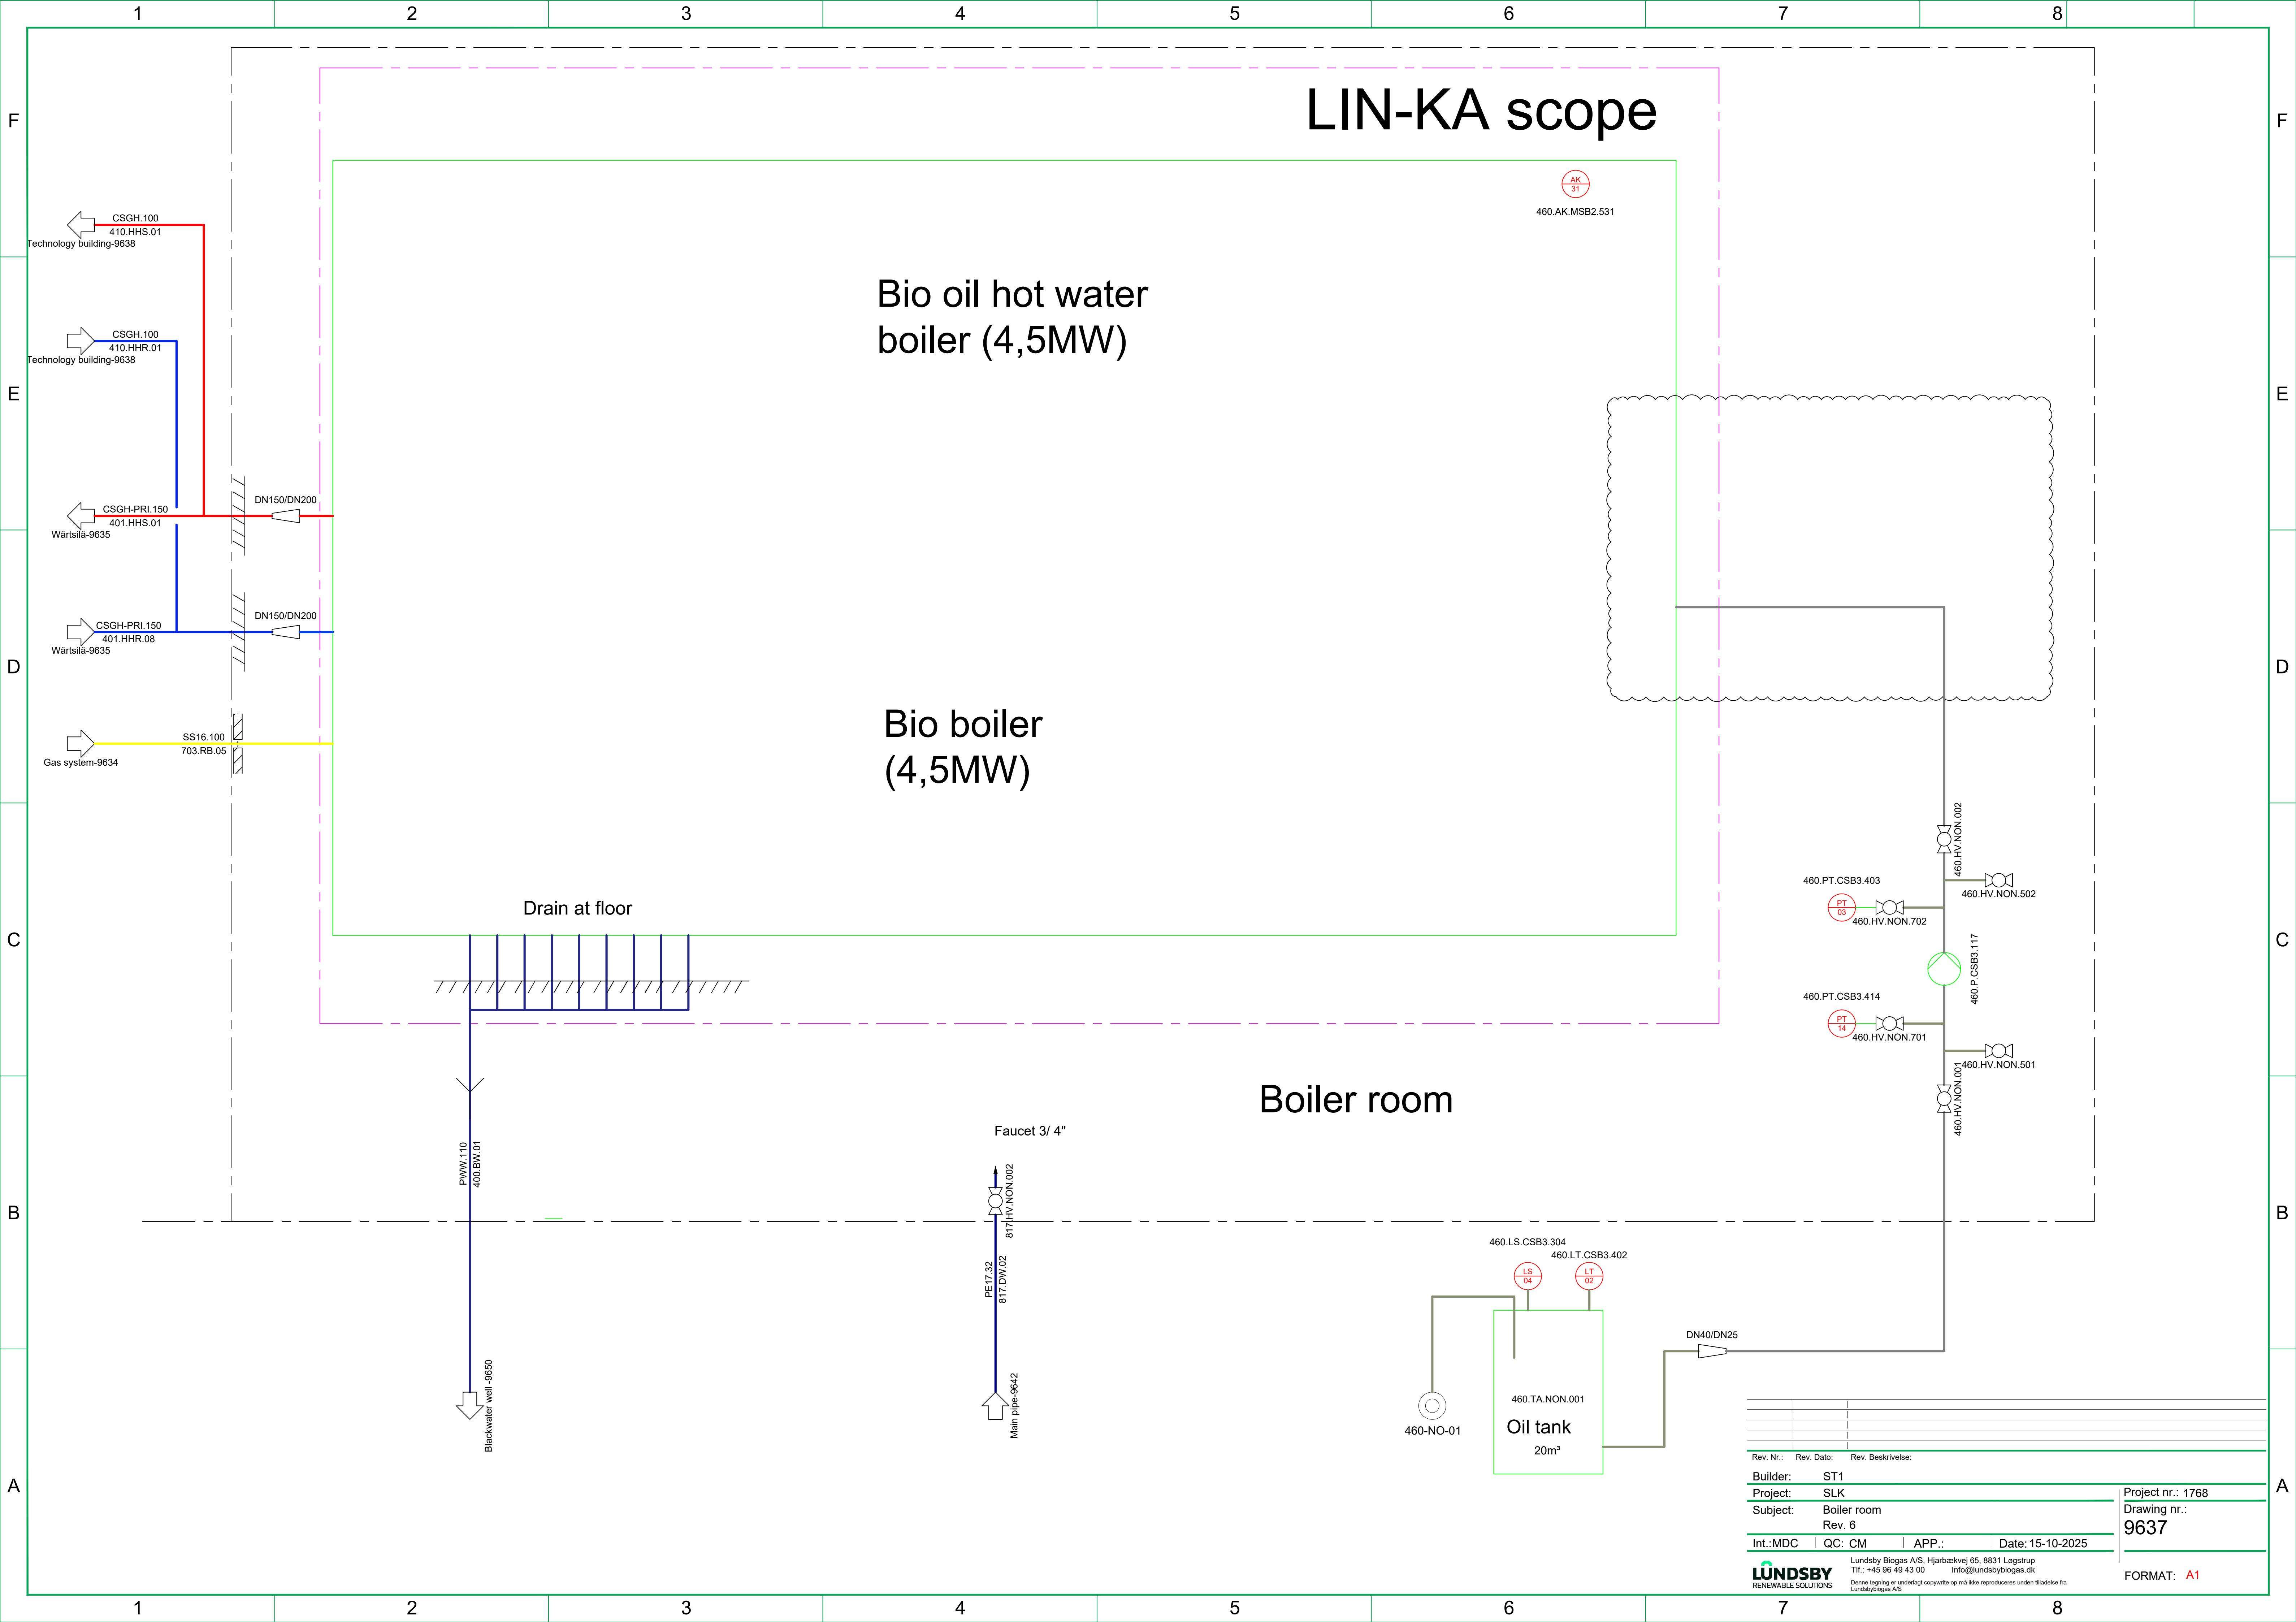

LIN-KA scope

Bio oil hot water boiler (4,5MW)

Bio boiler (4,5MW)

Boiler room

AK 31
460.AK.MSB2.531

CSGH.100
410.HHS.01
Technology building-9638

CSGH.100
410.HHR.01
Technology building-9638

CSGH-PRI.150
401.HHS.01
Wartsila-9635

CSGH-PRI.150
401.HHR.08
Wartsila-9635

SS16.100
703.RB.05
Gas system-9634

Drain at floor

PWW.110
400.BW.01
Blackwater well -9650

Faucet 3/ 4"

PE17.32
817.DW.02
Main pipe-9642

460.LS.CSB3.304
460.LT.CSB3.402

460.TA.NON.001
Oil tank
20m³

460-NO-01

460.HV.NON.002

460.PT.CSB3.403
460.HV.NON.702


460.PT.CSB3.414
460.HV.NON.701

460.HV.NON.502

460.P.CSB3.117

460.HV.NON.501

Rev. Nr.:	Rev. Dato:	Rev. Beskrivelse:
Builder:	ST1	
Project:	SLK	
Subject:	Boiler room	
Rev. 6		
Int.:MDC	QC: CM	APP.: Date: 15-10-2025
LUNDSBY RENEWABLE SOLUTIONS		
Lundsby Biogas A/S, Hjarbækvej 65, 8831 Løgstrup Tlf.: +45 96 49 43 00 Info@lundsbybiogas.dk		
Denne tegning er underlagt copywrite op på ikke reproduceres uden tilladelse fra Lundsbybiogas A/S		
Project nr.: 1768		Drawing nr.: 9637
FORMAT: A1		

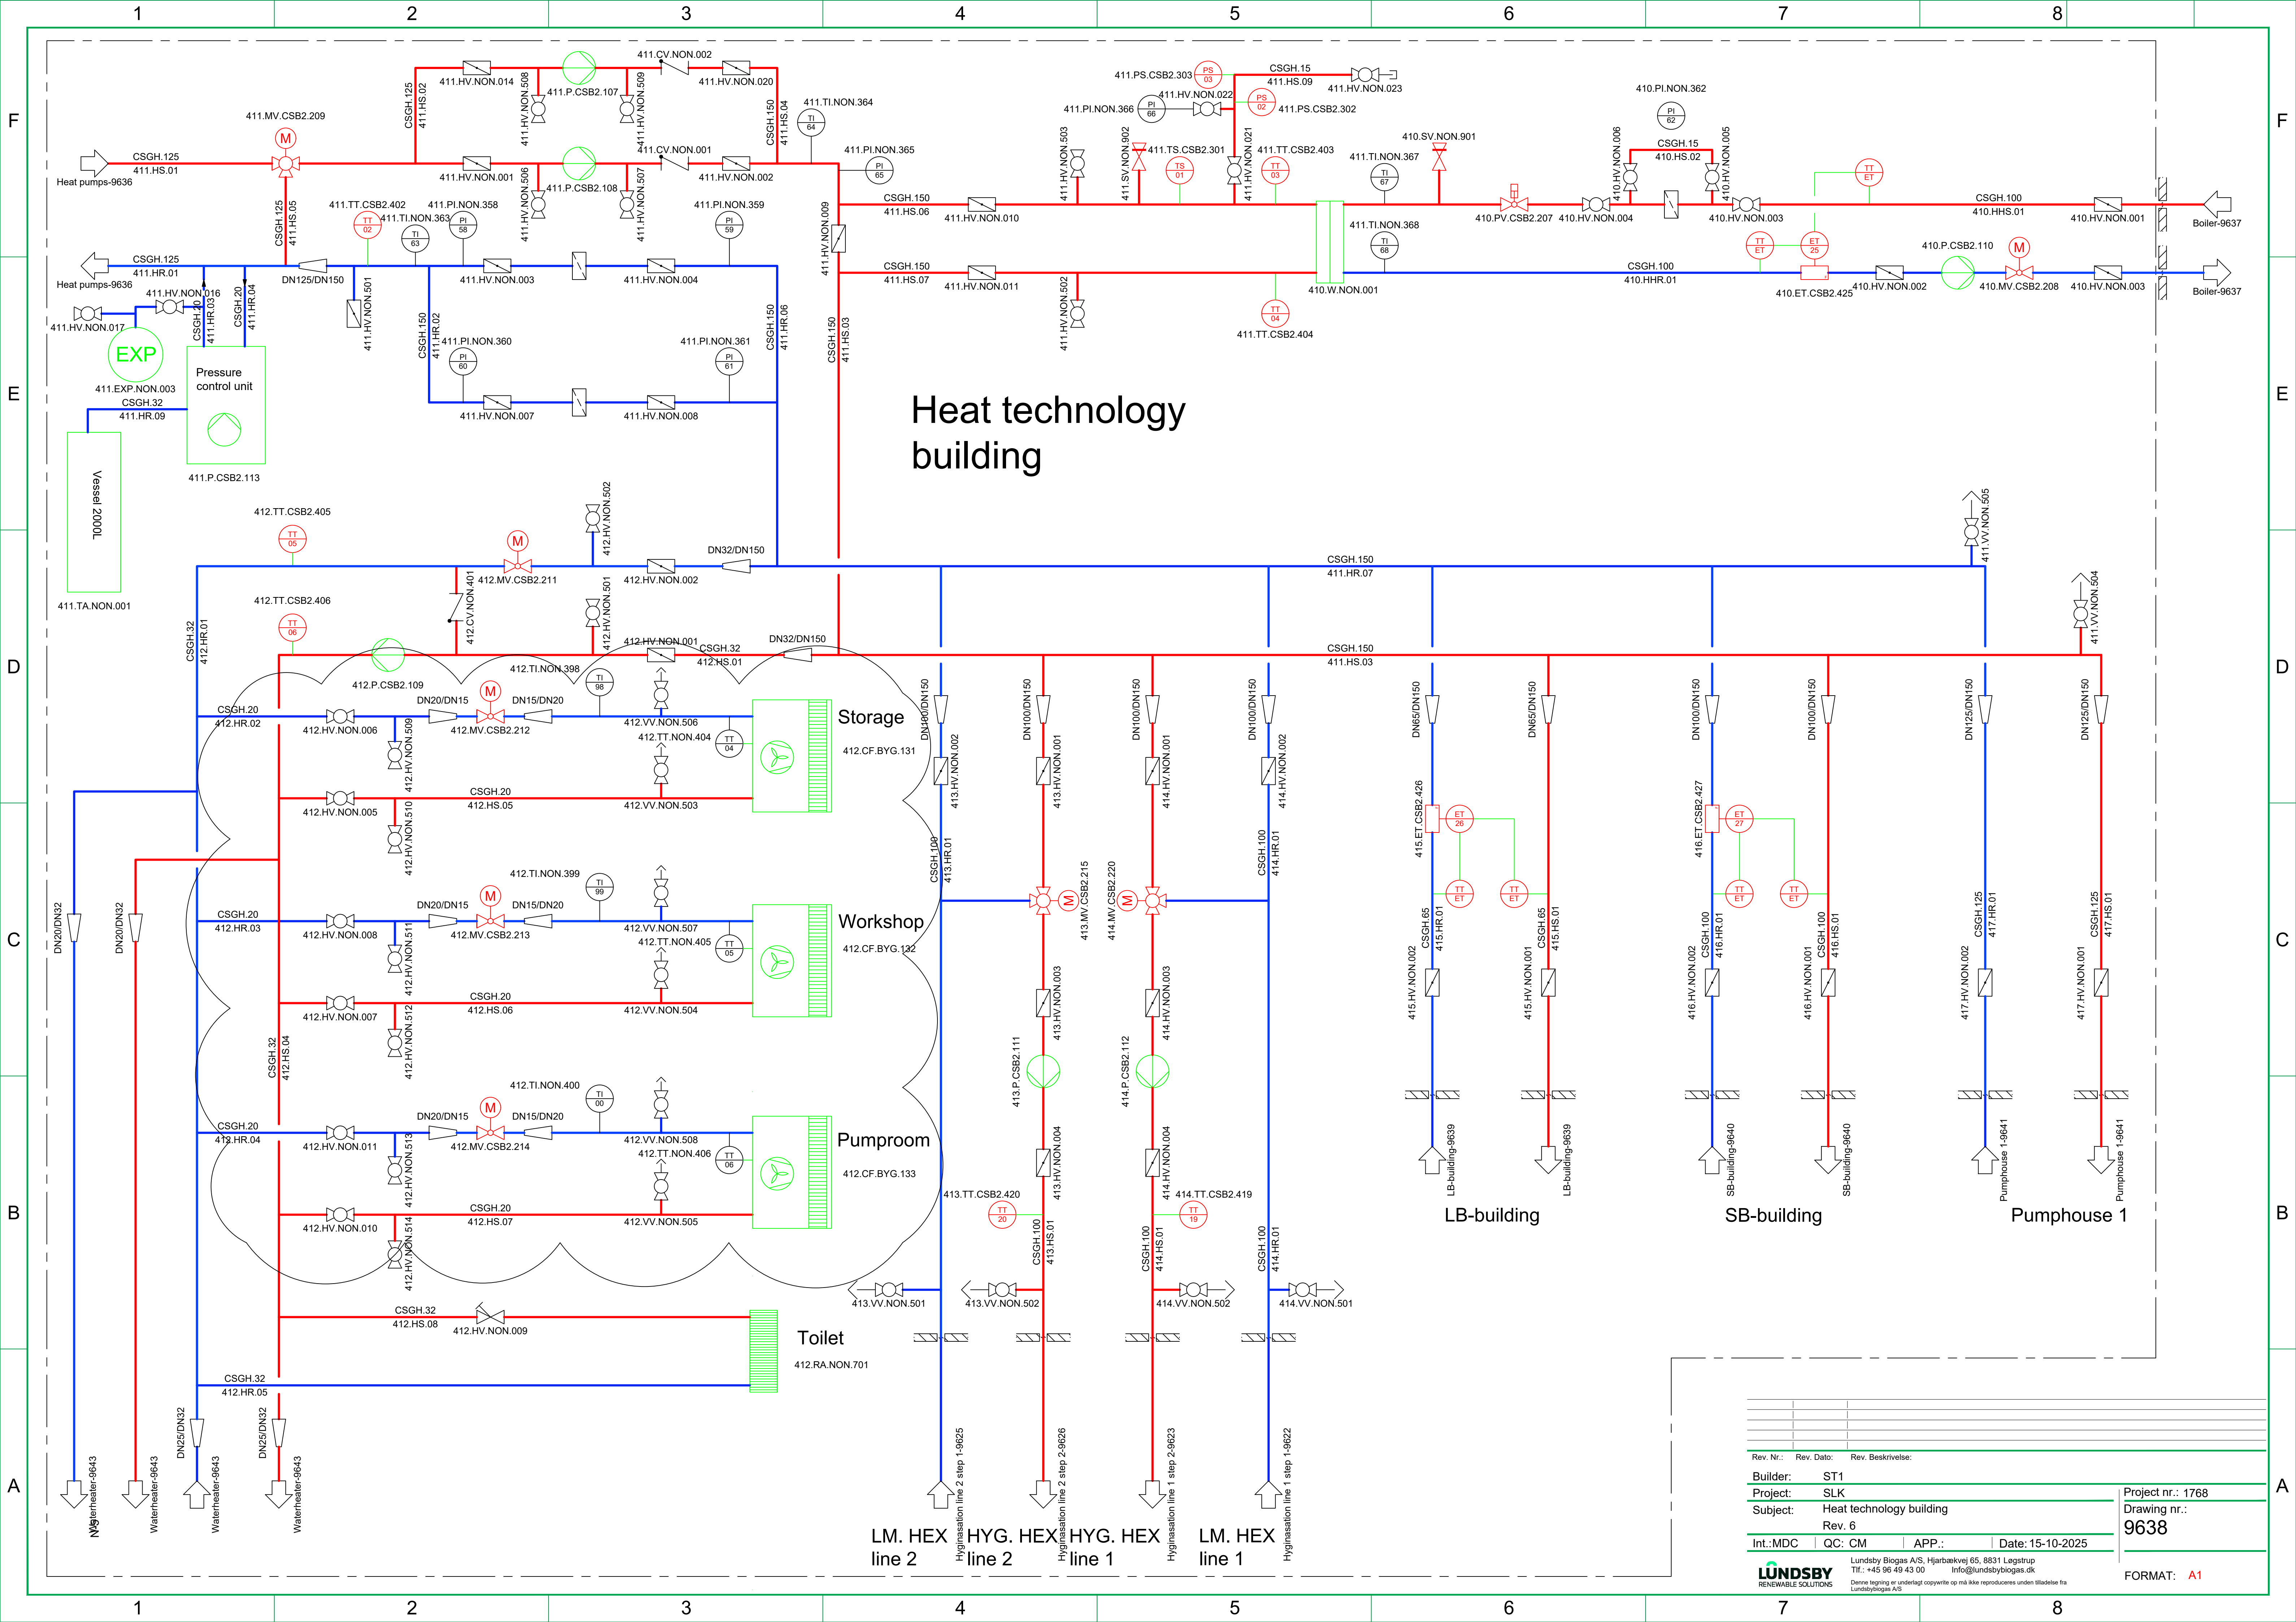

Heat technology building

Storage

Workshop

Pumproom

Toilet


LB-building

SB-building

Pumphouse 1


Rev. Nr.:	Rev. Dato:	Rev. Beskrivelse:
Builder:	ST1	
Project:	SLK	
Subject:	Heat technology building	
Rev. 6		
Int.:MDC	QC: CM	APP.: Date: 15-10-2025
LUNDSBY RENEWABLE SOLUTIONS		
Lundsby Biogas A/S, Hjarbækvej 65, 8831 Løgstrup Tlf.: +45 96 49 43 00 info@lundsbybiogas.dk		
Denne tegning er underlagt copyright og må ikke reproduceres uden tilladelse fra Lundsbybiogas A/S		
Project nr.: 1768		FORMAT: A1
Drawing nr.: 9638		

LB-Building

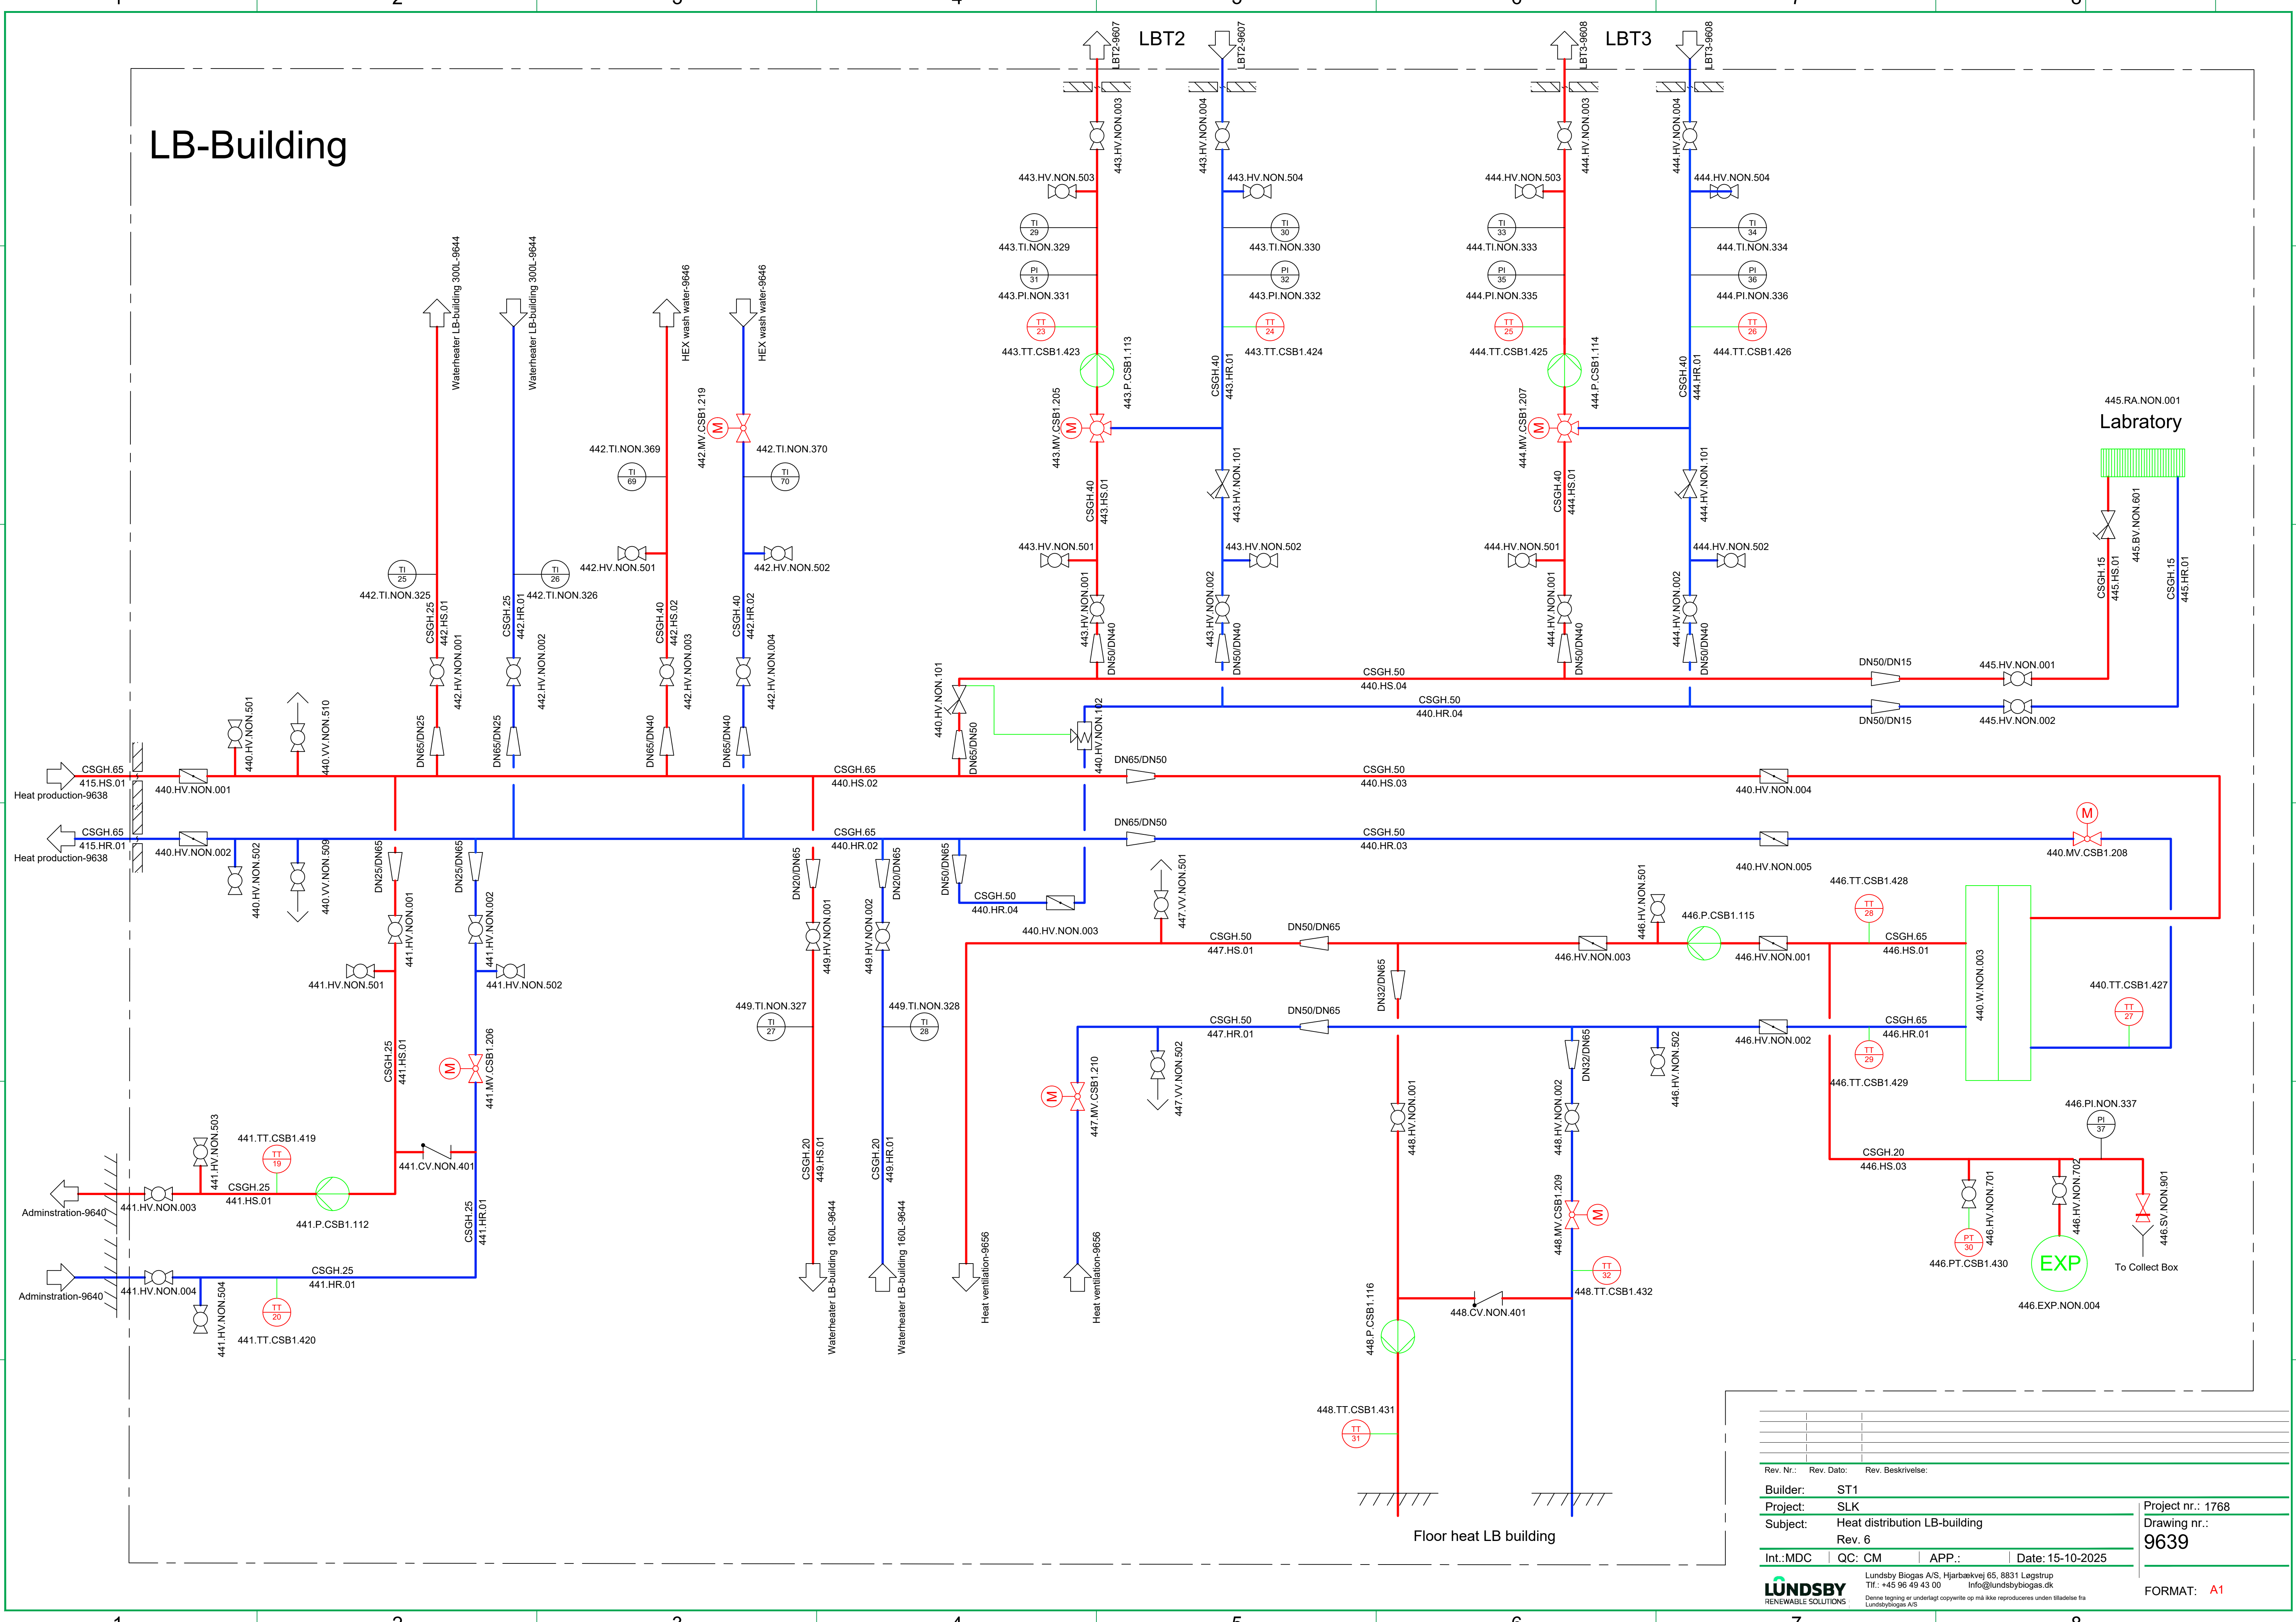


Rev. Nr.:	Rev. Dato:	Rev. Beskrivelse:
Builder:	ST1	
Project:	SLK	
Subject:	Heat distribution LB-building	
Rev. 6		
Int.:MDC	QC: CM	APP.: Date: 15-10-2025
LUNDSBY RENEWABLE SOLUTIONS		
Lundsby Biogas A/S, Hjarbækvej 65, 8831 Løgstrup Tlf.: +45 96 49 43 00 info@lundsbybiogas.dk		
Denne tegning er underlagt copyright og må ikke reproduceres uden tilladelse fra Lundsbybiogas A/S		
Project nr.: 1768		Drawing nr.: 9639
FORMAT: A1		

SB-Building

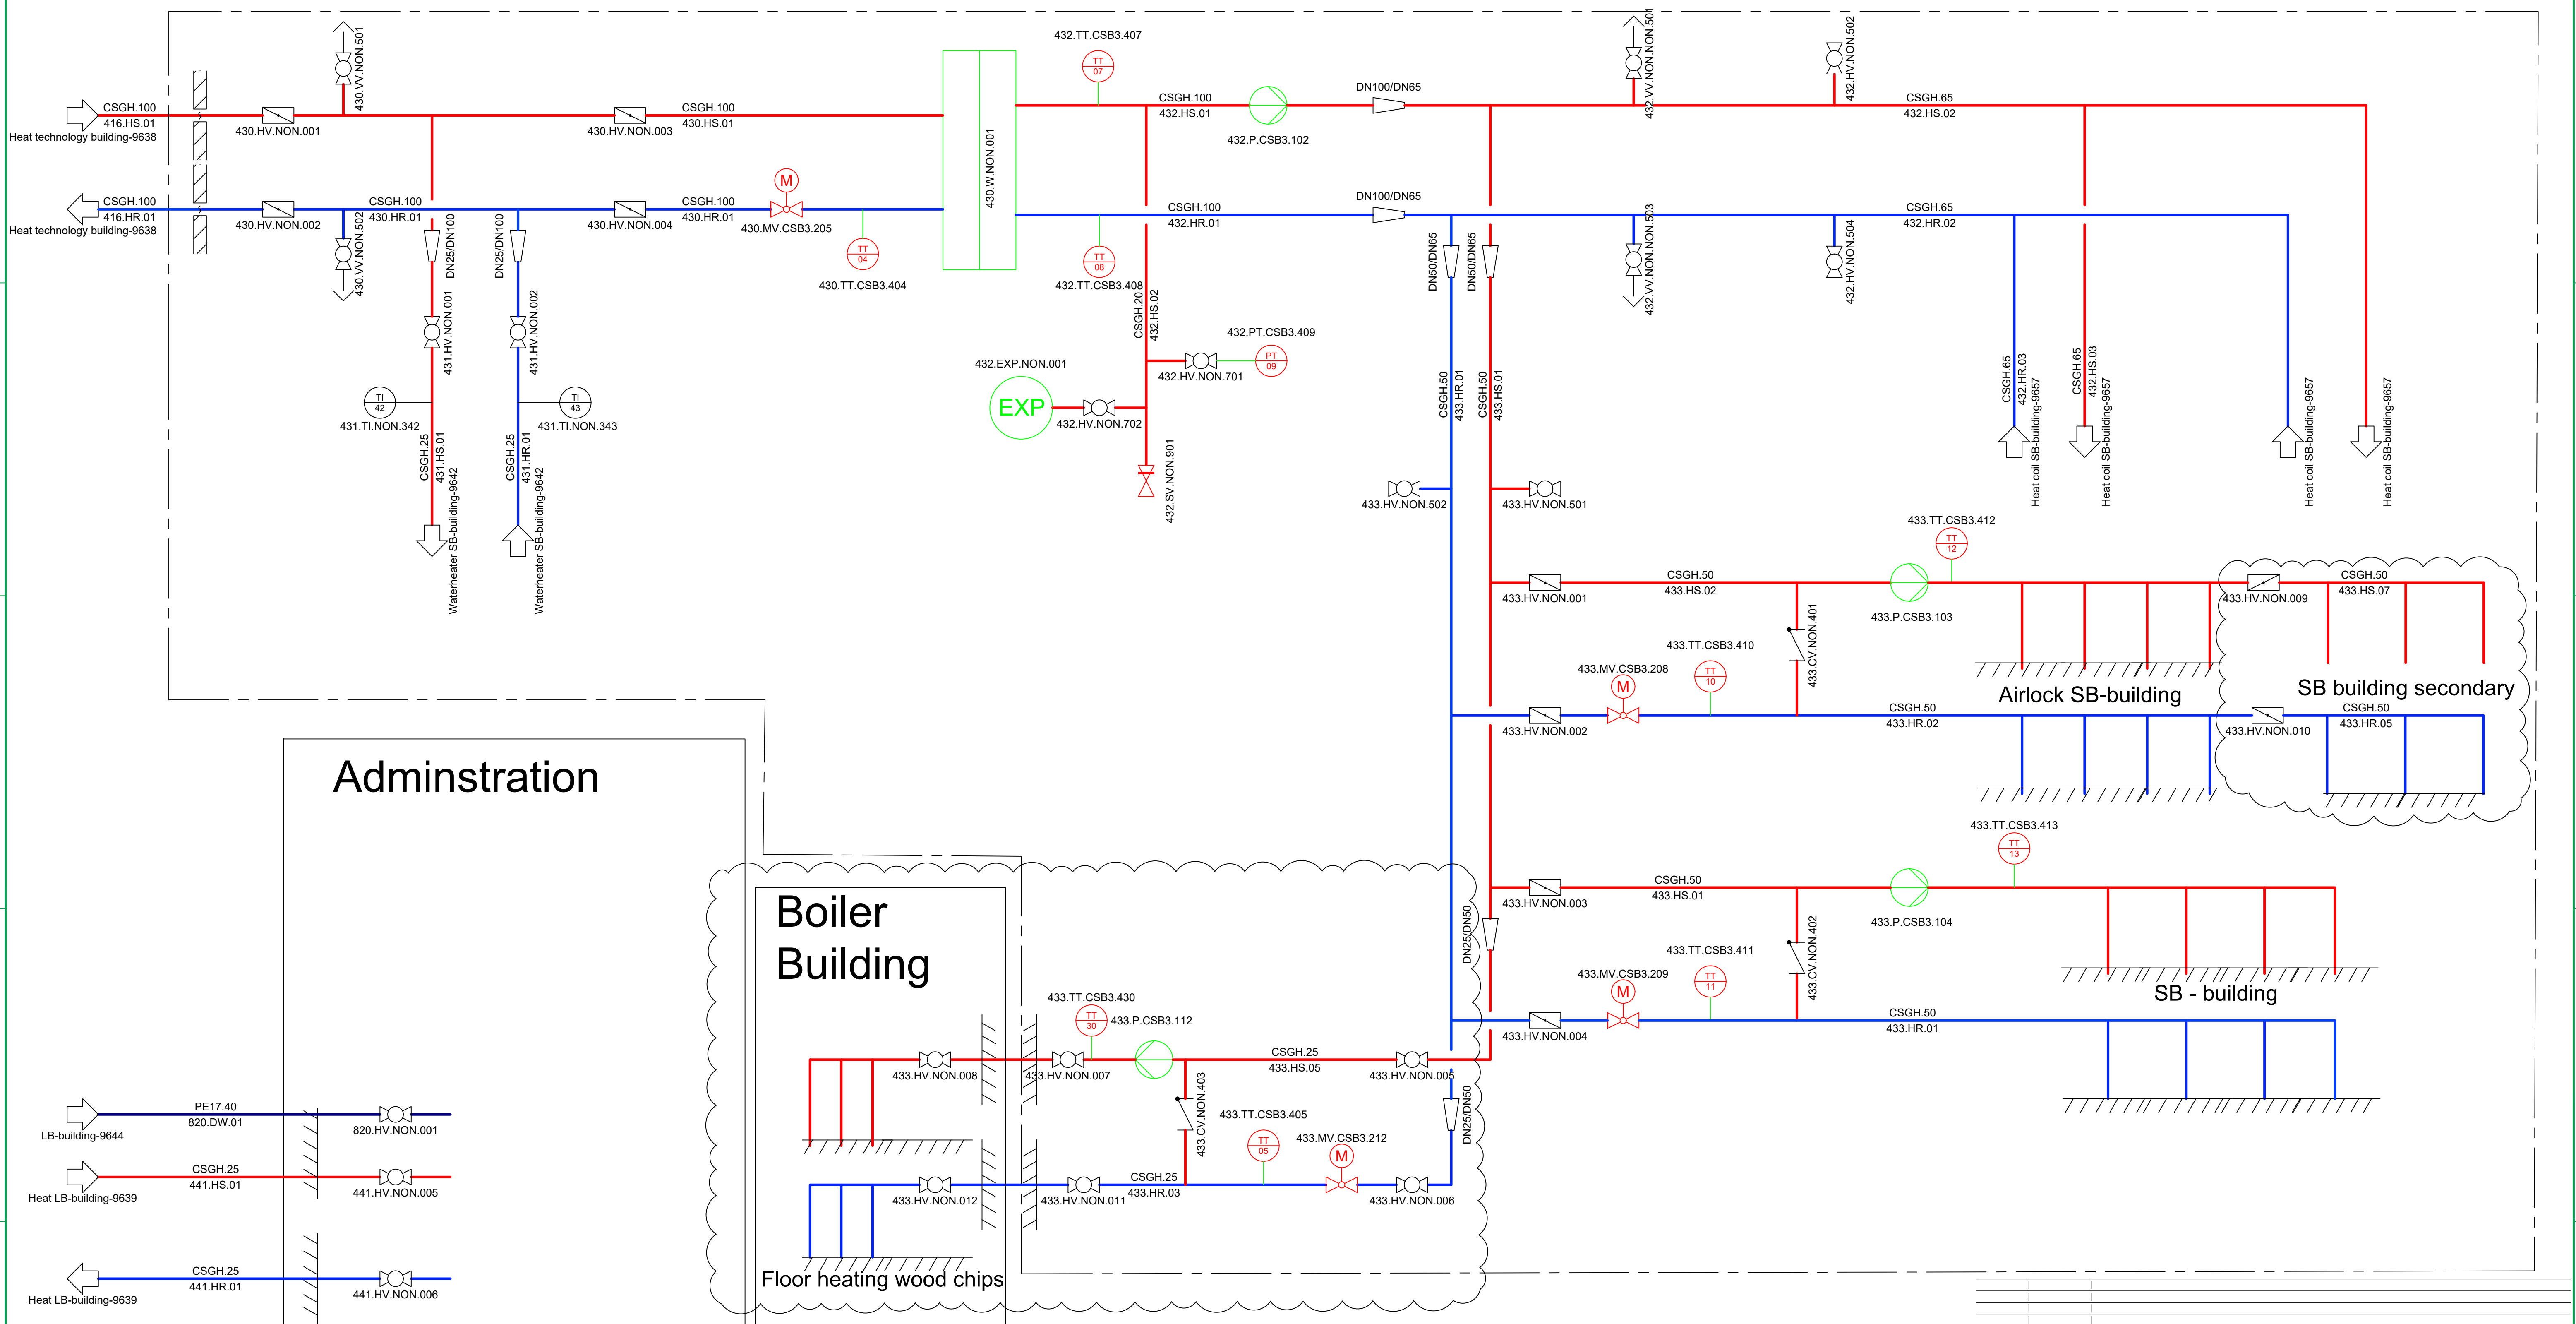

Rev. Nr.:		Rev. Dato:		Rev. Beskrivelse:	
Builder:		ST1			
Project:		SLK			
Subject:		Heat distribution SB-building			
		Rev. 6			
Int.:MDC		QC: CM	APP.:	Date: 15-10-2025	
		Lundsby Biogas A/S, Hjarbækvej 65, 8831 Legstrup Tlf.: +45 96 49 43 00 Info@lundsbybiogas.dk Denne tegning er udelagt copyretet på må ikke reproduceres under titillade fra Lundsby Biogas			
		Project nr.:		1768	
		Drawing nr.:		9640	
		FORMAT:		A1	

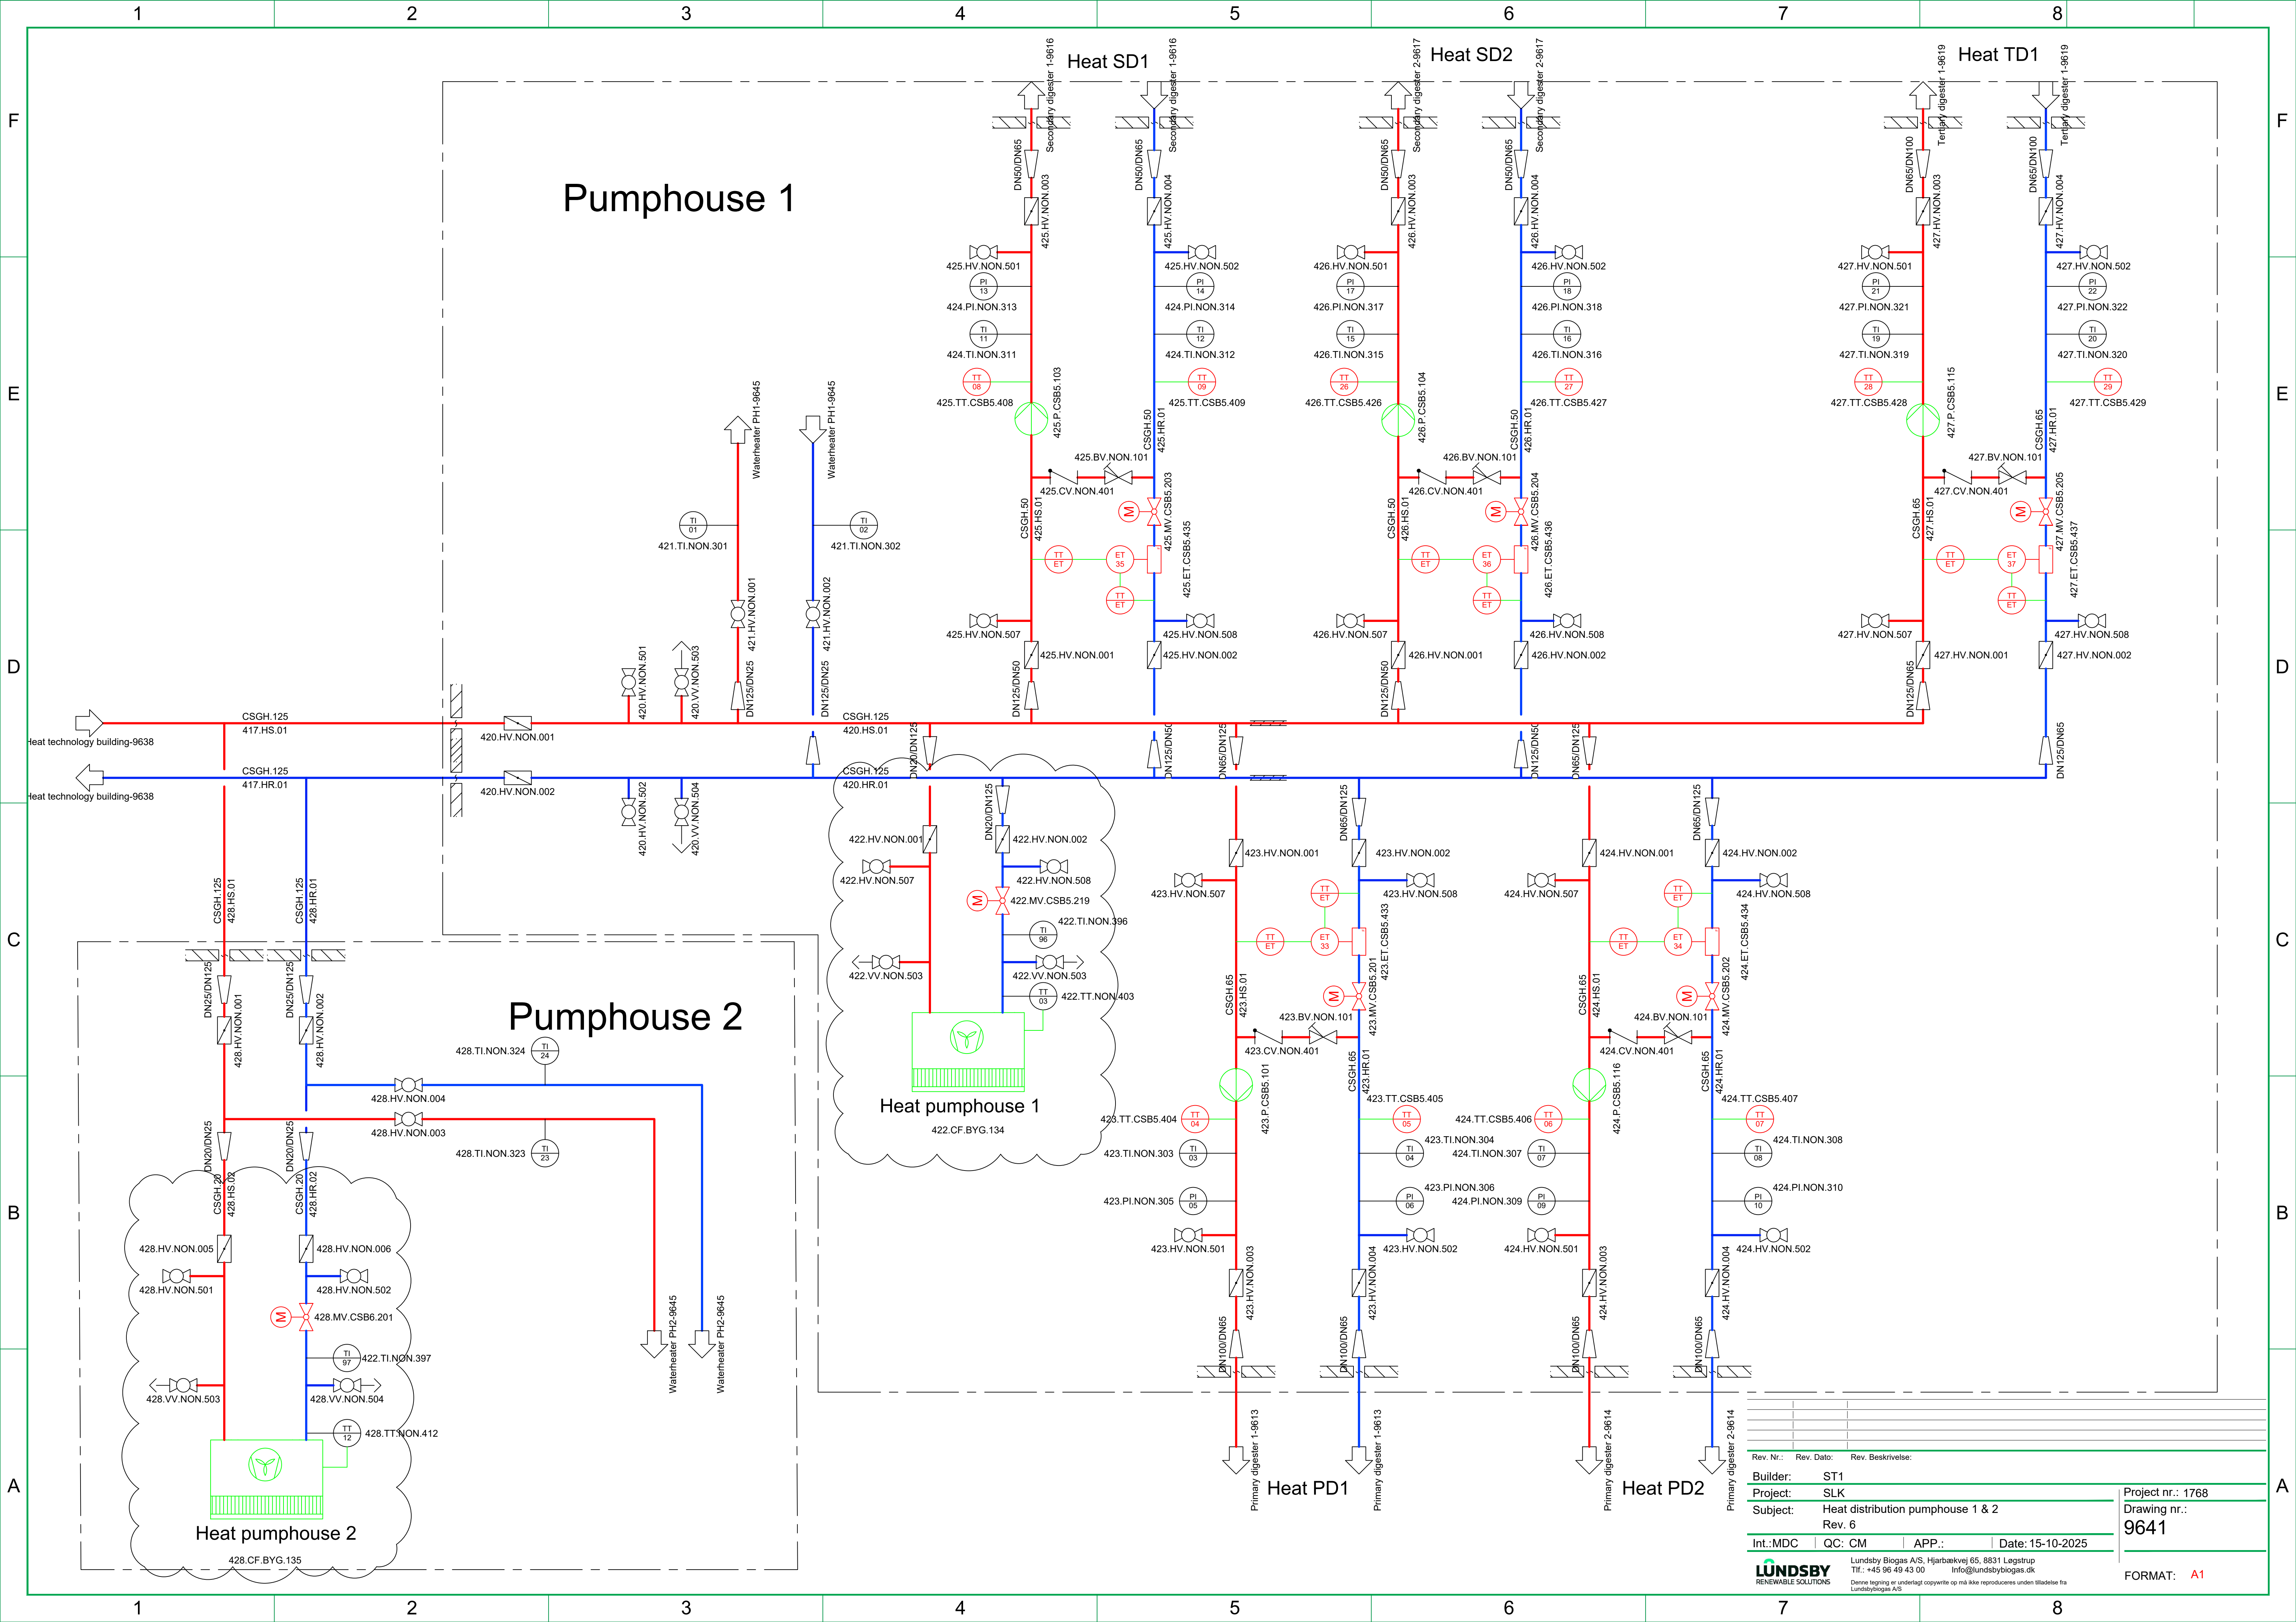


Rev. Nr.:	Rev. Dato:	Rev. Beskrivelse:
Builder:	ST1	
Project:	SLK	
Subject:	Heat distribution pumphouse 1 & 2	
Int.:MDC	QC: CM	APP.: Date: 15-10-2025
Rev. 6		
Project nr.:	1768	
Drawing nr.:	9641	
FORMAT:	A1	

LUNDSBY
RENEWABLE SOLUTIONS


Lundsby Biogas A/S, Hjarbækvej 65, 8831 Løgstrup
Tlf.: +45 96 49 43 00
info@lundsbybiogas.dk
Denne tegning er underlagt copyright op på ikke reproduceres uden tilladelse fra Lundsbybiogas A/S

SB-Building

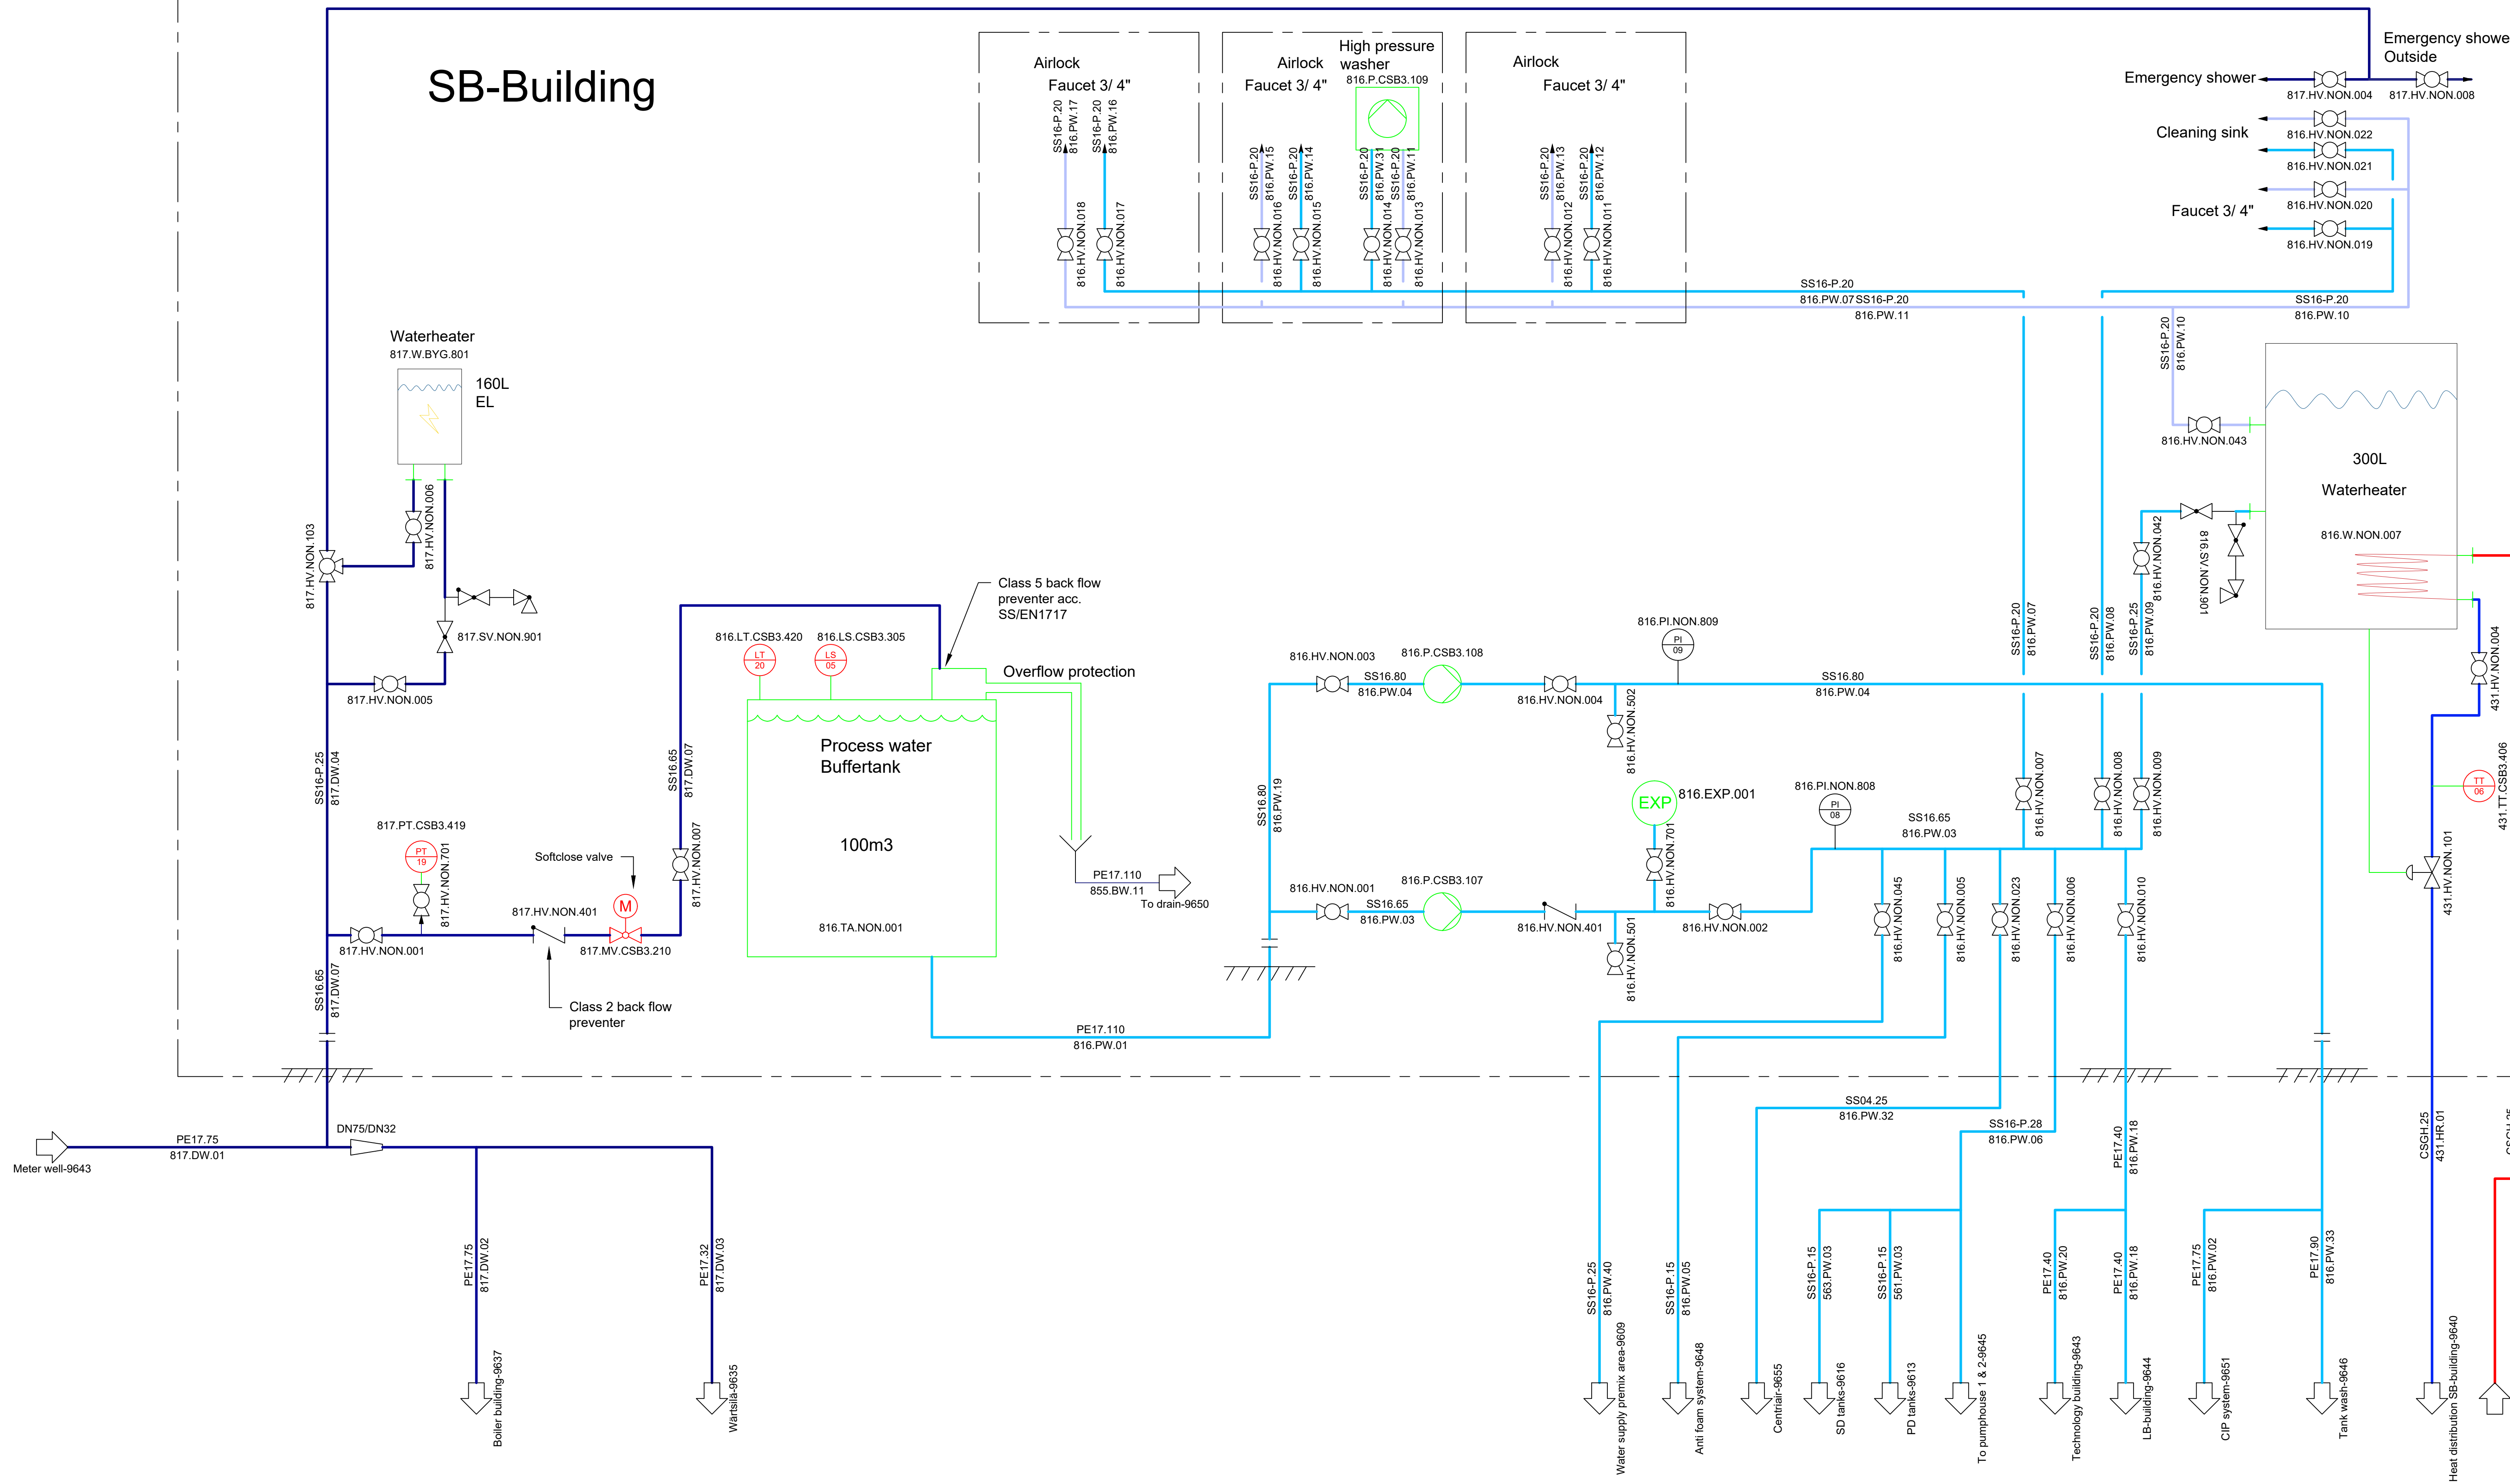


Rev. Nr.:	Rev. Dato:	Rev. Beskrivelse:
Builder:	ST1	
Project:	SLK	
Subject:	Water distribution SB-building	
Rev. 6		
Int.:MDC	QC:CM	APP.:
		Date: 15-10-2025
LUNDSBY RENEWABLE SOLUTIONS		
Lundsby Biogas A/S, Hjarbækvej 65, 8831 Løgstrup Tlf.: +45 96 49 43 00 info@lundsbybiogas.dk		
Denne tegning er underlagt copyright op på ikke reproduceres uden tilladelse fra Lundsbybiogas A/S		
Project nr.: 1768		
Drawing nr.: 9642		
FORMAT: A1		


Technology building

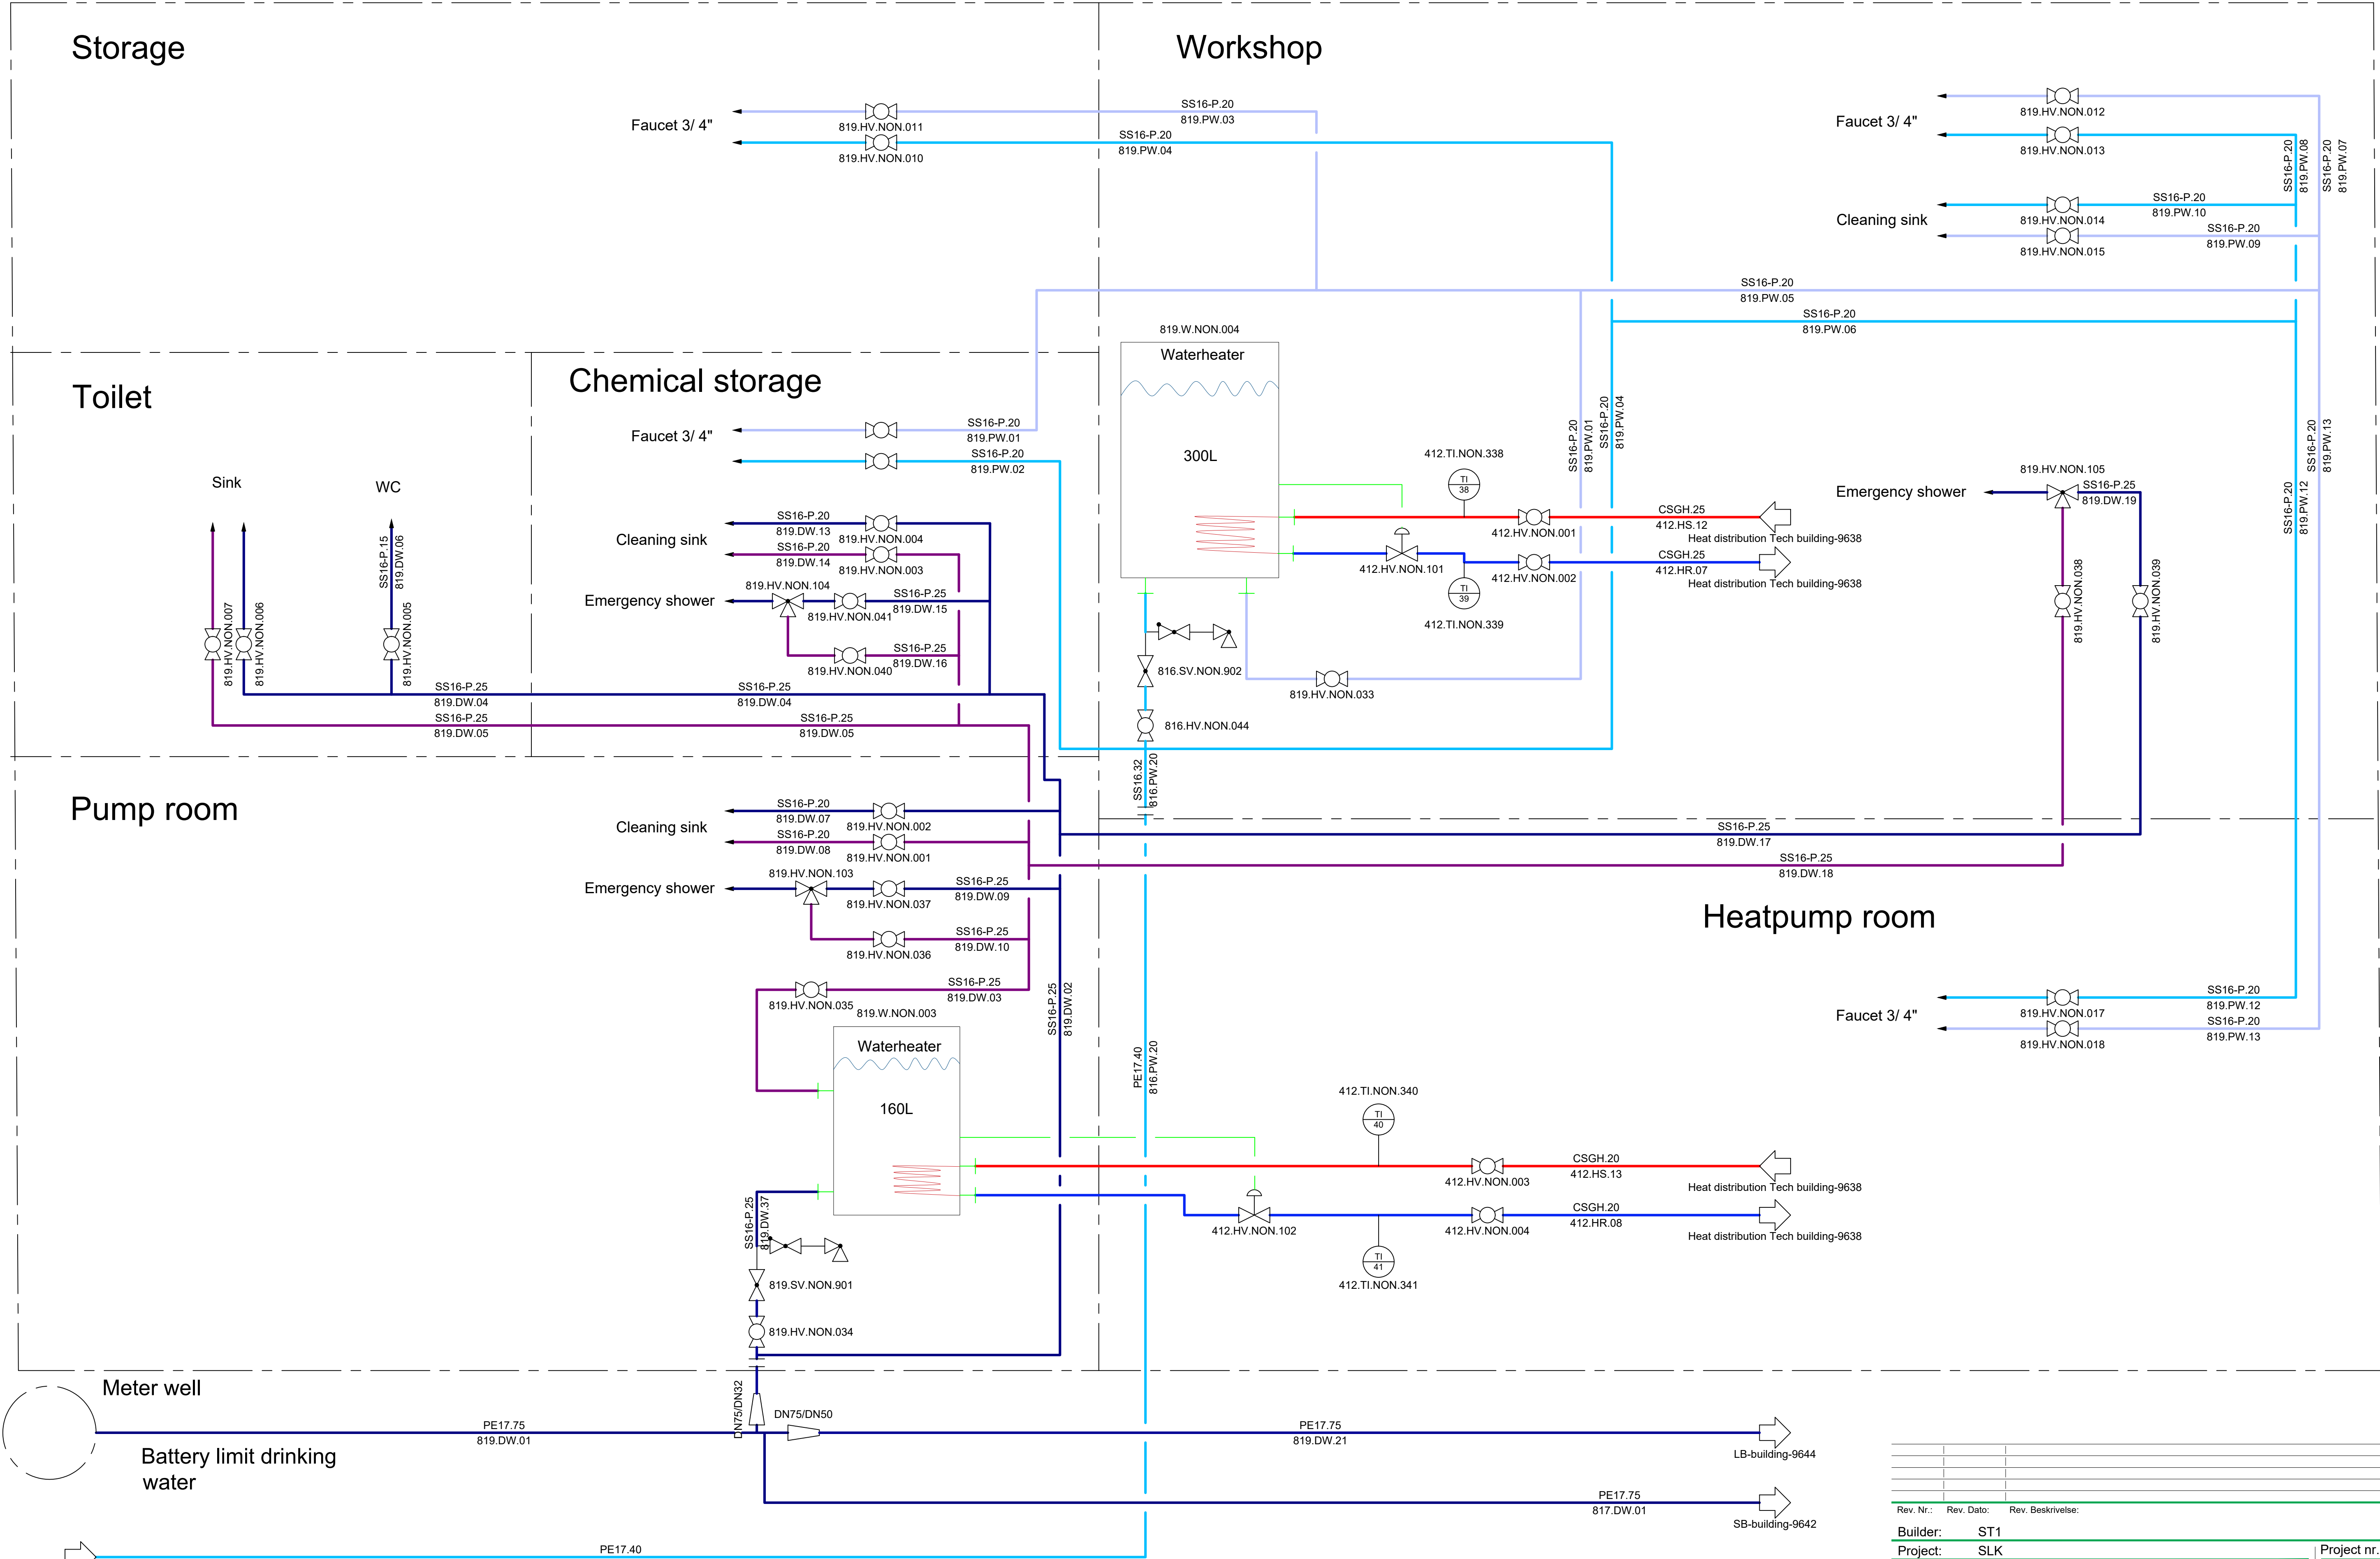

Rev. Nr.:	Rev. Dato:	Rev. Beskrivelse:
Builder:	ST1	
Project:	SLK	
Subject:	Water distribution Tech building	
Rev. 6		
Int.:MDC	QC:CM	APP.:
		Date: 15-10-2025
LUNDSBY RENEWABLE SOLUTIONS Lundsby Biogas A/S, Hjarbækvej 65, 8831 Løgstrup Tlf.: +45 96 49 43 00 info@lundsbybiogas.dk Denne tegning er underlagt copywrite op på ikke reproduceres uden tilladelse fra Lundsbybiogas A/S		
Project nr.: 1768		
Drawing nr.: 9643		
FORMAT: A1		

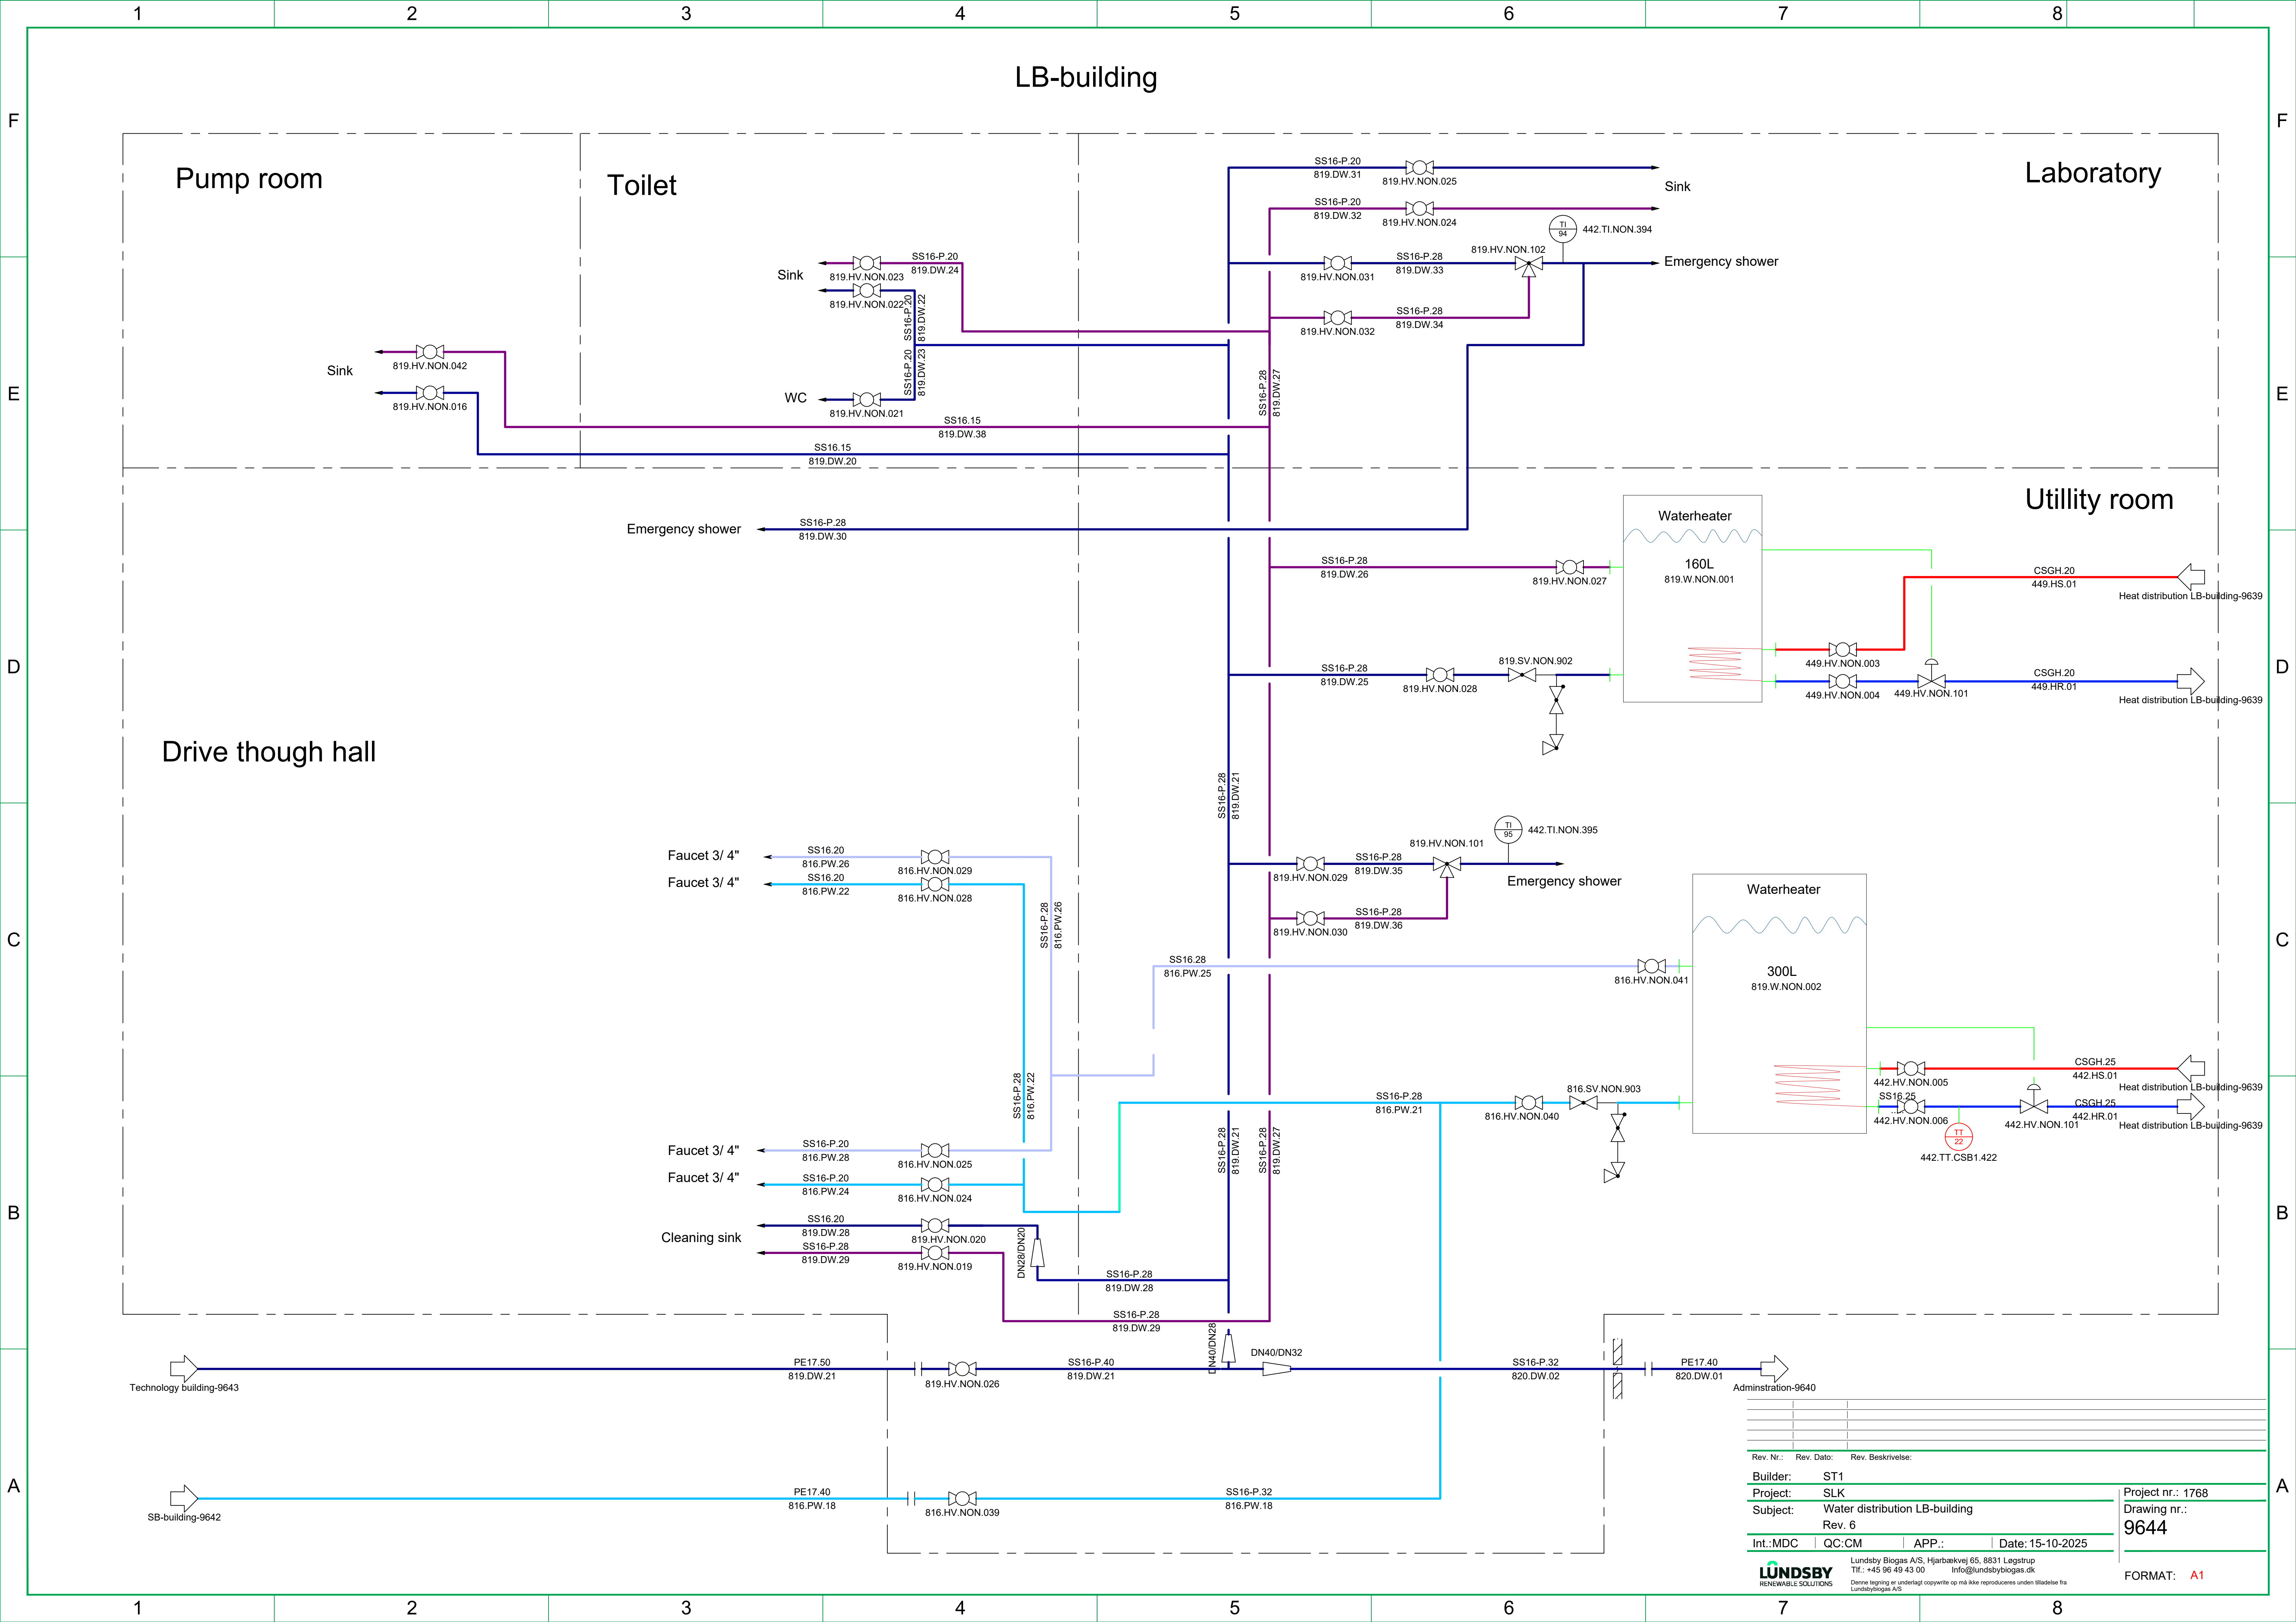

Pumphouse 1

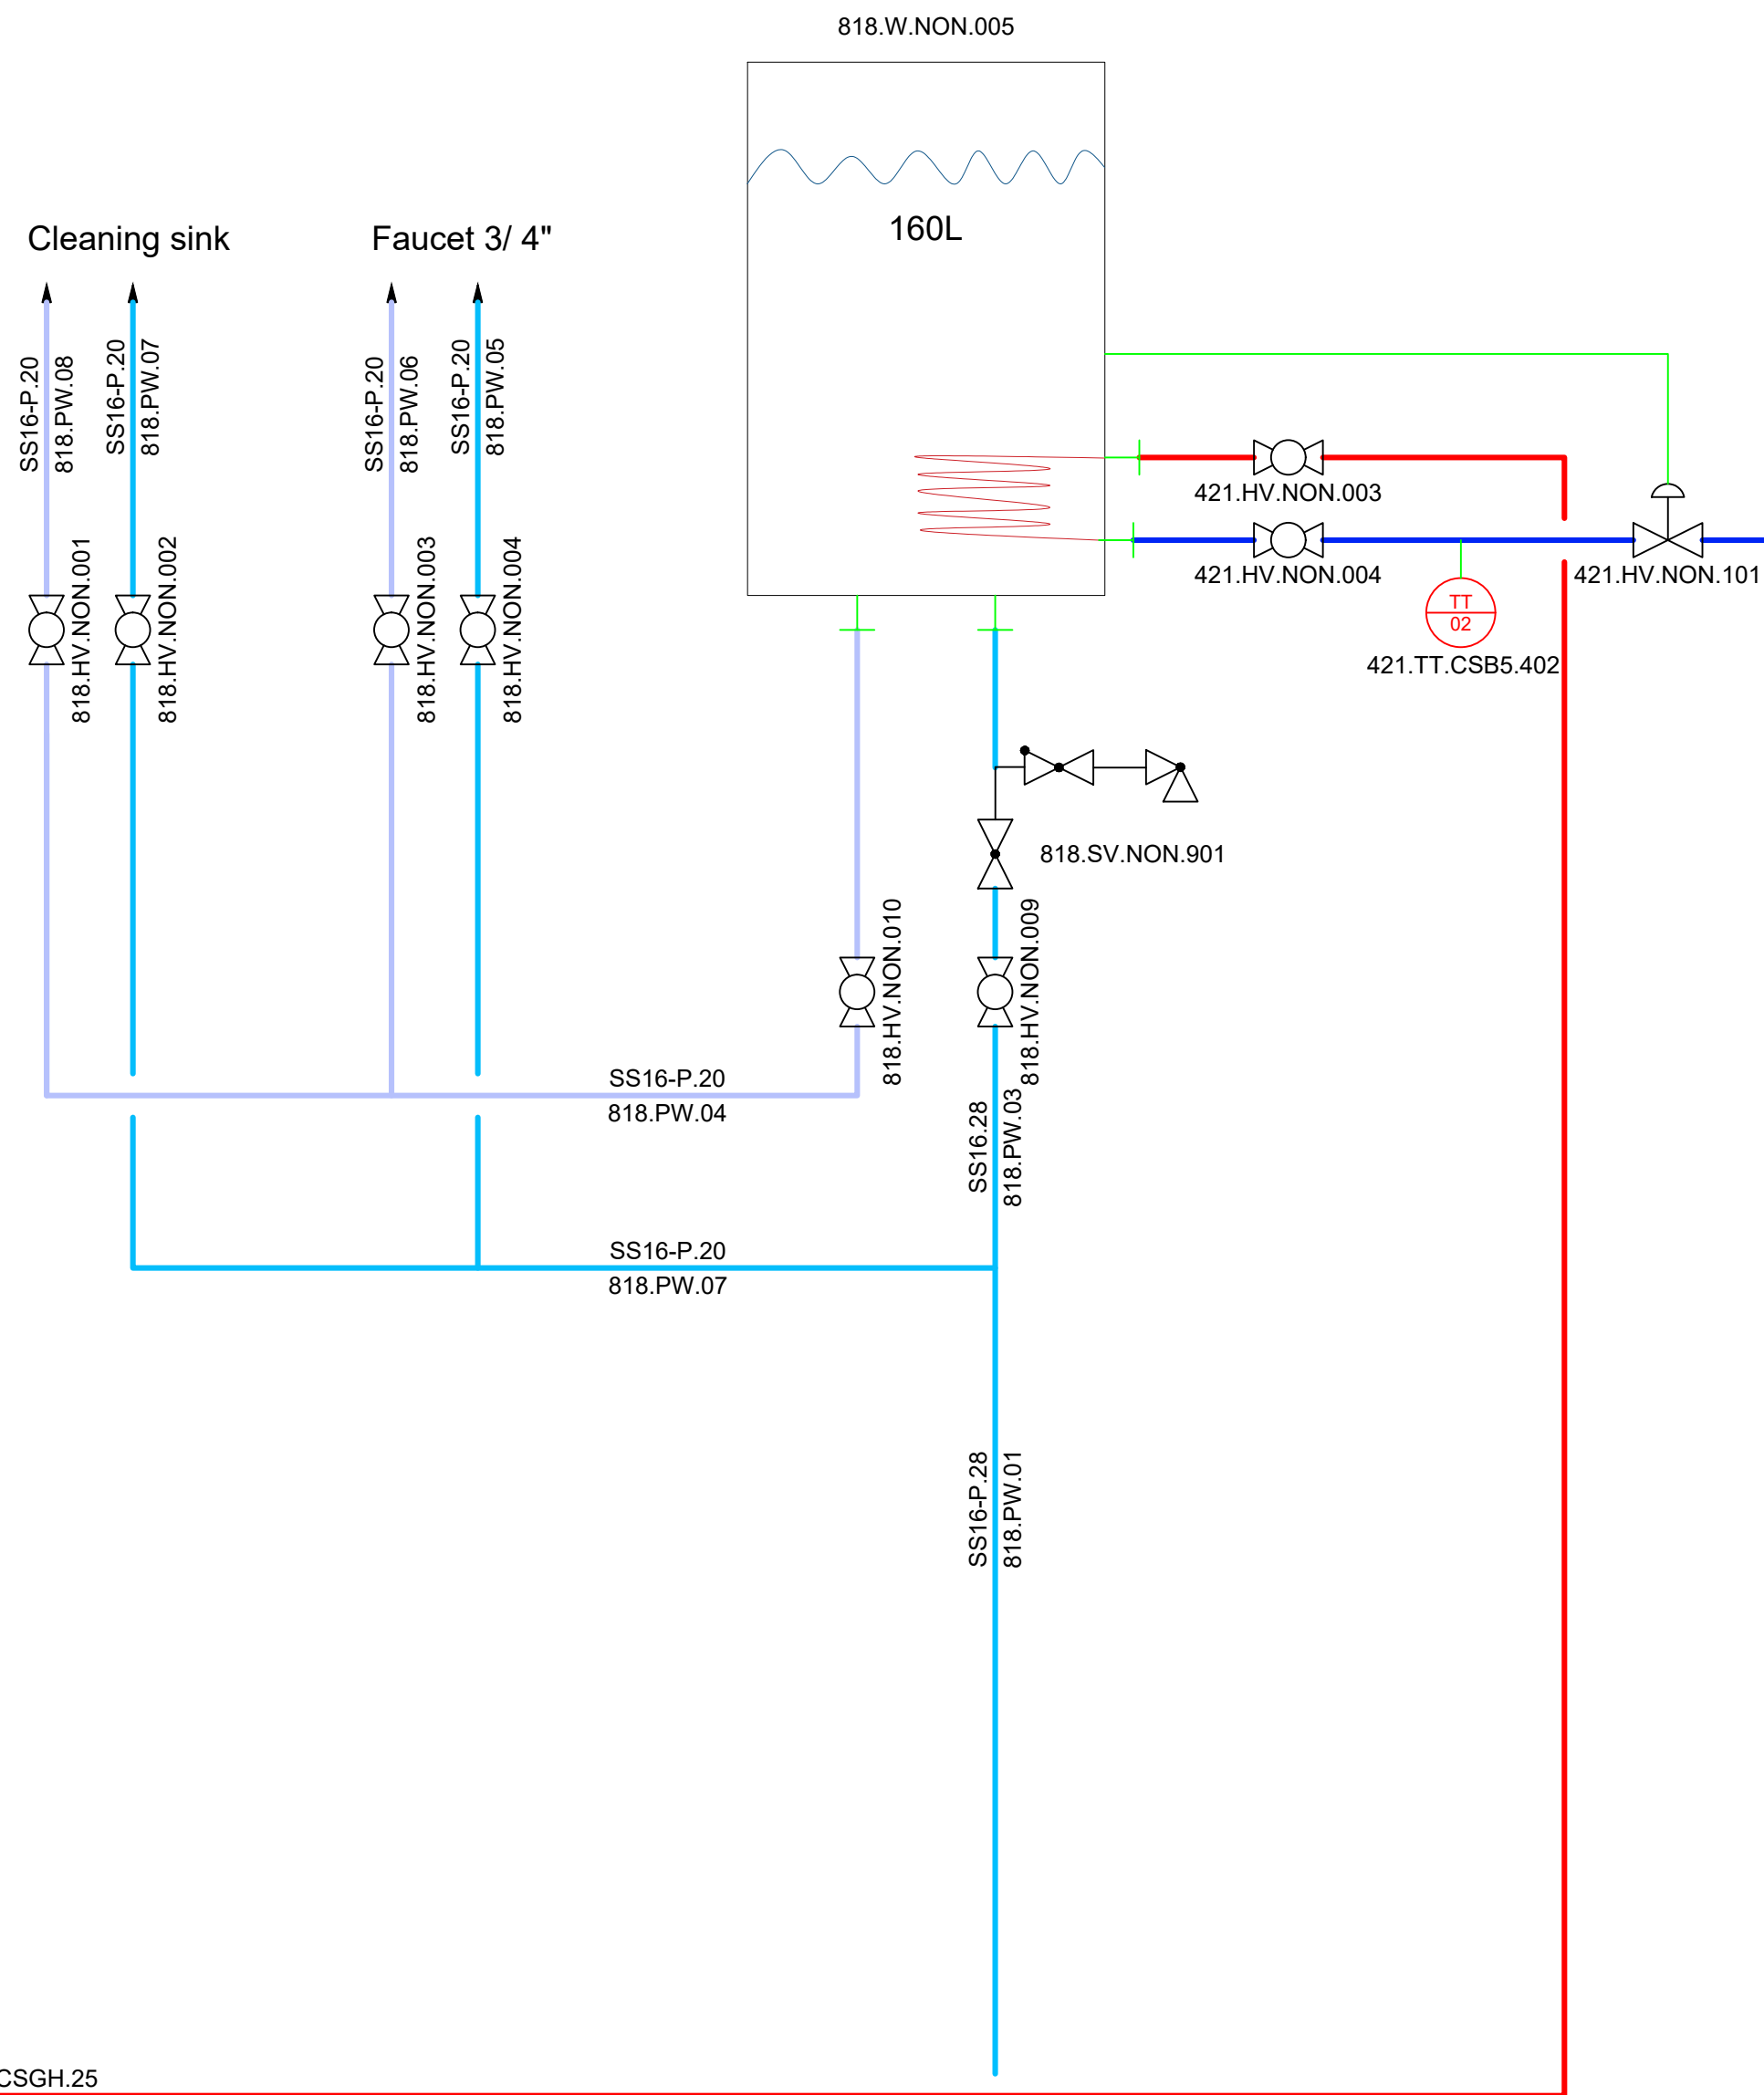


Heat distribution PH1-9641
CSGH.25
421.HS.01

Heat distribution PH1-9641
CSGH.25
421.HR.01

SB-building-9642
SS16-P.28
816.PW.06

Pumphouse 2

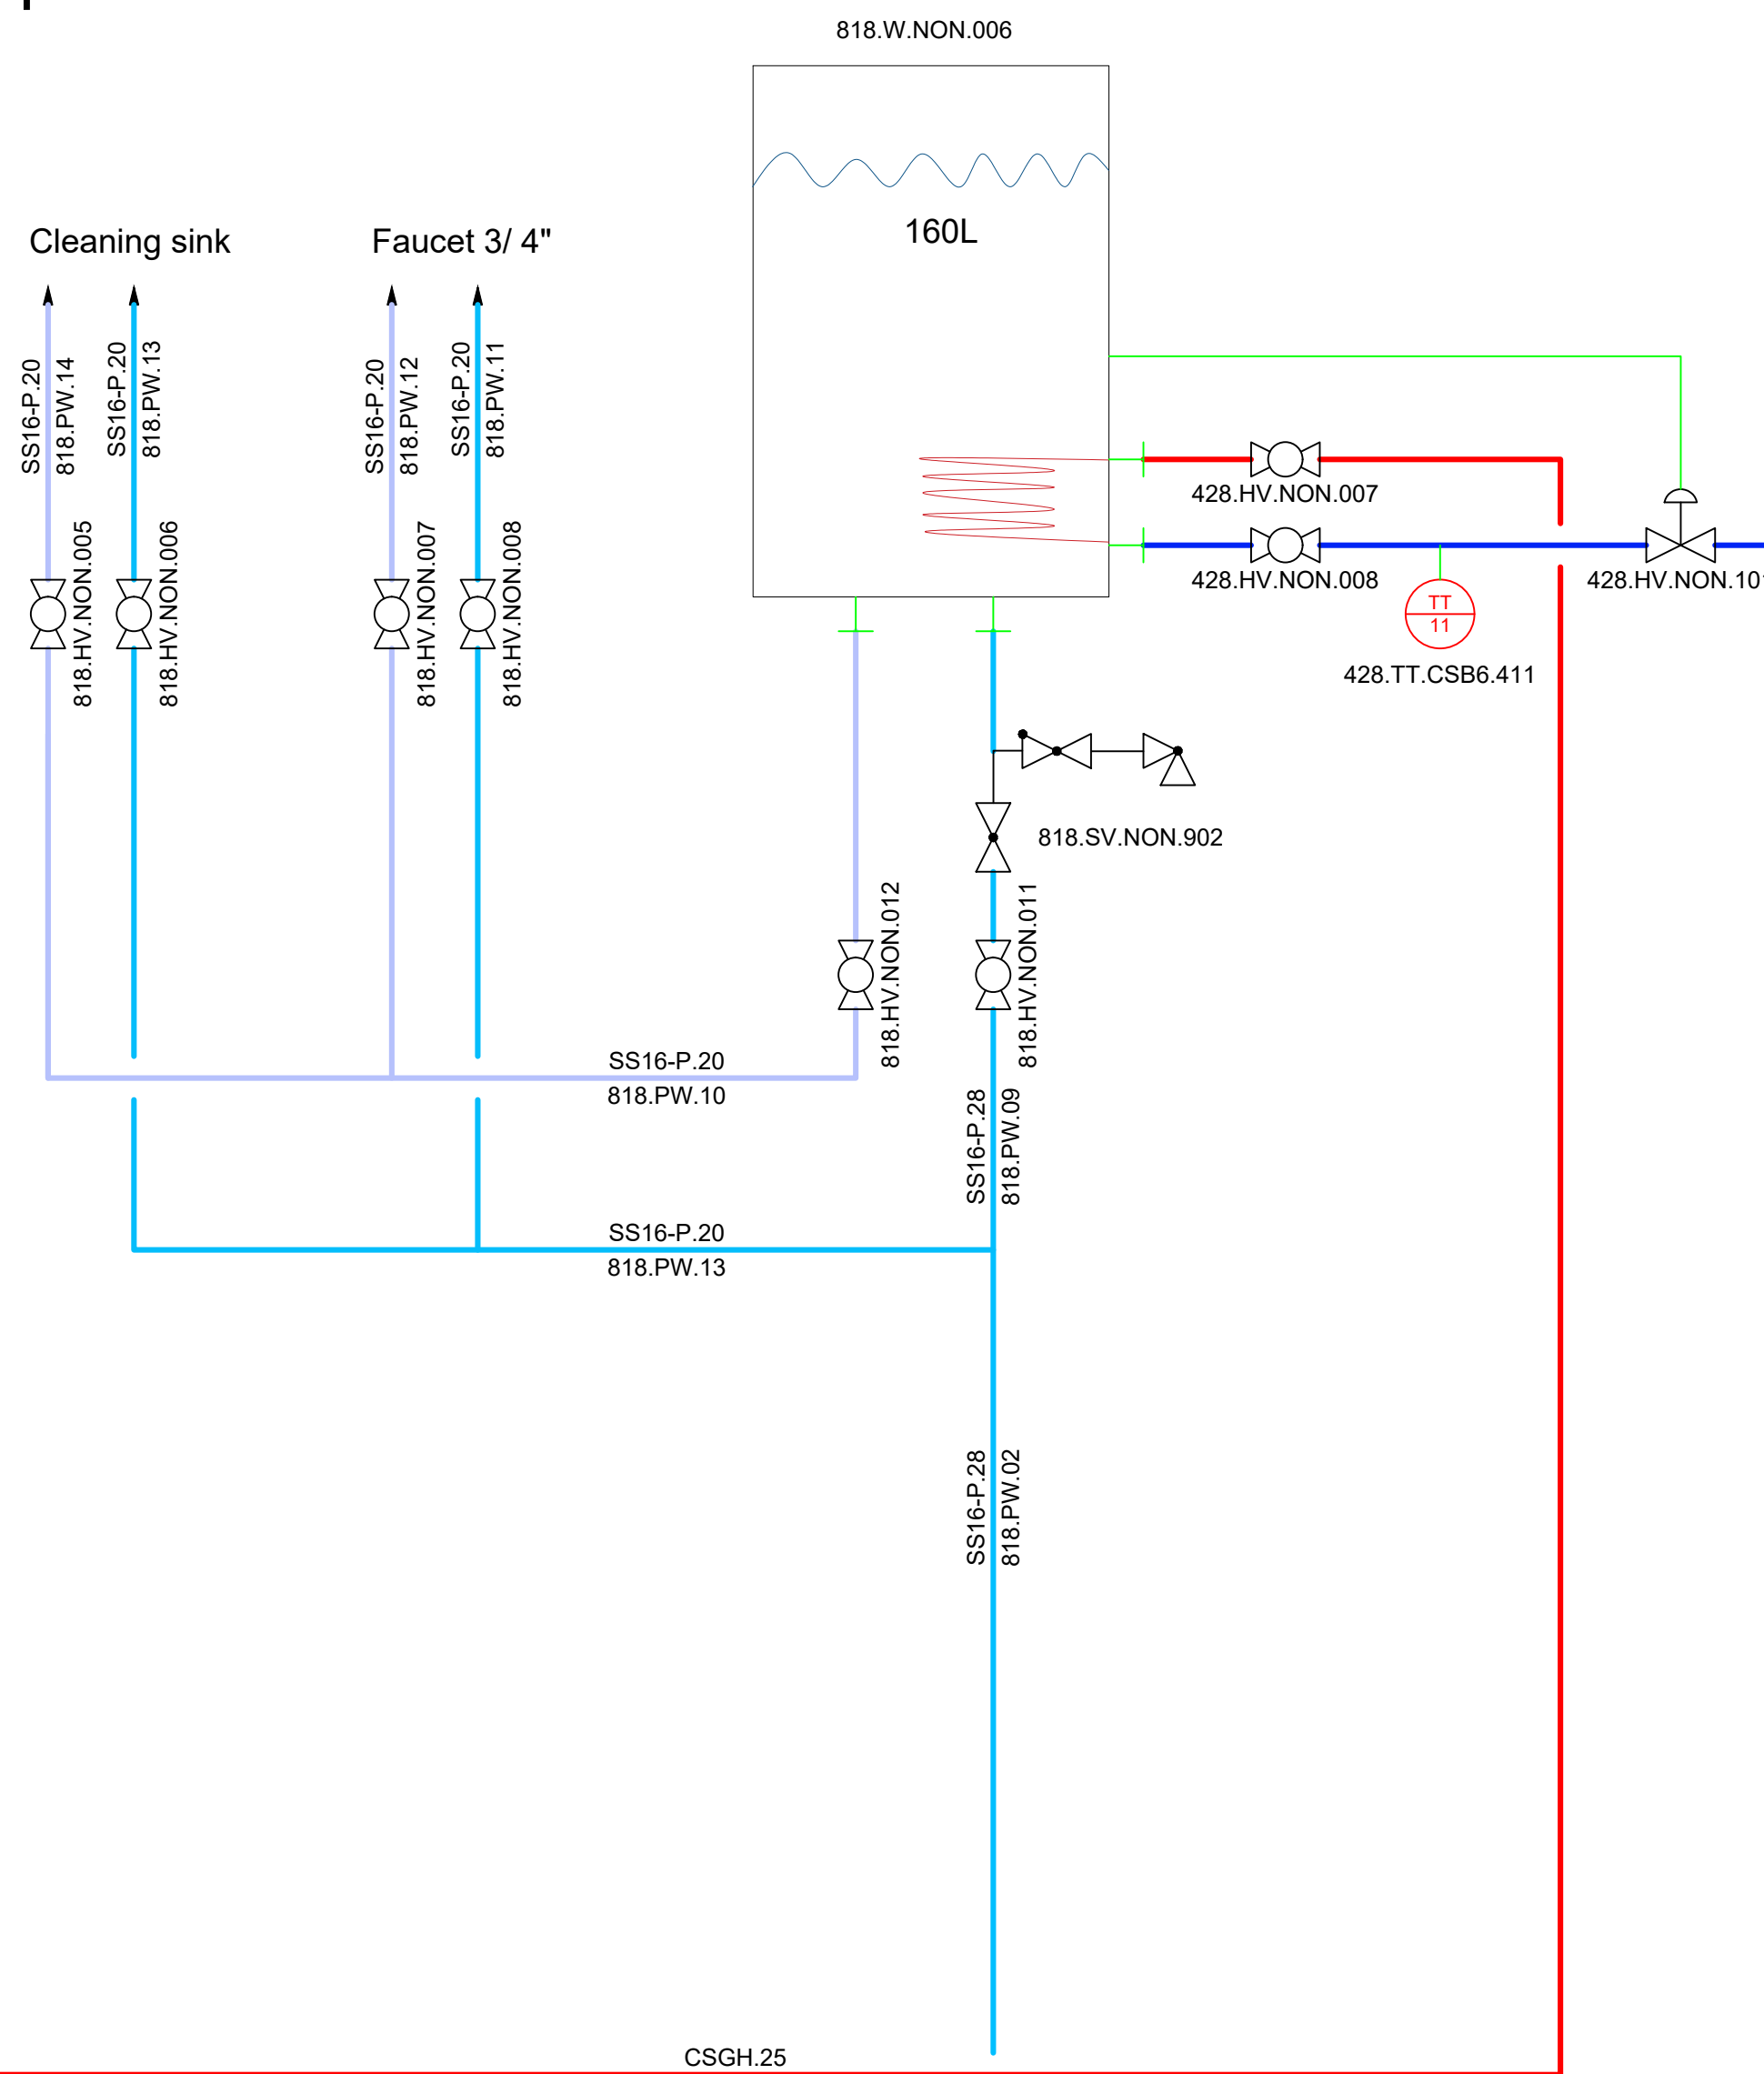


Heat distribution PH2-9641
CSGH.25
428.HS.01


Heat distribution PH2-9641
CSGH.25
428.HR.01


SS16-P.28
816.PW.06

Rev. Nr.:	Rev. Dato:	Rev. Beskrivelse:
Builder:	ST1	
Project:	SLK	
Subject:	Water distribution pumphouse 1 & 2	
Rev. 6		
Int.:MDC	QC:CM	APP.:
Date: 15-10-2025		
LUNDSBY RENEWABLE SOLUTIONS		
Lundsby Biogas A/S, Hjarbækvej 65, 8831 Løgstrup Tlf.: +45 96 49 43 00 info@lundsbybiogas.dk		
Denne tegning er underlagt copyright og må ikke reproduceres uden tilladelse fra Lundsbybiogas A/S		
Project nr.: 1768		Drawing nr.: 9645
FORMAT: A1		

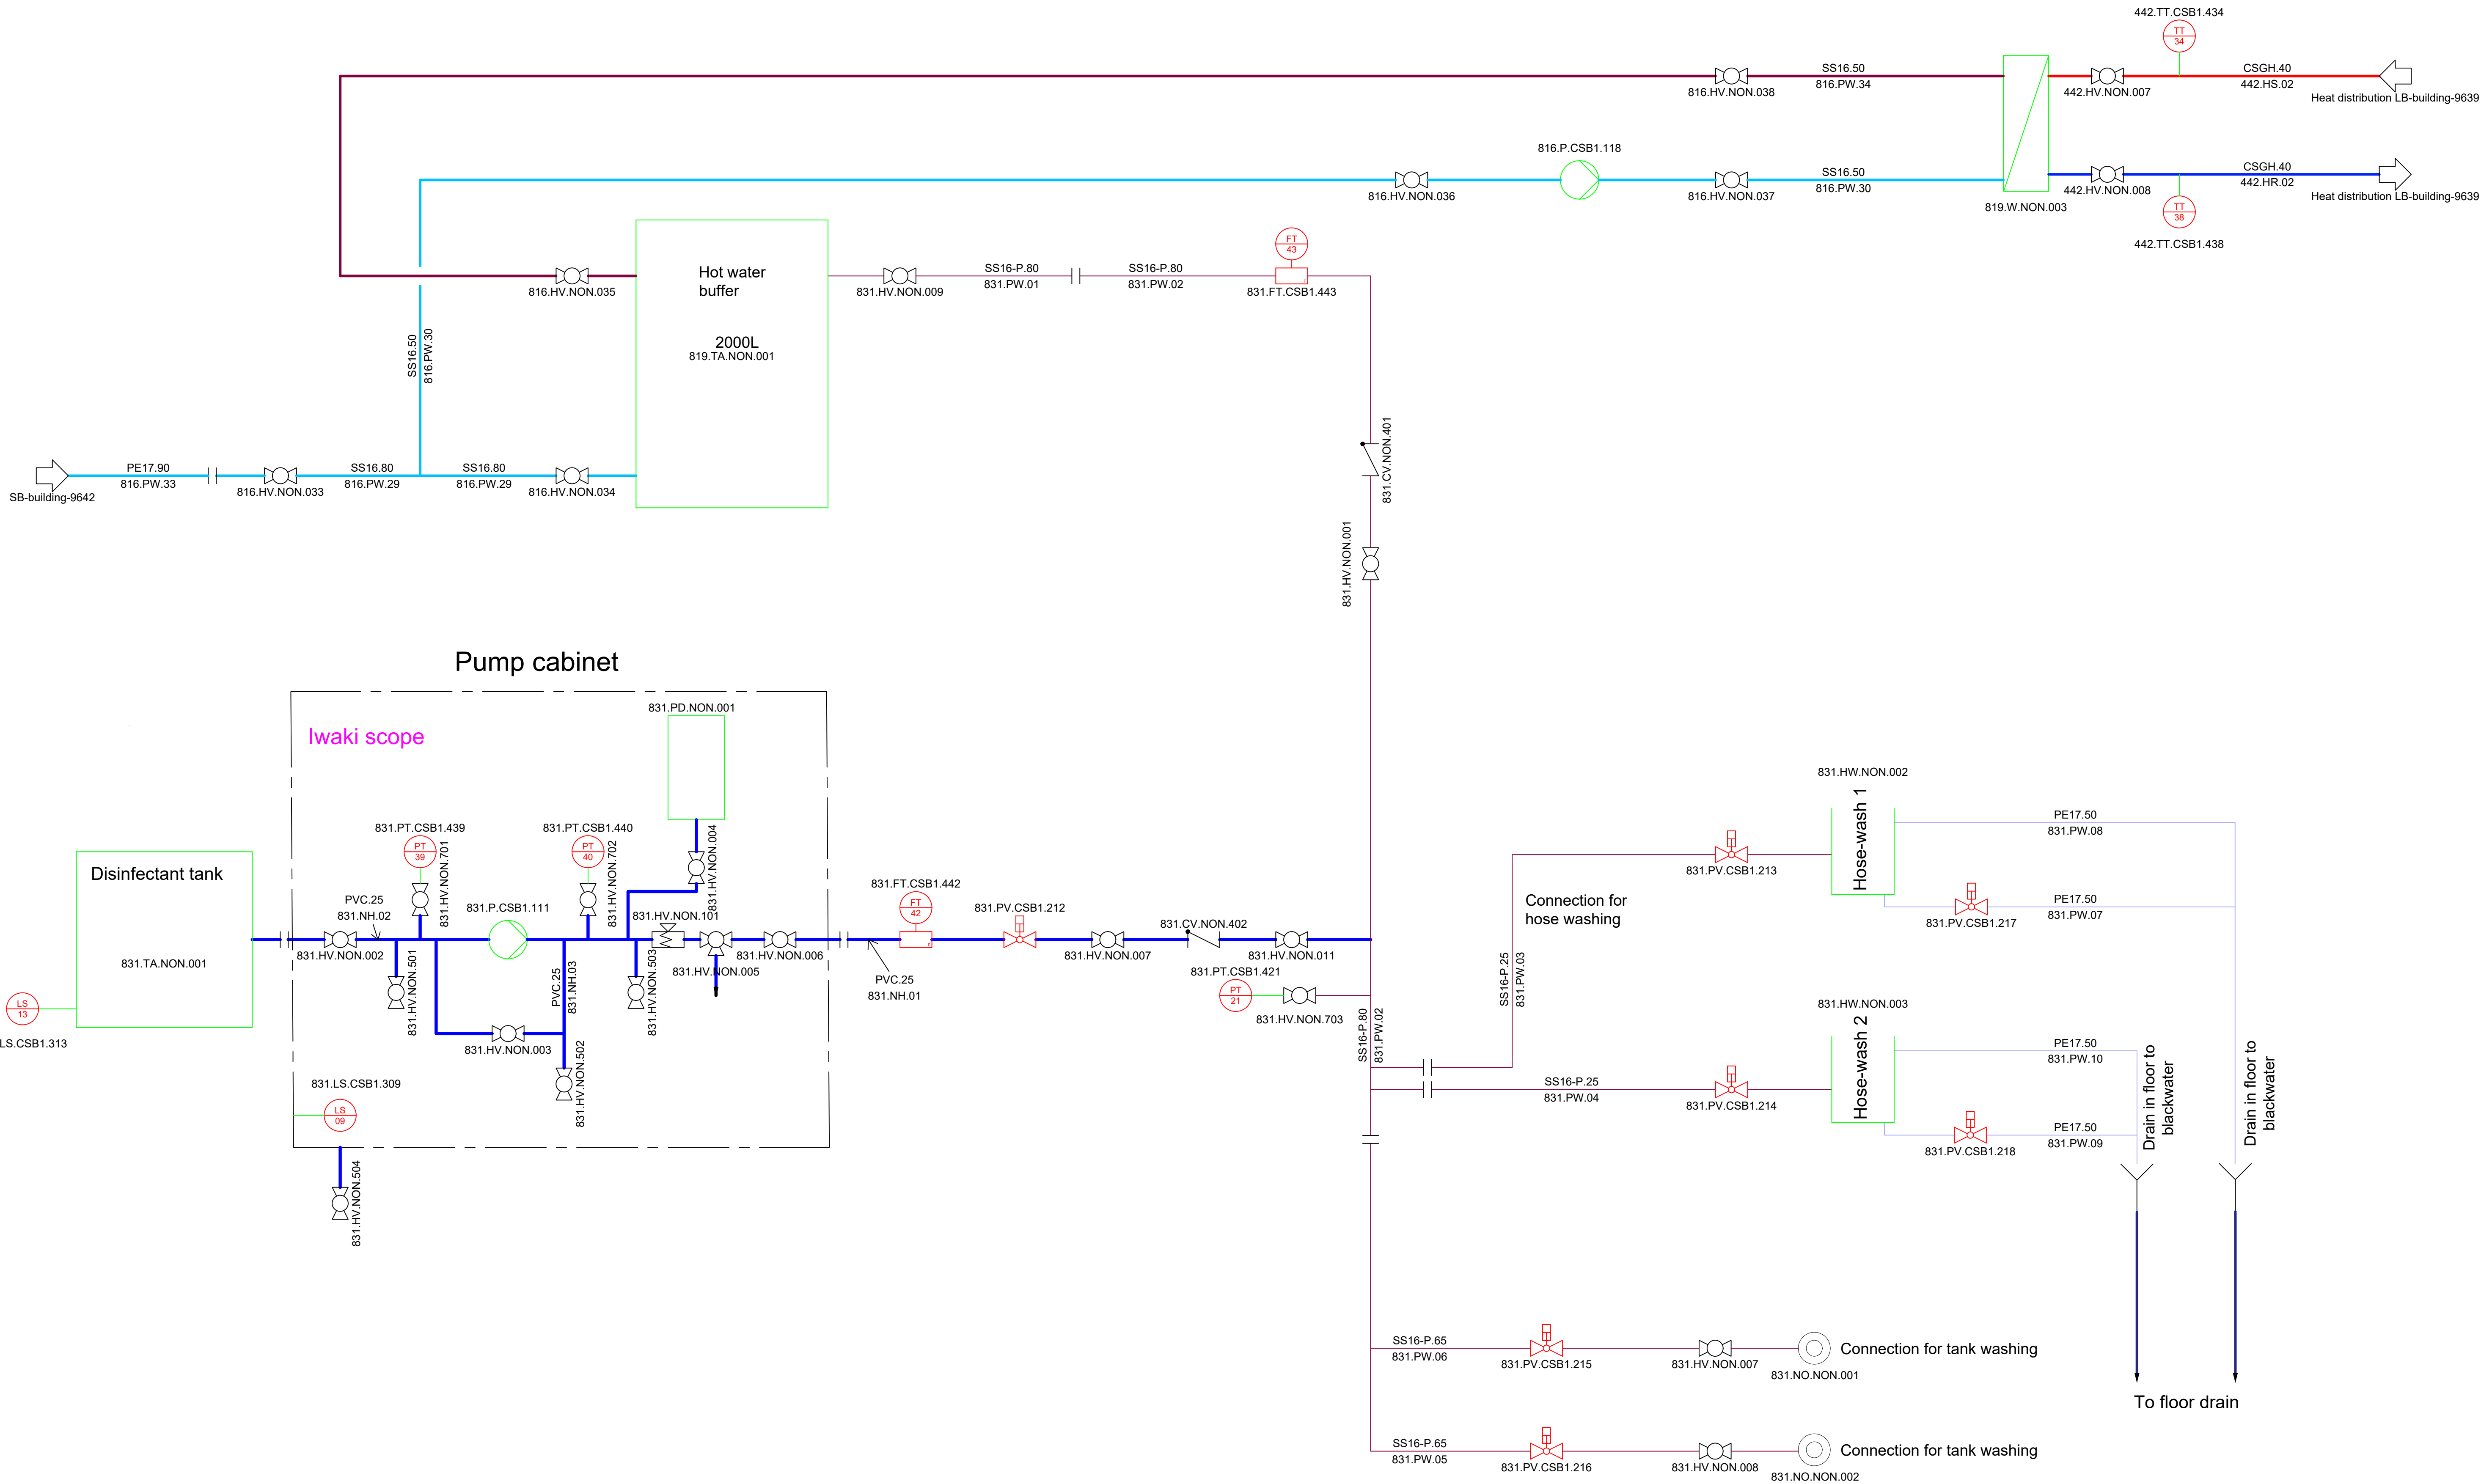


Rev. Nr.:	Rev. Dato:	Rev. Beskrivelse:	
Builder:	ST1		
Project:	SLK		
Subject:	Wash system		
Rev. 6			
Int.:MDC	QC: CM	APP.:	Date: 15-10-2025
LUNDSBY RENEWABLE SOLUTIONS			Lundsby Biogas A/S, Hjarbækvej 65, 8831 Løgstrup Tlf.: +45 96 49 43 00 info@lundsbybiogas.dk Denne tegning er underlagt copyright op på ikke reproduceres uden tilladelse fra Lundsbybiogas A/S
			Sags nr.: 1768 Tegn. nr.: 9646 FORMAT: A1

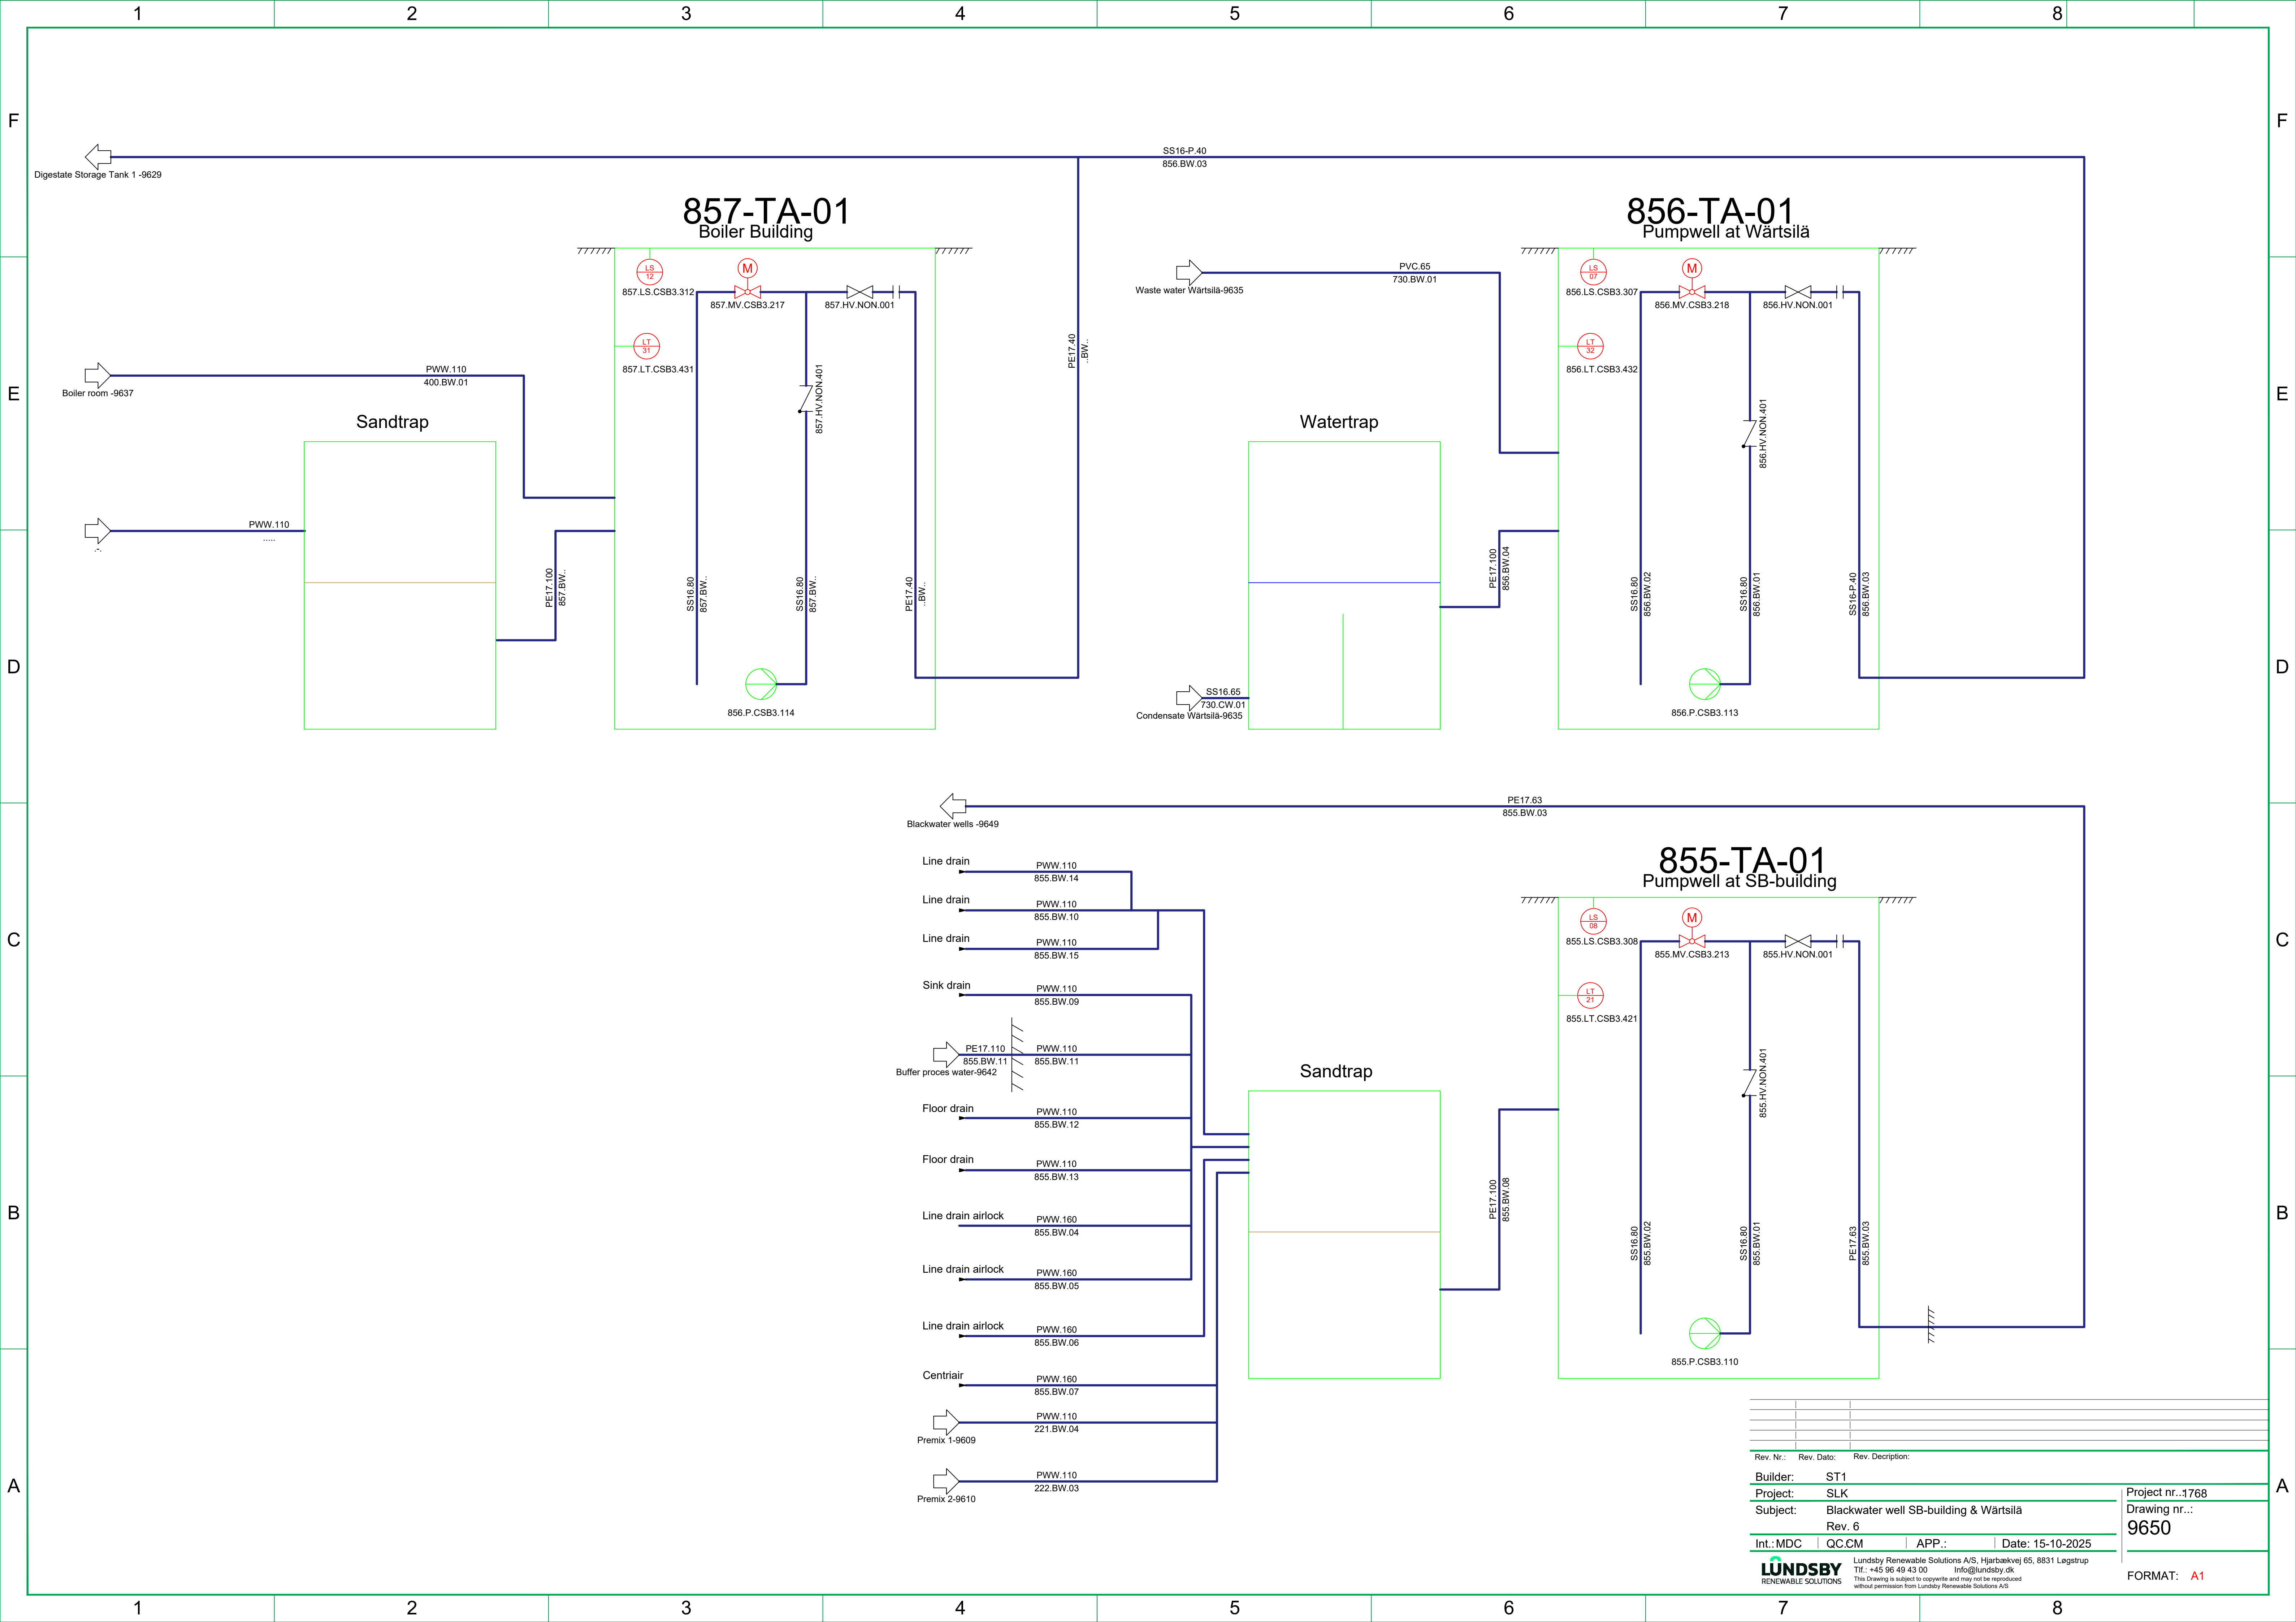

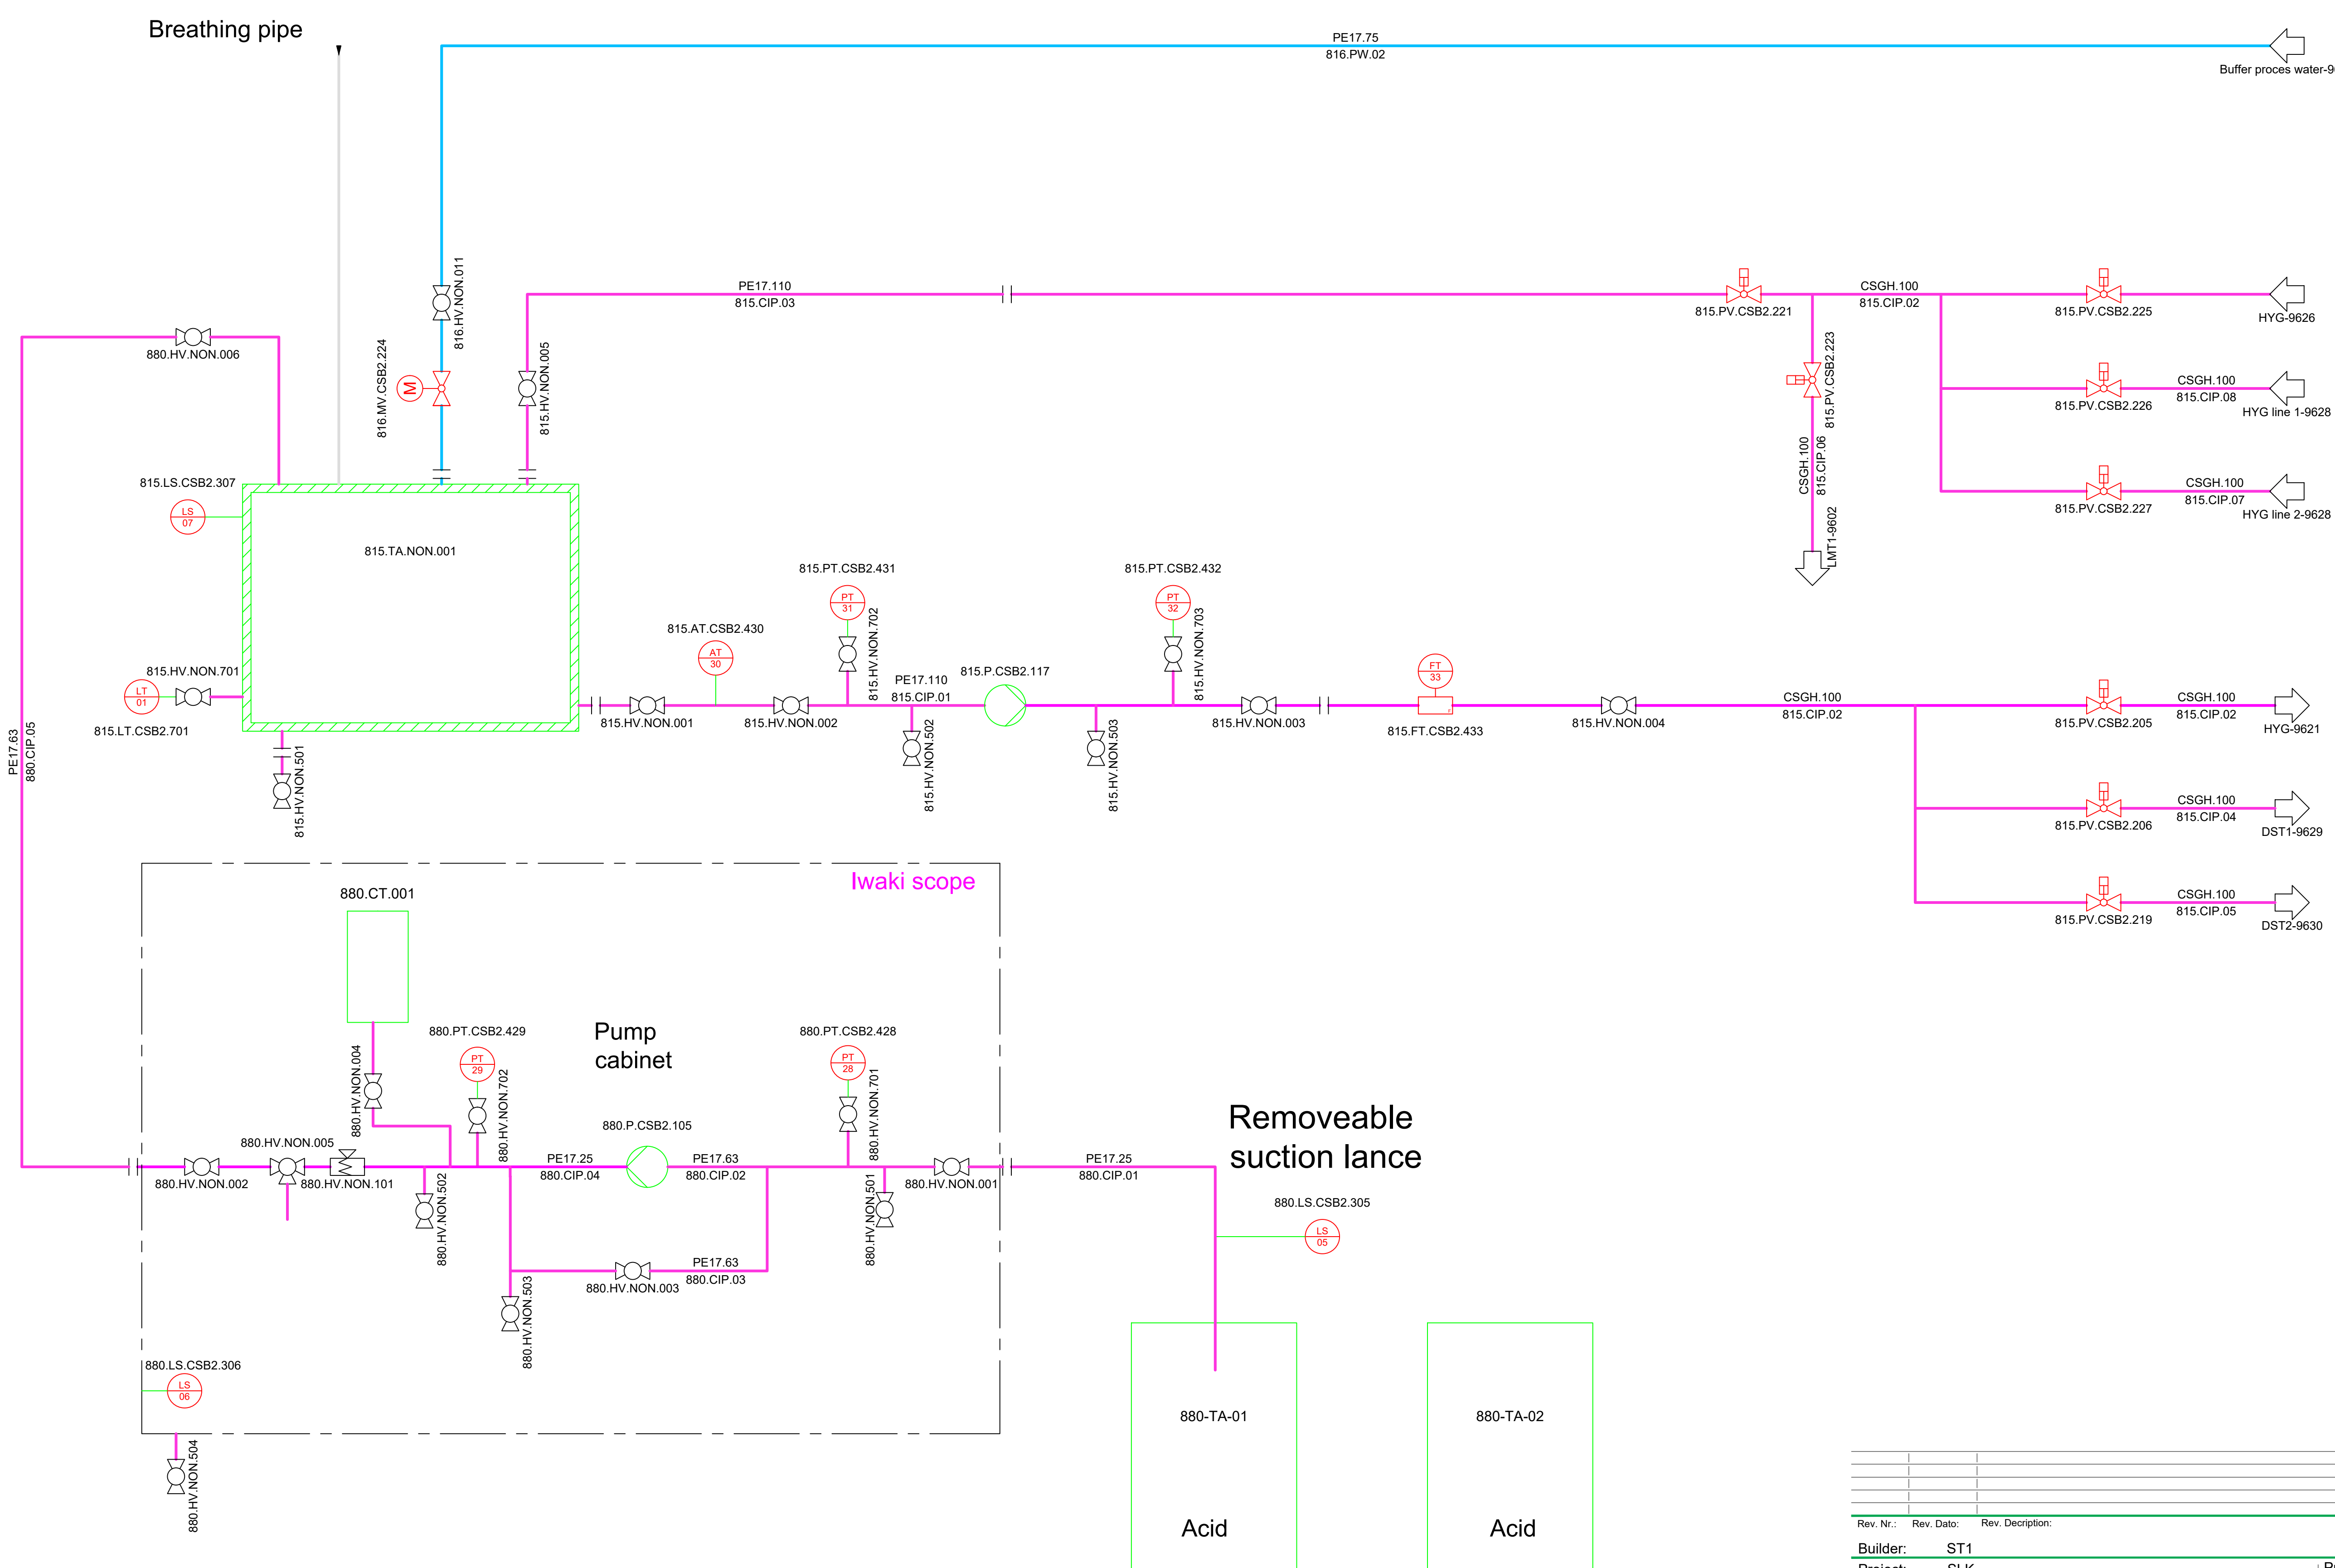


Rev. Nr.:	Rev. Dato:	Rev. Description:	
Builder:	ST1		
Project:	SLK		
Subject:	CIP facility		
	Rev. 6		
Int.:MDC	QC.CM	APP.:	Date: 15-10-2025
LUNDSBY RENEWABLE SOLUTIONS			Lundsby Renewable Solutions A/S, Hjarbækvej 65, 8831 Legstrup Tlf.: +45 96 49 43 00 Info@lundsby.dk This Drawing is subject to copyright and may not be reproduced without permission from Lundsby Renewable Solutions A/S
Project nr...1768 Drawing nr...: 9651			FORMAT: A1


Pumphouse 1
JA Trykluft scope

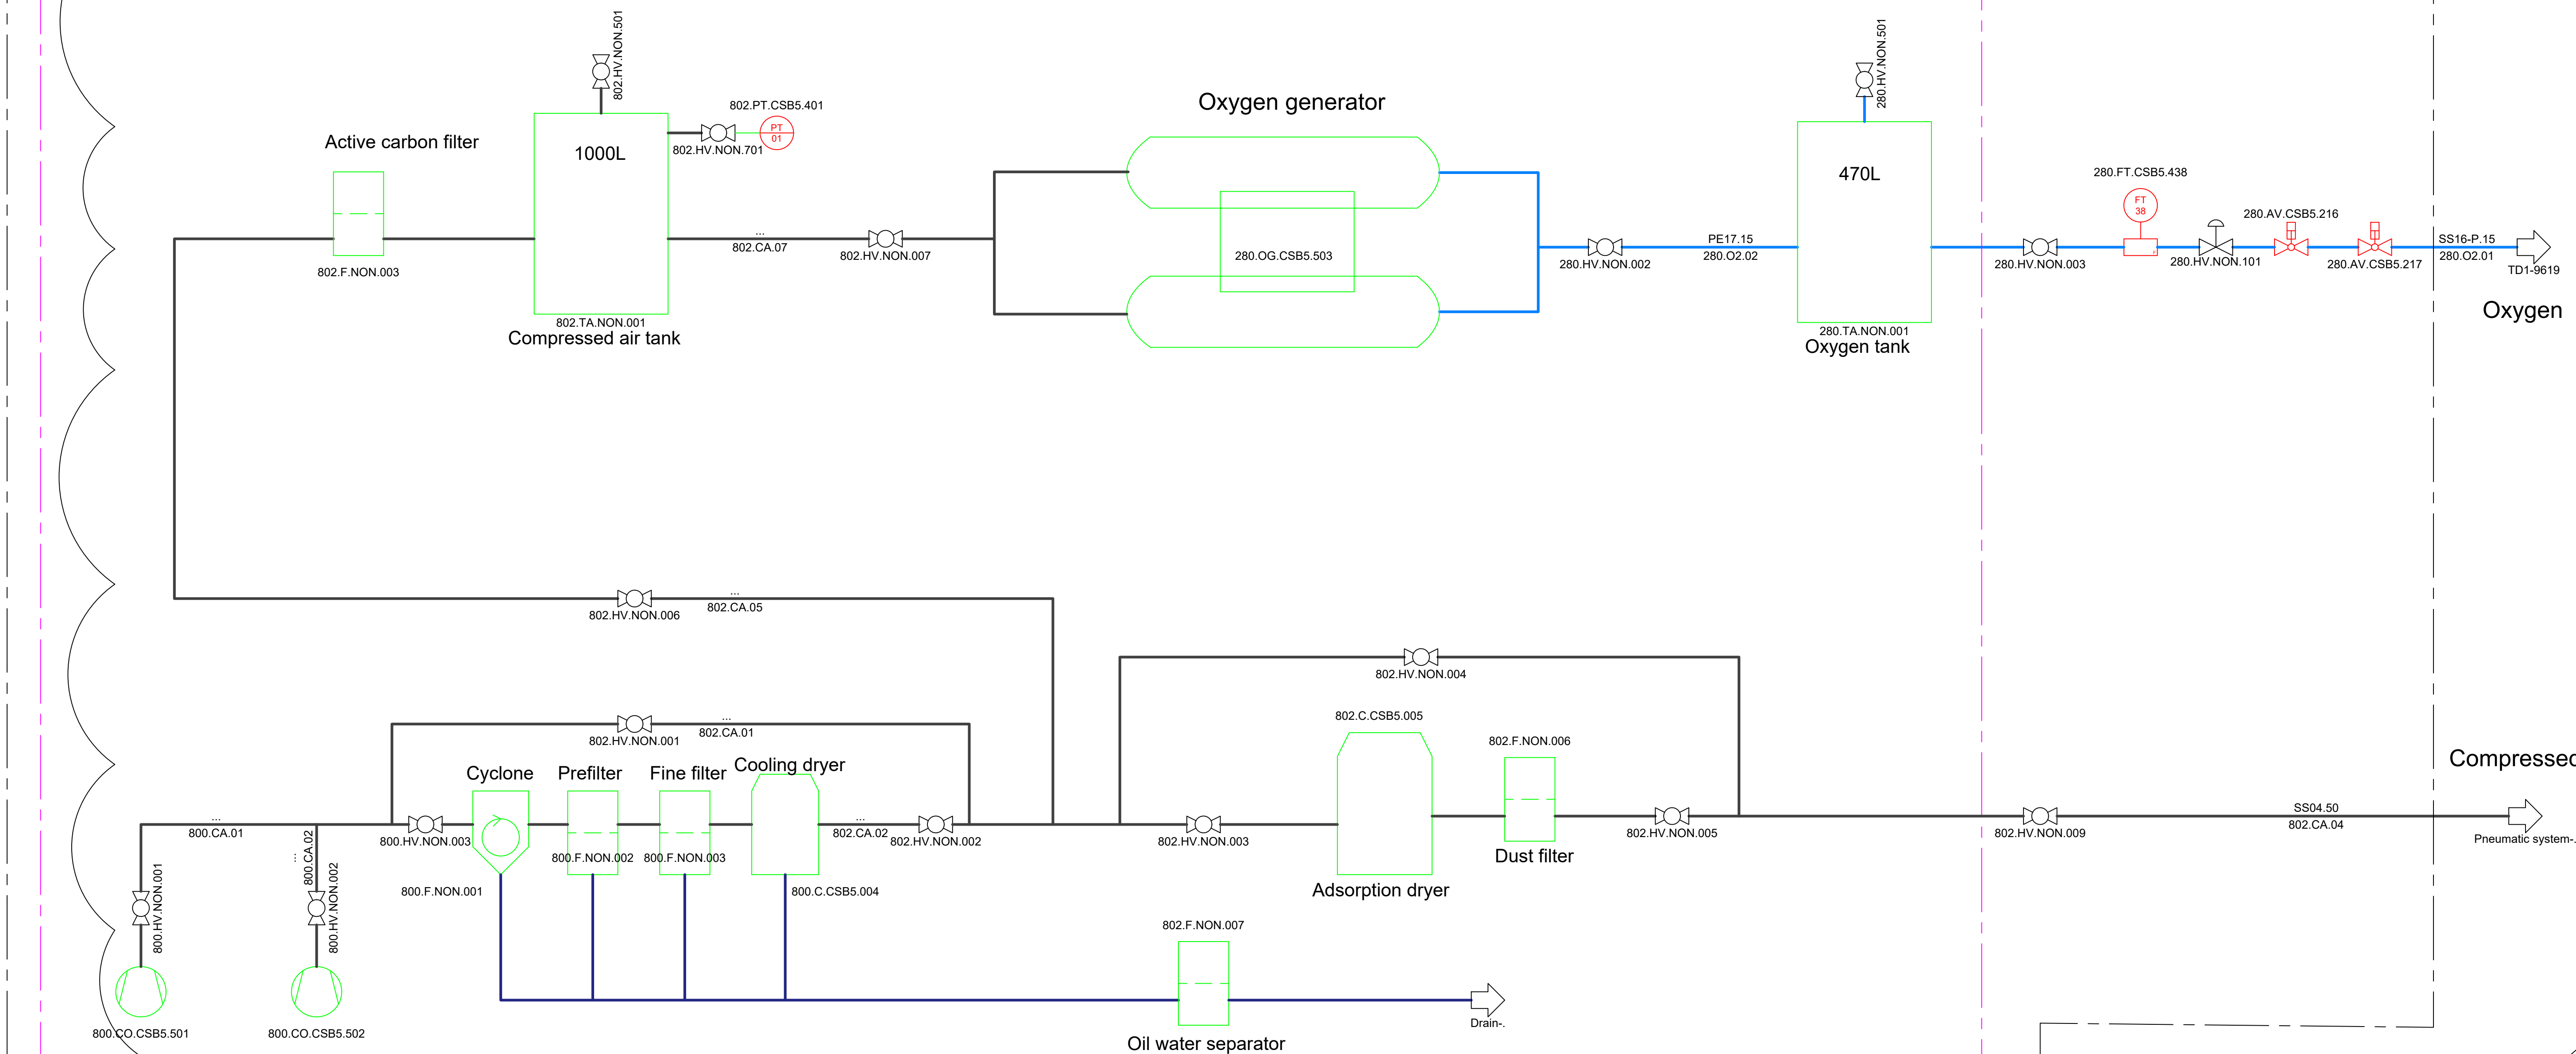


Rev. Nr.:	Rev. Dato:	Rev. Description:	
Builder:	ST1		
Project:	SLK		
Subject:	Compressed air & Oxygen		
Rev. 6			
Int.:MDC	QC:CM	APP.:	Date: 15-10-2025
LUNDSBY RENEWABLE SOLUTIONS			Lundsby Renewable Solutions A/S, Hjarbækvej 65, 8831 Løgstrup Tlf.: +45 96 49 43 00 Info@lundsby.dk This drawing is subject to copyright and may not be reproduced without permission from Lundsby Renewable Solutions A/S
Project nr.:1768 Drawing nr.: 9652			FORMAT: A1

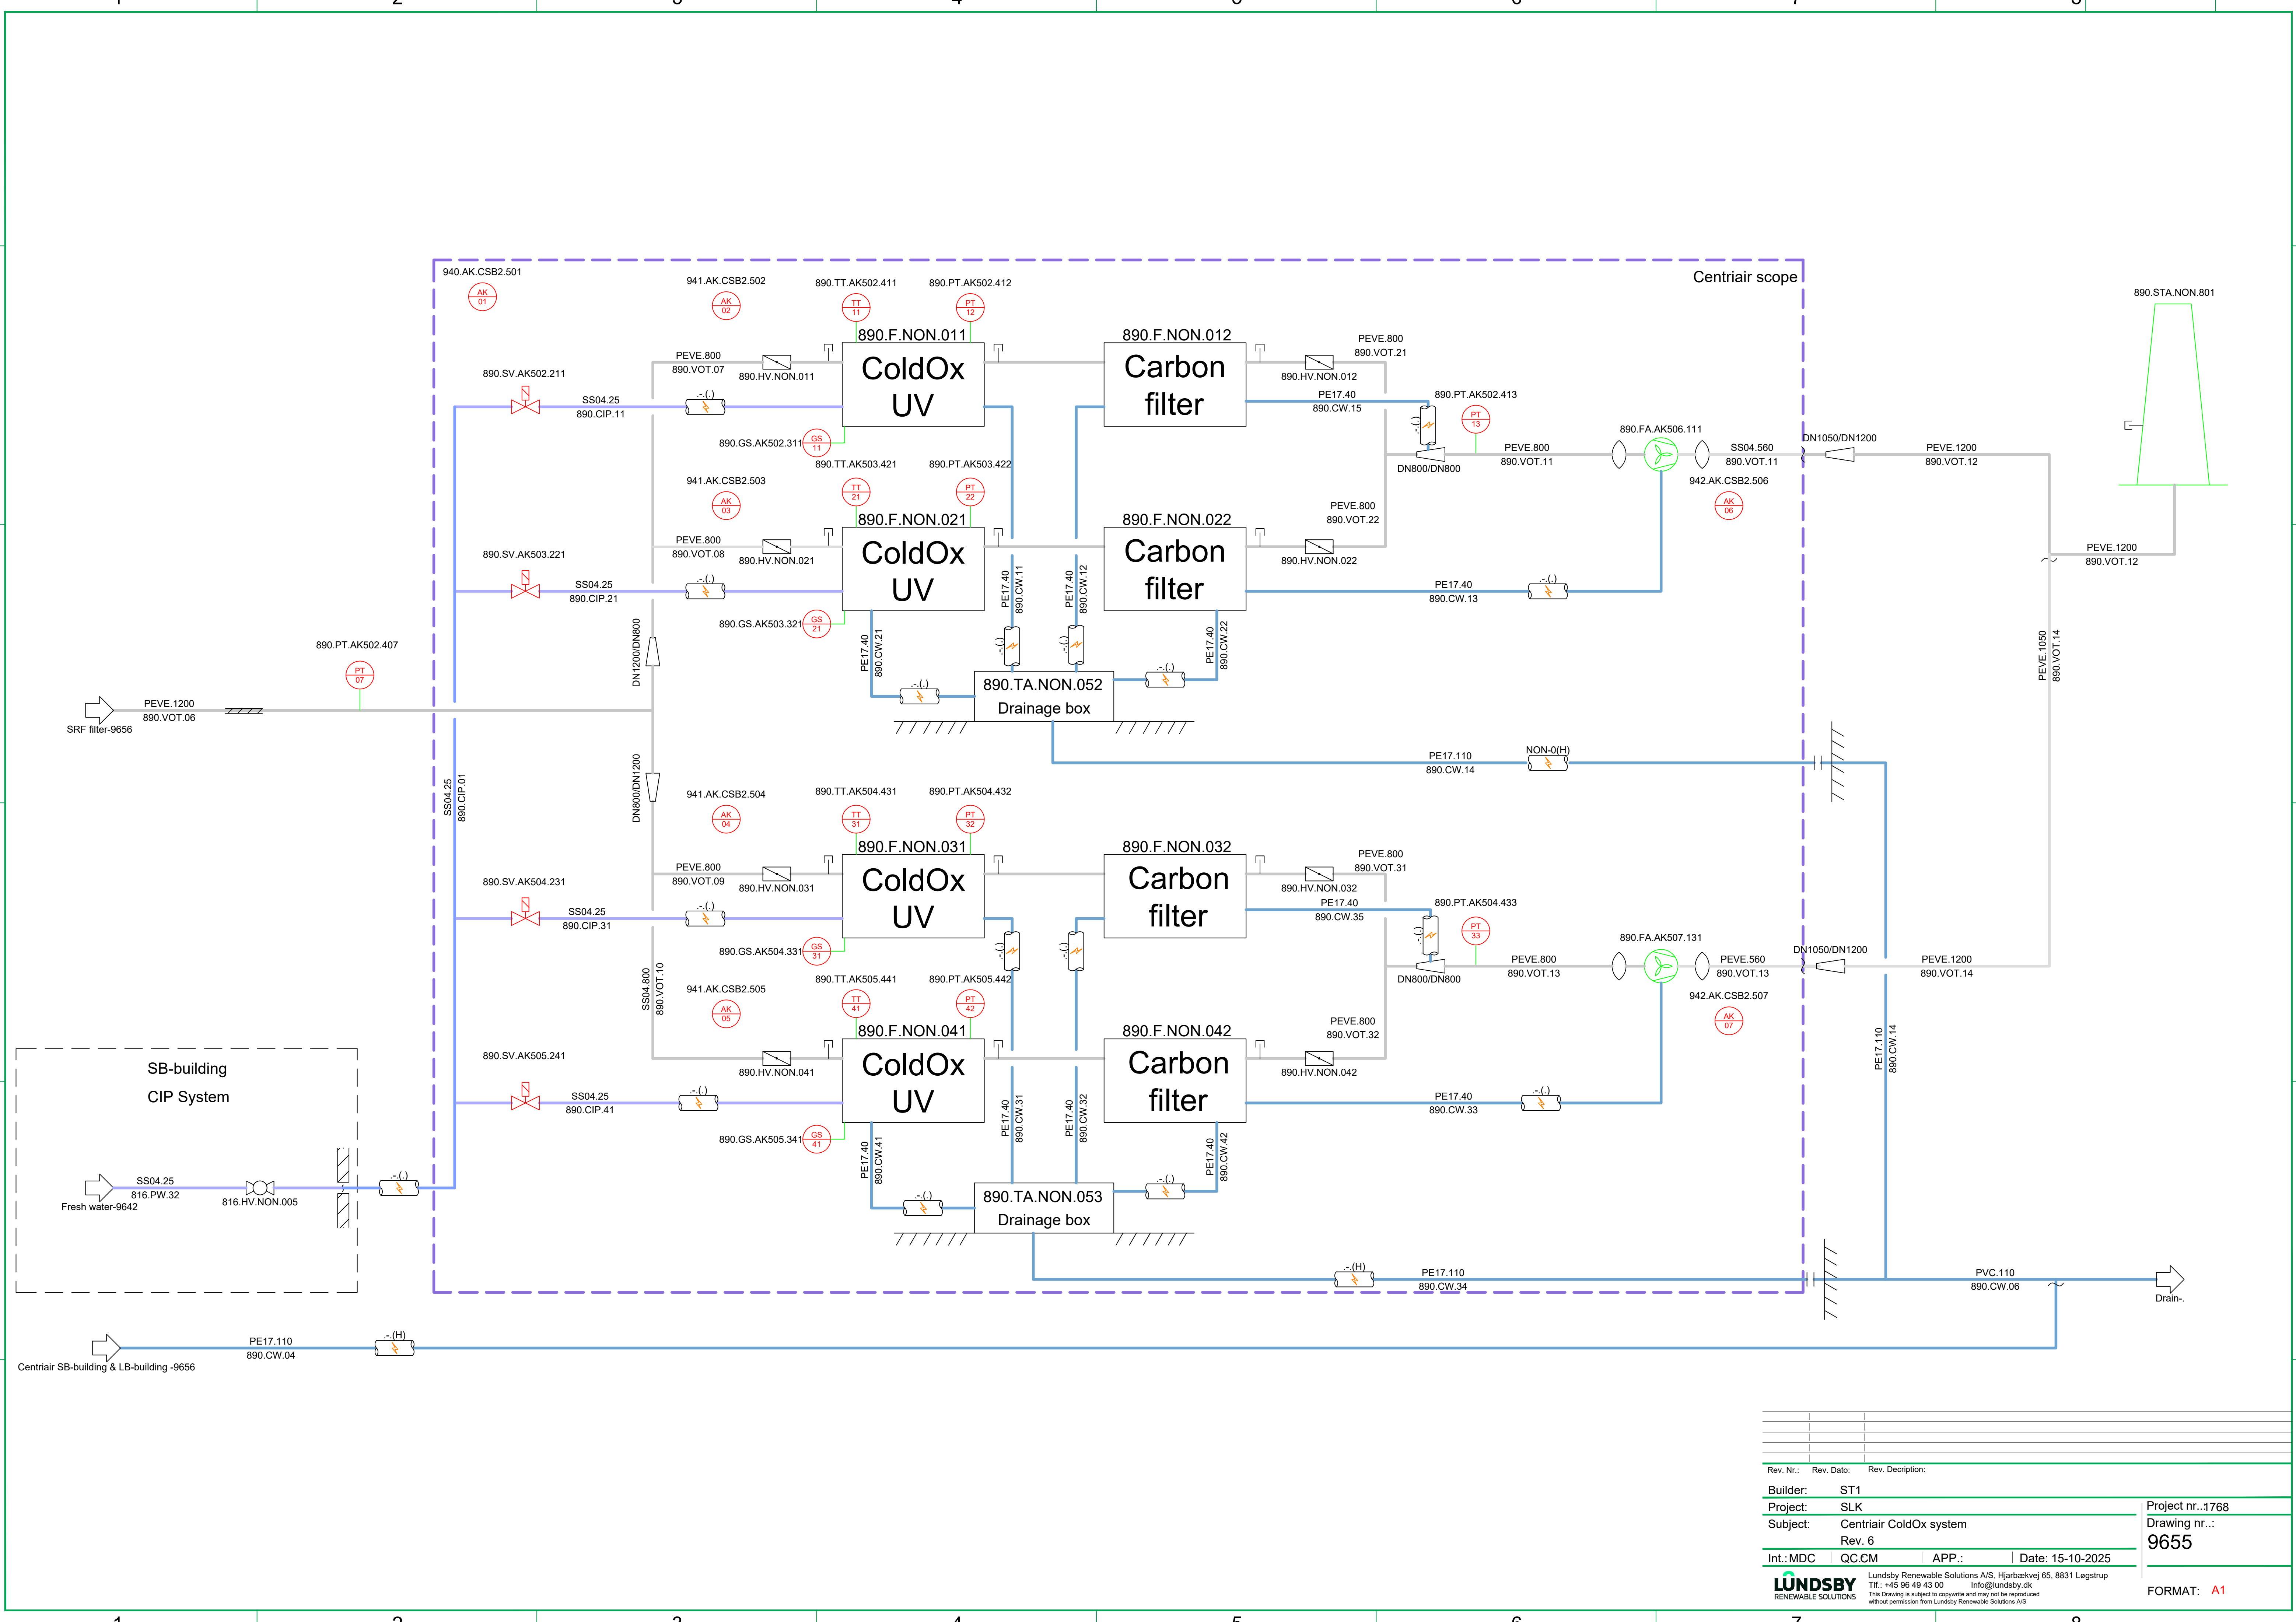

Rev. Nr.:	Rev. Dato:	Rev. Description:
Builder:	ST1	
Project:	SLK	
Subject:	Centriair ColdOx system	
Rev. 6		
Int.:MDC	QC:CM	APP.:
Date: 15-10-2025		
LUNDSBY RENEWABLE SOLUTIONS		
Lundsby Renewable Solutions A/S, Hjarbækvej 65, 8831 Løgstrup Tlf.: +45 96 49 43 00 info@lundsby.dk This drawing is subject to copyright and may not be reproduced without permission from Lundsby Renewable Solutions A/S		
Project nr.:1768 Drawing nr.: 9655		FORMAT: A1

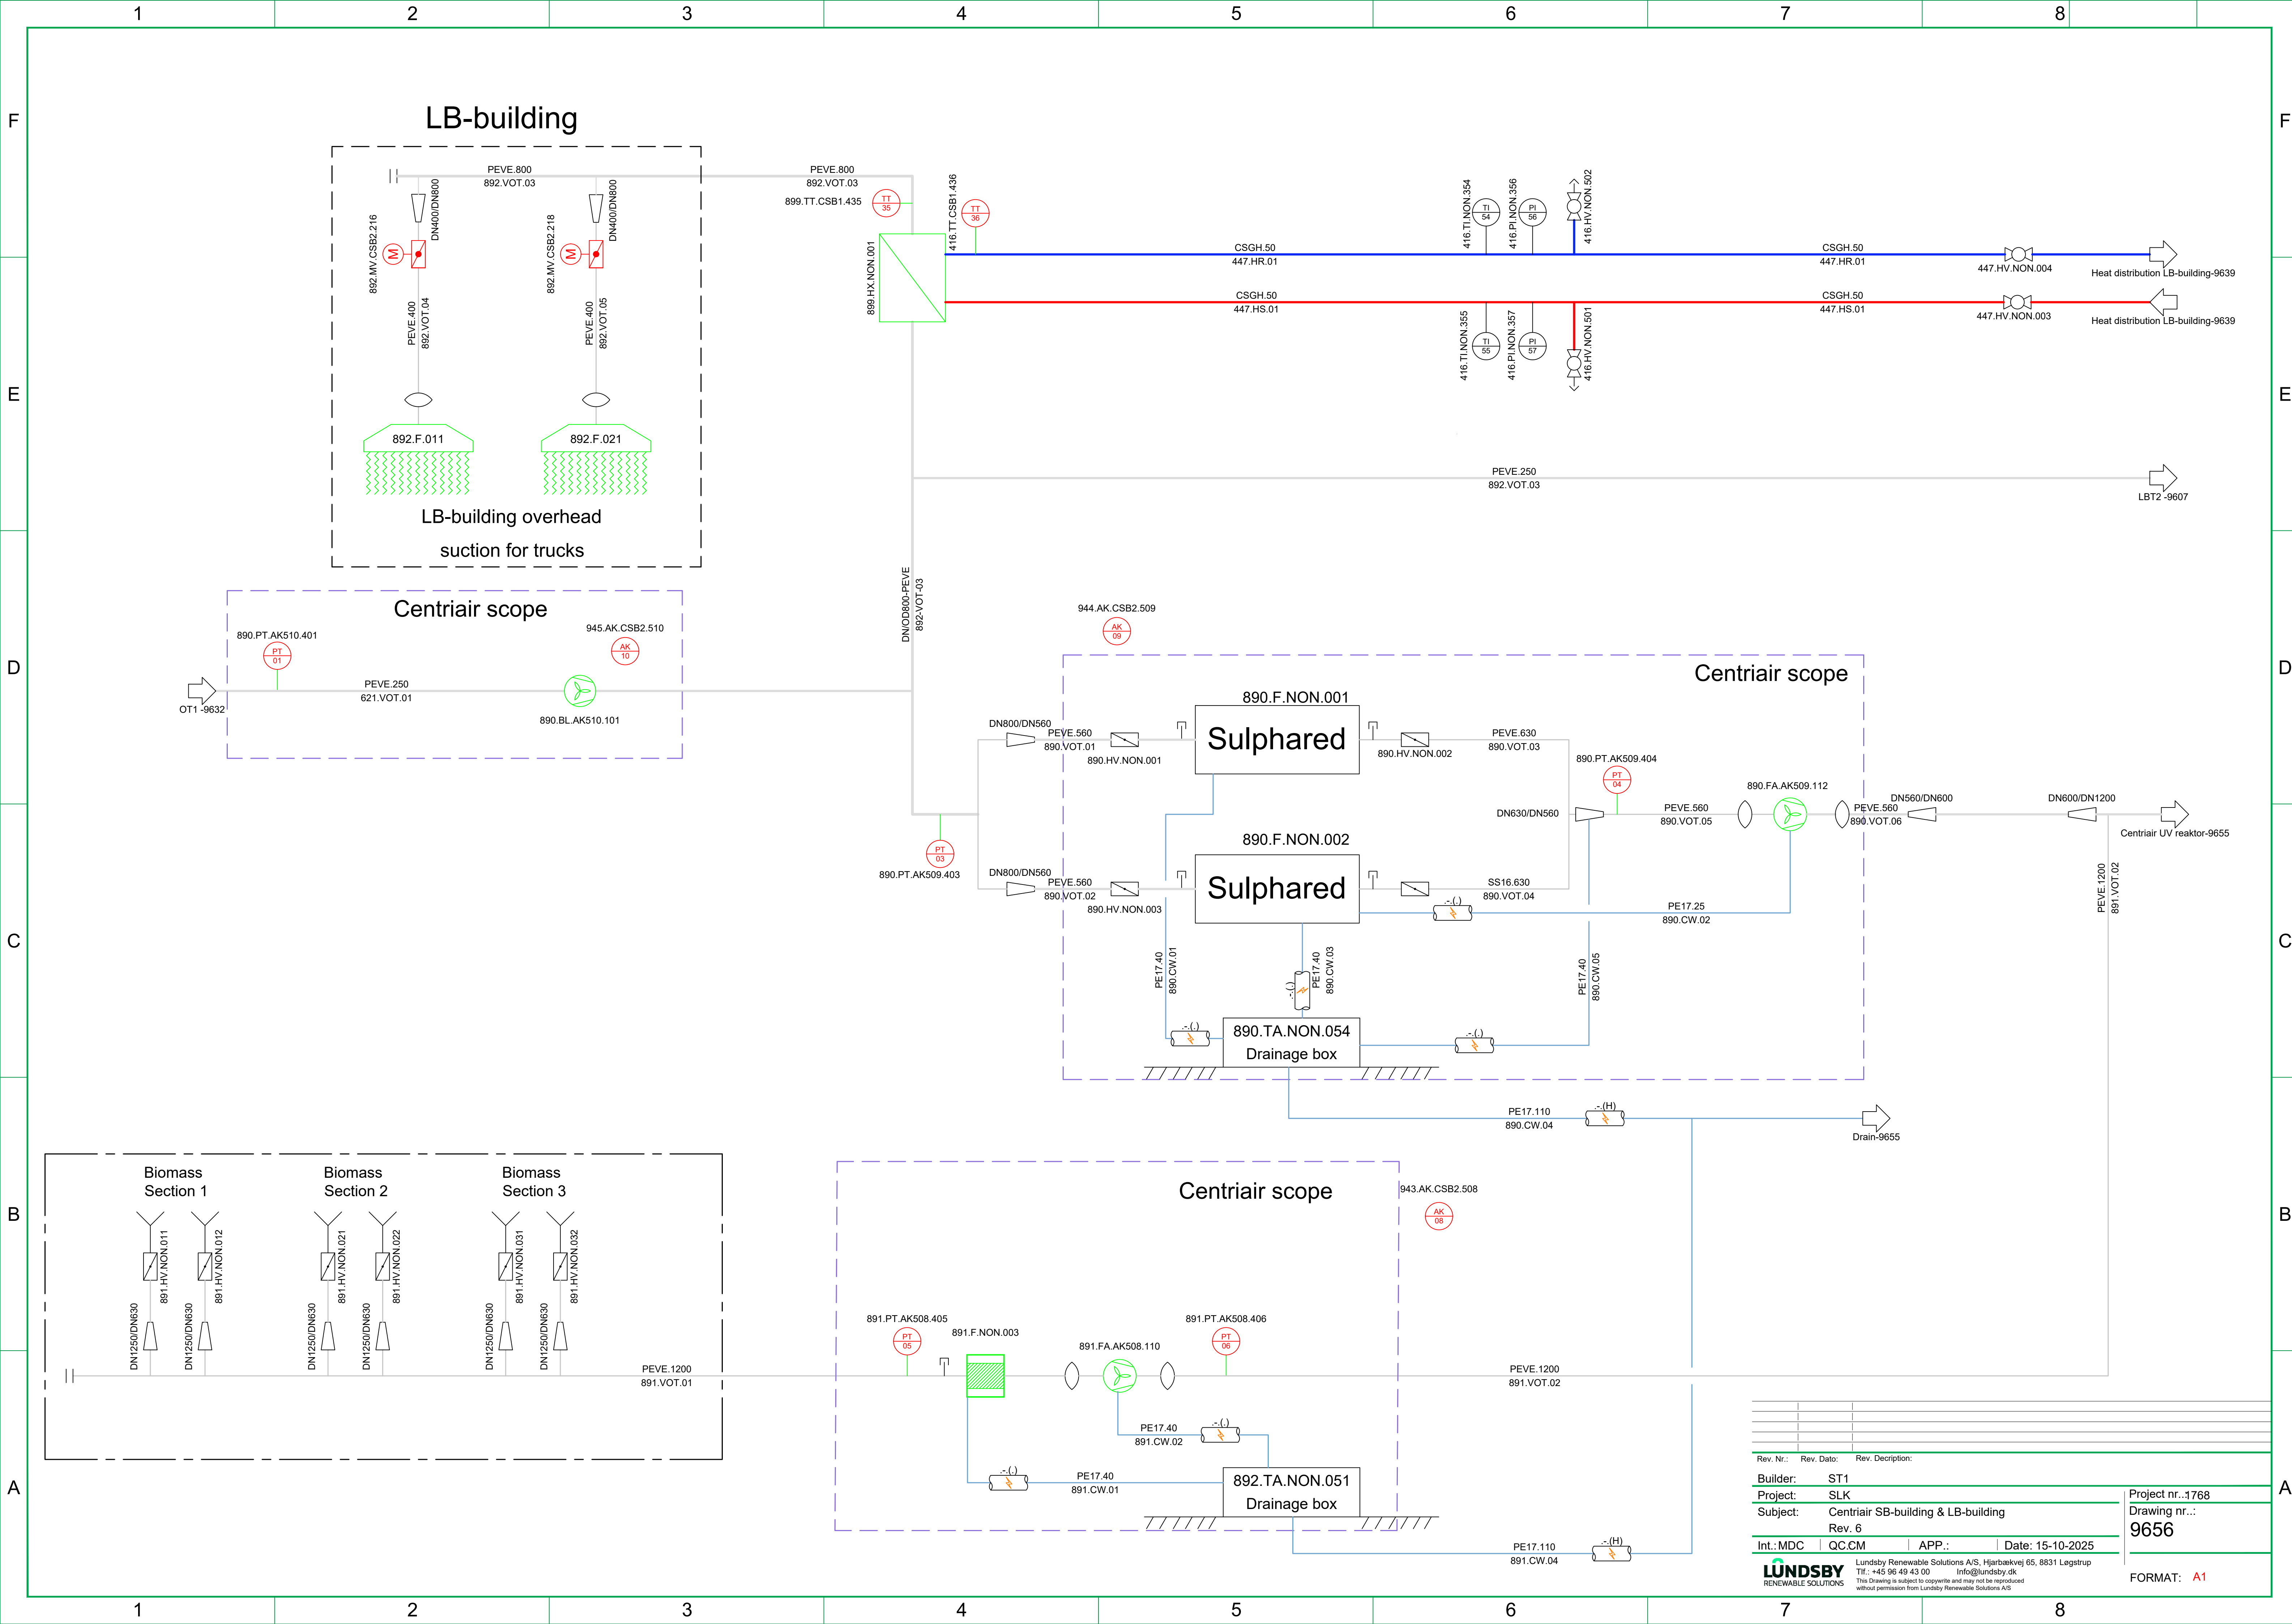

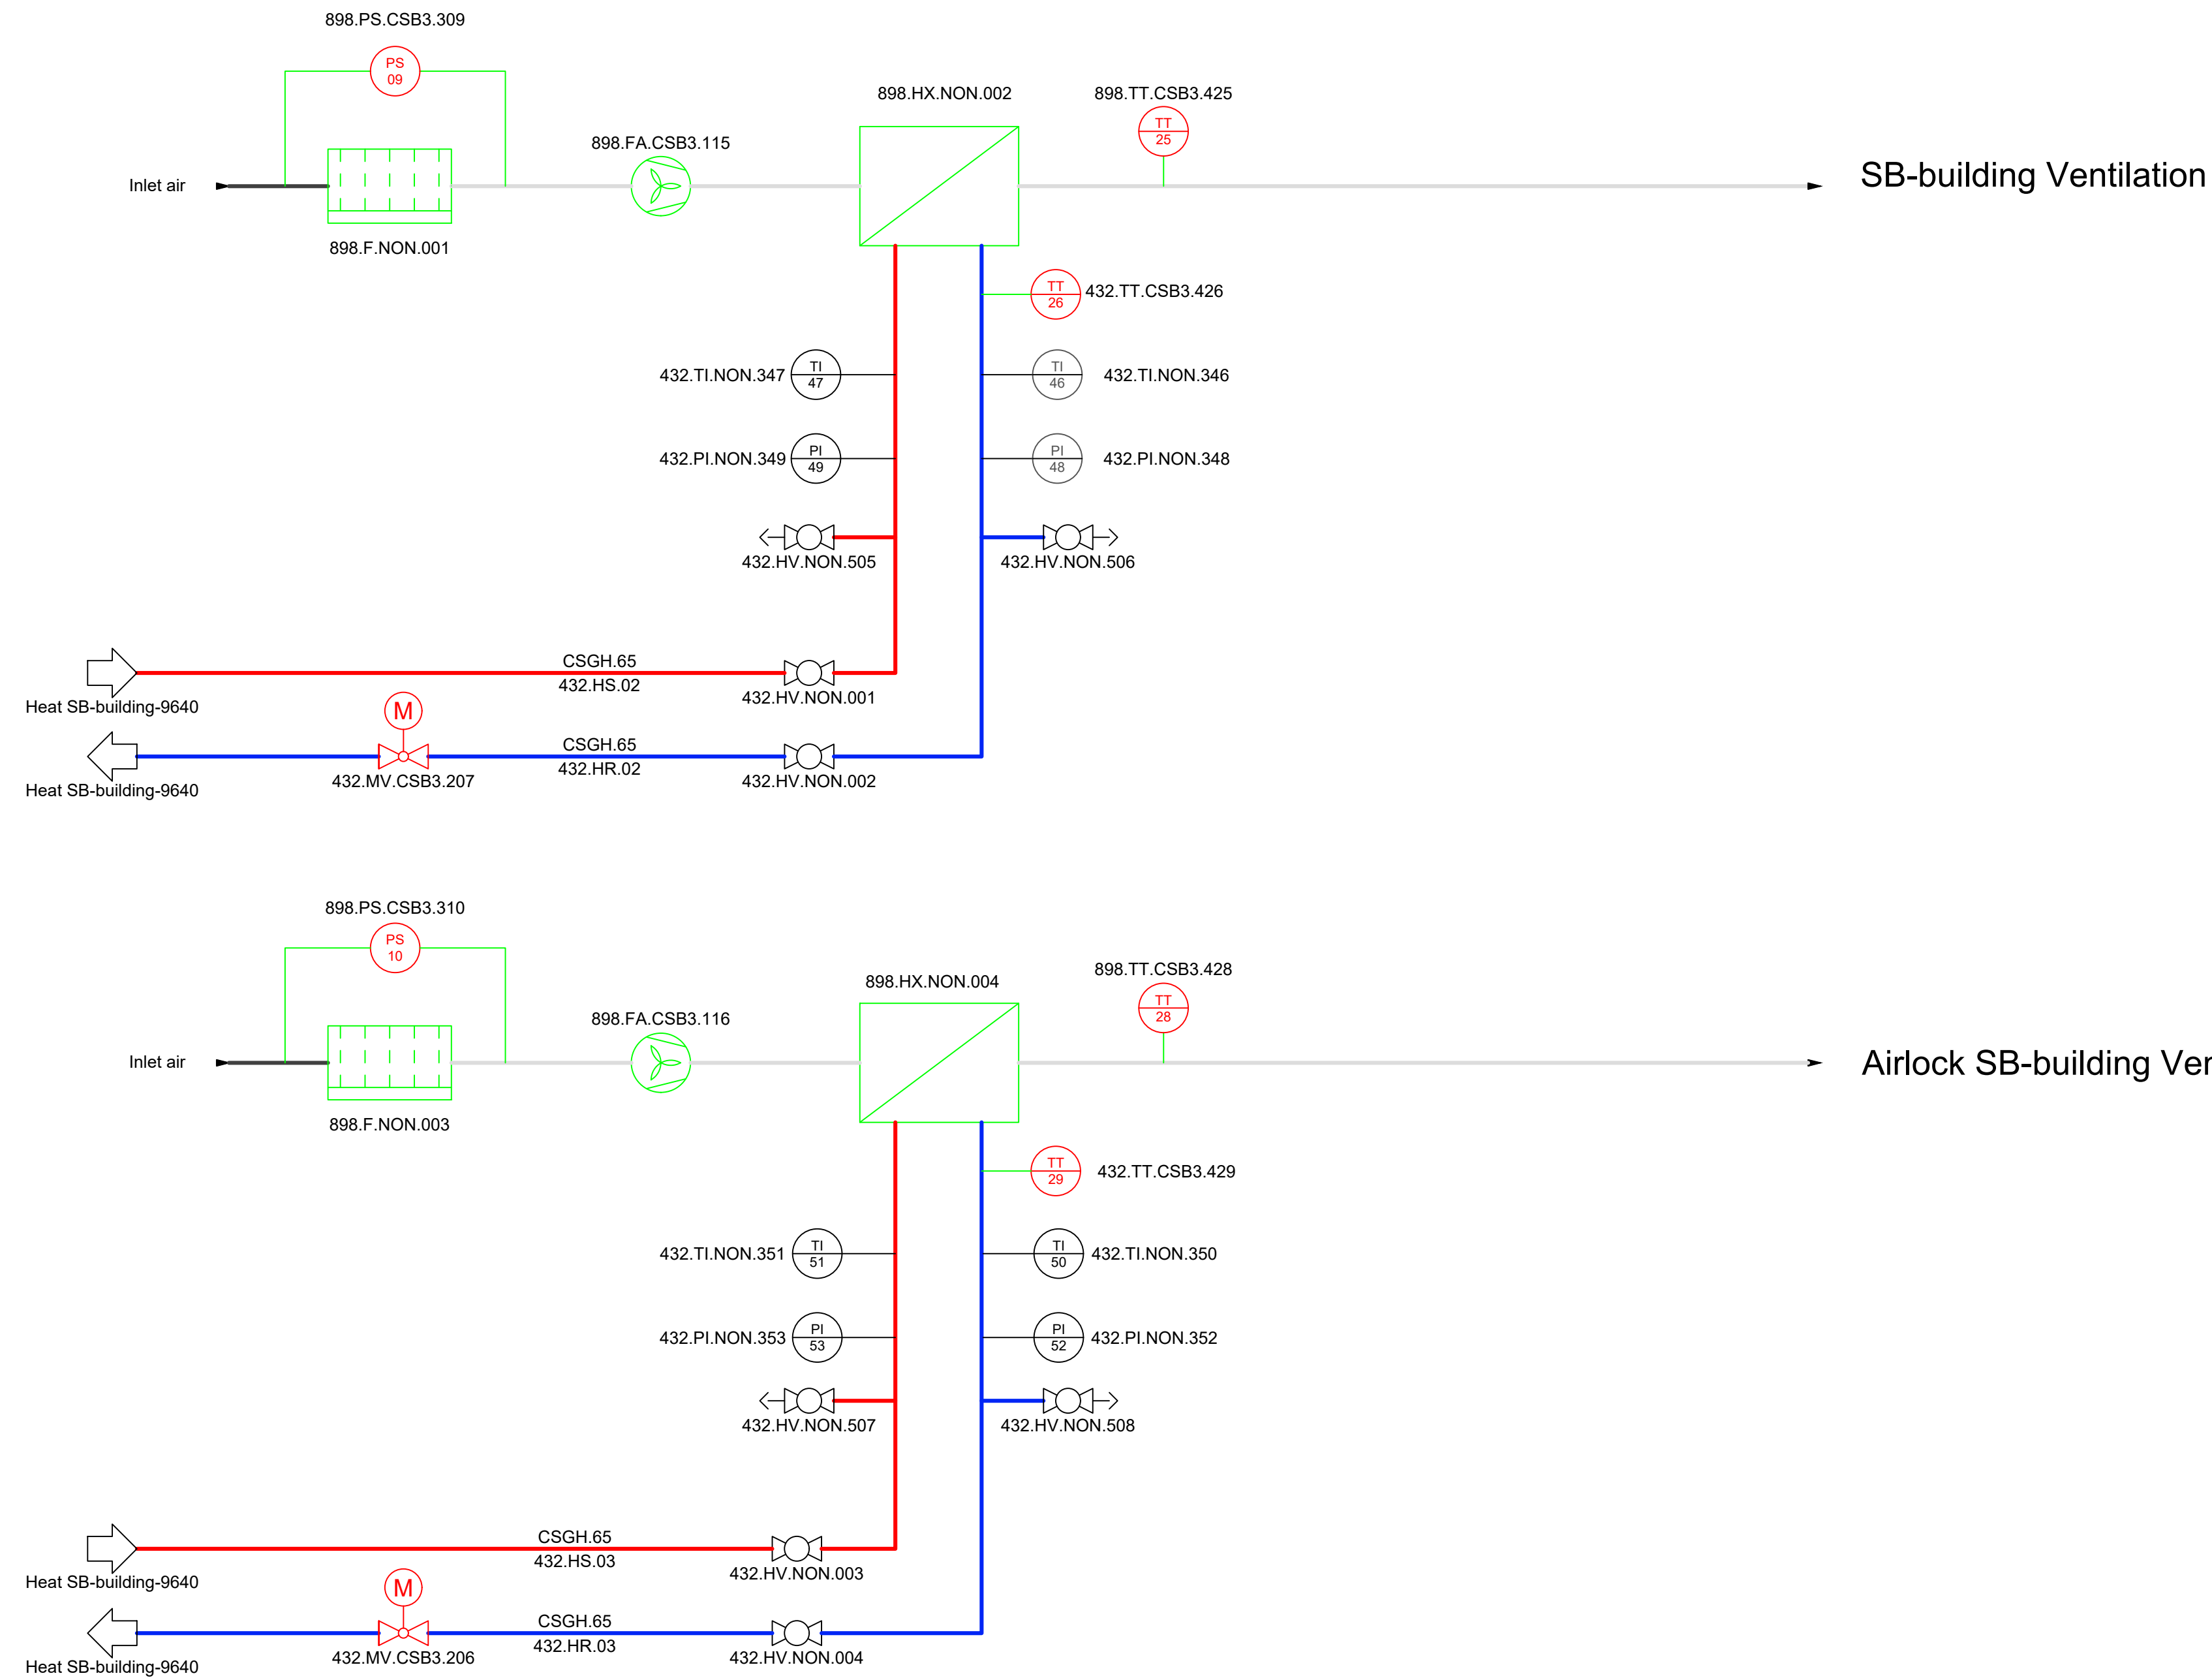

Rev. Nr.:	Rev. Dato:	Rev. Description:	
Builder:	ST1		
Project:	SLK		
Subject:	Ventilation SB-building		
Rev. 6			
Int.:MDC	QC.: CM	APP.:	Date: 15-10-2025
LUNDSBY RENEWABLE SOLUTIONS			Lundsby Renewable Solutions A/S, Hjarbækvej 65, 8831 Løgstrup Tlf.: +45 96 49 43 00 Info@lundsby.dk This Drawing is subject to copyright and may not be reproduced without permission from Lundsby Renewable Solutions A/S
Project nr.: 1768 Drawing nr.: 9657			FORMAT: A1