






Structure of the tagging system

Structure of the component tagging

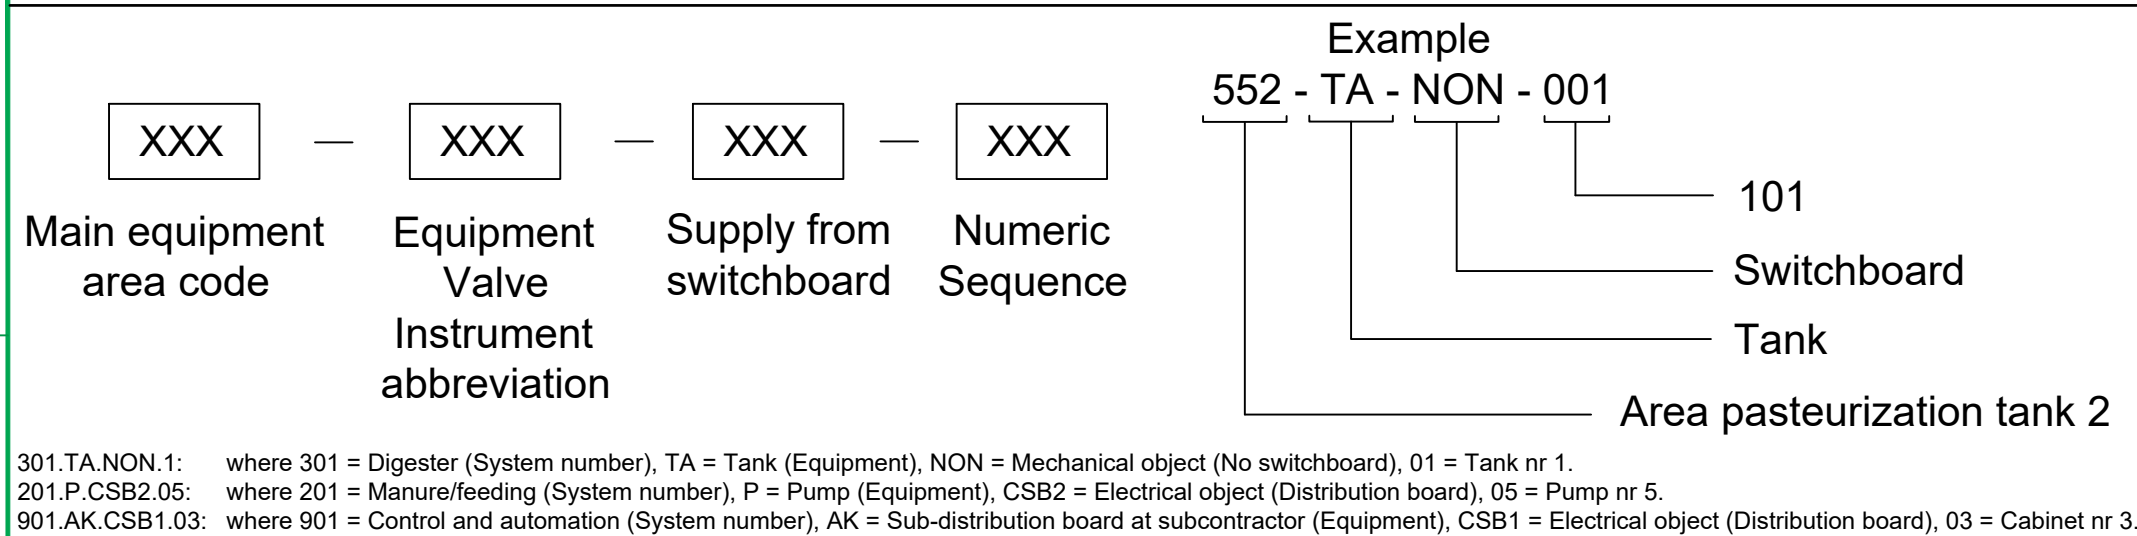

301.TA.NON.1: where 301 = Digester (System number), TA = Tank (Equipment), NON = Mechanical object (No switchboard), 01 = Tank nr 1.
201.P.CSB2.05: where 201 = Manure/feeding (System number), P = Pump (Equipment), CSB2 = Electrical object (Distribution board), 05 = Pump nr 5.
901.AK.CSB1.03: where 901 = Control and automation (System number), AK = Sub-distribution board at subcontractor (Equipment), CSB1 = Electrical object (Distribution board), 03 = Cabinet nr 3.

Lines

 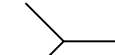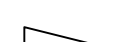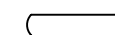Description	Symbol
Subcontractor scope	
Boundary line	
Page connector	
Start pipe - Not linked to page	
End pipe - Not linked to page	
Fald/ Slope	
Insulation	
Electrical Heat tracing	

Building/Area/Tank


Description	Code
Primary digester	PD
Secondary digester	SD
Digester storage	DST
Liquid manure tank	LMT
Liquid biomass tank	LBT
Outlet tank	OT
Blackwater tank	BWT
Tech building	TB
Admin building	ADB
Solid biomass building	SBB
Liquid biomass building	LBB
Plansilo	PS
Pump house	PH
Hygienization tanks	HYG
Flare	FLA
Stack	STA
Odour treatment facility	OD
Upgrade facility	UPG
Liquifaction facility	LIQ
Oil boiler	OB
Wood boiler	WB
Transformer	TR

Media code

Media	Pipe color	RBG color	Code
Heat Return		0,37,245	HR
Heat Supply		255,0,0	HS
Heat Hot Return		255,223,127	HHR
Heat Hot Supply		238,129,129	HHS
Cooling Supply		0,255,183	CS
Cooling Return		126,189,189	CR
Black Water		36,39,132	BW
CIP		253,53,223	CIP
Process Water		170,170,255	PW
Technical Water		69,78,104	TW
Drinking Water		0,0,129	DW
Drinking Water Hot		0,127,255	DWH
Condensate		108,163,208	CW
Steam		255,82,82	ST
Steam Condensate		189,0,0	STC
Liquid Manure (Slurry)		240,130,40	LM
Liquid Biomass (Substrat)		128,0,255	LB
Process Biomass		165,103,82	PB
Hygienized Biomass		169,130,0	HB
Recirculated Biomass		165,103,82	RCB
Ferric Chloride FeCl		145,255,71	FeCl
Ventilation Odour Treatment		199,199,199	VOT
Ventilation Fresh Air		199,199,199	VFA
Compressed Air		64,64,64	CA
Oxygen		0,128,255	O2
Raw Biogas		255,255,0	RB
Return/reject Gas		116,118,4	RG
Nature Gas		0,255,127	NG
Instrument Leader		Green	N/A

Structure of the pipeline tagging system

The pipetag consists of various information about the pipe
Full pipeline tag as shown below

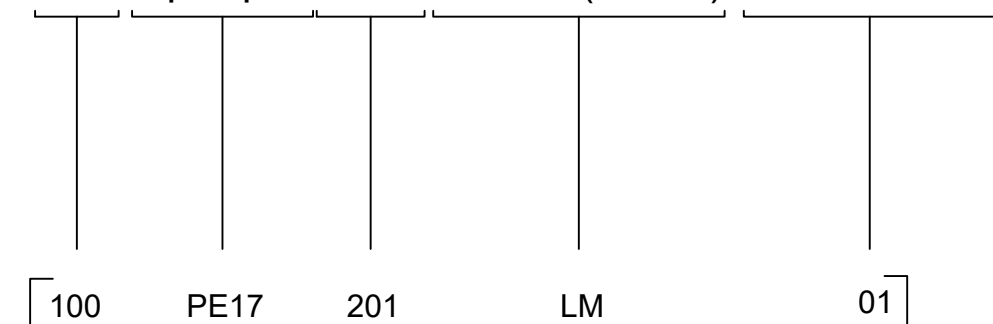

Example

Two (2) digits. Starts with 01
[01]

- Two (2) to four (4) characters (letters)
- [LM - Liquid manure]

Three (3) digits
[201 - Manure feeding in tank 1]

Pipe Spec name
[PE17 - PE100 SDR17]

Pipe size
DN indication for Metric pipes
OD indication for PE-pipe
[This example is OD 100 mm]

The pipe tag will be shown on the P&ID as follows: PipeSpec-Size
Area-Service-Serialnumber

Example of line tag notation on P&ID: PE17-110
201-LM-01

Line color corresponding to table above.
The part below the pipeline is the Unique Line Tag.
Unique Line Tag is generated automatically when creating complete Line Tag.
Unique Line Tag is used by the P3D system when designing pipes in the 3D model and when generating Isometrics.

Rev. Nr.:	Rev. Dato:	Rev. Description:
Builder:	ST1	
Project:	SLK	
Subject:	PID Legend	
	Rev. 6	
Int.: MDC	QC.: CM	APP.: Date: 15-10-2025




Lundbys
 RENEWABLE SOLUTIONS


Lundsby Renewable Solutions A/S, Hjarbækvej 65, 8831 Lægstrup
 Tlf.: +45 96 49 43 00 Info@lundbsby.dk
This Drawing is subject to copyright and may not be reproduced
 without permission from Lundsby Renewable Solutions A/S

Project nr.: 1768
 Drawing nr.:
PID Legend


FORMAT: **A1**


1	2	3	4	5	6	7	8																																						
Valves			Equipment			Piping		Instruments																																					
Hand valves			Pumps / Compressors / Blowers			Piping symbols		Description																																					
Symbols	Code	Description	Symbols	Code	Description	Symbols	Code	Description																																					
	HV	General valve		P	Pump (General)		MX	Bio mixer	Instruments will be tagged XXX - XX - XXX - XXX Main area code Letter code Switchboard Numeric sequence First letter XX Succeeding letter XX Numeric sequence Temperature indication 01 Level switch 02 Instruments with succeeding letter T is an analog signal. Instruments with succeeding letter S is a digital signal. <table><tr><th>Instruments</th><th>Abbreviation</th></tr><tr><td>Analyze Indicator</td><td>AI</td></tr><tr><td>Analyse Transmitter</td><td>AT</td></tr><tr><td>Energi Transmitter</td><td>ET</td></tr><tr><td>Flow Indicator</td><td>FI</td></tr><tr><td>Flow Transmitter</td><td>FT</td></tr><tr><td>Flow Switch</td><td>FS</td></tr><tr><td>Flow Transmitter</td><td>FT</td></tr><tr><td>General Switch</td><td>GS</td></tr><tr><td>Level Switch</td><td>LS</td></tr><tr><td>Level Indicator</td><td>LI</td></tr><tr><td>Level Transmitter</td><td>LT</td></tr><tr><td>Pressure Indicator</td><td>PI</td></tr><tr><td>Pressure Switch</td><td>PS</td></tr><tr><td>Pressure Transmitter</td><td>PT</td></tr><tr><td>Thermometer</td><td>TI</td></tr><tr><td>Temperature Transmitter</td><td>TT</td></tr><tr><td>Weight Transmitter</td><td>WT</td></tr></table>	Instruments	Abbreviation	Analyze Indicator	AI	Analyse Transmitter	AT	Energi Transmitter	ET	Flow Indicator	FI	Flow Transmitter	FT	Flow Switch	FS	Flow Transmitter	FT	General Switch	GS	Level Switch	LS	Level Indicator	LI	Level Transmitter	LT	Pressure Indicator	PI	Pressure Switch	PS	Pressure Transmitter	PT	Thermometer	TI	Temperature Transmitter	TT	Weight Transmitter	WT
Instruments	Abbreviation	
Analyze Indicator	AI	
Analyse Transmitter	AT	
Energi Transmitter	ET	
Flow Indicator	FI	
Flow Transmitter	FT	
Flow Switch	FS	
Flow Transmitter	FT	
General Switch	GS	
Level Switch	LS	
Level Indicator	LI	
Level Transmitter	LT	
Pressure Indicator	PI	
Pressure Switch	PS	
Pressure Transmitter	PT	
Thermometer	TI	
Temperature Transmitter	TT	
Weight Transmitter	WT	
	HV	Ball valve		P	Positive displacement pump		MC	Premix																																					
	HV	Butterfly valve		P	Helical rotor pump		CV	Debris lift unit																																					
	HV	Globe valve		P	Centrifugal pump		CV	Screw conveyor																																					
	HV	Three way valve		P	Peristaltic pump		CV	Belt conveyor																																					
	HV	Ground covered valve		MC	Rotacut		CRA	Crane																																					
	BV	Balancing valve		MC	Shredder		CH	ISO Stack - Chimney																																					
				FA	Blower		FL	Flare																																					
				CO	General compressor		PD	Pulsation damper																																					
							SP	Screw press																																					
Actuated valves / Regulating valves			Heating and Cooling	
	MV/RV	Motor ball valve		HX	Heat exchanger - Shell & tube	
	MV/RV	Motor butterfly valve		HX	Heat exchanger - plate	
	AV/RV	Pneumatic ball valve		HX	Heat exchanger - double pipe	
	AV/RV	Pneumatic valve		HX	Heating coil (in tank)	
	AV	Solenoid valve		HS	Heatpump	
Safety valves			Tank equipment			Tanks																																							
	SV	Exhaust valve covers		AG	ISO Agitator - Propeller		DT	Digester tank	<table><tr><th>Category</th><th>Numbers</th></tr><tr><td>Manual valves</td><td>001-099</td></tr><tr><td>Manual regulation valves</td><td>101-199</td></tr><tr><td>Pneumatic, electrical, solenoid</td><td>201-299</td></tr><tr><td>-</td><td>301-399</td></tr><tr><td>Check, Non-return valves</td><td>401-499</td></tr><tr><td>Drain, venting valves</td><td>501-599</td></tr><tr><td>Self-regulating valves (thermal/pressure)</td><td>601-699</td></tr><tr><td>Instrument valves</td><td>701-799</td></tr><tr><td>-</td><td>801-899</td></tr><tr><td>Safety valves</td><td>901-999</td></tr></table> Revision clouds	Category	Numbers	Manual valves	001-099	Manual regulation valves	101-199	Pneumatic, electrical, solenoid	201-299	-	301-399	Check, Non-return valves	401-499	Drain, venting valves	501-599	Self-regulating valves (thermal/pressure)	601-699	Instrument valves	701-799	-	801-899	Safety valves	901-999														
Category	Numbers	
Manual valves	001-099	
Manual regulation valves	101-199	
Pneumatic, electrical, solenoid	201-299	
-	301-399	
Check, Non-return valves	401-499	
Drain, venting valves	501-599	
Self-regulating valves (thermal/pressure)	601-699	
Instrument valves	701-799	
-	801-899	
Safety valves	901-999	
	SV	Safety valve		AG	Agitator		ST	Storage tank																																					
	SV	Breather valve		LA	Light		DT/ST	Storage tank with cover																																					
				CA	Camera		HT	Gas/Hyginisation tank																																					
				FH	Foam hatch		TA	Buried tank																																					
Mechanical valves			Filters and Vessels	
	PV	Pressure holding valve		AT	General filter / Forfilter	
	CV	Check valve		AT	General liquid	
	VV	Venting valve		AT	Drier - General	
Miscellaneous additional valve symbols				F	Suction hood	
		Operator lock mechanism		EXP	Expansion tank	

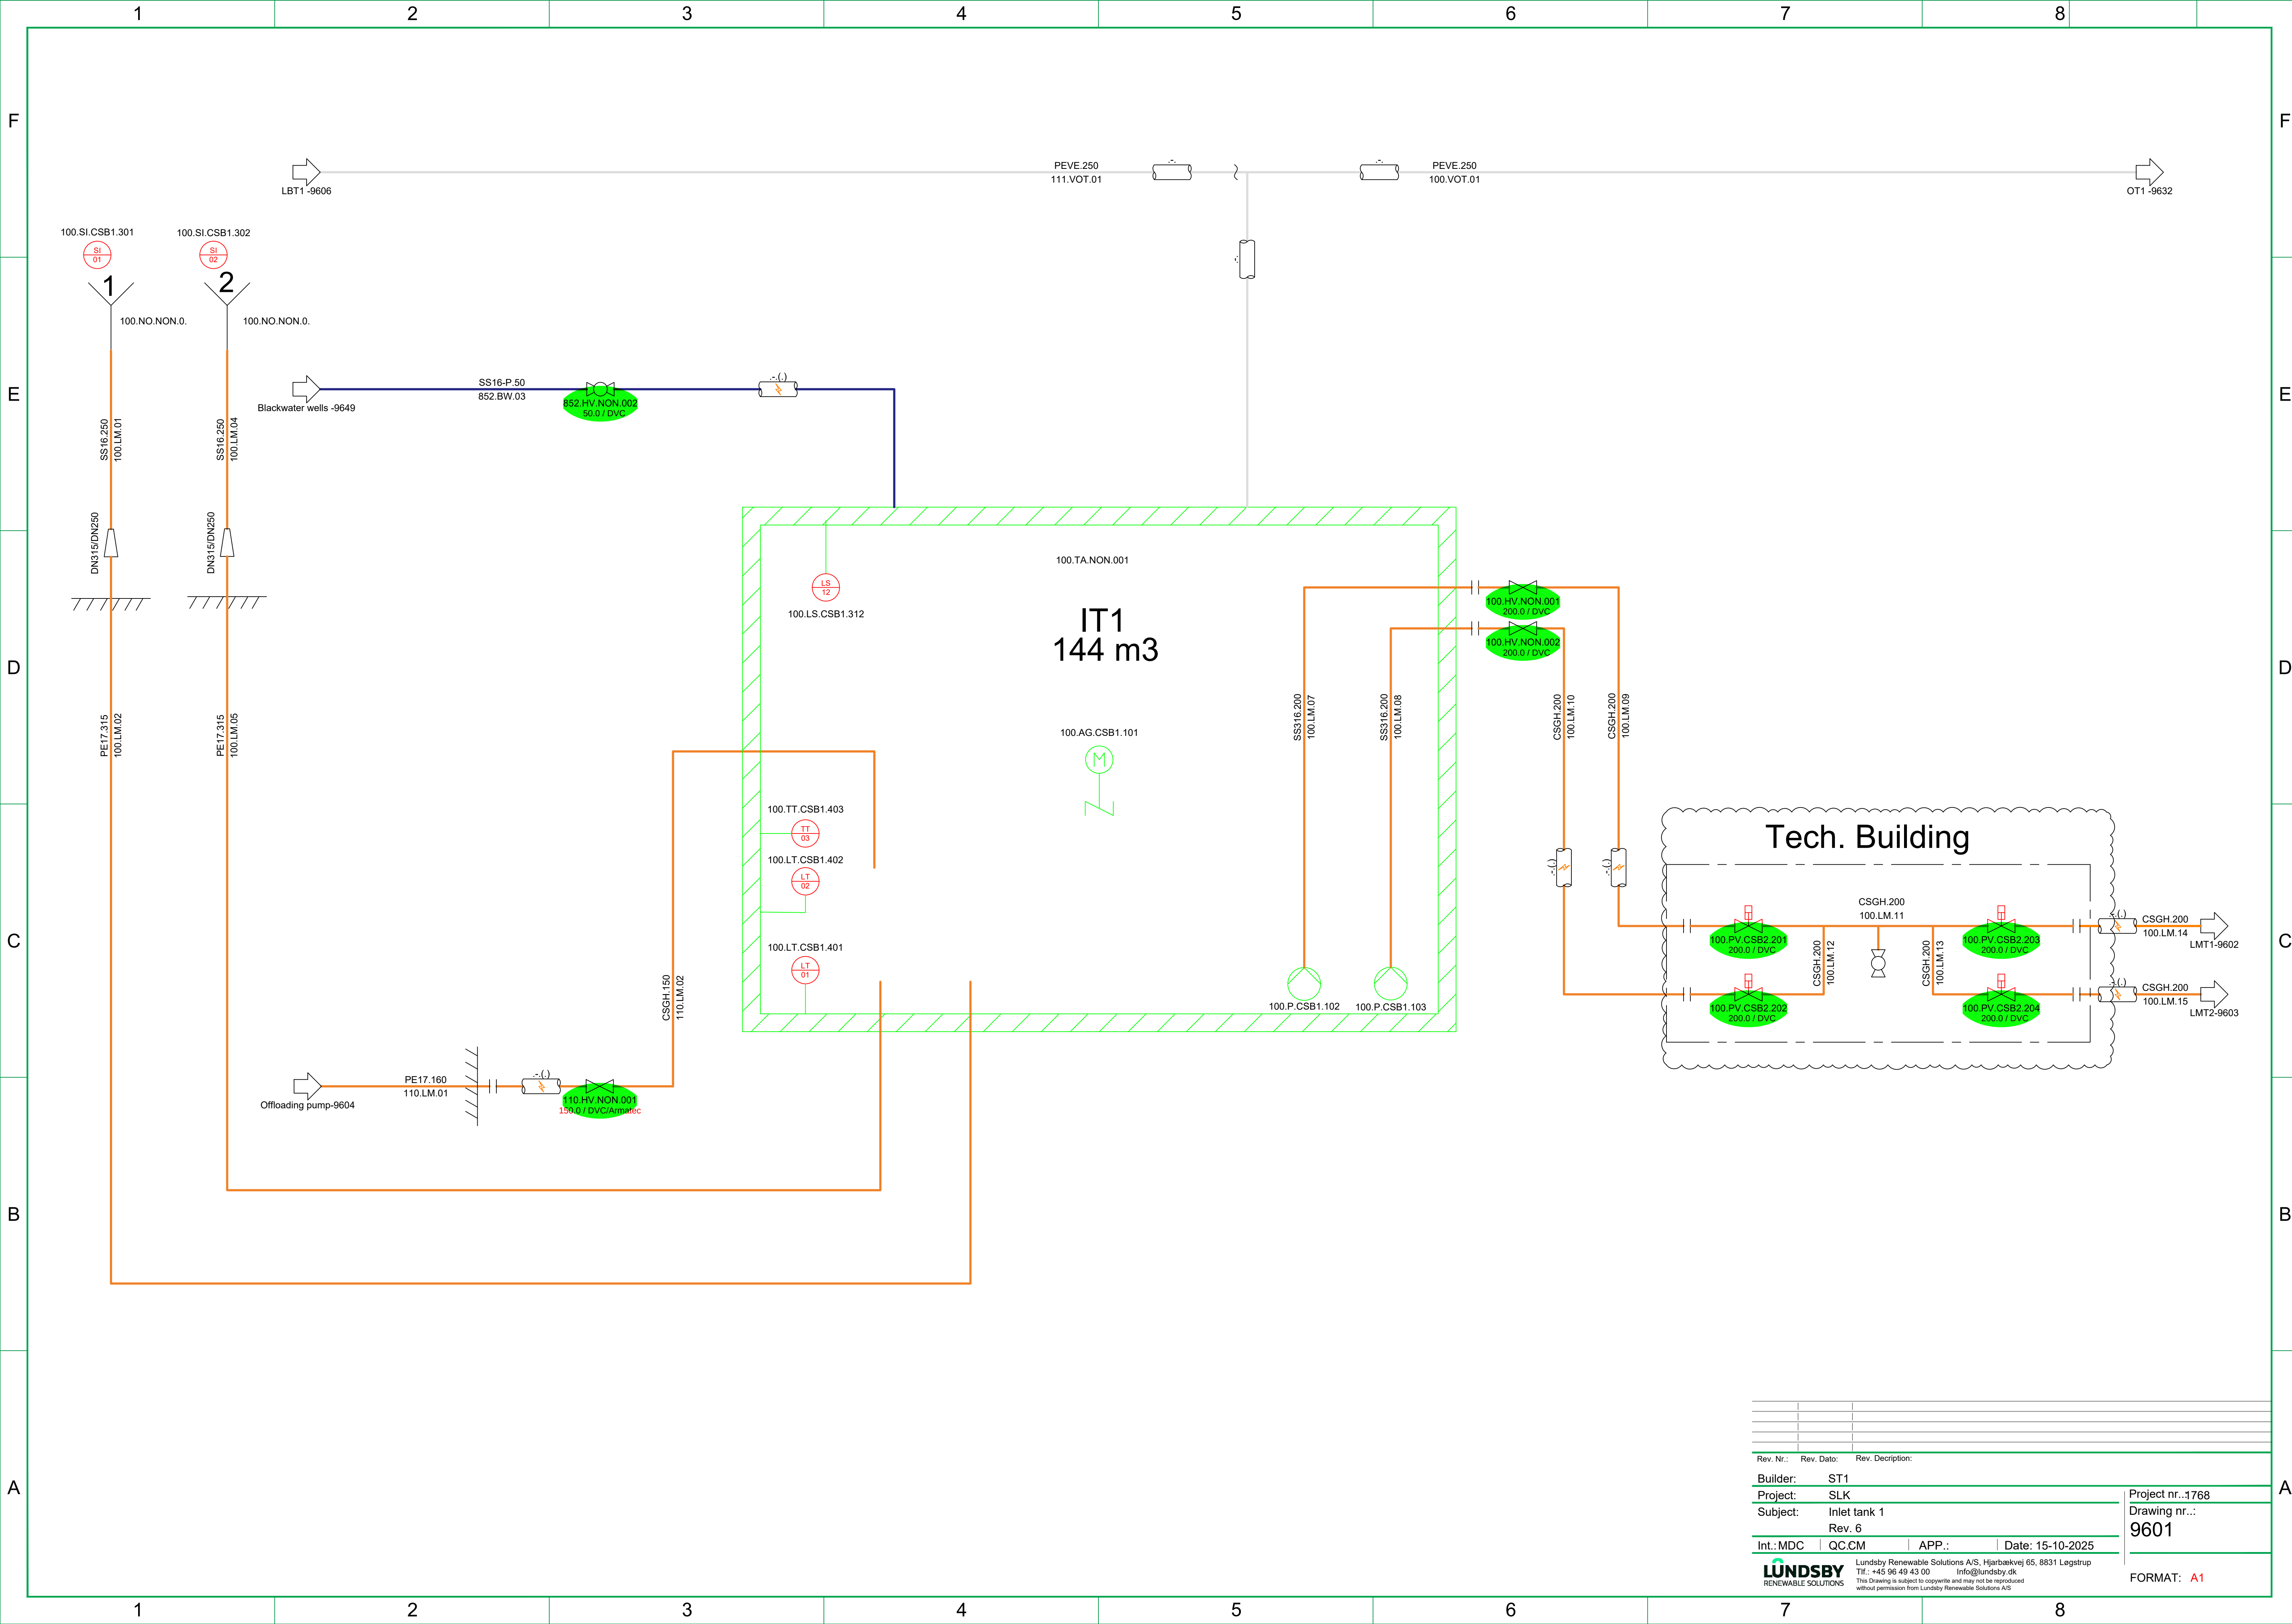

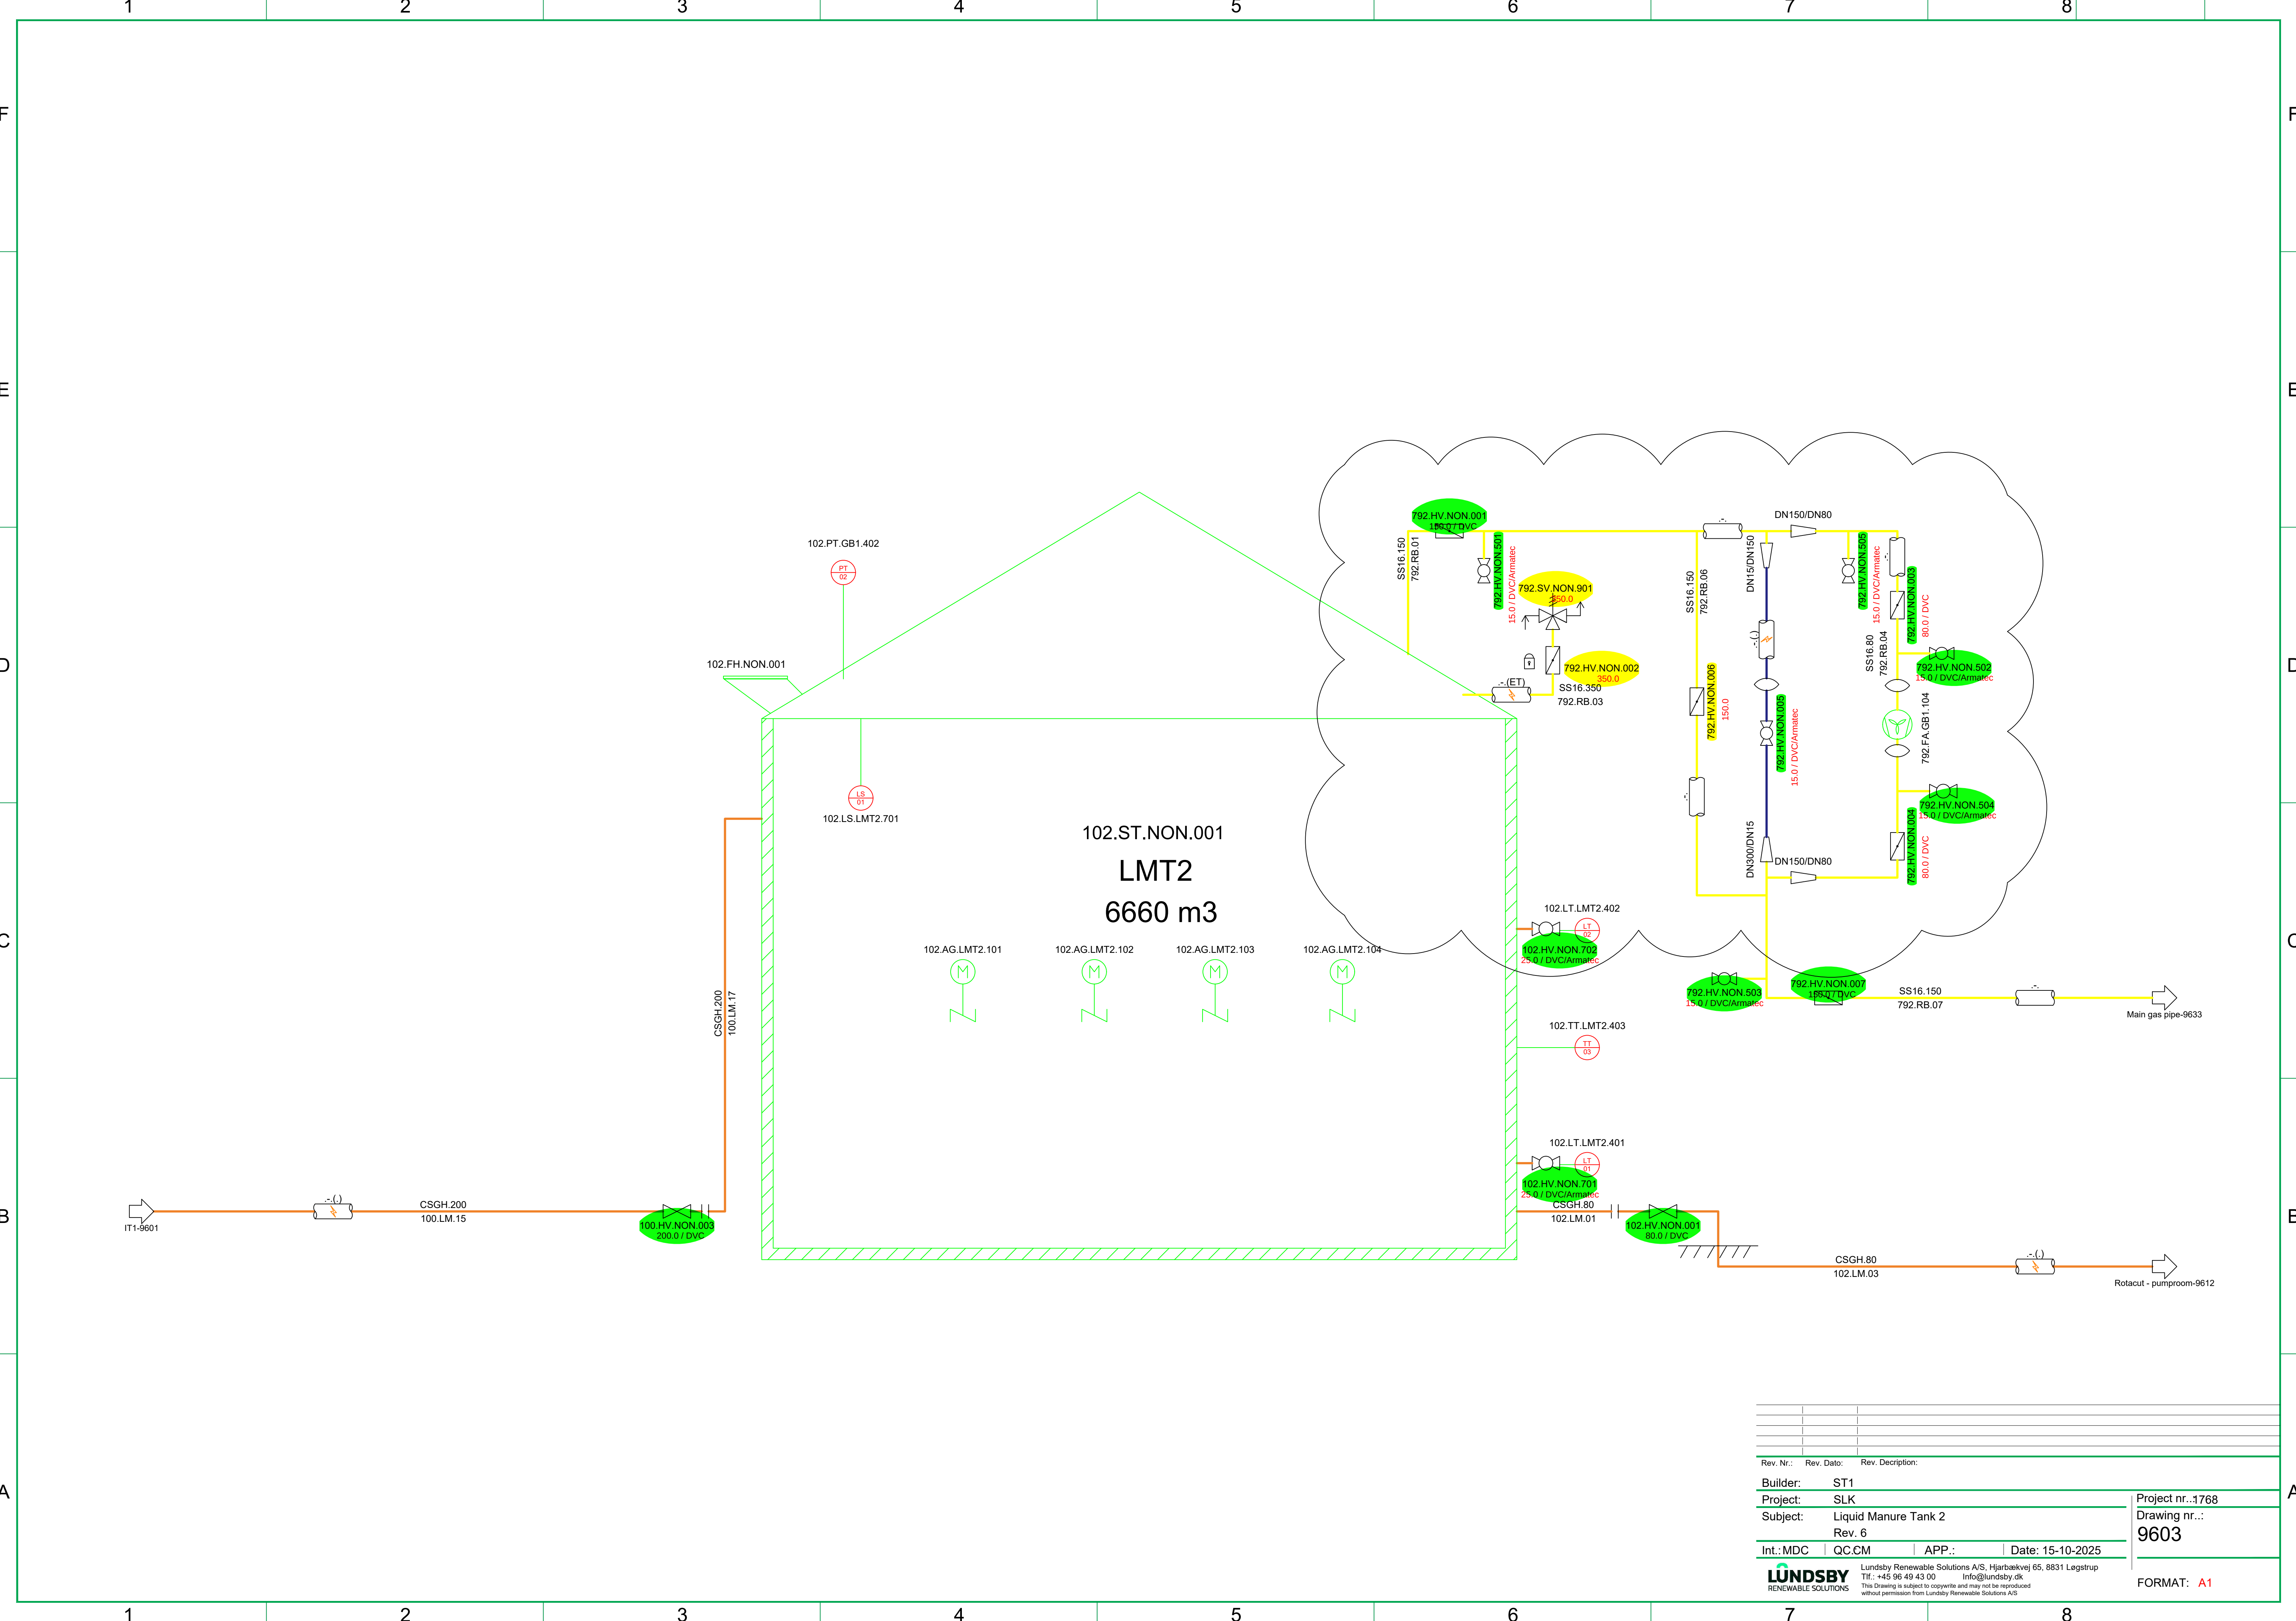


Rev. Nr.:	Rev. Dato:	Rev. Description:			
Builder:	ST1				
Project:	SLK				
Subject:	Liquid Manure Tank 2				
	Rev. 6				
Int.:MDC	QC:CM	APP.:	Date: 15-10-2025		
		Lundsby Renewable Solutions A/S, Hjarbækvej 65, 8831 Legstrup Tlf.: +45 96 49 43 00 Info@lundsby.dk This Drawing is subject to copyright and may not be reproduced without permission from Lundsby Renewable Solutions A/S			
		Project nr.:1768		Drawing nr.: 9603	
		FORMAT: A1			

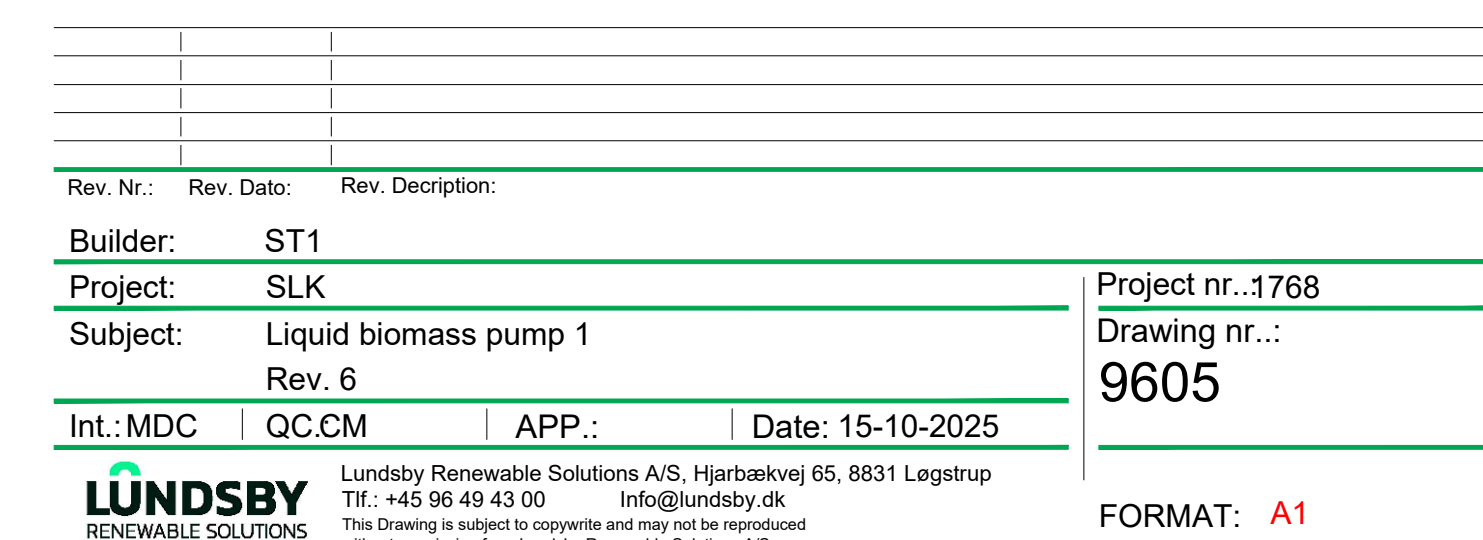


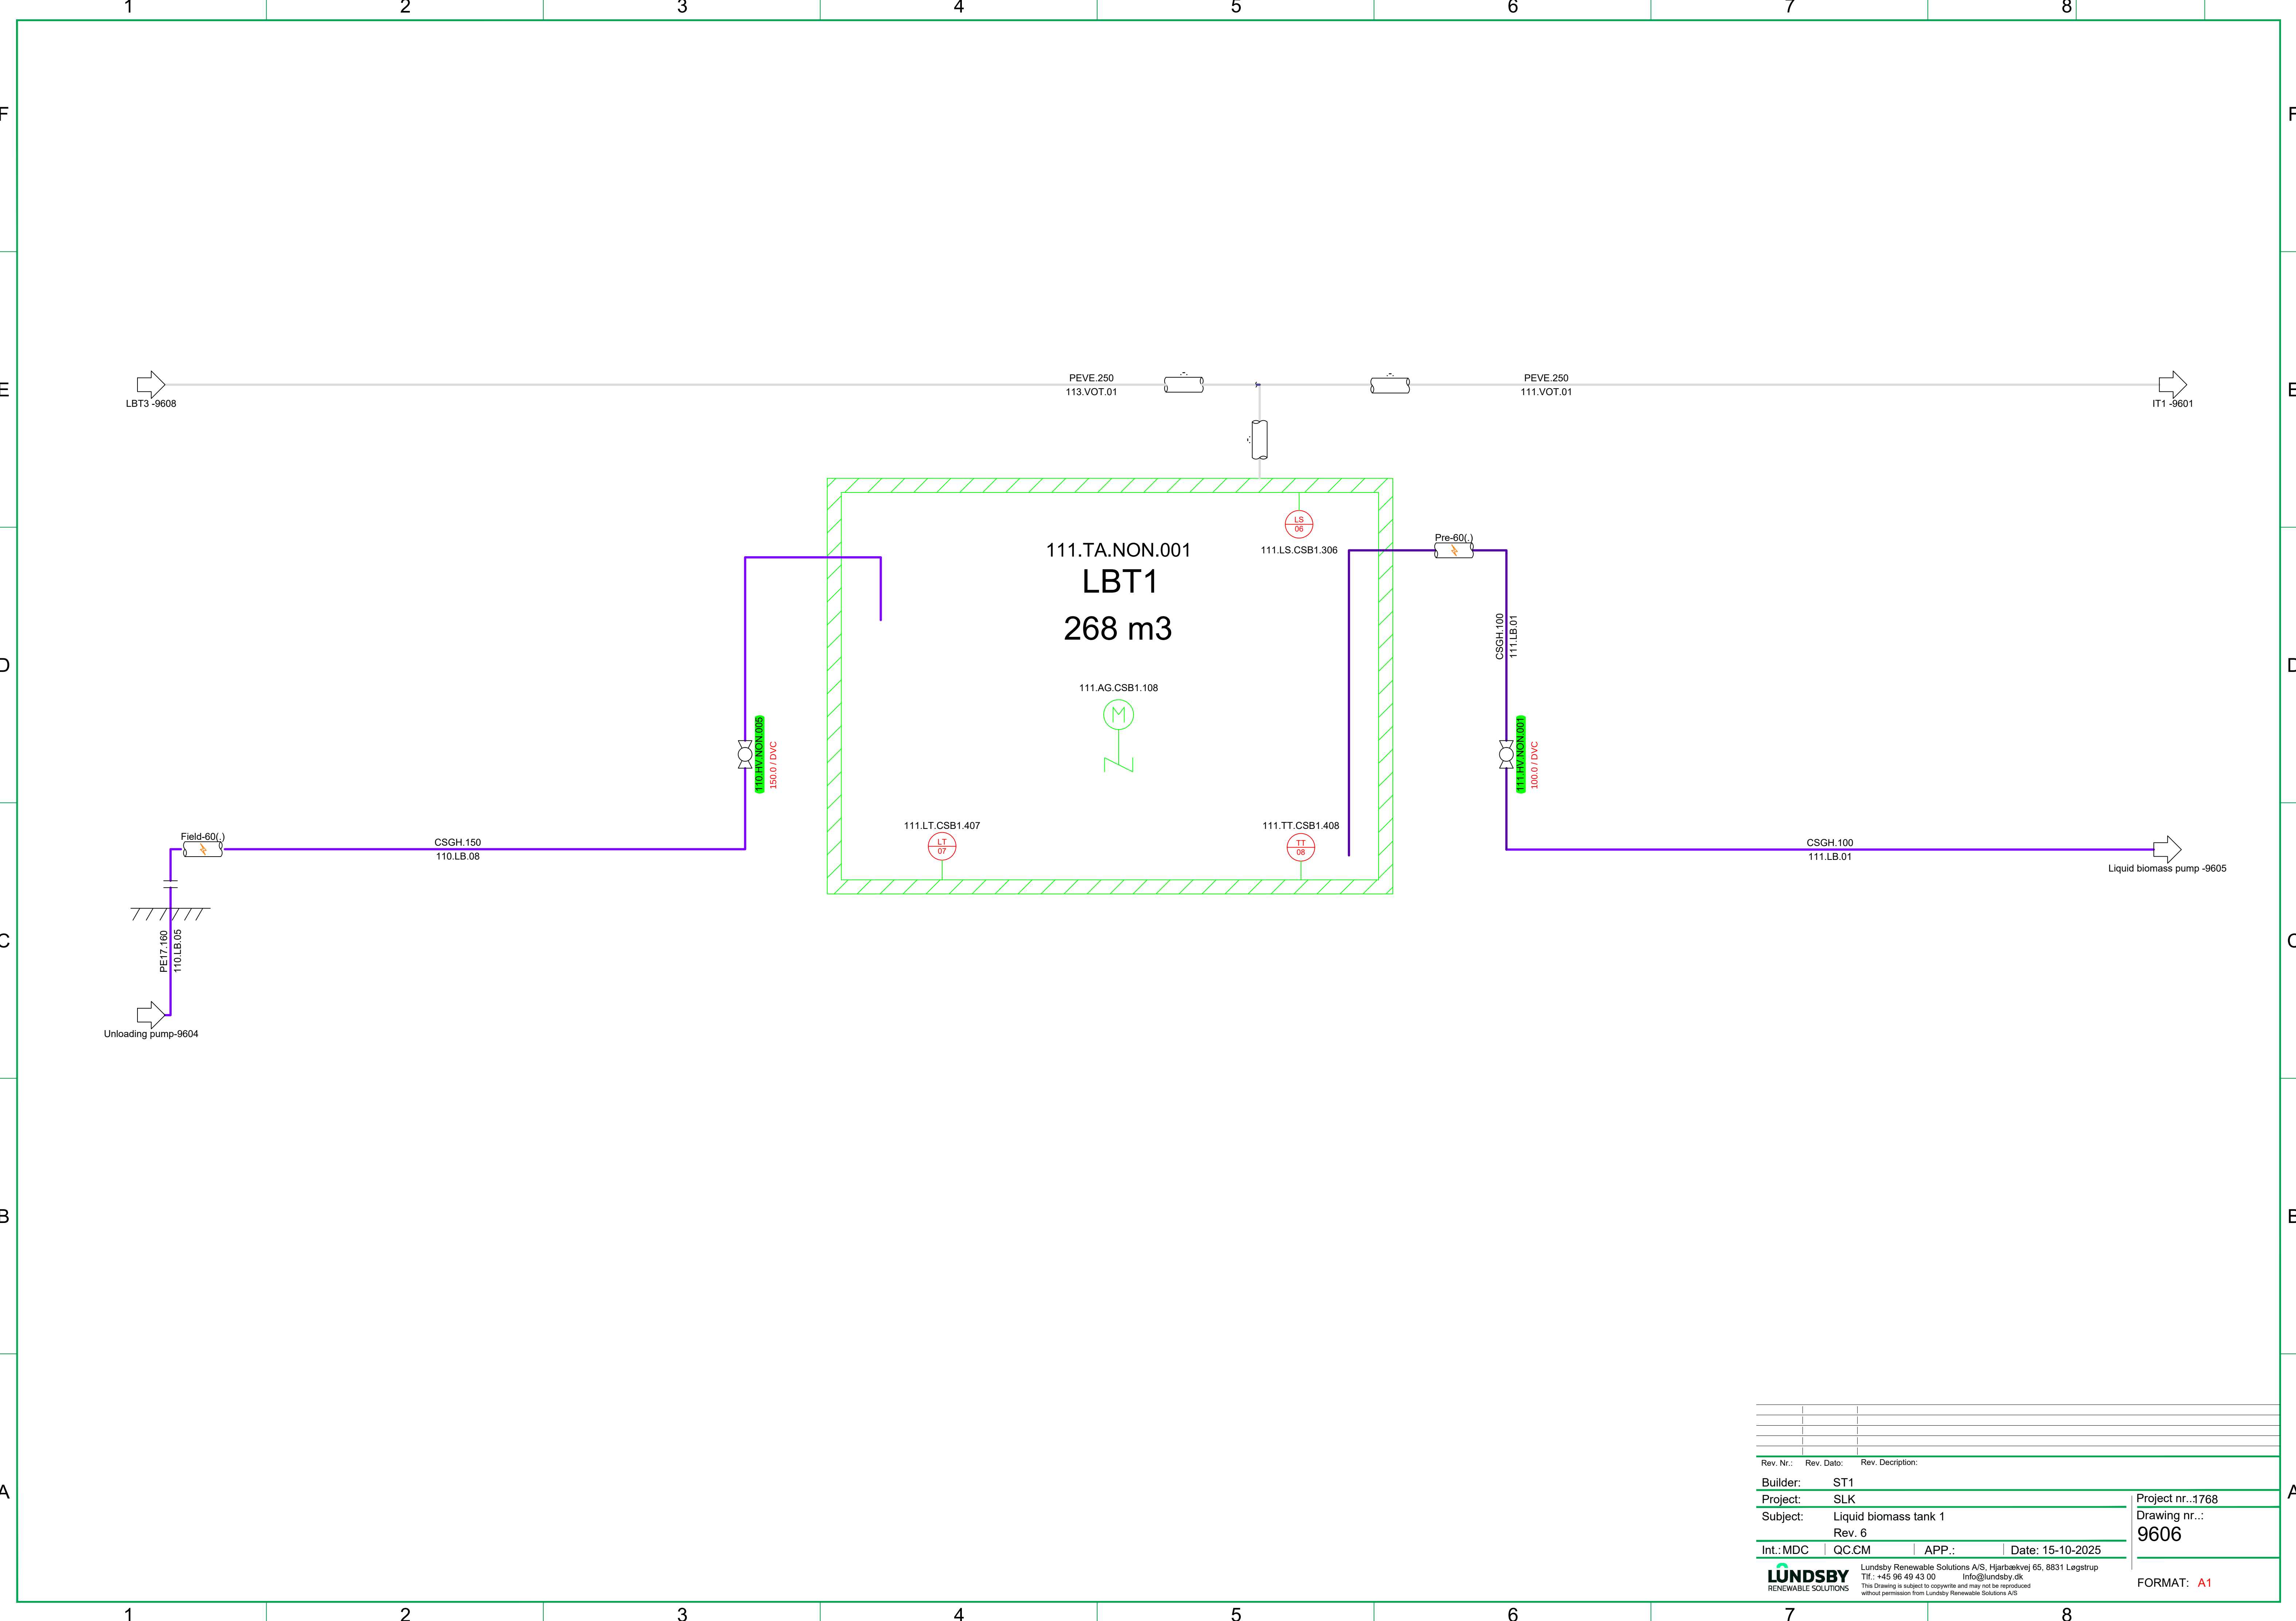


Rev. Nr.:	Rev. Dato:	Rev. Description:	Project nr...1768
Builder:	ST1		Drawing nr...: 9606
Project:	SLK		
Subject:	Liquid biomass tank 1		
	Rev. 6		
Int.:MDC	QC.CM	APP.:	Date: 15-10-2025
LUNDSBY RENEWABLE SOLUTIONS			Lundsby Renewable Solutions A/S, Hjarbækvej 65, 8831 Løgstrup Tlf.: +45 96 49 43 00 Info@lundsby.dk This Drawing is subject to copyright and may not be reproduced without permission from Lundsby Renewable Solutions A/S
			FORMAT: A1

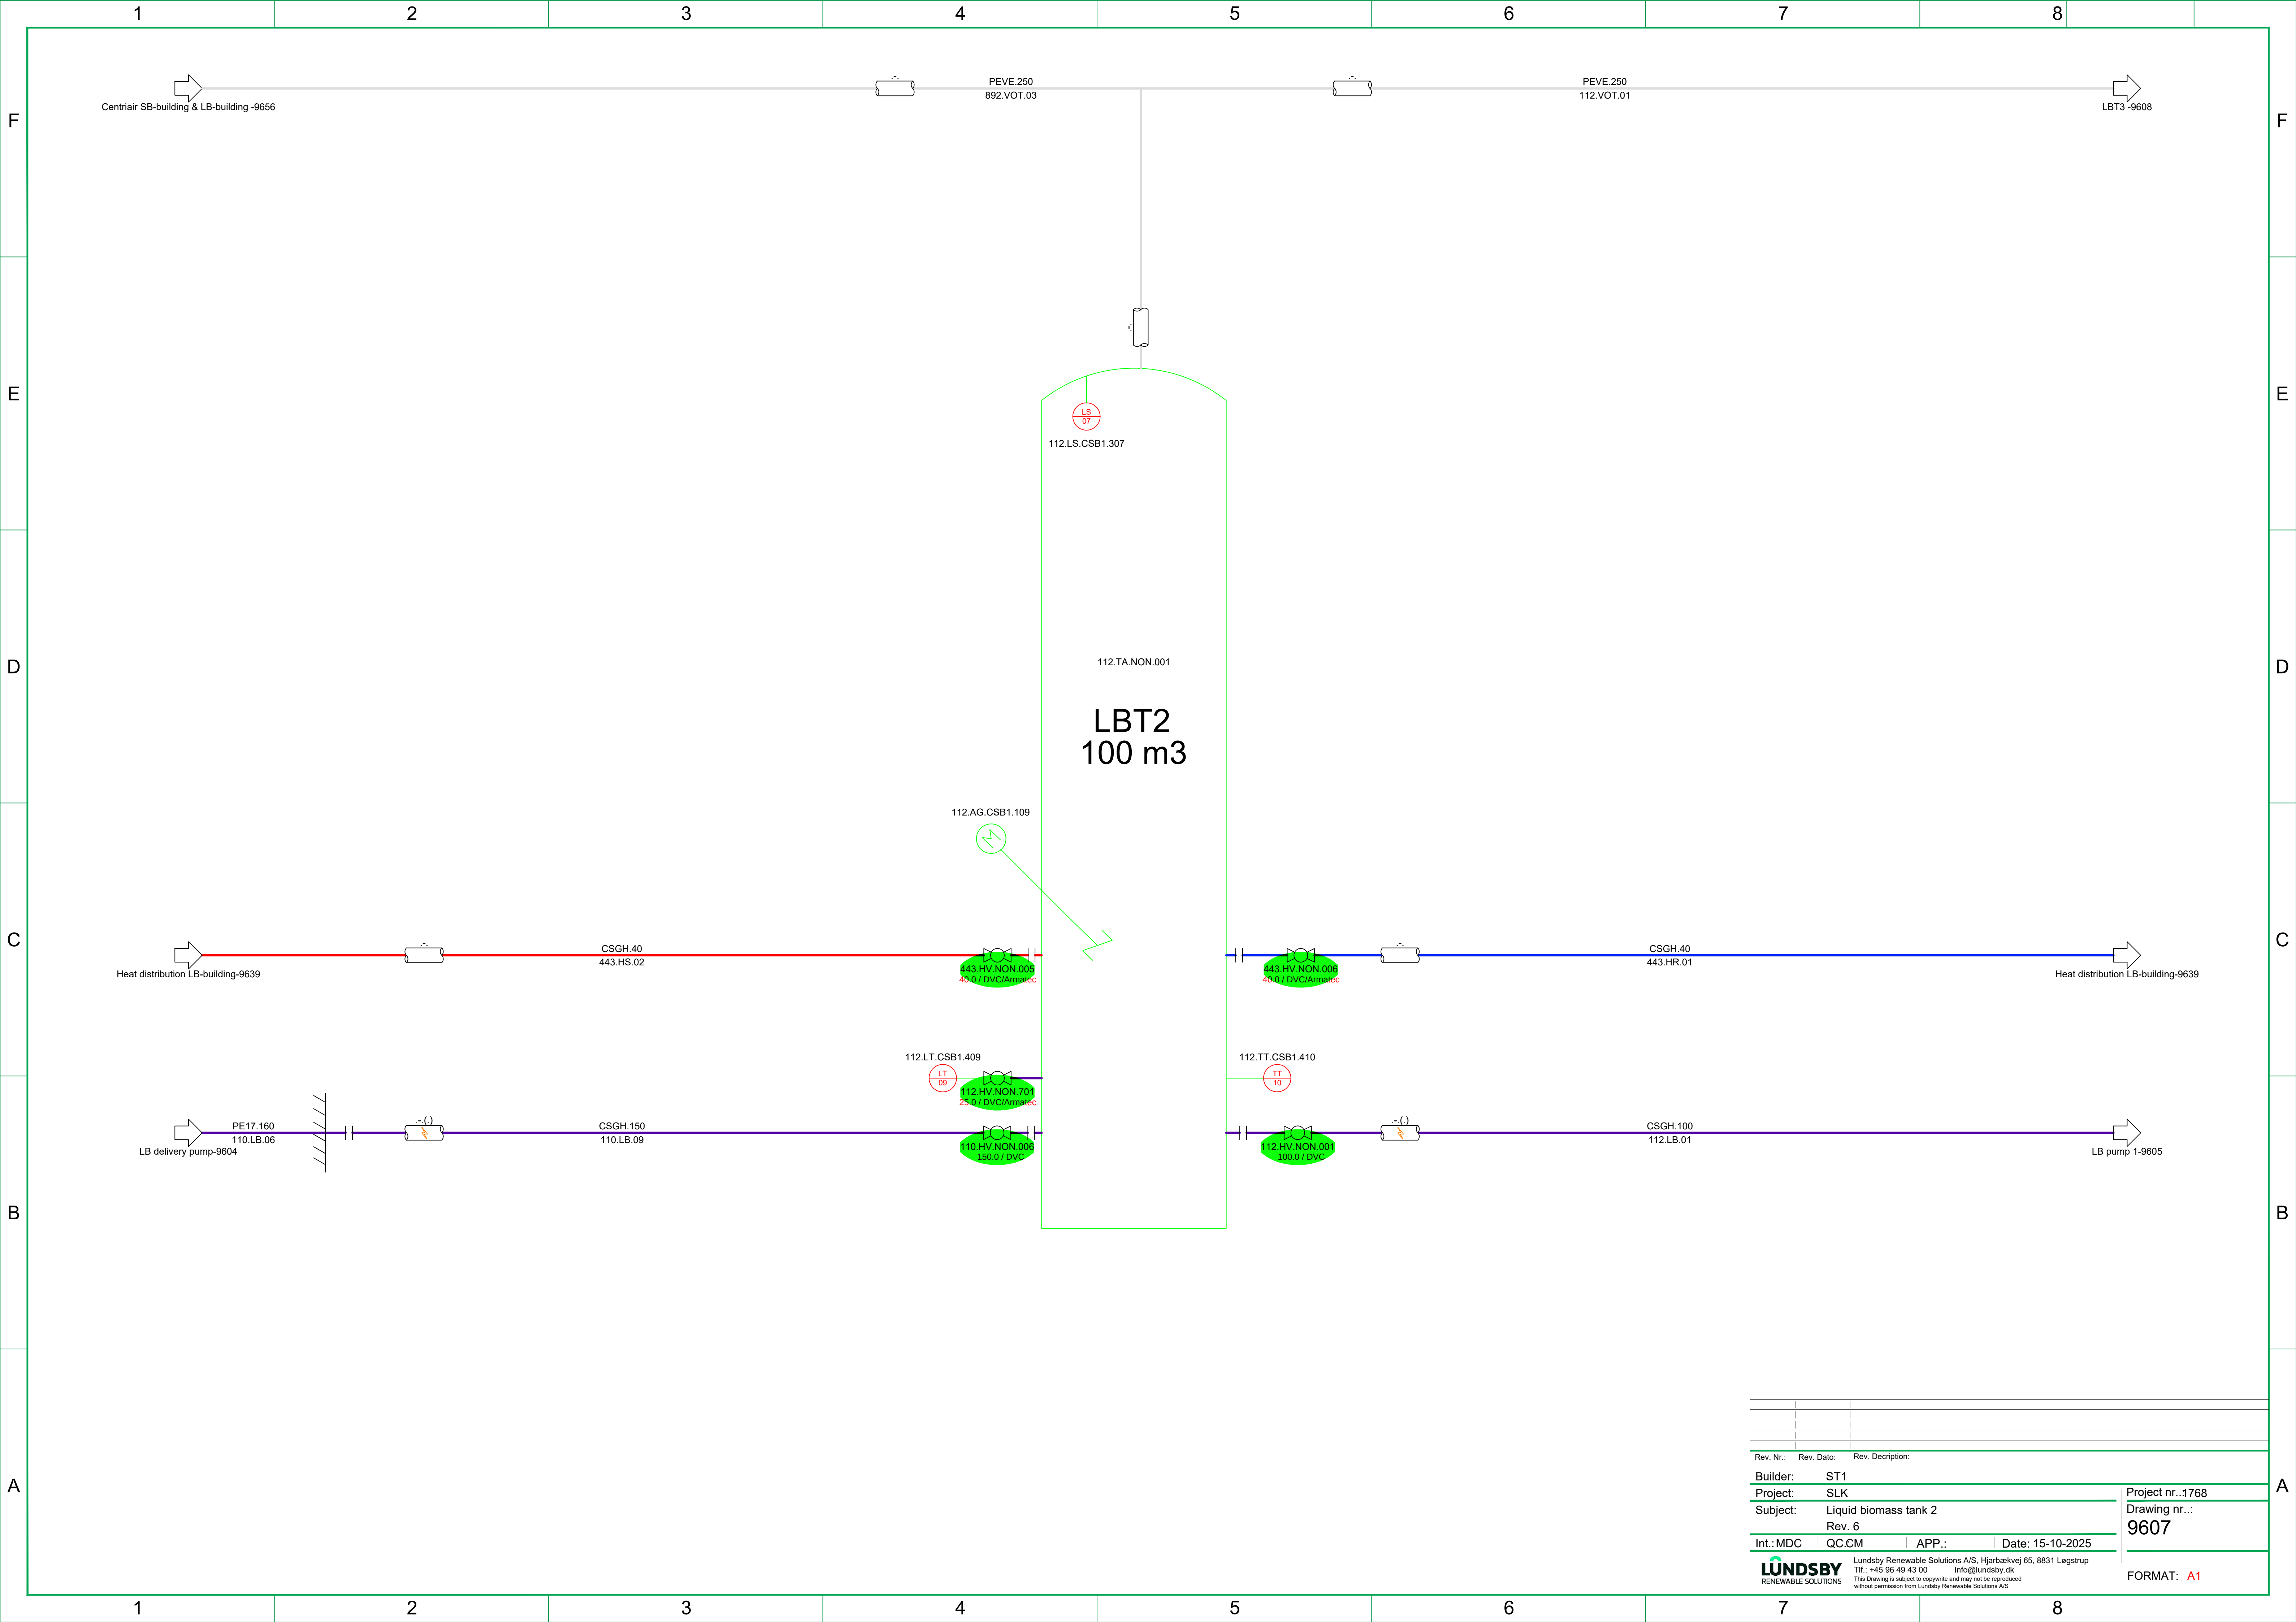


Rev. Nr.:	Rev. Dato:	Rev. Description:
Builder:	ST1	
Project:	SLK	
Subject:	Liquid biomass tank 2	
	Rev. 6	
Int.:MDC	QC:CM	APP.: Date: 15-10-2025
LUNDSBY RENEWABLE SOLUTIONS		
Lundsby Renewable Solutions A/S, Hjarbækvej 65, 8831 Løgstrup Tlf.: +45 96 49 43 00 Info@lundsby.dk This Drawing is subject to copyright and may not be reproduced without permission from Lundsby Renewable Solutions A/S		
Project nr...1768		Drawing nr...: 9607
FORMAT: A1		

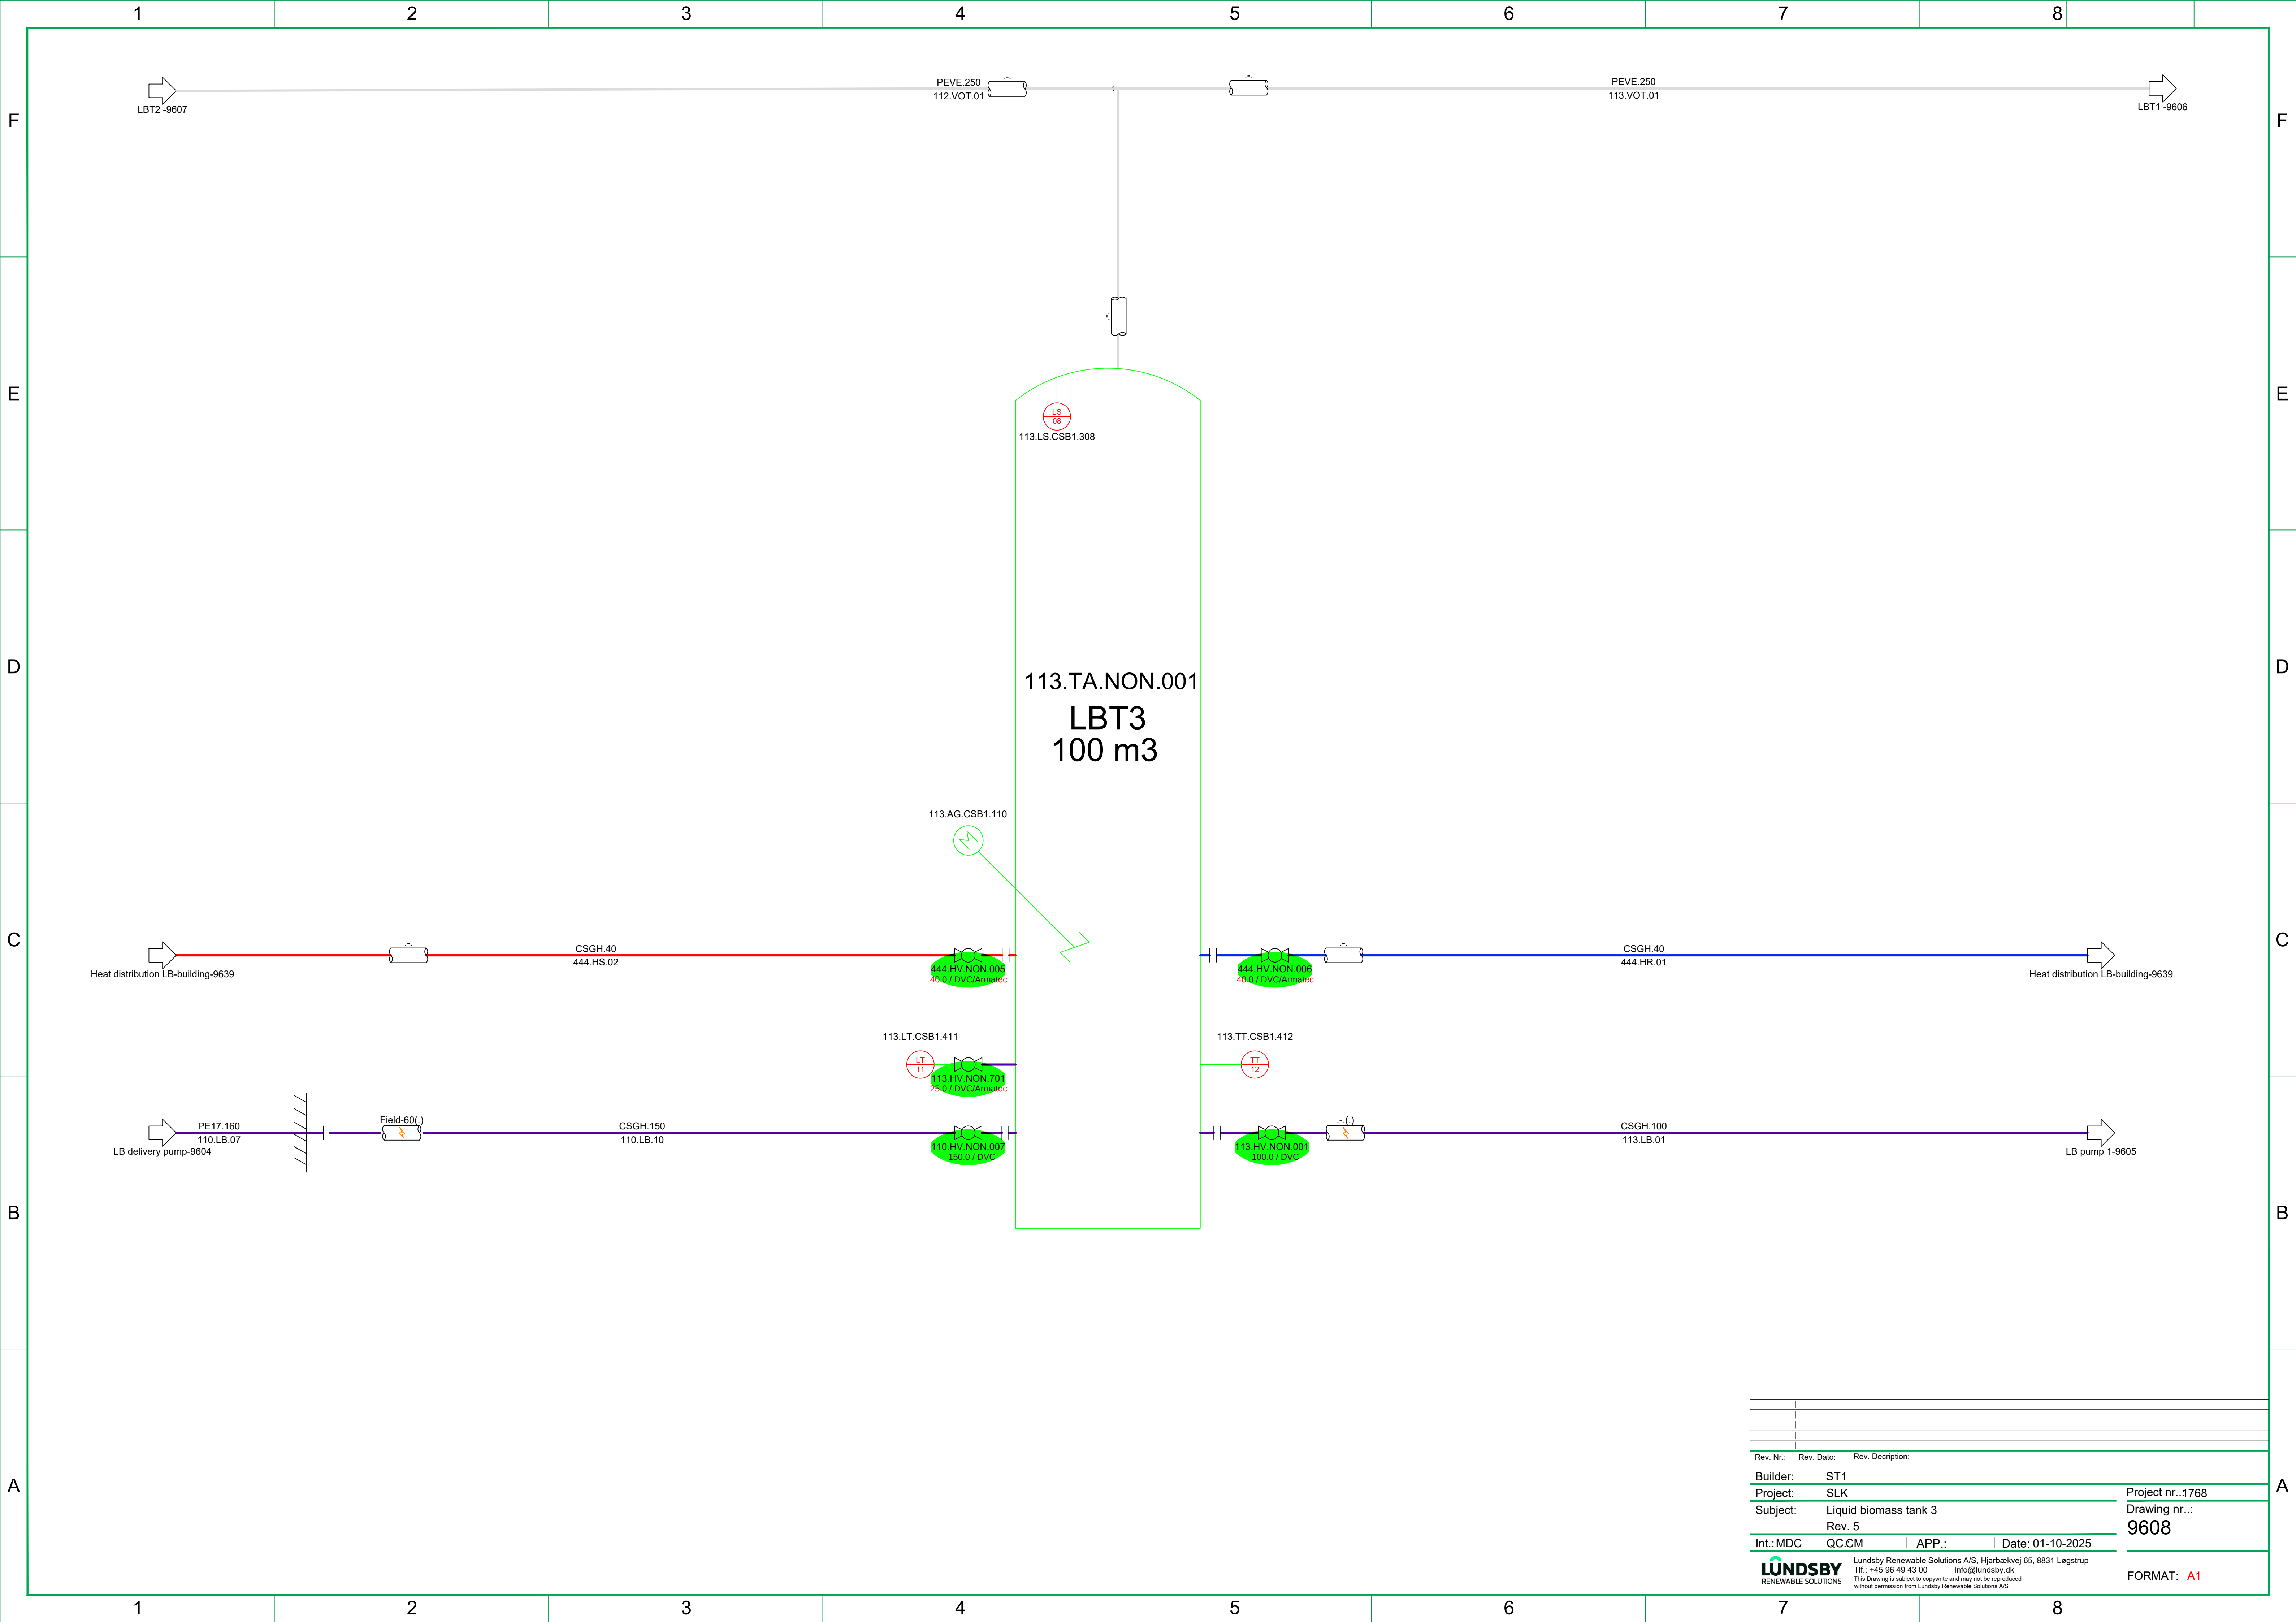


Rev. Nr.:	Rev. Dato:	Rev. Description:	
Builder:	ST1		
Project:	SLK		
Subject:	Liquid biomass tank 3		
	Rev. 5		
Int.:MDC	QC:CM	APP.:	Date: 01-10-2025
		Lundsby Renewable Solutions A/S, Hjarbækvej 65, 8831 Løgstrup Tlf.: +45 96 49 43 00 Info@lundsby.dk This Drawing is subject to copyright and may not be reproduced without permission from Lundsby Renewable Solutions A/S	
		Project nr...1768	
		Drawing nr... 9608	
		FORMAT: A1	

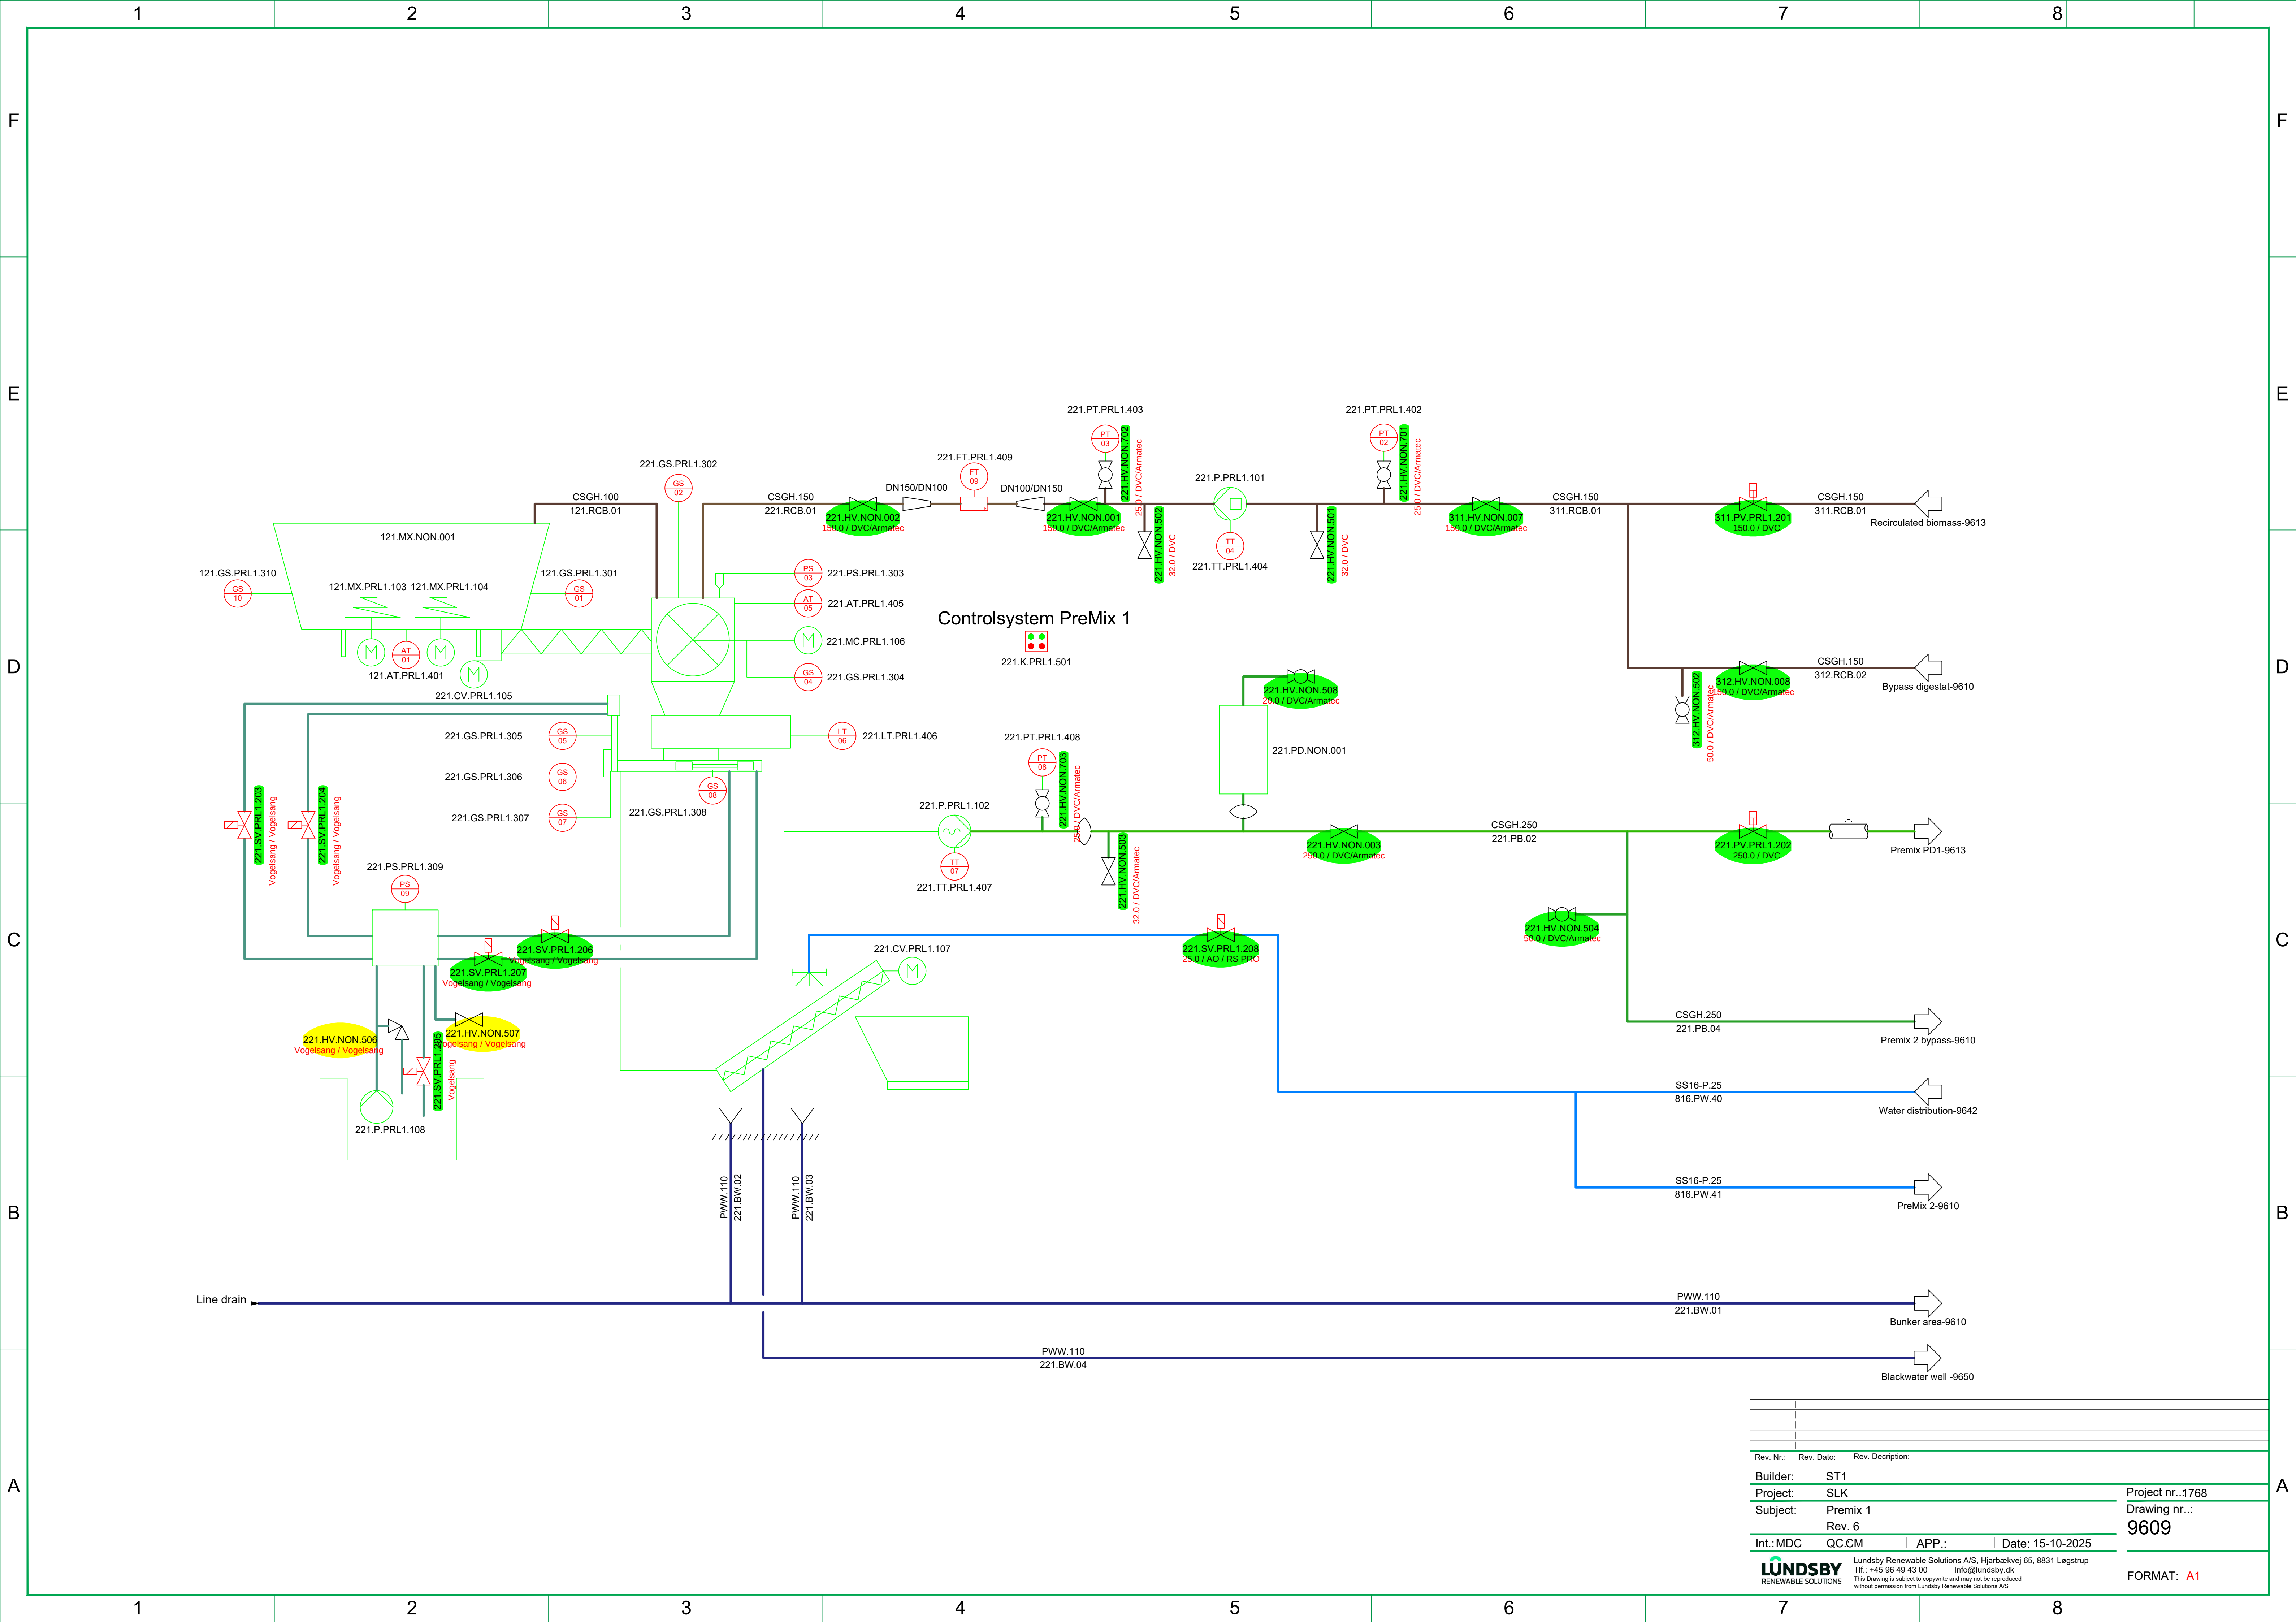

Rev. Nr.:	Rev. Dato:	Rev. Description:
Builder:	ST1	
Project:	SLK	
Subject:	Premix 1	
	Rev. 6	
Int.:MDC	QC:CM	APP.:Date: 15-10-2025
LUNDSBY RENEWABLE SOLUTIONS Lundsby Renewable Solutions A/S, Hjarbækvej 65, 8831 Løgstrup Tlf.: +45 96 49 43 00 info@lundsby.dk This drawing is subject to copyright and may not be reproduced without permission from Lundsby Renewable Solutions A/S		
Project nr.:1768		Drawing nr.:9609
FORMAT: A1		

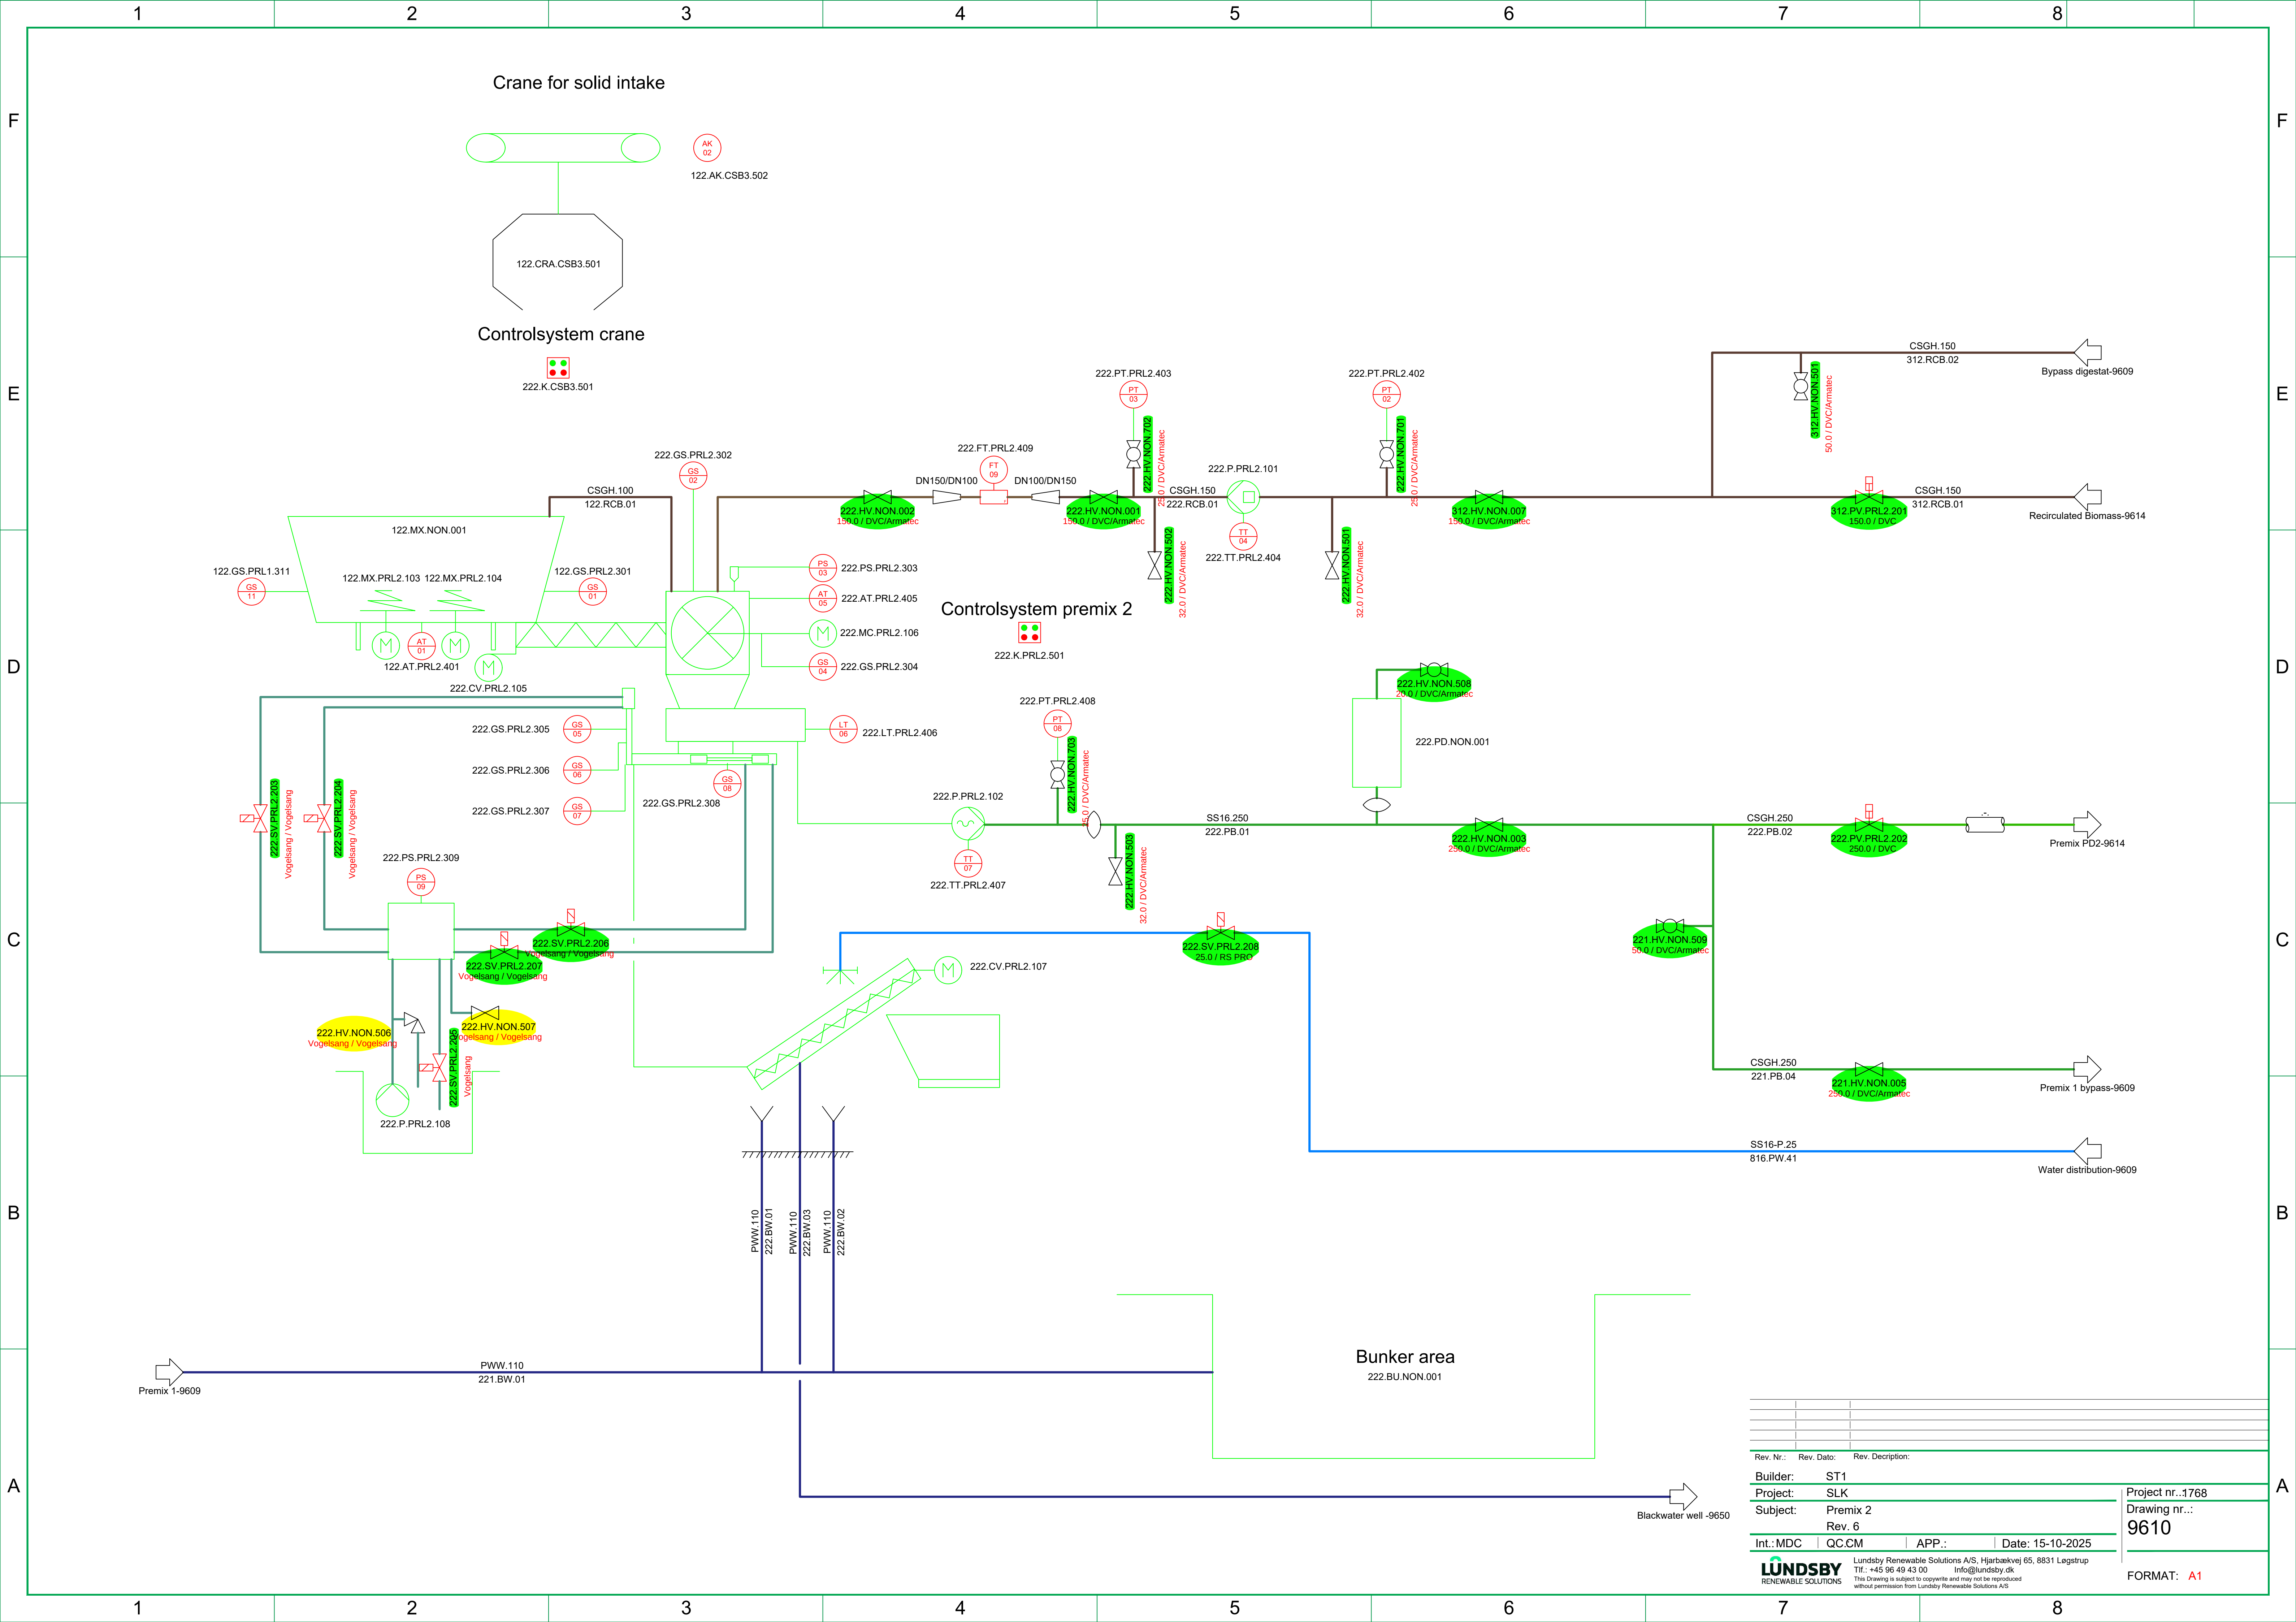


Rev. Nr.:	Rev. Dato:	Rev. Description:
Builder:	ST1	
Project:	SLK	
Subject:	Premix 2	
	Rev. 6	
Int.:MDC	QC:CM	APP.:
		Date: 15-10-2025
LUNDSBY RENEWABLE SOLUTIONS		
Lundsby Renewable Solutions A/S, Hjarbrøkkevej 65, 8831 Løgstrup Tlf.: +45 96 49 43 00 info@lundsby.dk This Drawing is subject to copyright and may not be reproduced without permission from Lundsby Renewable Solutions A/S		
Project nr.:1768 Drawing nr.: 9610		FORMAT: A1

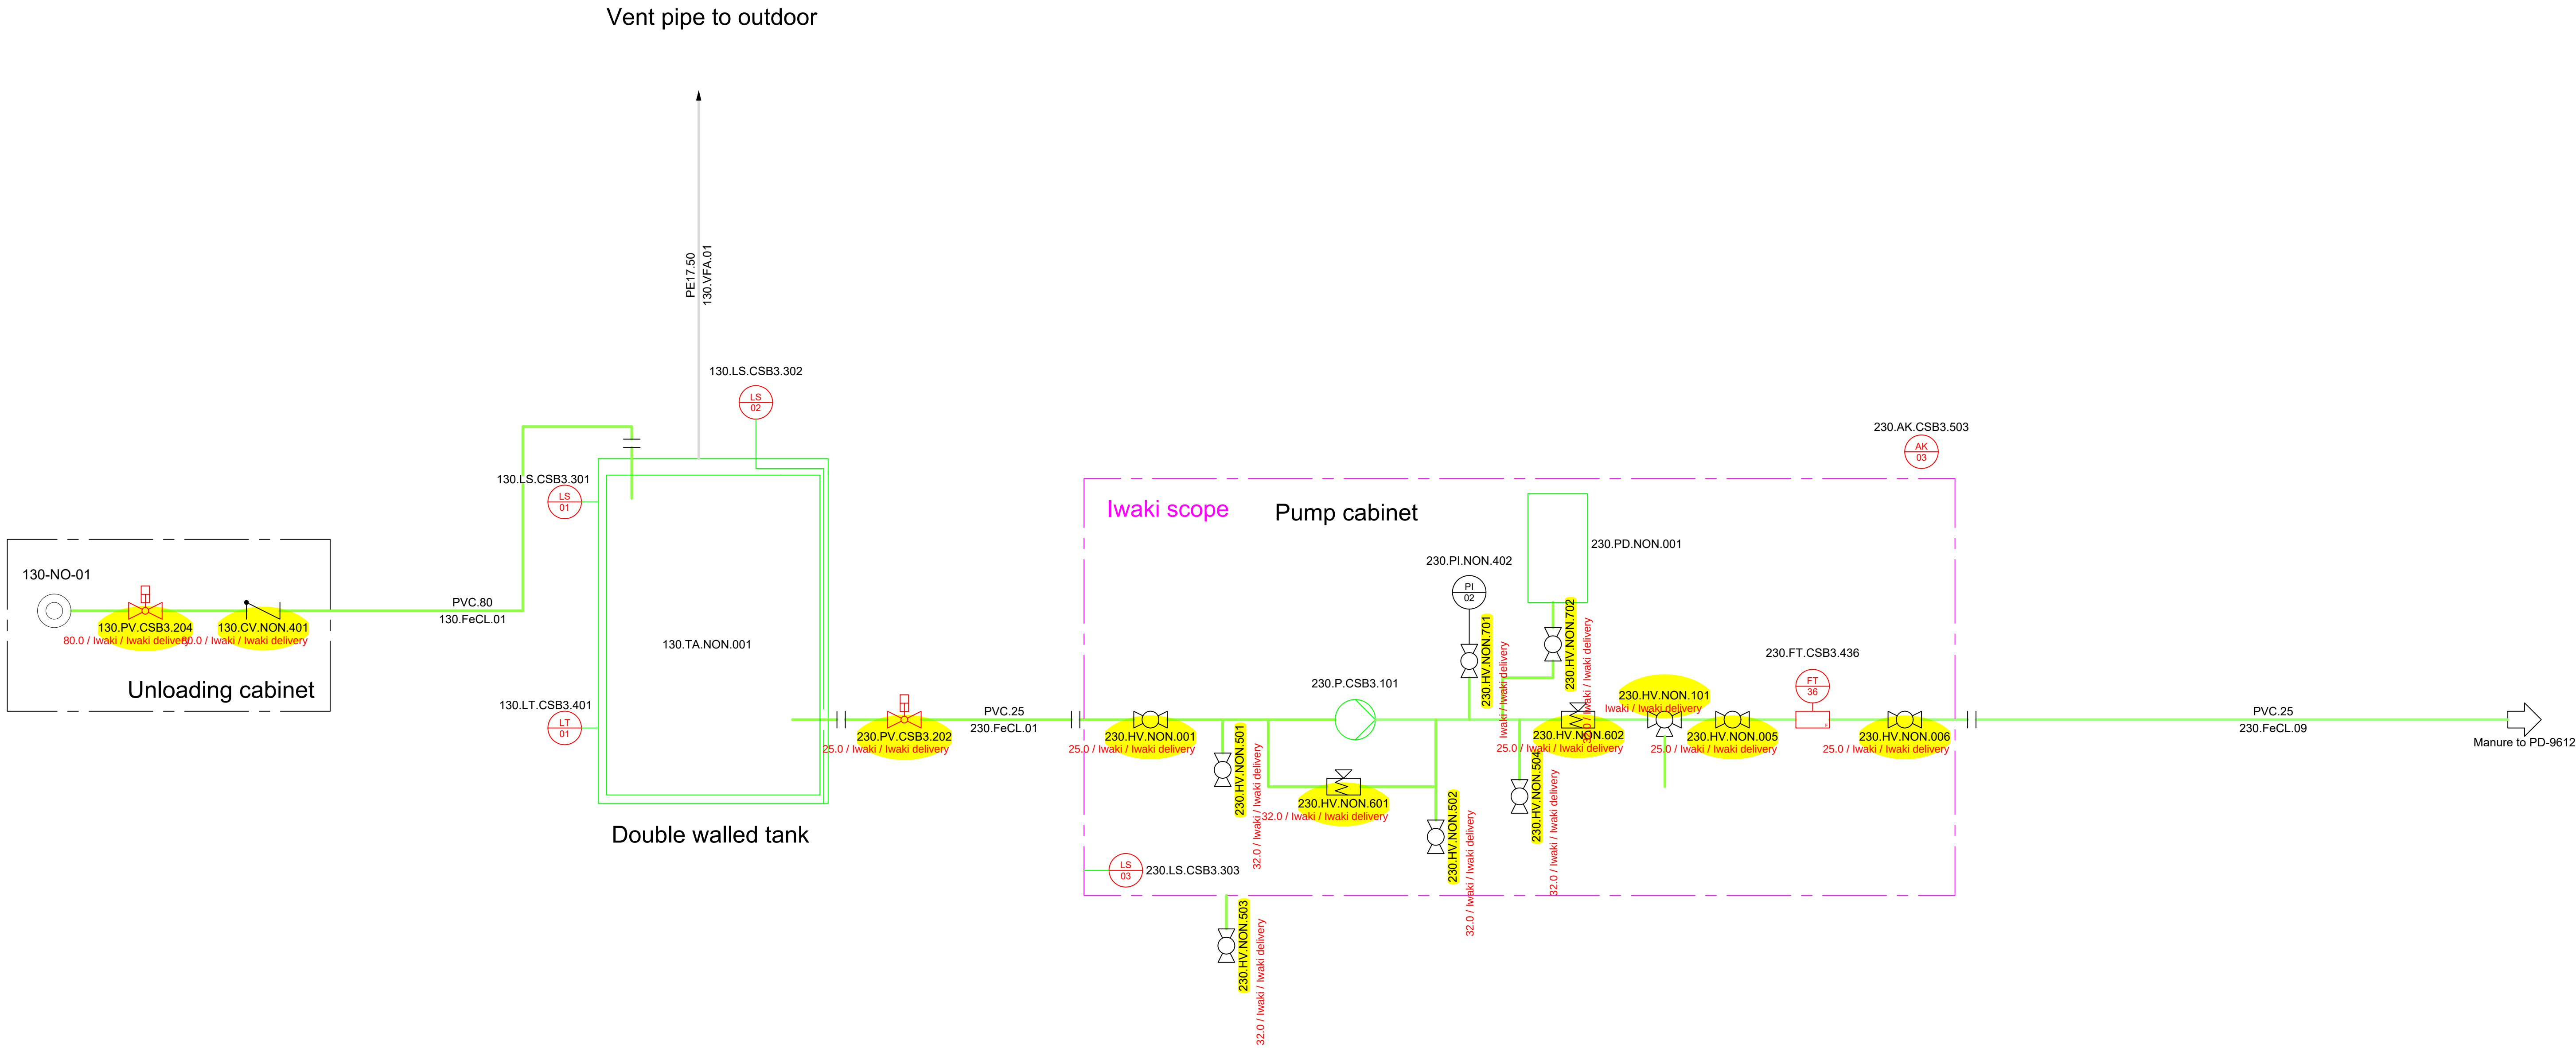


Rev. Nr.:	Rev. Dato:	Rev. Description:	
Builder:	ST1		
Project:	SLK		
Subject:	FECL system		
	Rev. 6		
Int.:MDC	QC:CM	APP.:	Date: 15-10-2025
LUNDSBY RENEWABLE SOLUTIONS			Lundsby Renewable Solutions A/S, Hjarbækvej 65, 8831 Løgstrup Tlf.: +45 96 49 43 00 Info@lundsby.dk This Drawing is subject to copyright and may not be reproduced without permission from Lundsby Renewable Solutions A/S
			Project nr.:1768 Drawing nr.: 9611 FORMAT: A1

Pumphouse 2

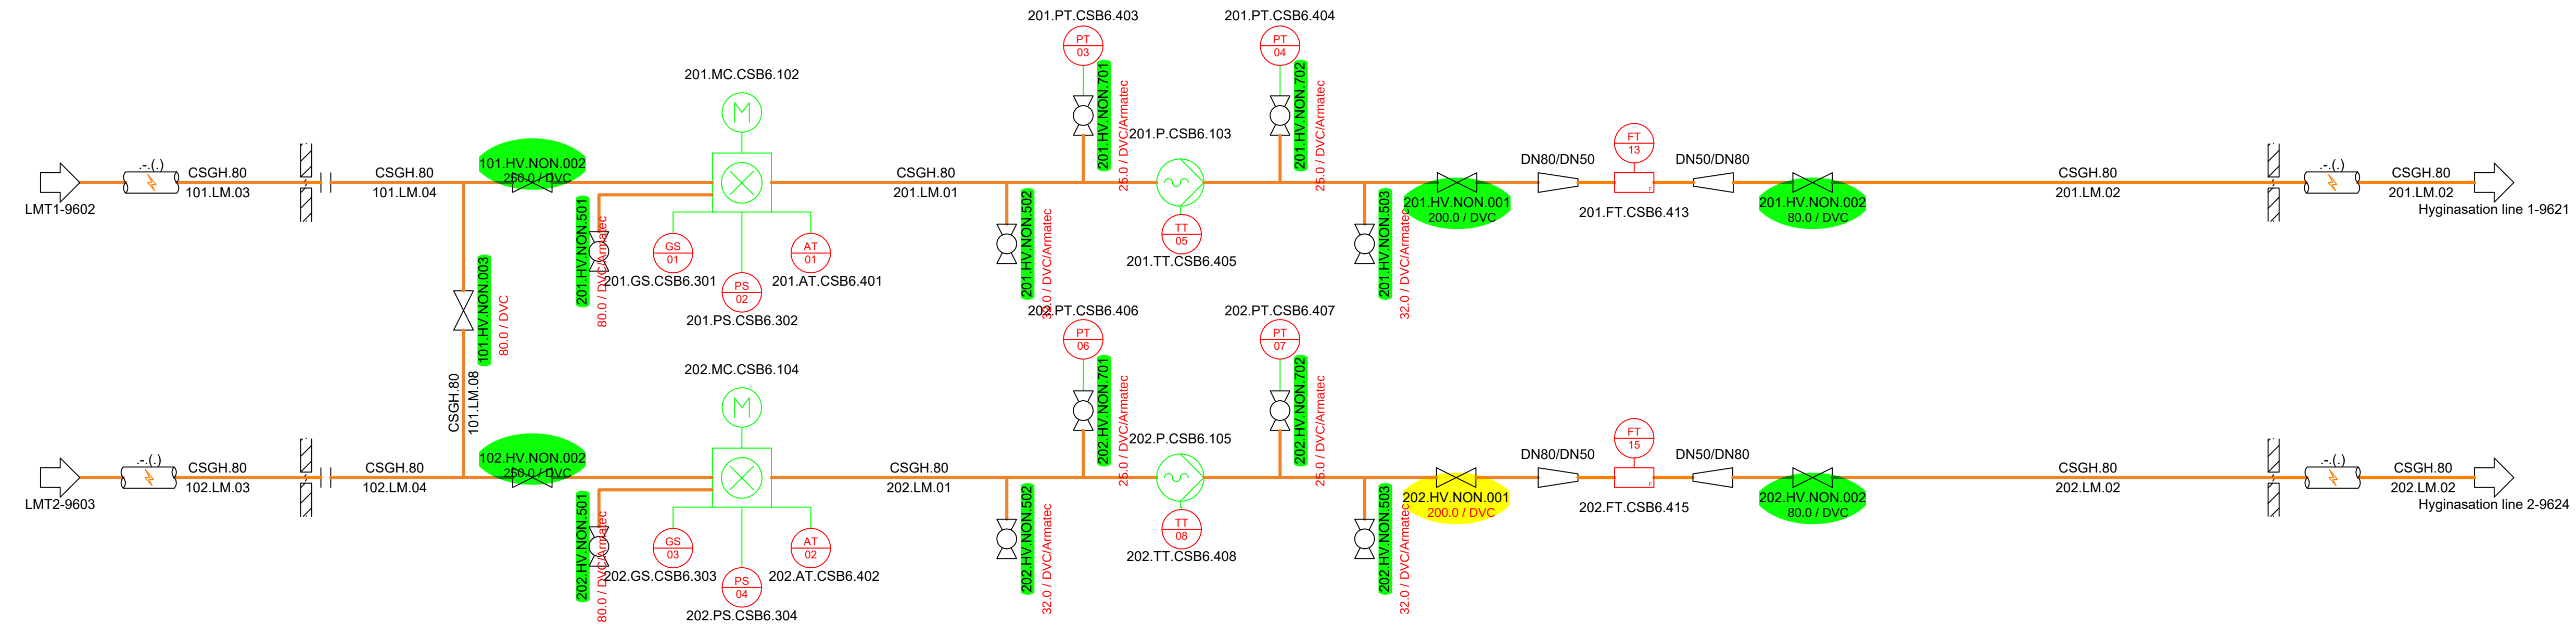



Tech
building

SB-building

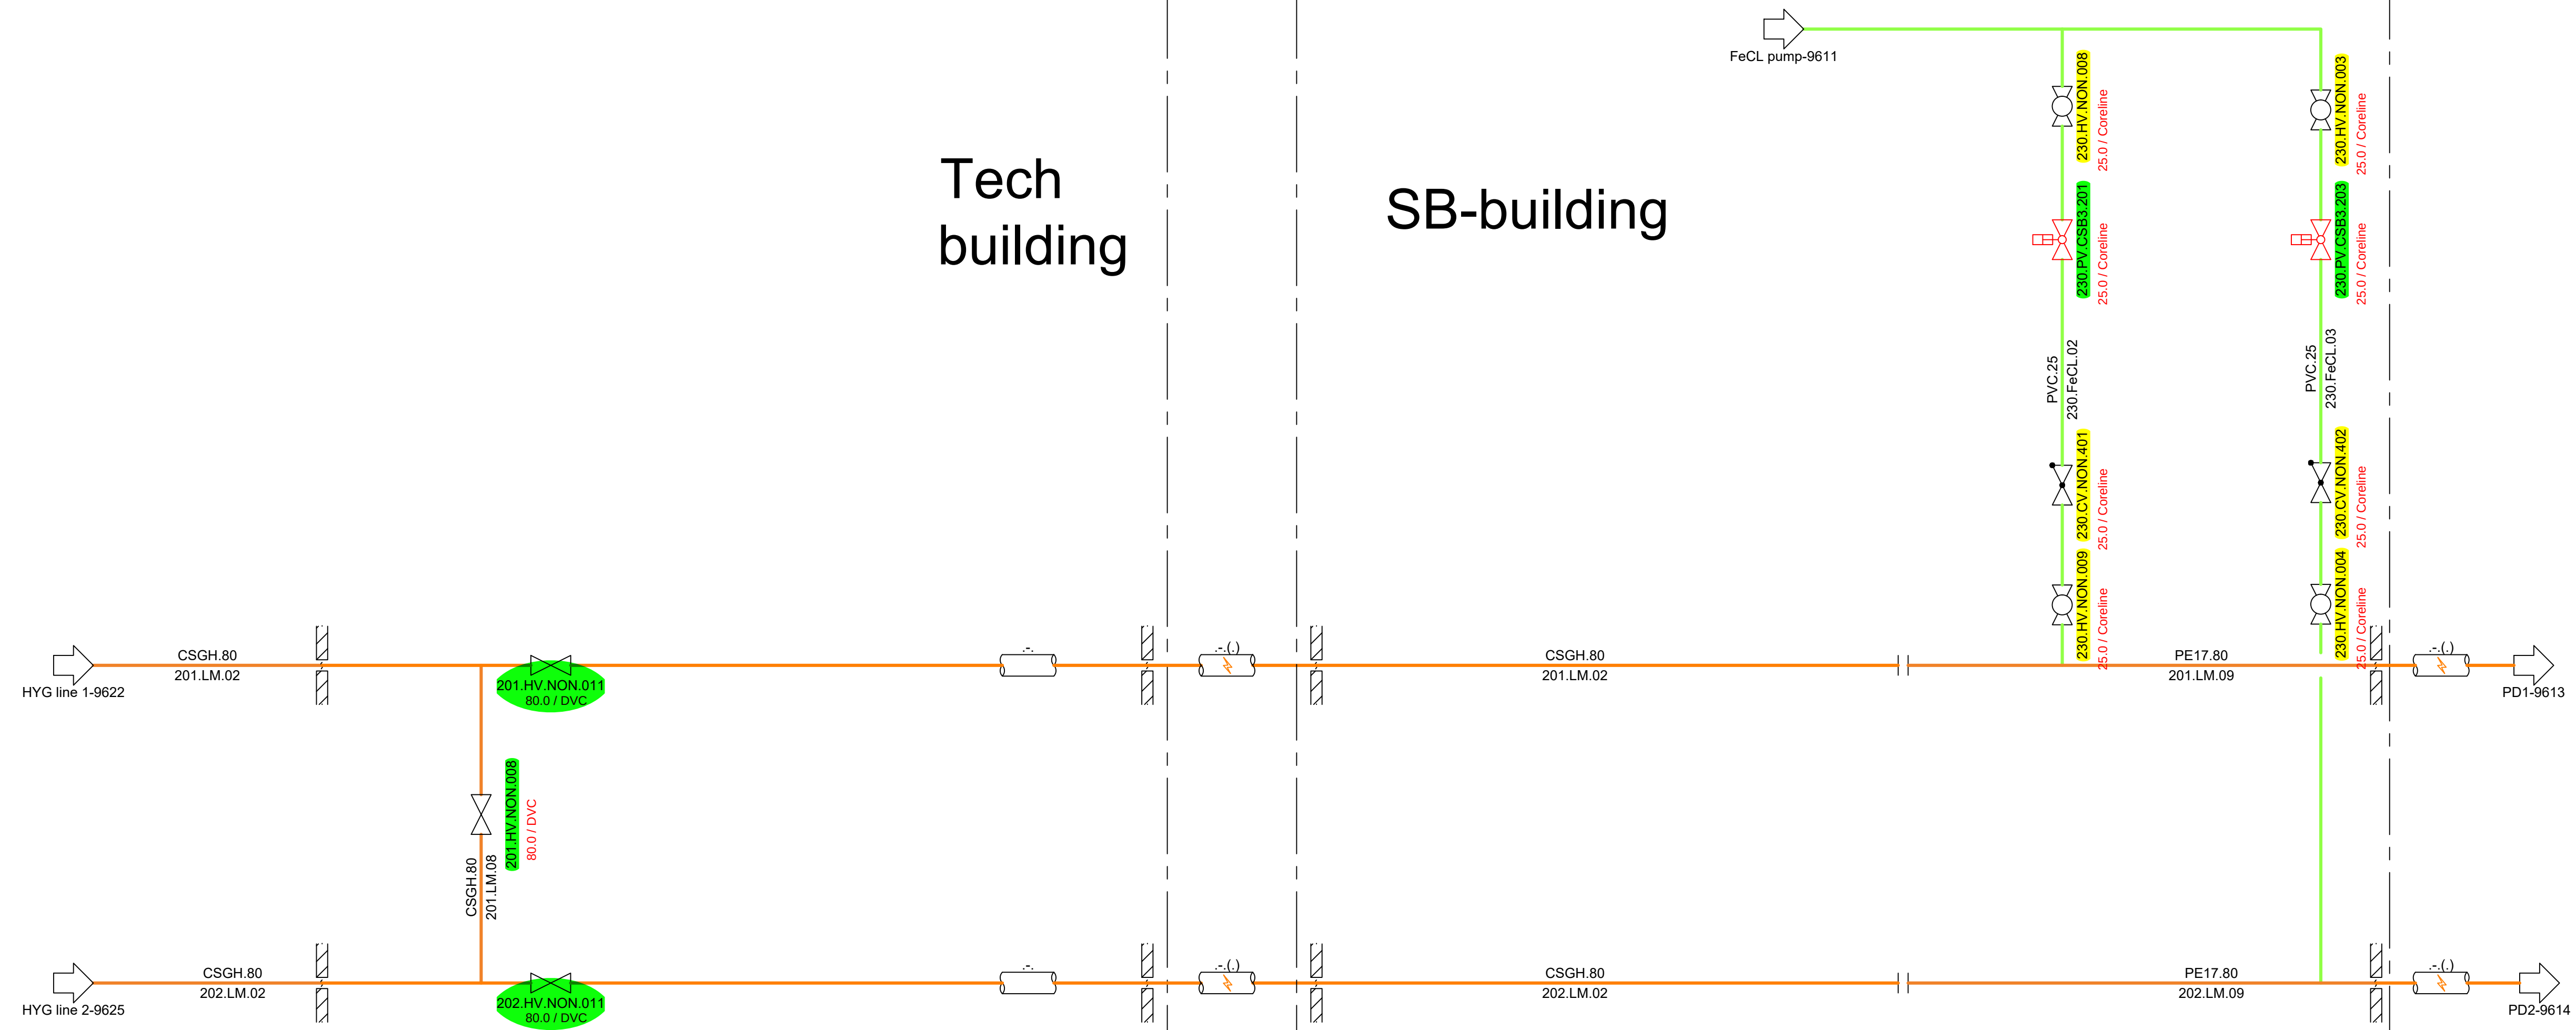

Rev. Nr.:	Rev. Dato:	Rev. Description:
Builder:	ST1	
Project:	SLK	
Subject:	Liquid manure pump	
Rev. 6		
Int.: MDC	QC.CM	APP.:
Date:	15-10-2025	
LUNDSBY RENEWABLE SOLUTIONS		
Lundsby Renewable Solutions A/S, Hjarbækvej 65, 8831 Lægstrup Tlf.: +45 96 49 43 00 info@lundsby.dk This Drawing is subject to copyright and may not be reproduced without permission from Lundsby Renewable Solutions A/S		
Project nr.: 1768		Drawing nr.: 9612
FORMAT: A1		

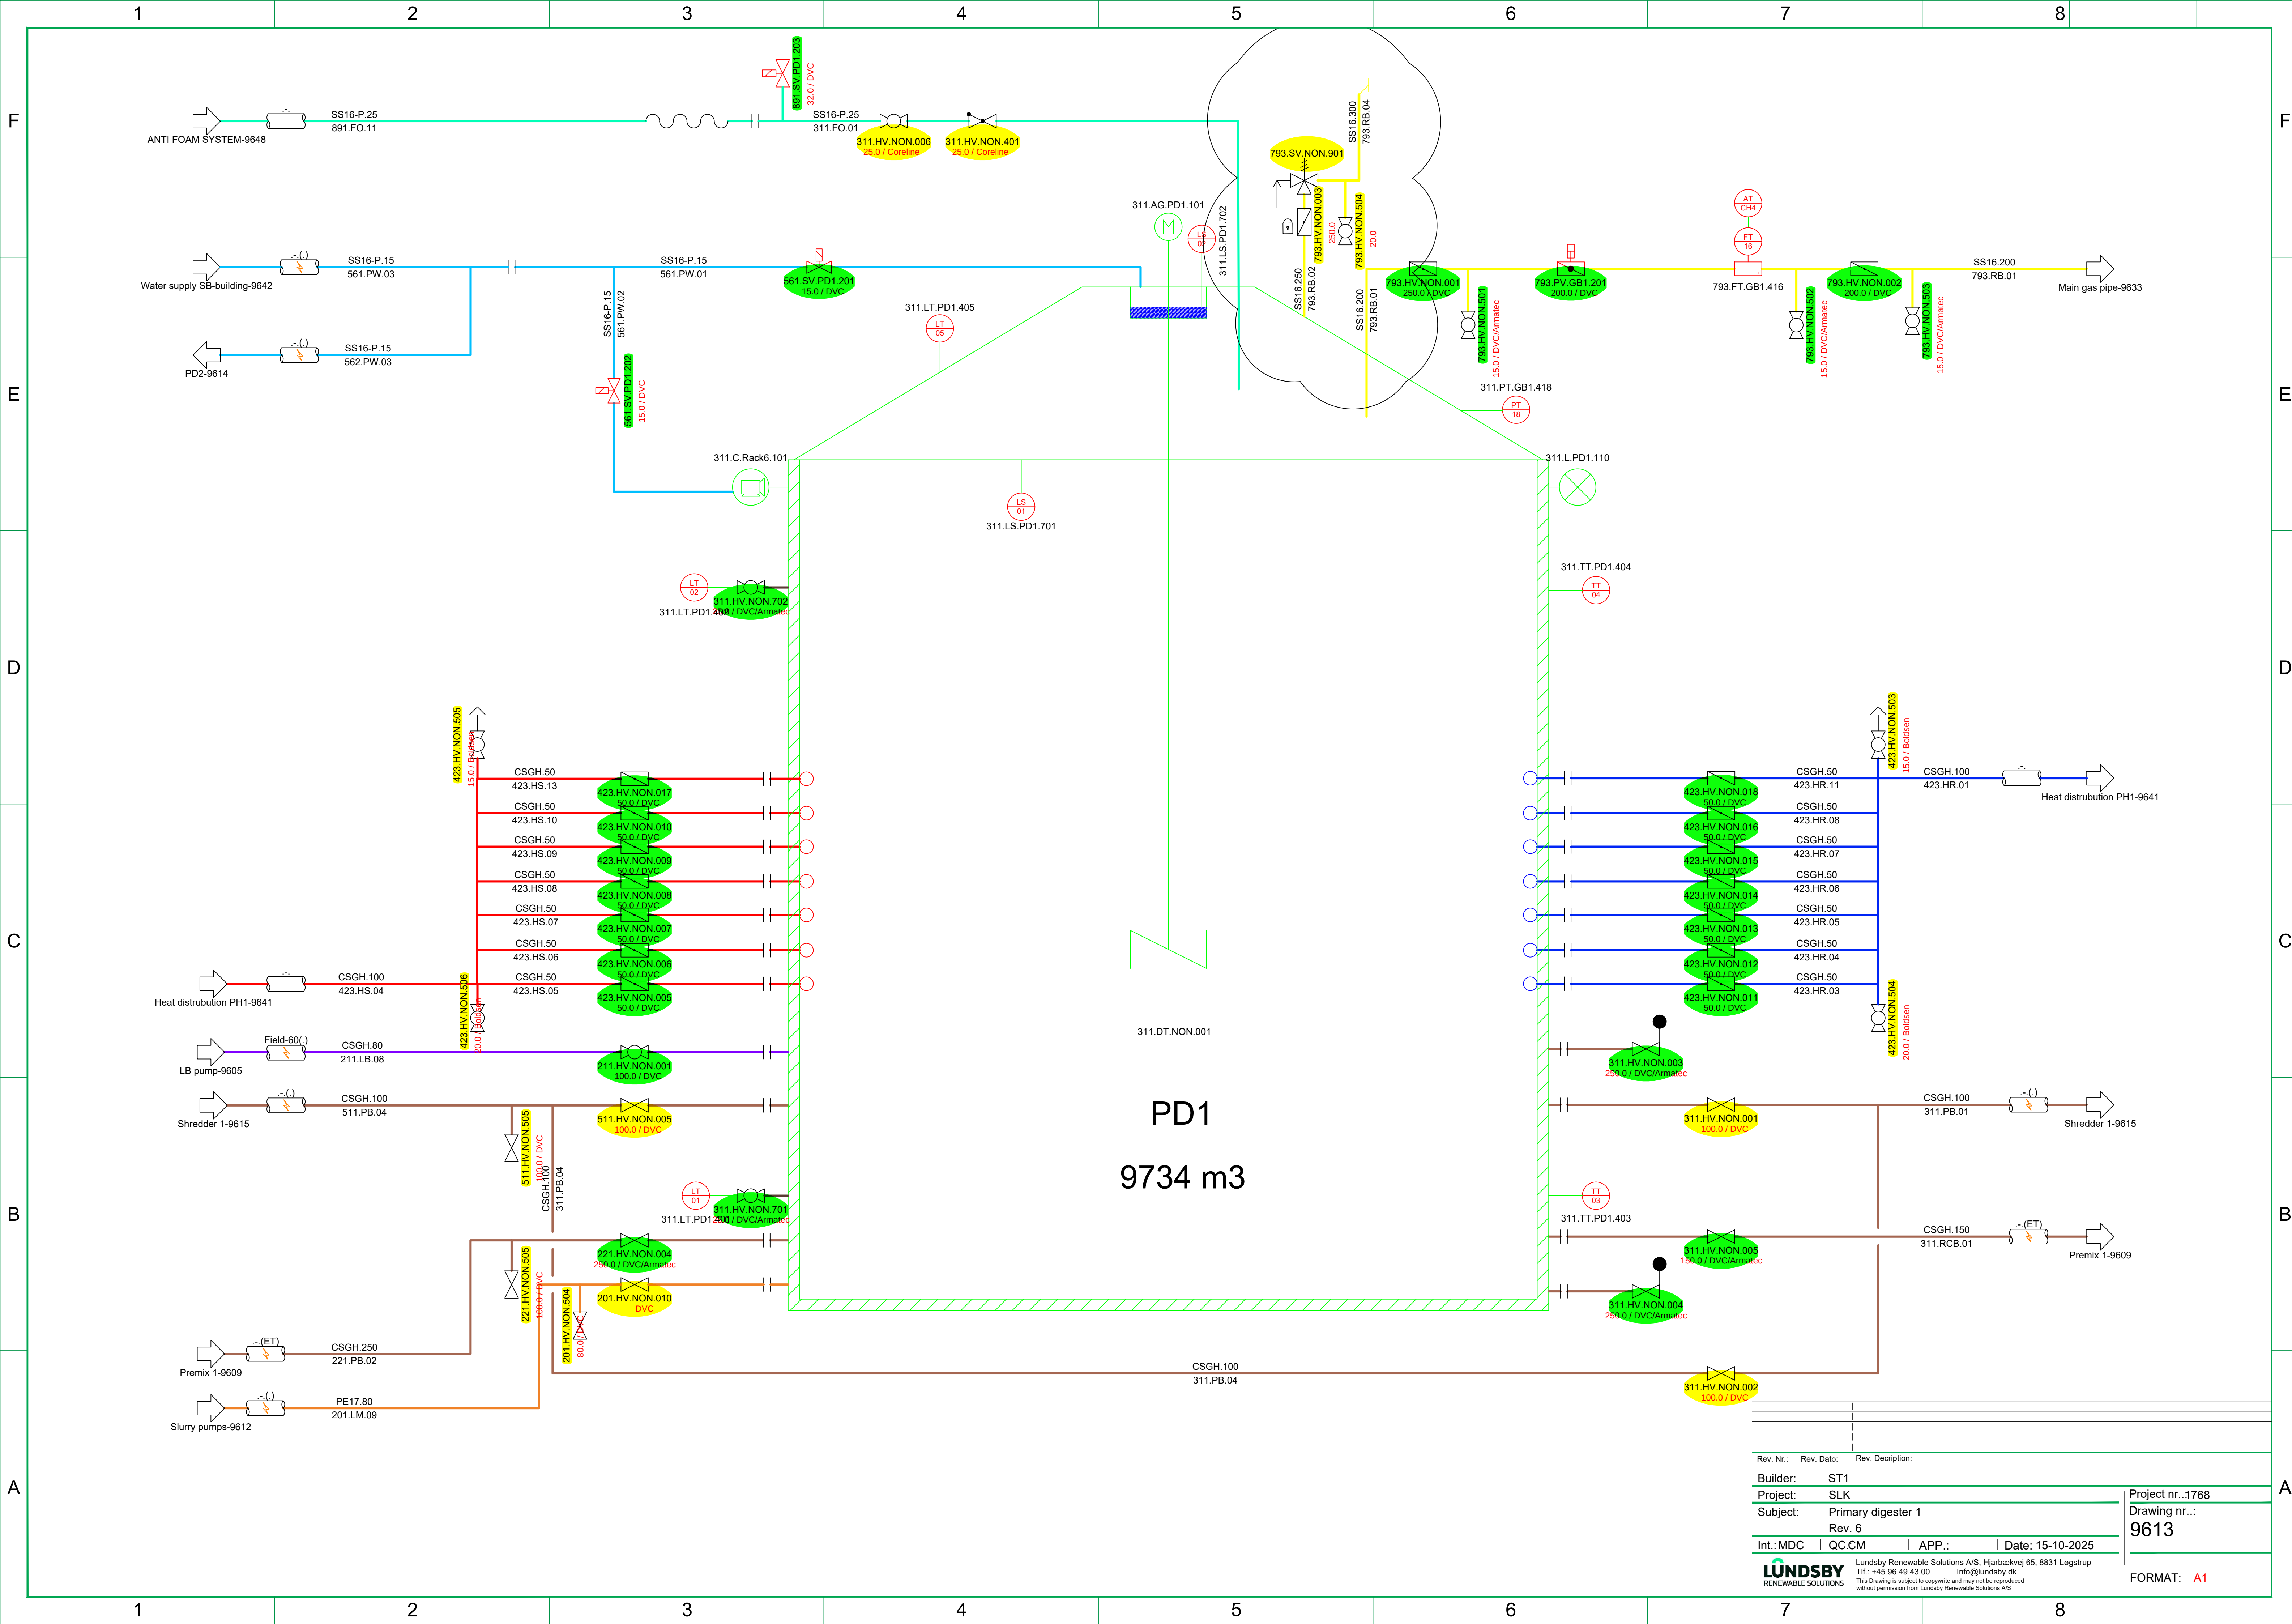


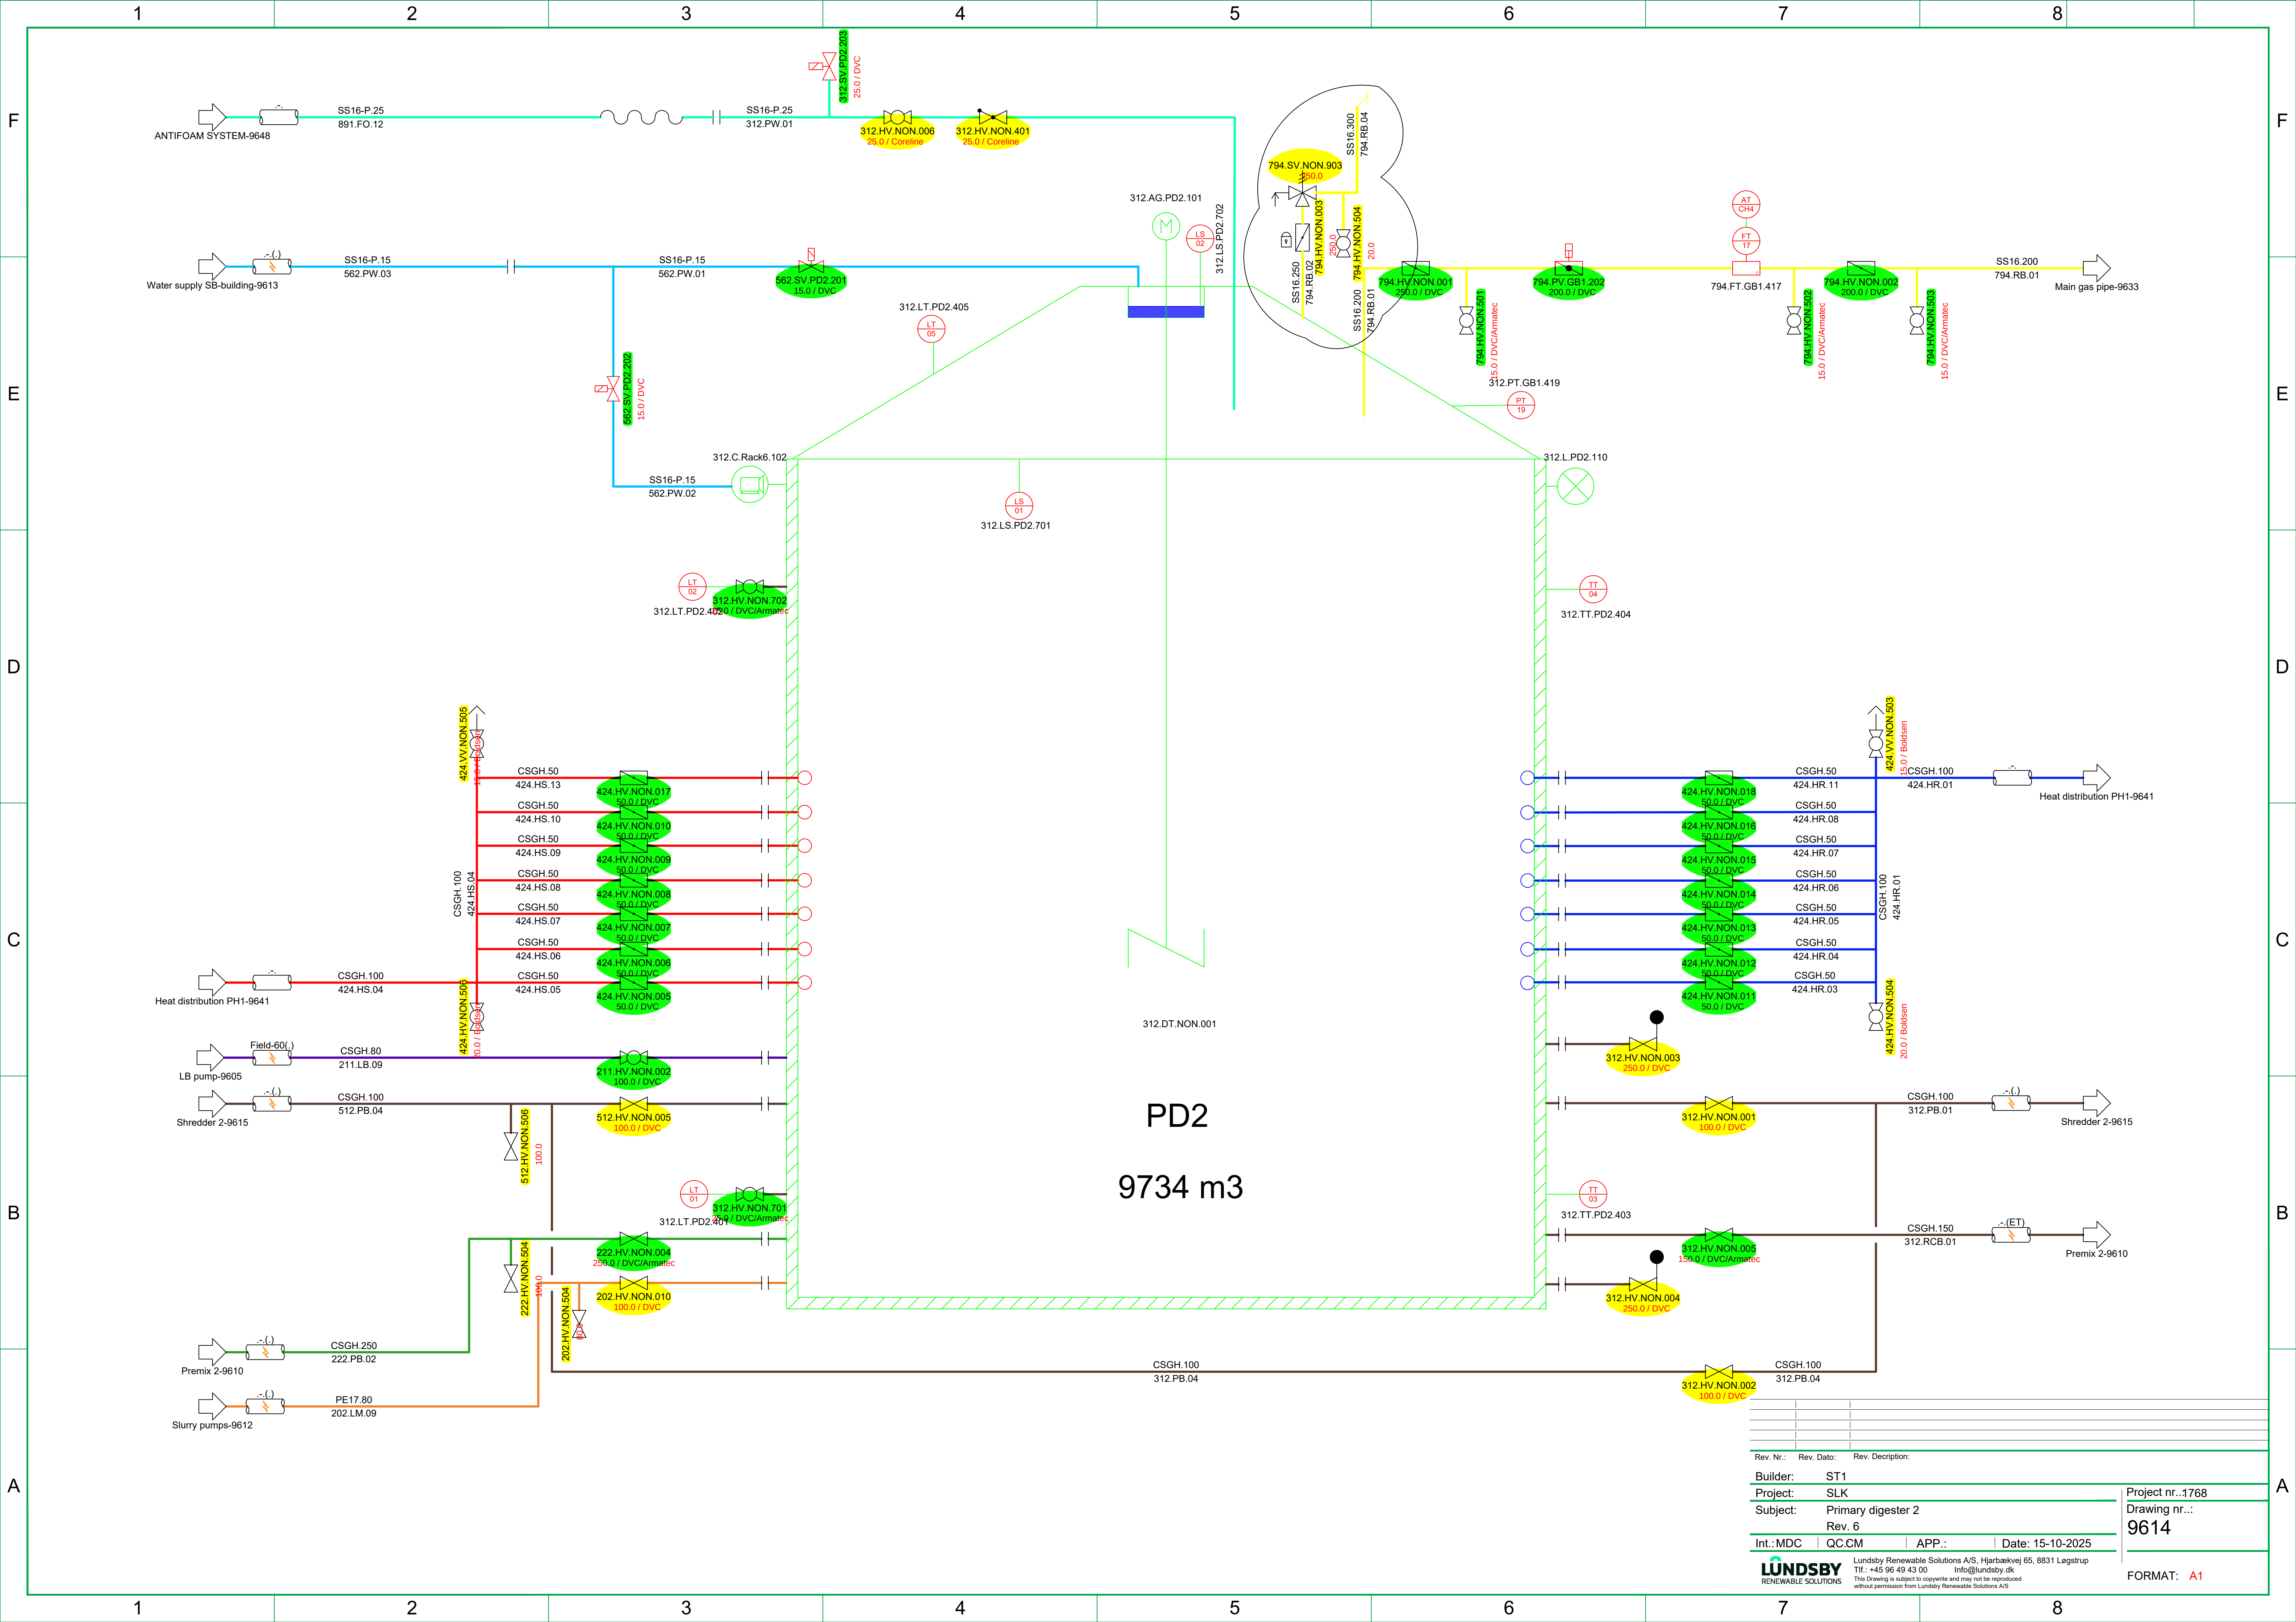


Rev. Nr.:	Rev. Dato:	Rev. Description:
Builder:	ST1	
Project:	SLK	
Subject:	Primary digester 2	
Rev. 6		
Int.:MDC	QC:CM	APP.:
Date:	15-10-2025	
LUNDSBY RENEWABLE SOLUTIONS		
Lundsby Renewable Solutions A/S, Hjarbækvej 65, 8831 Lægstrup Tlf.: +45 96 49 43 00 Info@lundsby.dk This drawing is subject to copyright and may not be reproduced without permission from Lundsby Renewable Solutions A/S		
Project nr.:1768 Drawing nr.: 9614		FORMAT: A1

Pumphouse 1

Shredder line 1

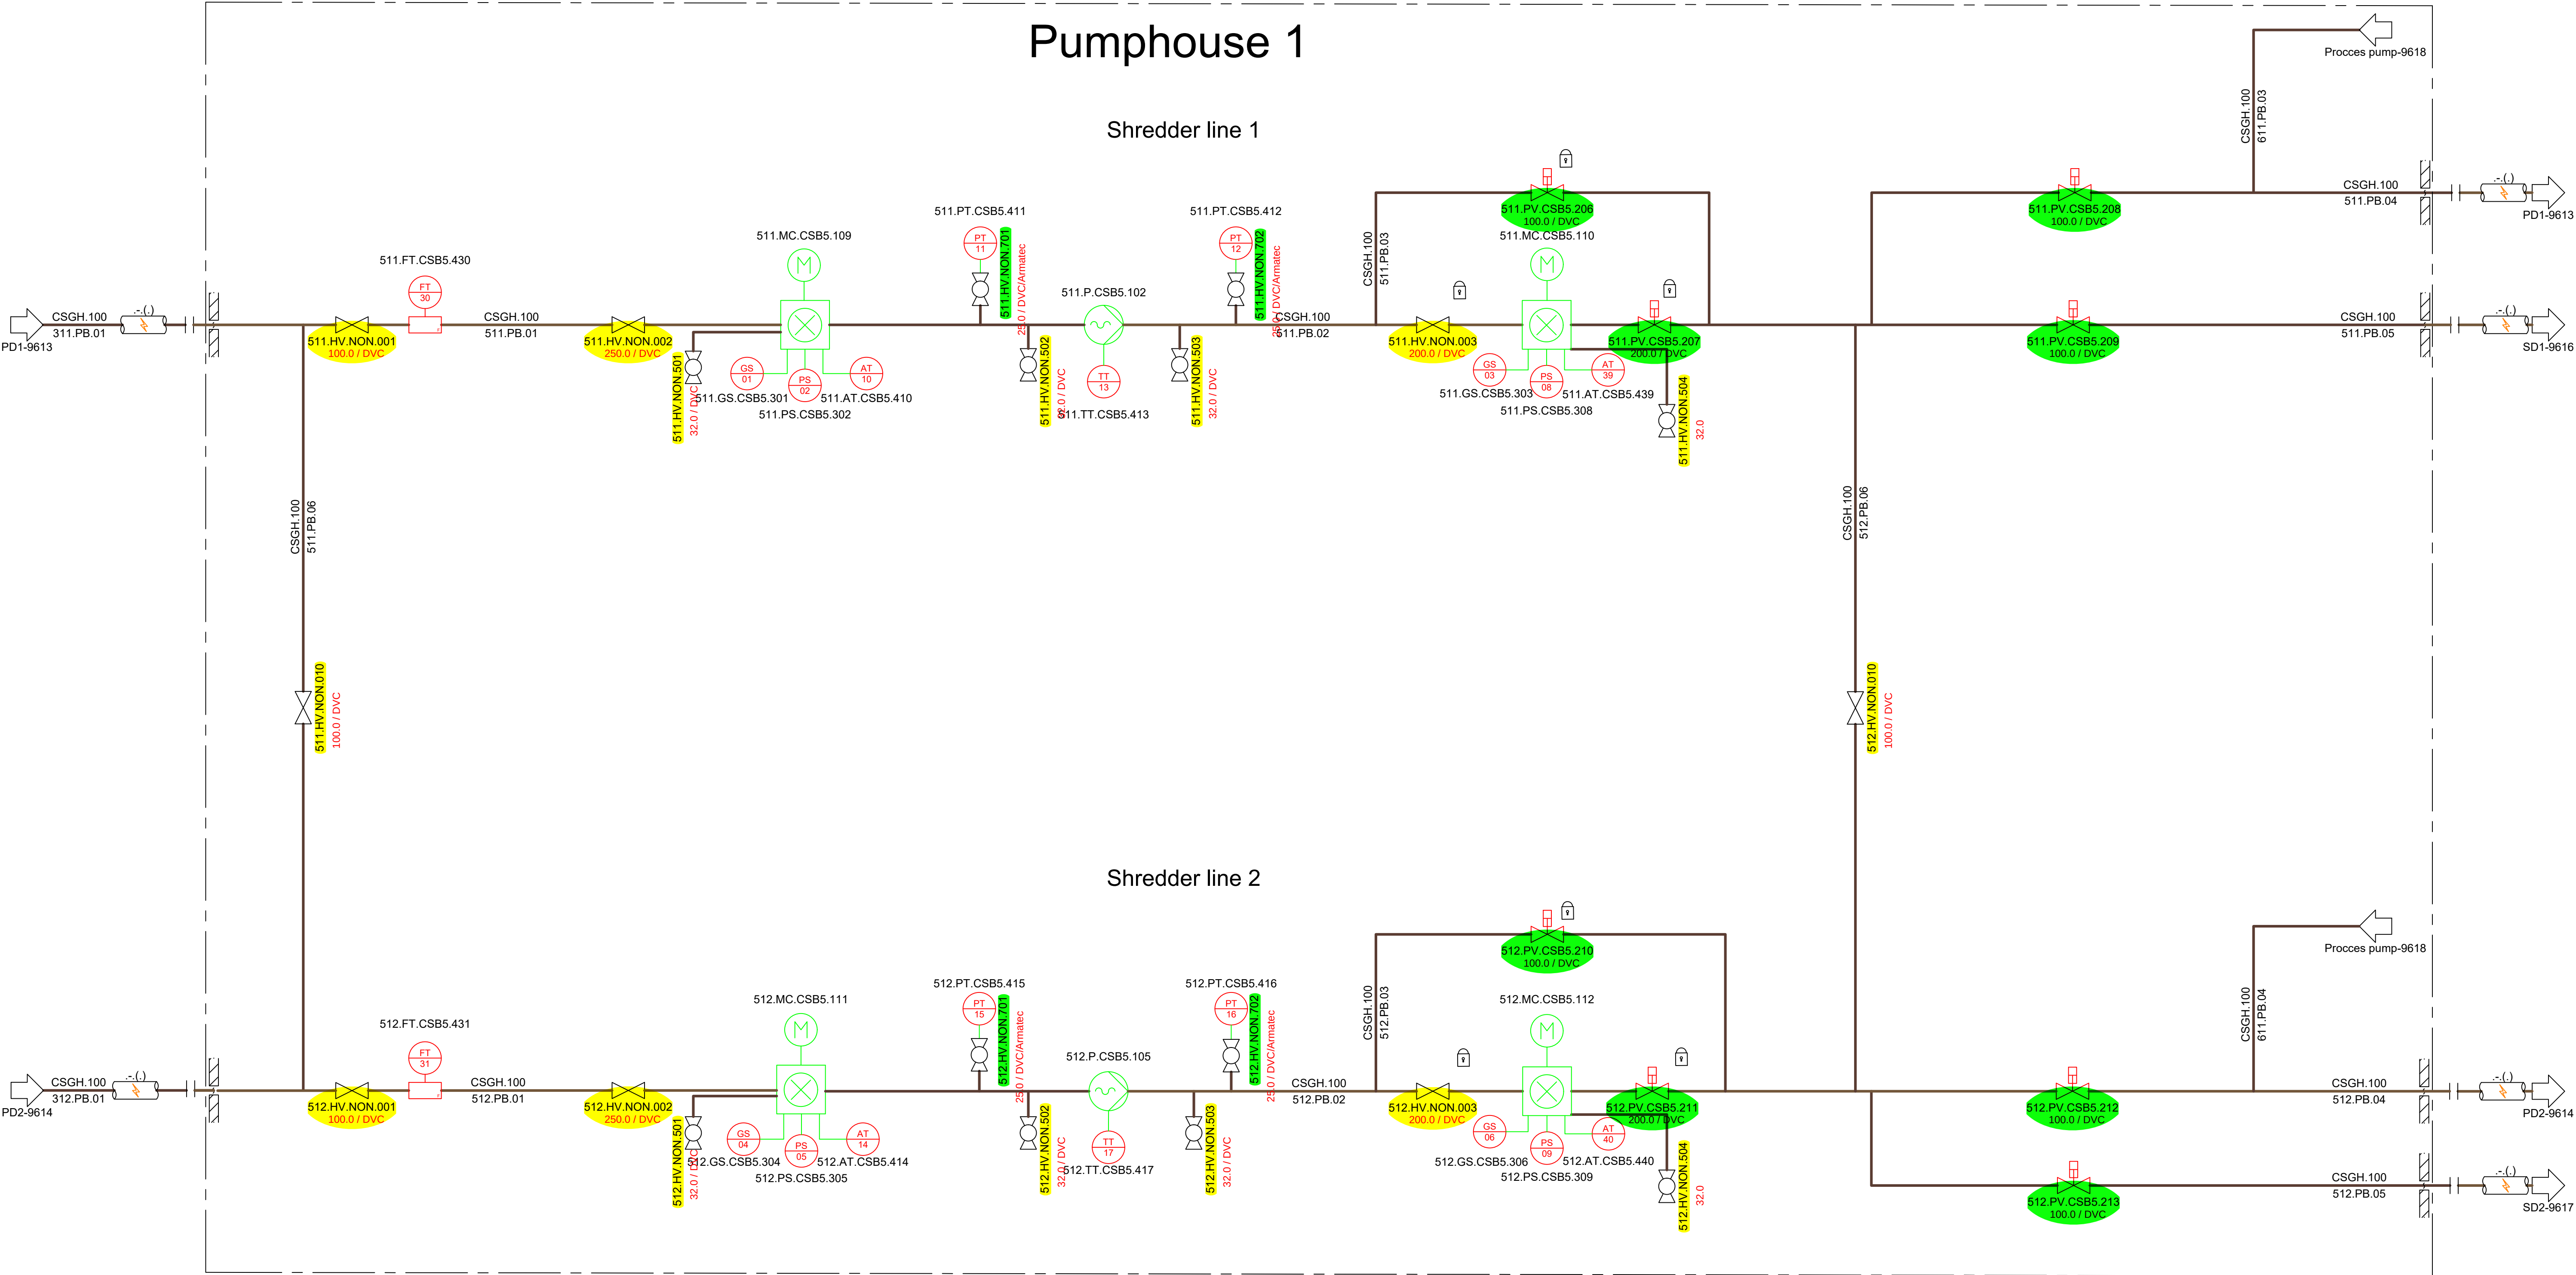


Rev. Nr.:	Rev. Dato:	Rev. Description:
Builder:	ST1	
Project:	SLK	
Subject:	Shredder line 1&2	
Rev. 6		
Int.:MDC	QC:CM	APP.:
Date: 15-10-2025		
Project nr.:1768		
Drawing nr.: 9615		
FORMAT: A1		

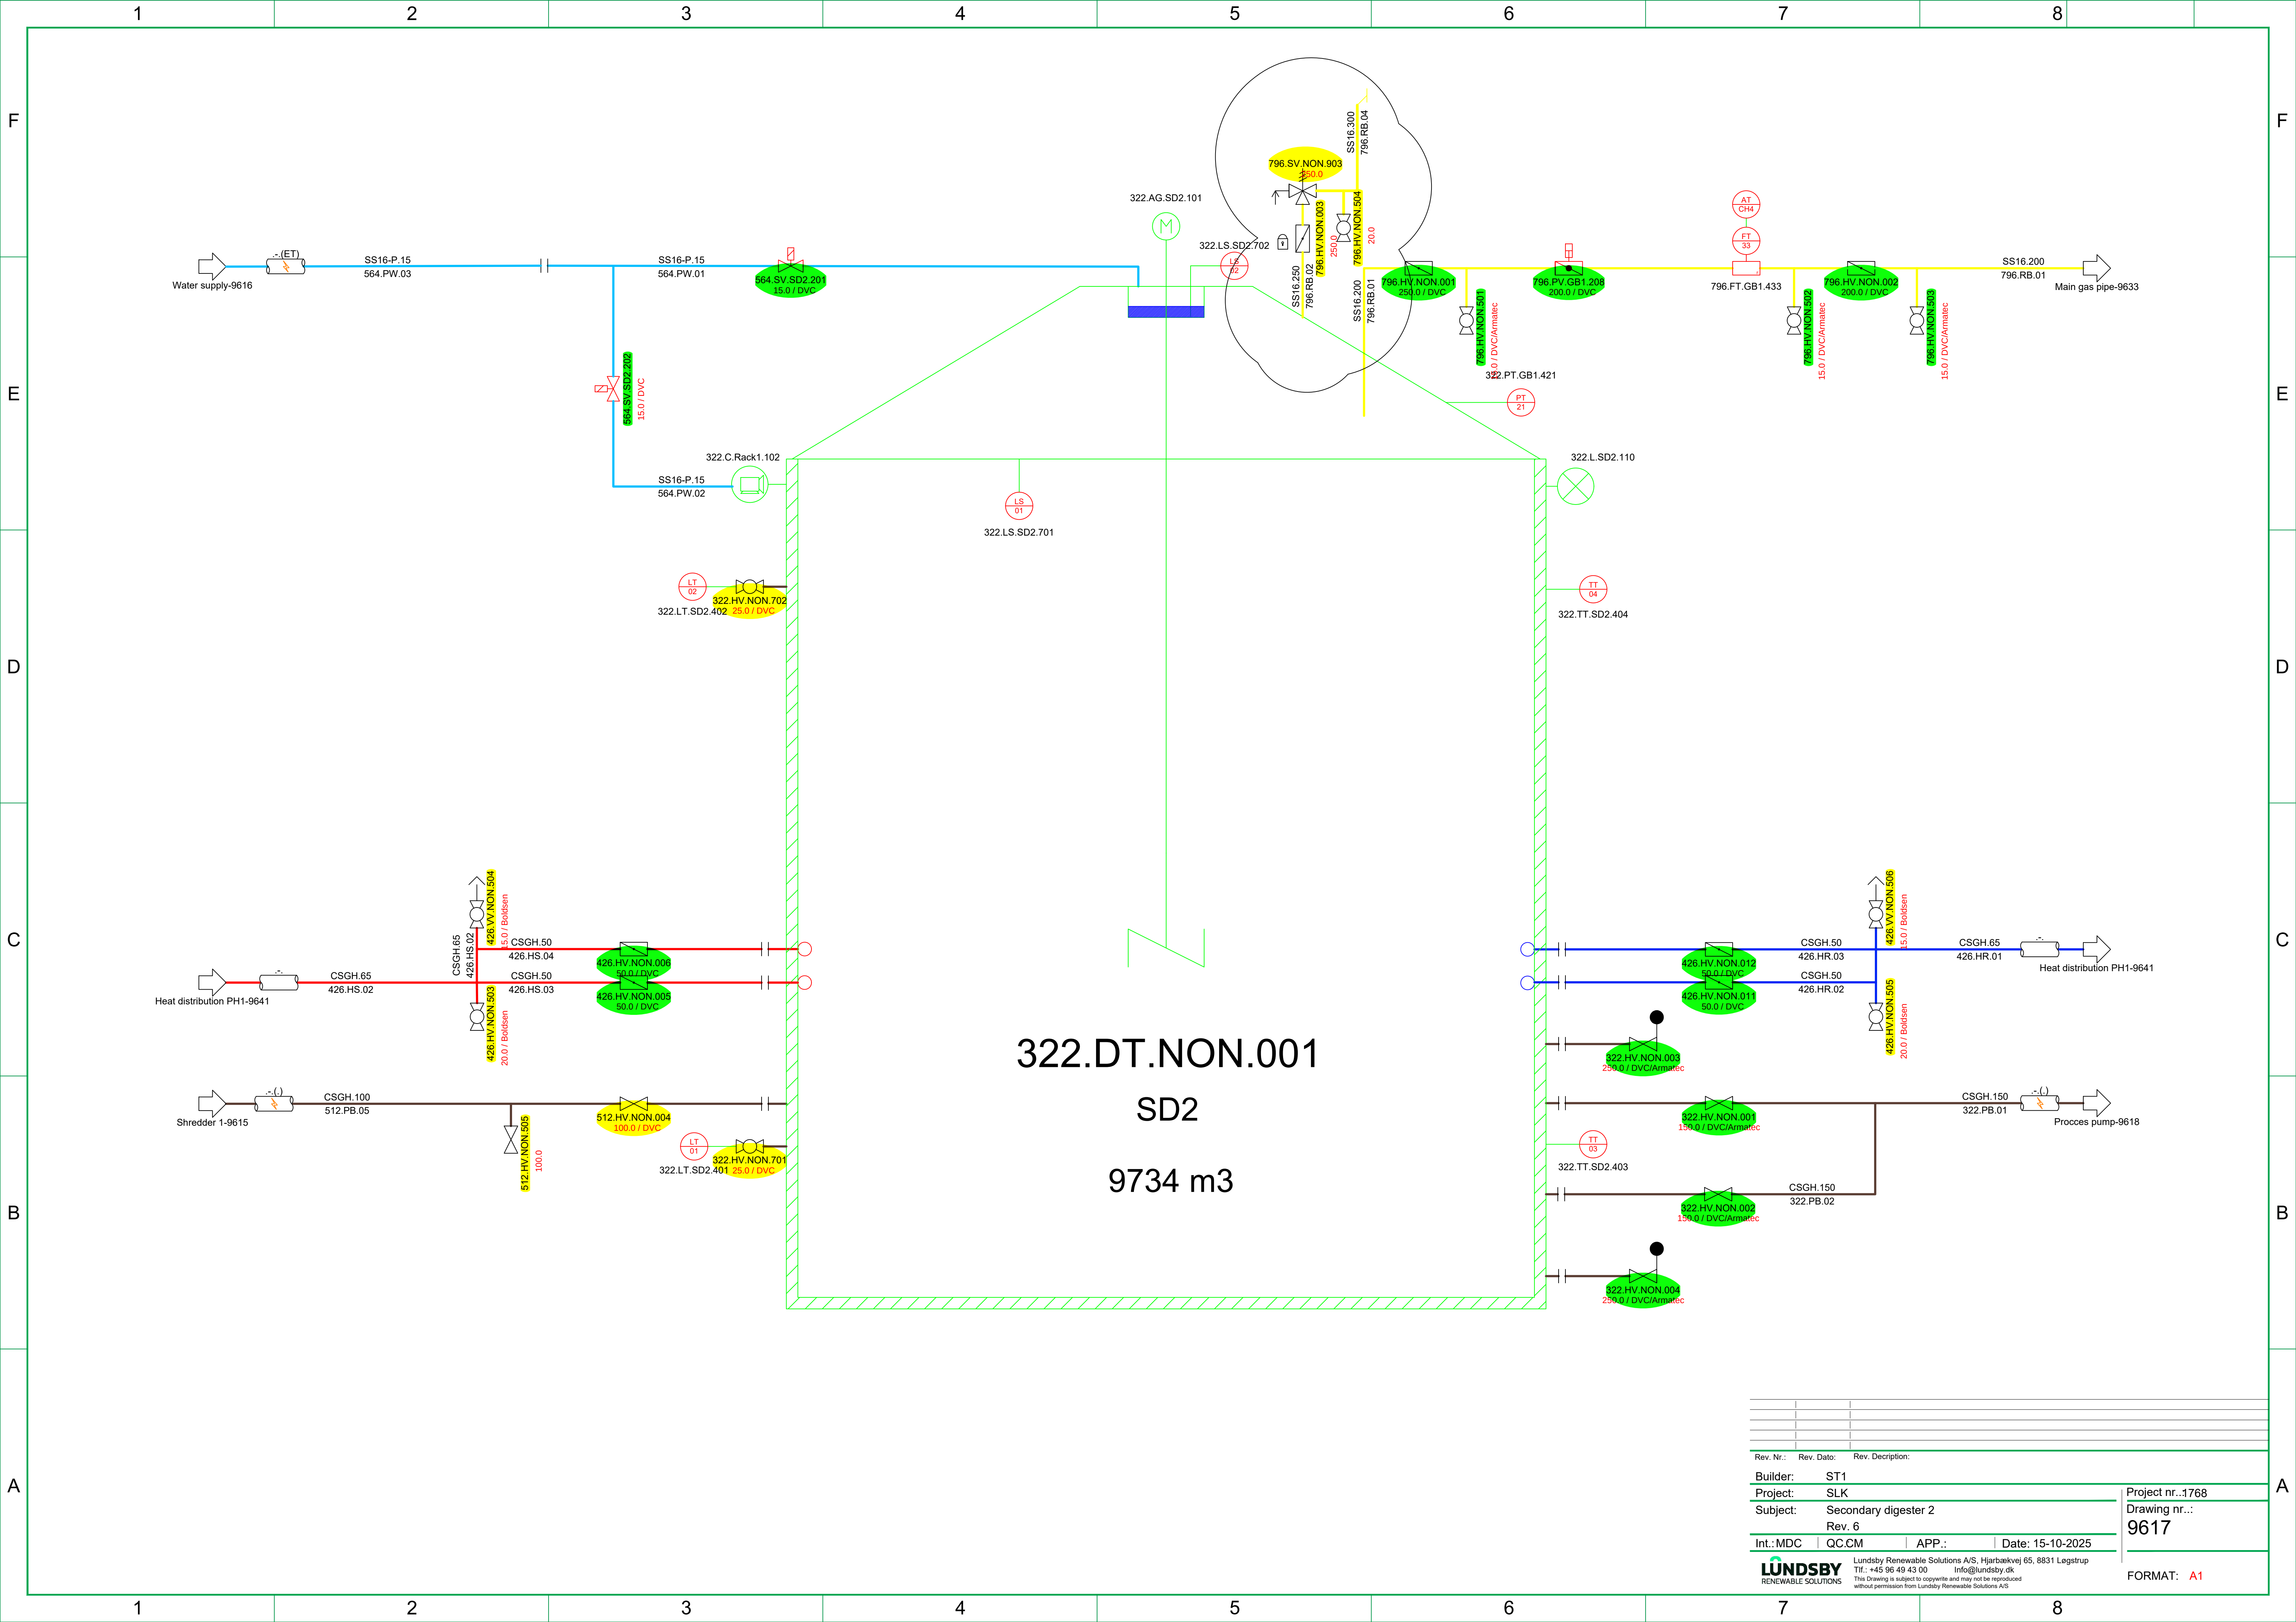


Rev. Nr.:	Rev. Dato:	Rev. Description:
Builder:	ST1	
Project:	SLK	
Subject:	Secondary digester 2	
Rev. 6		
Int.:MDC	QC:CM	APP.:
Date:	15-10-2025	
LUNDSBY RENEWABLE SOLUTIONS		
Lundsgby Renewable Solutions A/S, Hjarbrækvej 65, 8831 Lægstrup Tlf.: +45 96 49 43 00 Info@lundsgby.dk This Drawing is subject to copyright and may not be reproduced without permission from Lundsgby Renewable Solutions A/S		
Project nr.:1768 Drawing nr.: 9617		FORMAT: A1

Pumphouse 1

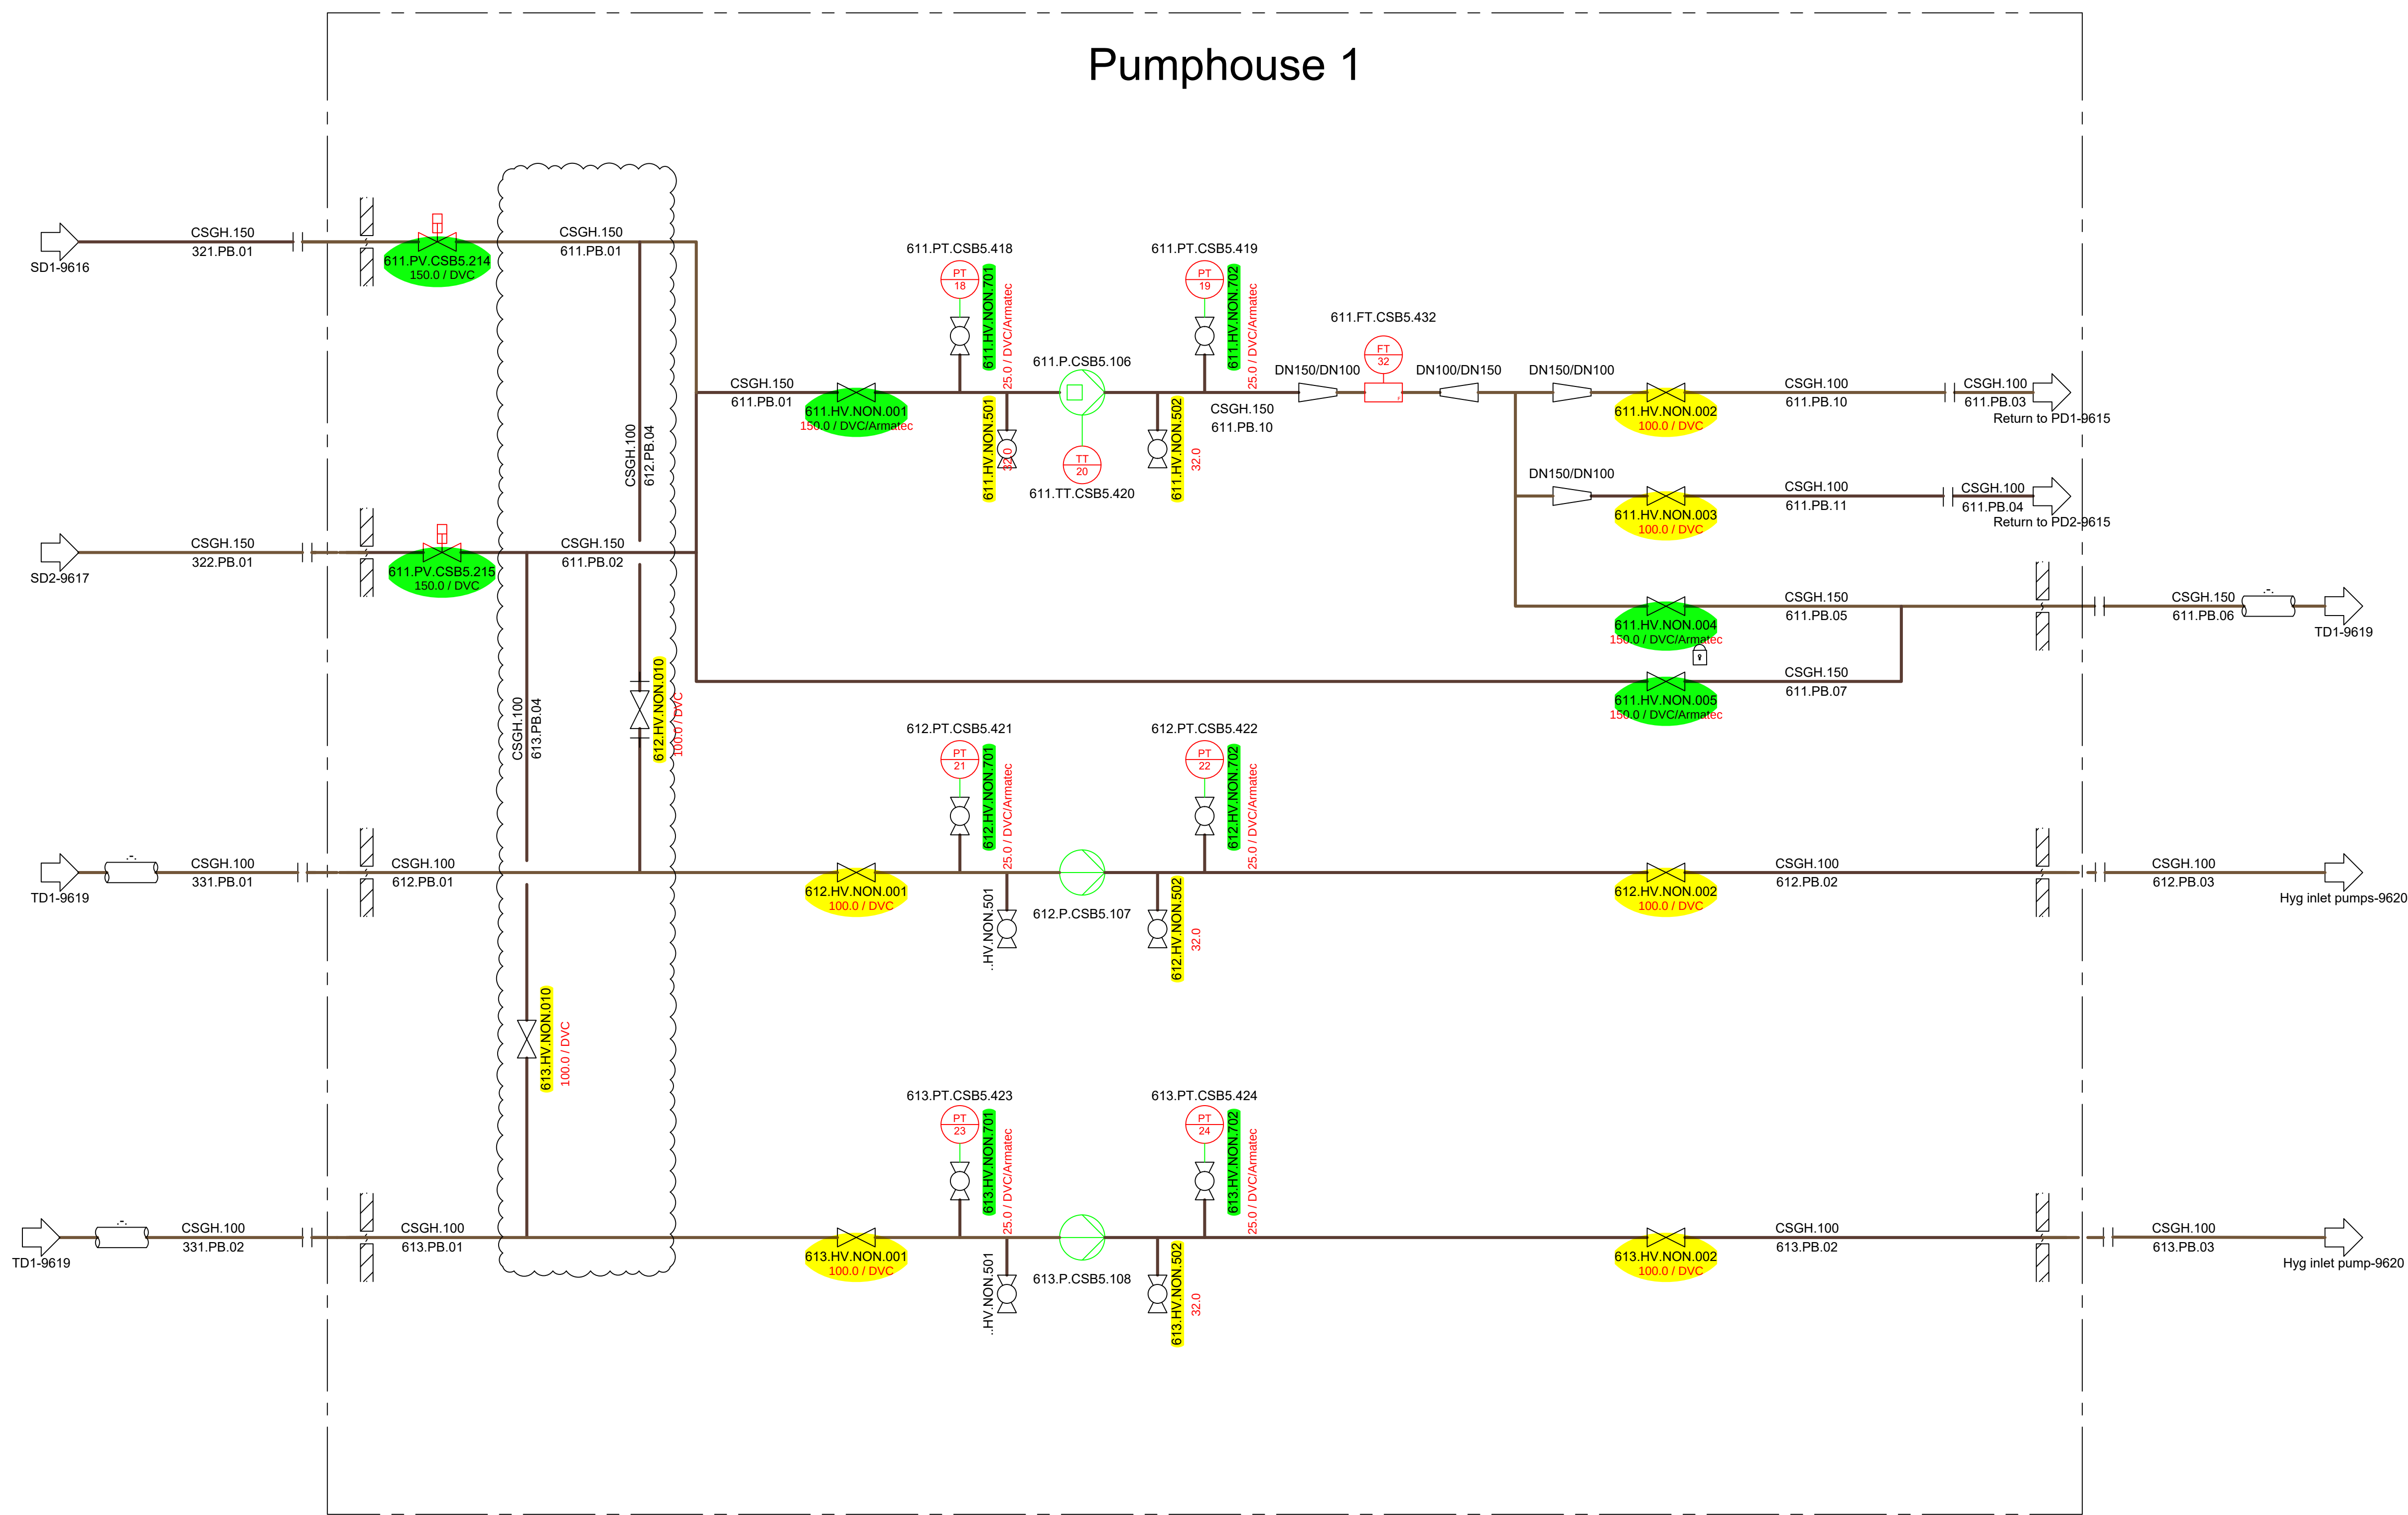


Rev. Nr.:	Rev. Dato:	Rev. Description:	
Builder:	ST1		
Project:	SLK		
Subject:	Procces pumps		
	Rev. 6		
Int.:MDC	QC:CM	APP.:	Date: 15-10-2025
LUNDSBY RENEWABLE SOLUTIONS			Lundsby Renewable Solutions A/S, Hjarbækvej 65, 8831 Løgstrup Tlf.: +45 96 49 43 00 Info@lundsby.dk This Drawing is subject to copyright and may not be reproduced without permission from Lundsby Renewable Solutions A/S
Project nr.:1768 Drawing nr.: 9618			FORMAT: A1

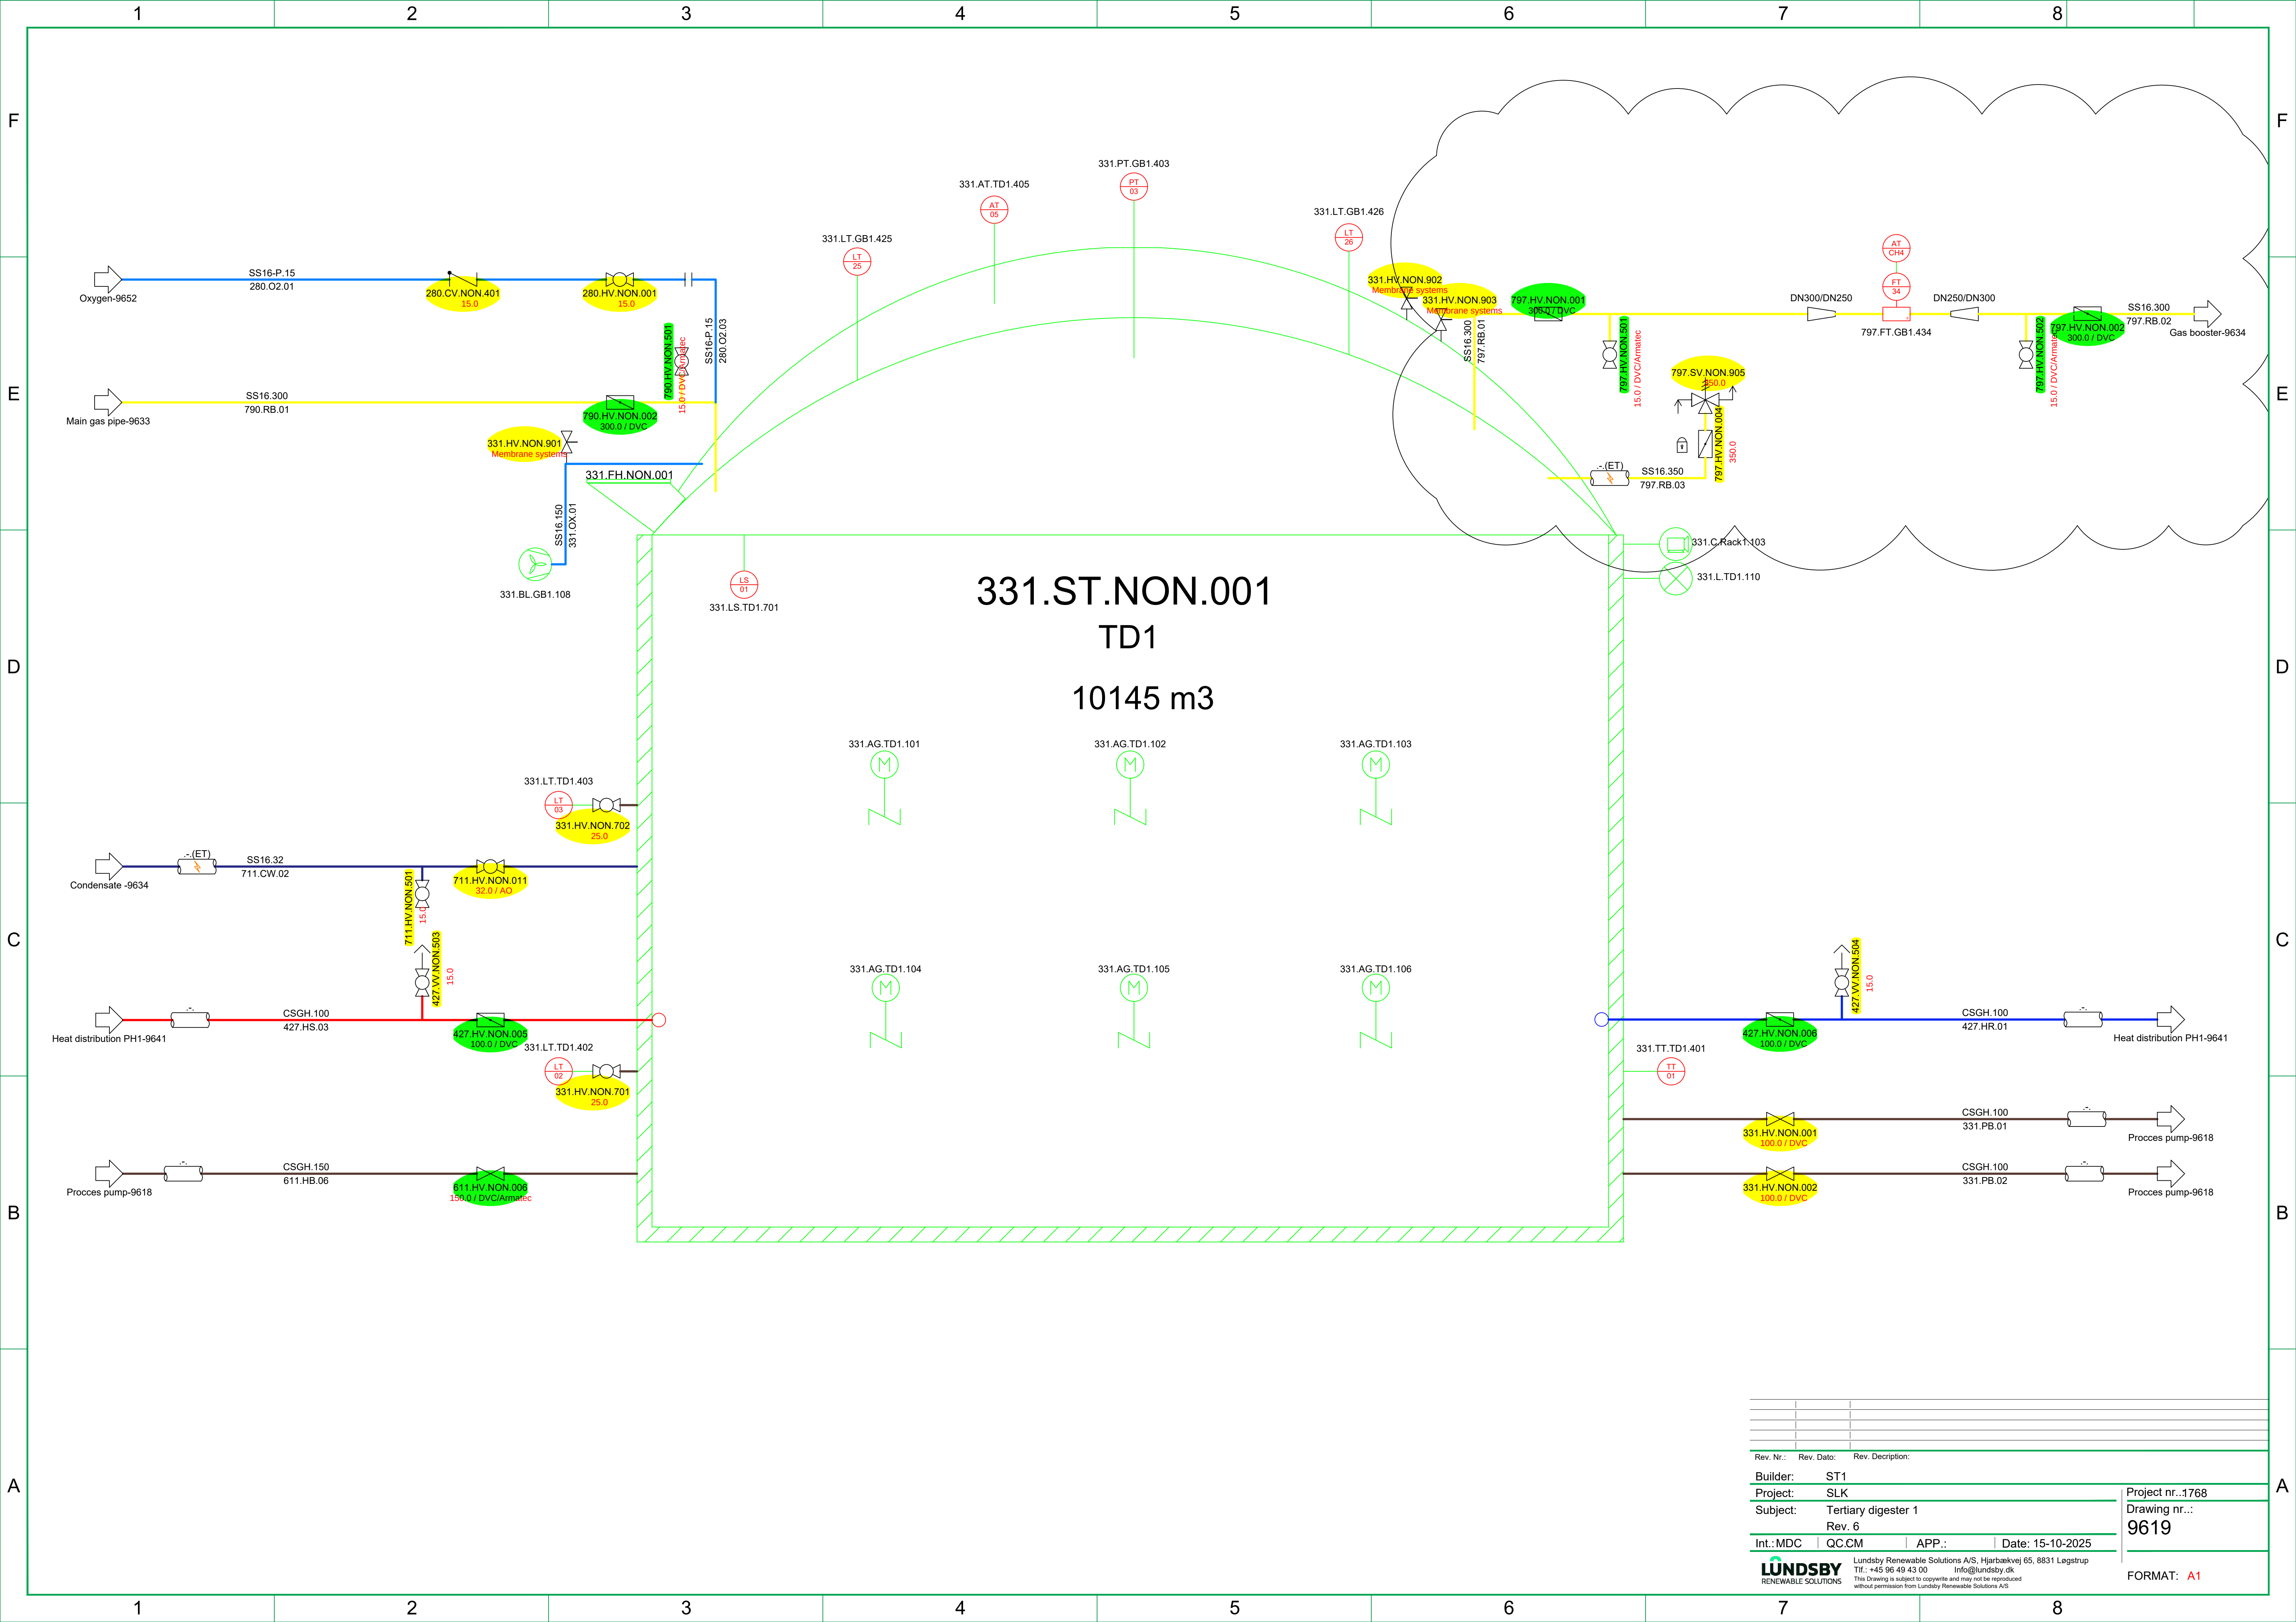



Rev. Nr.:	Rev. Dato:	Rev. Description:		
Builder:	ST1			
Project:	SLK			
Subject:	Tertiary digester 1			
	Rev. 6			
Int.:MDC	QC:CM	APP.:	Date: 15-10-2025	
		Lundsby Renewable Solutions A/S, Hjarbækvej 65, 8831 Legstrup Tlf.: +45 96 49 43 00 info@lundsby.dk This Drawing is subject to copyright and may not be reproduced without permission from Lundsby Renewable Solutions A/S		
		Project nr.:1768 Drawing nr.: 9619		FORMAT: A1


Tech Building

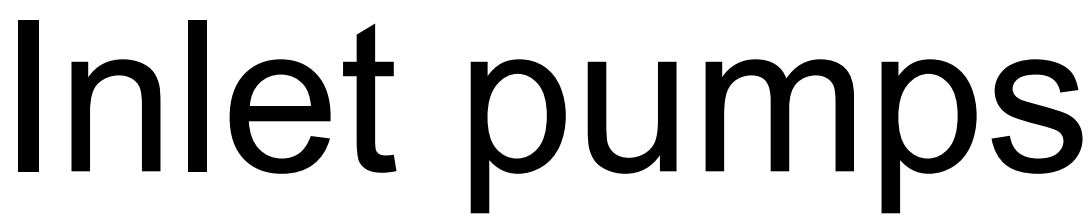


Rev. Nr.:		Rev. Dato:		Rev. Description:	
Builder:		ST1			
Project:		SLK			
Subject:		Hyginisation inlet pumps			
		Rev. 6			
Int.: MDC	QC.CM	APP.:	Date: 15-10-2025		
 Lundbsby Renewable Solutions AS, Hjarbakvej 65, 8831 Legstrup Tlf.: +45 96 49 43 00 Info@lundbsby.dk This Drawing is subject to copyright and may not be reproduced					
				Project nr..:4768	
				Drawing nr.: 9620	
				FORMAT: A1	

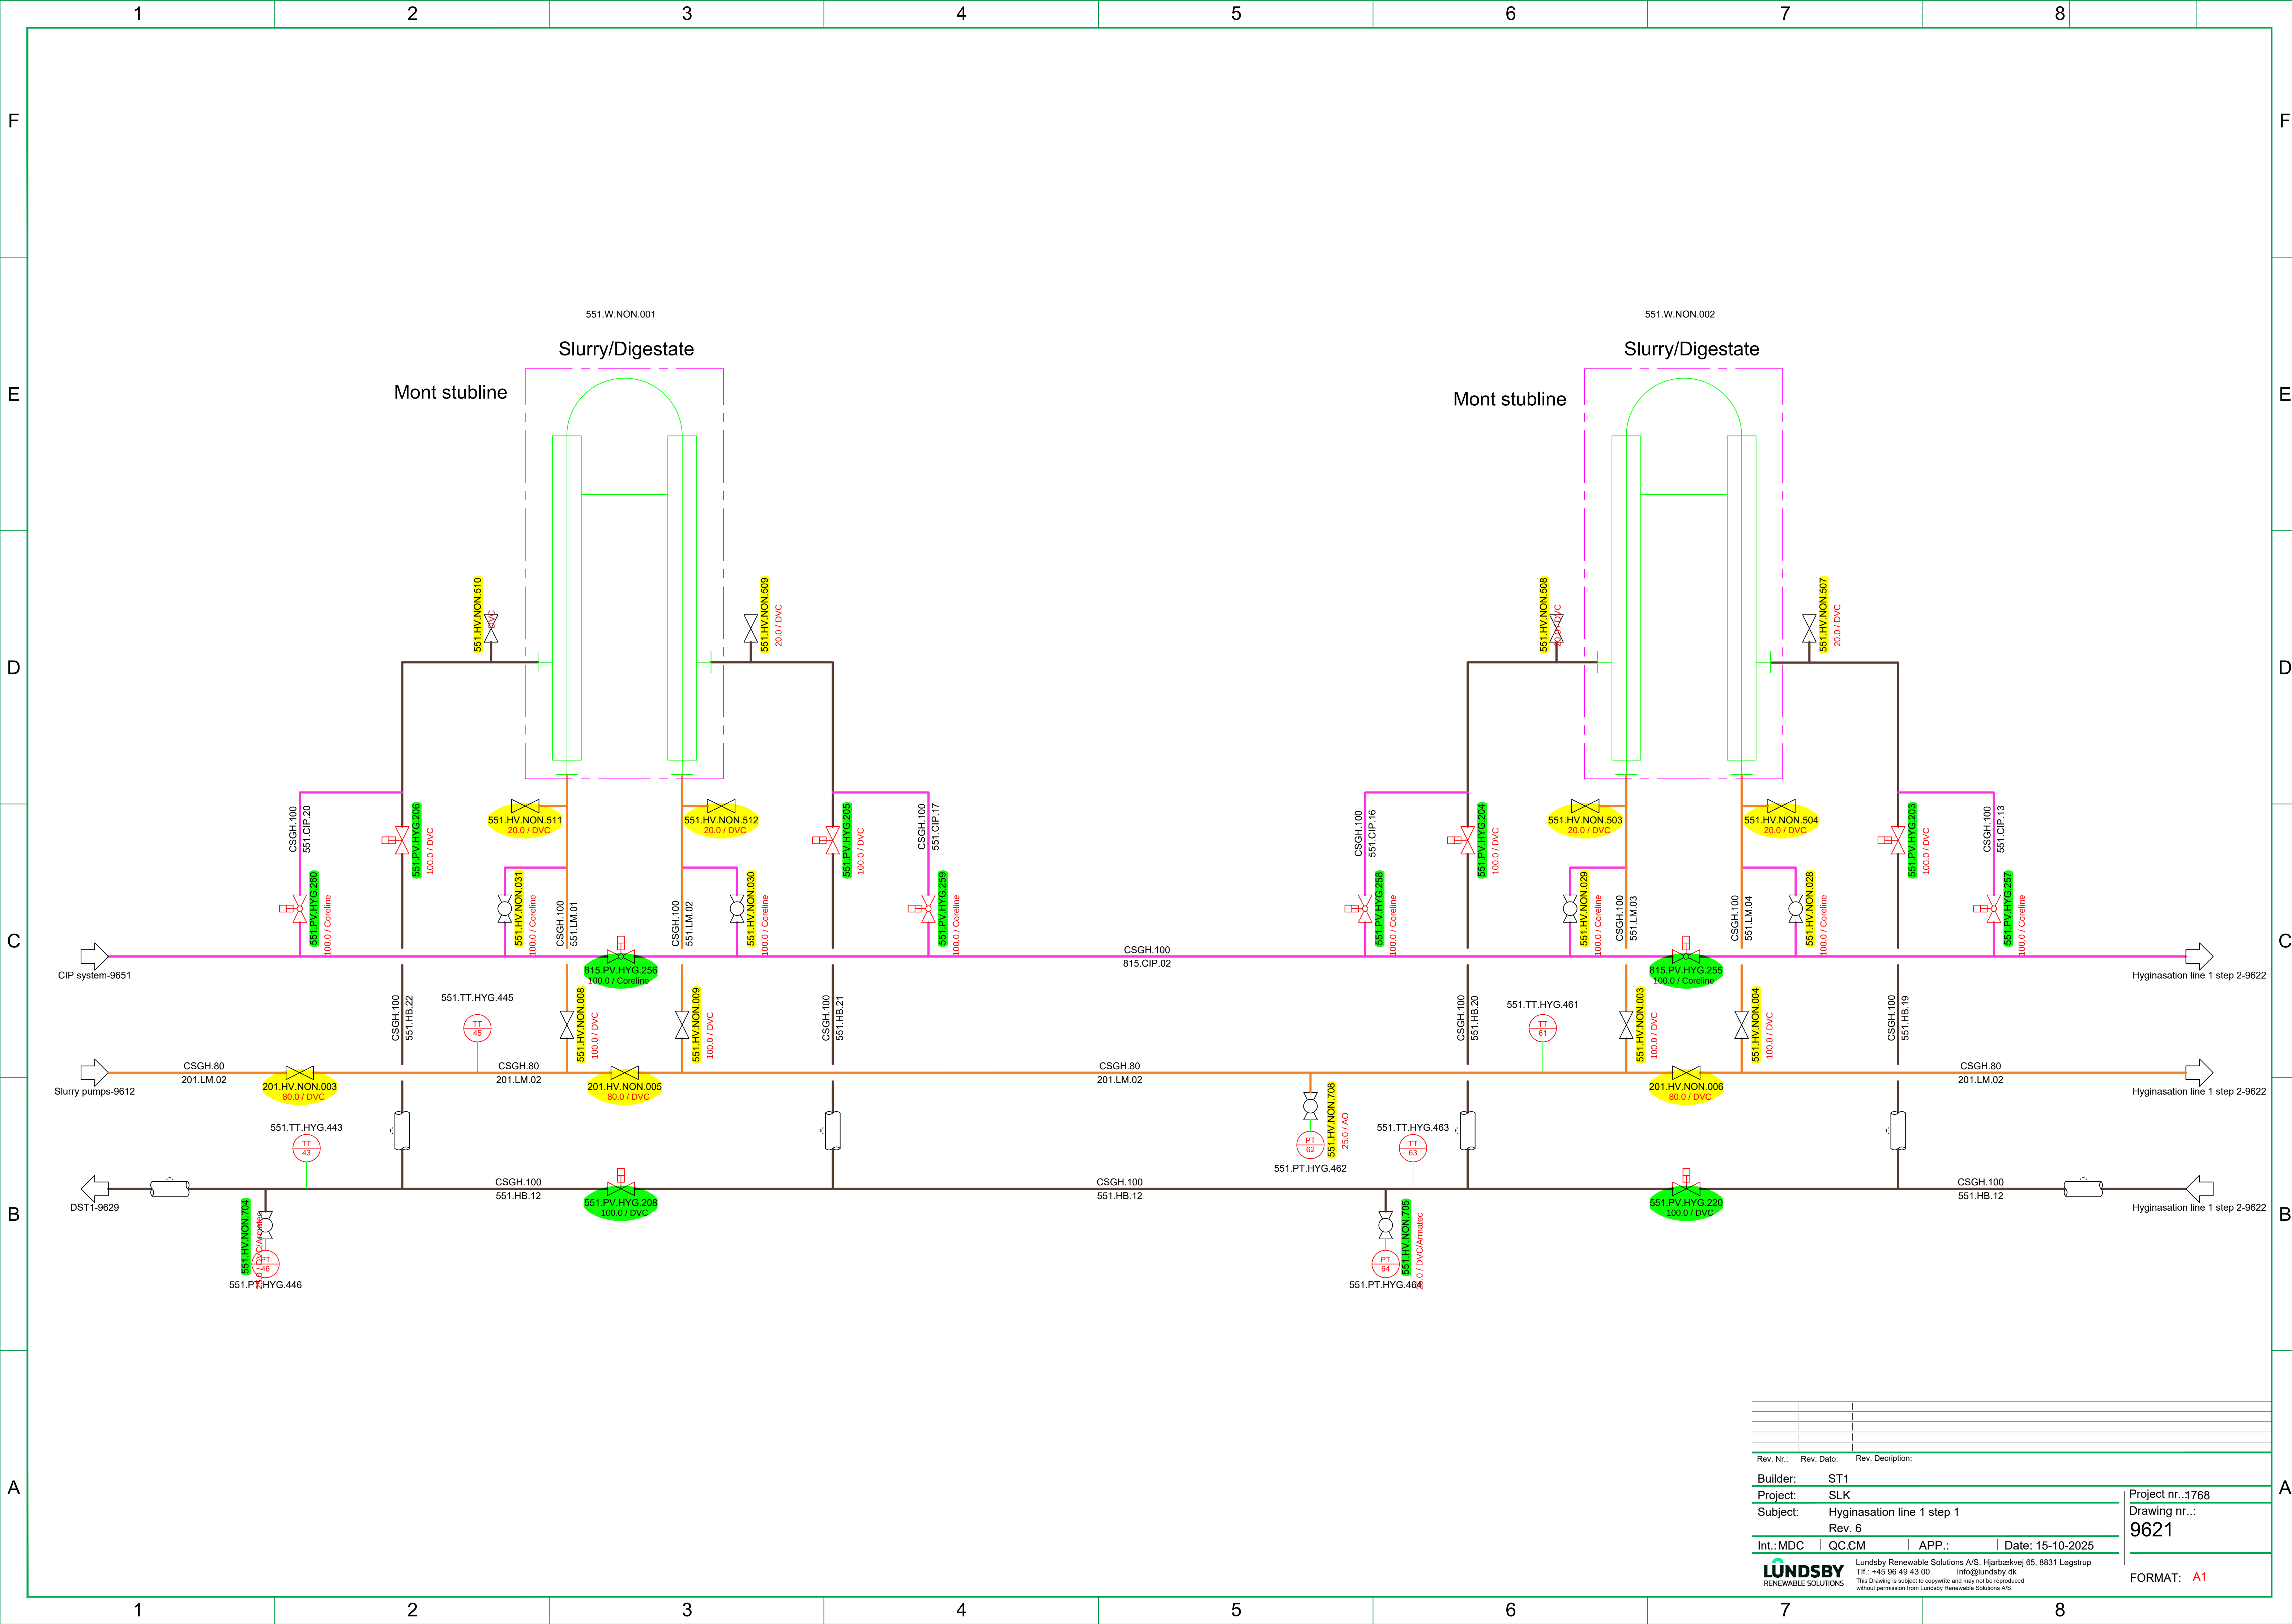

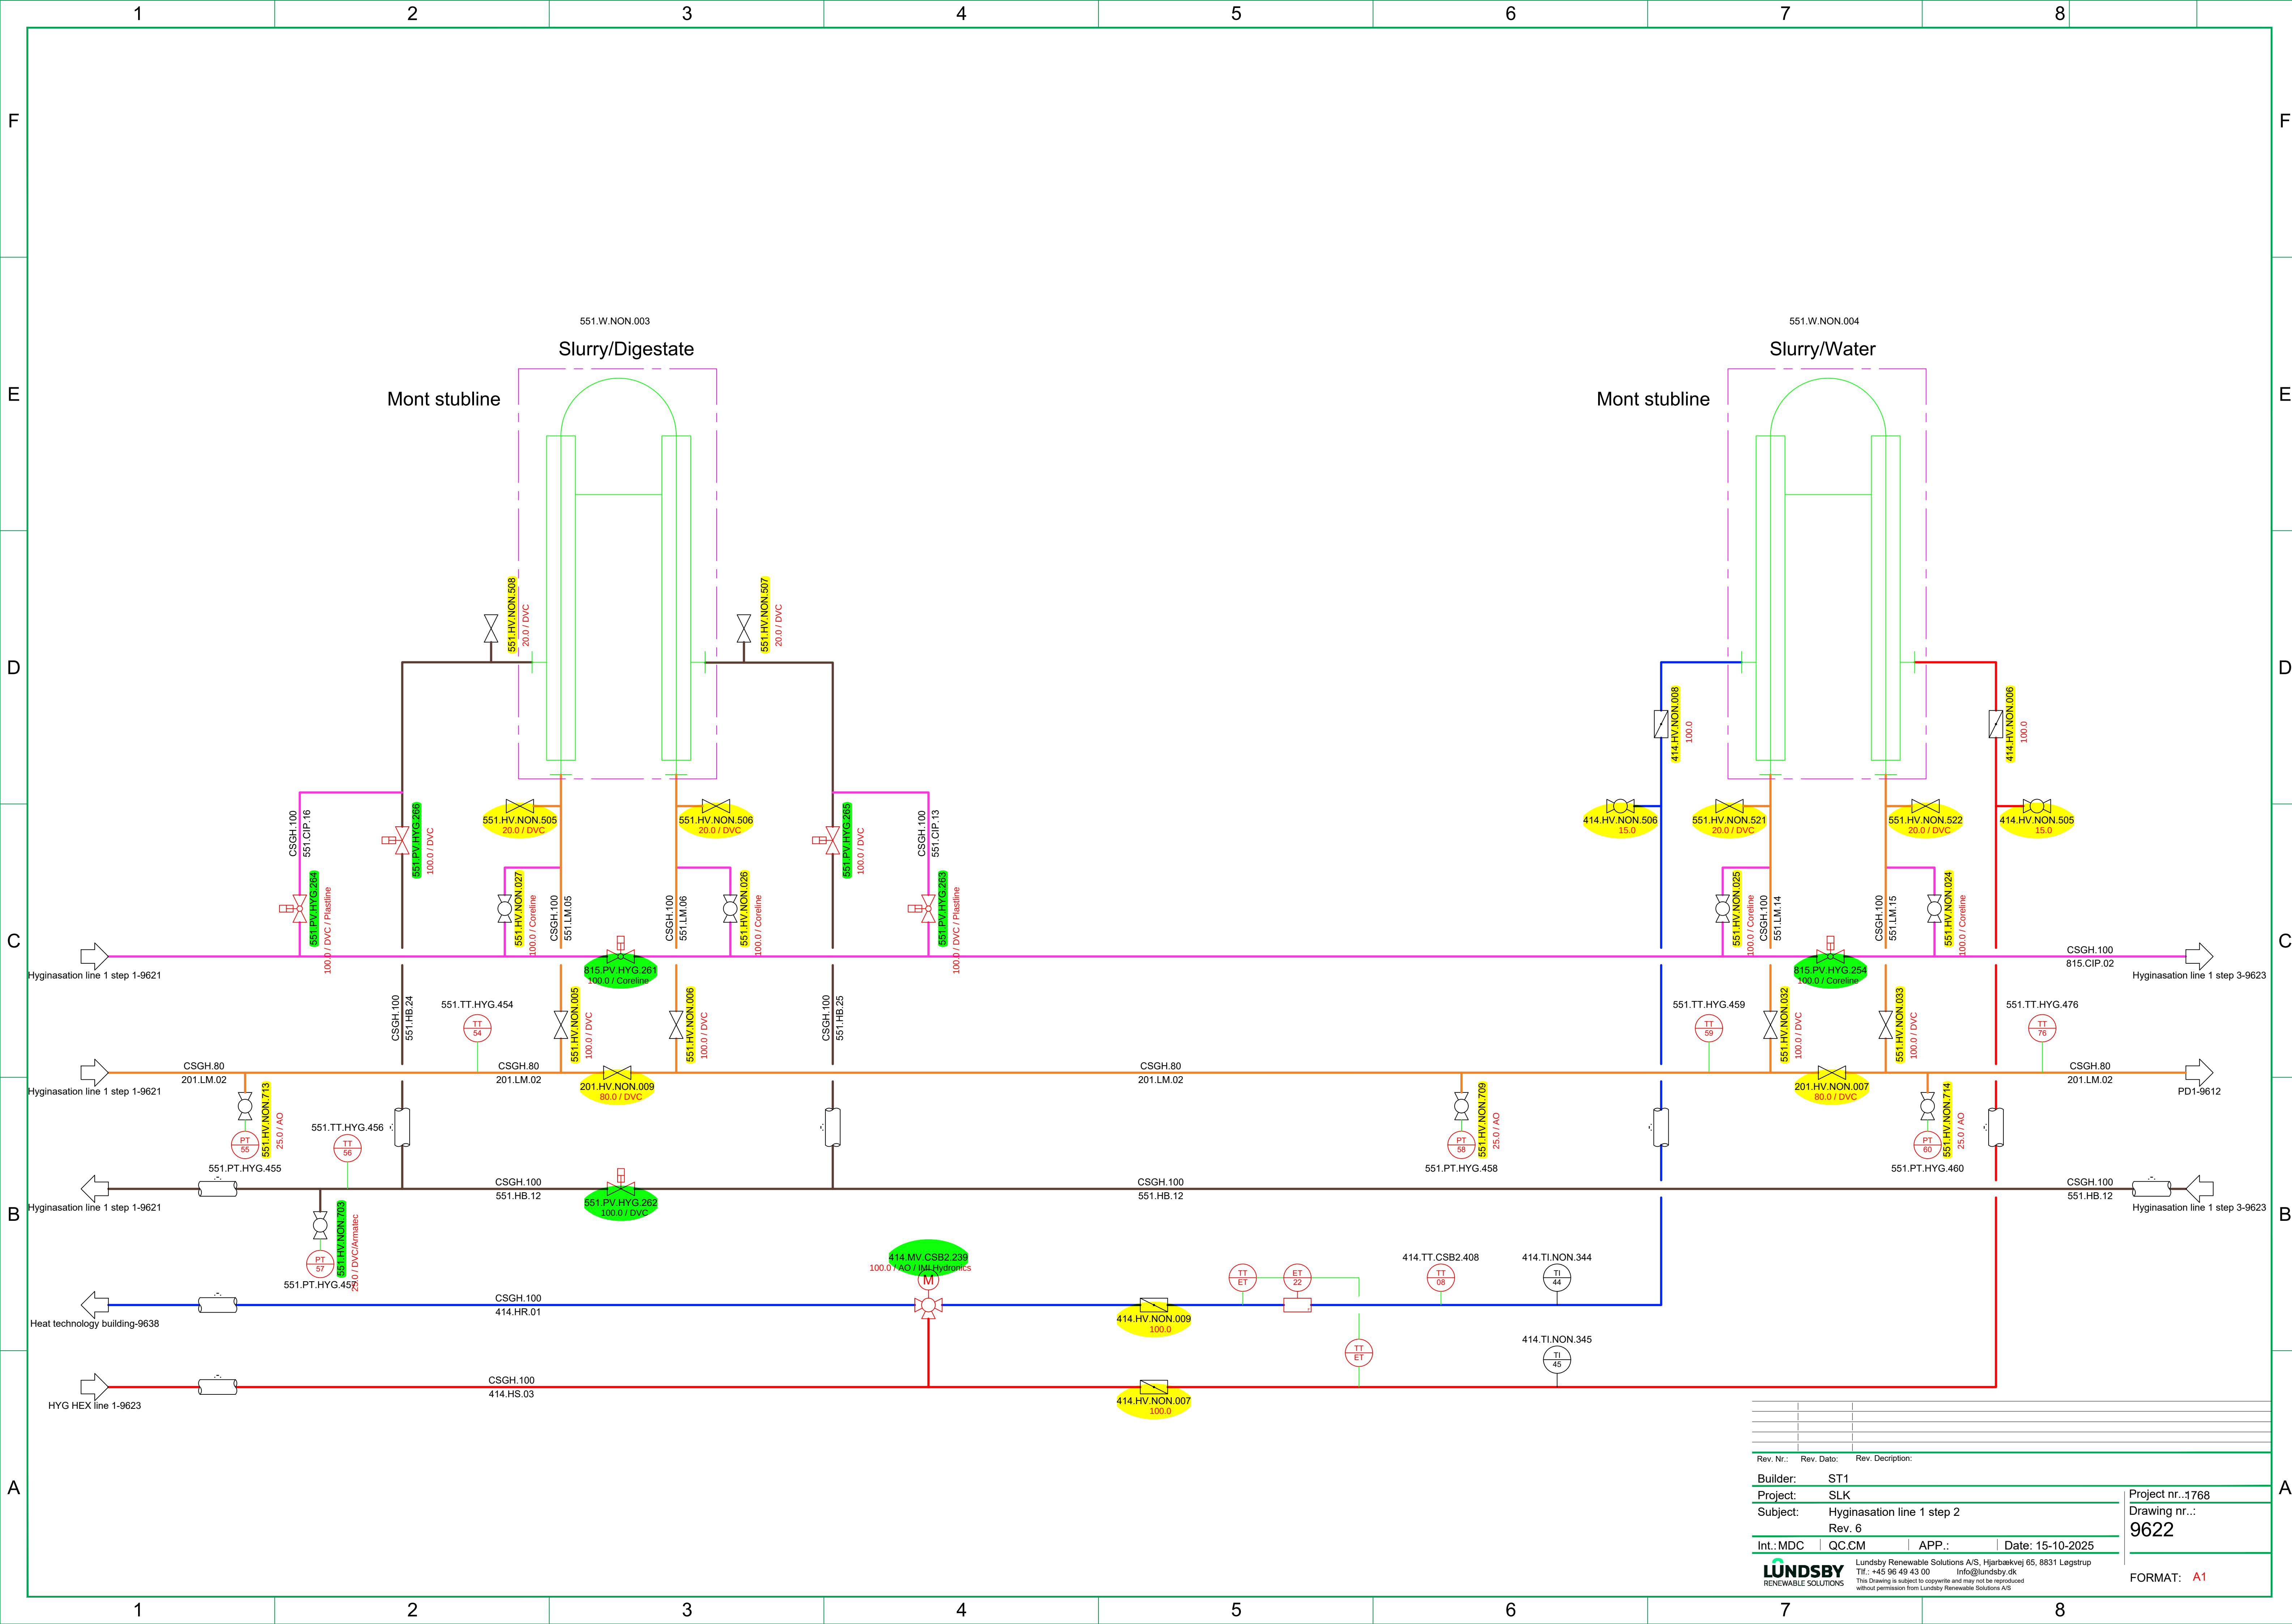


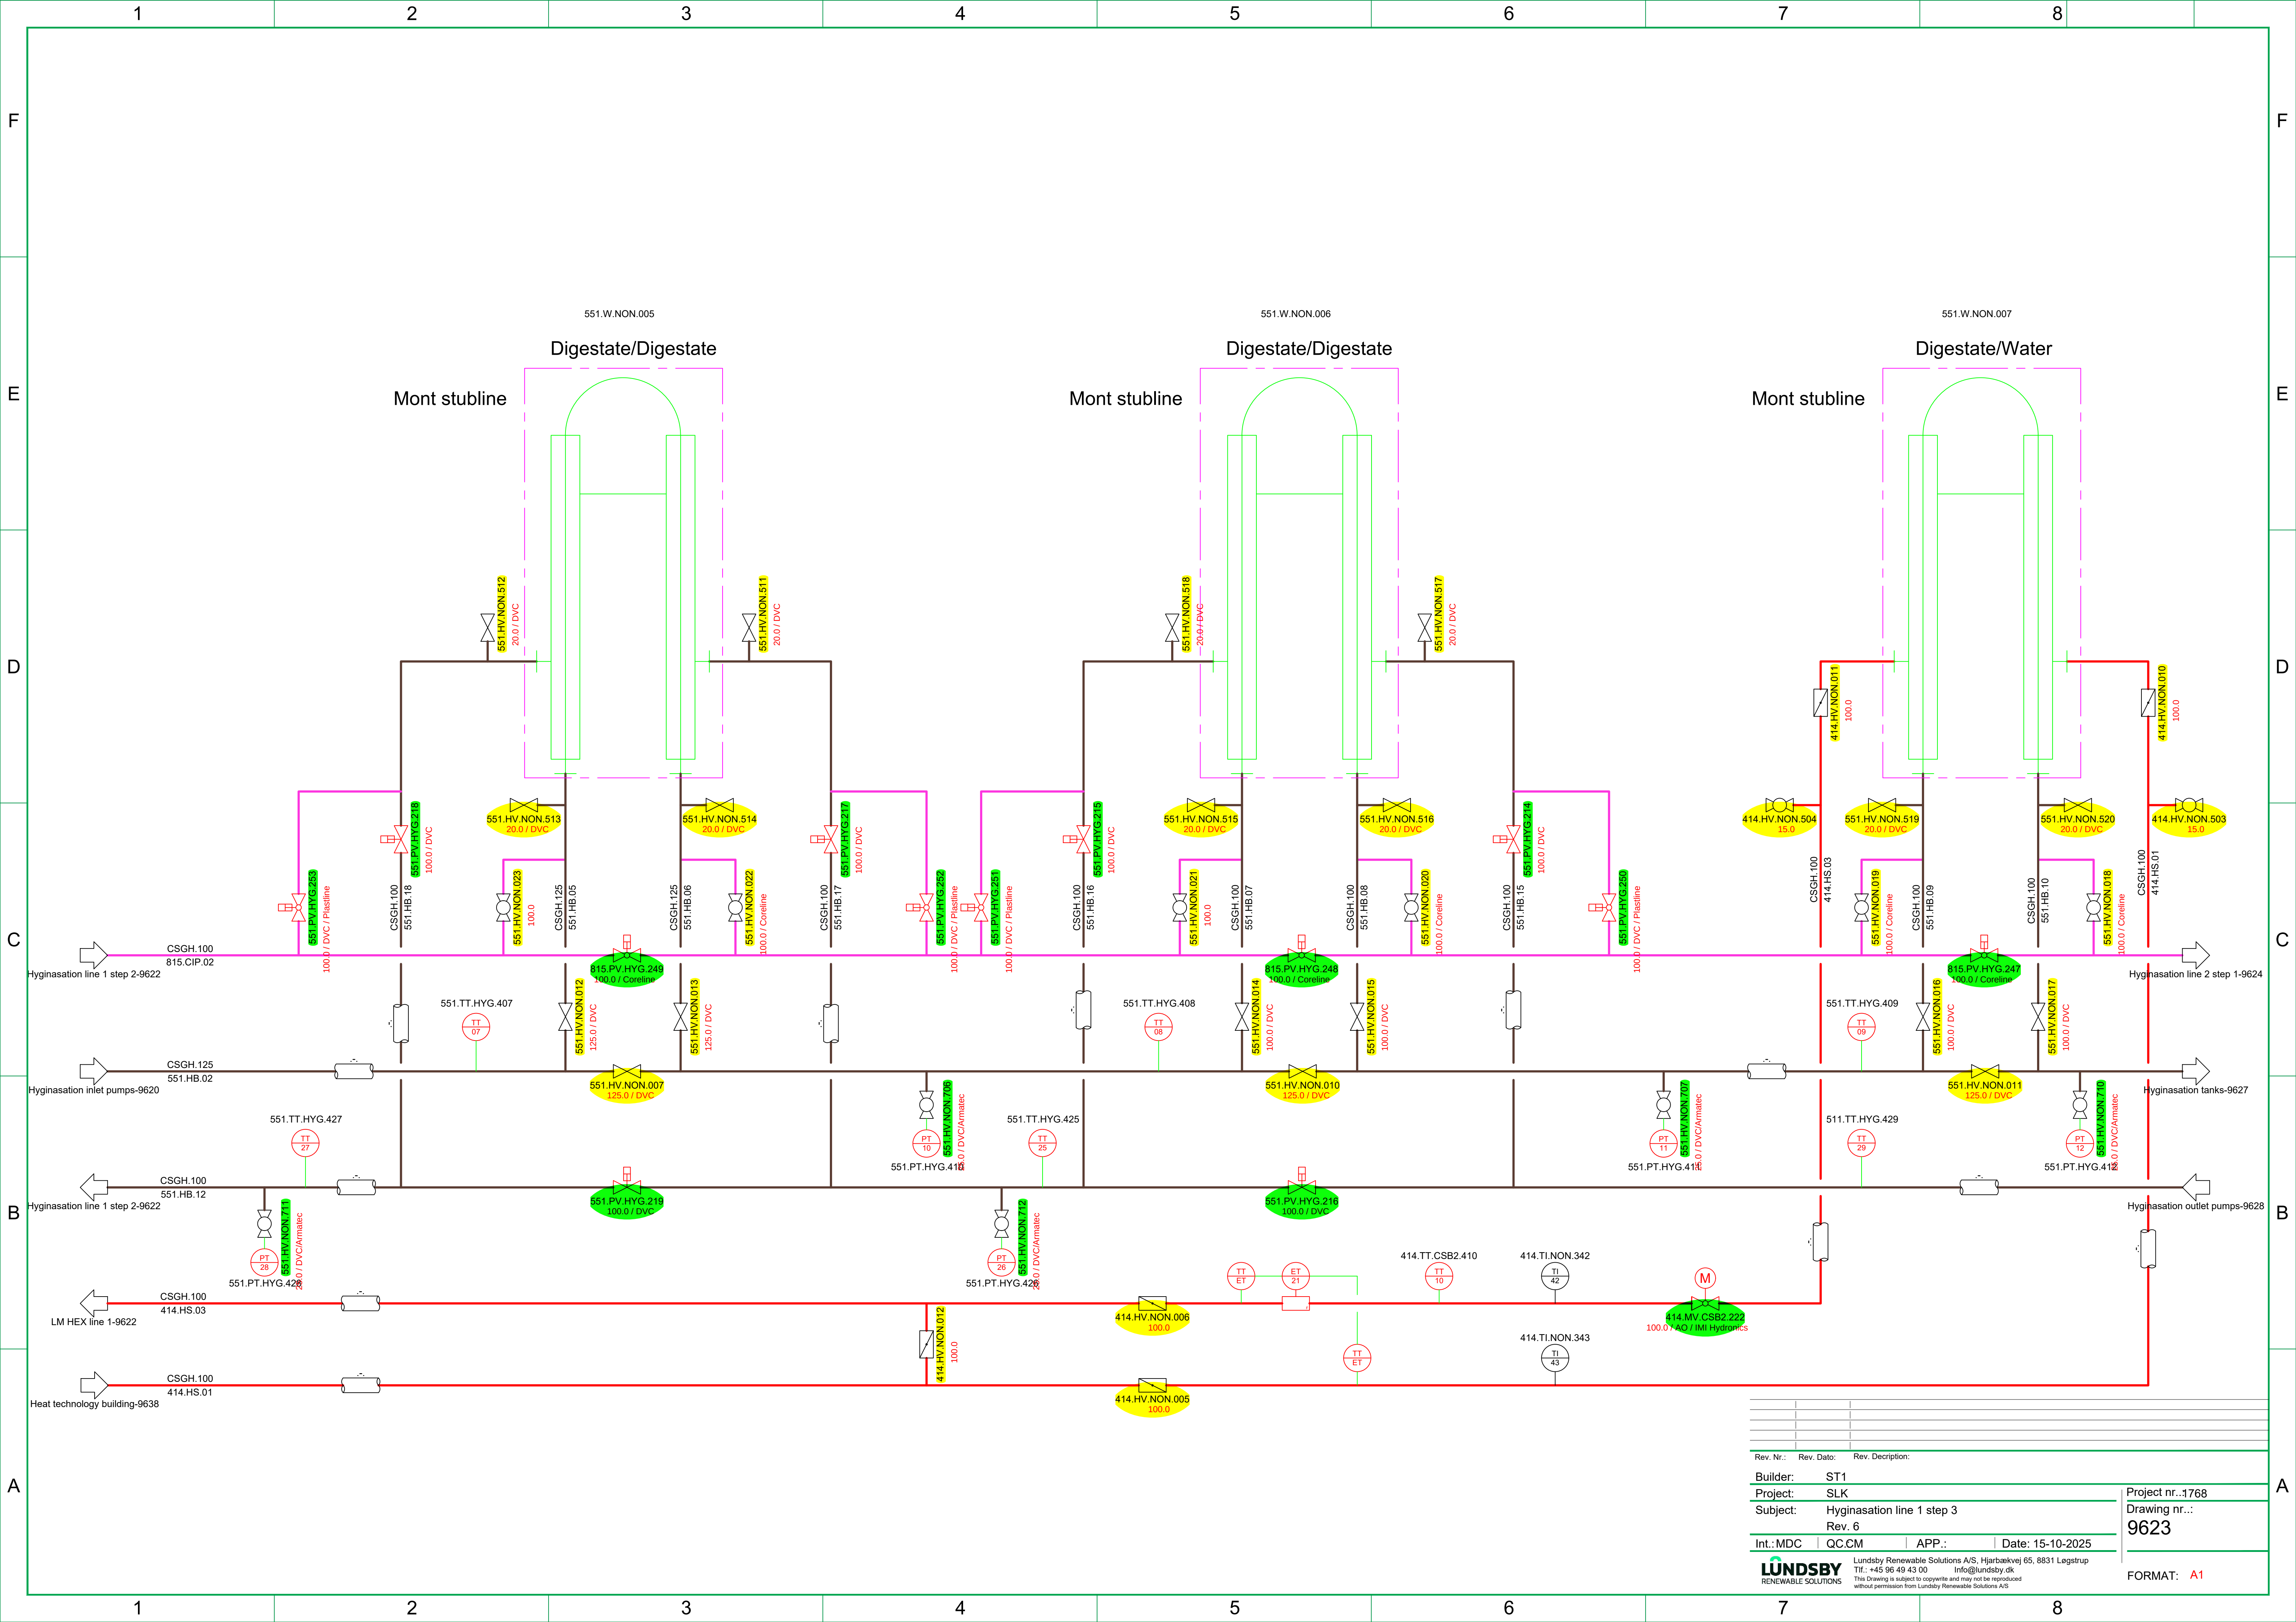

Rev. Nr.:	Rev. Dato:	Rev. Description:
Builder:	ST1	
Project:	SLK	
Subject:	Hyginasation line 1 step 3	
Rev. 6		
Int.:MDC	QC:CM	APP.:Date: 15-10-2025
LUNDSBY RENEWABLE SOLUTIONS		
Lundsby Renewable Solutions A/S, Hjarbrækvej 65, 8831 Legstrup Tlf.: +45 96 49 43 00 info@lundsby.dk This drawing is subject to copyright and may not be reproduced without permission from Lundsby Renewable Solutions A/S		
Project nr.:1768 Drawing nr.: 9623		FORMAT: A1

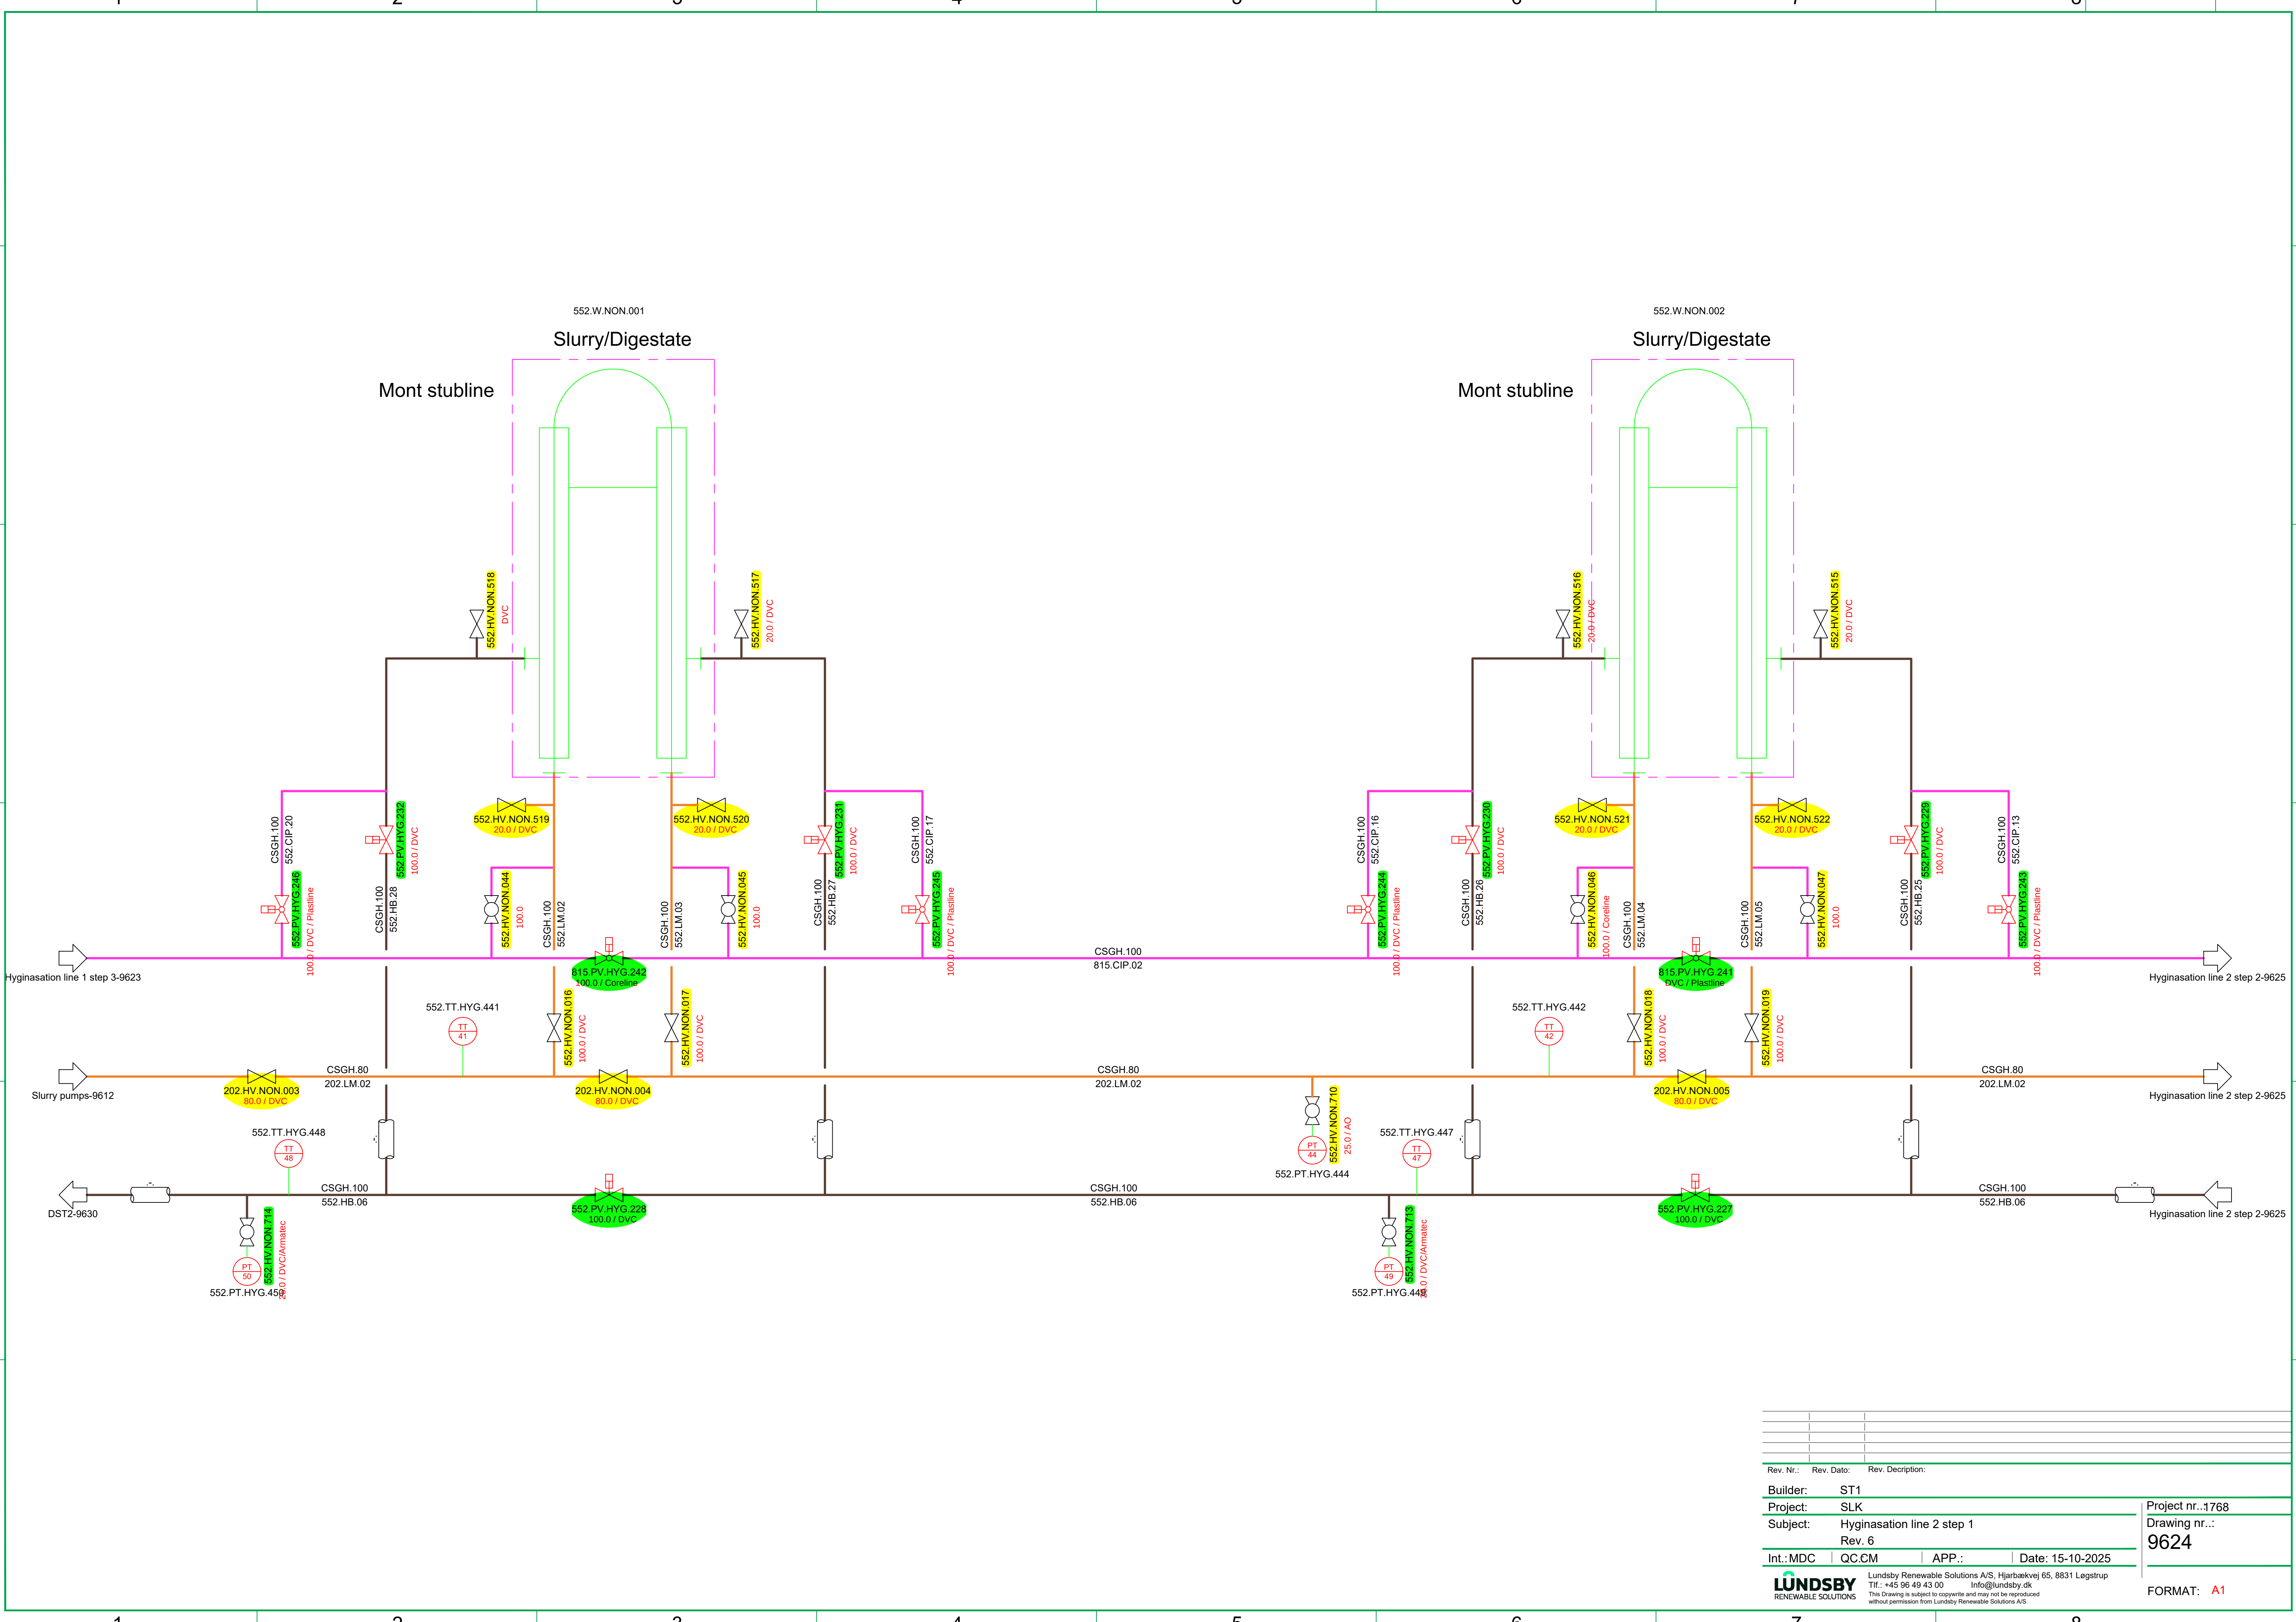

Rev. Nr.:	Rev. Dato:	Rev. Description:
Builder:	ST1	
Project:	SLK	
Subject:	Hyginasation line 2 step 1	
Rev. 6		
Int.:MDC	QC:CM	APP.:
Date:	15-10-2025	
LUNDSBY RENEWABLE SOLUTIONS		
Lundsby Renewable Solutions A/S, Hjarbrækvej 65, 8831 Løgstrup Tlf.: +45 96 49 43 00 info@lundsby.dk This Drawing is subject to copyright and may not be reproduced without permission from Lundsby Renewable Solutions A/S		
Project nr.:1768 Drawing nr.: 9624		FORMAT: A1

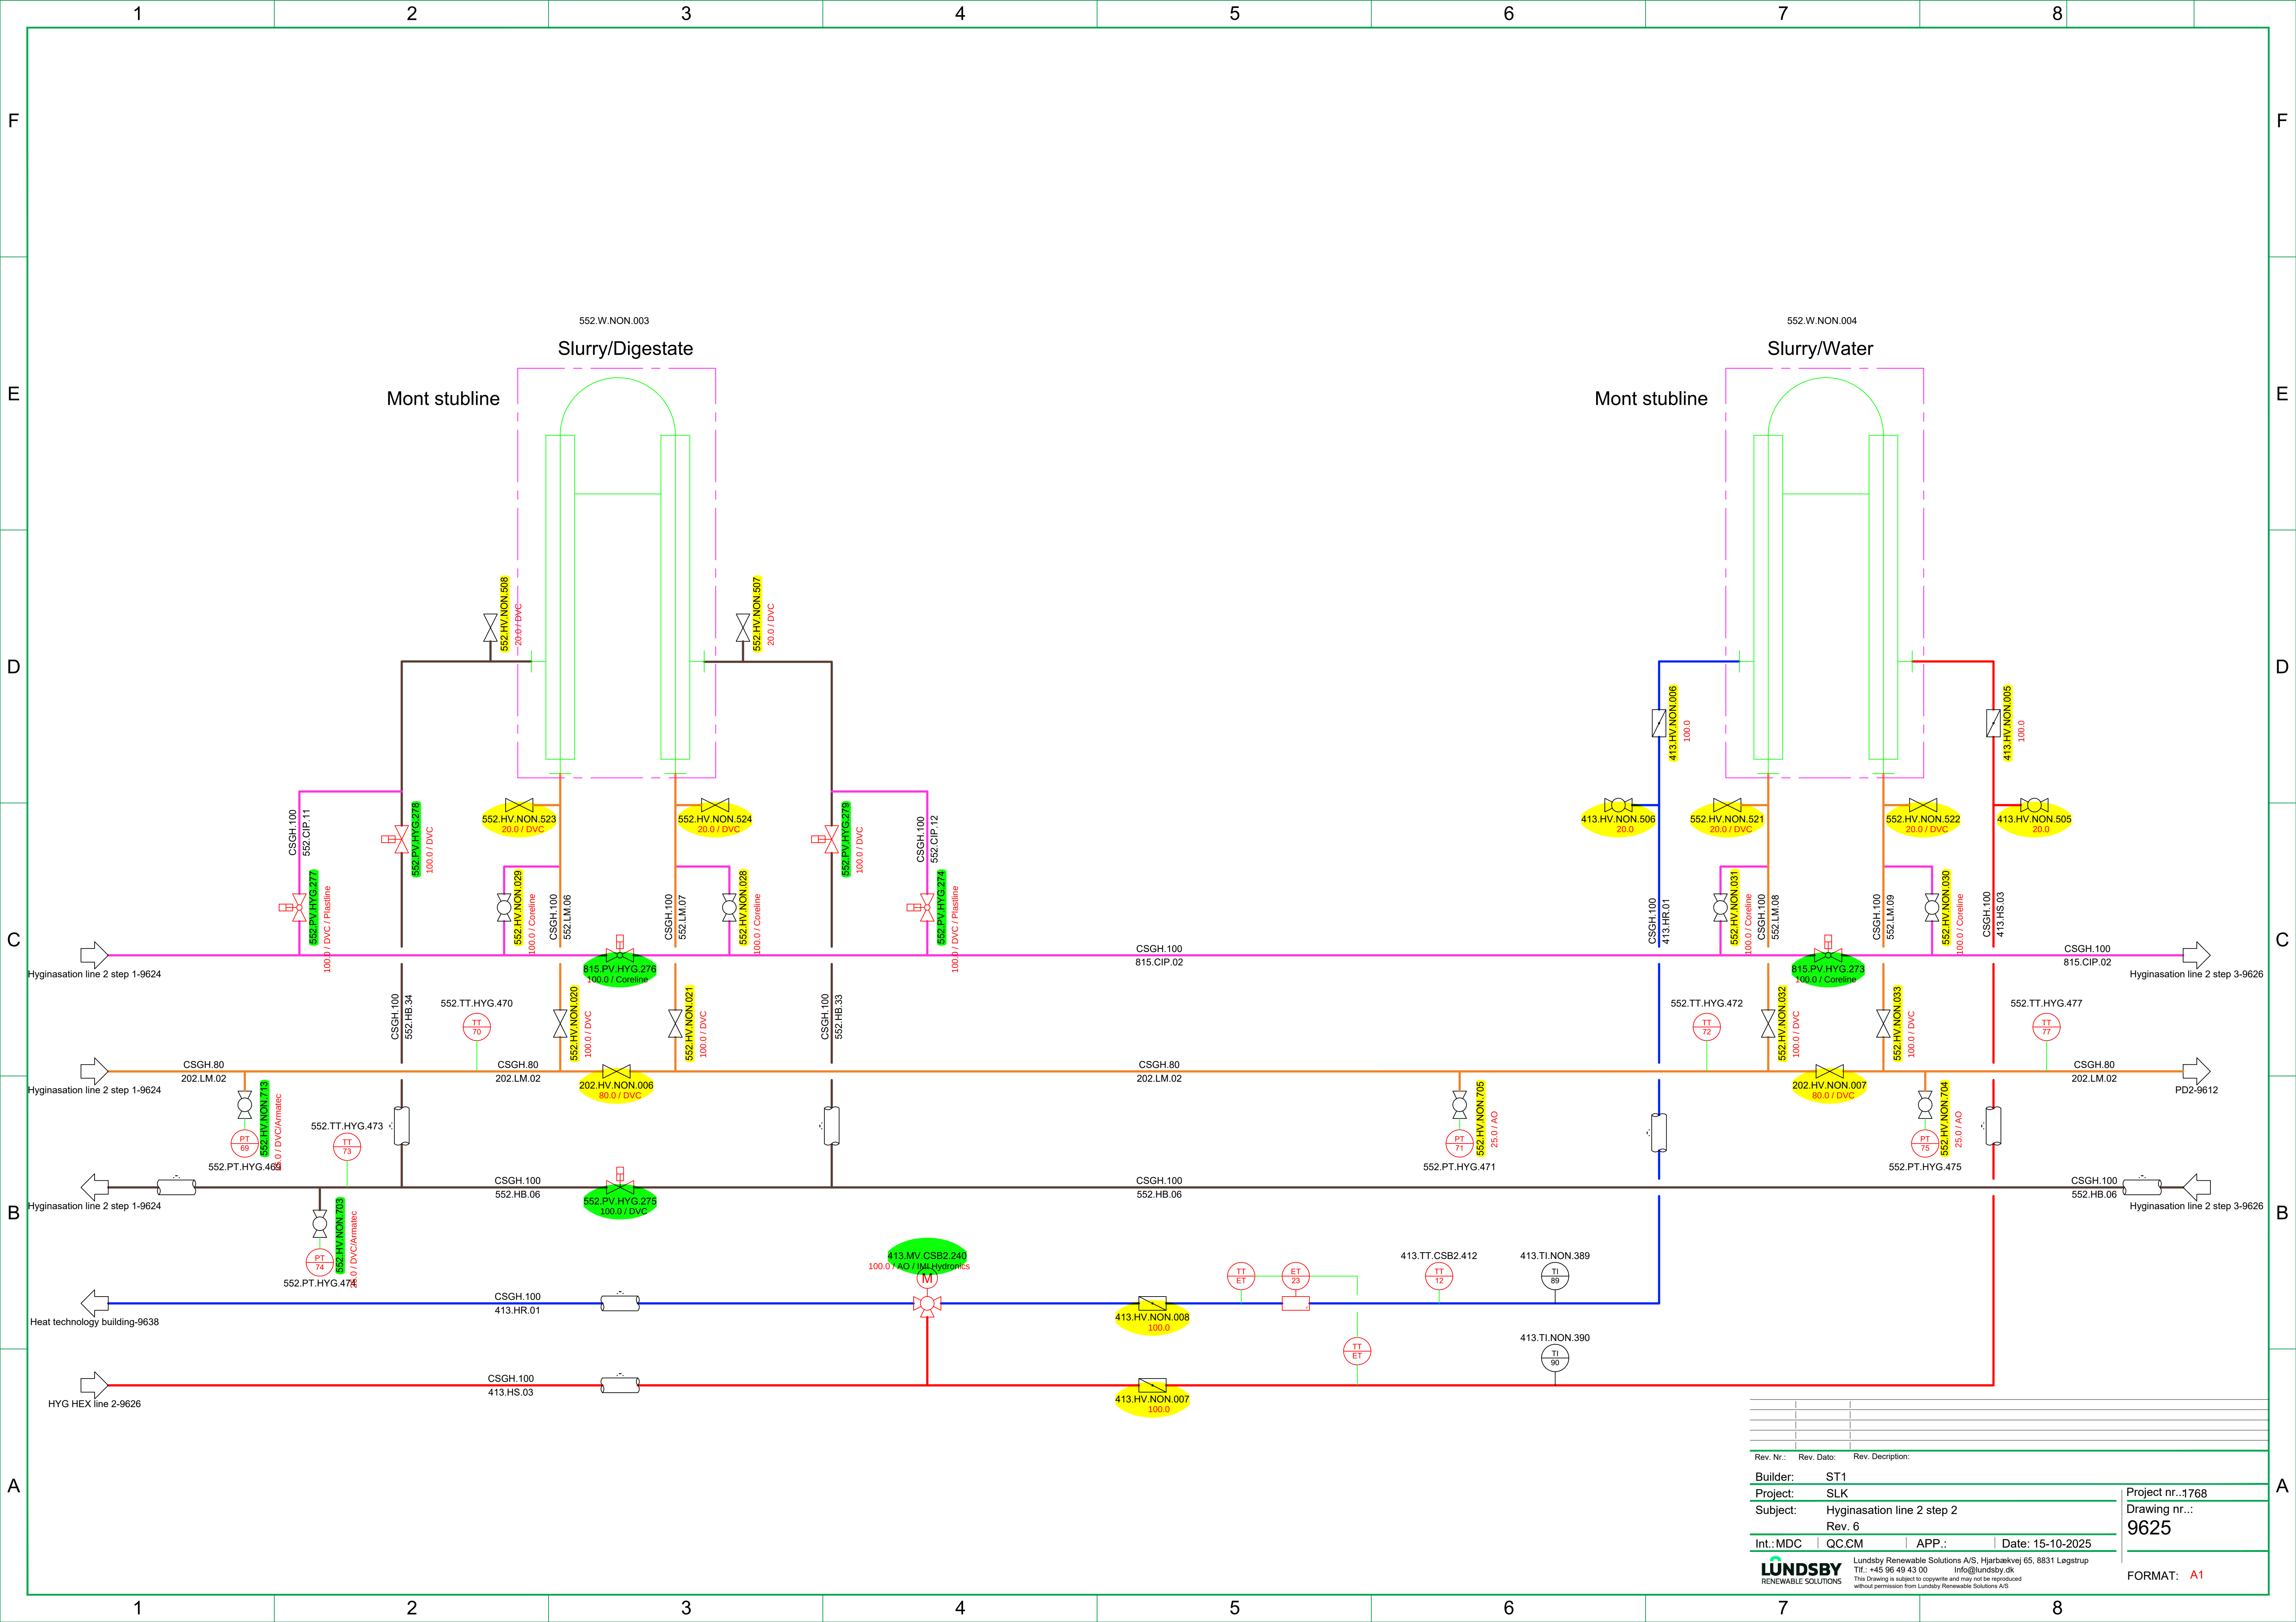


Rev. Nr.:	Rev. Dato:	Rev. Description:
Builder:	ST1	
Project:	SLK	
Subject:	Hyginasation line 2 step 2	
	Rev. 6	
Int.:MDC	QC:CM	APP.:
		Date: 15-10-2025

LUNDSBY
RENEWABLE SOLUTIONS


Lundsby Renewable Solutions A/S, Hjarbrækvej 65, 8831 Legstrup
Tlf.: +45 96 49 43 00 Info@lundsby.dk
This drawing is subject to copyright and may not be reproduced without permission from Lundsby Renewable Solutions A/S

Project nr.:1768
Drawing nr.:
9625

FORMAT: **A1**

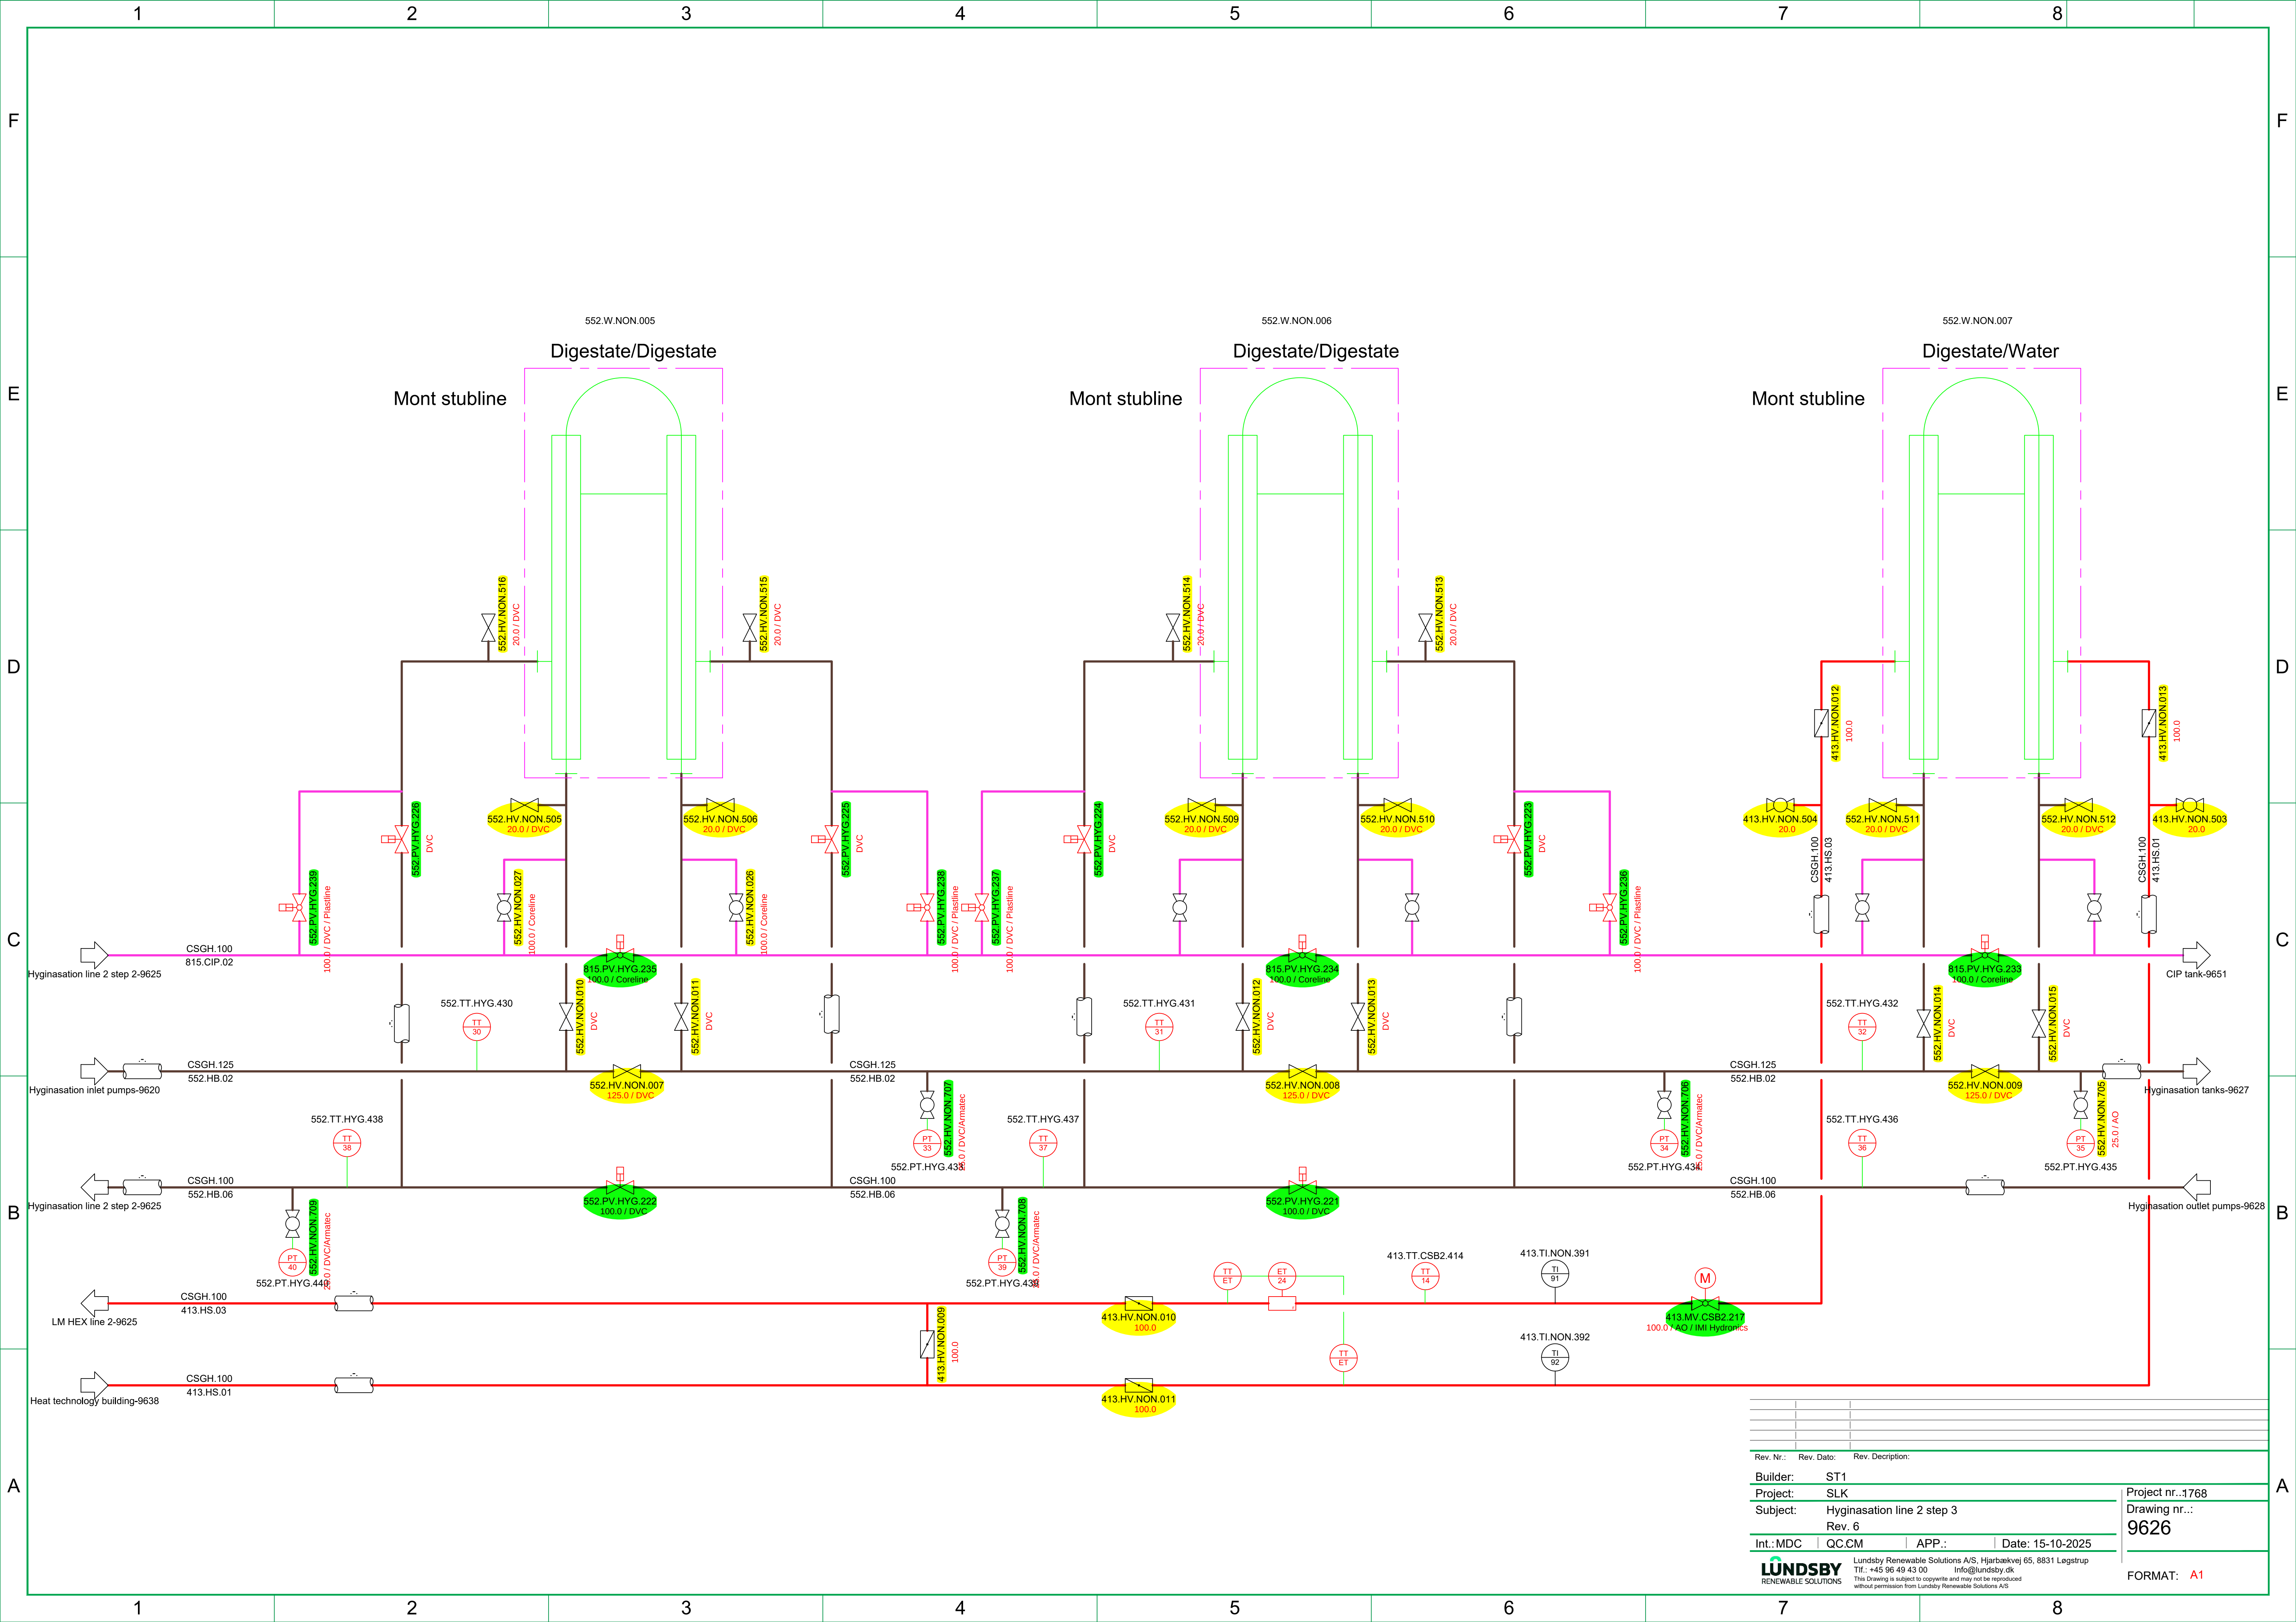


Rev. Nr.:	Rev. Dato:	Rev. Description:
Builder:	ST1	
Project:	SLK	
Subject:	Hyginasation line 2 step 3	
Rev. 6		
Int.:MDC	QC:CM	APP.: Date: 15-10-2025
LUNDSBY RENEWABLE SOLUTIONS		
Lundsby Renewable Solutions A/S, Hjarbrækvej 65, 8831 Lægstrup Tlf.: +45 96 49 43 00 Info@lundsby.dk This drawing is subject to copyright and may not be reproduced without permission from Lundsby Renewable Solutions A/S		
Project nr.:1768 Drawing nr.: 9626		FORMAT: A1

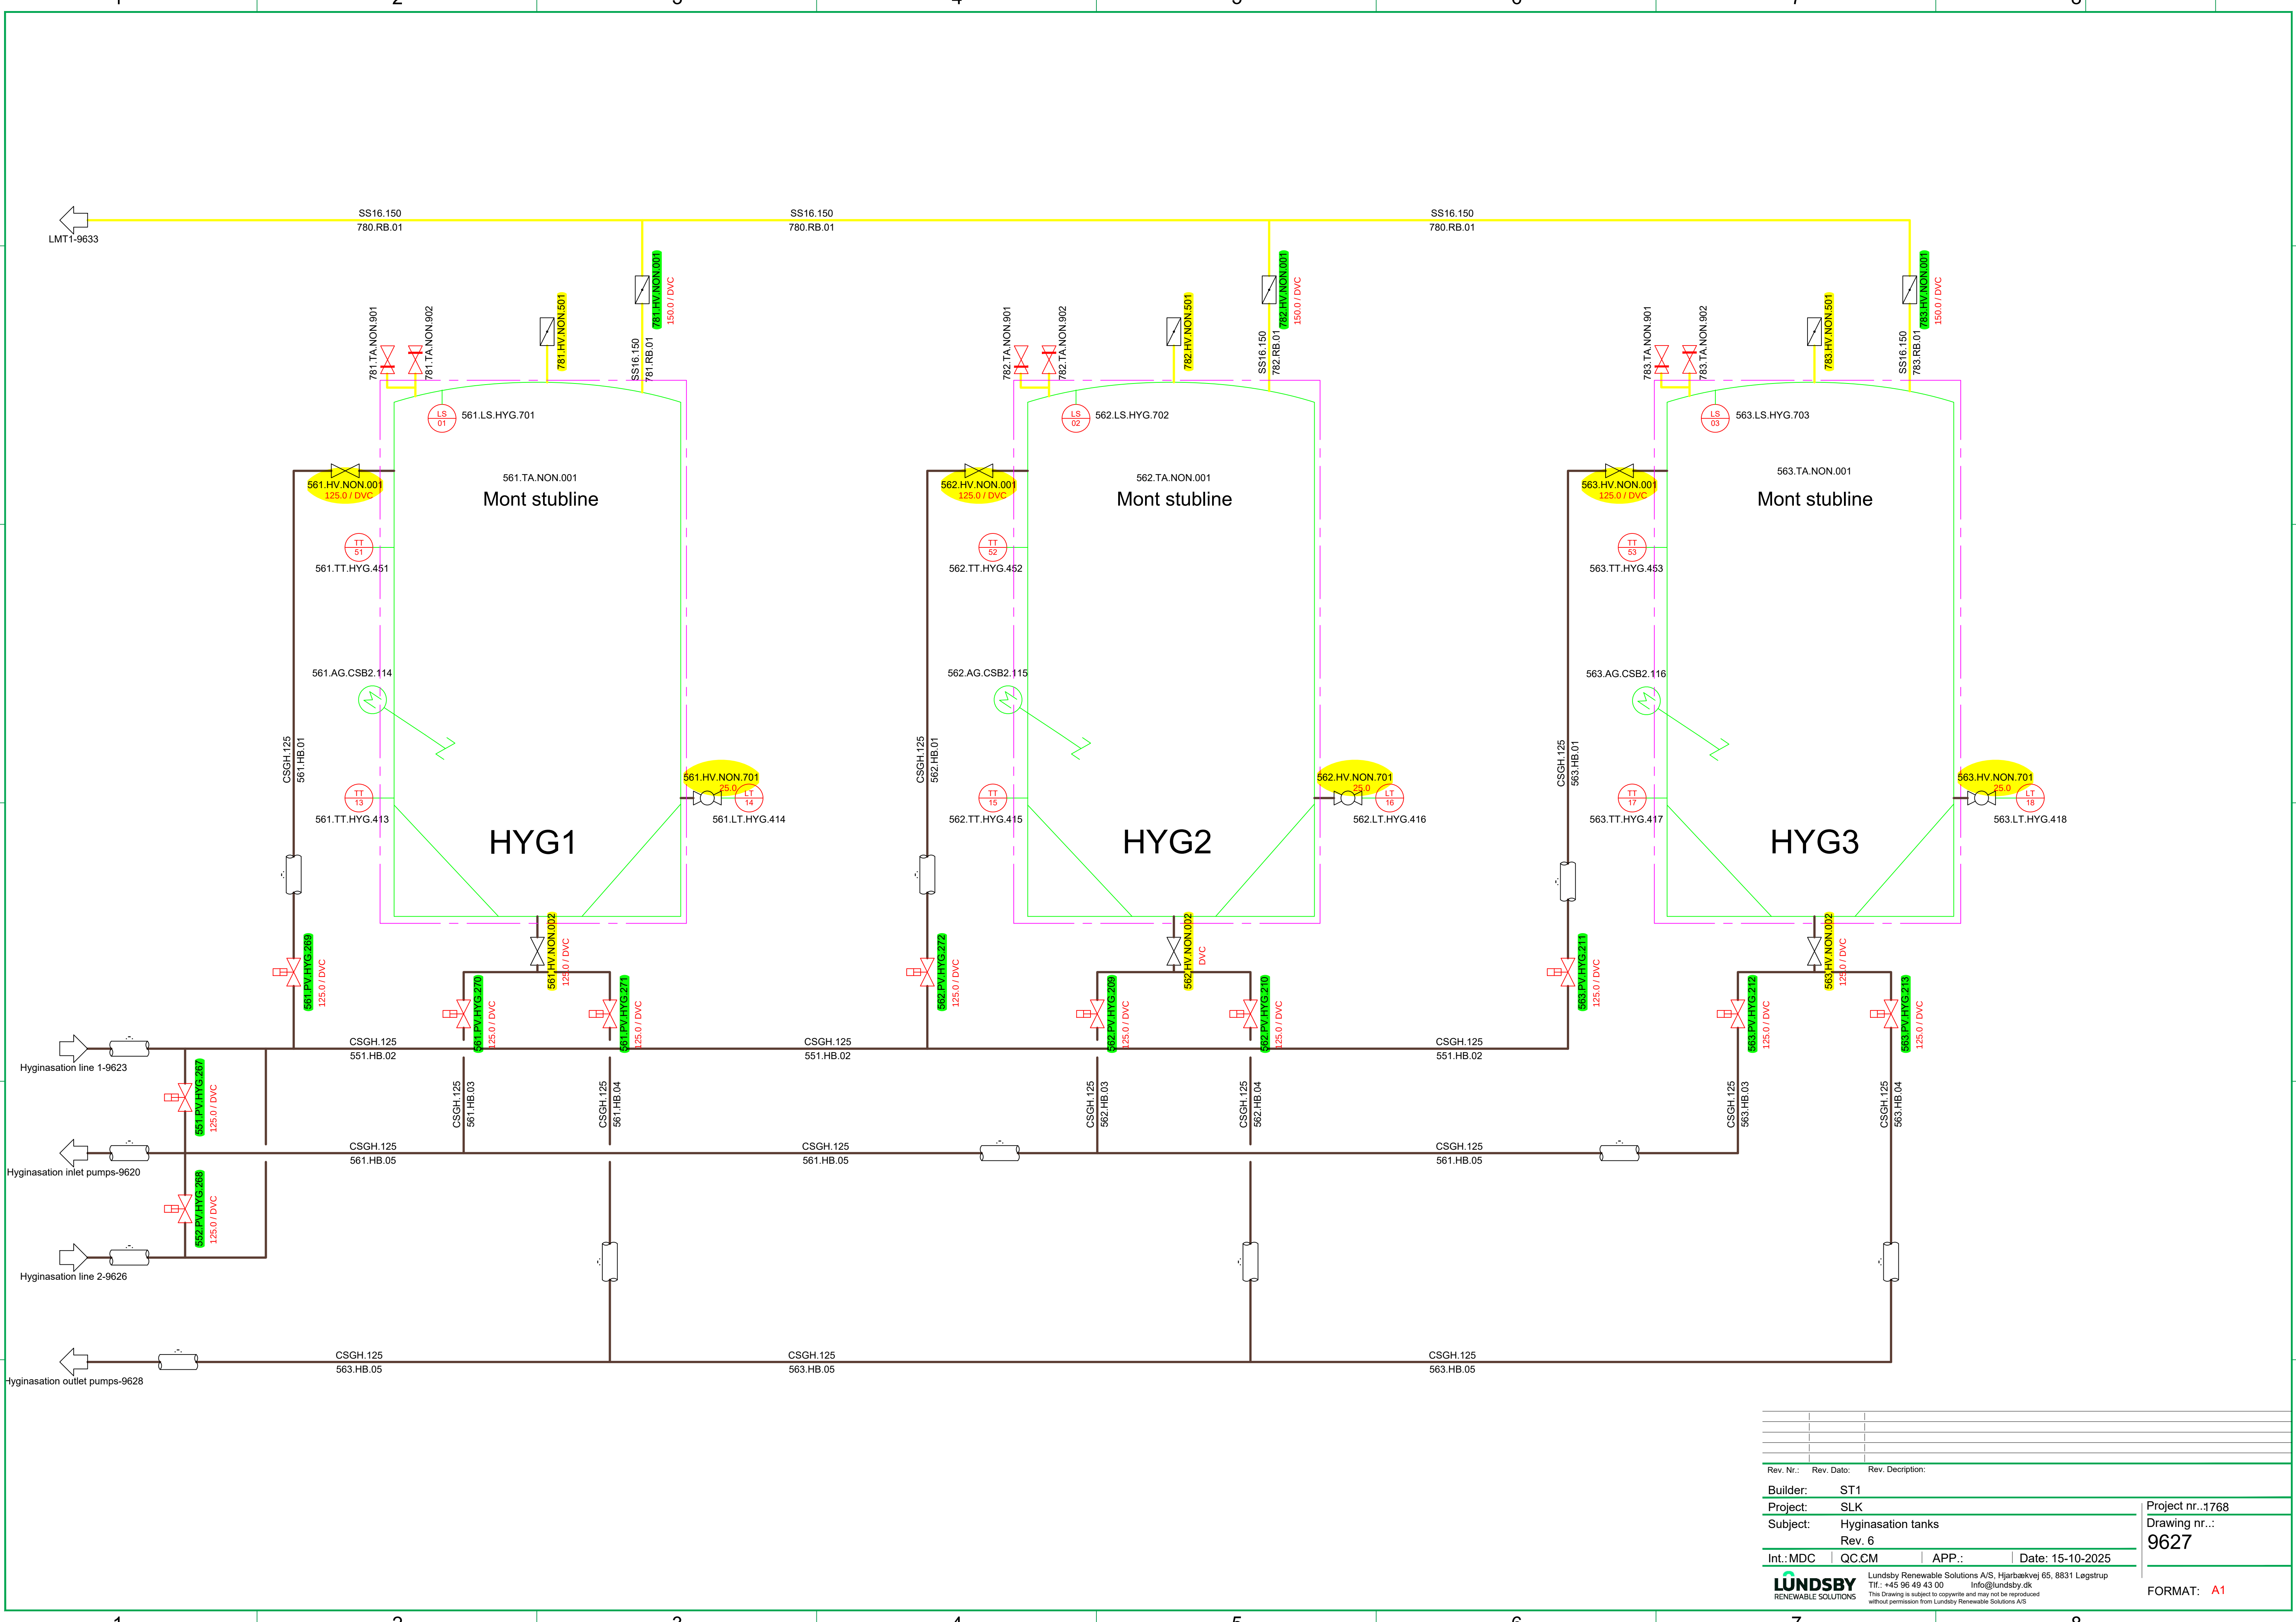


Rev. Nr.: Rev. Dato: Rev. Description:	
Builder: ST1	
Project: SLK	
Subject: Hyginasation tanks	
Rev. 6	
Int.: MDC	QC.CM
APP.:	Date: 15-10-2025
LUNDSBY RENEWABLE SOLUTIONS	
Lundsby Renewable Solutions A/S, Hjarbækvej 65, 8831 Løgstrup Tlf.: +45 96 49 43 00 info@lundsby.dk This drawing is subject to copyright and may not be reproduced without permission from Lundsby Renewable Solutions A/S	
Project nr.: 1768 Drawing nr.: 9627	
FORMAT: A1	

Tech Building


Outlet pumps

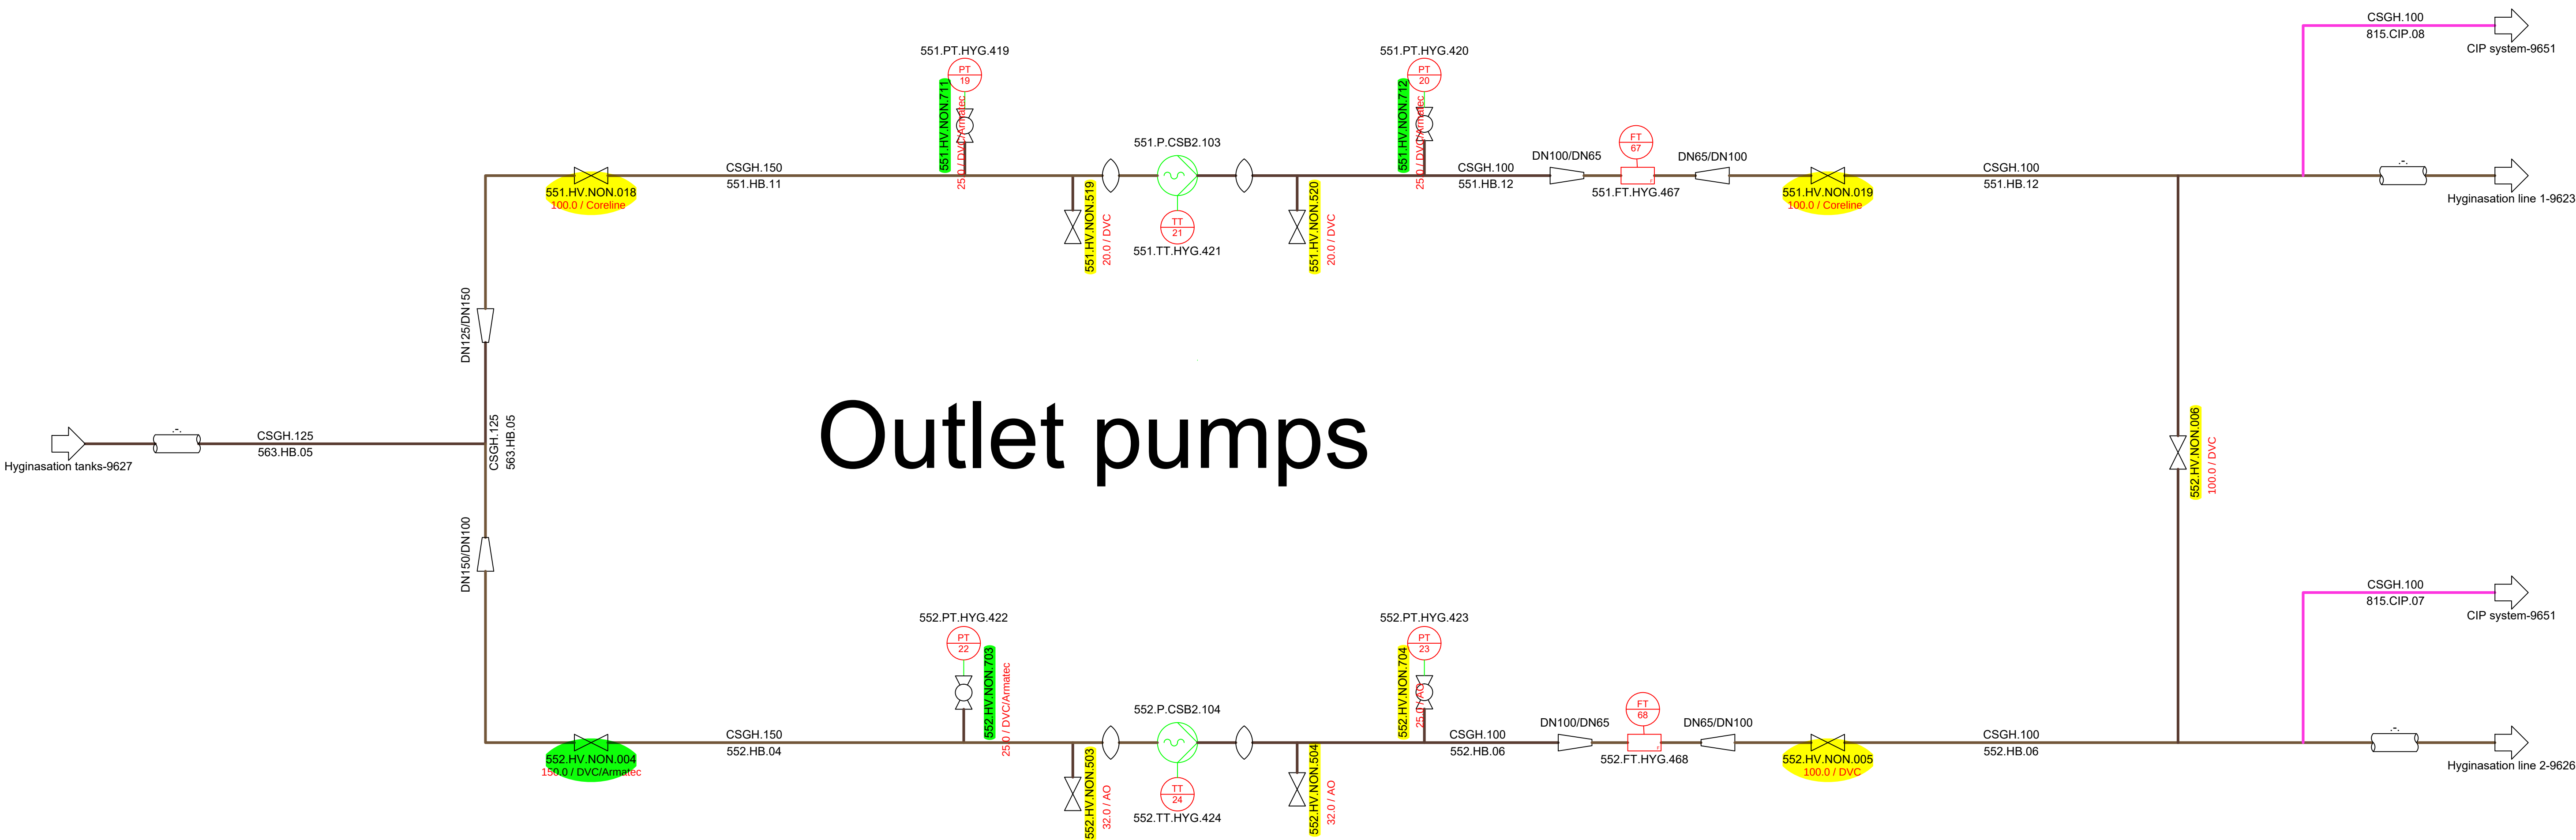


Rev. Nr.:	Rev. Dato:	Rev. Description:	Project nr.:1768
Builder:	ST1		Drawing nr.:9628
Project:	SLK		
Subject:	Hyginasation outlet pumps		
Rev. 6			
Int.:MDC	QC:CM	APP.:	Date: 15-10-2025
LUNDSBY RENEWABLE SOLUTIONS			FORMAT: A1

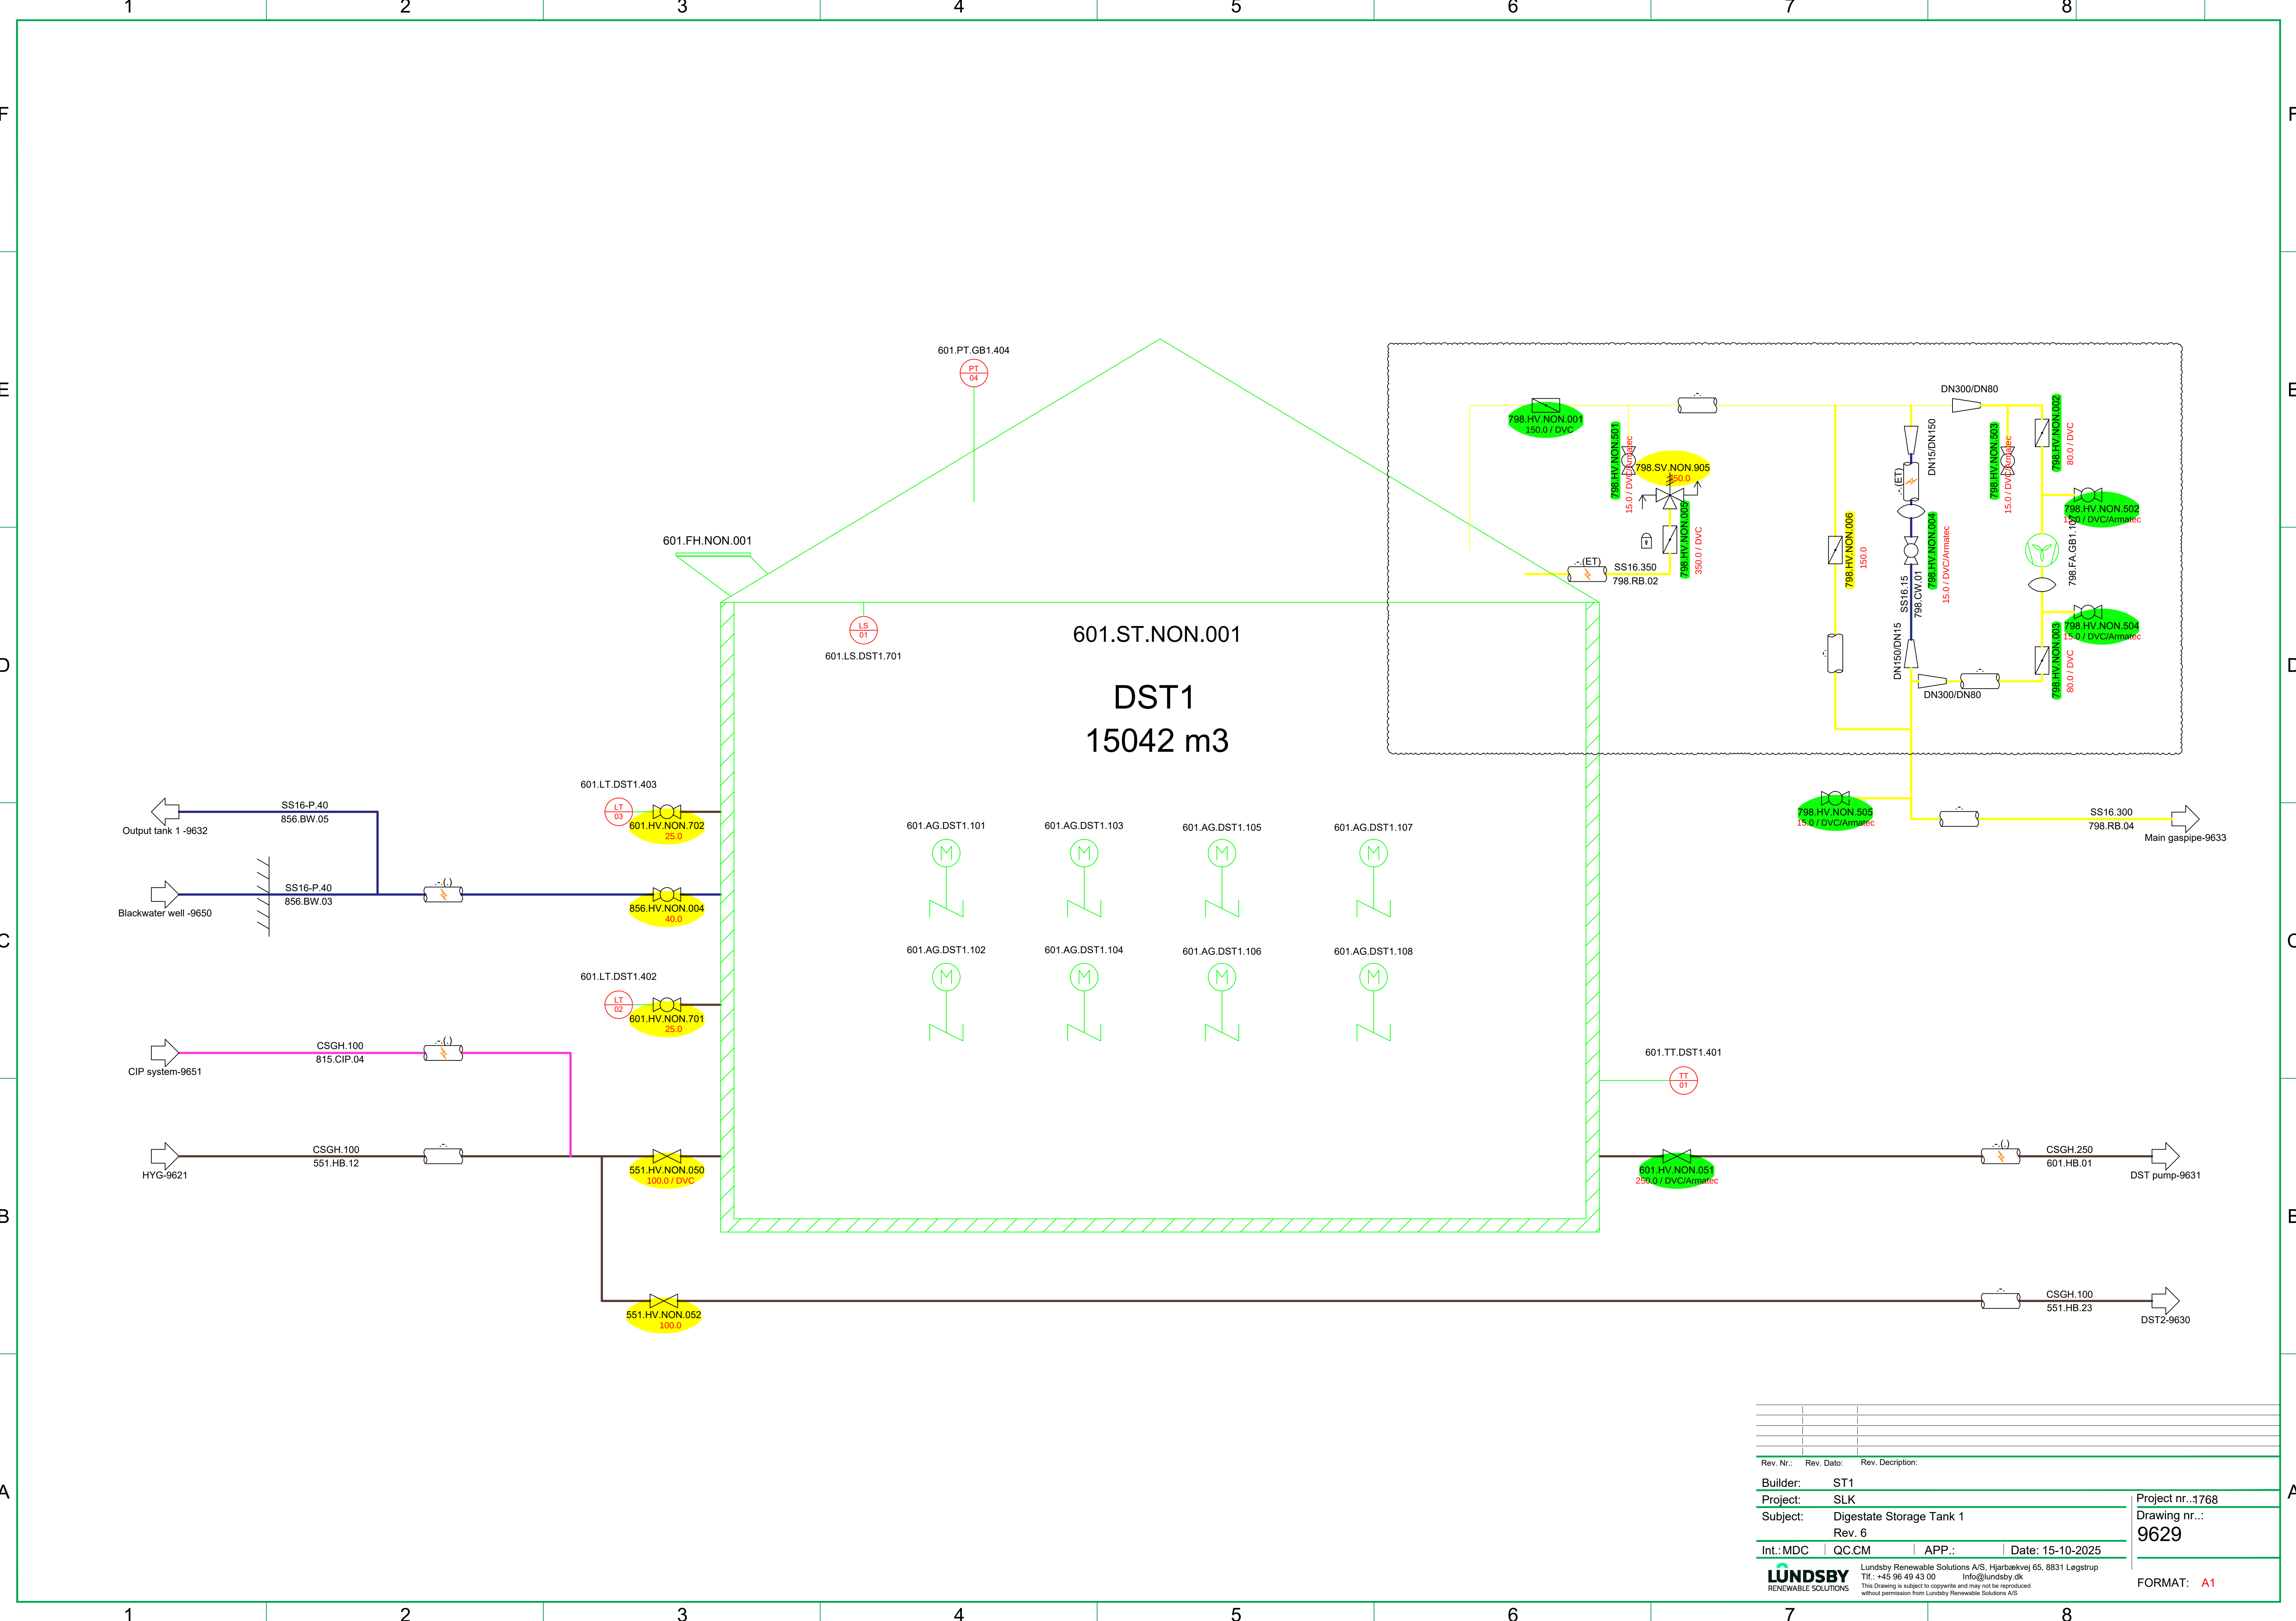


Rev. Nr.:	Rev. Dato:	Rev. Description:			
Builder:	ST1				
Project:	SLK				
Subject:	Digestate Storage Tank 1				
	Rev. 6				
Int.:MDC	QC:CM	APP.:	Date: 15-10-2025		
LUNDSBY RENEWABLE SOLUTIONS Lundsgby Renewable Solutions A/S, Hjarbrækvej 65, 8831 Løgstrup Tlf.: +45 96 49 43 00 Info@lundsgby.dk This Drawing is subject to copyright and may not be reproduced without permission from Lundsgby Renewable Solutions A/S					Project nr.:1768 Drawing nr.: 9629
FORMAT: A1					

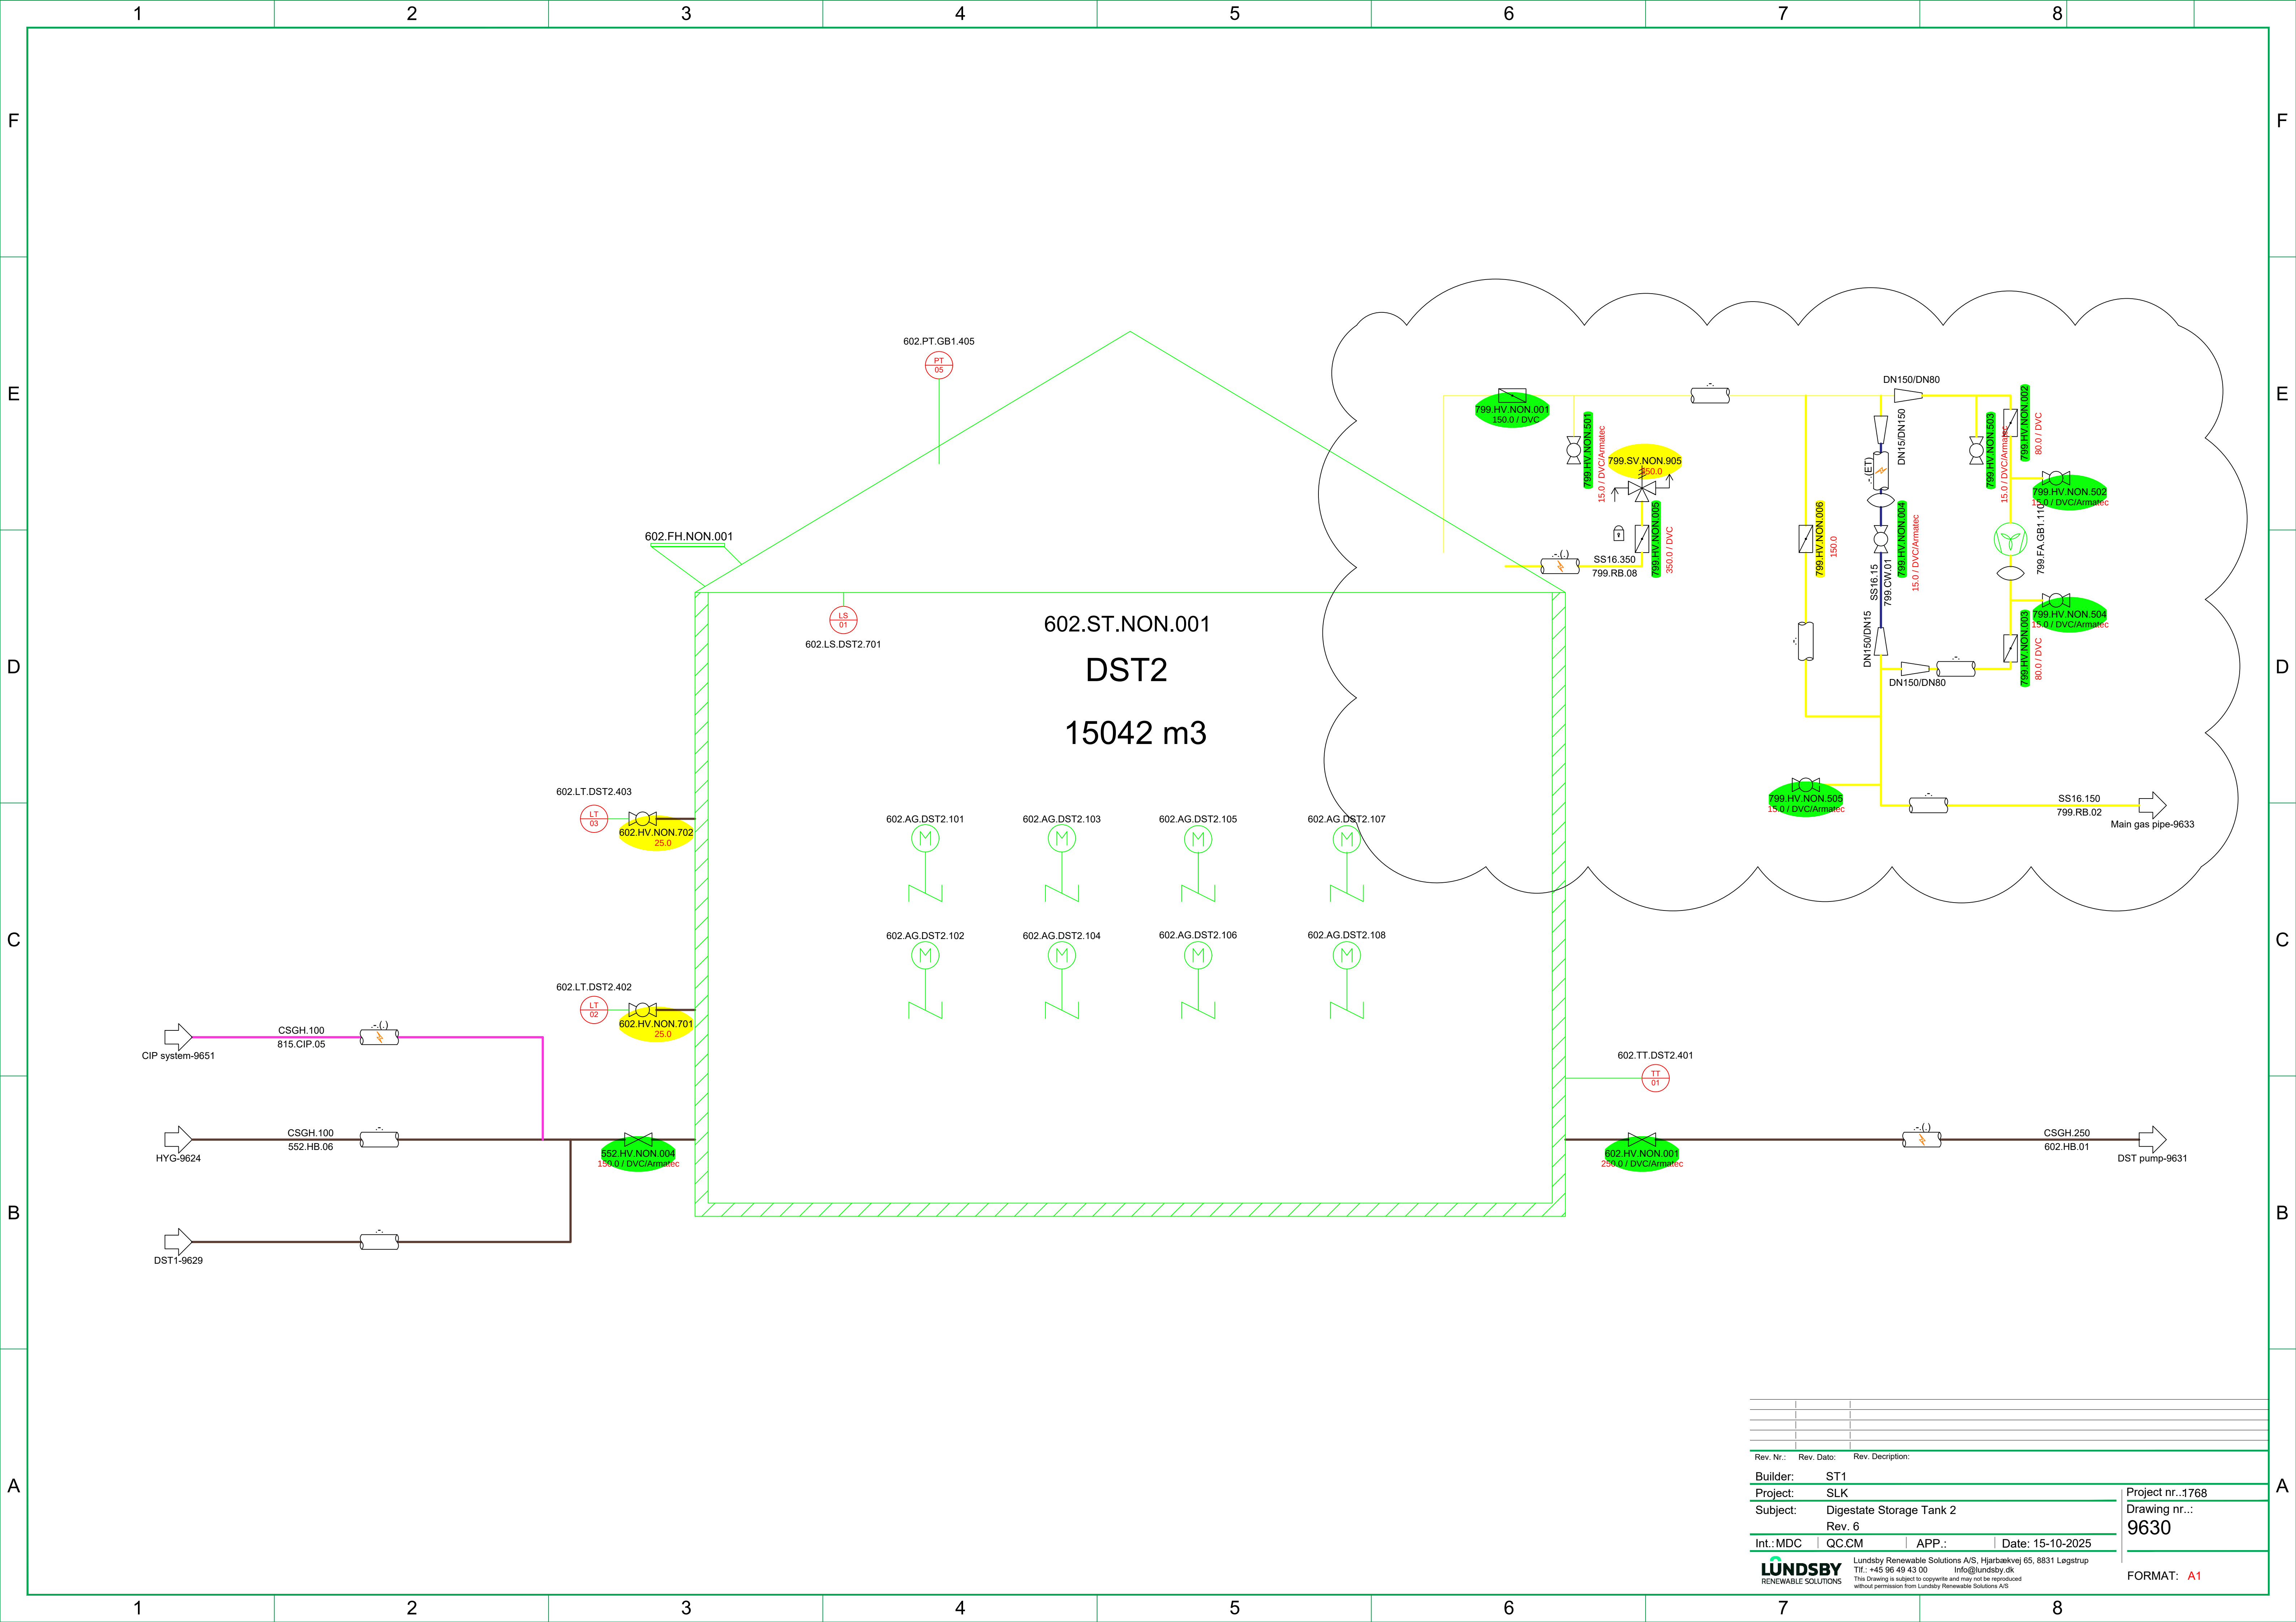


Rev. Nr.:	Rev. Dato:	Rev. Description:	
Builder:	ST1		
Project:	SLK		
Subject:	Digestate Storage Tank 2		
	Rev. 6		
Int.:MDC	QC:CM	APP.:	Date: 15-10-2025
LUNDSBY RENEWABLE SOLUTIONS			Lundsby Renewable Solutions A/S, Hjarbækvej 65, 8831 Løgstrup Tlf.: +45 96 49 43 00 info@lundsby.dk This drawing is subject to copyright and may not be reproduced without permission from Lundsby Renewable Solutions A/S
Project nr.:1768 Drawing nr.: 9630			FORMAT: A1

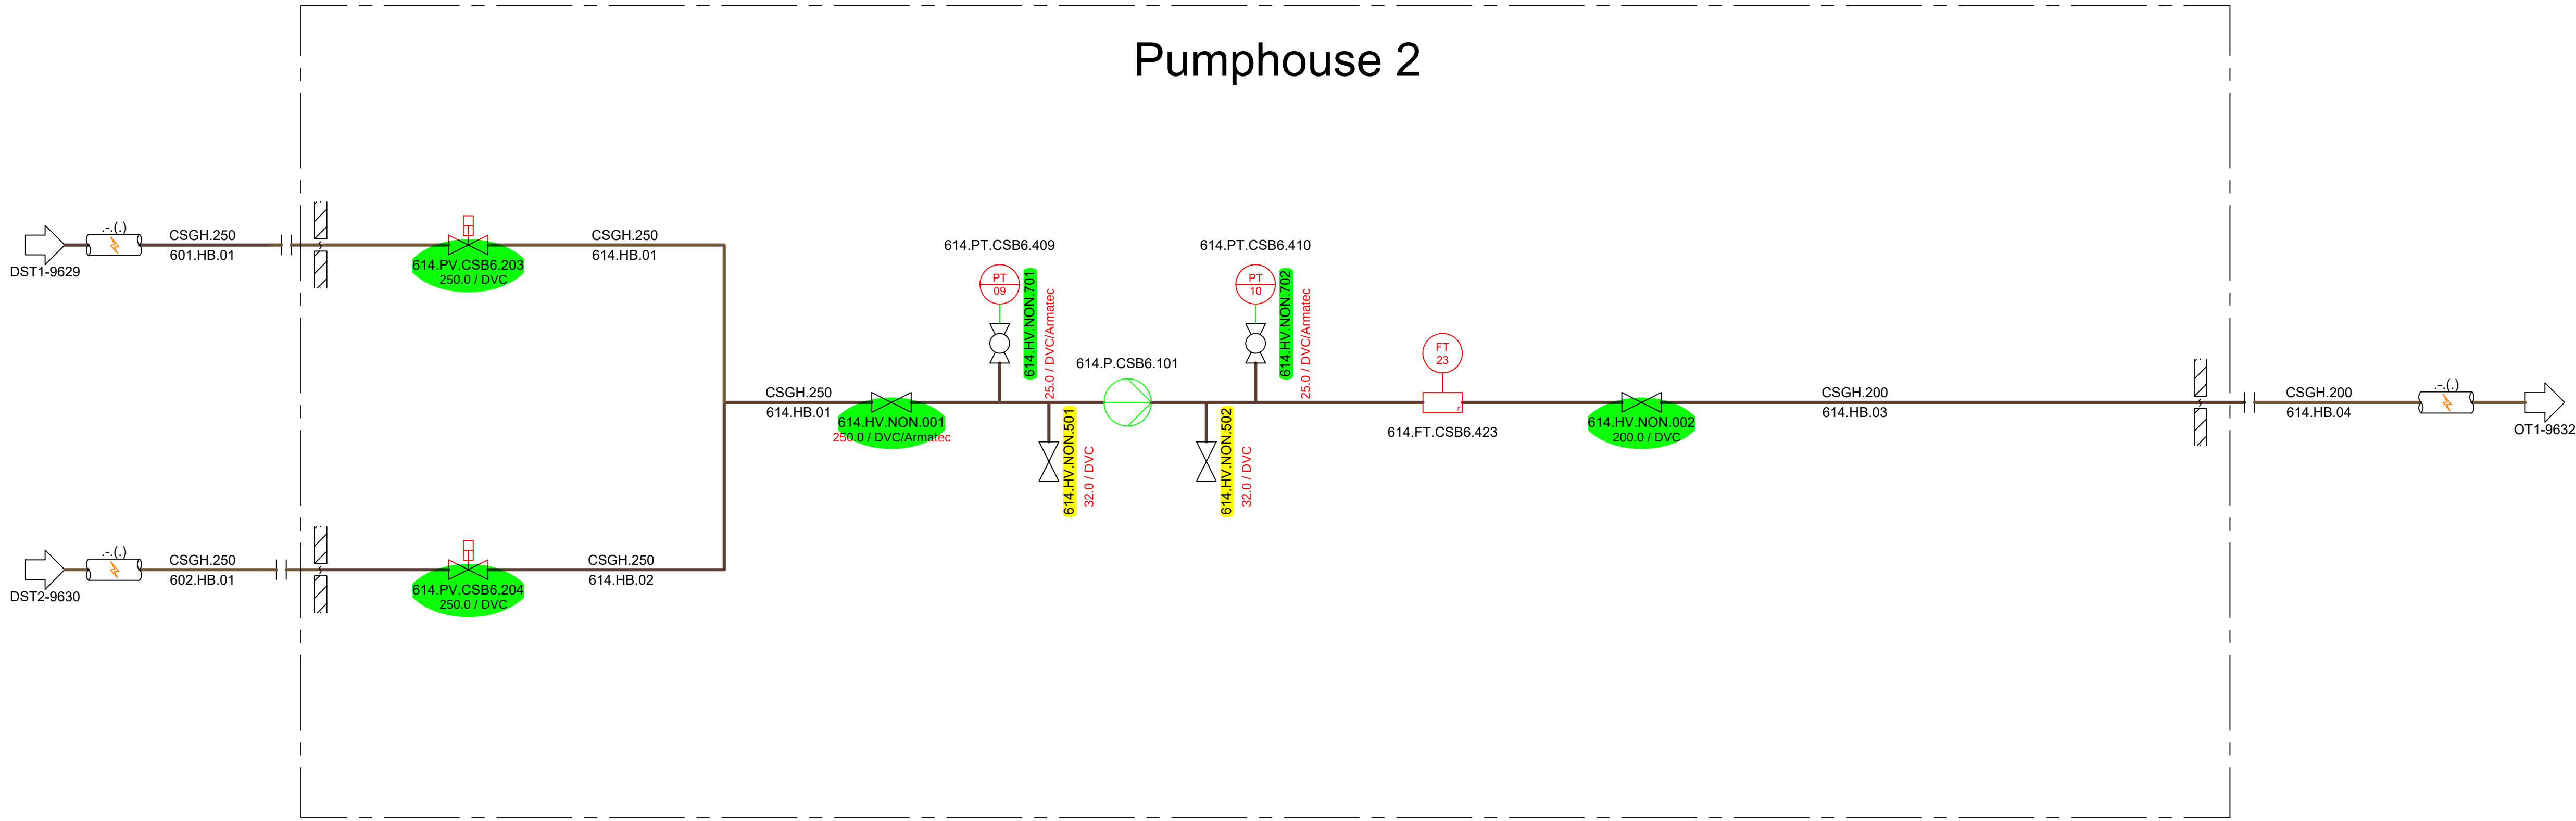


Rev. Nr.:	Rev. Dato:	Rev. Description:	Project nr...1768
Builder:	ST1		Drawing nr...:
Project:	SLK		9631
Subject:	DST pump		
	Rev. 6		
Int.:MDC	QC:CM	APP.:	Date: 15-10-2025
LUNDSBY RENEWABLE SOLUTIONS		Lundsby Renewable Solutions A/S, Hjarbækvej 65, 8831 Løgstrup Tlf.: +45 96 49 43 00 Info@lundsby.dk This Drawing is subject to copyright and may not be reproduced without permission from Lundsby Renewable Solutions A/S	
		FORMAT: A1	

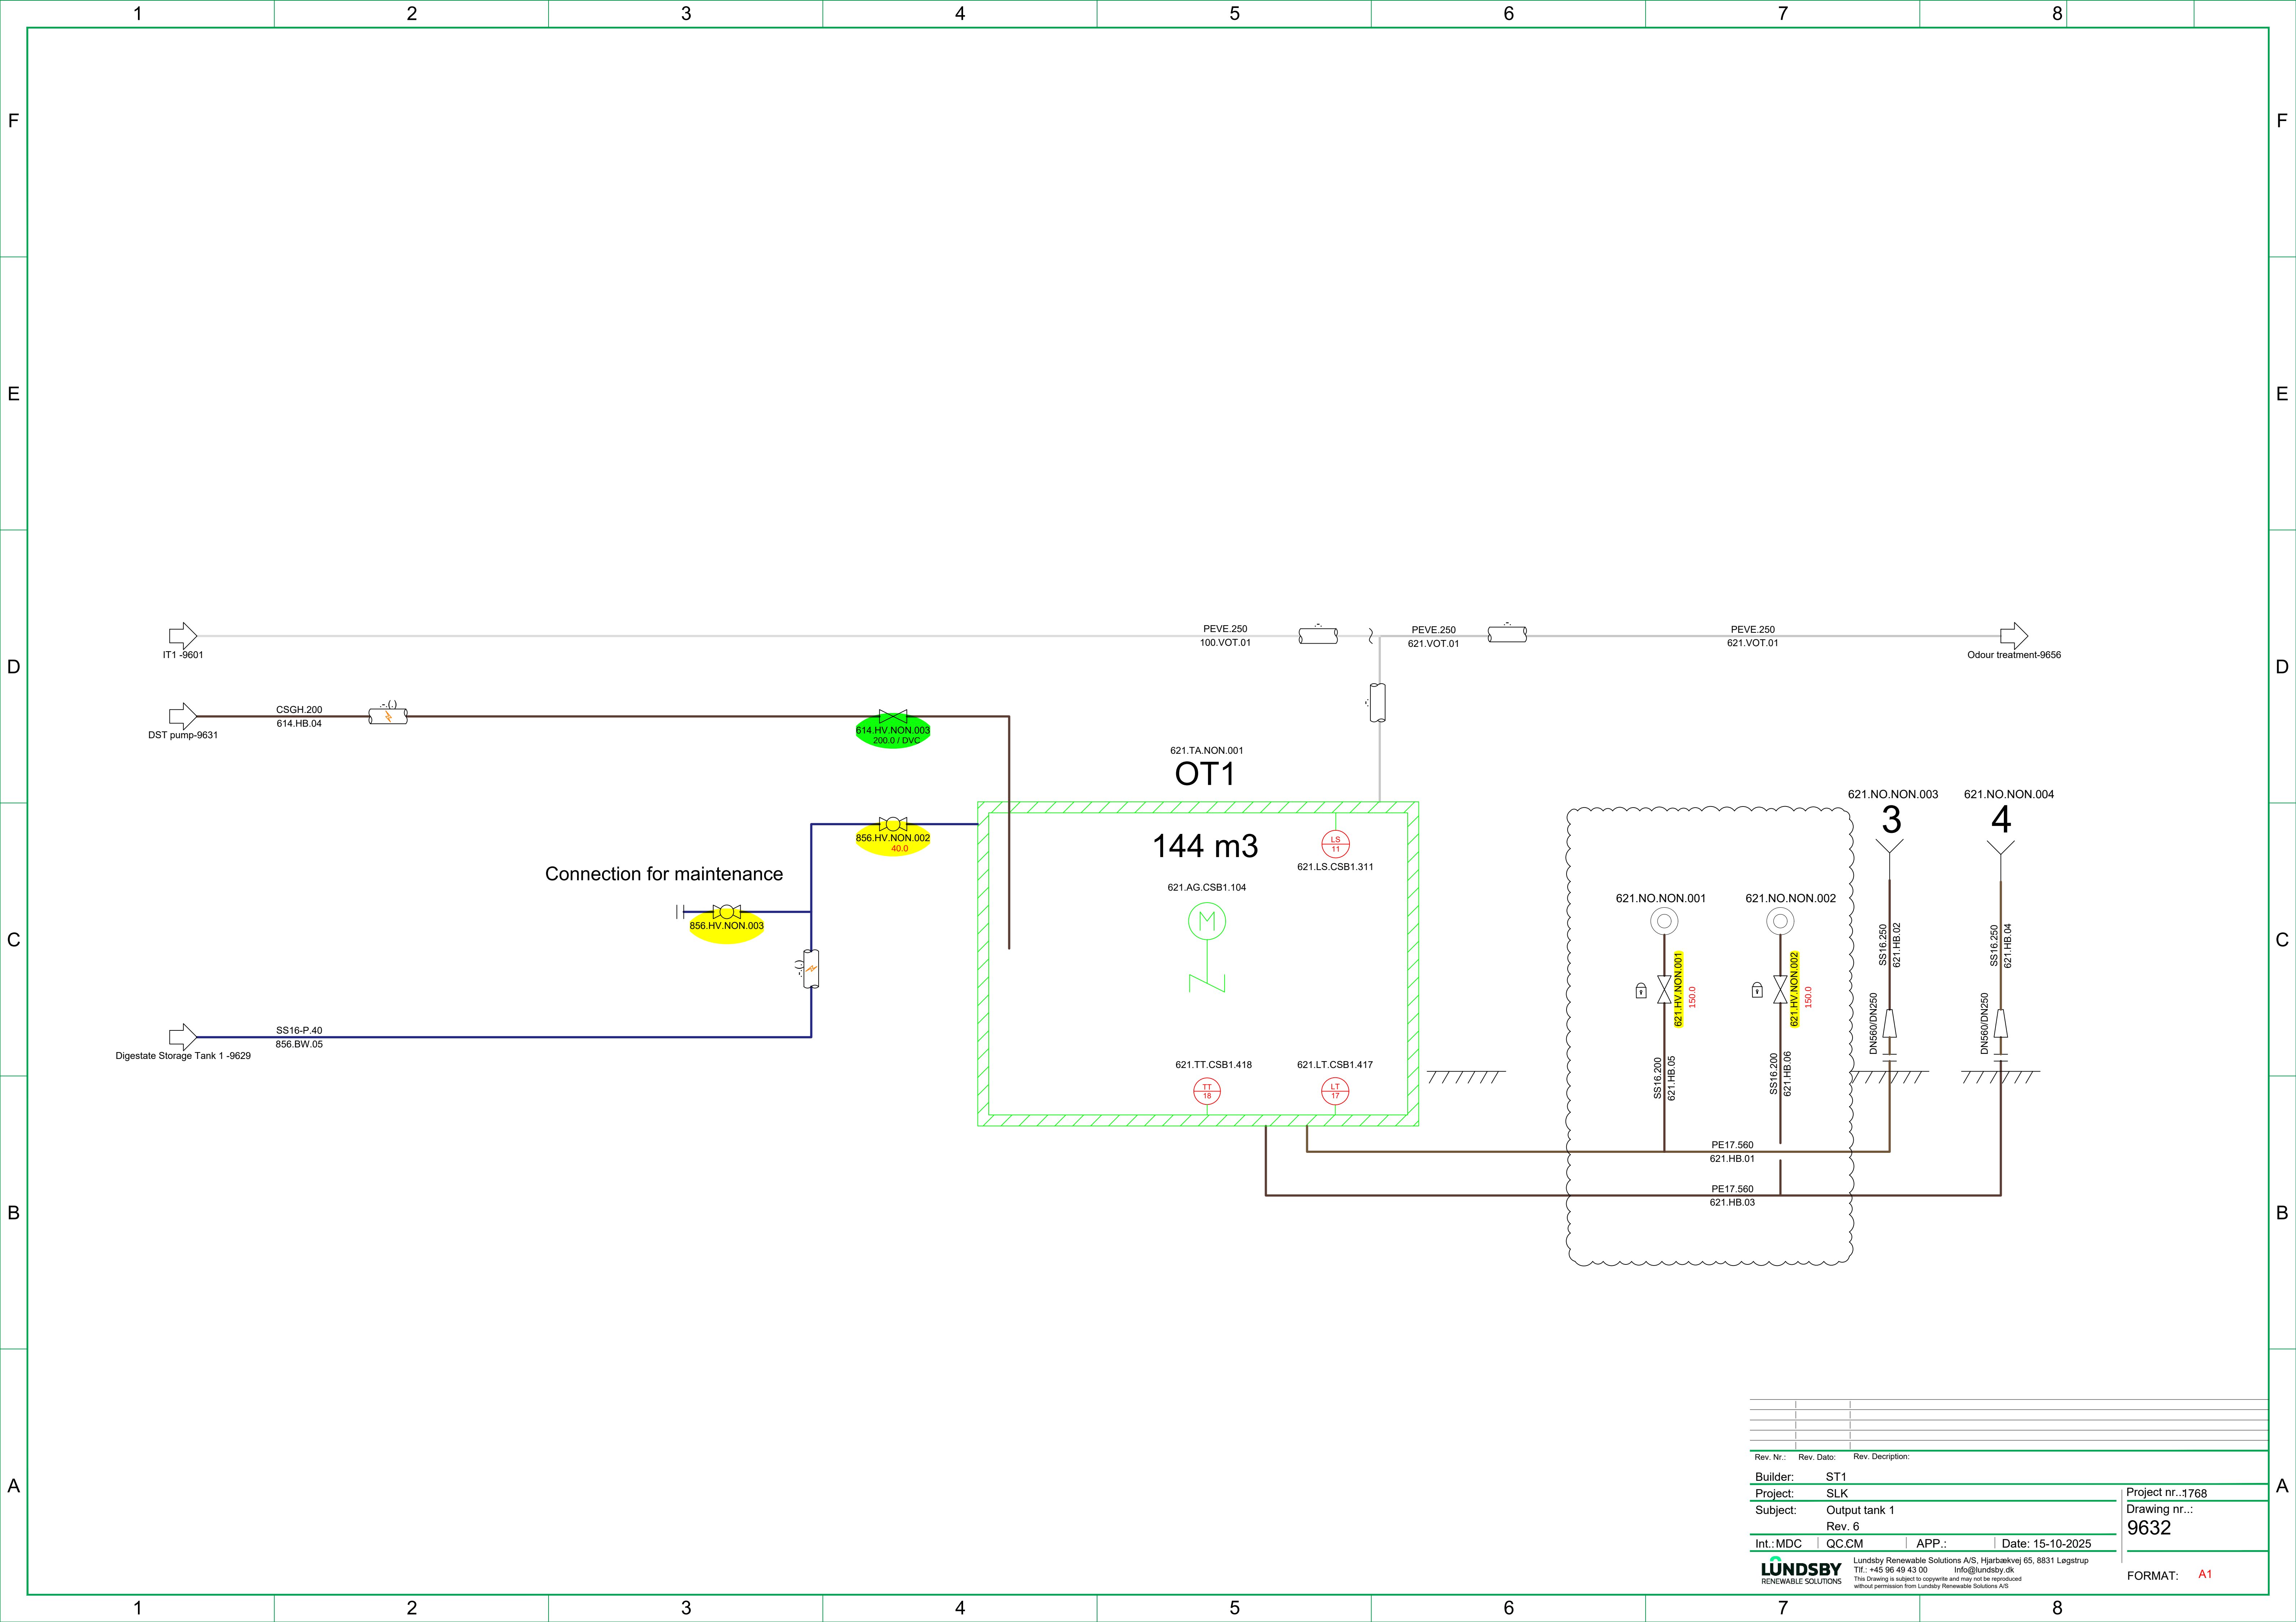

Rev. Nr.:	Rev. Dato:	Rev. Description:
Builder:	ST1	
Project:	SLK	
Subject:	Output tank 1	
Rev. 6		
Int.:MDC	QC:CM	APP.:Date: 15-10-2025
LUNDSBY RENEWABLE SOLUTIONS		
Lundsgby Renewable Solutions A/S, Hjarbrækvej 65, 8831 Lægstrup Tlf.: +45 96 49 43 00 Info@lundsgby.dk This Drawing is subject to copyright and may not be reproduced without permission from Lundsgby Renewable Solutions A/S		
Project nr.:1768 Drawing nr.: 9632		FORMAT: A1

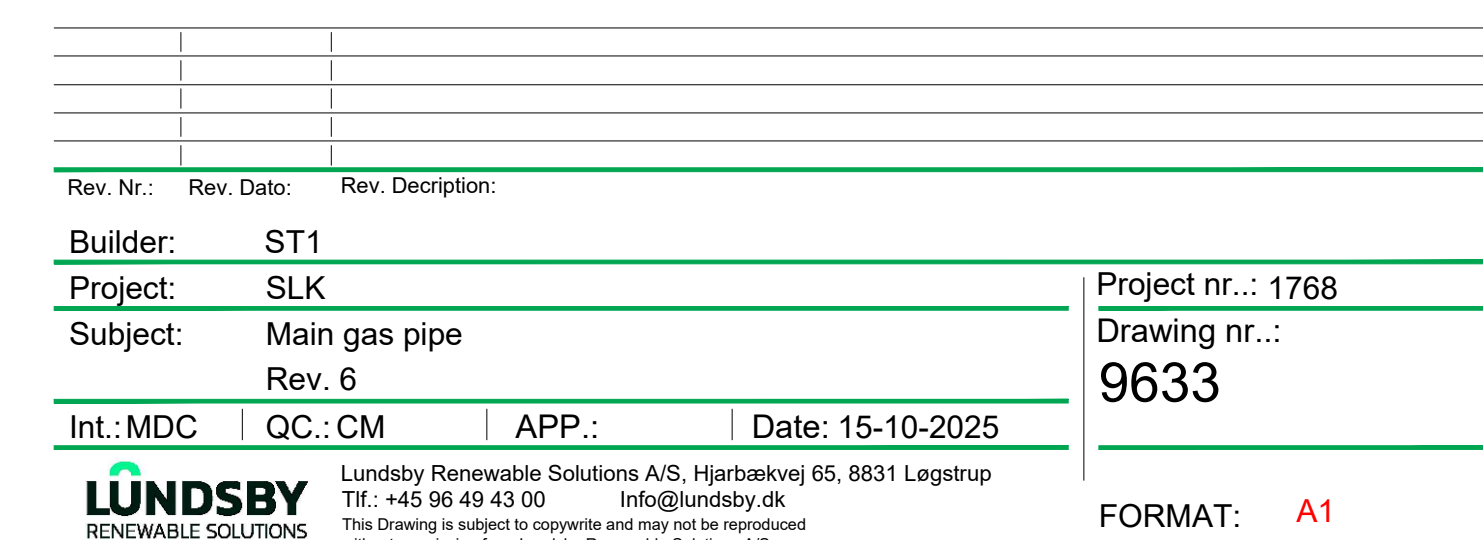

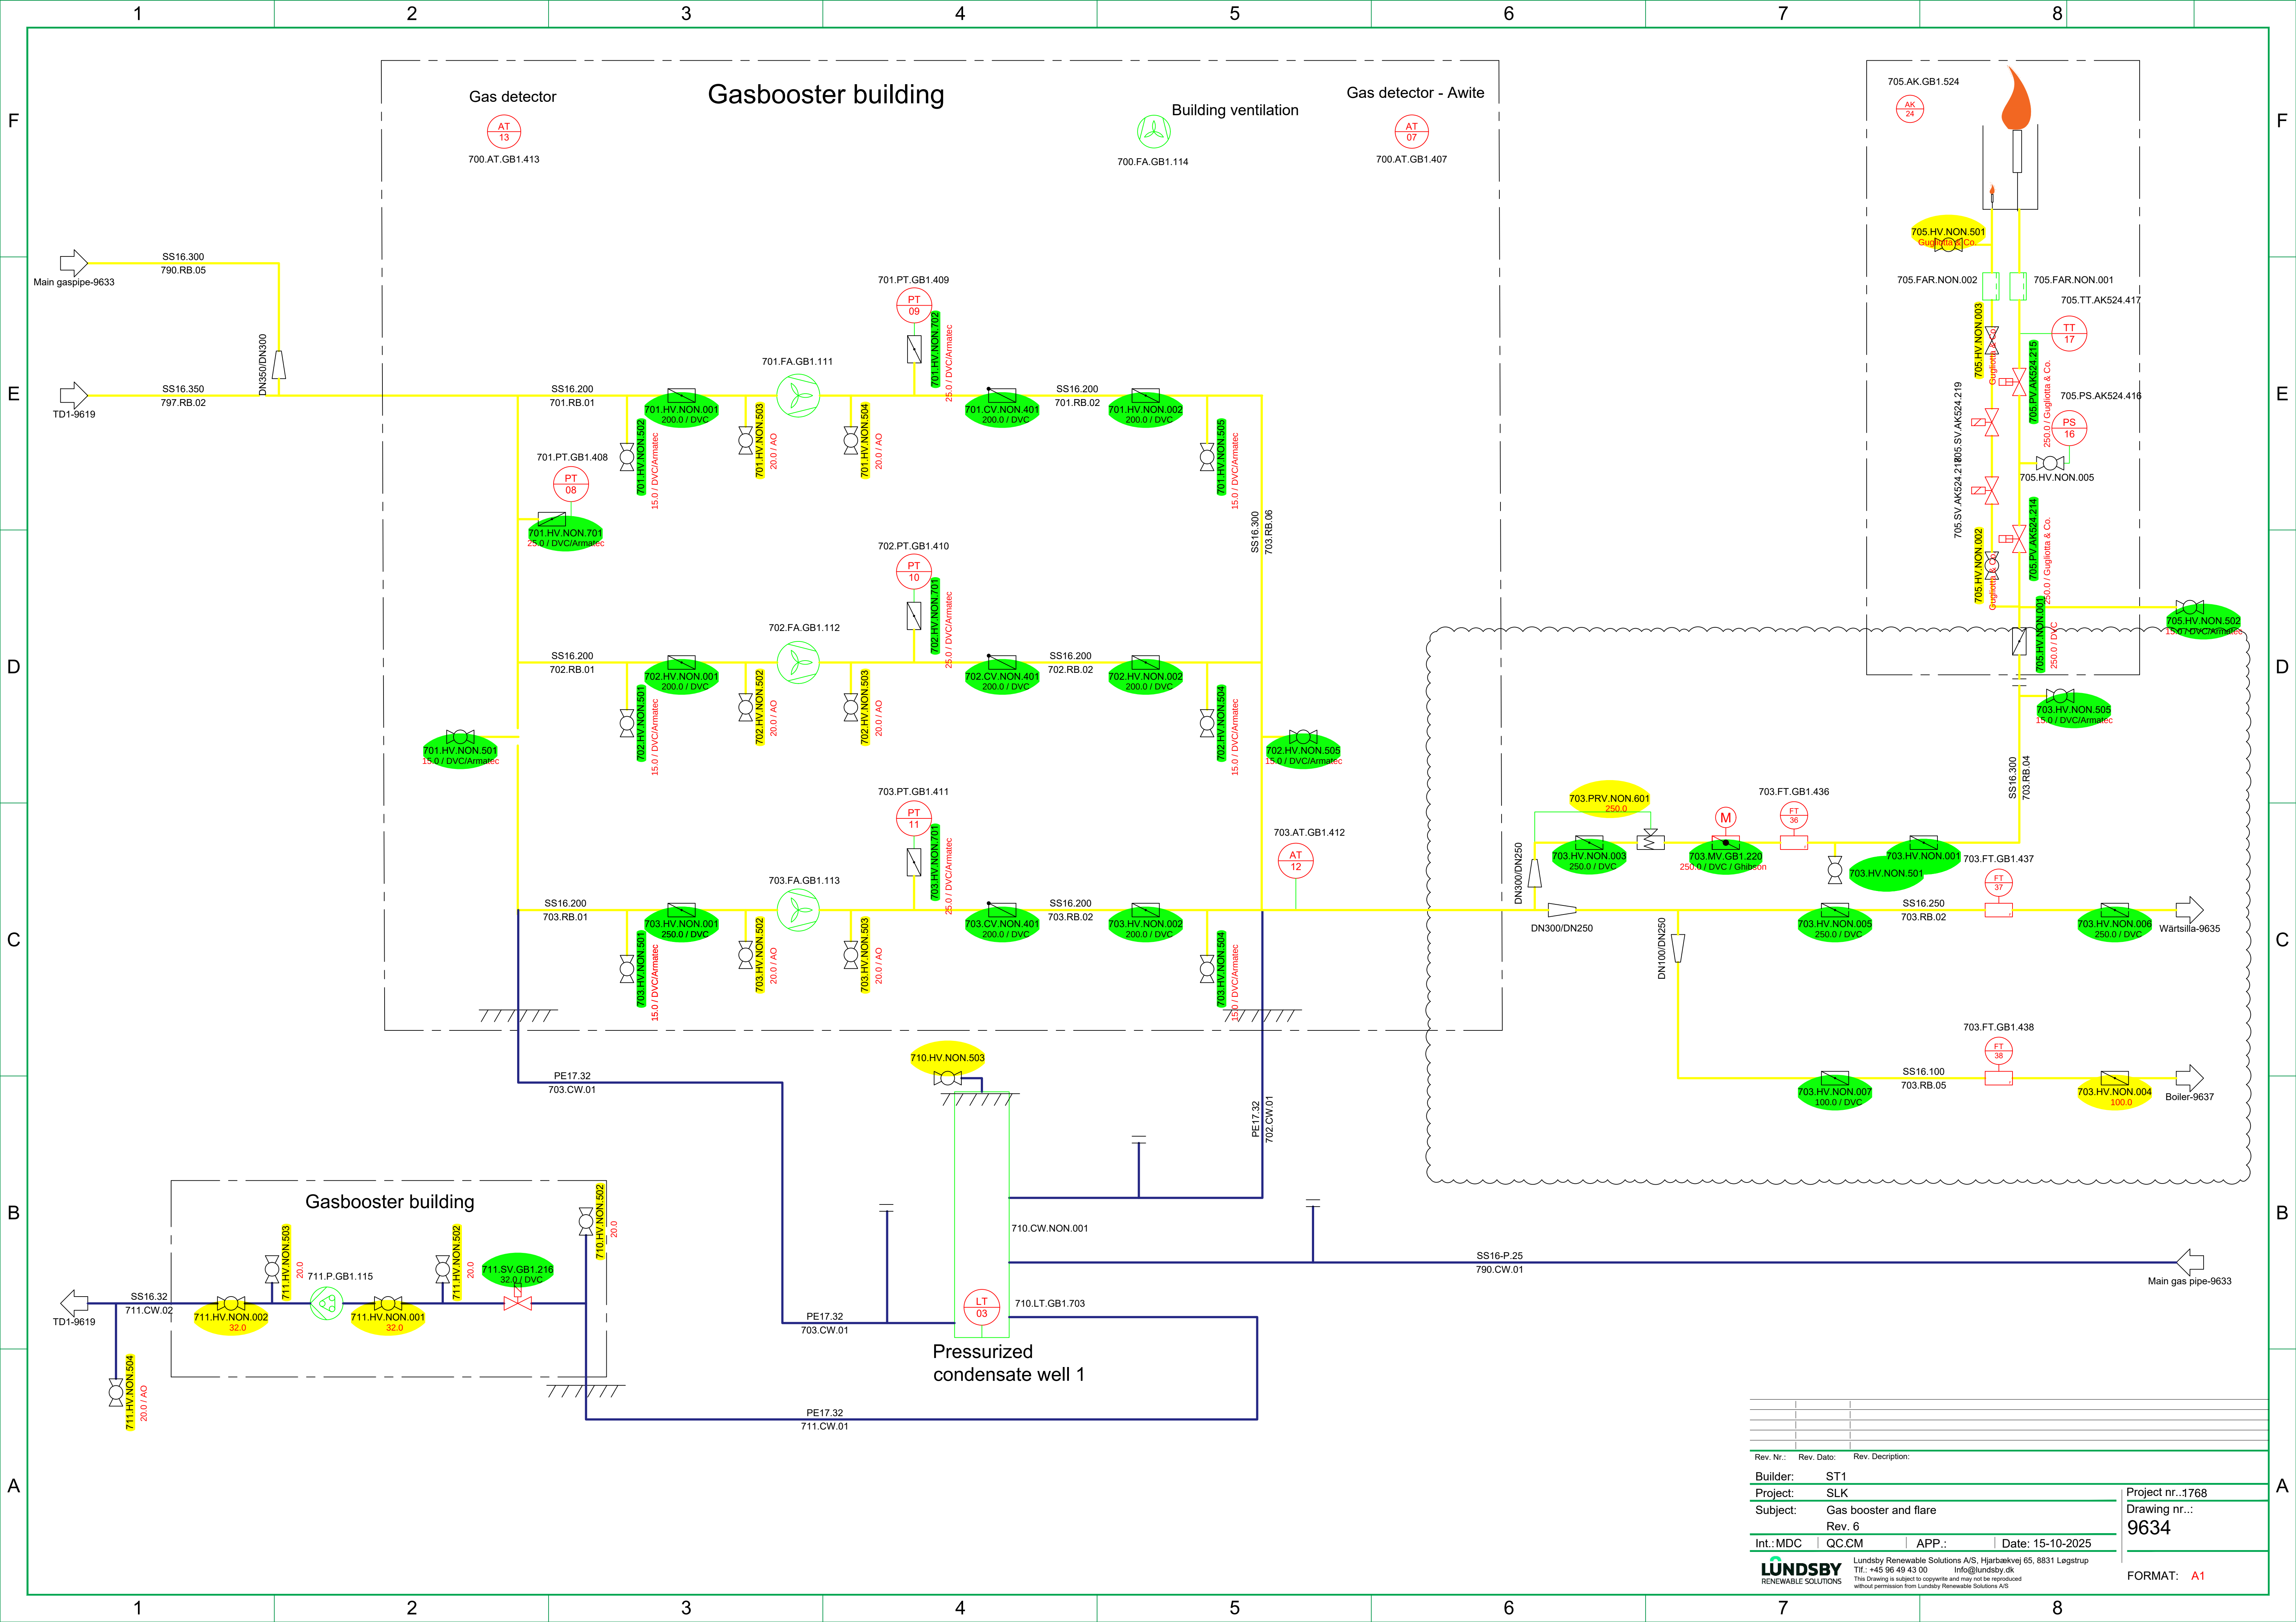


Rev. Nr.:	Rev. Dato:	Rev. Description:
Builder:	ST1	
Project:	SLK	
Subject:	Gas booster and flare	
Rev. 6		
Int.:MDC	QC:CM	APP.:
Date:	15-10-2025	
LUNDSBY RENEWABLE SOLUTIONS		
Lundsbys Renewable Solutions A/S, Hjarbækvej 65, 8831 Lægstrup Tlf.: +45 96 49 43 00 info@lundsbys.dk This Drawing is subject to copyright and may not be reproduced without permission from Lundsbys Renewable Solutions A/S		
Project nr.:1768 Drawing nr.: 9634		FORMAT: A1

Wärtsillä

730-UPG-01

730-LBG-01

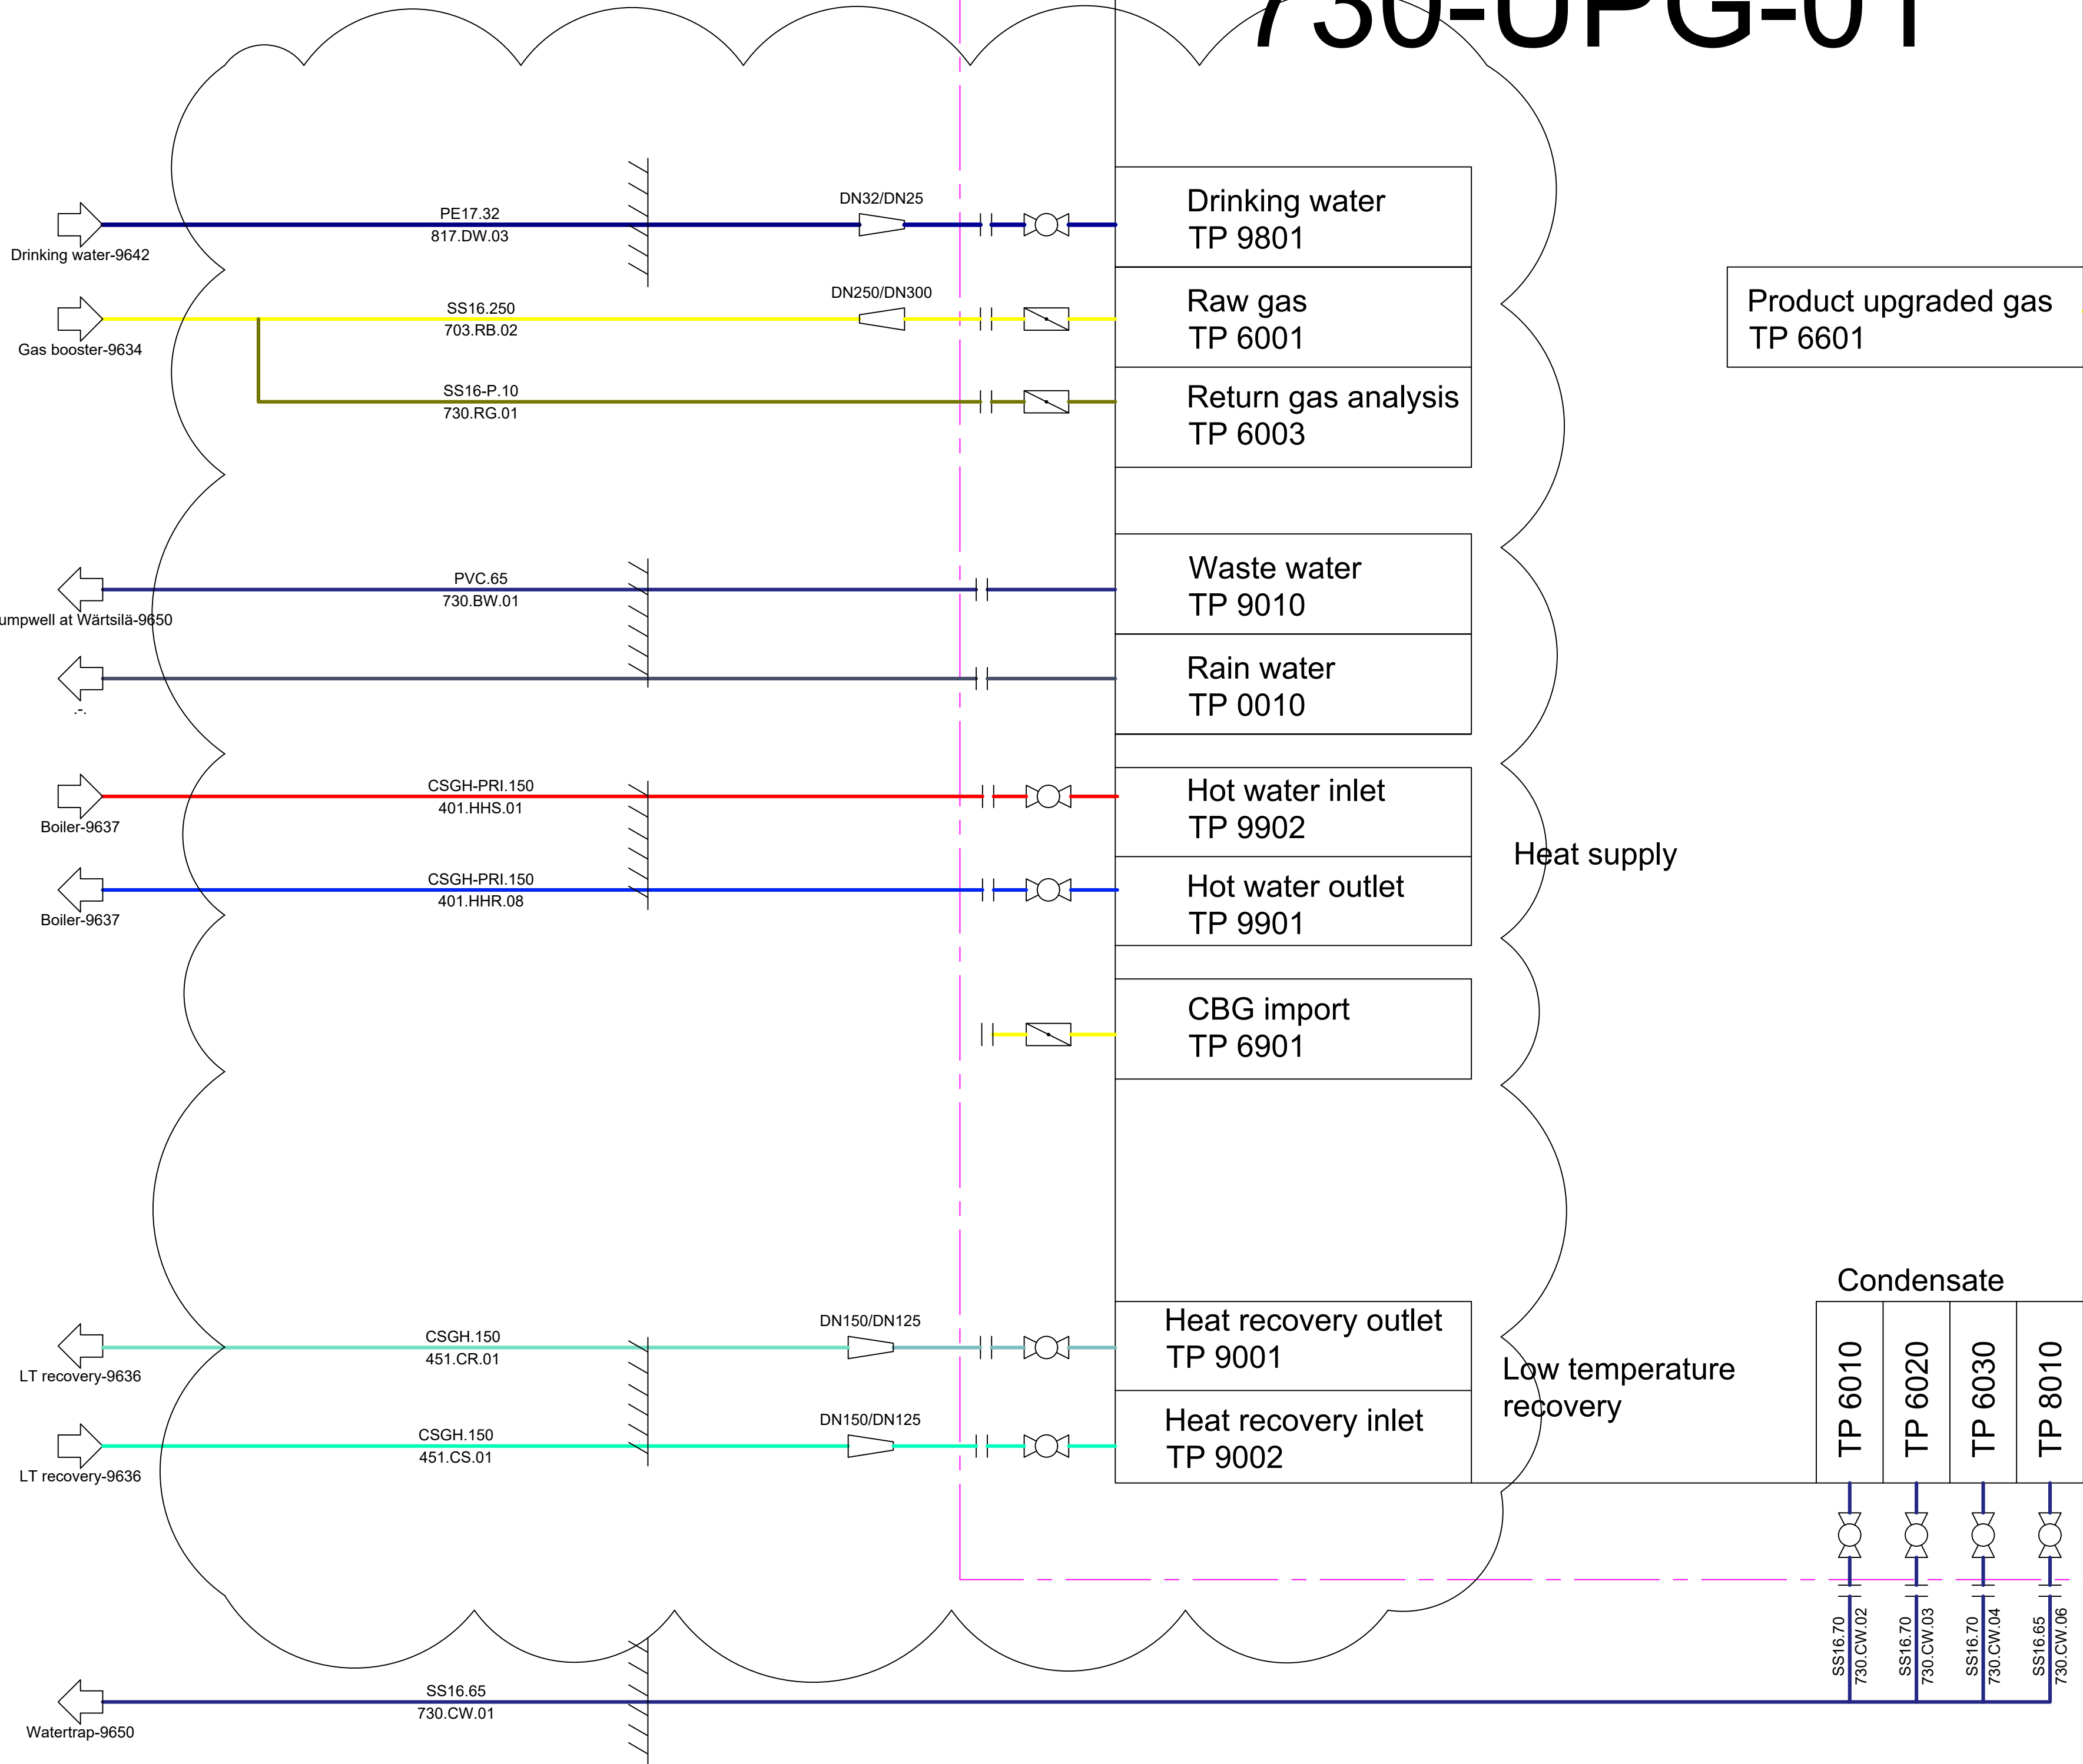

AK
22

730.AK.T4.522

AK
23

730.AK.T5.523

Product upgraded gas
TP 6601

BOG send-out
N7

Product upgraded gas
N1

Inlet

Liquefied gas
N2

Outlet

Instrument air
N11

Water spray system
inlet

Liquefied gas
N11

LBG send-out to truck
33S1800


Vapour return from
truck 33S1801

Nitrogen
N5


Rev. Nr.:	Rev. Dato:	Rev. Description:	
Builder:	ST1		
Project:	SLK		
Subject:	Upgrade		
	Rev. 6		
Int.:MDC	QC.CM	APP.:	Date: 15-10-2025
LUNDSBY RENEWABLE SOLUTIONS			Lundby Renewable Solutions A/S, Hjarbækvej 65, 8831 Løgstrup Tlf.: +45 96 49 43 00 Info@lundby.dk This Drawing is subject to copyright and may not be reproduced without permission from Lundby Renewable Solutions A/S
Project nr...:1768 Drawing nr...: 9635			FORMAT: A1


Technology
building

Heat pump scope

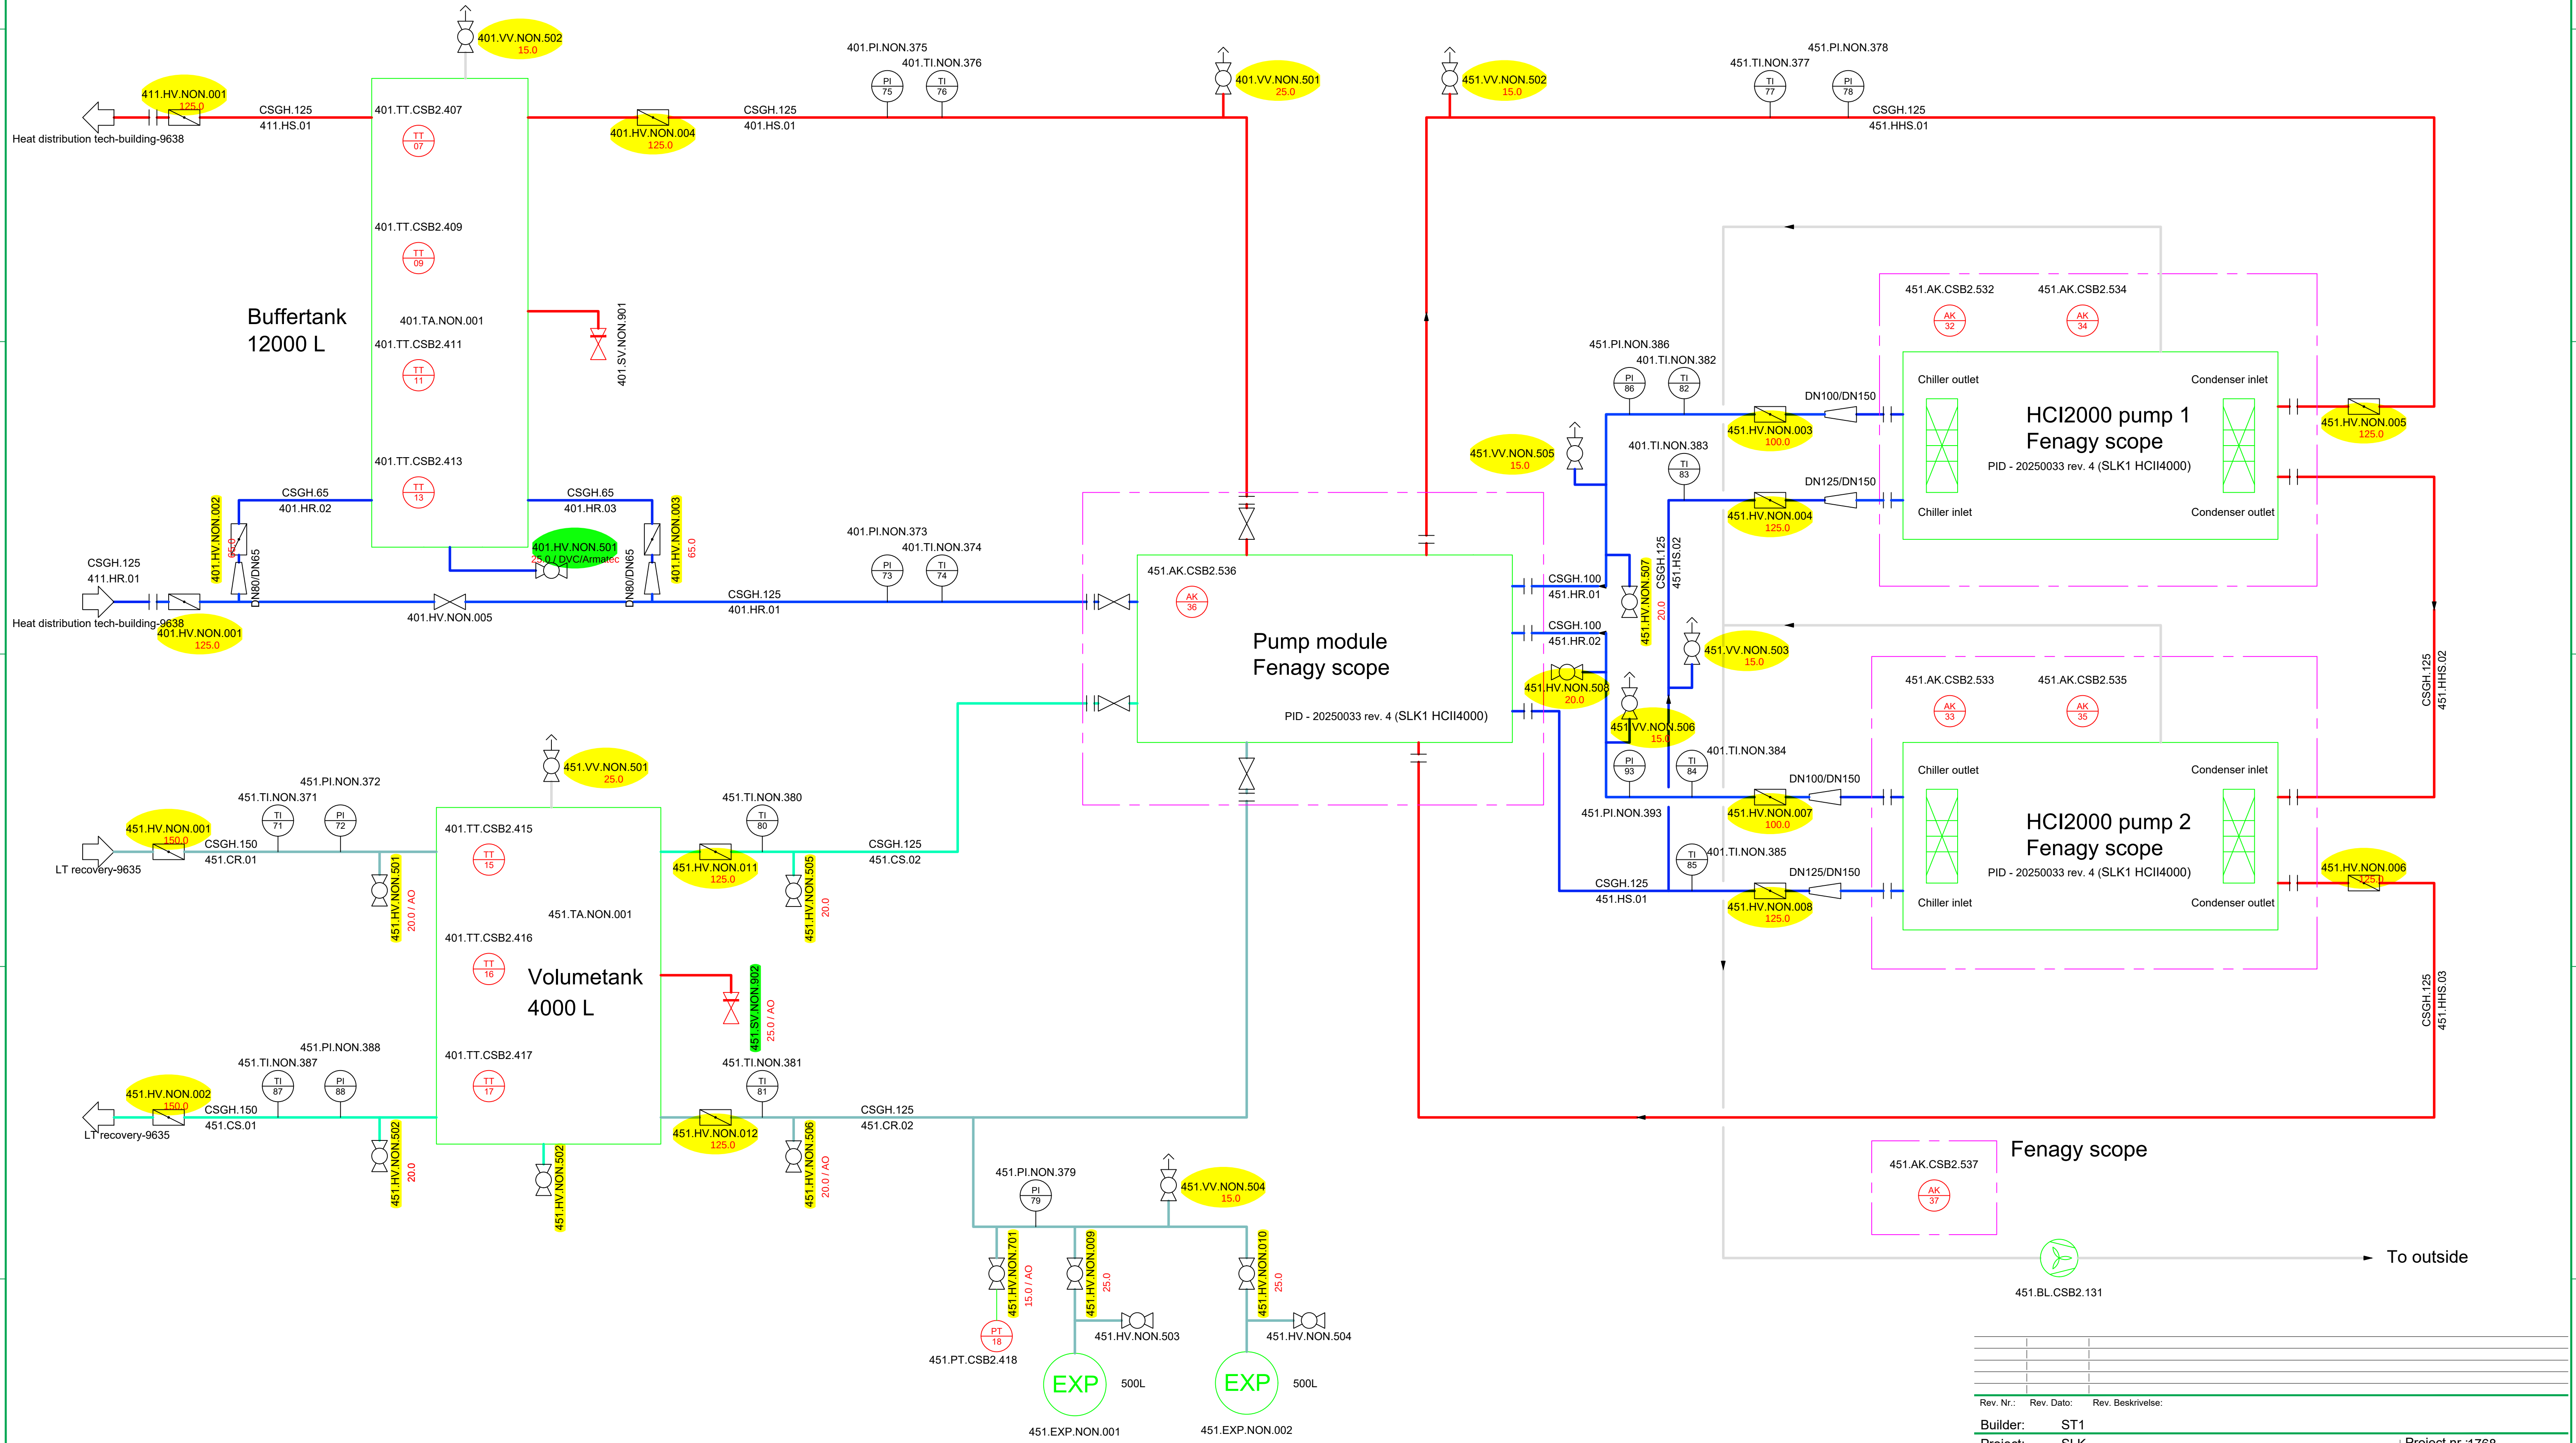


Rev. Nr.:	Rev. Dato:	Rev. Beskrivelse:
Builder:	ST1	
Project:	SLK	
Subject:	Heat pumps	
Rev.:	6	
Int.:MDC	QC: CM	APP.: Date: 15-10-2025
LUNDSBY RENEWABLE SOLUTIONS		
Lundsby Biogas A/S, Hjarbækvej 65, 8831 Løgstrup Tlf.: +45 96 49 43 00 info@lundsbybiogas.dk		
Denne tegning er underlagt copyright og må ikke reproduceres uden tilladelse fra Lundsbybiogas A/S		
Project nr.:1768 Drawing nr.: 9636		FORMAT: A1

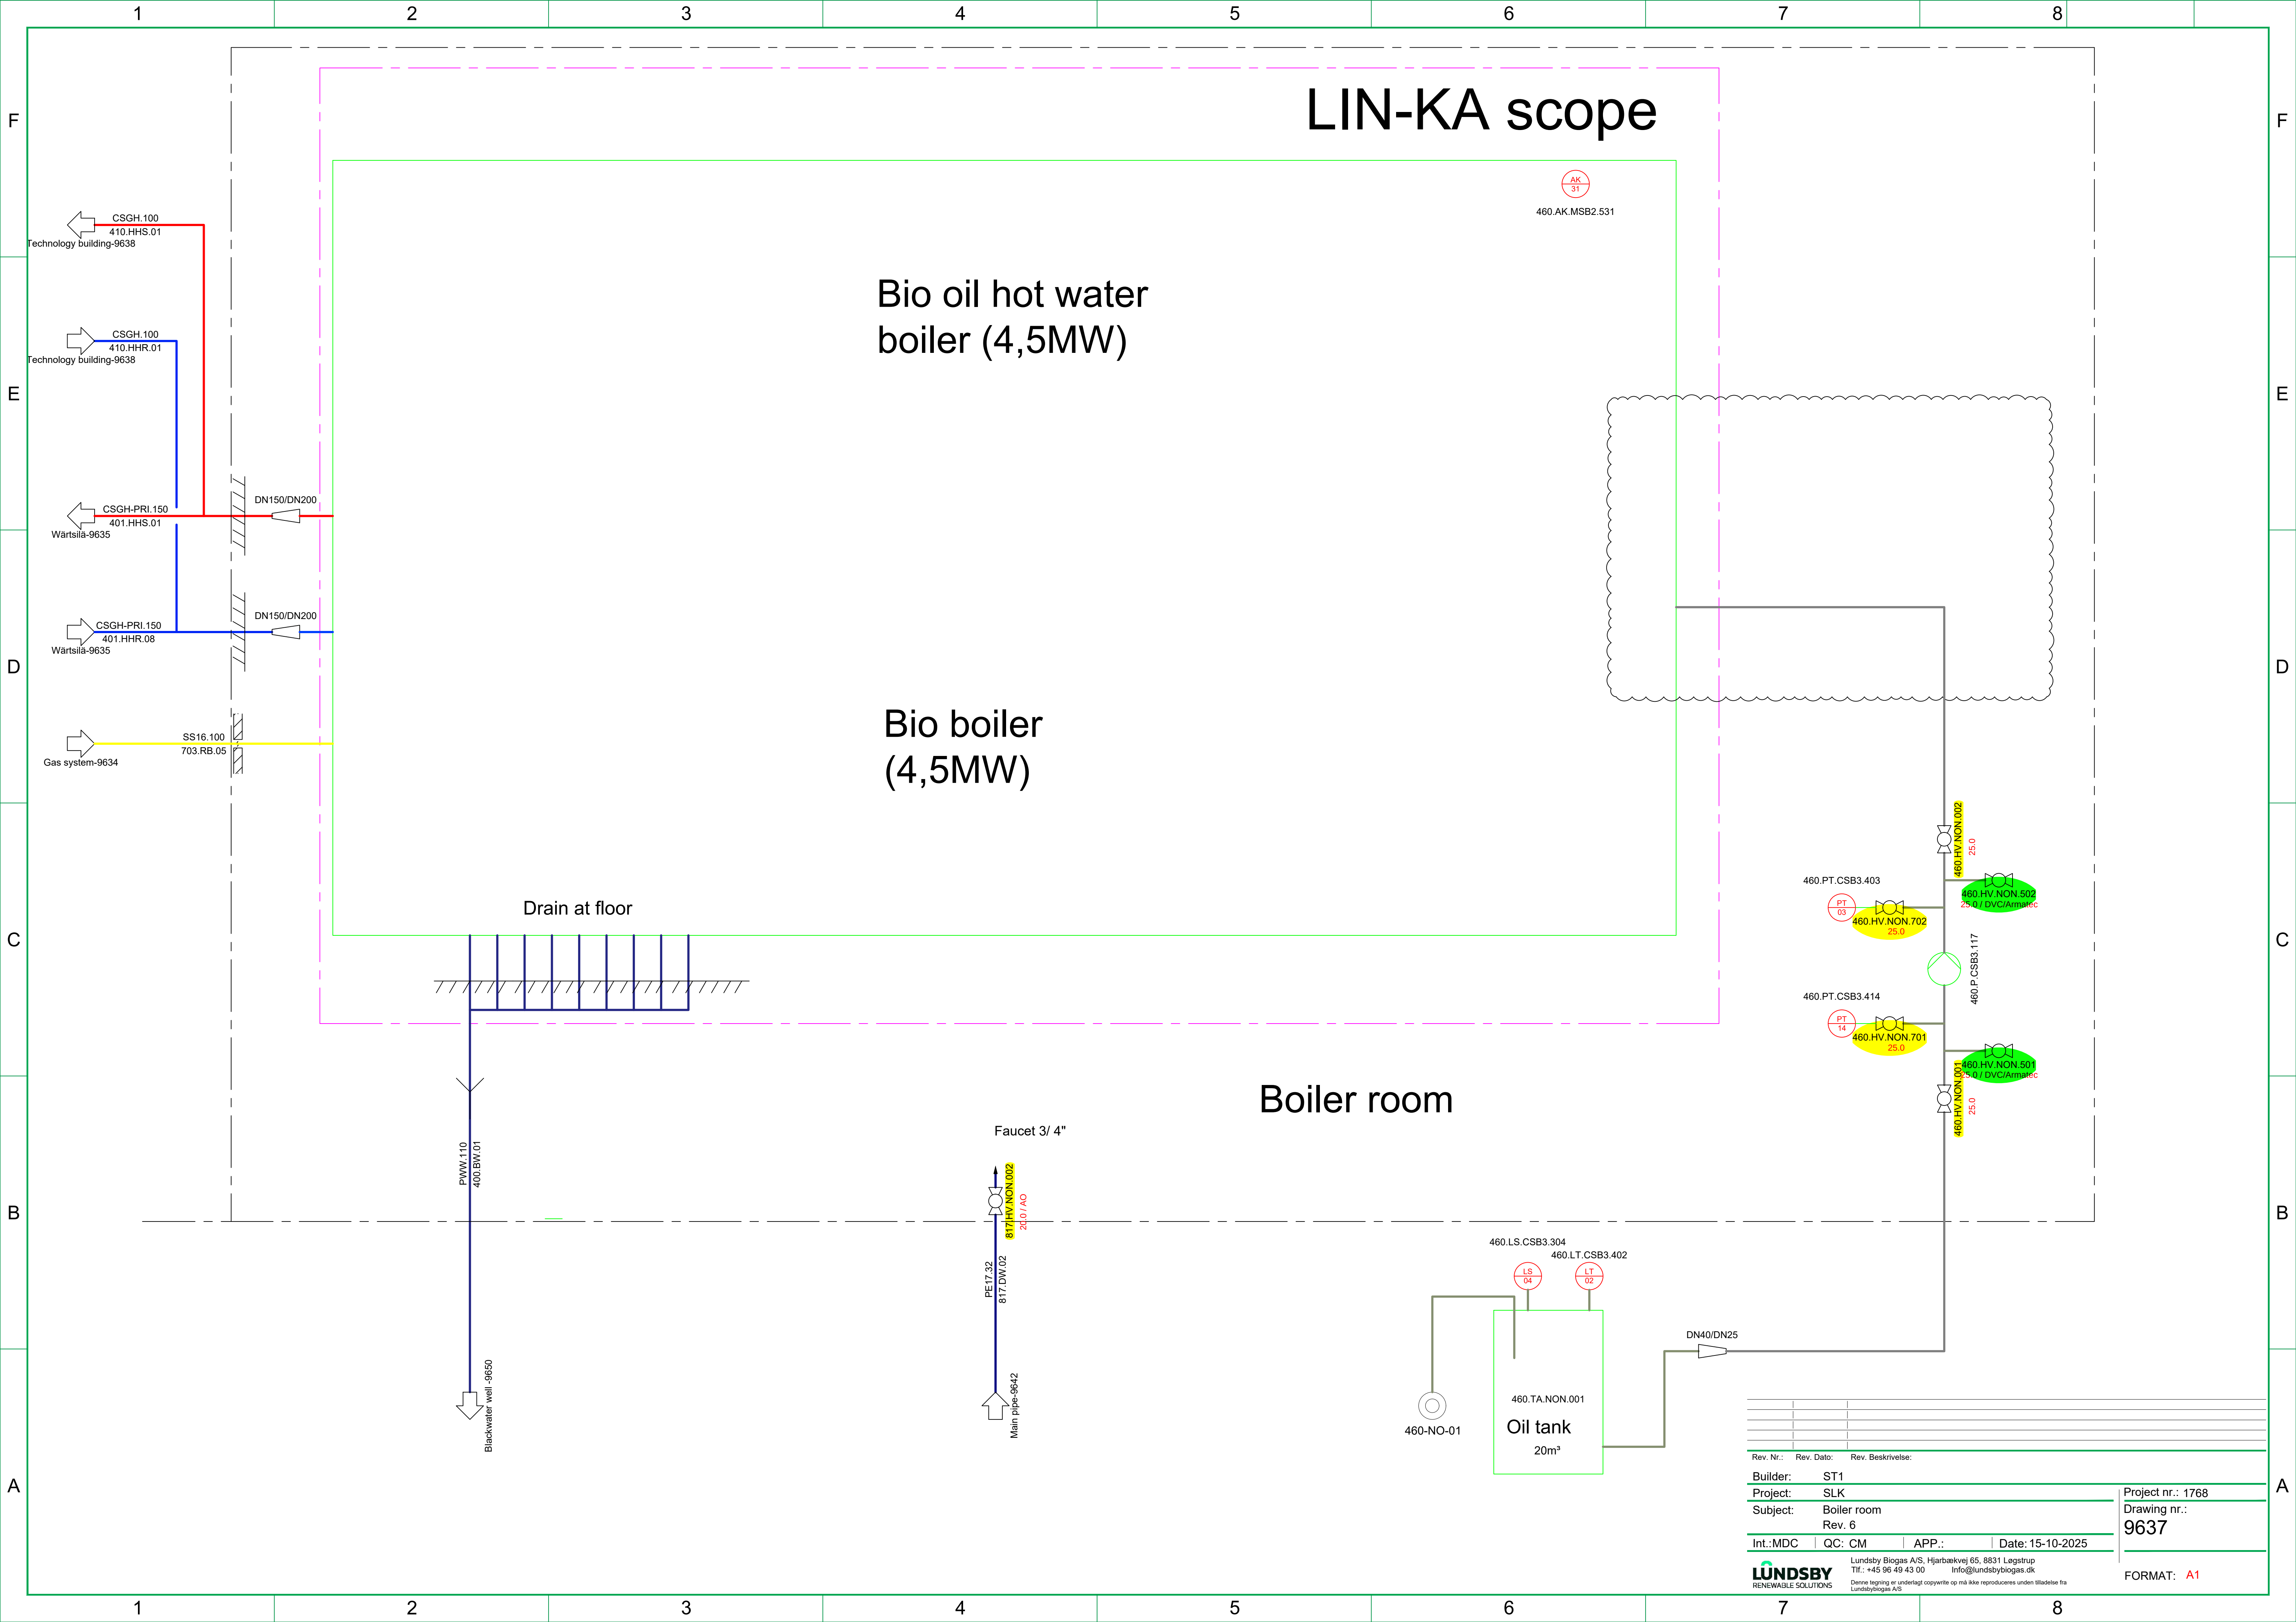

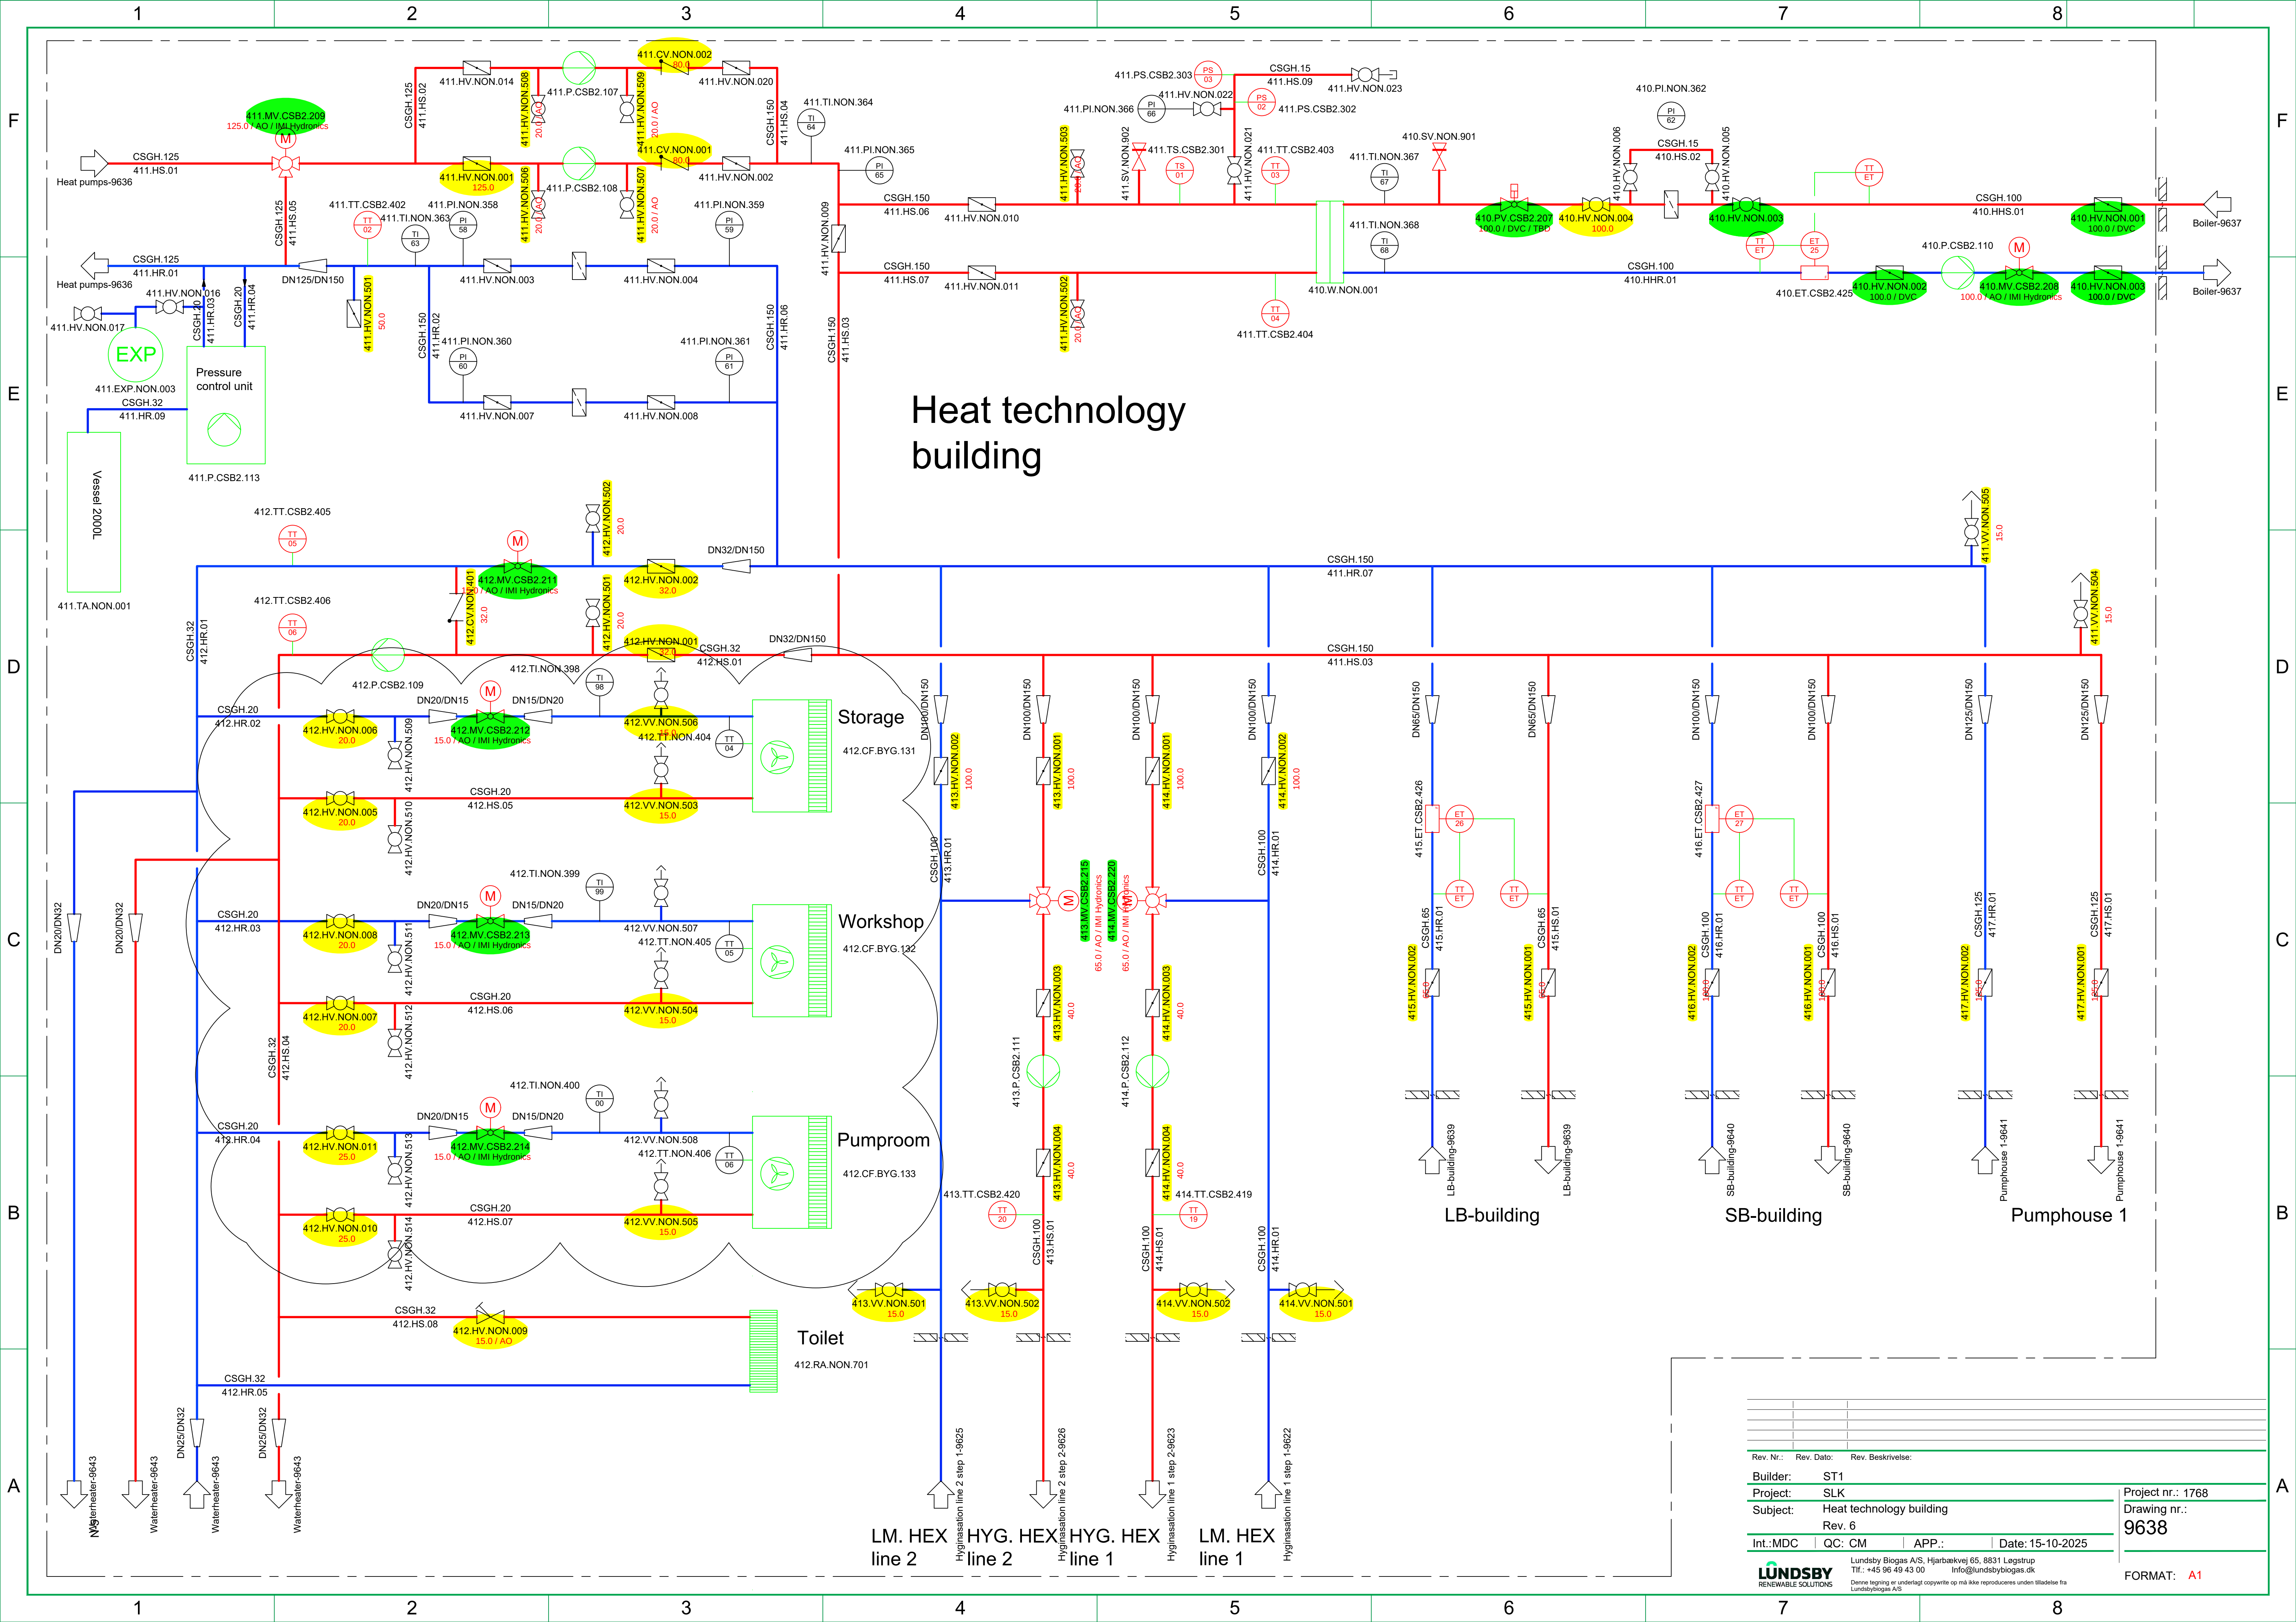

LB-Building

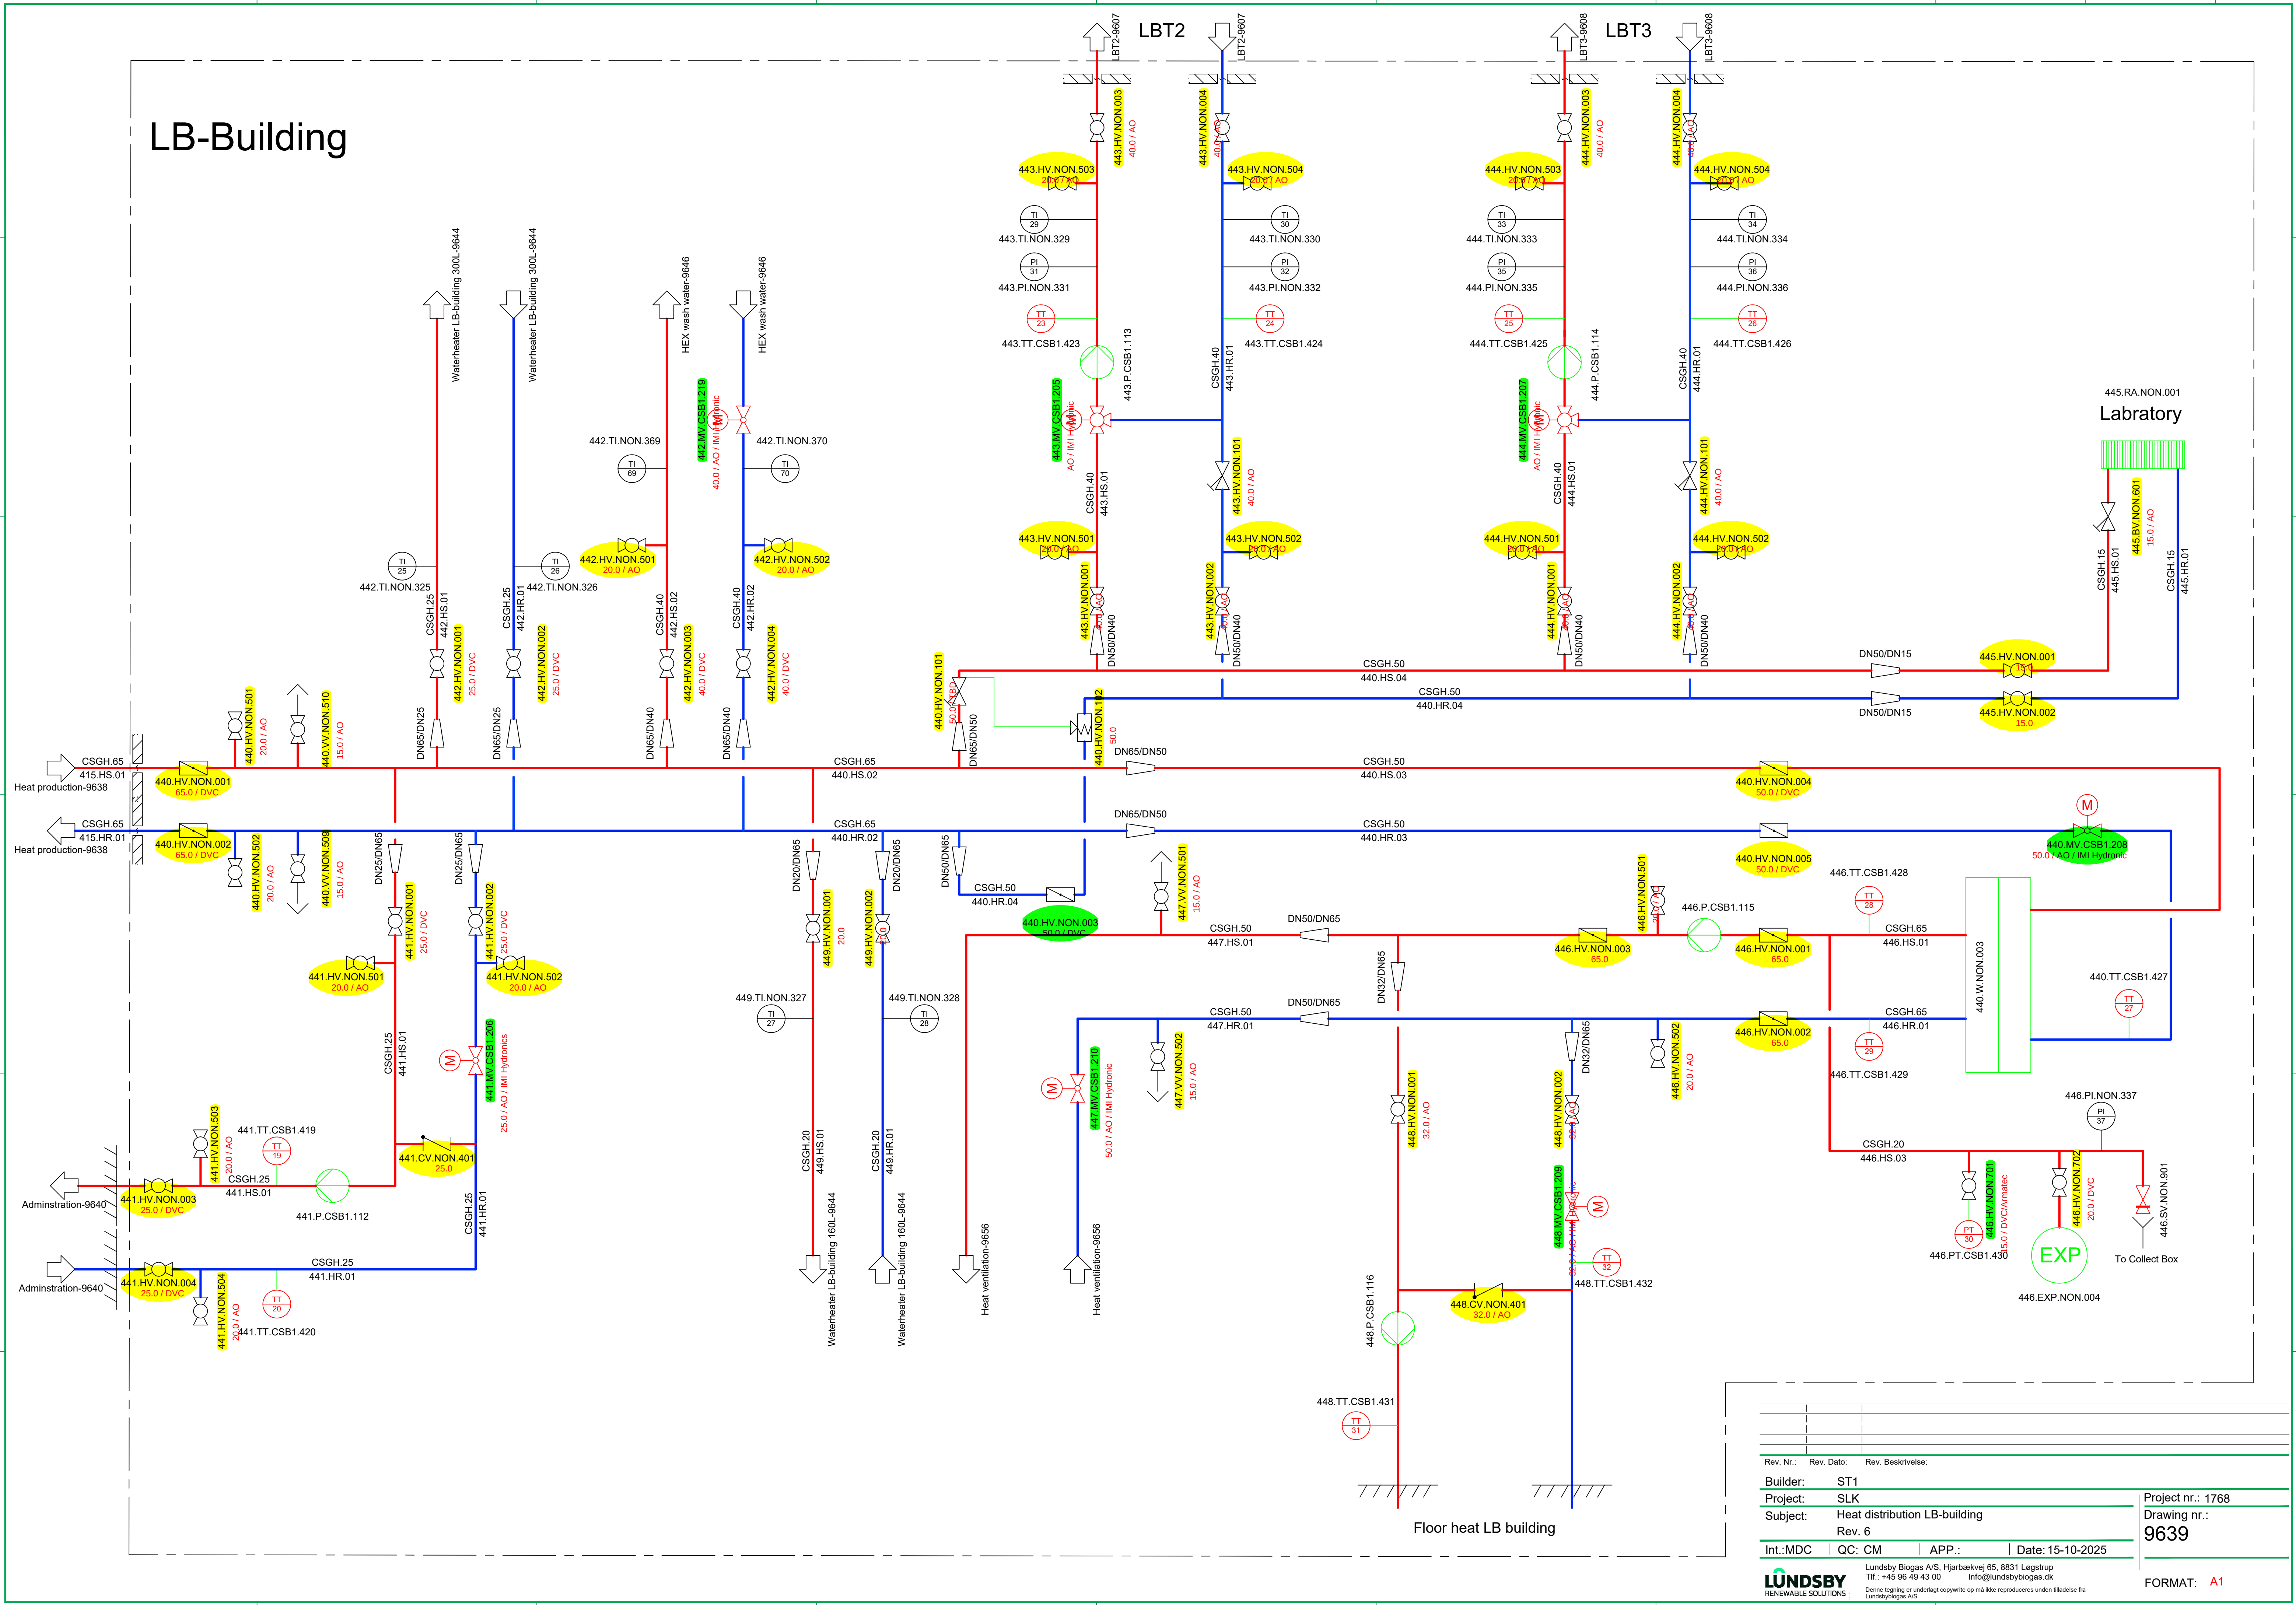

Rev. Nr.:	Rev. Dato:	Rev. Beskrivelse:


Builder:	ST1		
Project:	SLK		
Subject:	Heat distribution LB-building		
Rev. 6			
Int.:MDC	QC: CM	APP.:	Date: 15-10-2025

LUNDSBY
RENEWABLE SOLUTIONS

Lundsby Biogas A/S, Hjarbækvej 65, 8831 Løgstrup
Tlf.: +45 96 49 43 00
info@lundsbybiogas.dk
Denne tegning er underlagt copyright og må ikke reproduceres uden tilladelse fra Lundsbybiogas A/S

Project nr.: 1768
Drawing nr.: 9639
FORMAT: A1


SB-Building

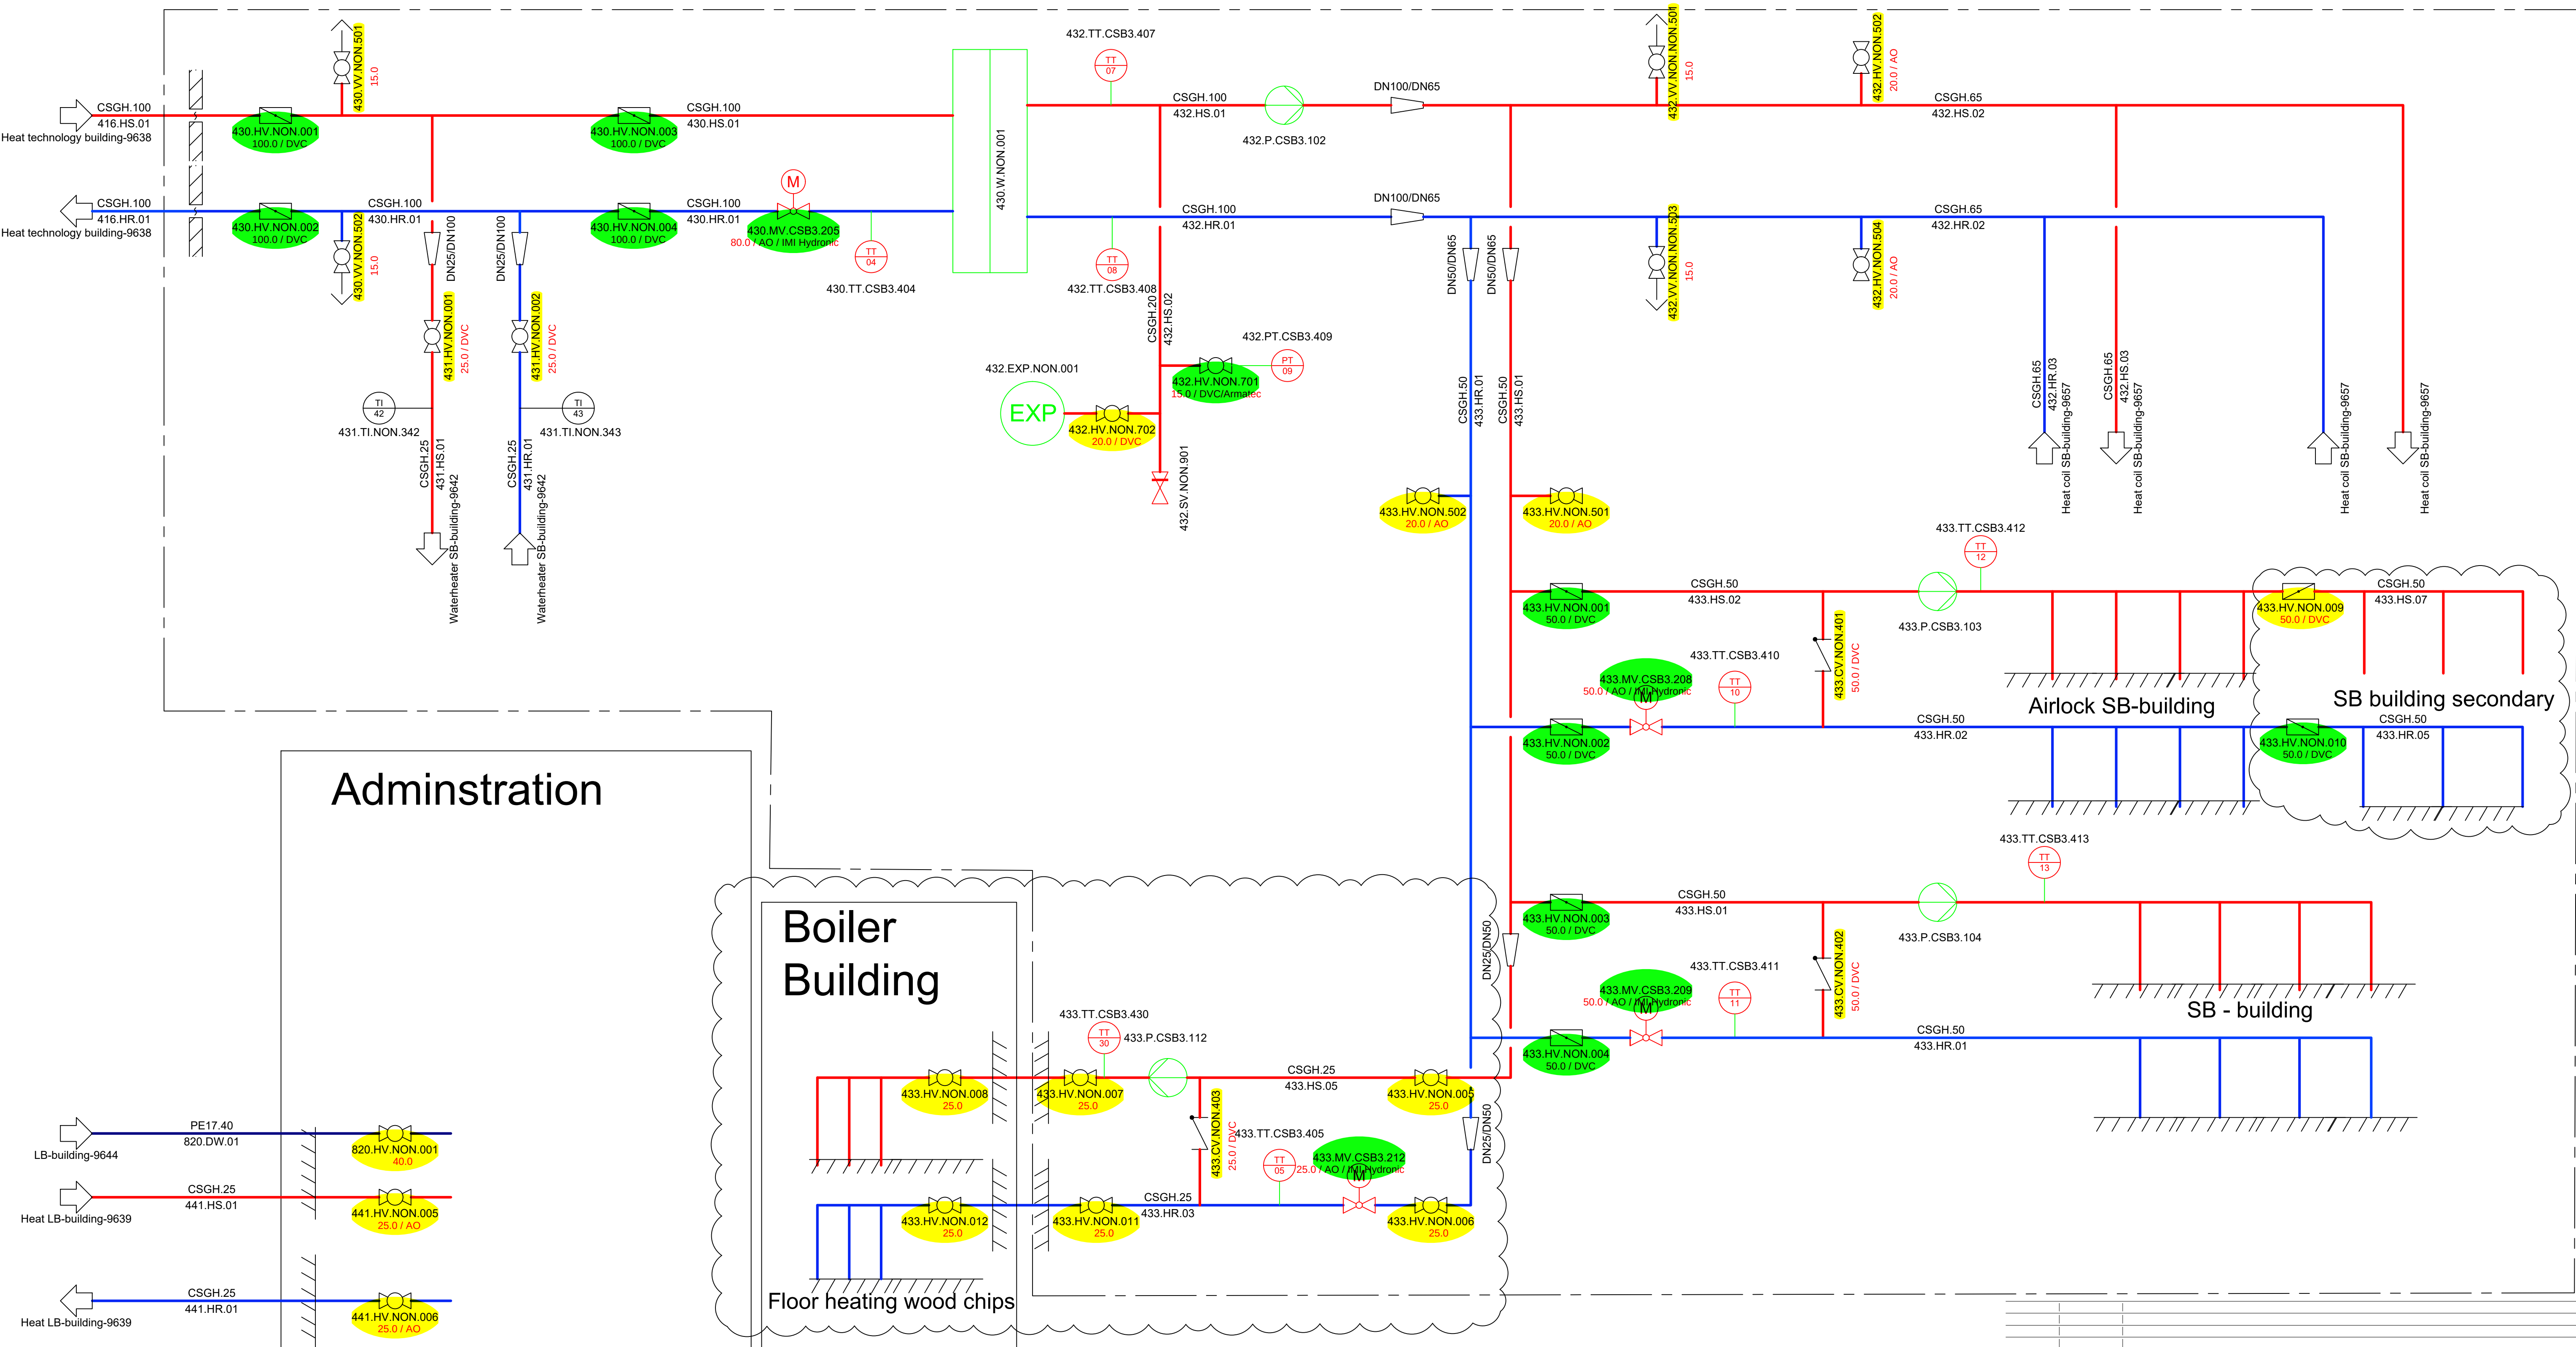


Rev. Nr.:	Rev. Dato:	Rev. Beskrivelse:
Builder:	ST1	
Project:	SLK	
Subject:	Heat distribution SB-building	
Int.:MDC	QC: CM	APP.:
Date:	15-10-2025	
Project nr.:	1768	
Drawing nr.:	9640	
FORMAT:	A1	

LUNDSBY
RENEWABLE SOLUTIONS

Lundsby Biogas A/S, Hjarbækvej 65, 8831 Løgstrup
Tlf.: +45 96 49 43 00
info@lundsbybiogas.dk
Denne tegning er underlagt copyright og må ikke reproduceres uden tilladelse fra Lundsbybiogas A/S

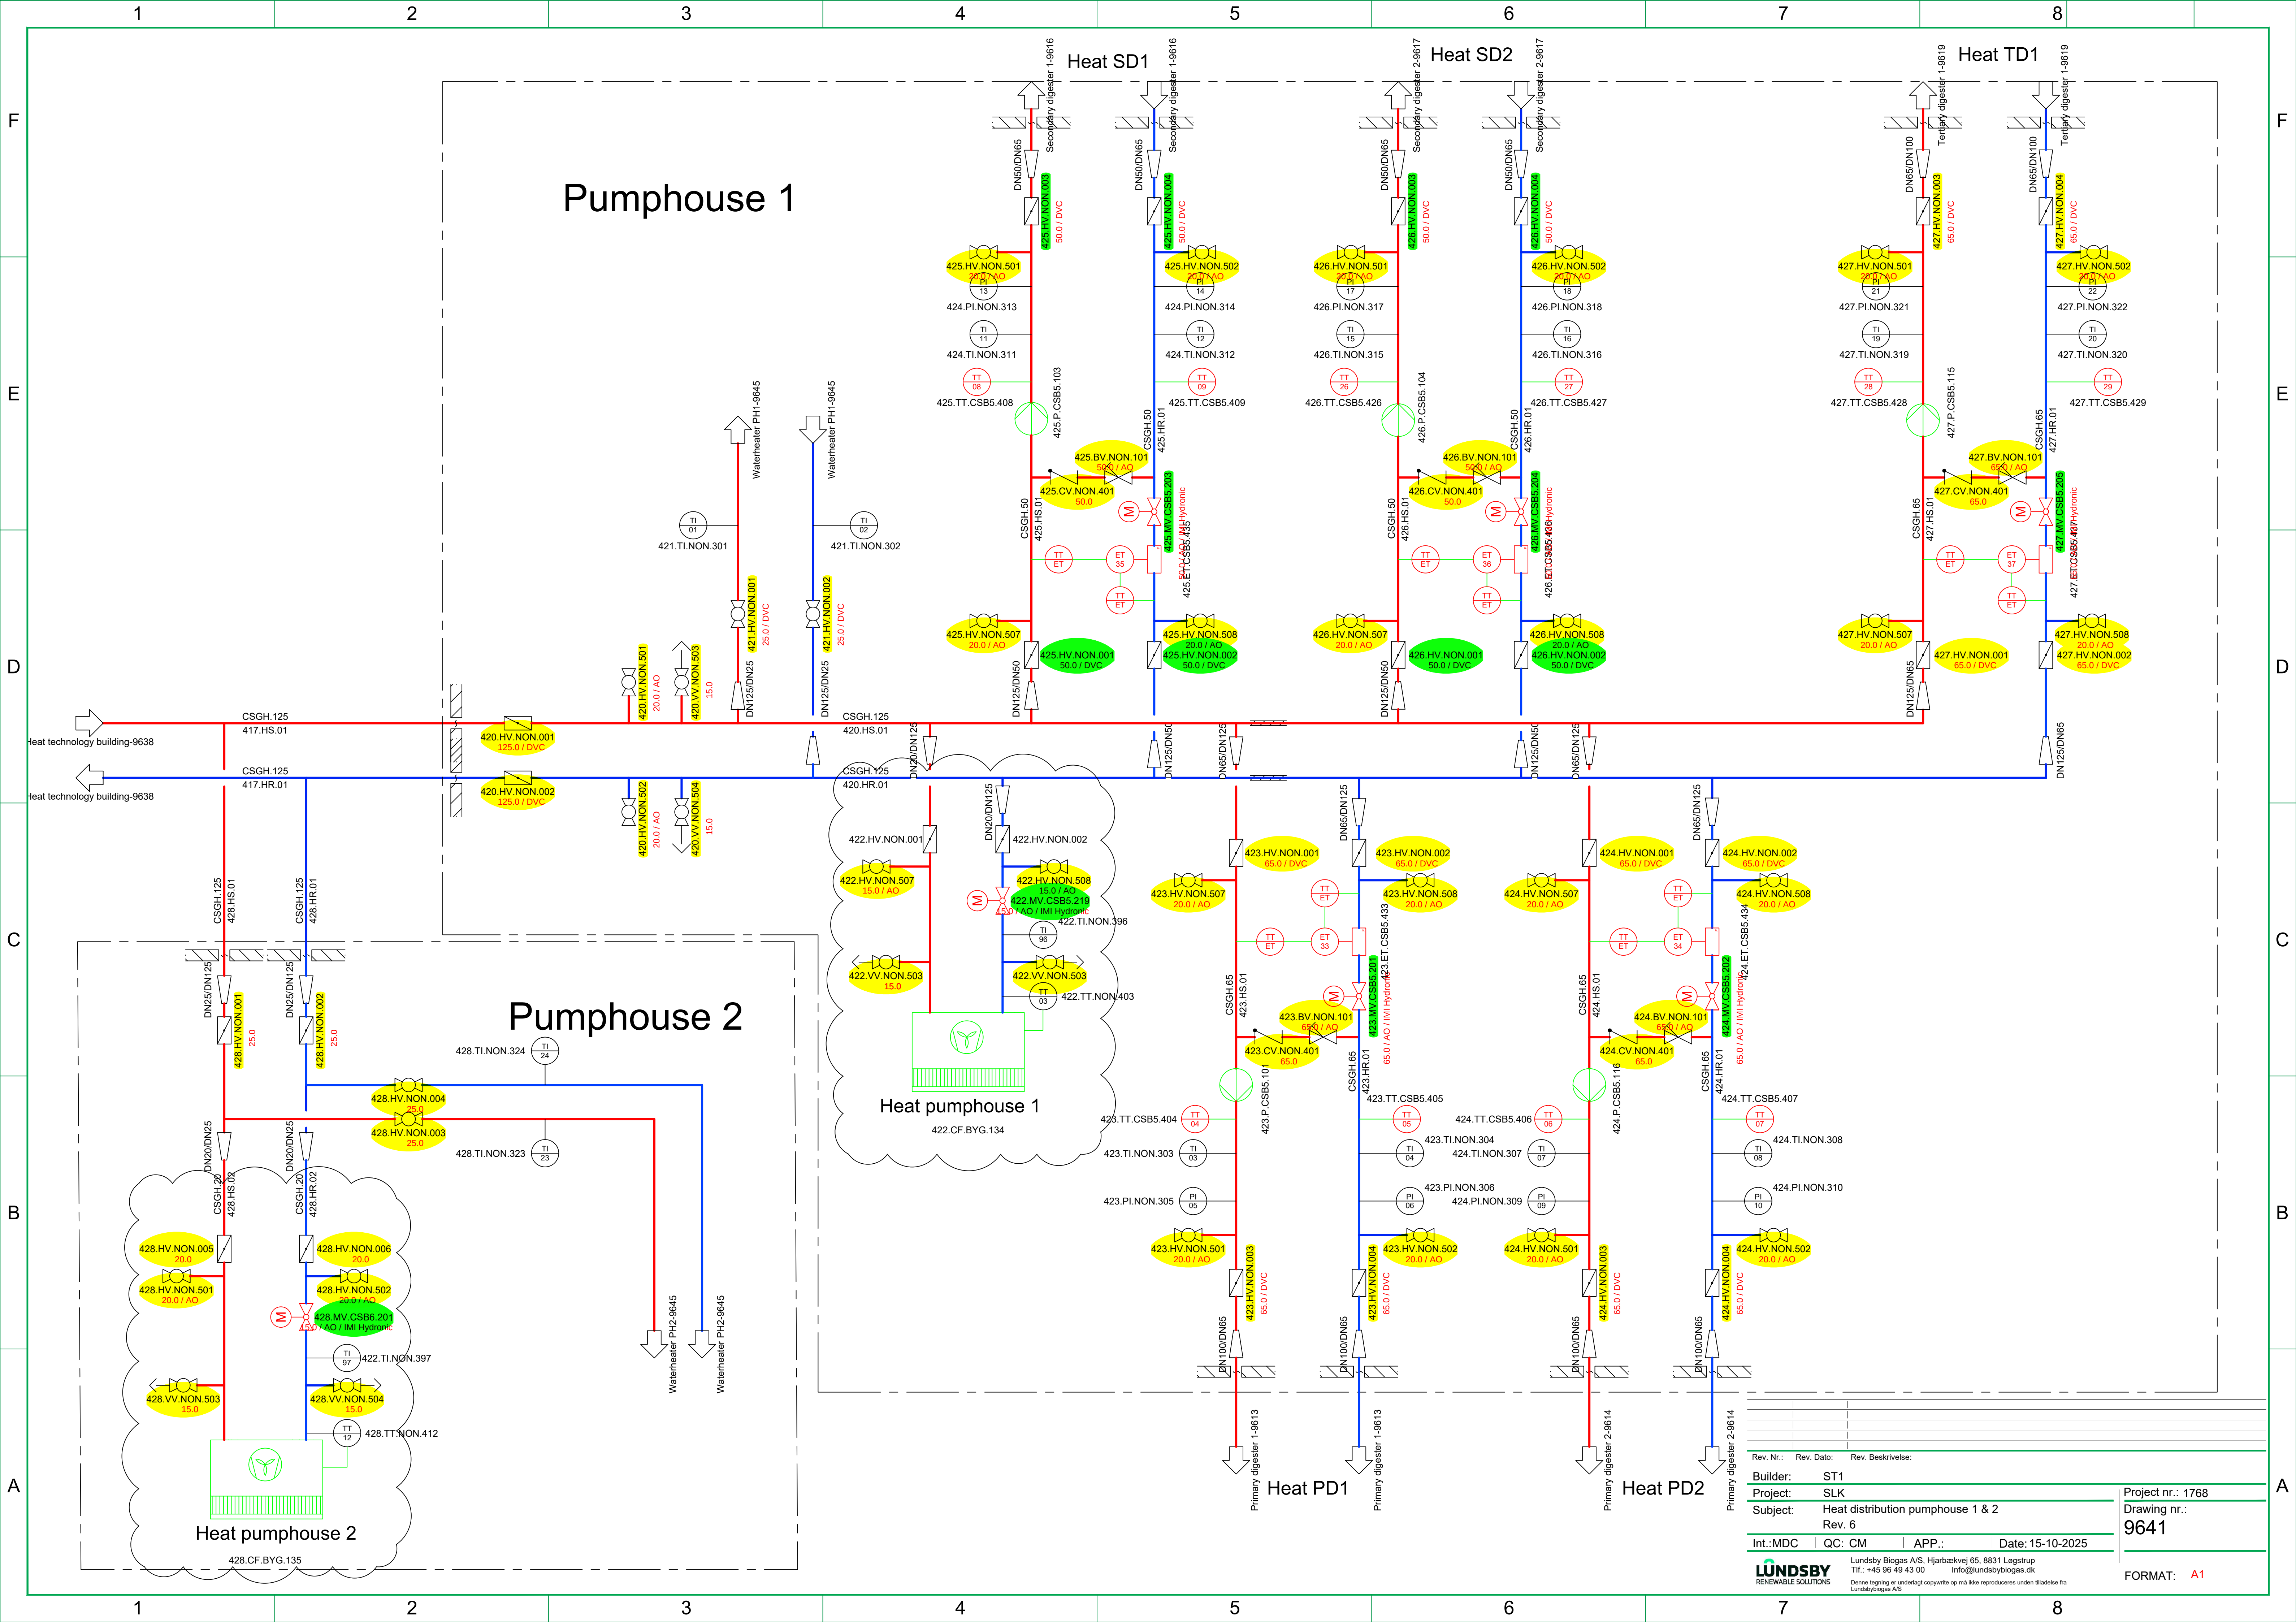


SB-Building

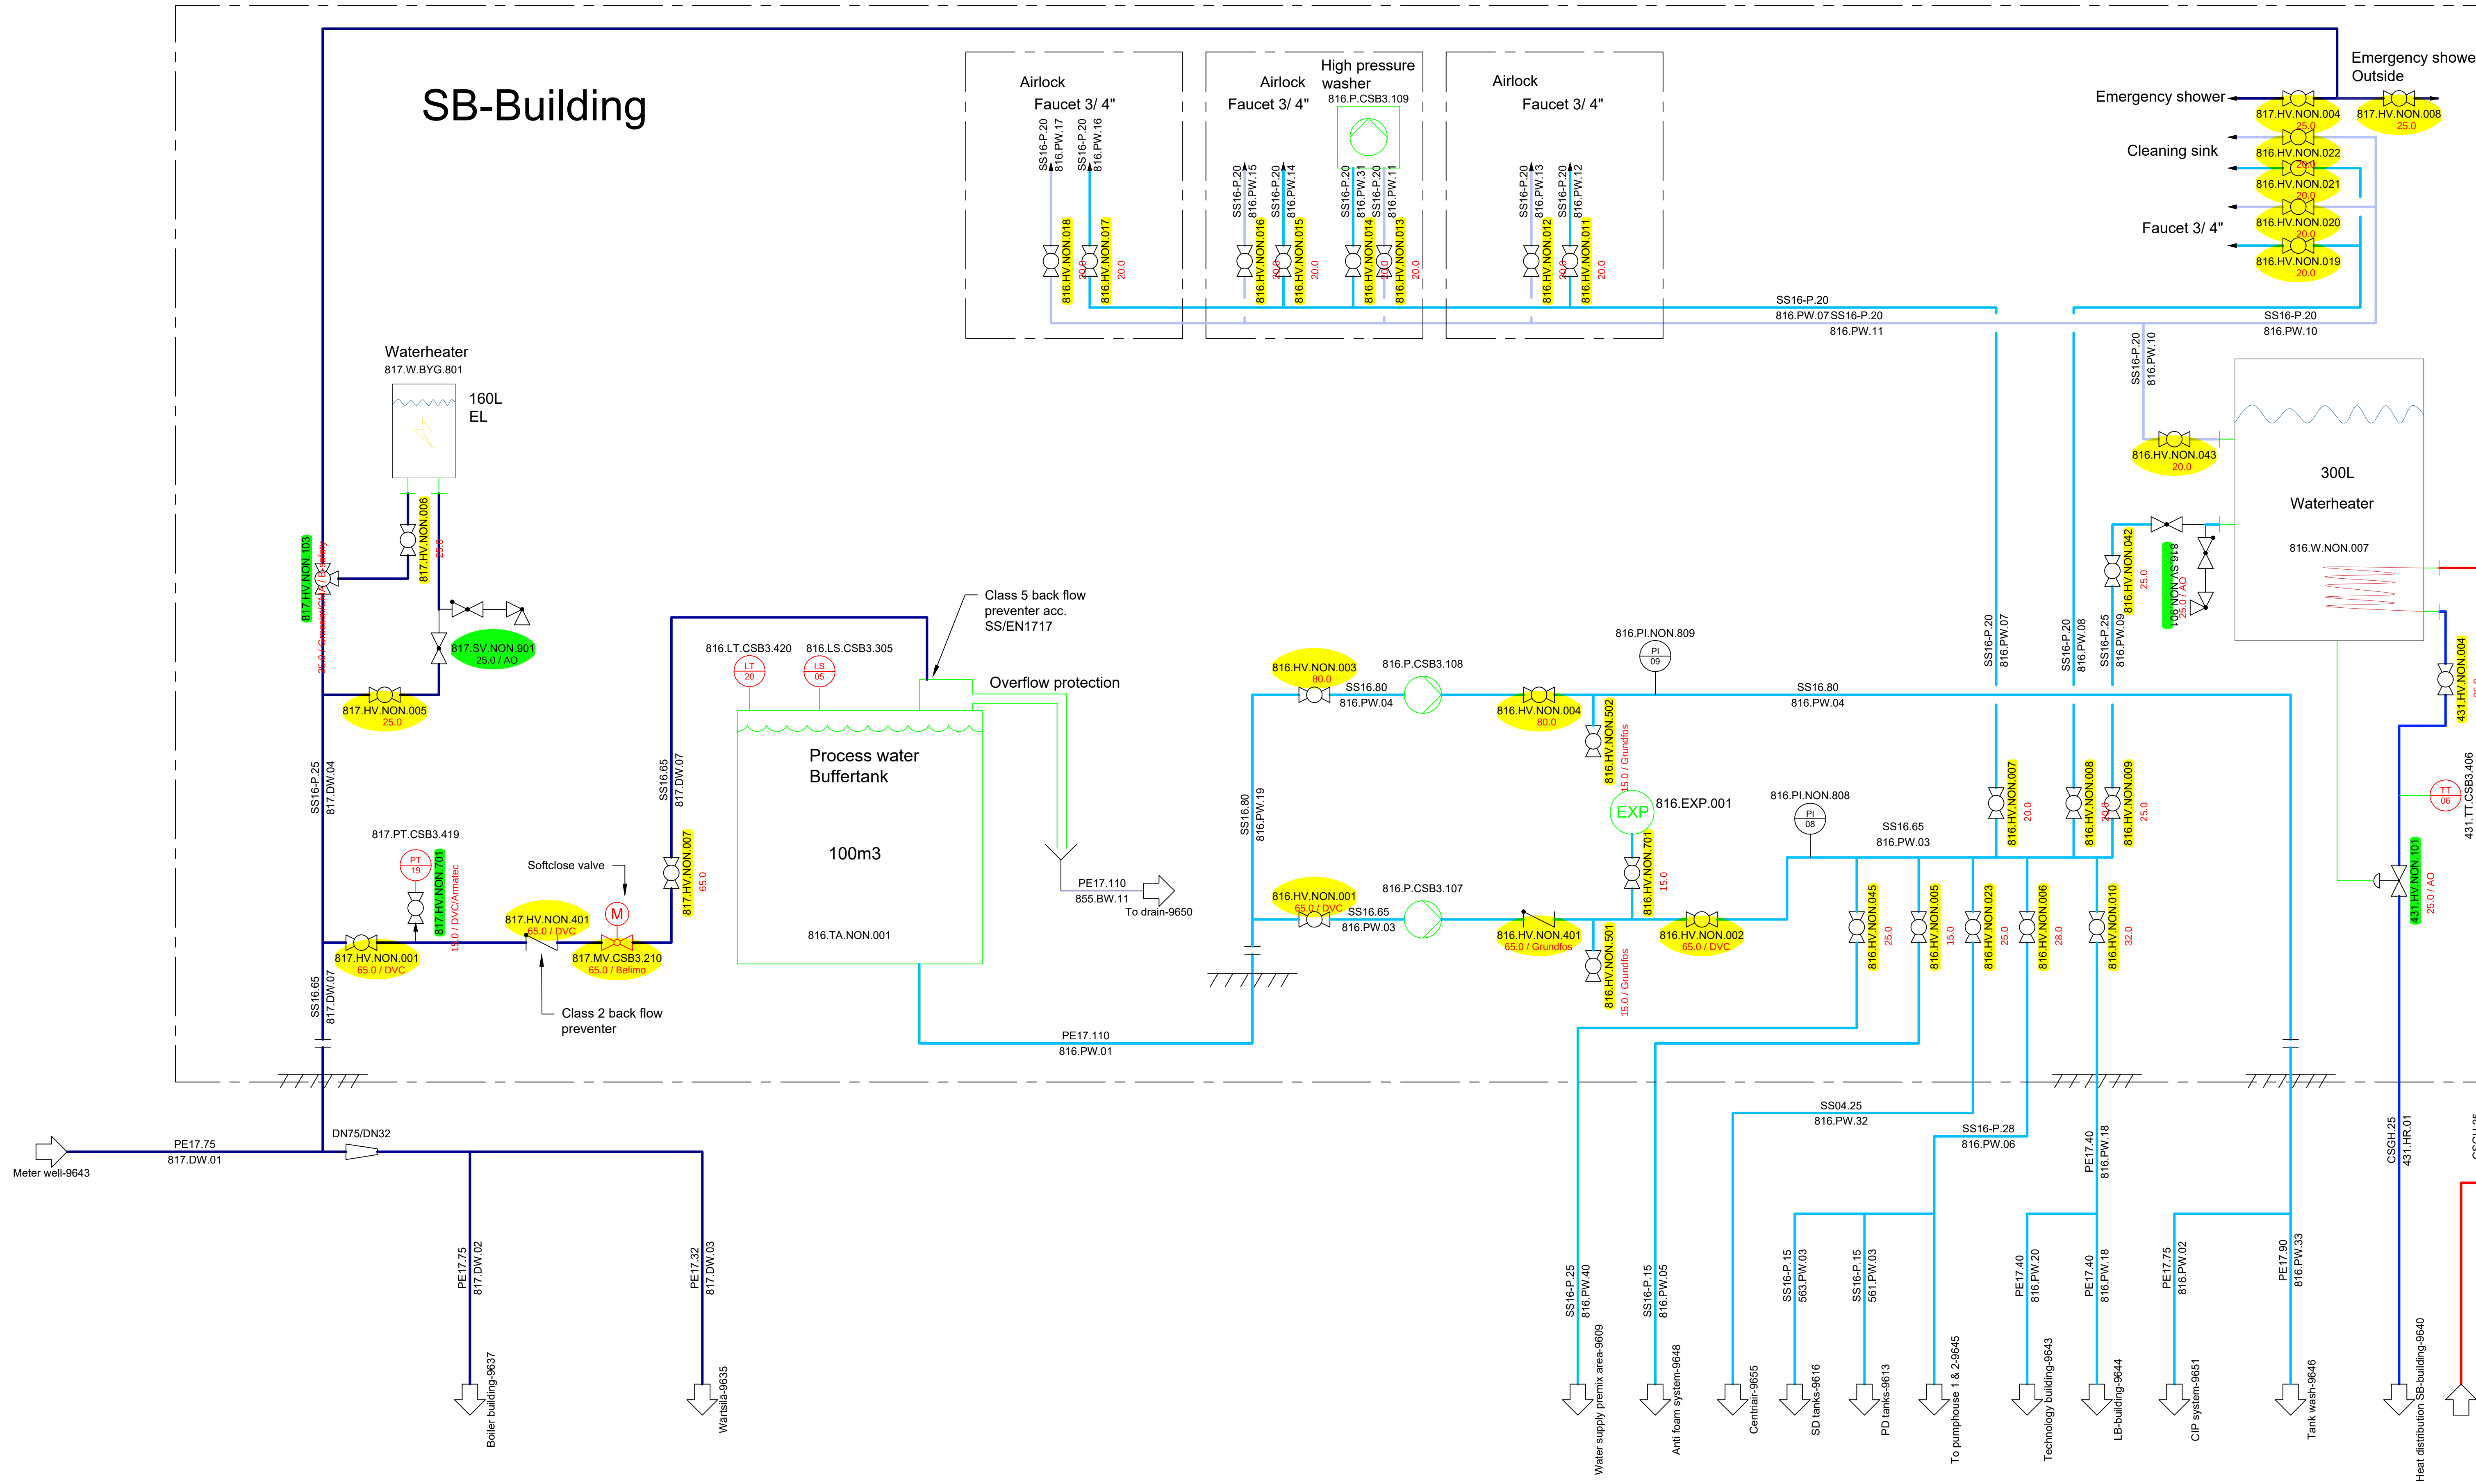


Rev. Nr.:	Rev. Dato:	Rev. Beskrivelse:
Builder:	ST1	
Project:	SLK	
Subject:	Water distribution SB-building	
Rev. 6		
Int.:MDC	QC:CM	APP.:
		Date: 15-10-2025
LUNDSBY RENEWABLE SOLUTIONS		
Lundsby Biogas A/S, Hjarbækvej 65, 8831 Løgstrup Tlf.: +45 96 49 43 00 info@lundsbybiogas.dk		
Denne tegning er underlagt copyright op på ikke reproduceres uden tilladelse fra Lundsbybiogas A/S		
Project nr.: 1768 Drawing nr.: 9642		FORMAT: A1

Technology building

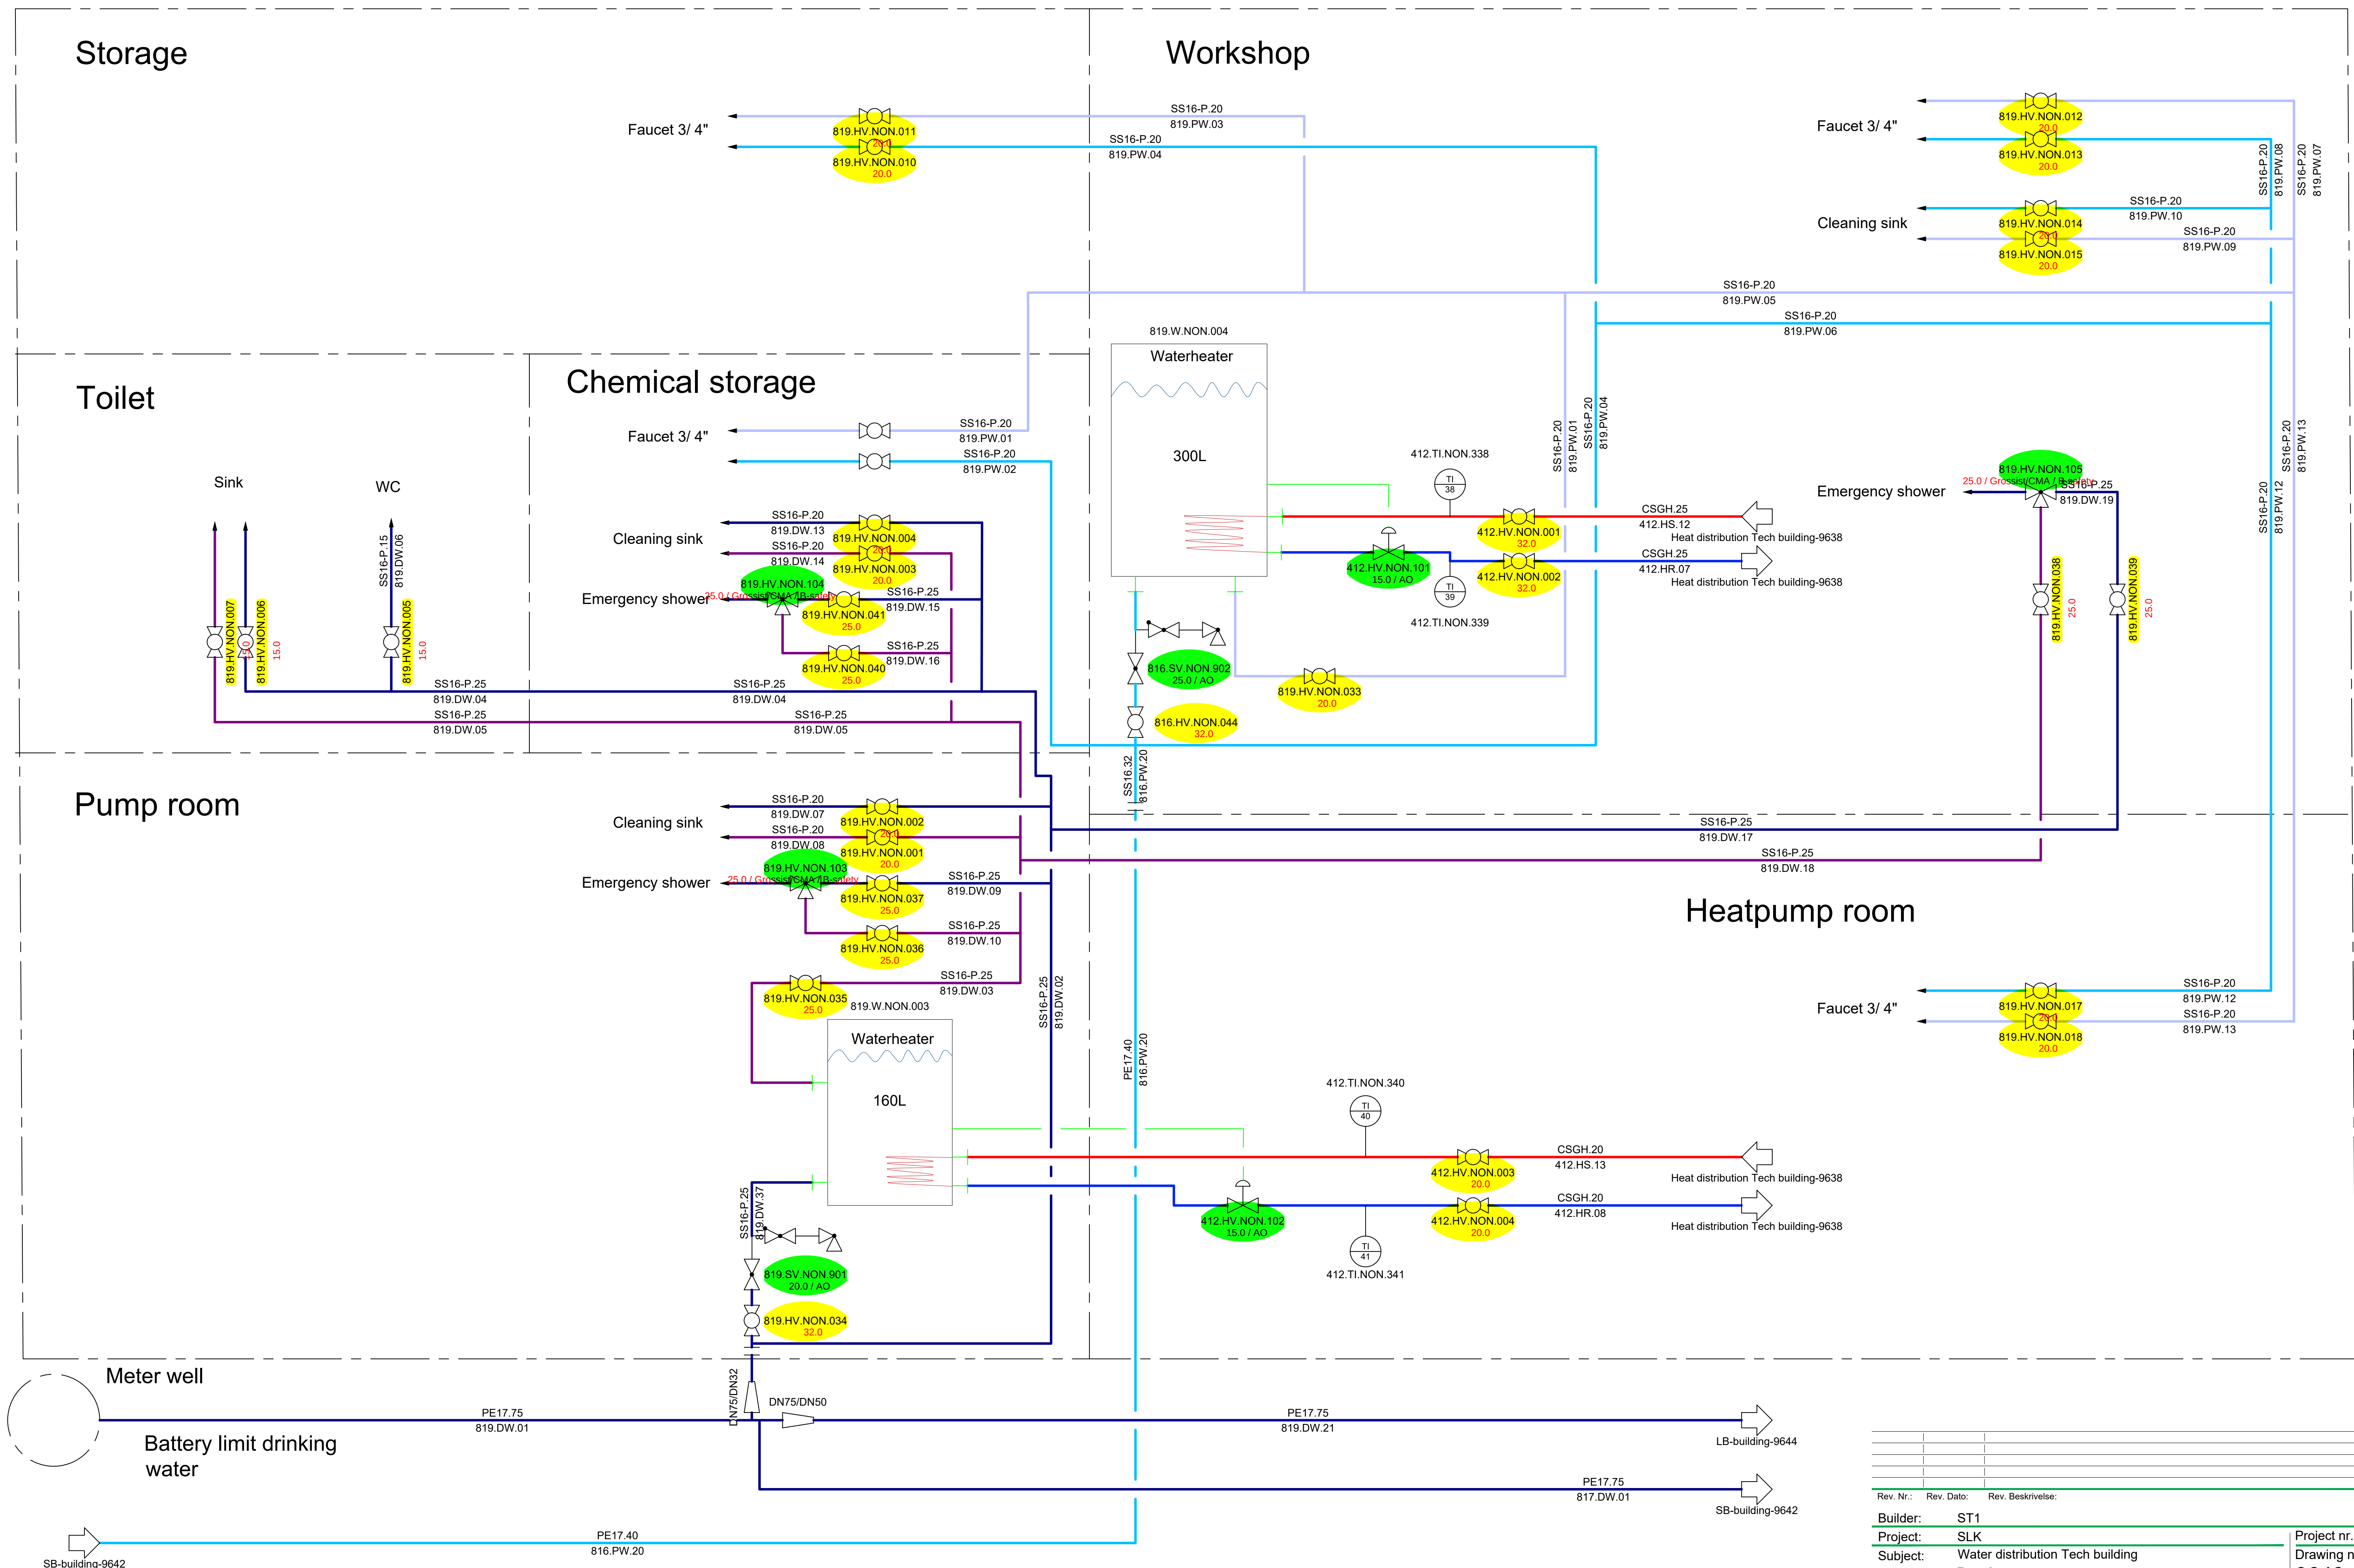



Rev. Nr.:	Rev. Dato:	Rev. Beskrivelse:
Builder:	ST1	
Project:	SLK	
Subject:	Water distribution Tech building	
Rev. 6		
Int.:MDC	QC:CM	APP.:
		Date: 15-10-2025
LUNDSBY RENEWABLE SOLUTIONS		
Lundsby Biogas A/S, Hjarbækvej 65, 8831 Løgstrup Tlf.: +45 96 49 43 00 info@lundsbybiogas.dk		
Denne tegning er underlagt copyright og må ikke reproduceres uden tilladelse fra Lundsbybiogas A/S		
Project nr.: 1768 Drawing nr.: 9643		FORMAT: A1

LB-building


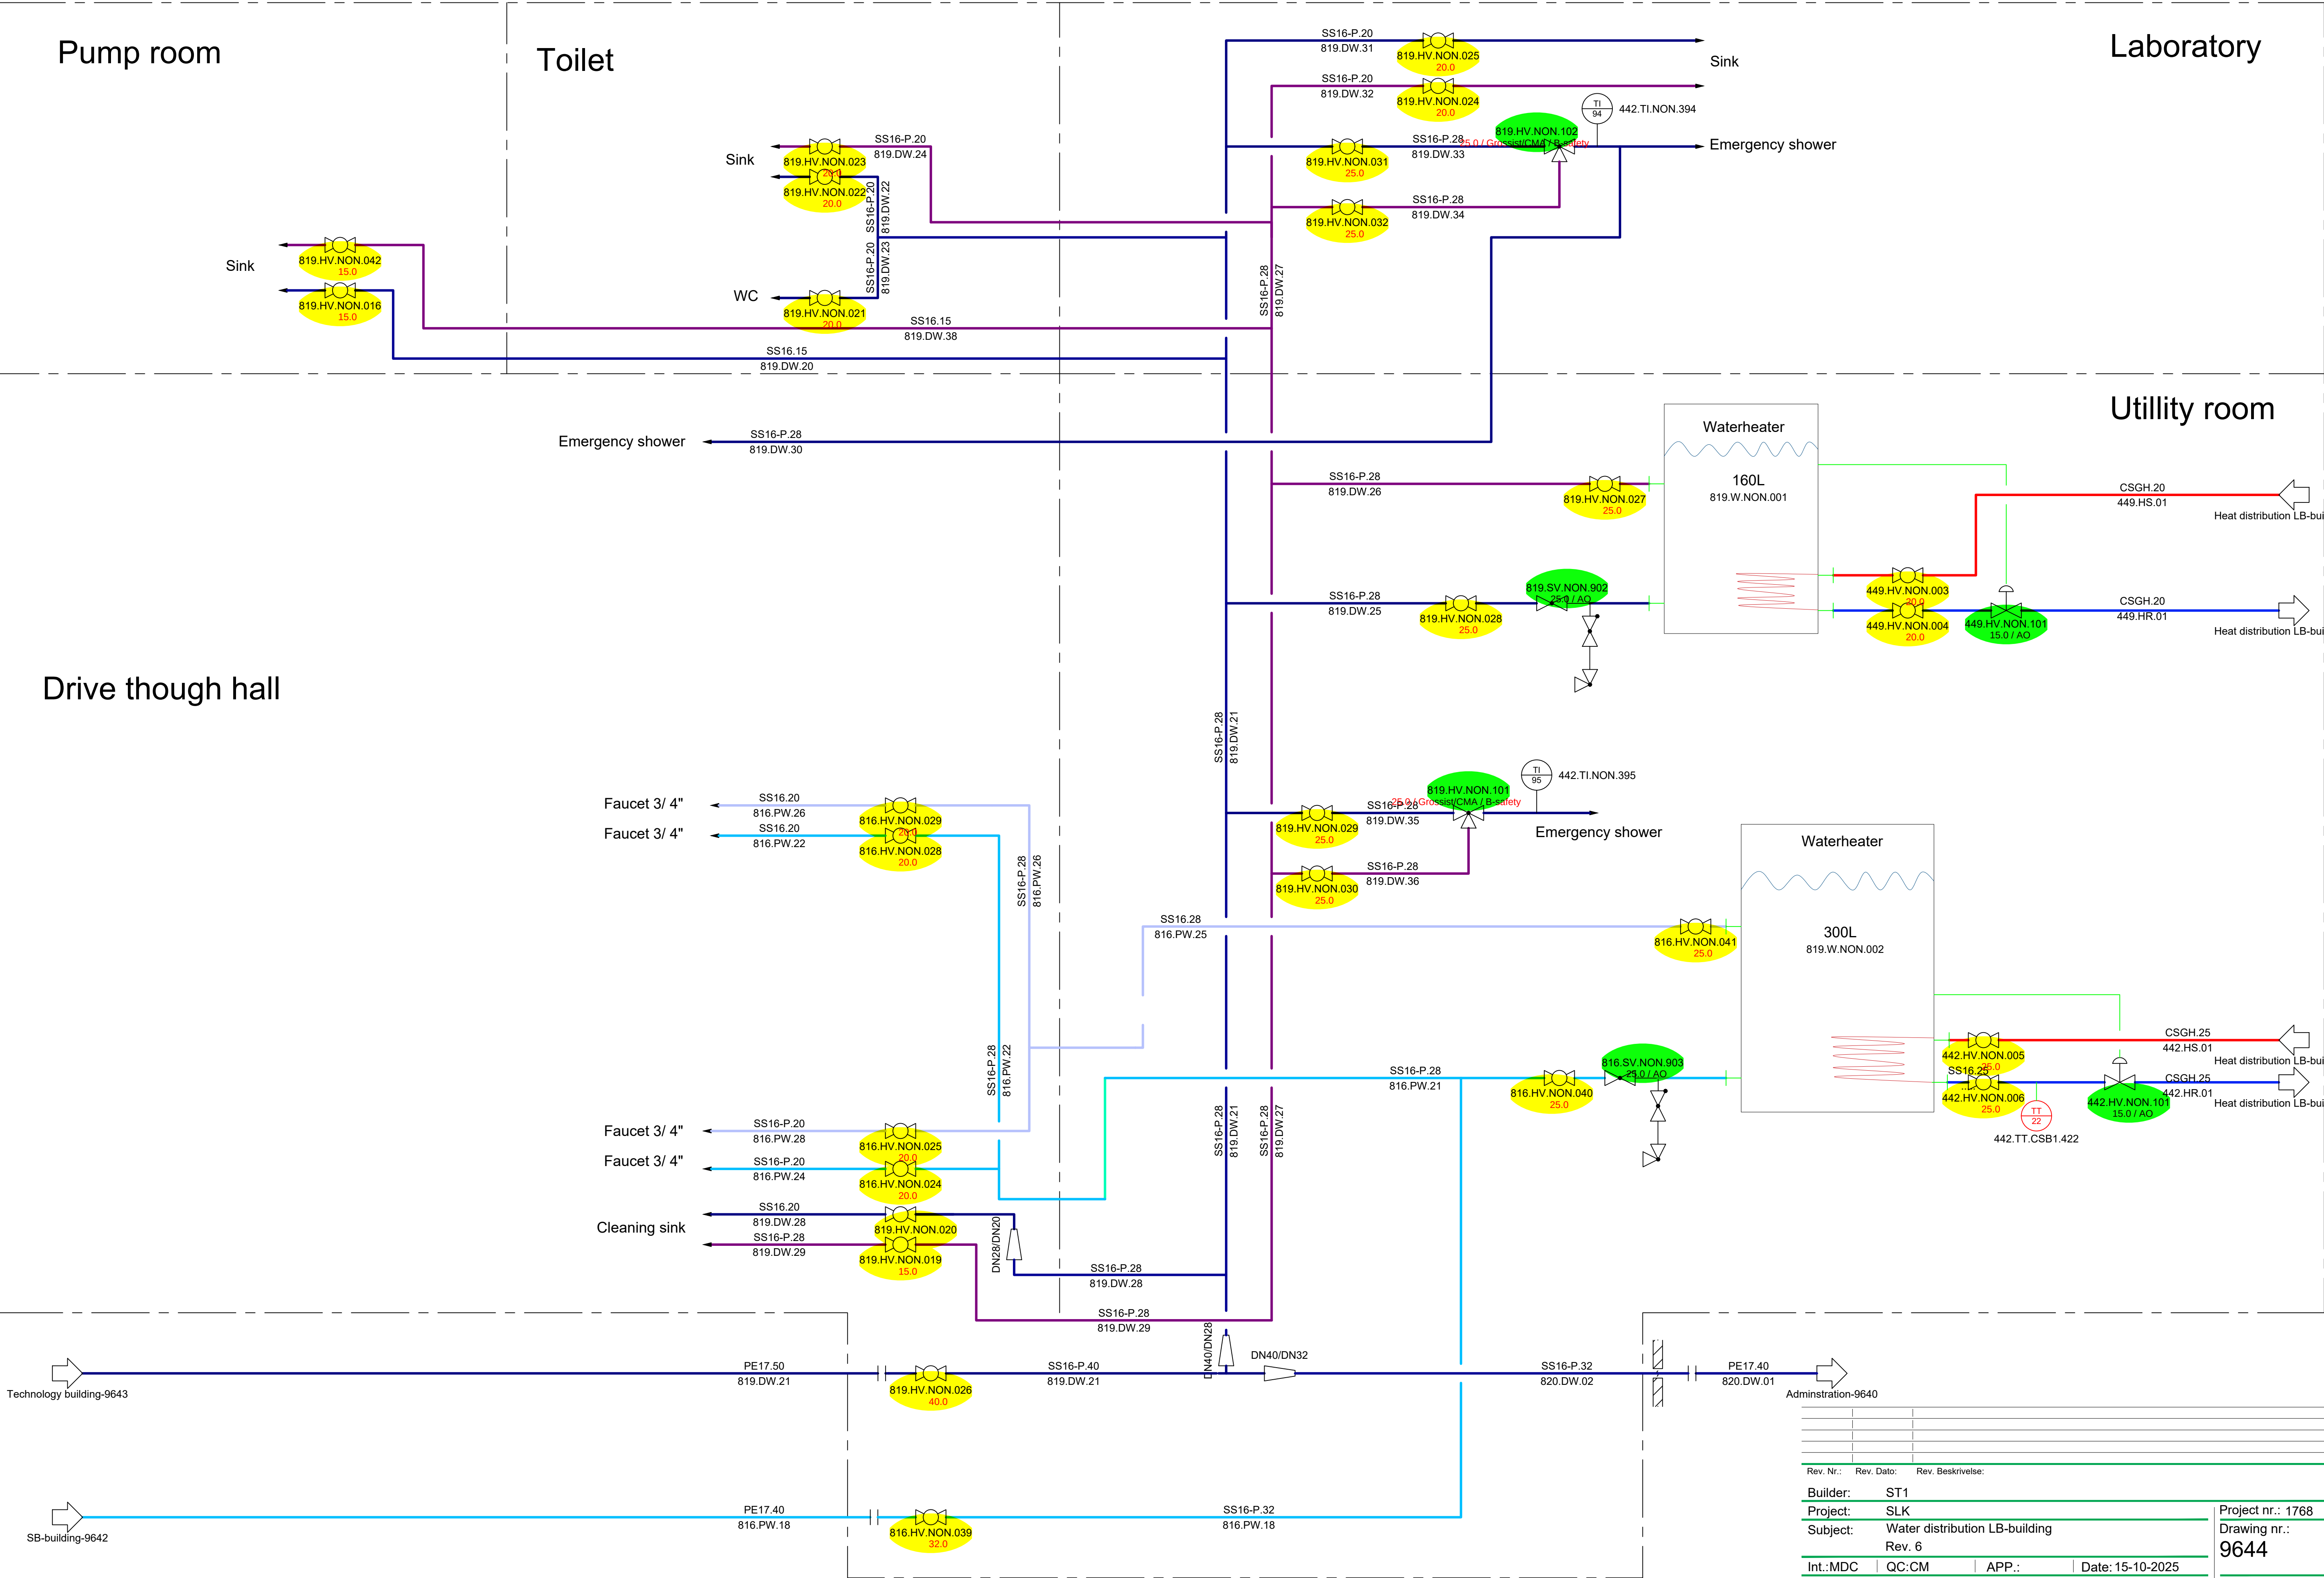


Rev. Nr.:	Rev. Dato:	Rev. Beskrivelse:
Builder:	ST1	
Project:	SLK	
Subject:	Water distribution LB-building	
Rev.:	6	
Int.:MDC	QC:CM	APP.:
Date:	15-10-2025	
LUNDSBY RENEWABLE SOLUTIONS		
Lundsby Biogas A/S, Hjarbækvej 65, 8831 Løgstrup Tlf.: +45 96 49 43 00 info@lundsbybiogas.dk Denne tegning er underlagt copyright og må ikke reproduceres uden tilladelse fra Lundsbybiogas A/S		
Project nr.: 1768 Drawing nr.: 9644		FORMAT: A1


Pumphouse 1

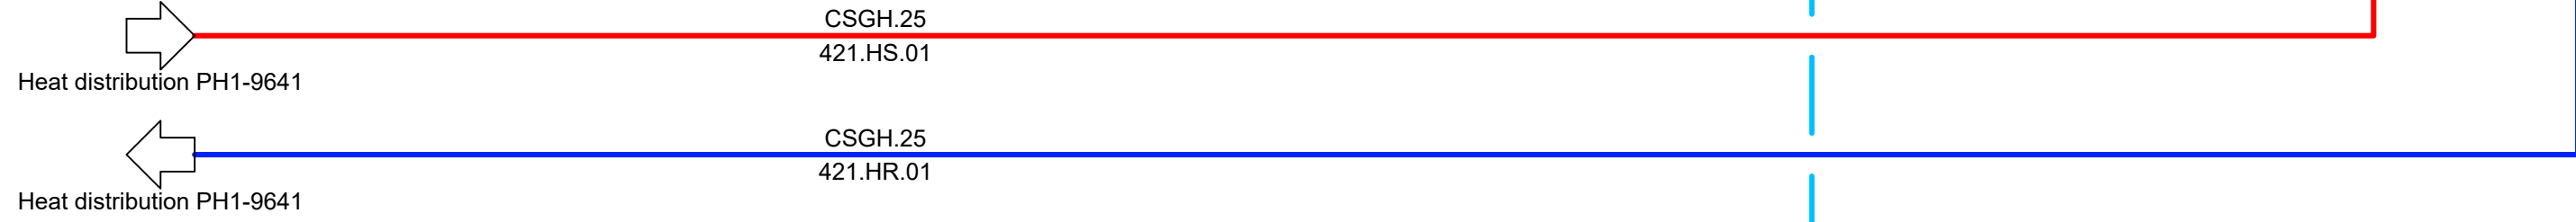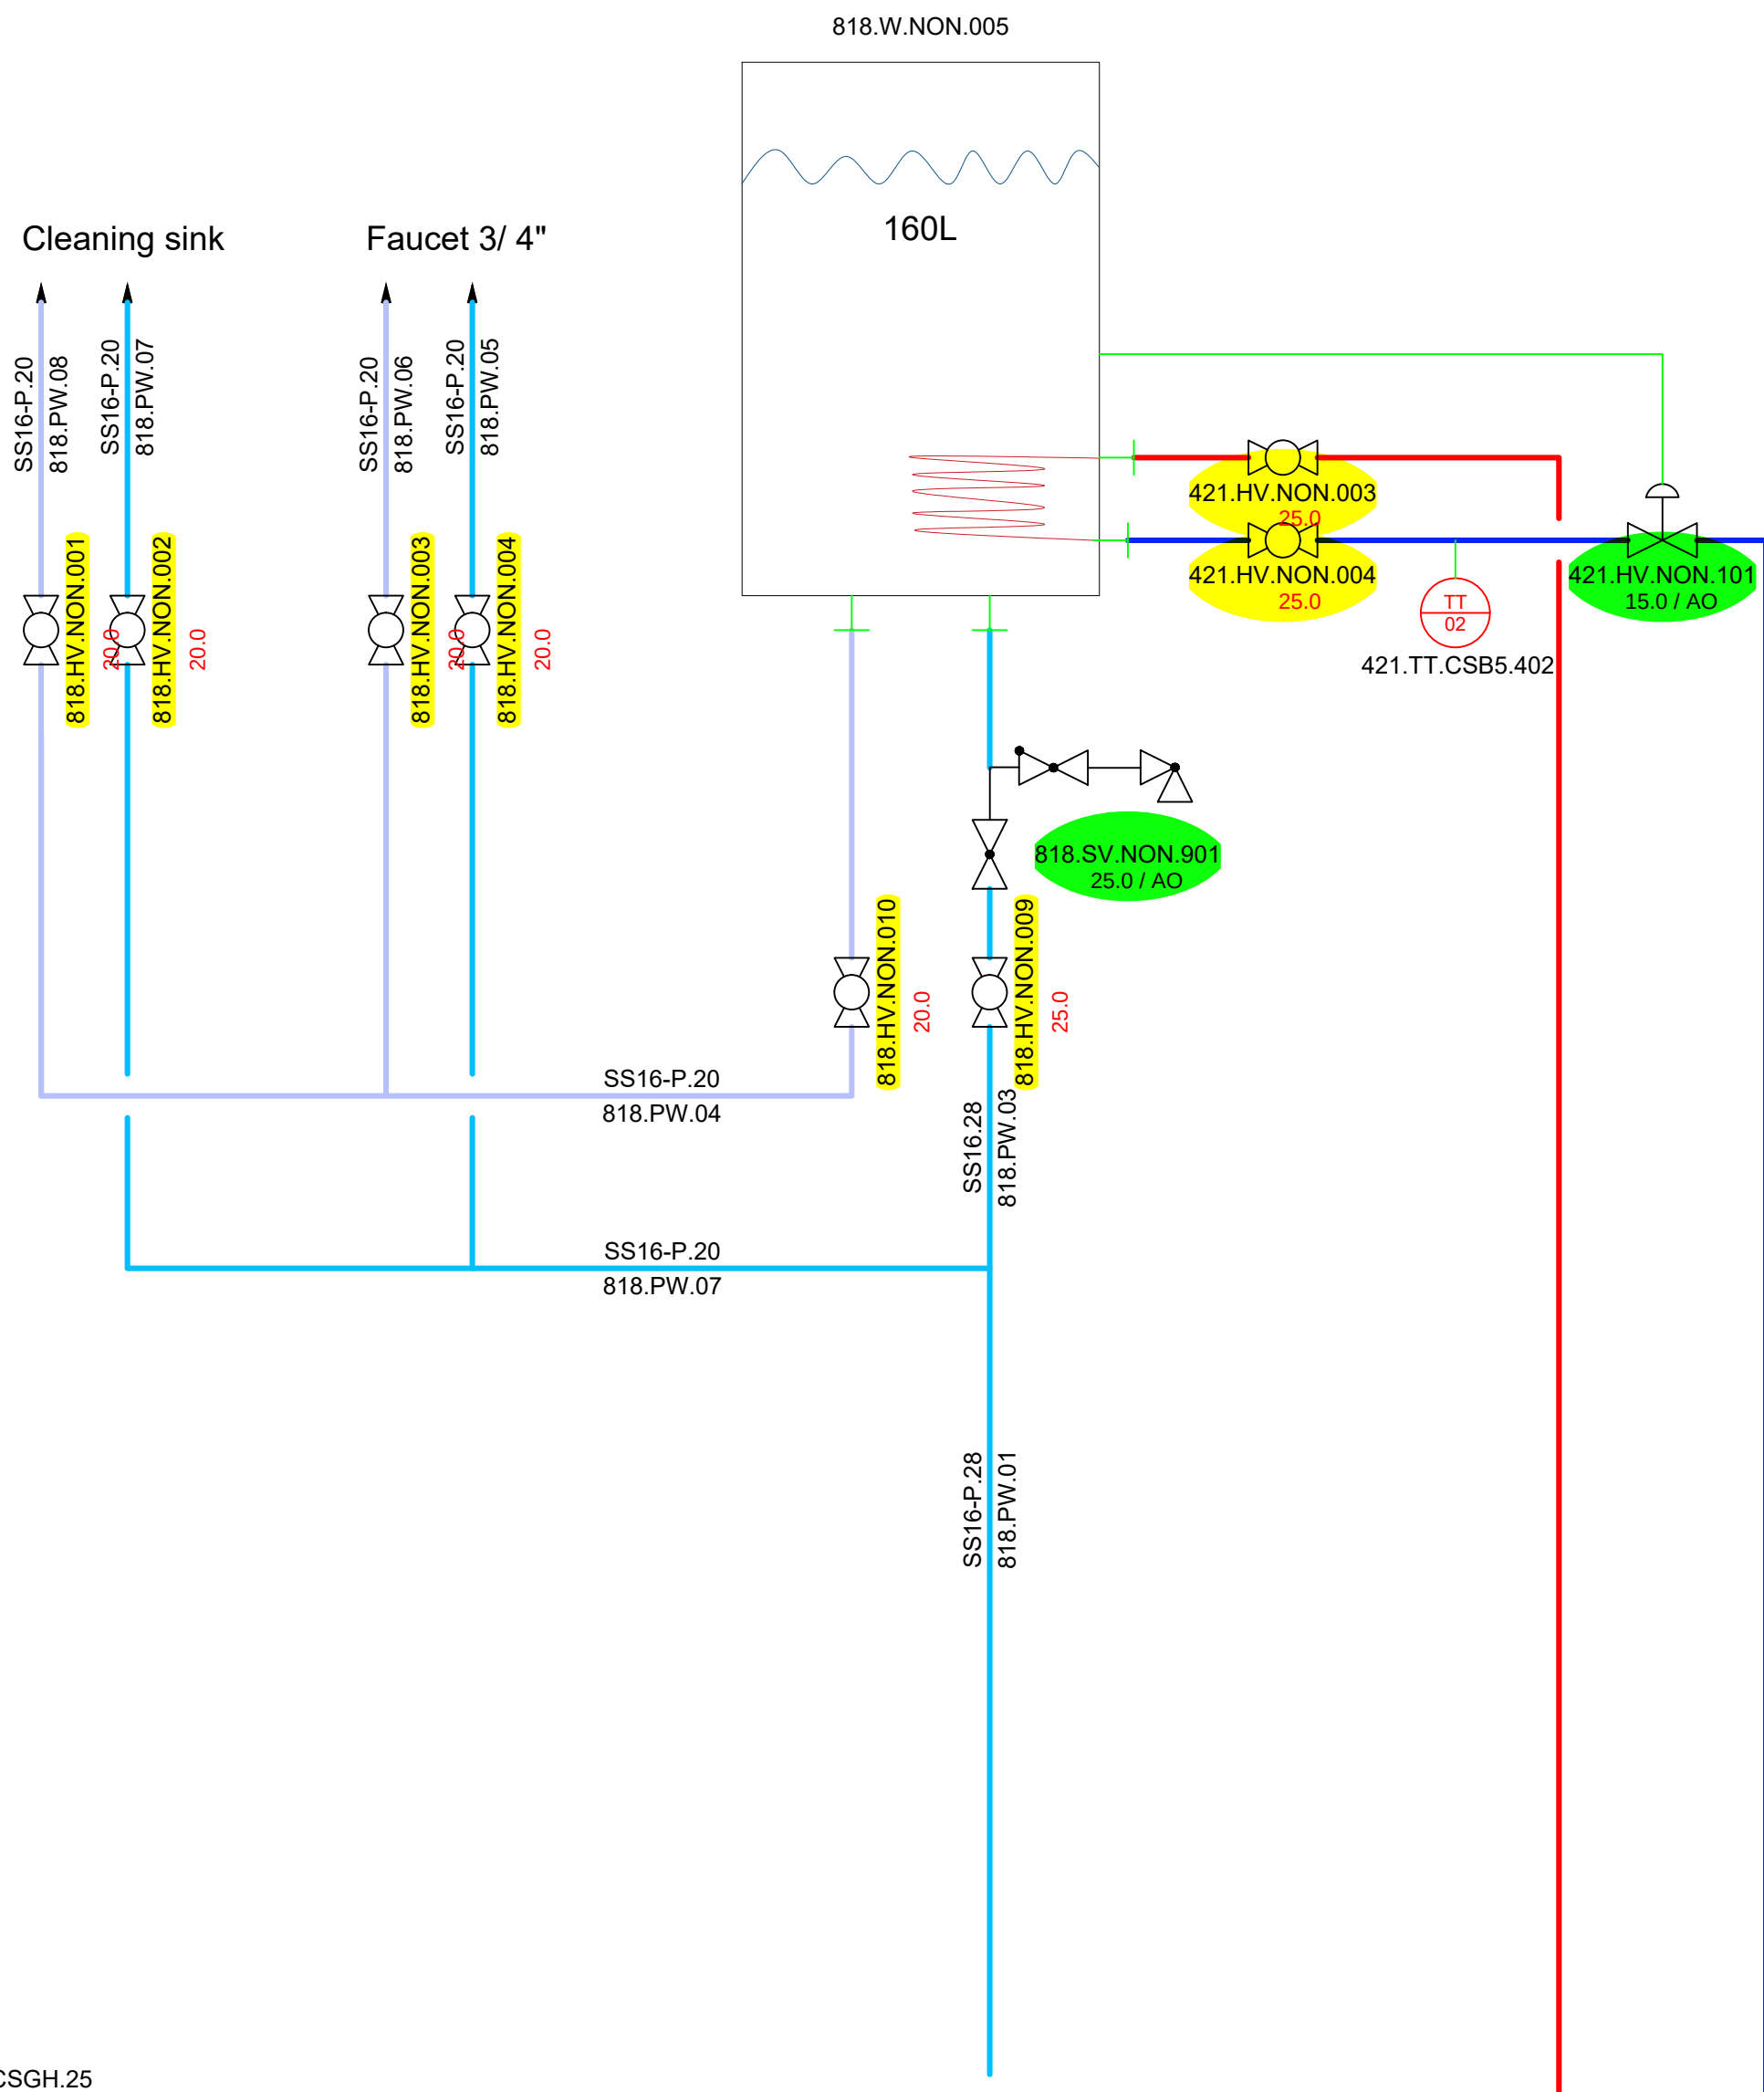


Pumphouse 2

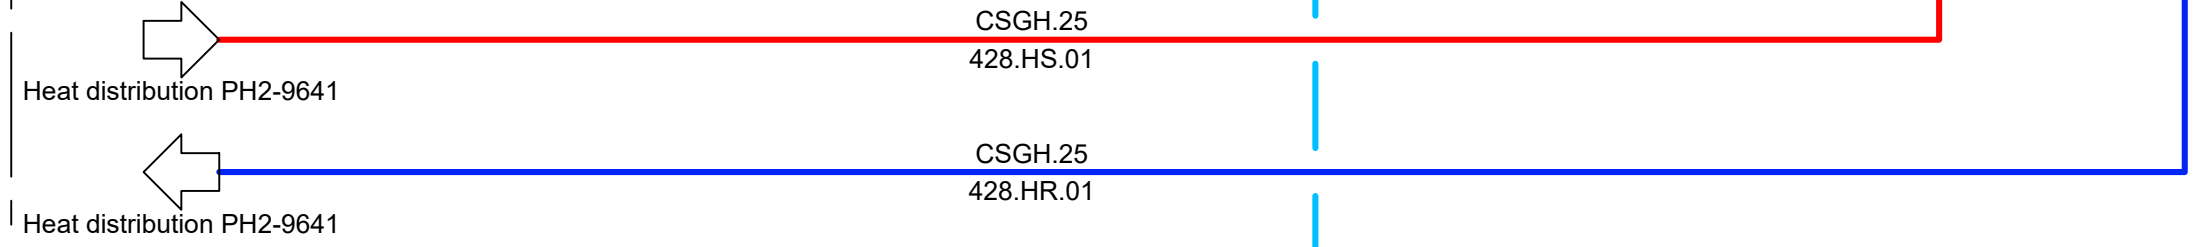
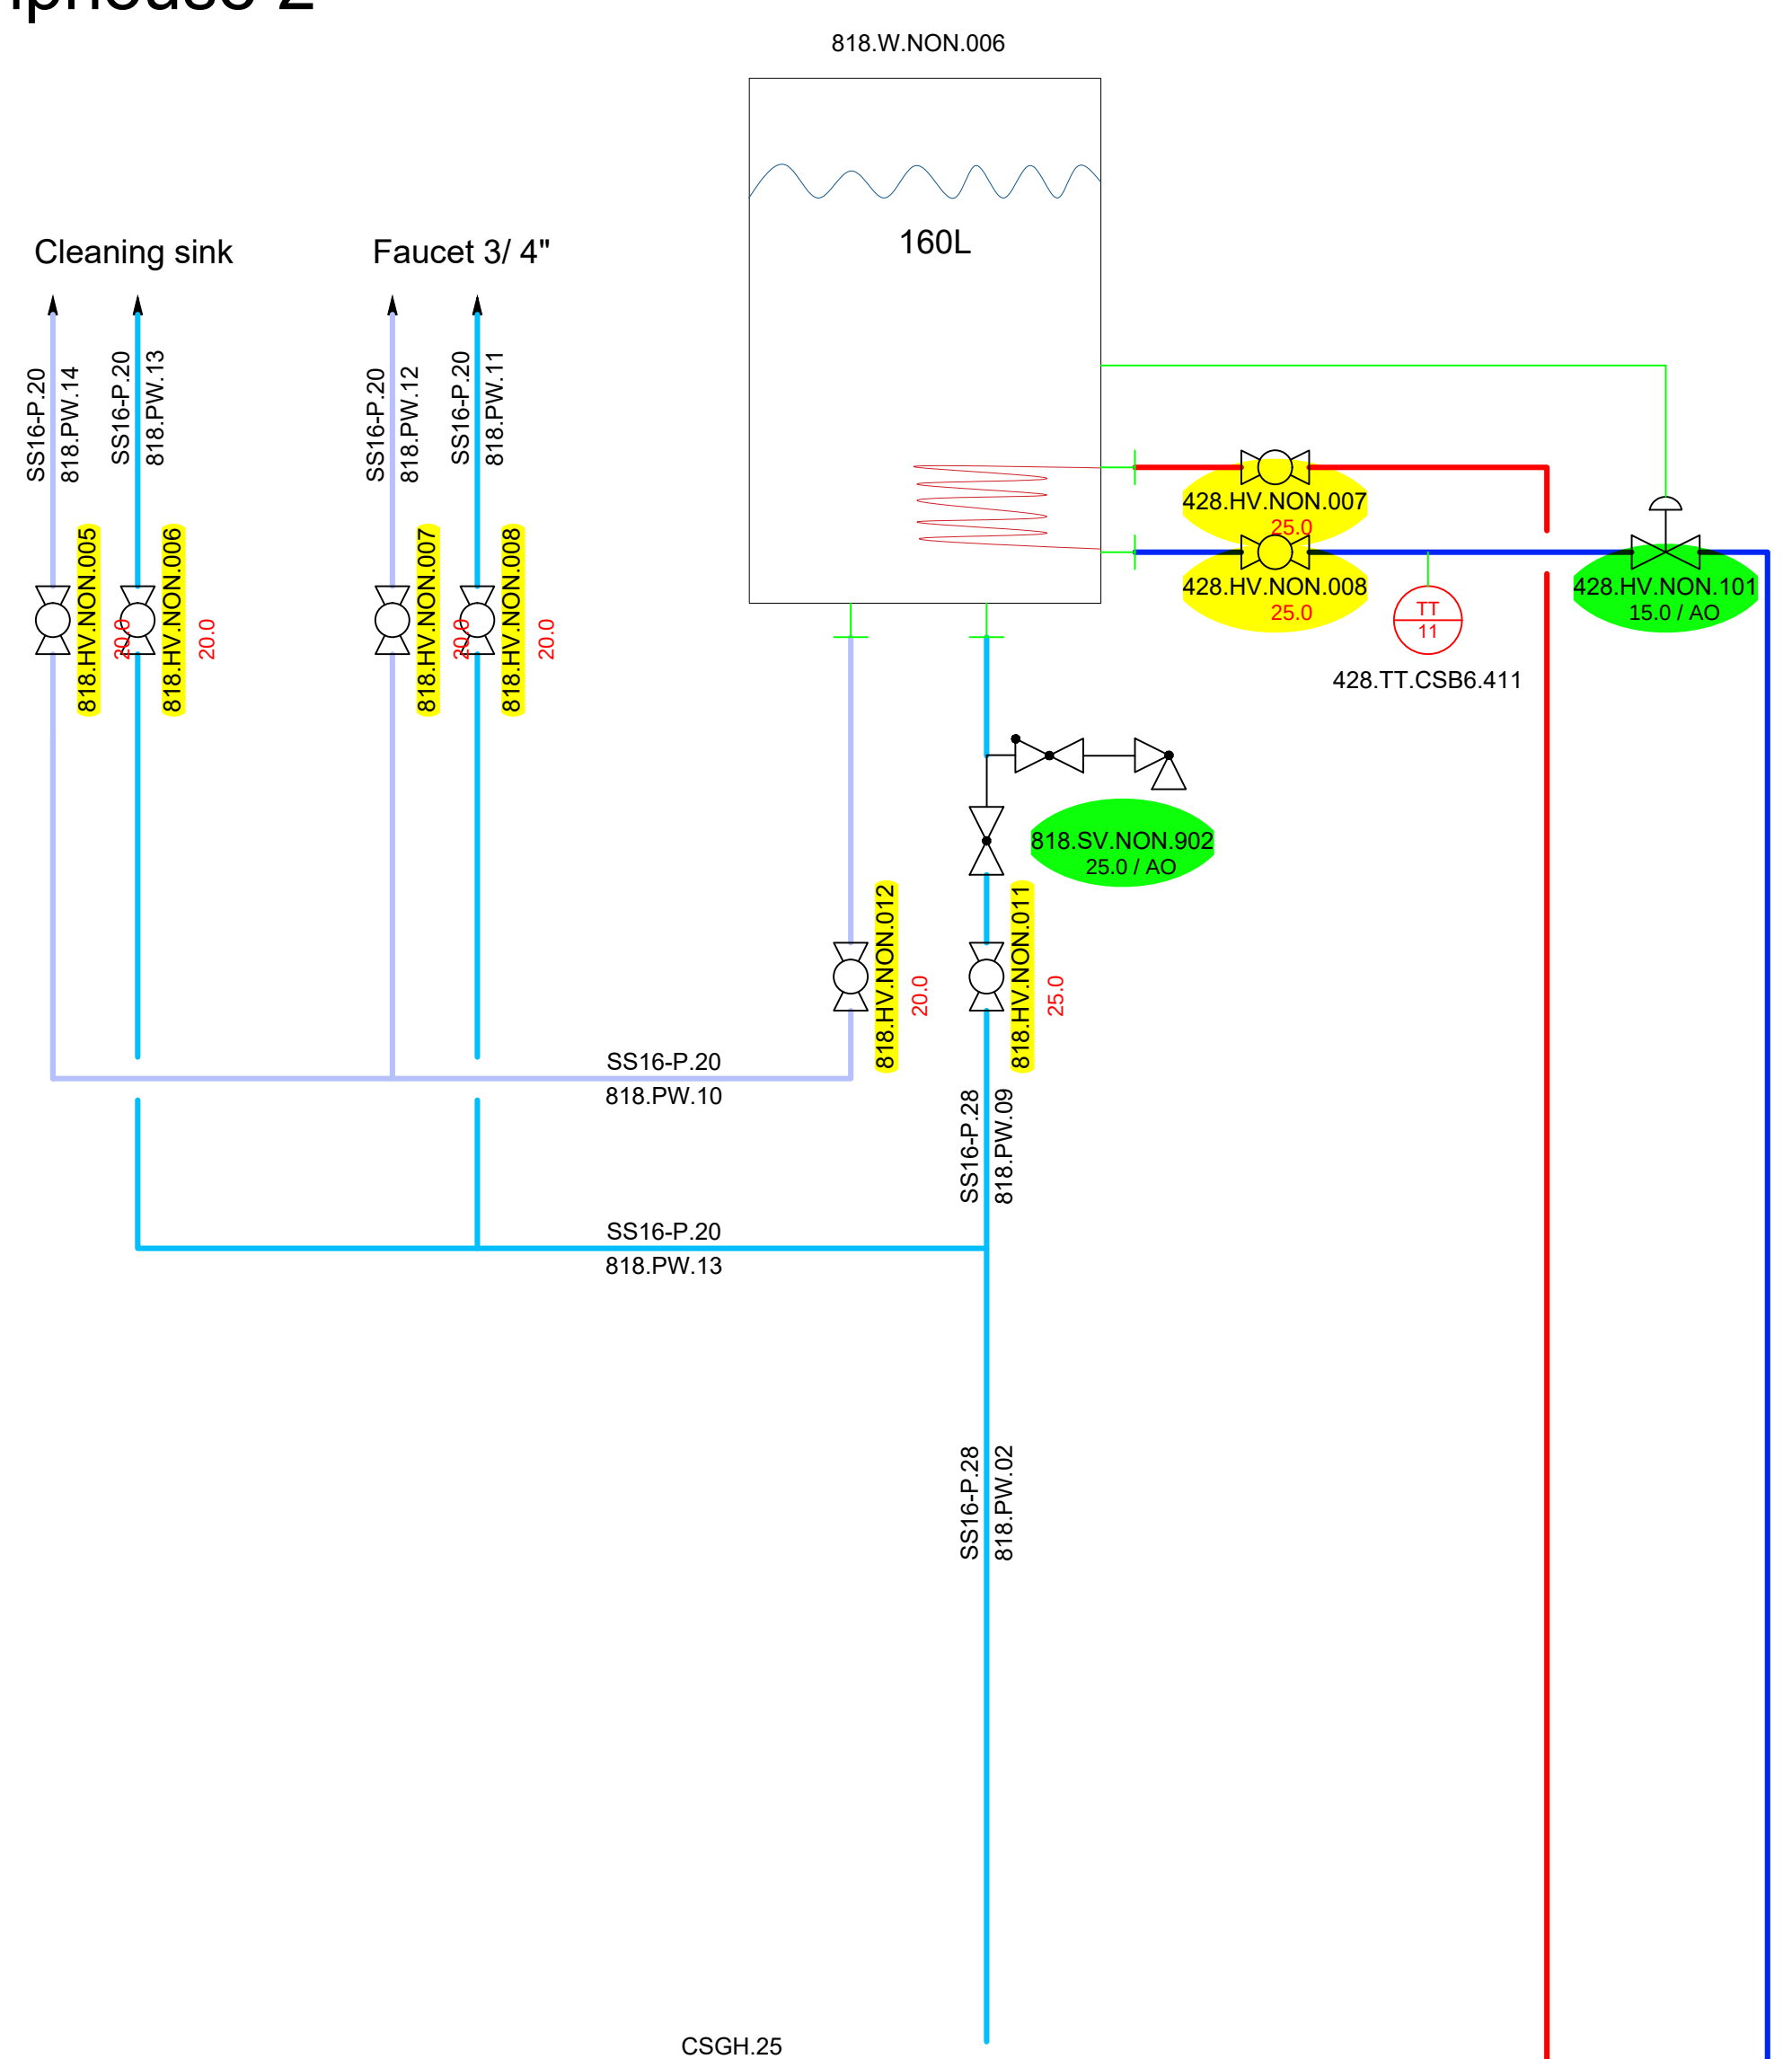


Rev. Nr.:	Rev. Dato:	Rev. Beskrivelse:
Builder:	ST1	
Project:	SLK	
Subject:	Water distribution pumphouse 1 & 2	
Rev. 6		
Int.:MDC	QC:CM	APP.: Date: 15-10-2025
LUNDSBY RENEWABLE SOLUTIONS		
Lundsby Biogas A/S, Hjarbækvej 65, 8831 Løgstrup Tlf.: +45 96 49 43 00 info@lundsbybiogas.dk		
Denne tegning er underlagt copyright op på ikke reproduceres uden tilladelse fra Lundsbybiogas A/S		
Project nr.: 1768		Drawing nr.: 9645
FORMAT: A1		

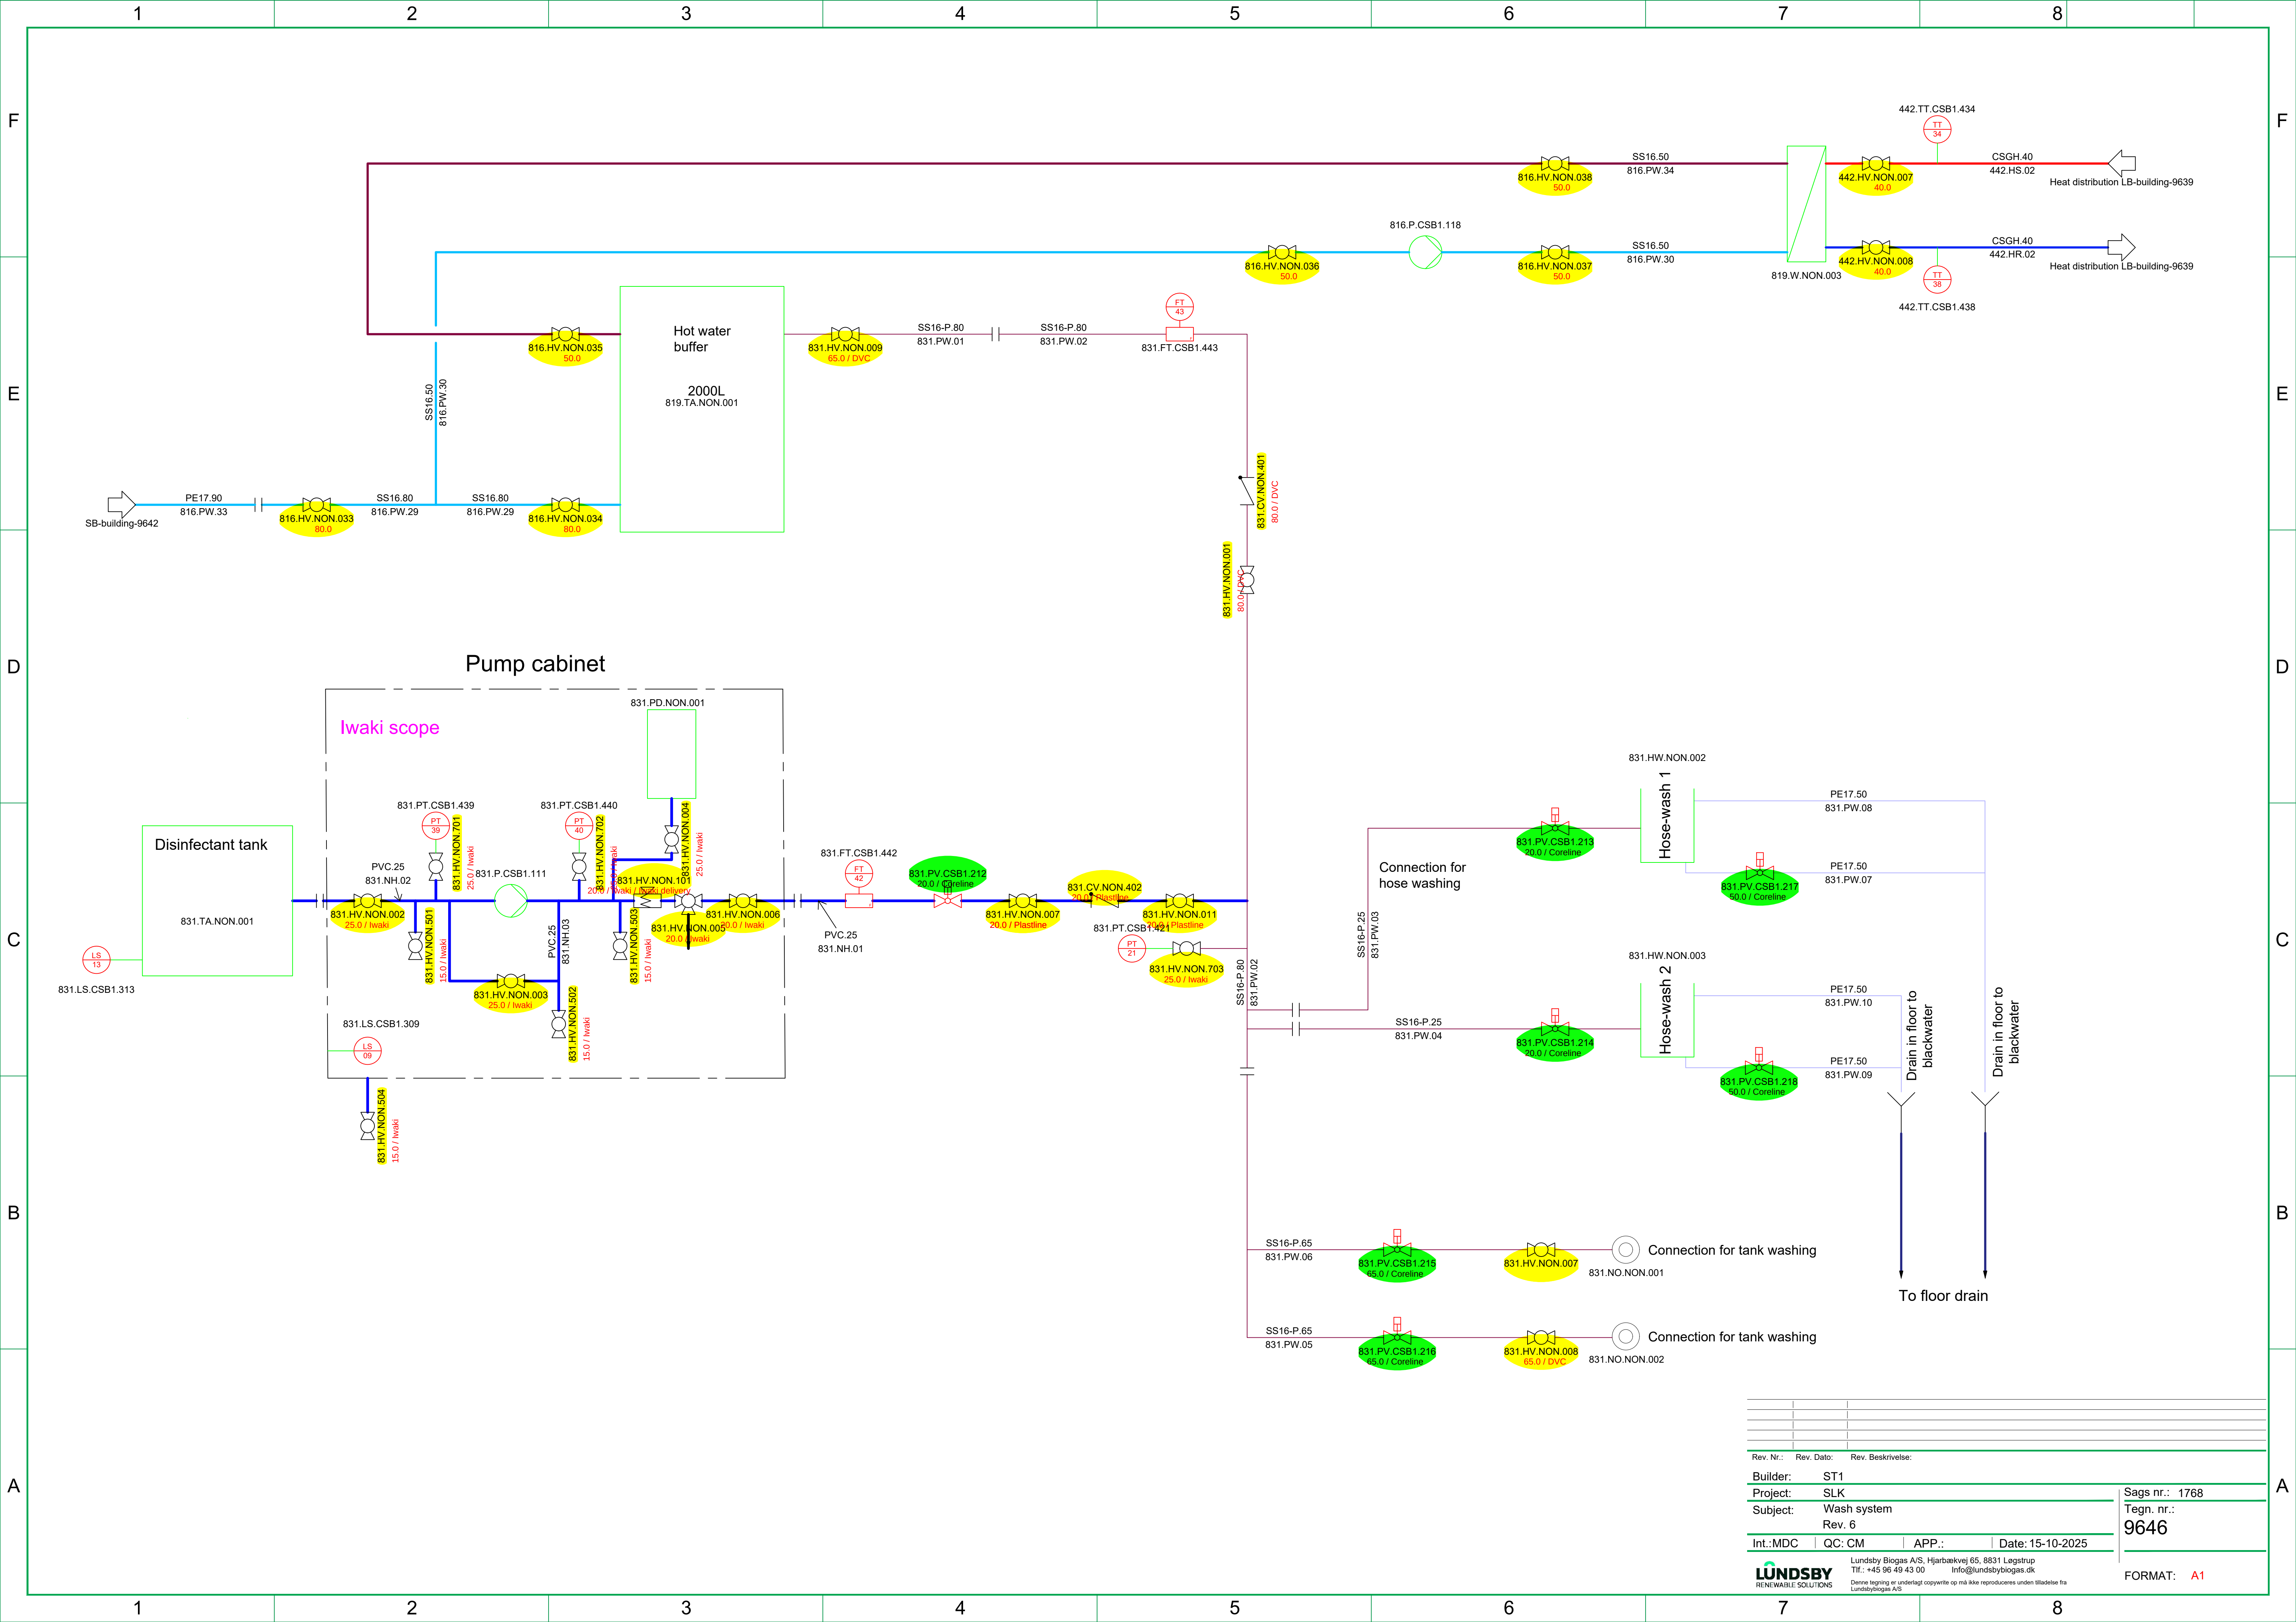


Rev. Nr.:	Rev. Dato:	Rev. Beskrivelse:	
Builder:	ST1		
Project:	SLK		
Subject:	Wash system		
Rev. 6			
Int.:MDC	QC: CM	APP.:	Date: 15-10-2025
LUNDSBY RENEWABLE SOLUTIONS			Lundsby Biogas A/S, Hjarbækvej 65, 8831 Løgstrup Tlf.: +45 96 49 43 00 info@lundsbybiogas.dk Denne tegning er underlagt copyright op på ikke reproduceres uden tilladelse fra Lundsbybiogas A/S
Sags nr.: 1768 Tegn. nr.: 9646			FORMAT: A1

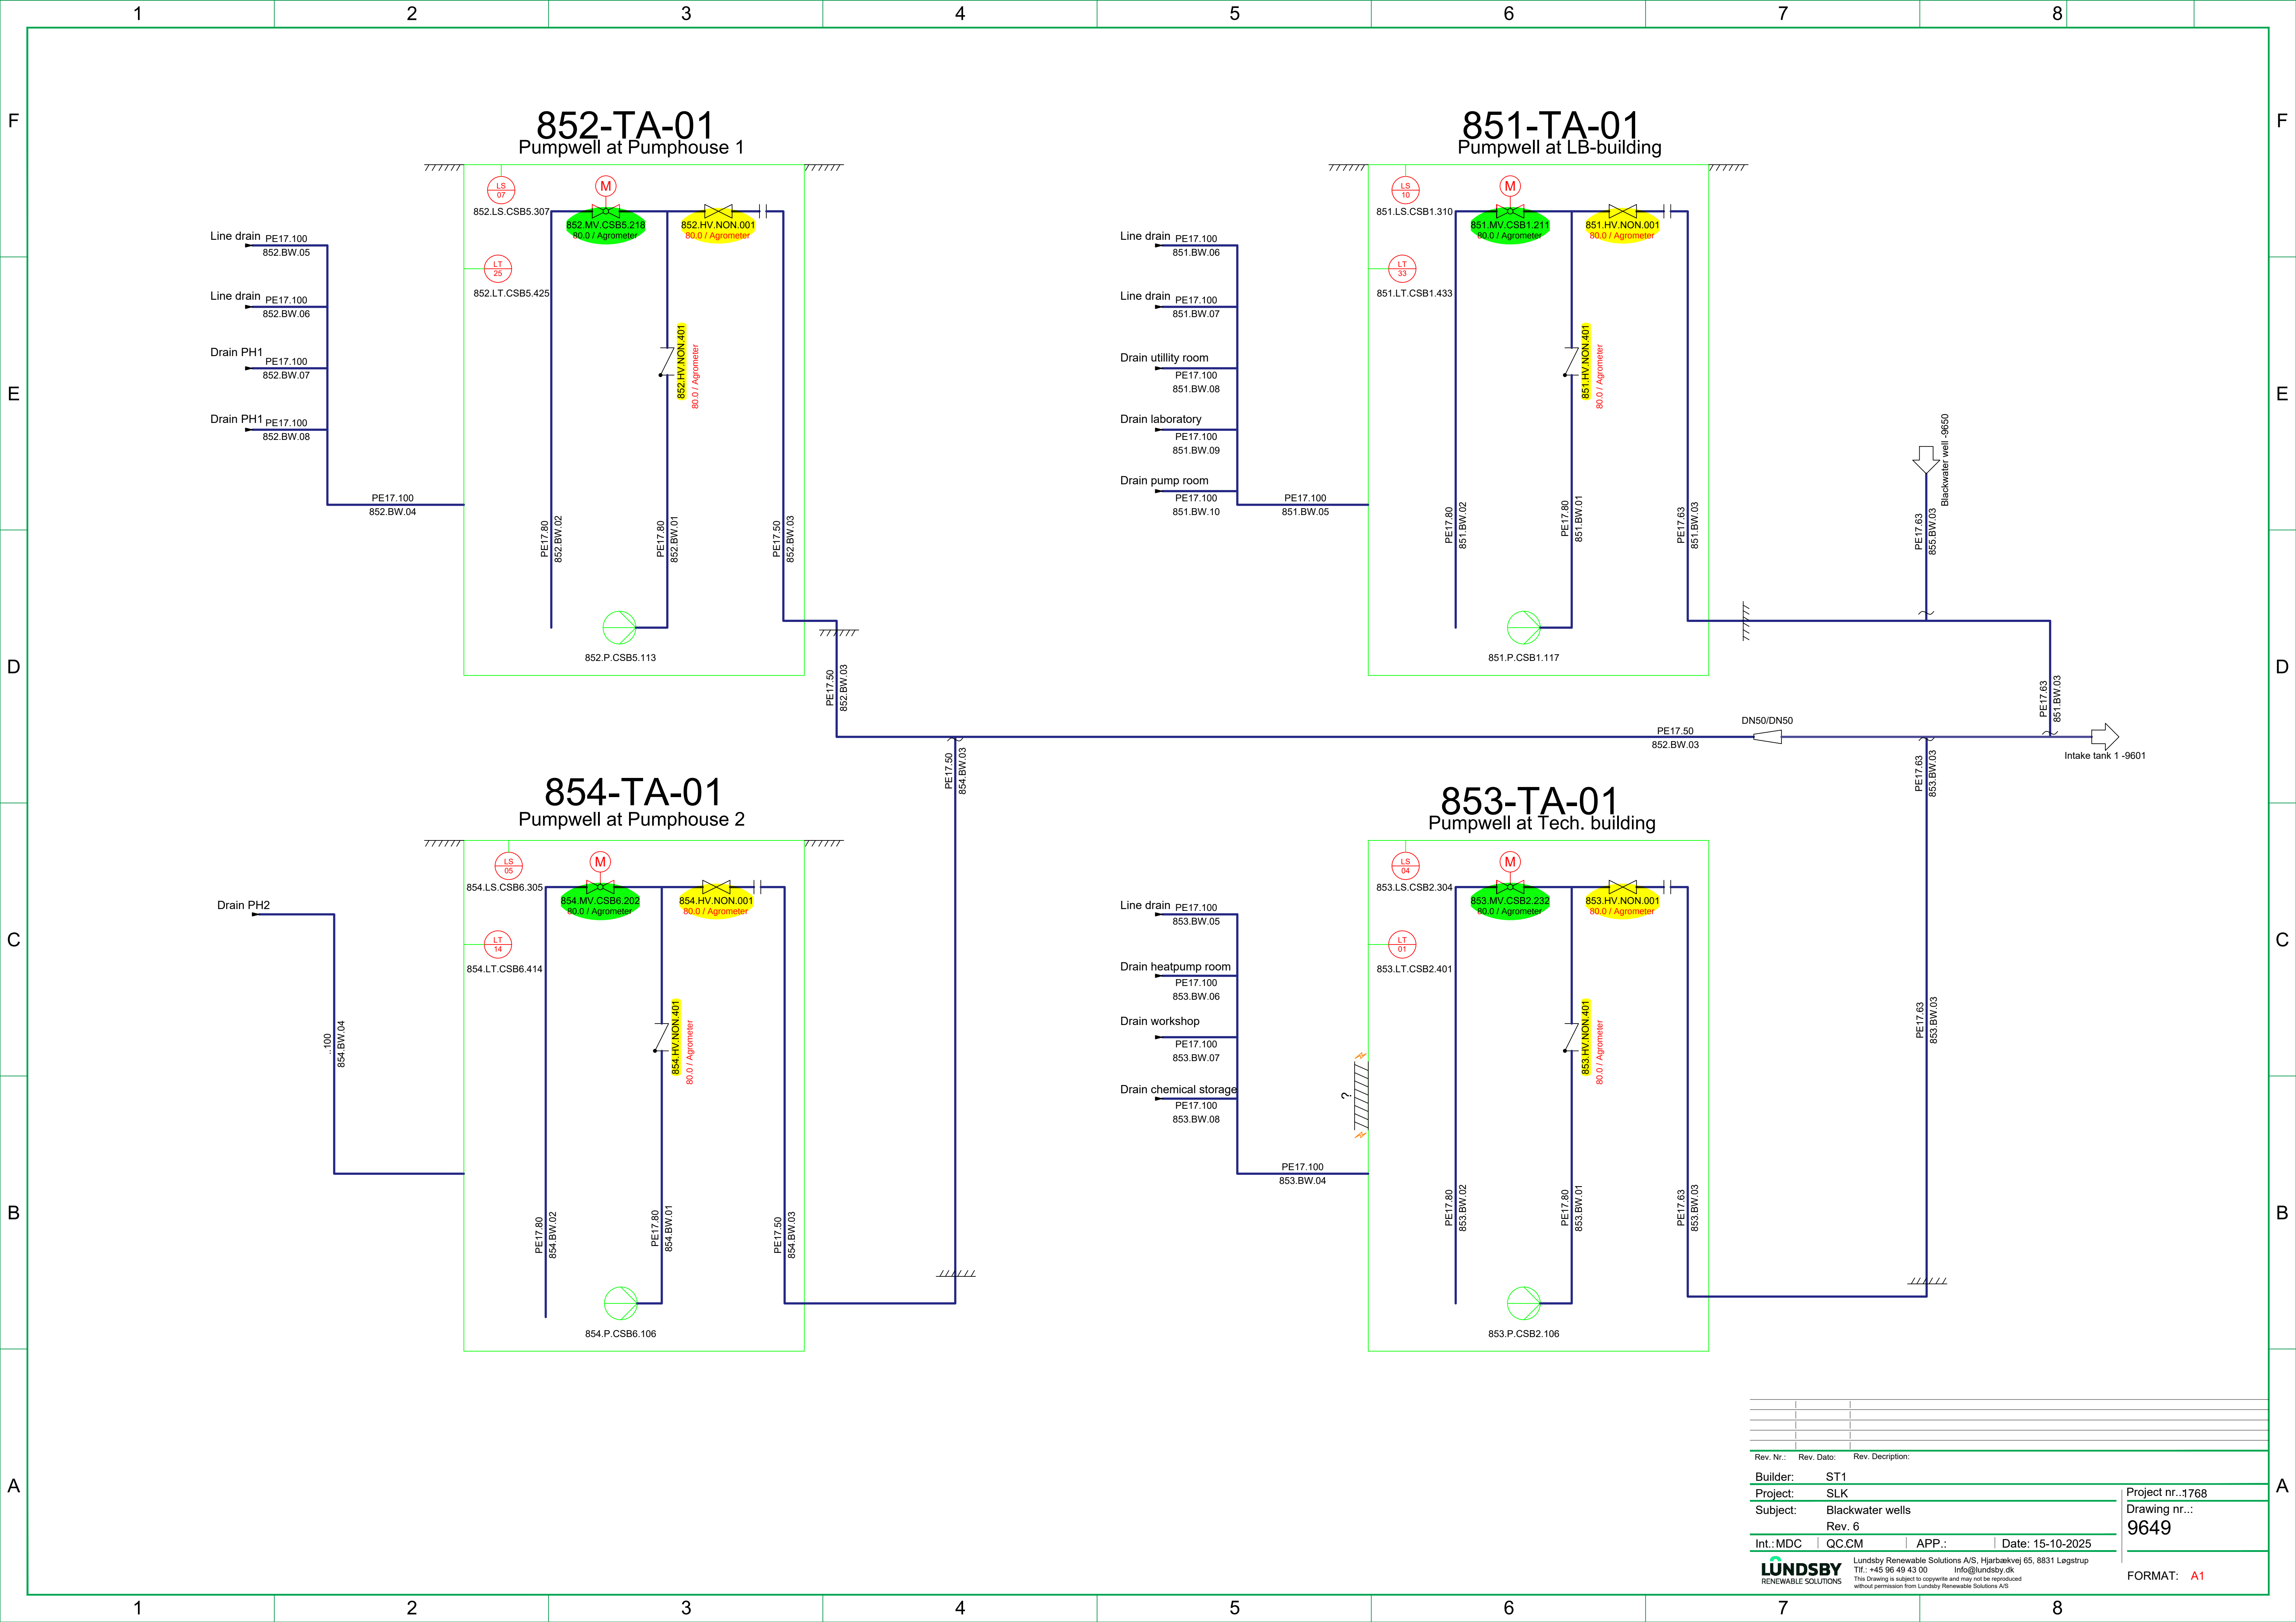

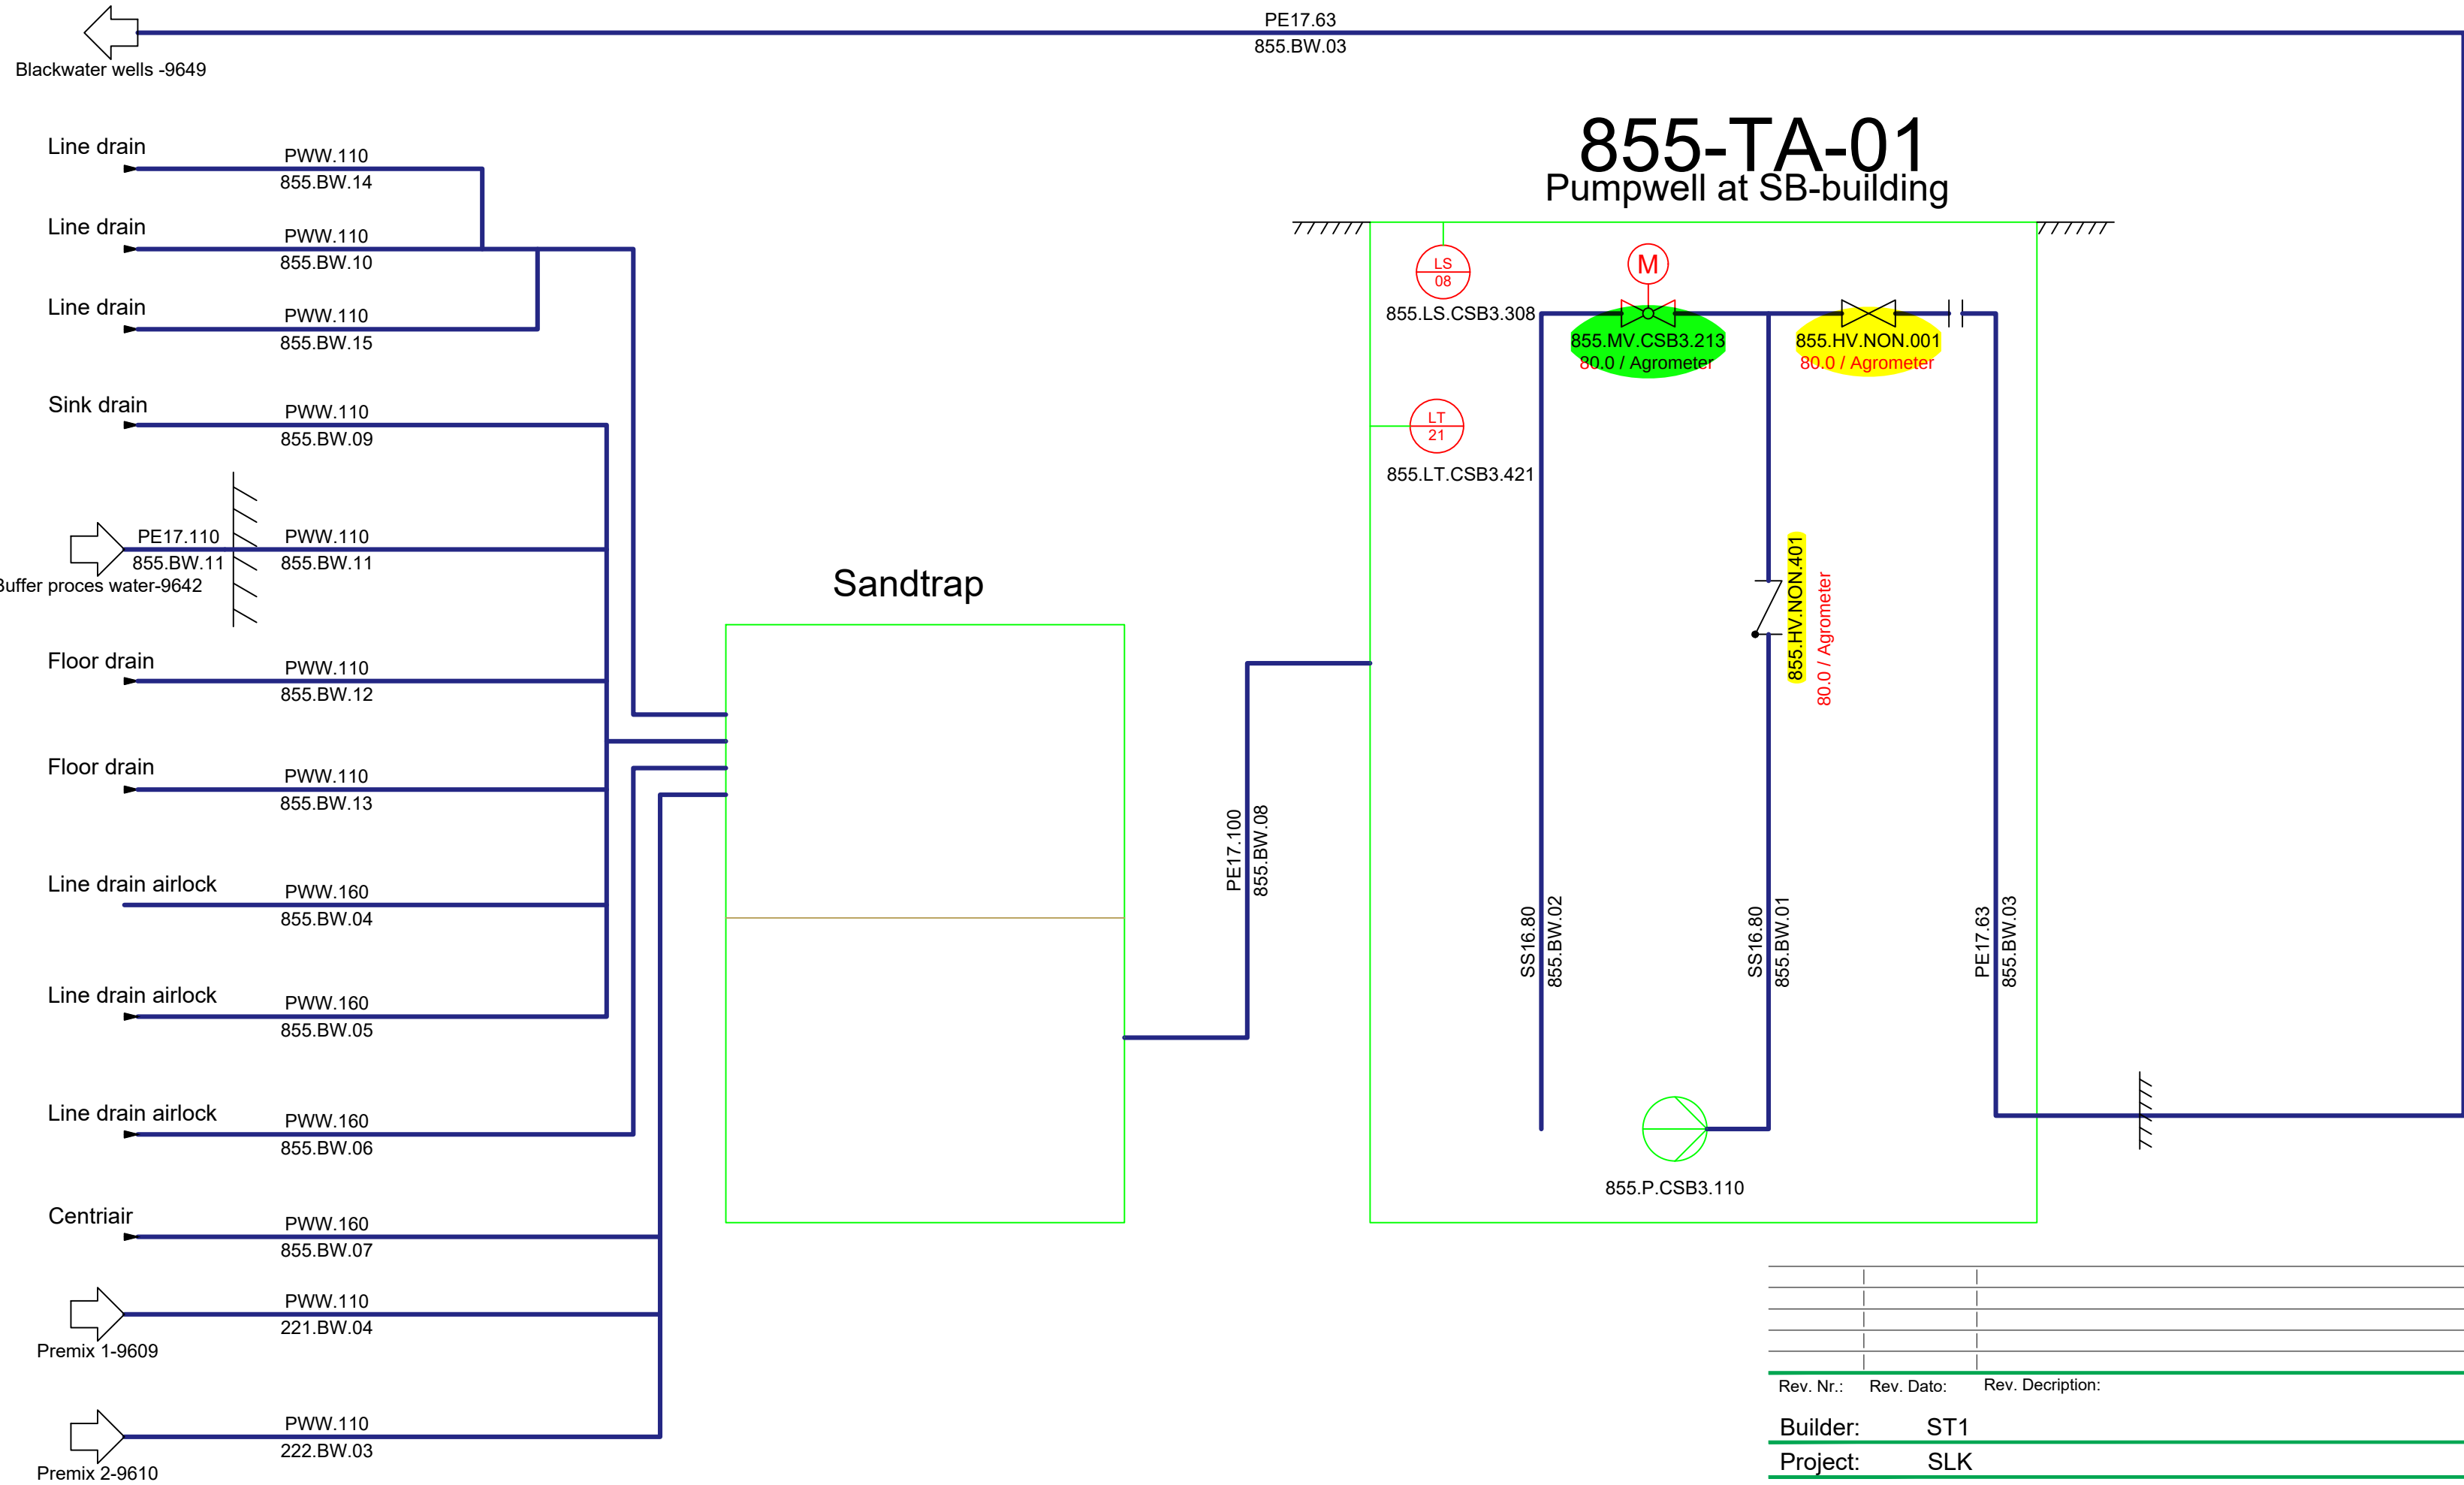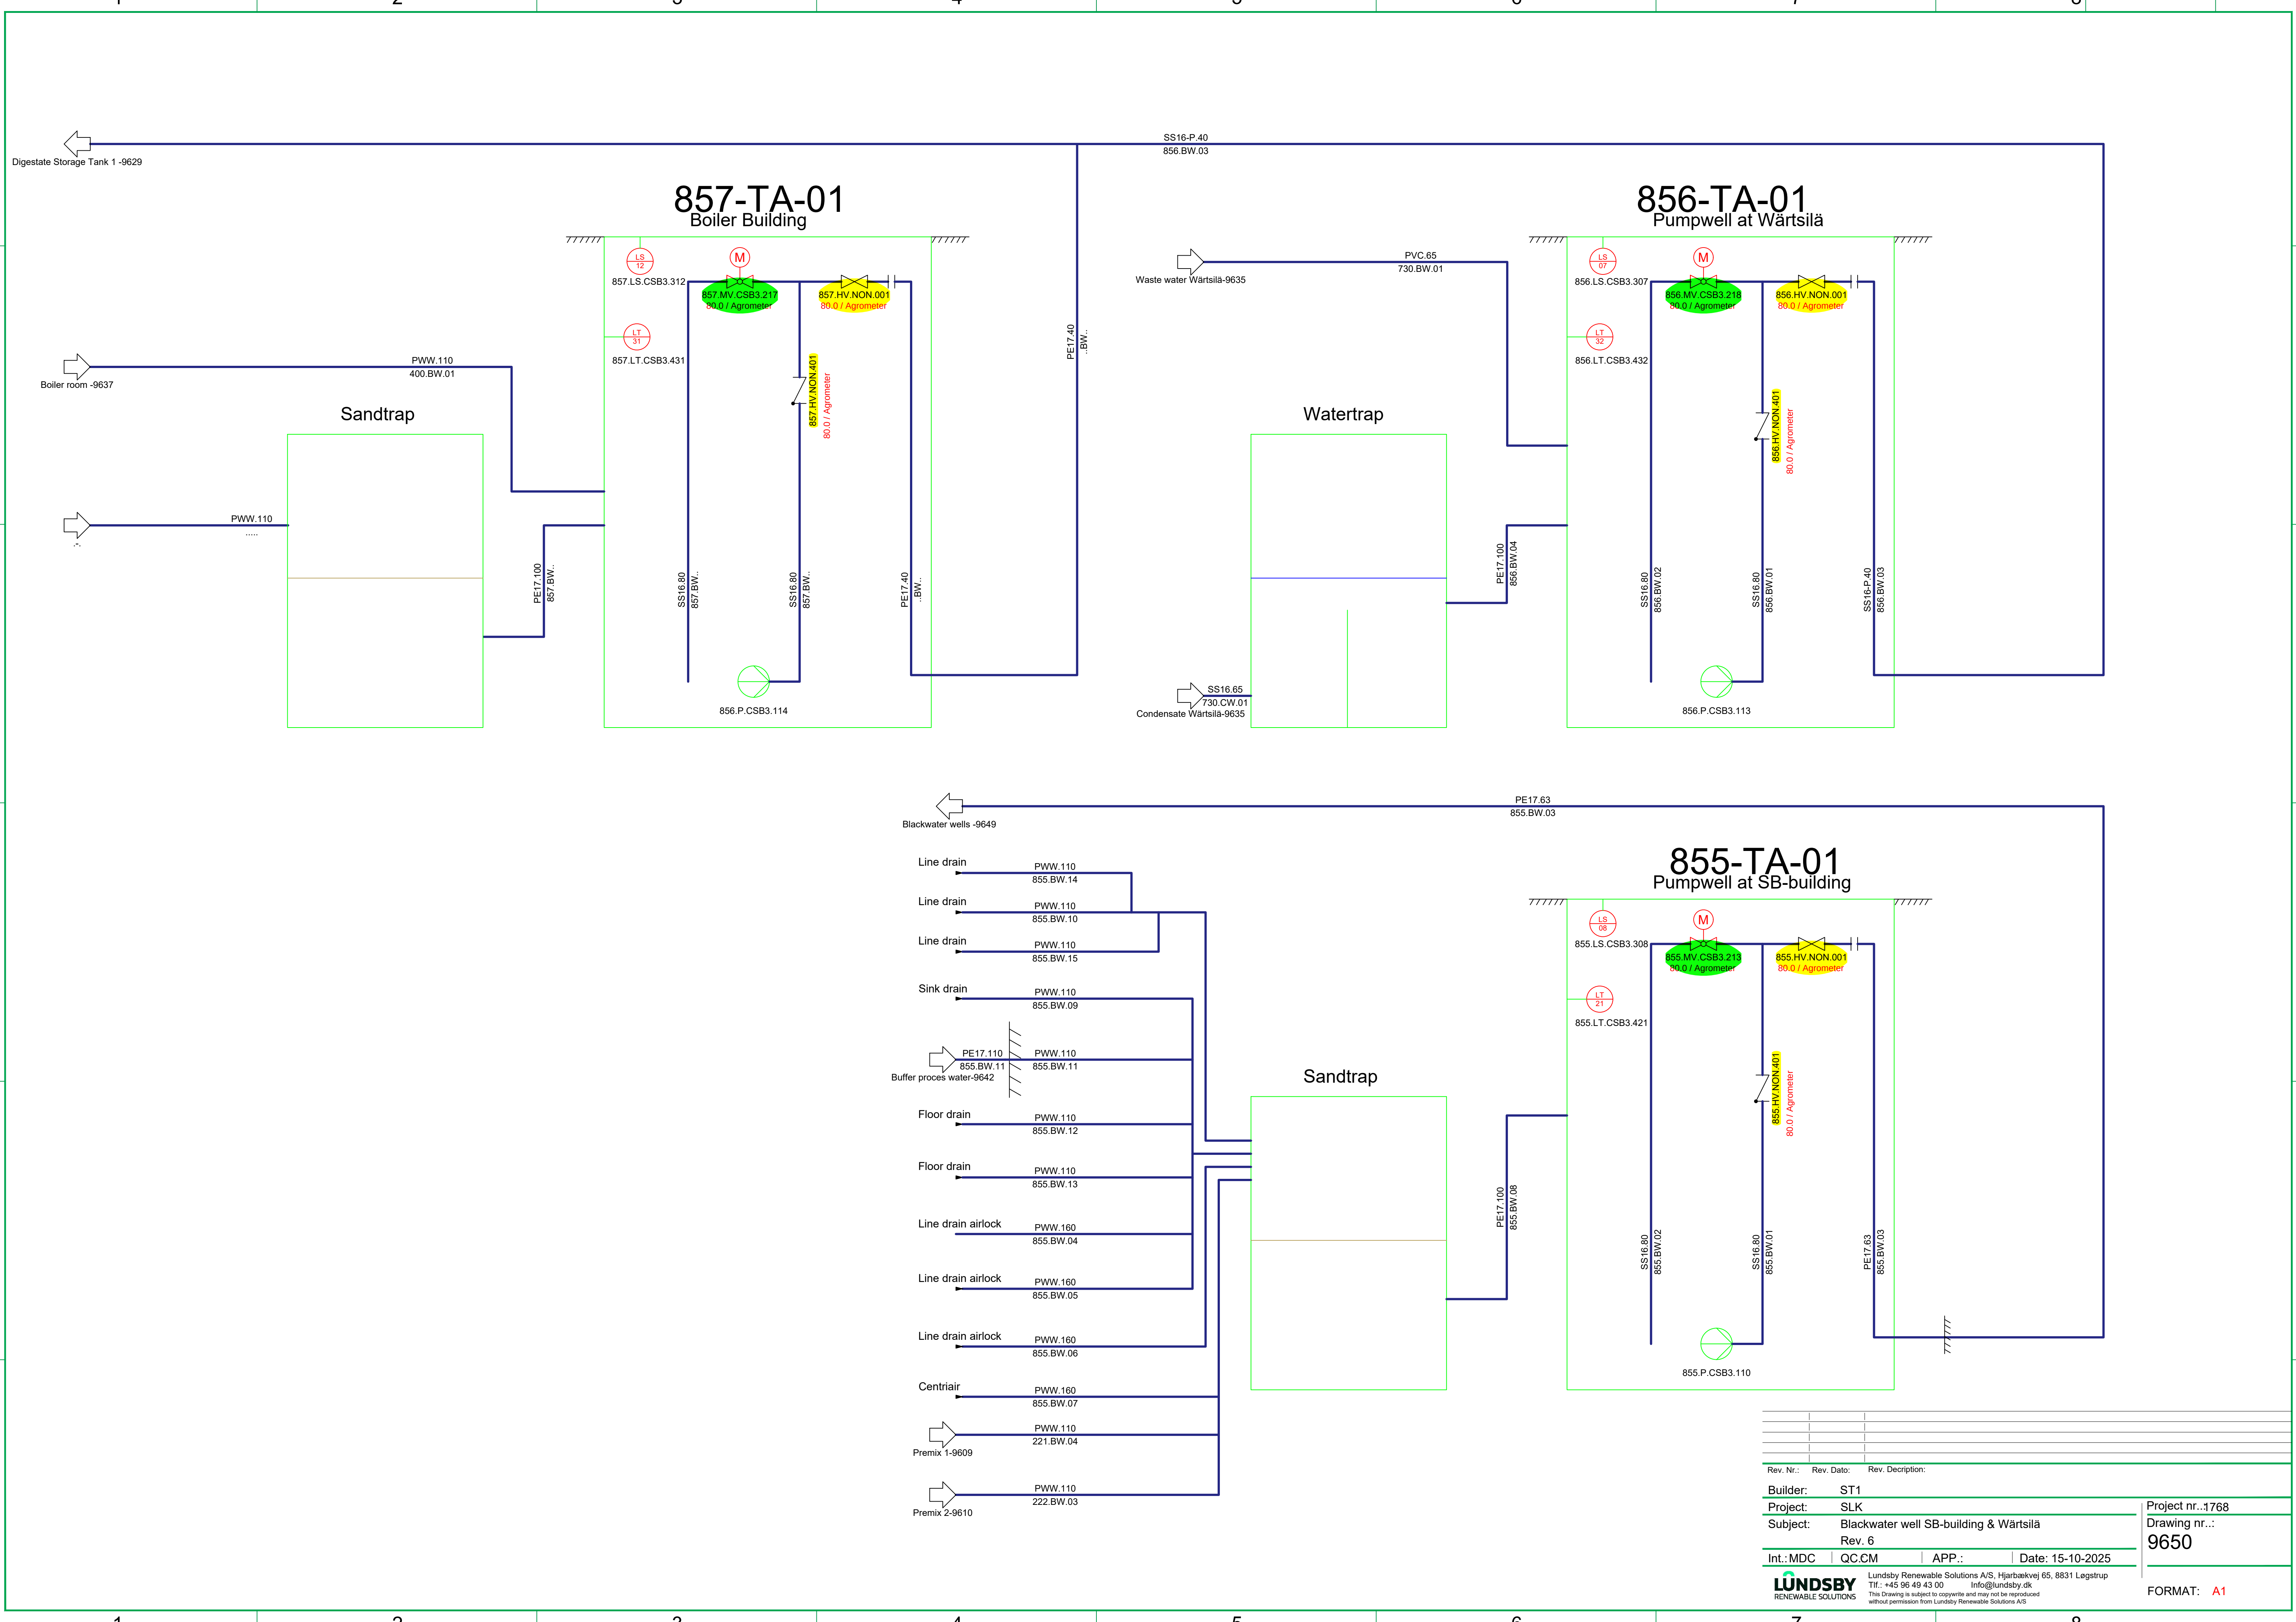


Rev. Nr.:	Rev. Dato:	Rev. Description:
Builder:	ST1	
Project:	SLK	
Subject:	Blackwater well SB-building & Wärtsilä	
Rev. 6		
Int.:MDC	QC:CM	APP.:
Date:	15-10-2025	
LUNDSBY RENEWABLE SOLUTIONS		
Lundsby Renewable Solutions A/S, Hjarbækvej 65, 8831 Løgstrup		
Tlf.: +45 96 49 43 00		
Info@lundsby.dk		
This Drawing is subject to copyright and may not be reproduced without permission from Lundsby Renewable Solutions A/S		
Project nr.:1768		Drawing nr.: 9650
FORMAT: A1		

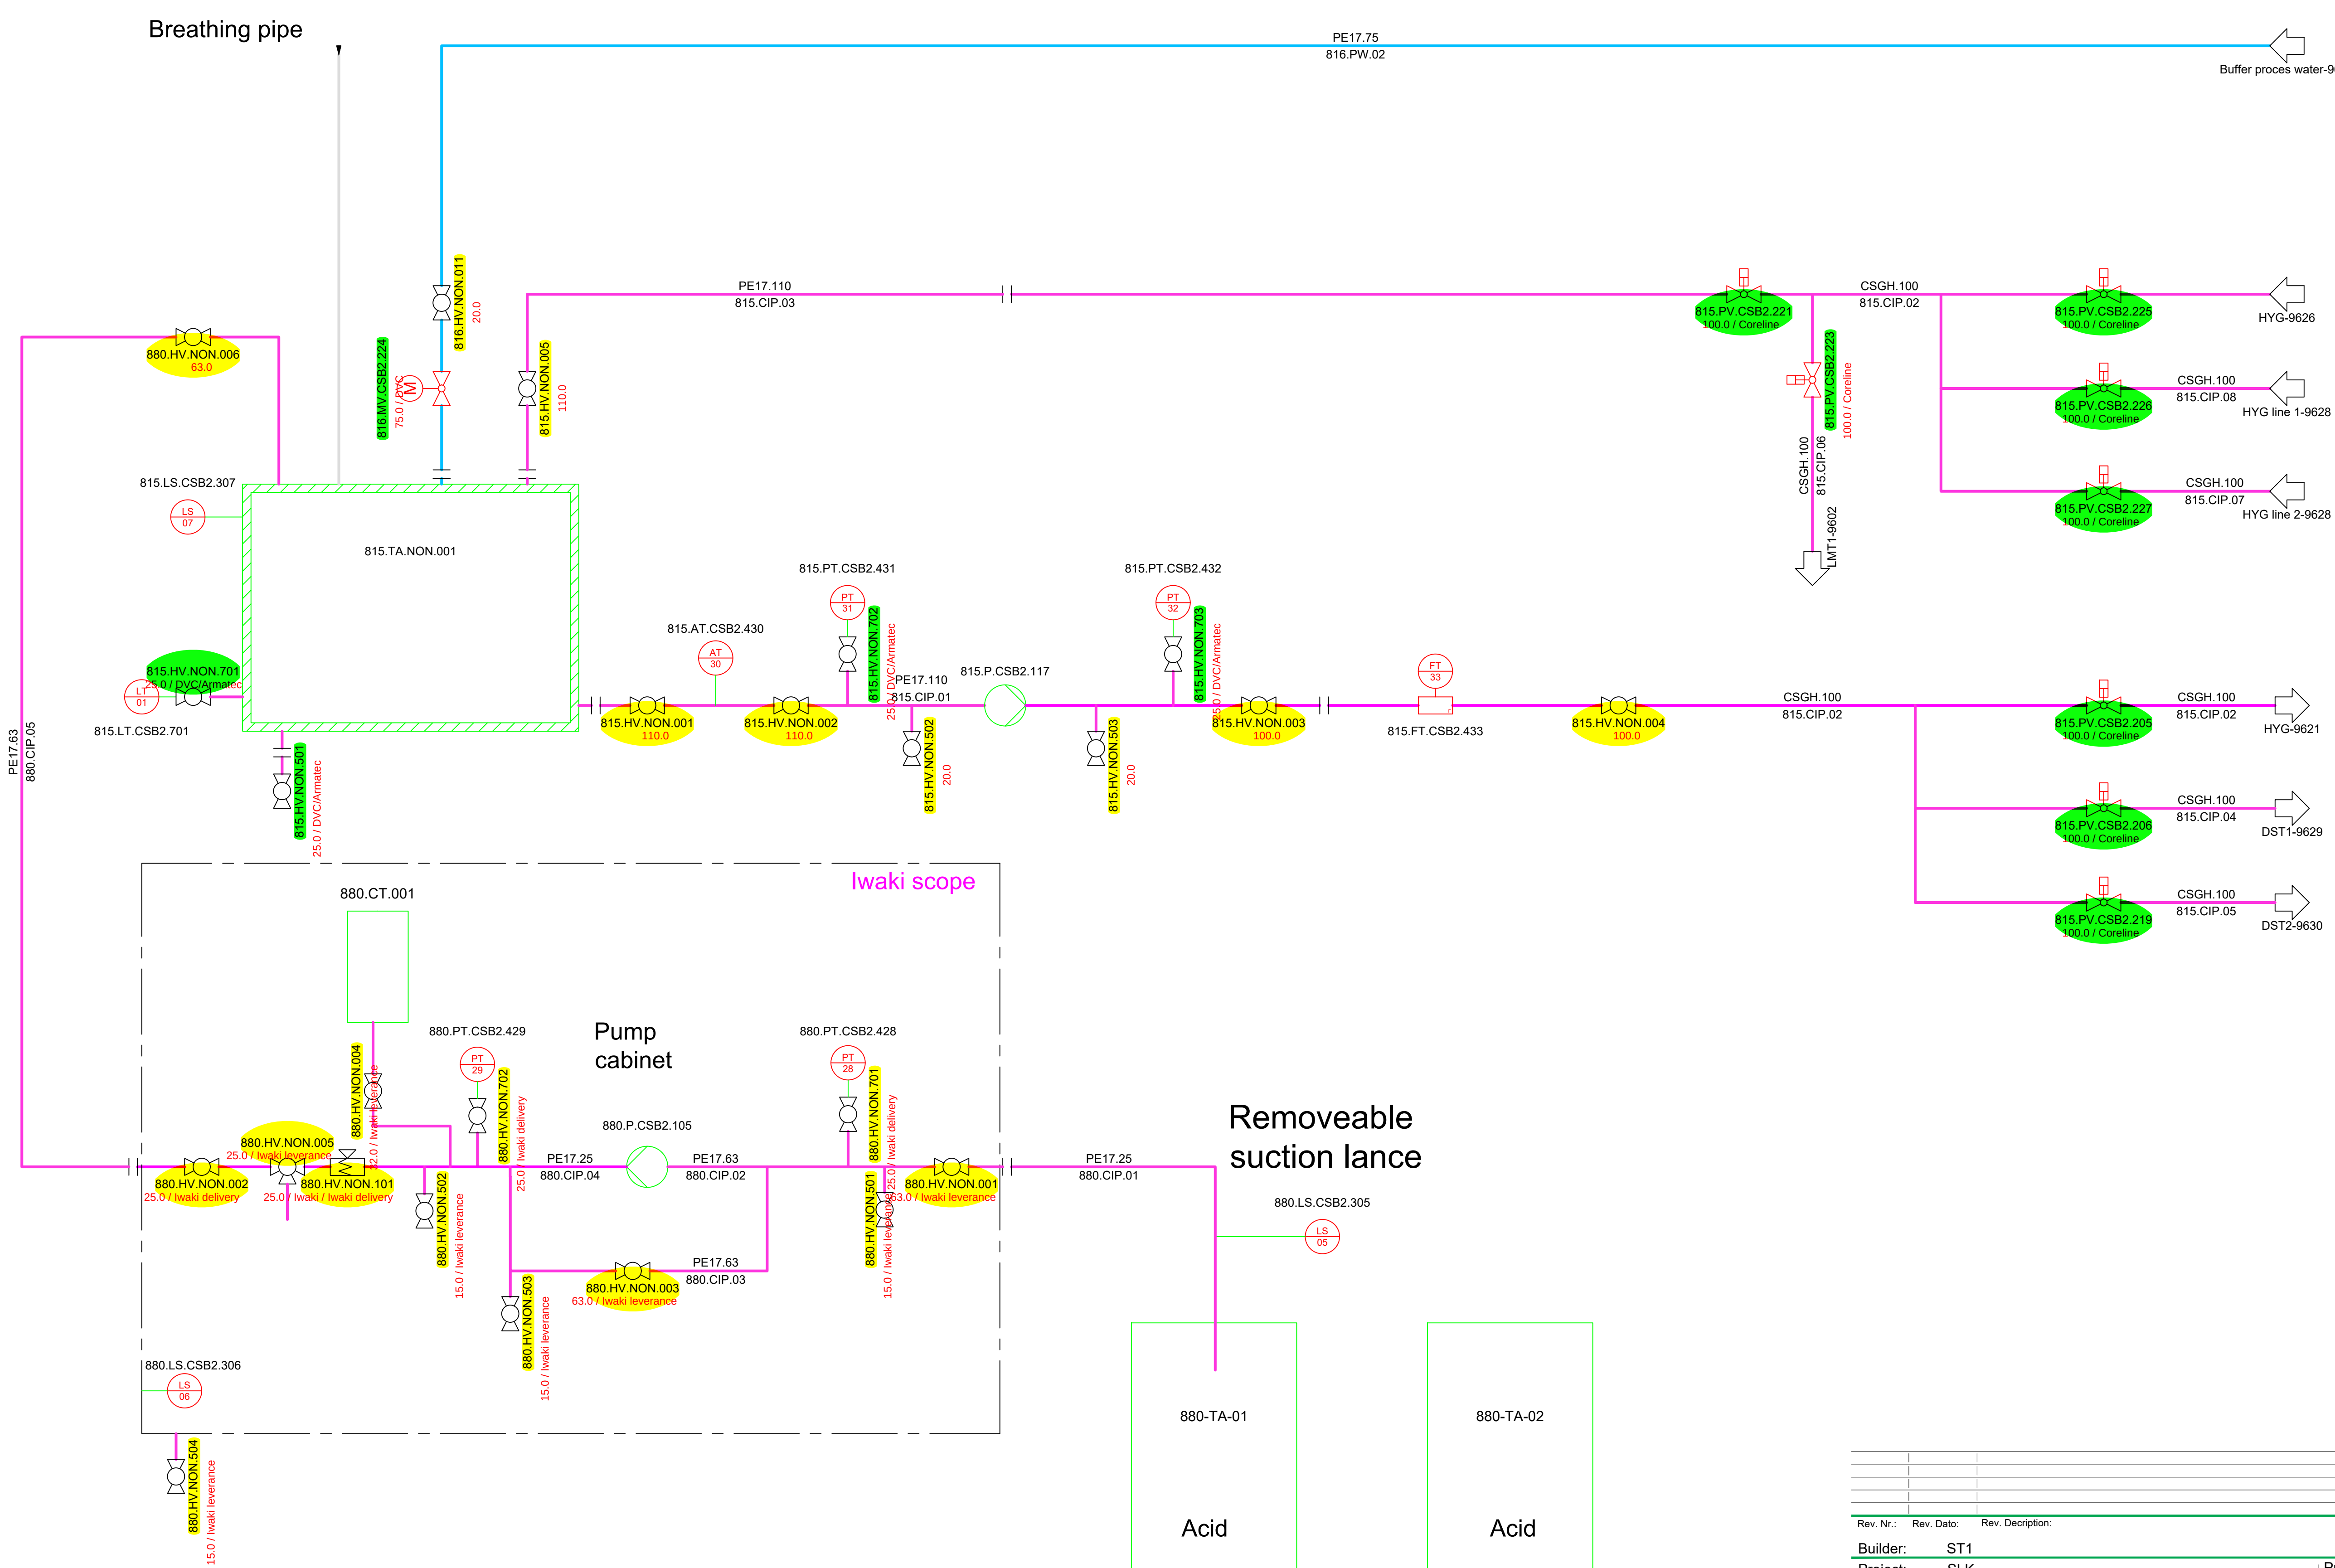


Rev. Nr.:	Rev. Dato:	Rev. Description:
Builder:	ST1	
Project:	SLK	
Subject:	CIP facility	
Rev. 6		
Int.:MDC	QC.CM	APP.:
Date:	15-10-2025	
LUNDSBY RENEWABLE SOLUTIONS		
Lundsby Renewable Solutions A/S, Hjarbrækvej 65, 8831 Løgstrup Tlf.: +45 96 49 43 00 Info@lundsby.dk This Drawing is subject to copyright and may not be reproduced without permission from Lundsby Renewable Solutions A/S		
Project nr.:1768 Drawing nr.: 9651		FORMAT: A1


Pumphouse 1
JA Trykluft scope

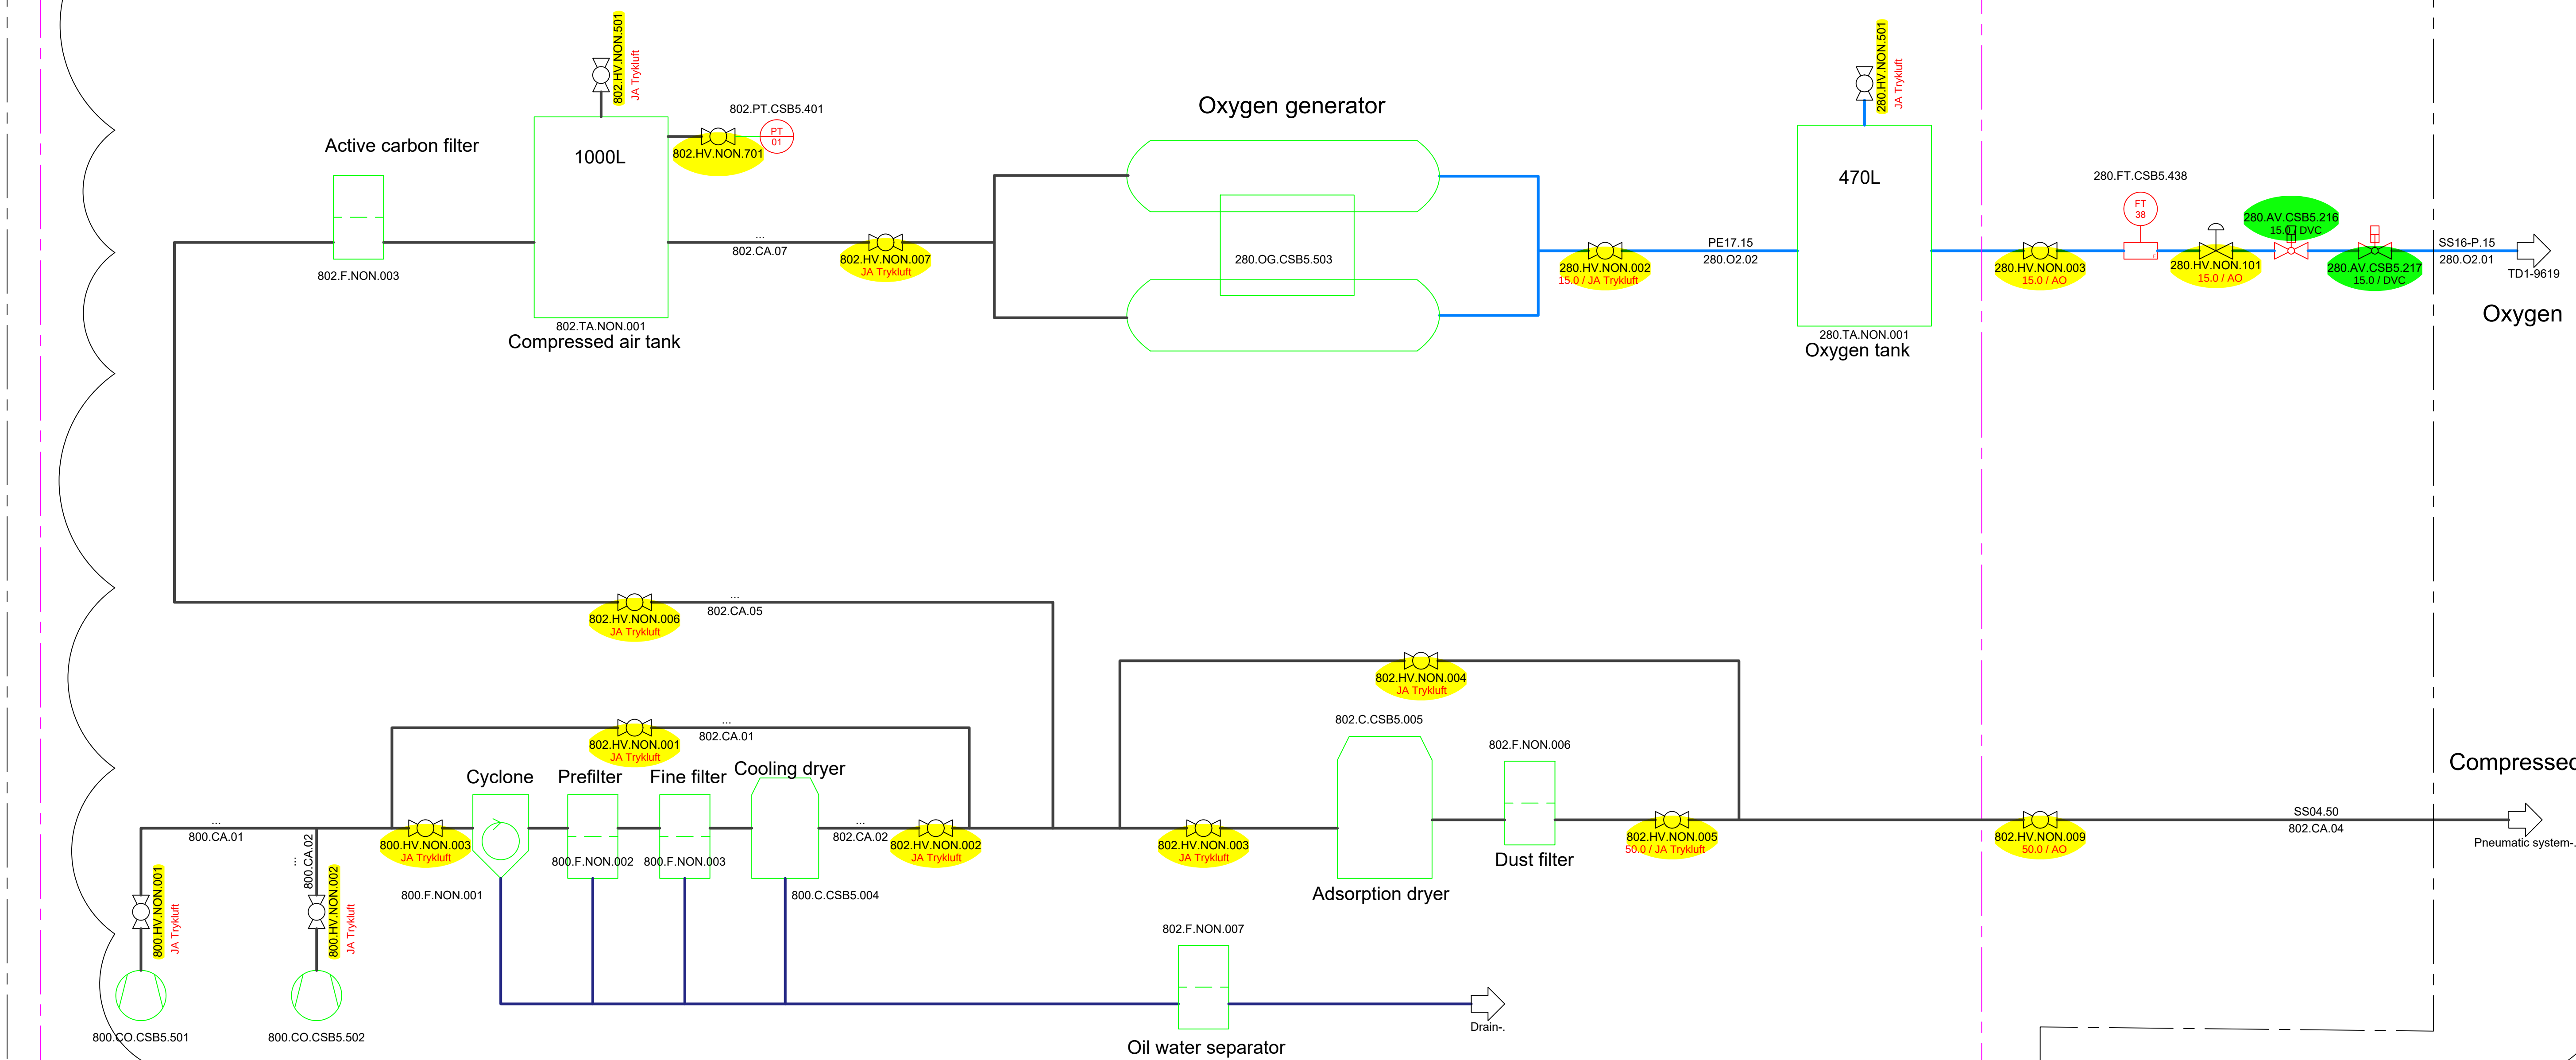


Rev. Nr.:	Rev. Dato:	Rev. Description:	
Builder:	ST1		
Project:	SLK		
Subject:	Compressed air & Oxygen		
Rev. 6			
Int.:MDC	QC.CM	APP.:	Date: 15-10-2025
LUNDSBY RENEWABLE SOLUTIONS			Lundsby Renewable Solutions A/S, Hjarbækvej 65, 8831 Legstrup Tlf.: +45 96 49 43 00 Info@lundsby.dk This drawing is subject to copyright and may not be reproduced without permission from Lundsby Renewable Solutions A/S
Project nr.:1768 Drawing nr.: 9652			FORMAT: A1

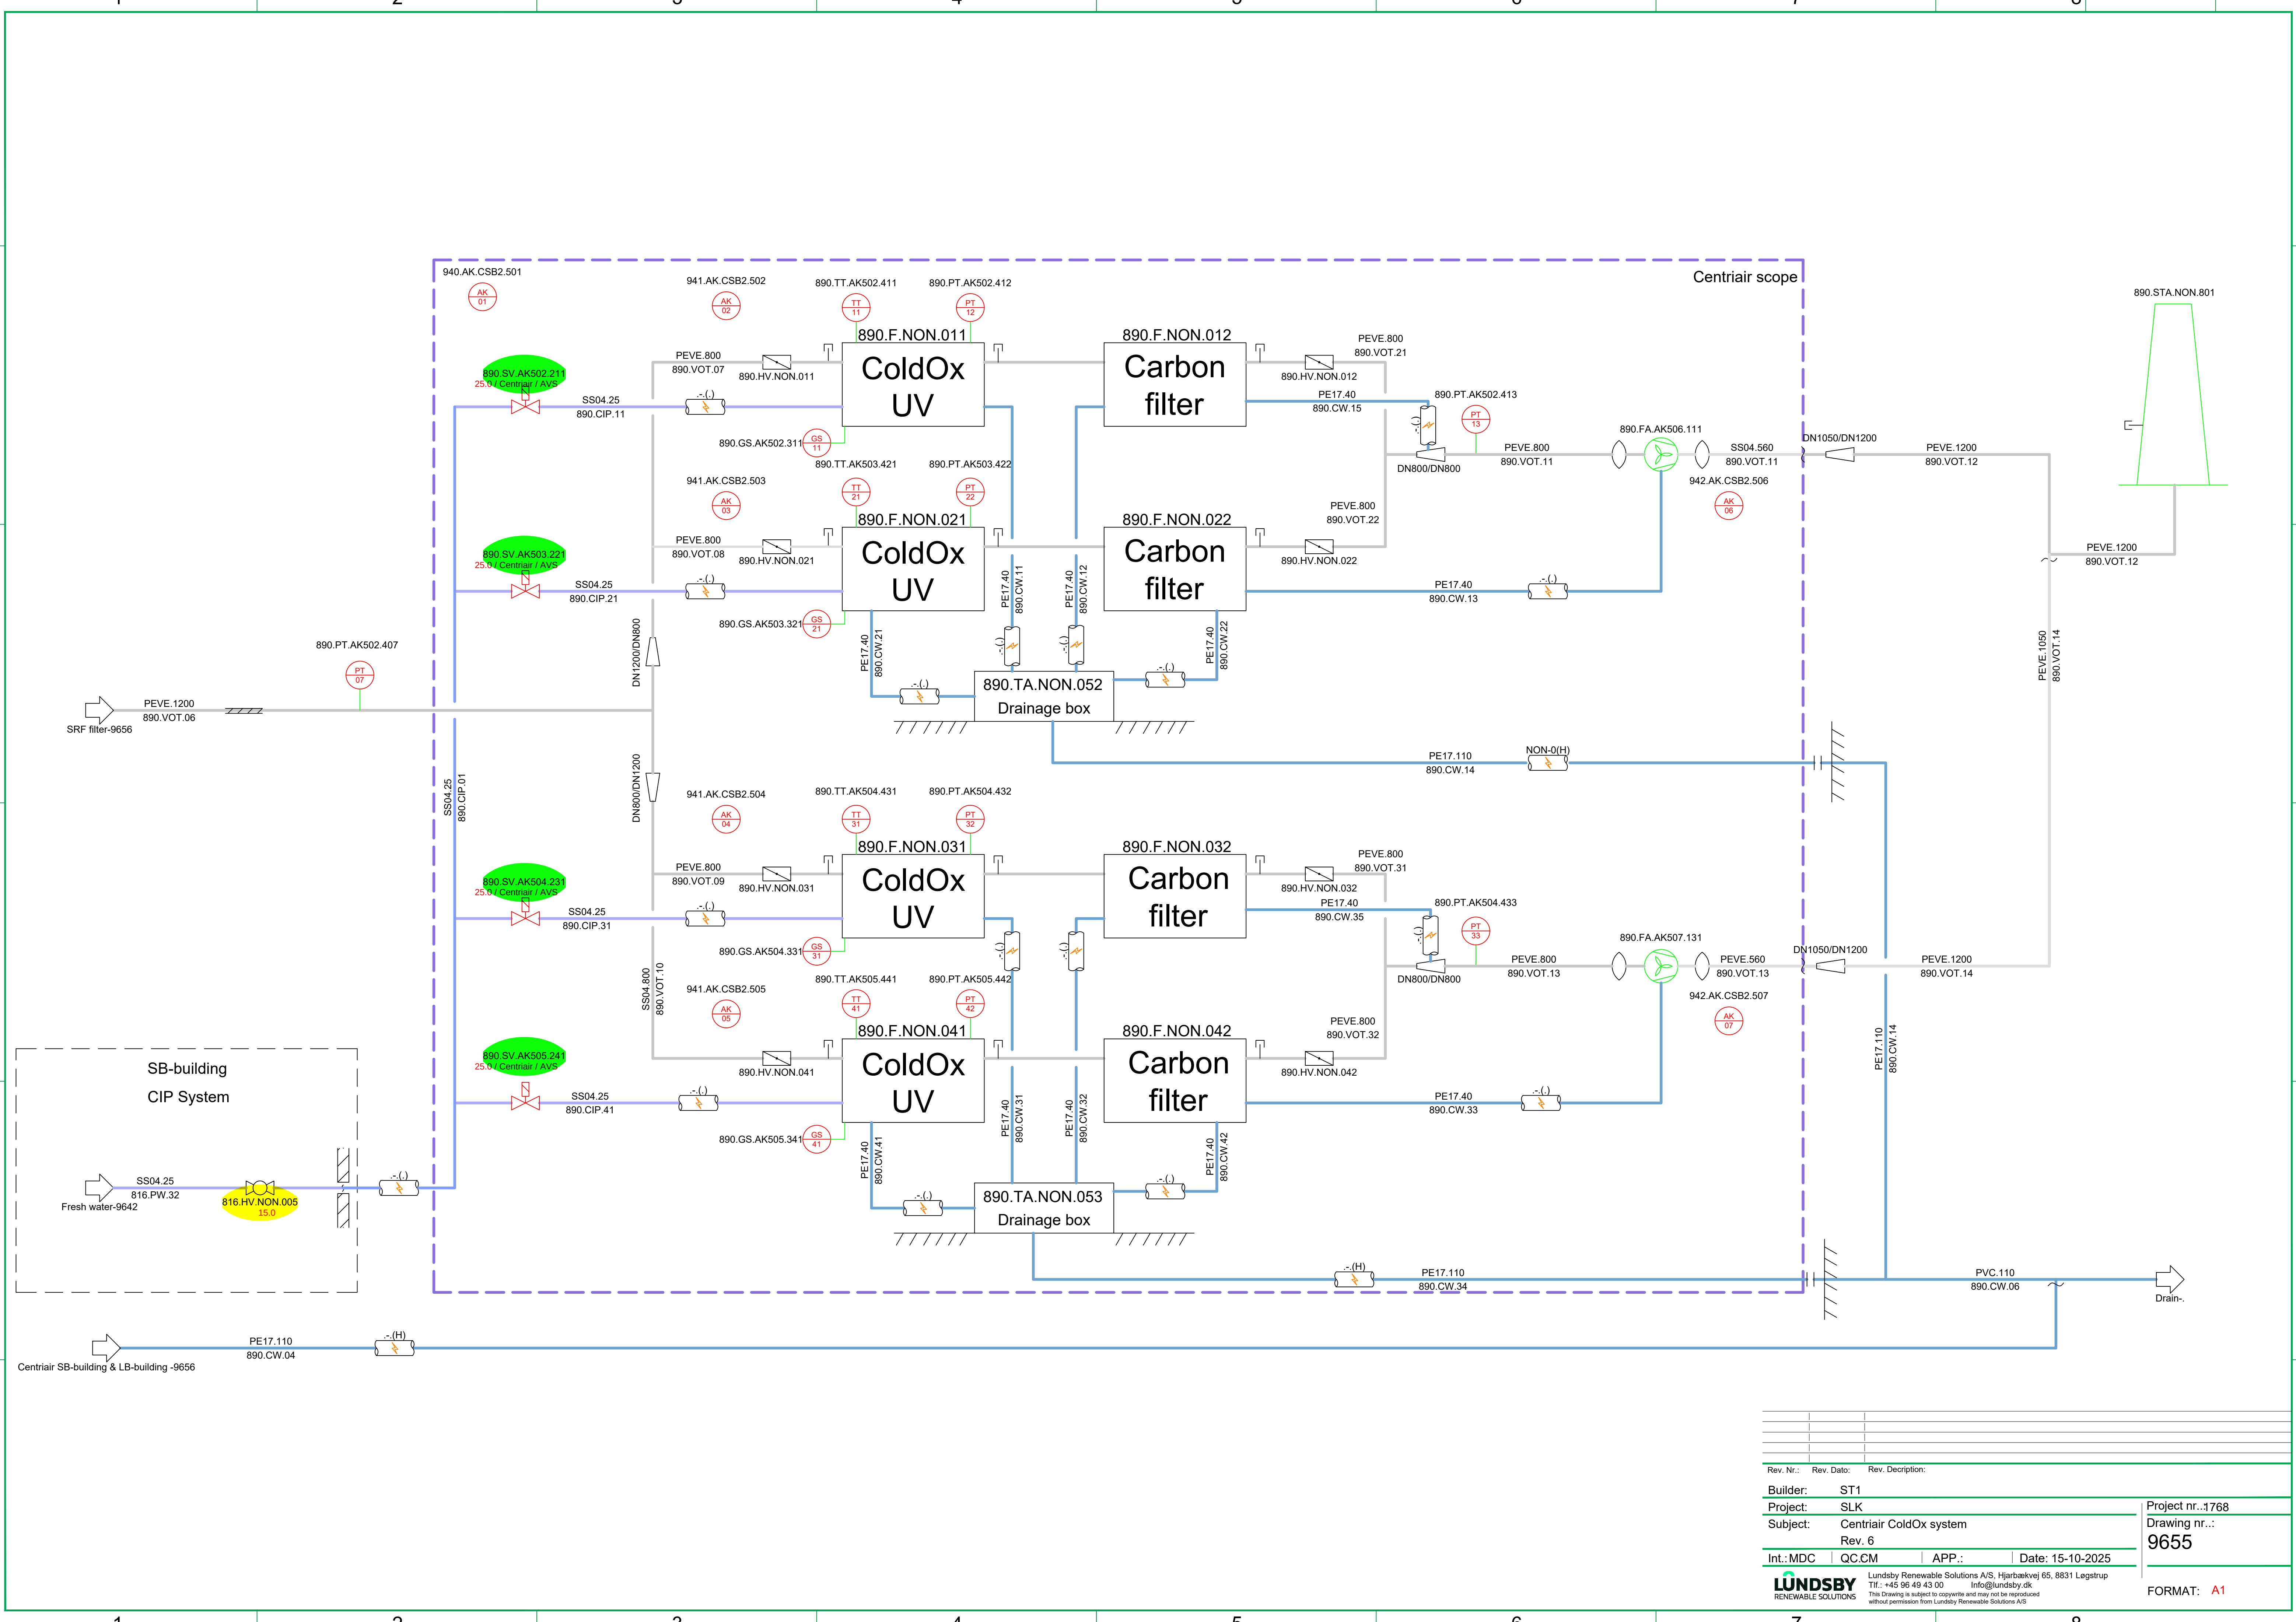

Rev. Nr.:	Rev. Dato:	Rev. Description:
Builder:	ST1	
Project:	SLK	
Subject:	Centriair ColdOx system	
Rev. 6		
Int.:MDC	QC:CM	APP.:
		Date: 15-10-2025
LUNDSBY RENEWABLE SOLUTIONS		
Lundsby Renewable Solutions A/S, Hjarbækvej 65, 8831 Løgstrup Tlf.: +45 96 49 43 00 info@lundsby.dk This drawing is subject to copyright and may not be reproduced without permission from Lundsby Renewable Solutions A/S		
Project nr.:1768 Drawing nr.: 9655		FORMAT: A1

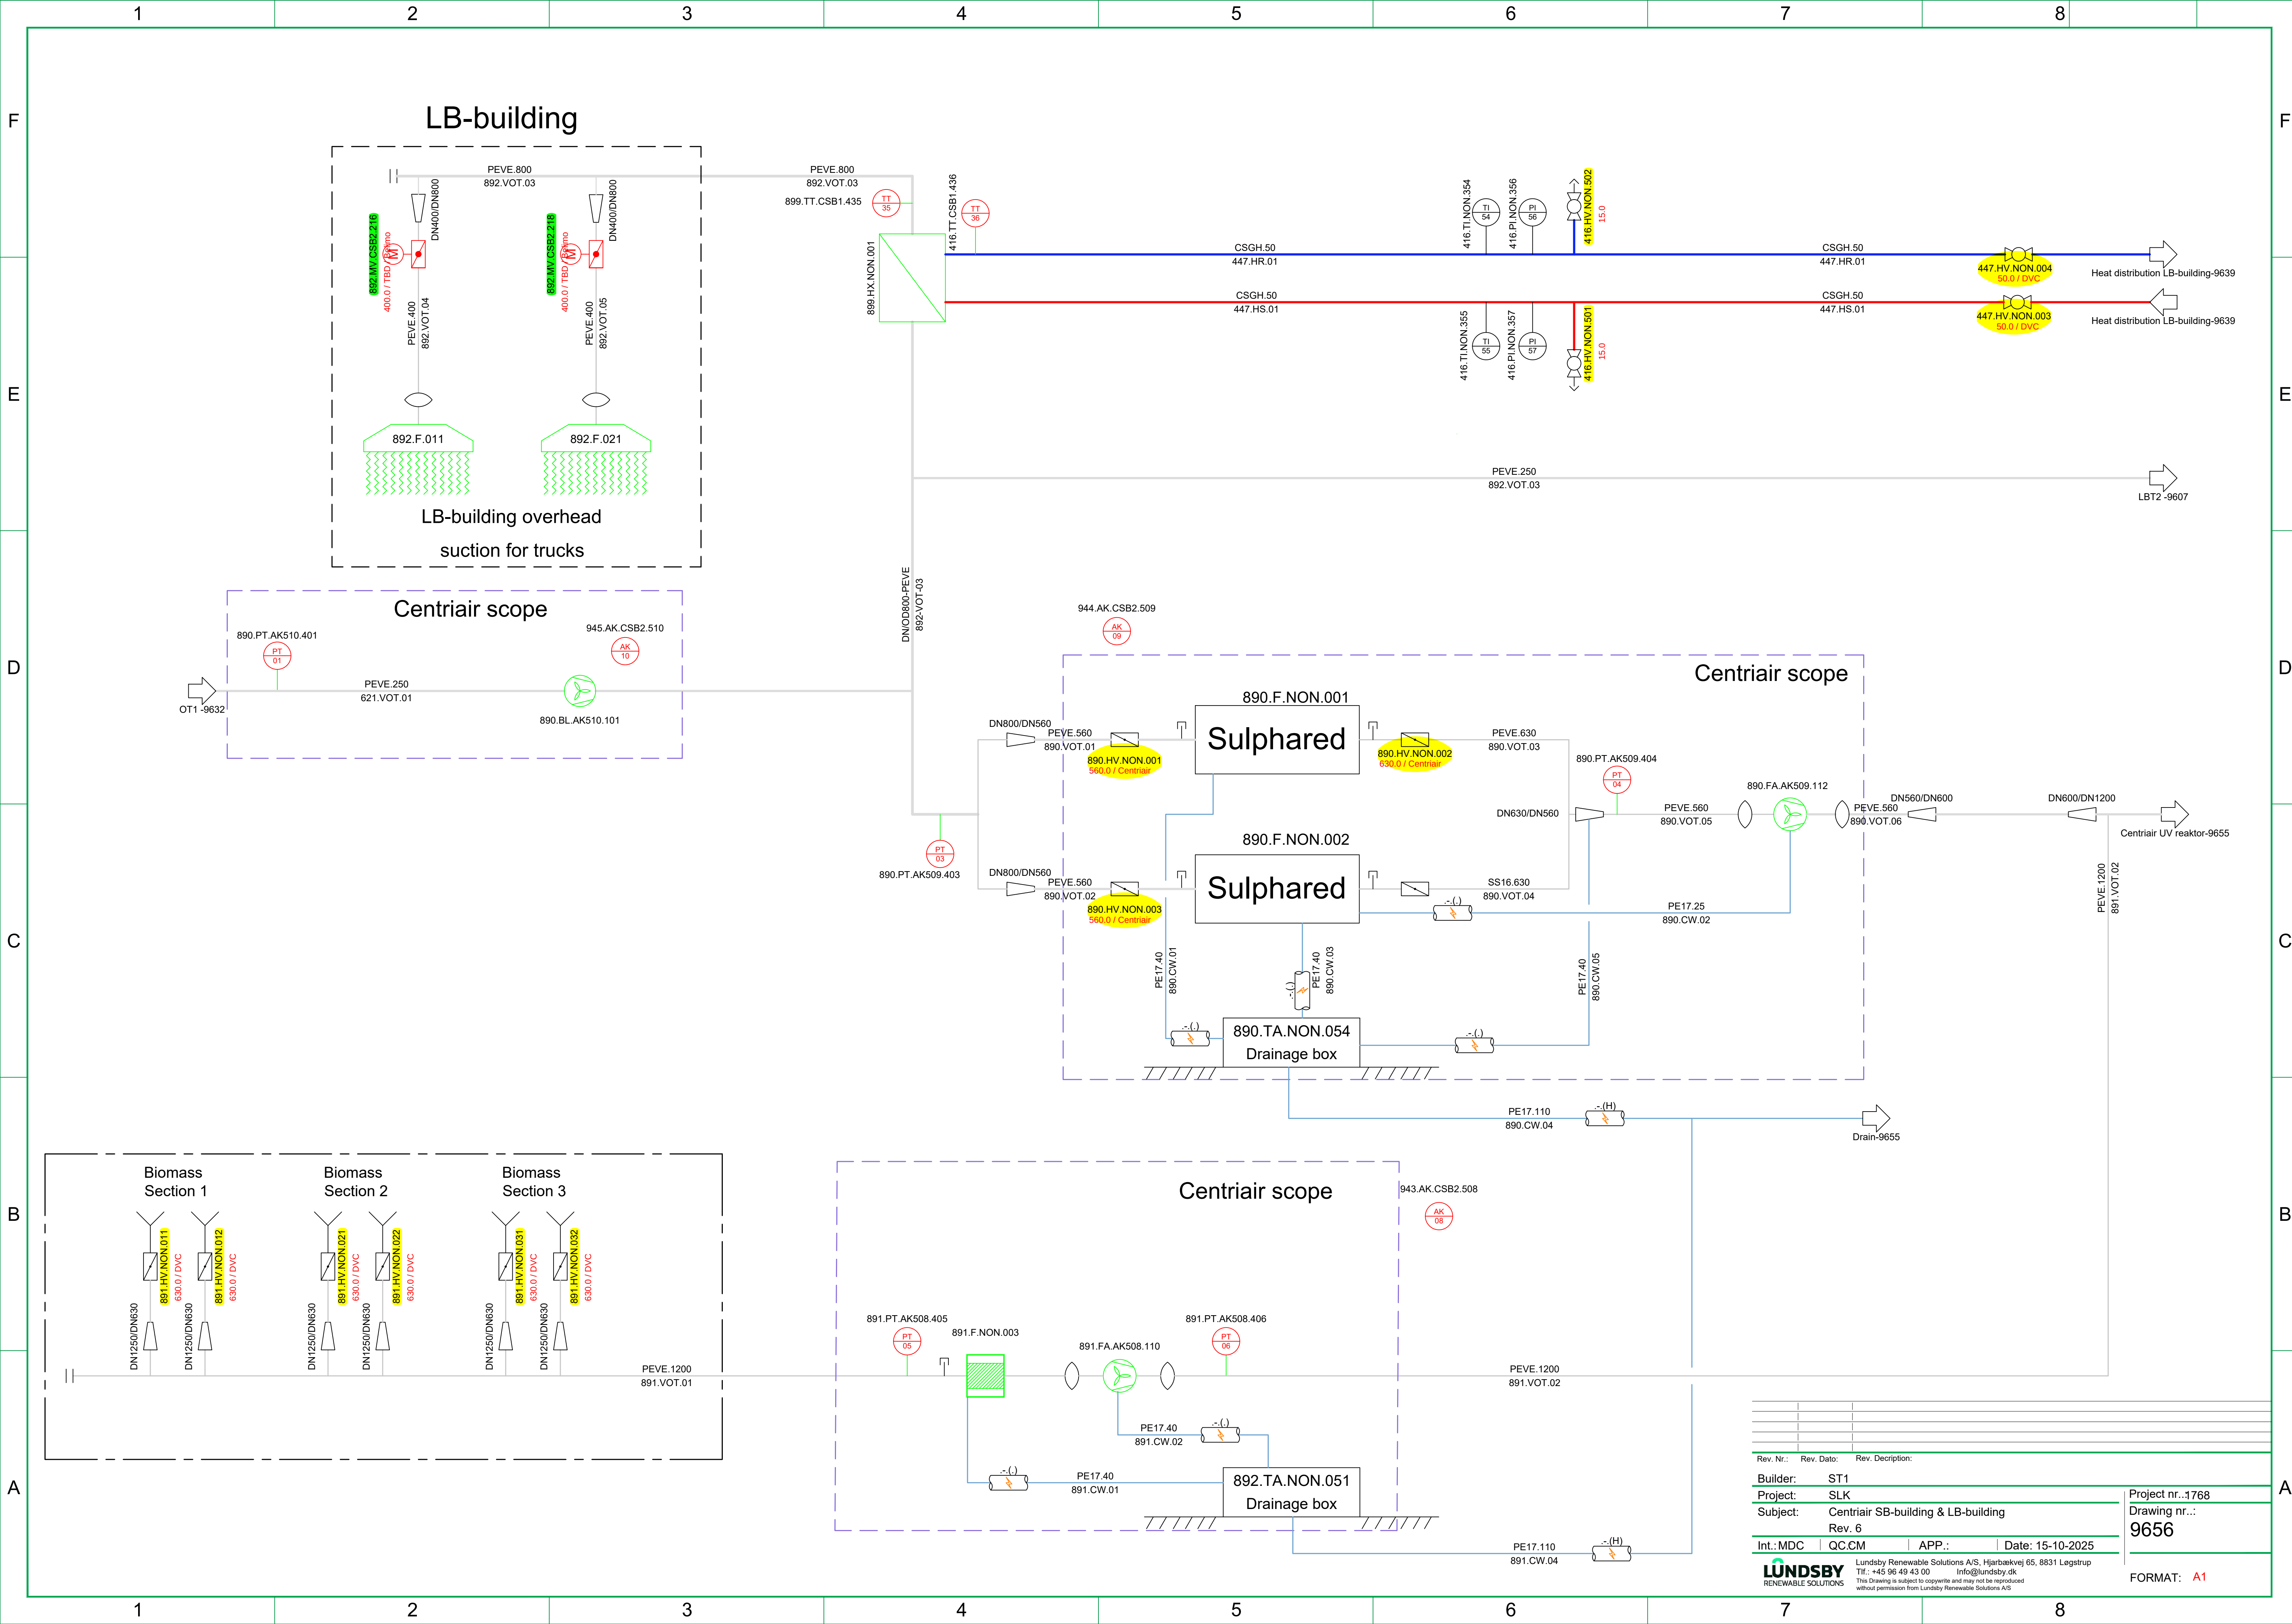

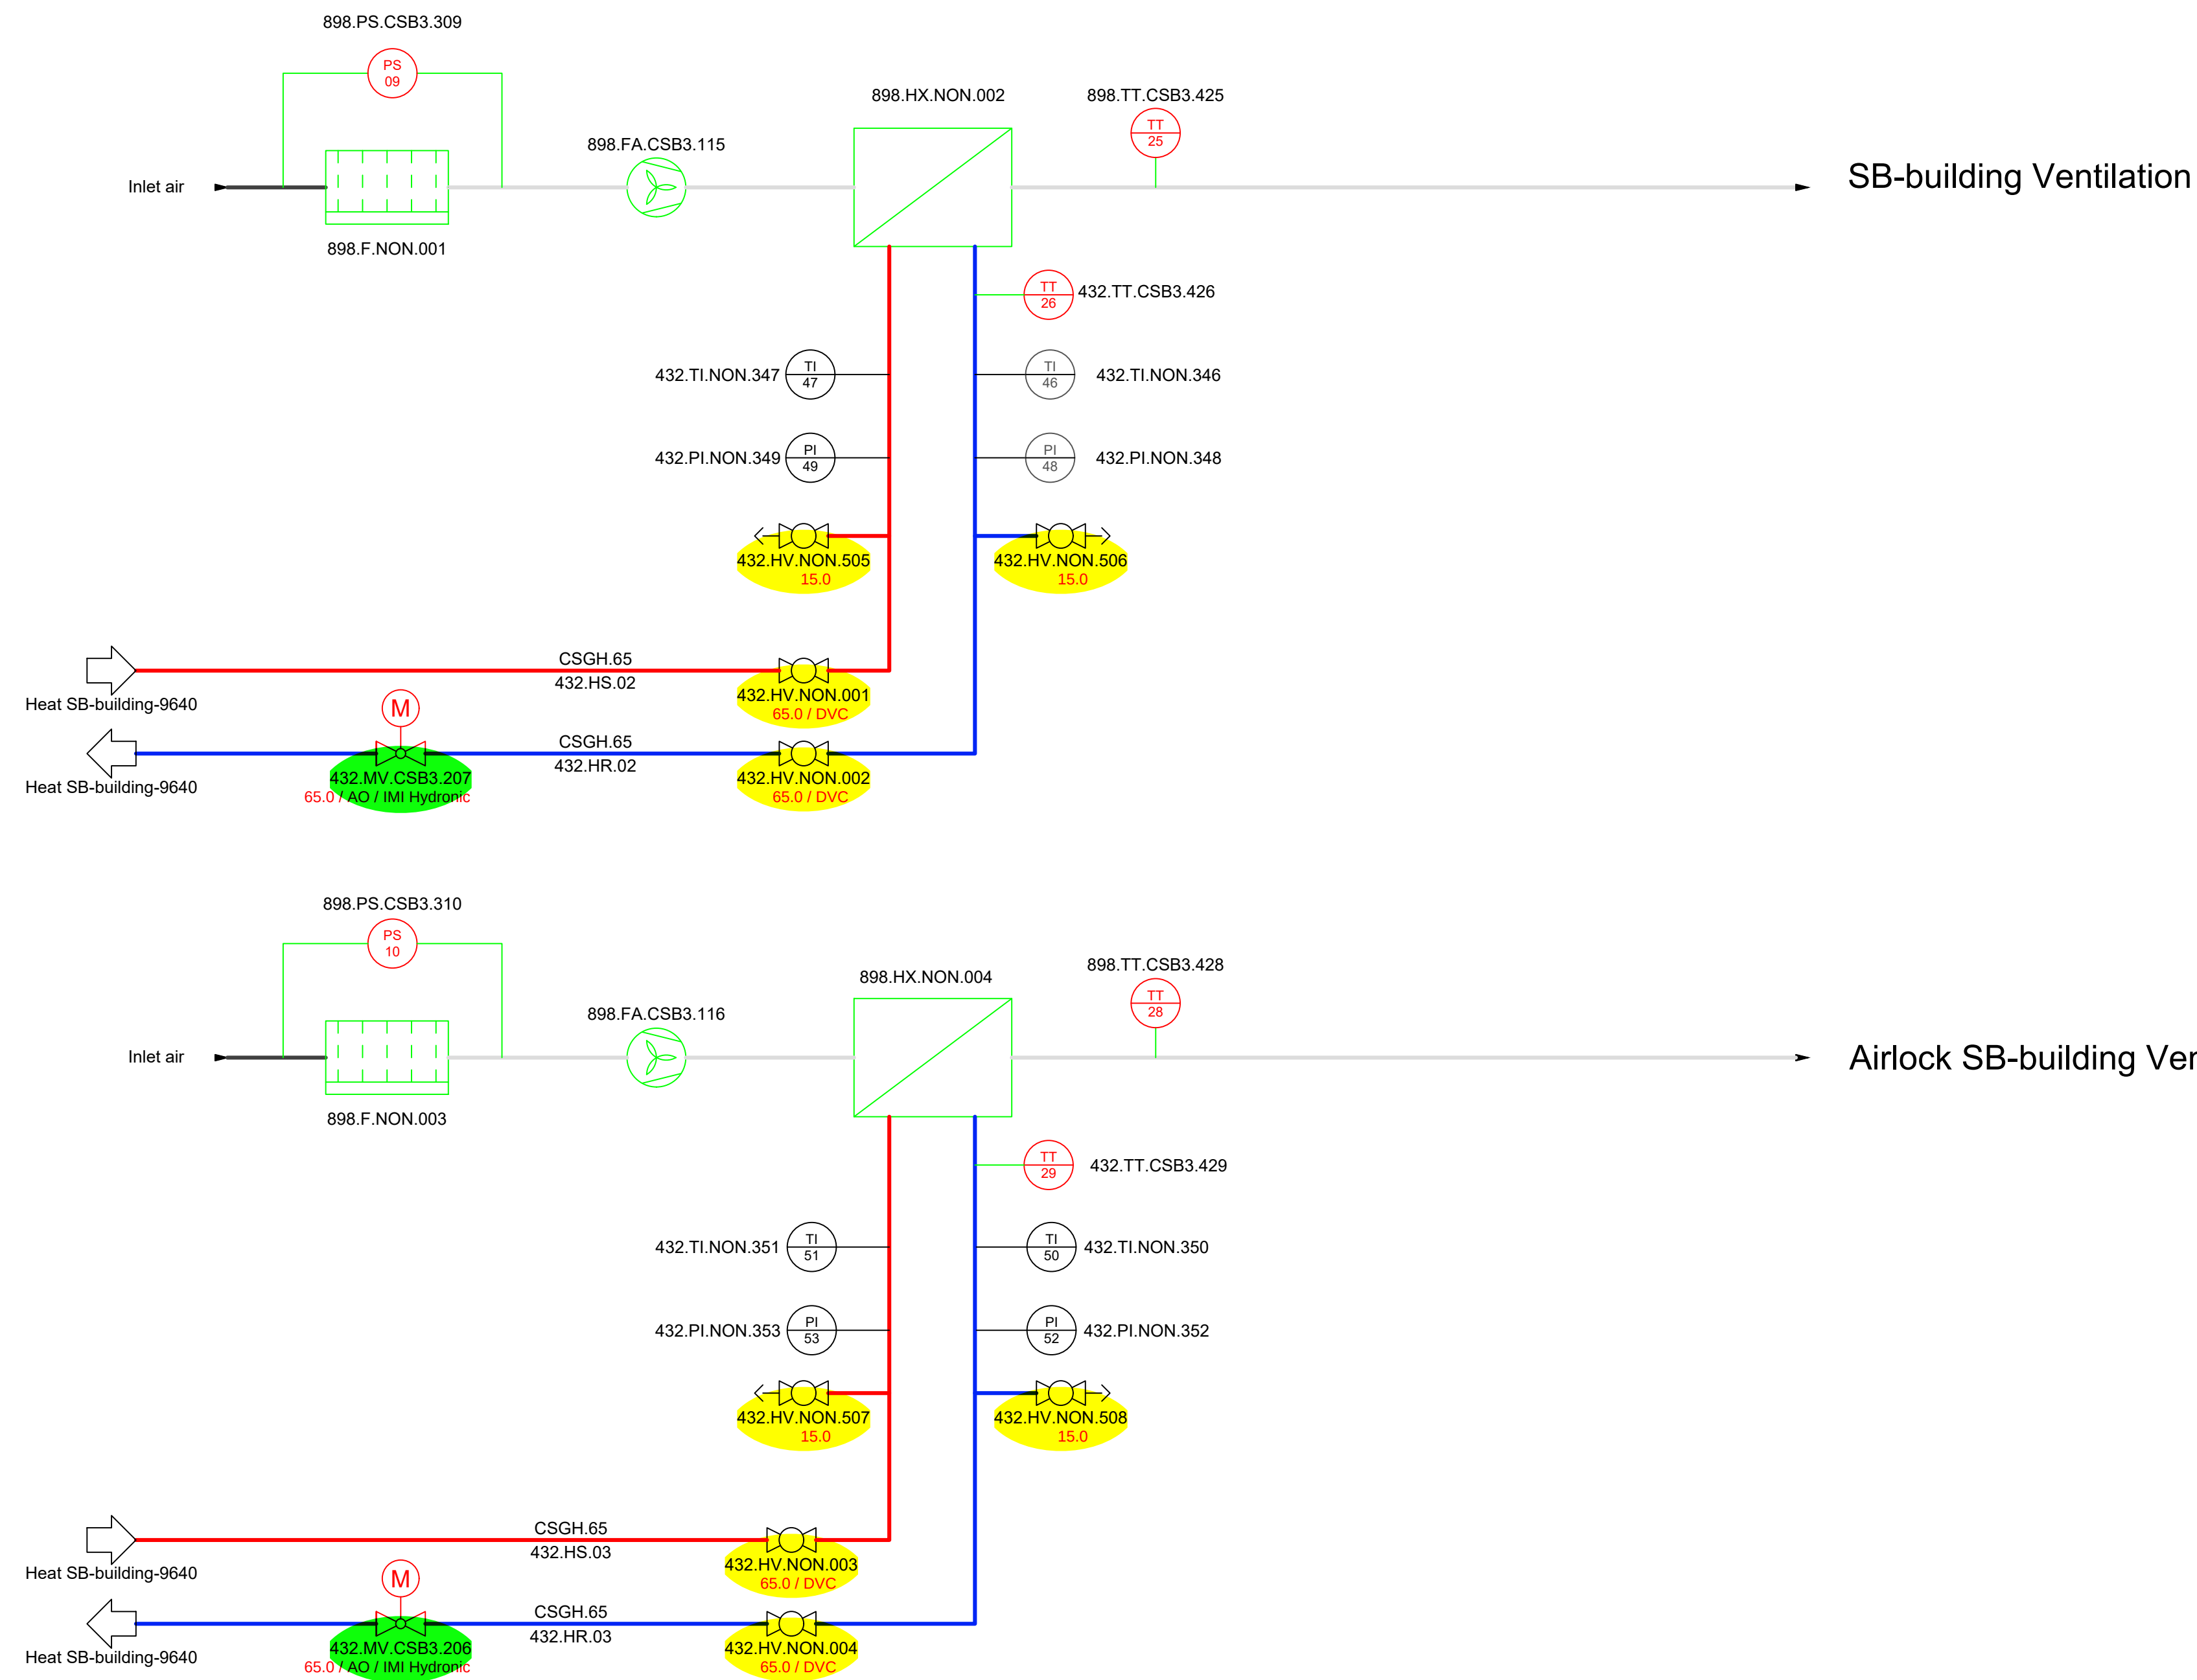

Rev. Nr.:	Rev. Dato:	Rev. Description:	
Builder:	ST1		
Project:	SLK		
Subject:	Ventilation SB-building		
Rev. 6			
Int.:MDC	QC.:CM	APP.:	Date: 15-10-2025
LUNDSBY RENEWABLE SOLUTIONS			Lundsby Renewable Solutions A/S, Hjarbækvej 65, 8831 Løgstrup Tlf.: +45 96 49 43 00 Info@lundsby.dk This Drawing is subject to copyright and may not be reproduced without permission from Lundsby Renewable Solutions A/S
Project nr.: 1768 Drawing nr.: 9657			FORMAT: A1