




1	2	3	4	5	6	7	8	
Structure of the tagging system	
Structure of the component tagging			Lines		Bulding/Area/Tank		Media code	
XXX — XXX — XXX — XXX Main equipment area codeEquipment ValveInstrument abbreviationSupply from switchboardNumeric Sequence Example 552 - TA - NON - 001 101 Switchboard Tank Area pasteurization tank 2 301.TA.NON.1: where 301 = Digester (System number), TA = Tank (Equipment), NON = Mechanical object (No switchboard), 01 = Tank nr 1. 201.P.CSB2.05: where 201 = Manure/feeding (System number), P = Pump (Equipment), CSB2 = Electrical object (Distribution board), 05 = Pump nr 5. 901.AK.CSB1.03: where 901 = Control and automation (System number), AK = Sub-distribution board at subcontractor (Equipment), CSB1 = Electrical object (Distribution board), 03 = Cabinet nr 3.			Description Symbol Subcontractor scope Boundary line Page connector Start pipe - Not linked to page End pipe - Not linked to page Fald/ Slope Insulation Electrical Heat tracing		Description Code Primary digester Secondary digester Digester storage Liquid manure tank Liquid biomass tank Outlet tank Blackwater tank Tech building Admin building Solid biomass building Liquid biomass building Plansilo Pump house Hygienization tanks Flare Stack Odour treatment facility Upgrade facility Liquifaction facility Oil boiler Wood boiler Transformer		Media Pipe color RBG color Code Heat Return Heat Supply Heat Hot Return Heat Hot Supply Cooling Supply Cooling Return Black Water CIP Process Water Technical Water Drinking Water Drinking Water Hot Condensate Steam Steam Condensate Liquid Manure (Slurry) Liquid Biomass (Substrat) Process Biomass Hygienized Biomass Recirculated Biomass Ferric Chloride FeCl Ventilation Odour Treatment Ventilation Fresh Air Compressed Air Oxygen Raw Biogas Return/reject Gas Nature Gas	
<table><tr><th>System:</th><th colspan="2">System number:</th></tr><tr><td>Reception</td><td>100-199</td><td></td></tr><tr><td>Manure tank</td><td></td><td>100-109</td></tr><tr><td>Fat/Liquid Substrate tank</td><td></td><td>110-119</td></tr><tr><td>Dry Dosificator tank</td><td></td><td>120-129</td></tr><tr><td>FeCl tank</td><td></td><td>130-139</td></tr><tr><td>Glycerol tank</td><td></td><td>140-149</td></tr><tr><td>Cereals silo</td><td></td><td>160-169</td></tr><tr><td>Water tank</td><td></td><td>170-179</td></tr><tr><td>LPG tank</td><td></td><td>180-189</td></tr><tr><td>Beets and root crops</td><td></td><td>190-191</td></tr><tr><td>Feeding in</td><td>200-299</td><td></td></tr><tr><td>Manure feeding</td><td></td><td>200-209</td></tr><tr><td>Fat/Liquid Substrate feeding</td><td></td><td>210-219</td></tr><tr><td>Dry Dosificator</td><td></td><td>220-229</td></tr><tr><td>FeCl feeding</td><td></td><td>230-239</td></tr><tr><td>Glycerol feeding</td><td></td><td>240-249</td></tr><tr><td>Pasteurization before digester</td><td></td><td>250</td></tr><tr><td>Cereal feeding</td><td></td><td>260</td></tr><tr><td>Water feeding</td><td></td><td>270</td></tr><tr><td>Oxygen/air dozing</td><td></td><td>280</td></tr><tr><td>Mixing tank</td><td></td><td>290</td></tr><tr><td>Digester</td><td>300-399</td><td></td></tr><tr><td>Primary Digester</td><td></td><td>300-309</td></tr><tr><td>Secondary Digester</td><td></td><td>310-319</td></tr><tr><td>Tertiary Digester</td><td></td><td>320-329</td></tr><tr><td>Line X</td><td></td><td>3X0</td></tr><tr><td>Heating system</td><td>400-499</td><td></td></tr><tr><td>Heating system</td><td></td><td>400-449</td></tr><tr><td>Cooling system</td><td></td><td>450-459</td></tr><tr><td>Feeding out</td><td>500-599</td><td></td></tr><tr><td>Pump</td><td></td><td>500 - 509</td></tr><tr><td>Pasteurization after digester</td><td></td><td>550</td></tr><tr><td>Biofertilizer tank</td><td>600-699</td><td></td></tr><tr><td>Biofertilizer tank 1</td><td></td><td>601</td></tr><tr><td>Biofertilizer tank 2</td><td></td><td>602</td></tr><tr><td>Separation</td><td></td><td>610 - 619</td></tr><tr><td>Gas treatment</td><td>700-799</td><td></td></tr><tr><td>Components on general gas pipe</td><td></td><td>700</td></tr><tr><td>Condensate pit</td><td></td><td>710</td></tr><tr><td>Flare</td><td></td><td>720</td></tr><tr><td>Upgrading unit/CHP/boiler</td><td></td><td>730</td></tr><tr><td>Stripper air combustion</td><td></td><td>740</td></tr><tr><td>RTO</td><td></td><td>750</td></tr><tr><td>High pressure compressor station</td><td></td><td>760</td></tr><tr><td>LNG plant</td><td></td><td>770</td></tr><tr><td>Propane dosing</td><td></td><td>780</td></tr><tr><td>Support system</td><td>800-899</td><td></td></tr><tr><td>Instrument air</td><td></td><td>800</td></tr><tr><td>Hydraulic system</td><td></td><td>805</td></tr><tr><td>Water</td><td></td><td>810</td></tr><tr><td>Backflow protection system</td><td></td><td>815</td></tr><tr><td>Heat tracing cable</td><td></td><td>820</td></tr><tr><td>Car wash</td><td></td><td>830</td></tr><tr><td>Building/container</td><td></td><td>840</td></tr><tr><td>Pumpwell</td><td></td><td>850</td></tr><tr><td>Oil separator</td><td></td><td>860</td></tr><tr><td></td><td></td><td>870</td></tr><tr><td>Dosing equipment</td><td></td><td>880</td></tr><tr><td>Odour cntro/ventilation system</td><td></td><td>890</td></tr><tr><td>Electrical and Control</td><td>900-999</td><td></td></tr><tr><td>Control and automation</td><td></td><td>900-949*</td></tr><tr><td>Server and IT</td><td></td><td>950*</td></tr><tr><td>Electrical power high voltage (>1000V)</td><td></td><td>980-989*</td></tr><tr><td>Electrical power low voltage</td><td></td><td>990-999*</td></tr></table>			System:	System number:		Reception	100-199		Manure tank		100-109	Fat/Liquid Substrate tank		110-119	Dry Dosificator tank		120-129	FeCl tank		130-139	Glycerol tank		140-149	Cereals silo		160-169	Water tank		170-179	LPG tank		180-189	Beets and root crops		190-191	Feeding in	200-299		Manure feeding		200-209	Fat/Liquid Substrate feeding		210-219	Dry Dosificator		220-229	FeCl feeding		230-239	Glycerol feeding		240-249	Pasteurization before digester		250	Cereal feeding		260	Water feeding		270	Oxygen/air dozing		280	Mixing tank		290	Digester	300-399		Primary Digester		300-309	Secondary Digester		310-319	Tertiary Digester		320-329	Line X		3X0	Heating system	400-499		Heating system		400-449	Cooling system		450-459	Feeding out	500-599		Pump		500 - 509	Pasteurization after digester		550	Biofertilizer tank	600-699		Biofertilizer tank 1		601	Biofertilizer tank 2		602	Separation		610 - 619	Gas treatment	700-799		Components on general gas pipe		700	Condensate pit		710	Flare		720	Upgrading unit/CHP/boiler		730	Stripper air combustion		740	RTO		750	High pressure compressor station		760	LNG plant		770	Propane dosing		780	Support system	800-899		Instrument air		800	Hydraulic system		805	Water		810	Backflow protection system		815	Heat tracing cable		820	Car wash		830	Building/container		840	Pumpwell		850	Oil separator		860			870	Dosing equipment		880	Odour cntro/ventilation system		890	Electrical and Control	900-999		Control and automation		900-949*	Server and IT		950*	Electrical power high voltage (>1000V)		980-989*	Electrical power low voltage		990-999*	<table><tr><th>Pipe Spec list</th><th>Code</th></tr><tr><td>Carbon steel P235TR1</td><td>CSTR</td></tr><tr><td>Carbon steel P235GH</td><td>CSGH</td></tr><tr><td>Preinsulated Carbon steel P235GH</td><td>CSGH-PRI</td></tr><tr><td>Stainless steel pipes 1.4304</td><td>SS16 / SS16-P</td></tr><tr><td>PE100 SDR17</td><td>PE17</td></tr><tr><td>Preinsulated PE100 SDR17</td><td>PE17-PRI</td></tr><tr><td>PE100 SDR11</td><td>PE11</td></tr><tr><td>PE pipes for ventilation</td><td>PEVE</td></tr><tr><td>PE Drain Pipes</td><td>PWW</td></tr><tr><td>Electrical Conduit And Piping</td><td>ELCP</td></tr><tr><td>Ventilation Steel</td><td>VENTS</td></tr><tr><td>Ventilation Plastic</td><td>VENTP</td></tr><tr><td>?</td><td>Unknown</td></tr></table>		Pipe Spec list	Code	Carbon steel P235TR1	CSTR	Carbon steel P235GH	CSGH	Preinsulated Carbon steel P235GH	CSGH-PRI	Stainless steel pipes 1.4304	SS16 / SS16-P	PE100 SDR17	PE17	Preinsulated PE100 SDR17	PE17-PRI	PE100 SDR11	PE11	PE pipes for ventilation	PEVE	PE Drain Pipes	PWW	Electrical Conduit And Piping	ELCP	Ventilation Steel	VENTS	Ventilation Plastic	VENTP	?	Unknown	Structure of the pipeline tagging system		
System:	System number:	
Reception	100-199	
Manure tank		100-109	
Fat/Liquid Substrate tank		110-119	
Dry Dosificator tank		120-129	
FeCl tank		130-139	
Glycerol tank		140-149	
Cereals silo		160-169	
Water tank		170-179	
LPG tank		180-189	
Beets and root crops		190-191	
Feeding in	200-299	
Manure feeding		200-209	
Fat/Liquid Substrate feeding		210-219	
Dry Dosificator		220-229	
FeCl feeding		230-239	
Glycerol feeding		240-249	
Pasteurization before digester		250	
Cereal feeding		260	
Water feeding		270	
Oxygen/air dozing		280	
Mixing tank		290	
Digester	300-399	
Primary Digester		300-309	
Secondary Digester		310-319	
Tertiary Digester		320-329	
Line X		3X0	
Heating system	400-499	
Heating system		400-449	
Cooling system		450-459	
Feeding out	500-599	
Pump		500 - 509	
Pasteurization after digester		550	
Biofertilizer tank	600-699	
Biofertilizer tank 1		601	
Biofertilizer tank 2		602	
Separation		610 - 619	
Gas treatment	700-799	
Components on general gas pipe		700	
Condensate pit		710	
Flare		720	
Upgrading unit/CHP/boiler		730	
Stripper air combustion		740	
RTO		750	
High pressure compressor station		760	
LNG plant		770	
Propane dosing		780	
Support system	800-899	
Instrument air		800	
Hydraulic system		805	
Water		810	
Backflow protection system		815	
Heat tracing cable		820	
Car wash		830	
Building/container		840	
Pumpwell		850	
Oil separator		860	
		870	
Dosing equipment		880	
Odour cntro/ventilation system		890	
Electrical and Control	900-999	
Control and automation		900-949*	
Server and IT		950*	
Electrical power high voltage (>1000V)		980-989*	
Electrical power low voltage		990-999*	
Pipe Spec list	Code	
Carbon steel P235TR1	CSTR	
Carbon steel P235GH	CSGH	
Preinsulated Carbon steel P235GH	CSGH-PRI	
Stainless steel pipes 1.4304	SS16 / SS16-P	
PE100 SDR17	PE17	
Preinsulated PE100 SDR17	PE17-PRI	
PE100 SDR11	PE11	
PE pipes for ventilation	PEVE	
PE Drain Pipes	PWW	
Electrical Conduit And Piping	ELCP	
Ventilation Steel	VENTS	
Ventilation Plastic	VENTP	
?	Unknown	
The pipetag consists of various information about the pipe Full pipeline tag as shown below Size-PipeSpec-Area-Service (Medie)-Serial number [100 PE17 201 LM 01] Example Two (2) digits. Starts with 01 [01] Two (2) to four (4) characters (letters) [LM - Liquid manure] Three (3) digits [201 - Manure feeding in tank 1] Pipe Spec name [PE17 - PE100 SDR17] Pipe size DN indication for Metric pipes OD indication for PE-pipe [This example is OD 100 mm]			The pipe tag will be shown on the P&ID as follows: PipeSpec-Size Area-Service-Serialnumber Example of line tag notation on P&ID: PE17-110 201-LM-01 Line color corresponding to table above. The part below the pipeline is the Unique Line Tag. Unique Line Tag is generated automatically when creating complete Line Tag. Unique Line Tag is used by the P3D system when designing pipes in the 3D model and when generating Isometrics.	
<table><tr><td>Rev. Nr.:</td><td>Rev. Date:</td><td>Rev. Description:</td></tr><tr><td>Builder:</td><td>ST1</td><td></td></tr><tr><td>Project:</td><td>SLK</td><td></td></tr><tr><td>Subject:</td><td>PID Legend</td><td></td></tr><tr><td>Rev. 6</td><td></td><td></td></tr><tr><td>Int.:MDC</td><td>QC.:CM</td><td>APP.: Date: 15-10-2025</td></tr><tr><td colspan="3"> LUNDSBY RENEWABLE SOLUTIONS Lundsby Renewable Solutions A/S, Hjarbækvej 65, 8831 Legstrup Tlf.: +45 96 49 43 00 Info@lundsby.dk This Drawing is subject to copyright and may not be reproduced without permission from Lundsby Renewable Solutions A/S </td></tr></table>			Rev. Nr.:	Rev. Date:	Rev. Description:	Builder:	ST1		Project:	SLK		Subject:	PID Legend		Rev. 6			Int.:MDC	QC.:CM	APP.: Date: 15-10-2025	LUNDSBY RENEWABLE SOLUTIONS Lundsby Renewable Solutions A/S, Hjarbækvej 65, 8831 Legstrup Tlf.: +45 96 49 43 00 Info@lundsby.dk This Drawing is subject to copyright and may not be reproduced without permission from Lundsby Renewable Solutions A/S			Project nr.:1768 Drawing nr.: PID Legend FORMAT: A1	
Rev. Nr.:	Rev. Date:	Rev. Description:	
Builder:	ST1	
Project:	SLK	
Subject:	PID Legend	
Rev. 6	
Int.:MDC	QC.:CM	APP.: Date: 15-10-2025	
LUNDSBY RENEWABLE SOLUTIONS Lundsby Renewable Solutions A/S, Hjarbækvej 65, 8831 Legstrup Tlf.: +45 96 49 43 00 Info@lundsby.dk This Drawing is subject to copyright and may not be reproduced without permission from Lundsby Renewable Solutions A/S	
1	2	3	4	5	6	7	8	

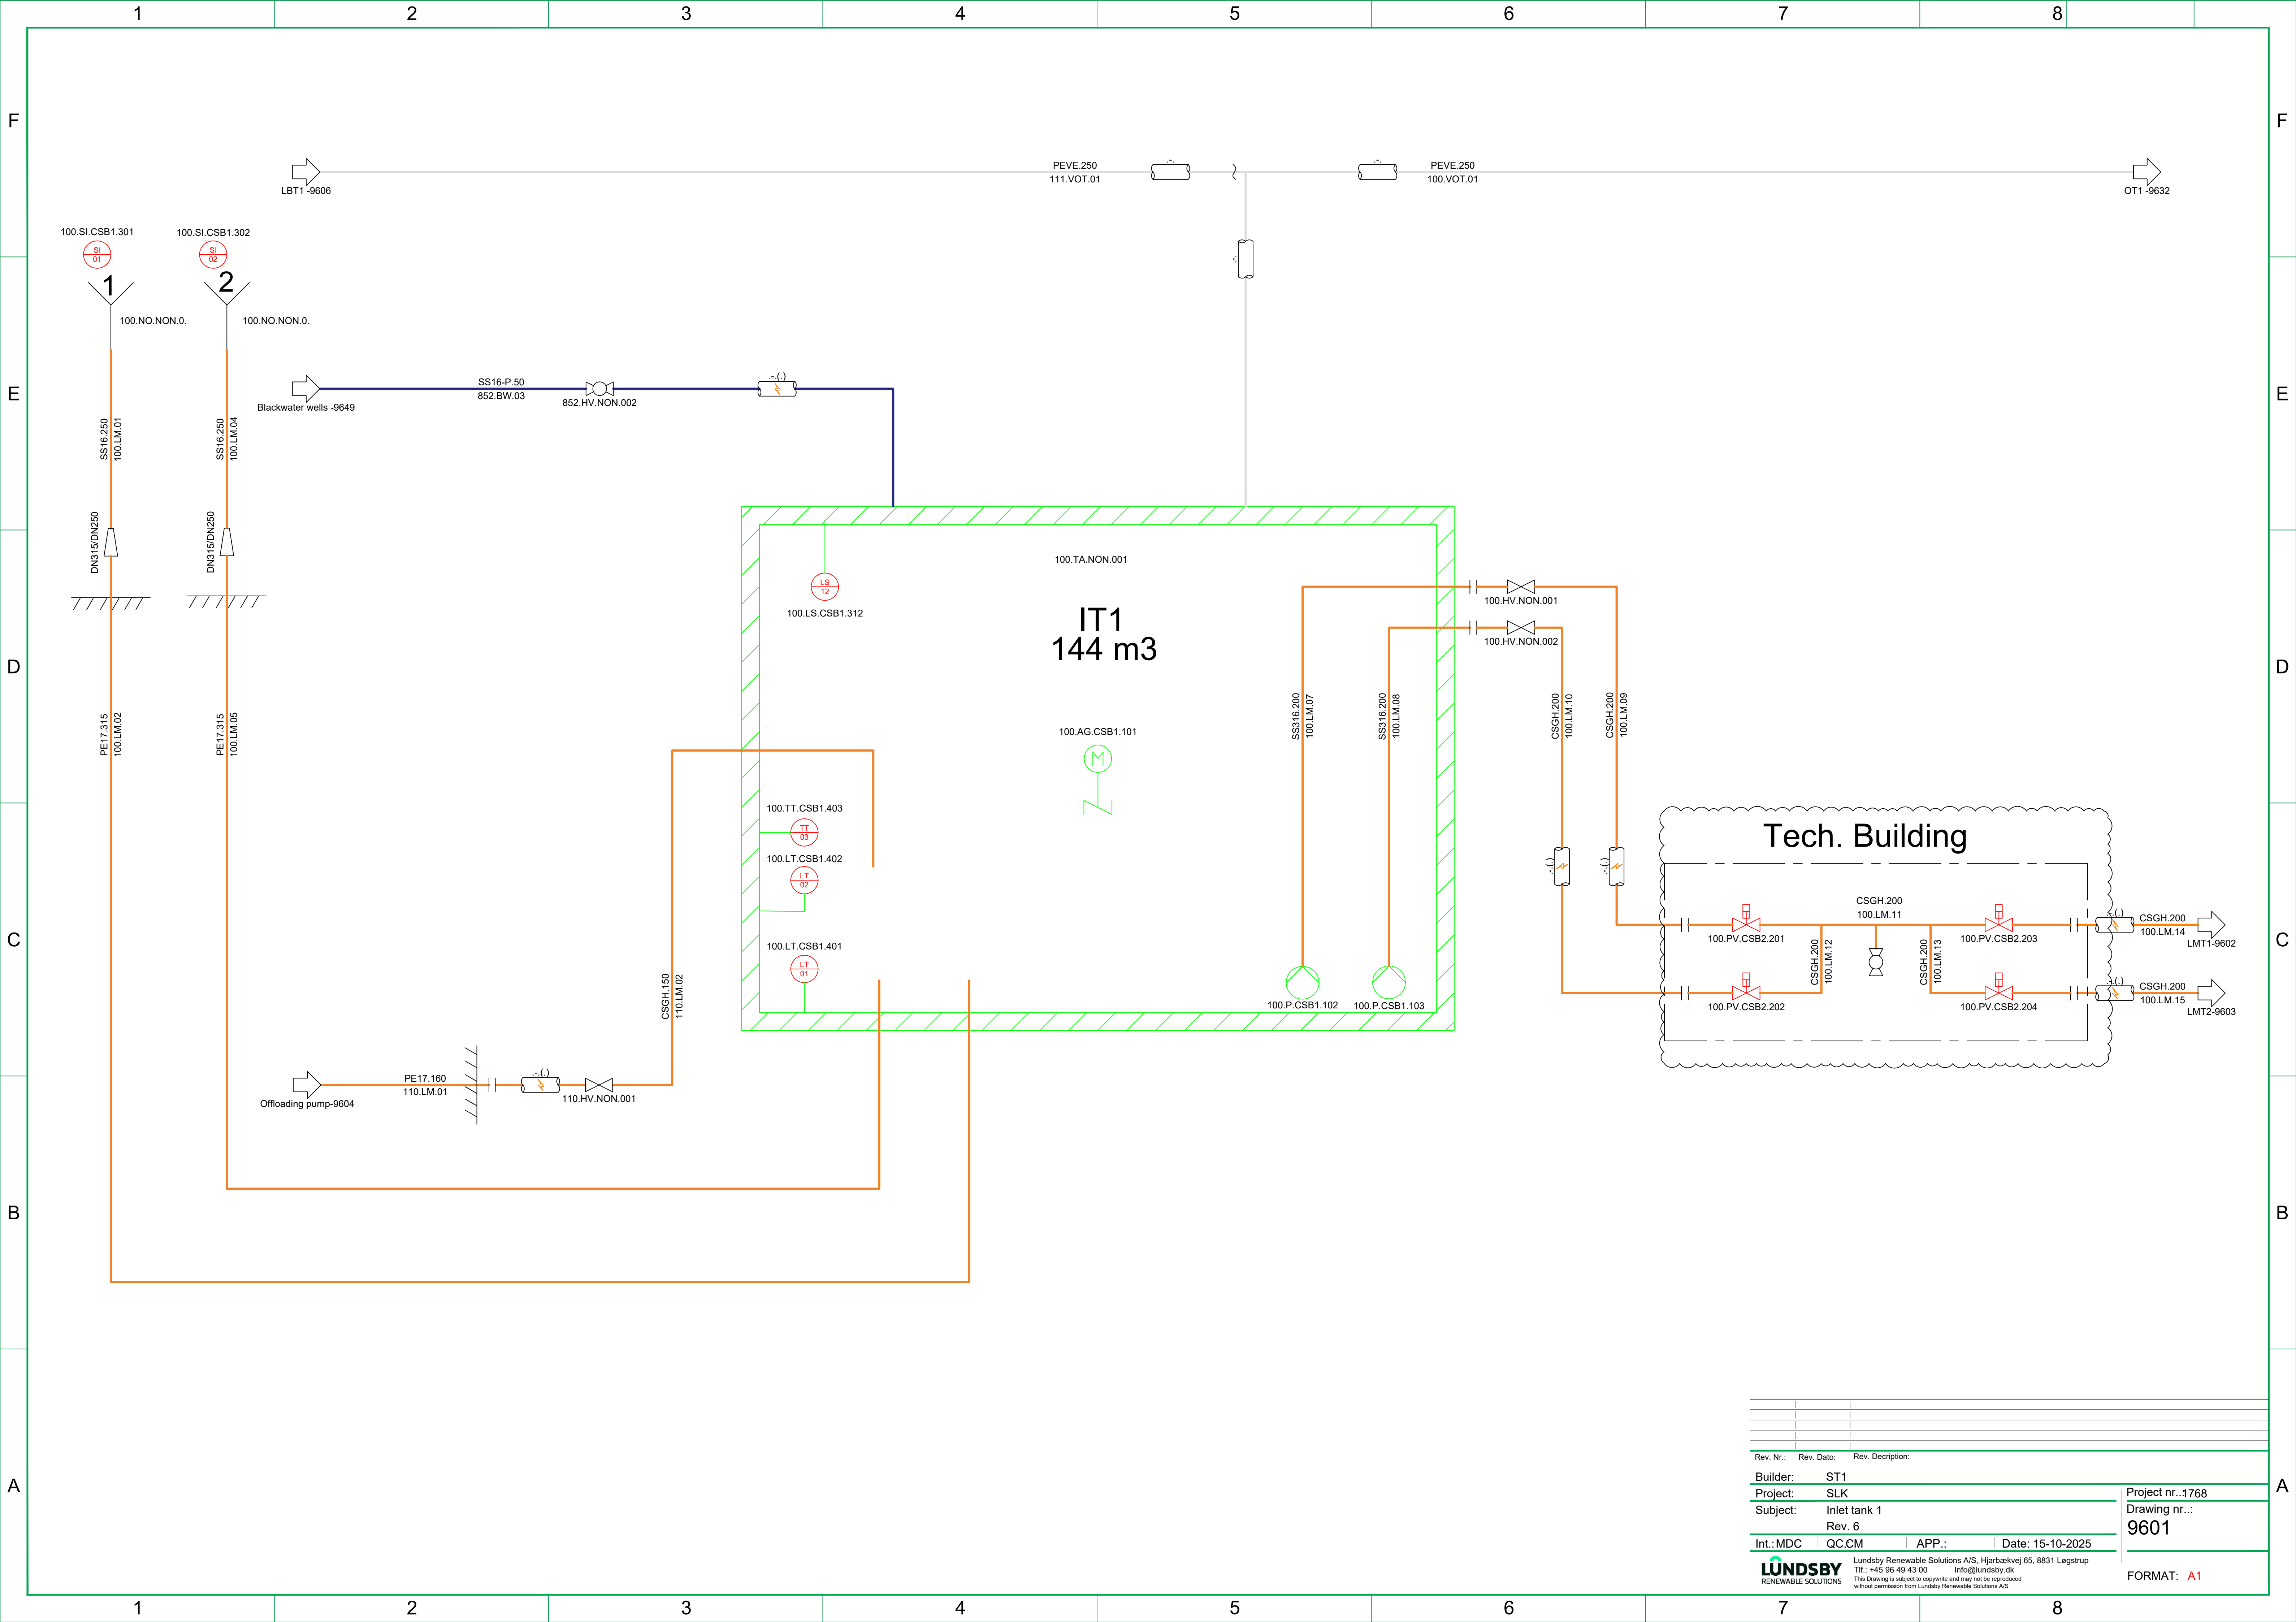


Rev. Nr.:	Rev. Dato:	Rev. Description:
Builder:	ST1	
Project:	SLK	
Subject:	Inlet tank 1	
	Rev. 6	
Int.:MDC	QC:CM	APP.:
		Date: 15-10-2025
LUNDSBY RENEWABLE SOLUTIONS		
Lundsby Renewable Solutions A/S, Hjarbækvej 65, 8831 Løgstrup Tlf.: +45 96 49 43 00 Info@lundsby.dk This drawing is subject to copyright and may not be reproduced without permission from Lundsby Renewable Solutions A/S		
Project nr.:1768		Drawing nr.: 9601
FORMAT: A1		

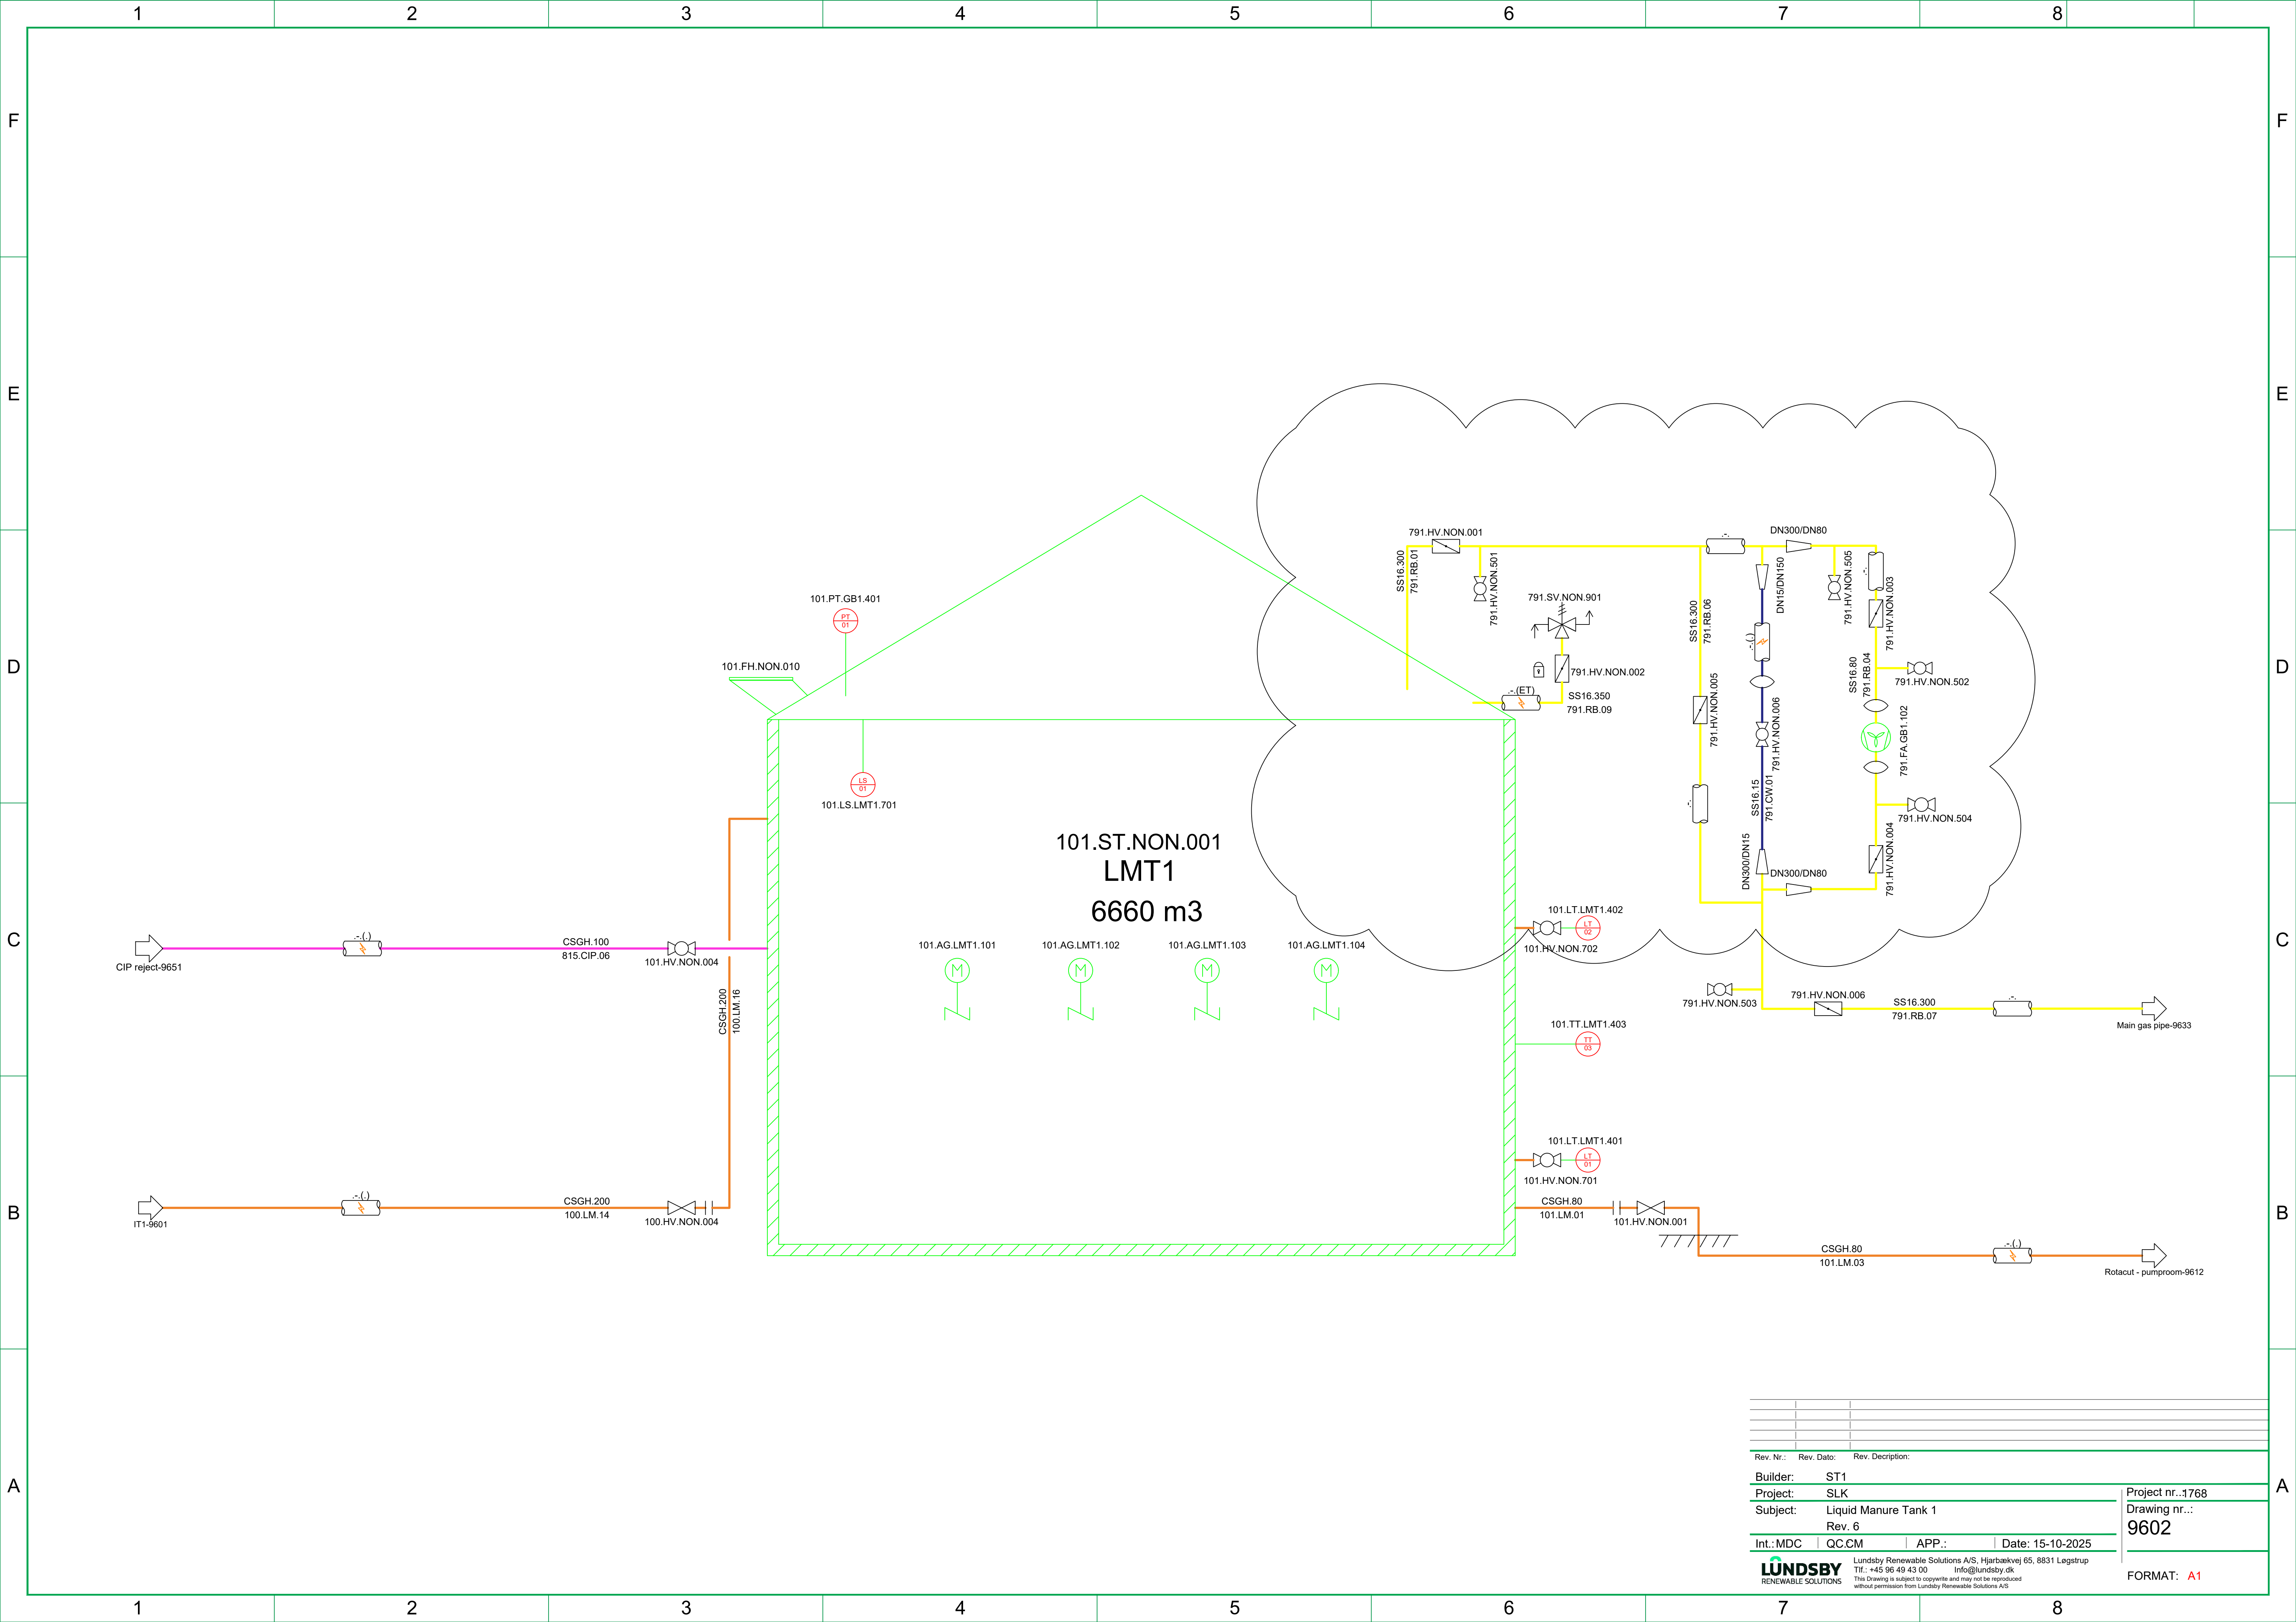


Rev. Nr.:	Rev. Dato:	Rev. Description:	
Builder:	ST1		
Project:	SLK		
Subject:	Liquid Manure Tank 1		
Rev. 6			
Int.:MDC	QC:CM	APP.:	Date: 15-10-2025
LUNDSBY RENEWABLE SOLUTIONS			Lundsby Renewable Solutions A/S, Hjarbækvej 65, 8831 Løgstrup Tlf.: +45 96 49 43 00 Info@lundsby.dk This Drawing is subject to copyright and may not be reproduced without permission from Lundsby Renewable Solutions A/S
Project nr.:1768 Drawing nr.: 9602			FORMAT: A1

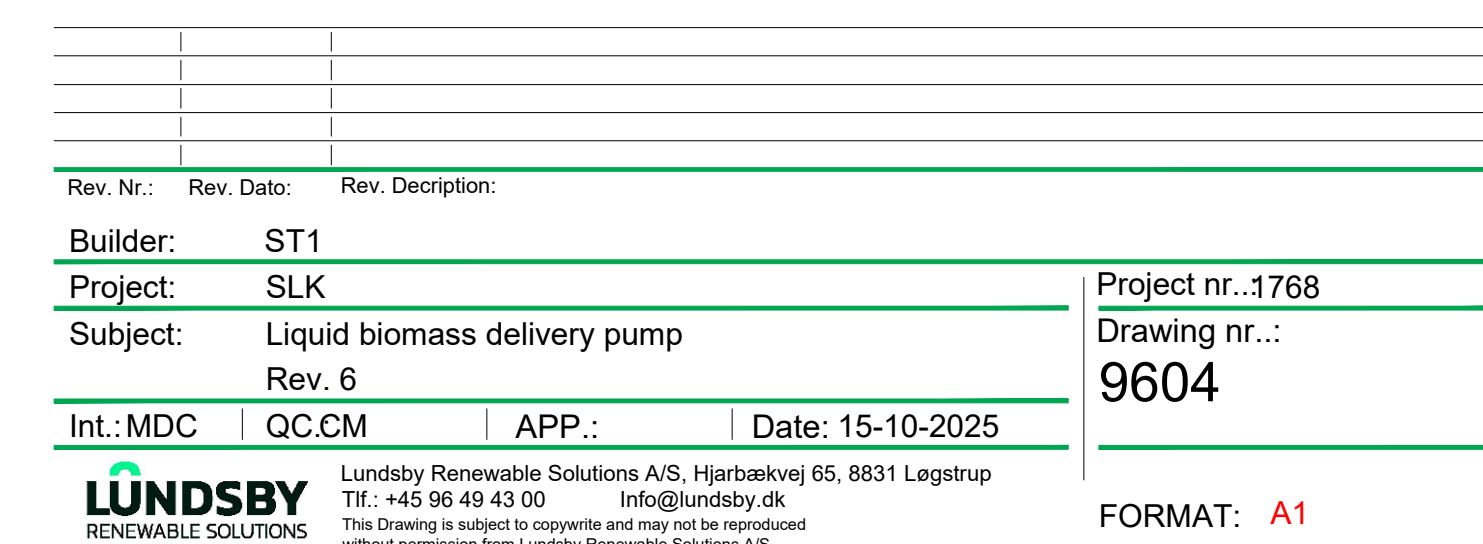


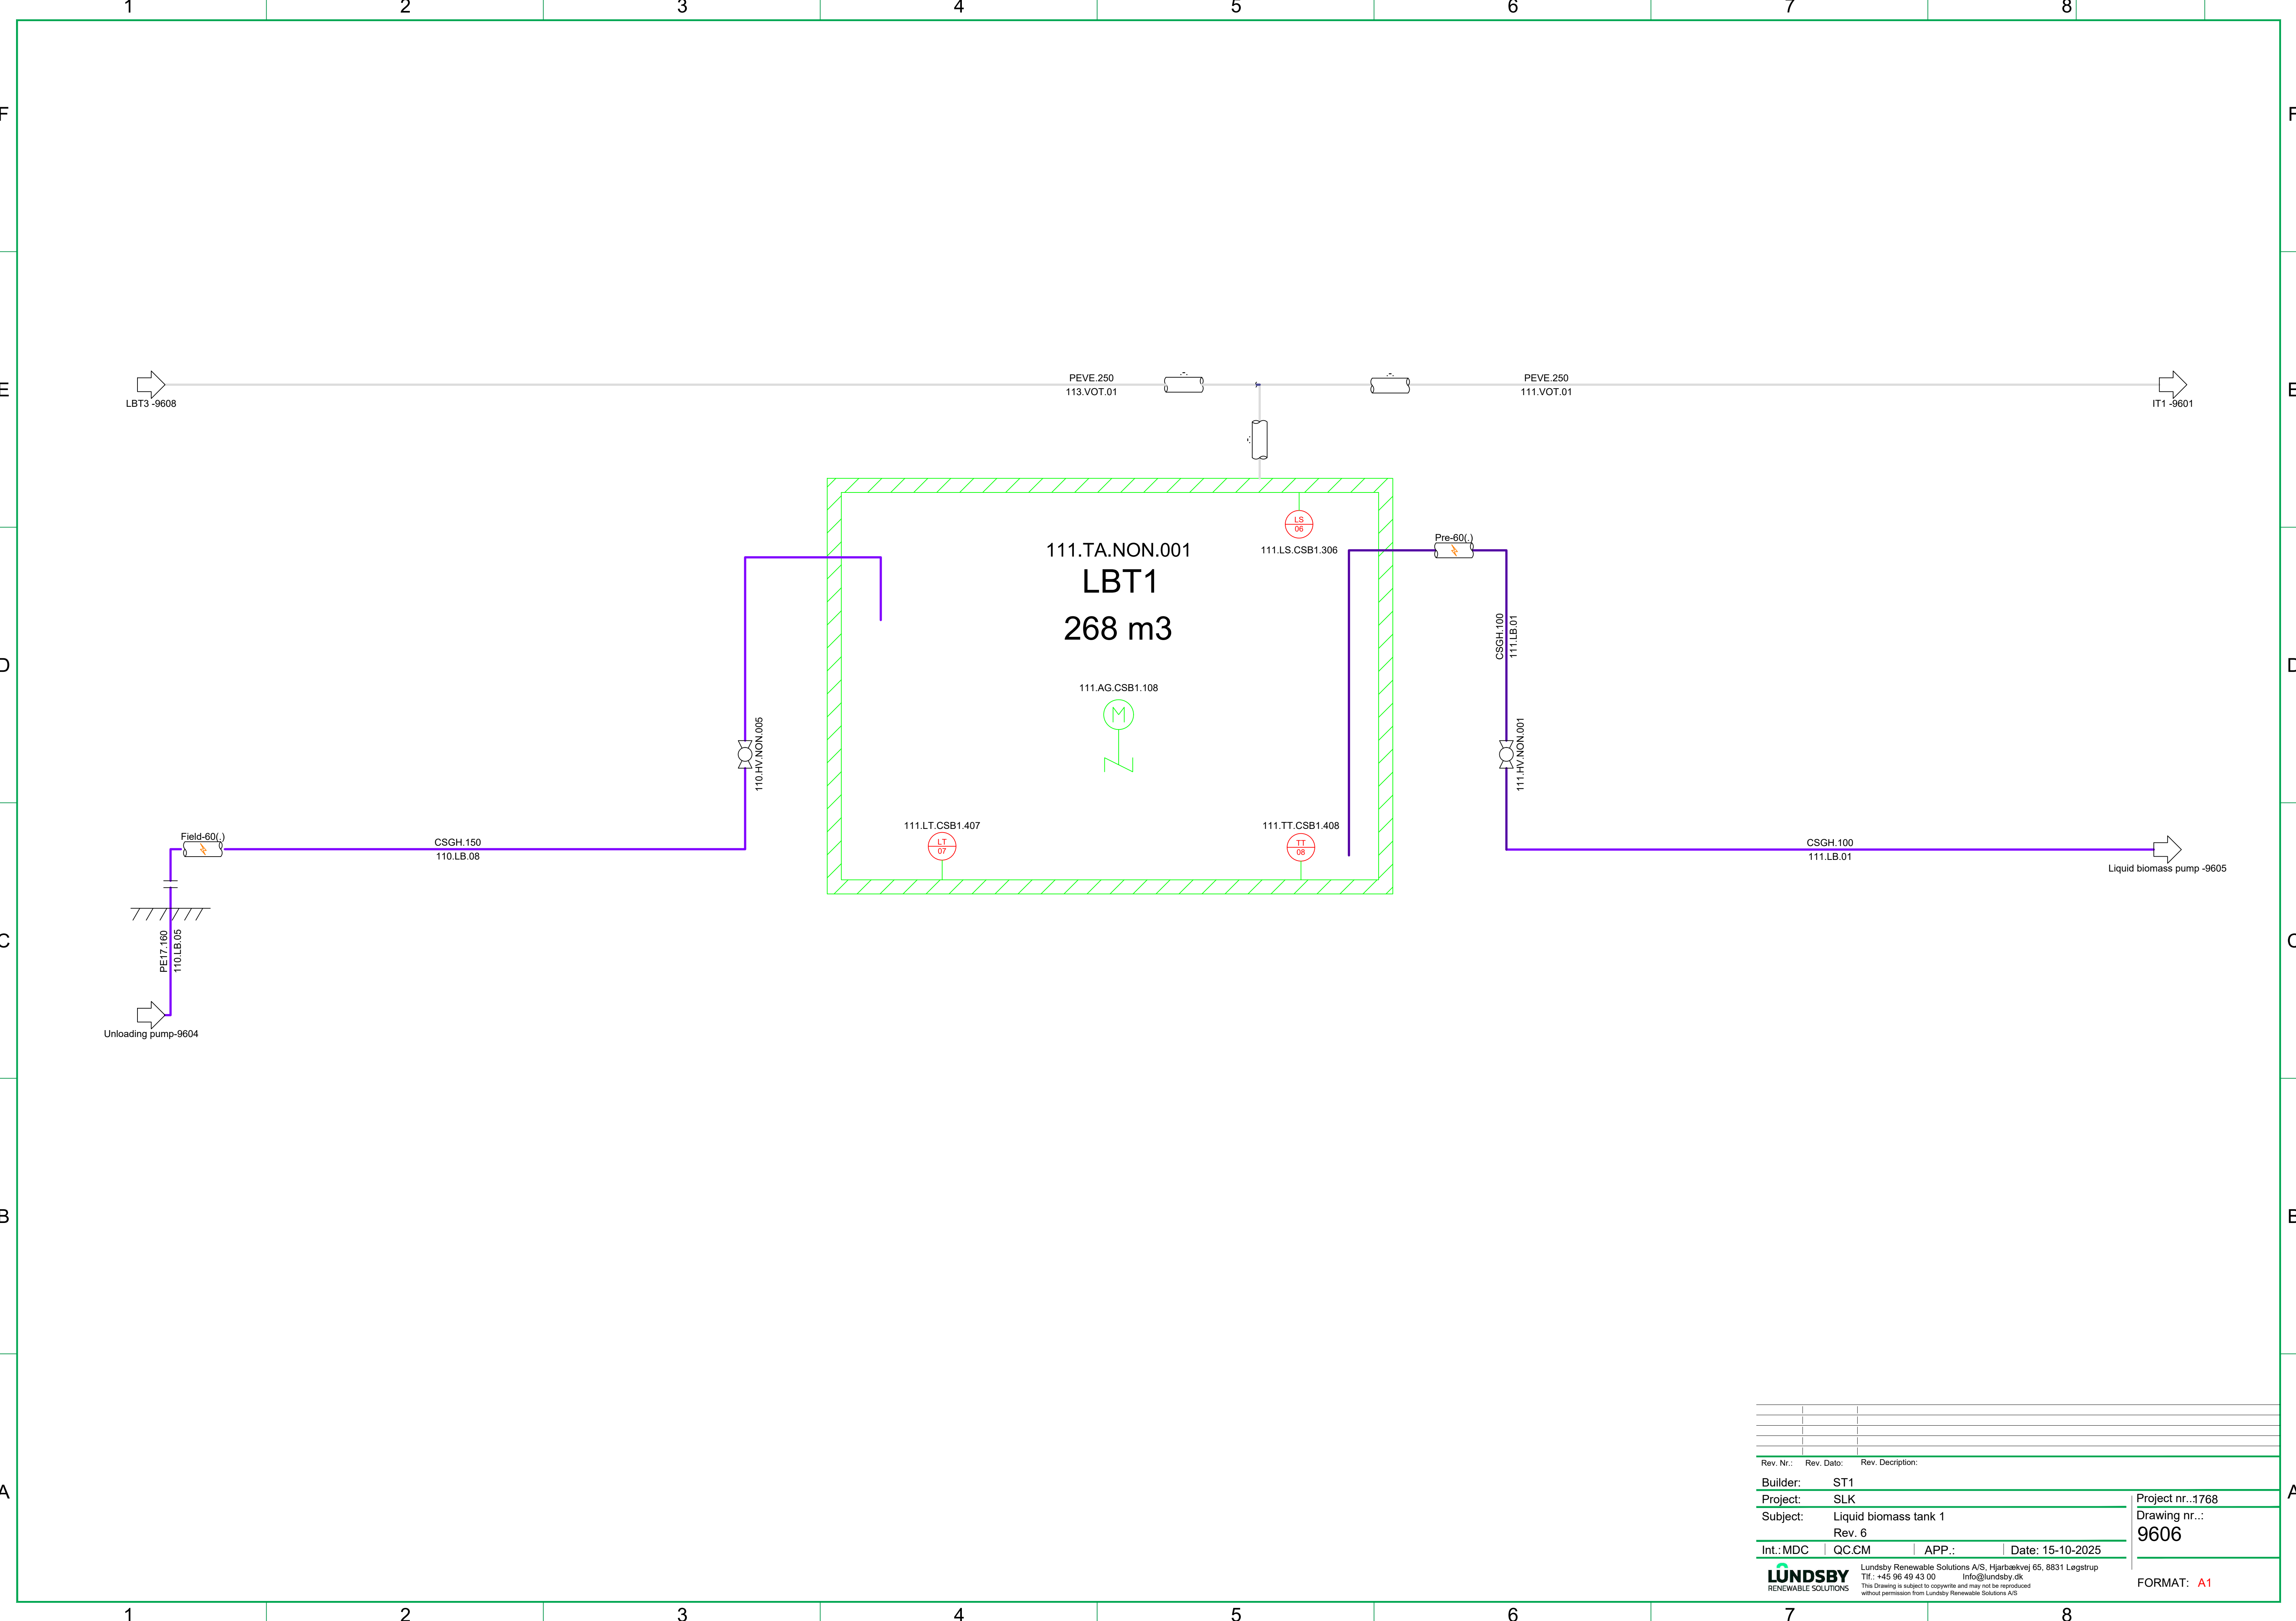


Rev. Nr.:	Rev. Dato:	Rev. Description:	Project nr...1768
Builder:	ST1		Drawing nr...: 9606
Project:	SLK		
Subject:	Liquid biomass tank 1		
	Rev. 6		
Int.:MDC	QC.CM	APP.:	Date: 15-10-2025
LUNDSBY RENEWABLE SOLUTIONS			FORMAT: A1

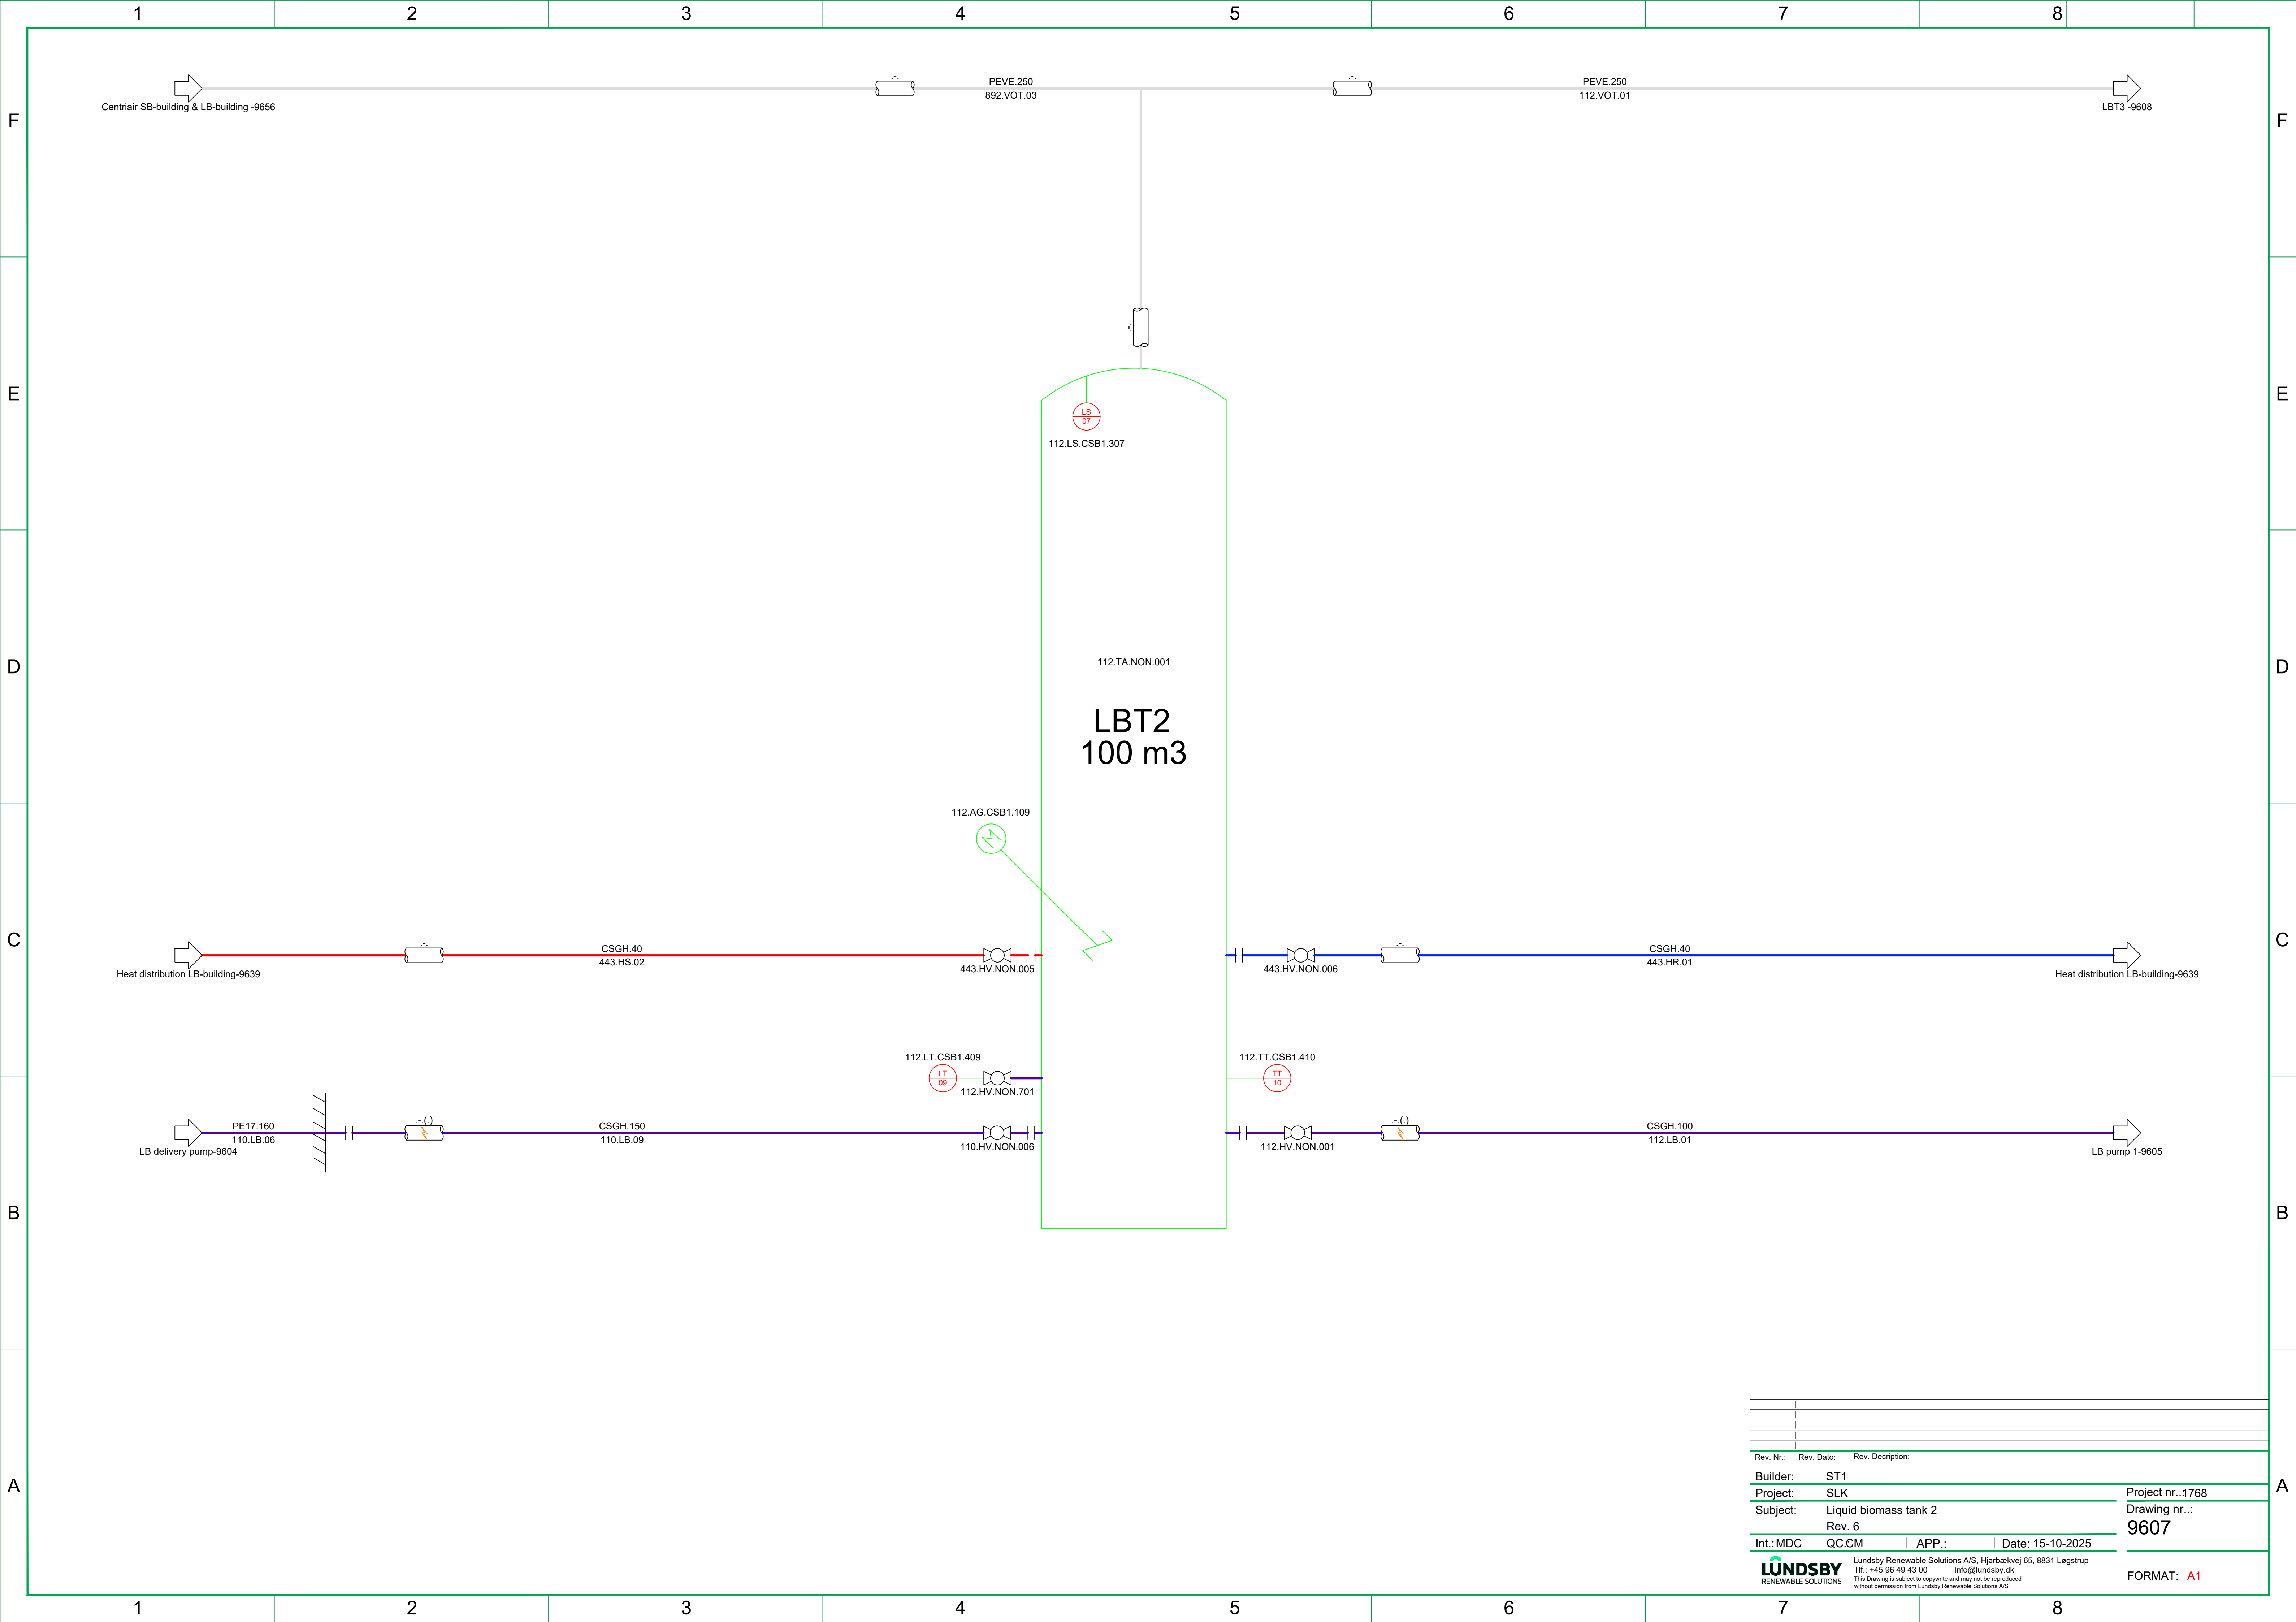


Rev. Nr.:	Rev. Dato:	Rev. Description:
Builder:	ST1	
Project:	SLK	
Subject:	Liquid biomass tank 2	
Rev. 6		
Int.:MDC	QC:CM	APP.:Date: 15-10-2025
LUNDSBY RENEWABLE SOLUTIONS		
Lundsby Renewable Solutions A/S, Hjarbækvej 65, 8831 Løgstrup Tlf.: +45 96 49 43 00 Info@lundsby.dk This Drawing is subject to copyright and may not be reproduced without permission from Lundsby Renewable Solutions A/S		
Project nr...1768 Drawing nr...: 9607		FORMAT: A1

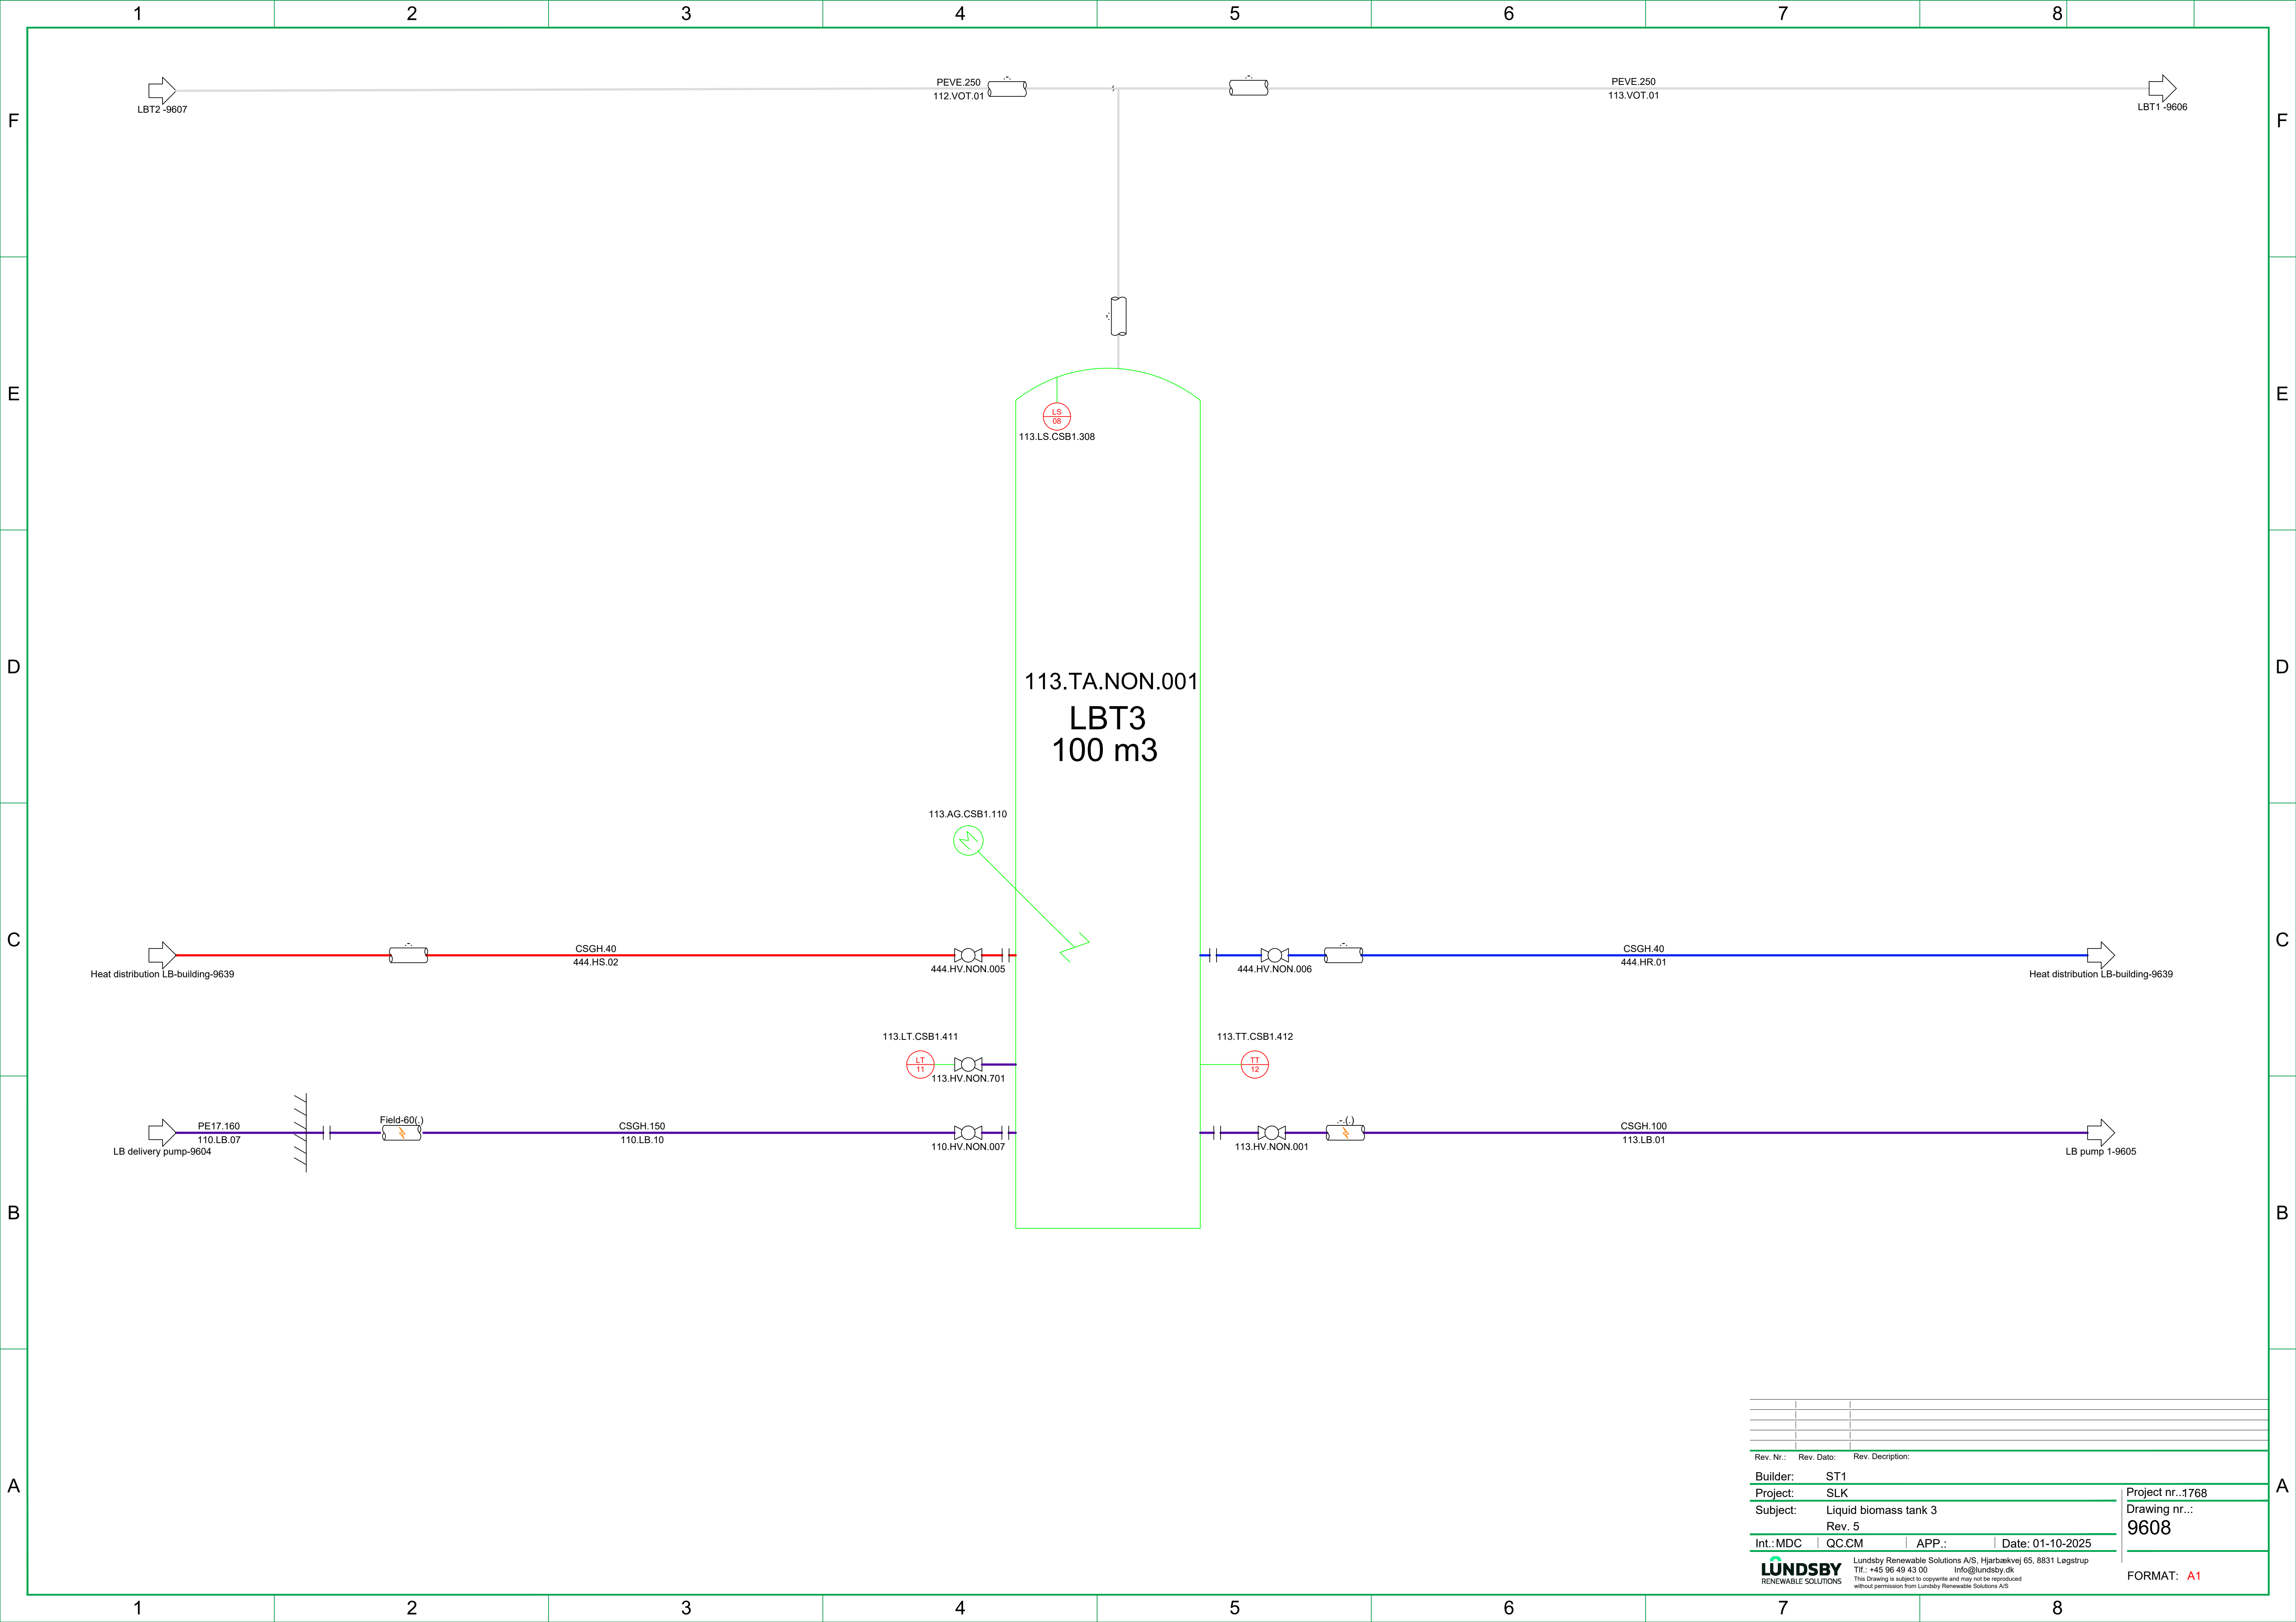


Rev. Nr.:	Rev. Dato:	Rev. Description:	
Builder:	ST1		
Project:	SLK		
Subject:	Liquid biomass tank 3		
	Rev. 5		
Int.:MDC	QC:CM	APP.:	Date: 01-10-2025
		Lundsby Renewable Solutions A/S, Hjarbækvej 65, 8831 Løgstrup Tlf.: +45 96 49 43 00 Info@lundsby.dk This Drawing is subject to copyright and may not be reproduced without permission from Lundsby Renewable Solutions A/S	
		Project nr.:1768 Drawing nr.: 9608	
		FORMAT: A1	

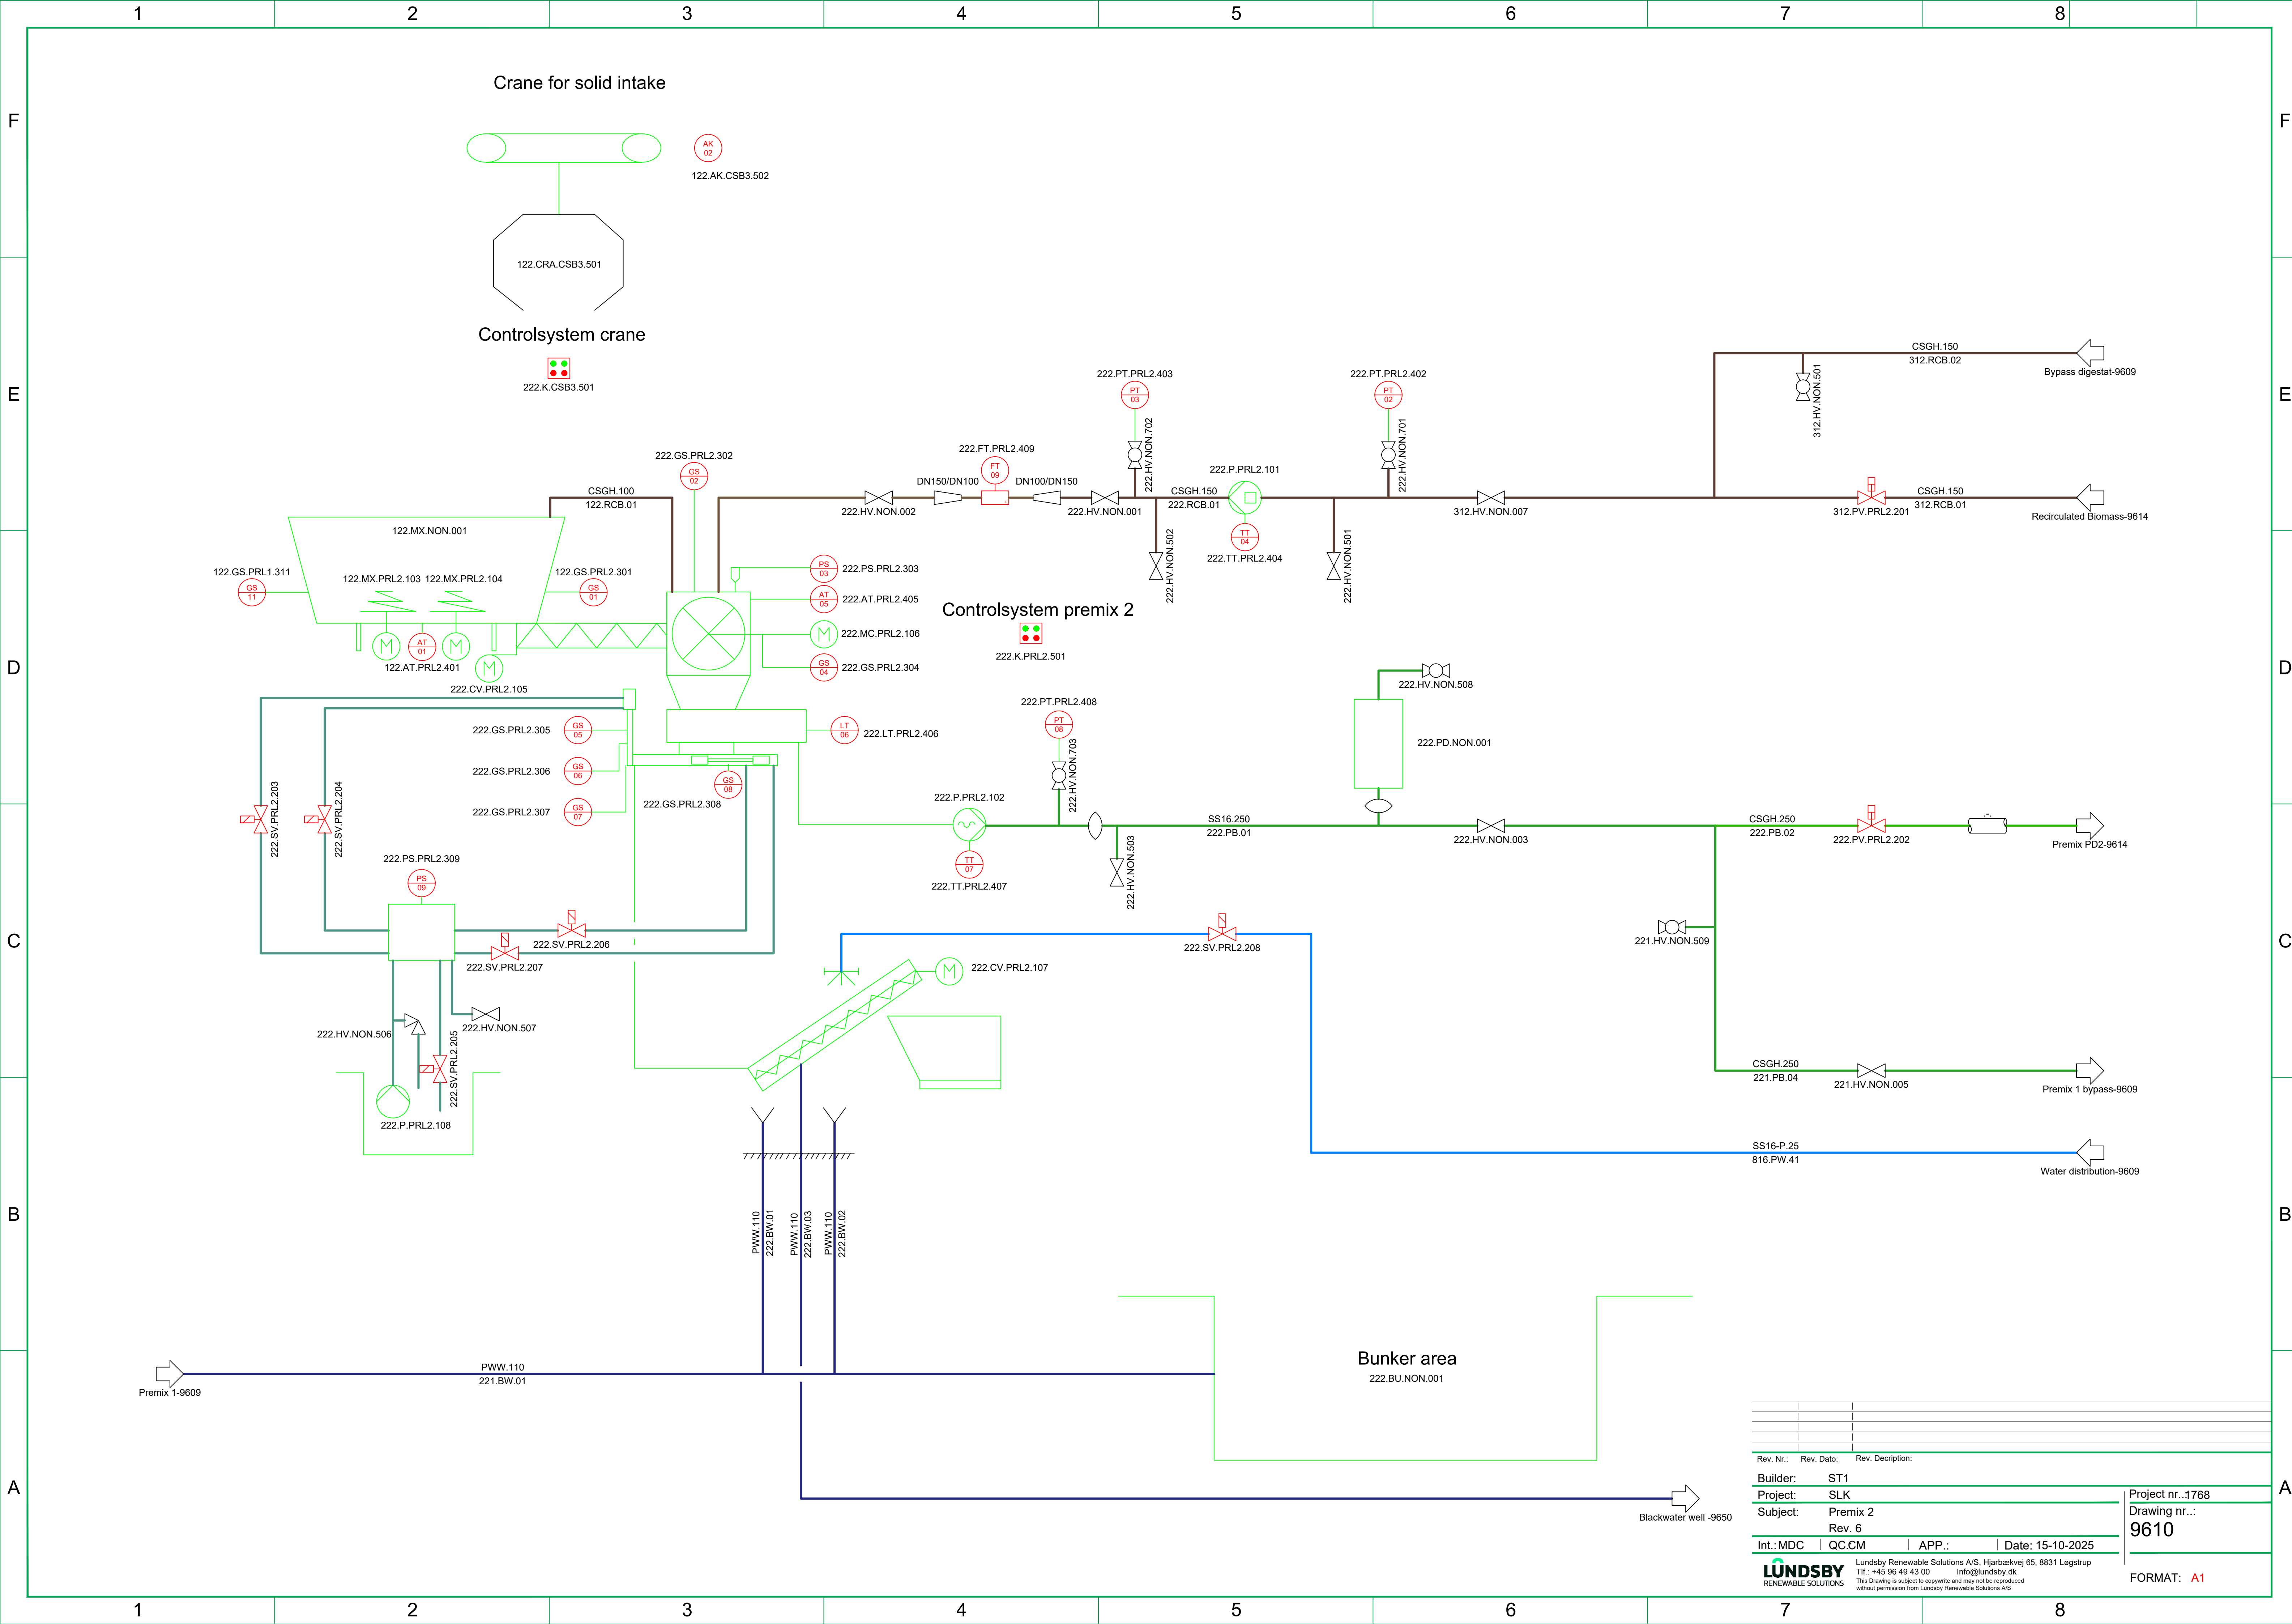

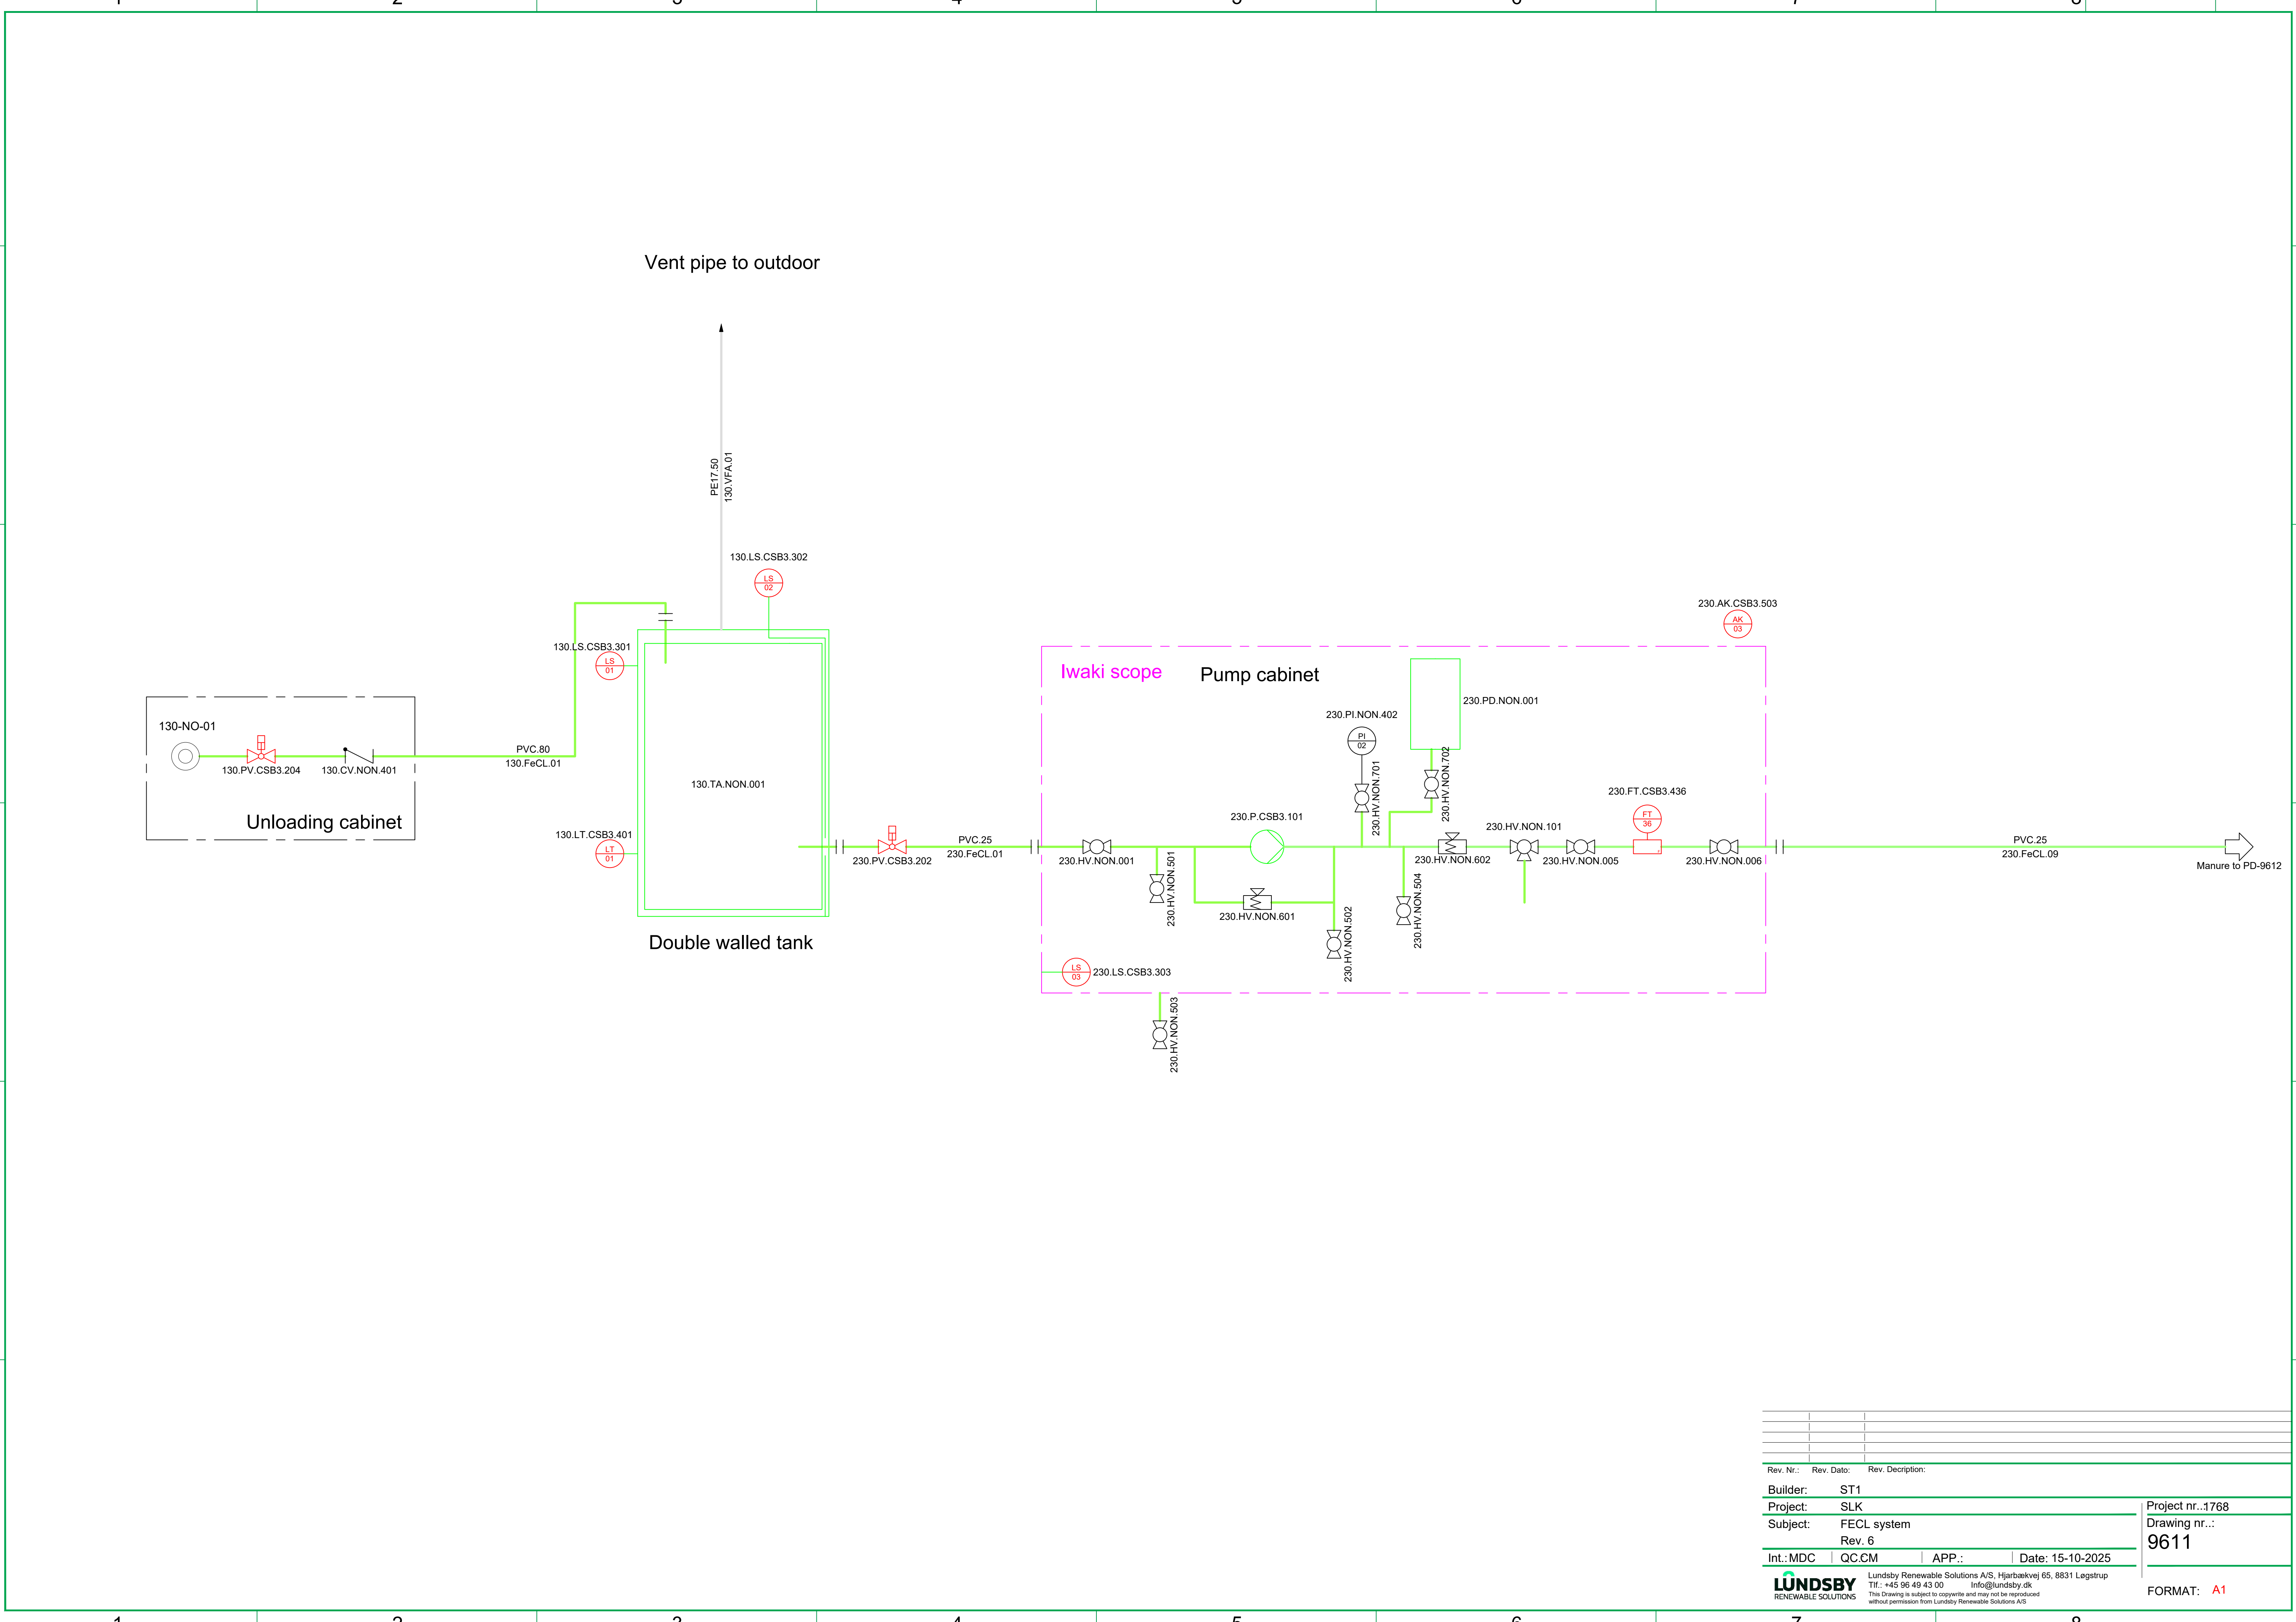


Rev. Nr.:	Rev. Dato:	Rev. Description:			
Builder:	ST1				
Project:	SLK				
Subject:	FECL system				
	Rev. 6				
Int.: MDC	QC.CM	APP.:	Date: 15-10-2025		
 LUNDSBY RENEWABLE SOLUTIONS Lundsby Renewable Solutions A/S, Hjarbækvej 65, 8831 Løgstrup Tlf.: +45 96 49 43 00 Info@lundsby.dk This Drawing is subject to copyright and may not be reproduced without permission from Lundsby Renewable Solutions A/S					
			Project nr...1768		
			Drawing nr...: 9611		
			FORMAT: A1		

Pumphouse 2

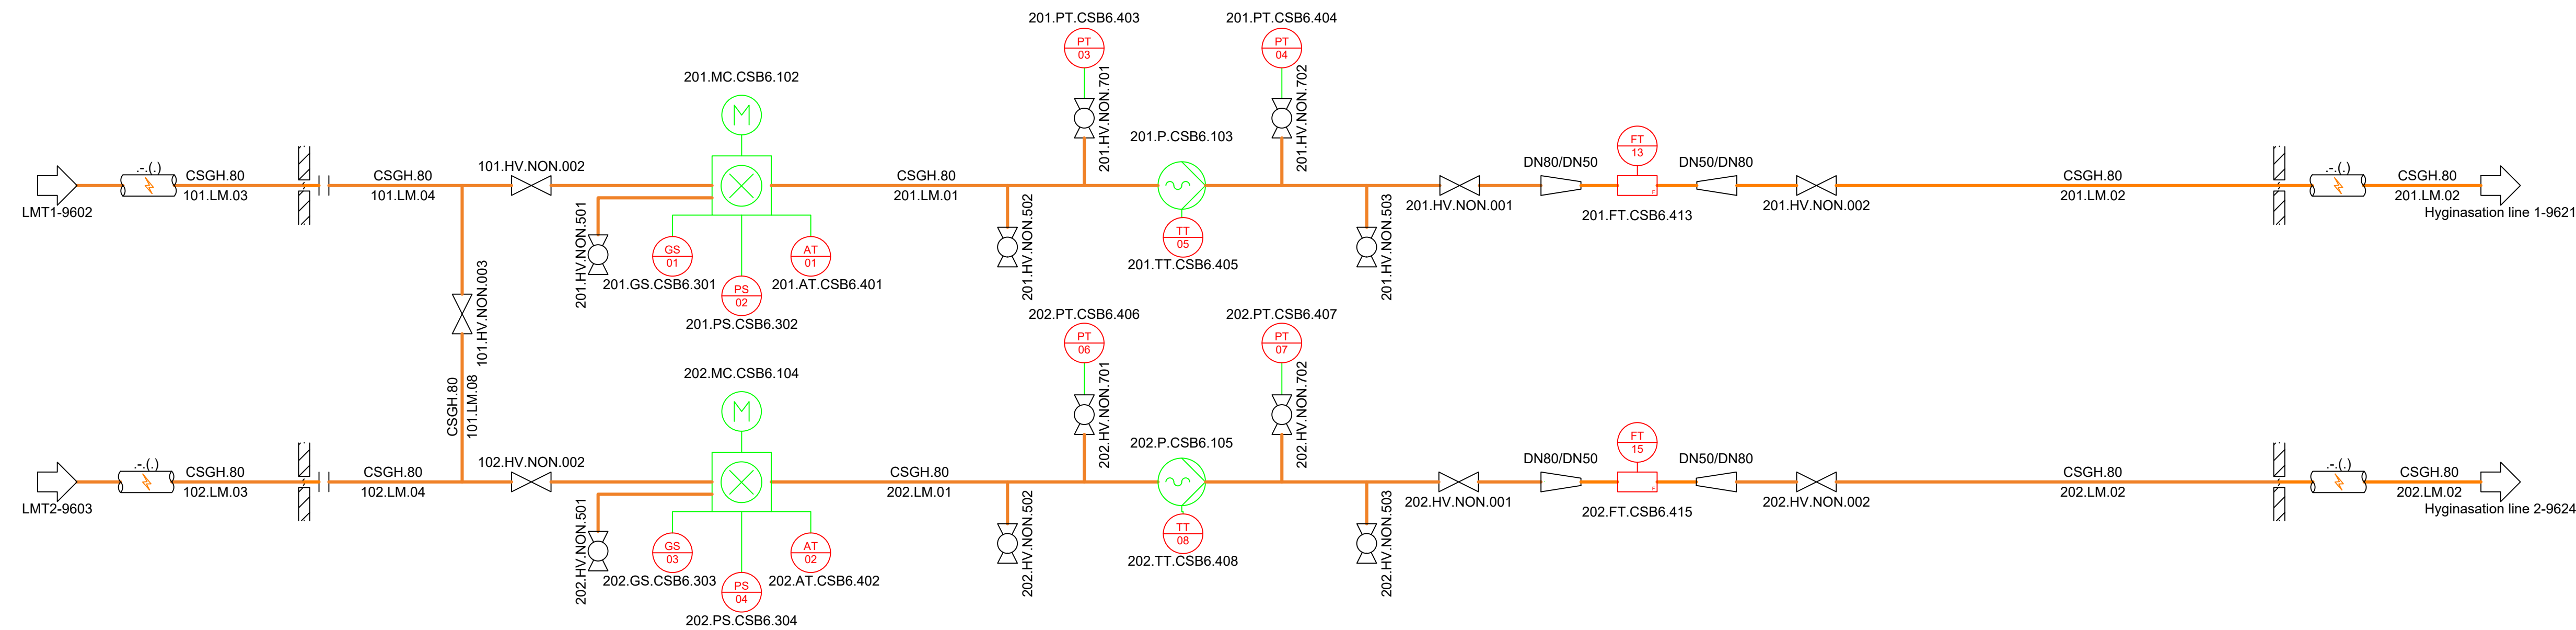


Tech
building


SB-building

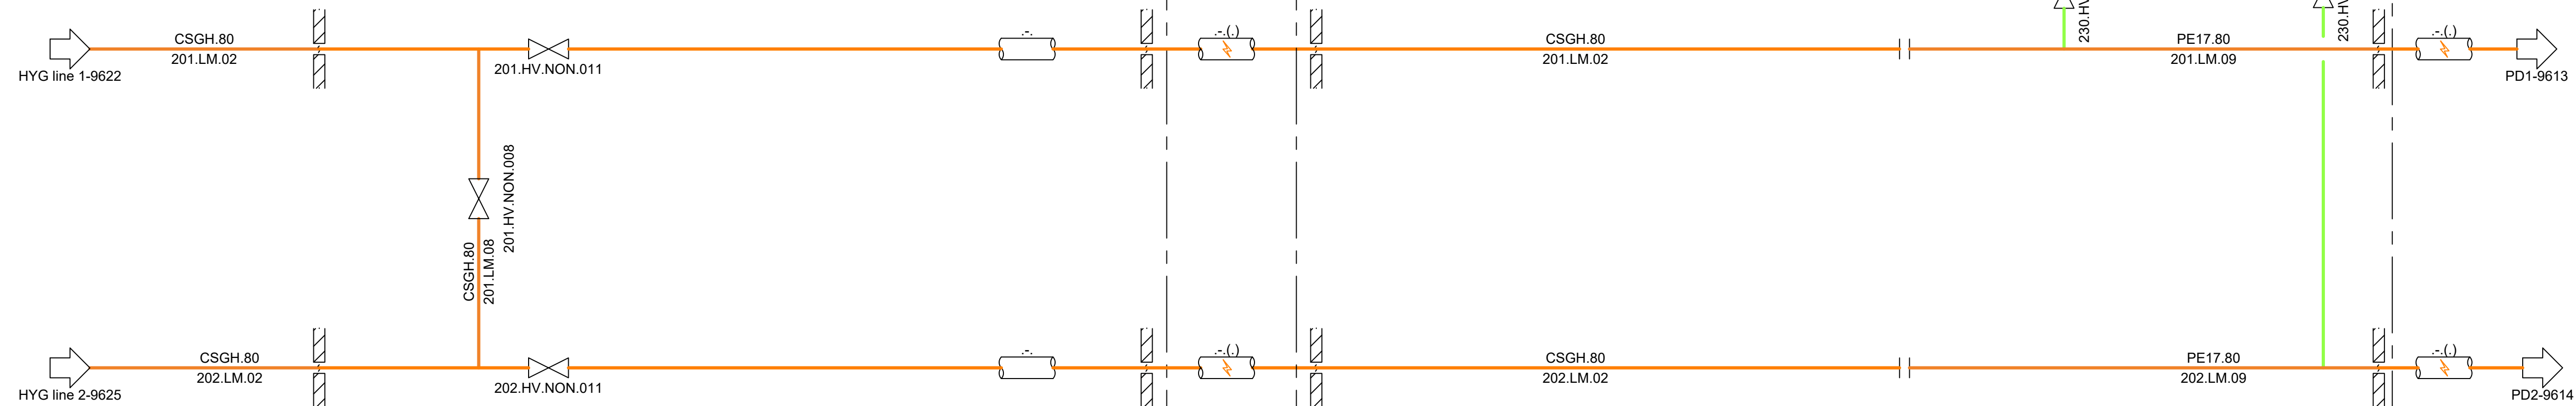


Rev. Nr.:	Rev. Dato:	Rev. Description:
Builder:	ST1	
Project:	SLK	
Subject:	Liquid manure pump	
Rev. 6		
Int.: MDC	QC.CM	APP.:
Date: 15-10-2025		
LUNDSBY RENEWABLE SOLUTIONS		
Lundsby Renewable Solutions A/S, Hjarbækvej 65, 8831 Løgstrup Tlf.: +45 96 49 43 00 Info@lundsby.dk This Drawing is subject to copyright and may not be reproduced without permission from Lundsby Renewable Solutions A/S		
Project nr.: 1768 Drawing nr.: 9612		FORMAT: A1

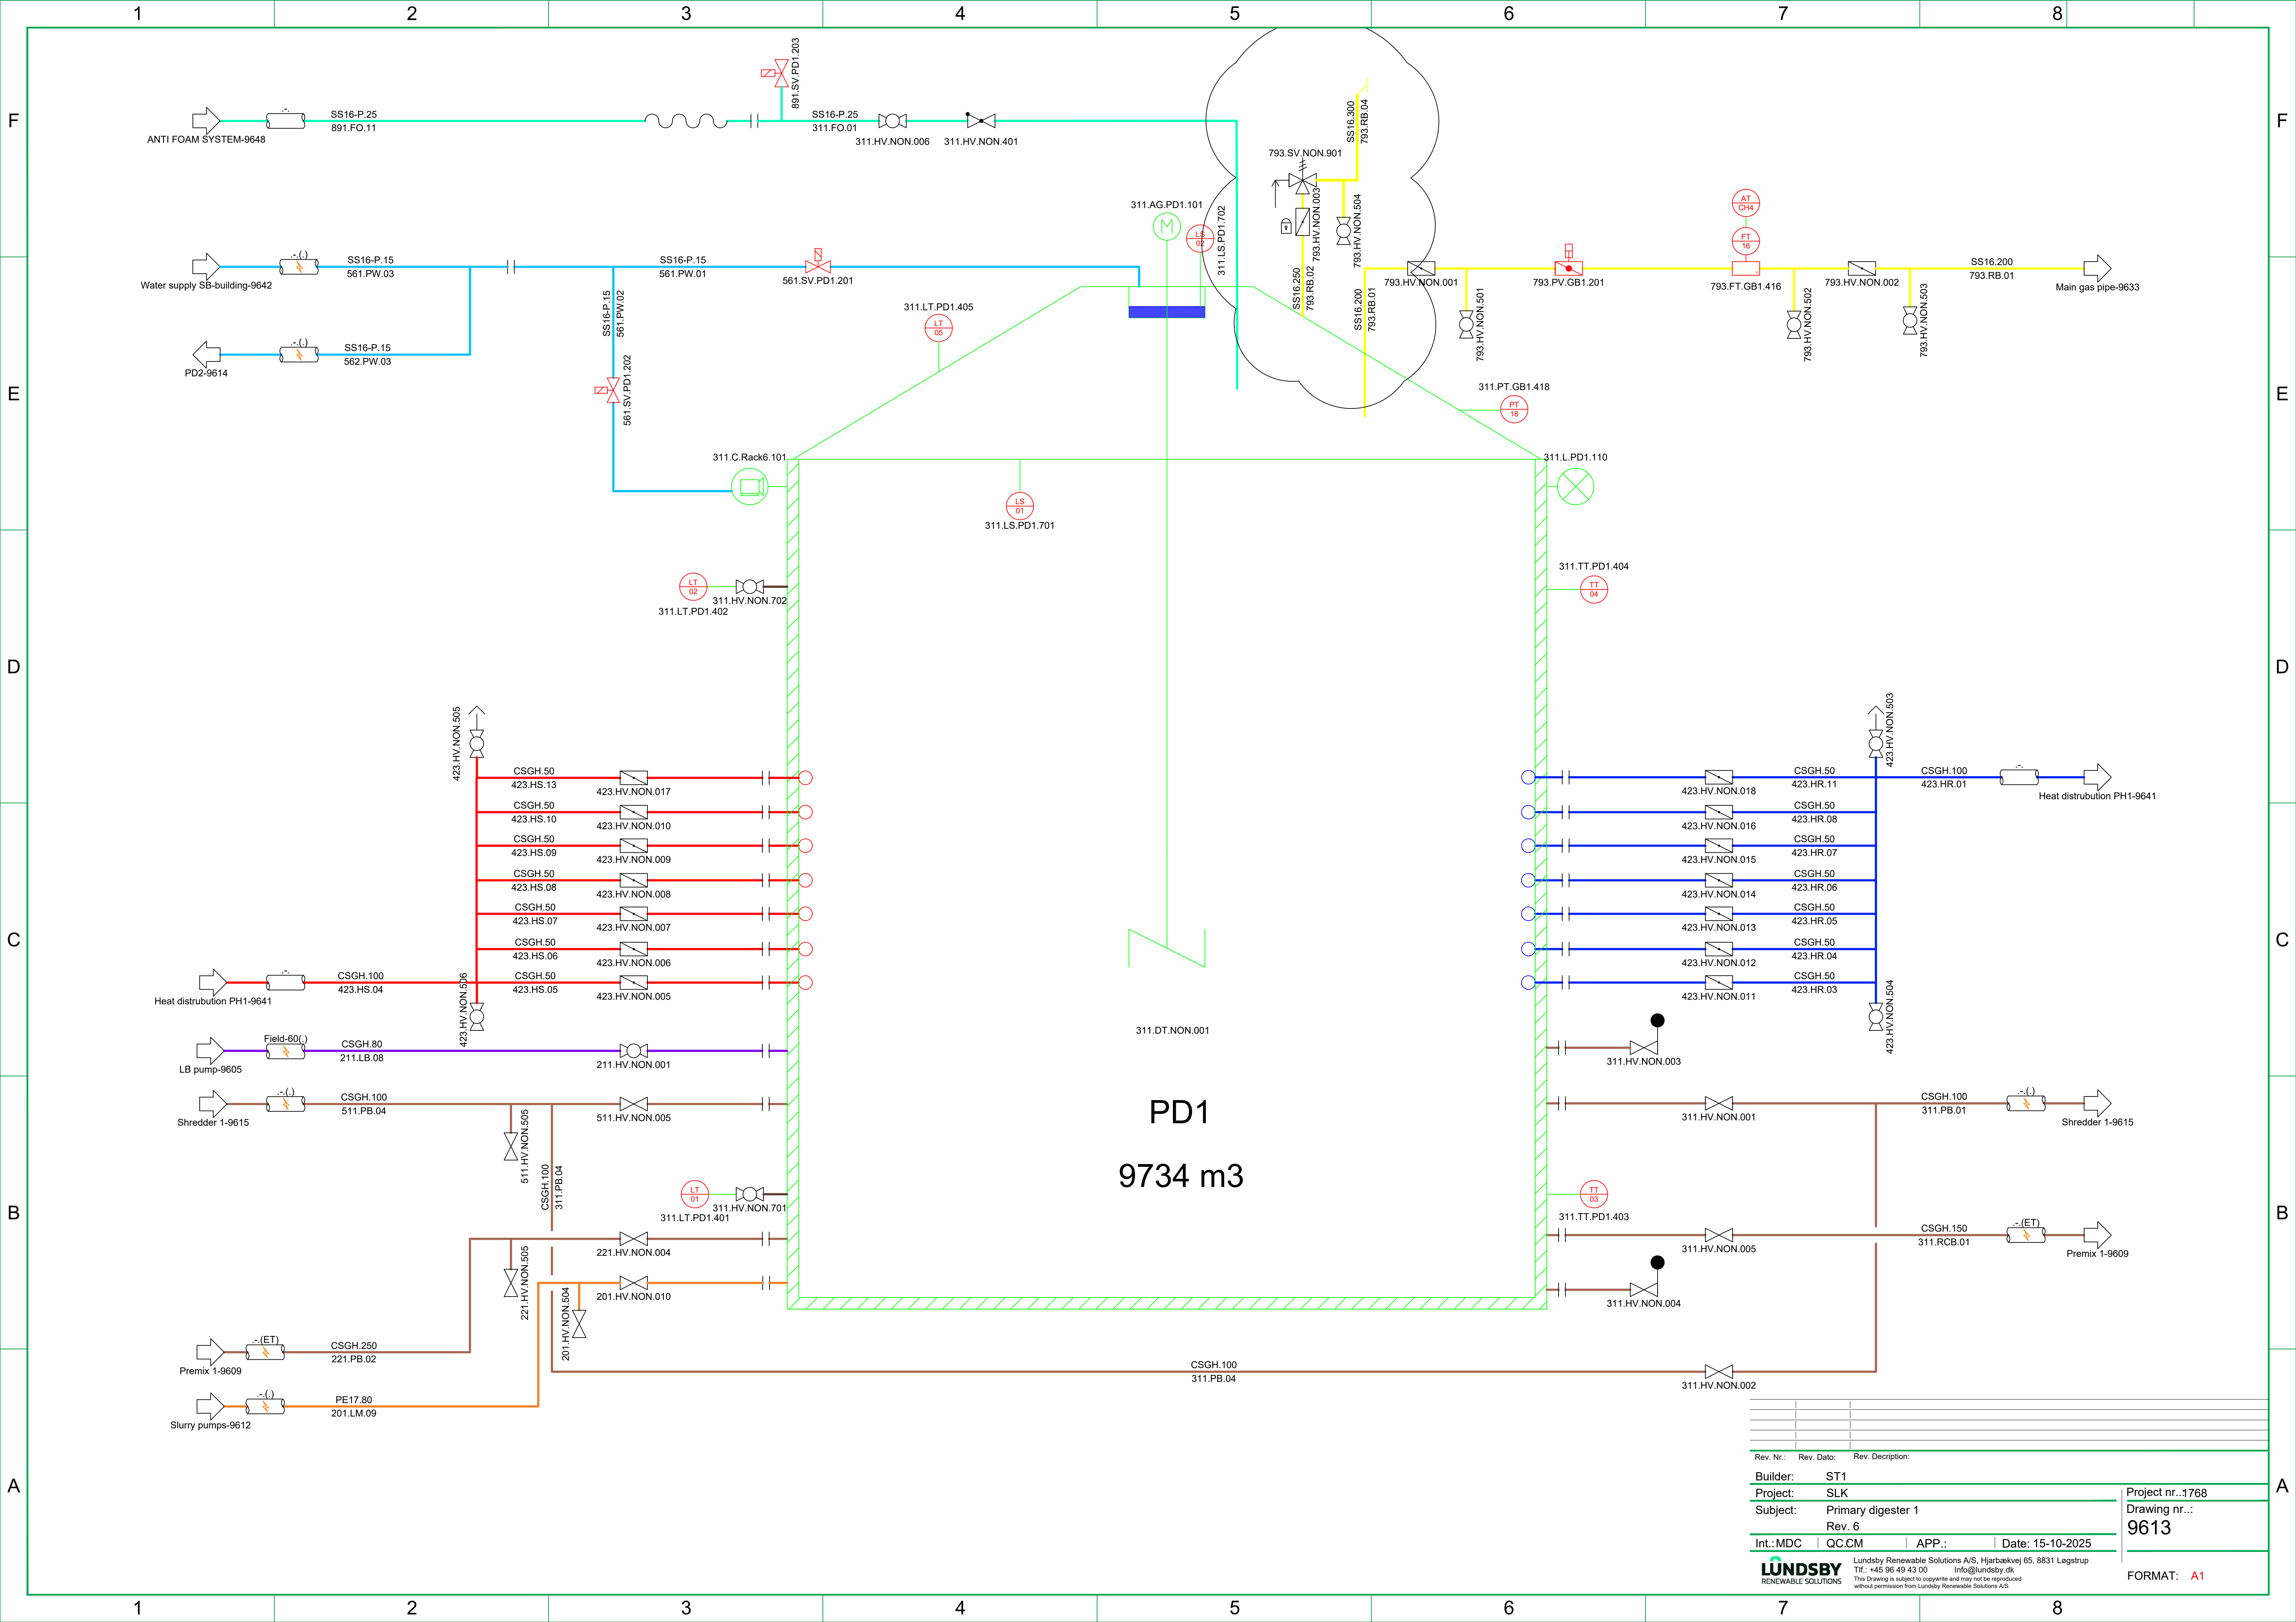


Rev. Nr.:	Rev. Dato:	Rev. Description:
Builder:	ST1	
Project:	SLK	
Subject:	Primary digester 1	
Rev. 6		
Int.:MDC	QC:CM	APP.:
Date: 15-10-2025		
LUNDSBY RENEWABLE SOLUTIONS		
Lundsby Renewable Solutions A/S, Hjarbækvej 65, 8831 Legstrup Tlf.: +45 96 49 43 00 Info@lundsby.dk This drawing is subject to copyright and may not be reproduced without permission from Lundsby Renewable Solutions A/S		
Project nr.:1768 Drawing nr.: 9613		FORMAT: A1

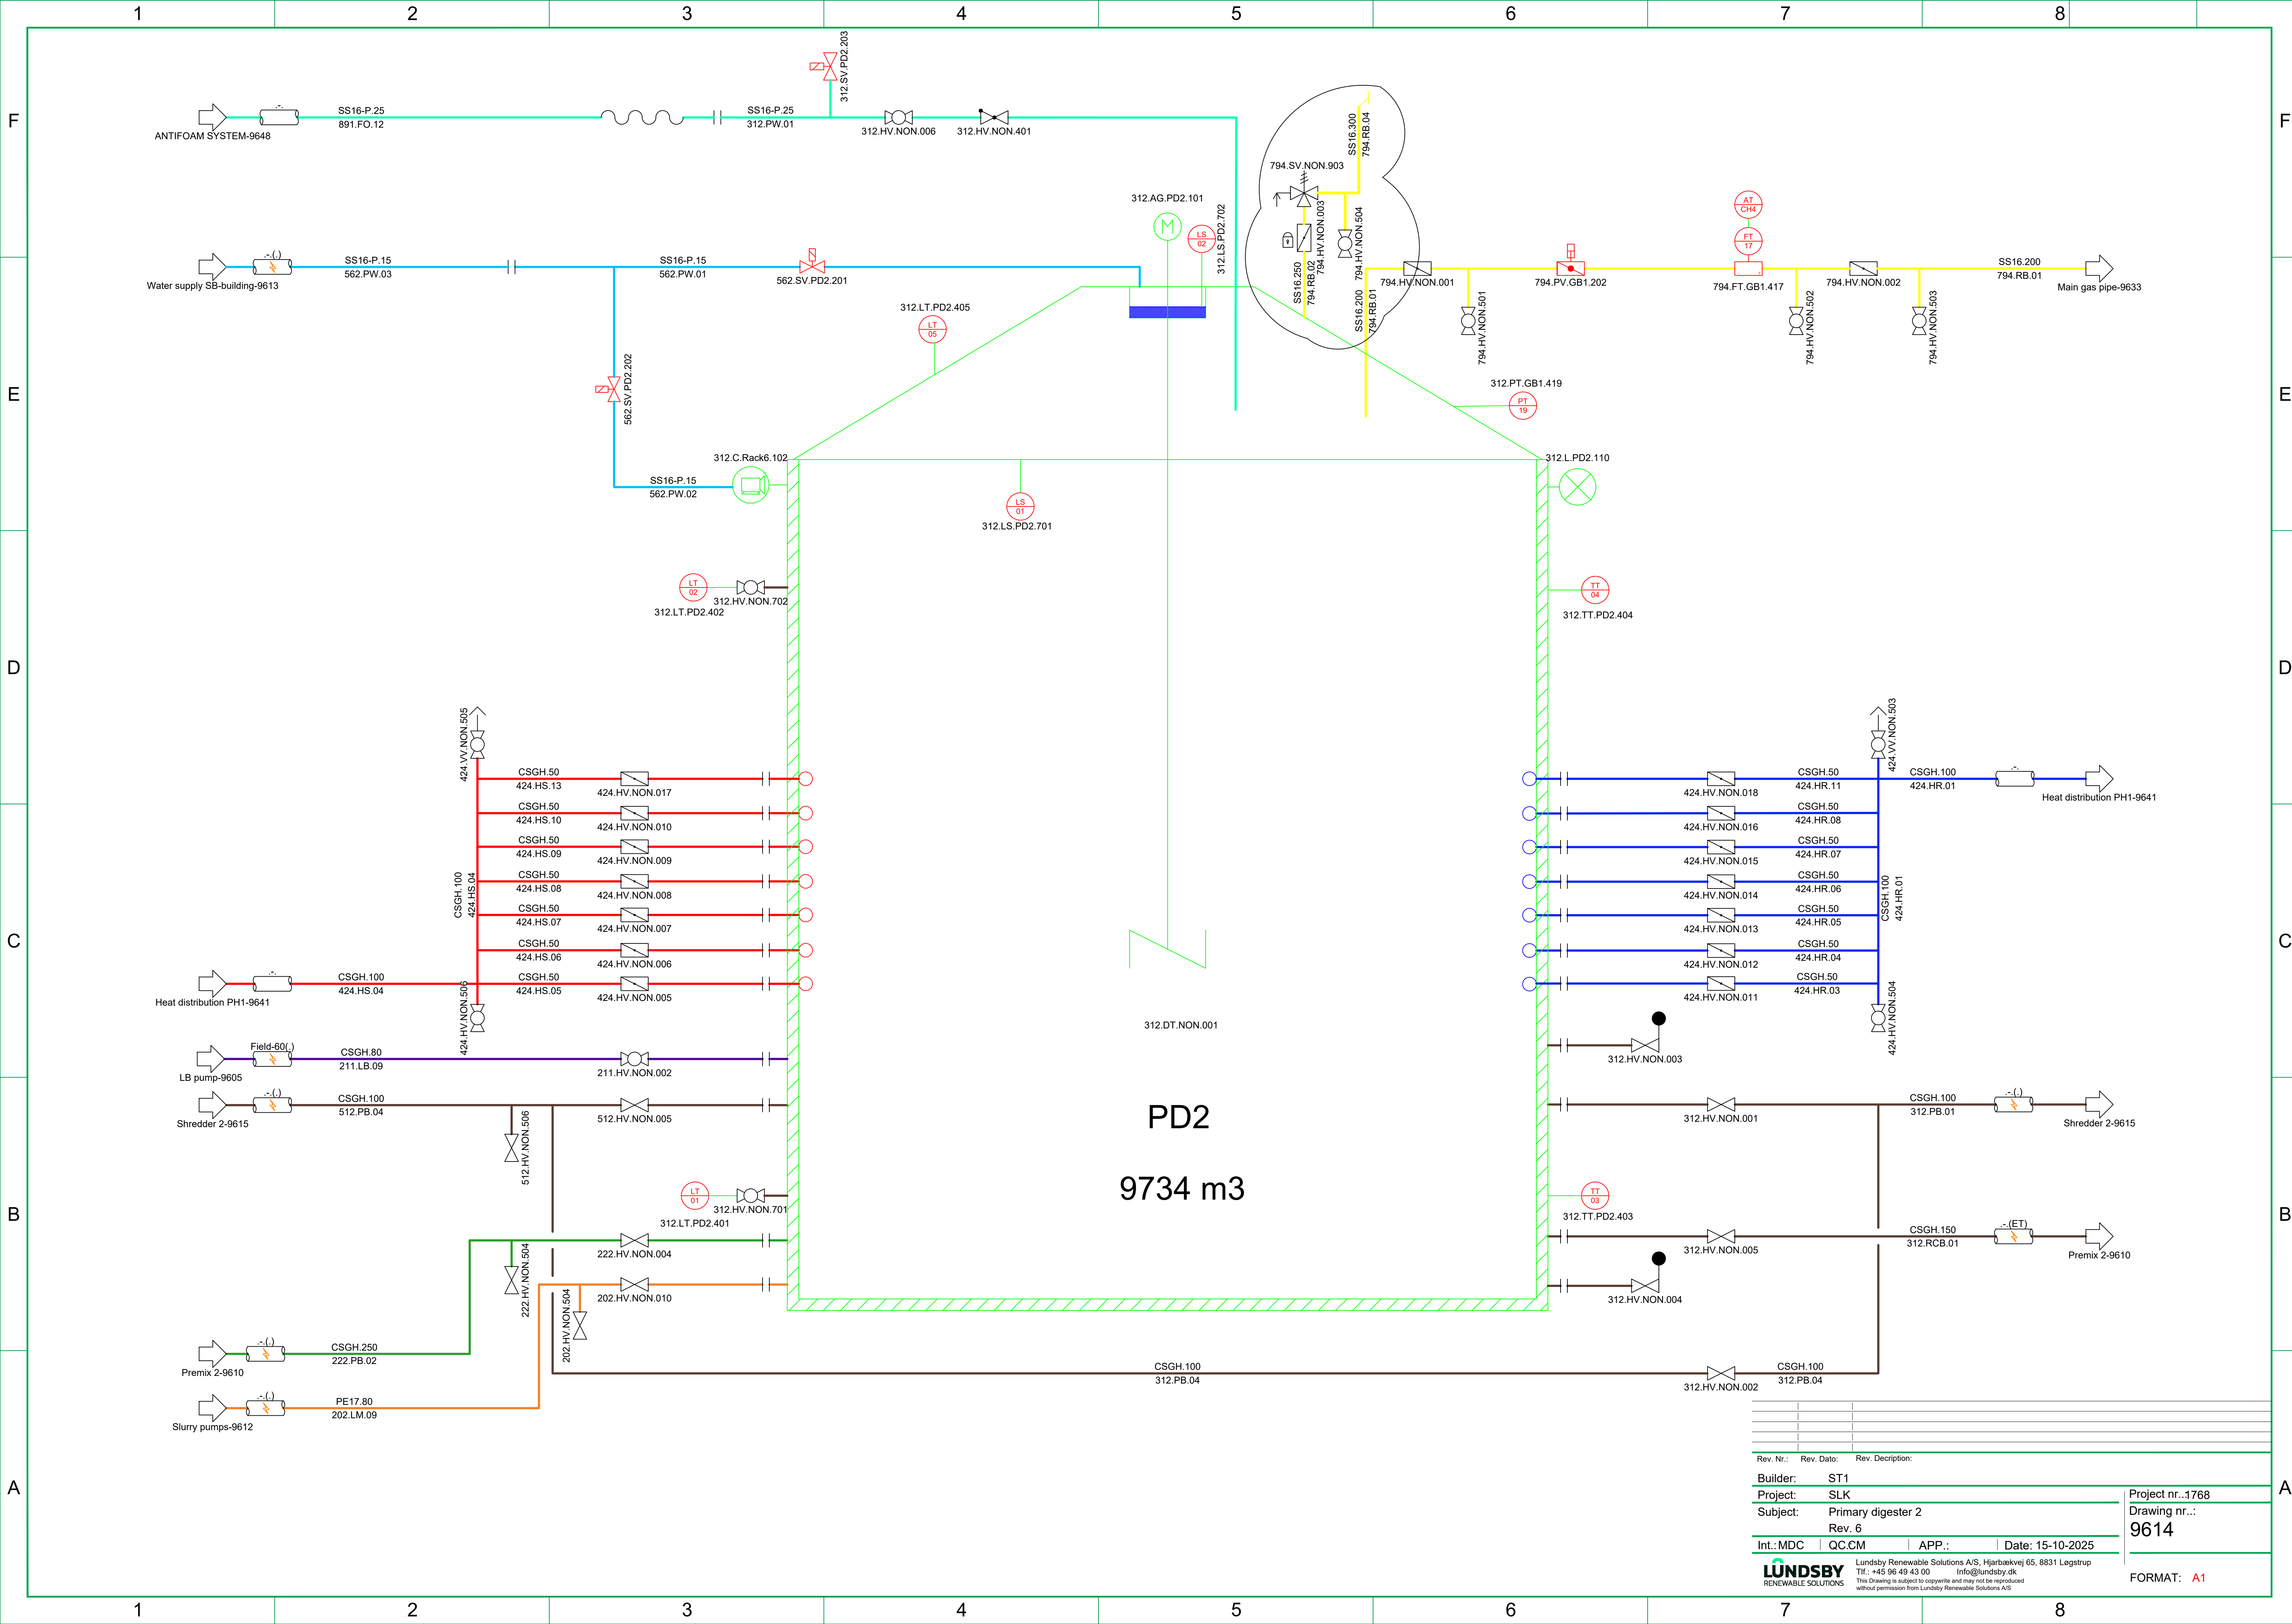


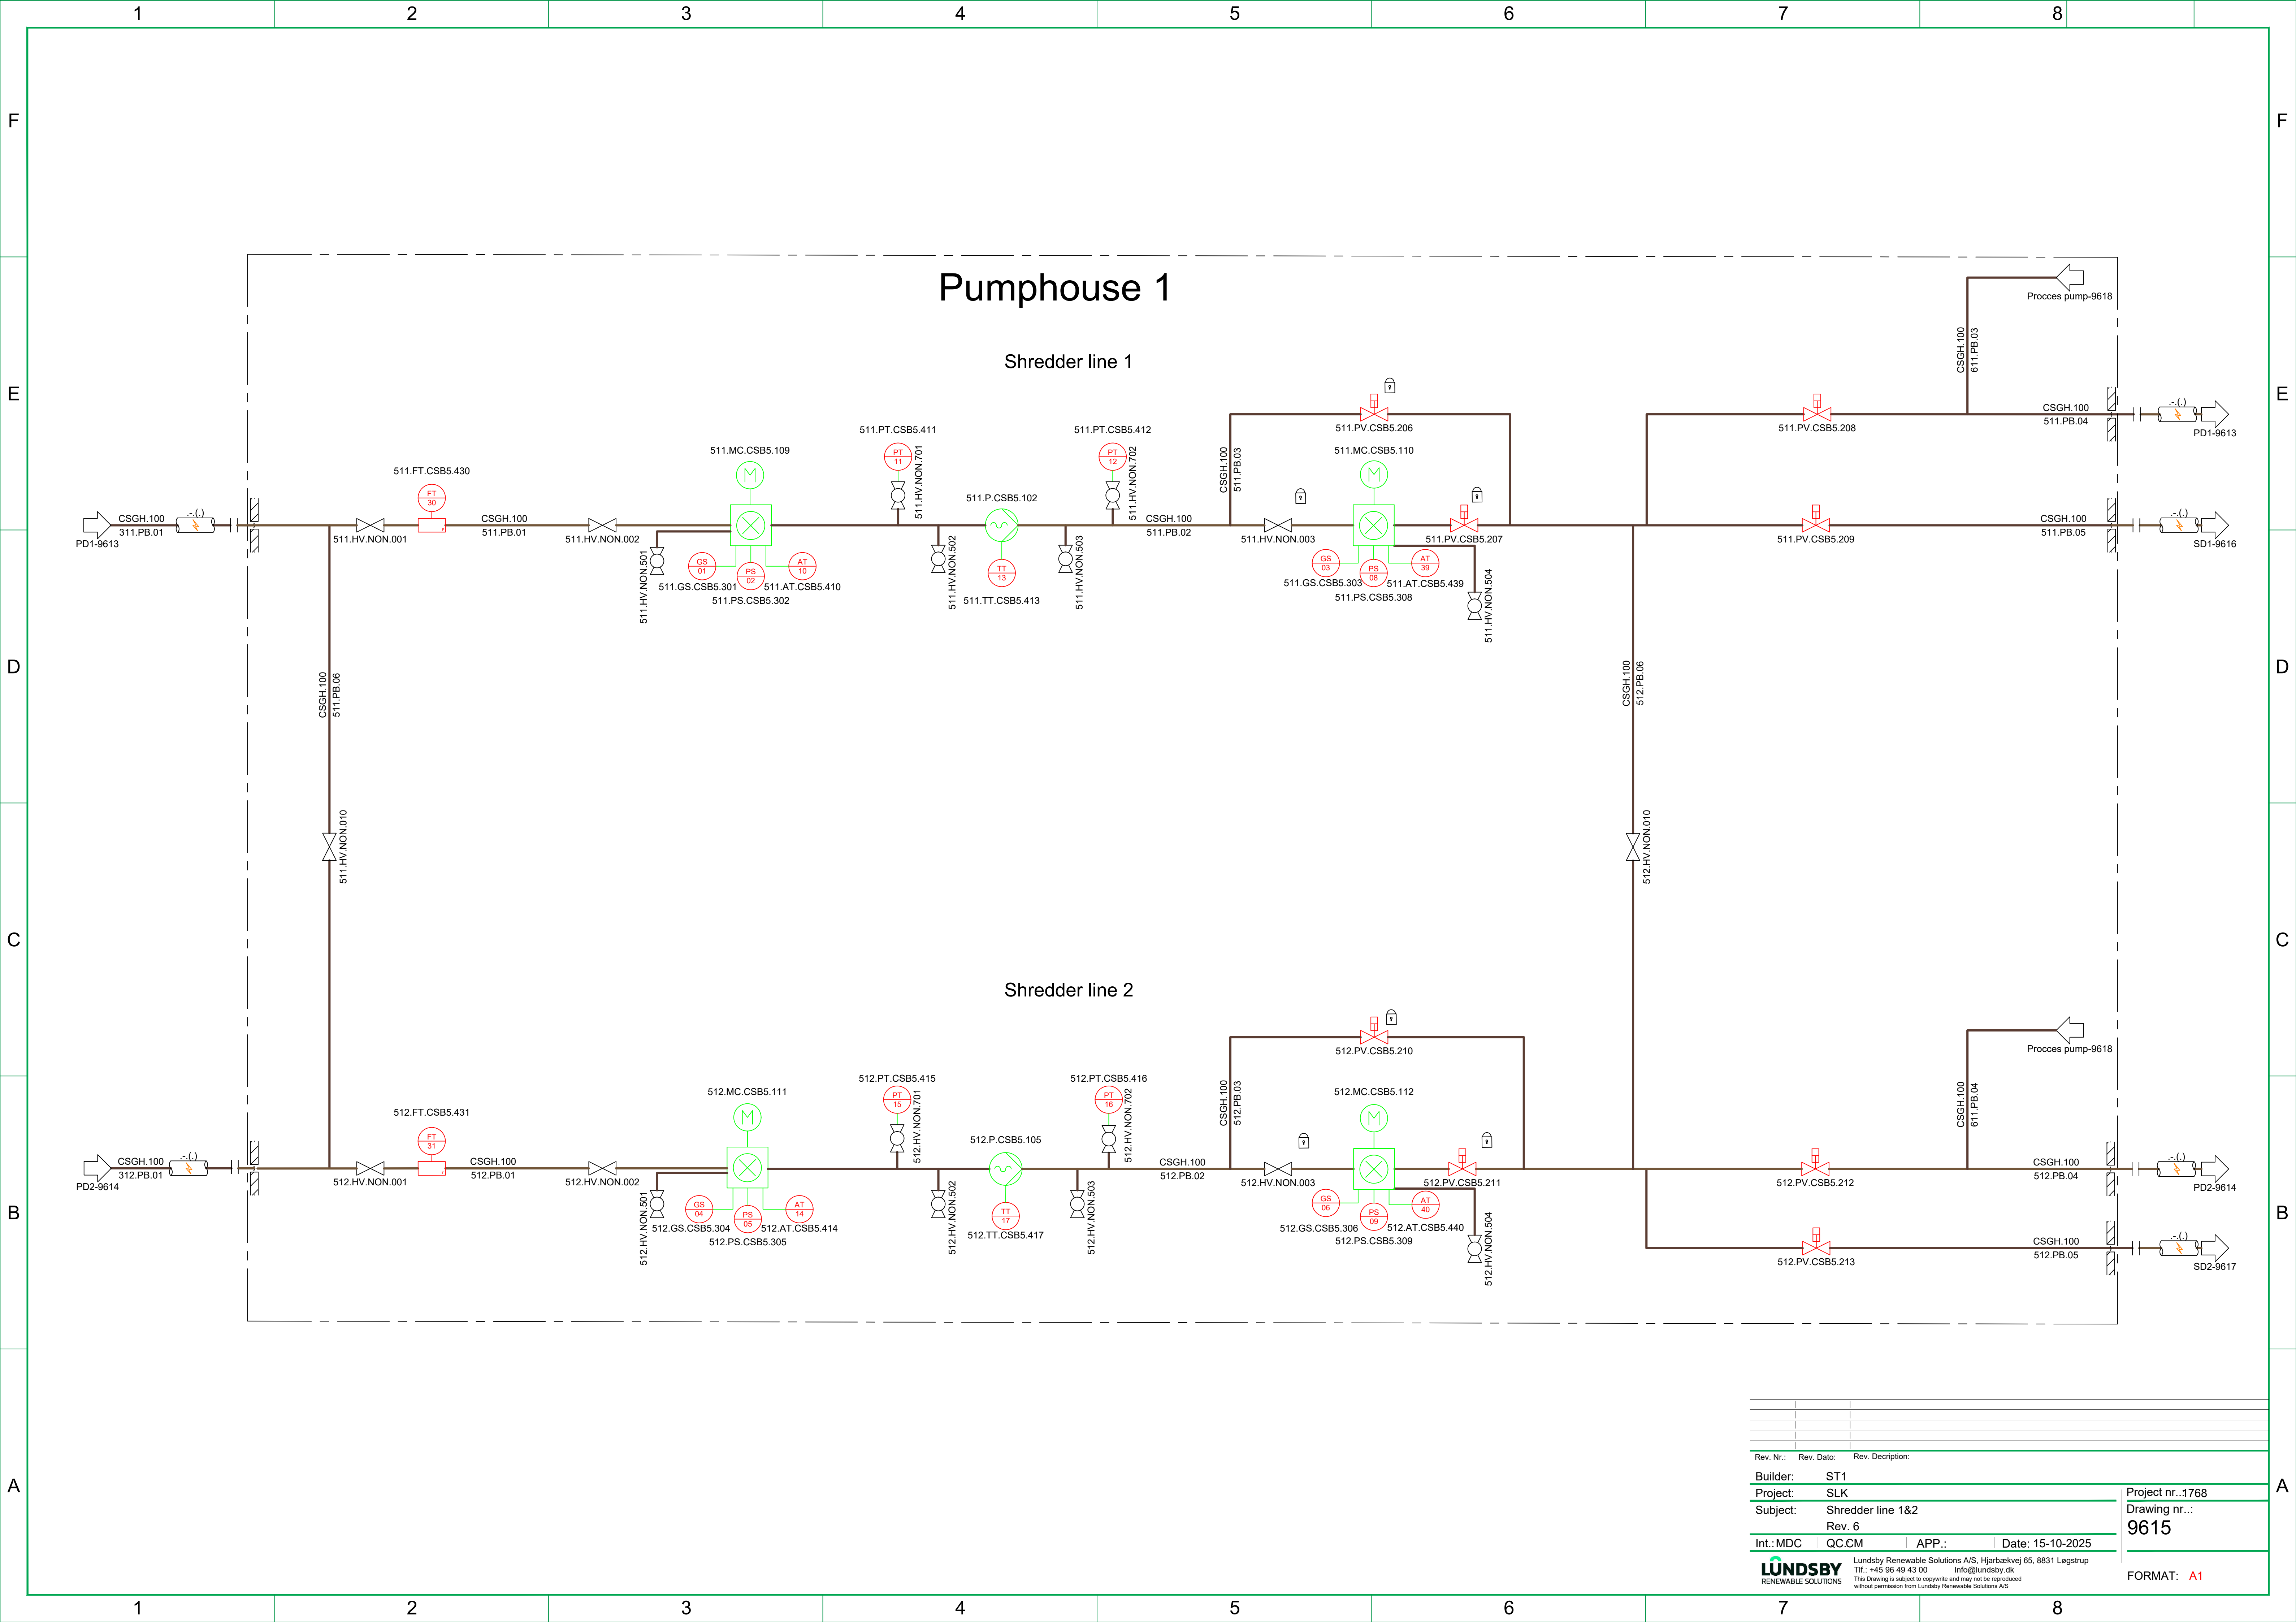


Rev. Nr.:	Rev. Dato:	Rev. Description:
Builder:	ST1	
Project:	SLK	
Subject:	Shredder line 1&2	
	Rev. 6	
Int.:MDC	QC:CM	APP.:Date: 15-10-2025
LUNDSBY RENEWABLE SOLUTIONS		
Lundsby Renewable Solutions A/S, Hjarbrækvej 65, 8831 Lægstrup Tlf.: +45 96 49 43 00 Info@lundsby.dk This Drawing is subject to copyright and may not be reproduced without permission from Lundsby Renewable Solutions A/S		
Project nr.:1768 Drawing nr.: 9615		FORMAT: A1

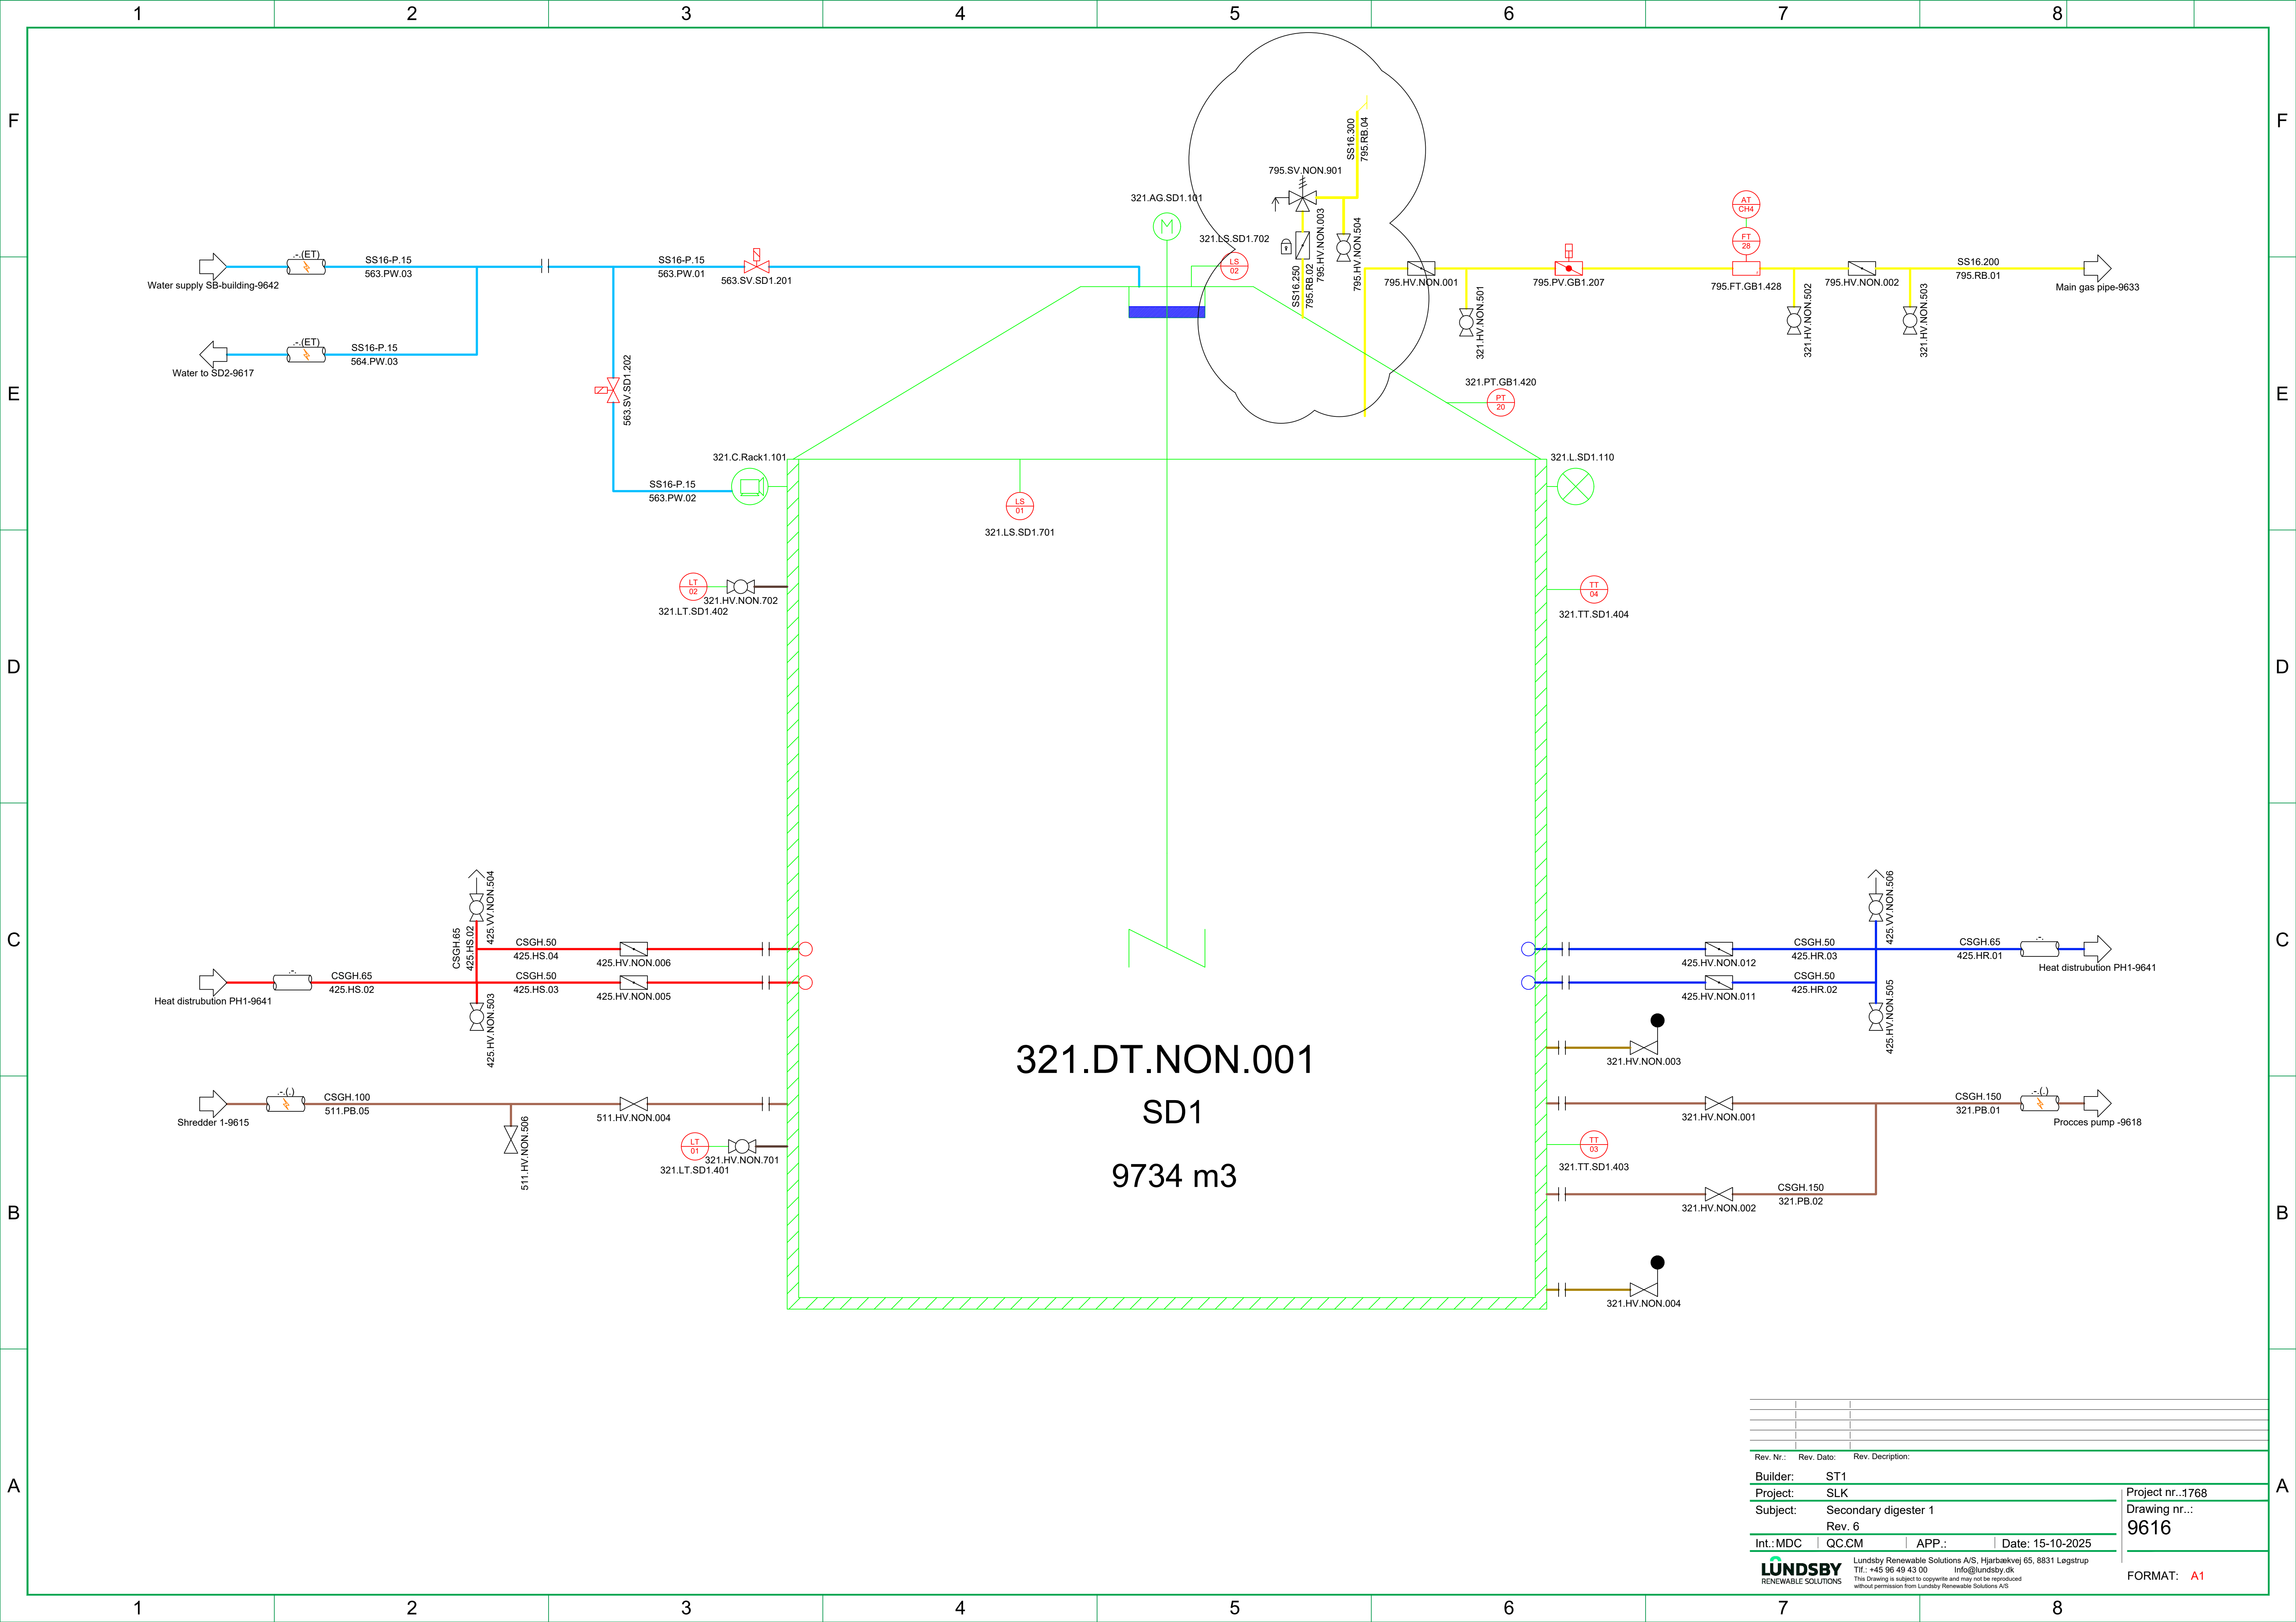

Rev. Nr.:	Rev. Dato:	Rev. Description:
Builder:	ST1	
Project:	SLK	
Subject:	Secondary digester 1	
Rev. 6		
Int.:MDC	QC.CM	APP.:
Date:	15-10-2025	
LUNDSBY RENEWABLE SOLUTIONS		
Lundsby Renewable Solutions A/S, Hjarbækvej 65, 8831 Lægstrup Tlf.: +45 96 49 43 00 Info@lundsby.dk This Drawing is subject to copyright and may not be reproduced without permission from Lundsby Renewable Solutions A/S		
Project nr.:1768 Drawing nr.: 9616		FORMAT: A1

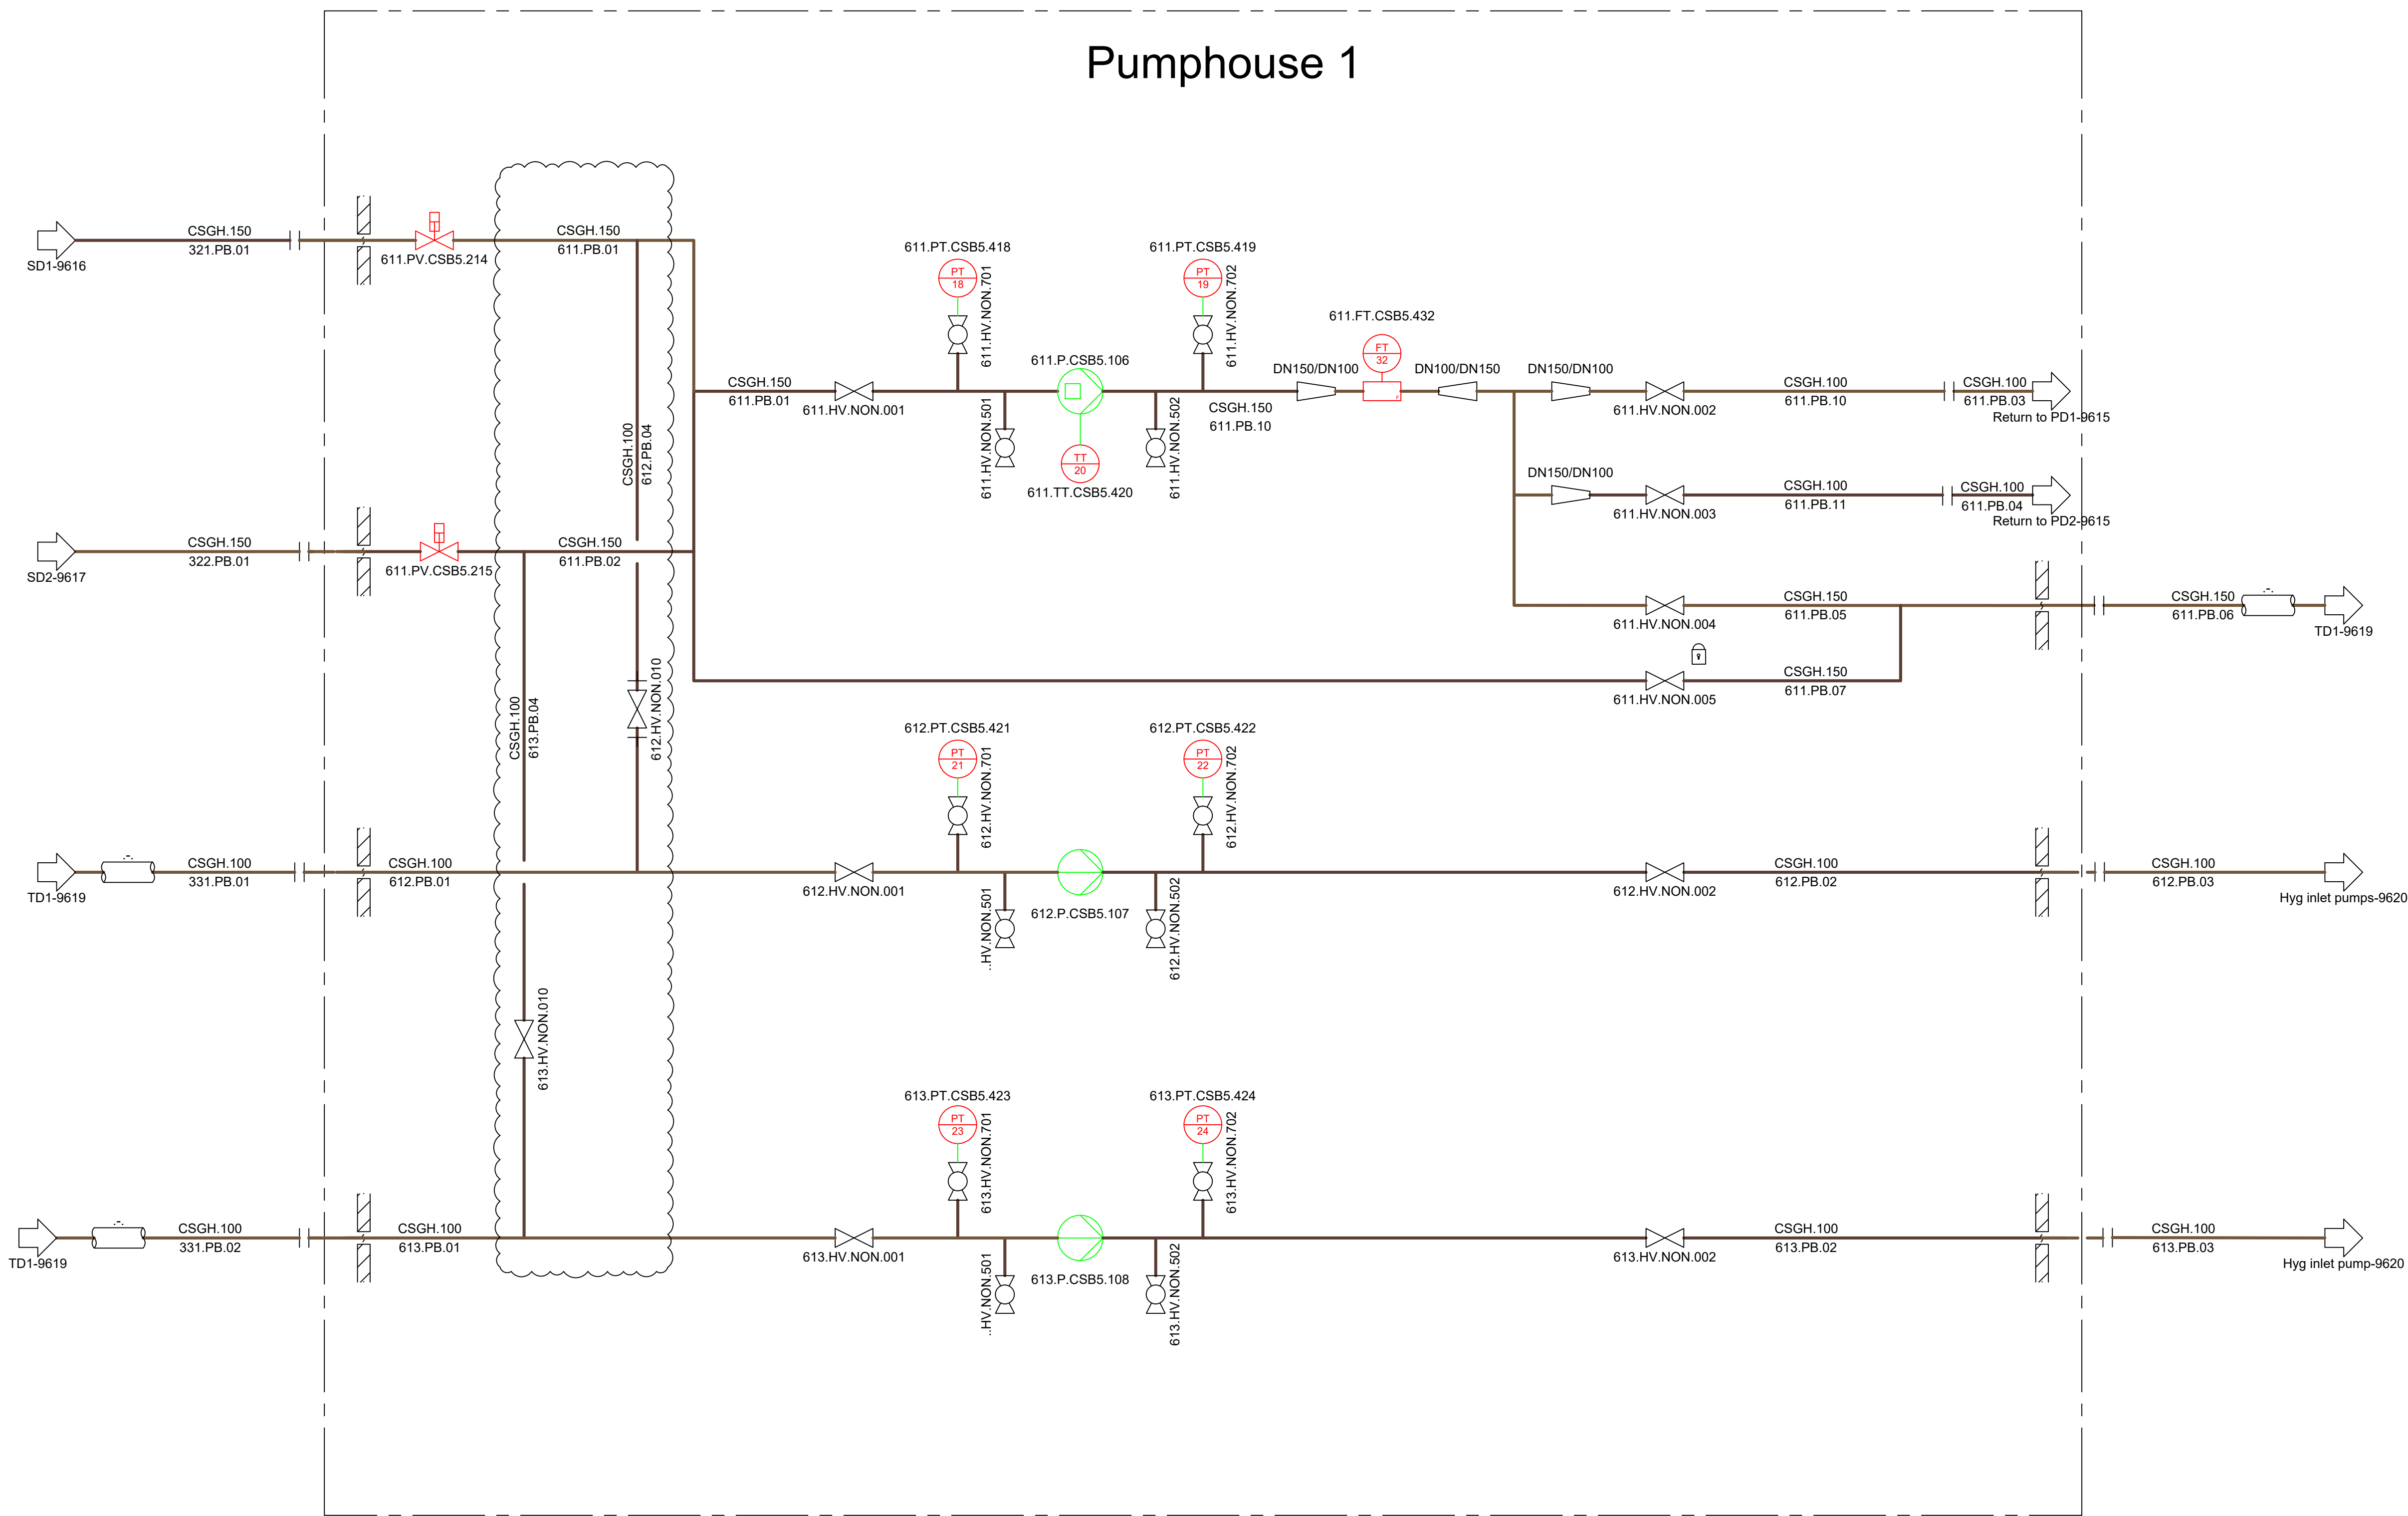


Rev. Nr.:	Rev. Dato:	Rev. Description:	
Builder:	ST1		
Project:	SLK		
Subject:	Procces pumps		
Rev. 6			
Int.:MDC	QC.CM	APP.:	Date: 15-10-2025
LUNDSBY RENEWABLE SOLUTIONS			Lundsby Renewable Solutions A/S, Hjarbækvej 65, 8831 Løgstrup Tlf.: +45 96 49 43 00 Info@lundsby.dk This Drawing is subject to copyright and may not be reproduced without permission from Lundsby Renewable Solutions A/S
Project nr...1768 Drawing nr...: 9618			FORMAT: A1

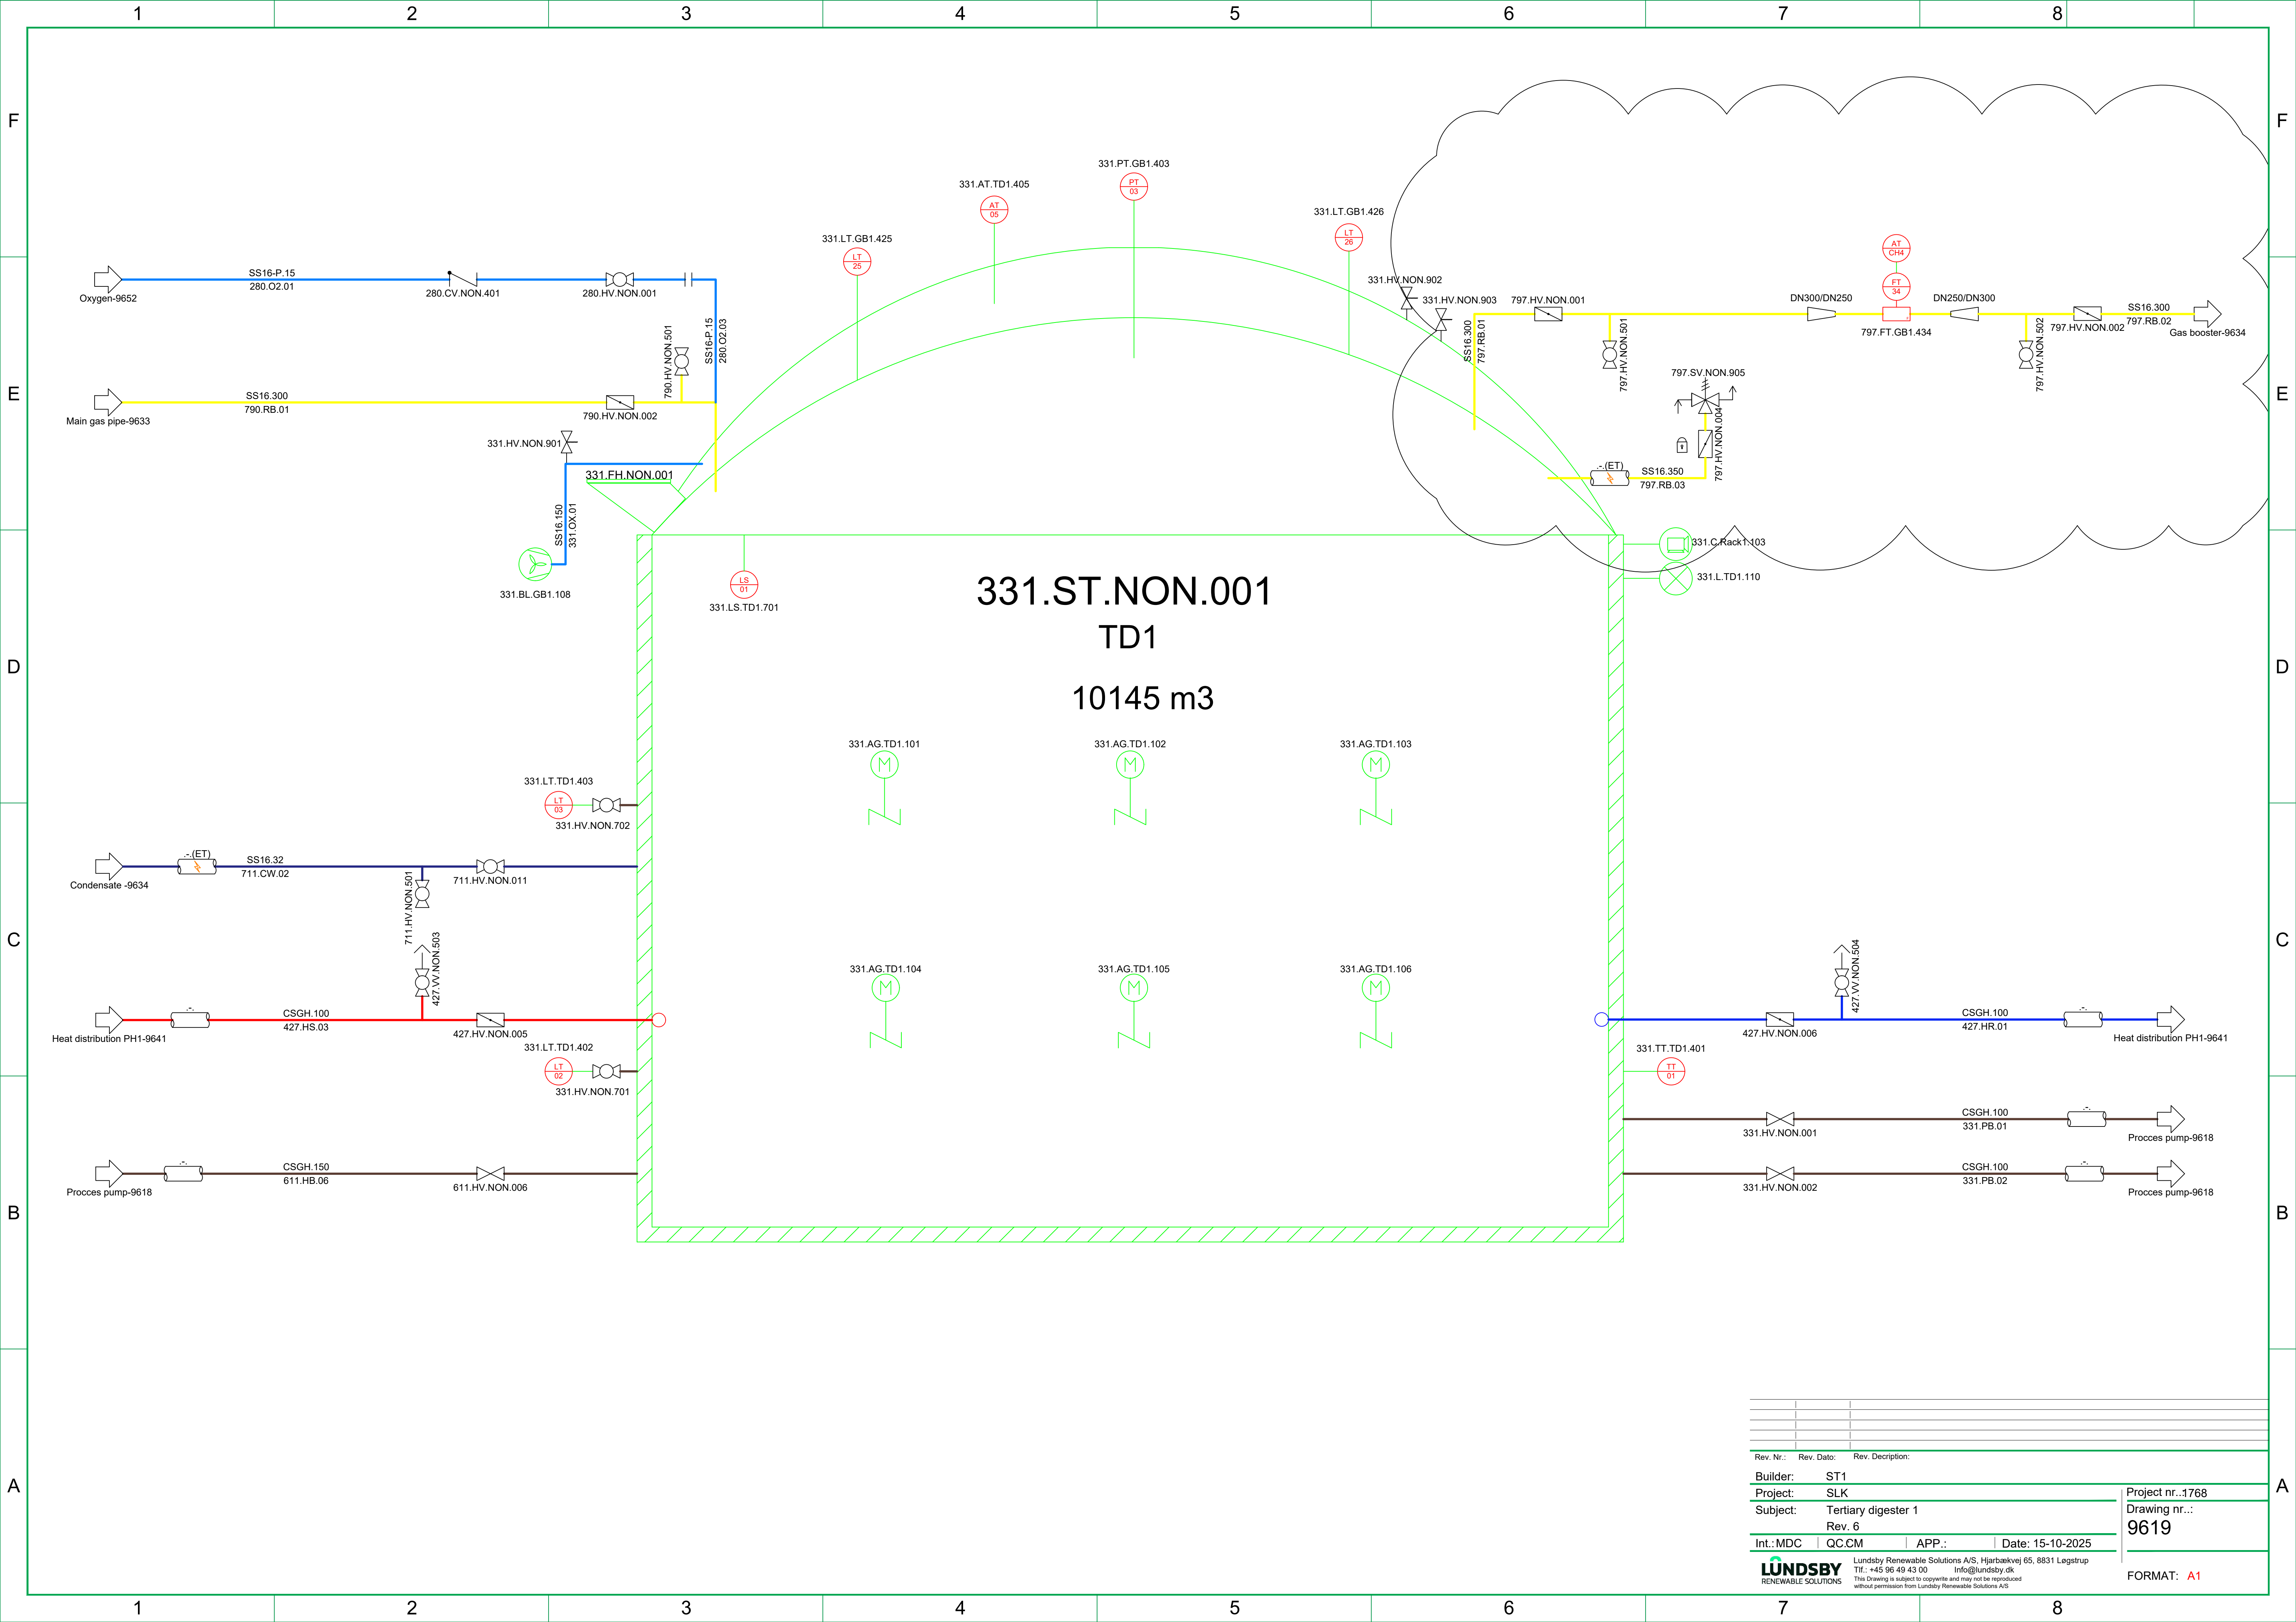


Rev. Nr.:	Rev. Dato:	Rev. Description:			
Builder:	ST1				
Project:	SLK				
Subject:	Tertiary digester 1				
	Rev. 6				
Int.: MDC	QC.CM	APP.:	Date: 15-10-2025		
		Lundsby Renewable Solutions A/S, Hjarbækvej 65, 8831 Løgstrup Tlf.: +45 96 49 43 00 Info@lundsby.dk This Drawing is subject to copyright and may not be reproduced without permission from Lundsby Renewable Solutions A/S			
		Project nr.:1768		Drawing nr.: 9619	
		FORMAT: A1			

Tech Building


Inlet pumps

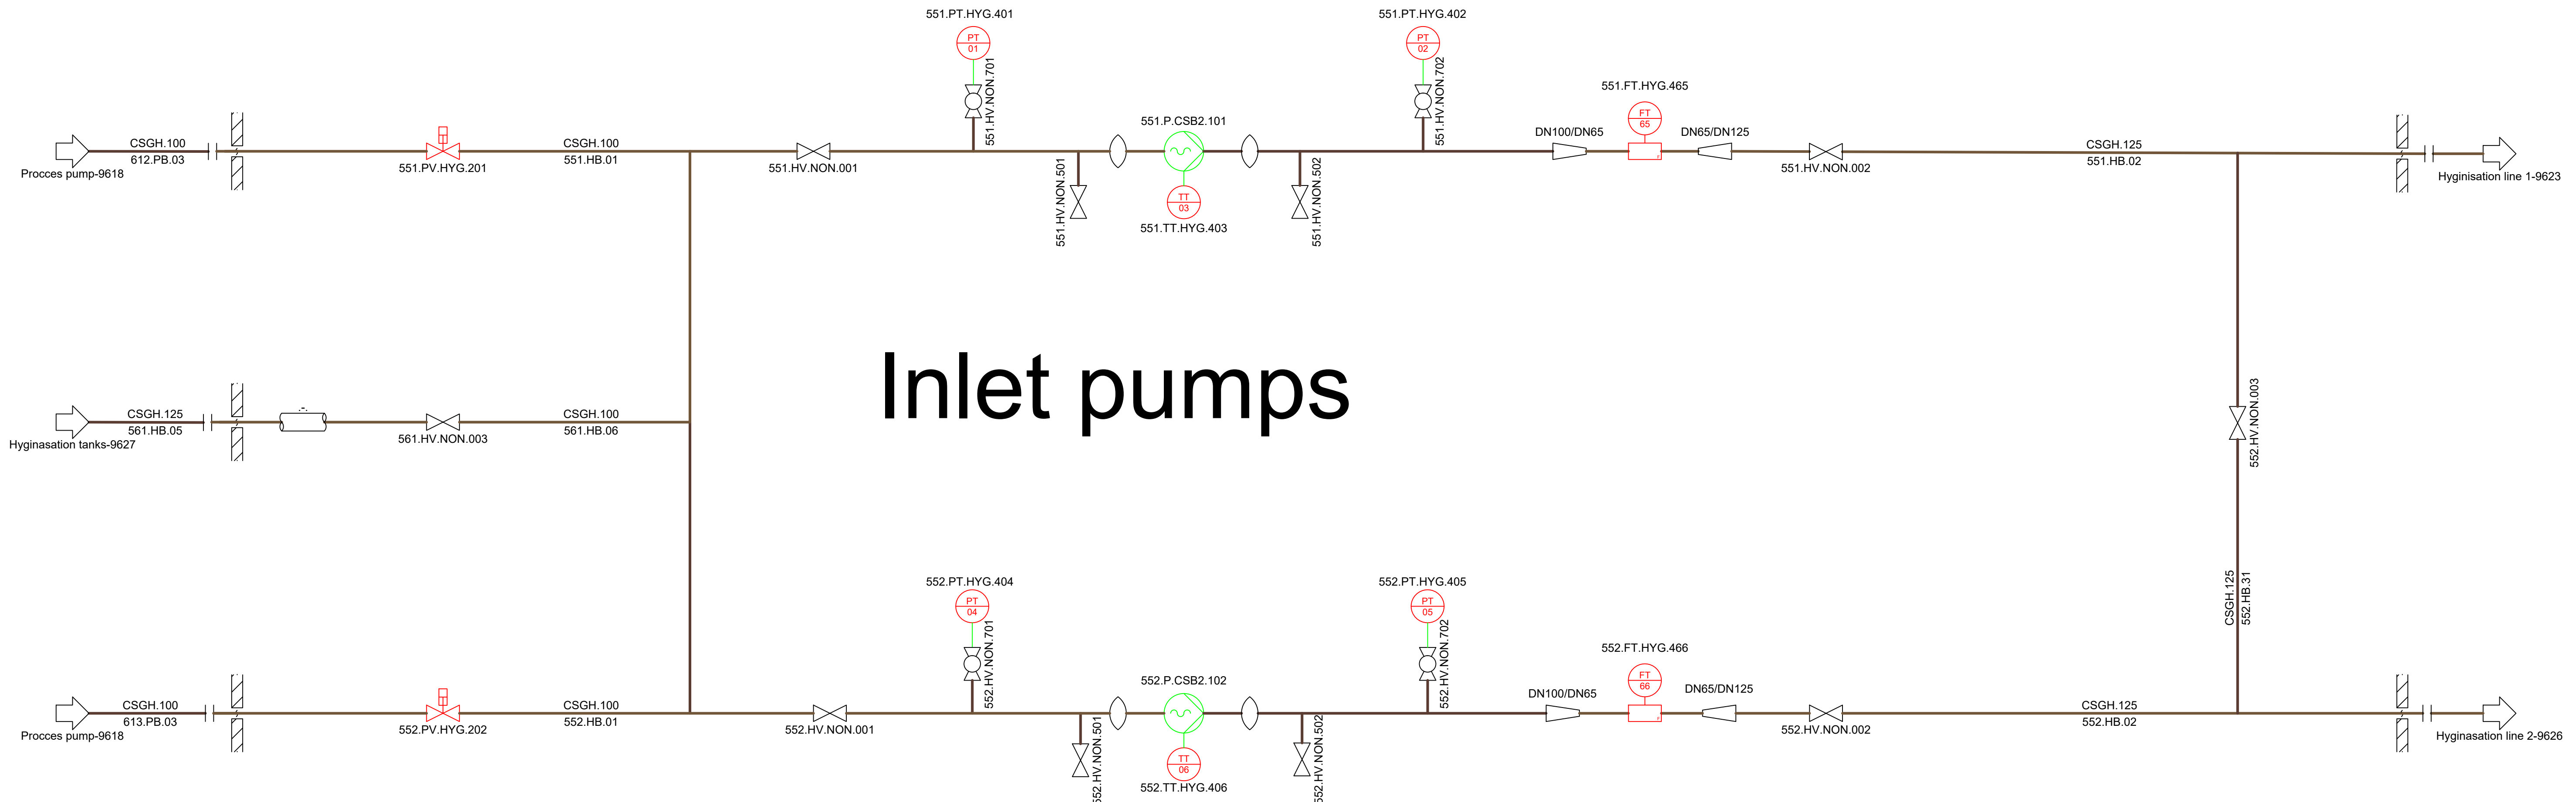


Rev. Nr.:	Rev. Dato:	Rev. Description:	
Builder:	ST1		
Project:	SLK		
Subject:	Hyginisation inlet pumps		
	Rev. 6		
Int.:MDC	QC.CM	APP.:	Date: 15-10-2025
LUNDSBY RENEWABLE SOLUTIONS			Lundsby Renewable Solutions A/S, Hjarbækvej 65, 8831 Løgstrup Tlf.: +45 96 49 43 00 Info@lundsby.dk This Drawing is subject to copyright and may not be reproduced without permission from Lundsby Renewable Solutions A/S
			Project nr.:1768 Drawing nr.: 9620 FORMAT: A1

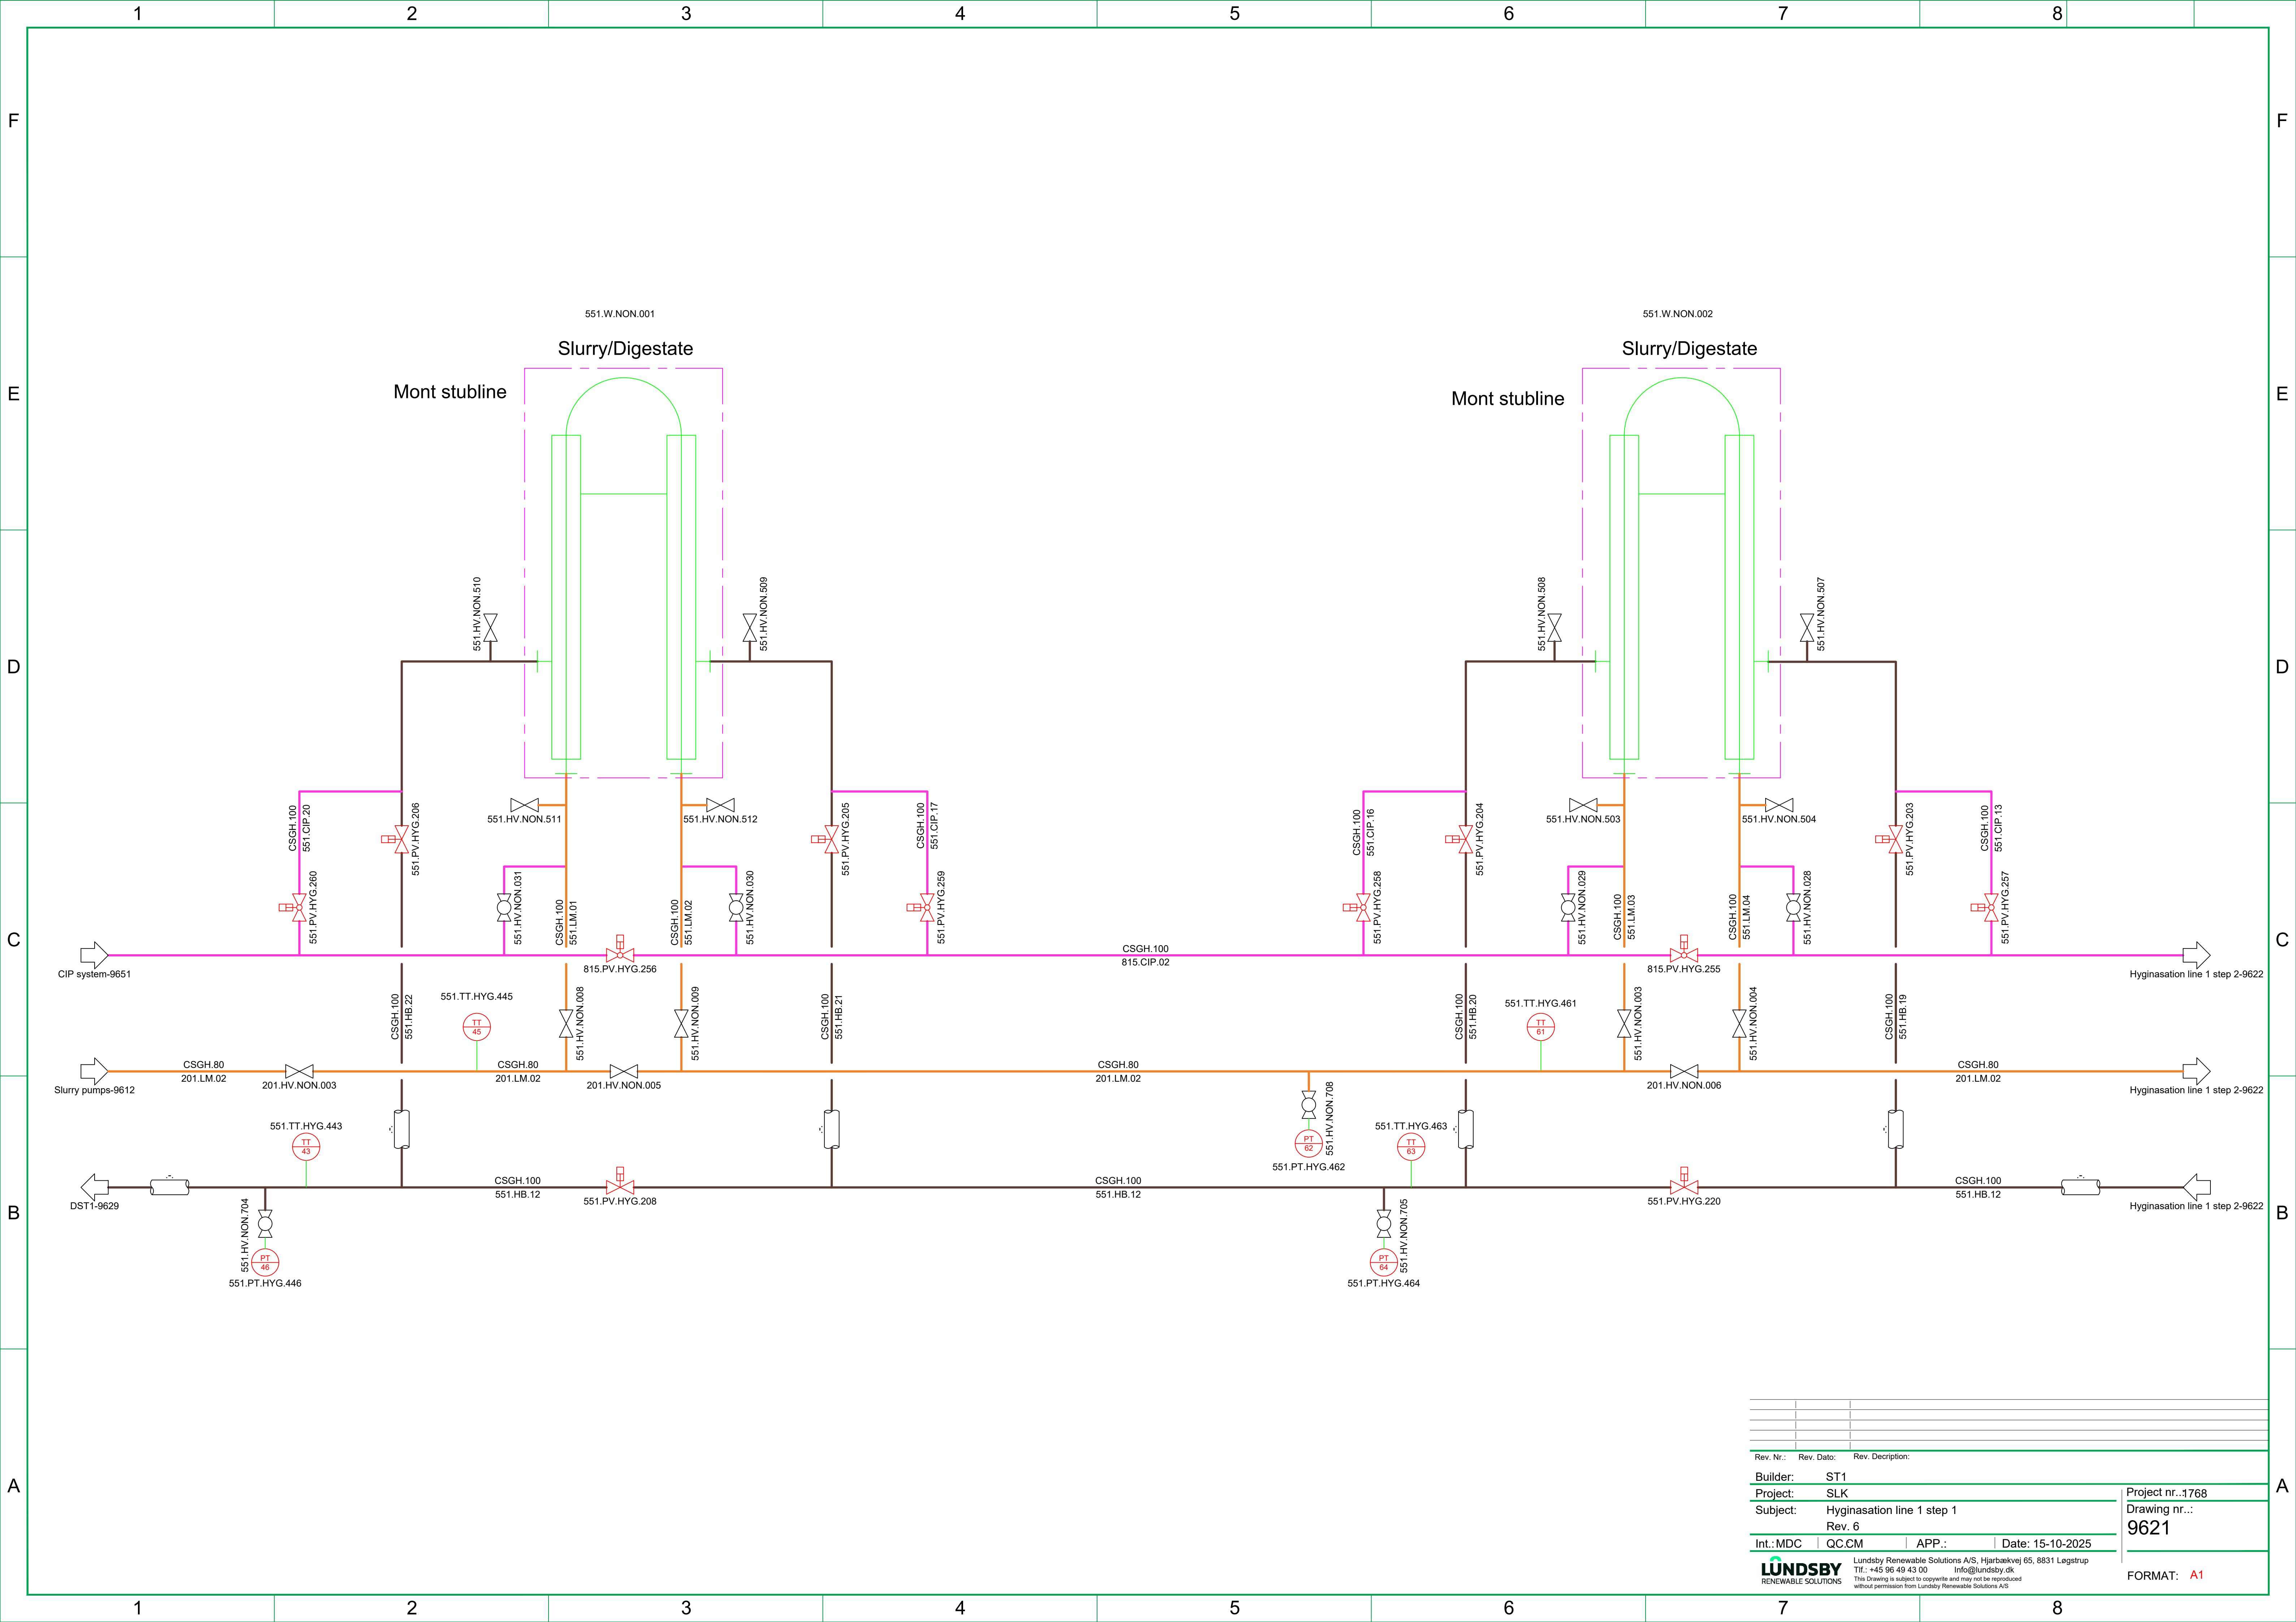



Rev. Nr.:	Rev. Dato:	Rev. Description:
Builder:	ST1	
Project:	SLK	
Subject:	Hyginasation line 1 step 1	
Rev. 6		
Int.:MDC	QC:CM	APP.:
Date: 15-10-2025		
LUNDSBY RENEWABLE SOLUTIONS		
Lundsby Renewable Solutions A/S, Hjarbækvej 65, 8831 Løgstrup Tlf.: +45 96 49 43 00 Info@lundsby.dk This Drawing is subject to copyright and may not be reproduced without permission from Lundsby Renewable Solutions A/S		
Project nr.:1768 Drawing nr.: 9621		FORMAT: A1

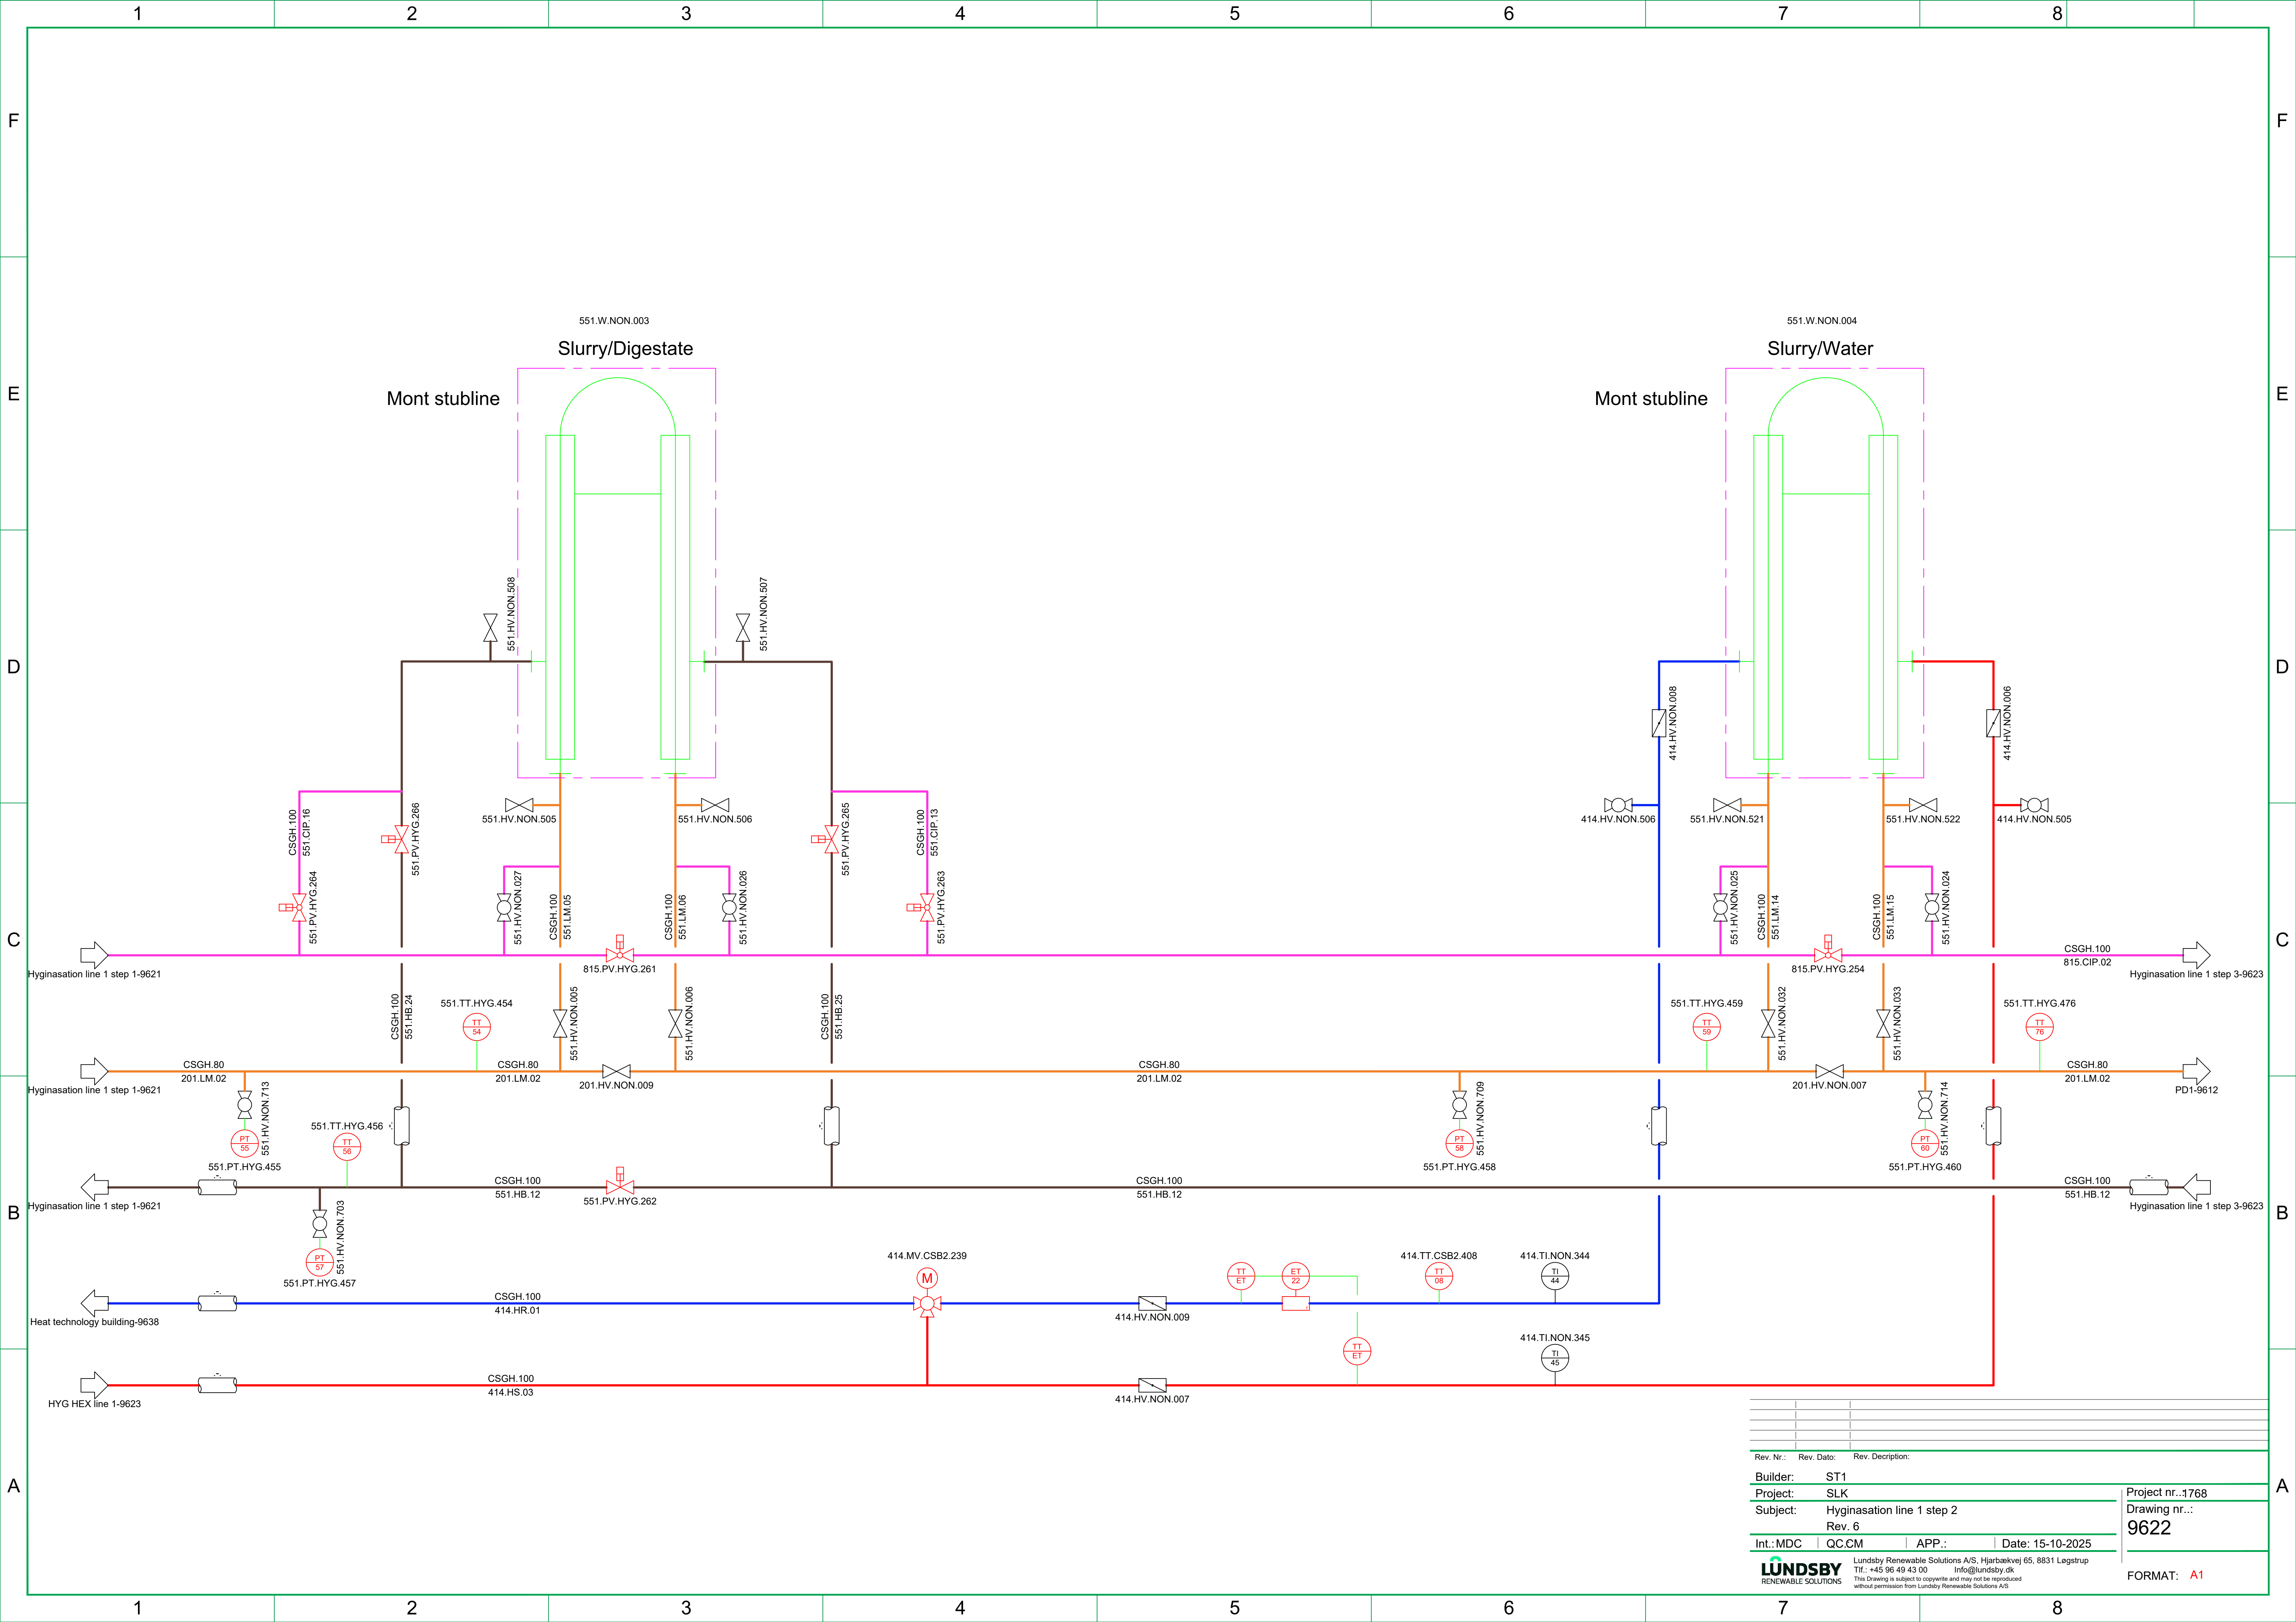


Rev. Nr.:	Rev. Dato:	Rev. Description:
Builder:	ST1	
Project:	SLK	
Subject:	Hyginasation line 1 step 2	
	Rev. 6	
Int.:MDC	QC:CM	APP.:Date: 15-10-2025
LUNDSBY RENEWABLE SOLUTIONS Lundsby Renewable Solutions A/S, Hjarbækvej 65, 8831 Løgstrup Tlf.: +45 96 49 43 00 Info@lundsby.dk This Drawing is subject to copyright and may not be reproduced without permission from Lundsby Renewable Solutions A/S		
Project nr.:1768		Drawing nr.:9622
FORMAT: A1		

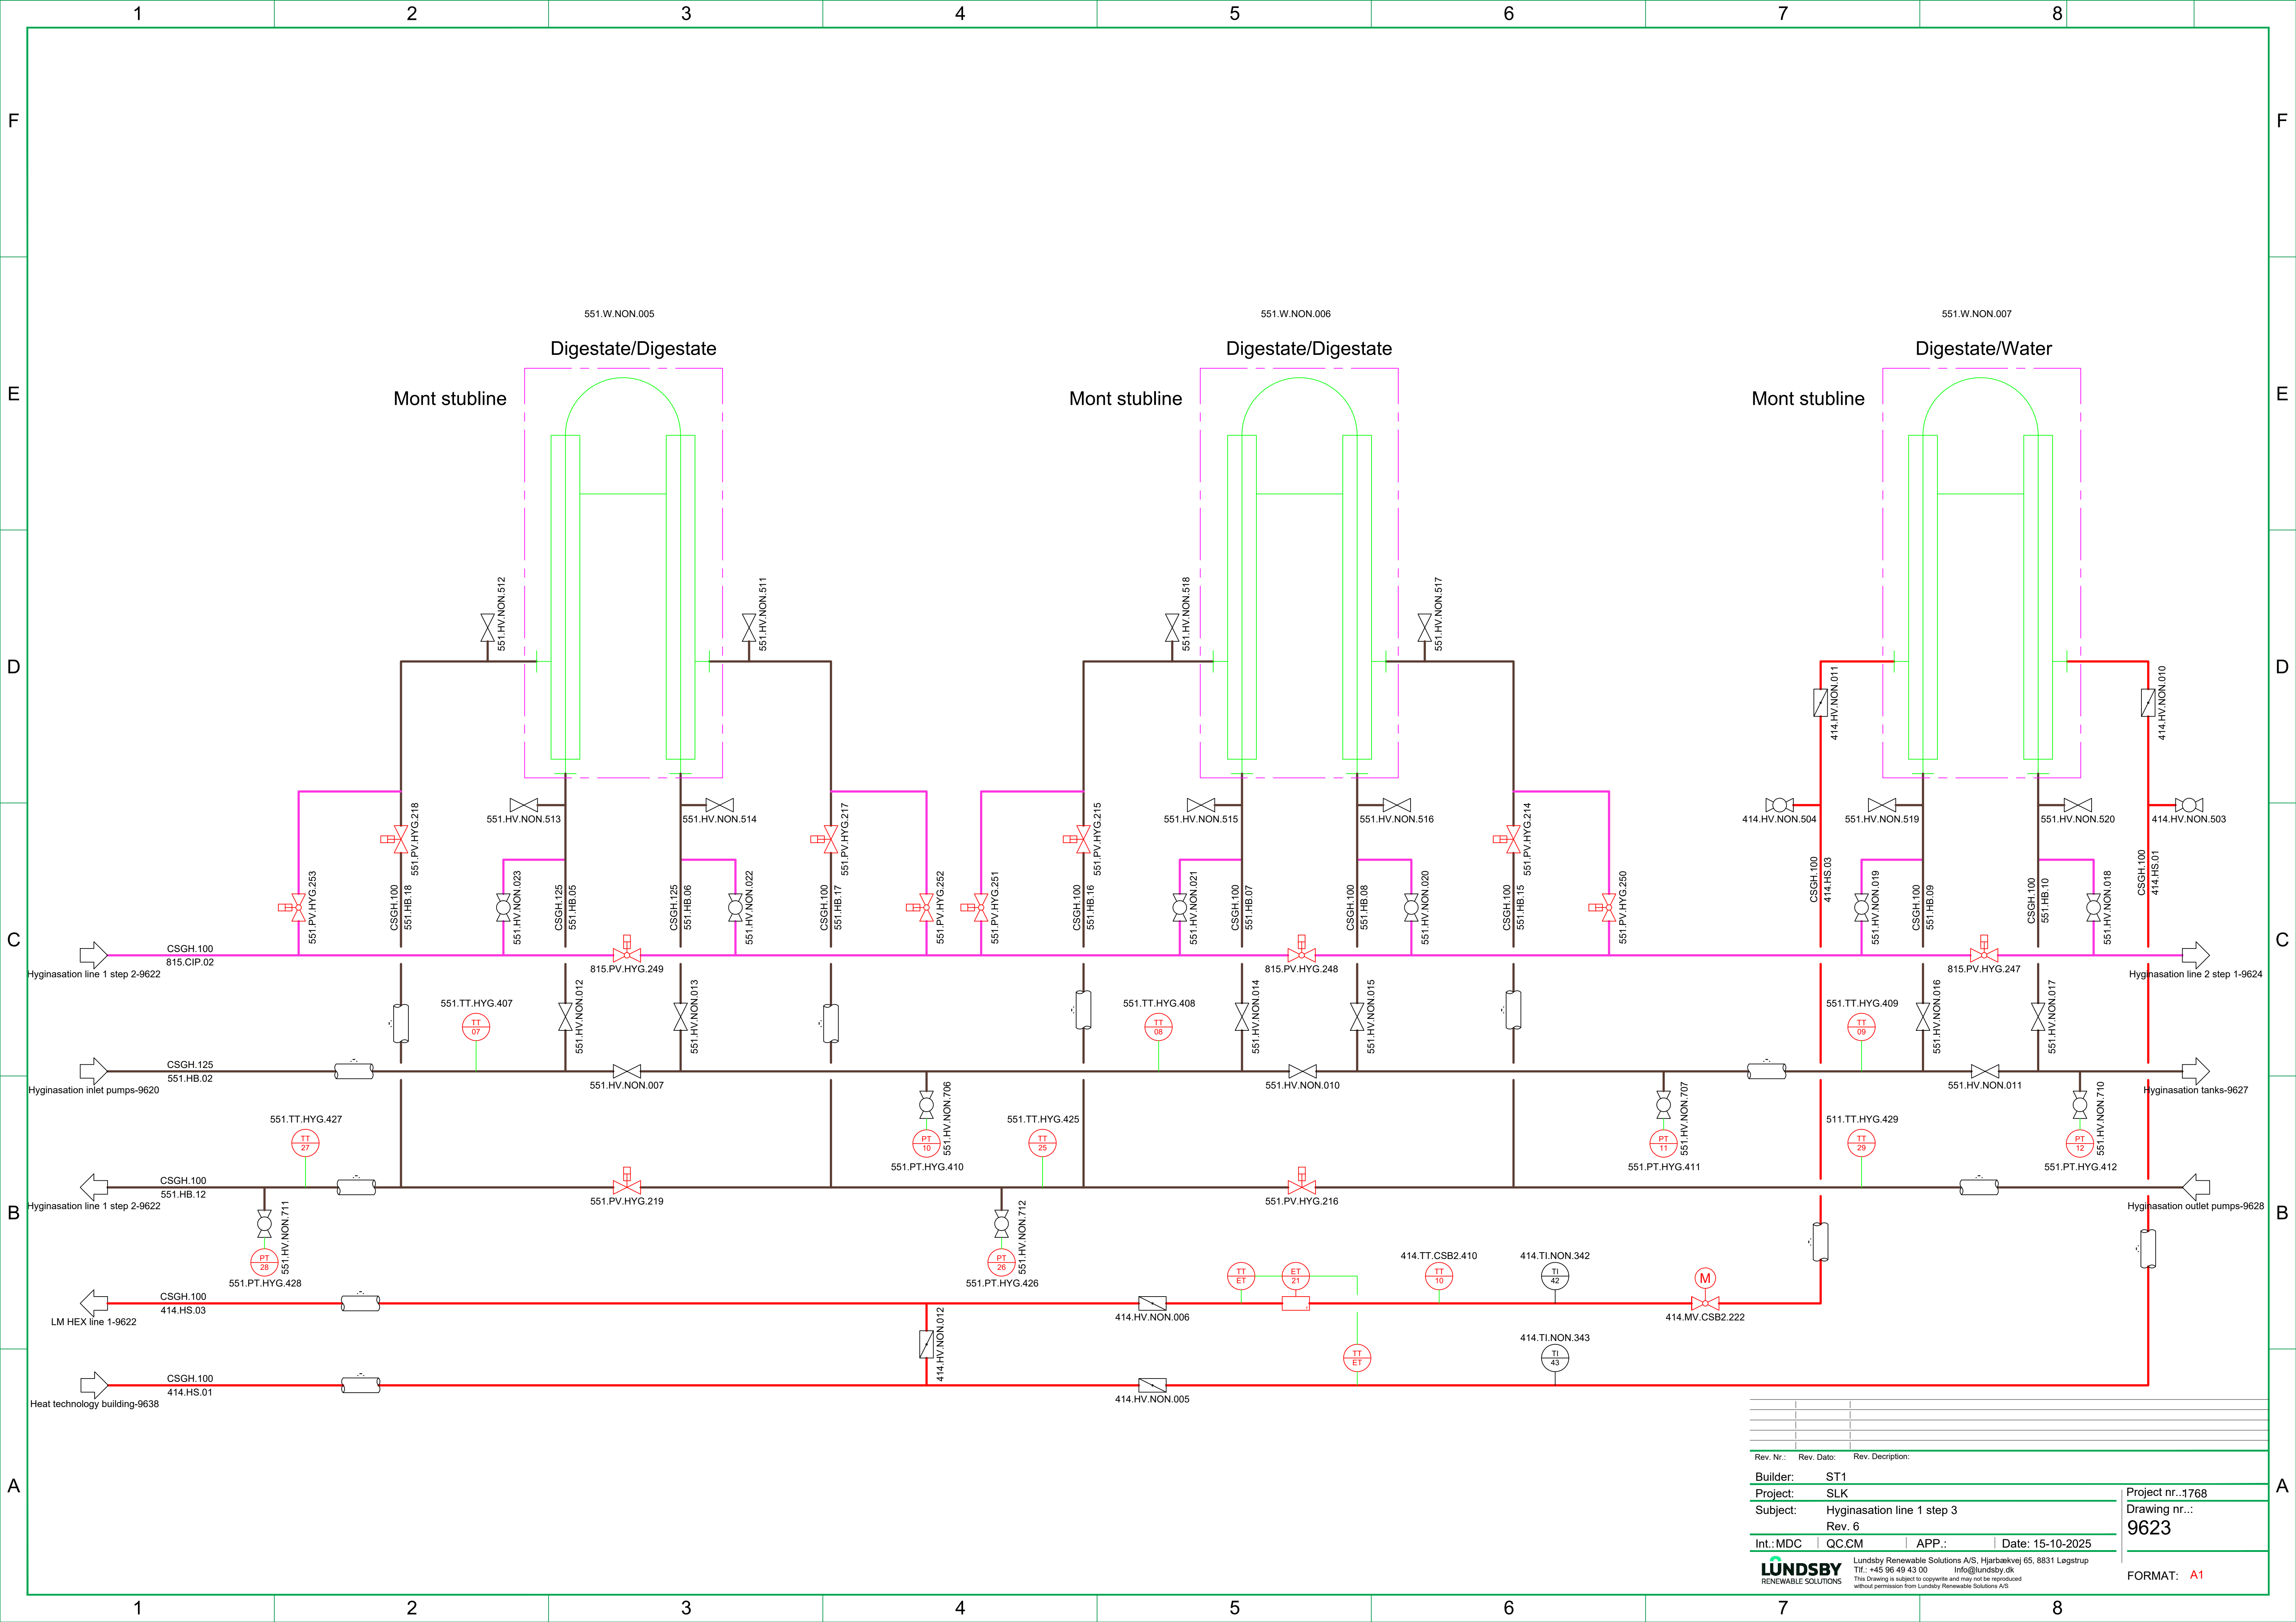


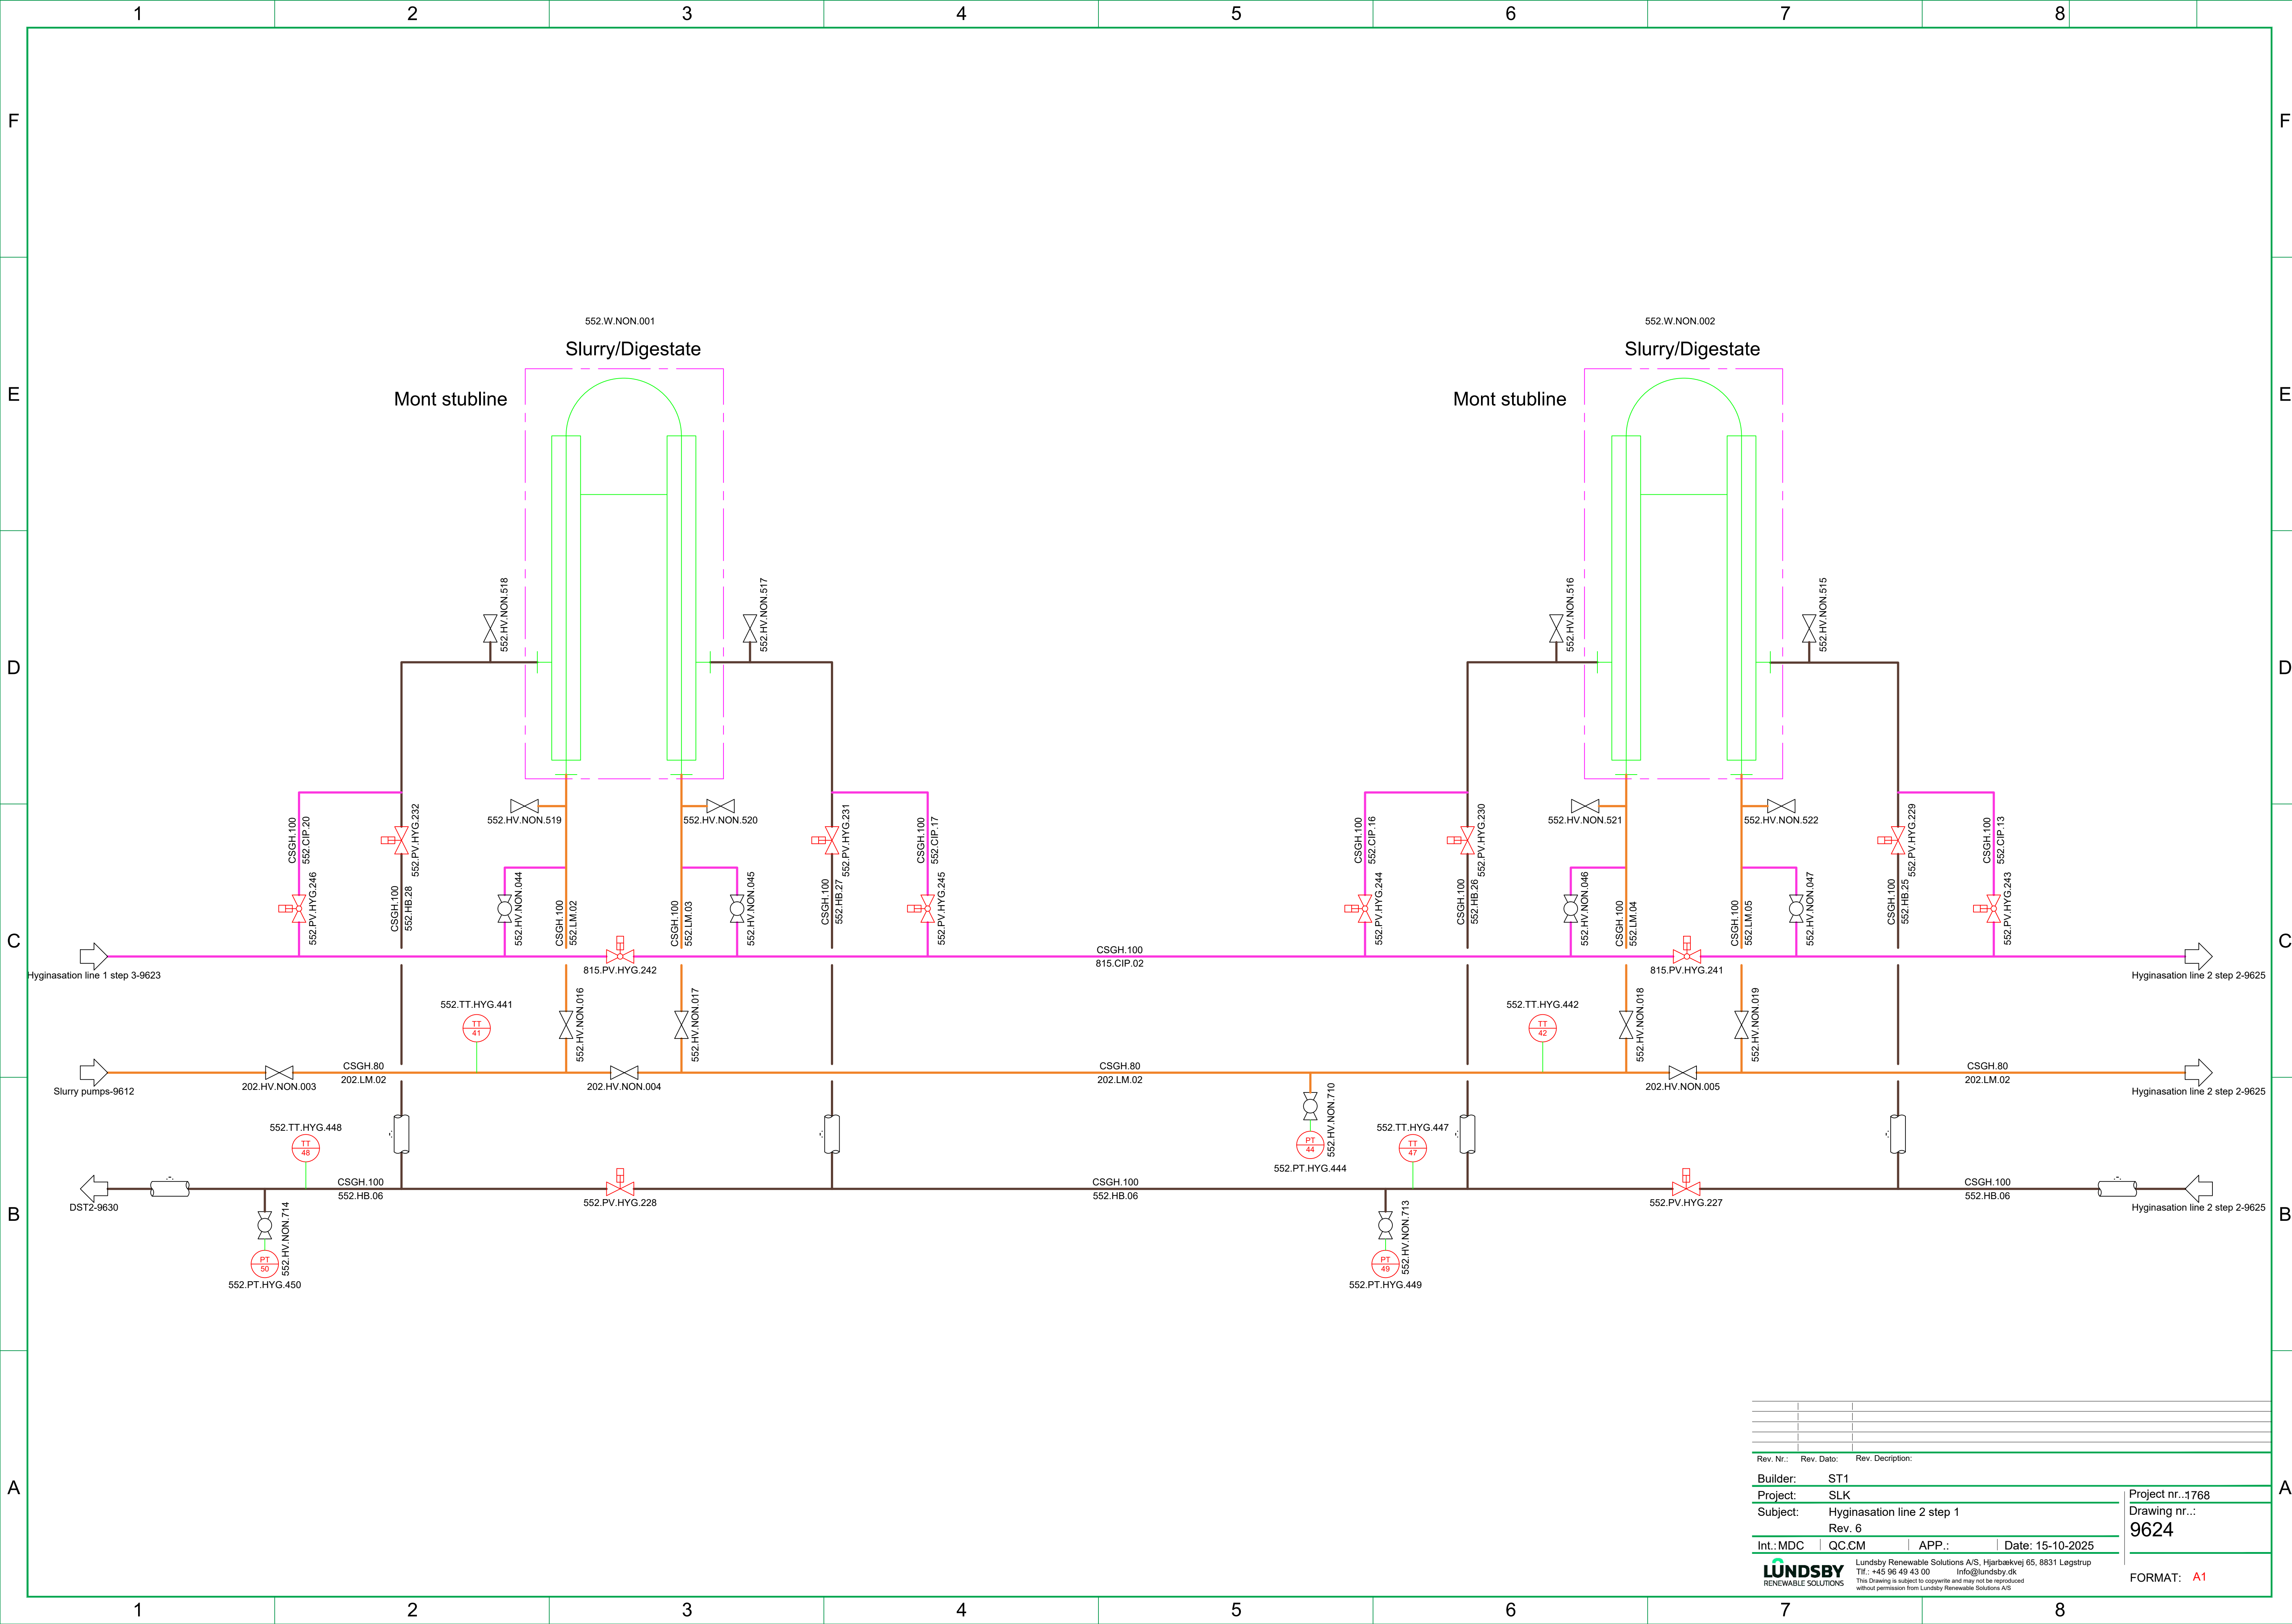

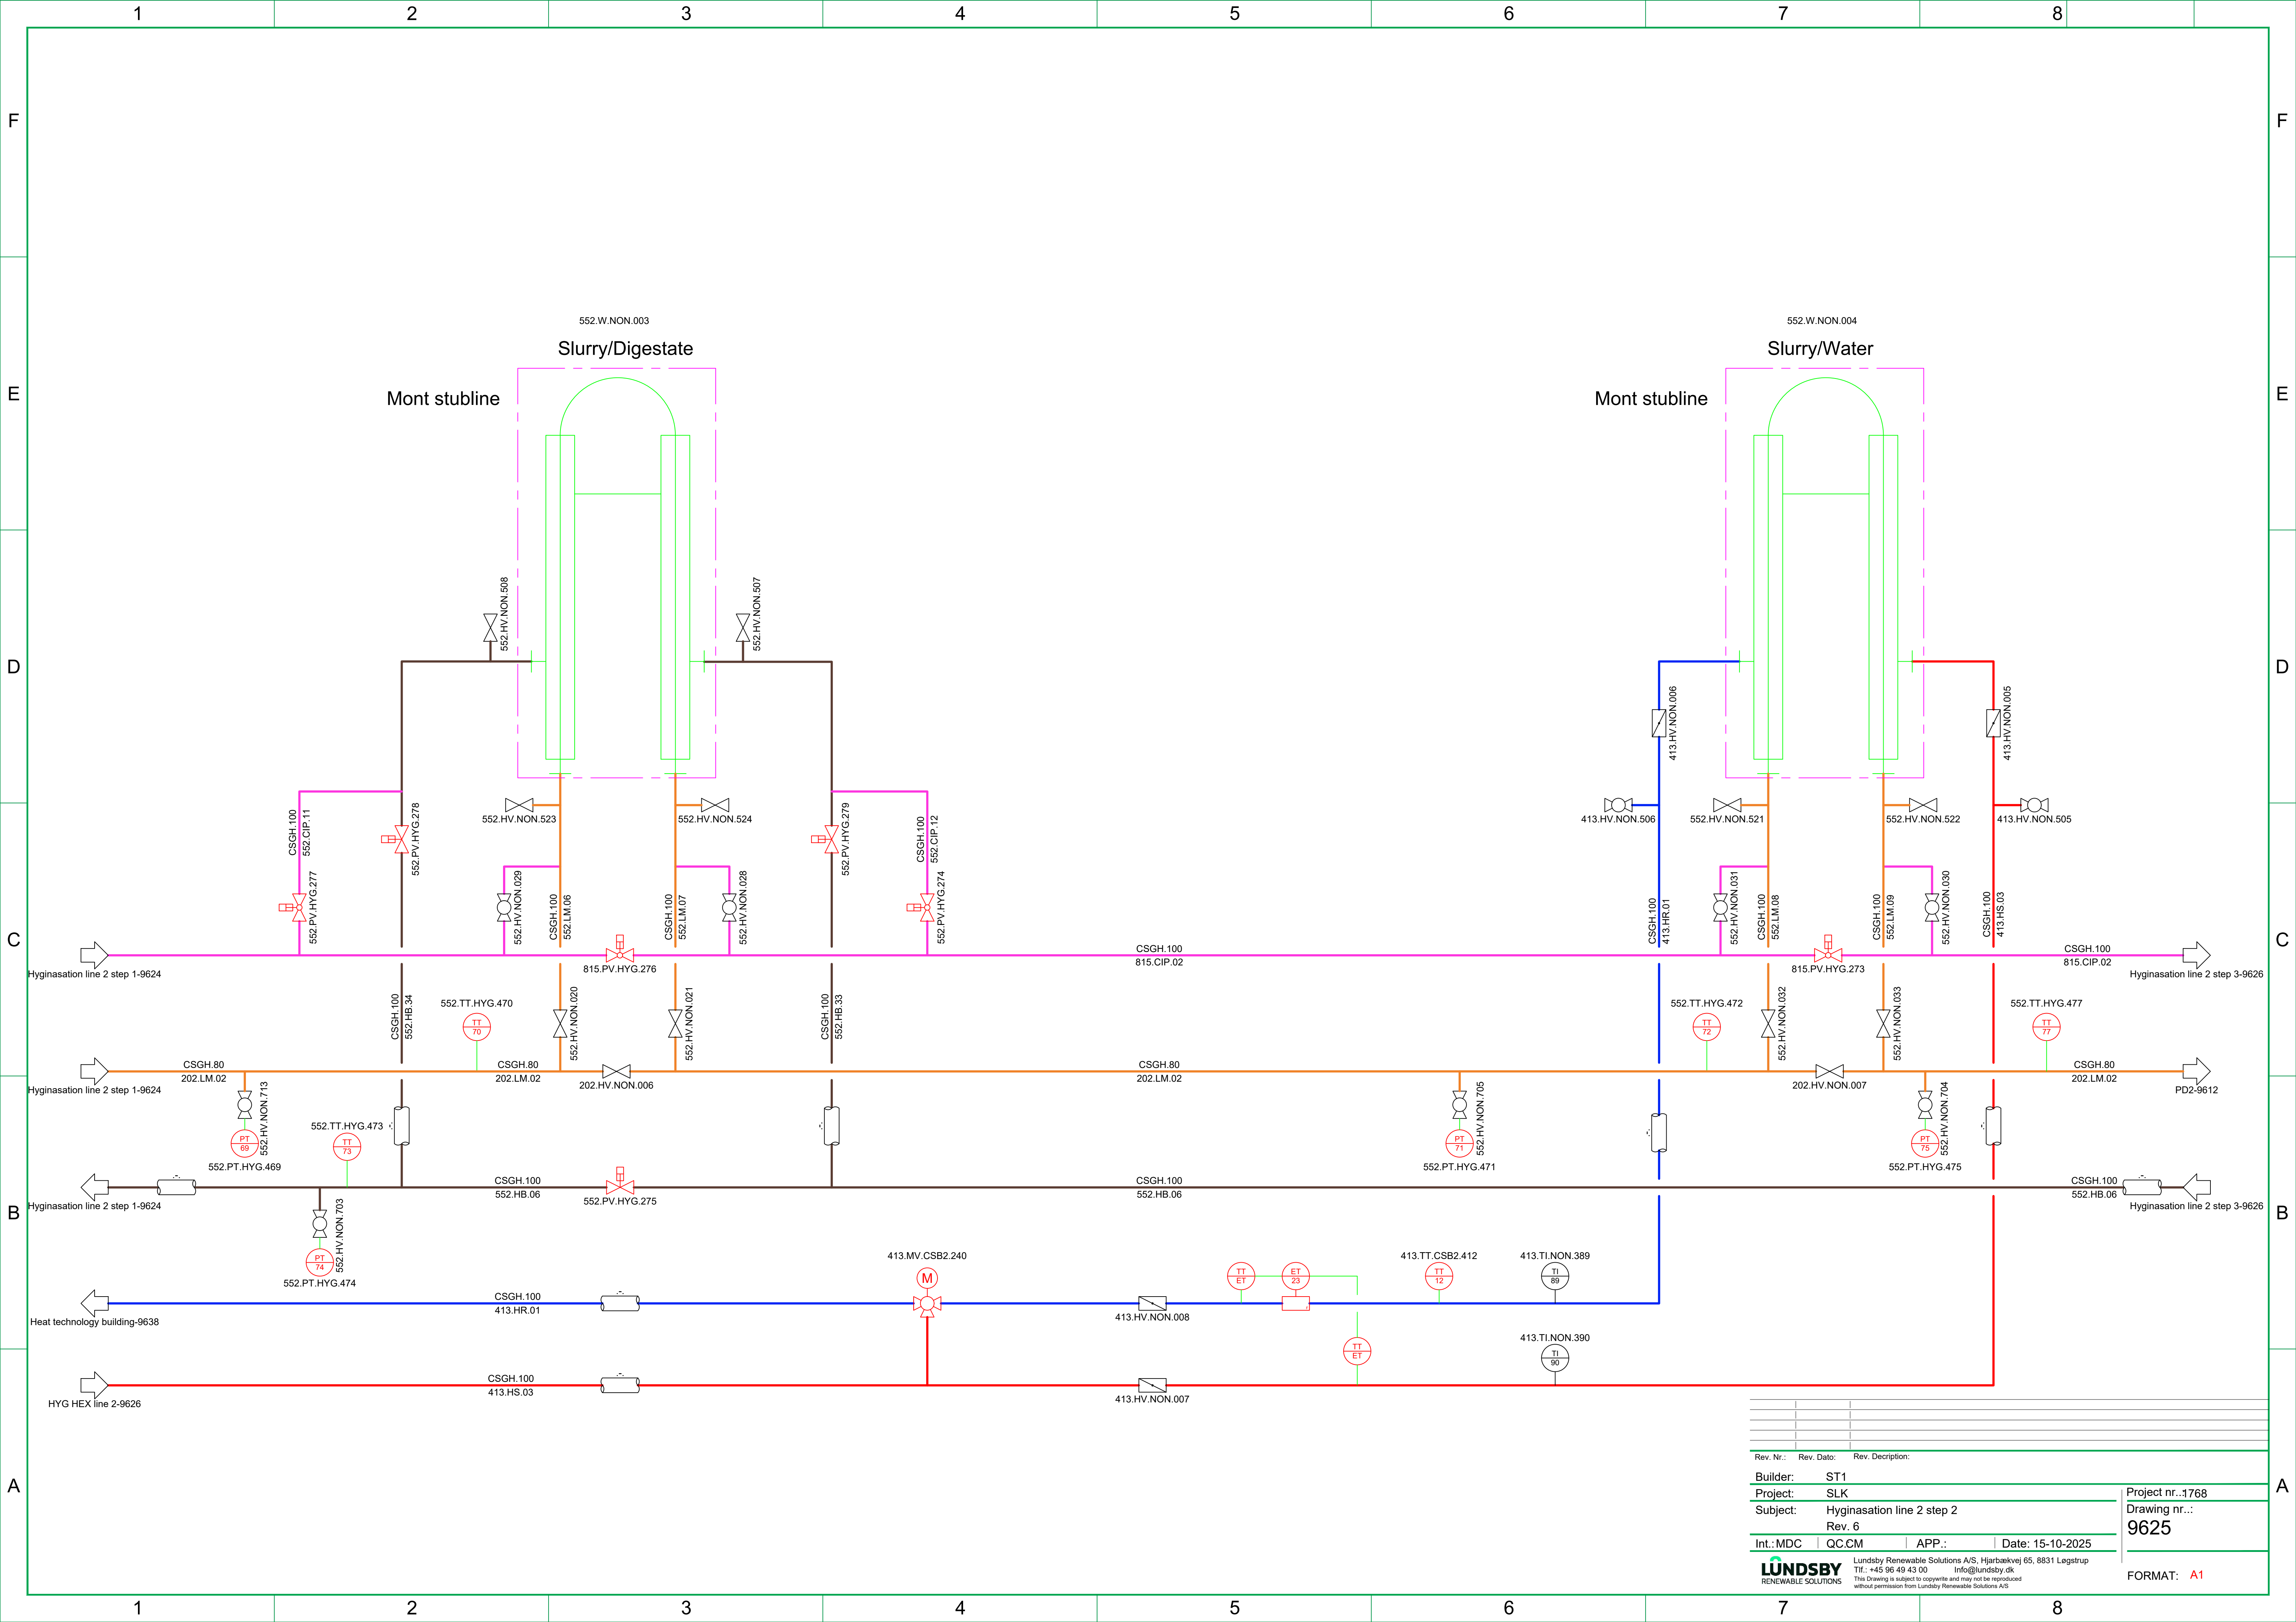

Rev. Nr.:	Rev. Dato:	Rev. Description:
Builder:	ST1	
Project:	SLK	
Subject:	Hyginasation line 2 step 2	
Rev. 6		
Int.: MDC	QC: CM	APP.: Date: 15-10-2025
LUNDSBY RENEWABLE SOLUTIONS		
Lundsgby Renewable Solutions A/S, Hjarbrækvej 65, 8831 Løgstrup Tlf.: +45 96 49 43 00 Info@lundsgby.dk This Drawing is subject to copyright and may not be reproduced without permission from Lundsgby Renewable Solutions A/S		
Project nr.: 1768 Drawing nr.: 9625		FORMAT: A1

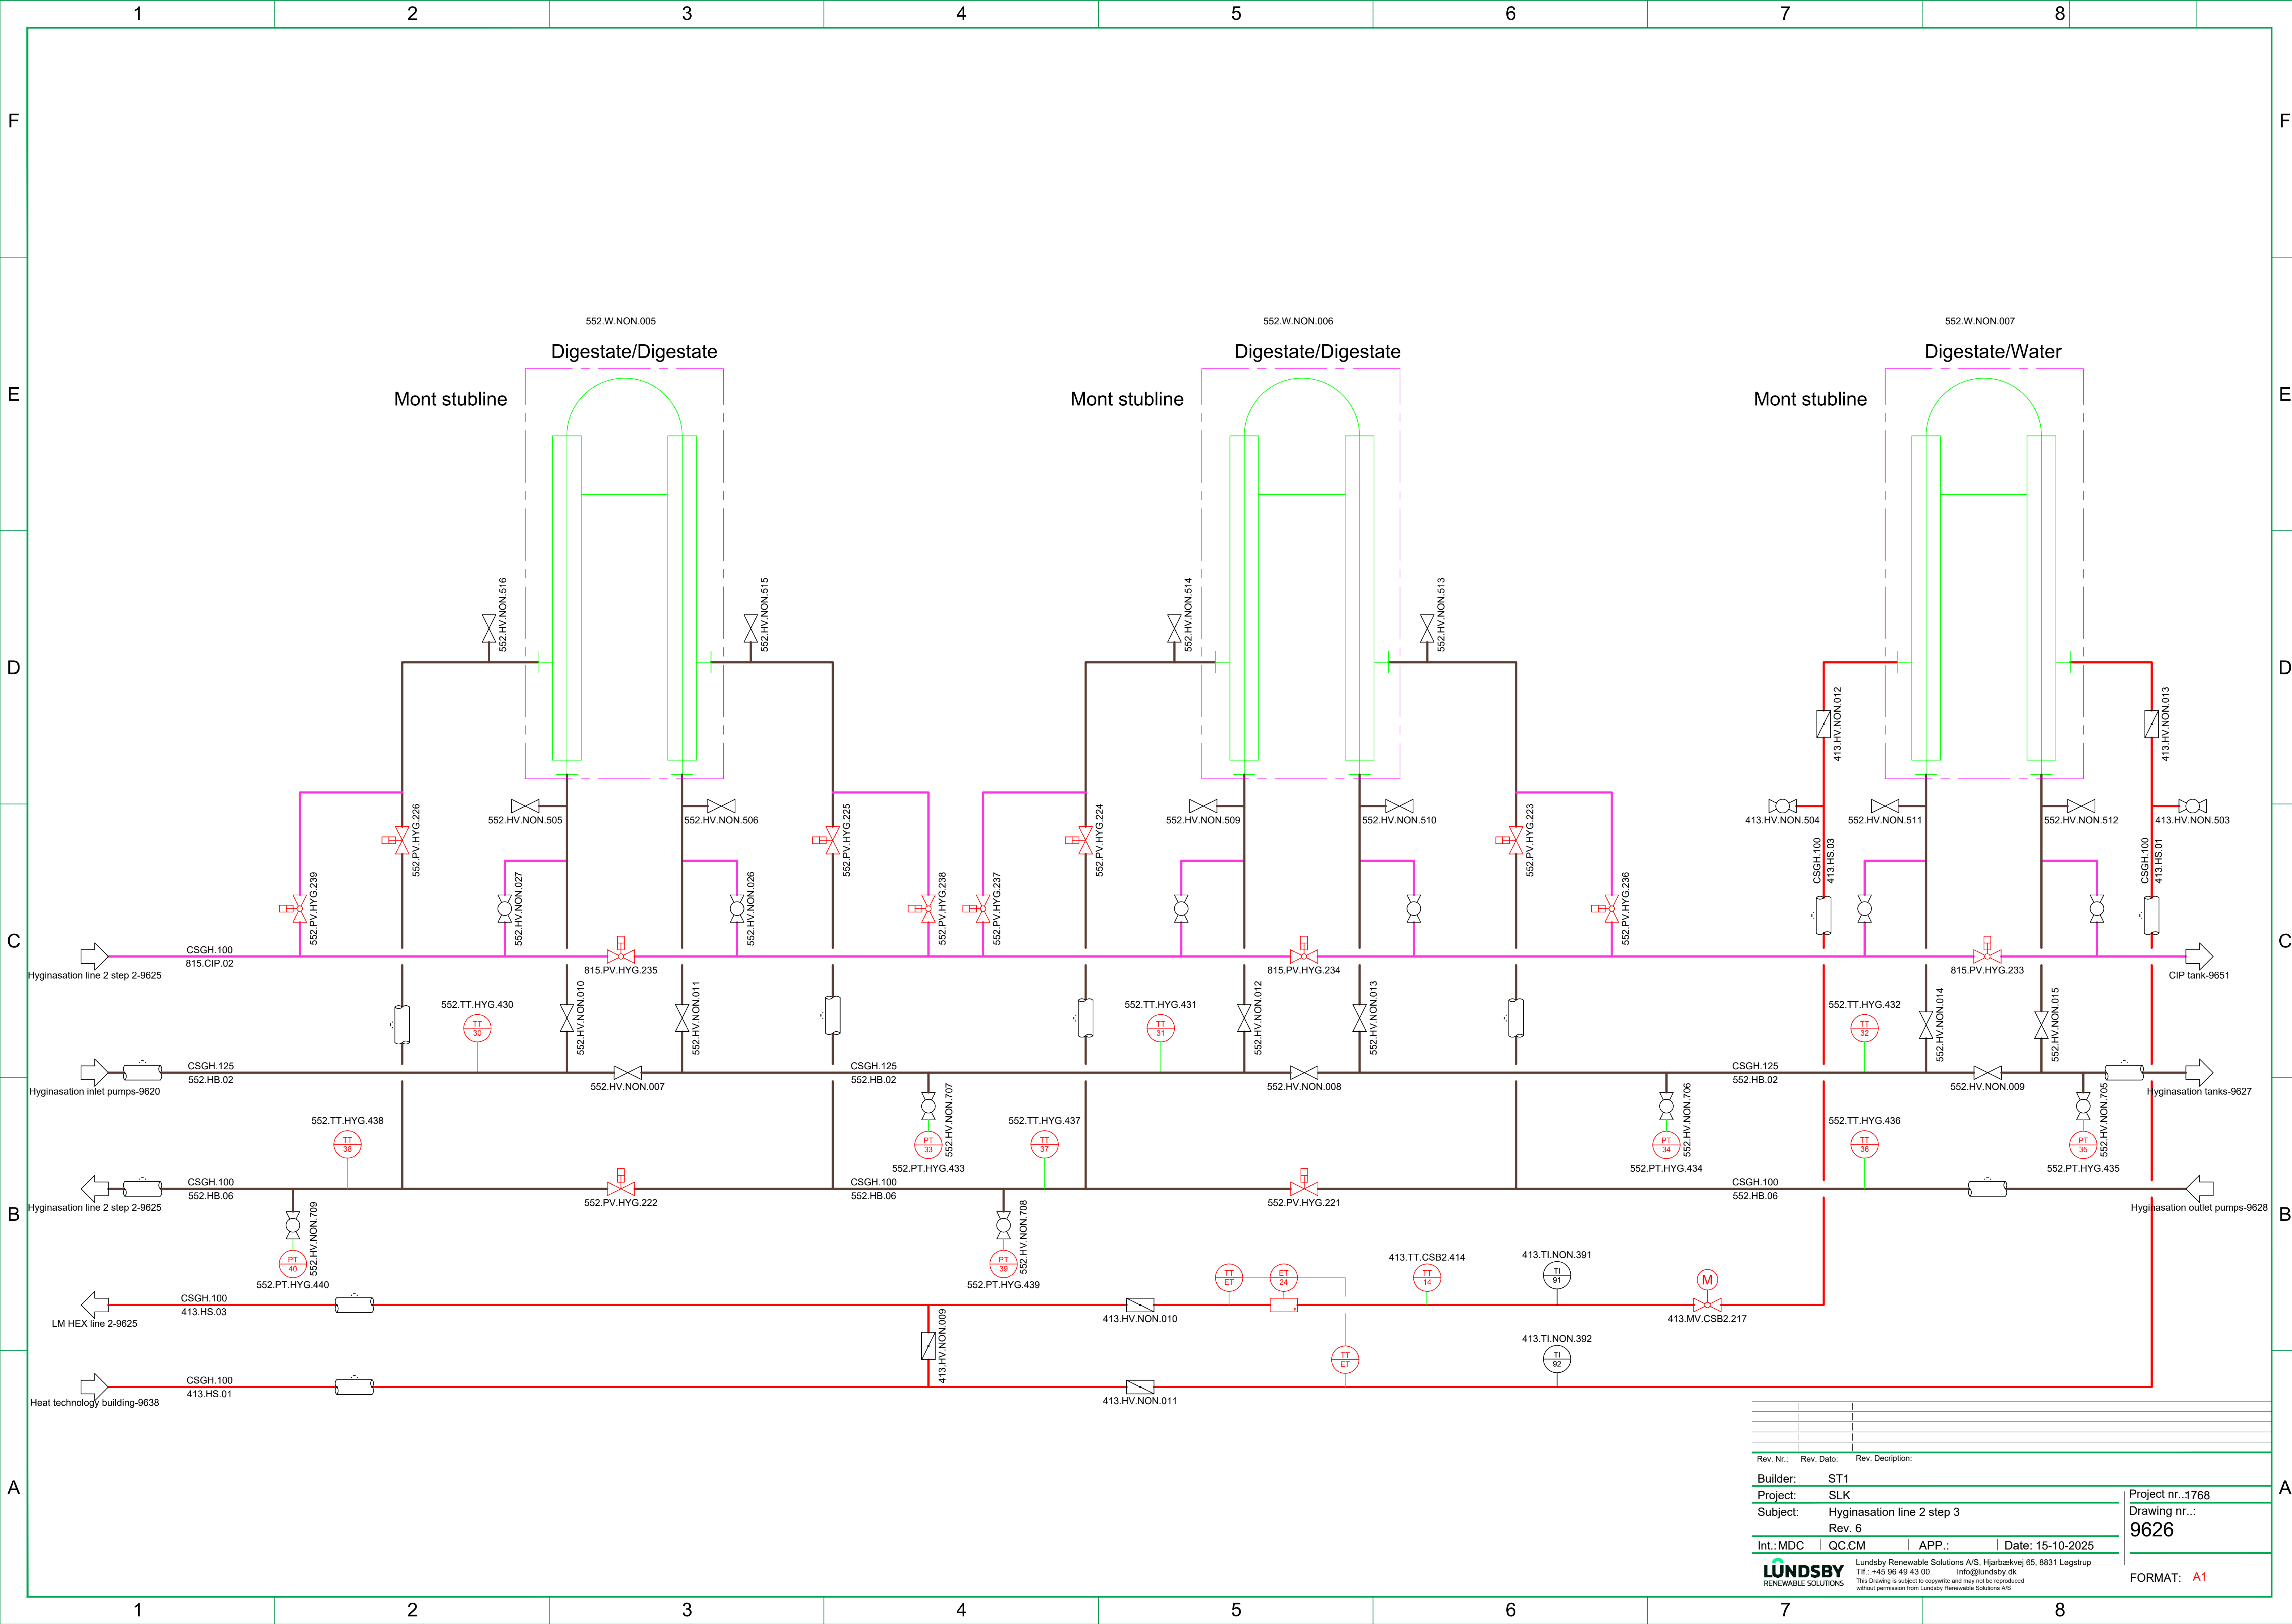


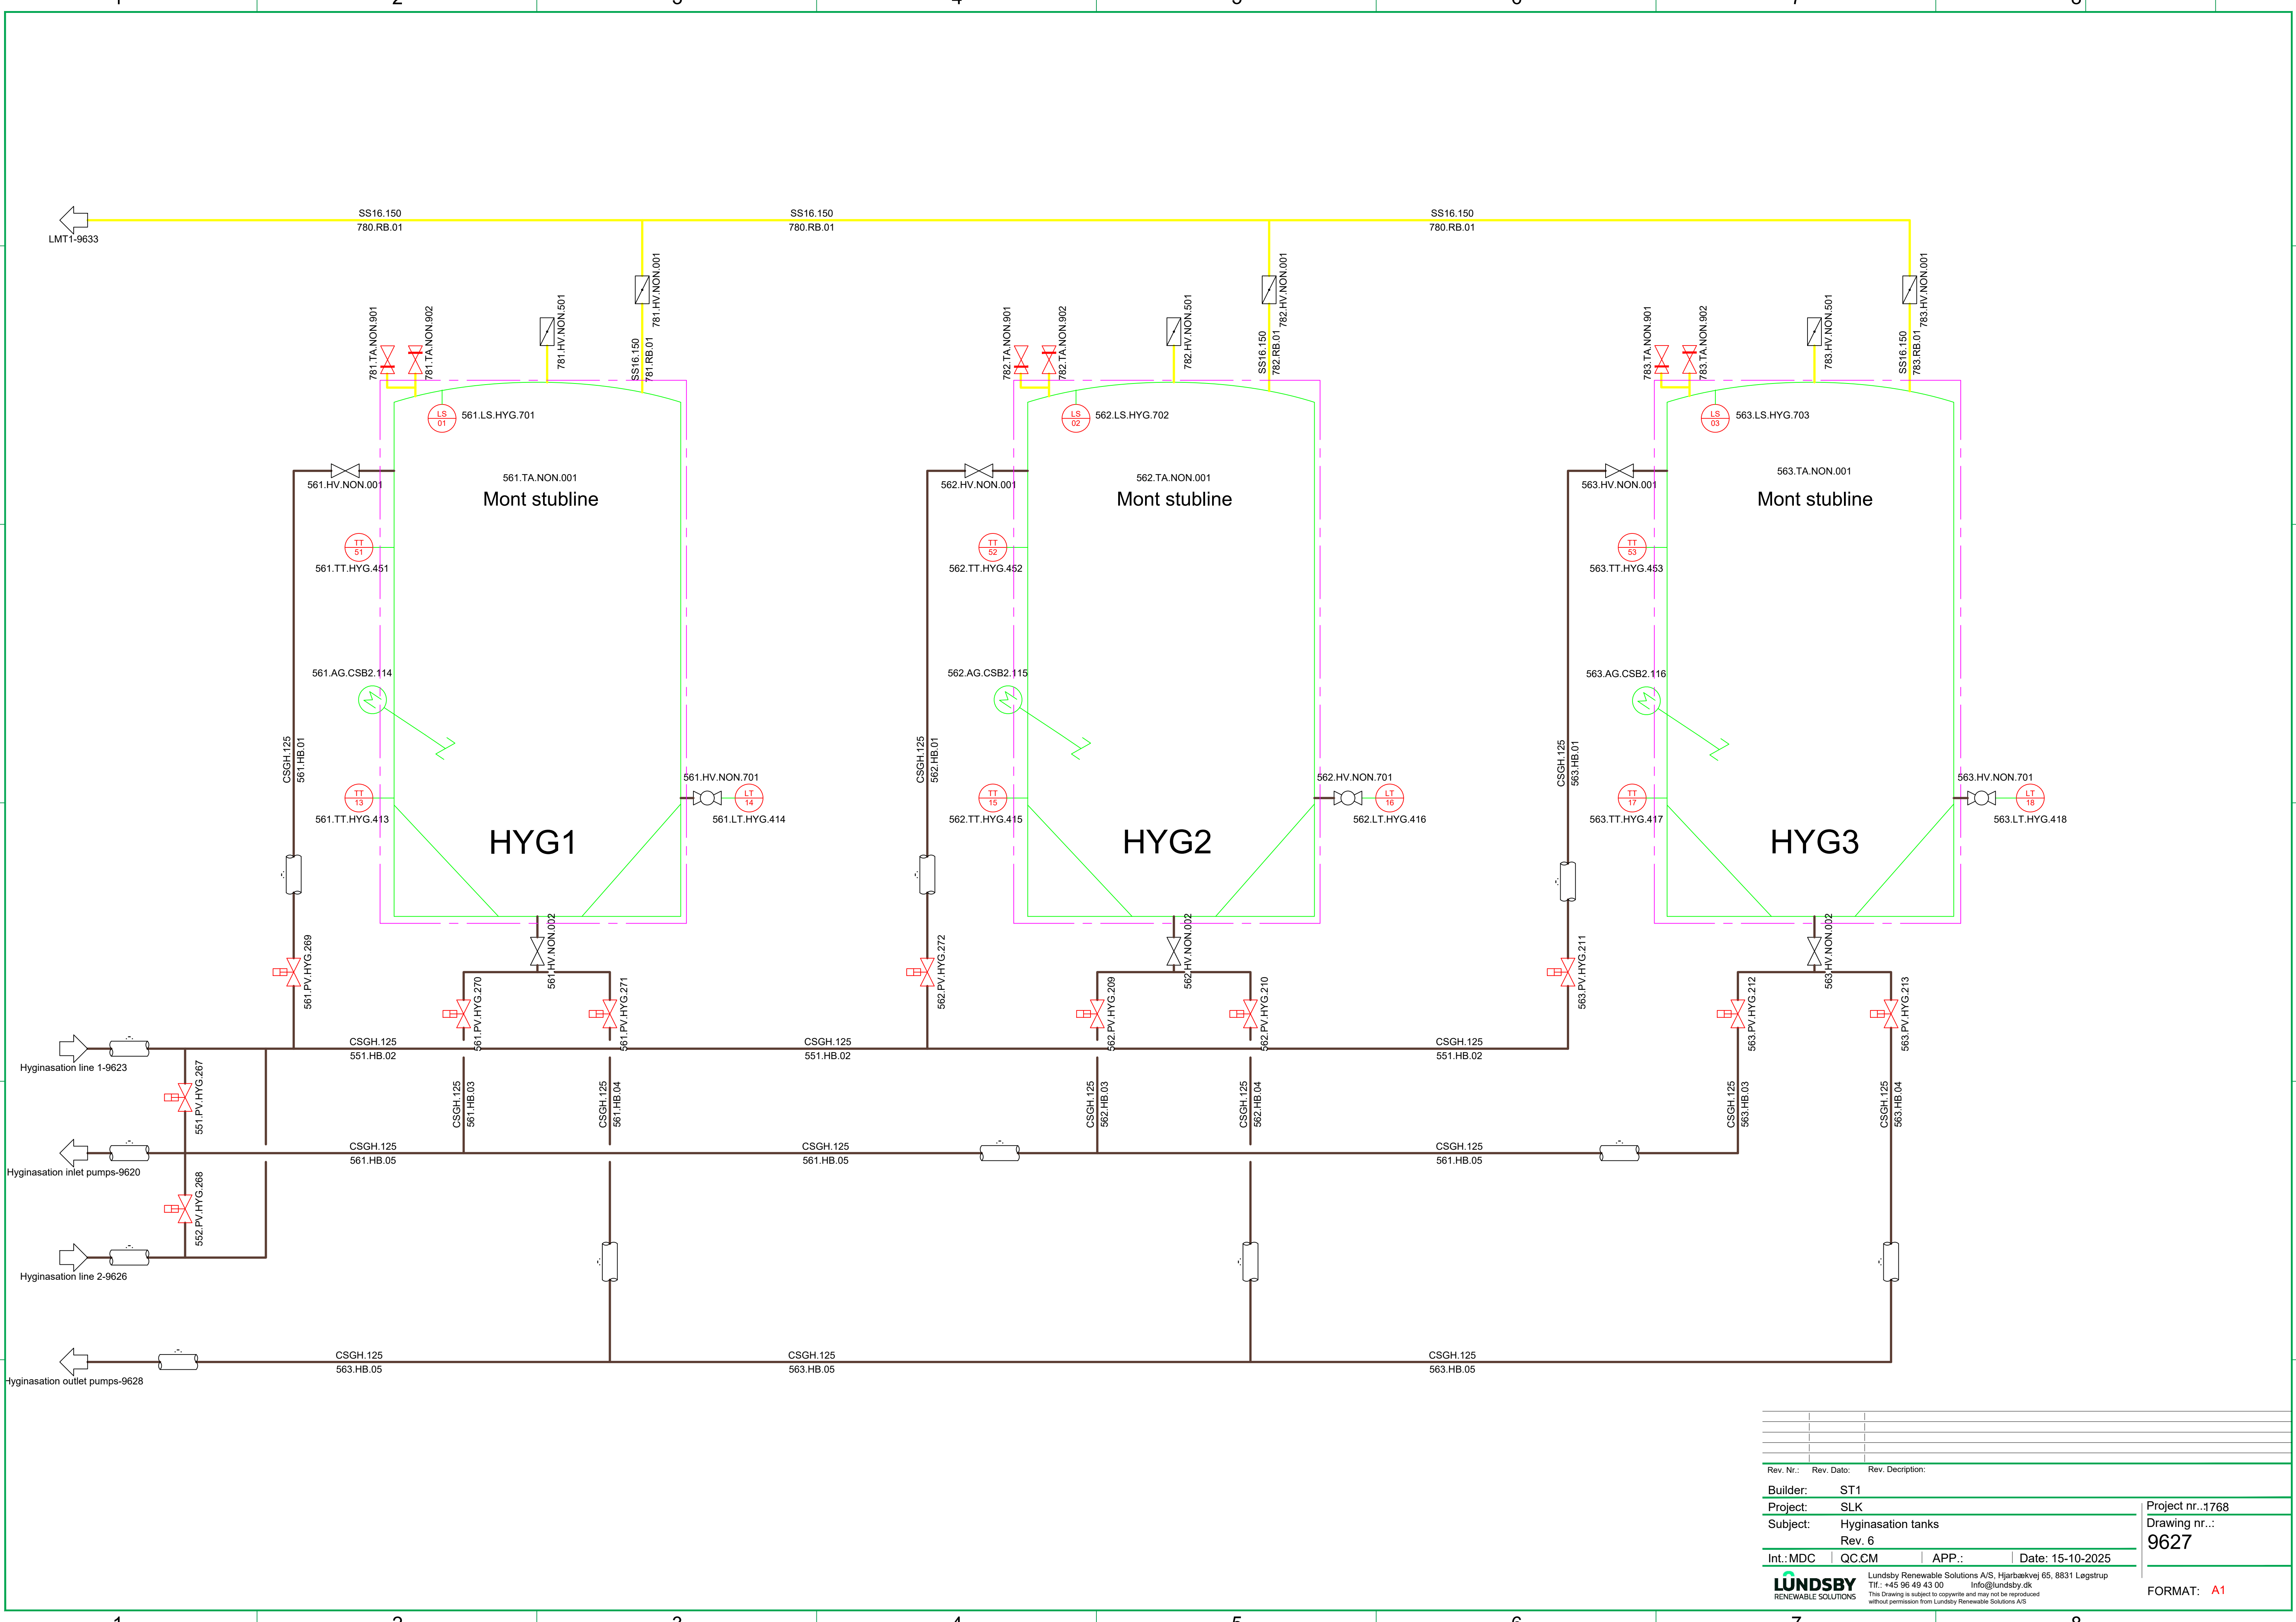


Rev. Nr.:	Rev. Dato:	Rev. Description:
Builder:	ST1	
Project:	SLK	
Subject:	Hyginasation tanks	
Rev. 6		
Int.: MDC	QC.CM	APP.:
Date: 15-10-2025		
LUNDSBY RENEWABLE SOLUTIONS		
Lundsby Renewable Solutions A/S, Hjarbækvej 65, 8831 Løgstrup Tlf.: +45 96 49 43 00 Info@lundsby.dk This Drawing is subject to copyright and may not be reproduced without permission from Lundsby Renewable Solutions A/S		
Project nr.: 1768		Drawing nr.: 9627
FORMAT: A1		

Tech Building


Outlet pumps

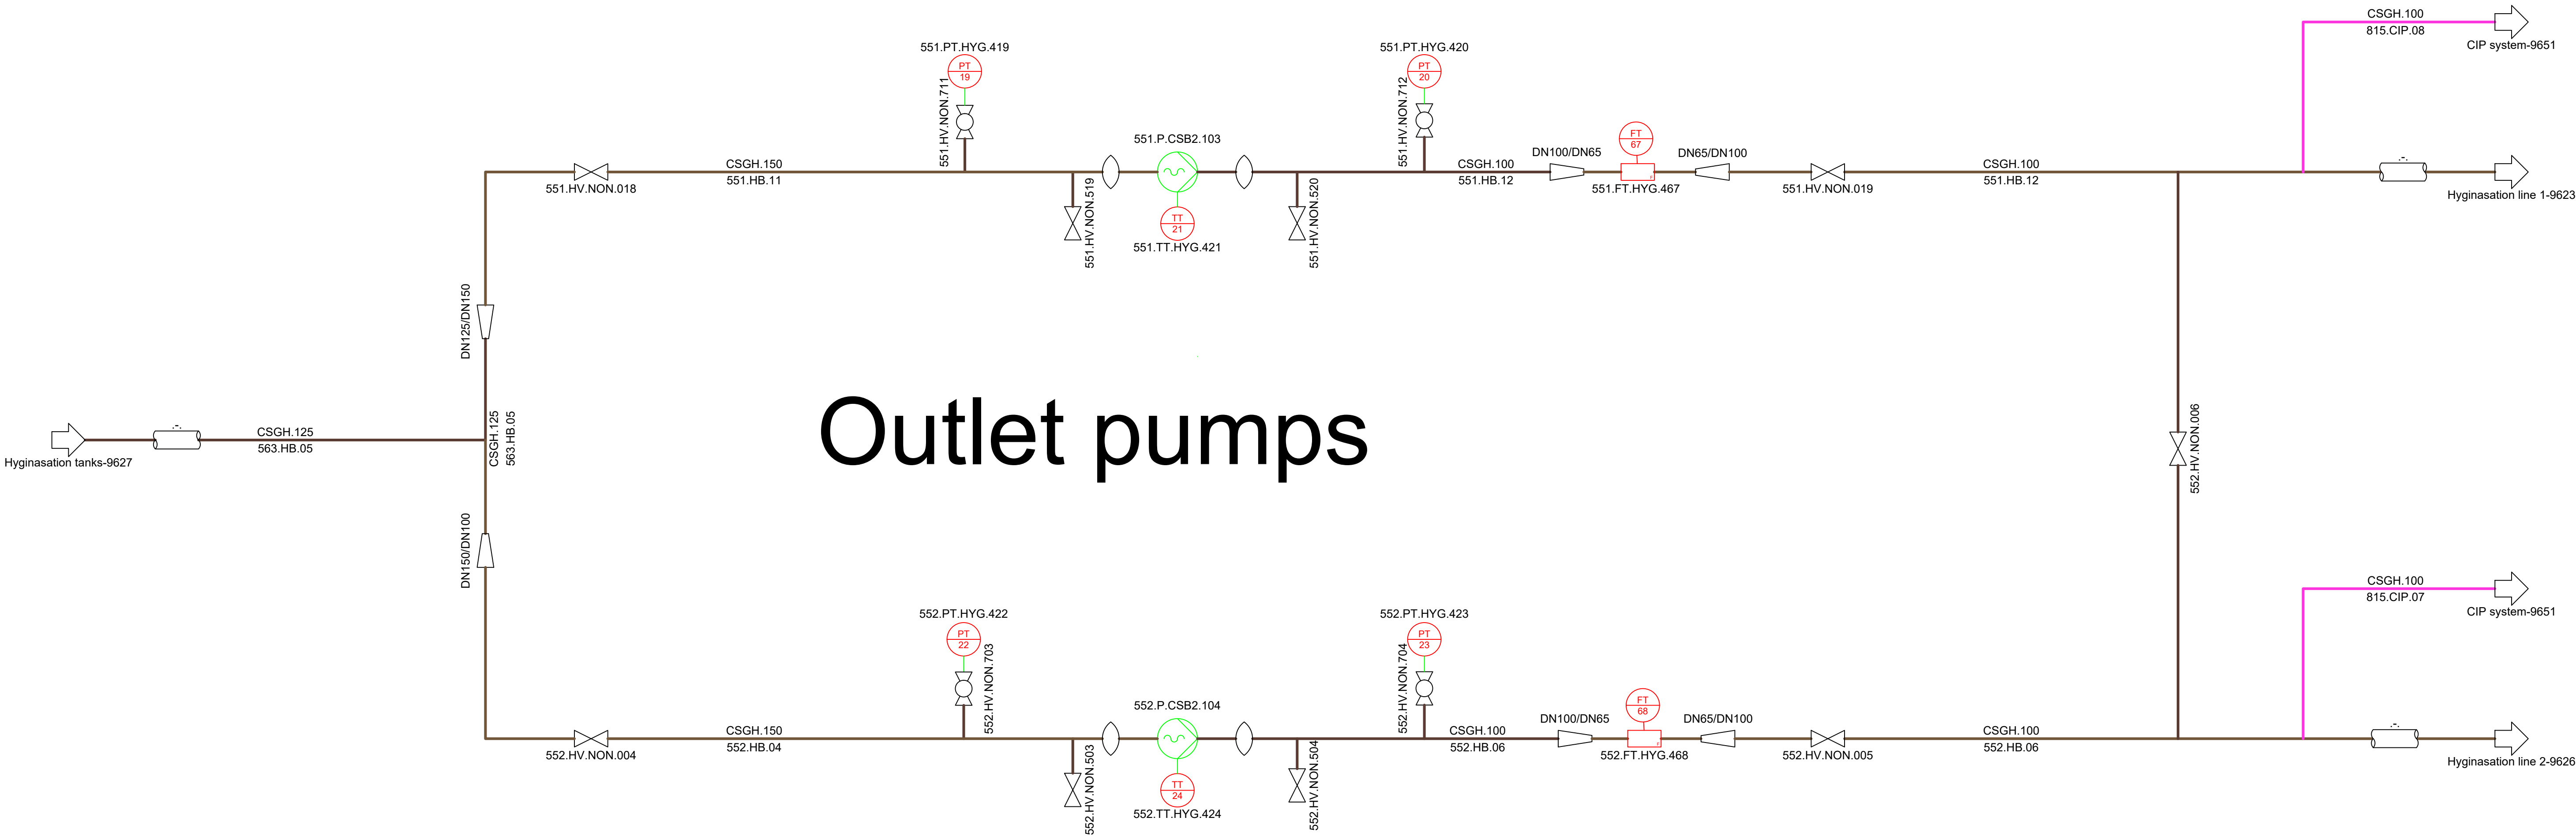


Rev. Nr.:	Rev. Dato:	Rev. Description:	
Builder:	ST1		
Project:	SLK		
Subject:	Hyginasation outlet pumps		
	Rev. 6		
Int.:MDC	QC:CM	APP.:	Date: 15-10-2025
LUNDSBY RENEWABLE SOLUTIONS			Lundsby Renewable Solutions A/S, Hjarbækvej 65, 8831 Løgstrup Tlf.: +45 96 49 43 00 Info@lundsby.dk This Drawing is subject to copyright and may not be reproduced without permission from Lundsby Renewable Solutions A/S
			Project nr.:1768 Drawing nr.: 9628 FORMAT: A1

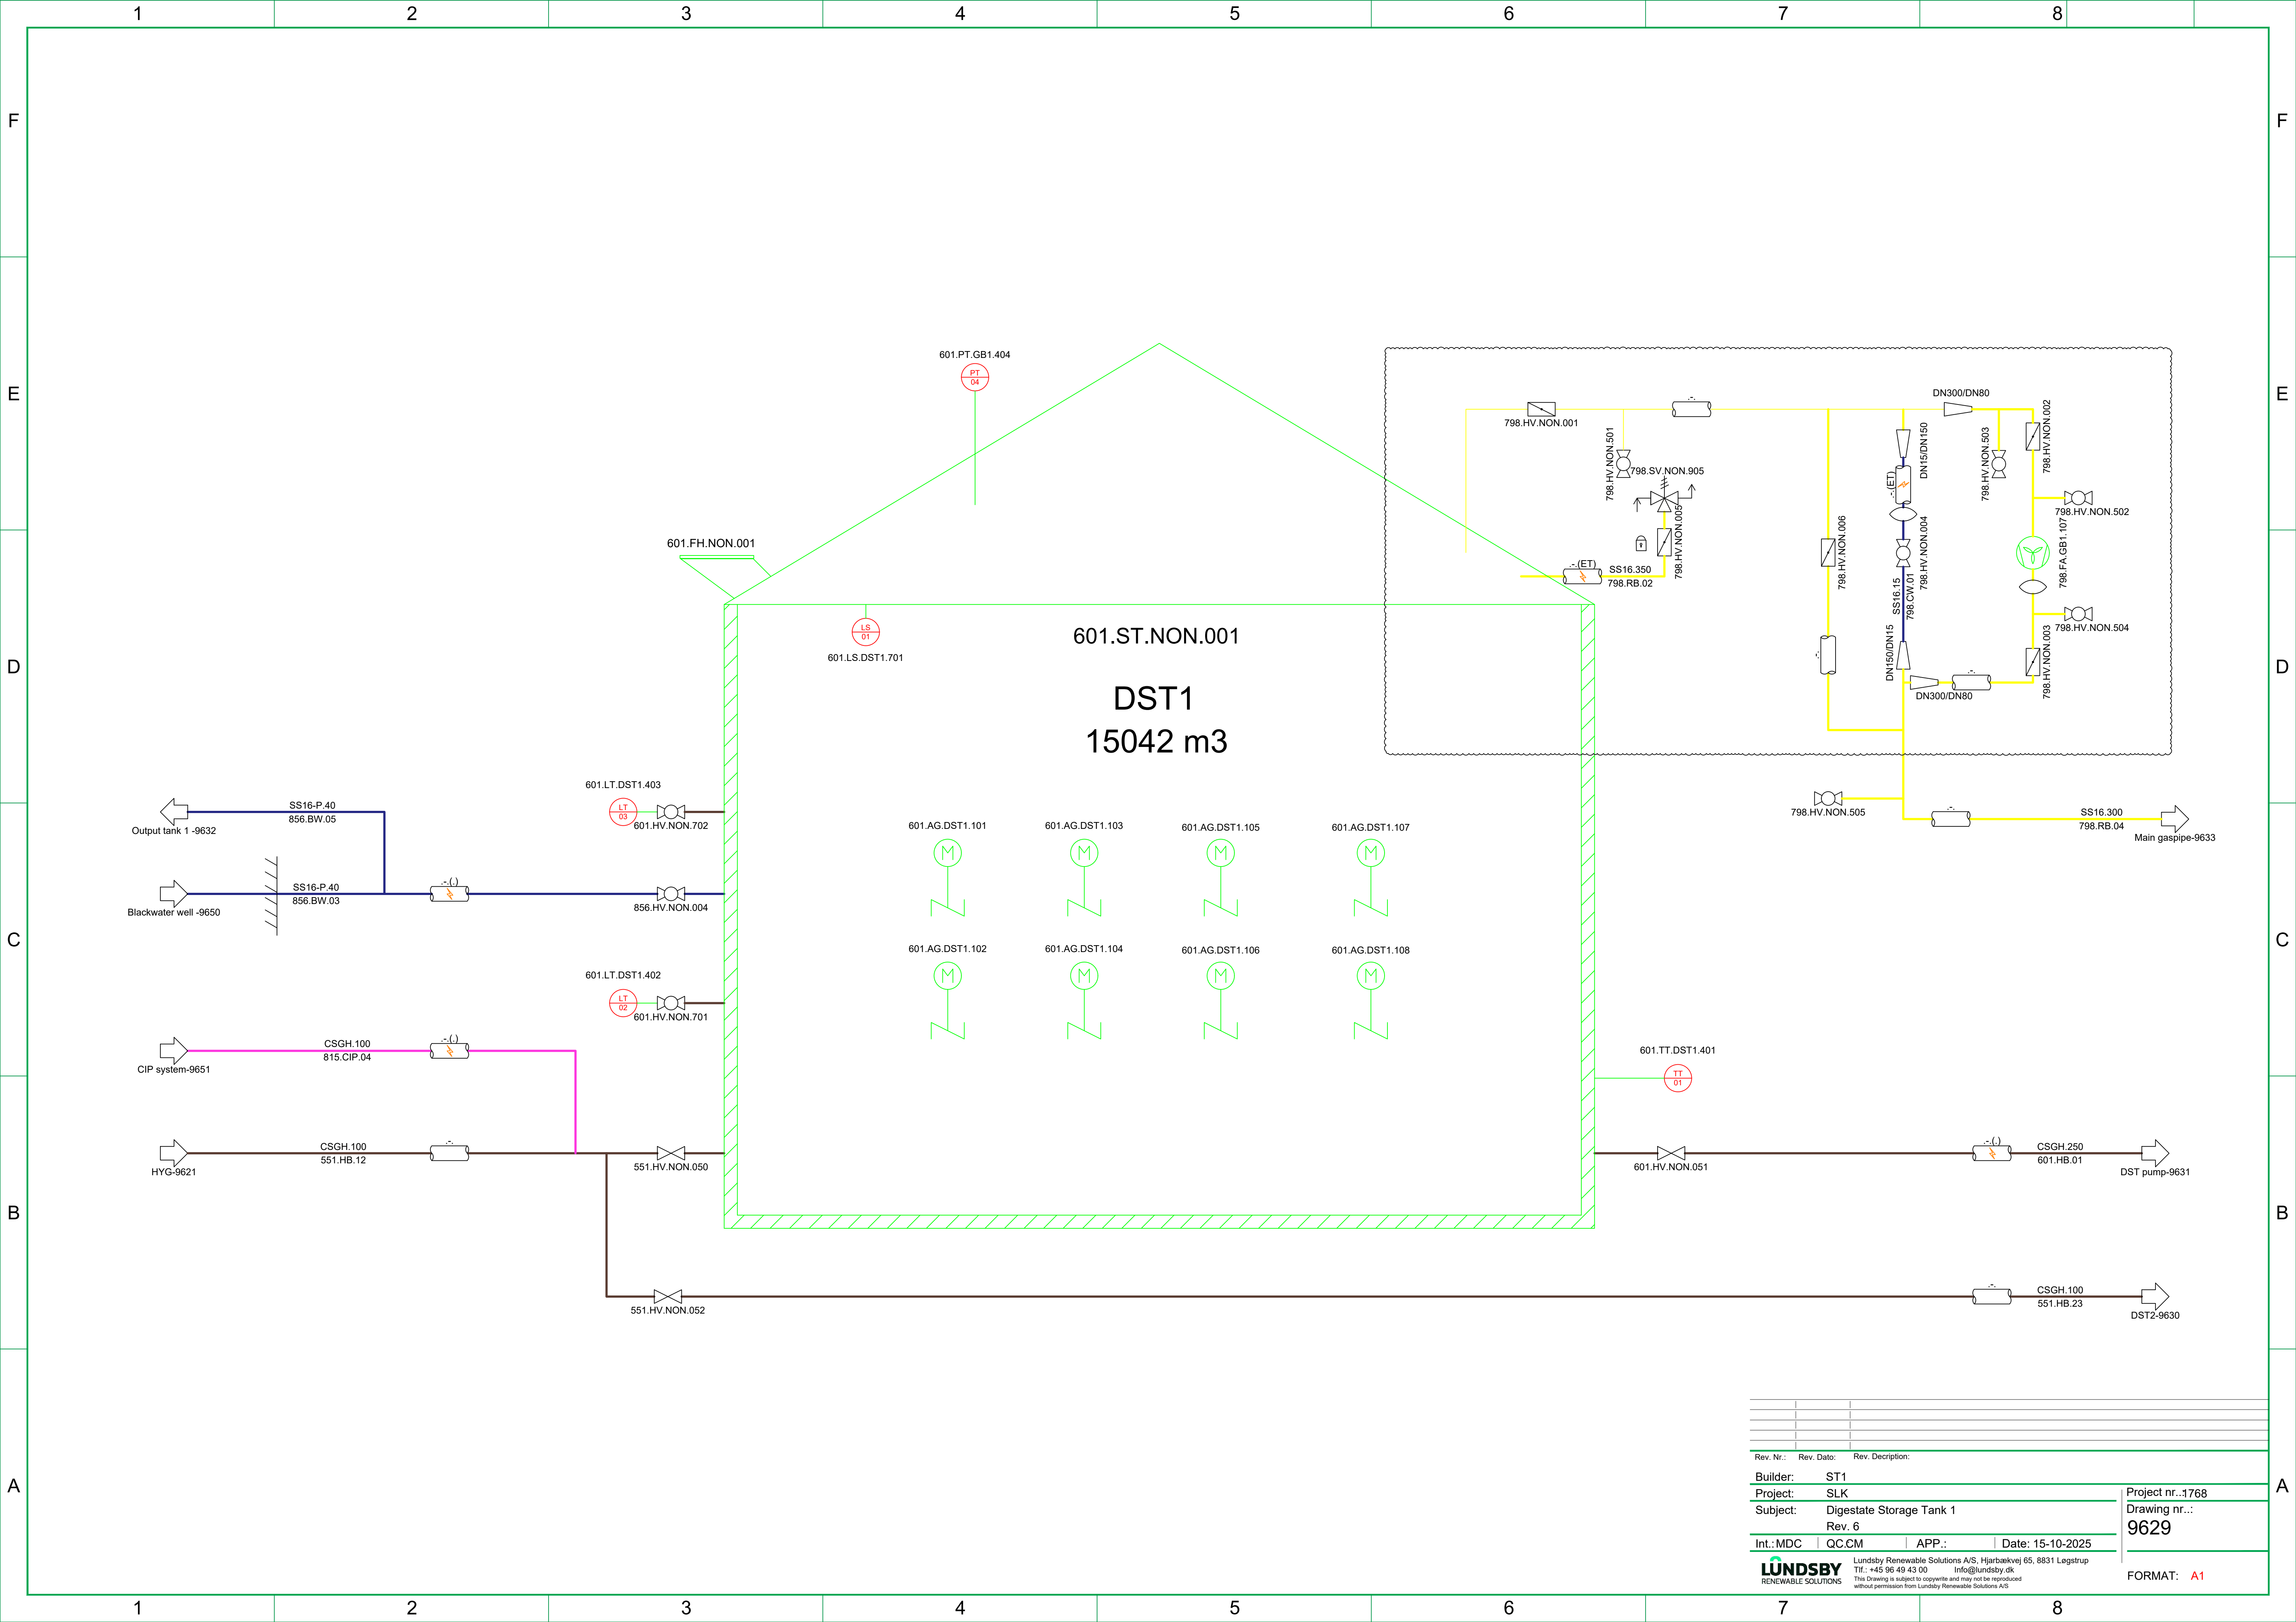


Rev. Nr.:	Rev. Dato:	Rev. Description:	
Builder:	ST1		
Project:	SLK		
Subject:	Digestate Storage Tank 1		
Rev. 6			
Int.:MDC	QC:CM	APP.:	Date: 15-10-2025
LUNDSBY RENEWABLE SOLUTIONS			Lundsby Renewable Solutions A/S, Hjarbækvej 65, 8831 Løgstrup Tlf.: +45 96 49 43 00 Info@lundsby.dk This drawing is subject to copyright and may not be reproduced without permission from Lundsby Renewable Solutions A/S
Project nr...1768 Drawing nr...: 9629			FORMAT: A1

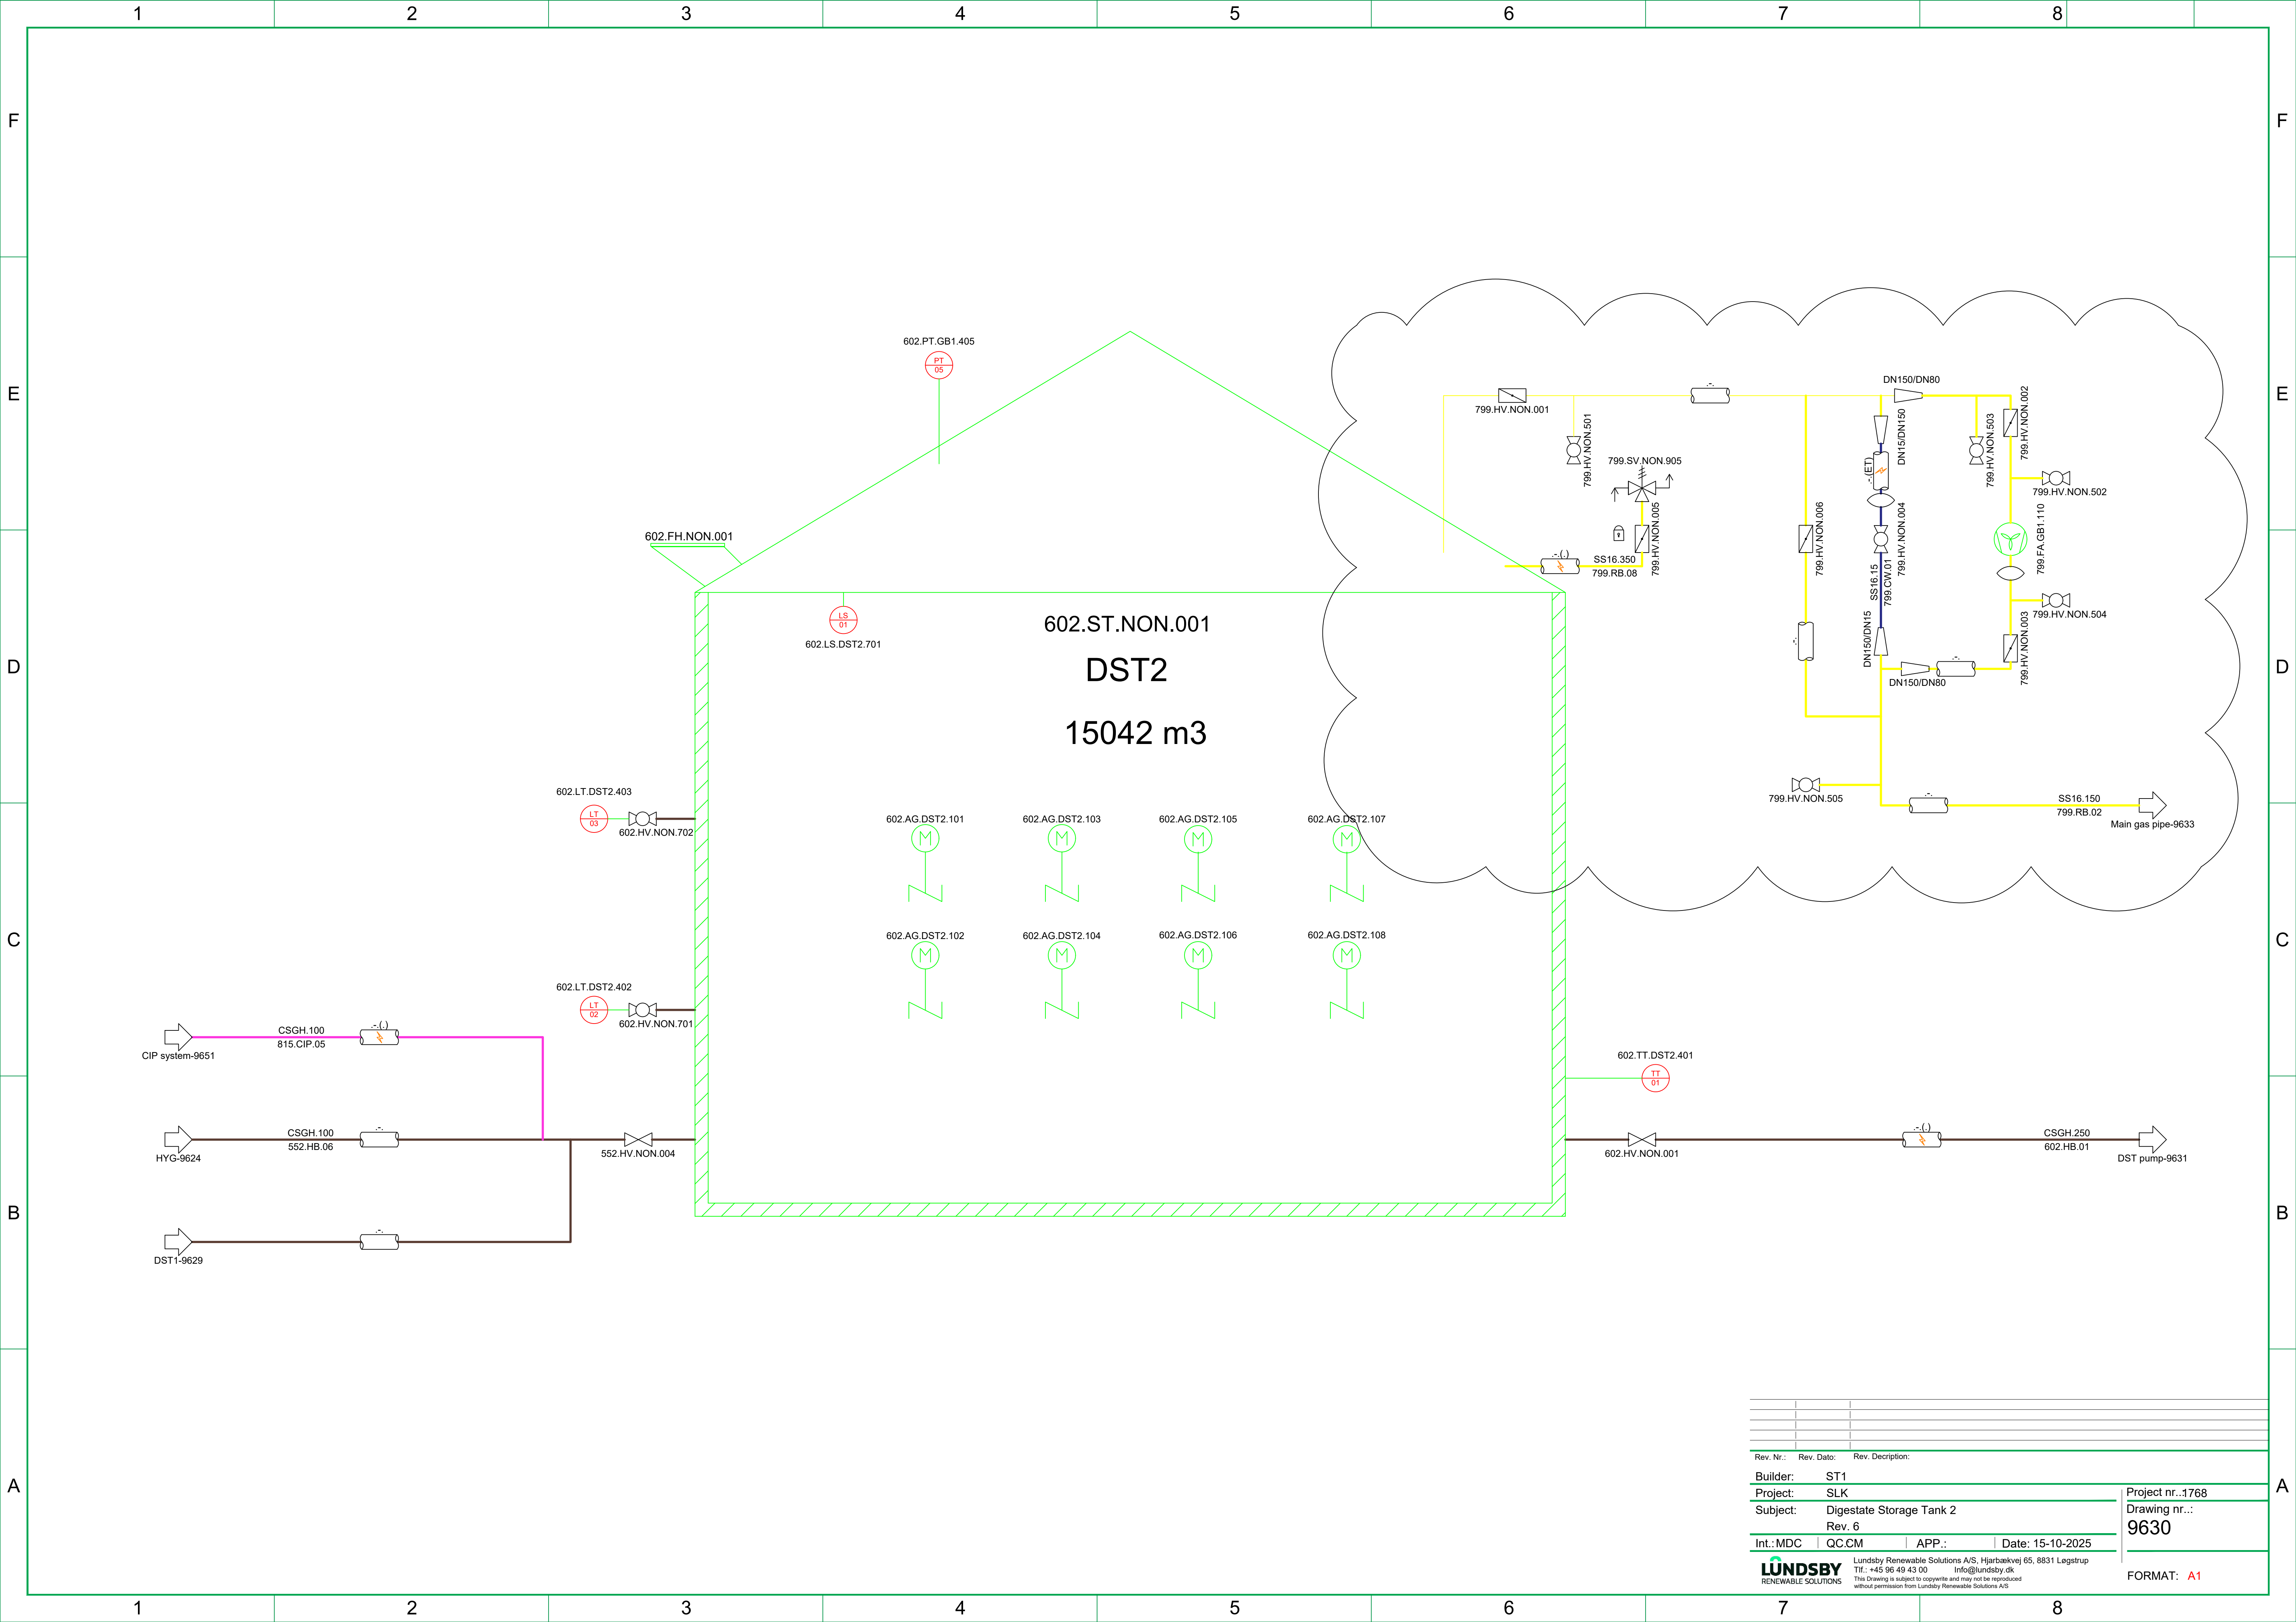


Rev. Nr.: Rev. Dato: Rev. Description:			Project nr.:1768	
Builder: ST1			Drawing nr.: 9630	
Project: SLK			Date: 15-10-2025	
Subject: Digestate Storage Tank 2			Format: A1	
Rev. 6			Lundsgby Renewable Solutions A/S, Hjarbrækvej 65, 8831 Lægstrup	
Int.:MDC QC:CM APP.:			Tlf.: +45 96 49 43 00 Info@lundsgby.dk	
Lundsgby Renewable Solutions			This Drawing is subject to copyright and may not be reproduced without permission from Lundsgby Renewable Solutions A/S	

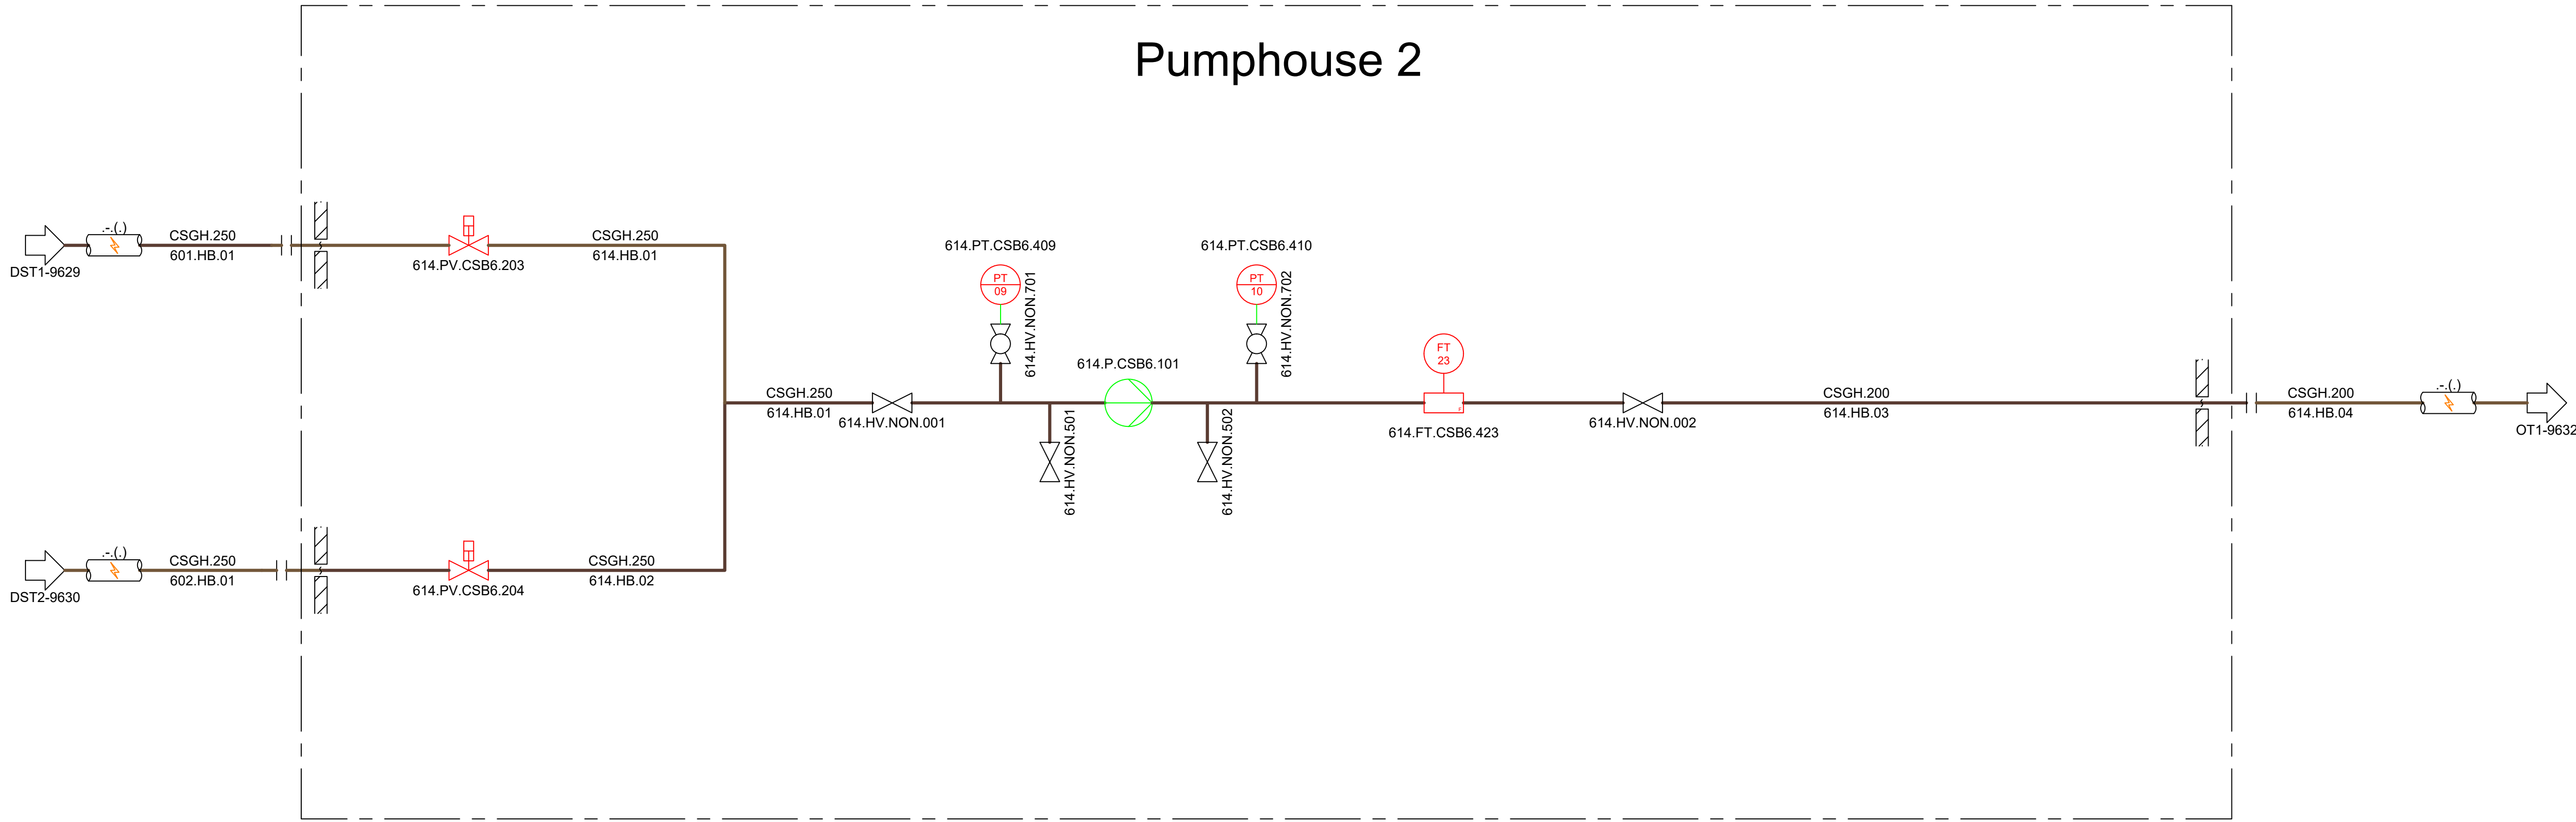

Rev. Nr.:	Rev. Dato:	Rev. Description:	Project nr...1768
Builder:	ST1		Drawing nr...:
Project:	SLK		9631
Subject:	DST pump		
	Rev. 6		
Int.:MDC	QC:CM	APP.:	Date: 15-10-2025
LUNDSBY RENEWABLE SOLUTIONS		Lundsby Renewable Solutions A/S, Hjarbækvej 65, 8831 Løgstrup Tlf.: +45 96 49 43 00 Info@lundsby.dk This Drawing is subject to copyright and may not be reproduced without permission from Lundsby Renewable Solutions A/S	
		FORMAT: A1	

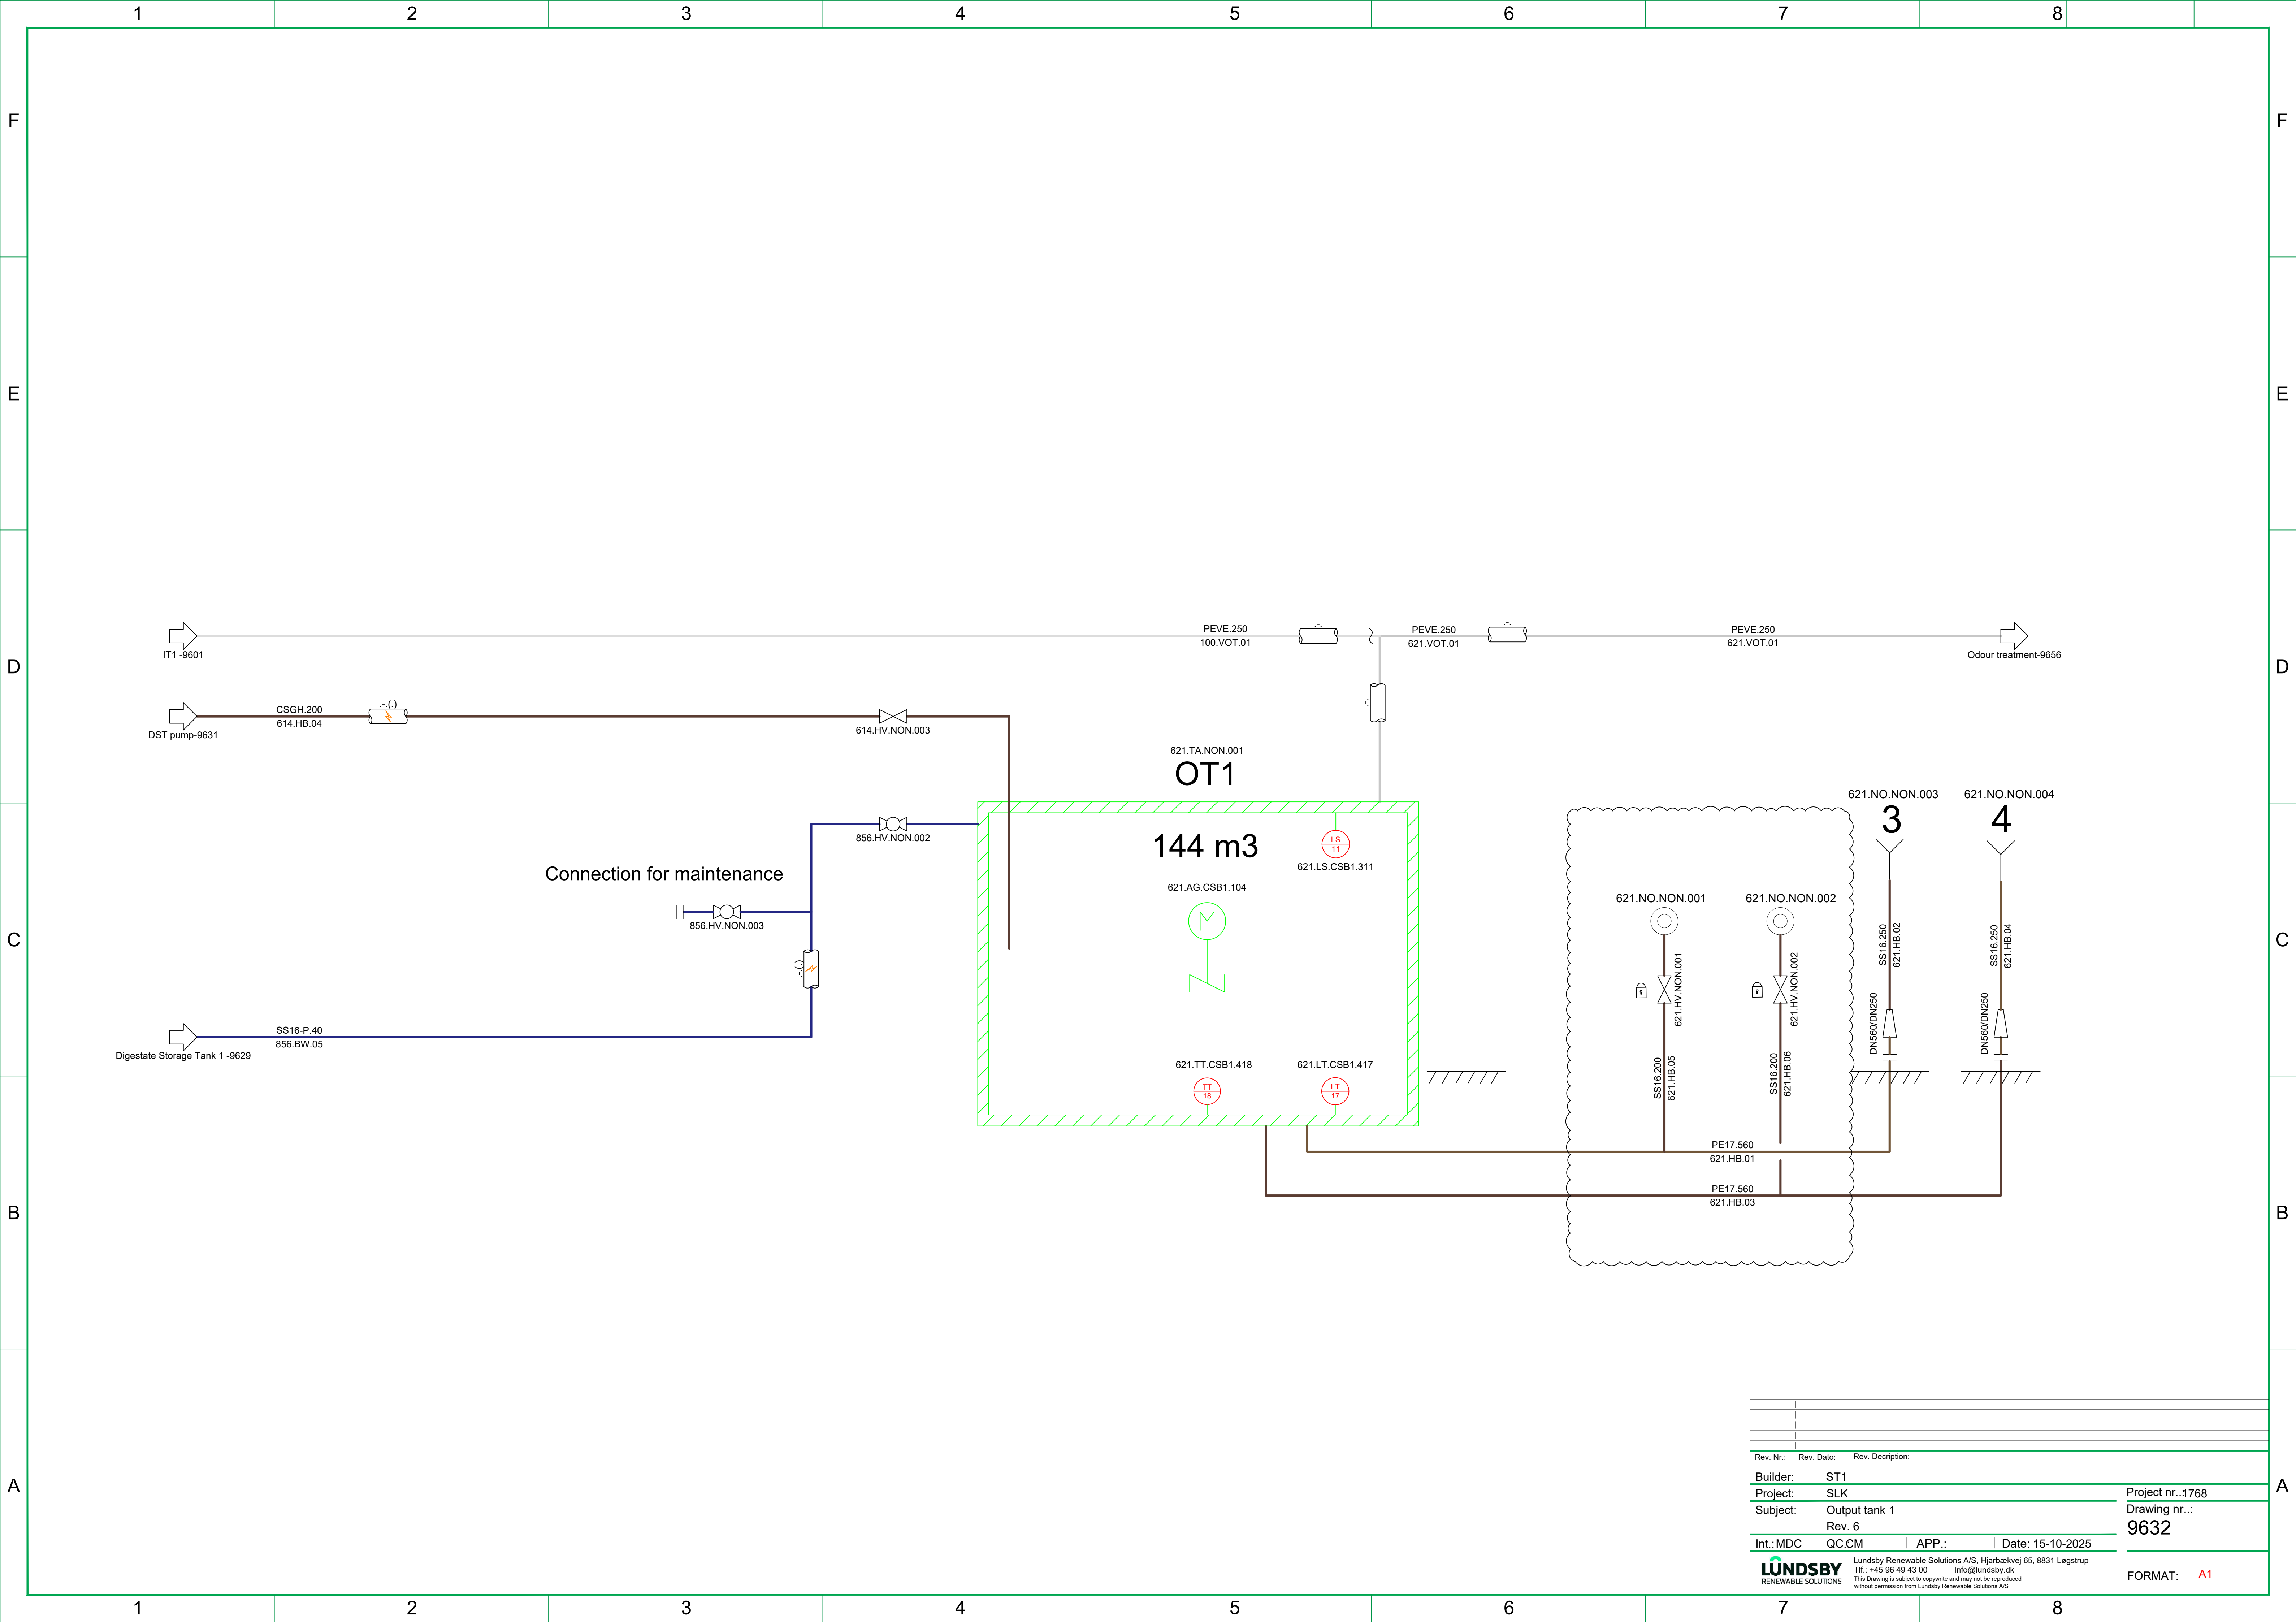

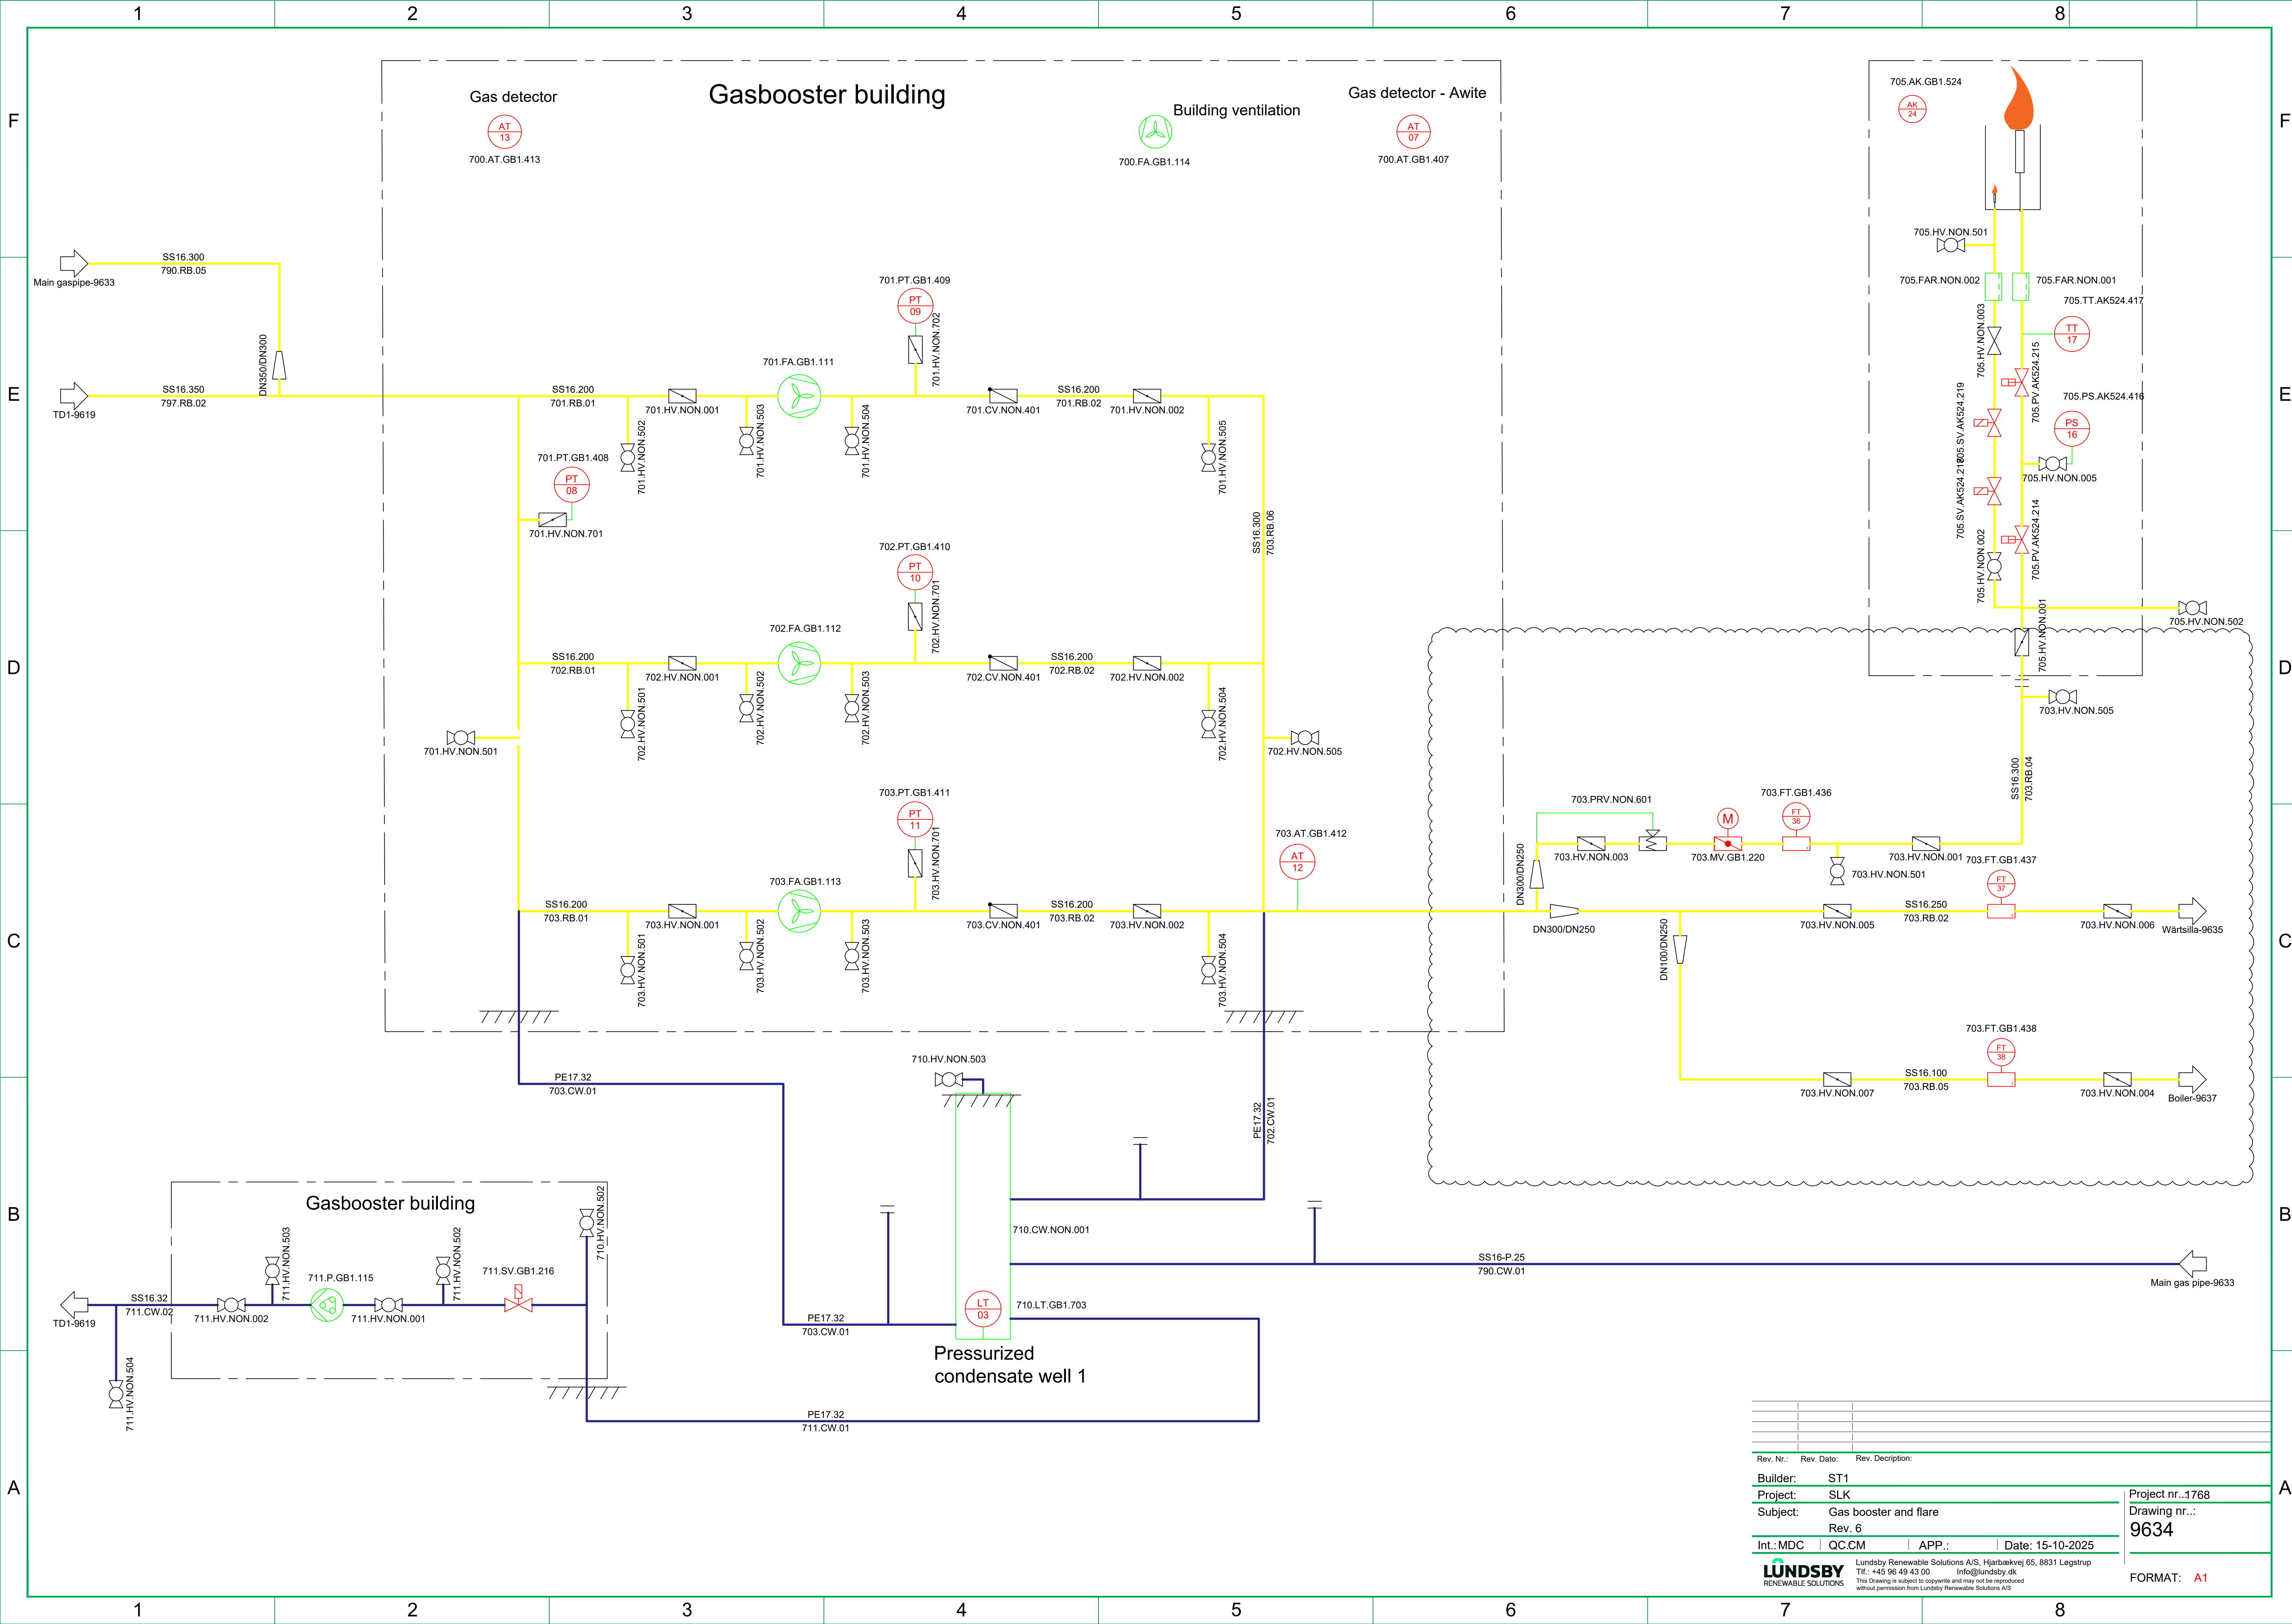

AK
22
730.AK.T4.522

730.AK.T4.522

AK
23

30.AK.T5.5

Product upgraded gas
TP 6601

Product upgraded gas
N1

Nitrogen
N5

Water spray system
inlet

TP 6010

TP 6020

TP 6030

TP 8010

Heat recovery inlet
TP 9002

Low temperature recovery

SS16.70
730.CW.02SS16.70
730.CW.03SS16.70
730.CW.04SS16.65
730.CW.06

Rev. Nr.:	Rev. Dato:	Rev. Description:
-----------	------------	-------------------

Builder: ST1

Project:	SLK
----------	-----

Subject: Upgrade
Rev. 6

Int.:MDC	QC:CM	APP.:	Date: 15-10-2025
----------	-------	-------	------------------

LUNDSBY Lundsby Renewable Solutions A/S, Hjarbækvej 65, 8831 Løgstrup
Tlf : +45 96 49 43 00 Info@lundsby.dk

LONGSDORF
RENEWABLE SOLUTIONS

Lundsby Renewable Solutions A/S, Hjarbækvej 65, 8831 Løgstrup
Tlf.: +45 96 49 43 00 Info@lundsby.dk
This Drawing is subject to copyright and may not be reproduced
without written permission from Lundsby Renewable Solutions A/S.

Project nr.:1768


Drawing nr.:

9635


FORMAT: A1

Technology
building

Heat pump scope

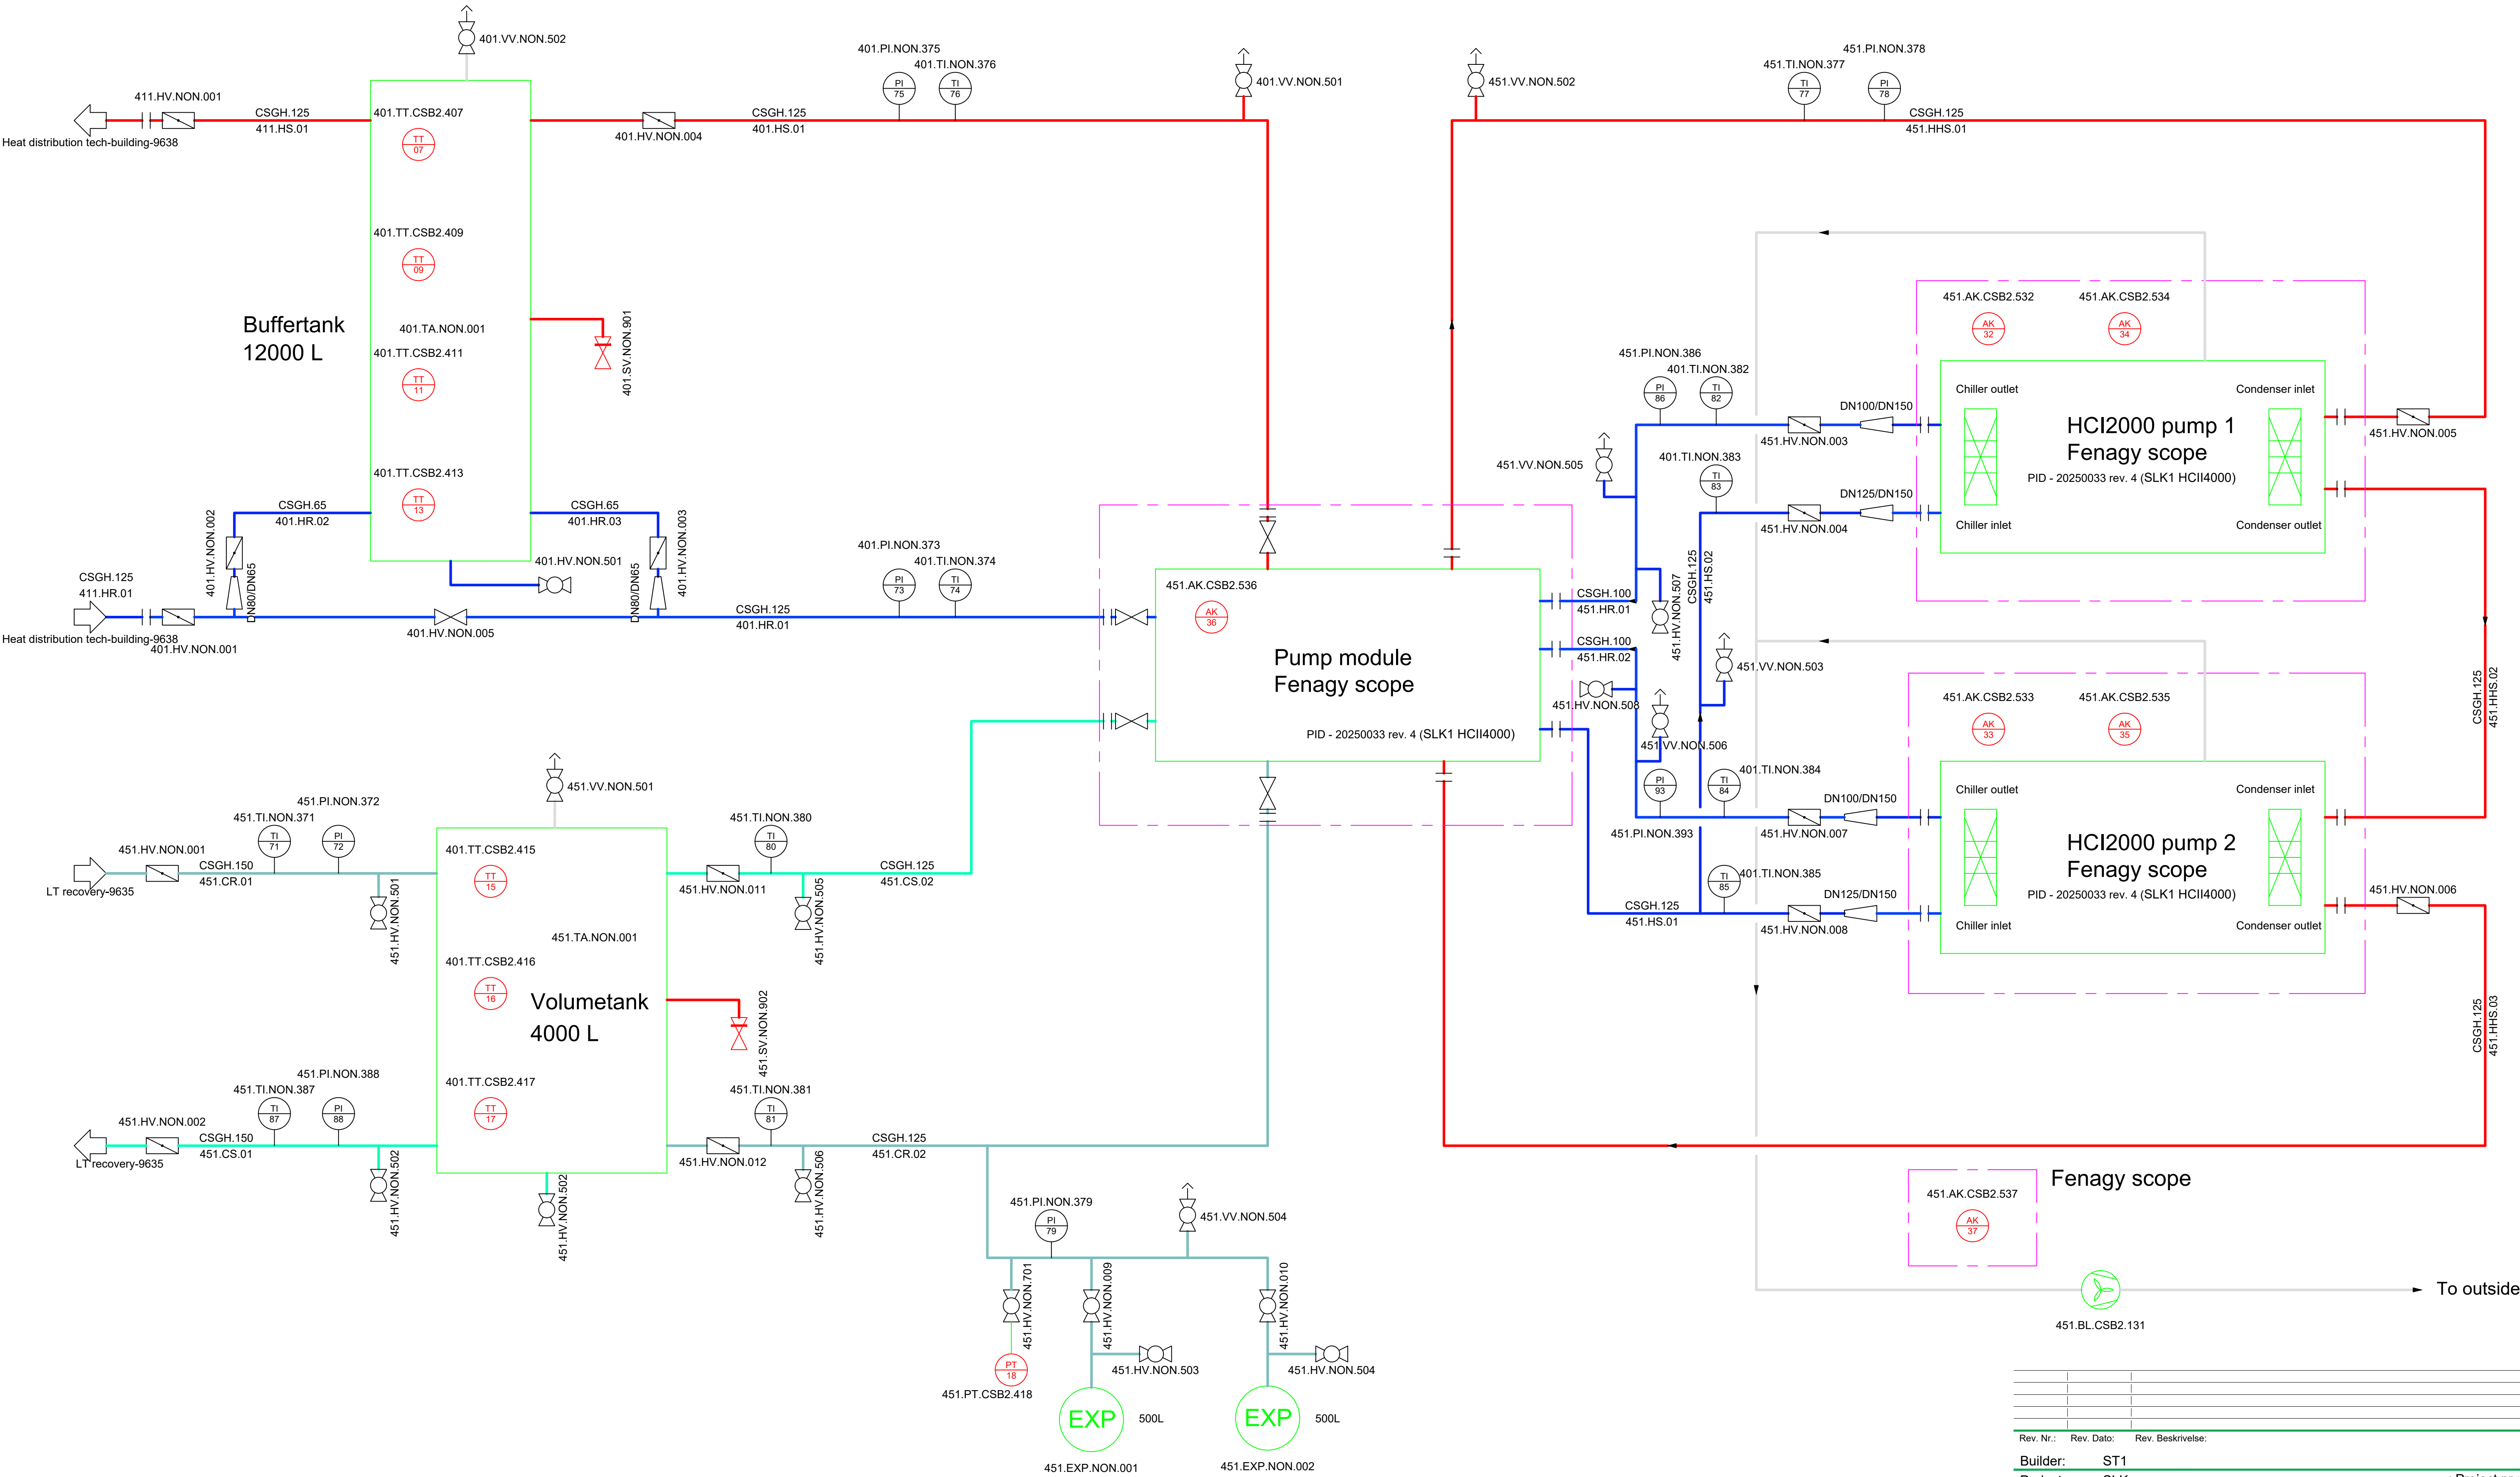

Rev. Nr.:	Rev. Dato:	Rev. Beskrivelse:	
Builder:	ST1		
Project:	SLK		
Subject:	Heat pumps		
Rev.:	6		
Int.:MDC	QC:CM	APP.:	Date: 15-10-2025
LUNDSBY RENEWABLE SOLUTIONS			Lundsby Biogas A/S, Hjarbækvej 65, 8831 Løgstrup Tlf.: +45 96 49 43 00 info@lundsbybiogas.dk Denne tegning er underlagt copyright og må ikke reproduceres uden tilladelse fra Lundsbybiogas A/S
Project nr.:1768 Drawing nr.: 9636			FORMAT: A1

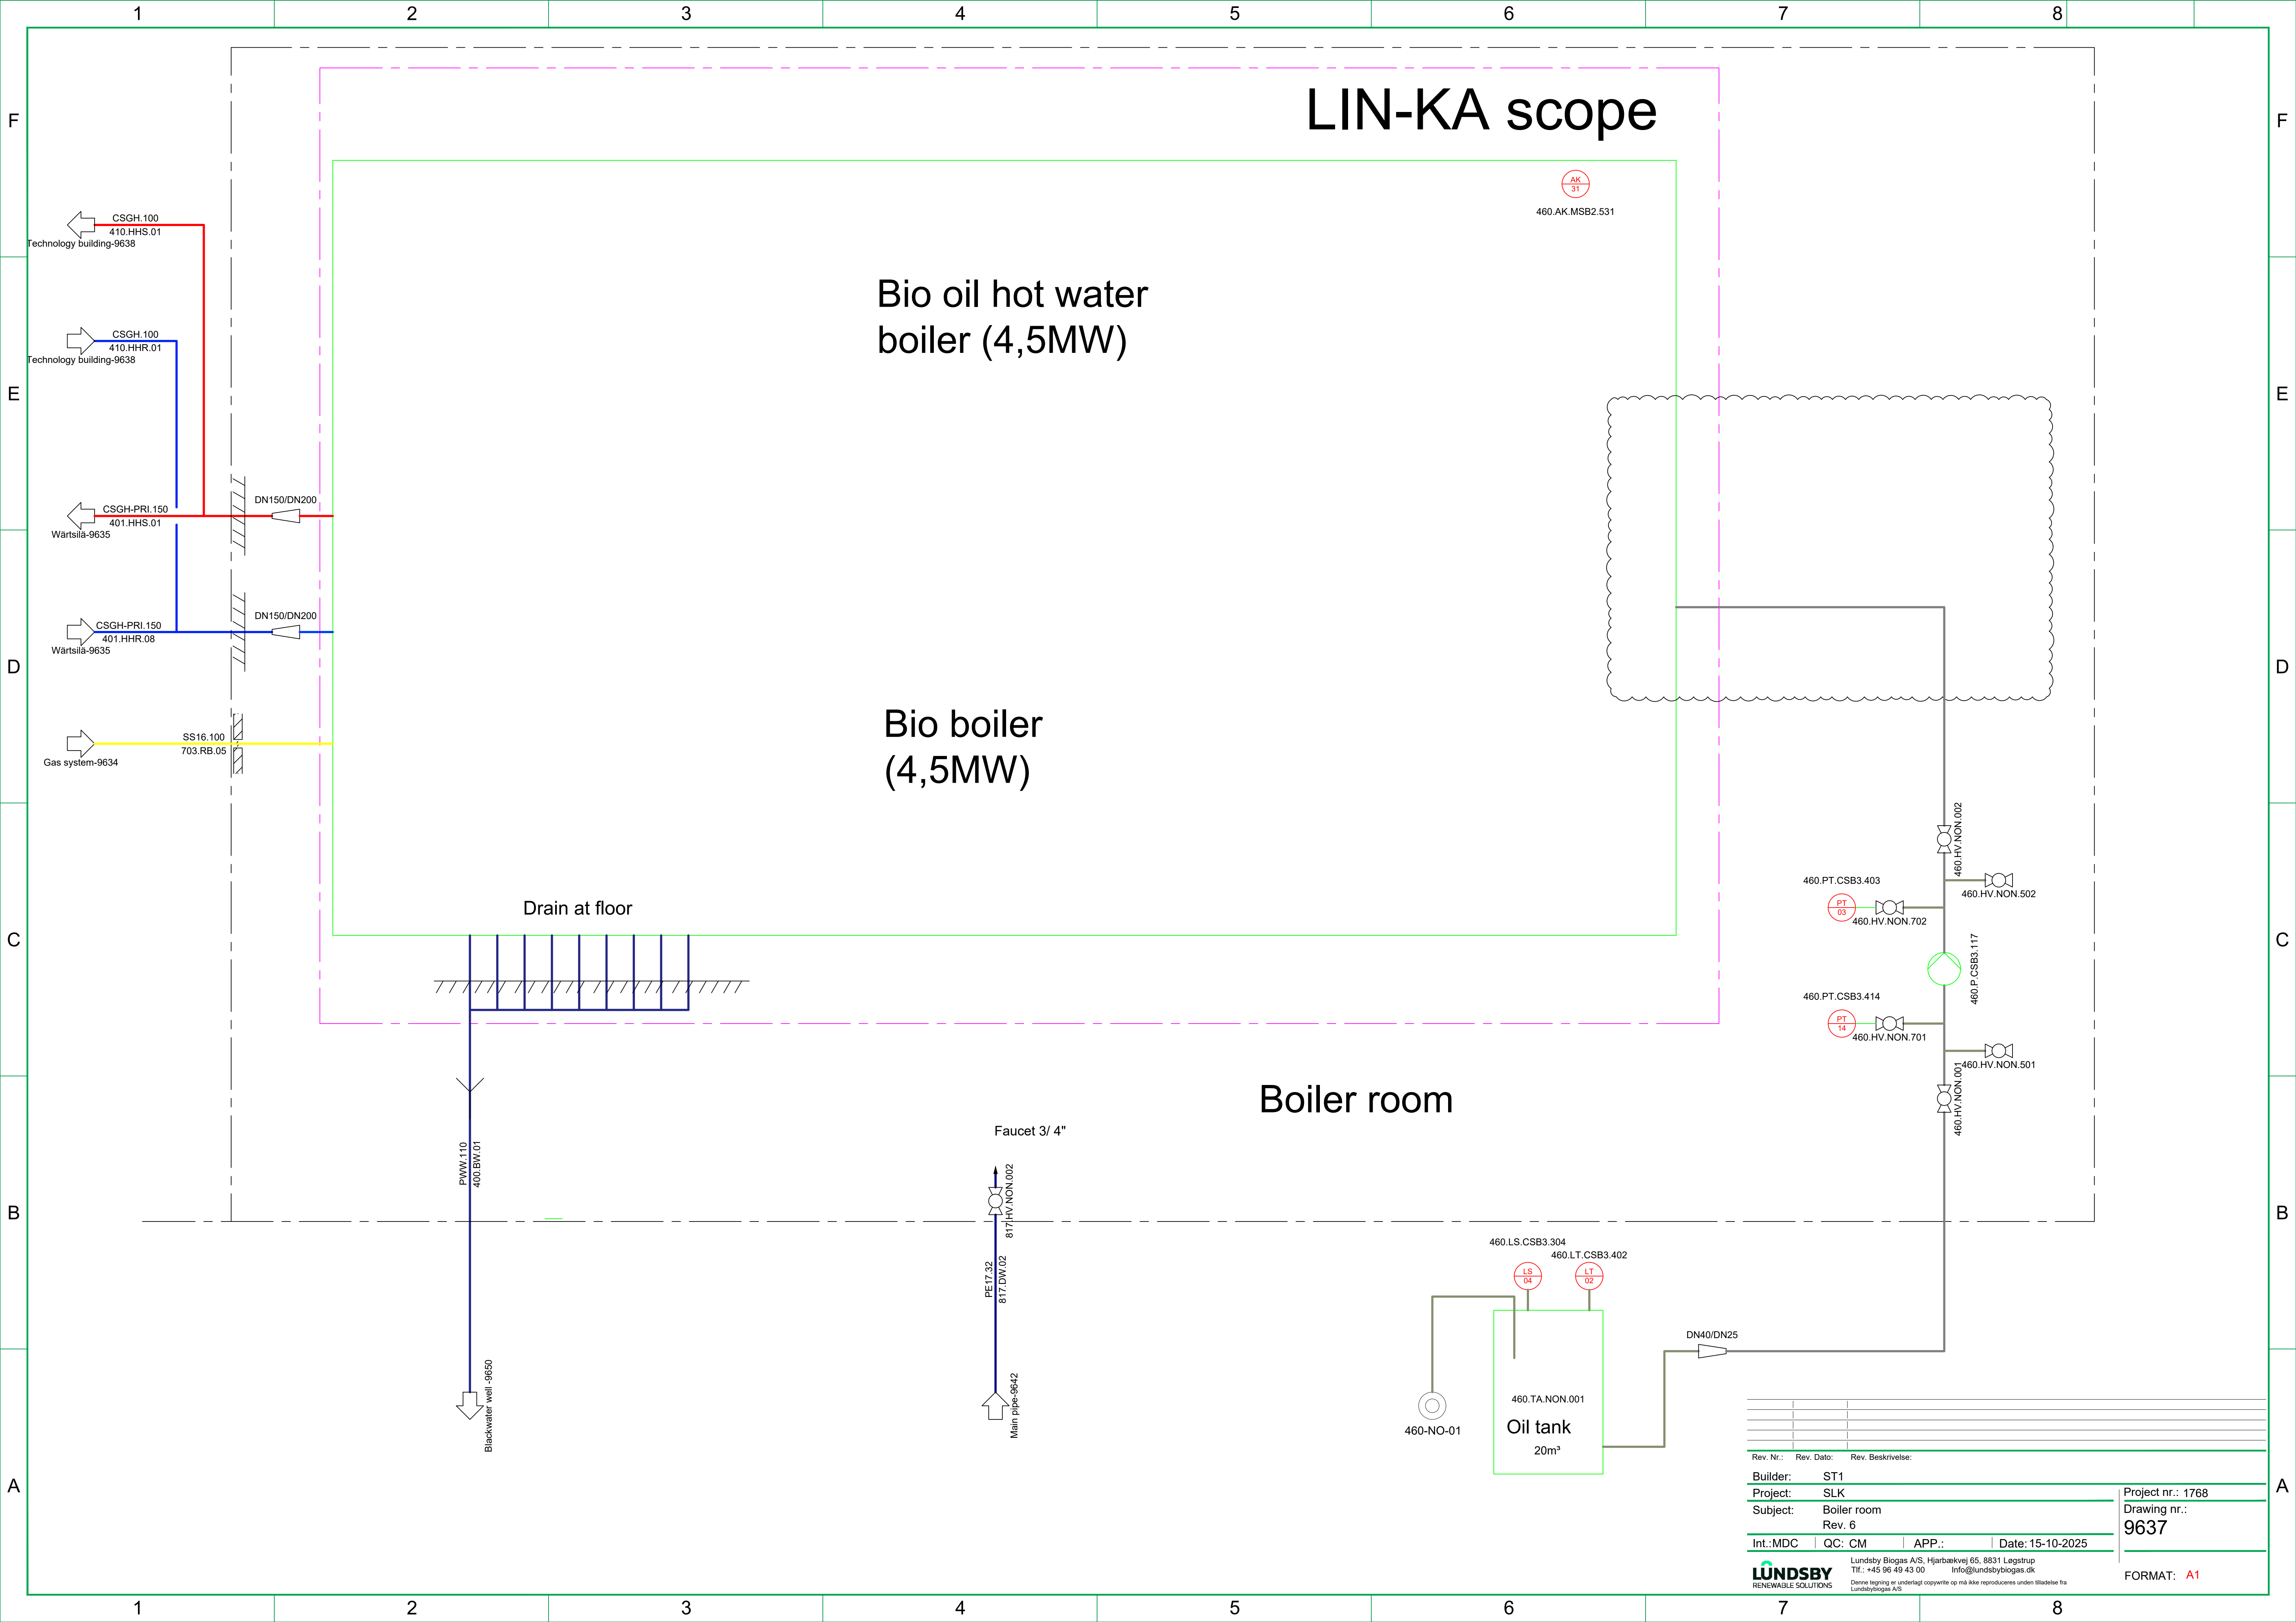

LIN-KA scope

Bio oil hot water boiler (4,5MW)

Bio boiler (4,5MW)

Boiler room

AK 31
460.AK.MSB2.531


Drain at floor

Faucet 3/ 4"


460.LS.CSB3.304
460.LT.CSB3.402

460.TA.NON.001
Oil tank
20m³

Rev. Nr.:	Rev. Dato:	Rev. Beskrivelse:	
Builder:	ST1		
Project:	SLK		
Subject:	Boiler room		
Rev. 6			
Int.:MDC	QC: CM	APP.:	Date: 15-10-2025
LUNDSBY RENEWABLE SOLUTIONS			Lundsby Biogas A/S, Hjarbækvej 65, 8831 Løgstrup Tlf.: +45 96 49 43 00 Info@lundsbybiogas.dk Denne tegning er underlagt copywrite op på ikke reproduceres uden tilladelse fra Lundsbybiogas A/S
			Project nr.: 1768 Drawing nr.: 9637 FORMAT: A1

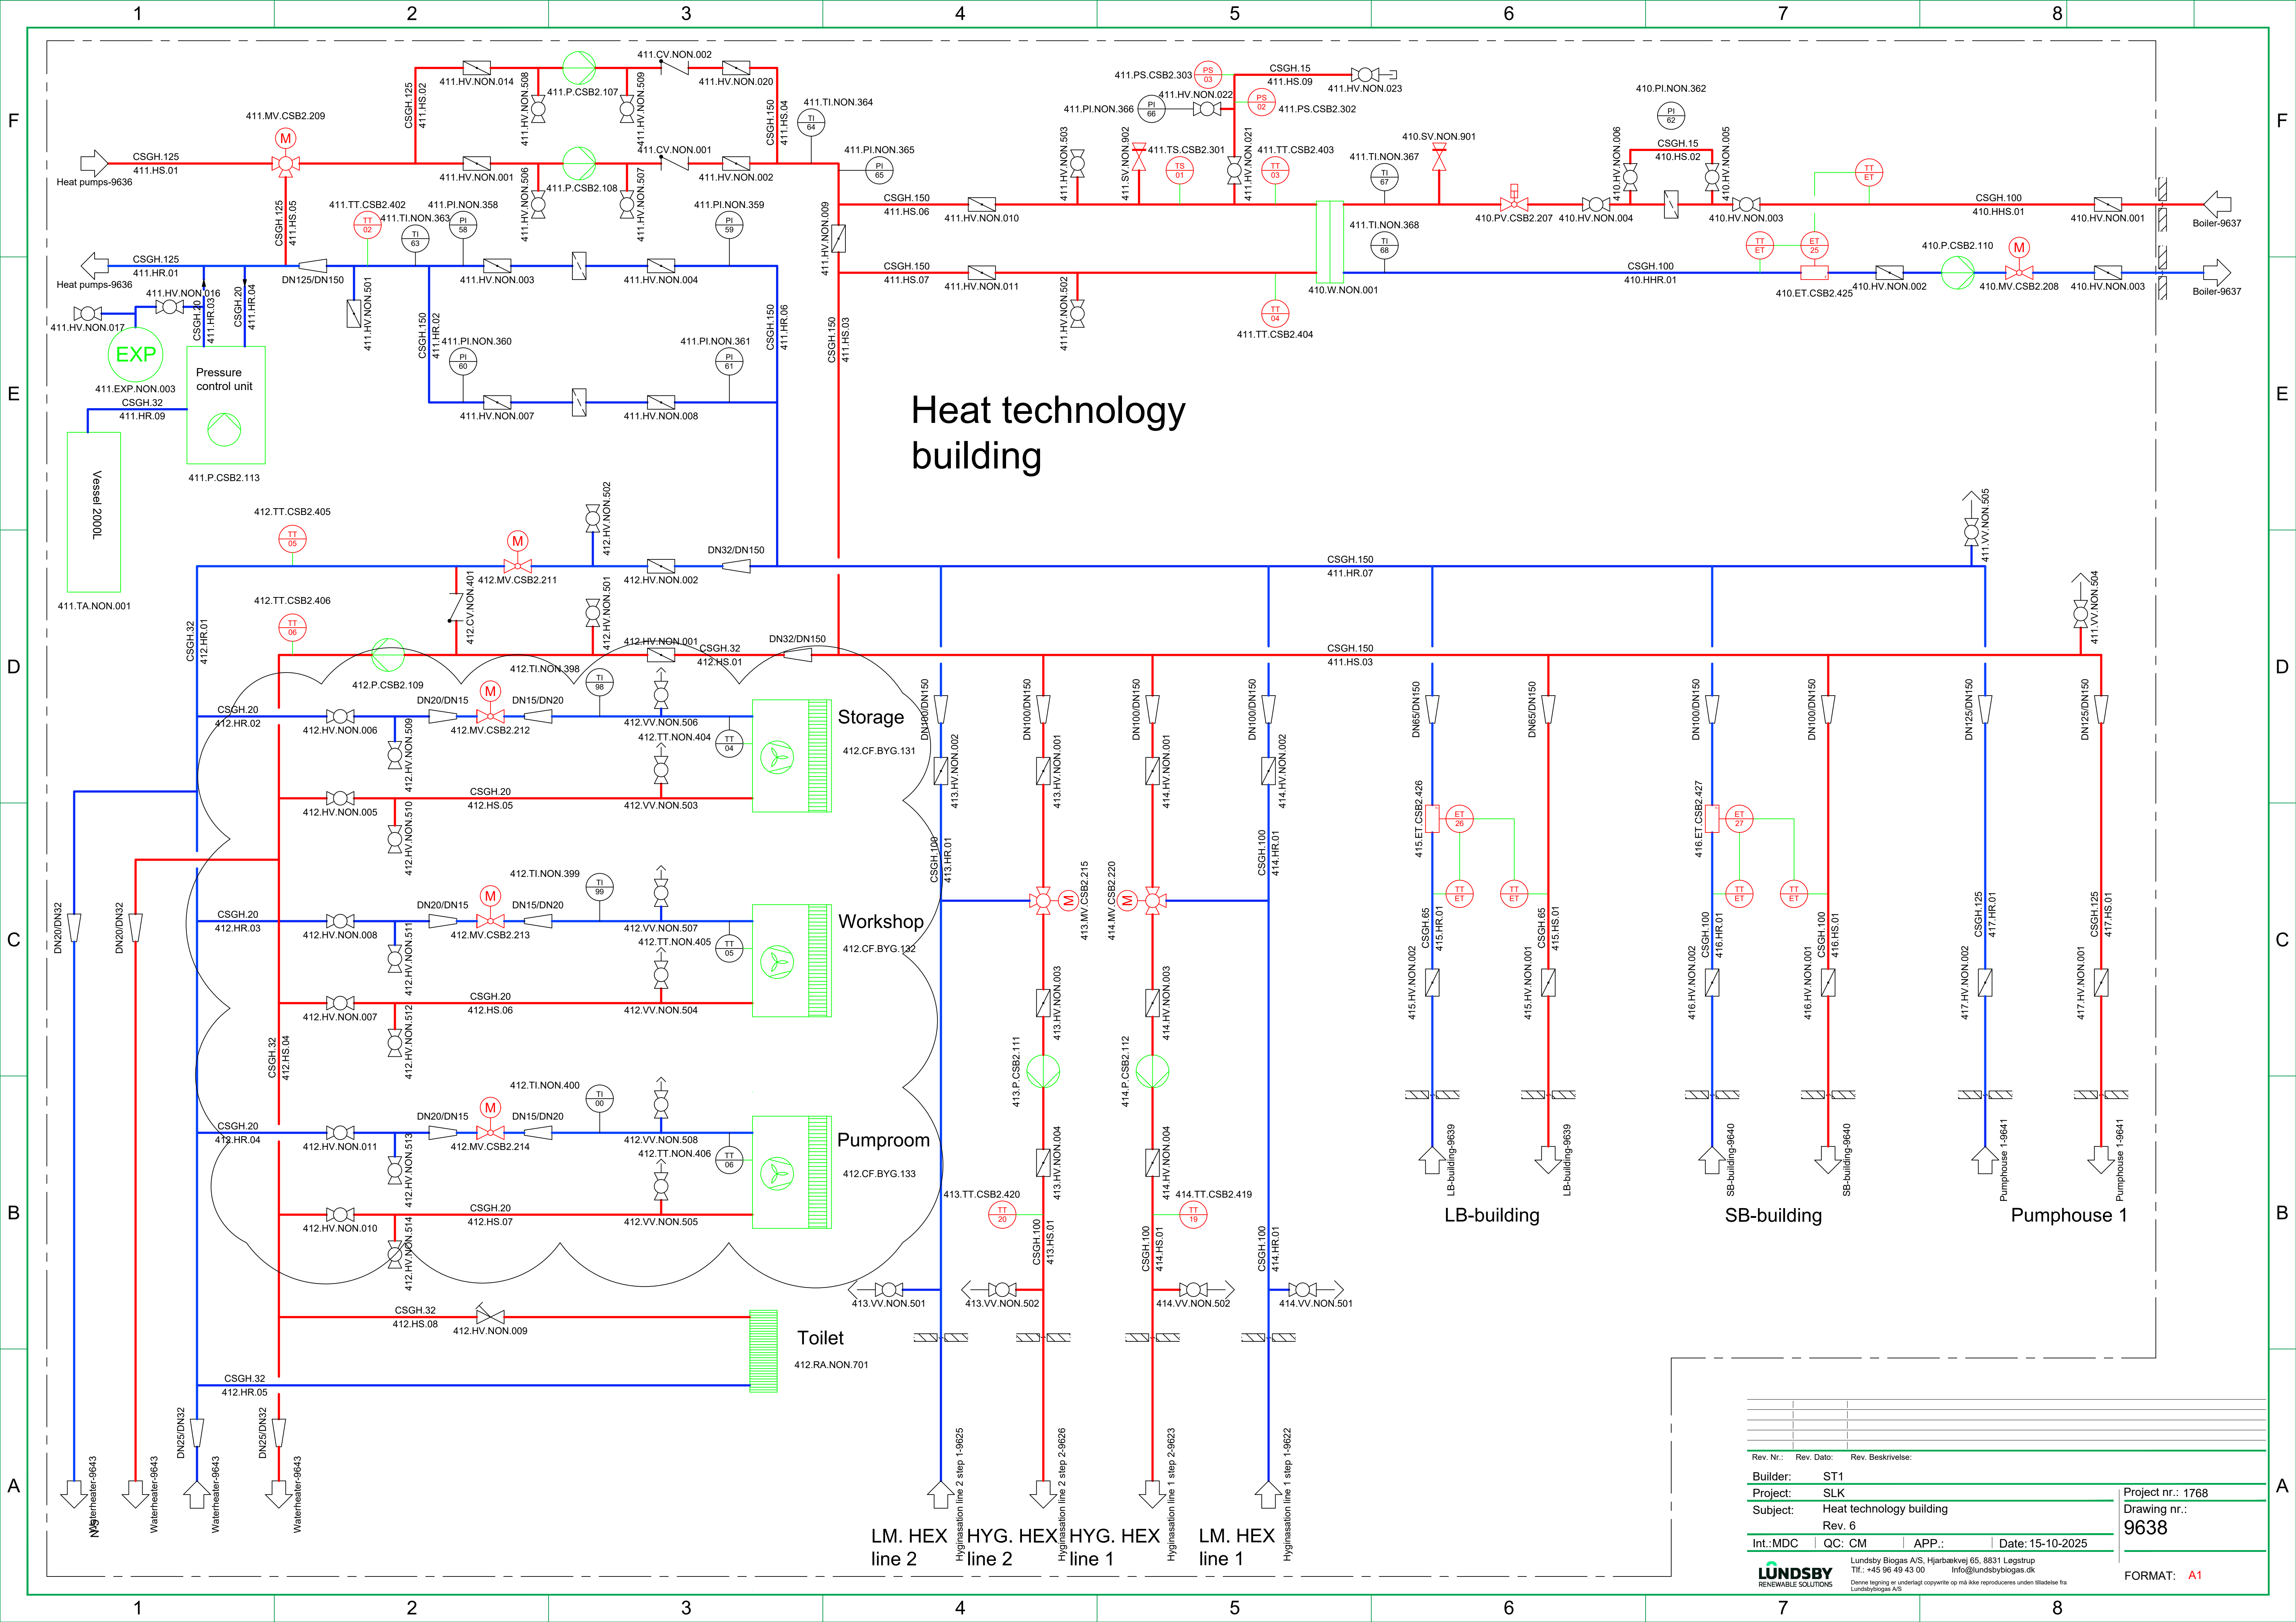

LB-Building

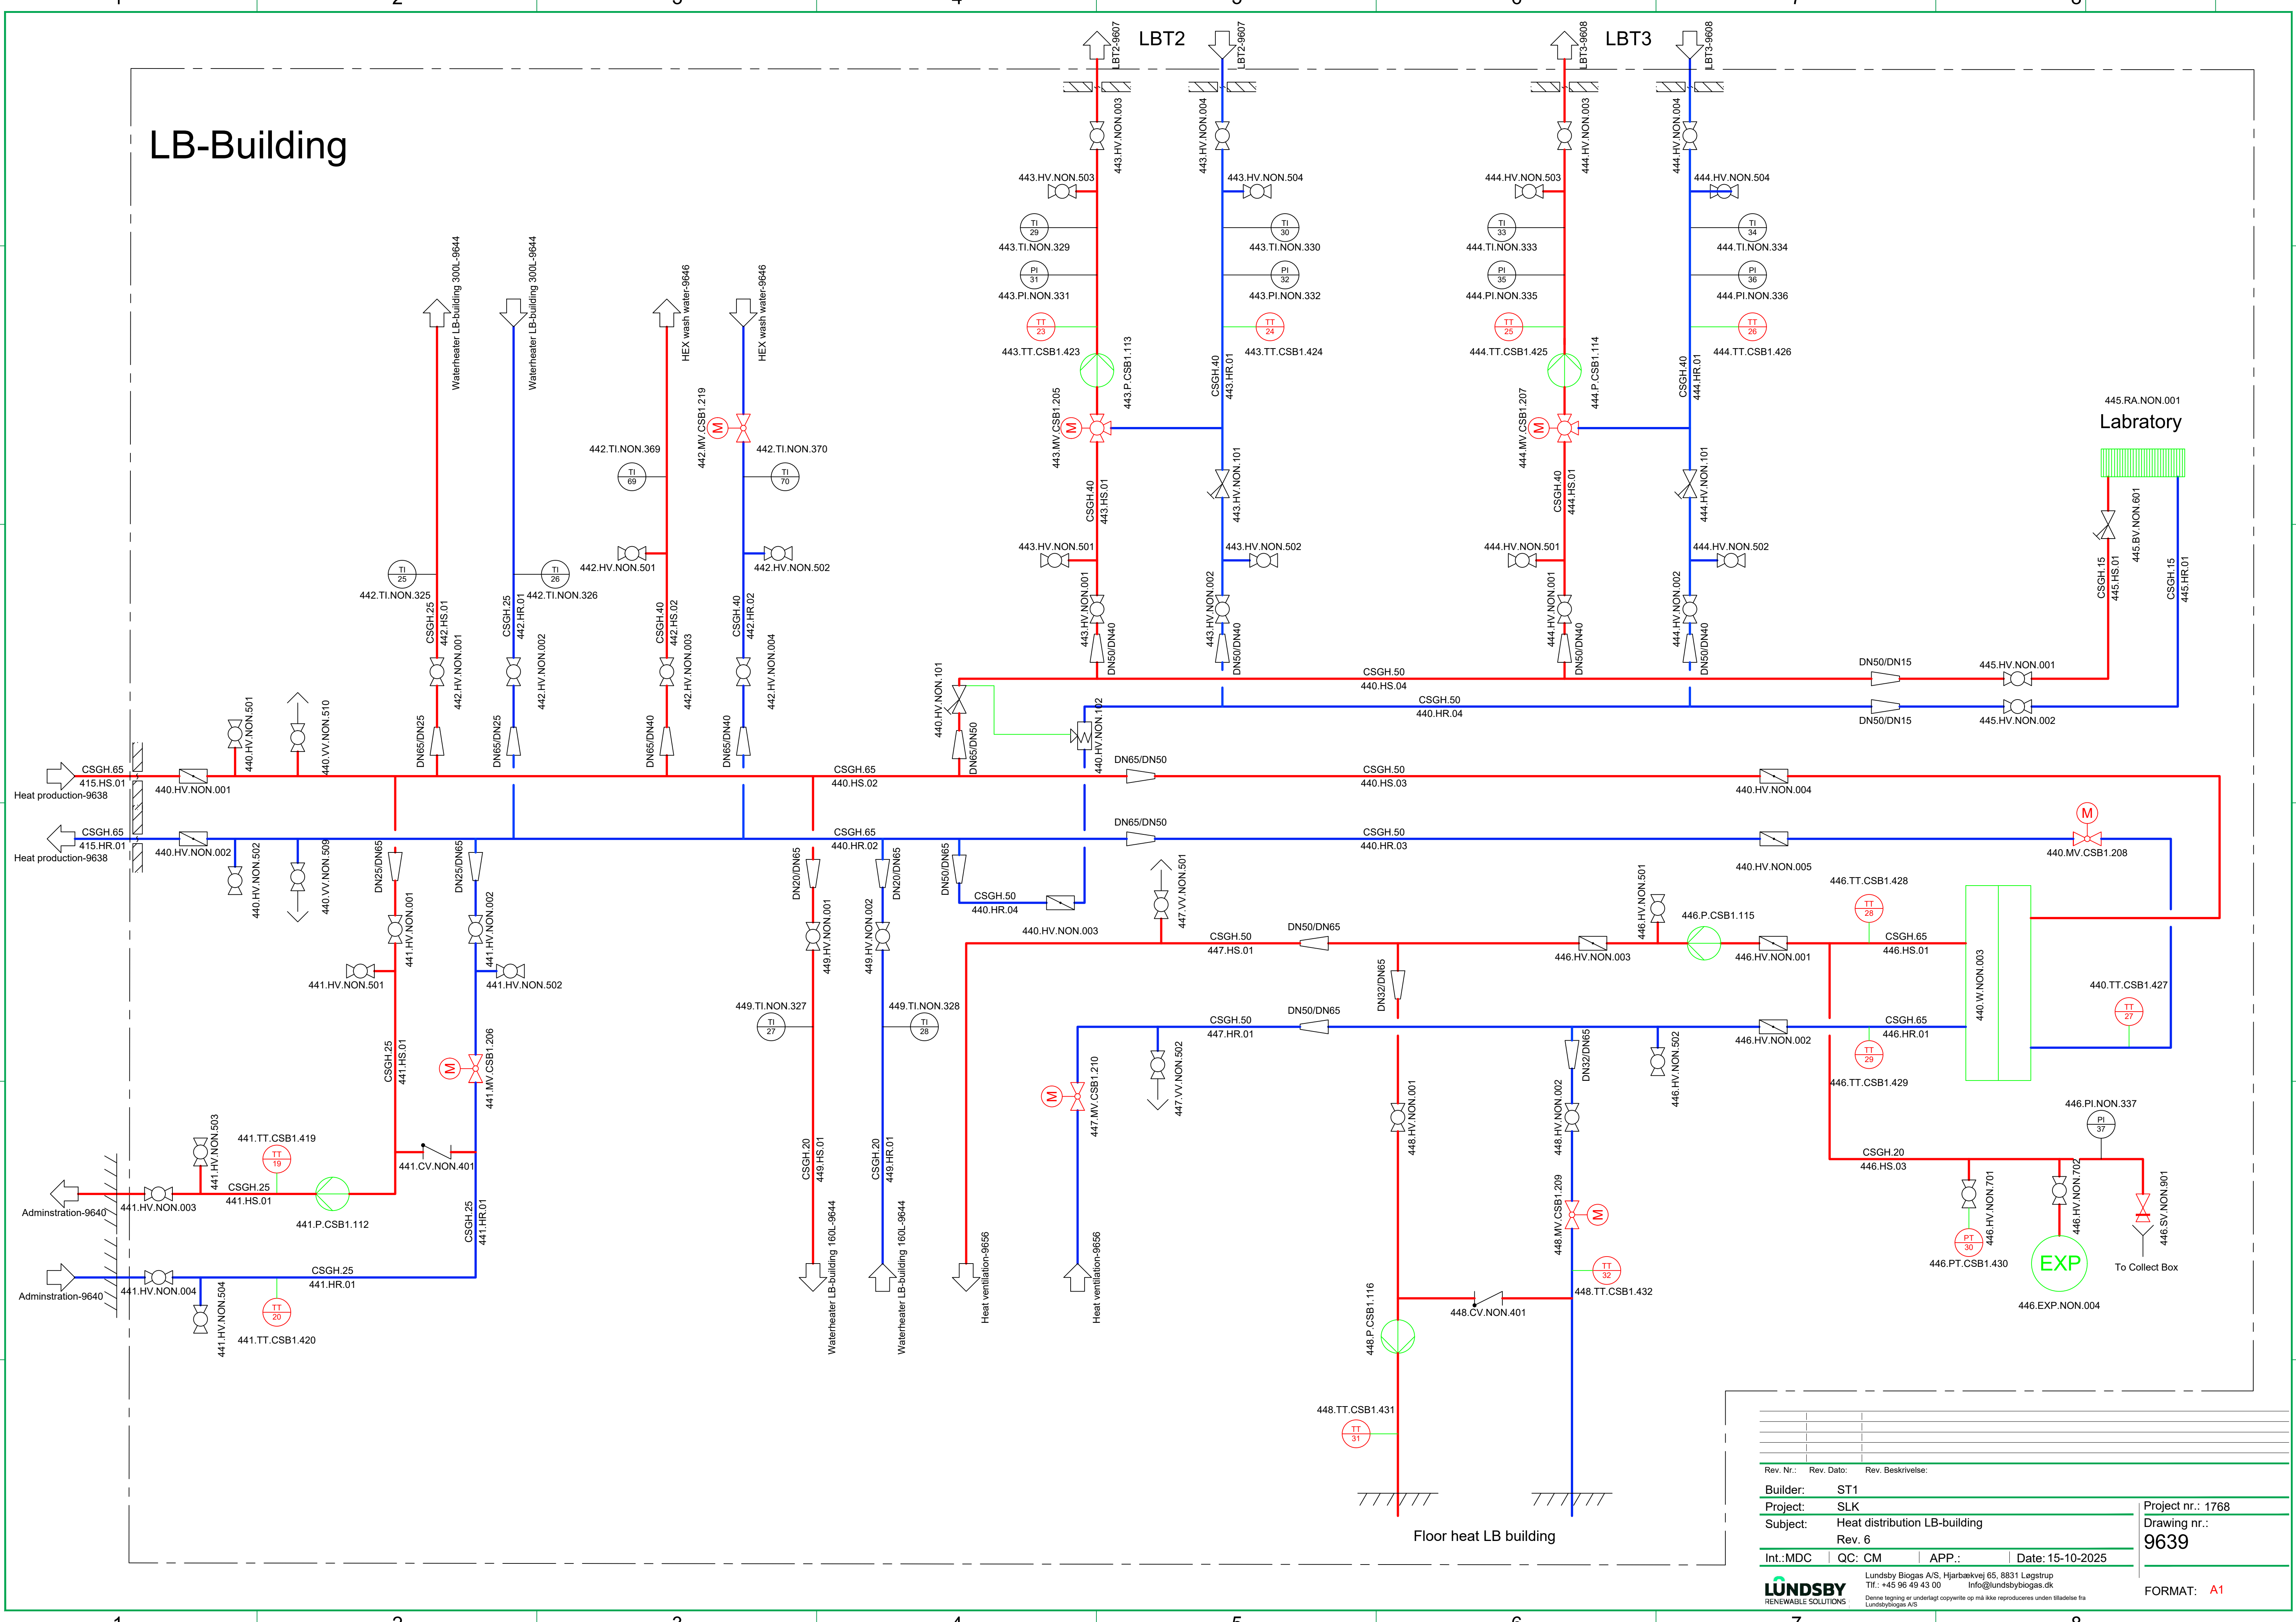

Rev. Nr.:	Rev. Dato:	Rev. Beskrivelse:


Builder:	ST1		
Project:	SLK		
Subject:	Heat distribution LB-building		
Rev. 6			
Int.:MDC	QC: CM	APP.:	Date: 15-10-2025

LUNDSBY
RENEWABLE SOLUTIONS


Lundsby Biogas A/S, Hjarbækvej 65, 8831 Løgstrup
Tlf.: +45 96 49 43 00
info@lundsbybiogas.dk
Denne tegning er underlagt copyright og må ikke reproduceres uden tilladelse fra Lundsbybiogas A/S

Project nr.: 1768
Drawing nr.:
9639
FORMAT: **A1**

SB-Building

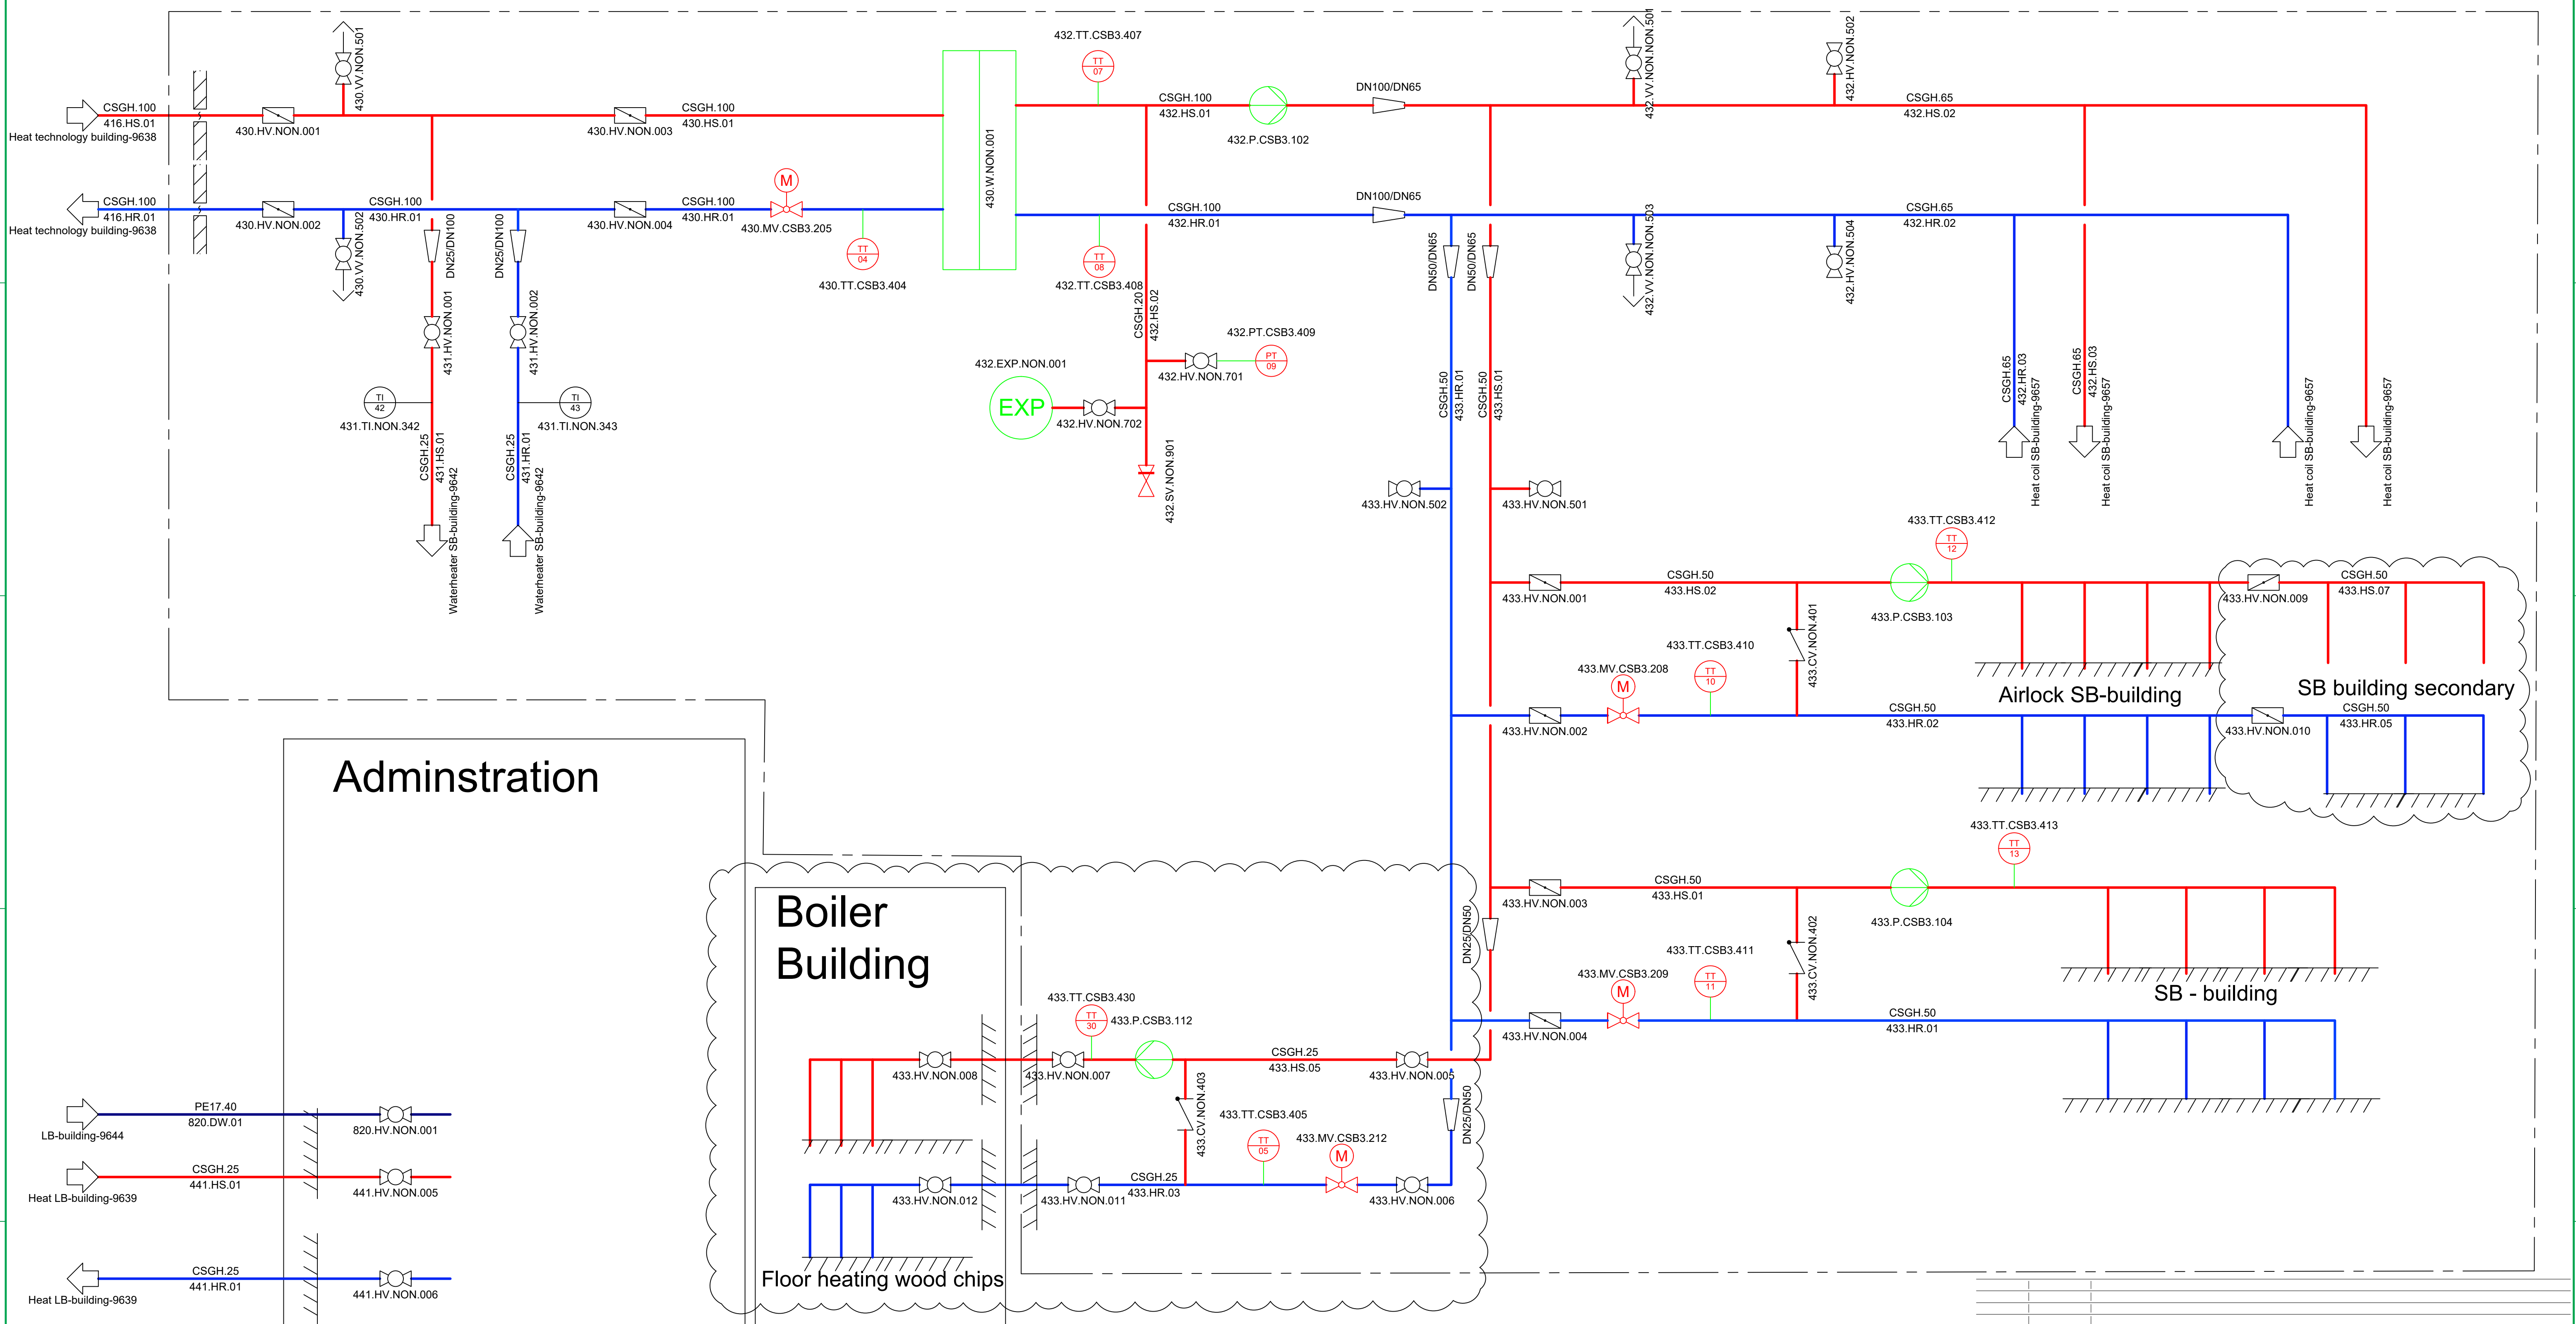


Rev. Nr.:	Rev. Dato:	Rev. Beskrivelse:	
Builder:	ST1		
Project:	SLK		
Subject:	Heat distribution SB-building		
	Rev. 6		
Int.:MDC	QC: CM	APP.:	Date: 15-10-2025
 Lundsby Biogas A/S, Hjarbækvej 65, 8831 Legstrup Tlf.: +45 96 49 43 00 Info@lundsbybiogas.dk Denne tegning er udelagt copyretet og må ikke reproduceres uden tilladelse fra Lundsby Biogas A/S			Project nr.: 1768 Drawing nr.: 9640 FORMAT: A1

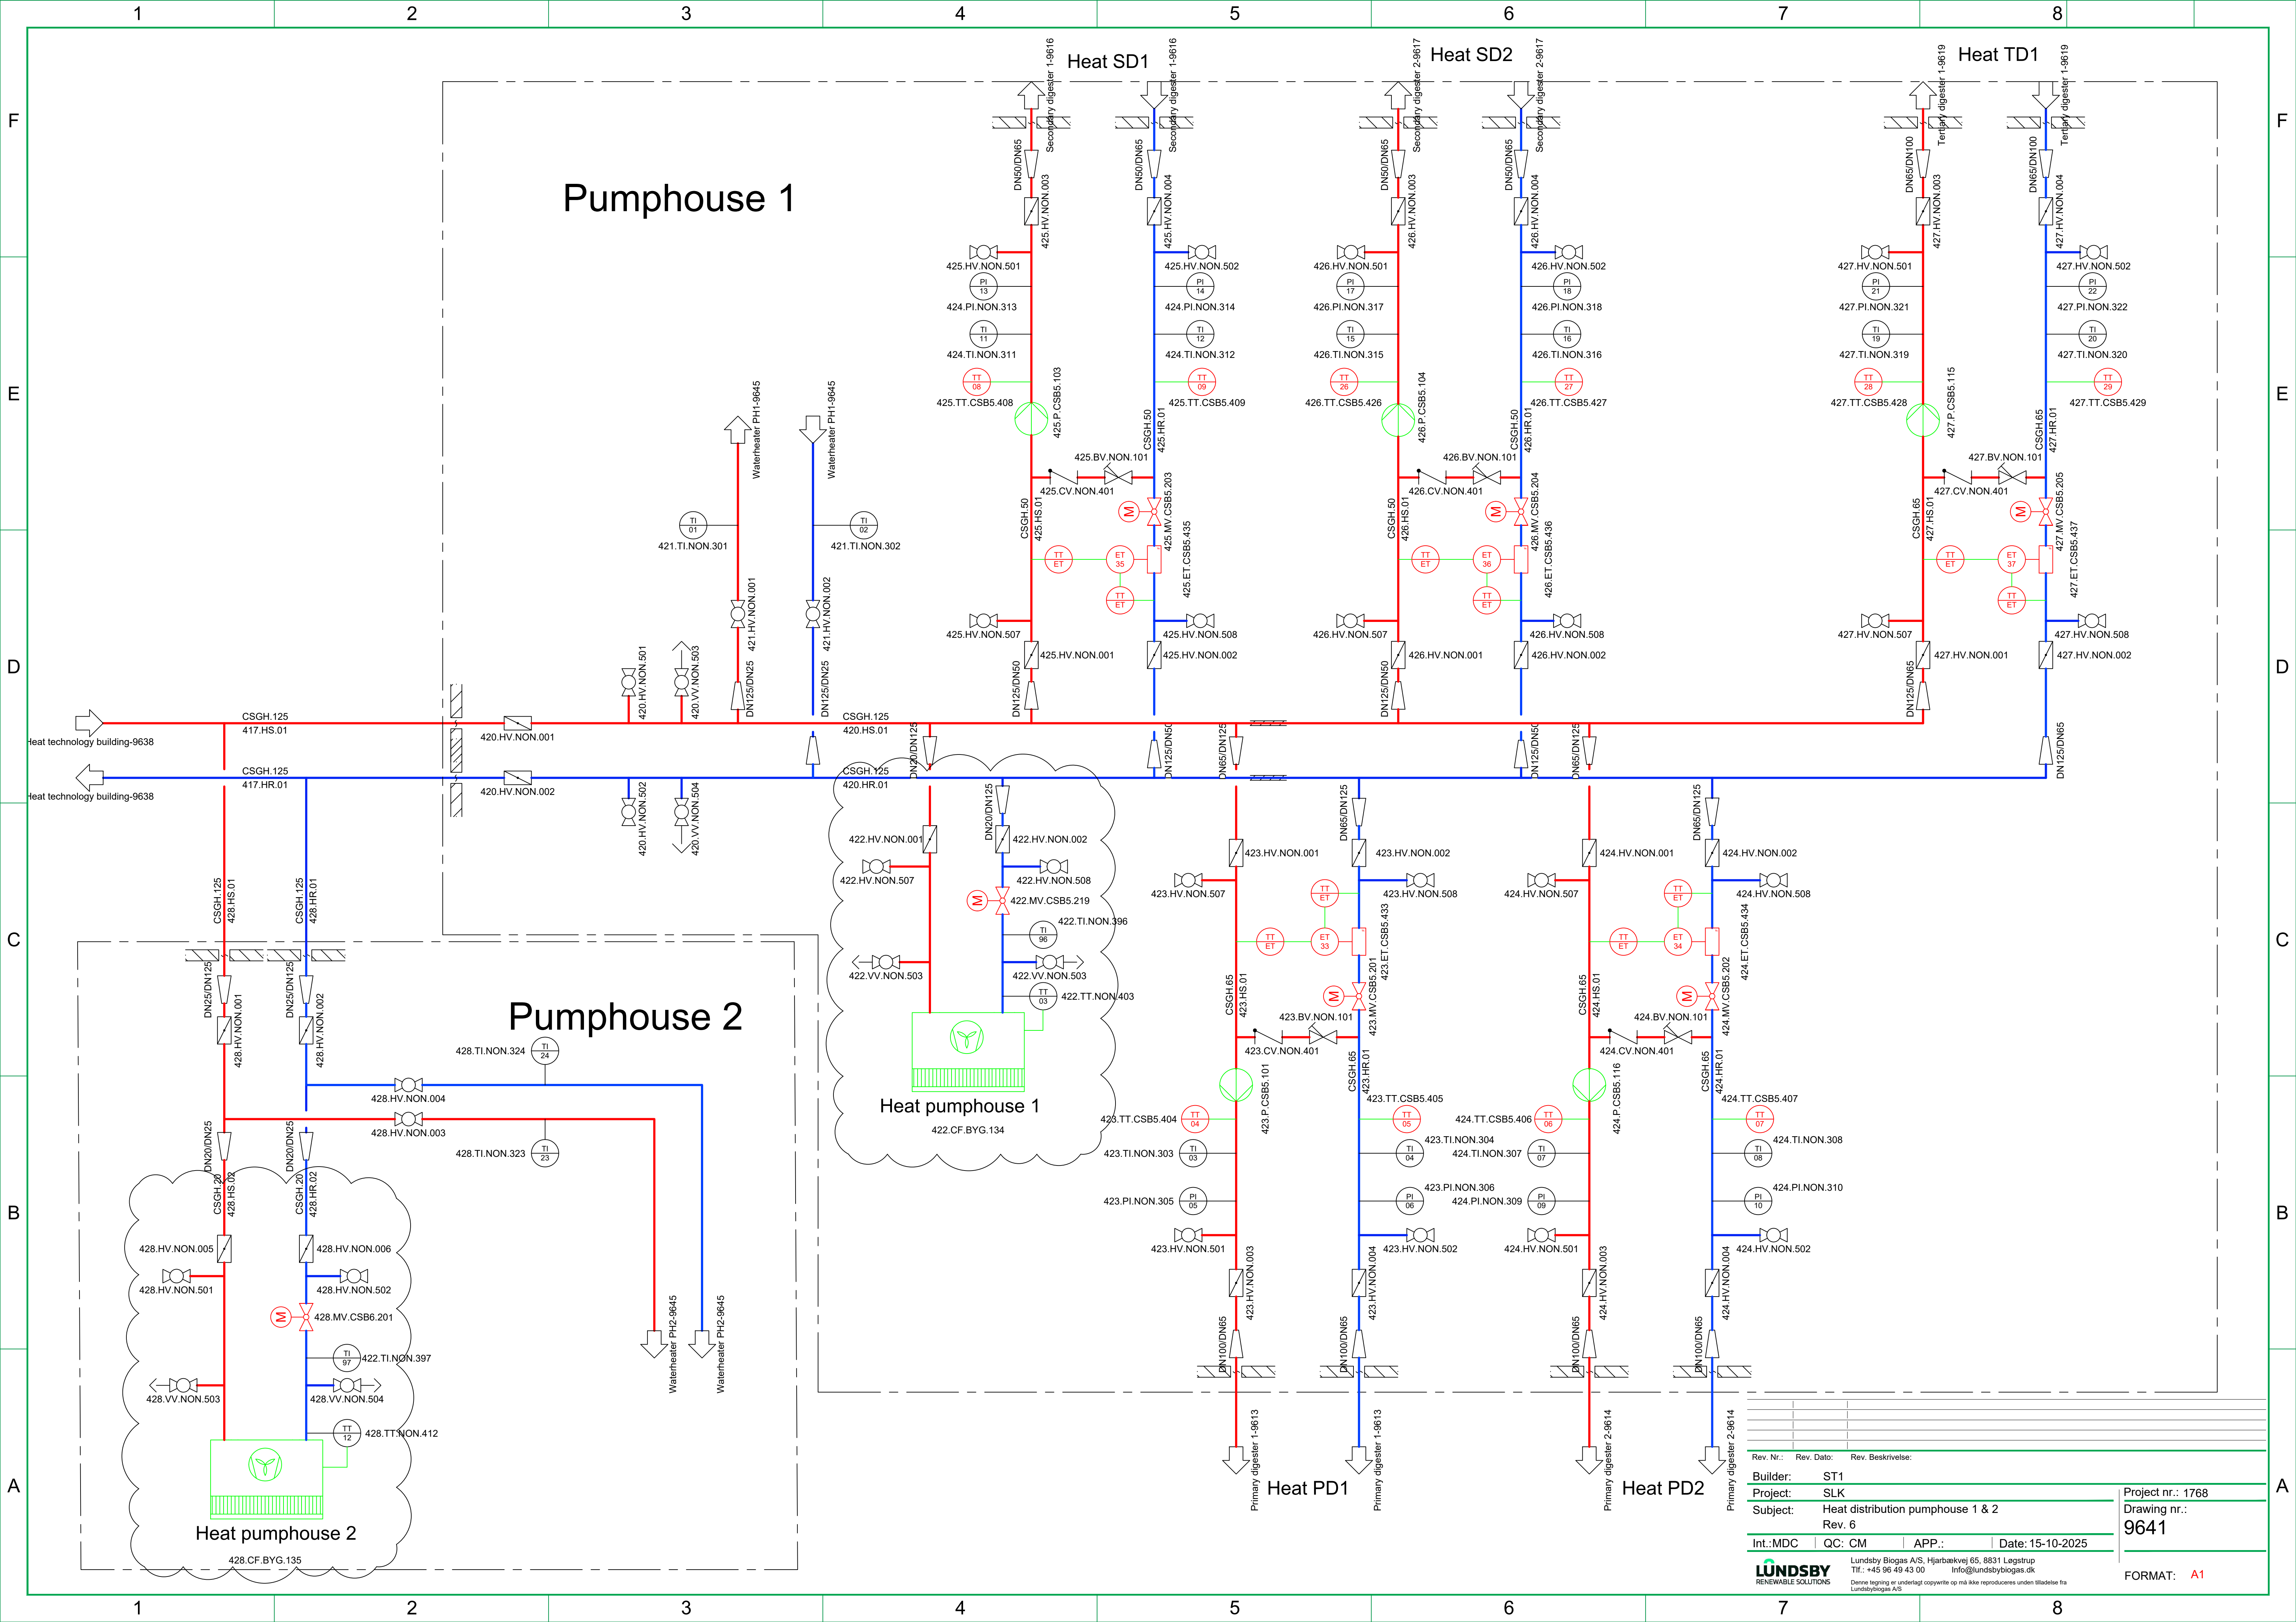


Rev. Nr.:	Rev. Dato:	Rev. Beskrivelse:
Builder:	ST1	
Project:	SLK	
Subject:	Heat distribution pumphouse 1 & 2	
Int.:MDC	QC: CM	APP.: Date: 15-10-2025
Rev. 6		
Project nr.: 1768		
Drawing nr.: 9641		
FORMAT: A1		
LUNDSBY RENEWABLE SOLUTIONS		
Lundsby Biogas A/S, Hjarbækvej 65, 8831 Løgstrup		
Tlf.: +45 96 49 43 00		
Info@lundsbybiogas.dk		
Denne tegning er underlagt copyright op på ikke reproduceres uden tilladelse fra Lundsbybiogas A/S		

SB-Building

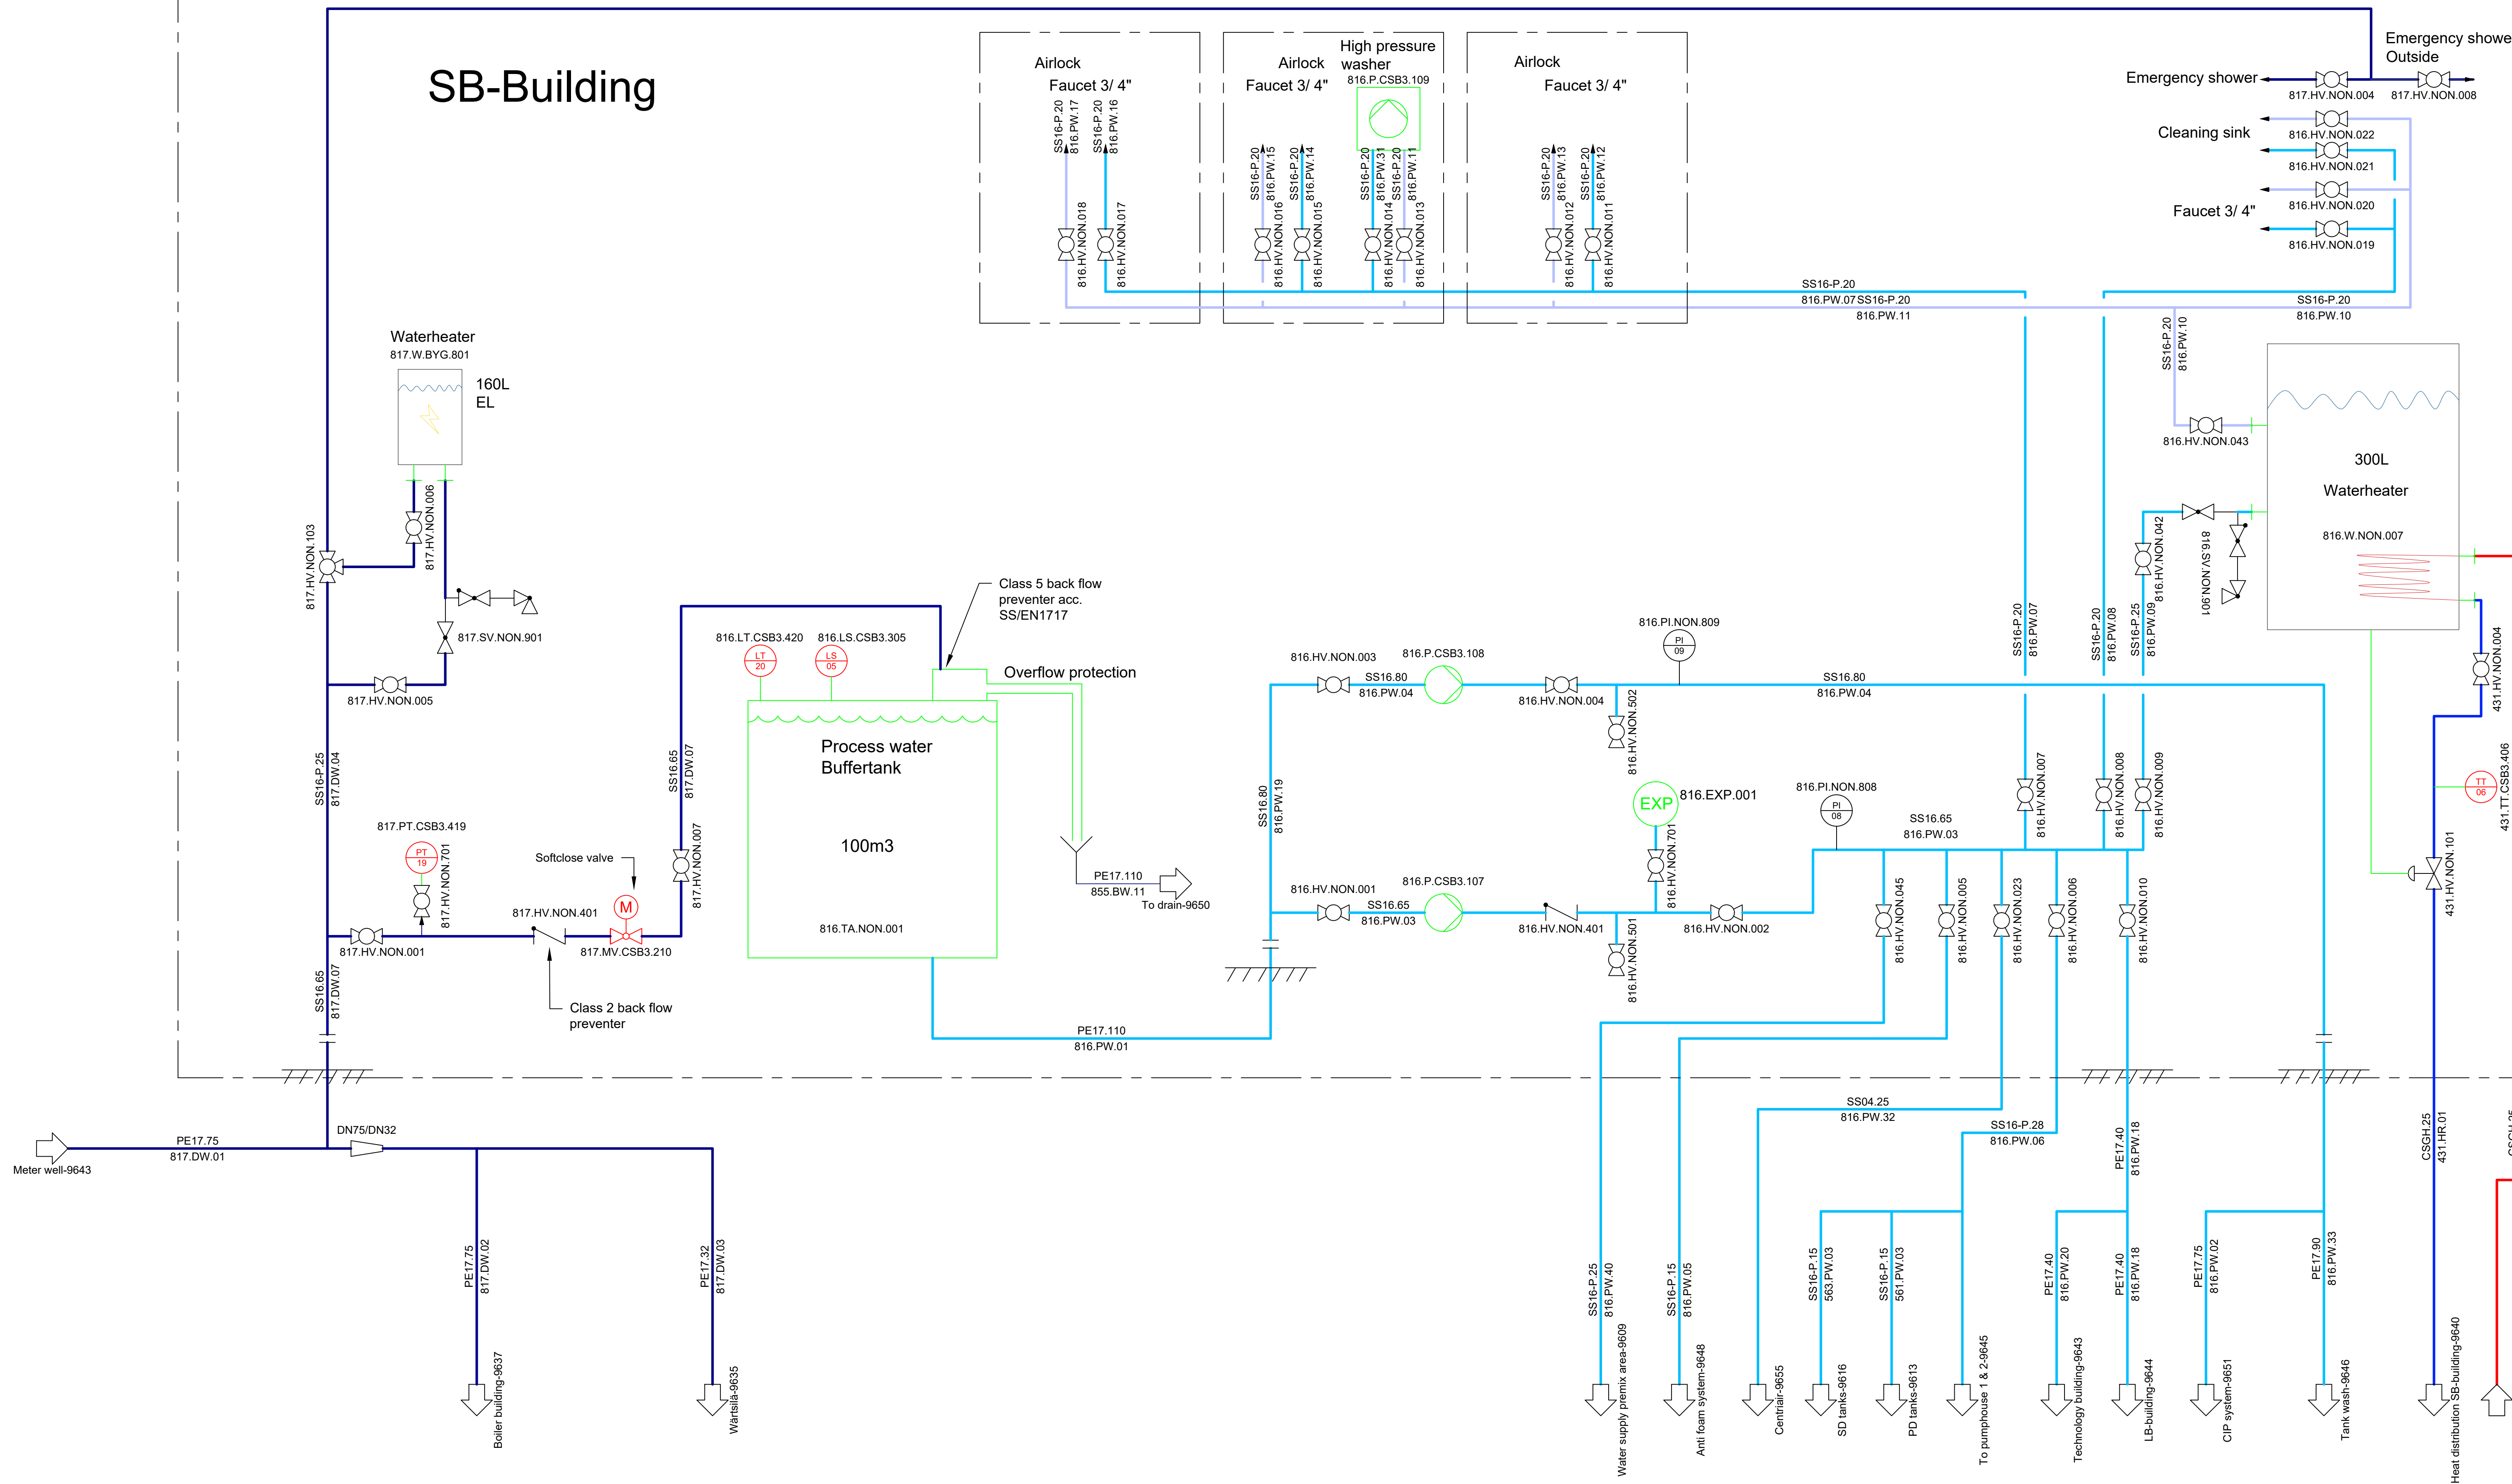


Rev. Nr.:	Rev. Dato:	Rev. Beskrivelse:
Builder:	ST1	
Project:	SLK	
Subject:	Water distribution SB-building	
Rev. 6		
Int.:MDC	QC:CM	APP.:Date: 15-10-2025
LUNDSBY RENEWABLE SOLUTIONS		
Lundsby Biogas A/S, Hjarbækvej 65, 8831 Løgstrup Tlf.: +45 96 49 43 00 info@lundsbybiogas.dk		
Denne tegning er underlagt copyright op på ikke reproduceres uden tilladelse fra Lundsbybiogas A/S		
Project nr.: 1768 Drawing nr.: 9642		FORMAT: A1

Technology building

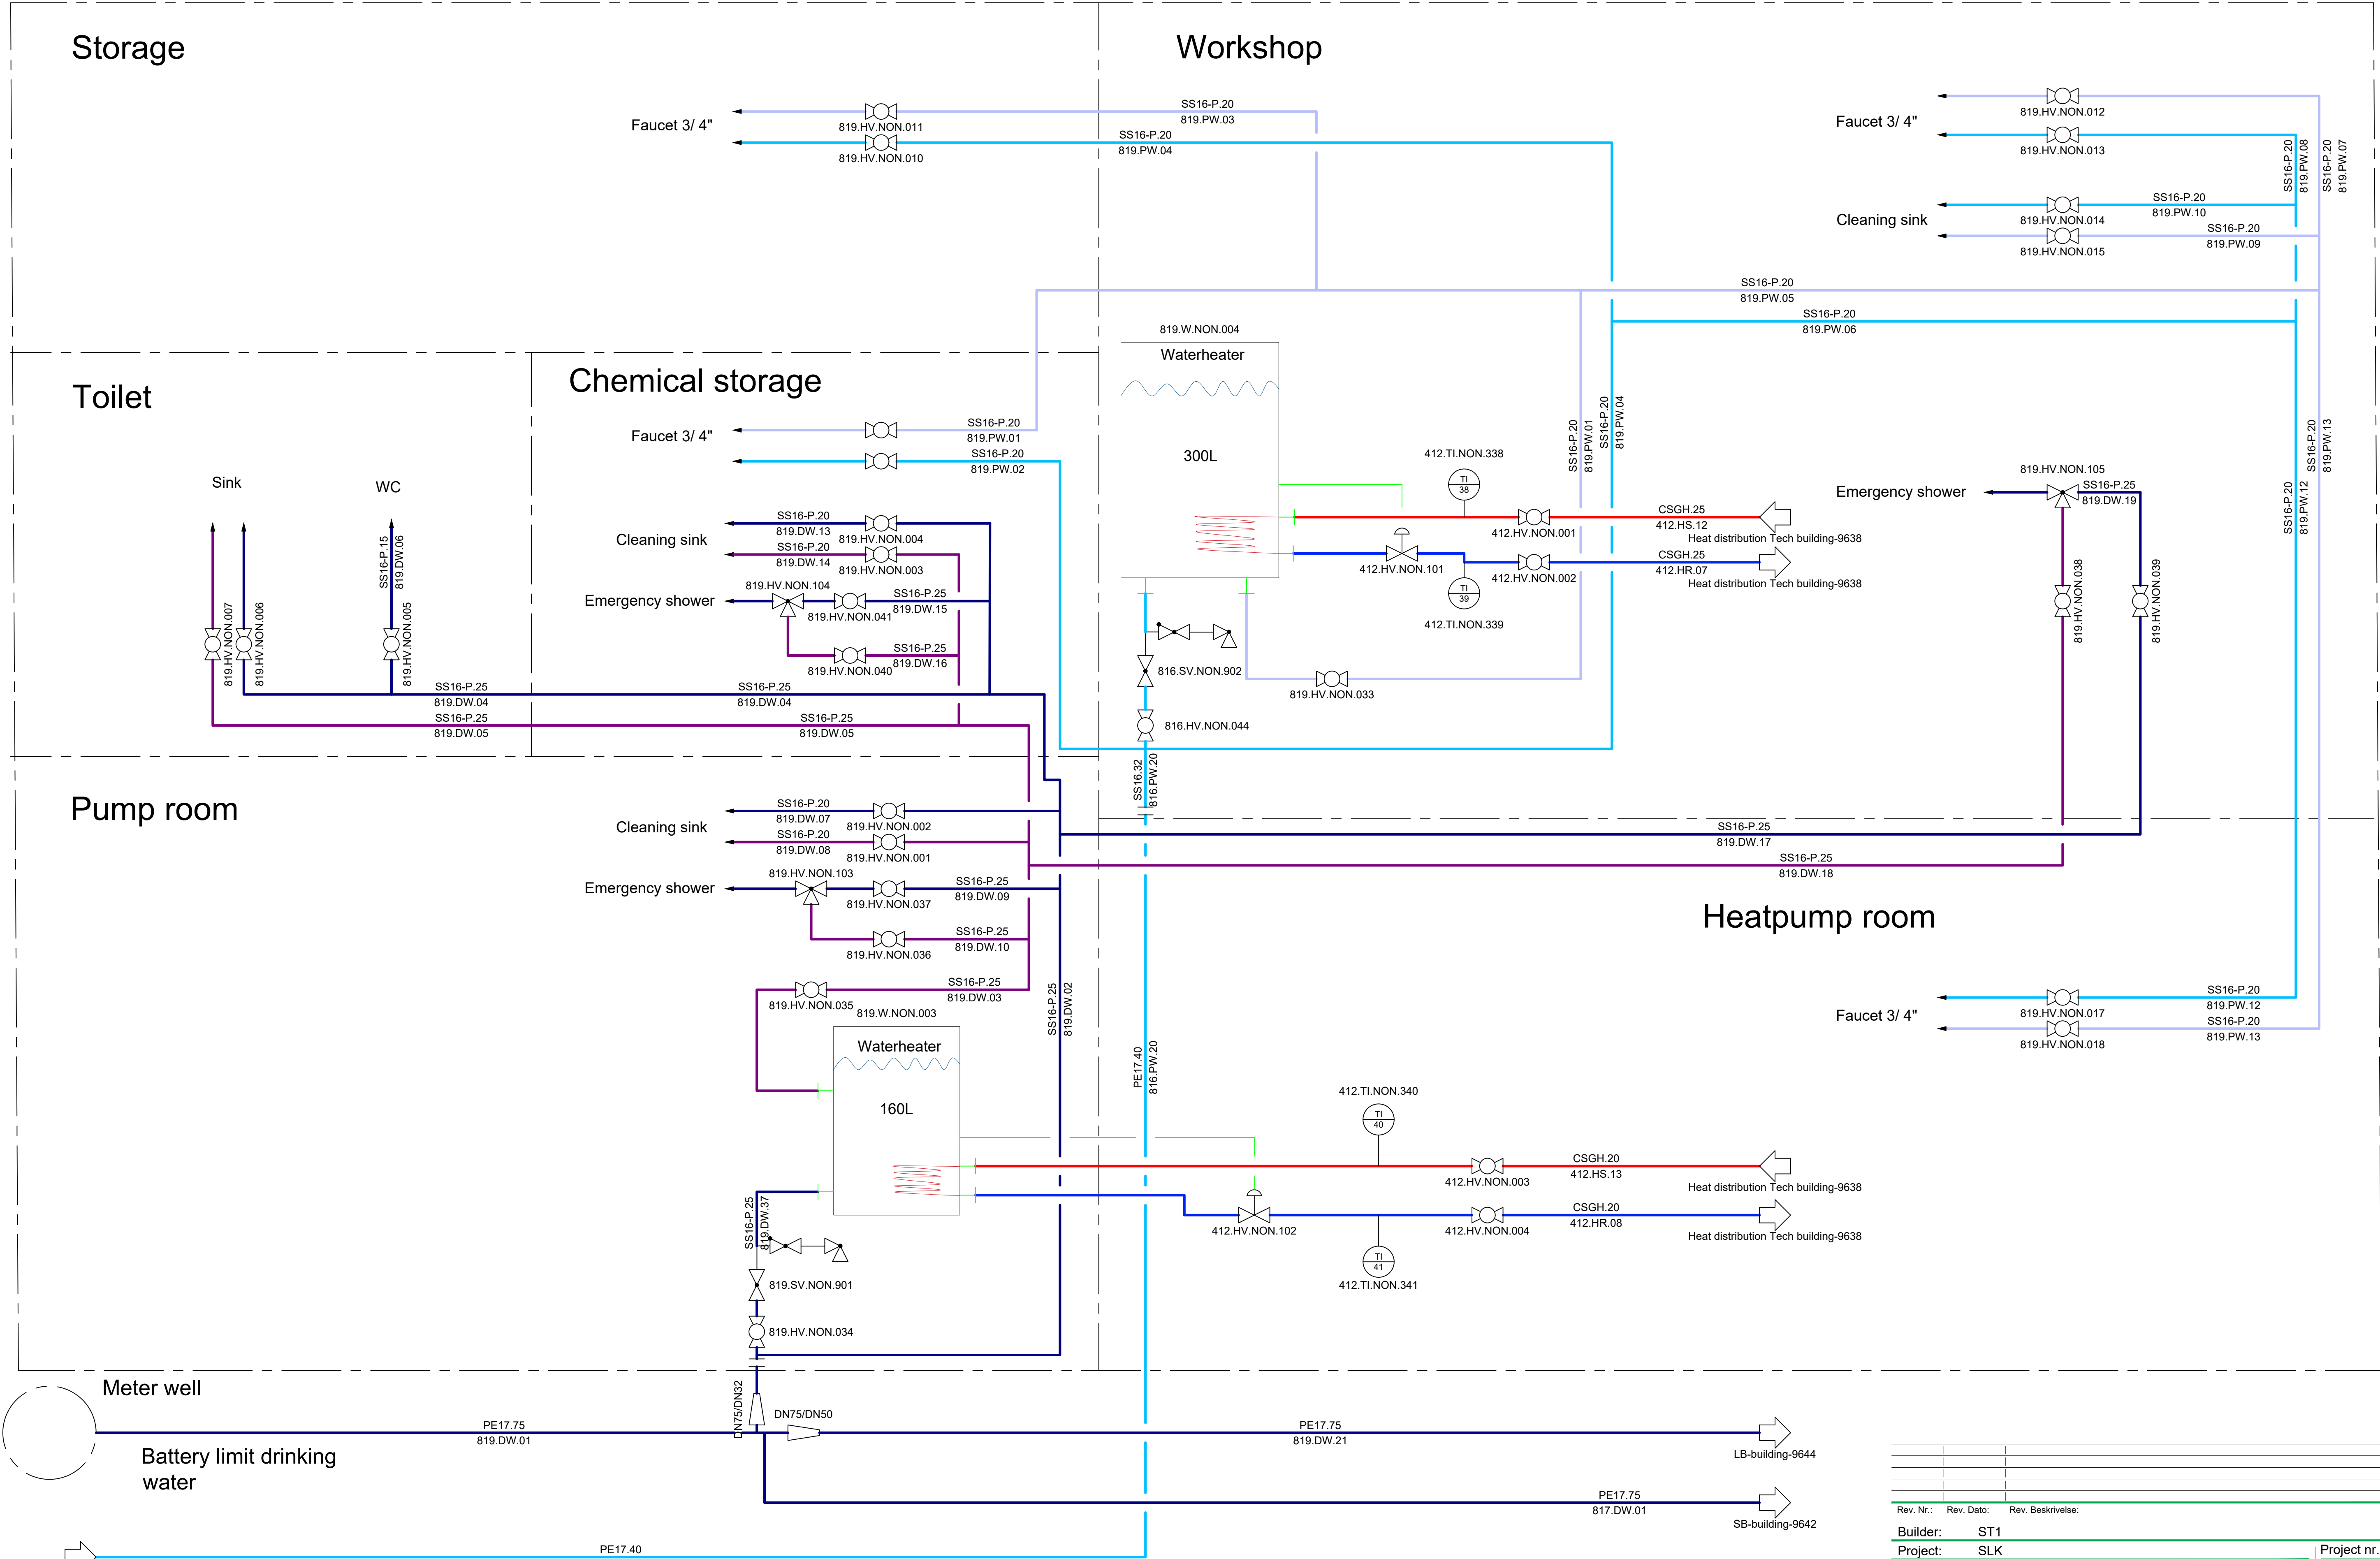


Rev. Nr.:	Rev. Dato:	Rev. Beskrivelse:	
Builder:	ST1		
Project:	SLK		
Subject:	Water distribution Tech building		
Rev. 6			
Int.:MDC	QC:CM	APP.:	Date: 15-10-2025
LUNDSBY RENEWABLE SOLUTIONS			Lundsby Biogas A/S, Hjarbækvej 65, 8831 Løgstrup Tlf.: +45 96 49 43 00 info@lundsbybiogas.dk Denne tegning er underlagt copywrite op på ikke reproduceres uden tilladelse fra Lundsbybiogas A/S
Project nr.: 1768 Drawing nr.: 9643			FORMAT: A1

LB-building

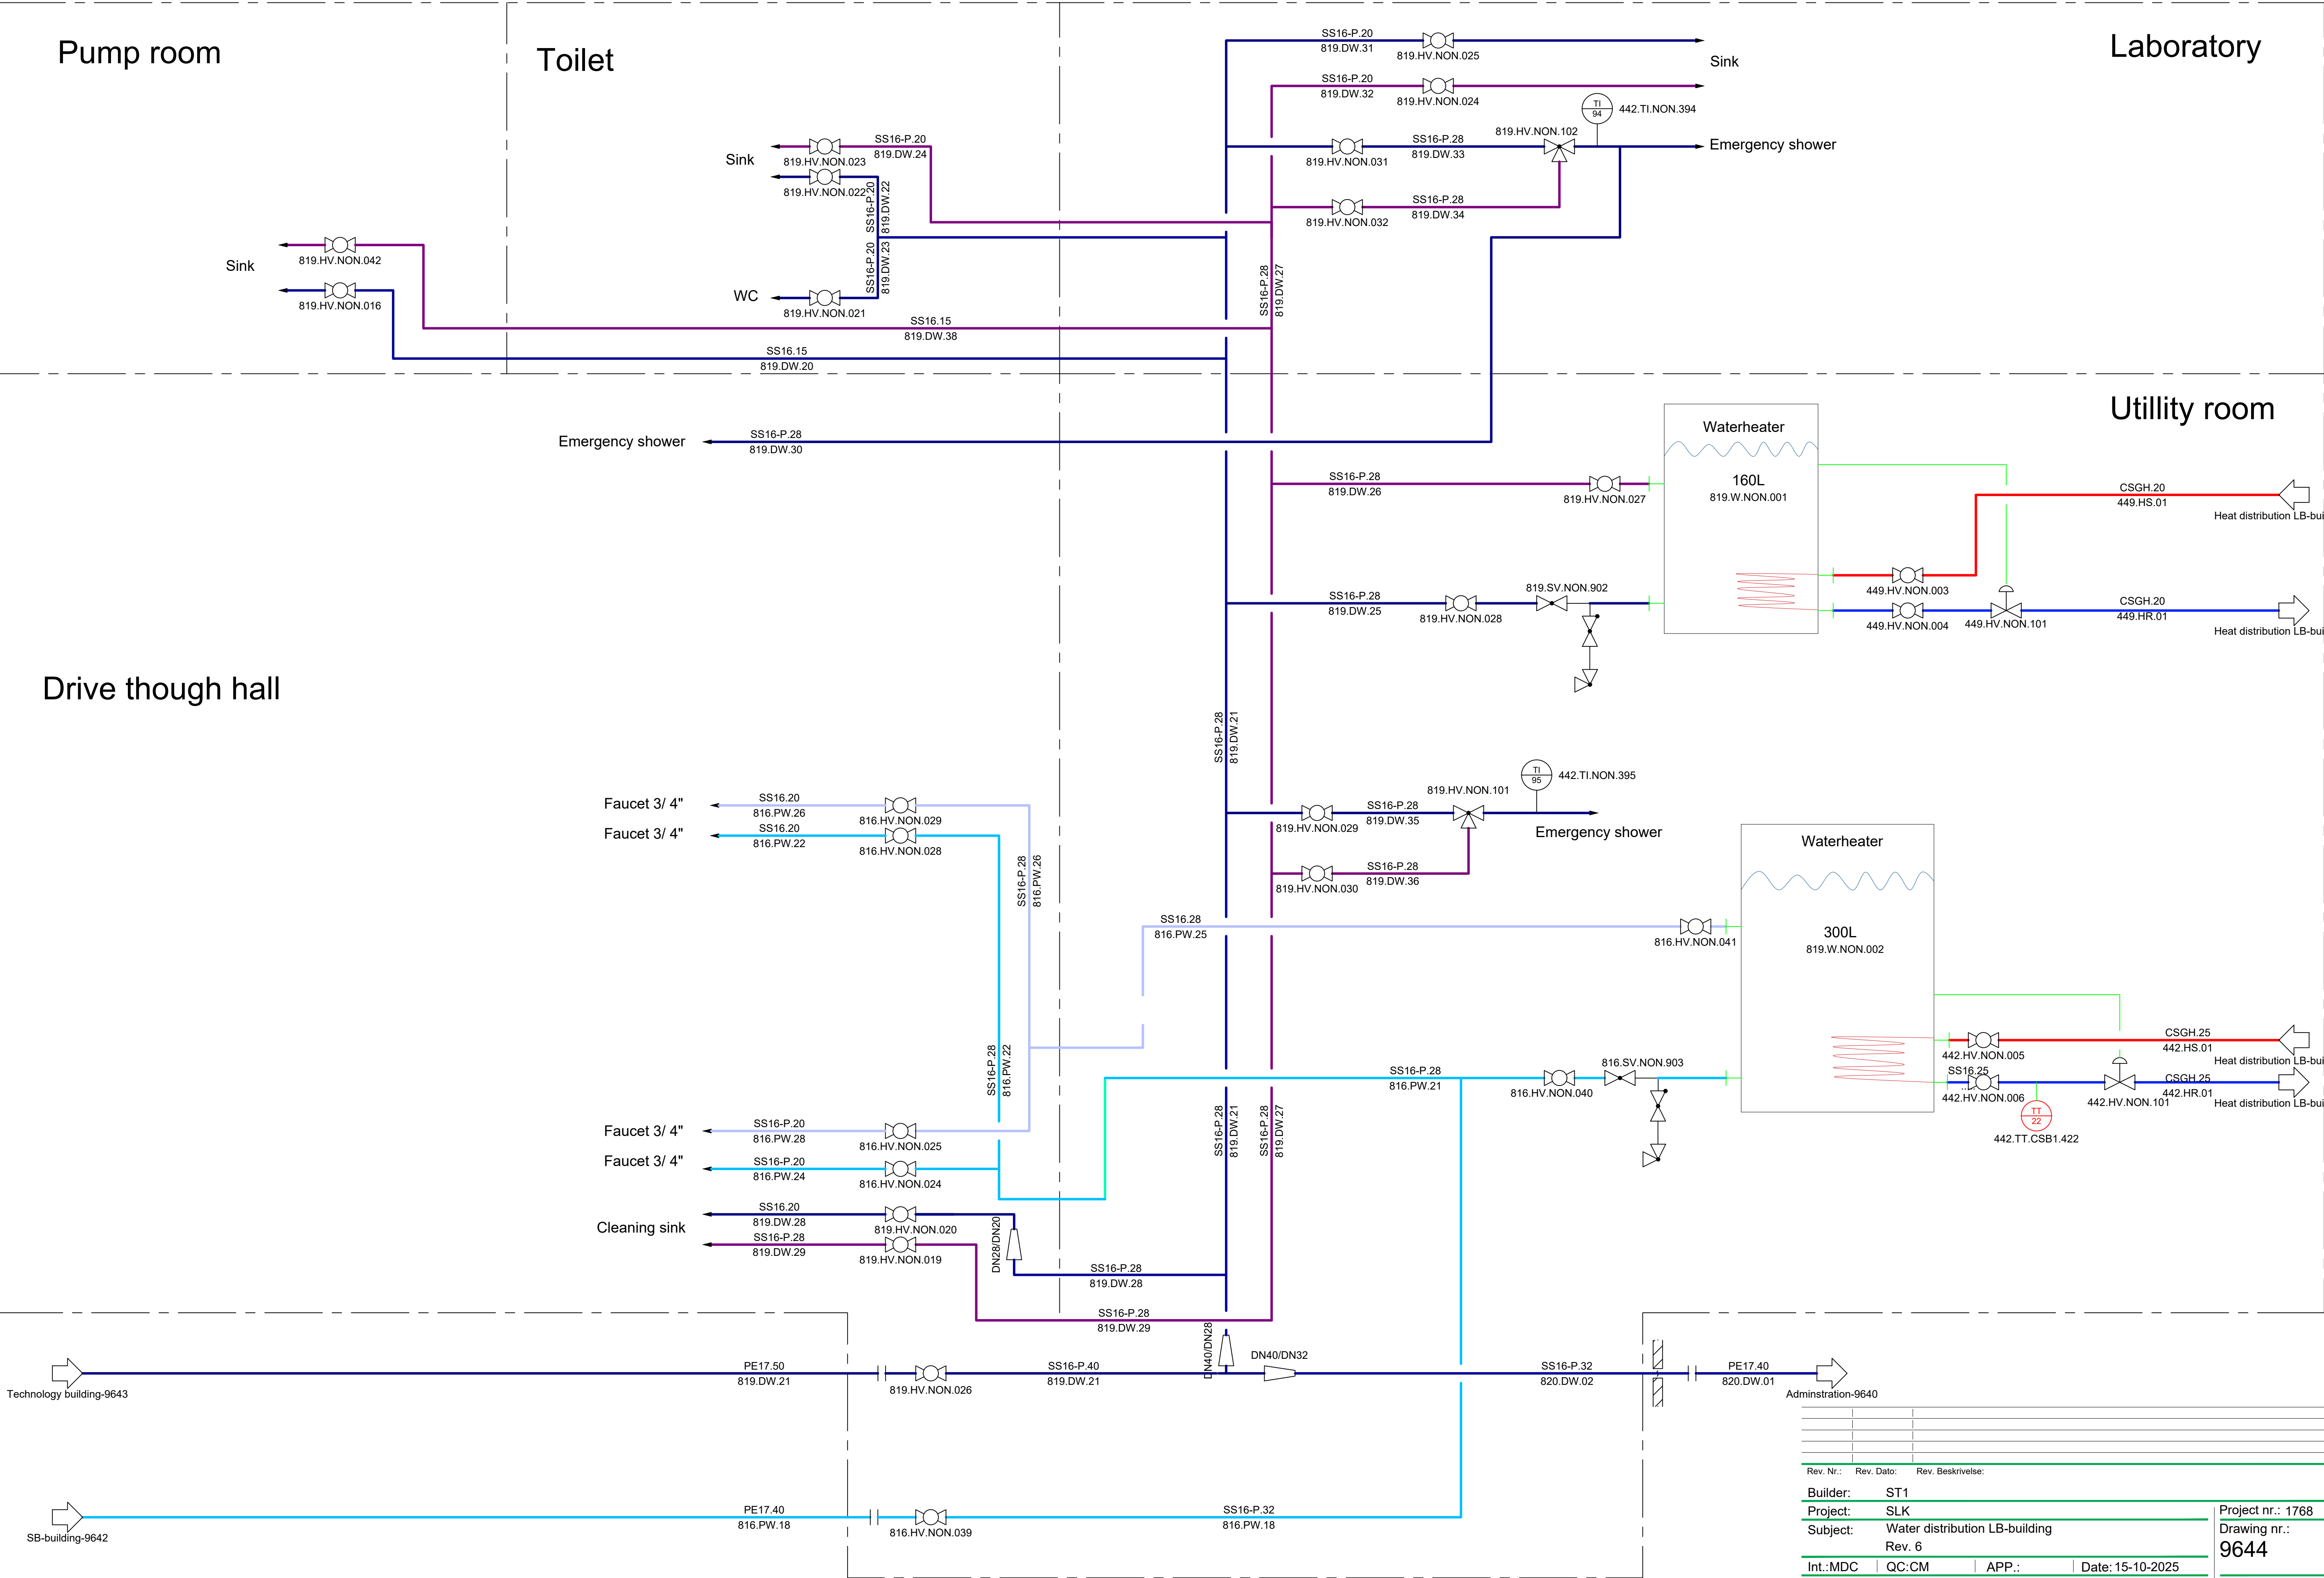

Rev. Nr.:	Rev. Dato:	Rev. Beskrivelse:
Builder:	ST1	
Project:	SLK	
Subject:	Water distribution LB-building	
Rev. 6		
Int.:MDC	QC:CM	APP.: Date: 15-10-2025
LUNDSBY RENEWABLE SOLUTIONS Lundsby Biogas A/S, Hjarbækvej 65, 8831 Løgstrup Tlf.: +45 96 49 43 00 Info@lundsbybiogas.dk Denne tegning er underlagt copywrite op må ikke reproduceres uden tilladelse fra Lundsbybiogas A/S		
Project nr.: 1768		
Drawing nr.: 9644		
FORMAT: A1		

Pumphouse 1

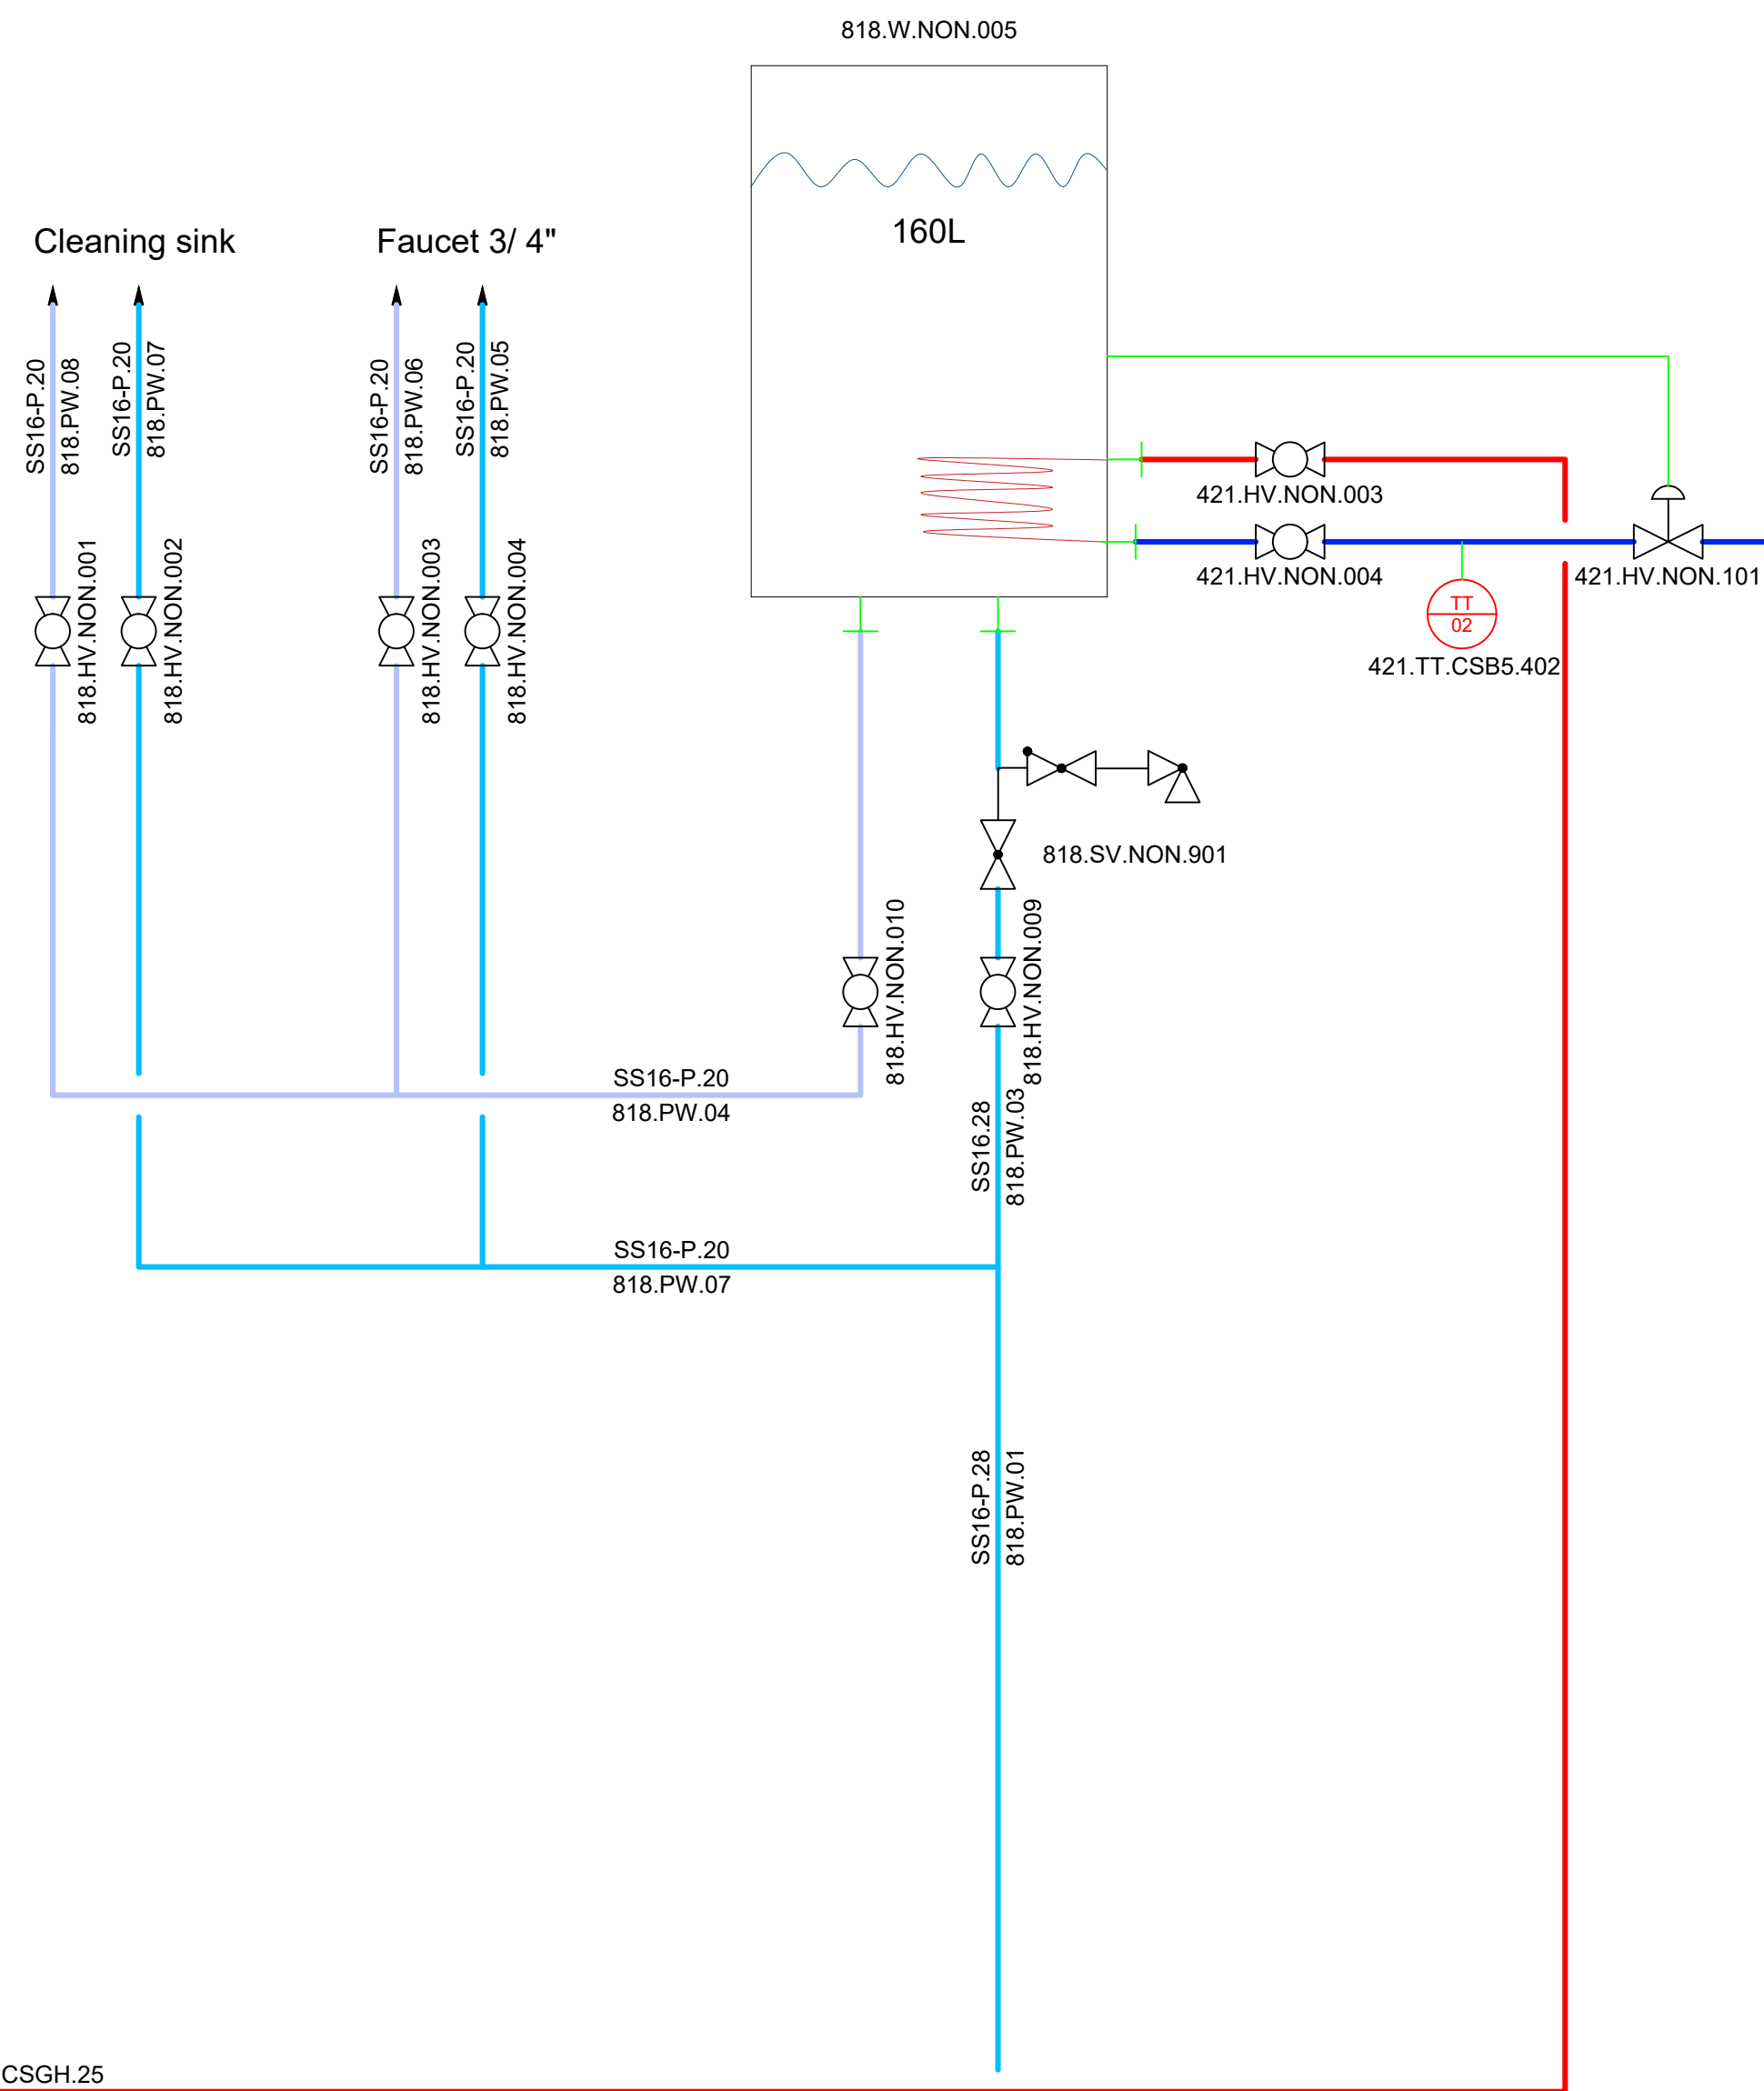


Heat distribution PH1-9641
CSGH.25
421.HS.01

Heat distribution PH1-9641
CSGH.25
421.HR.01

SB-building-9642
SS16-P.28
816.PW.06

Pumphouse 2

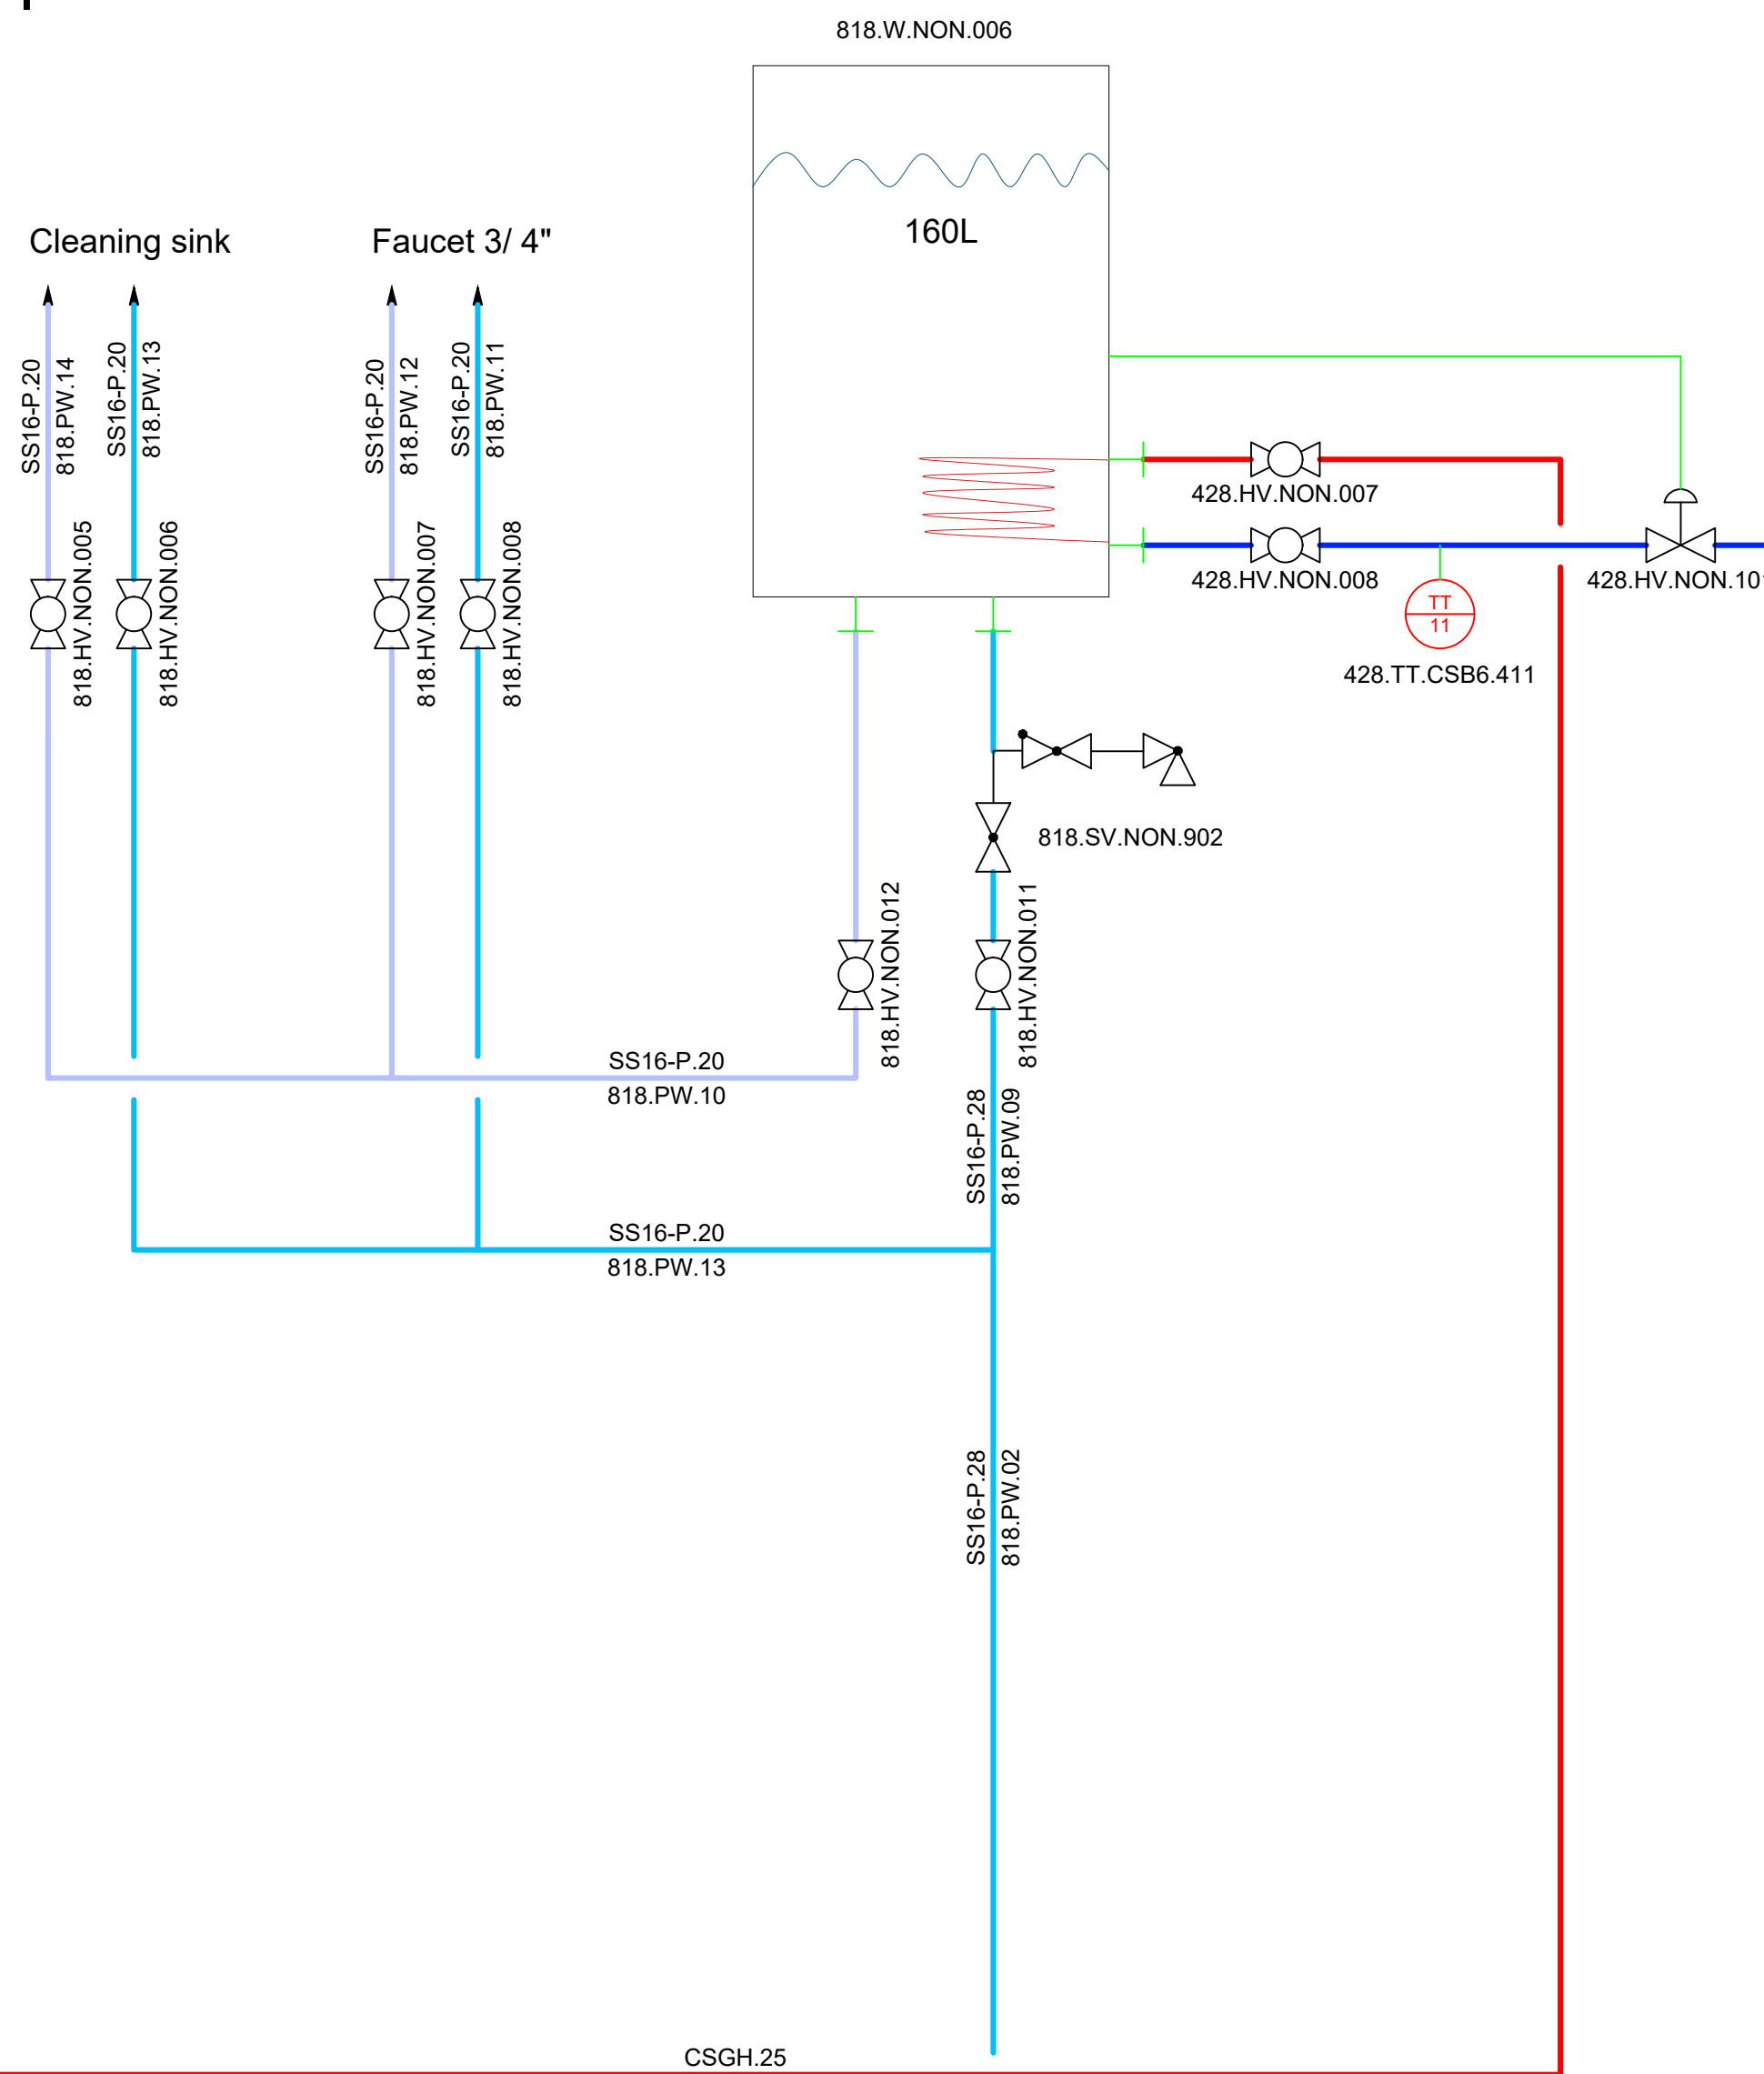



Heat distribution PH2-9641
CSGH.25
428.HS.01

Heat distribution PH2-9641
CSGH.25
428.HR.01


SS16-P.28
816.PW.06

Rev. Nr.:	Rev. Dato:	Rev. Beskrivelse:
Builder:	ST1	
Project:	SLK	
Subject:	Water distribution pumphouse 1 & 2	
Rev. 6		
Int.:MDC	QC:CM	APP.:
Date:	15-10-2025	
LUNDSBY RENEWABLE SOLUTIONS		
Lundsby Biogas A/S, Hjarbækvej 65, 8831 Løgstrup Tlf.: +45 96 49 43 00 info@lundsbybiogas.dk Denne tegning er underlagt copyright og må ikke reproduceres uden tilladelse fra Lundsbybiogas A/S		
Project nr.: 1768		Drawing nr.: 9645
FORMAT: A1		

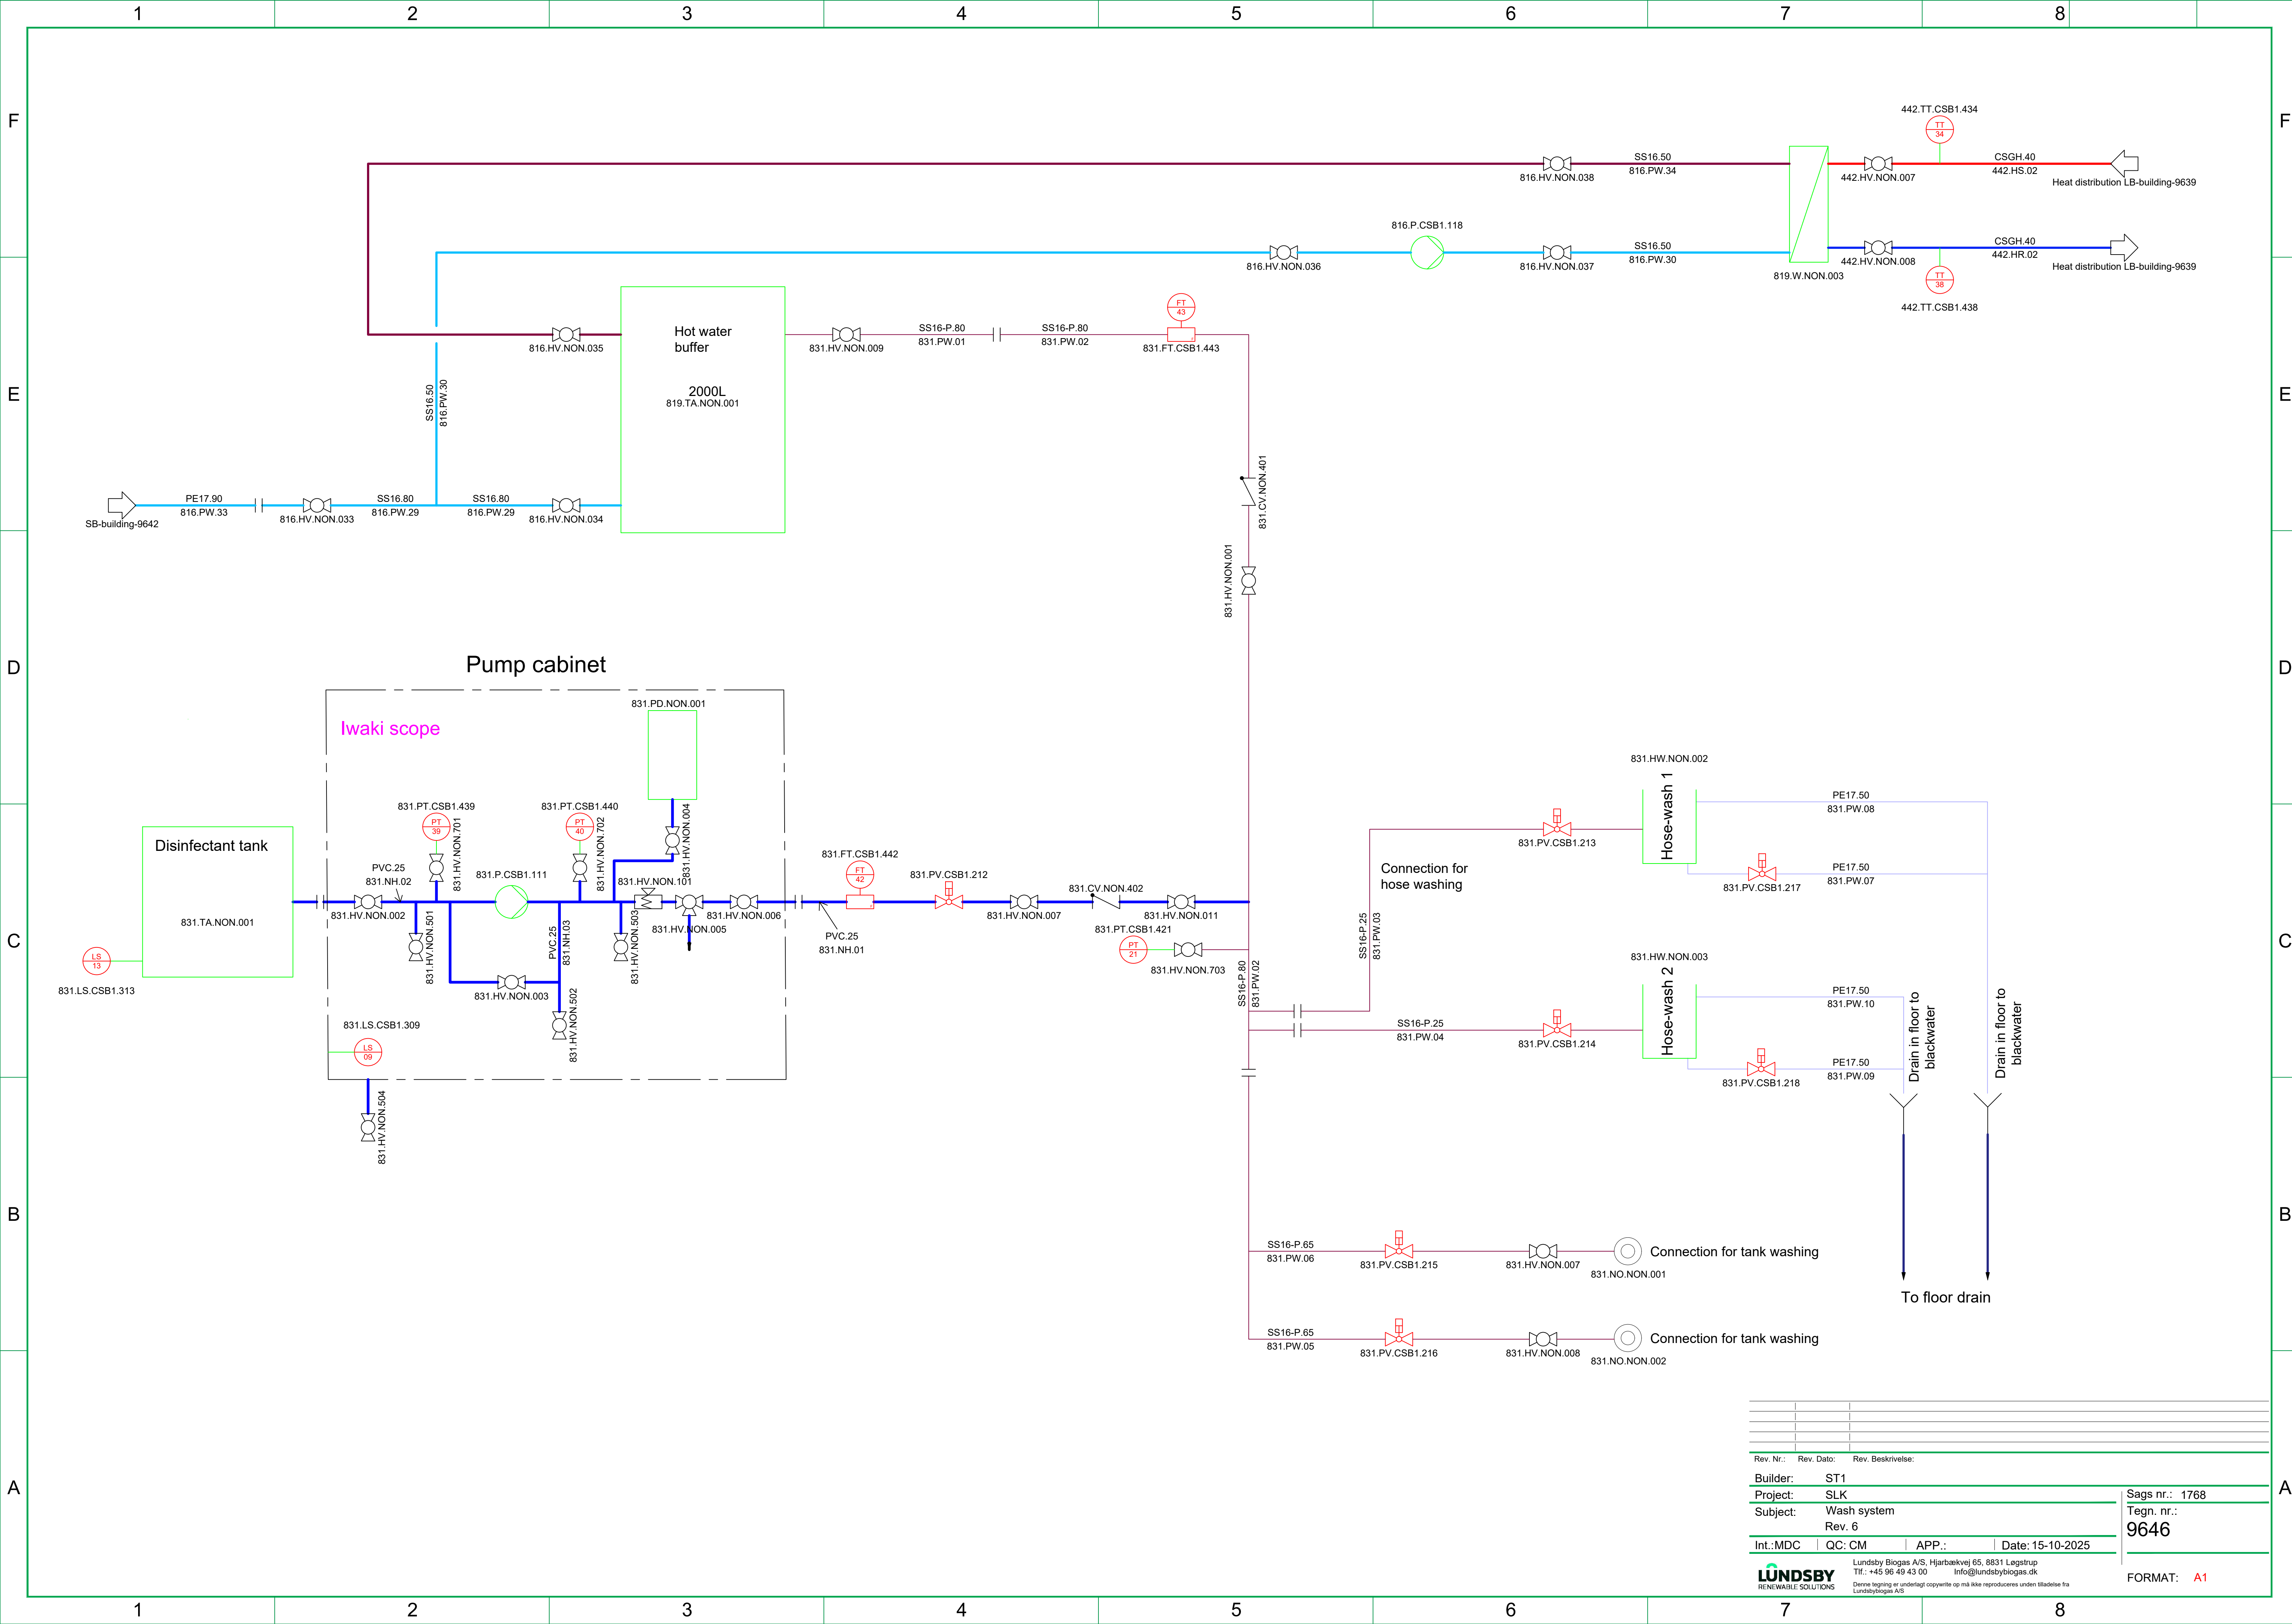


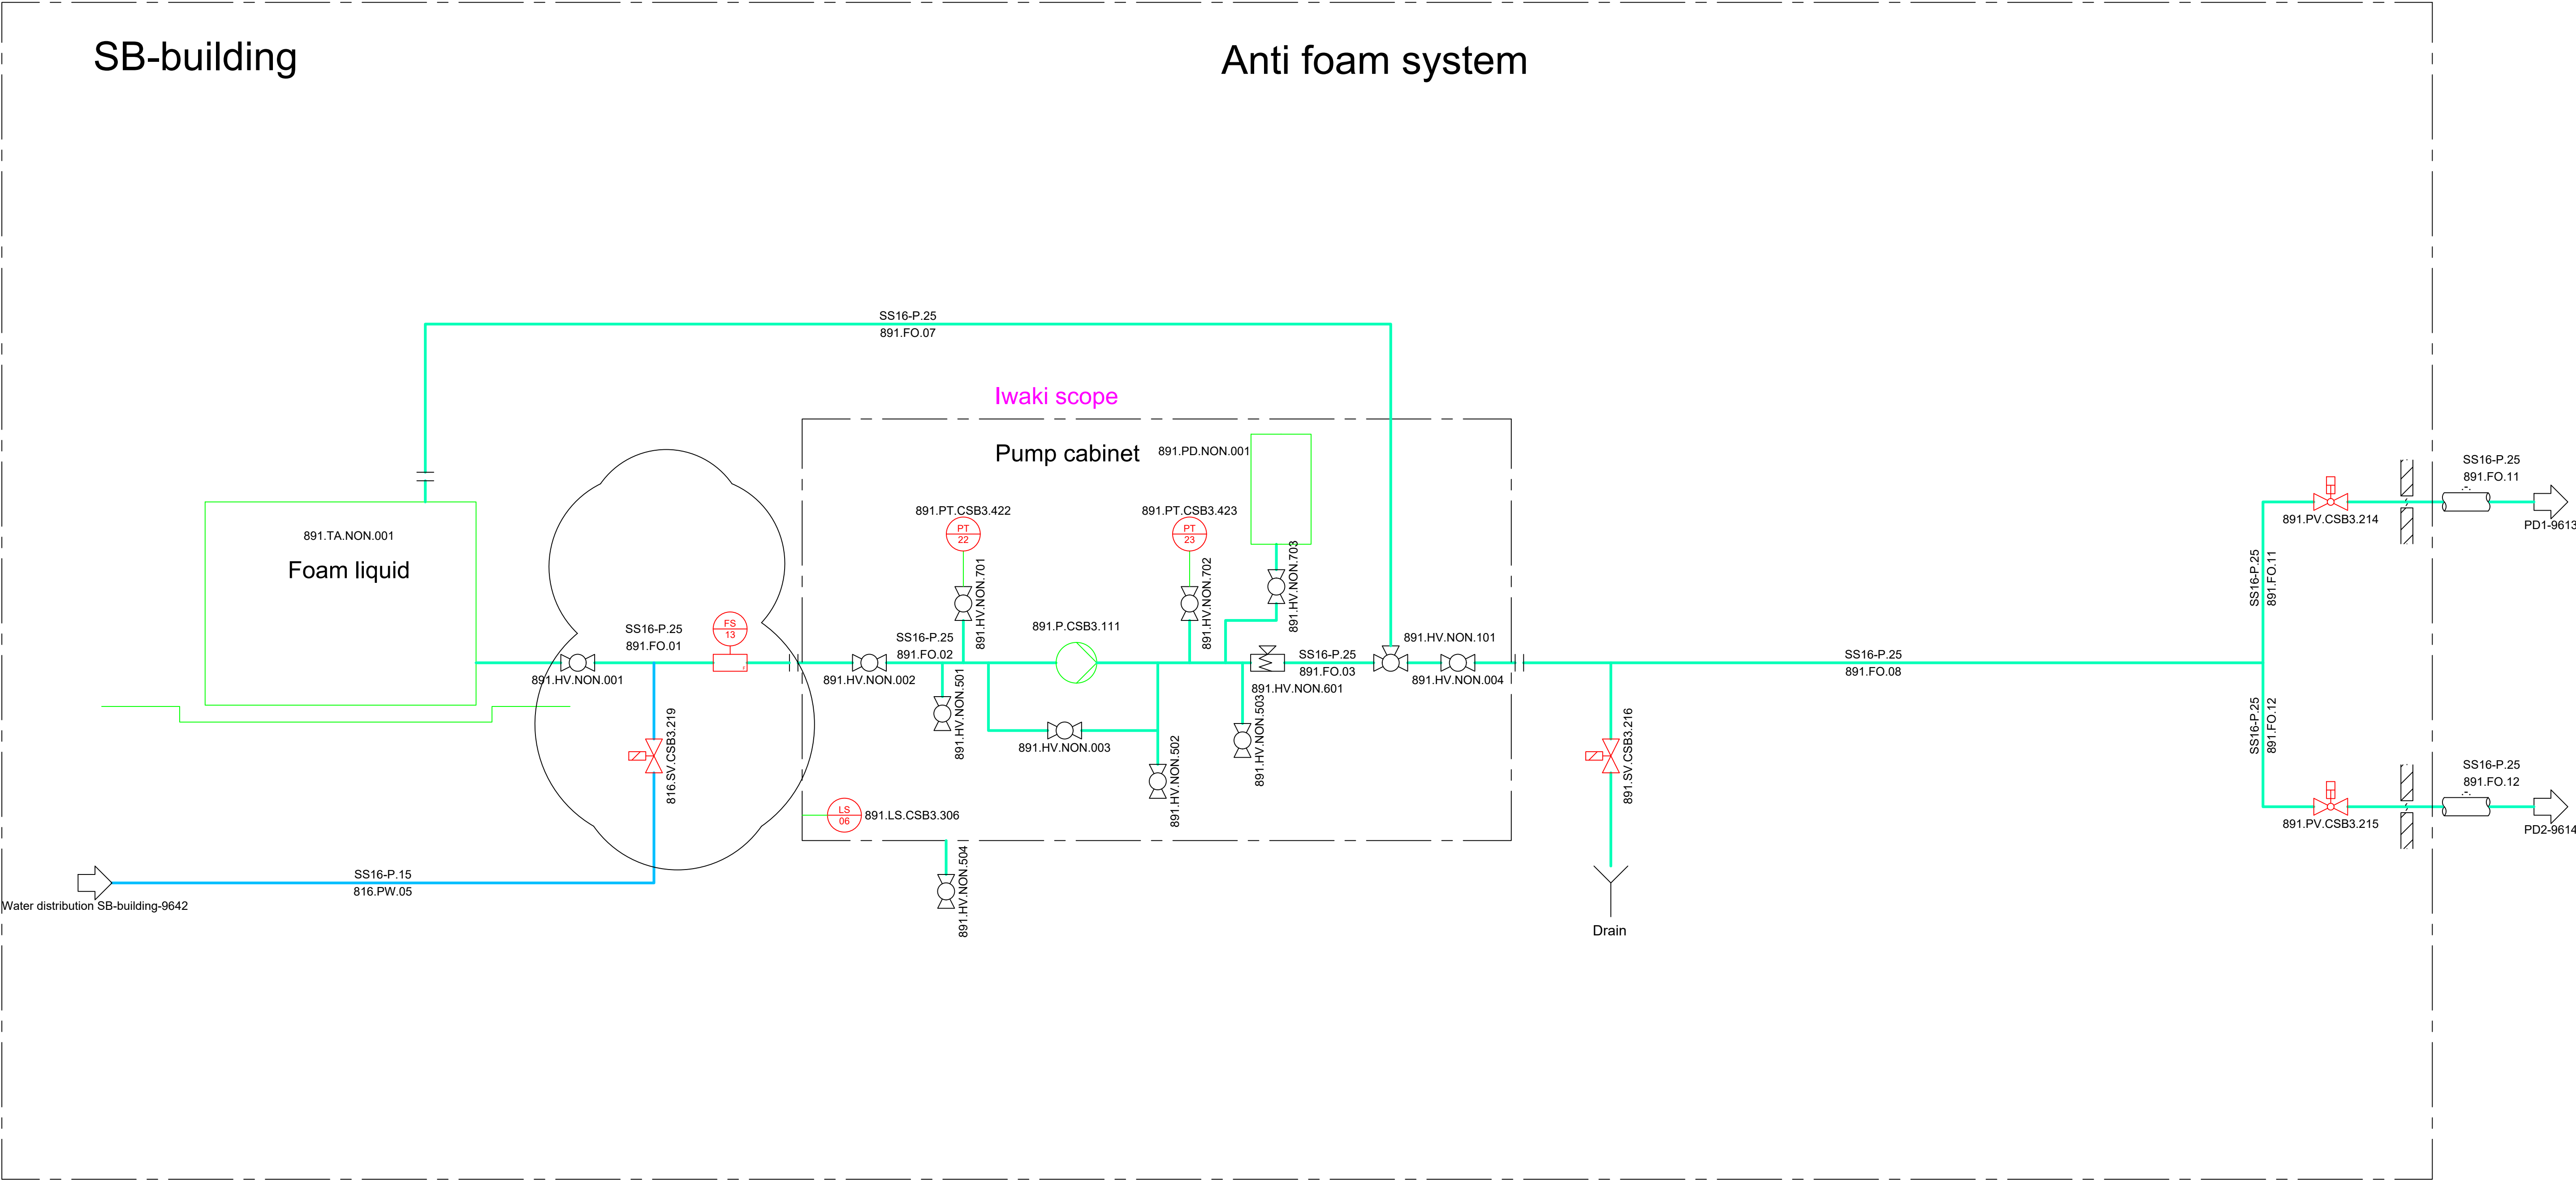


Rev. Nr.:	Rev. Dato:	Rev. Description:	
Builder:	ST1		
Project:	SLK		
Subject:	Anti foam system		
Rev. 6			
Int.:MDC	QC.CM	APP.:	Date: 15-10-2025
LUNDSBY RENEWABLE SOLUTIONS			Lundby Renewable Solutions A/S, Hjarbækvej 65, 8831 Legstrup Tlf.: +45 96 49 43 00 Info@lundby.dk This Drawing is subject to copyright and may not be reproduced without permission from Lundby Renewable Solutions A/S
Project nr.:1768 Drawing nr.: 9648			FORMAT: A1

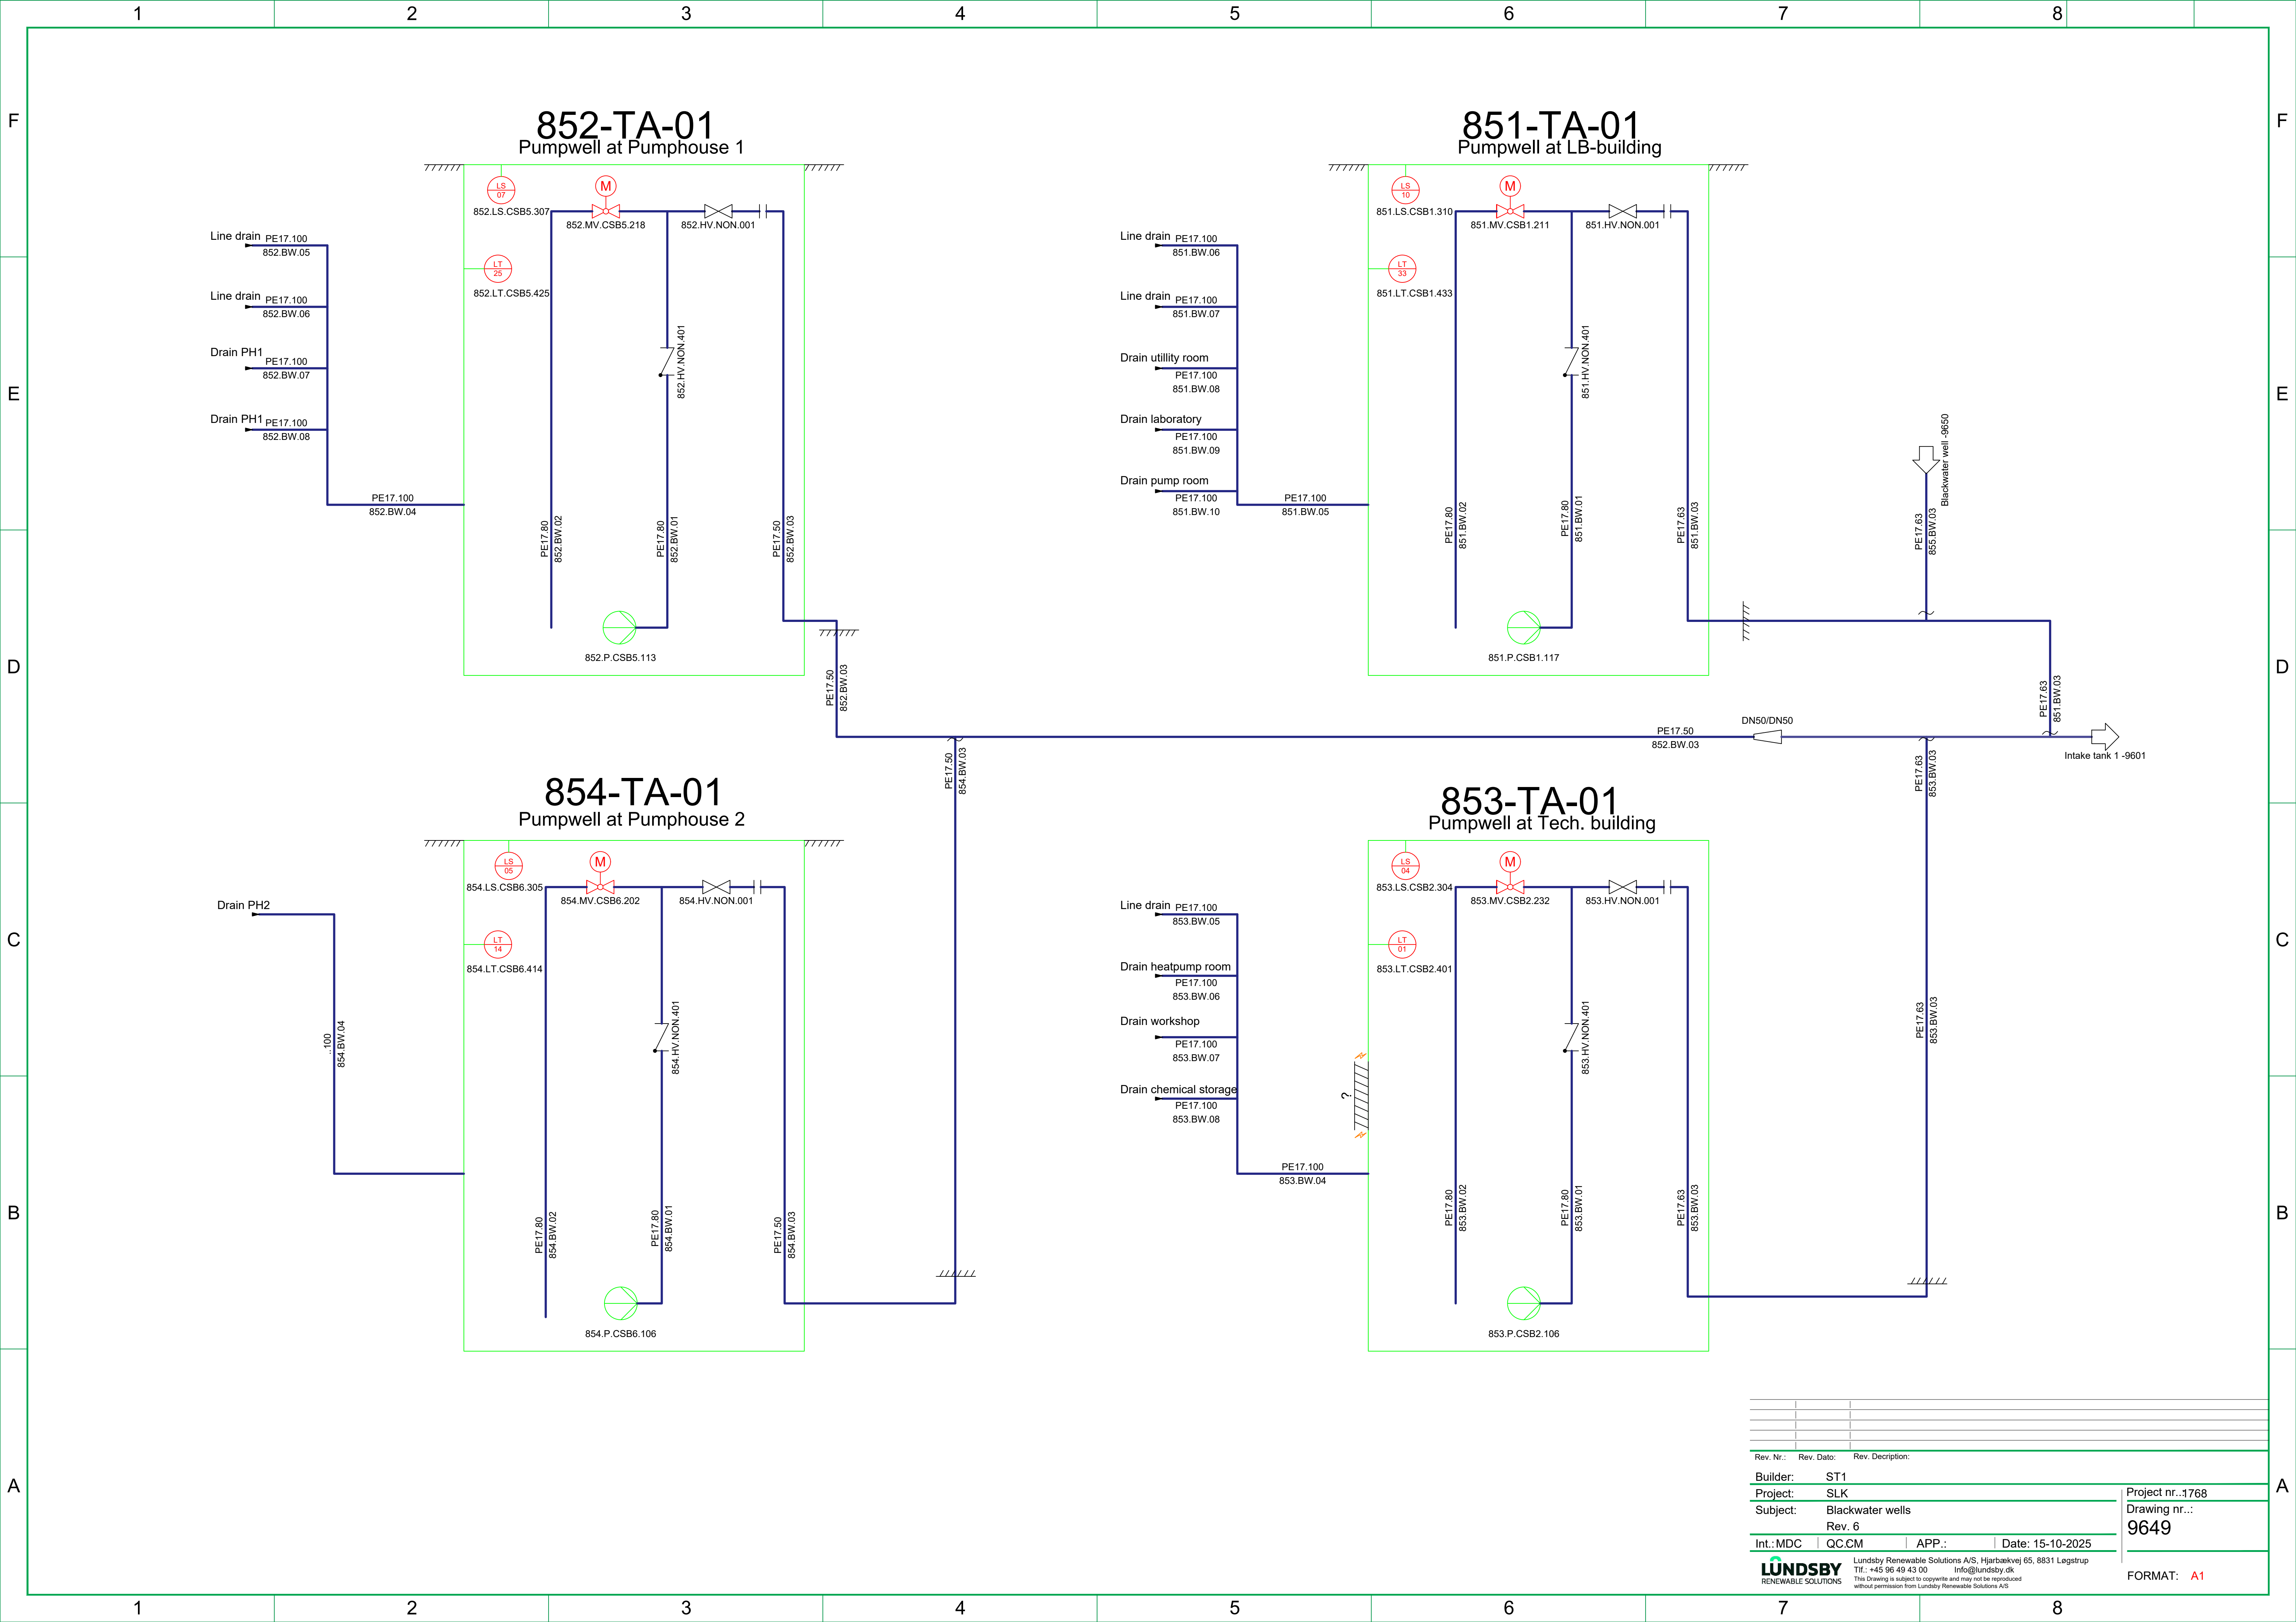

Rev. Nr.:	Rev. Dato:	Rev. Description:			
Builder:	ST1				
Project:	SLK				
Subject:	Blackwater wells				
	Rev. 6				
Int.:MDC	QC:CM	APP.:		Date: 15-10-2025	
		Lundsby Renewable Solutions A/S, Hjarbækvej 65, 8831 Løgstrup Tlf.: +45 96 49 43 00 Info@lundsby.dk This Drawing is subject to copyright and may not be reproduced without permission from Lundsby Renewable Solutions A/S			
		Project nr.:1768		Drawing nr.: 9649	
		FORMAT: A1			

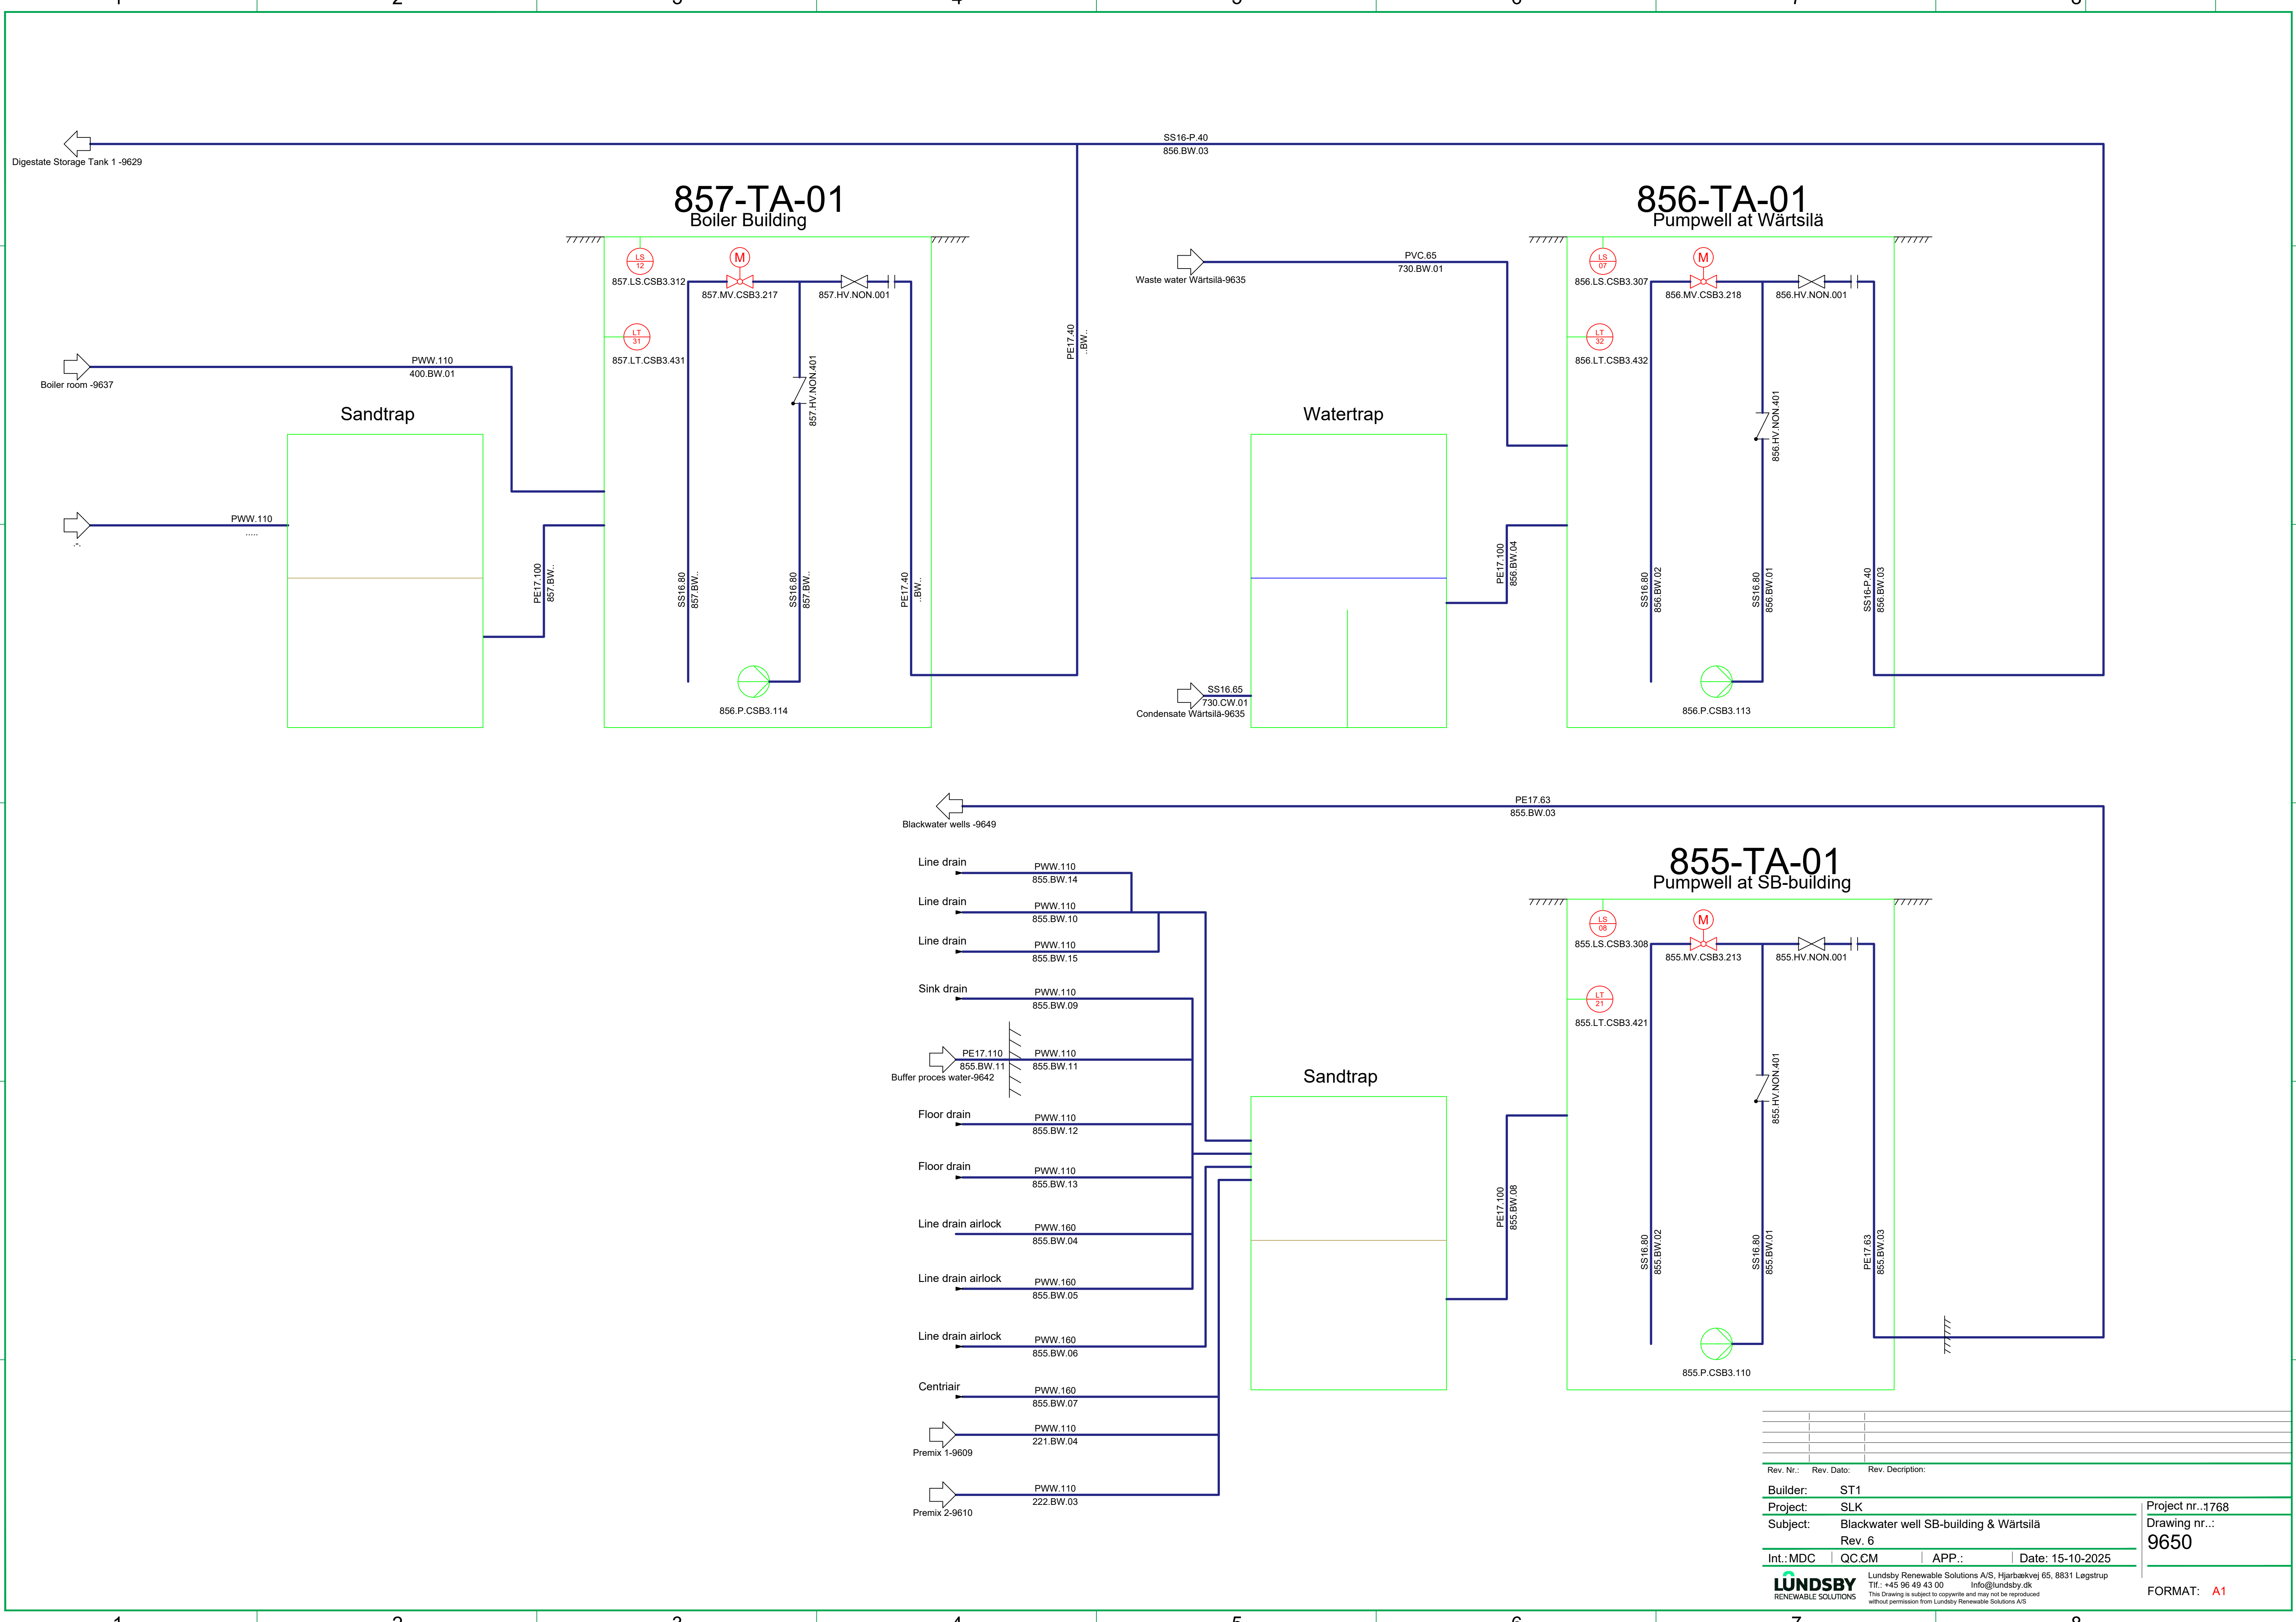


Rev. Nr.:	Rev. Dato:	Rev. Description:
Builder:	ST1	
Project:	SLK	
Subject:	Blackwater well SB-building & Wärtsilä	
	Rev. 6	
Int.:MDC	QC:CM	APP.:
		Date: 15-10-2025
LUNDSBYRENEWABLE SOLUTIONS Lundsby Renewable Solutions A/S, Hjarbækvej 65, 8831 Løgstrup Tlf.: +45 96 49 43 00 info@lundsby.dk This Drawing is subject to copyright and may not be reproduced without permission from Lundsby Renewable Solutions A/S		
Project nr.:1768		Drawing nr.:9650
FORMAT: A1		

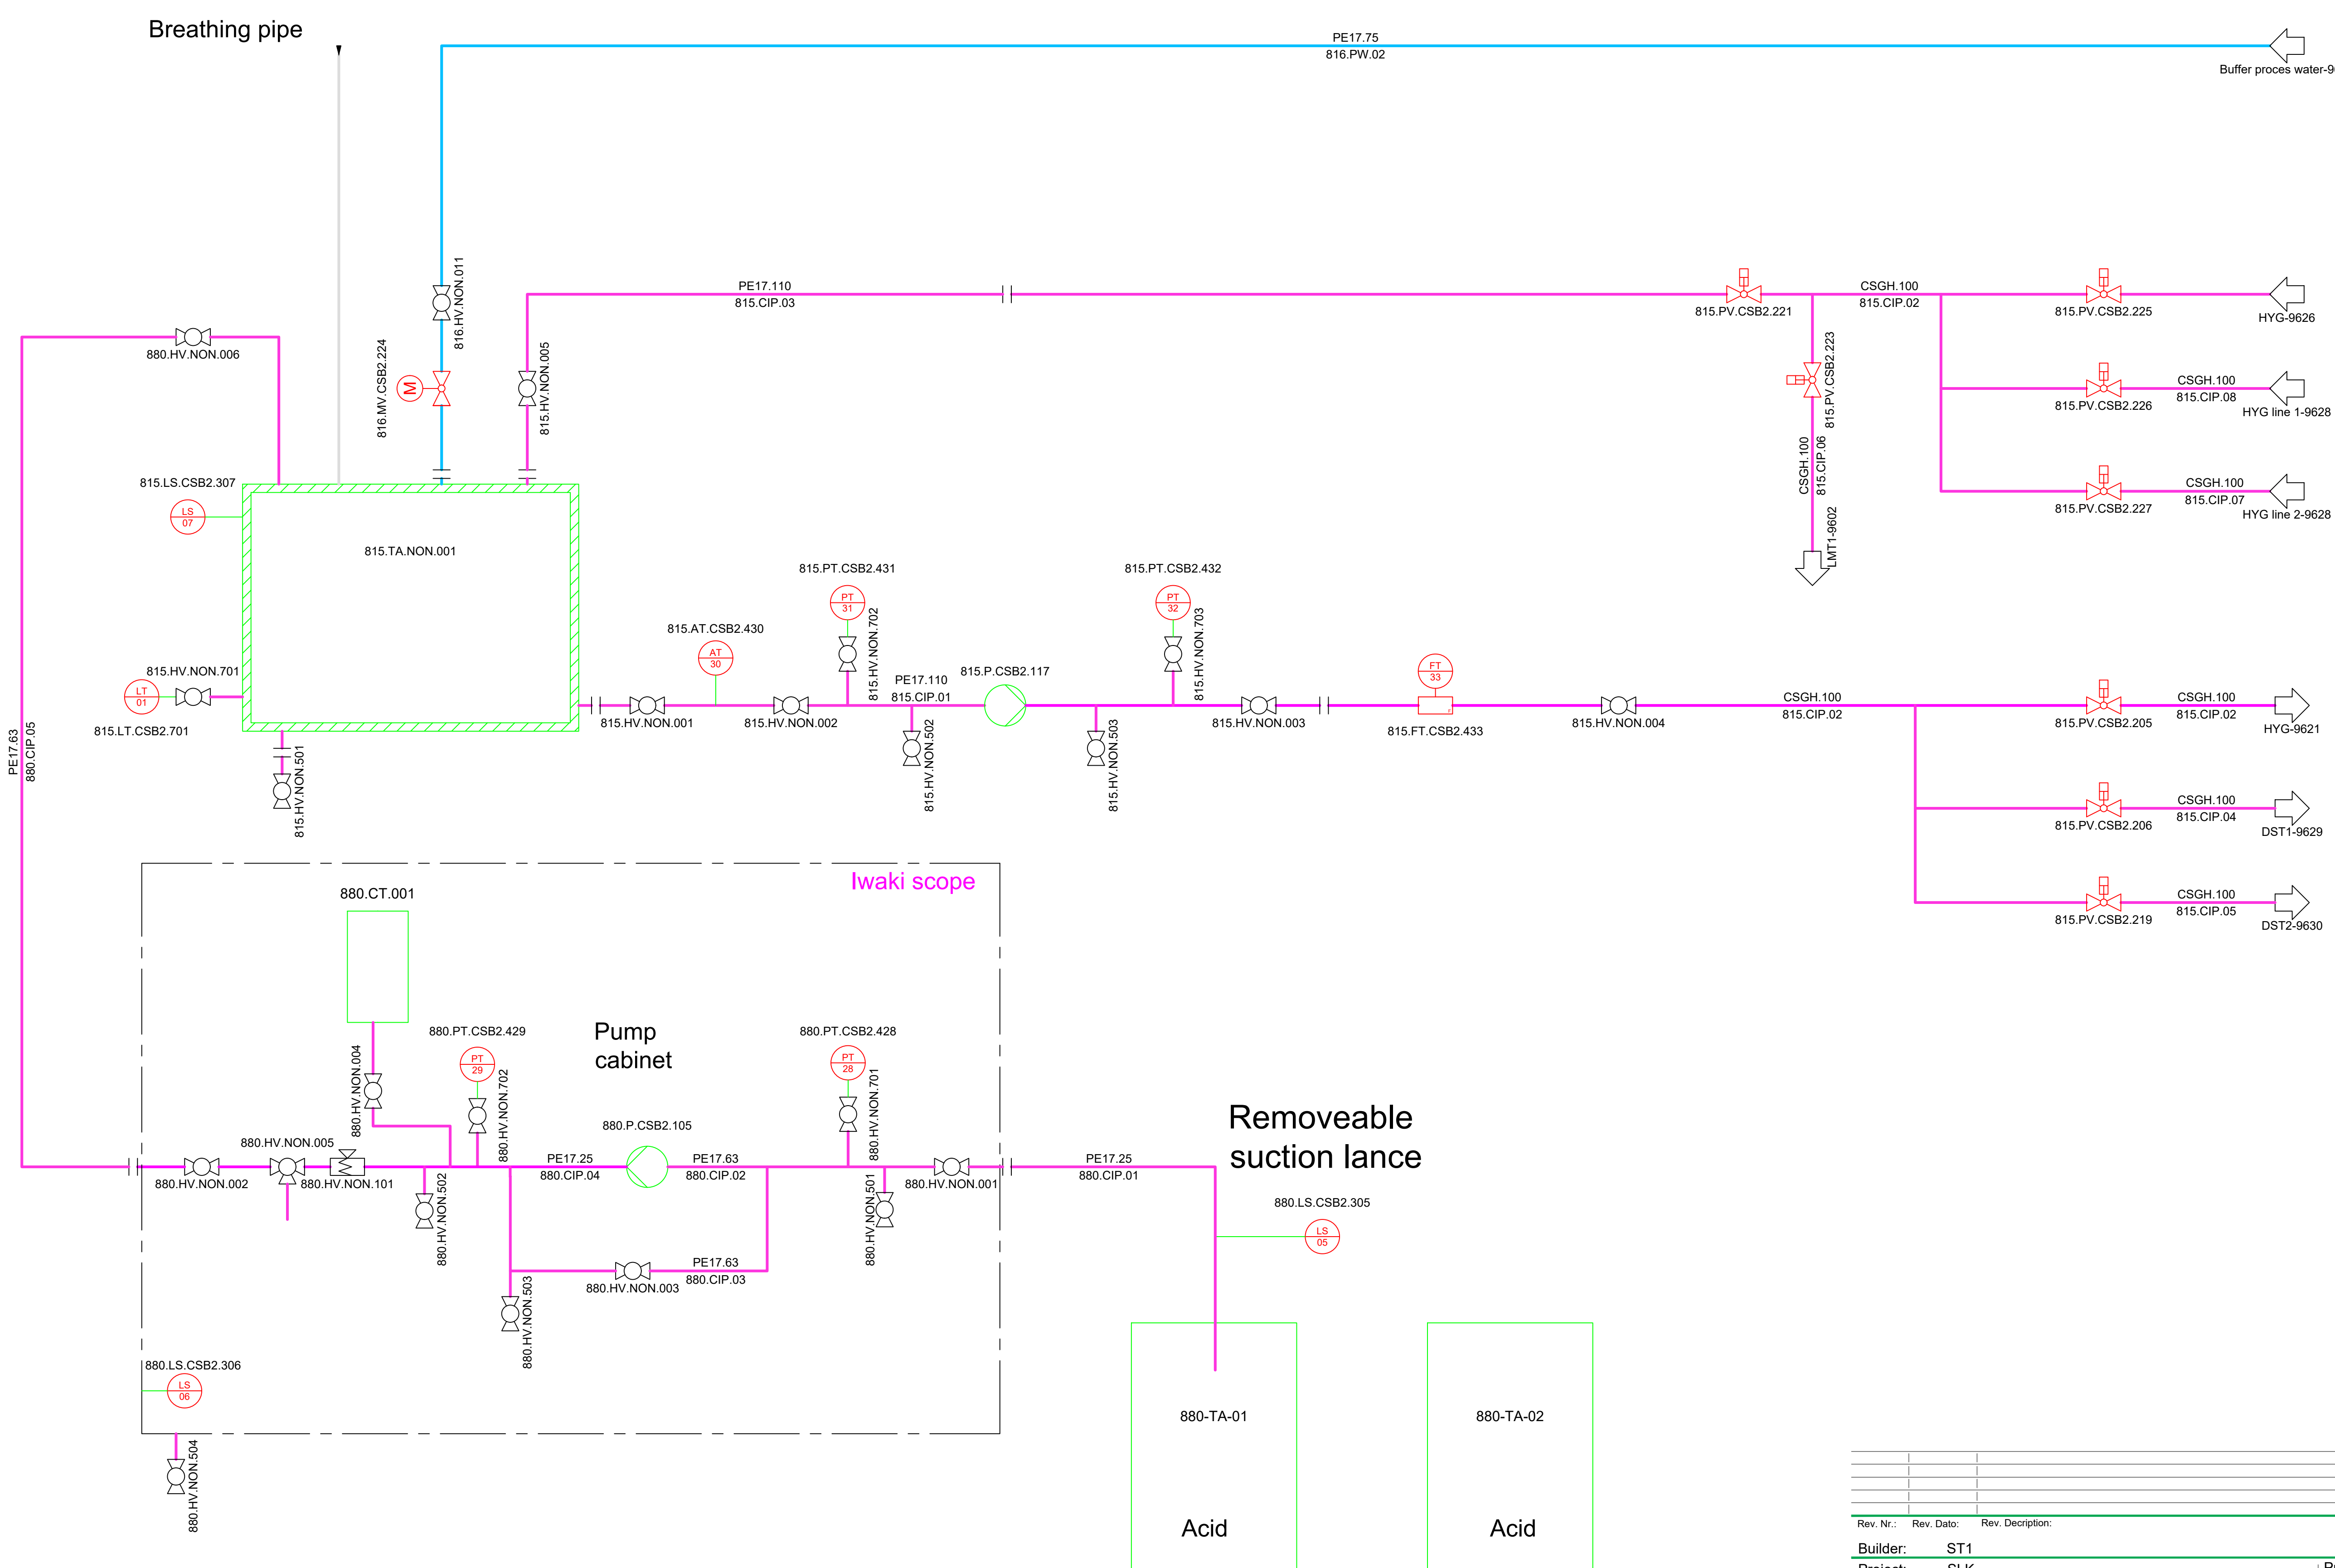

Rev. Nr.:	Rev. Dato:	Rev. Description:
Builder:	ST1	
Project:	SLK	
Subject:	CIP facility	
Rev. 6		
Int.:MDC	QC:CM	APP.:
Date:	15-10-2025	
LUNDSBY RENEWABLE SOLUTIONS		
Lundsby Renewable Solutions A/S, Hjarbækvej 65, 8831 Legstrup Tlf.: +45 96 49 43 00 Info@lundsby.dk This Drawing is subject to copyright and may not be reproduced without permission from Lundsby Renewable Solutions A/S		
Project nr...1768 Drawing nr... 9651		FORMAT: A1

Pumphouse 1

~~JA Trykluft scope~~

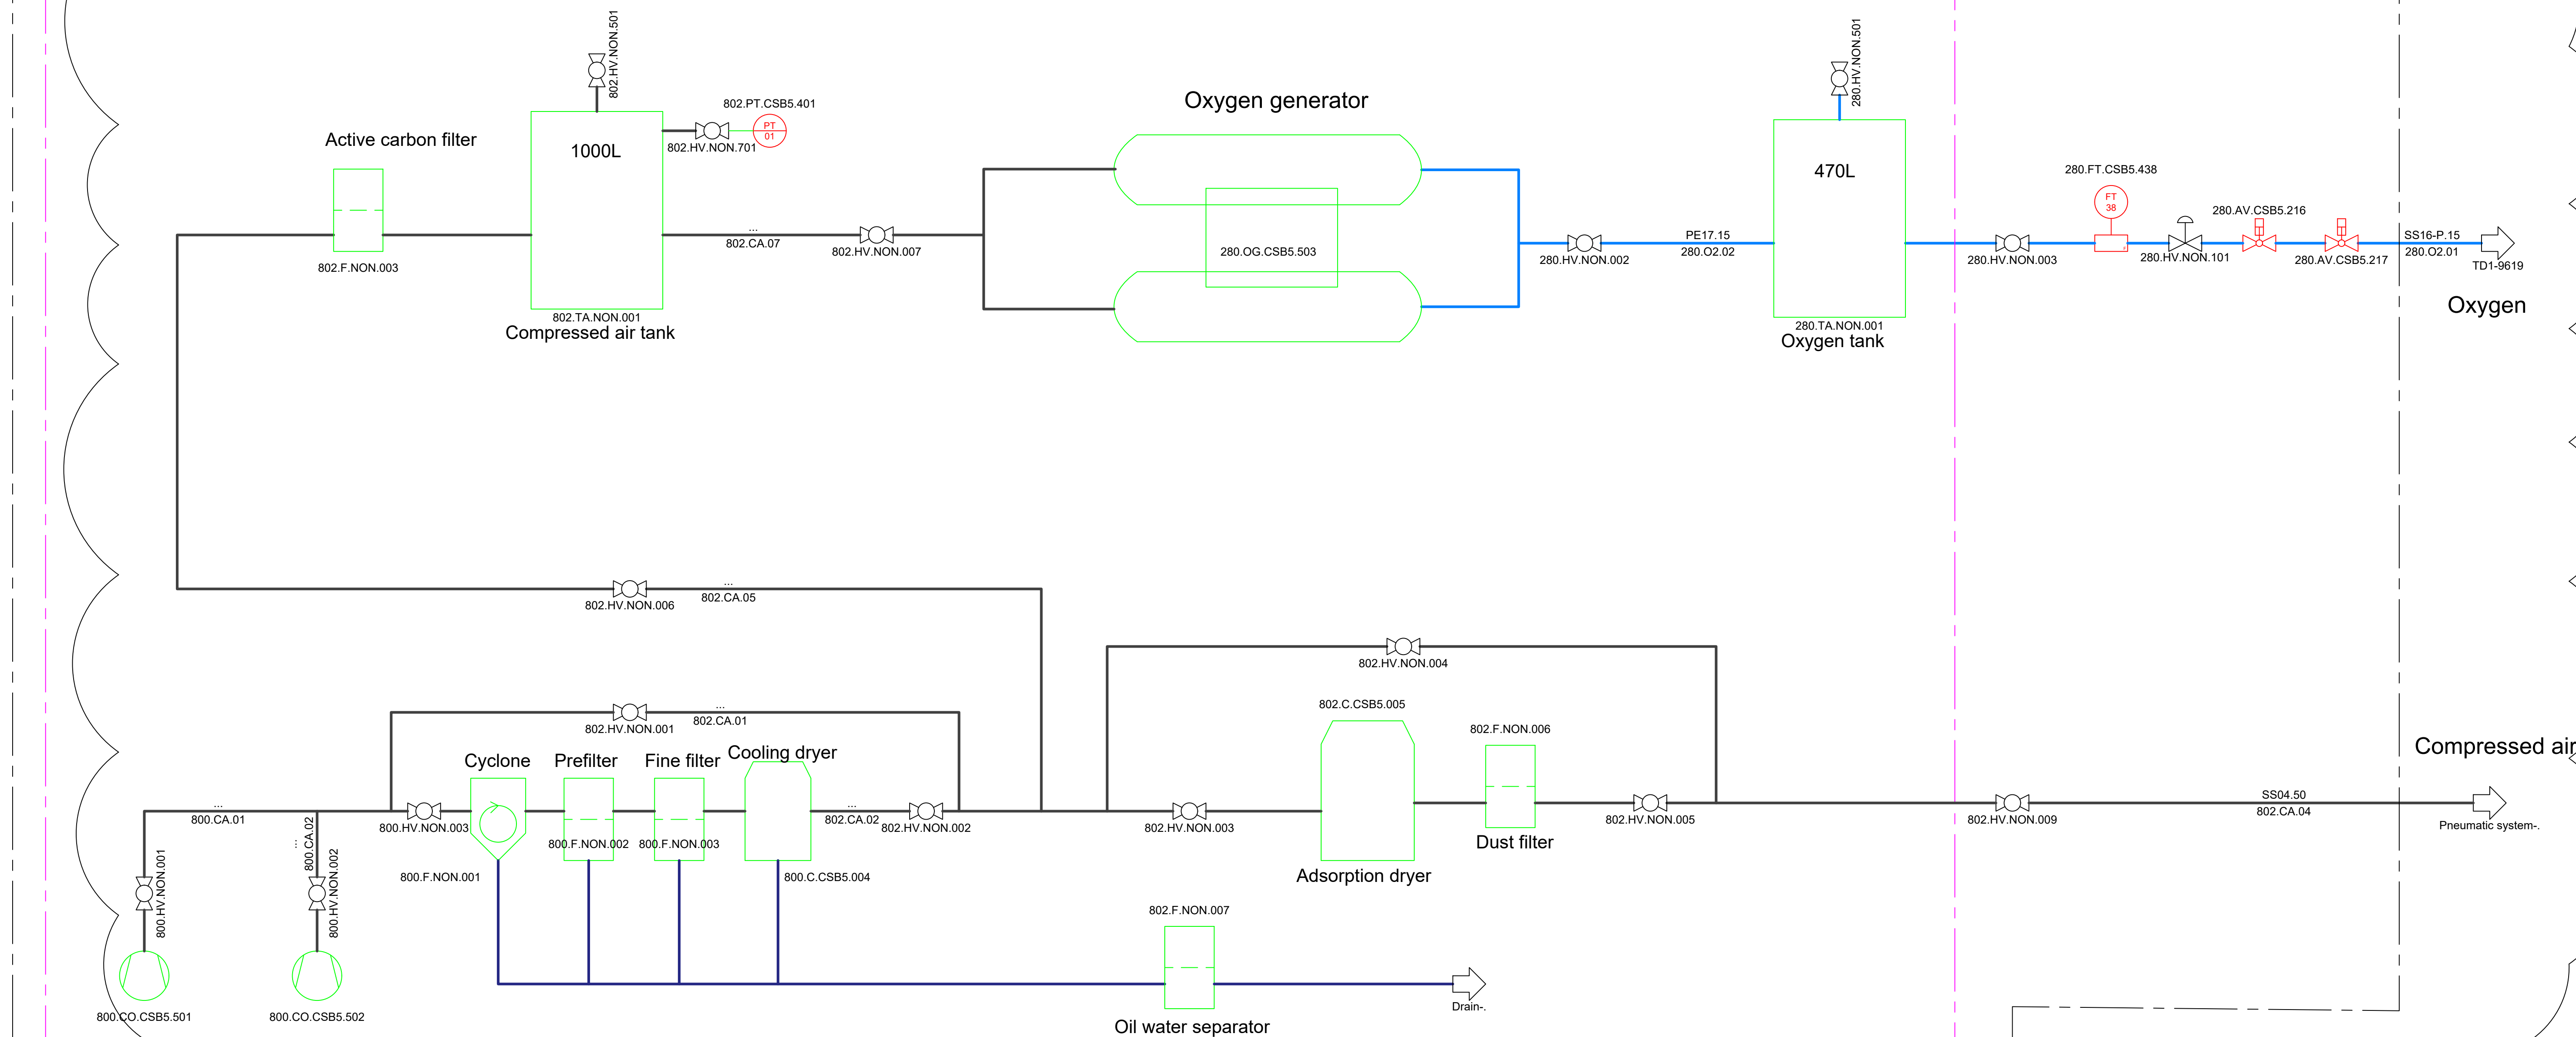

Rev. Nr.:	Rev. Dato:	Rev. Description:
------------------	-------------------	--------------------------

BUILDER:	ST1
Project:	SLK
Subject:	Compressed air & Oxygen
	Rev. 6


Int.: MDC	APP.:	Date: 15-10-2025
------------------	--------------	-------------------------

Lundsbys Renewable Solutions A/S, Hjarbækvej 65, 8831 Legstrup
Tlf.: +45 96 49 43 00 Info@lundsbys.dk
This Drawing is subject to copyright and may not be reproduced without permission from Lundsbys Renewable Solutions A/S

Project nr.1768


Drawing nr.:
9652

FORMAT: A1

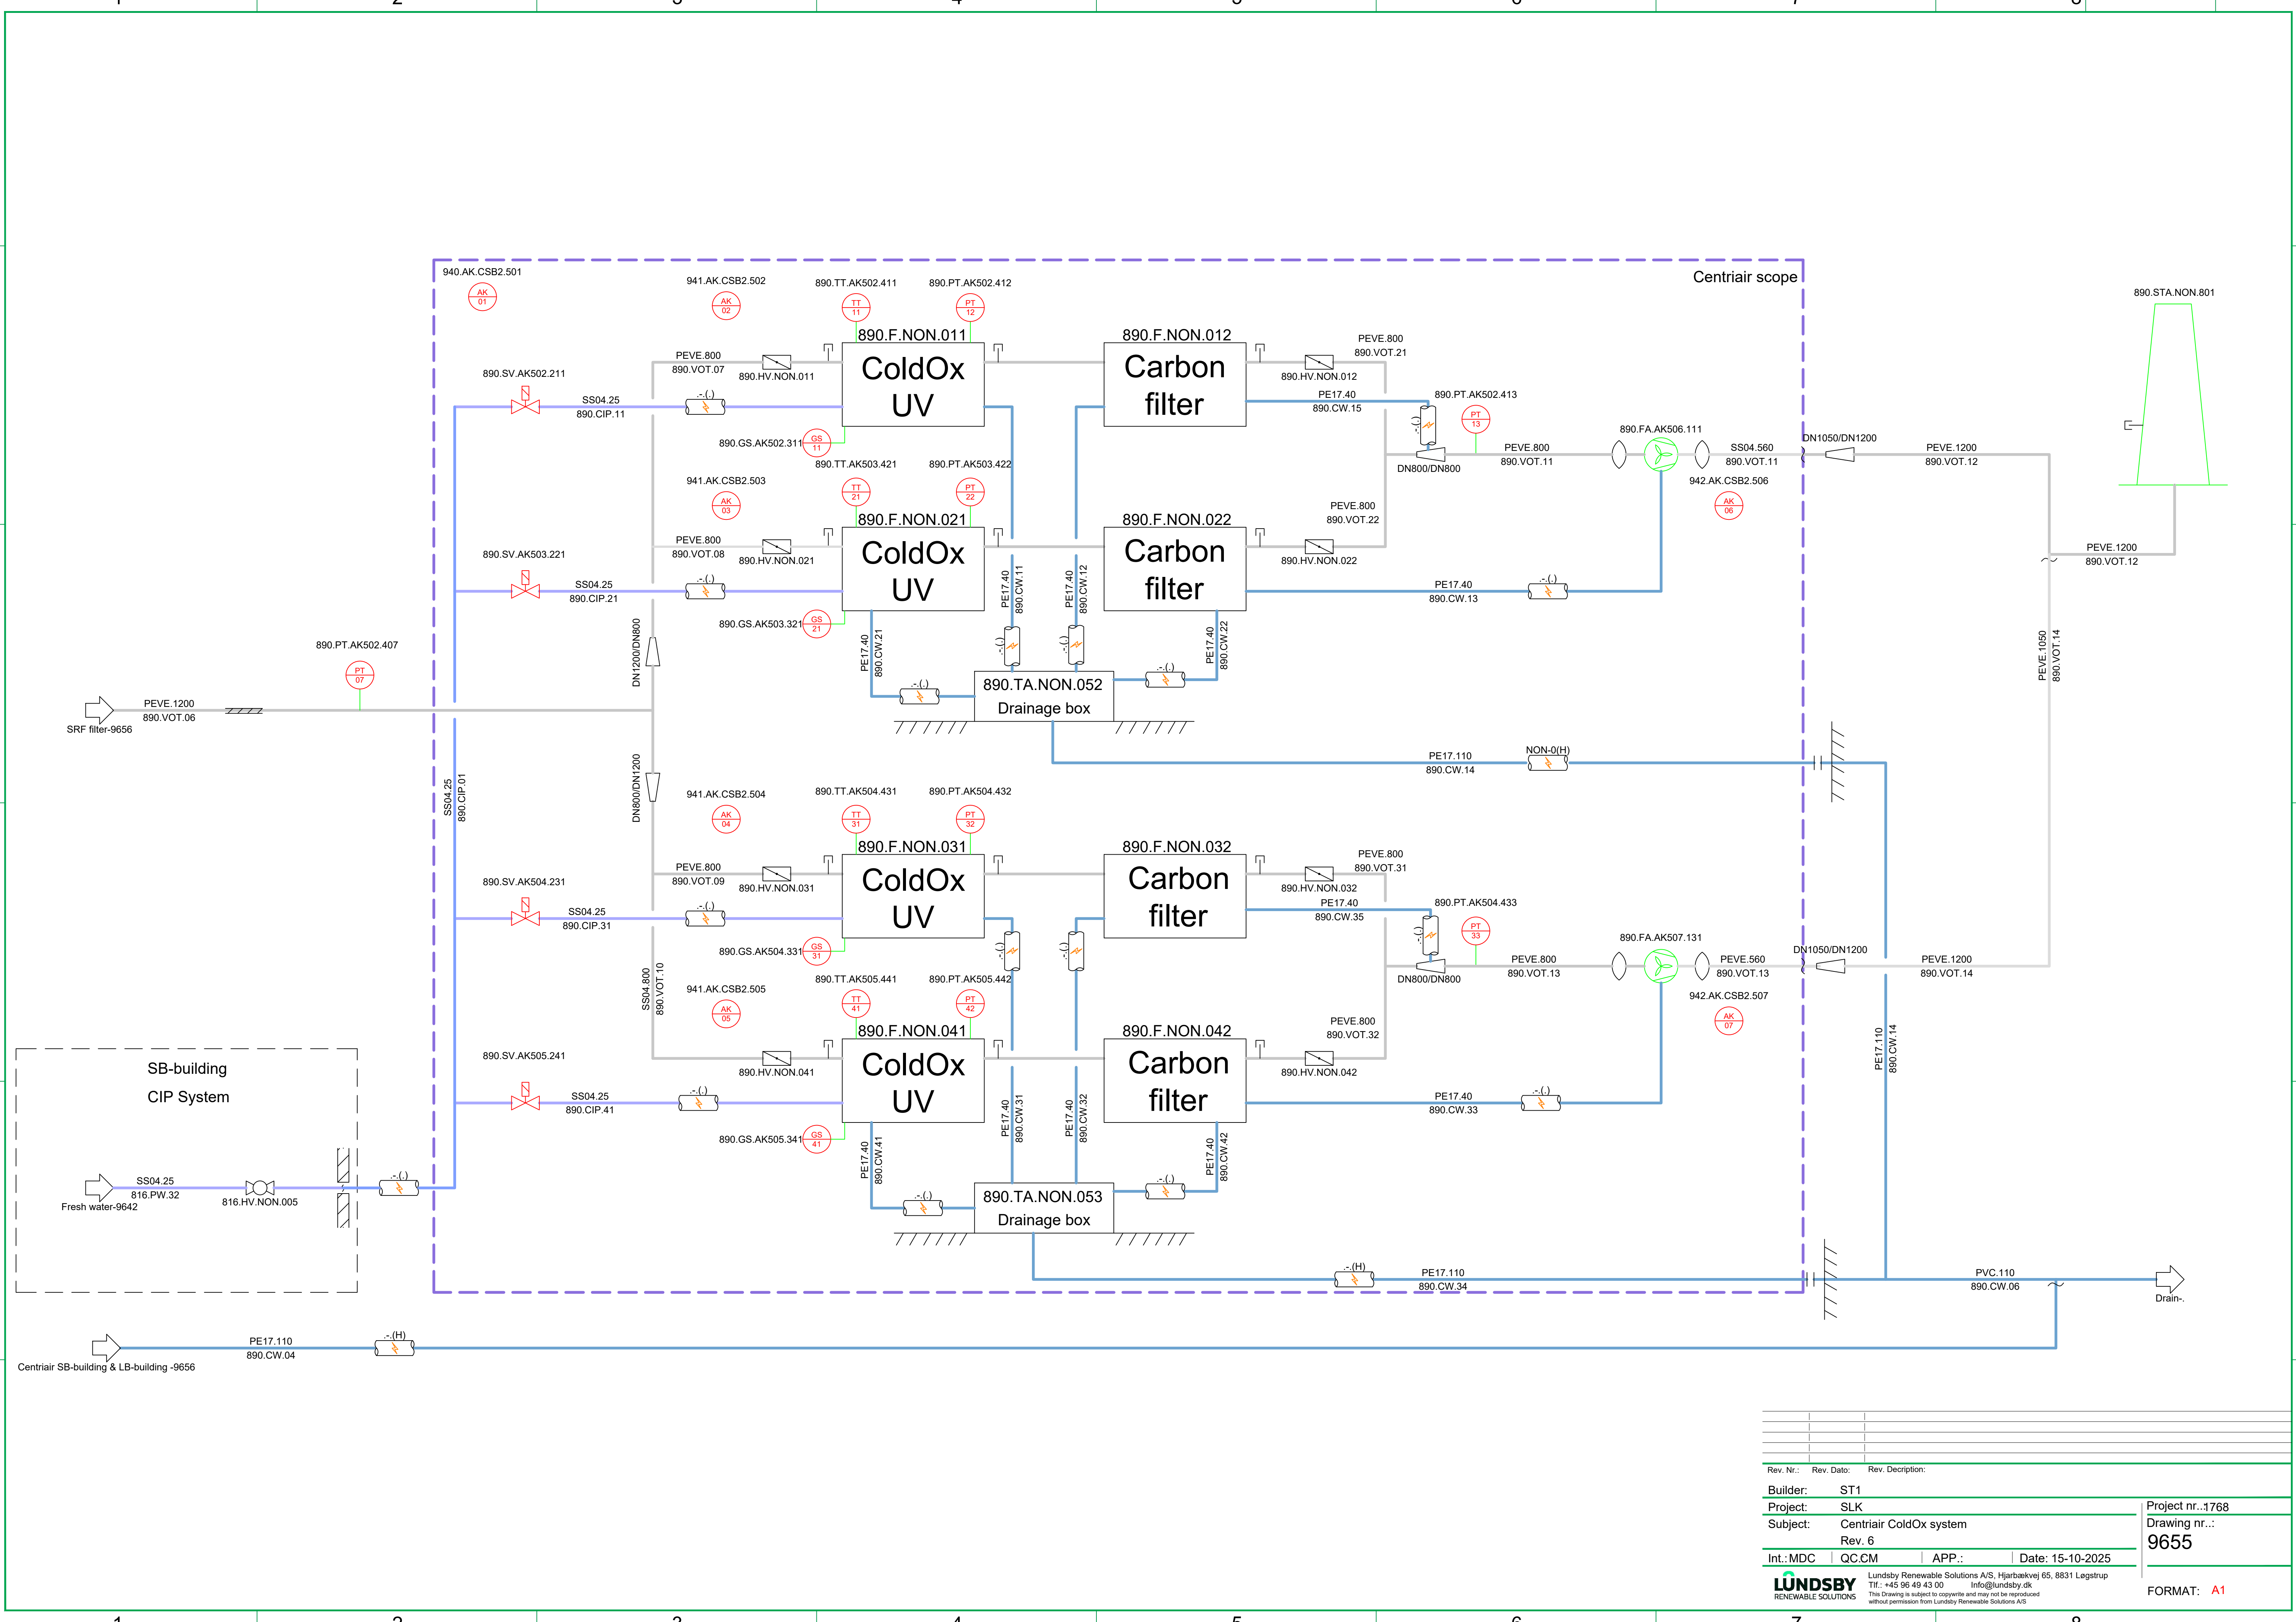


Rev. Nr.:	Rev. Dato:	Rev. Description:
Builder:	ST1	
Project:	SLK	
Subject:	Centriair ColdOx system	
Rev. 6		
Int.:MDC	QC:CM	APP.:Date: 15-10-2025
LUNDSBY RENEWABLE SOLUTIONS		
Lundsby Renewable Solutions A/S, Hjarbækvej 65, 8831 Løgstrup Tlf.: +45 96 49 43 00 info@lundsby.dk This drawing is subject to copyright and may not be reproduced without permission from Lundsby Renewable Solutions A/S		
Project nr.:1768 Drawing nr.: 9655		FORMAT: A1

LB-building

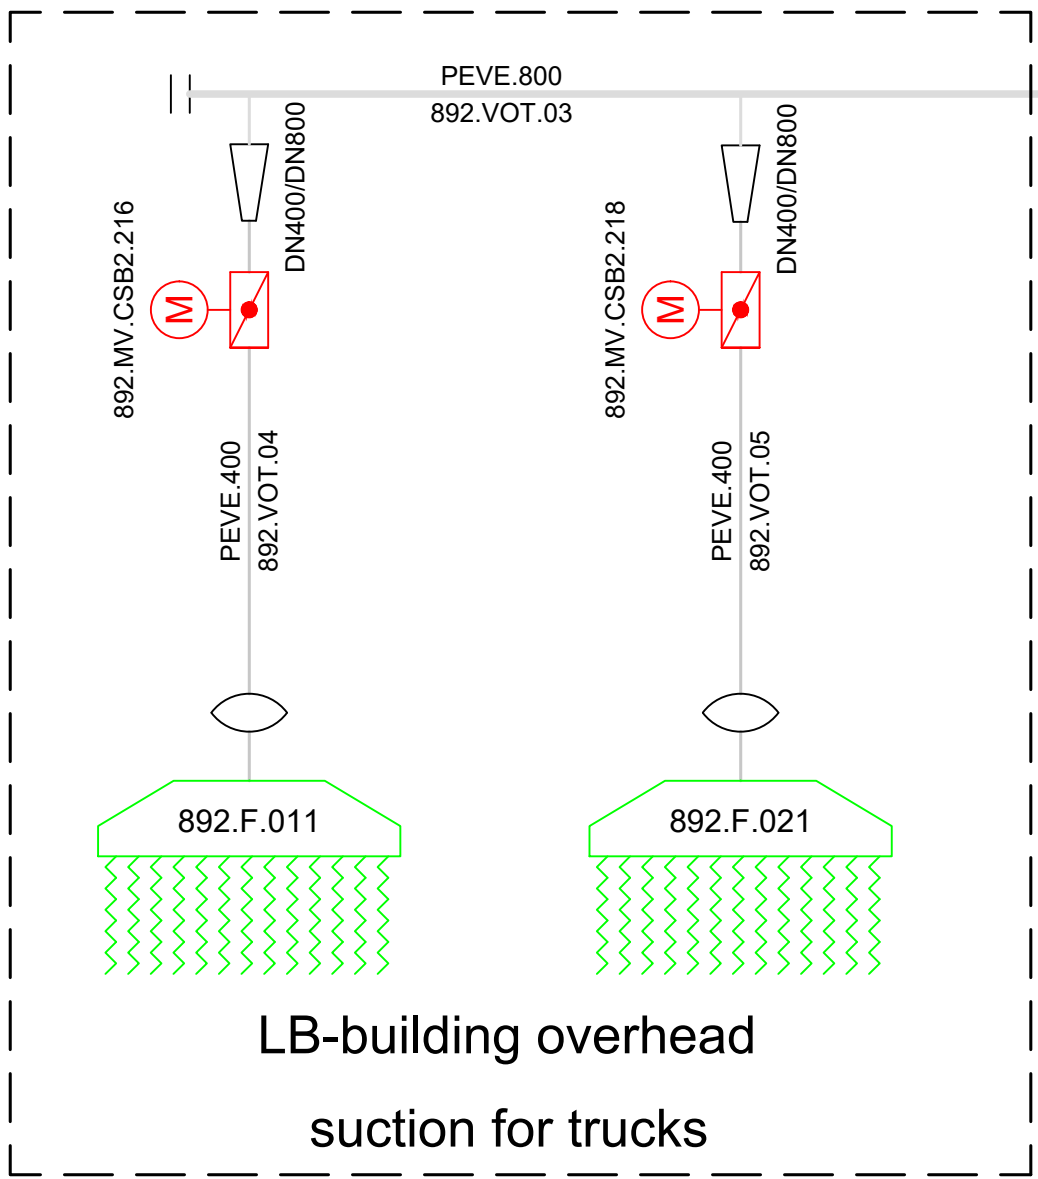


LB-building overhead
suction for trucks



Centriair scope

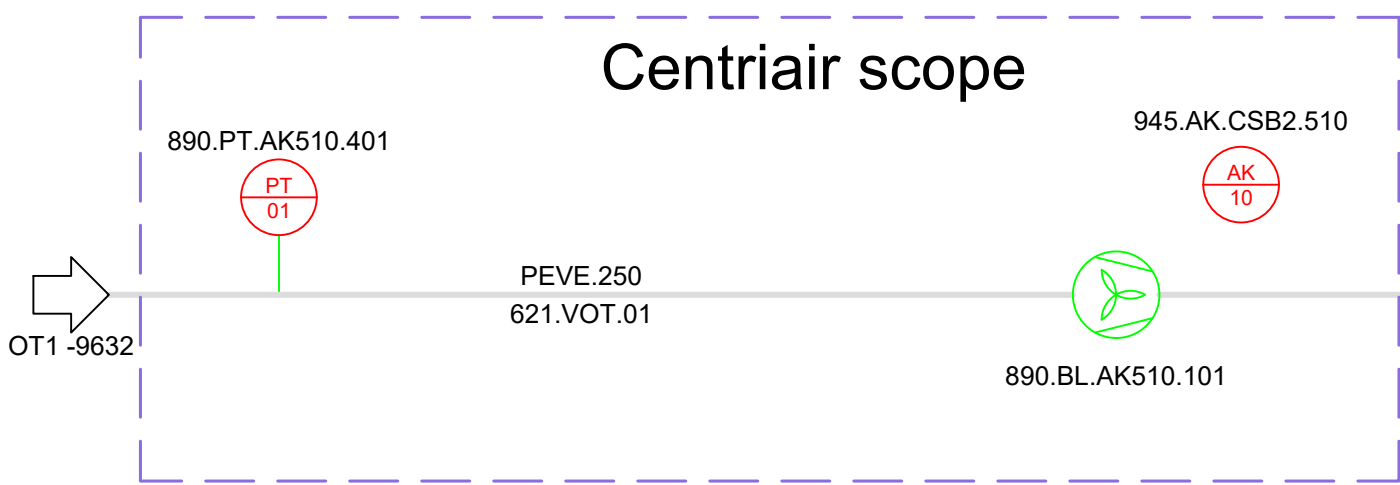


Centriair scope

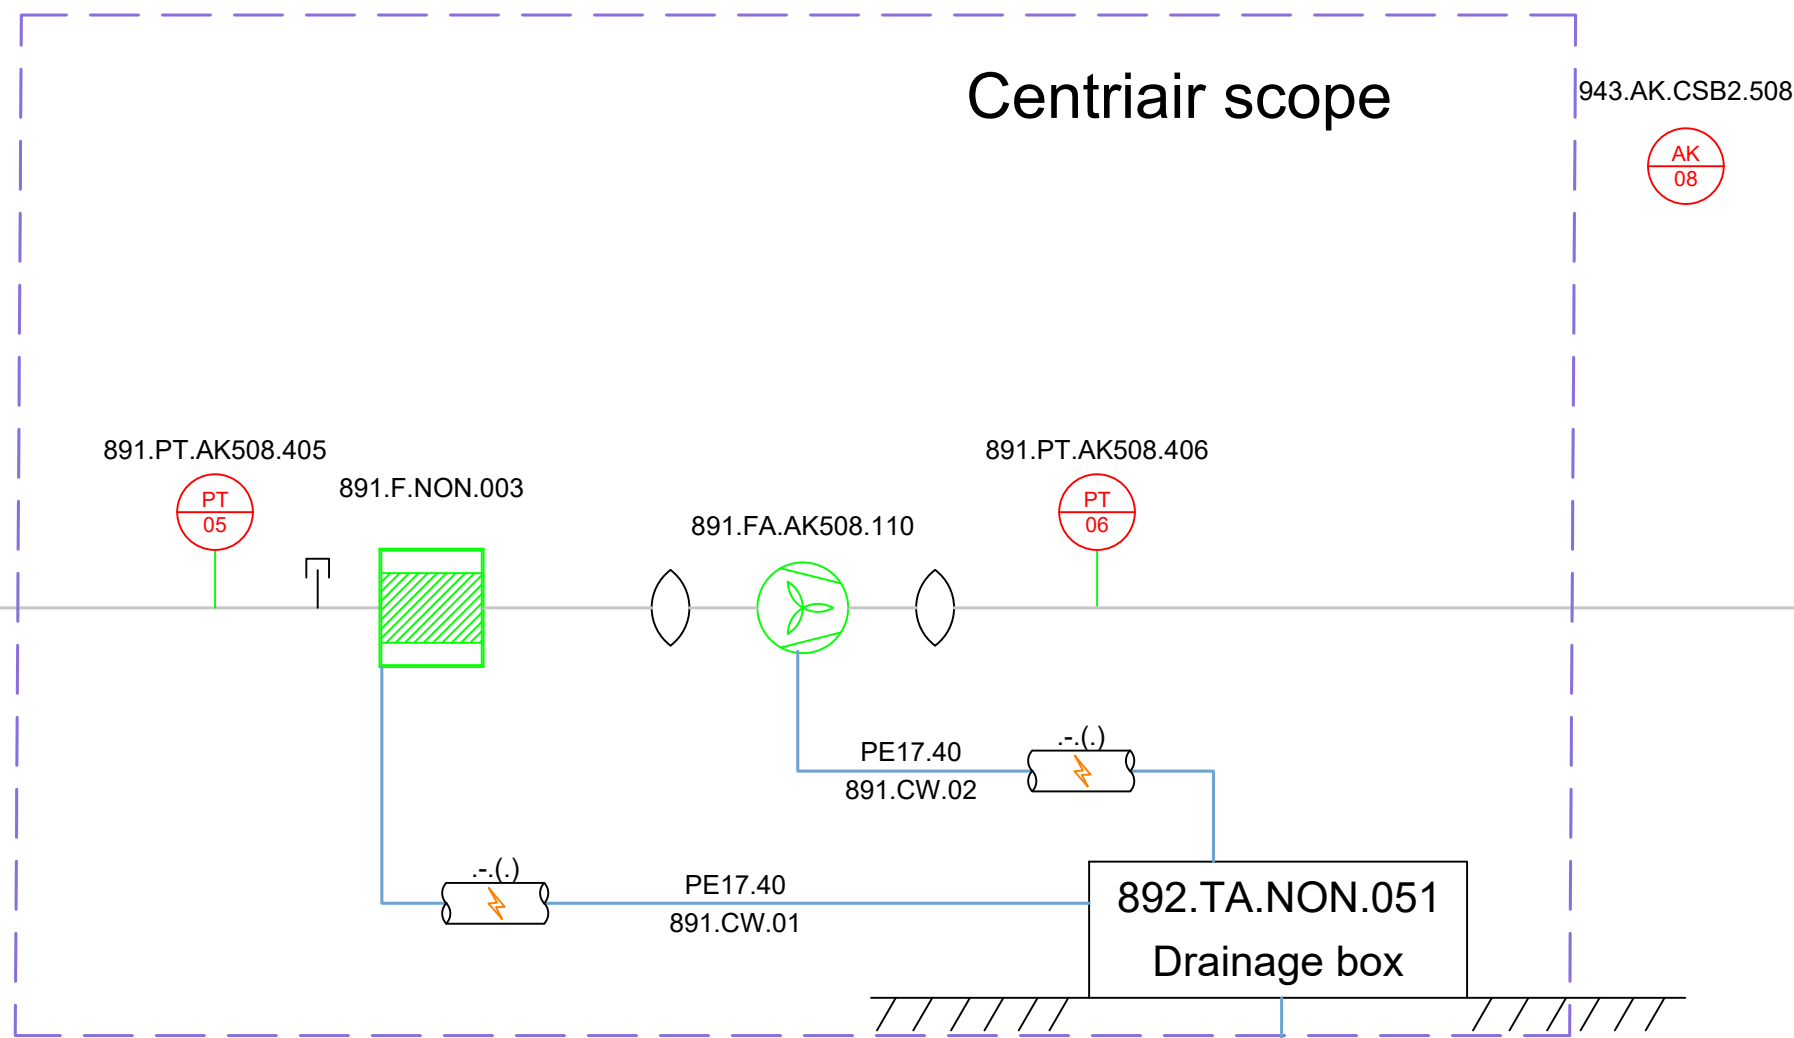

Centriair scope

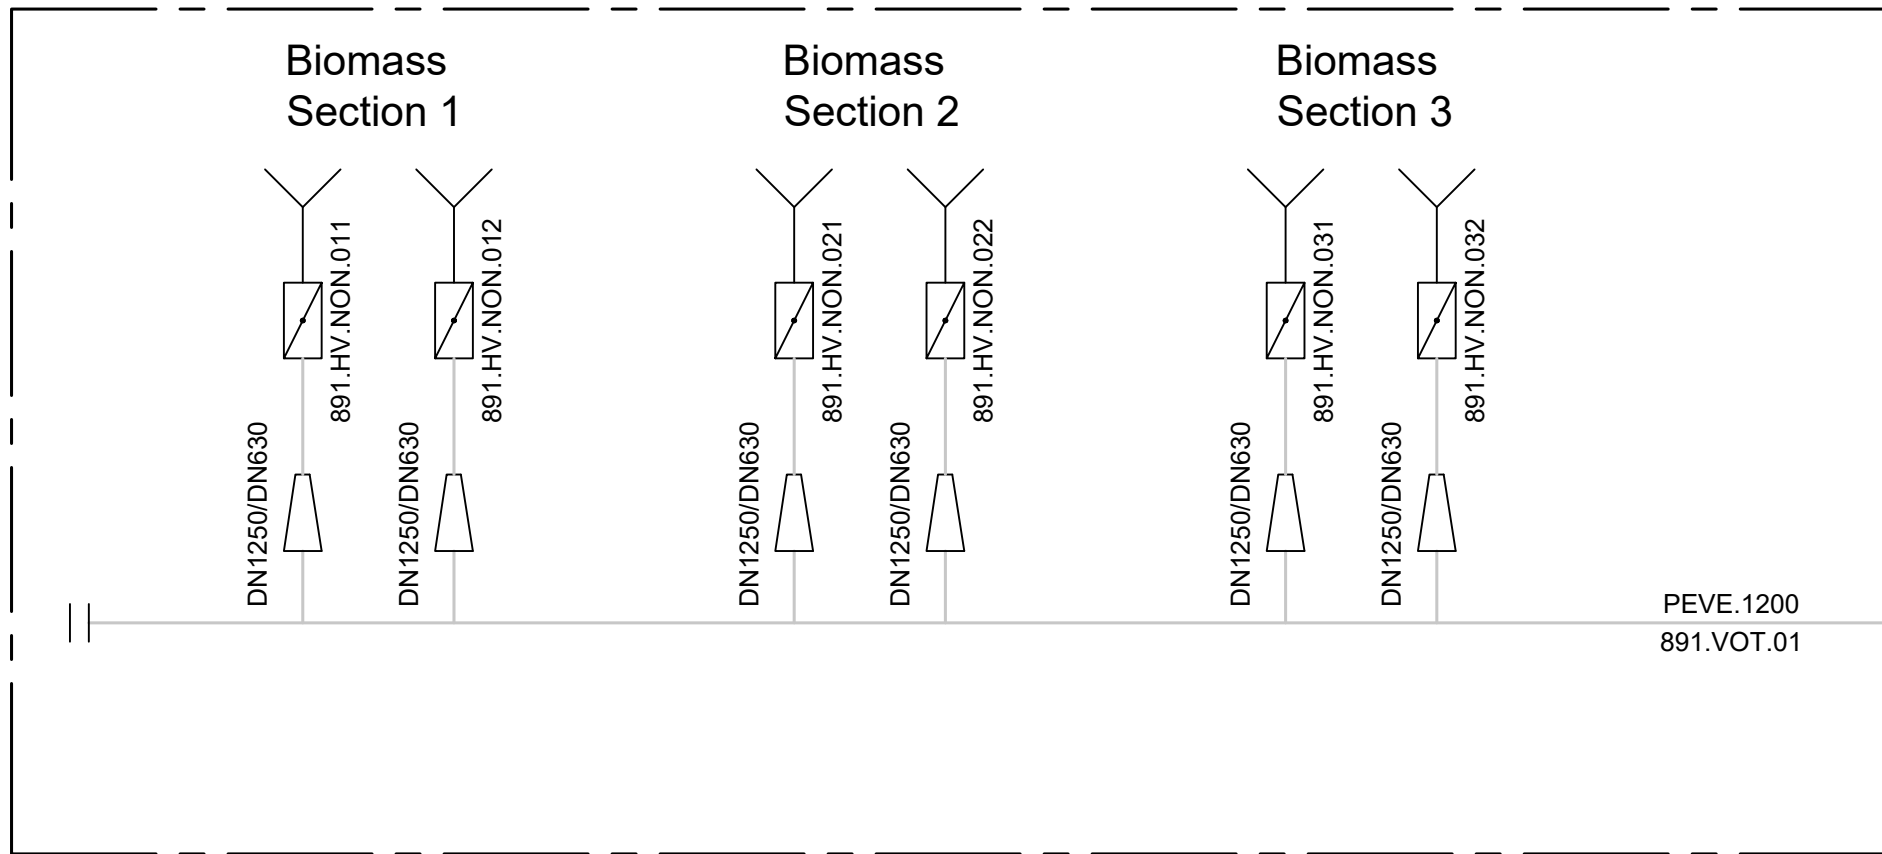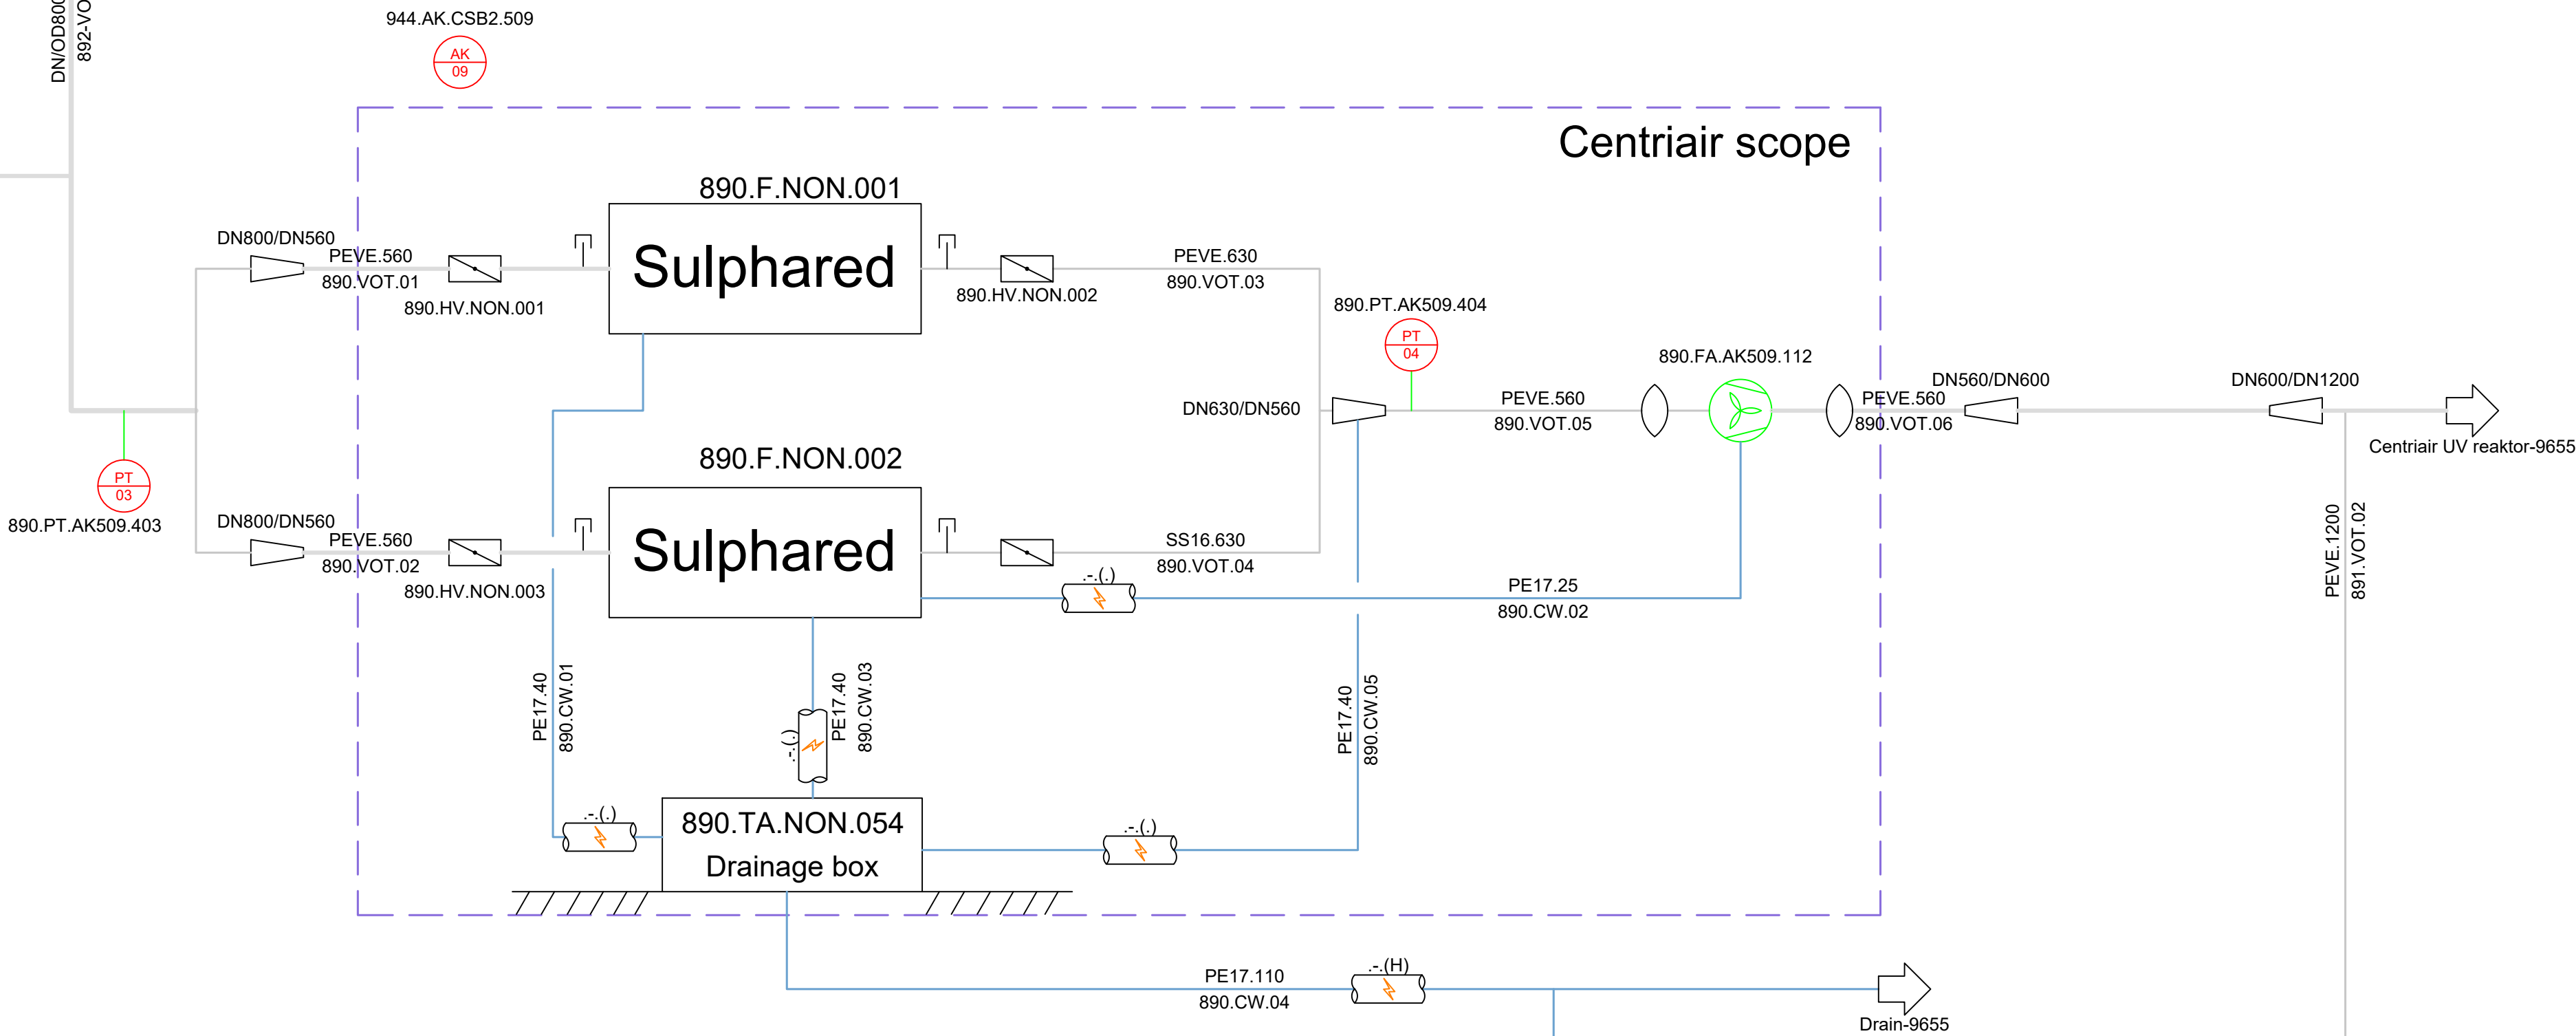

Rev. Nr.:	Rev. Dato:	Rev. Description:
Builder:	ST1	
Project:	SLK	
Subject:	Centriair SB-building & LB-building	
Rev. 6		
Int.:MDC	QC.CM	APP.:
Date: 15-10-2025		
LUNDSBY RENEWABLE SOLUTIONS		
Lundsby Renewable Solutions A/S, Hjarbækvej 65, 8831 Lægstrup Tlf.: +45 96 49 43 00 Info@lundsby.dk This Drawing is subject to copyright and may not be reproduced without permission from Lundsby Renewable Solutions A/S		
Project nr.:1768 Drawing nr.: 9656		FORMAT: A1

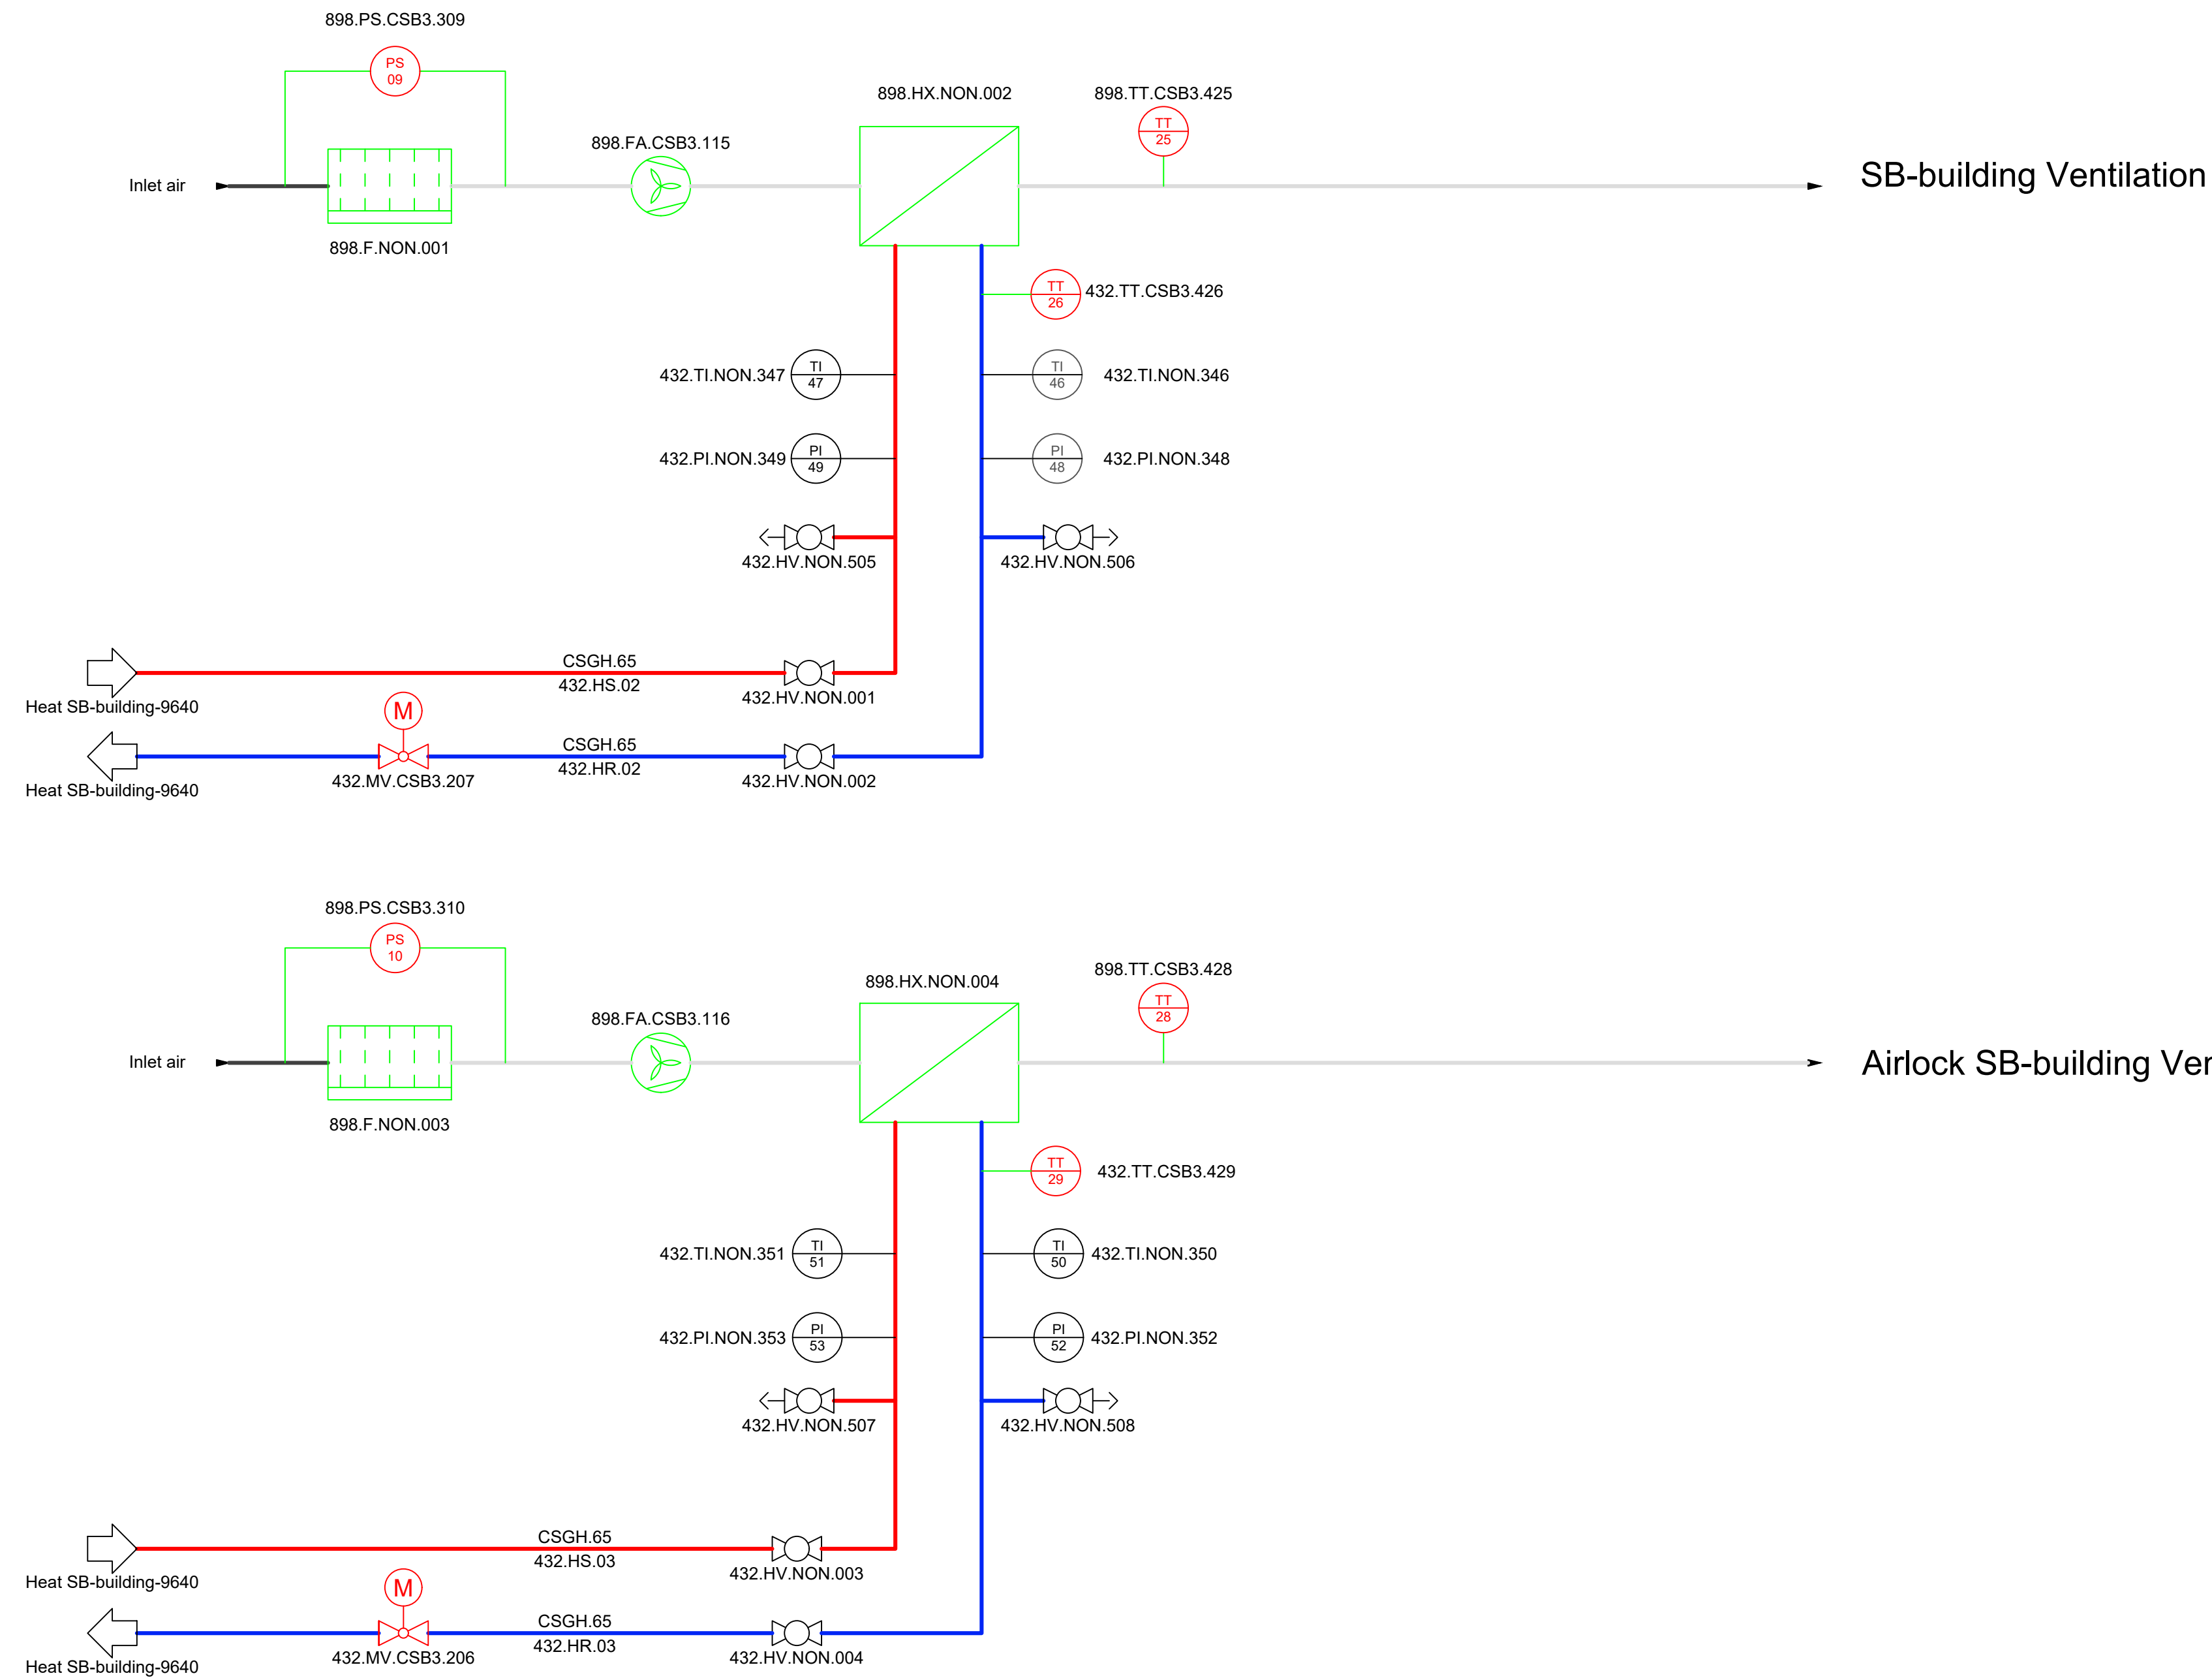

Rev. Nr.:	Rev. Dato:	Rev. Description:	Project nr...: 1768
Builder:	ST1		Drawing nr...: 9657
Project:	SLK		
Subject:	Ventilation SB-building		
Rev. 6			
Int.:MDC	QC.: CM	APP.:	Date: 15-10-2025
LUNDSBY RENEWABLE SOLUTIONS			FORMAT: A1