




Structure of the tagging system

Structure of the component tagging

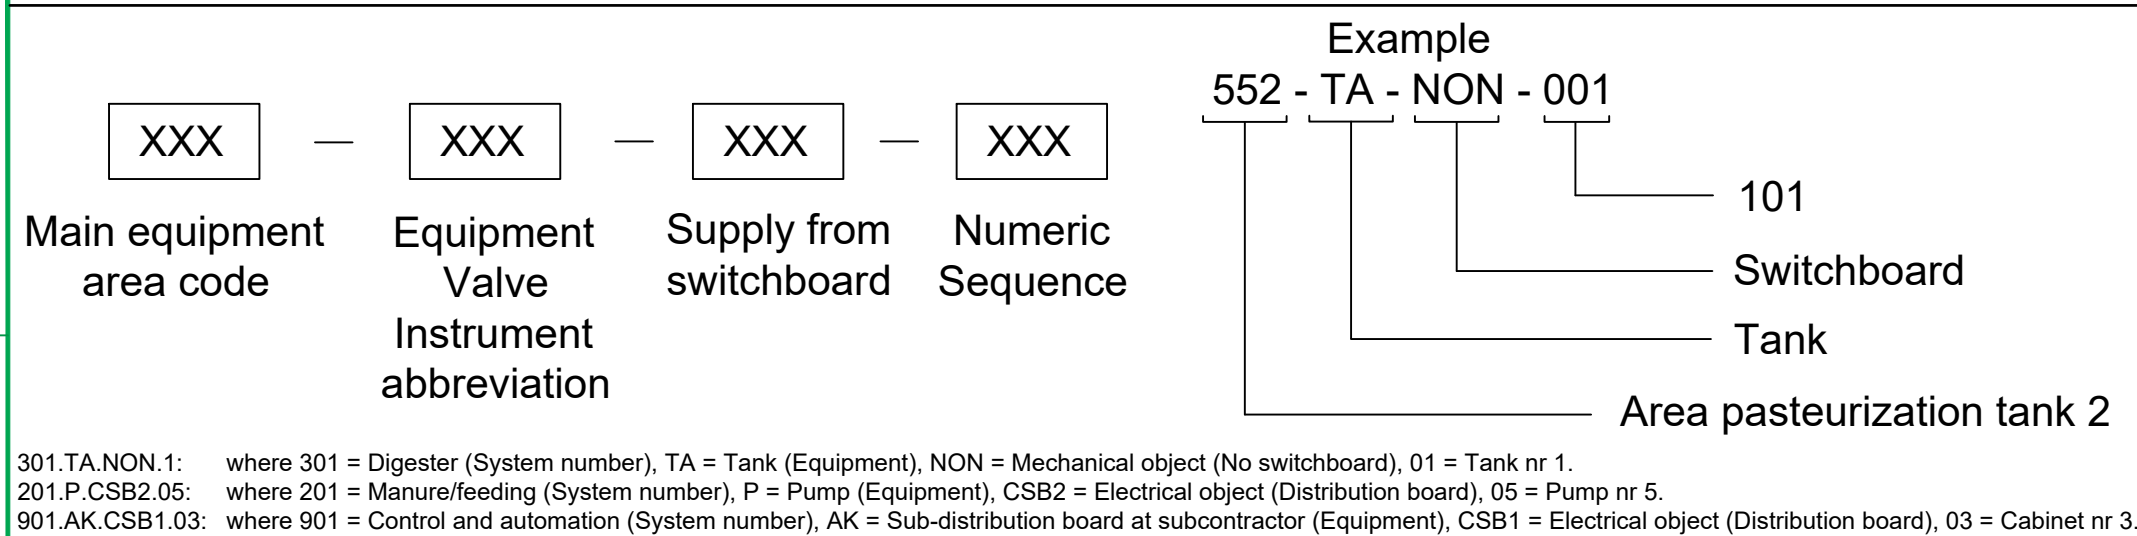

301.TA.NON.1: where 301 = Digester (System number), TA = Tank (Equipment), NON = Mechanical object (No switchboard), 01 = Tank nr 1.
201.P.CSB2.05: where 201 = Manure/feeding (System number), P = Pump (Equipment), CSB2 = Electrical object (Distribution board), 05 = Pump nr 5.
901.AK.CSB1.03: where 901 = Control and automation (System number), AK = Sub-distribution board at subcontractor (Equipment), CSB1 = Electrical object (Distribution board), 03 = Cabinet nr 3.

Lines

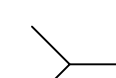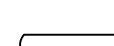Description	Symbol
Subcontractor scope	
Boundary line	
Page connector	
Start pipe - Not linked to page	
End pipe - Not linked to page	
Fald/ Slope	
Insulation	
Electrical Heat tracing	

Building/Area/Tank


Description	Code
Primary digester	PD
Secondary digester	SD
Digester storage	DST
Liquid manure tank	LMT
Liquid biomass tank	LBT
Outlet tank	OT
Blackwater tank	BWT
Tech building	TB
Admin building	ADB
Solid biomass building	SBB
Liquid biomass building	LBB
Plansilo	PS
Pump house	PH
Hygienization tanks	HYG
Flare	FLA
Stack	STA
Odour treatment facility	OD
Upgrade facility	UPG
Liquifaction facility	LIQ
Oil boiler	OB
Wood boiler	WB
Transformer	TR

Media code

Media	Pipe color	RBG color	Code
Heat Return		0,37,245	HR
Heat Supply		255,0,0	HS
Heat Hot Return		255,223,127	HHR
Heat Hot Supply		238,129,129	HHS
Cooling Supply		0,255,183	CS
Cooling Return		126,189,189	CR
Black Water		36,39,132	BW
CIP		253,53,223	CIP
Process Water		170,170,255	PW
Technical Water		69,78,104	TW
Drinking Water		0,0,129	DW
Drinking Water Hot		0,127,255	DWH
Condensate		108,163,208	CW
Steam		255,82,82	ST
Steam Condensate		189,0,0	STC
Liquid Manure (Slurry)		240,130,40	LM
Liquid Biomass (Substrat)		128,0,255	LB
Process Biomass		165,103,82	PB
Hygienized Biomass		169,130,0	HB
Recirculated Biomass		165,103,82	RCB
Ferric Chloride FeCl		145,255,71	FeCl
Ventilation Odour Treatment		199,199,199	VOT
Ventilation Fresh Air		199,199,199	VFA
Compressed Air		64,64,64	CA
Oxygen		0,128,255	O2
Raw Biogas		255,255,0	RB
Return/reject Gas		116,118,4	RG
Nature Gas		0,255,127	NG
Instrument Leader		Green	N/A

Structure of the pipeline tagging system

The pipetag consists of various information about the pipe
Full pipeline tag as shown below

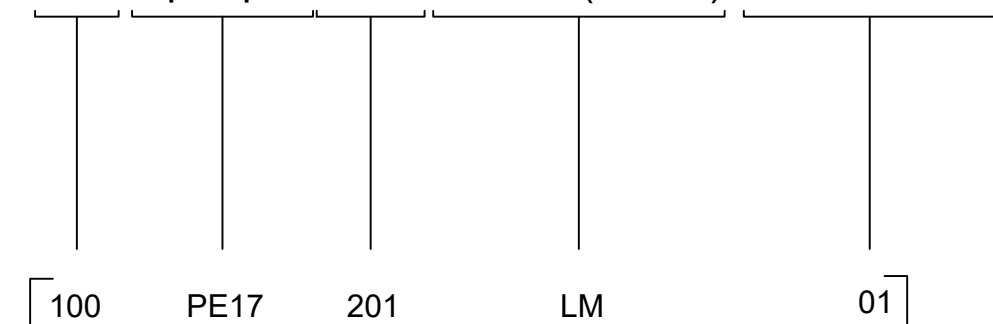

Example

Two (2) digits. Starts with 01
[01]

- Two (2) to four (4) characters (letters)
- [LM - Liquid manure]

Three (3) digits
[201 - Manure feeding in tank 1]

Pipe Spec name
[PE17 - PE100 SDR17]

Pipe size
DN indication for Metric pipes
OD indication for PE-pipe
[This example is OD 100 mm]

The pipe tag will be shown on the P&ID as follows: PipeSpec-Size
Area-Service-Serialnumber

Example of line tag notation on P&ID: PE17-110
201-LM-01

Line color corresponding to table above.
The part below the pipeline is the Unique Line Tag.
Unique Line Tag is generated automatically when creating complete Line Tag.
Unique Line Tag is used by the P3D system when designing pipes in the 3D model and when generating Isometrics.

Rev. Nr.:	Rev. Dato:	Rev. Description:
Builder:	ST1	
Project:	SLK	
Subject:	PID Legend	
	Rev. 6	
Int.: MDC	QC.: CM	APP.: Date: 15-10-2025



Lundbys
 RENEWABLE SOLUTIONS

Lundsby Renewable Solutions A/S, Hjarbækvej 65, 8831 Lægstrup
 Tlf.: +45 96 49 43 00 Info@lundbsby.dk
This Drawing is subject to copyright and may not be reproduced
 without permission from Lundsby Renewable Solutions A/S

Project nr.: 1768
 Drawing nr.:
PID Legend

FORMAT: **A1**

1	2	3	4	5	6	7	8																								
Valves		Equipment			Piping	Instruments																									
Hand valves		Pumps / Compressors / Blowers		Equipment	Piping symbols		Description																								
Symbols	Code	Description	Symbols	Code	Description	Symbols	Code	Description																							
	HV	General valve		P	Pump (General)		N/A	Offpage connector																							
	HV	Ball valve		P	Positive displacement pump		N/A	Flange connection																							
	HV	Butterfly valve		P	Helical rotor pump		N/A	Blind flange																							
	HV	Globe valve		P	Centrifugal pump		NO	Truck nozzle																							
	HV	Three way valve		P	Peristaltic pump		NO	Funnel/Drain																							
	HV	Ground covered valve		MC	Rotacut		AS	Expansion joint																							
	BV	Balancing valve		MC	Shredder		SN	Strainer																							
Actuated valves / Regulating valves		Heating and Cooling		<table><tr><th>Category</th><th>Numbers</th></tr><tr><td>Manual valves</td><td>001-099</td></tr><tr><td>Manual regulation valves</td><td>101-199</td></tr><tr><td>Pneumatic, electrical, solenoid</td><td>201-299</td></tr><tr><td>-</td><td>301-399</td></tr><tr><td>Check, Non-return valves</td><td>401-499</td></tr><tr><td>Drain, venting valves</td><td>501-599</td></tr><tr><td>Self-regulating valves (thermal/liquid)</td><td>601-699</td></tr><tr><td>Instrument valves</td><td>701-799</td></tr><tr><td>-</td><td>801-899</td></tr><tr><td>Safety valves</td><td>901-999</td></tr></table>		Category	Numbers	Manual valves	001-099	Manual regulation valves	101-199	Pneumatic, electrical, solenoid	201-299	-	301-399	Check, Non-return valves	401-499	Drain, venting valves	501-599	Self-regulating valves (thermal/liquid)	601-699	Instrument valves	701-799	-	801-899	Safety valves	901-999	Symbols		Code	Description
Category	Numbers																														
Manual valves	001-099																														
Manual regulation valves	101-199																														
Pneumatic, electrical, solenoid	201-299																														
-	301-399																														
Check, Non-return valves	401-499																														
Drain, venting valves	501-599																														
Self-regulating valves (thermal/liquid)	601-699																														
Instrument valves	701-799																														
-	801-899																														
Safety valves	901-999																														
	MV/RV	Motor ball valve		HX	Heat exchanger - Shell & tube		AJ	Concentric reducer																							
	MV/RV	Motor butterfly valve		HX	Heat exchanger - plate		AJ	Eccentric reducer																							
	AV/RV	Pneumatic ball valve		HX	Heat exchanger - double pipe		AX	Sample point																							
	AV/RV	Pneumatic valve		HX	Heating coil (in tank)		BS	Inline silencer																							
	AV	Solenoid valve		HS	Heatpump		BU	Electrical heat tracing																							
Safety valves		Tank equipment		Tanks			N/A	Going into the ground / Coming up from																							
	SV	Exhaust valve covers		AG	ISO Agitator - Propeller		DT	Digester tank																							
	SV	Safety valve		AG	Agitator		ST	Storage tank																							
	SV	Breather valve		LA	Light		DT/ST	Storage tank with cover																							
Mechanical valves		Filters and Vessels		HT		Gas/Hyginisation tank																									
	PV	Pressure holding valve		AT	General filter / Forfilter	Revision clouds																									
	CV	Check valve		AT	General liquid																										
	VV	Venting valve		AT	Drier - General																										
Miscellaneous additional valve symbols			F	Suction hood																											
		Operator lock mechanism		EXP	Expansion tank																										
Equipment		Tanks		Buried tank																											
	MX	Bio mixer		DT	Digester tank																										
	MC	Premix		ST	Storage tank																										
	CV	Debris lift unit		DT/ST	Storage tank with cover																										
	CV	Screw conveyor		HT	Gas/Hyginisation tank																										
	CV	Belt conveyor		TA	Buried tank																										
	CRA	Crane																													
	CH	ISO Stack - Chimney																													
	FL	Flare																													
	PD	Pulsation damper																													
	SP	Screw press																													

XXX

Main area code

XX

Letter code

XXX

Switchboard

XXX

Numeric sequence

First letter

XX

Succeeding letter

XX

Numeric sequence

Description

Field instrument

Instrument with connection to control

Example

T1

01

Temperature indication

LS

02

Level switch

Instruments will be tagged

Instruments with succeeding letter T is an analog signal.

Instruments with succeeding letter S is a digital signal.

Instruments	Abbreviation
Analyze Indicator	AI
Analyse Transmitter	AT
Energi Transmitter	ET
Flow Indicator	FI
Flow Transmitter	FT
Flow Switch	FS
Flow Transmitter	FT
General Switch	GS
Level Switch	LS
Level Indicator	LI
Level Transmitter	LT
Pressure Indicator	PI
Pressure Switch	PS
Pressure Transmitter	PT
Thermometer	TI
Temperature Transmitter	TT
Weight Transmitter	WT

Various instruments		
	FT	Flow transmitter
	EM	Energy meter
	SI	Siren
	M	Electric motor
	AK	Units with own switchboard
	K	Control box

Rev. Nr.:

Rev. Dato:

Rev. Beskrivelse:

Builder: ST1

Project: SLK

Subject: PID legend 2

Rev. 6

Int.:MDC

QC: CM

APP.:

Date: 15-10-2025

LUNDSBY

RENEWABLE SOLUTIONS

Lundsby Biogas A/S, Hjarbækvej 65, 8831 Løgstrup

Tlf.: +45 96 49 43 00

Info@lundsbybiogas.dk


Denne tegning er underlagt copyright op må ikke reproduceres uden tilladelse fra


Lundsbybiogas A/S

Project nr.: 1768


Drawing nr.: PID legend 2

FORMAT: A1

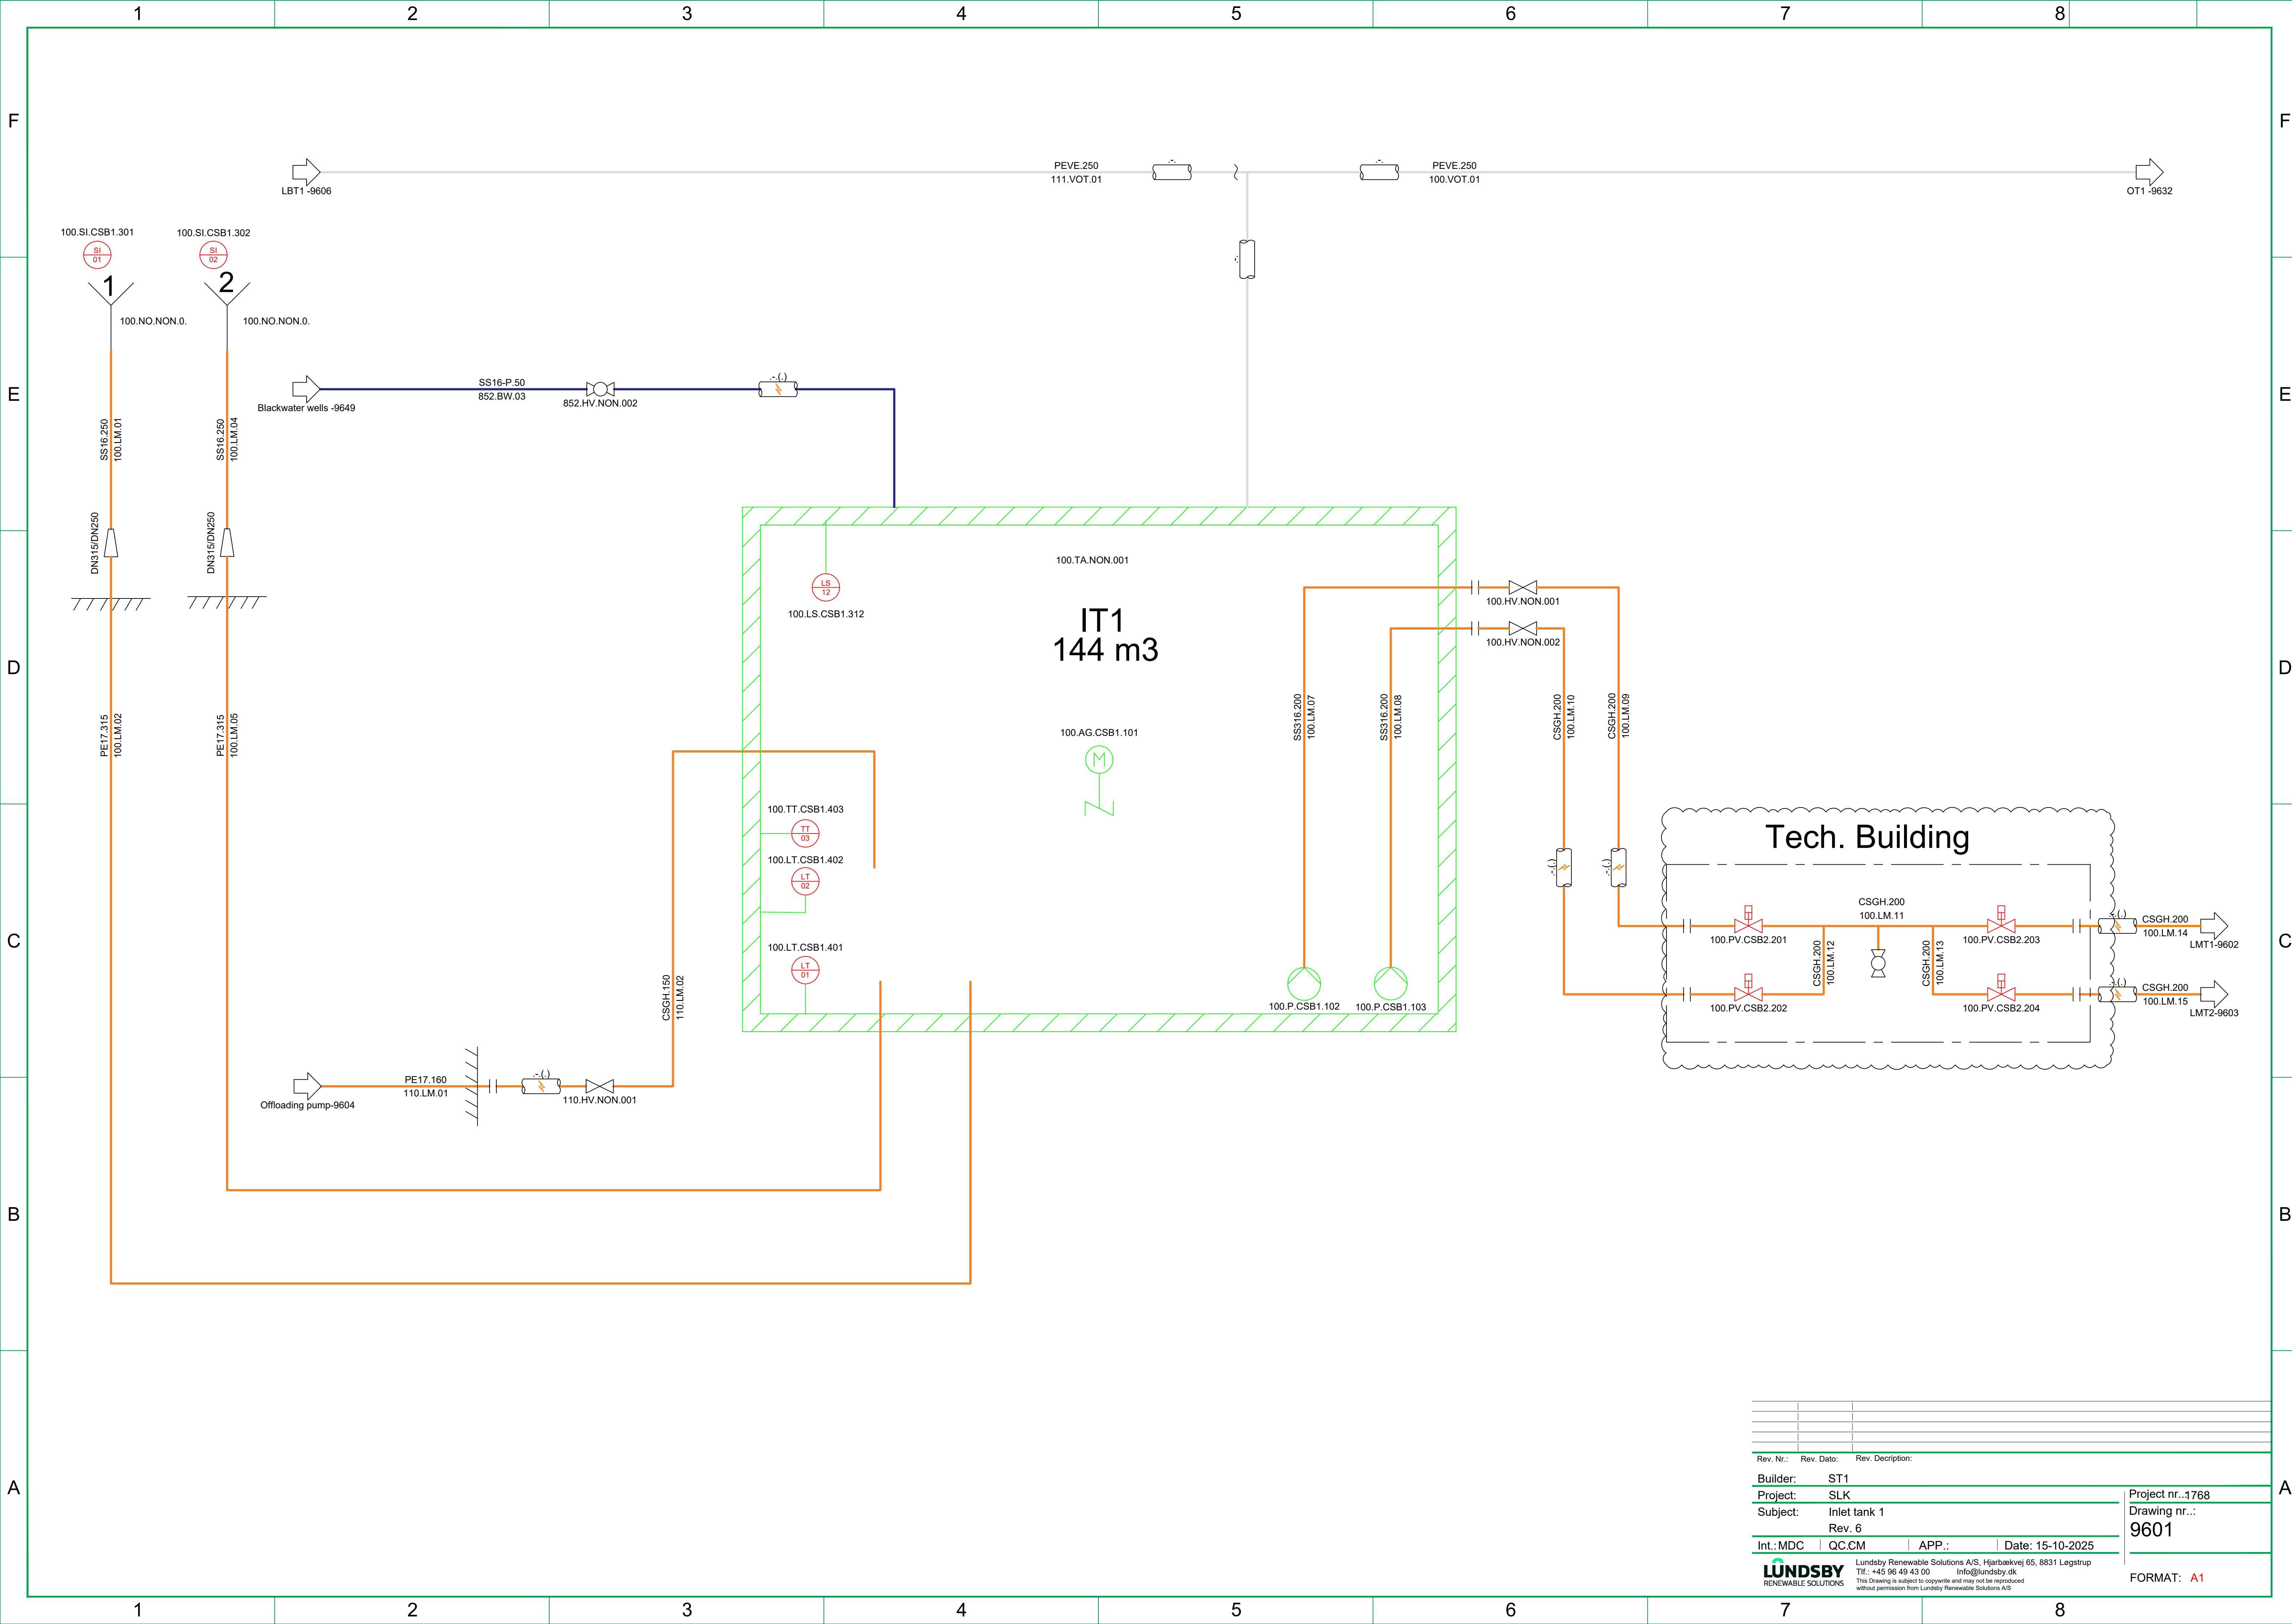


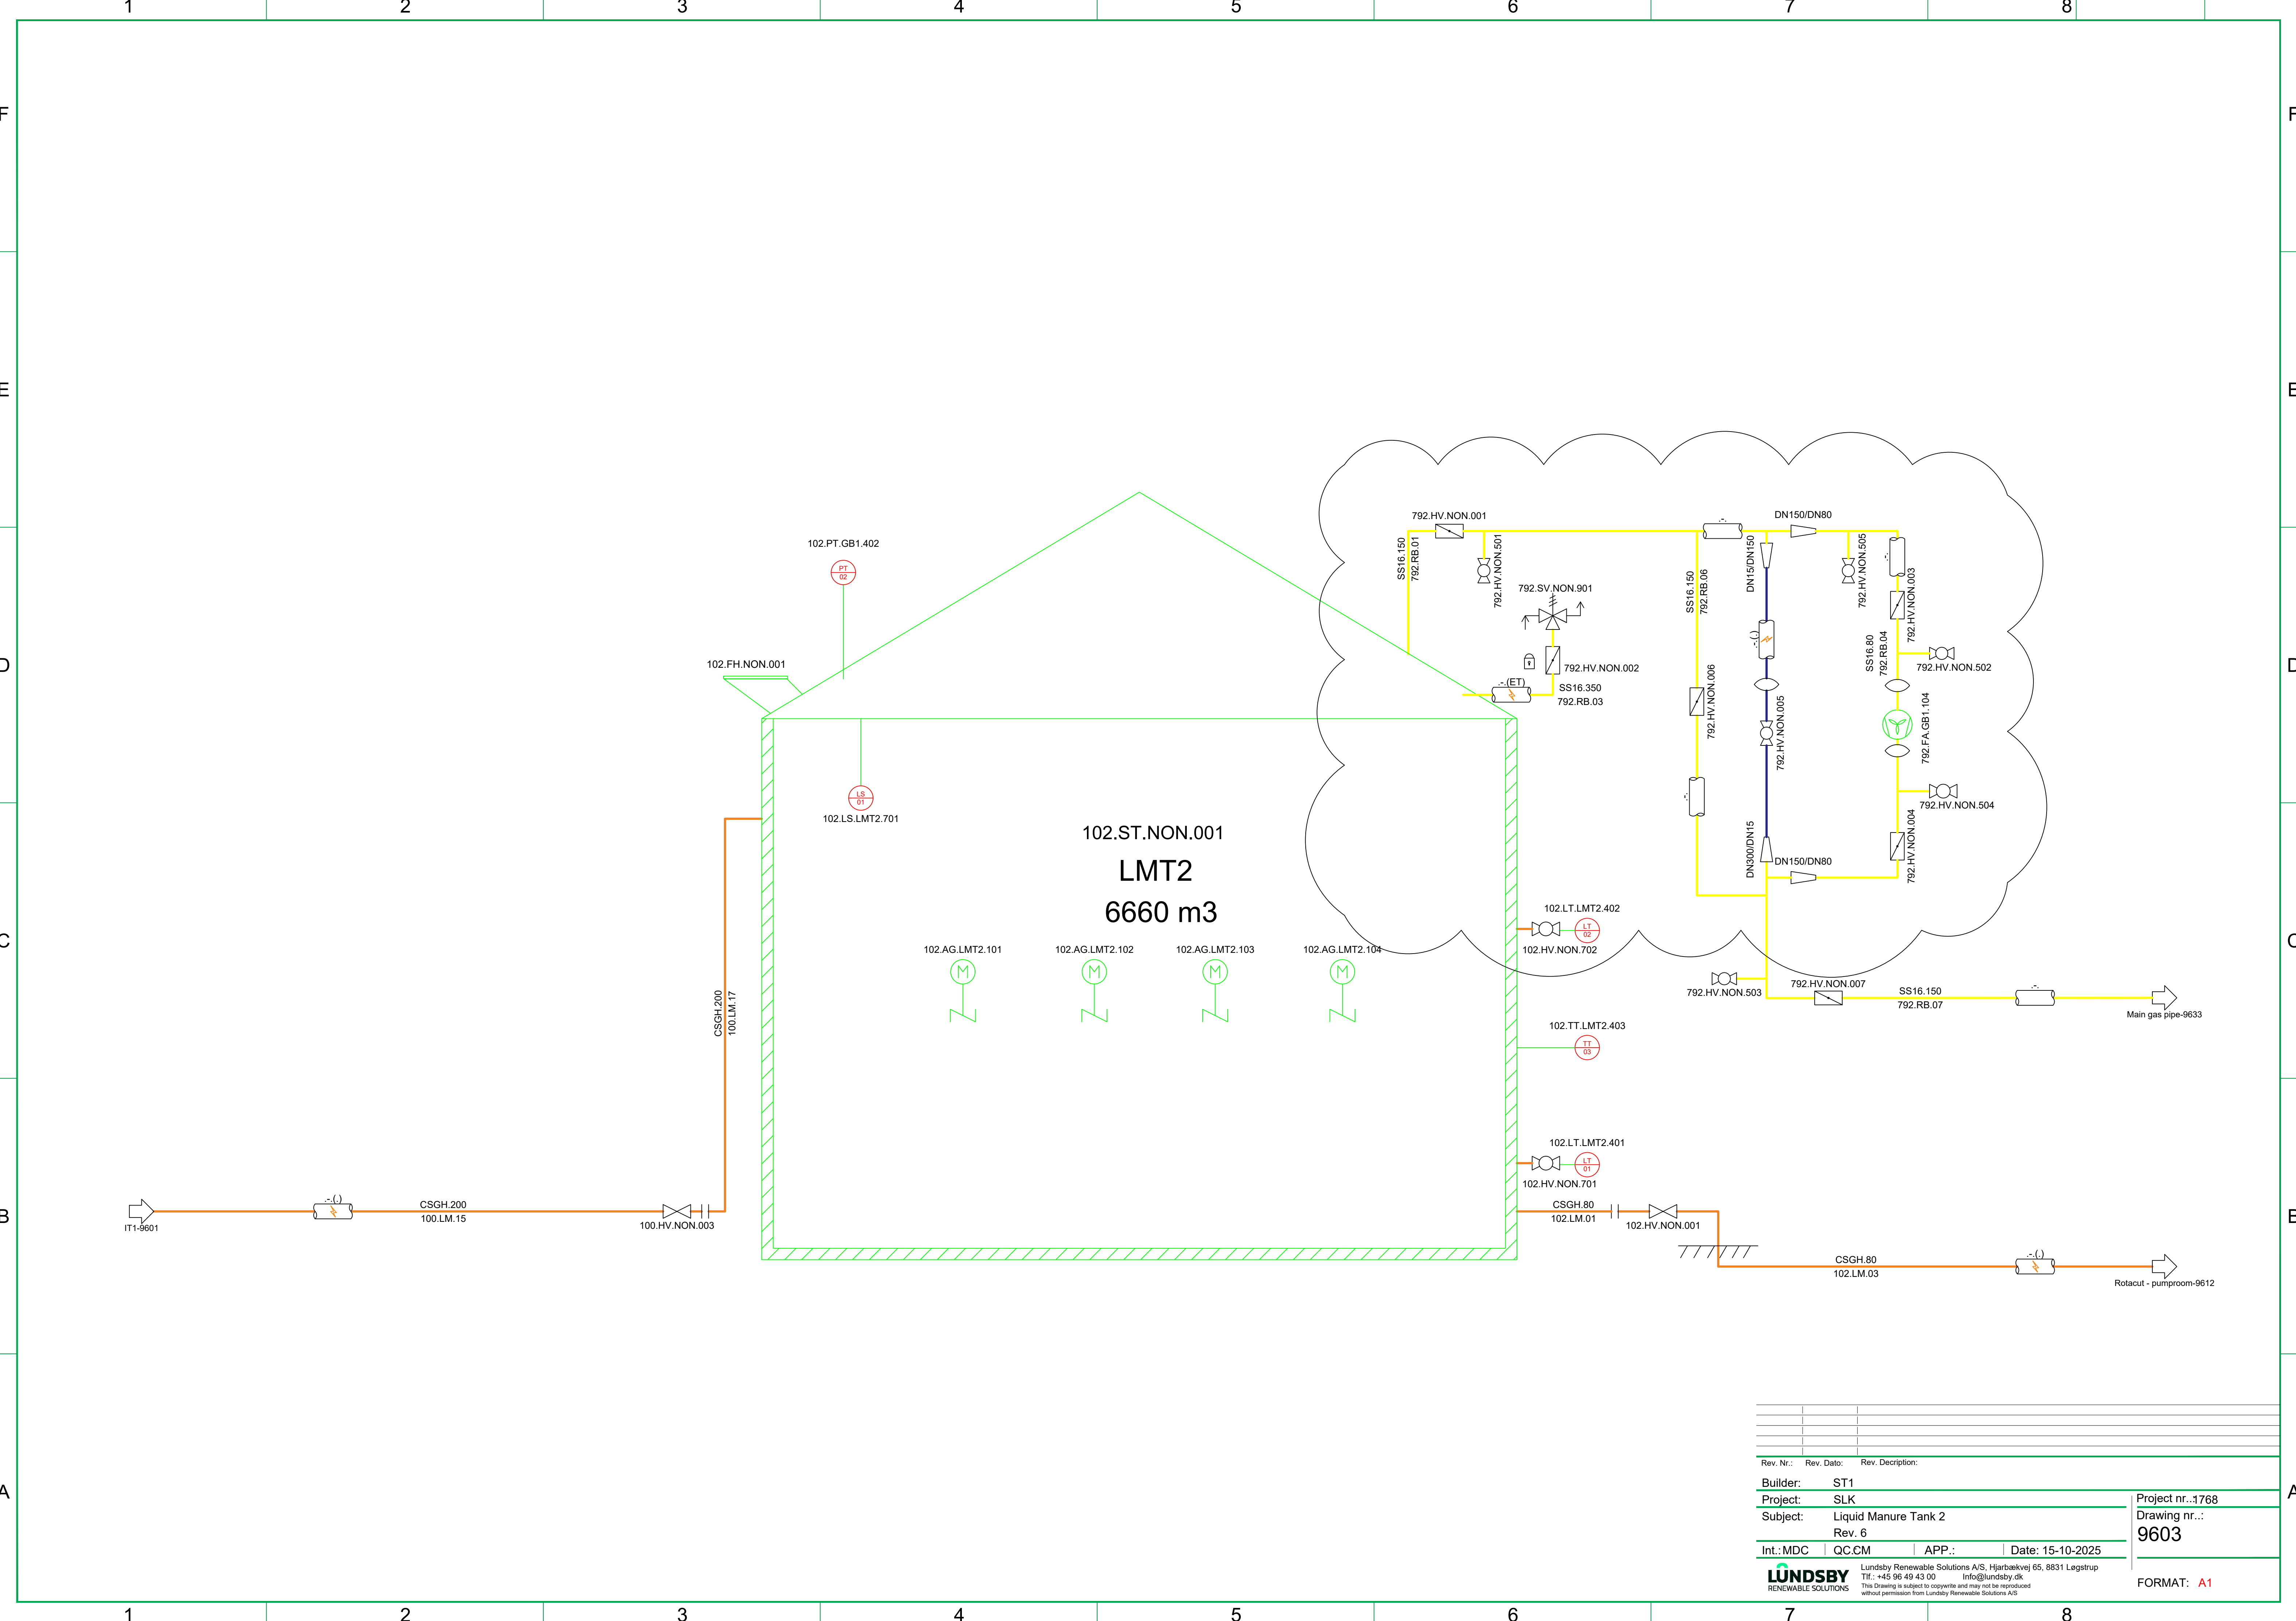


Rev. Nr.:	Rev. Dato:	Rev. Description:	
Builder:	ST1		
Project:	SLK		
Subject:	Liquid Manure Tank 2		
Rev. 6			
Int.:MDC	QC:CM	APP.:	Date: 15-10-2025
LUNDSBY RENEWABLE SOLUTIONS			Lundsby Renewable Solutions A/S, Hjarbækvej 65, 8831 Løgstrup Tlf.: +45 96 49 43 00 Info@lundsby.dk This Drawing is subject to copyright and may not be reproduced without permission from Lundsby Renewable Solutions A/S
Project nr.:1768 Drawing nr.: 9603			FORMAT: A1

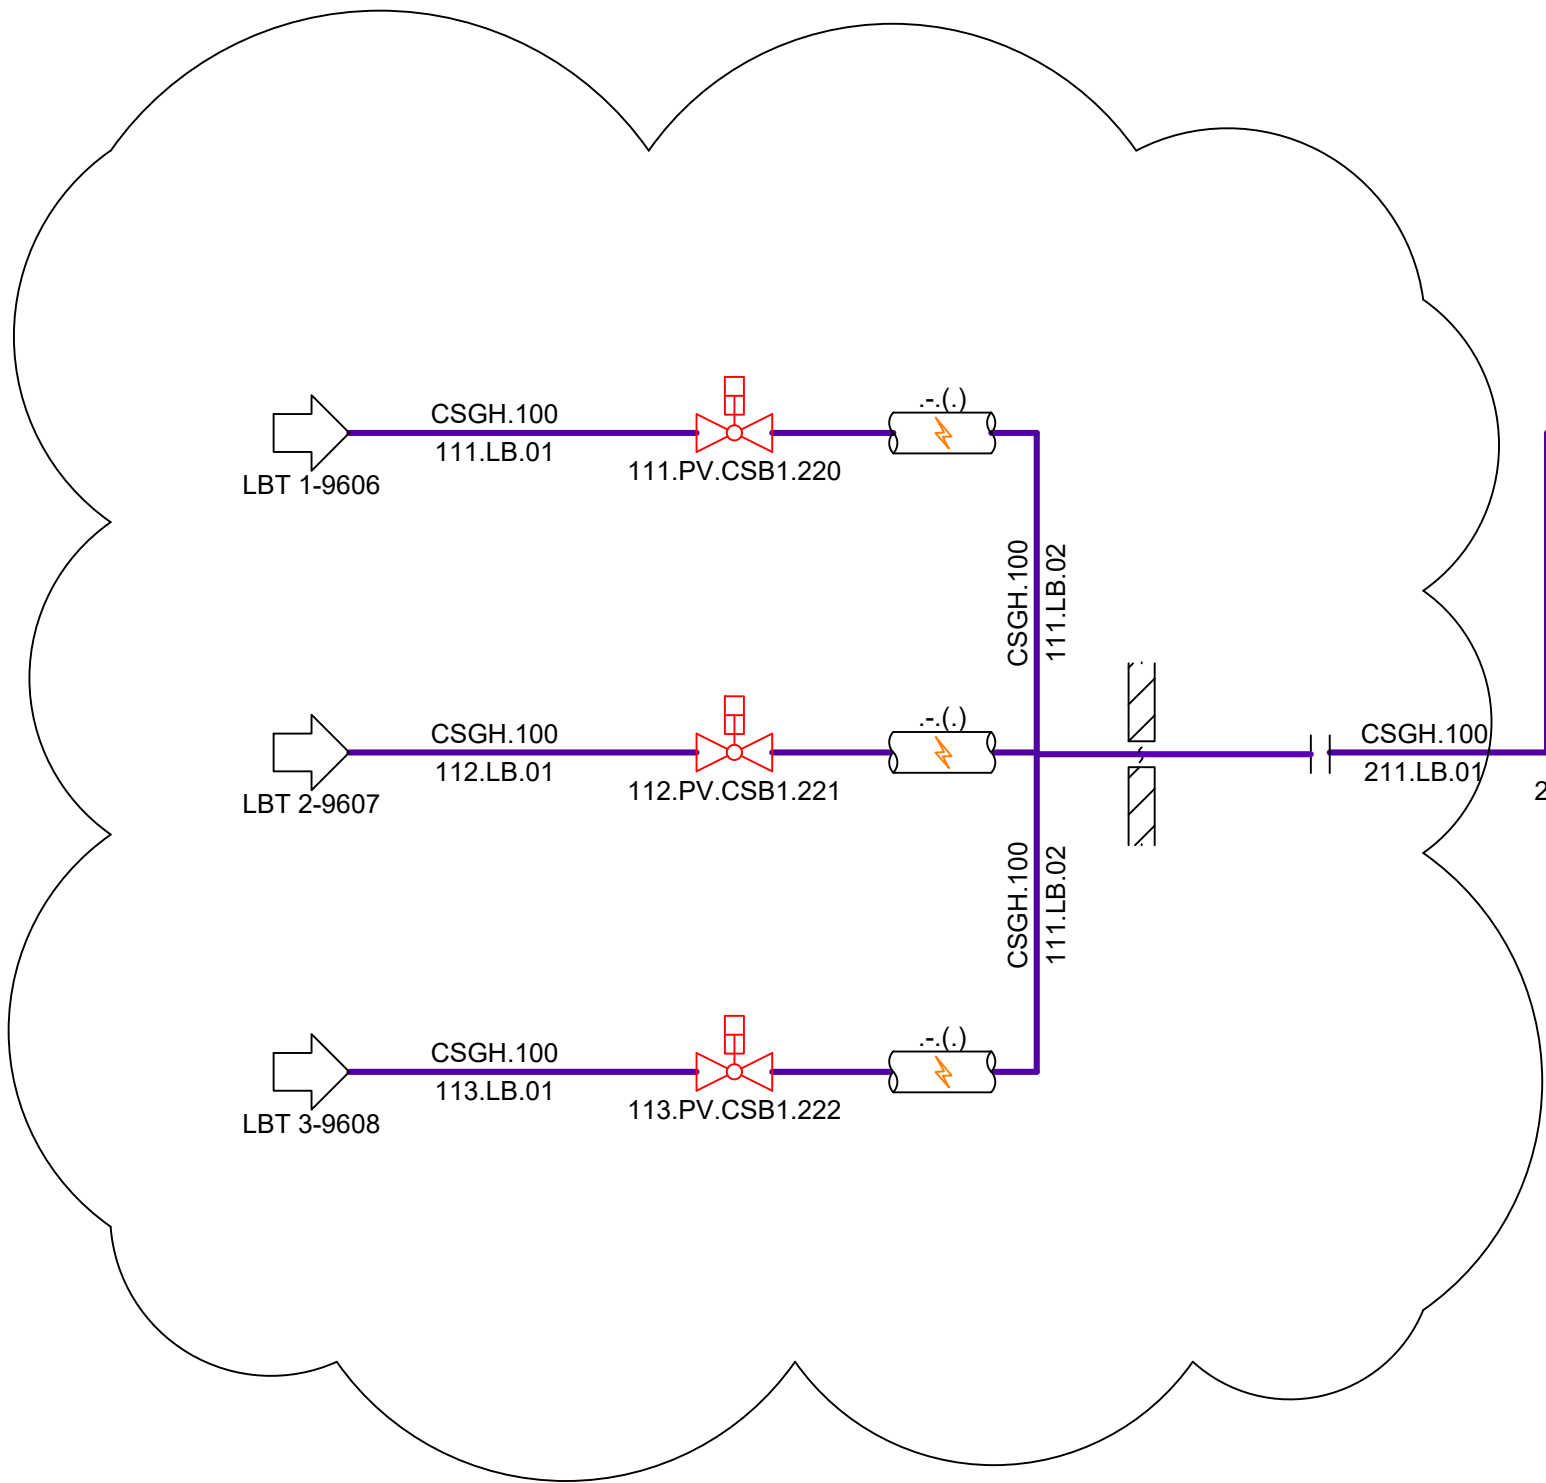


Rev. Nr.:		Rev. Dato:	Rev. Description:
Builder:		ST1	
Project:		SLK	
Subject:		Liquid biomass pump 1	
		Rev. 6	
Int.:MDC		QC:CM	APP.: Date: 15-10-2025
LUNDSBY		Lundsby Renewable Solutions A/S, Hjarbækvej 65, 8831 Løgstrup	
RENEWABLE SOLUTIONS		Tlf.: +45 96 49 43 00 Info@lundsby.dk	
		This Drawing is subject to copyright and may not be reproduced without permission from Lundsby Renewable Solutions A/S	
		Project nr.:1768	
		Drawing nr.: 9605	
		FORMAT: A1	

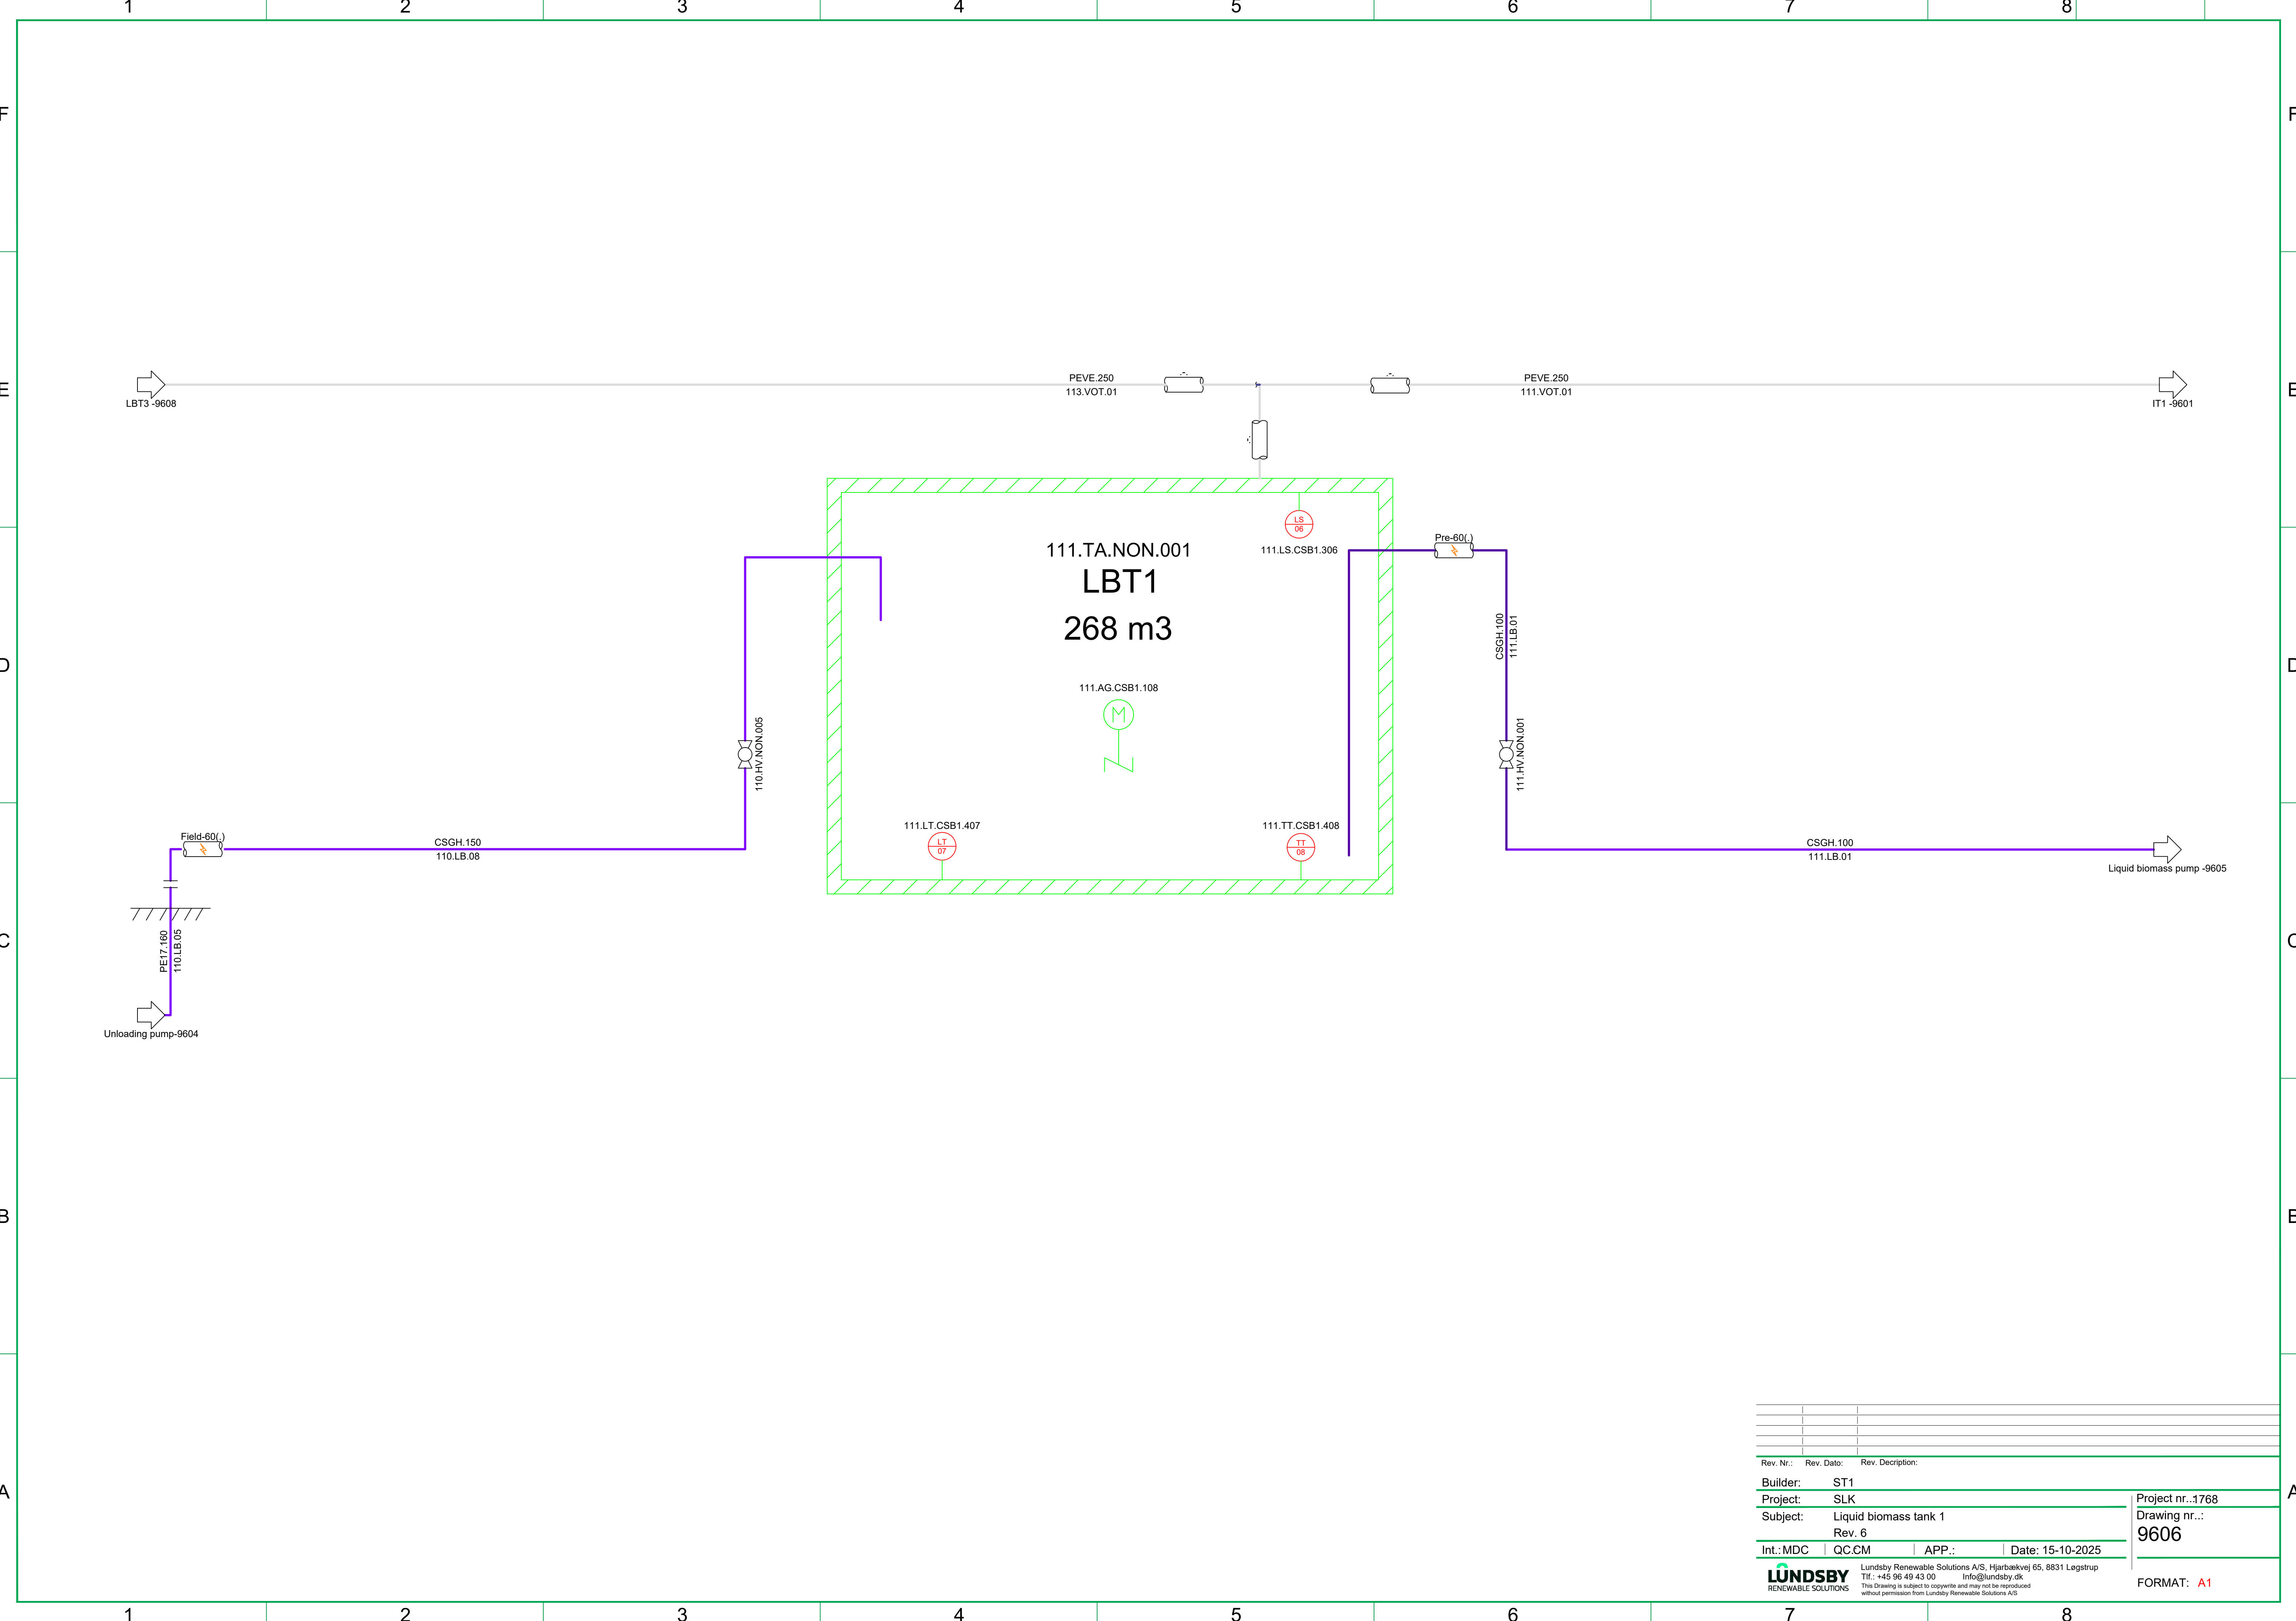


Rev. Nr.:	Rev. Dato:	Rev. Description:	
Builder:	ST1		
Project:	SLK		
Subject:	Liquid biomass tank 1		
	Rev. 6		
Int.:MDC	QC.CM	APP.:	Date: 15-10-2025
LUNDSBY RENEWABLE SOLUTIONS			Lundsby Renewable Solutions A/S, Hjarbækvej 65, 8831 Løgstrup Tlf.: +45 96 49 43 00 Info@lundsby.dk This Drawing is subject to copyright and may not be reproduced without permission from Lundsby Renewable Solutions A/S
			Project nr...1768 Drawing nr...: 9606 FORMAT: A1

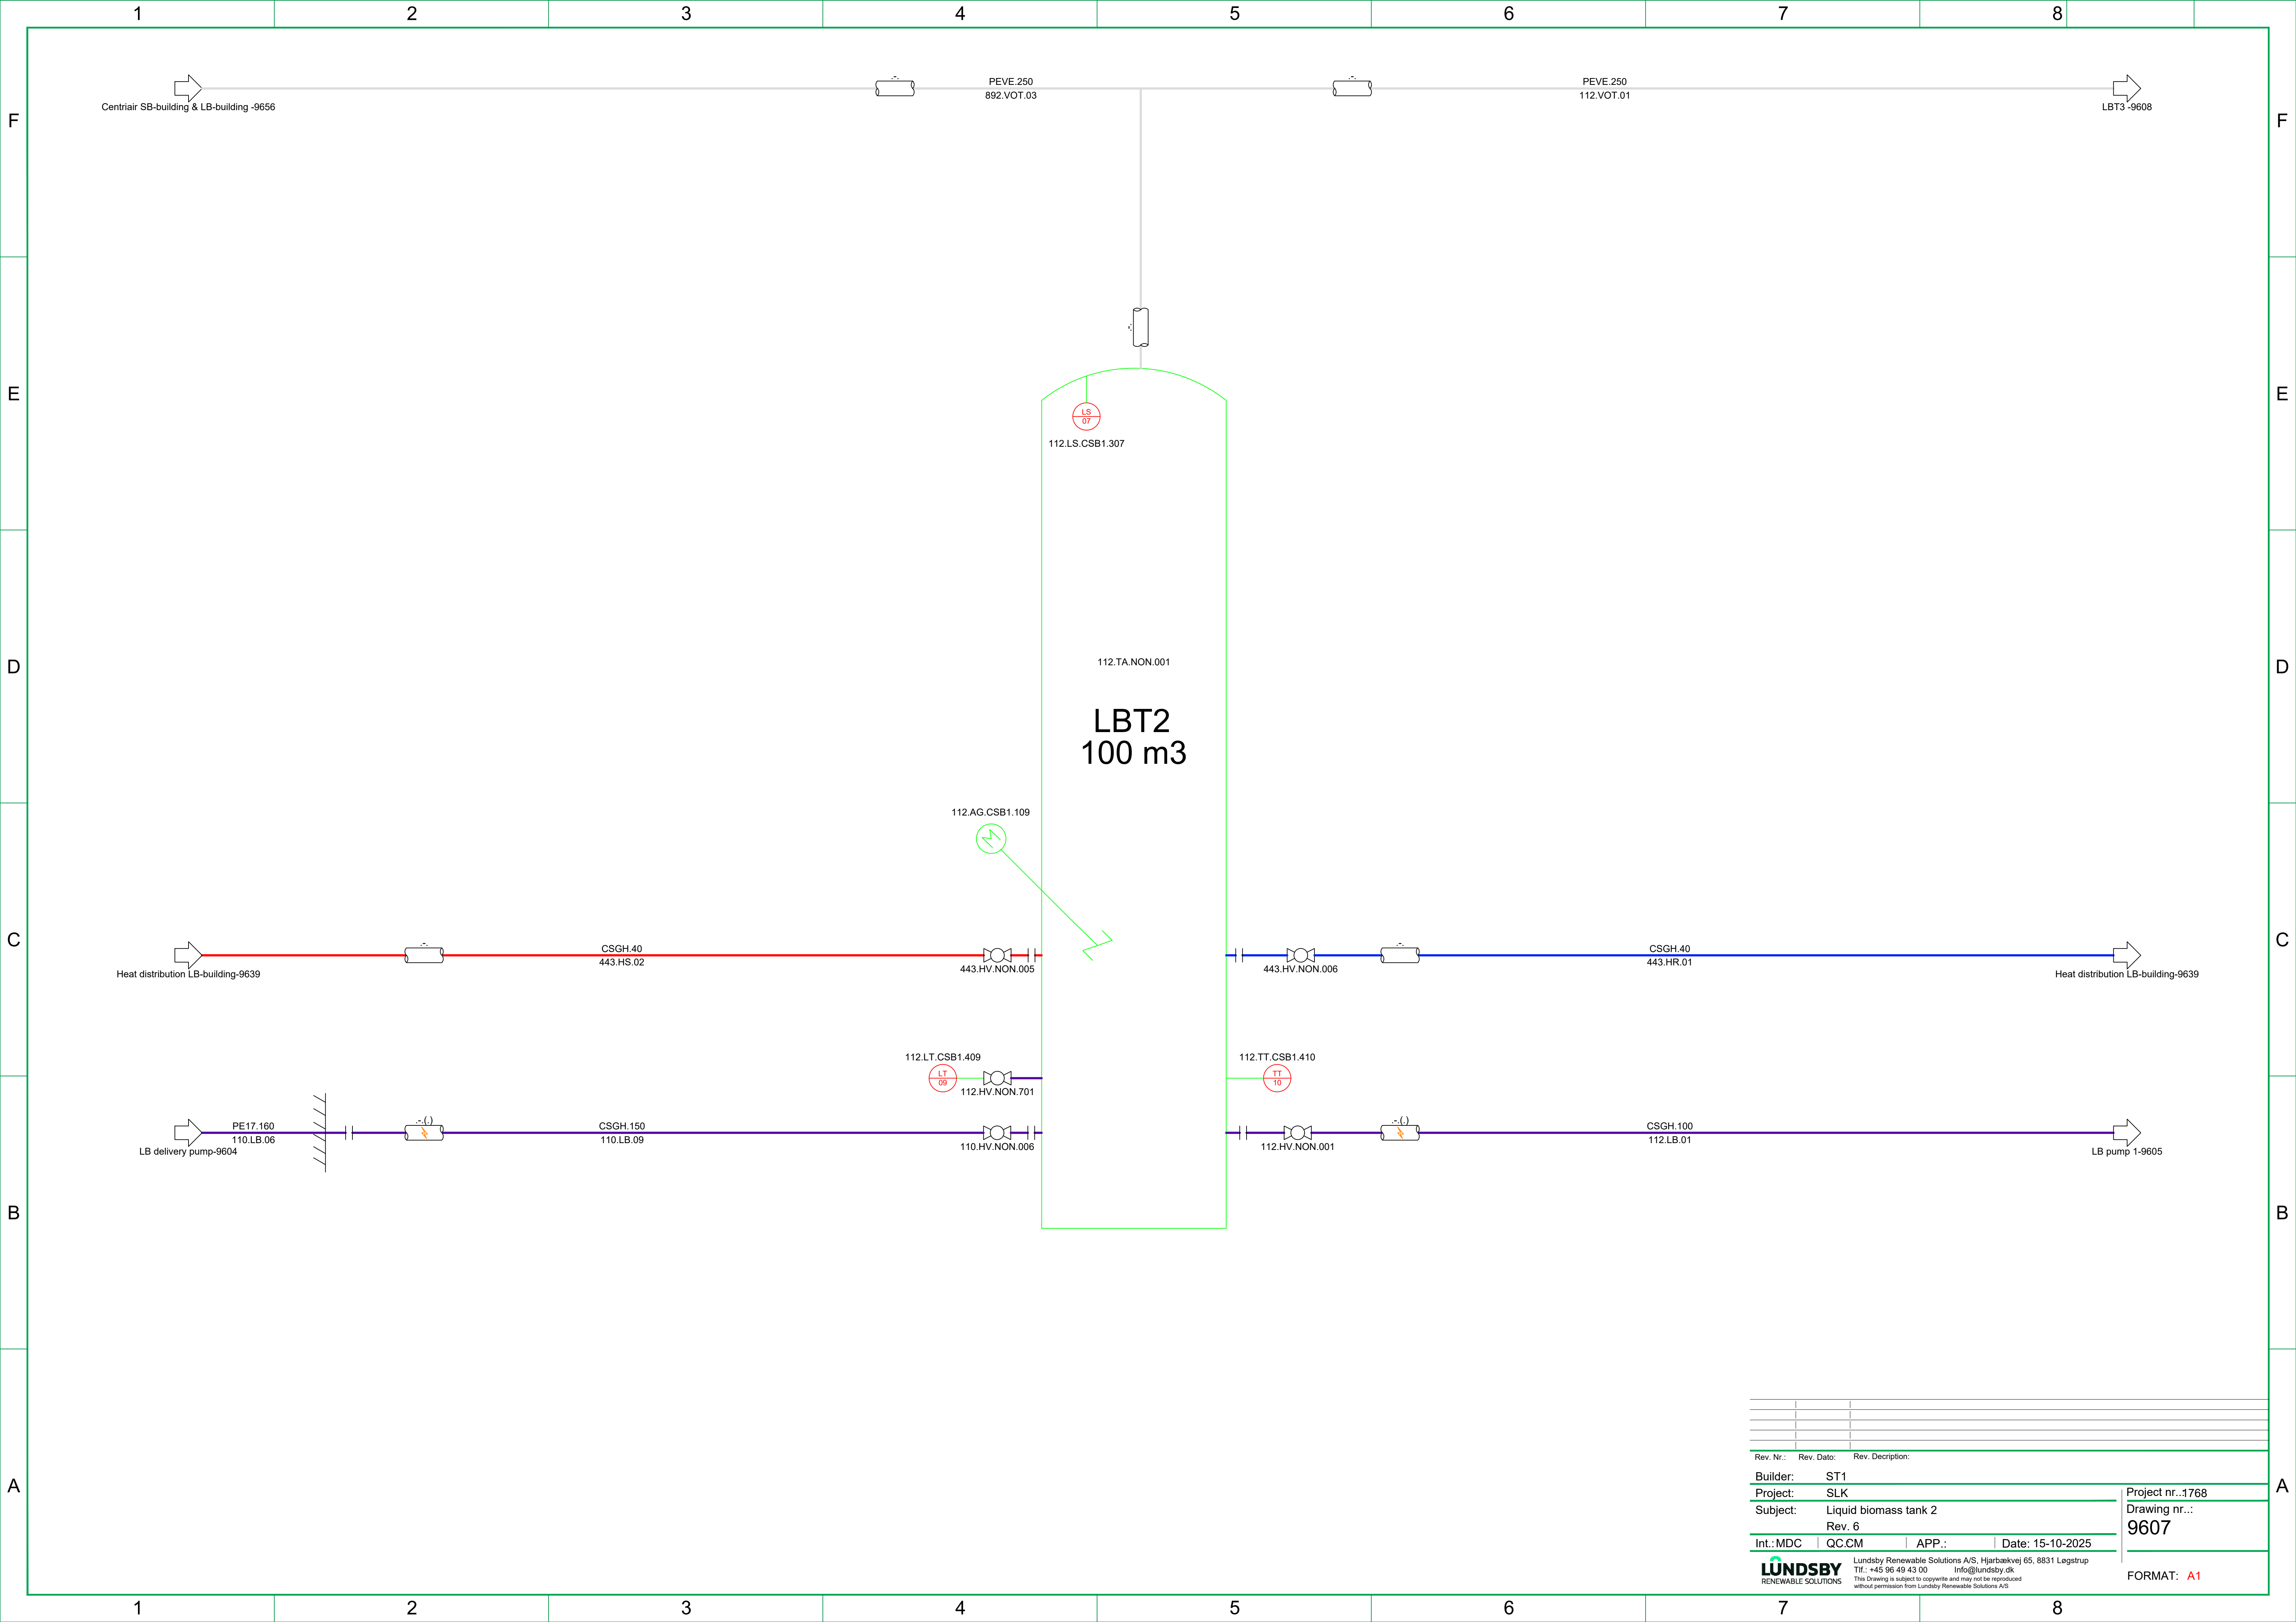



Rev. Nr.:	Rev. Dato:	Rev. Description:
Builder:	ST1	
Project:	SLK	
Subject:	Liquid biomass tank 2	
	Rev. 6	
Int.:MDC	QC:CM	APP.:Date: 15-10-2025
LUNDSBY RENEWABLE SOLUTIONS		
Lundsby Renewable Solutions A/S, Hjarbækvej 65, 8831 Løgstrup Tlf.: +45 96 49 43 00 Info@lundsby.dk This Drawing is subject to copyright and may not be reproduced without permission from Lundsby Renewable Solutions A/S		
Project nr...1768 Drawing nr...: 9607		FORMAT: A1

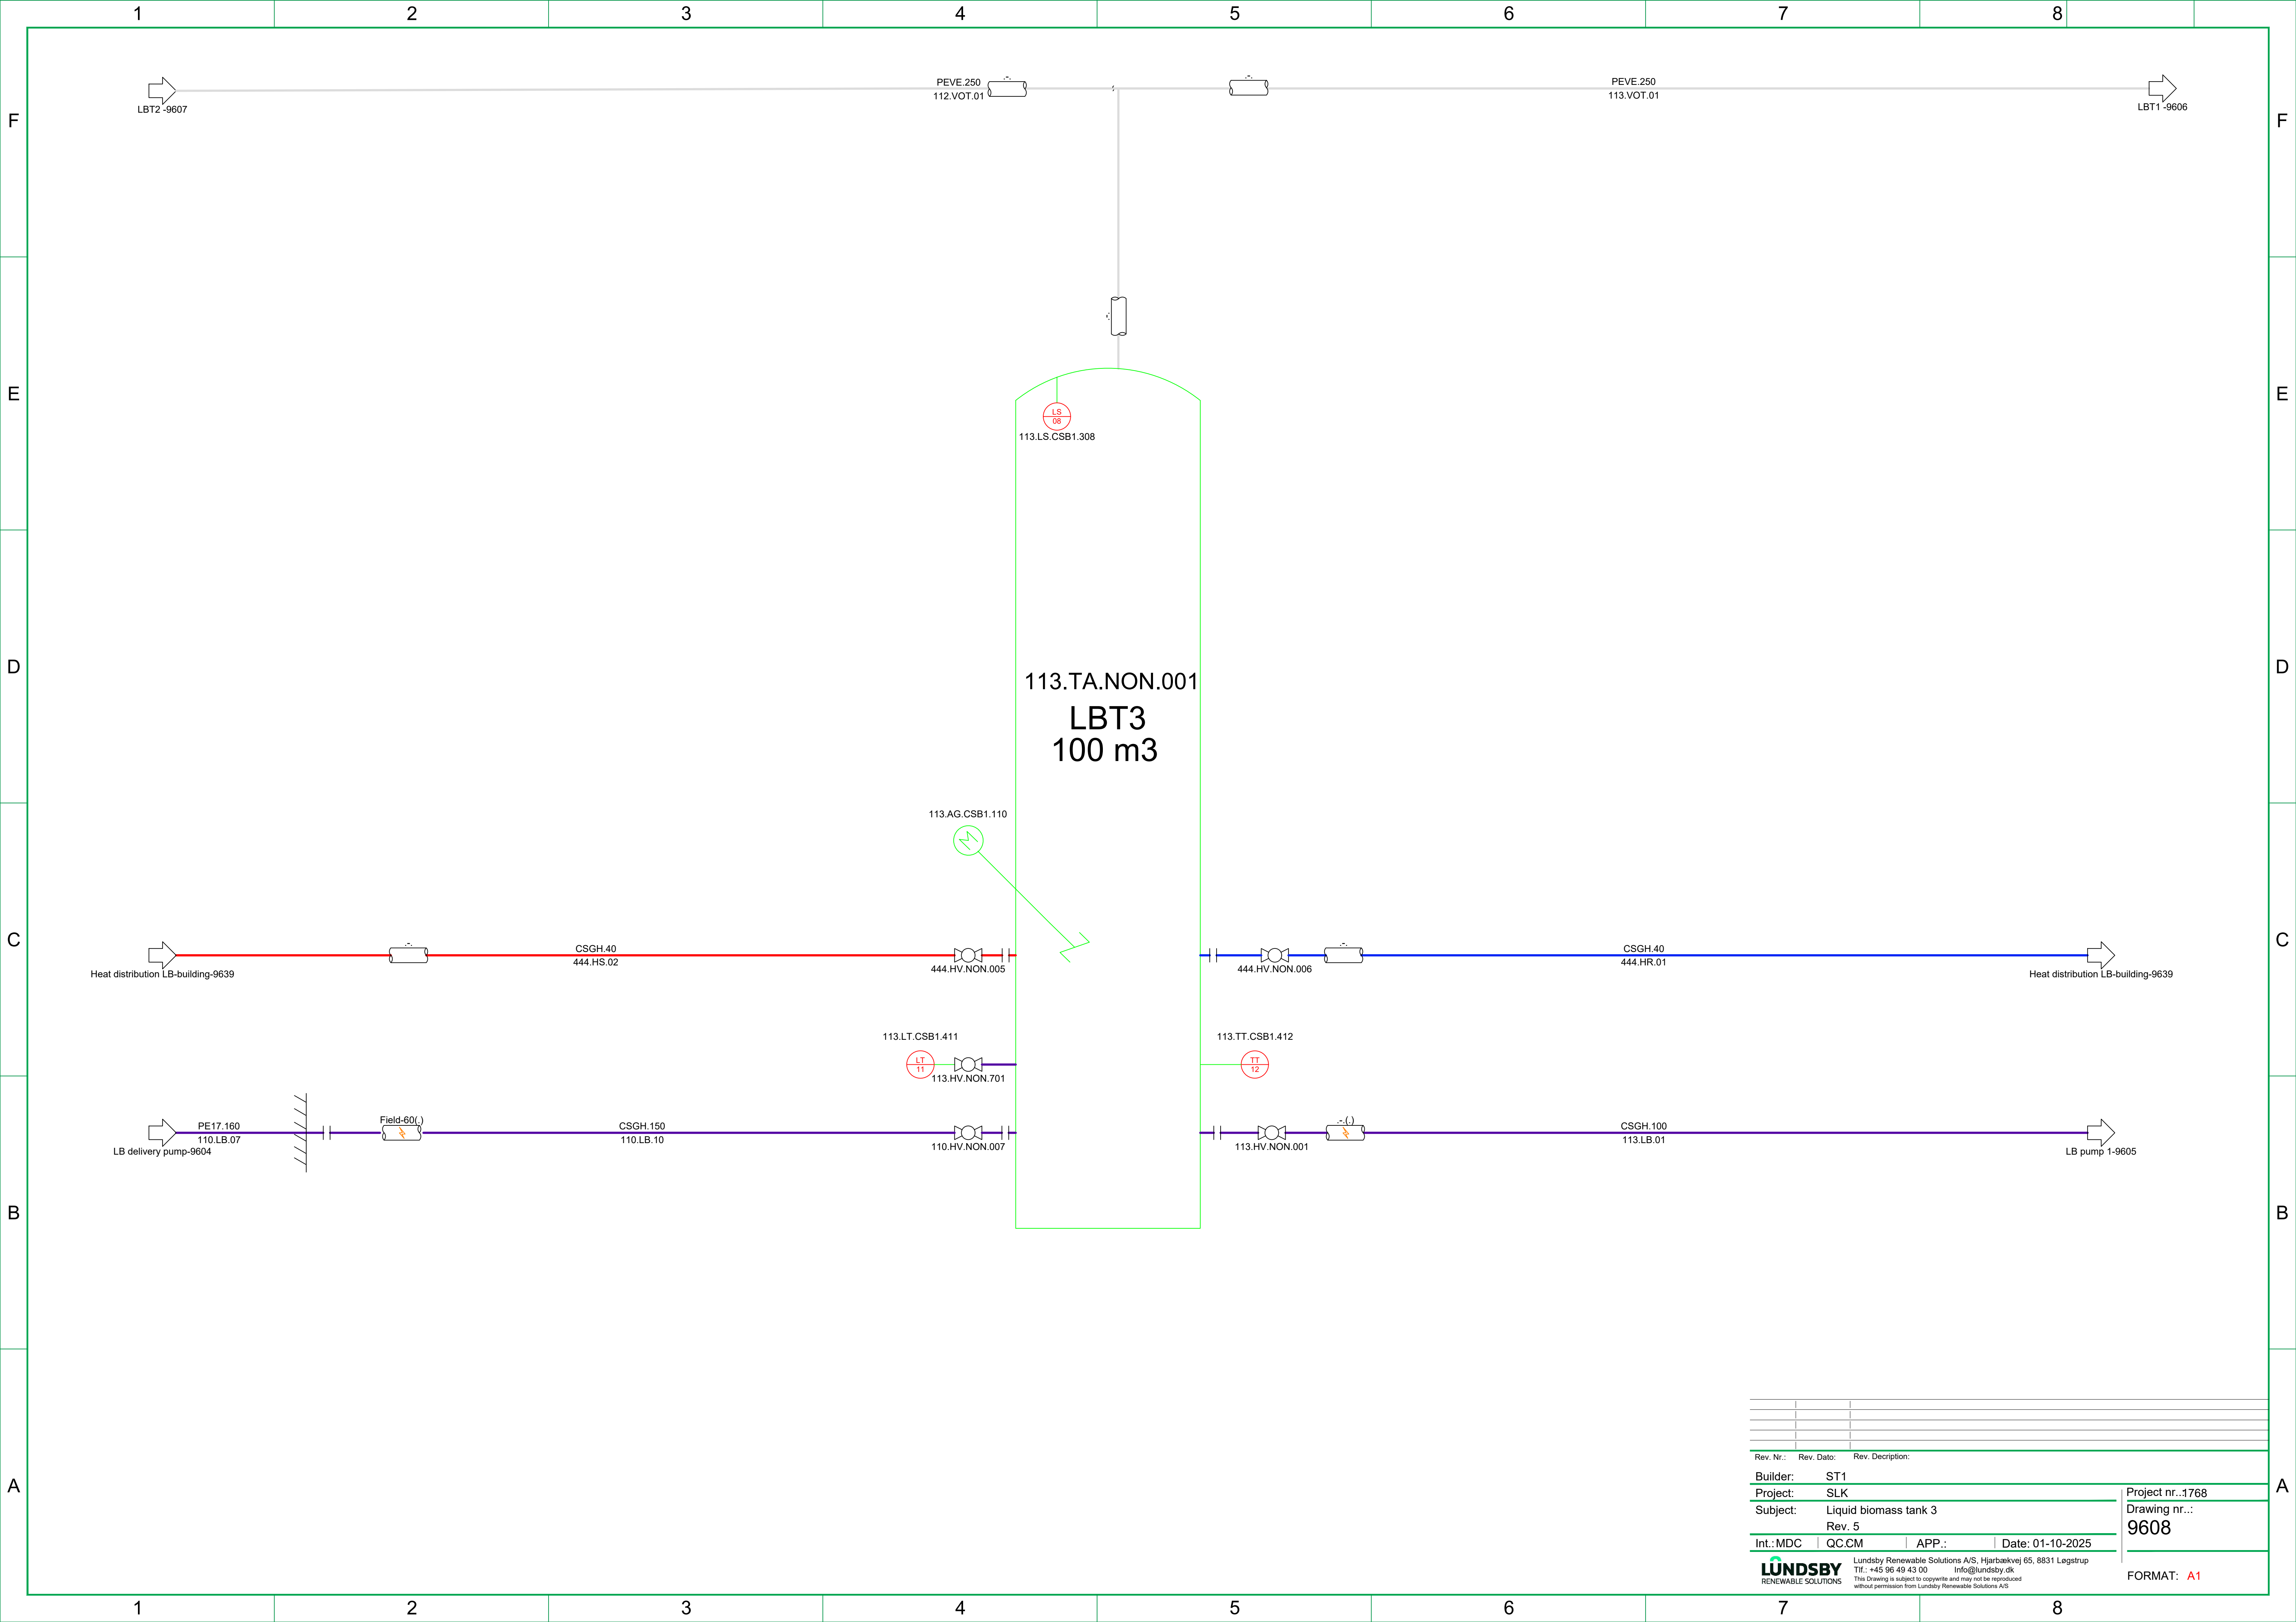

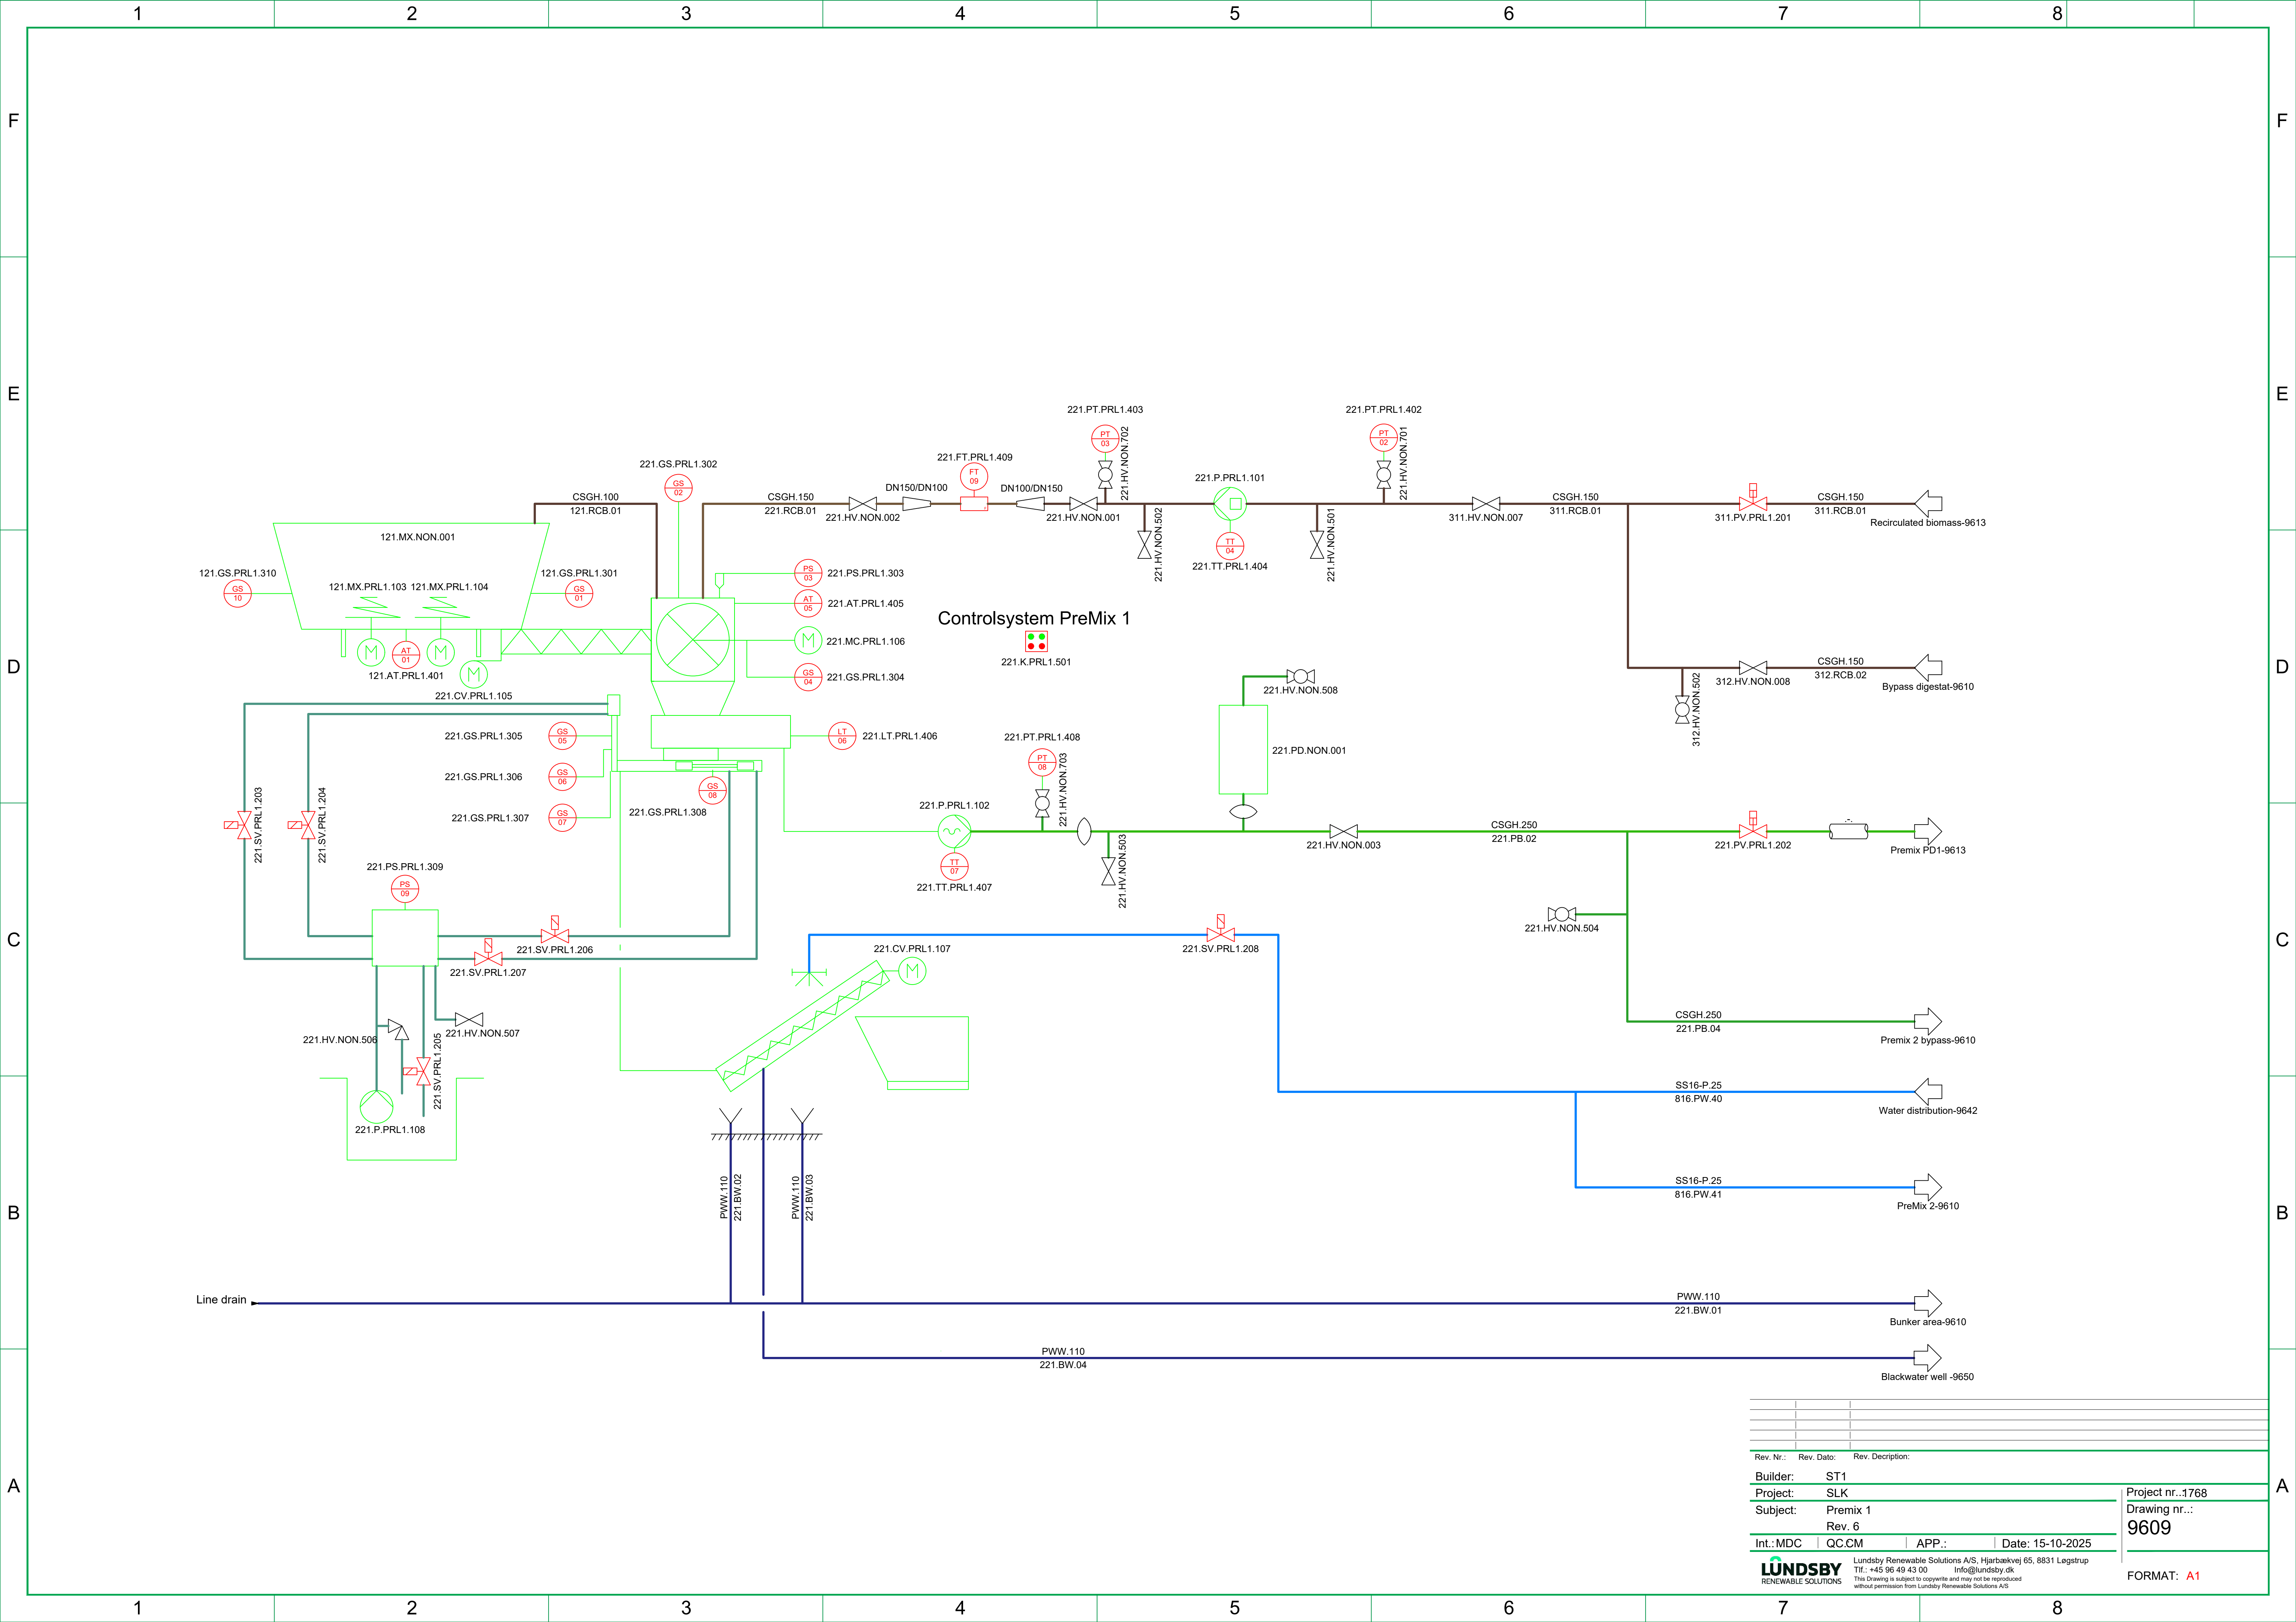


Rev. Nr.:	Rev. Dato:	Rev. Description:	
Builder:	ST1		
Project:	SLK		
Subject:	Premix 1		
	Rev. 6		
Int.:MDC	QC.CM	APP.:	Date: 15-10-2025
LUNDSBY RENEWABLE SOLUTIONS			Lundsby Renewable Solutions A/S, Hjarbækvej 65, 8831 Løgstrup Tlf.: +45 96 49 43 00 Info@lundsby.dk This drawing is subject to copyright and may not be reproduced without permission from Lundsby Renewable Solutions A/S
Project nr.:1768 Drawing nr.: 9609			FORMAT: A1

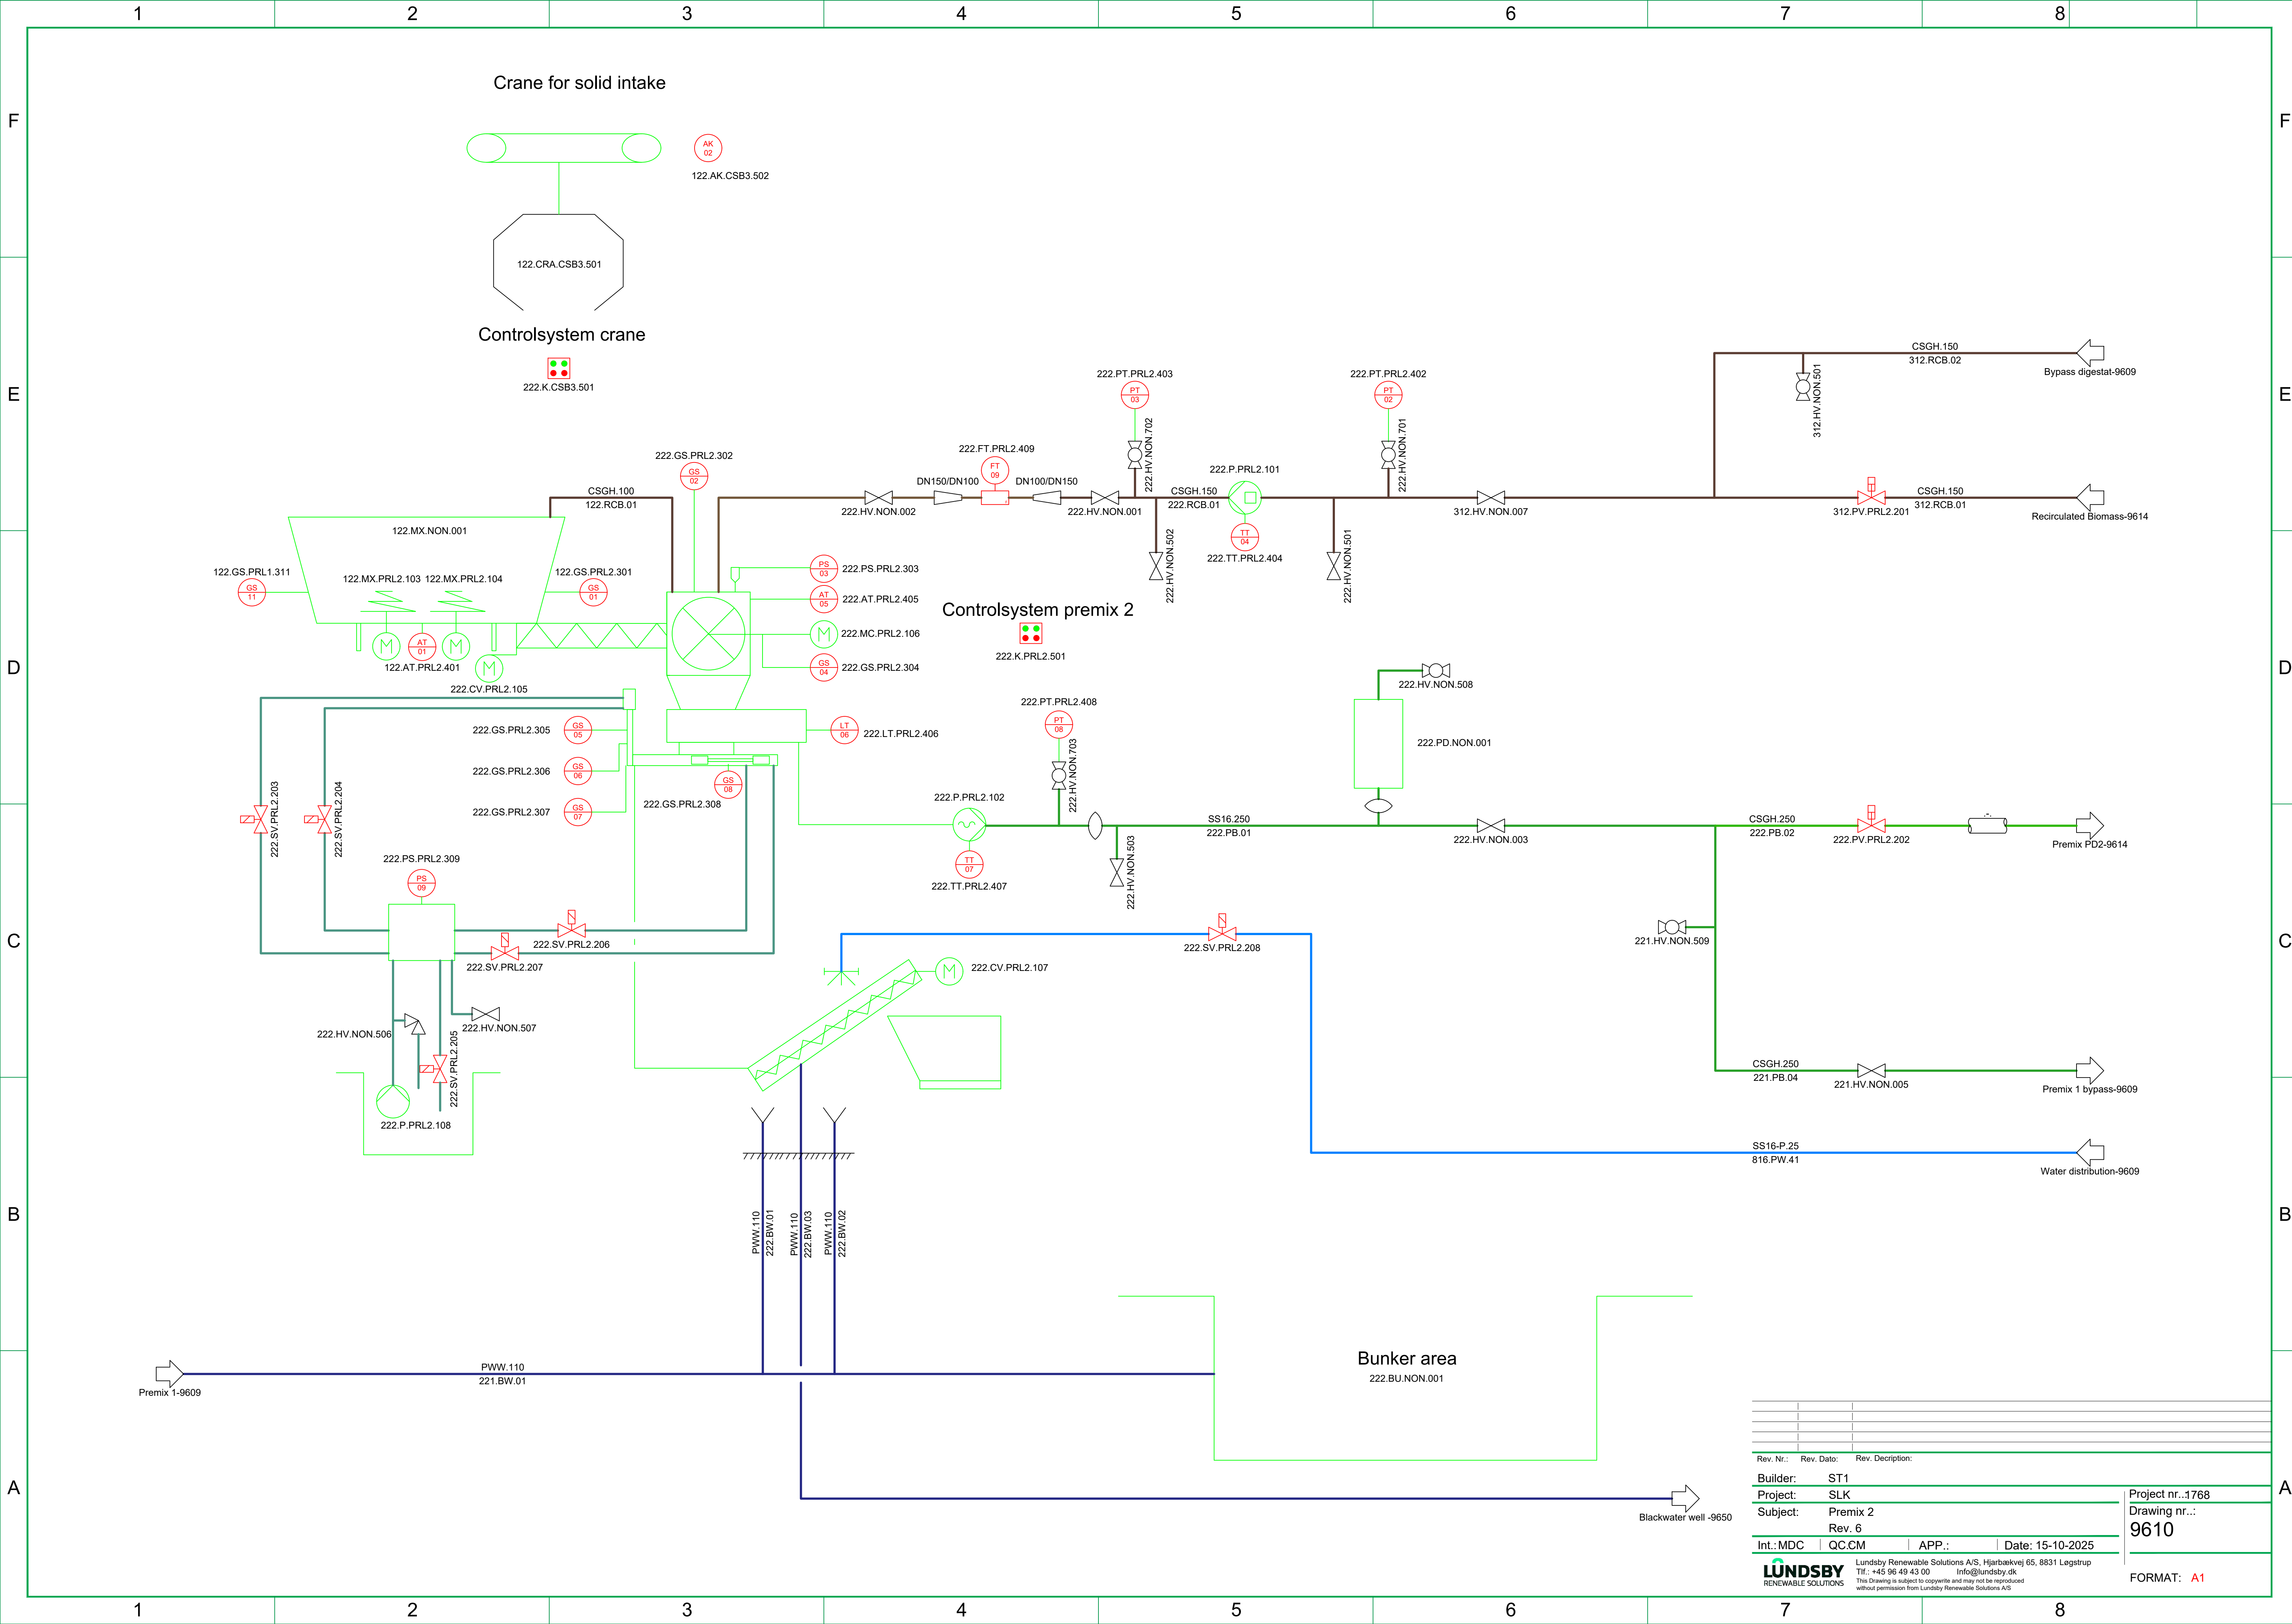

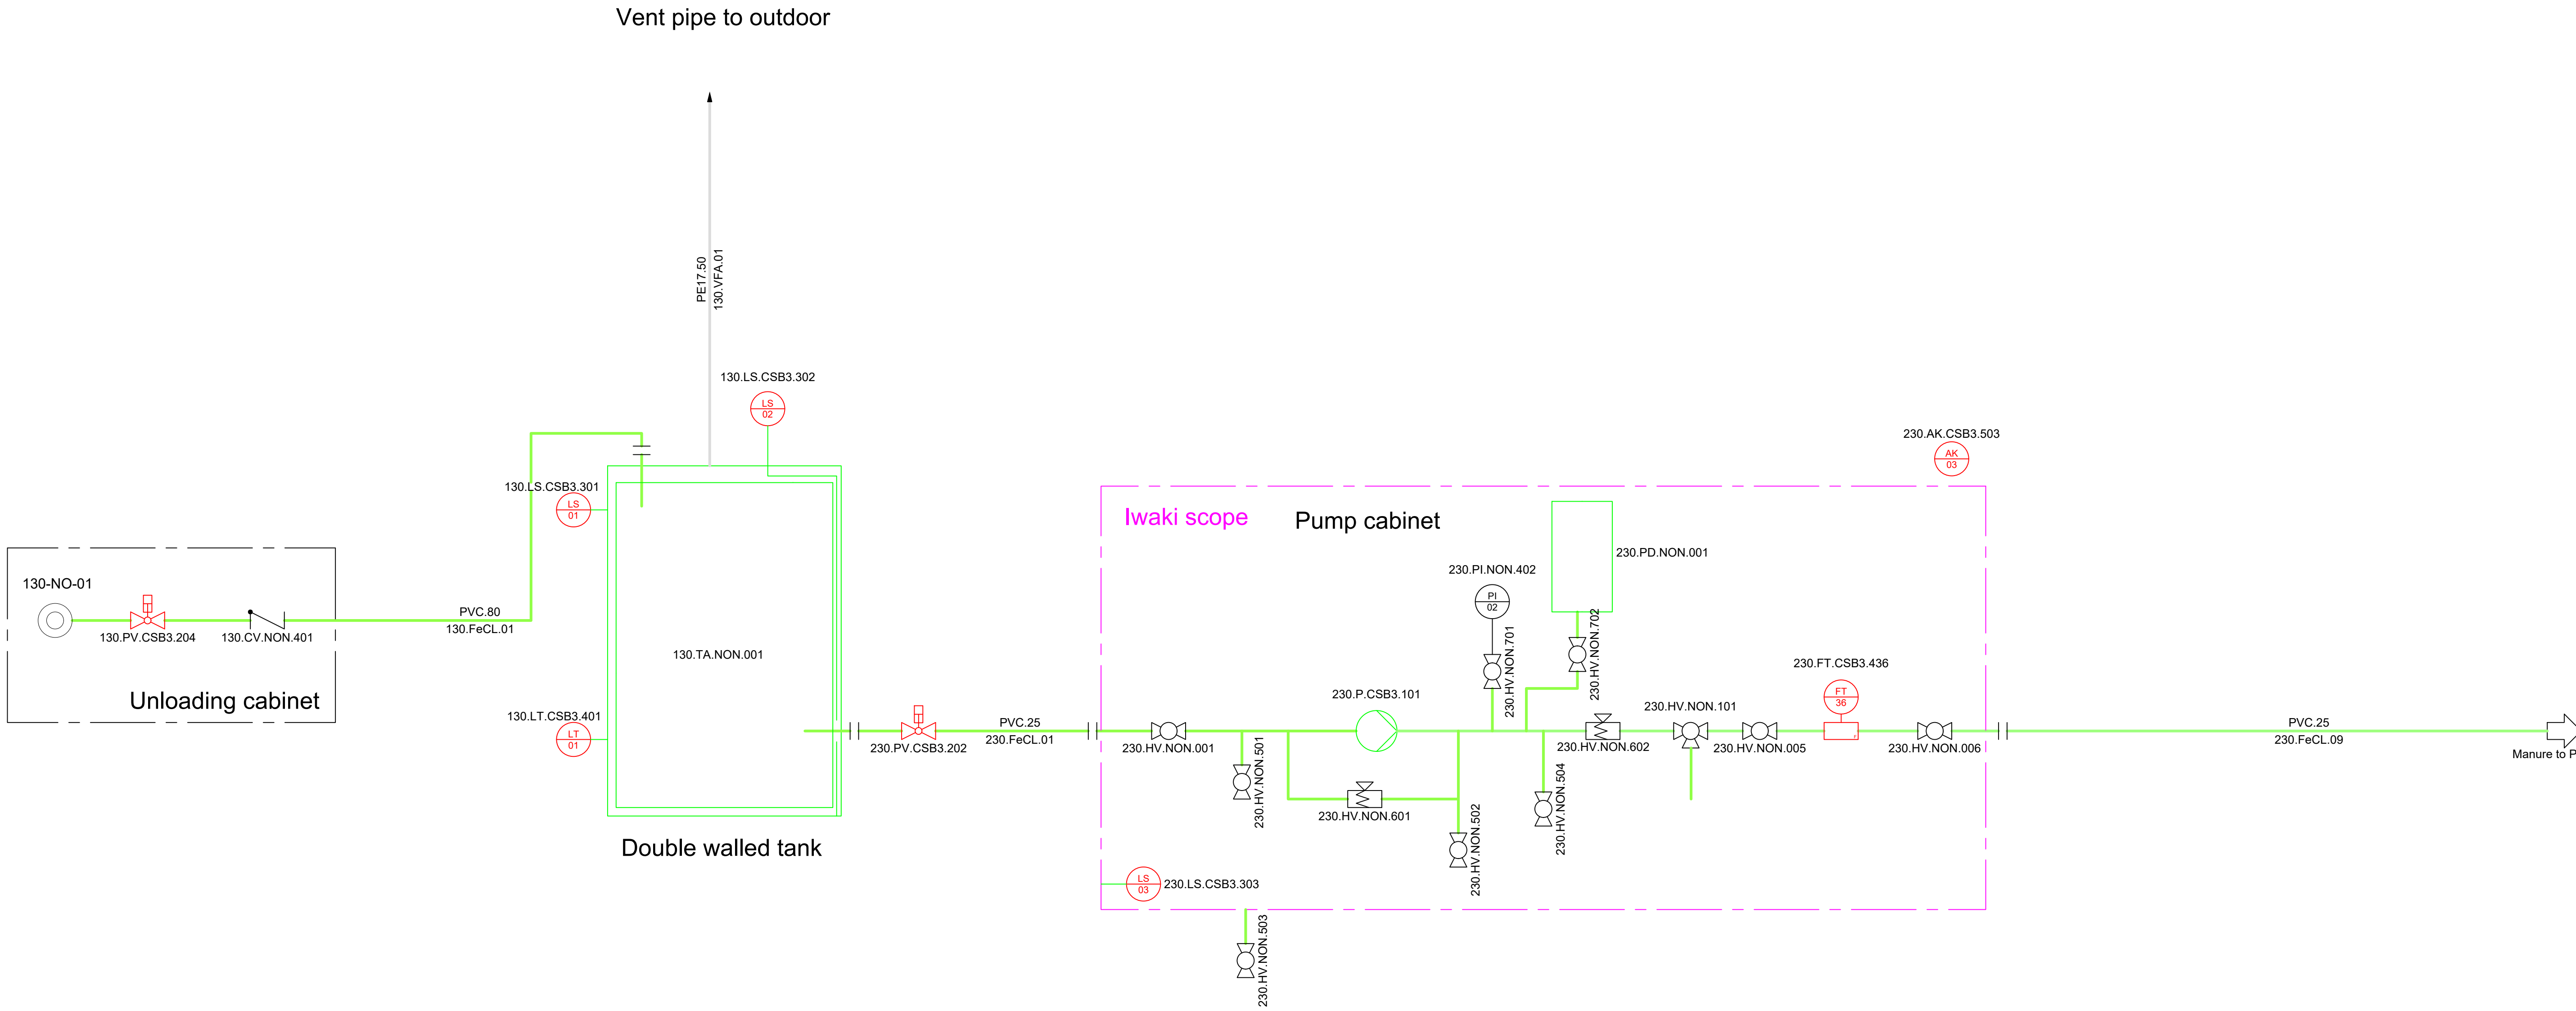


Pumphouse 2

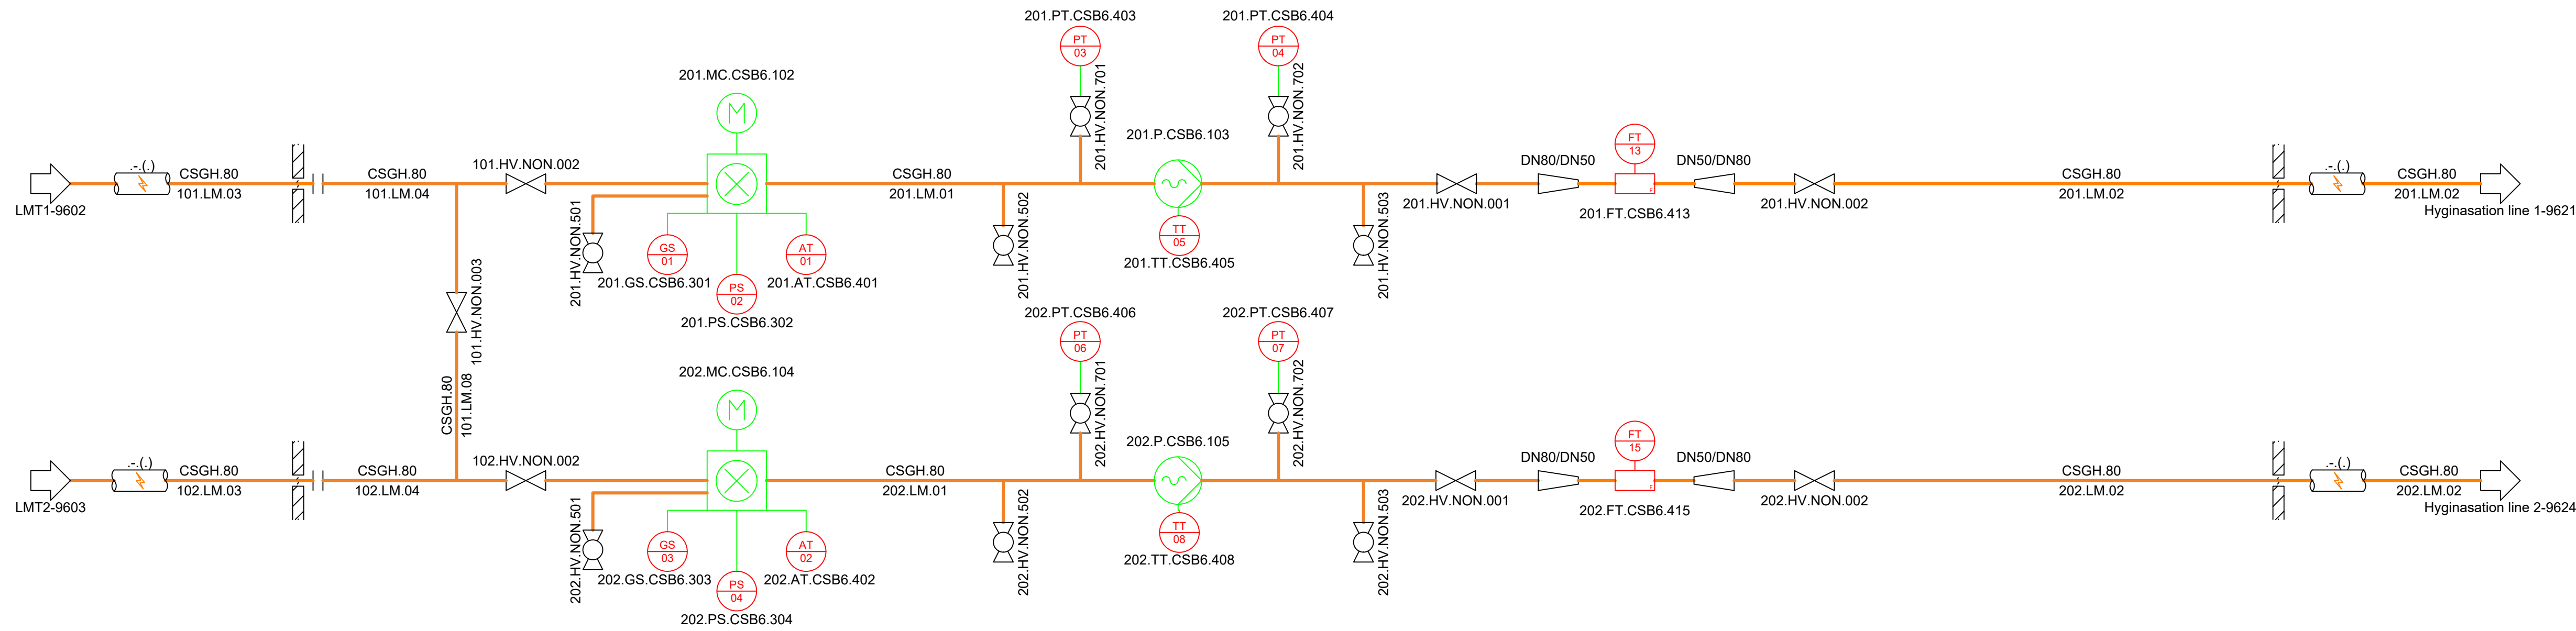


Tech
building


SB-building

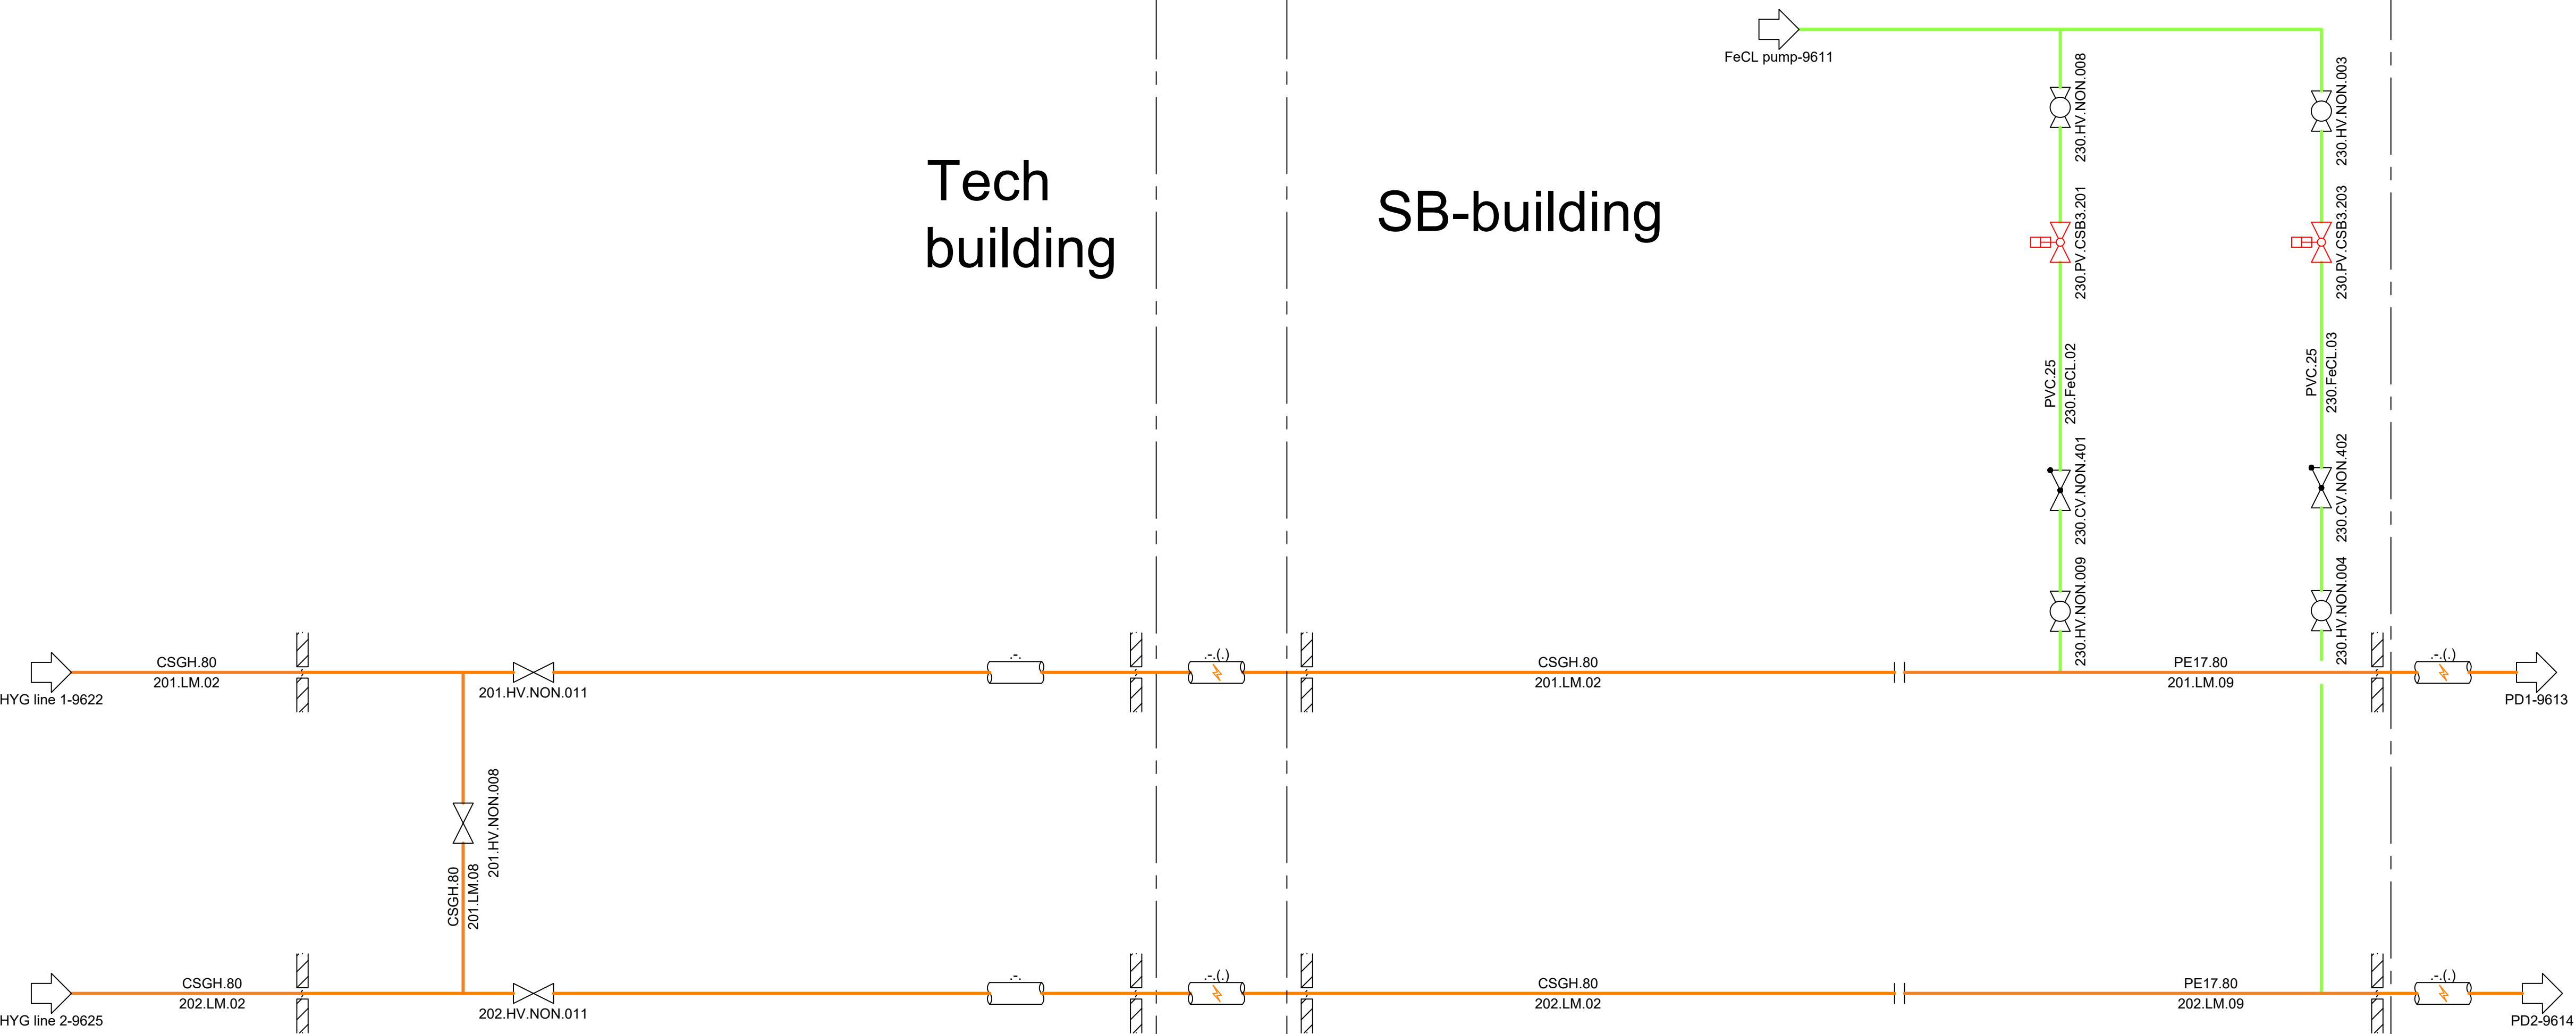


Rev. Nr.:	Rev. Dato:	Rev. Description:
Builder:	ST1	
Project:	SLK	
Subject:	Liquid manure pump	
Rev. 6		
Int.: MDC	QC.CM	APP.:
Date: 15-10-2025		
LUNDSBY RENEWABLE SOLUTIONS		
Lundsby Renewable Solutions A/S, Hjarbækvej 65, 8831 Lægstrup Tlf.: +45 96 49 43 00 Info@lundsby.dk This Drawing is subject to copyright and may not be reproduced without permission from Lundsby Renewable Solutions A/S		
Project nr.: 1768 Drawing nr.: 9612 FORMAT: A1		

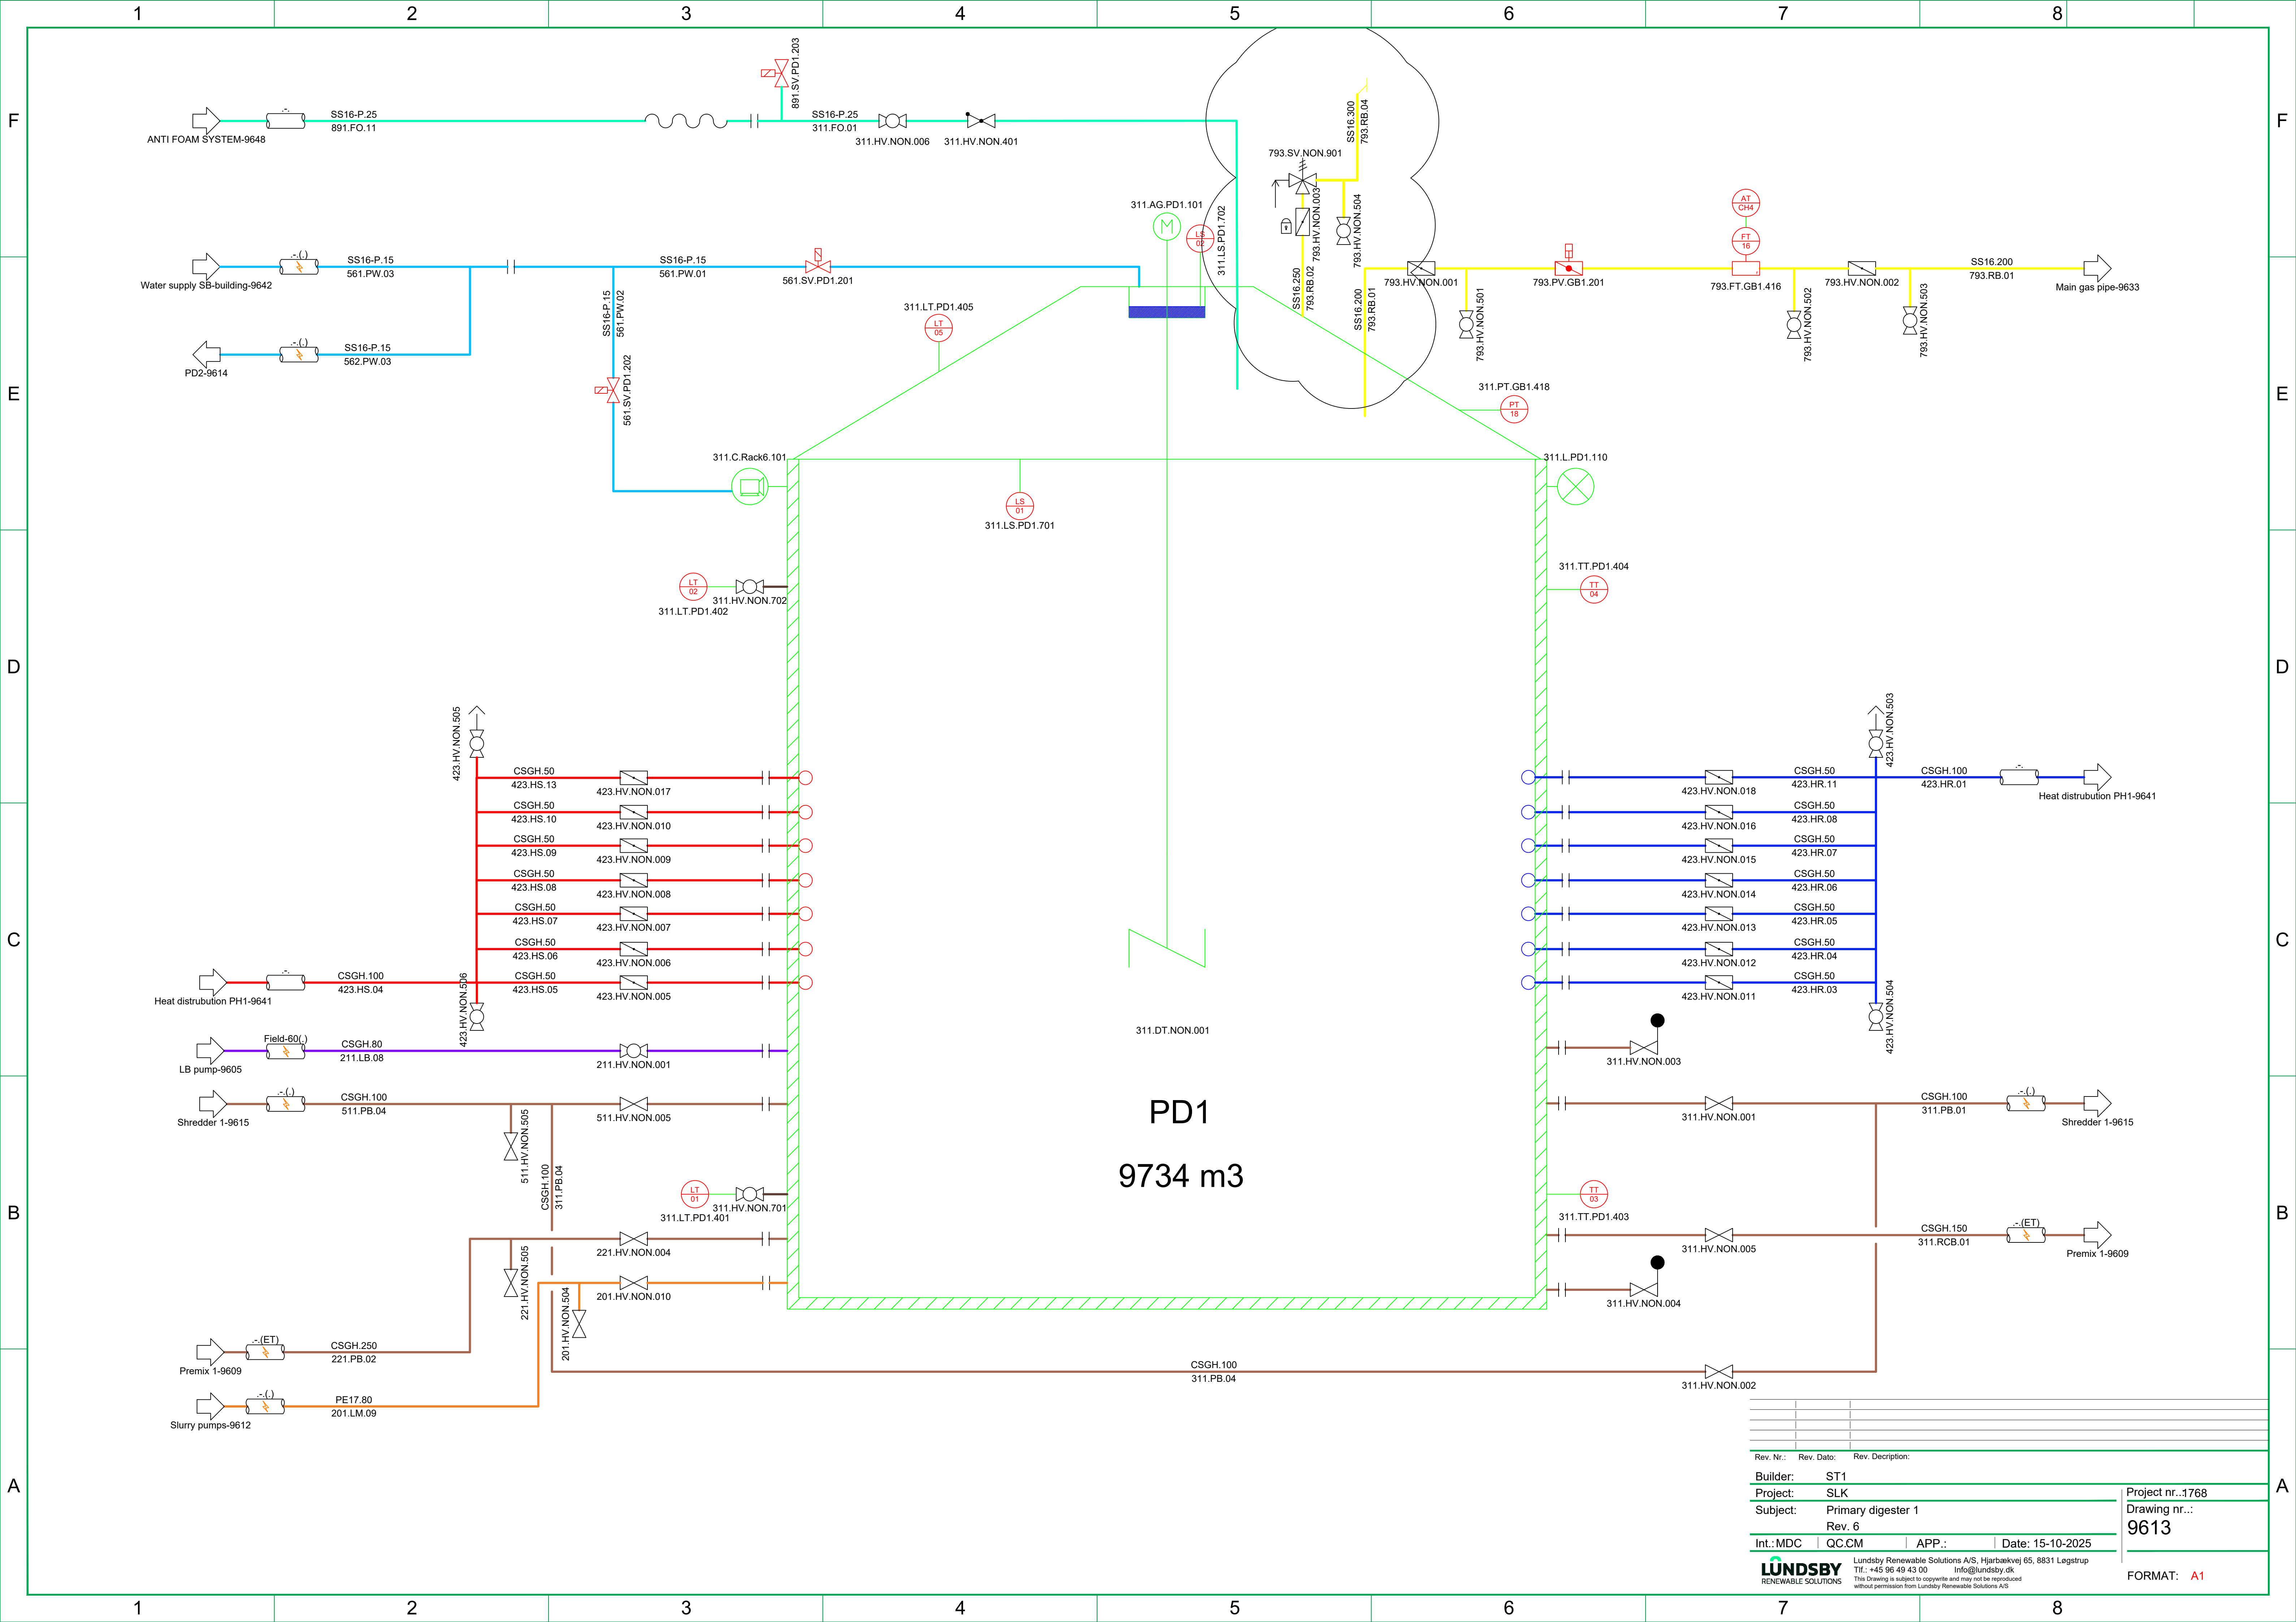


Rev. Nr.:	Rev. Dato:	Rev. Description:
Builder:	ST1	
Project:	SLK	
Subject:	Primary digester 1	
Rev. 6		
Int.:MDC	QC:CM	APP.:
Date: 15-10-2025		
LUNDSBY RENEWABLE SOLUTIONS		
Lundsby Renewable Solutions A/S, Hjarbækvej 65, 8831 Legstrup Tlf.: +45 96 49 43 00 Info@lundsby.dk This drawing is subject to copyright and may not be reproduced without permission from Lundsby Renewable Solutions A/S		
Project nr.:1768 Drawing nr.: 9613		FORMAT: A1

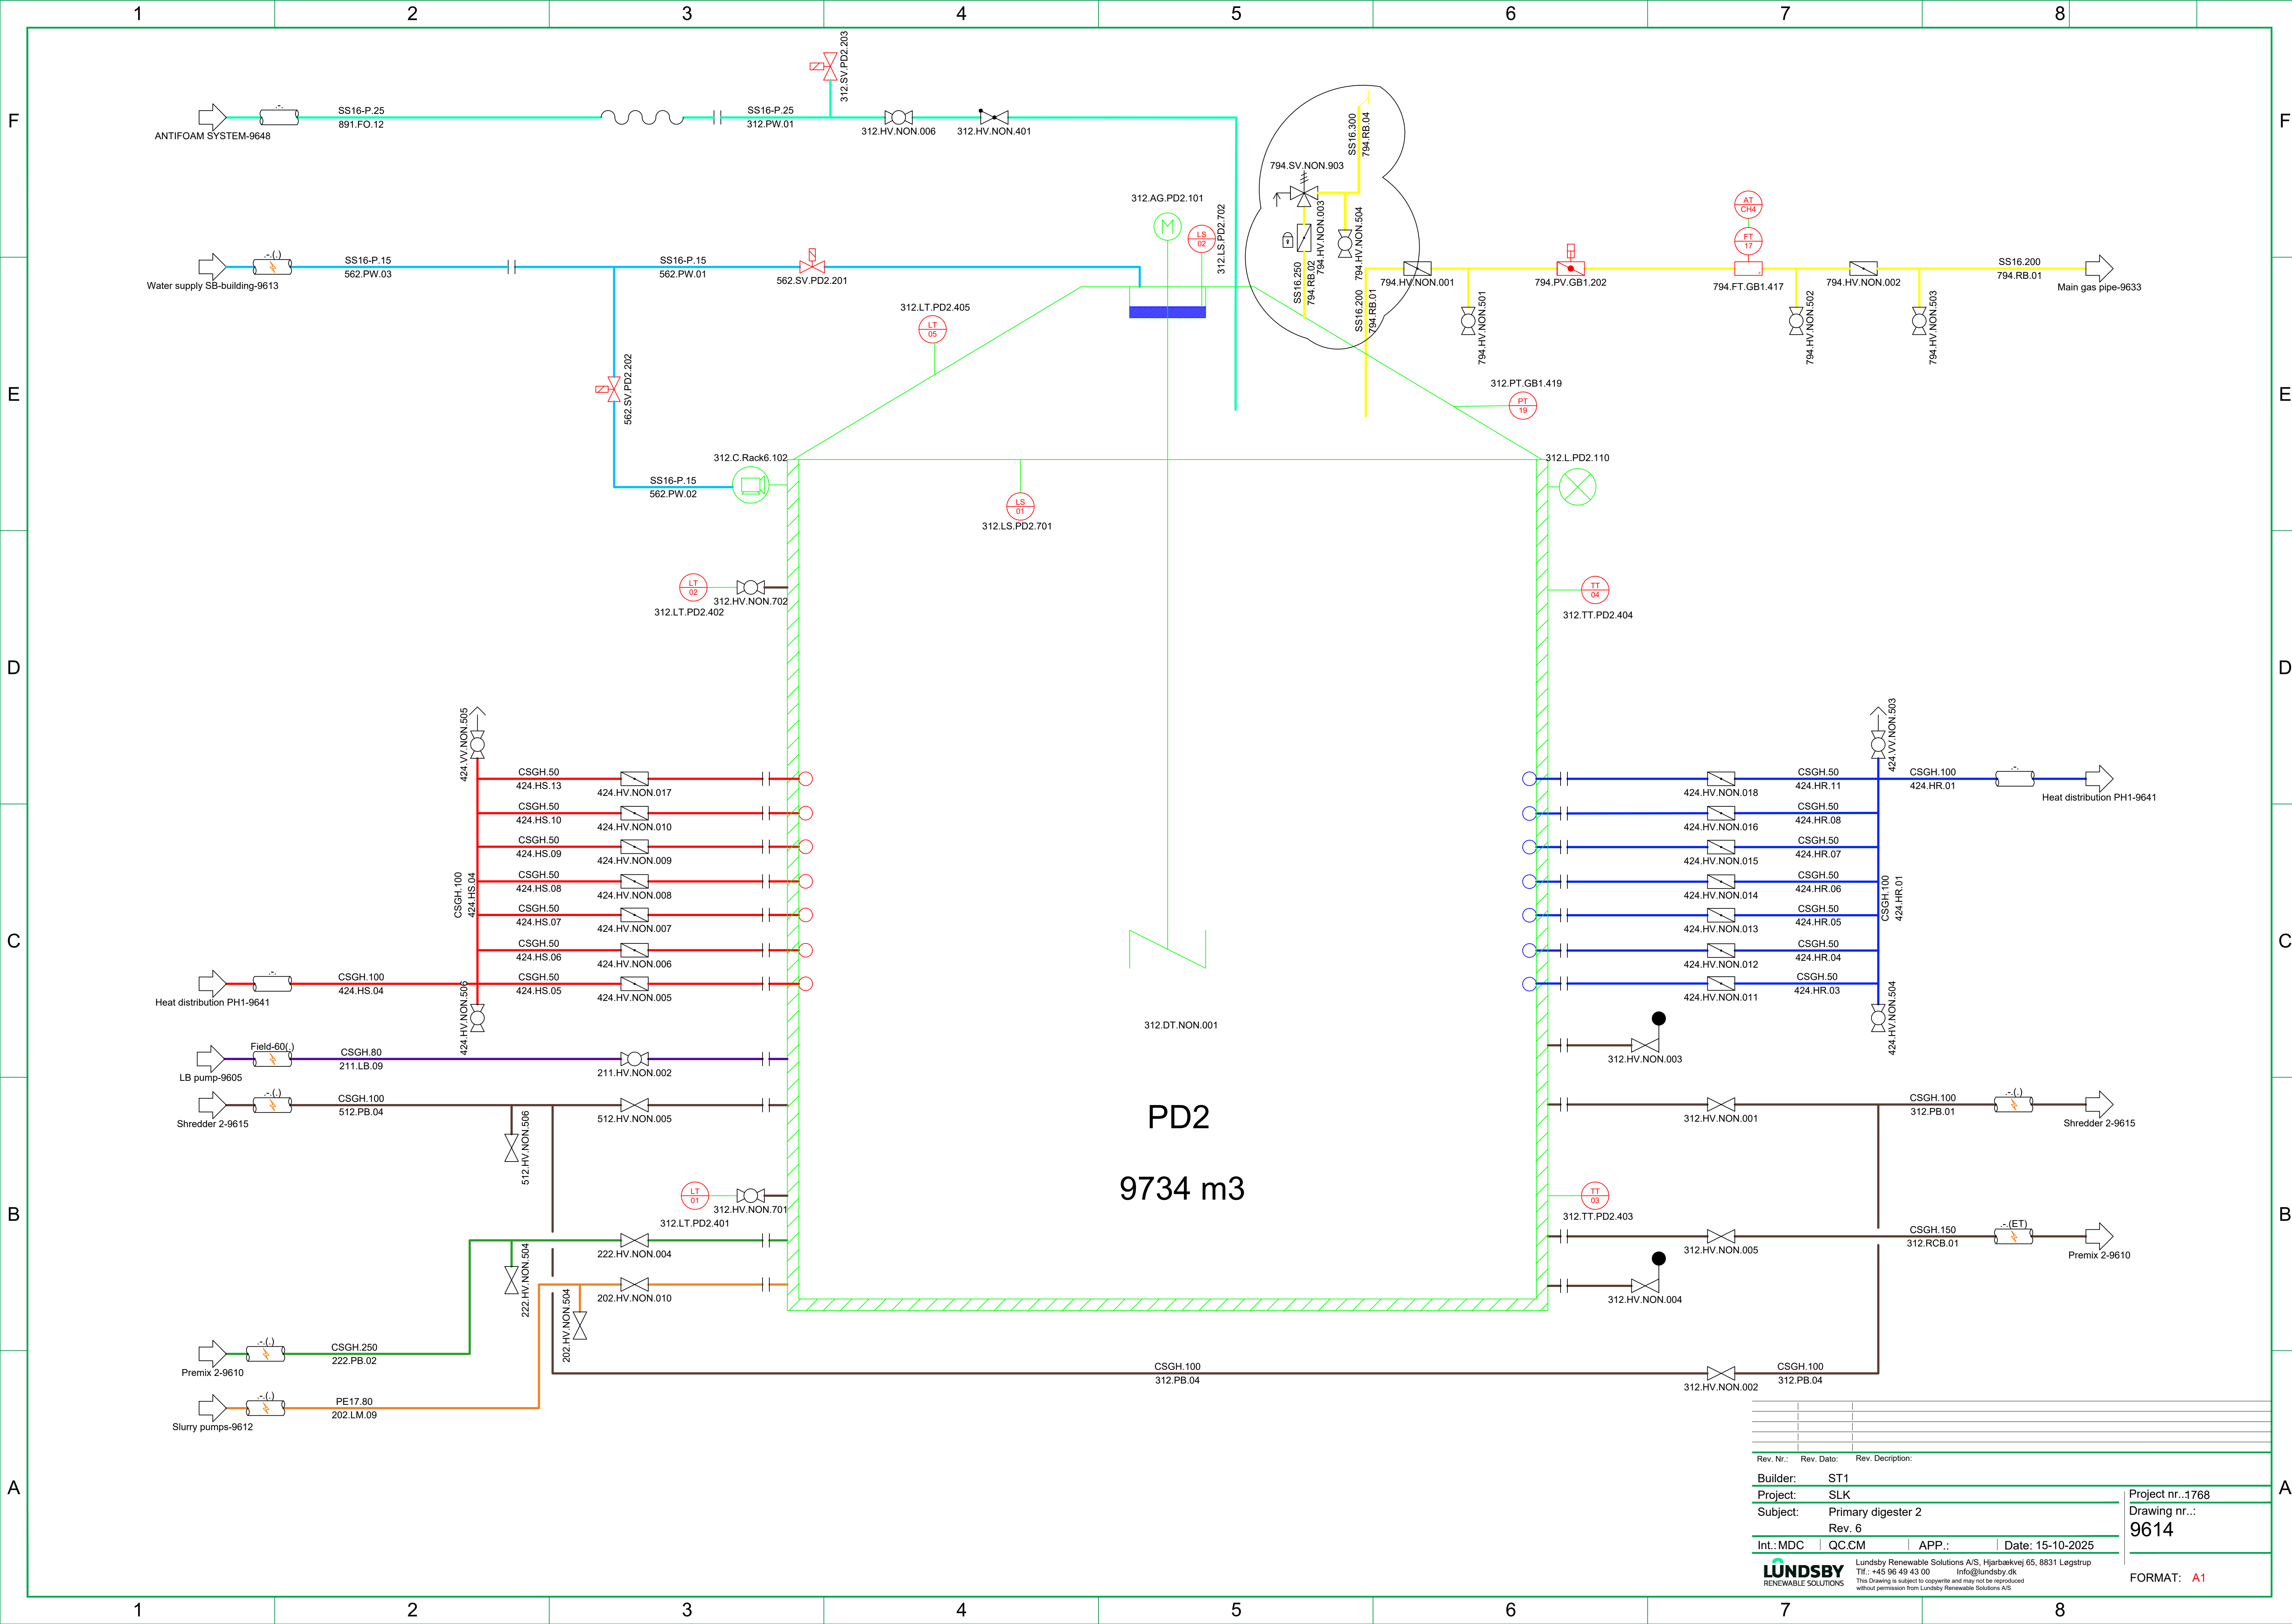


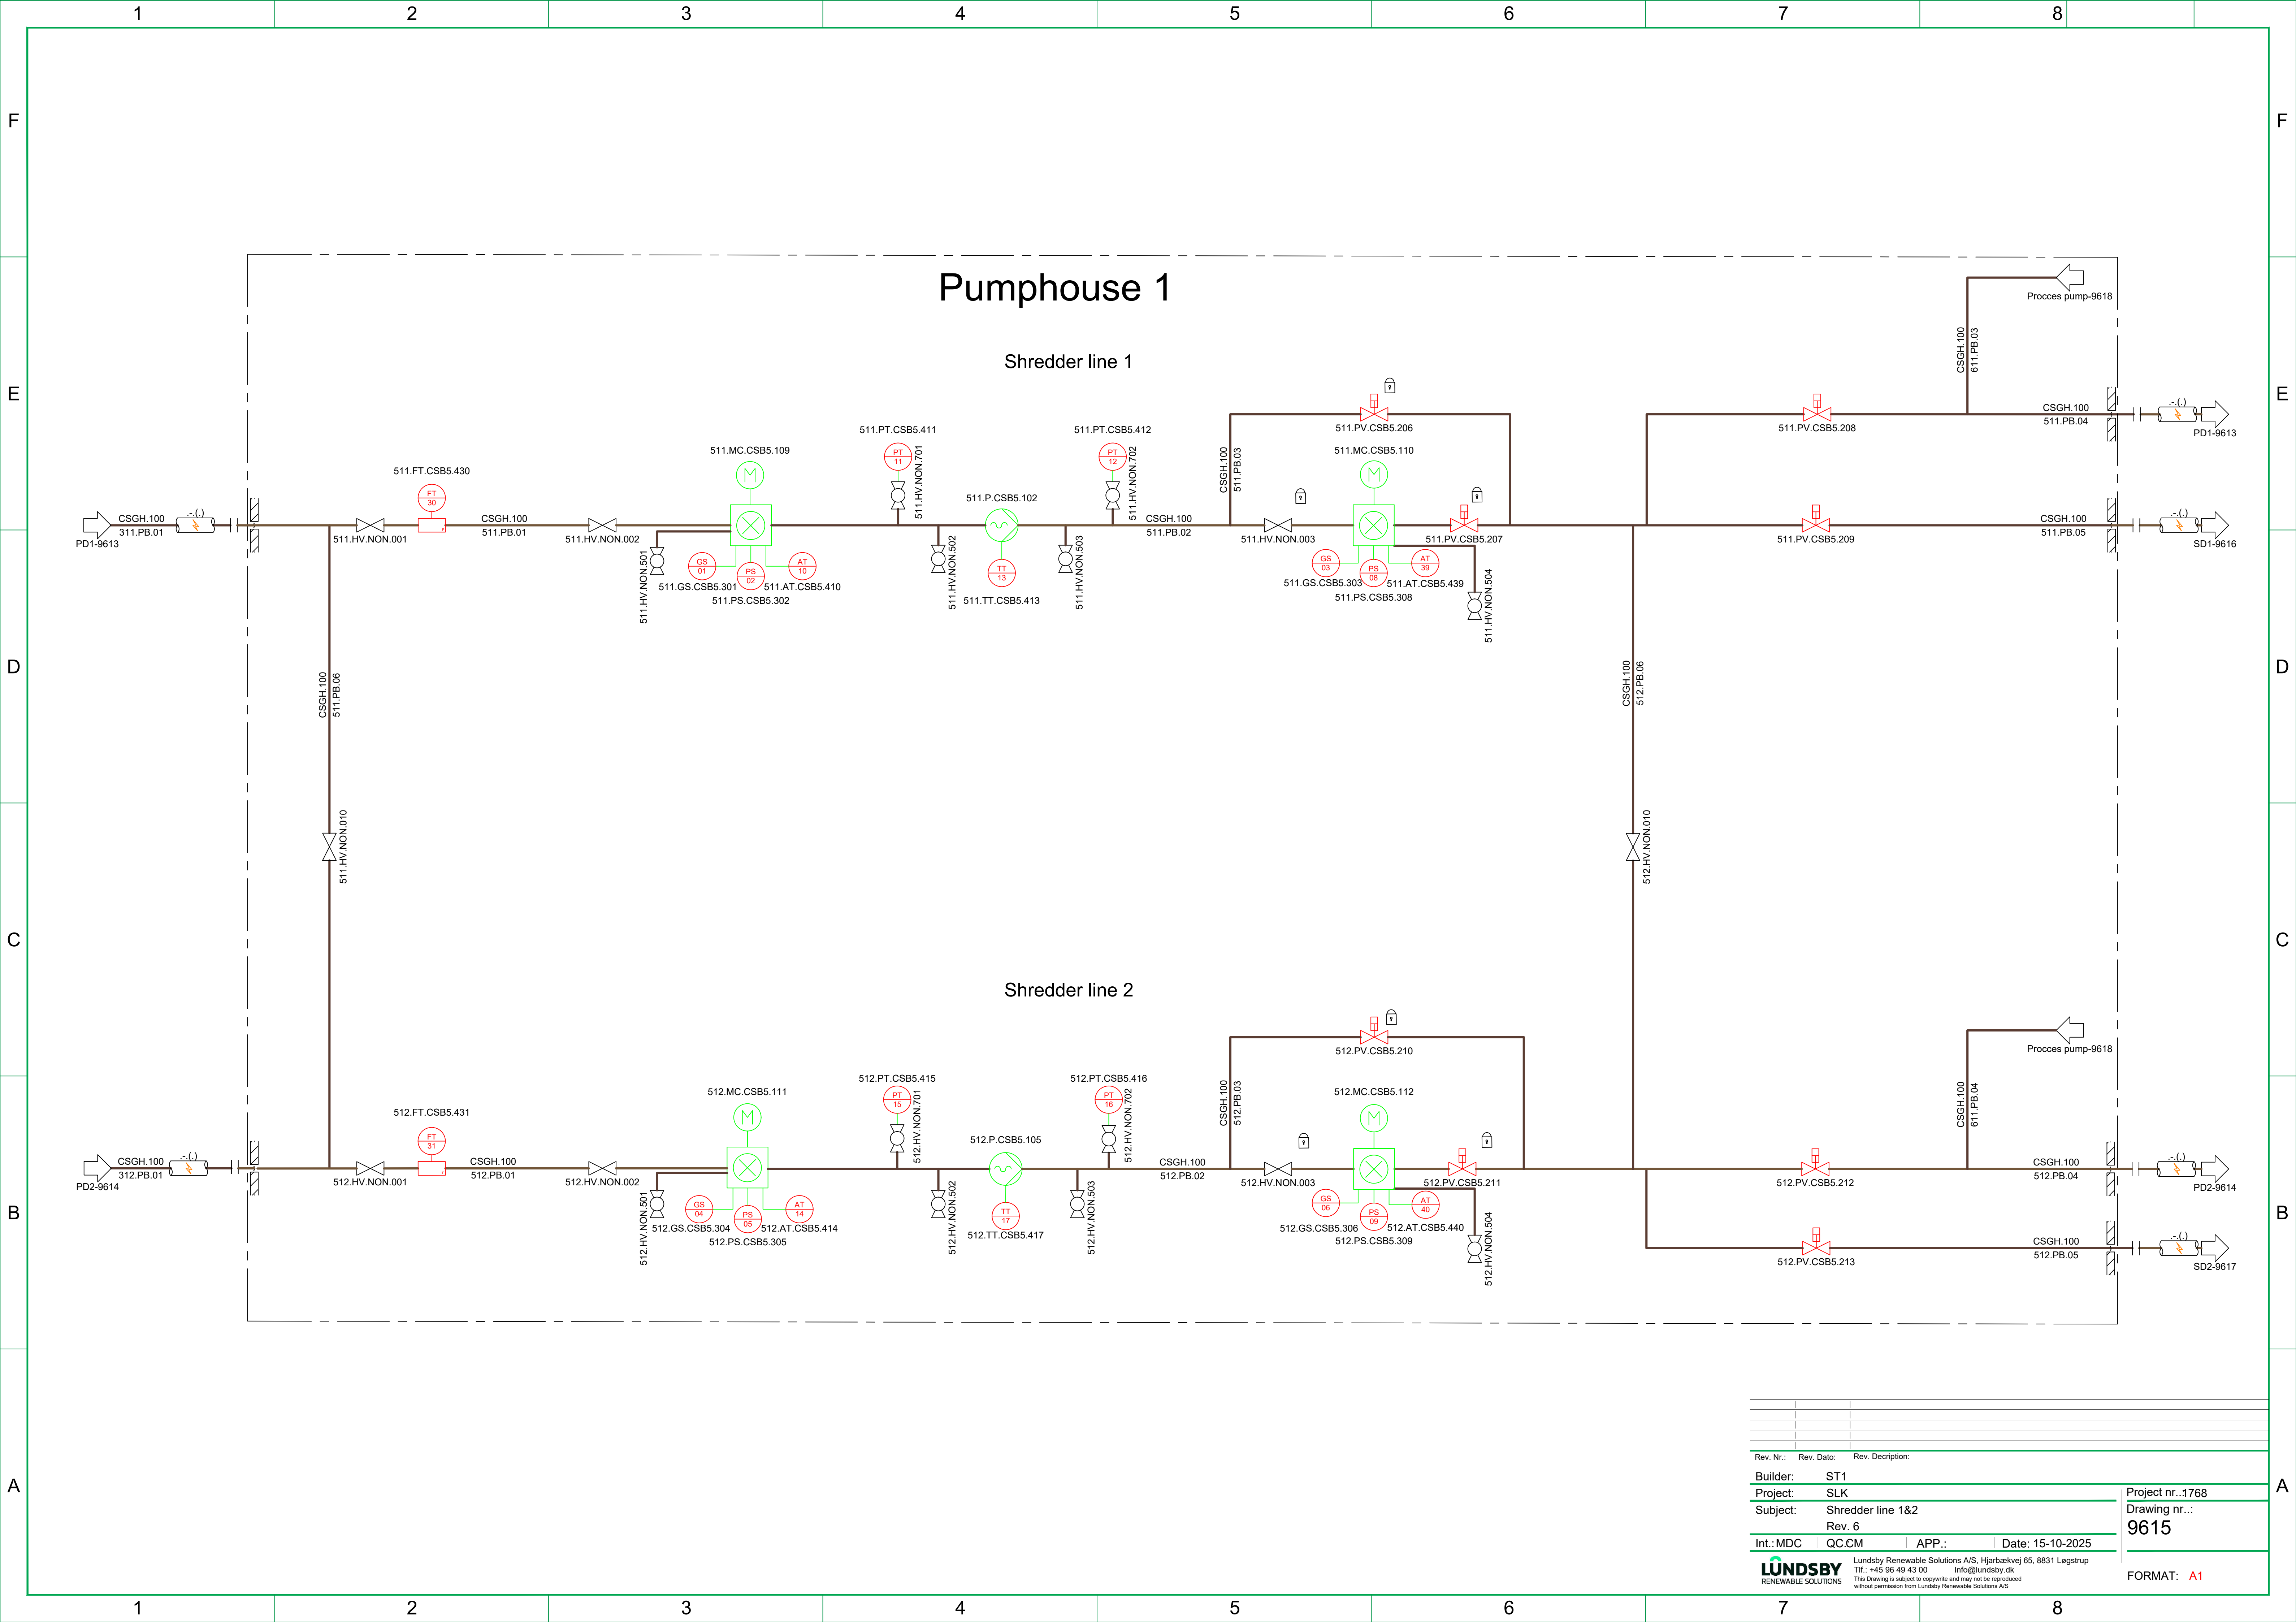


Rev. Nr.:	Rev. Dato:	Rev. Description:	
Builder:	ST1		
Project:	SLK		
Subject:	Shredder line 1&2		
	Rev. 6		
Int.:MDC	QC:CM	APP.:	Date: 15-10-2025
LUNDSBY RENEWABLE SOLUTIONS			Lundsby Renewable Solutions A/S, Hjarbrækvej 65, 8831 Lægstrup Tlf.: +45 96 49 43 00 Info@lundsby.dk This Drawing is subject to copyright and may not be reproduced without permission from Lundsby Renewable Solutions A/S
Project nr.:1768 Drawing nr.: 9615			FORMAT: A1

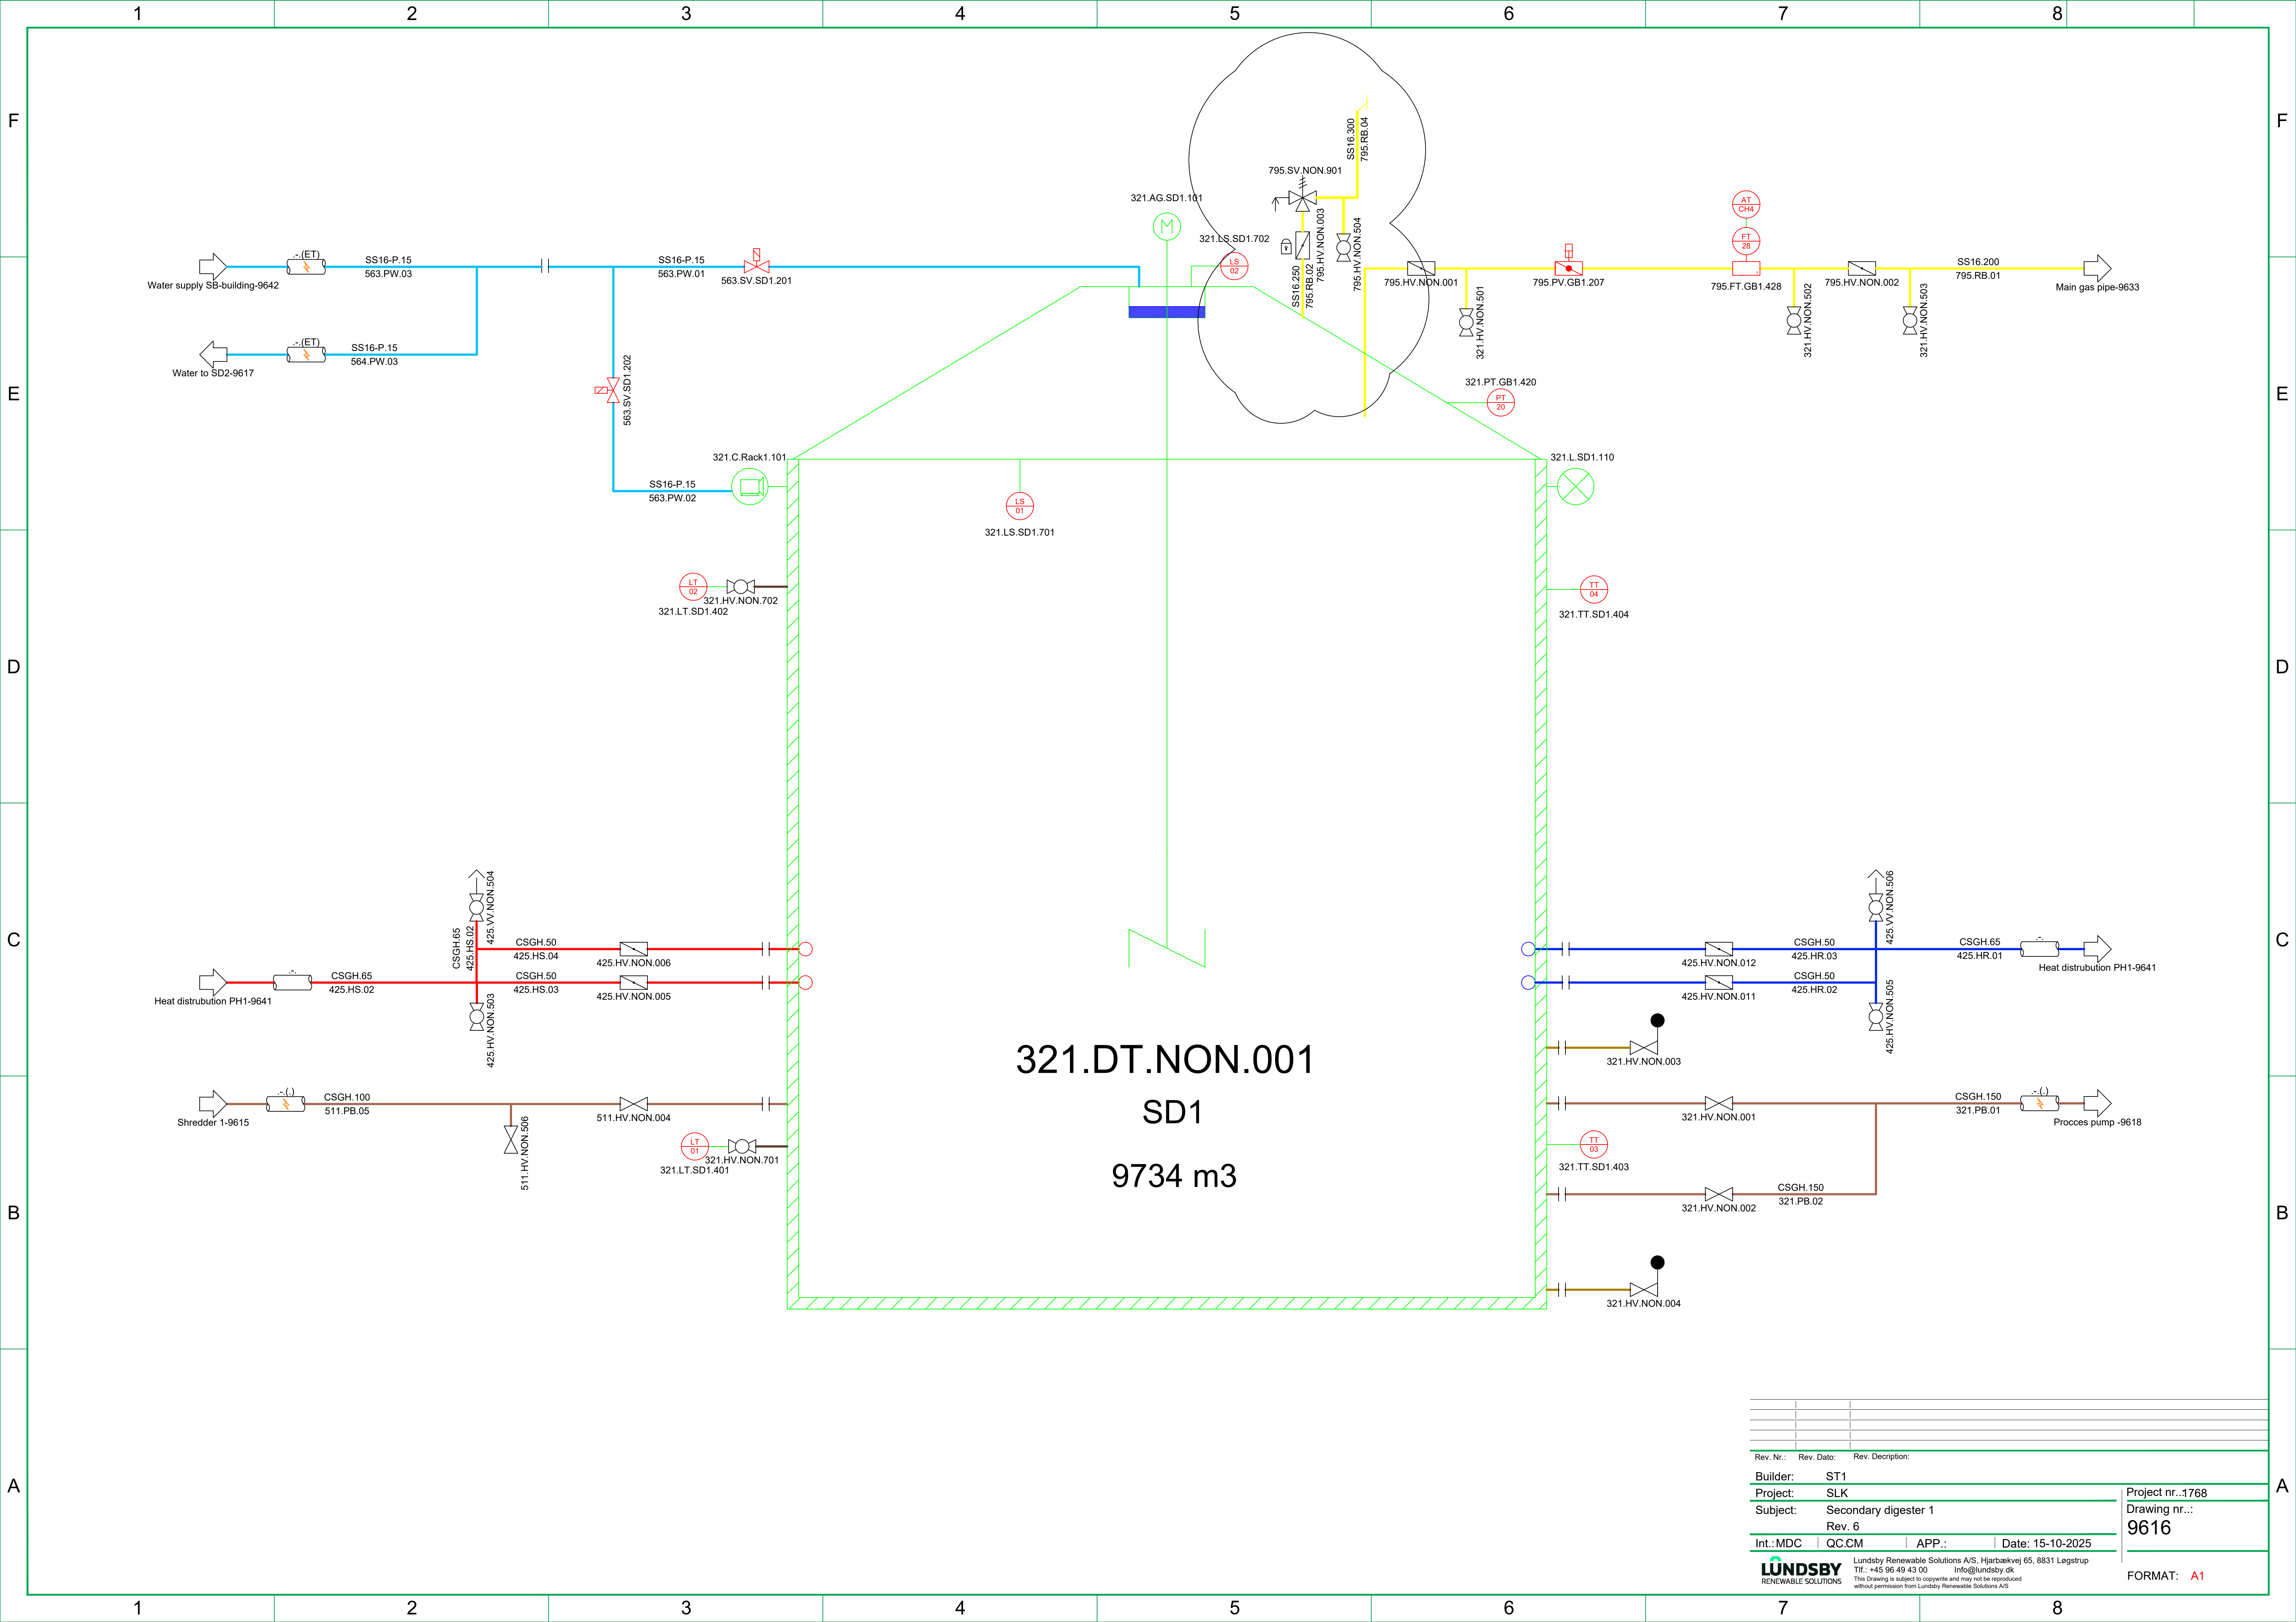


--	--	

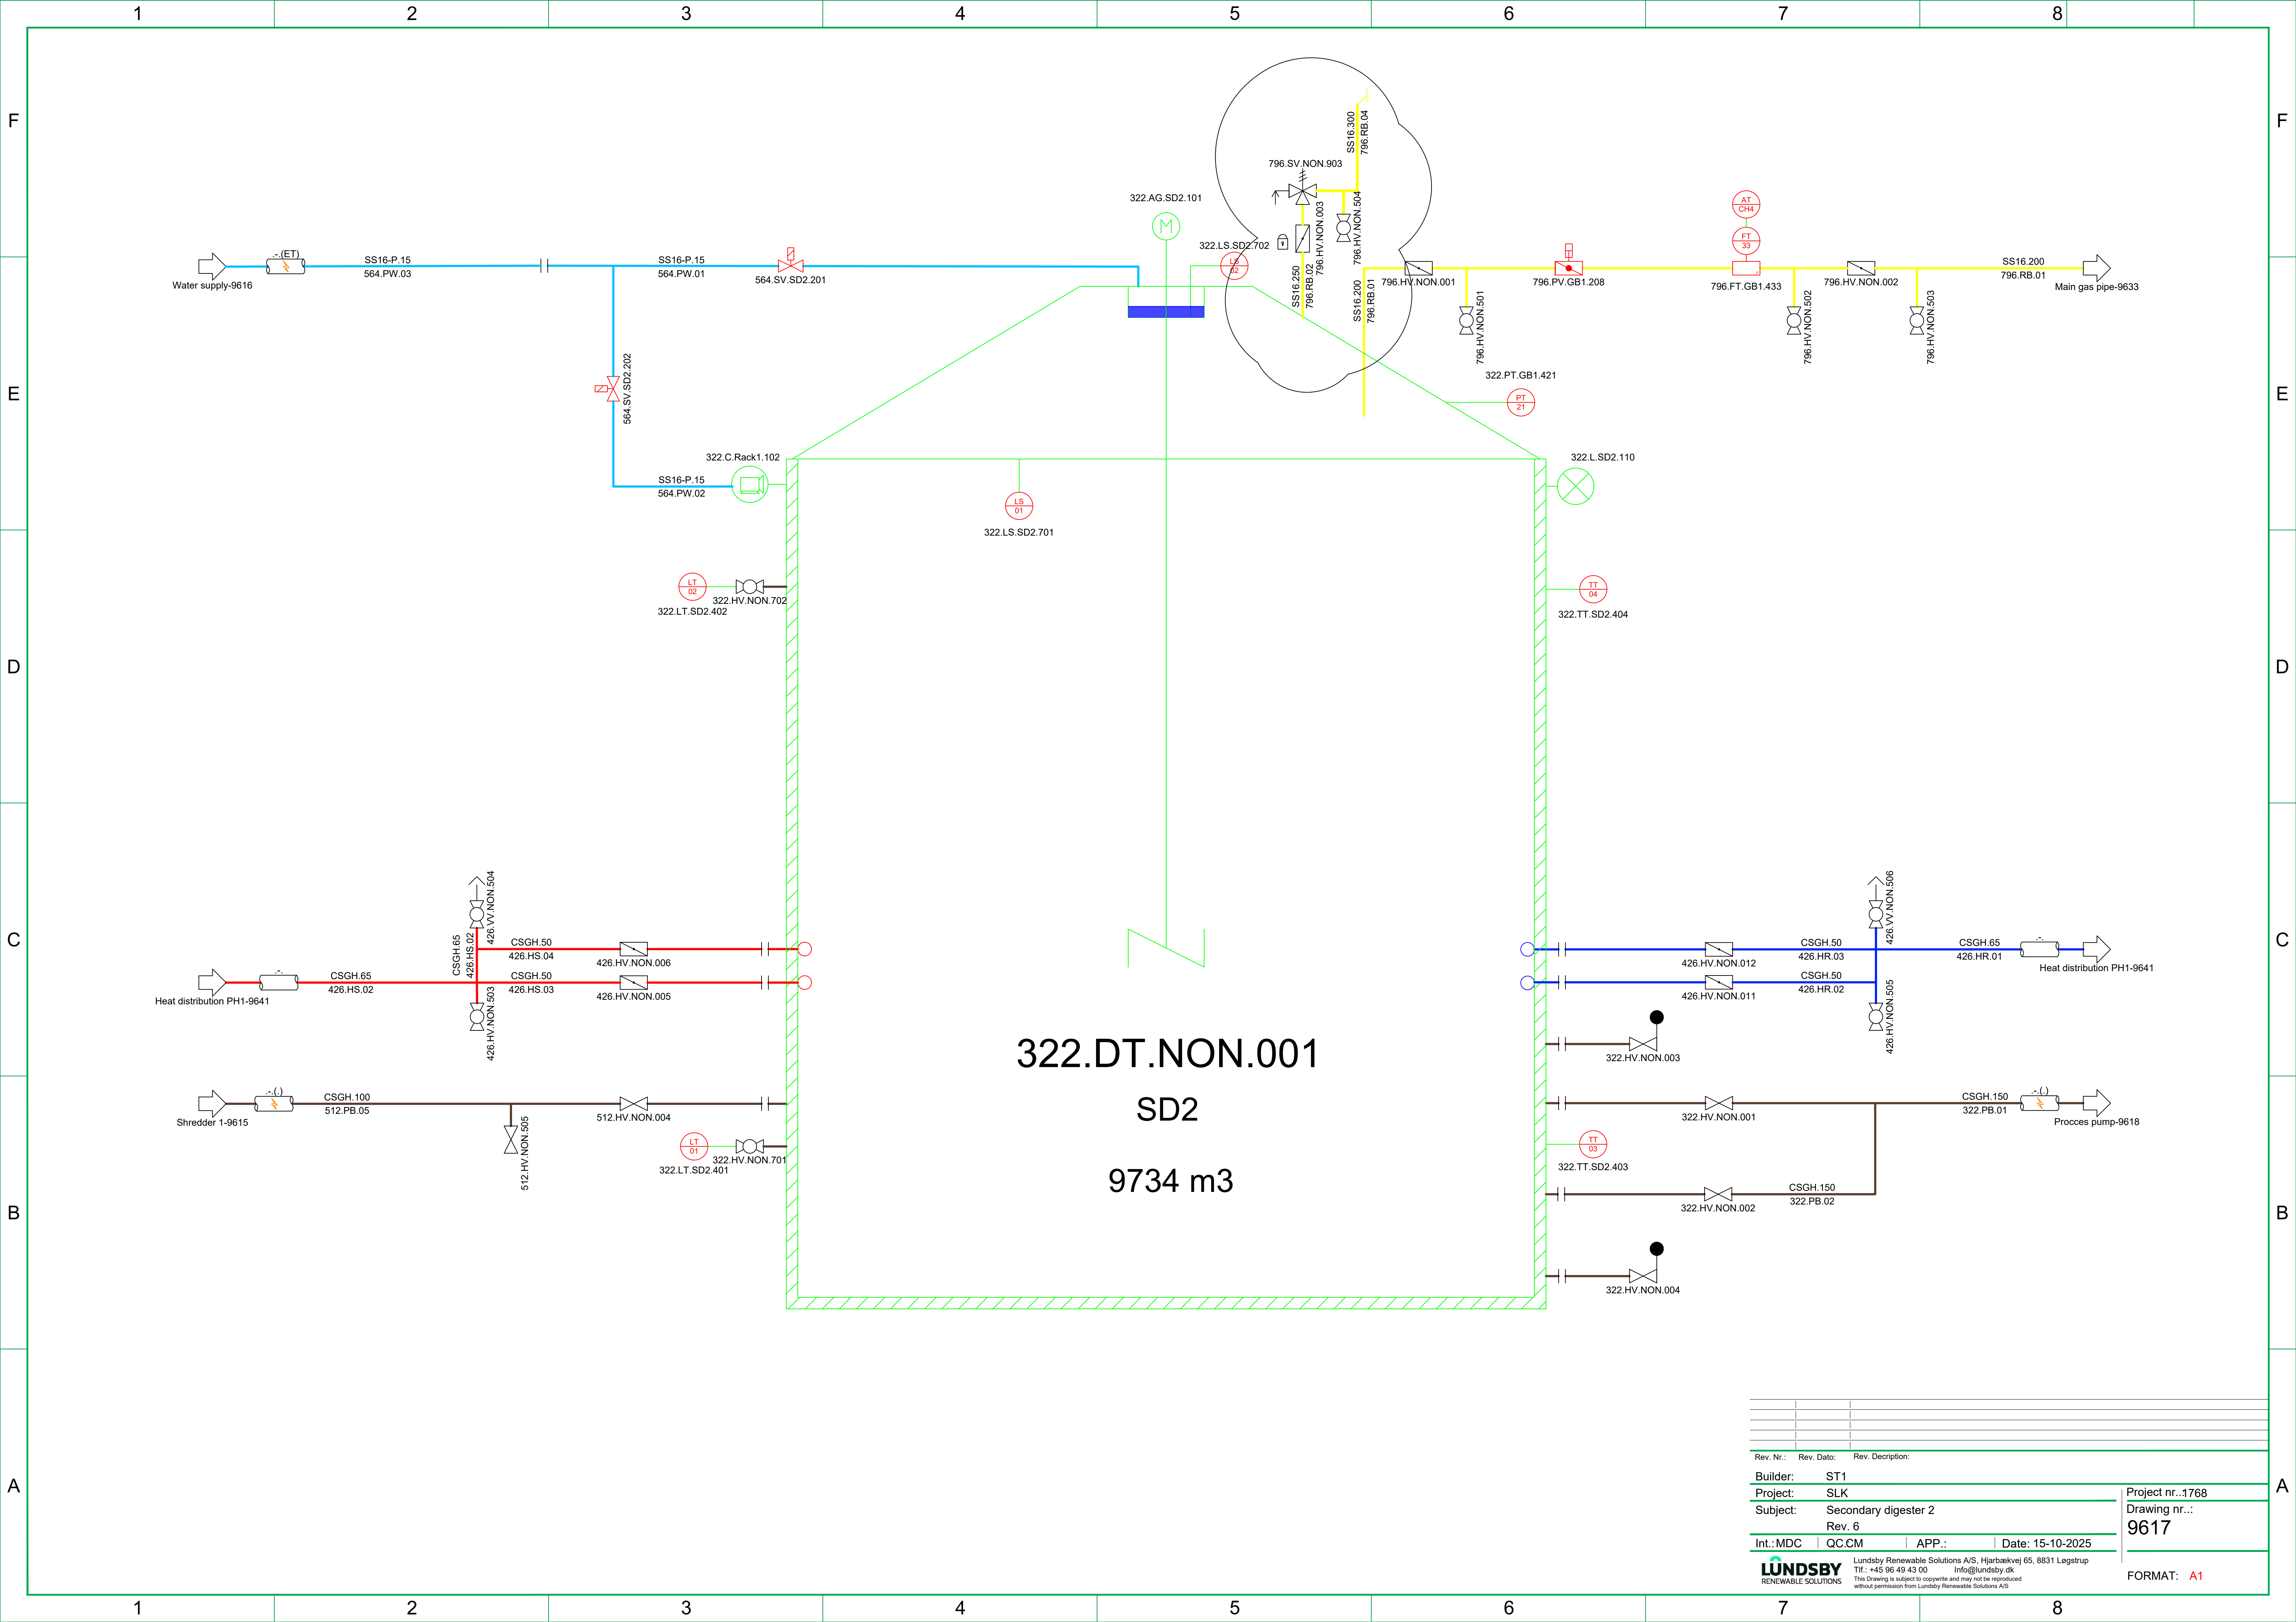

Rev. Nr.:	Rev. Dato:	Rev. Description:			
Builder:	ST1				
Project:	SLK				
Subject:	Secondary digester 2				
	Rev. 6				
Int.:MDC	QC:CM	APP.:	Date: 15-10-2025		
LUNDSBY RENEWABLE SOLUTIONS Lundsgby Renewable Solutions A/S, Hjarbækvej 65, 8831 Løgstrup Tlf.: +45 96 49 43 00 Info@lundsgby.dk This Drawing is subject to copyright and may not be reproduced without permission from Lundsgby Renewable Solutions A/S					
Project nr...1768 Drawing nr.: 9617					FORMAT: A1

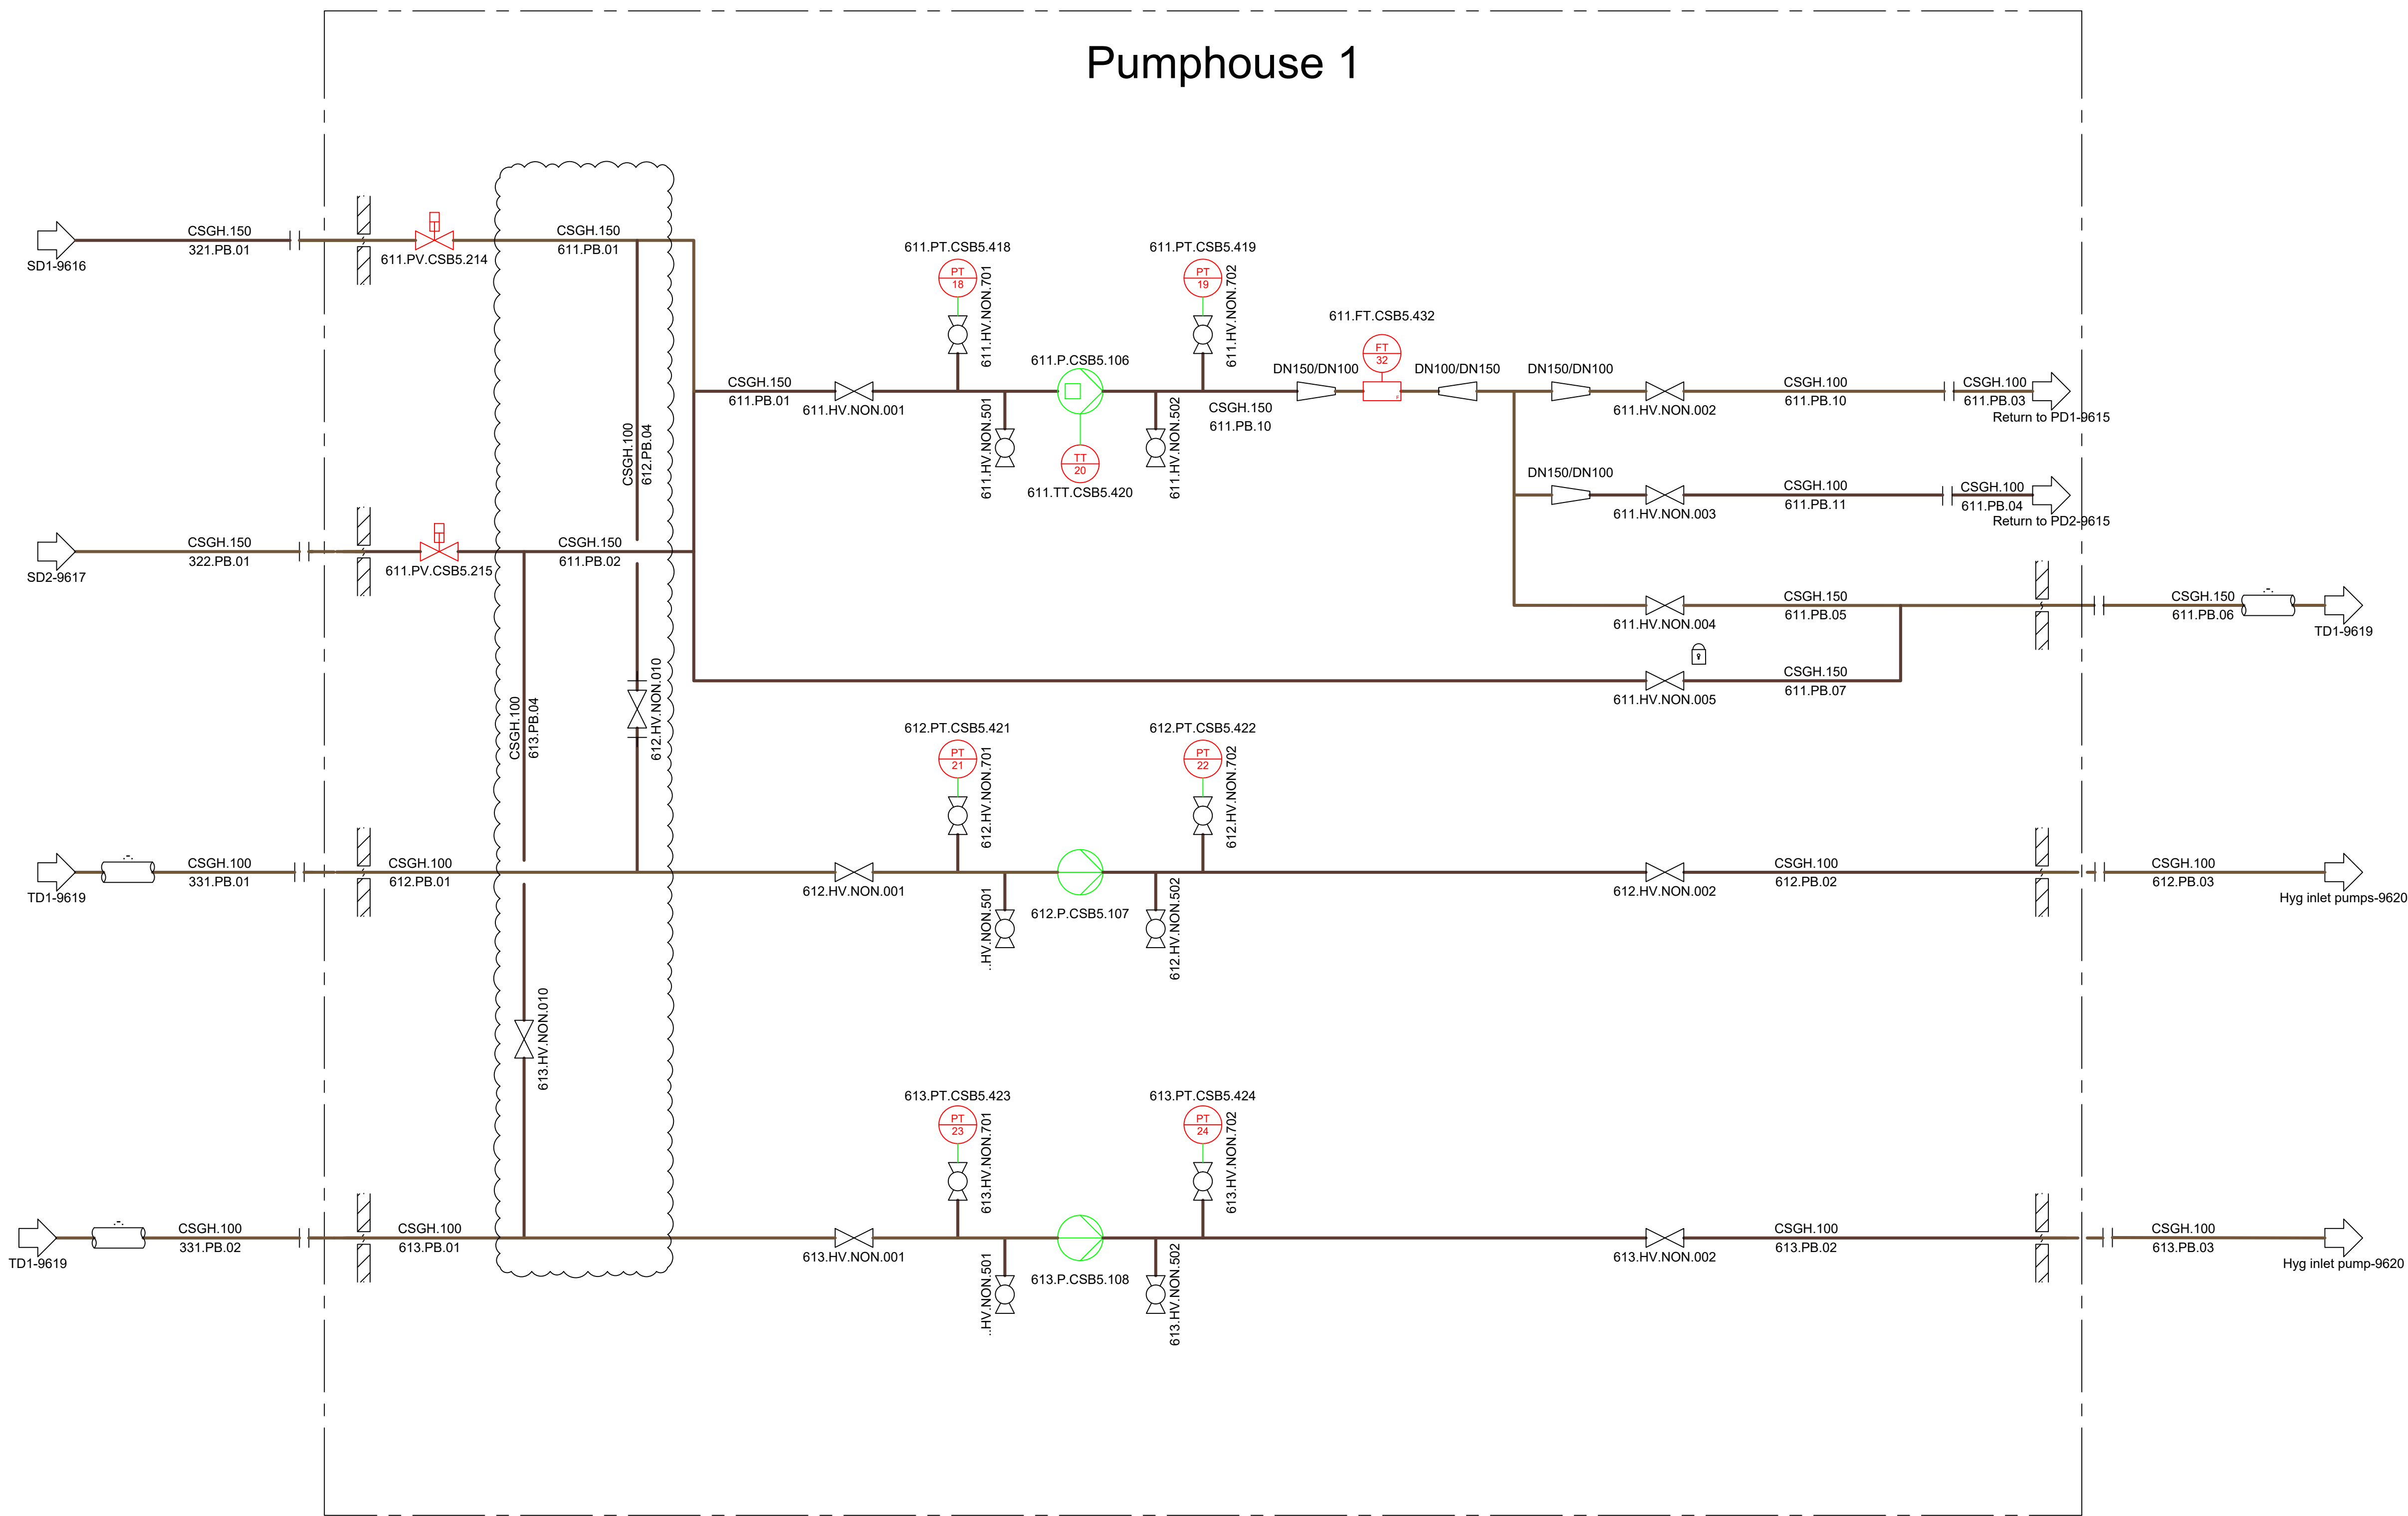


Rev. Nr.:	Rev. Dato:	Rev. Description:	
Builder:	ST1		
Project:	SLK		
Subject:	Procces pumps		
	Rev. 6		
Int.:MDC	QC.CM	APP.:	Date: 15-10-2025
LUNDSBY RENEWABLE SOLUTIONS			Lundsby Renewable Solutions A/S, Hjarbækvej 65, 8831 Løgstrup Tlf.: +45 96 49 43 00 Info@lundsby.dk This Drawing is subject to copyright and may not be reproduced without permission from Lundsby Renewable Solutions A/S
Project nr.:1768 Drawing nr.: 9618			FORMAT: A1

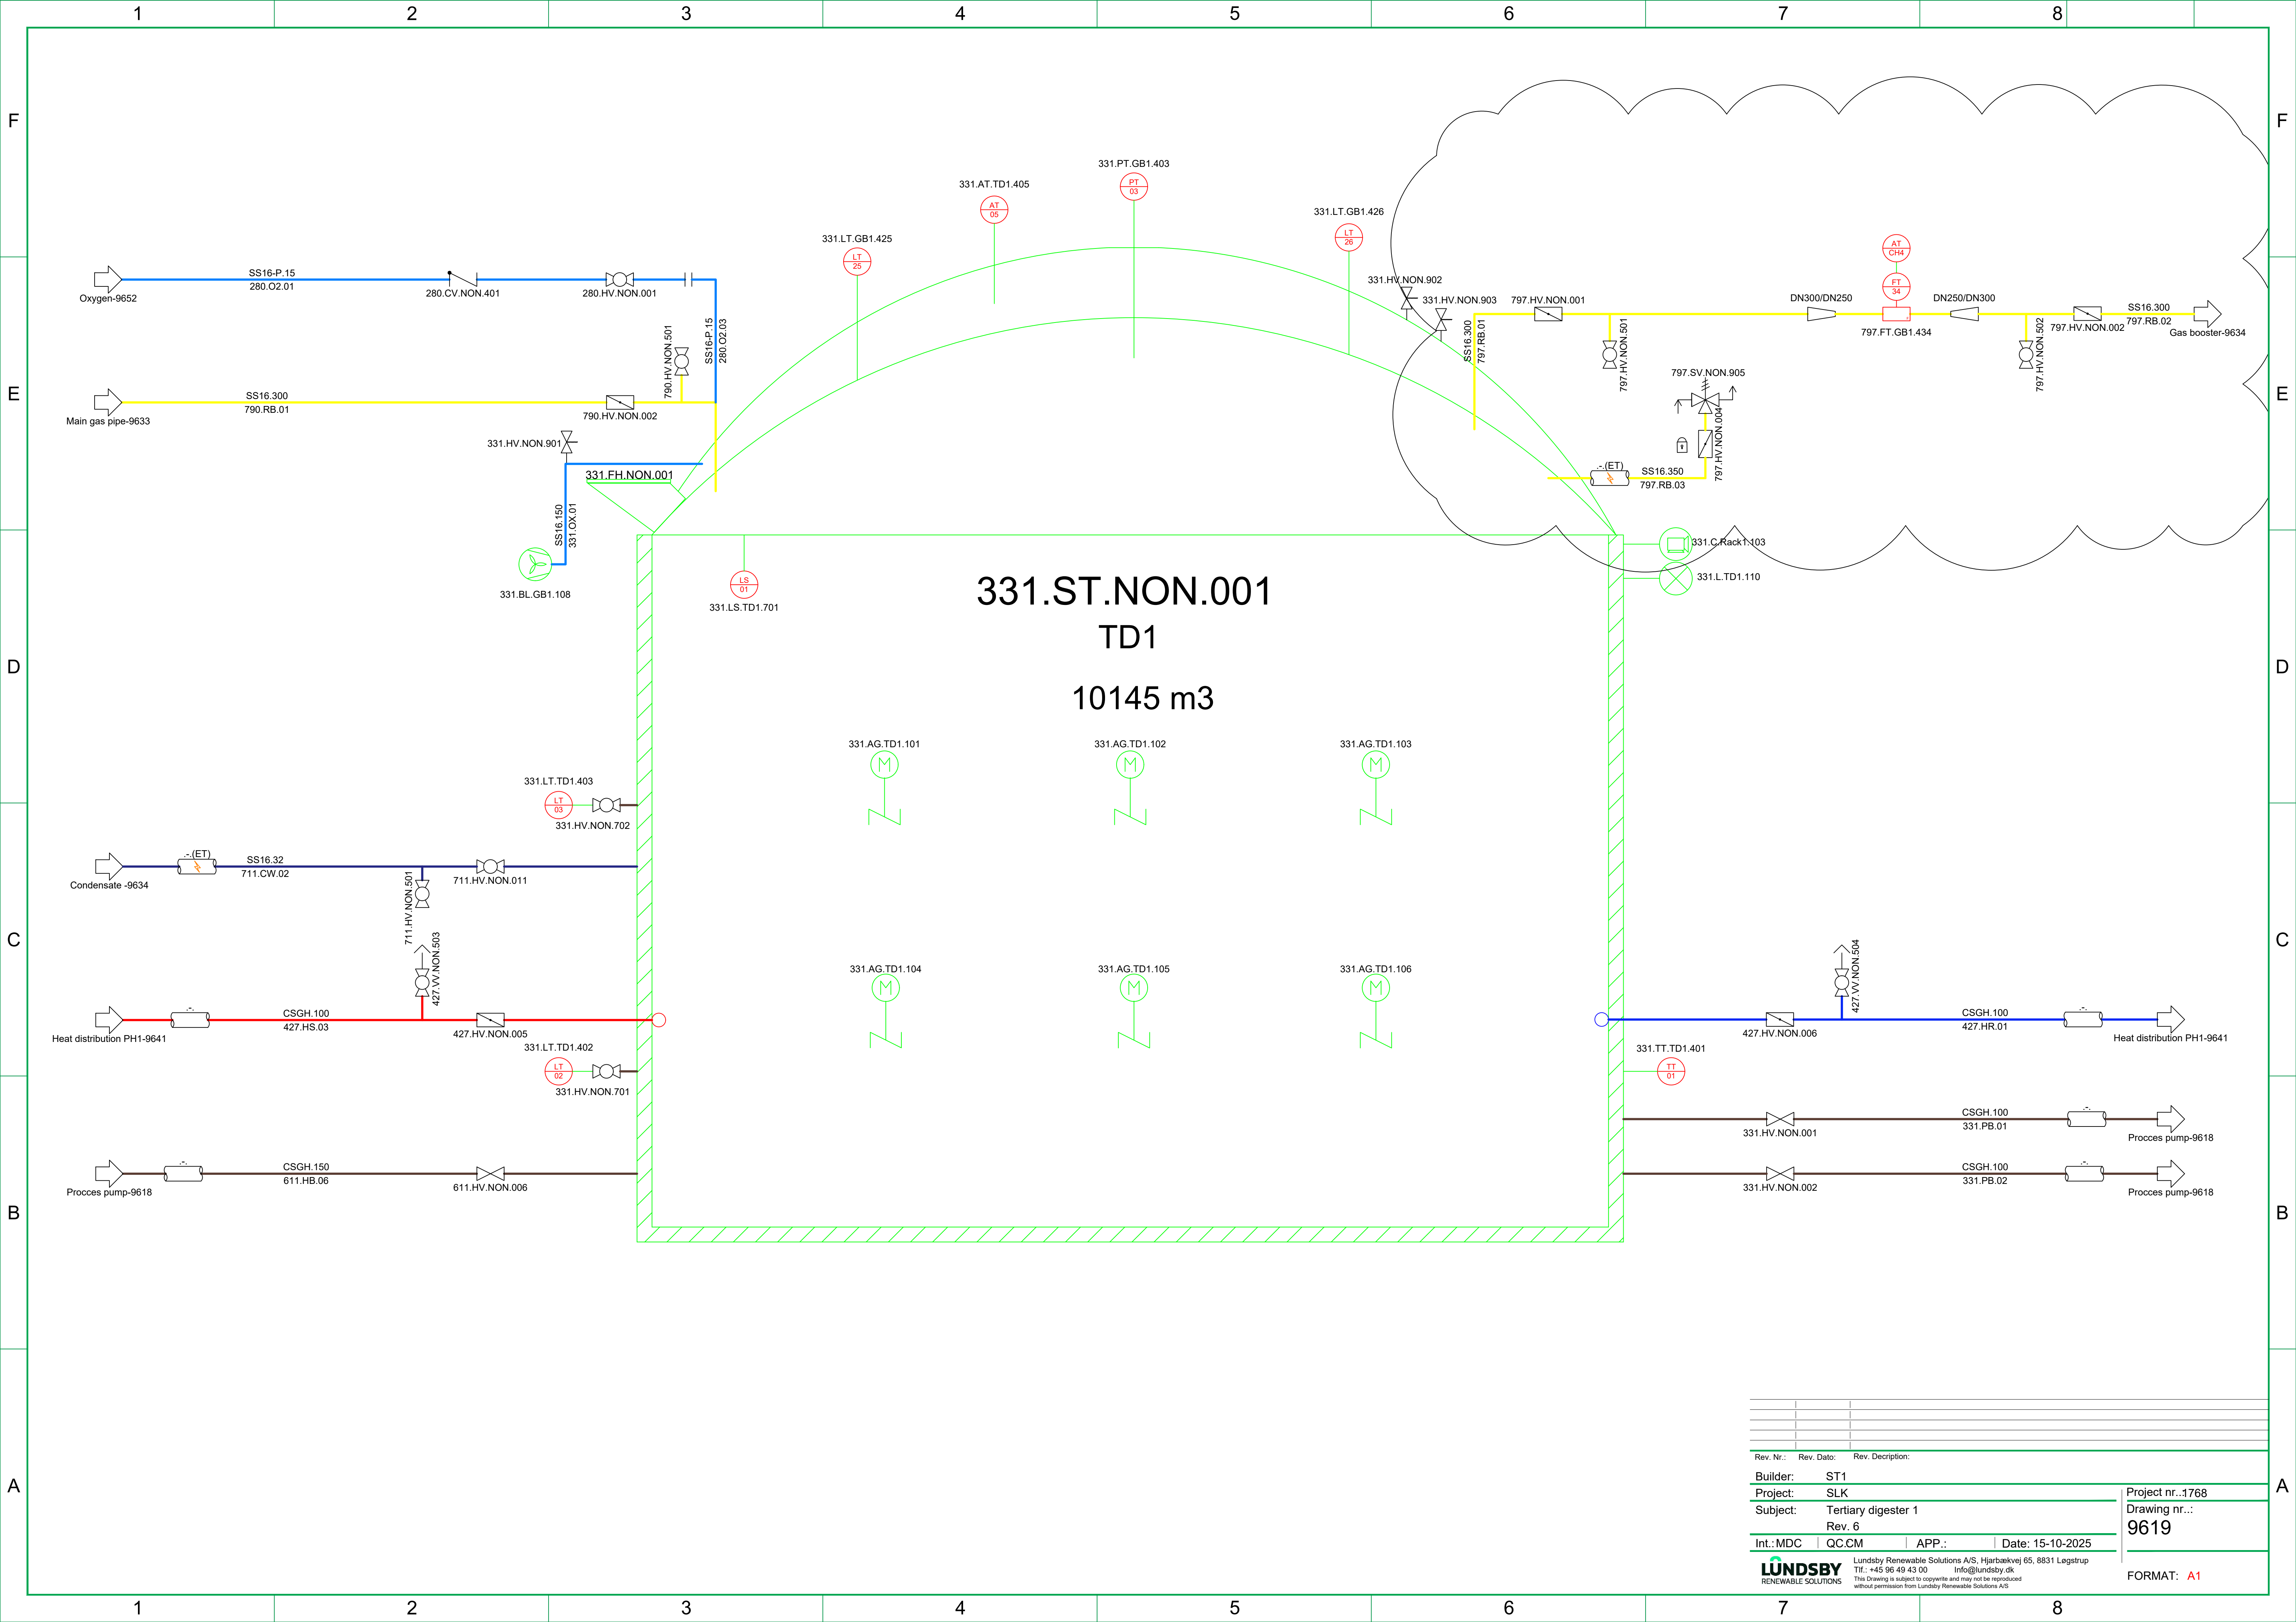


Tech Building


Inlet pumps

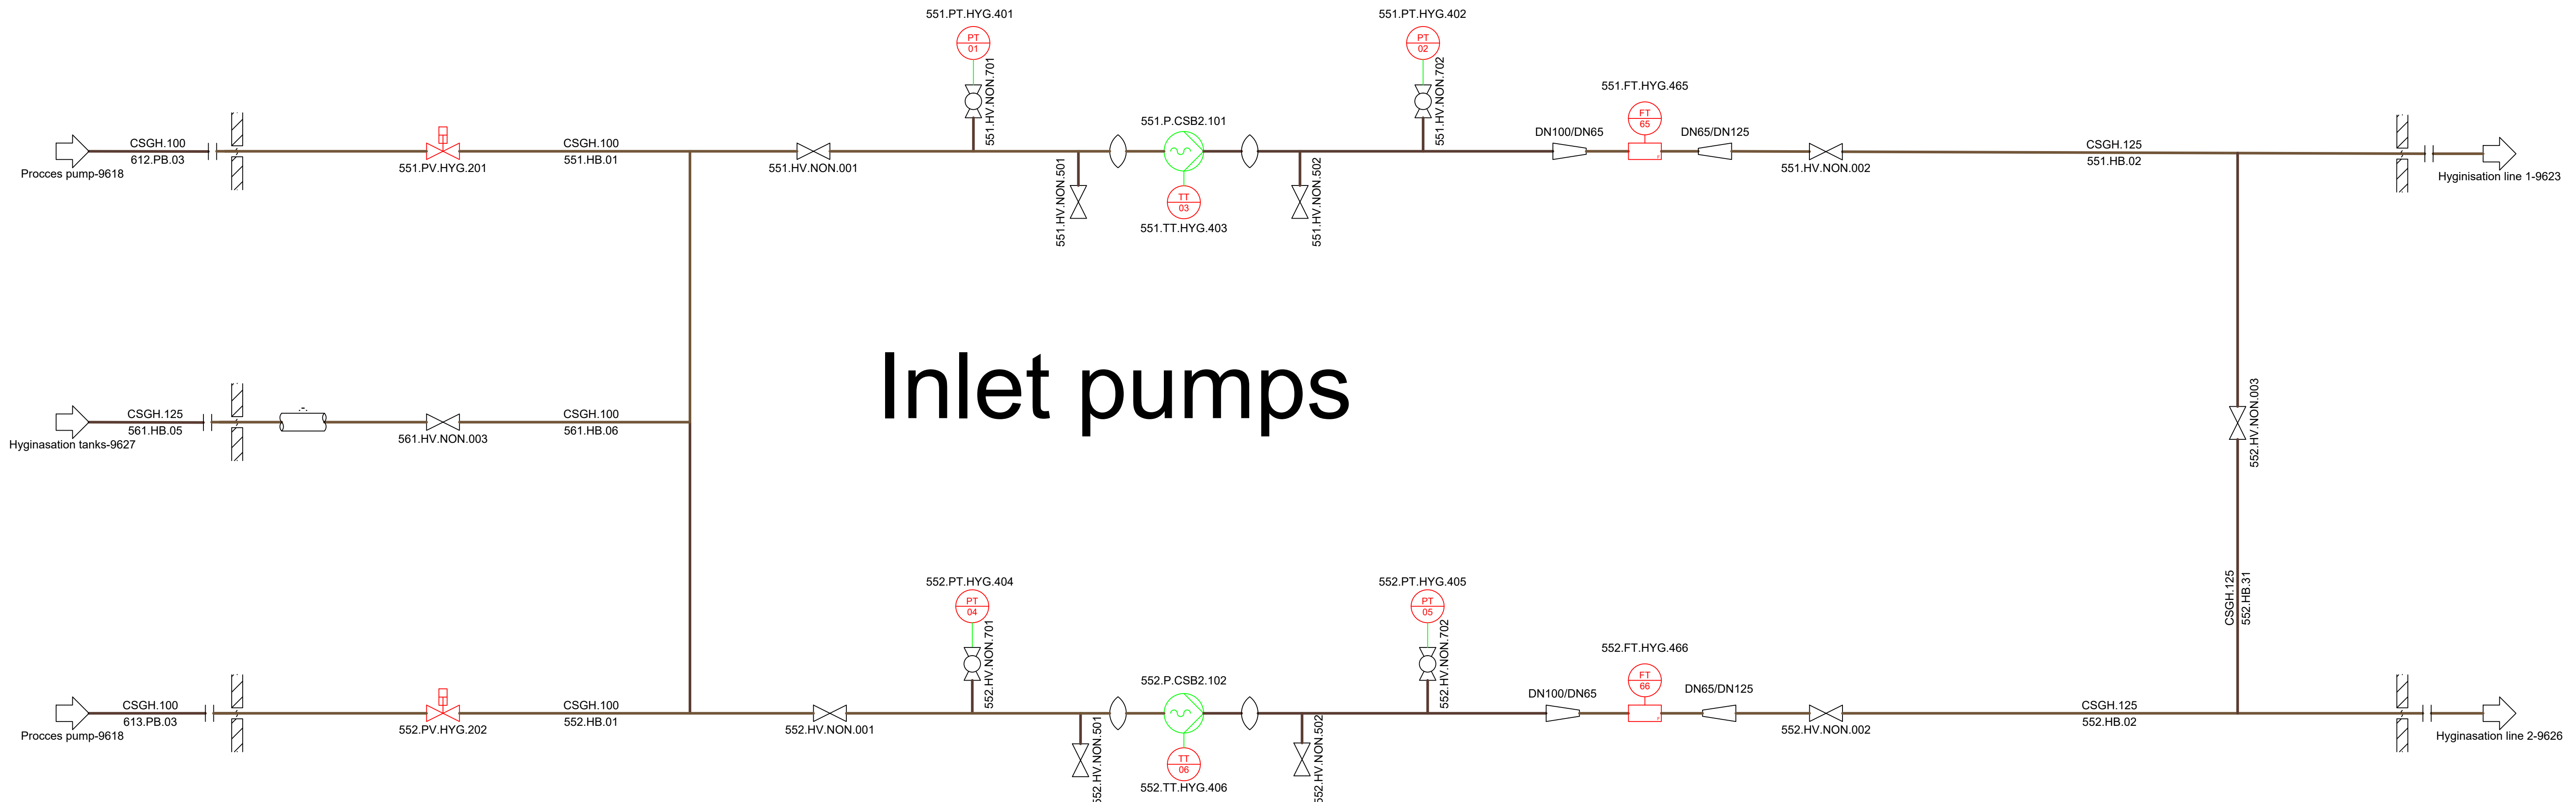


Rev. Nr.:	Rev. Dato:	Rev. Description:	
Builder:	ST1		
Project:	SLK		
Subject:	Hyginisation inlet pumps		
	Rev. 6		
Int.:MDC	QC:CM	APP.:	Date: 15-10-2025
LUNDSBY RENEWABLE SOLUTIONS			Lundsby Renewable Solutions A/S, Hjarbækvej 65, 8831 Løgstrup Tlf.: +45 96 49 43 00 Info@lundsby.dk This Drawing is subject to copyright and may not be reproduced without permission from Lundsby Renewable Solutions A/S
			Project nr.:1768 Drawing nr.: 9620 FORMAT: A1

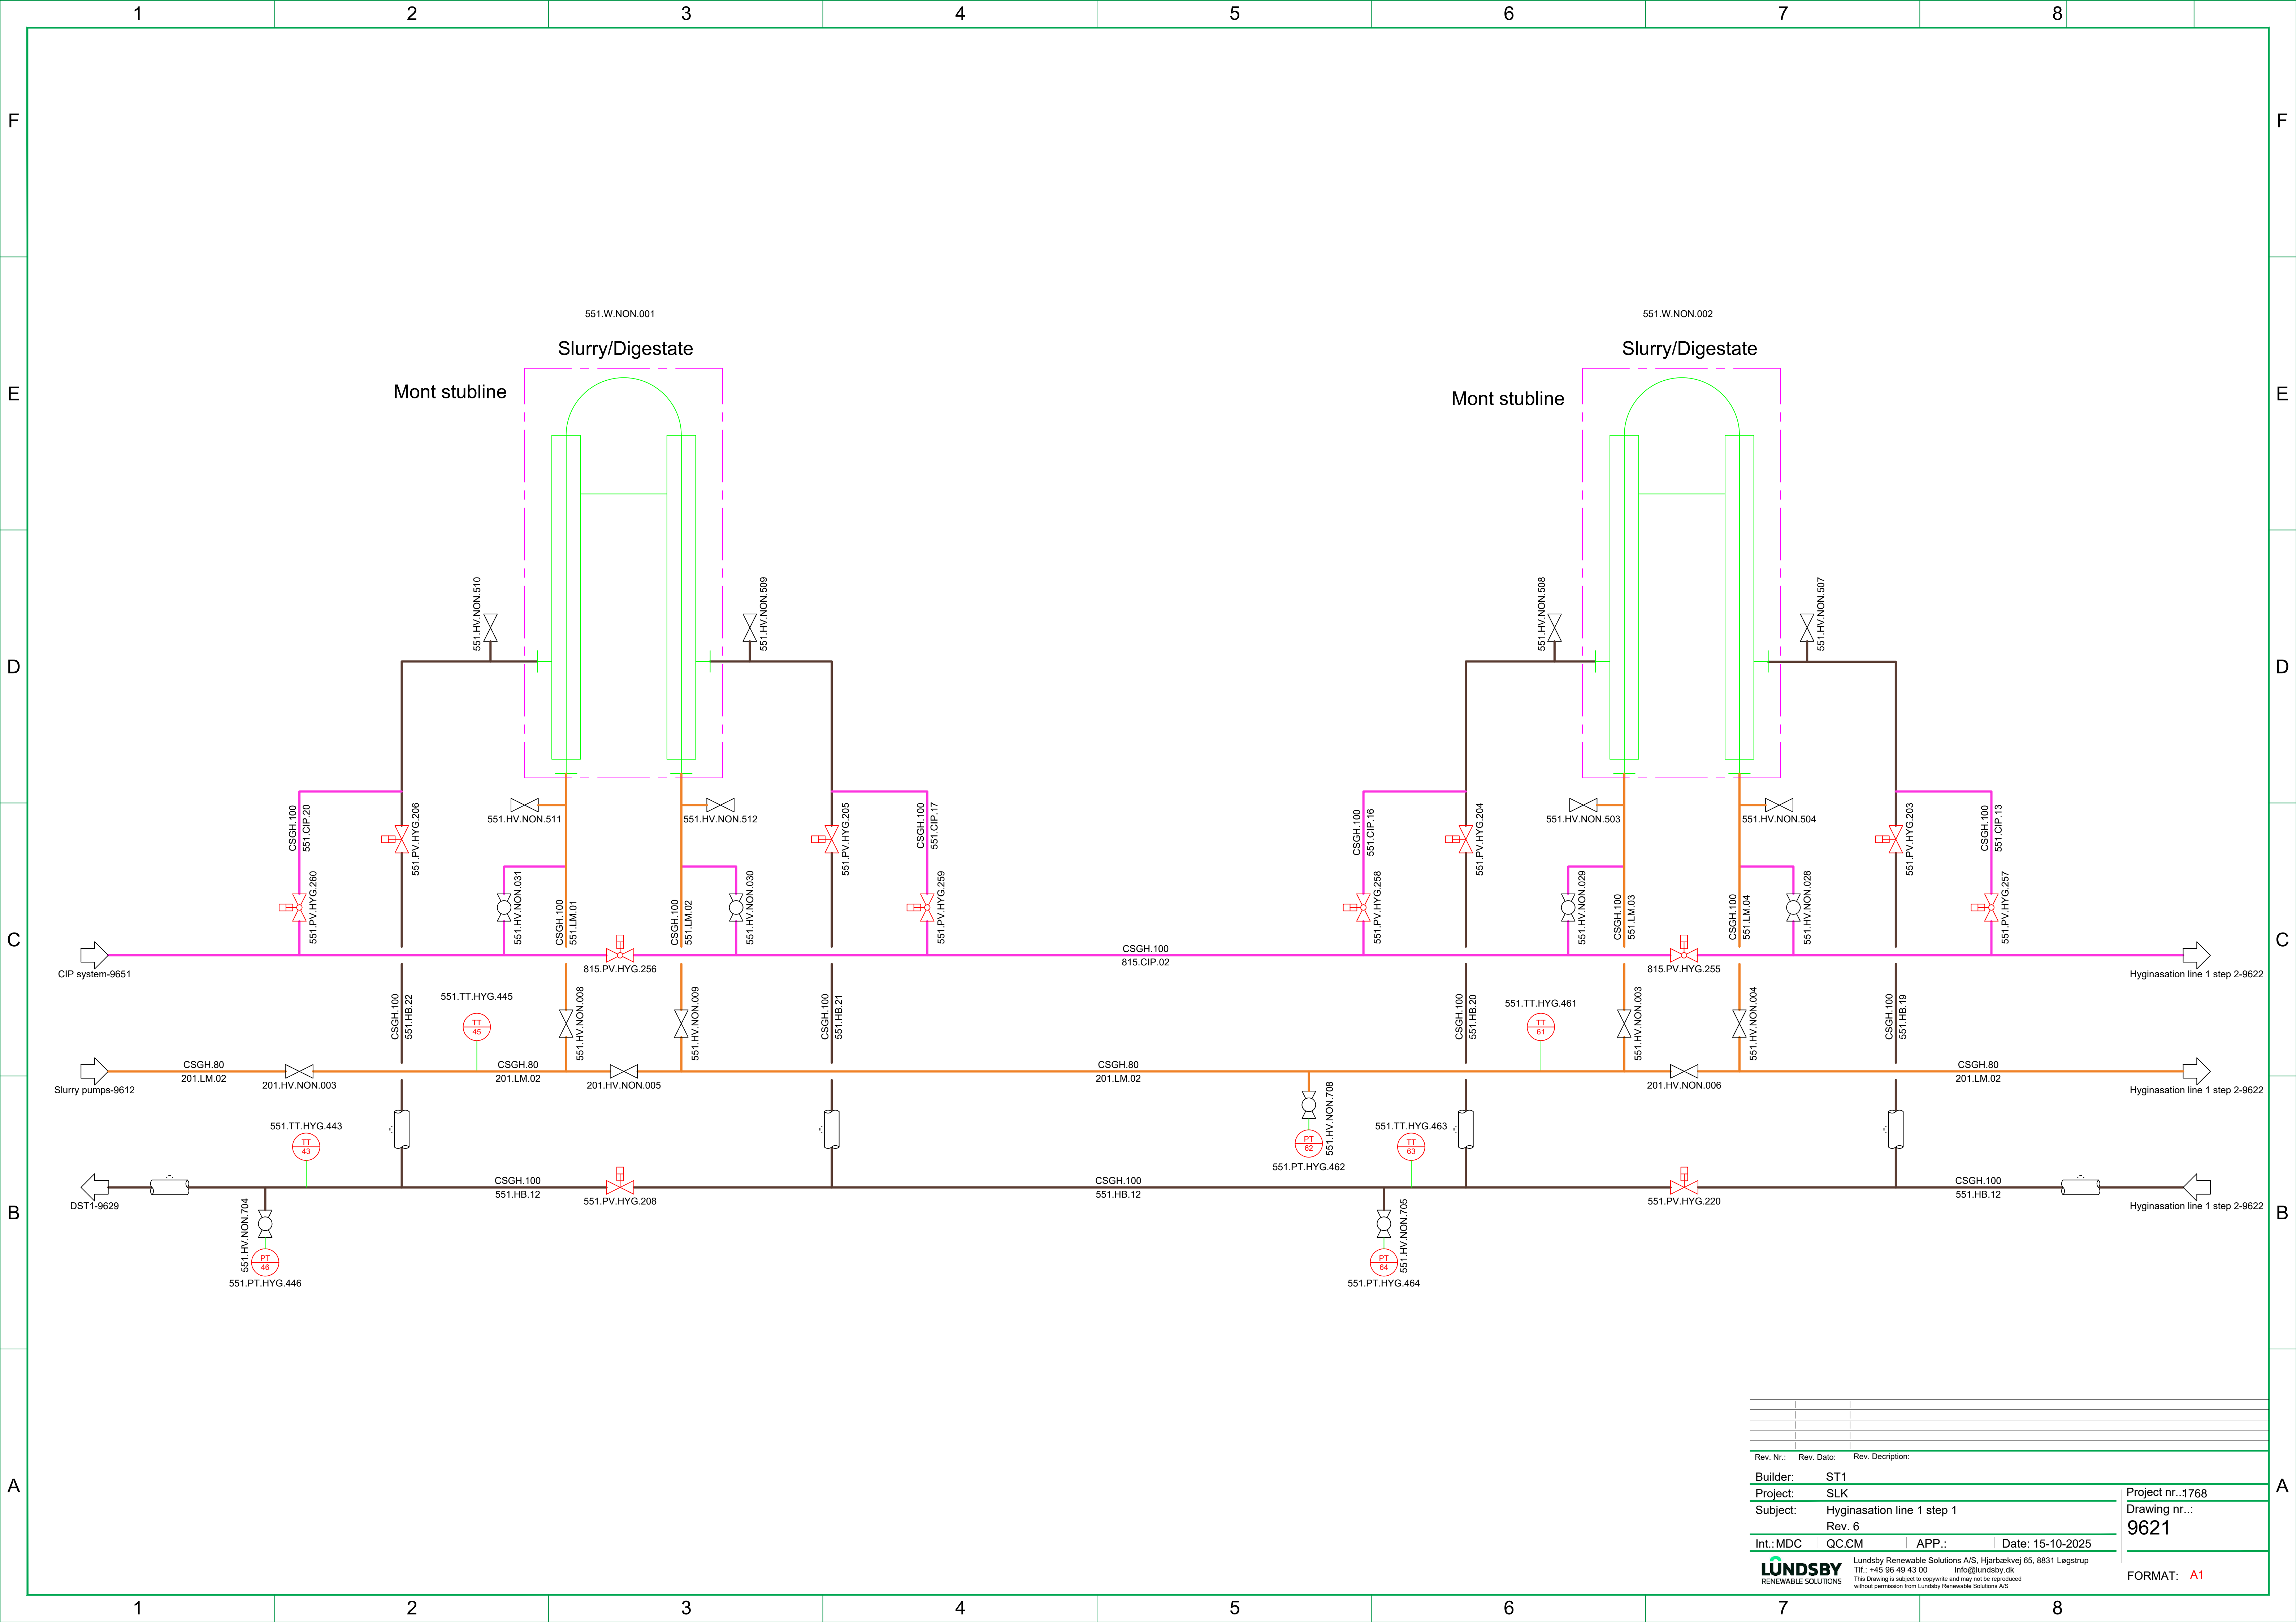


Rev. Nr.:	Rev. Dato:	Rev. Description:
Builder:	ST1	
Project:	SLK	
Subject:	Hyginasation line 1 step 1	
Rev. 6		
Int.:MDC	QC:CM	APP.:
Date: 15-10-2025		
LUNDSBY RENEWABLE SOLUTIONS		
Lundsby Renewable Solutions A/S, Hjarbækvej 65, 8831 Løgstrup Tlf.: +45 96 49 43 00 Info@lundsby.dk This Drawing is subject to copyright and may not be reproduced without permission from Lundsby Renewable Solutions A/S		
Project nr.:1768 Drawing nr.: 9621		FORMAT: A1

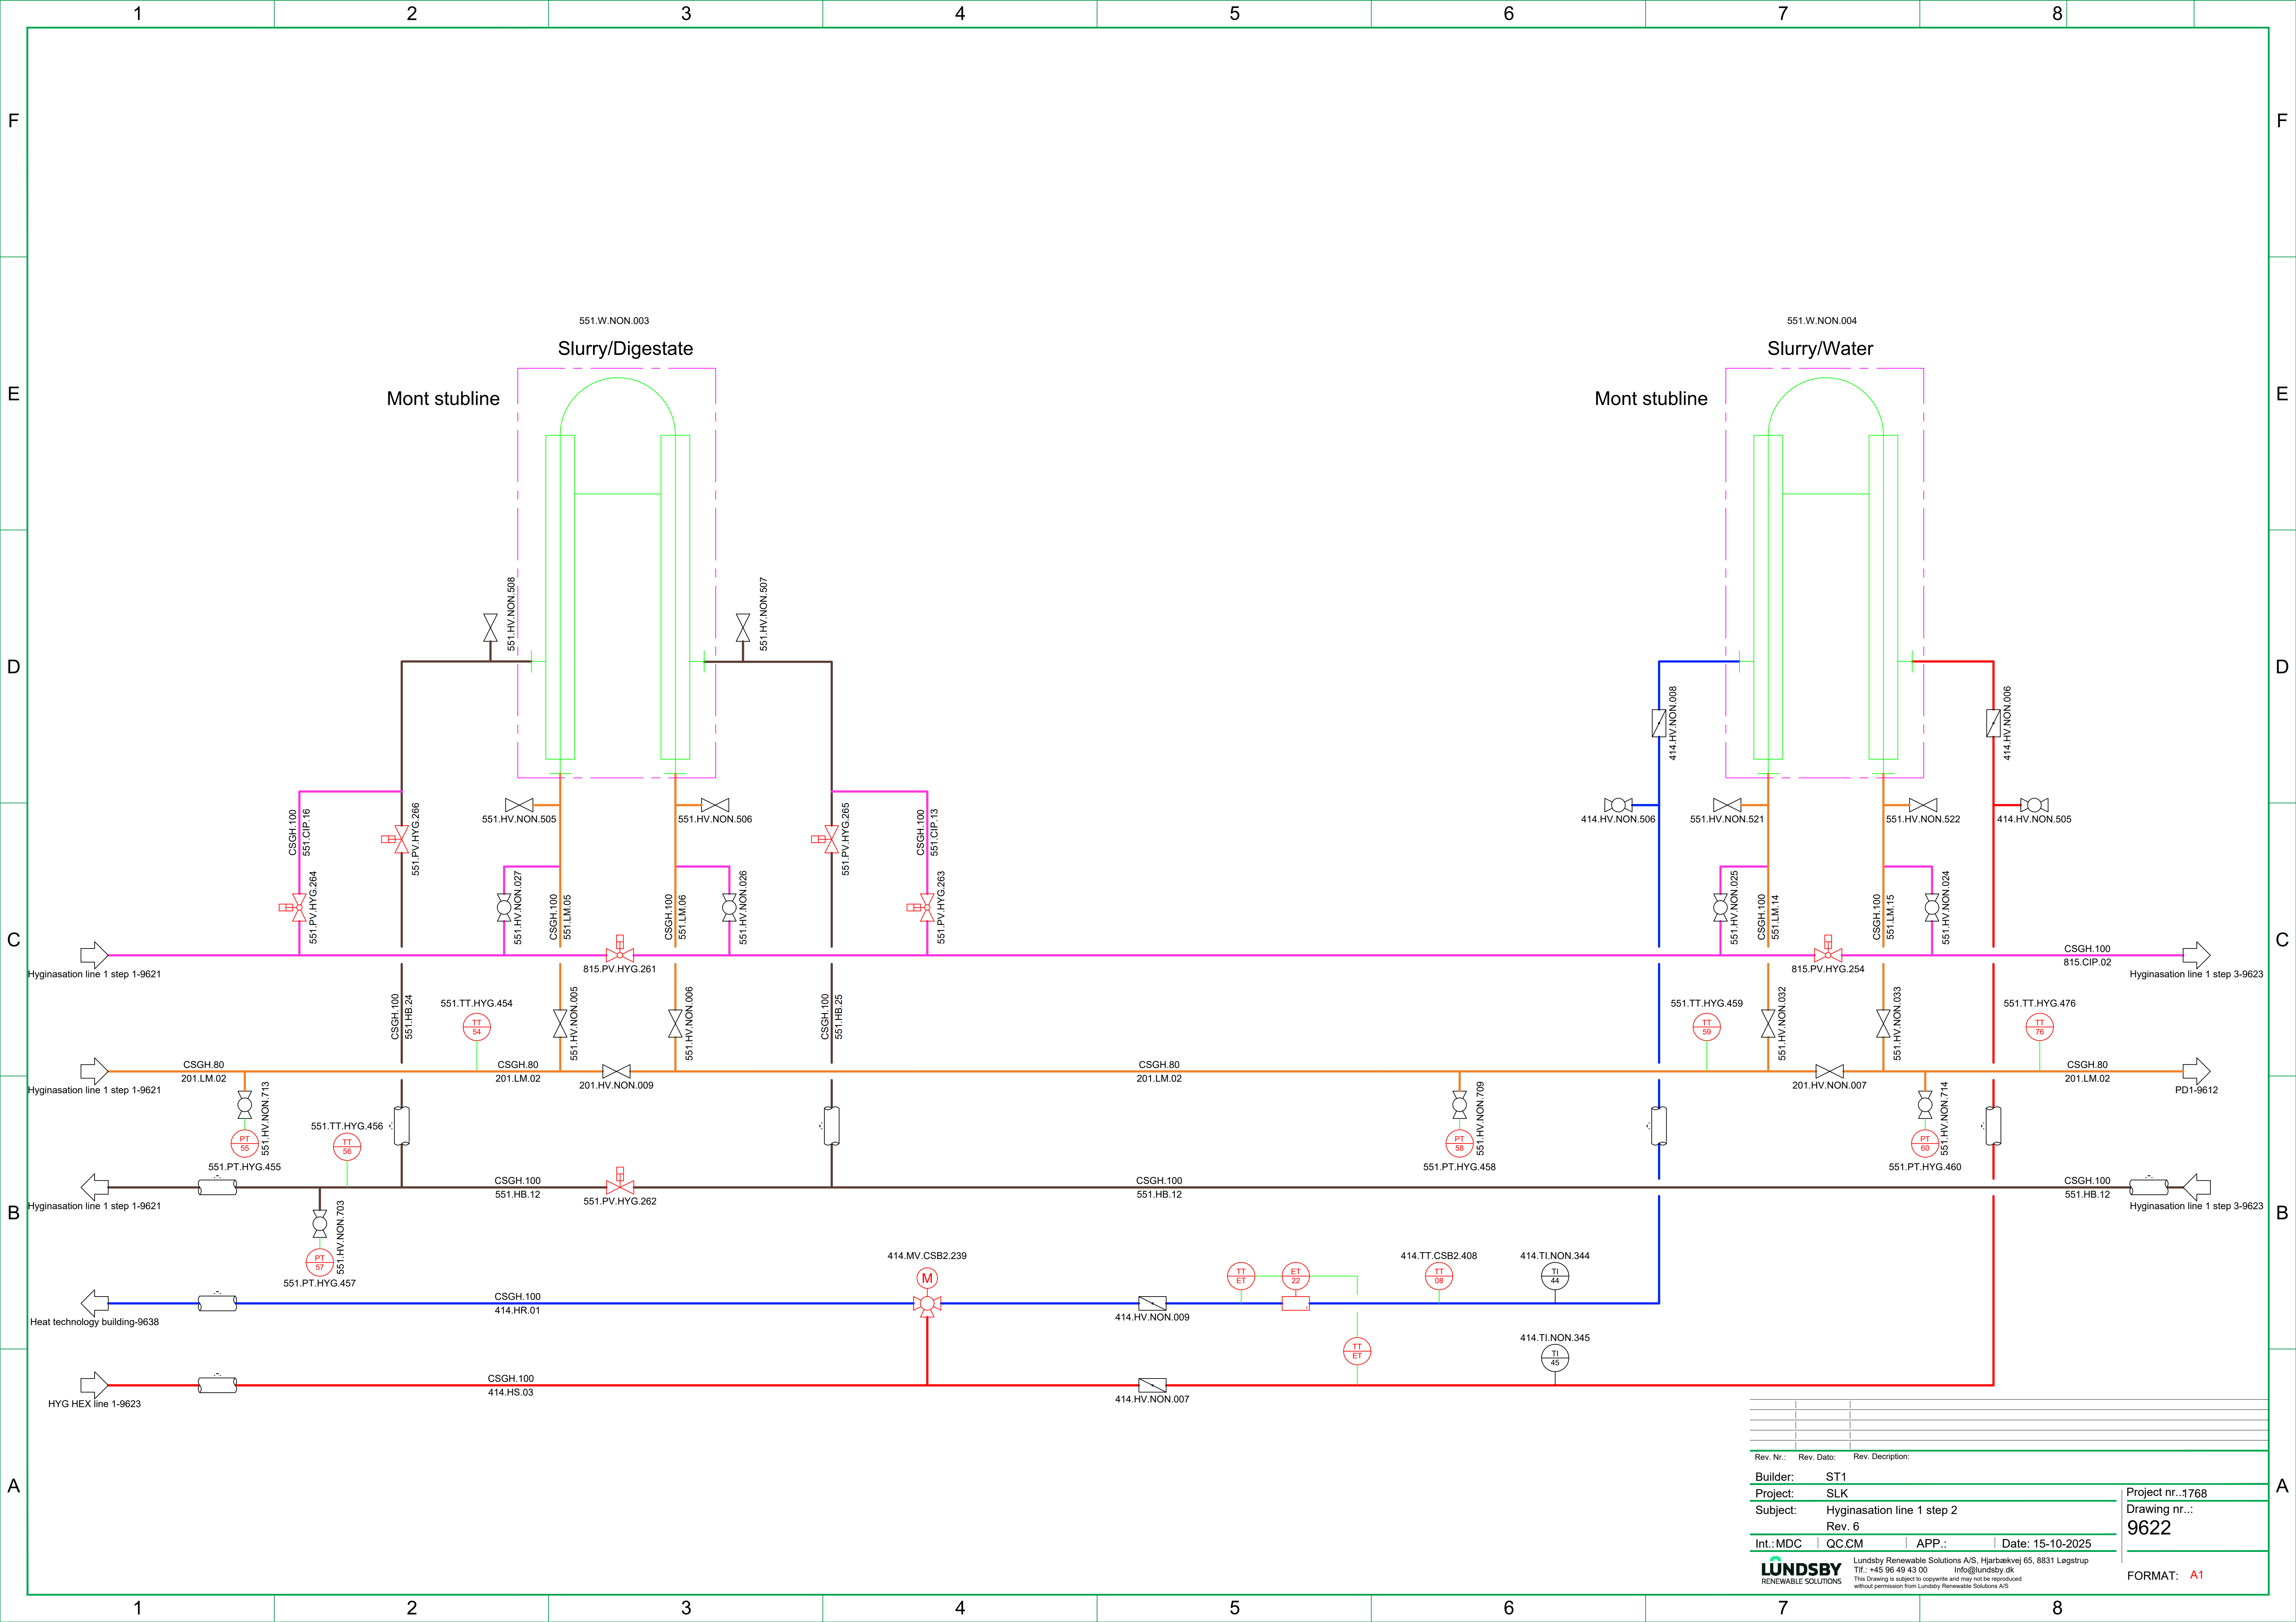



Rev. Nr.:	Rev. Dato:	Rev. Description:
Builder:	ST1	
Project:	SLK	
Subject:	Hyginasation line 1 step 2	
	Rev. 6	
Int.:MDC	QC:CM	APP.:Date: 15-10-2025
LUNDSBY RENEWABLE SOLUTIONS Lundsby Renewable Solutions A/S, Hjarbrækvej 65, 8831 Lægstrup Tlf.: +45 96 49 43 00 Info@lundsby.dk This Drawing is subject to copyright and may not be reproduced without permission from Lundsby Renewable Solutions A/S		
Project nr.:1768		Drawing nr.:9622
FORMAT: A1		

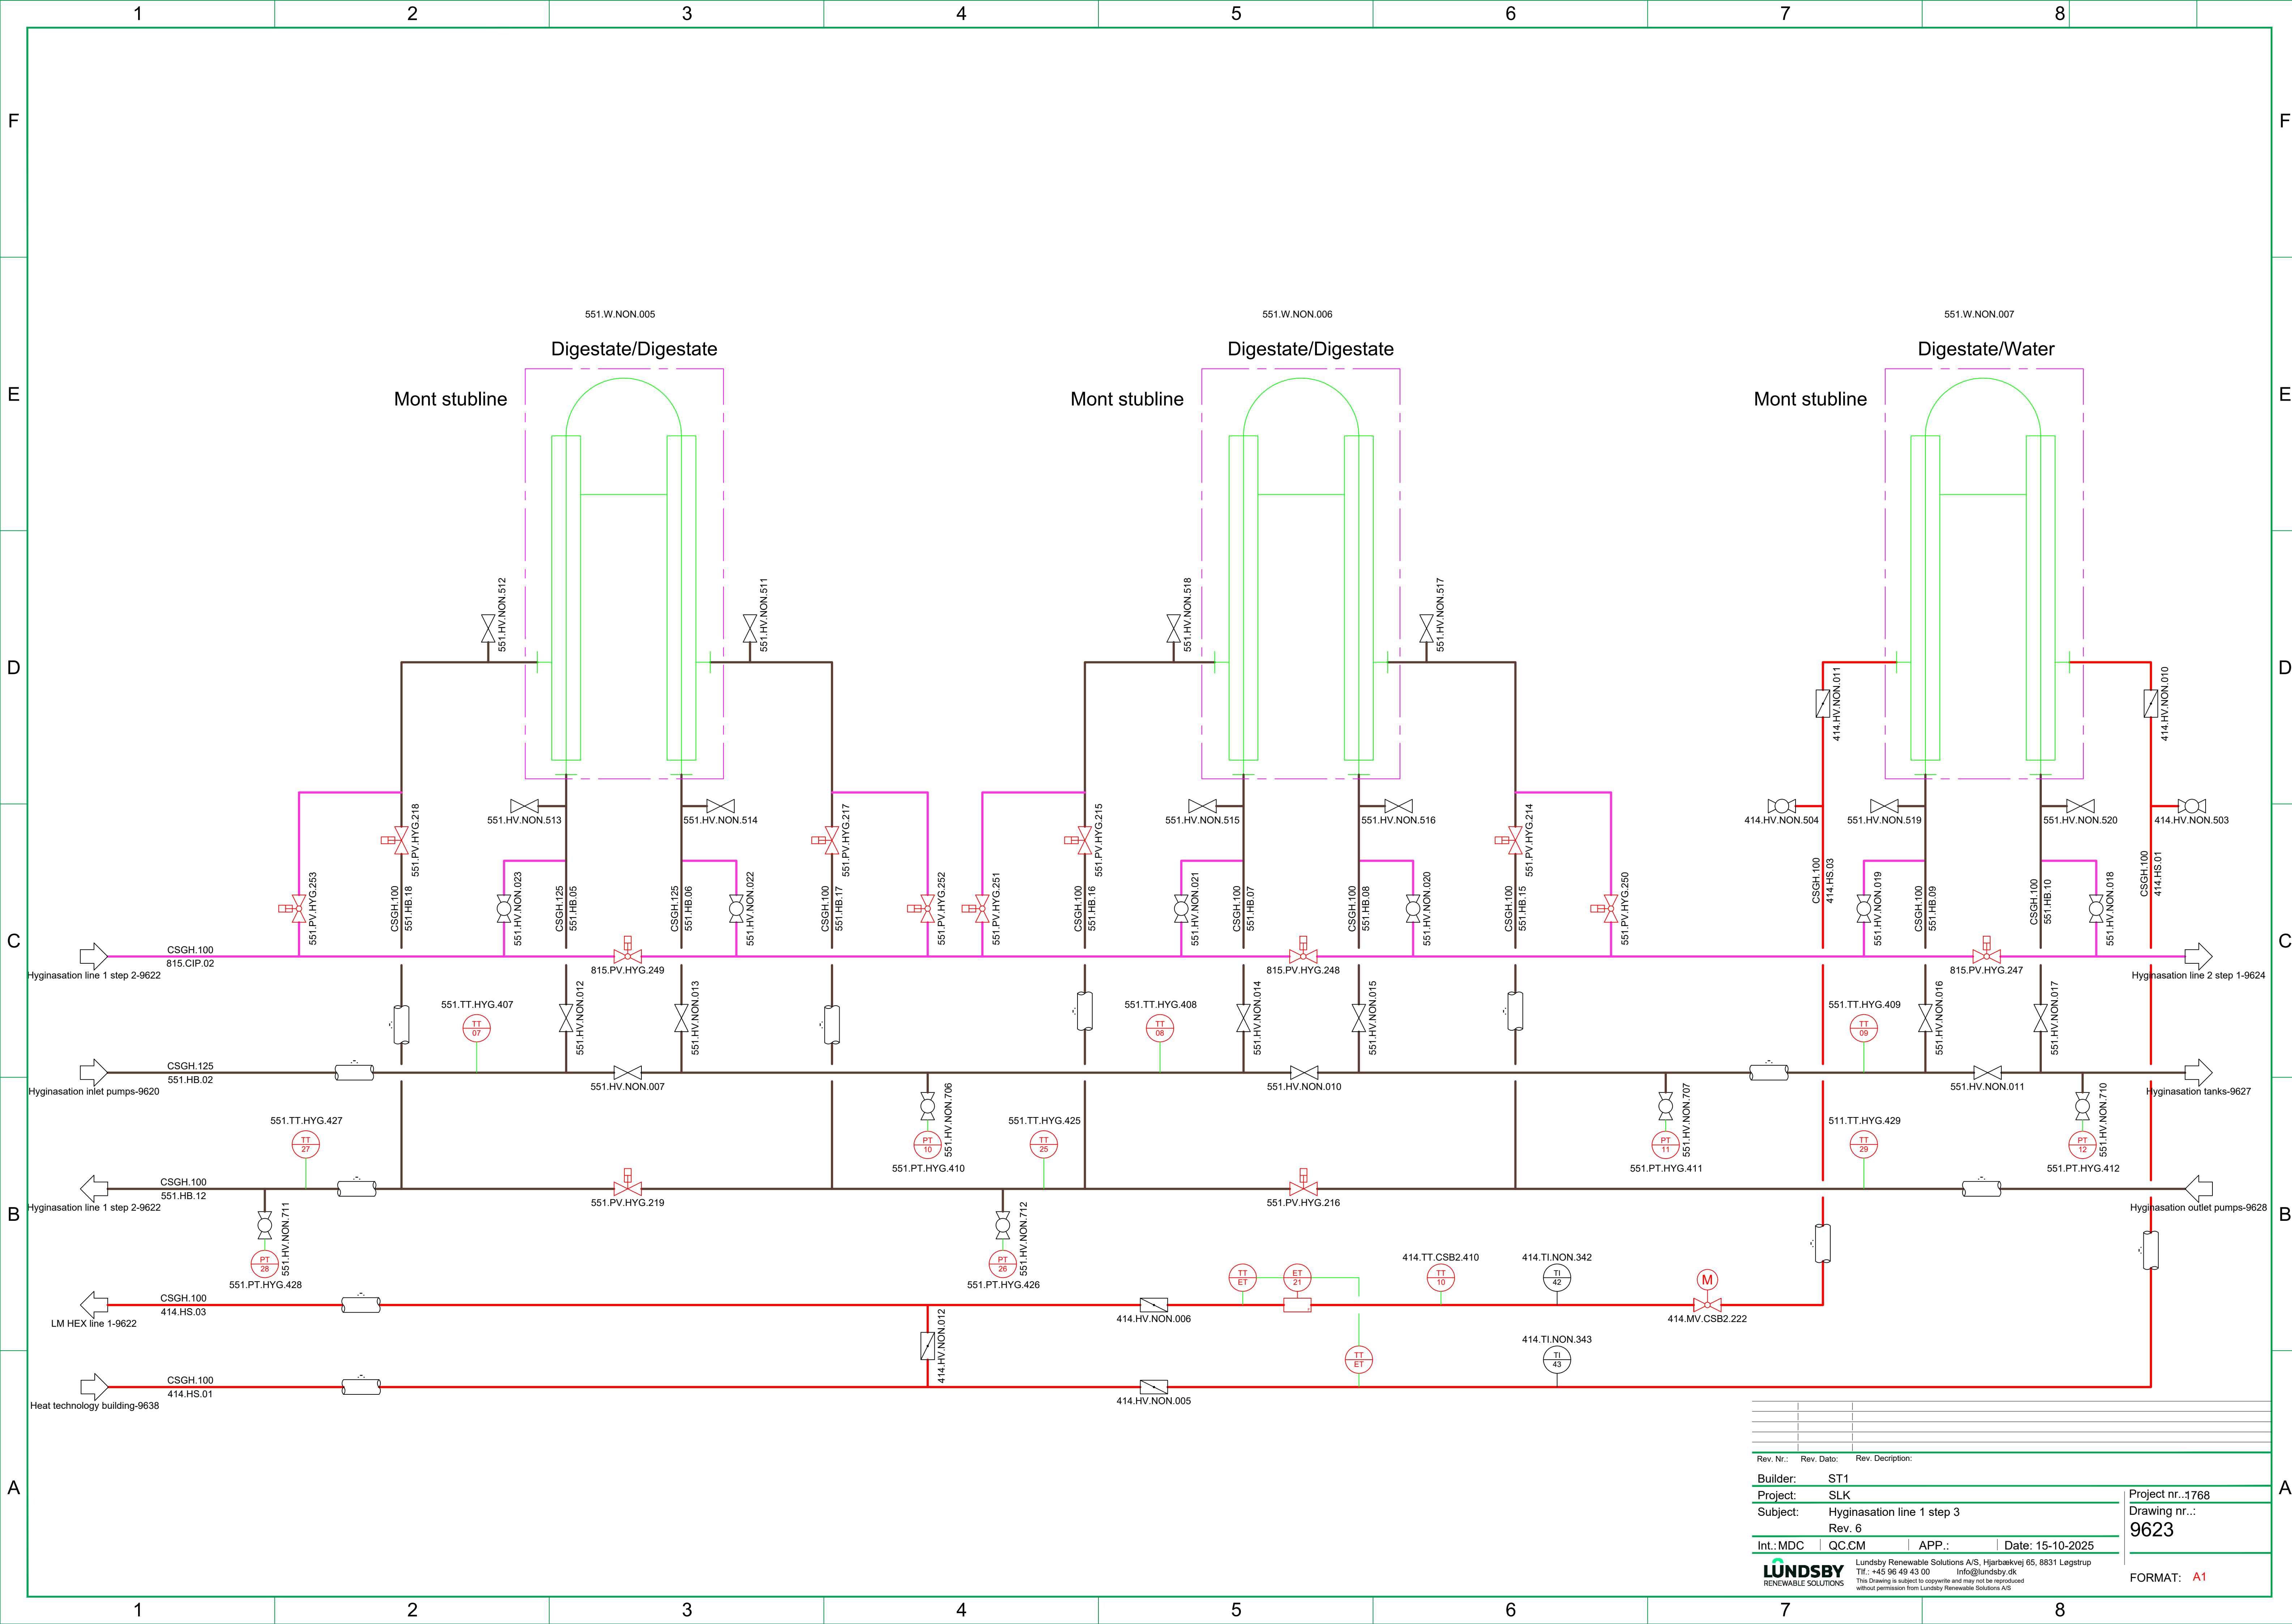

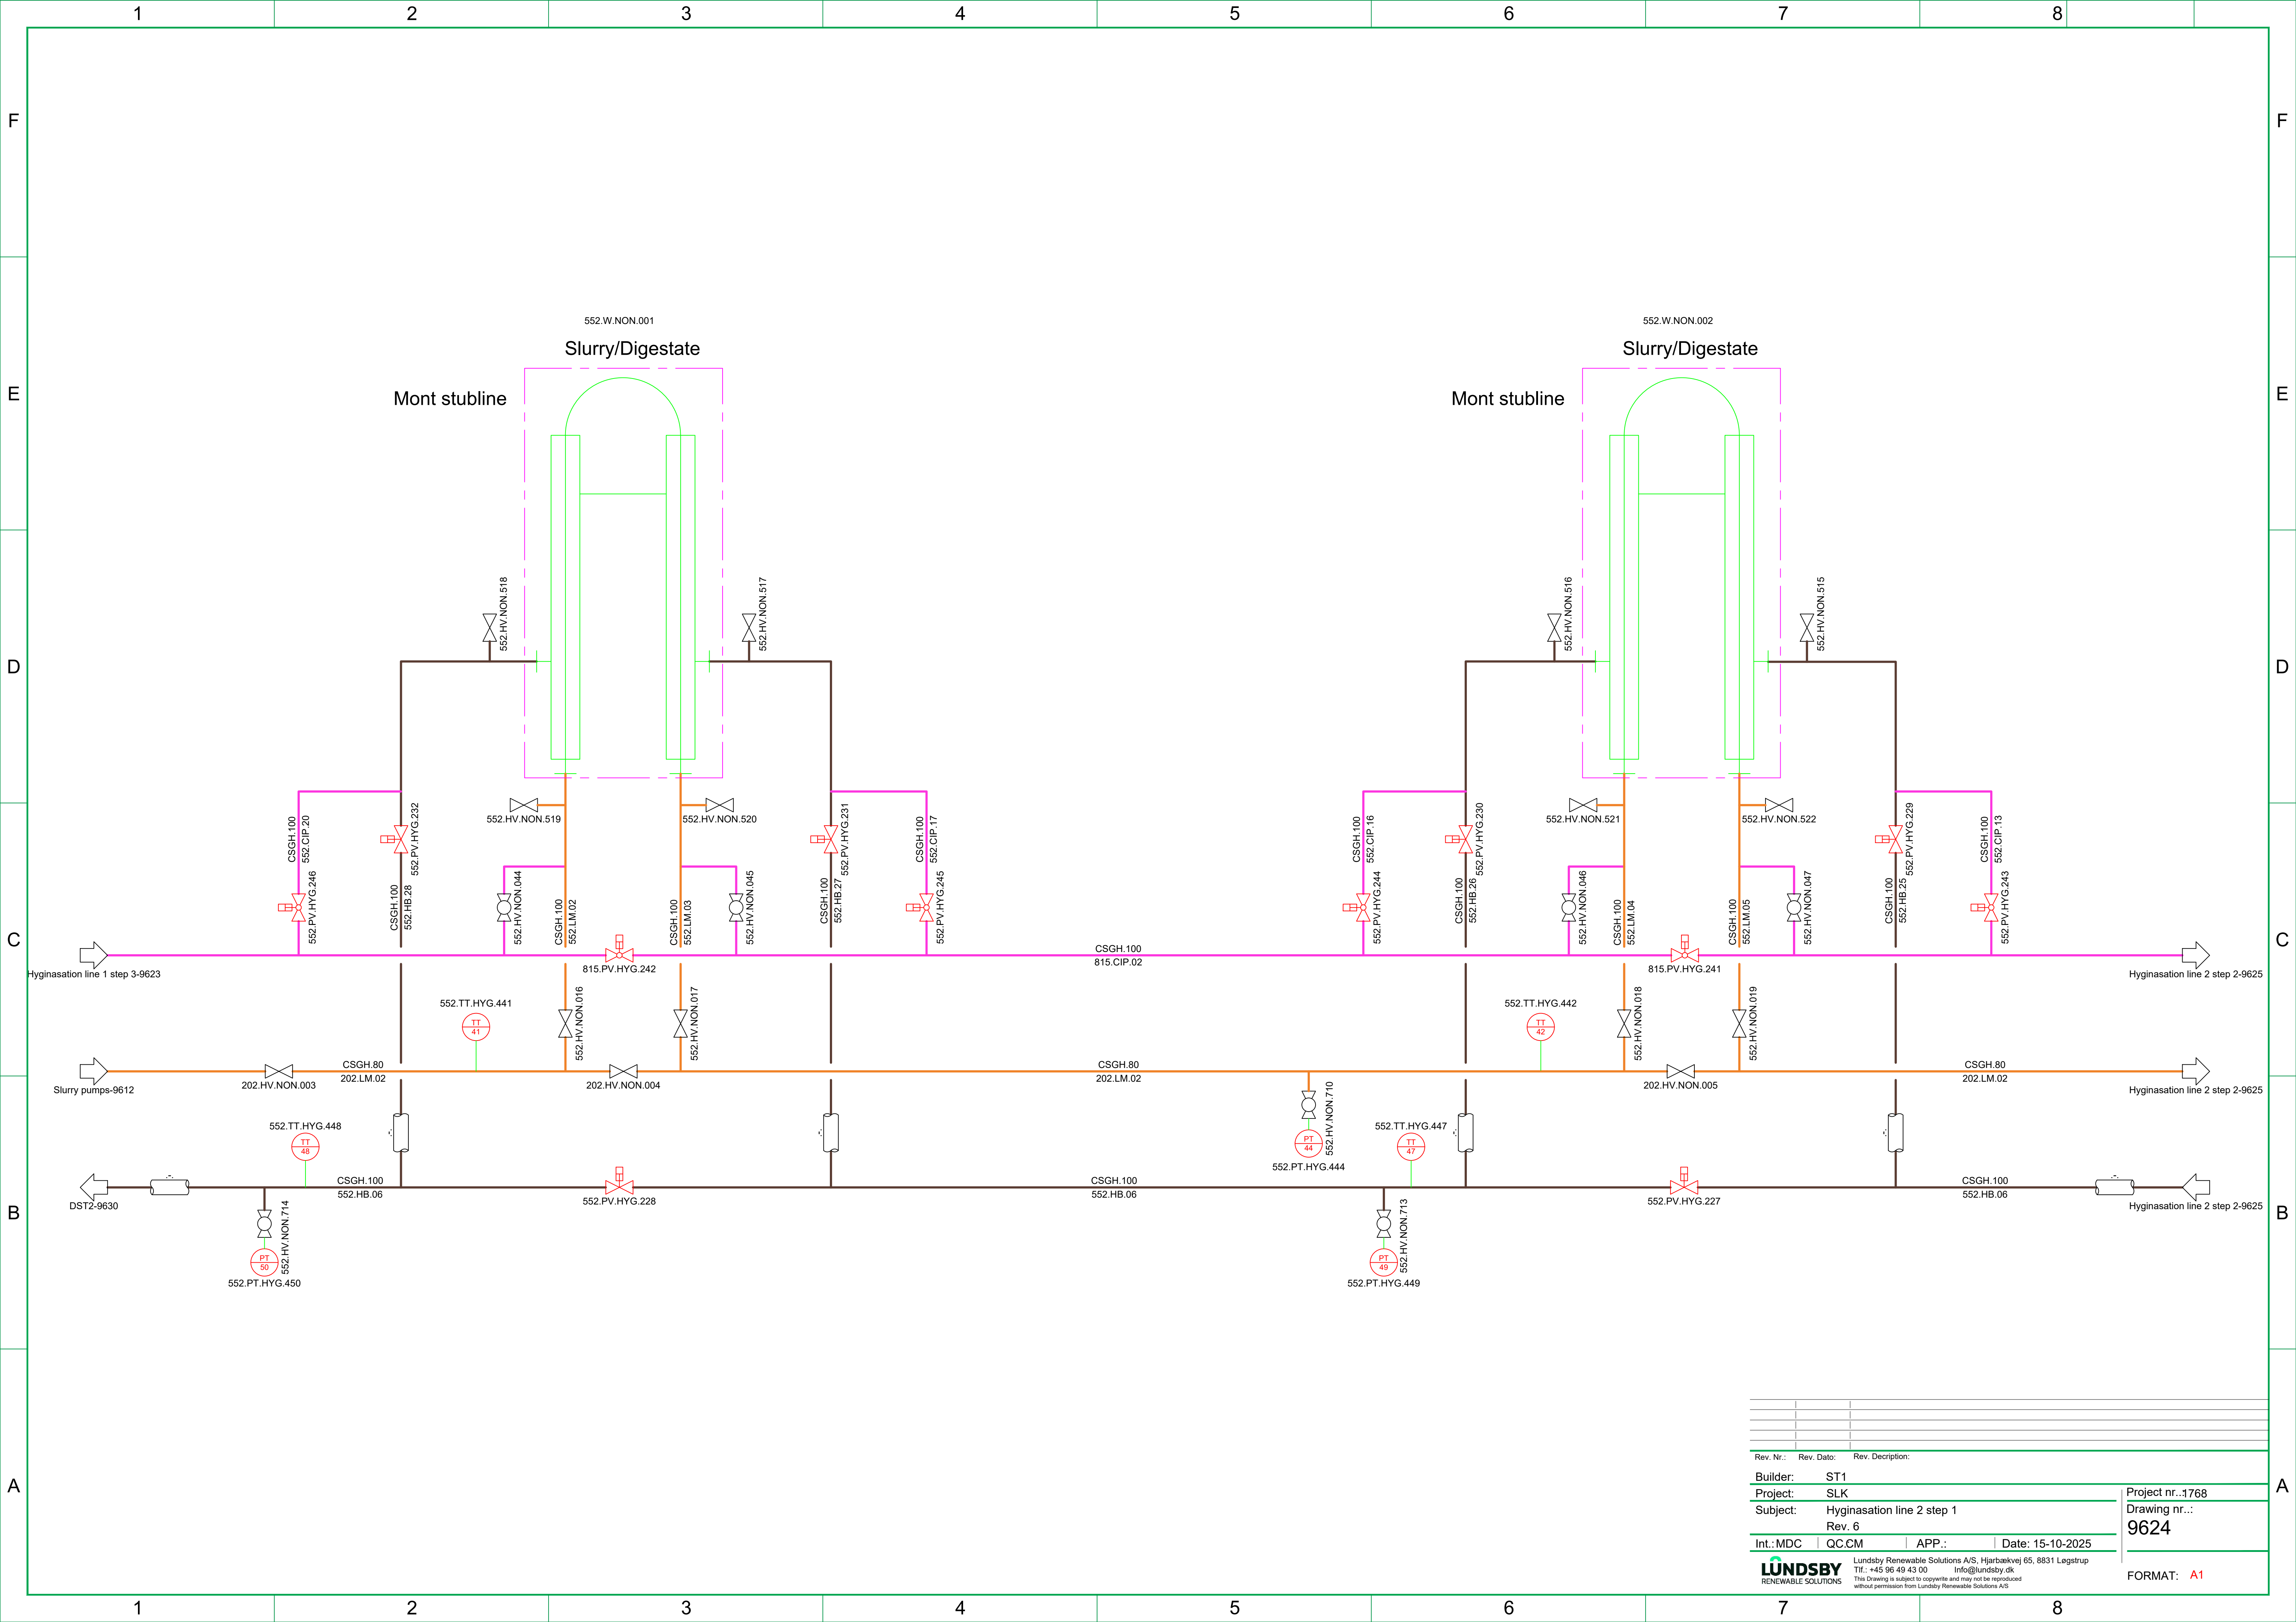


Rev. Nr.:	Rev. Dato:	Rev. Description:
Builder:	ST1	
Project:	SLK	
Subject:	Hyginasation line 2 step 1	
Rev. 6		
Int.:MDC	QC:CM	APP.:
Date: 15-10-2025		
LUNDSBY RENEWABLE SOLUTIONS		
Lundsby Renewable Solutions A/S, Hjarbækvej 65, 8831 Løgstrup Tlf.: +45 96 49 43 00 Info@lundsby.dk This Drawing is subject to copyright and may not be reproduced without permission from Lundsby Renewable Solutions A/S		
Project nr.:1768 Drawing nr.: 9624		FORMAT: A1

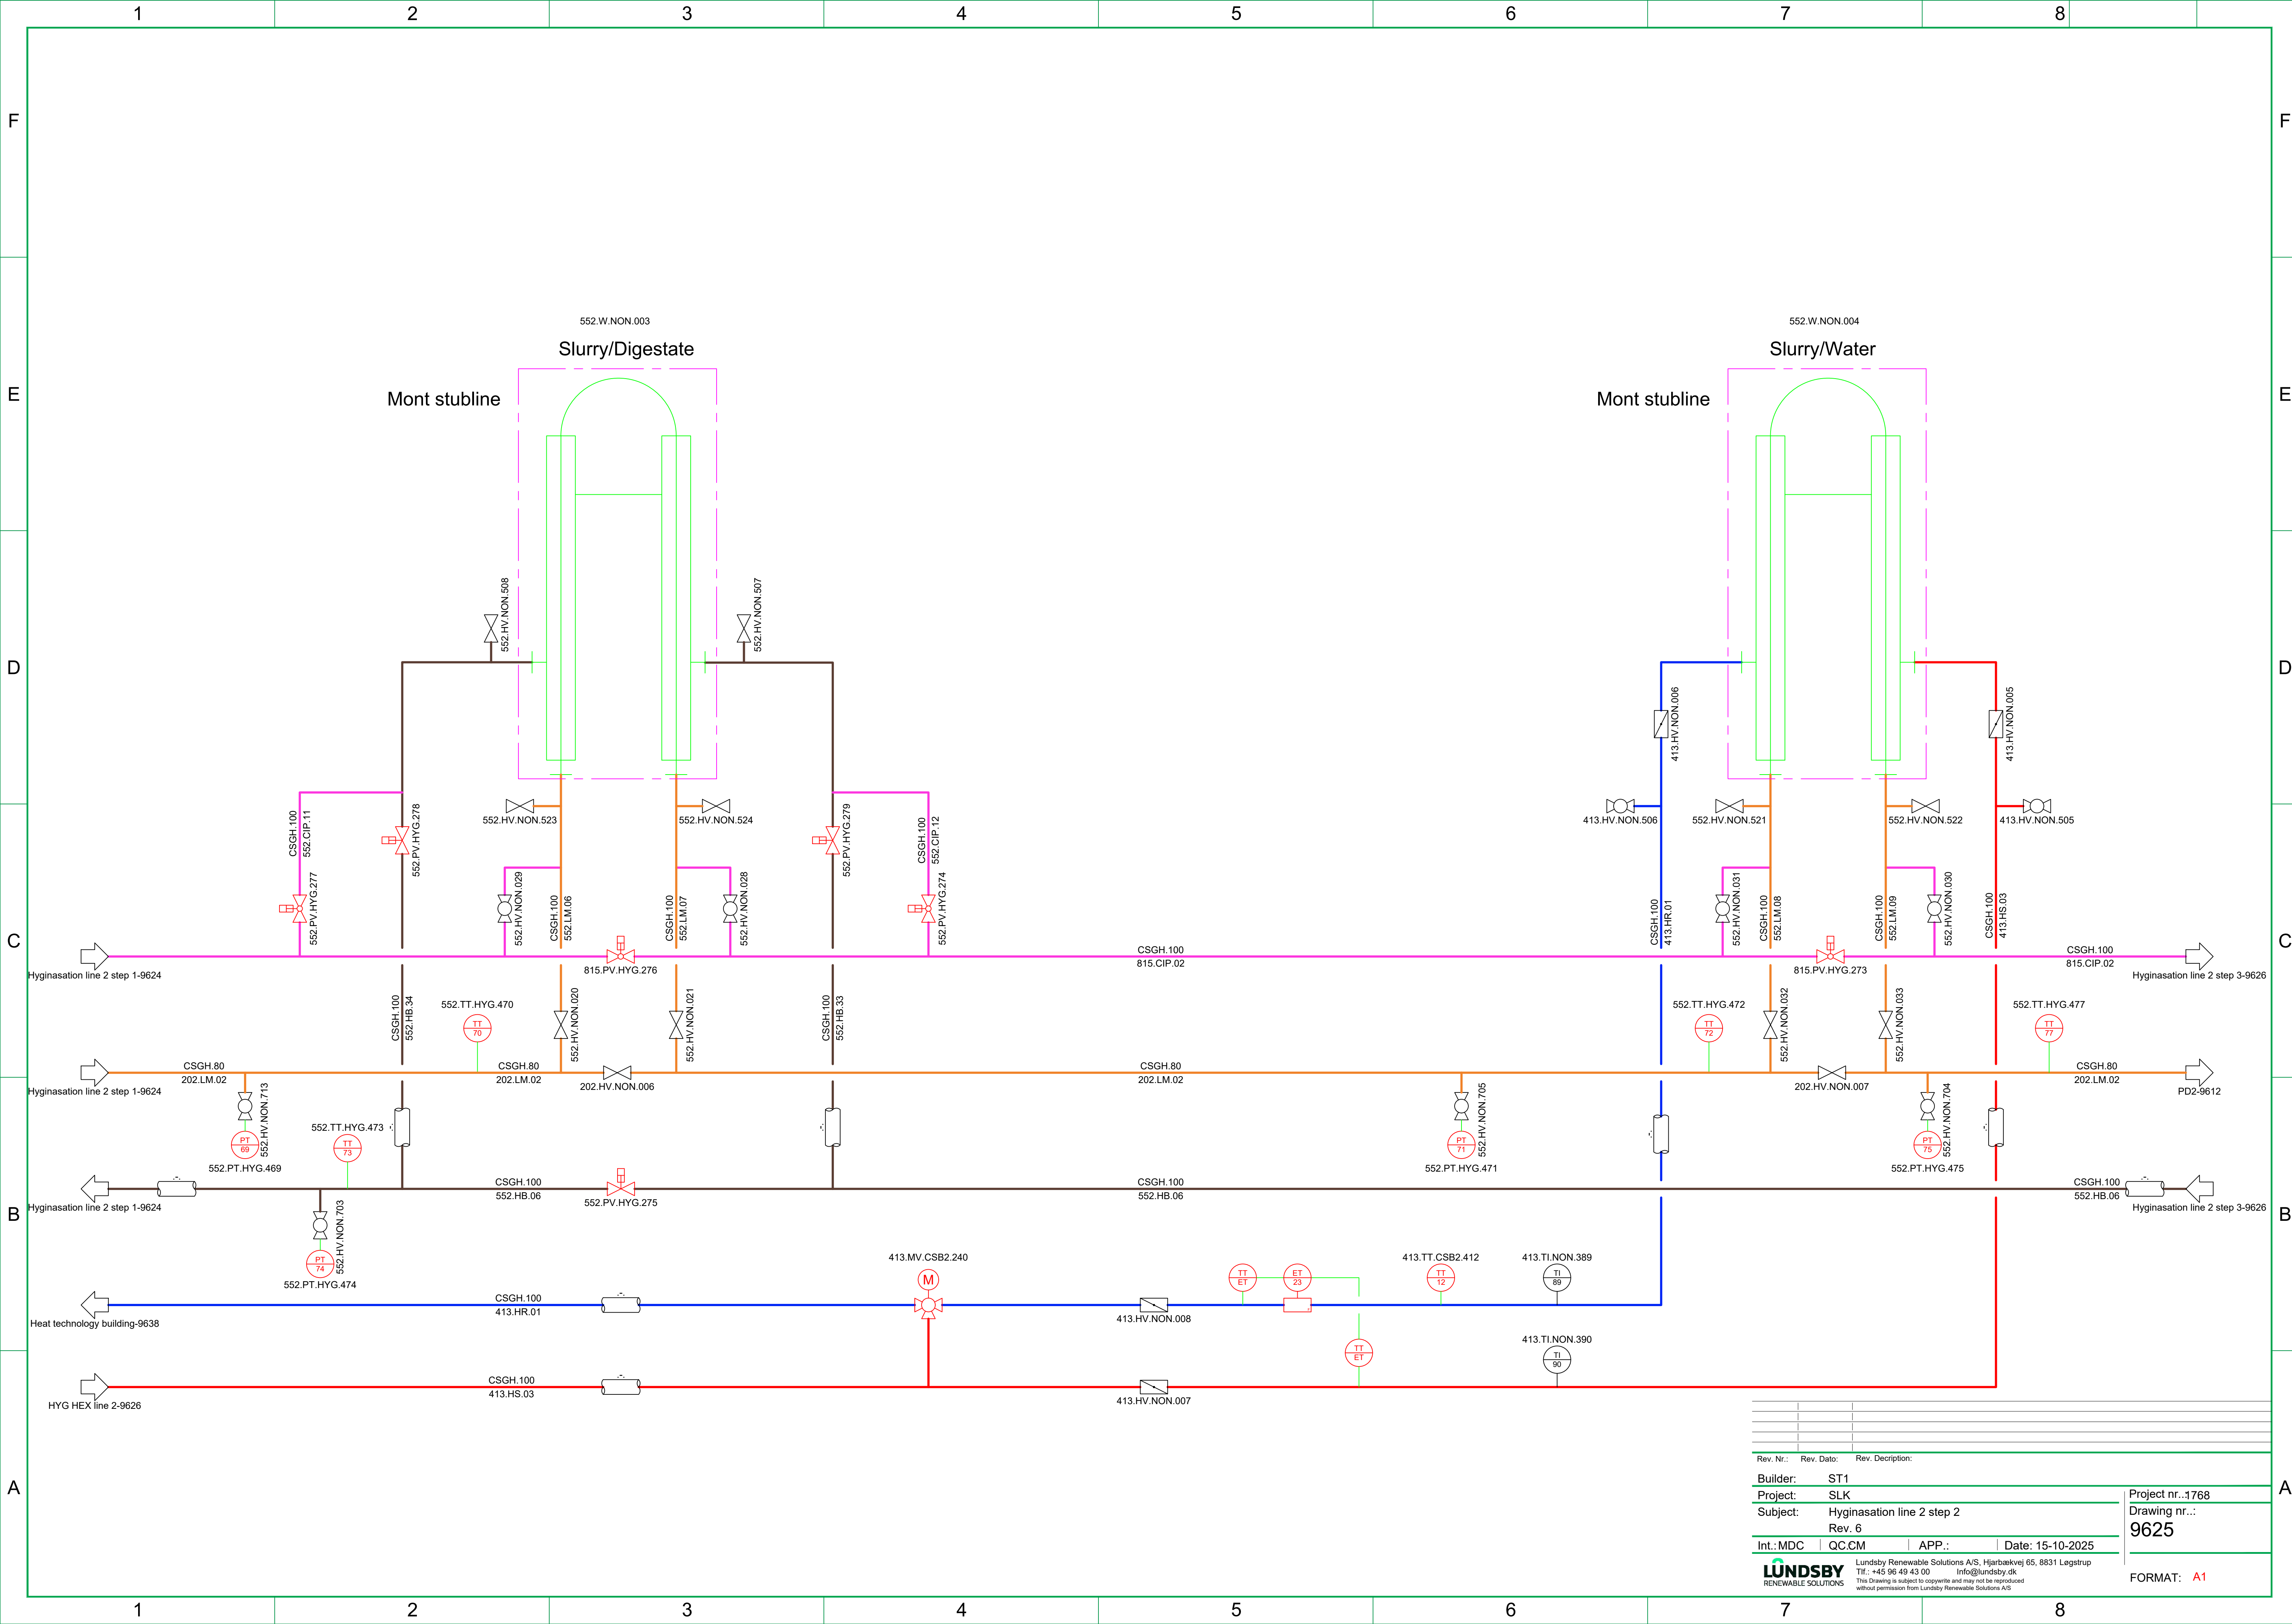

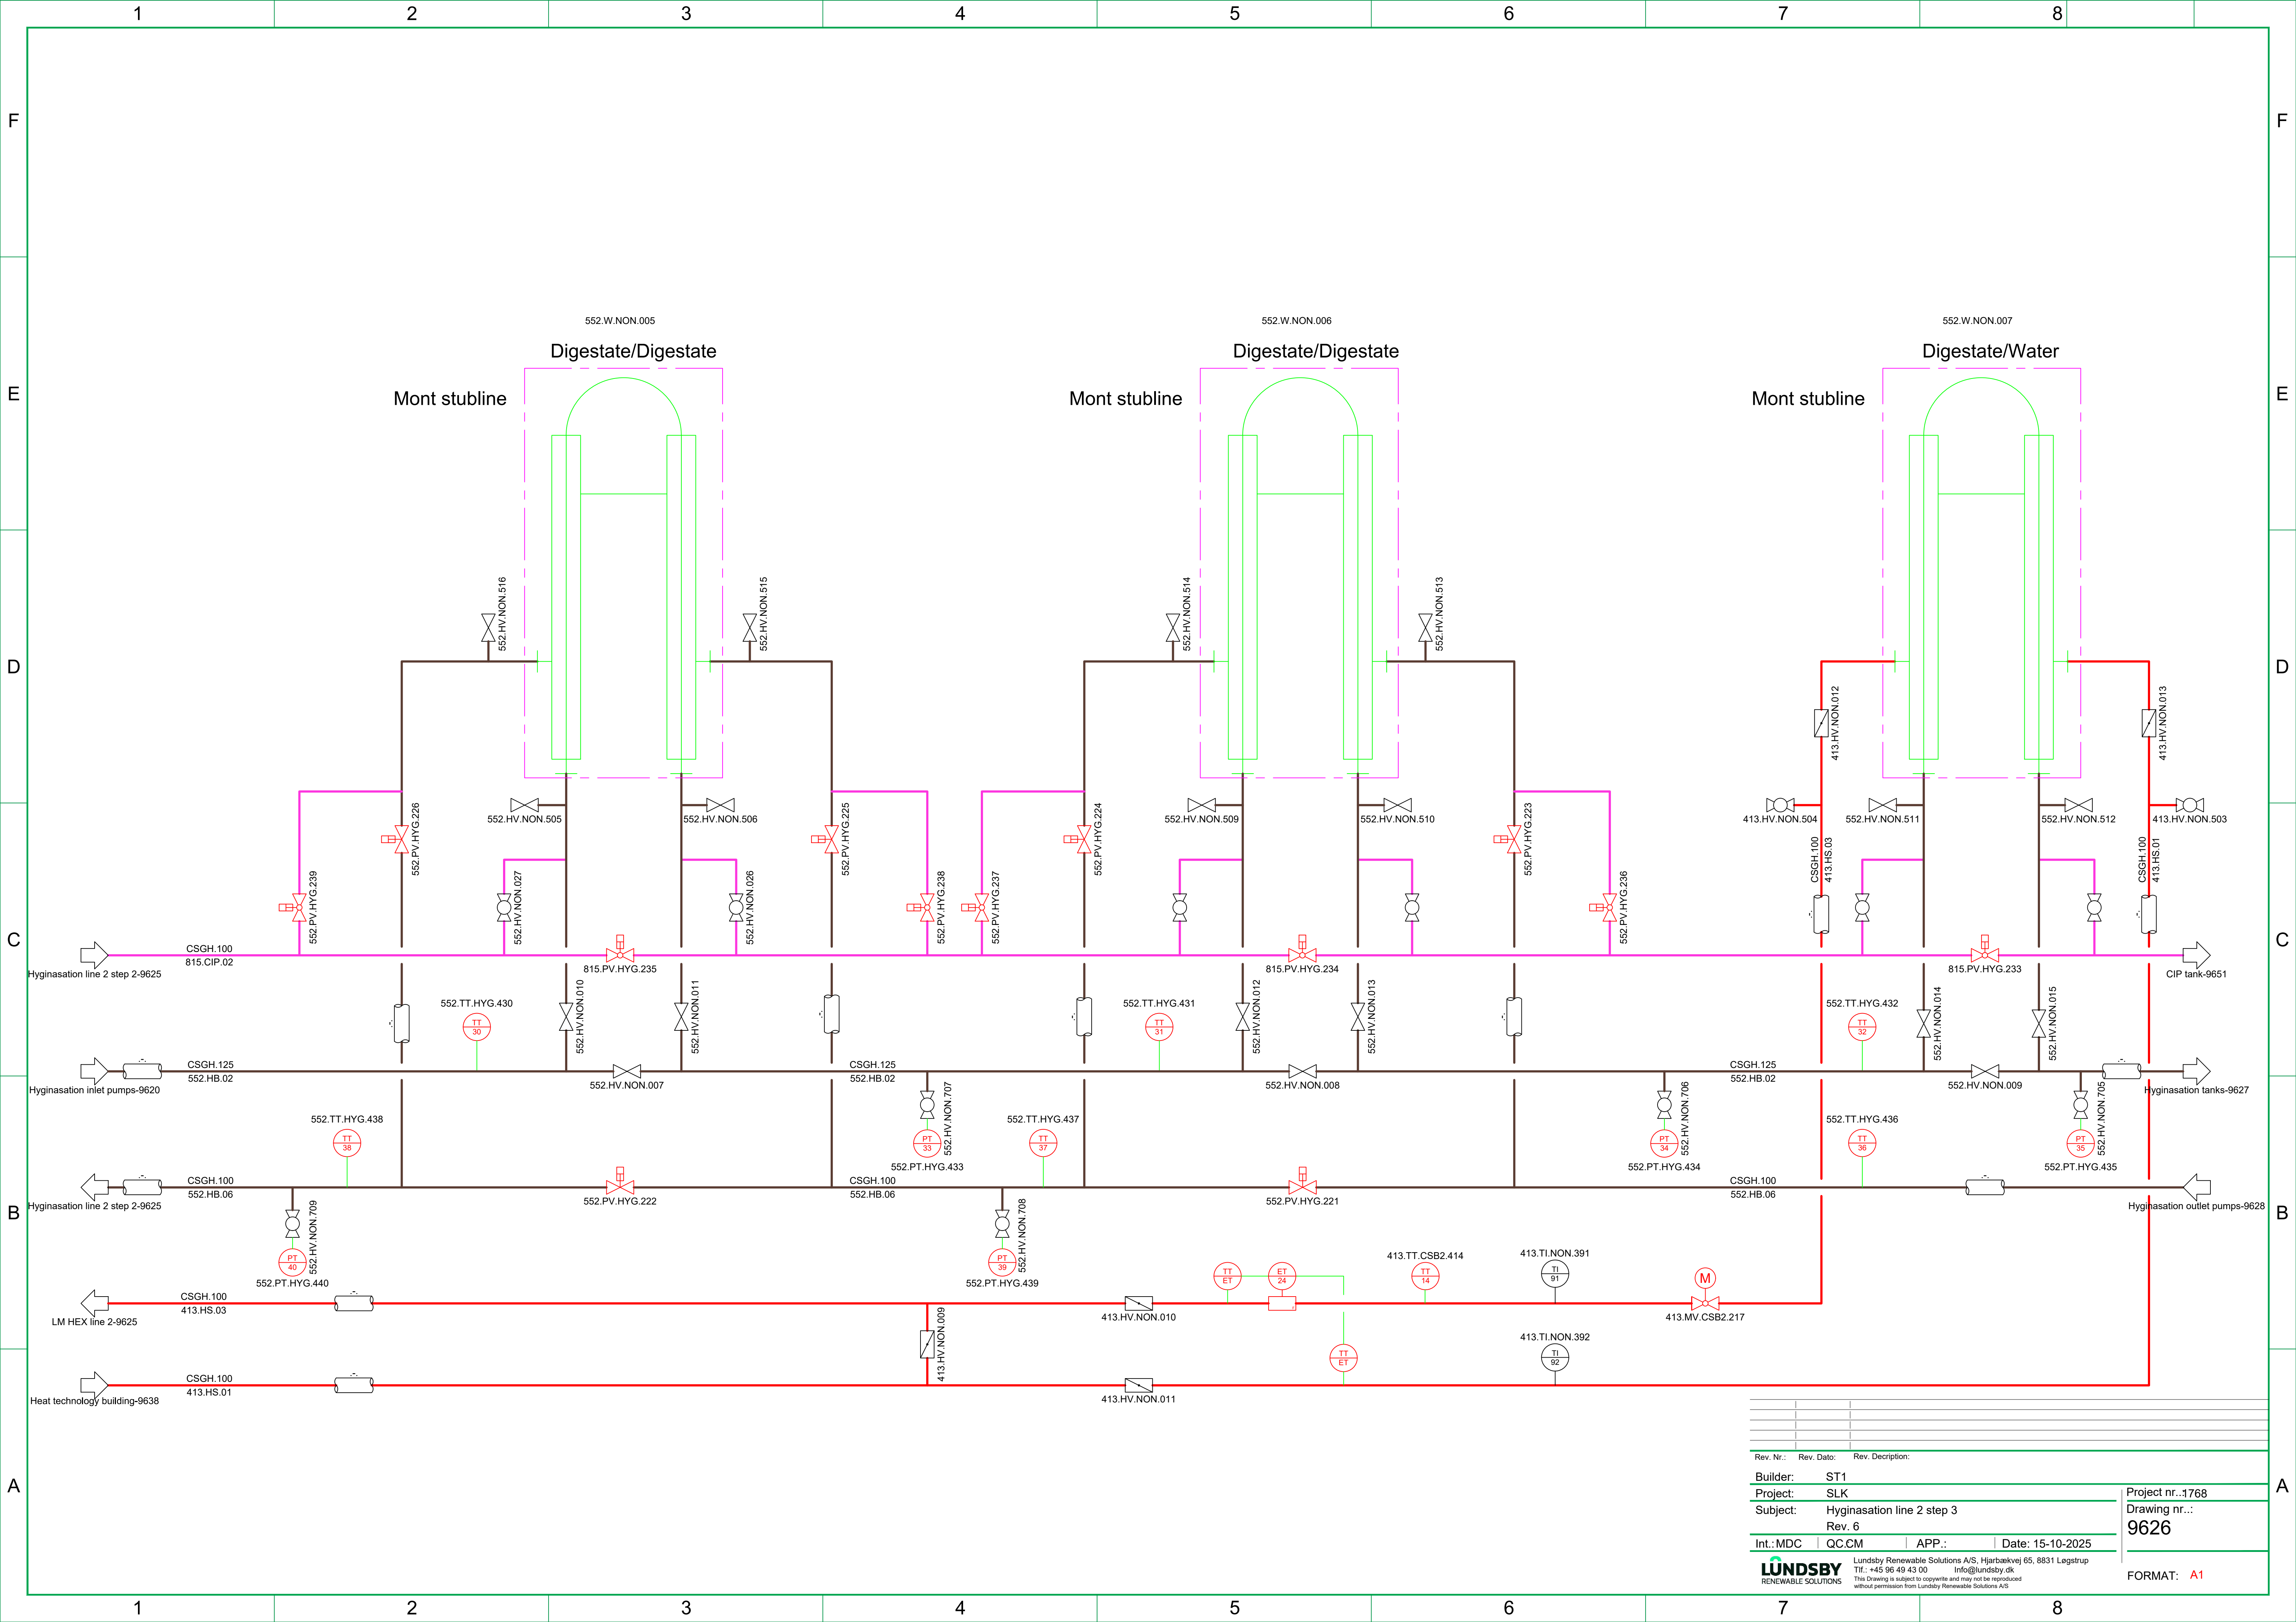


Rev. Nr.:	Rev. Dato:	Rev. Description:
Builder:	ST1	
Project:	SLK	
Subject:	Hyginasation line 2 step 3	
Rev. 6		
Int.:MDC	QC:CM	APP.: Date: 15-10-2025
LUNDSBY RENEWABLE SOLUTIONS		
Lundsby Renewable Solutions A/S, Hjarbrækvej 65, 8831 Lægstrup Tlf.: +45 96 49 43 00 info@lundsby.dk This Drawing is subject to copyright and may not be reproduced without permission from Lundsby Renewable Solutions A/S		
Project nr.:1768 Drawing nr.: 9626		FORMAT: A1

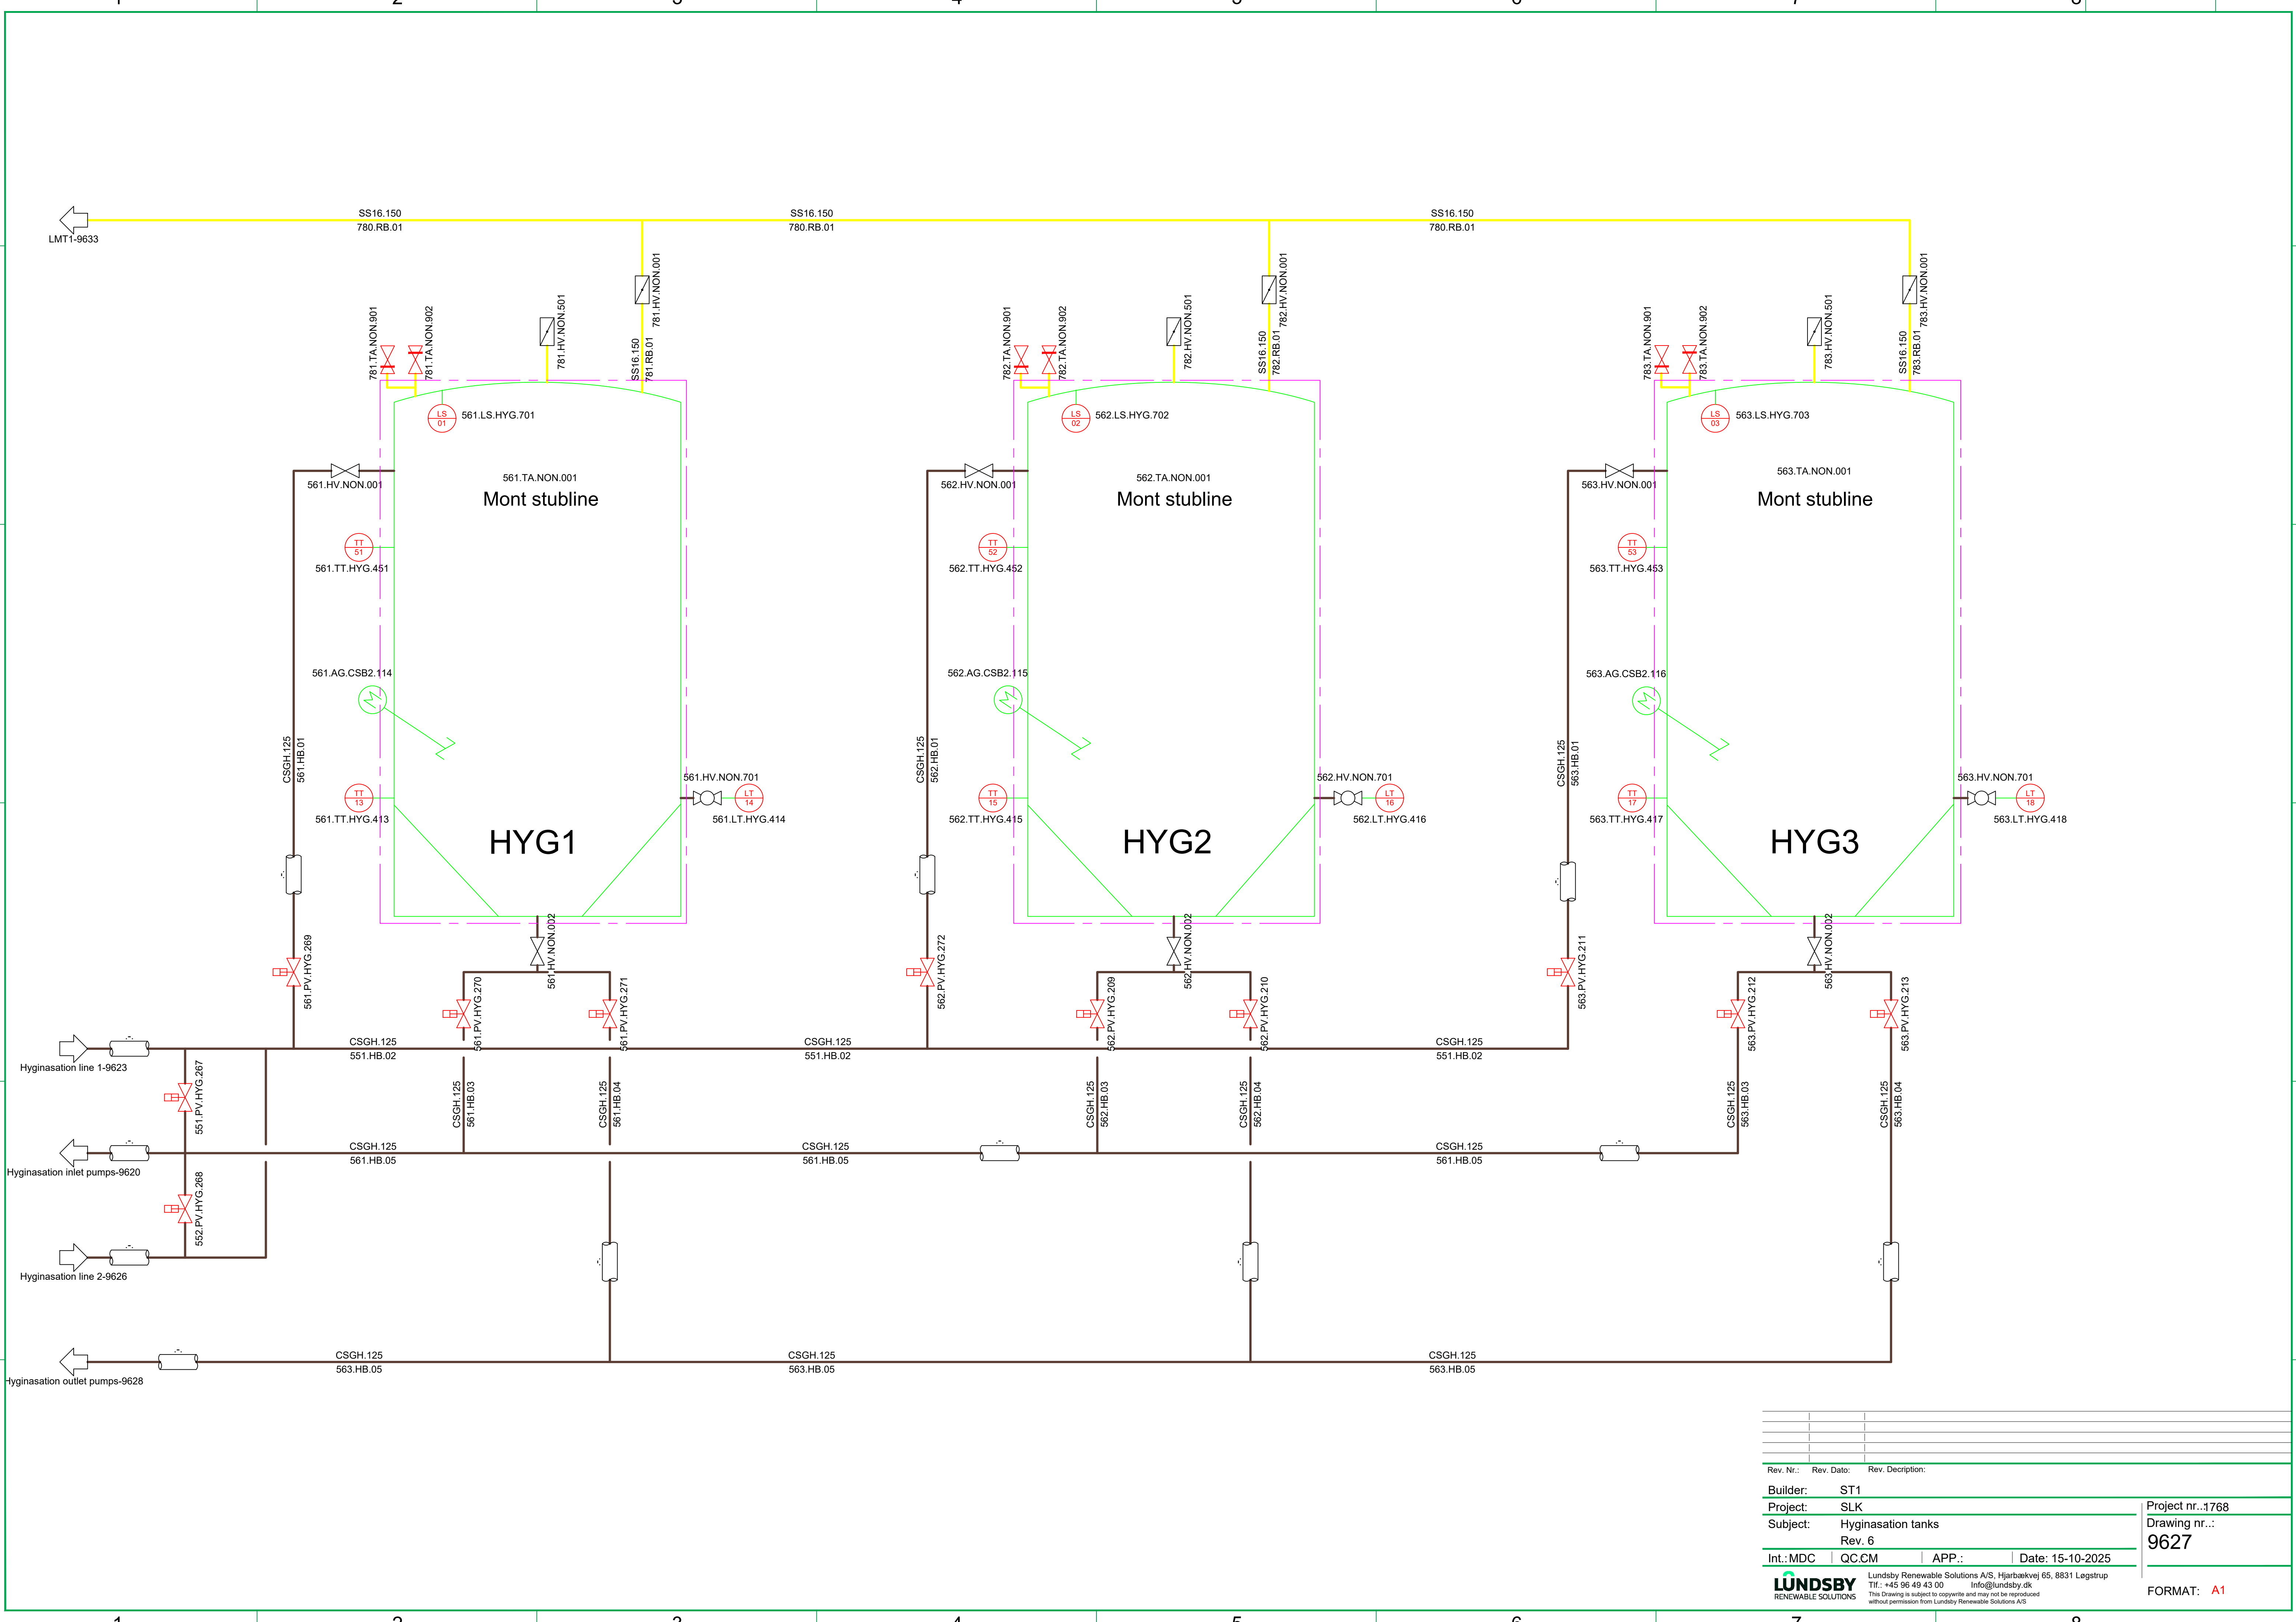


Rev. Nr.:	Rev. Dato:	Rev. Description:
Builder:	ST1	
Project:	SLK	
Subject:	Hyginasation tanks	
Rev. 6		
Int.:MDC	QC.CM	APP.:
Date: 15-10-2025		
LUNDSBY RENEWABLE SOLUTIONS		
Lundsby Renewable Solutions A/S, Hjarbækvej 65, 8831 Løgstrup Tlf.: +45 96 49 43 00 Info@lundsby.dk This Drawing is subject to copyright and may not be reproduced without permission from Lundsby Renewable Solutions A/S		
Project nr.:1768 Drawing nr.: 9627		FORMAT: A1

Tech Building


Outlet pumps

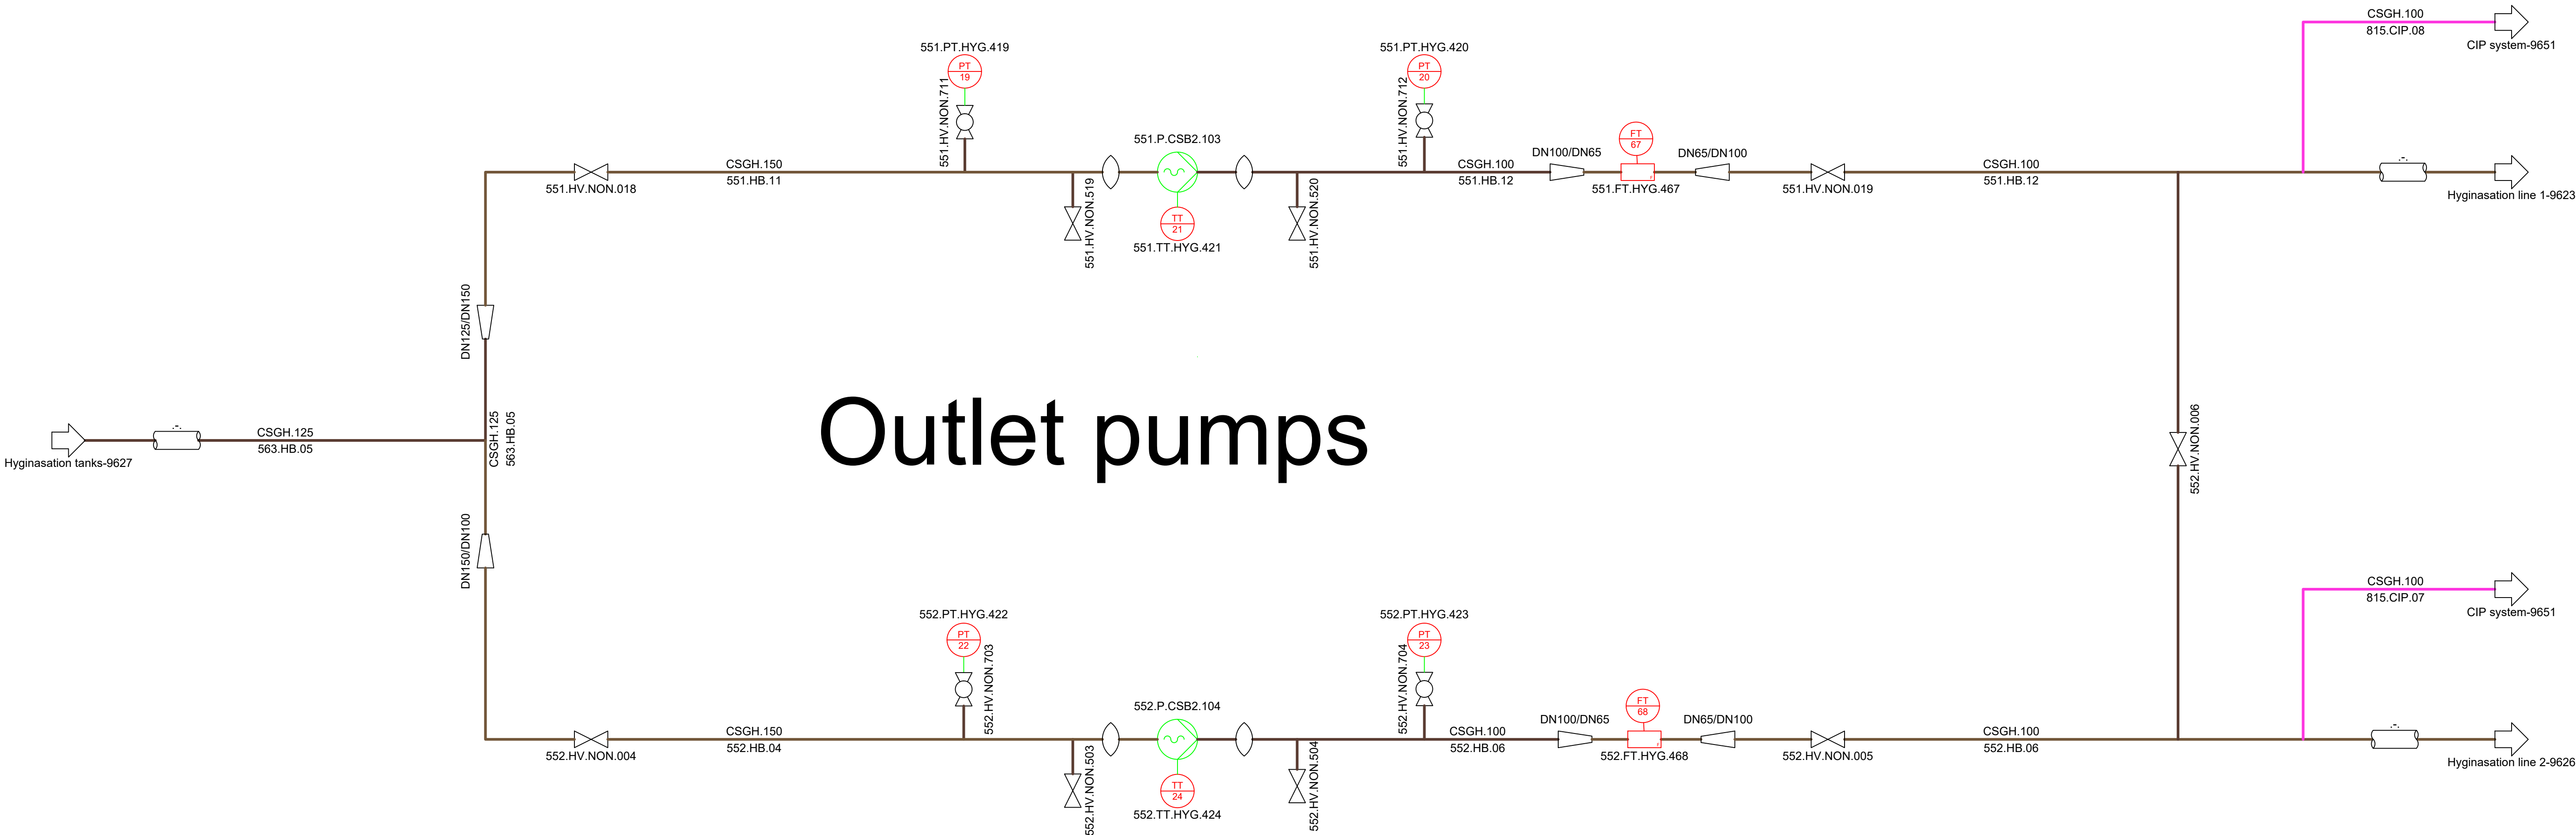


Rev. Nr.:	Rev. Dato:	Rev. Description:	
Builder:	ST1		
Project:	SLK		
Subject:	Hyginasation outlet pumps		
Rev. 6			
Int.:MDC	QC:CM	APP.:	Date: 15-10-2025
LUNDSBY RENEWABLE SOLUTIONS			Lundsby Renewable Solutions A/S, Hjarbækvej 65, 8831 Løgstrup Tlf.: +45 96 49 43 00 Info@lundsby.dk This Drawing is subject to copyright and may not be reproduced without permission from Lundsby Renewable Solutions A/S
Project nr.:1768 Drawing nr.: 9628			FORMAT: A1

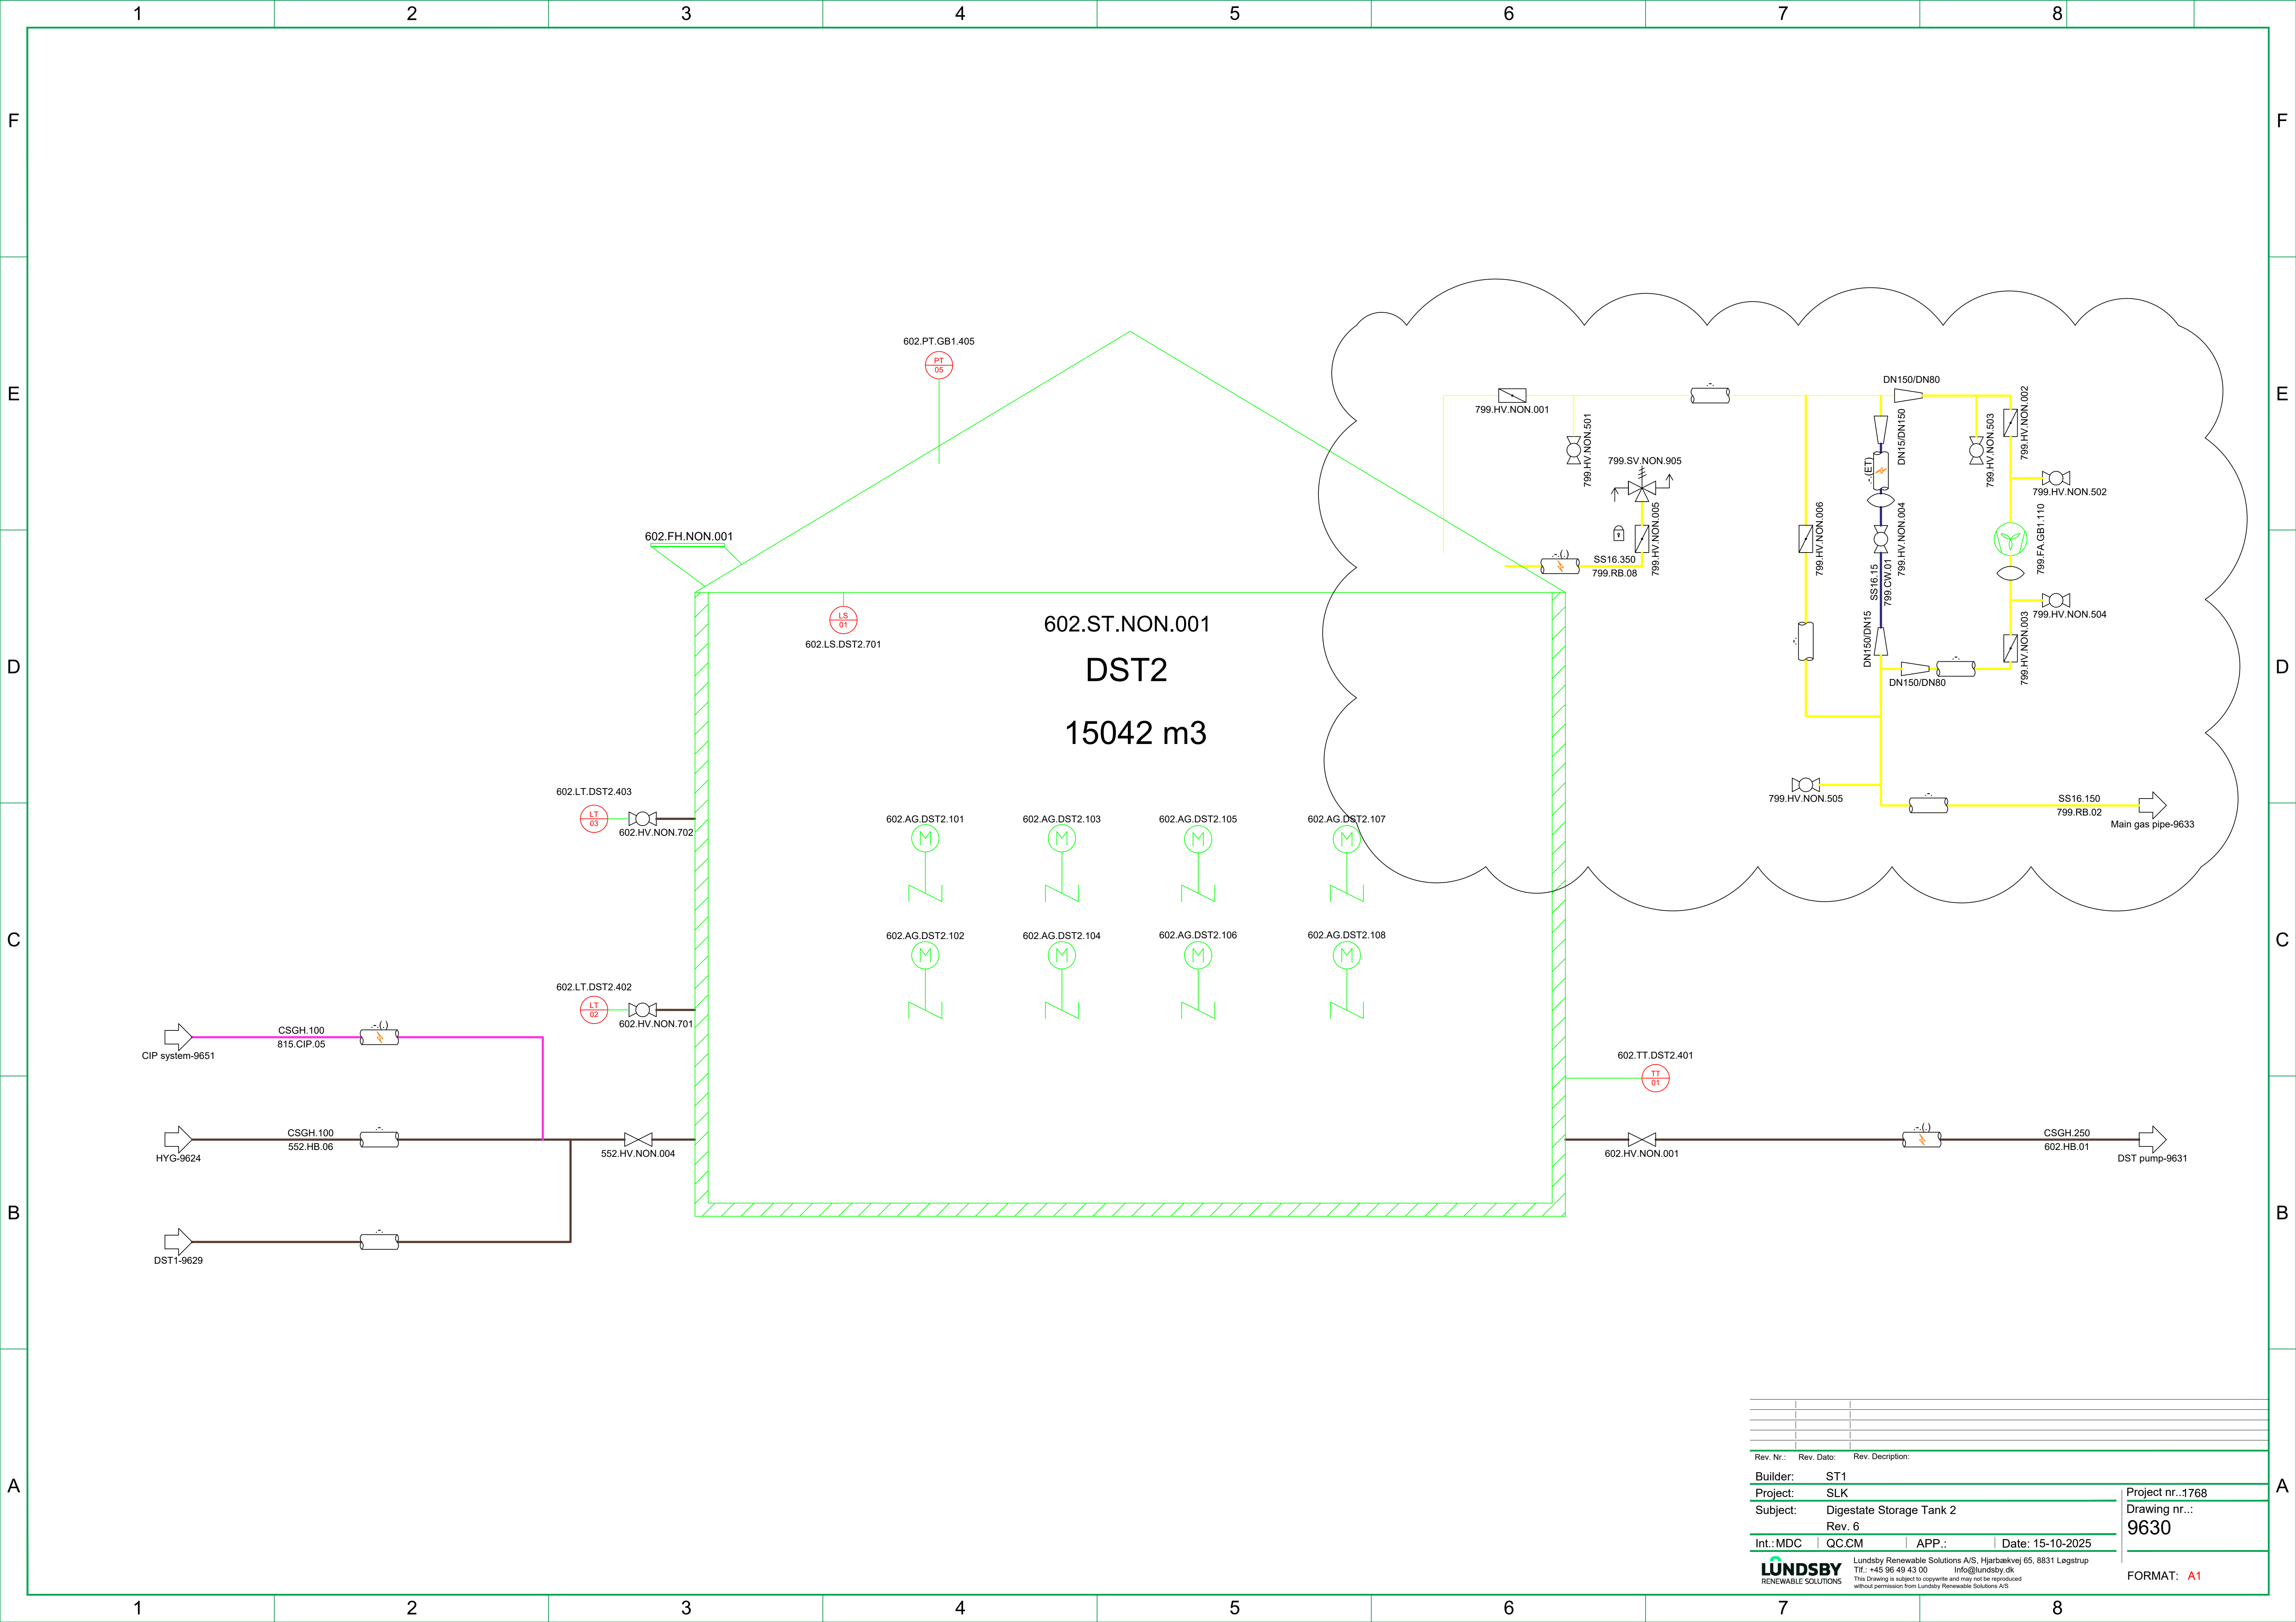


Rev. Nr.: Rev. Dato: Rev. Description:			Project nr.:1768	
Builder: ST1			Drawing nr.: 9630	
Project: SLK			Date: 15-10-2025	
Subject: Digestate Storage Tank 2			Format: A1	
Rev. 6			Lundsgby Renewable Solutions A/S, Hjarbrækvej 65, 8831 Lægstrup	
Int.:MDC QC:CM APP.:			Tlf.: +45 96 49 43 00 Info@lundsgby.dk	
Lundsgby Renewable Solutions A/S			This Drawing is subject to copyright and may not be reproduced without permission from Lundsgby Renewable Solutions A/S	

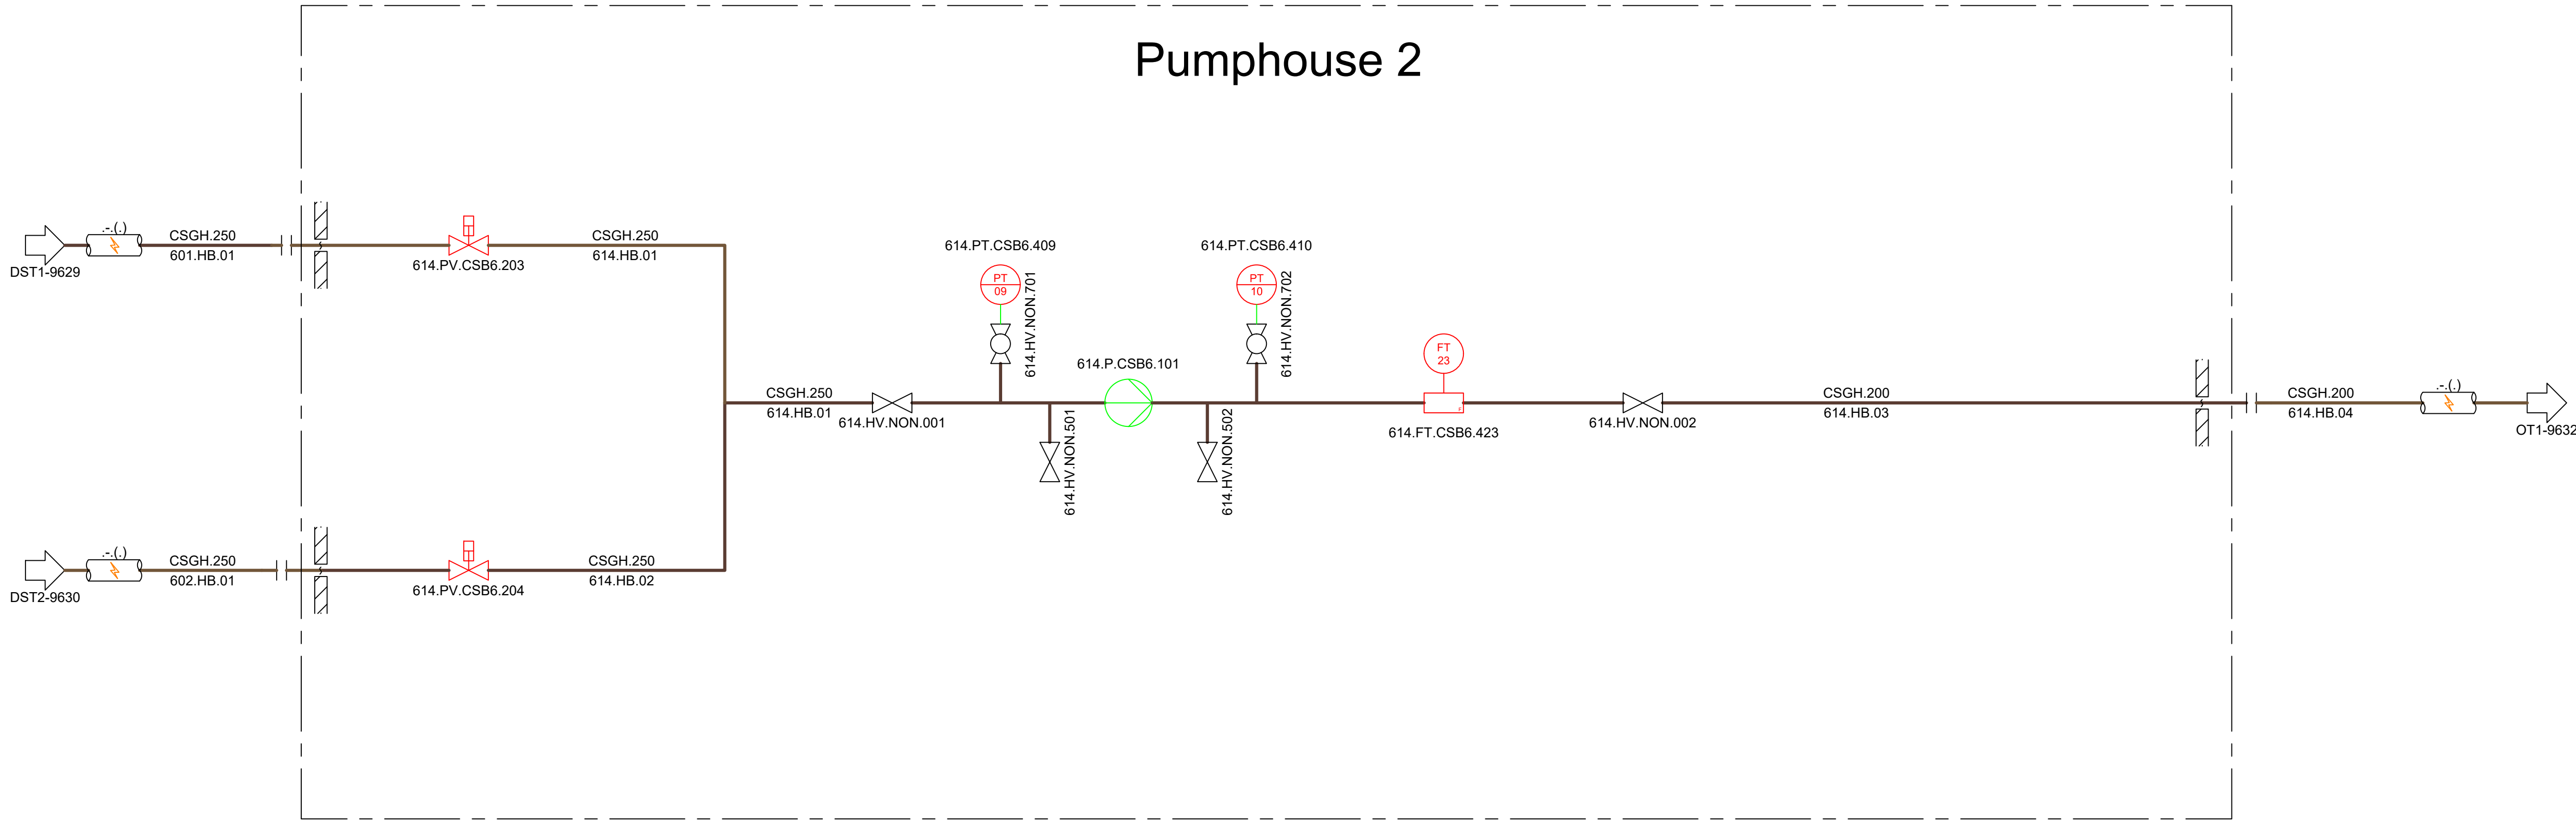

Rev. Nr.:	Rev. Dato:	Rev. Description:	Project nr...1768
Builder:	ST1		Drawing nr...:
Project:	SLK		9631
Subject:	DST pump		
	Rev. 6		
Int.:MDC	QC:CM	APP.:	Date: 15-10-2025
LUNDSBY RENEWABLE SOLUTIONS Lundsby Renewable Solutions A/S, Hjarbækvej 65, 8831 Løgstrup Tlf.: +45 96 49 43 00 Info@lundsby.dk This Drawing is subject to copyright and may not be reproduced without permission from Lundsby Renewable Solutions A/S			
FORMAT:			A1

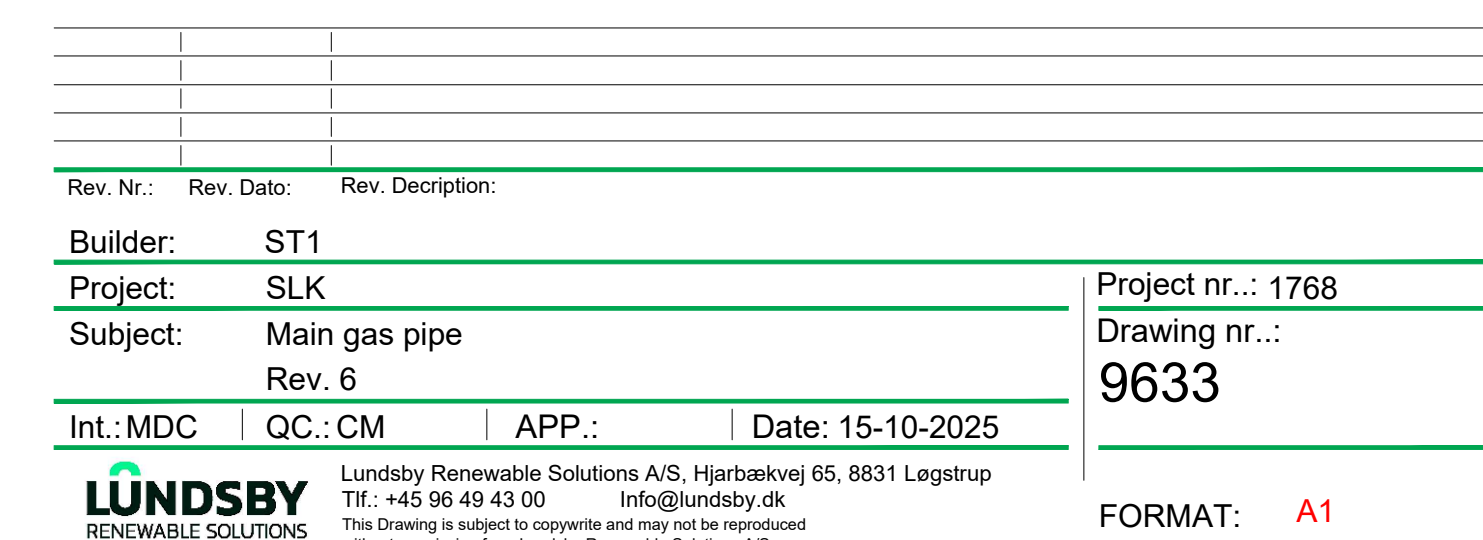


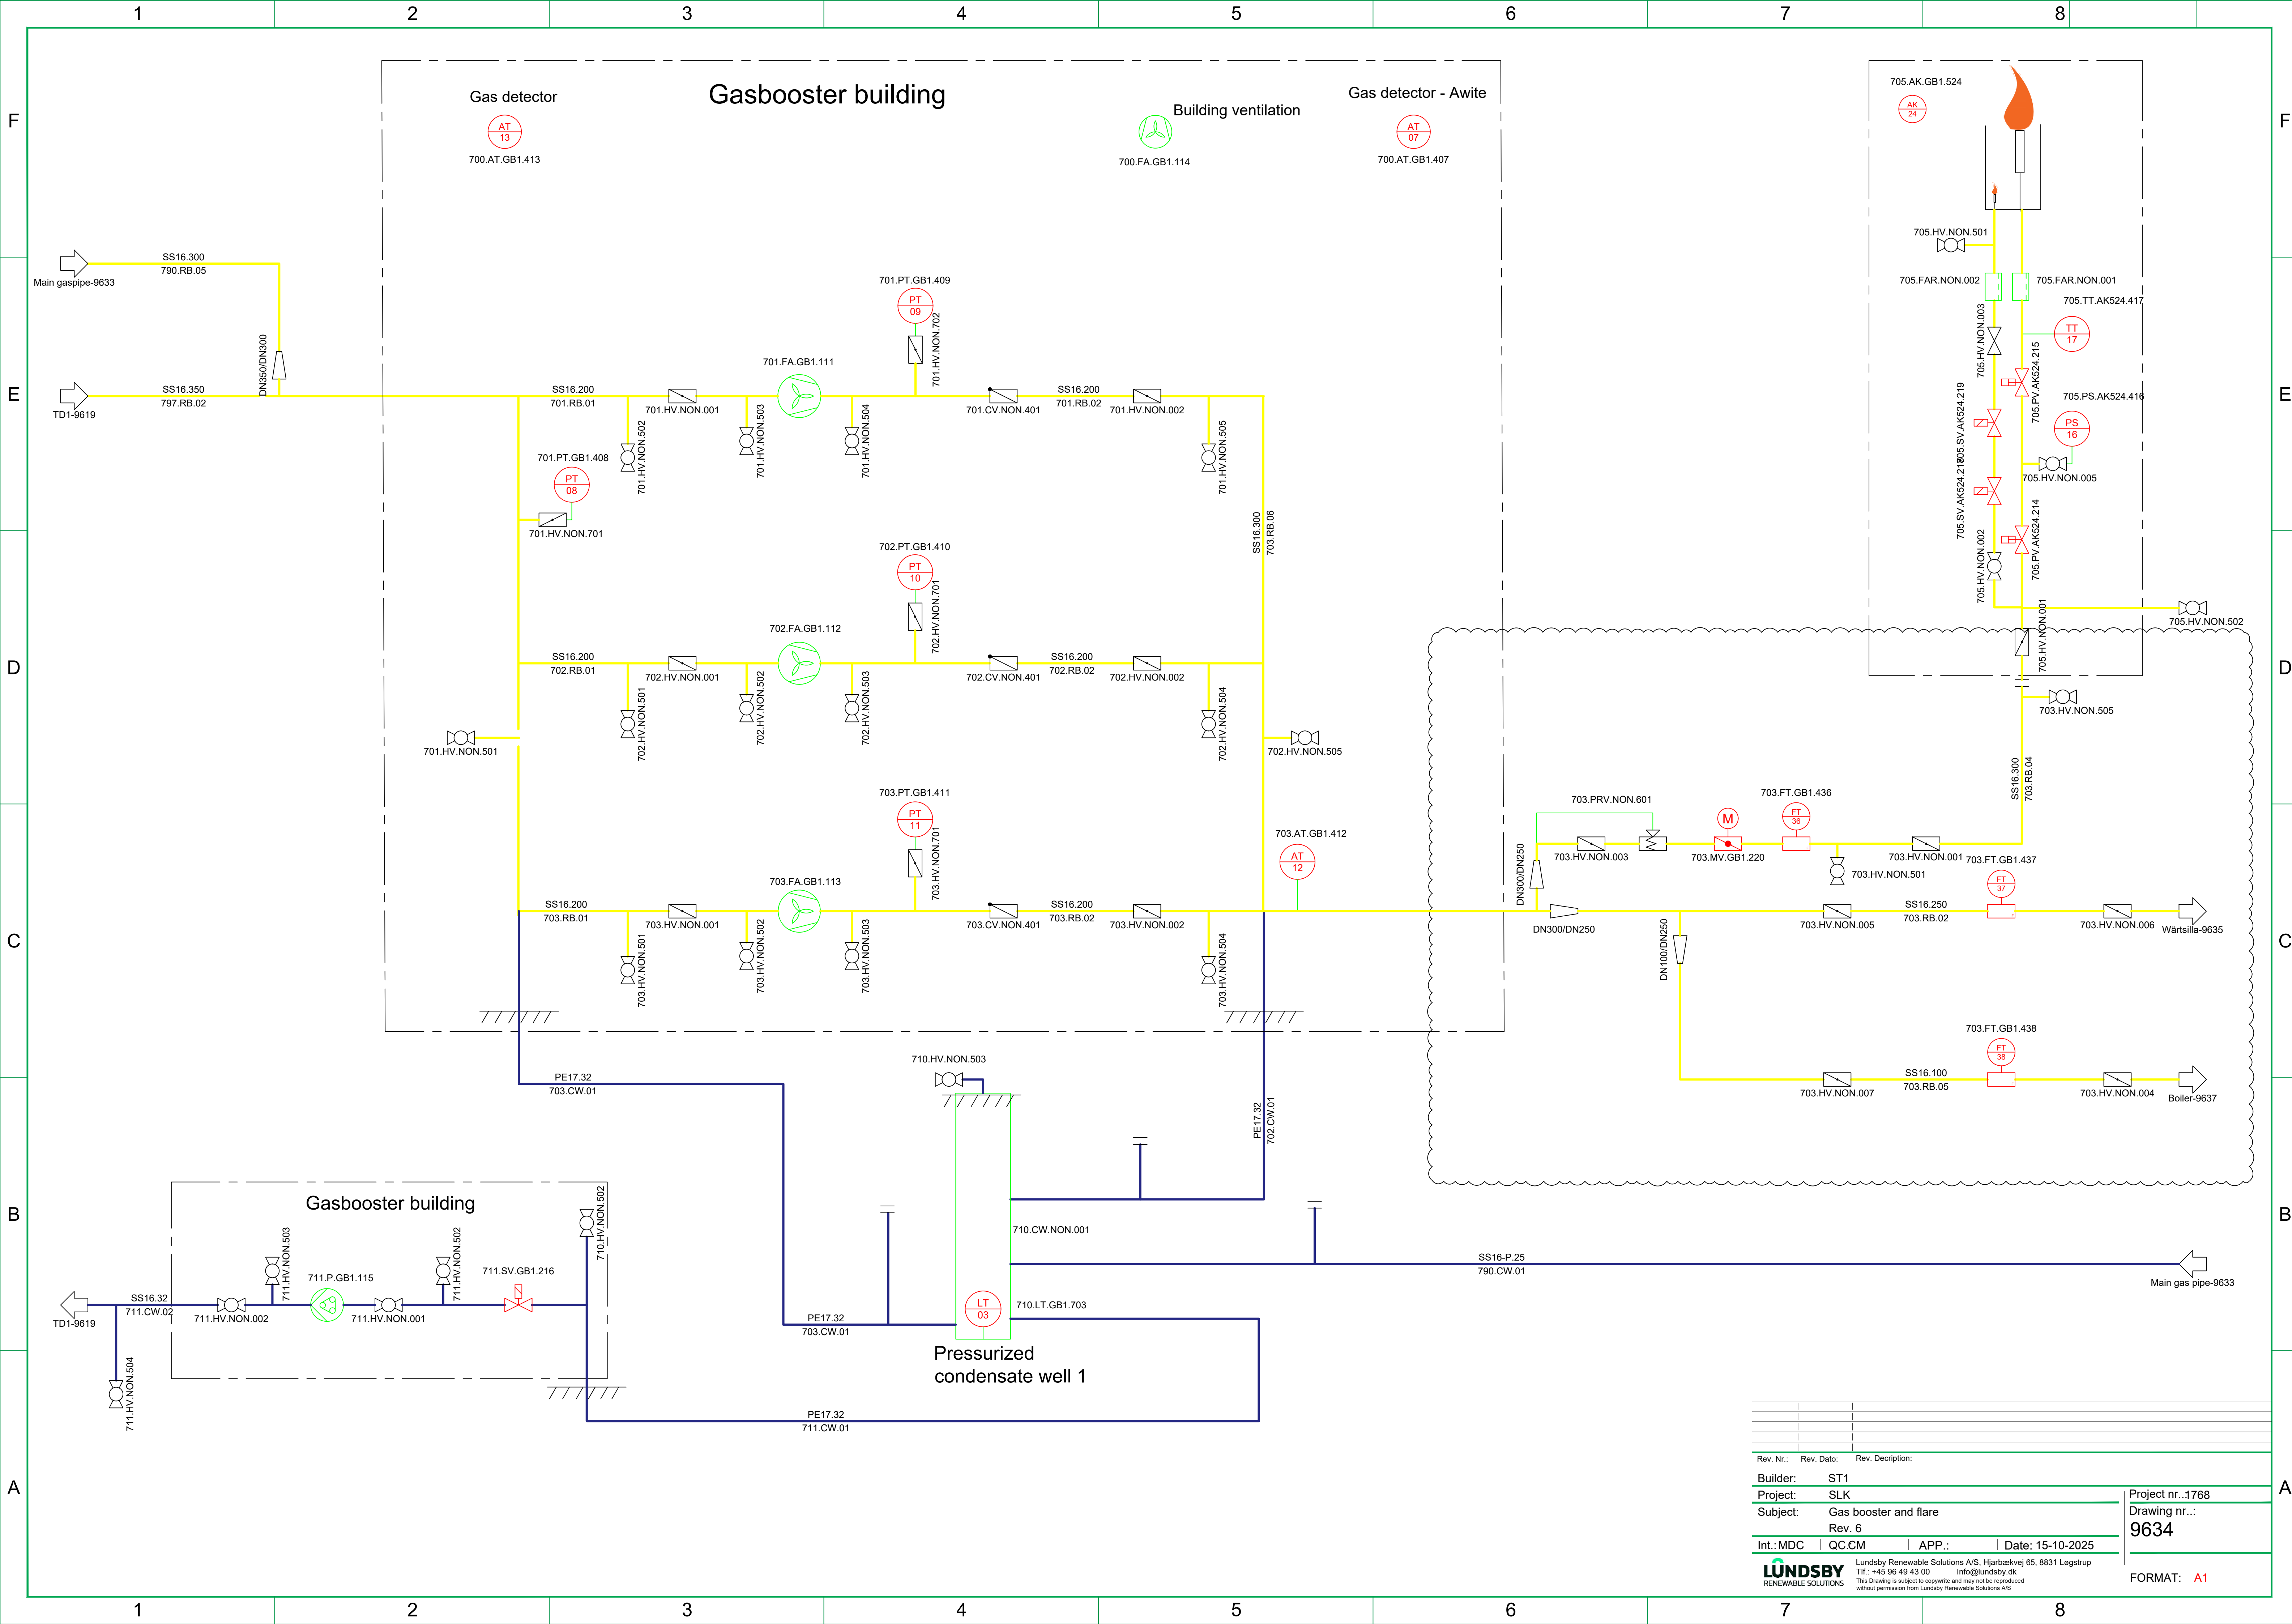


Wärtsillä

730-UPG-01

730-LBG-01

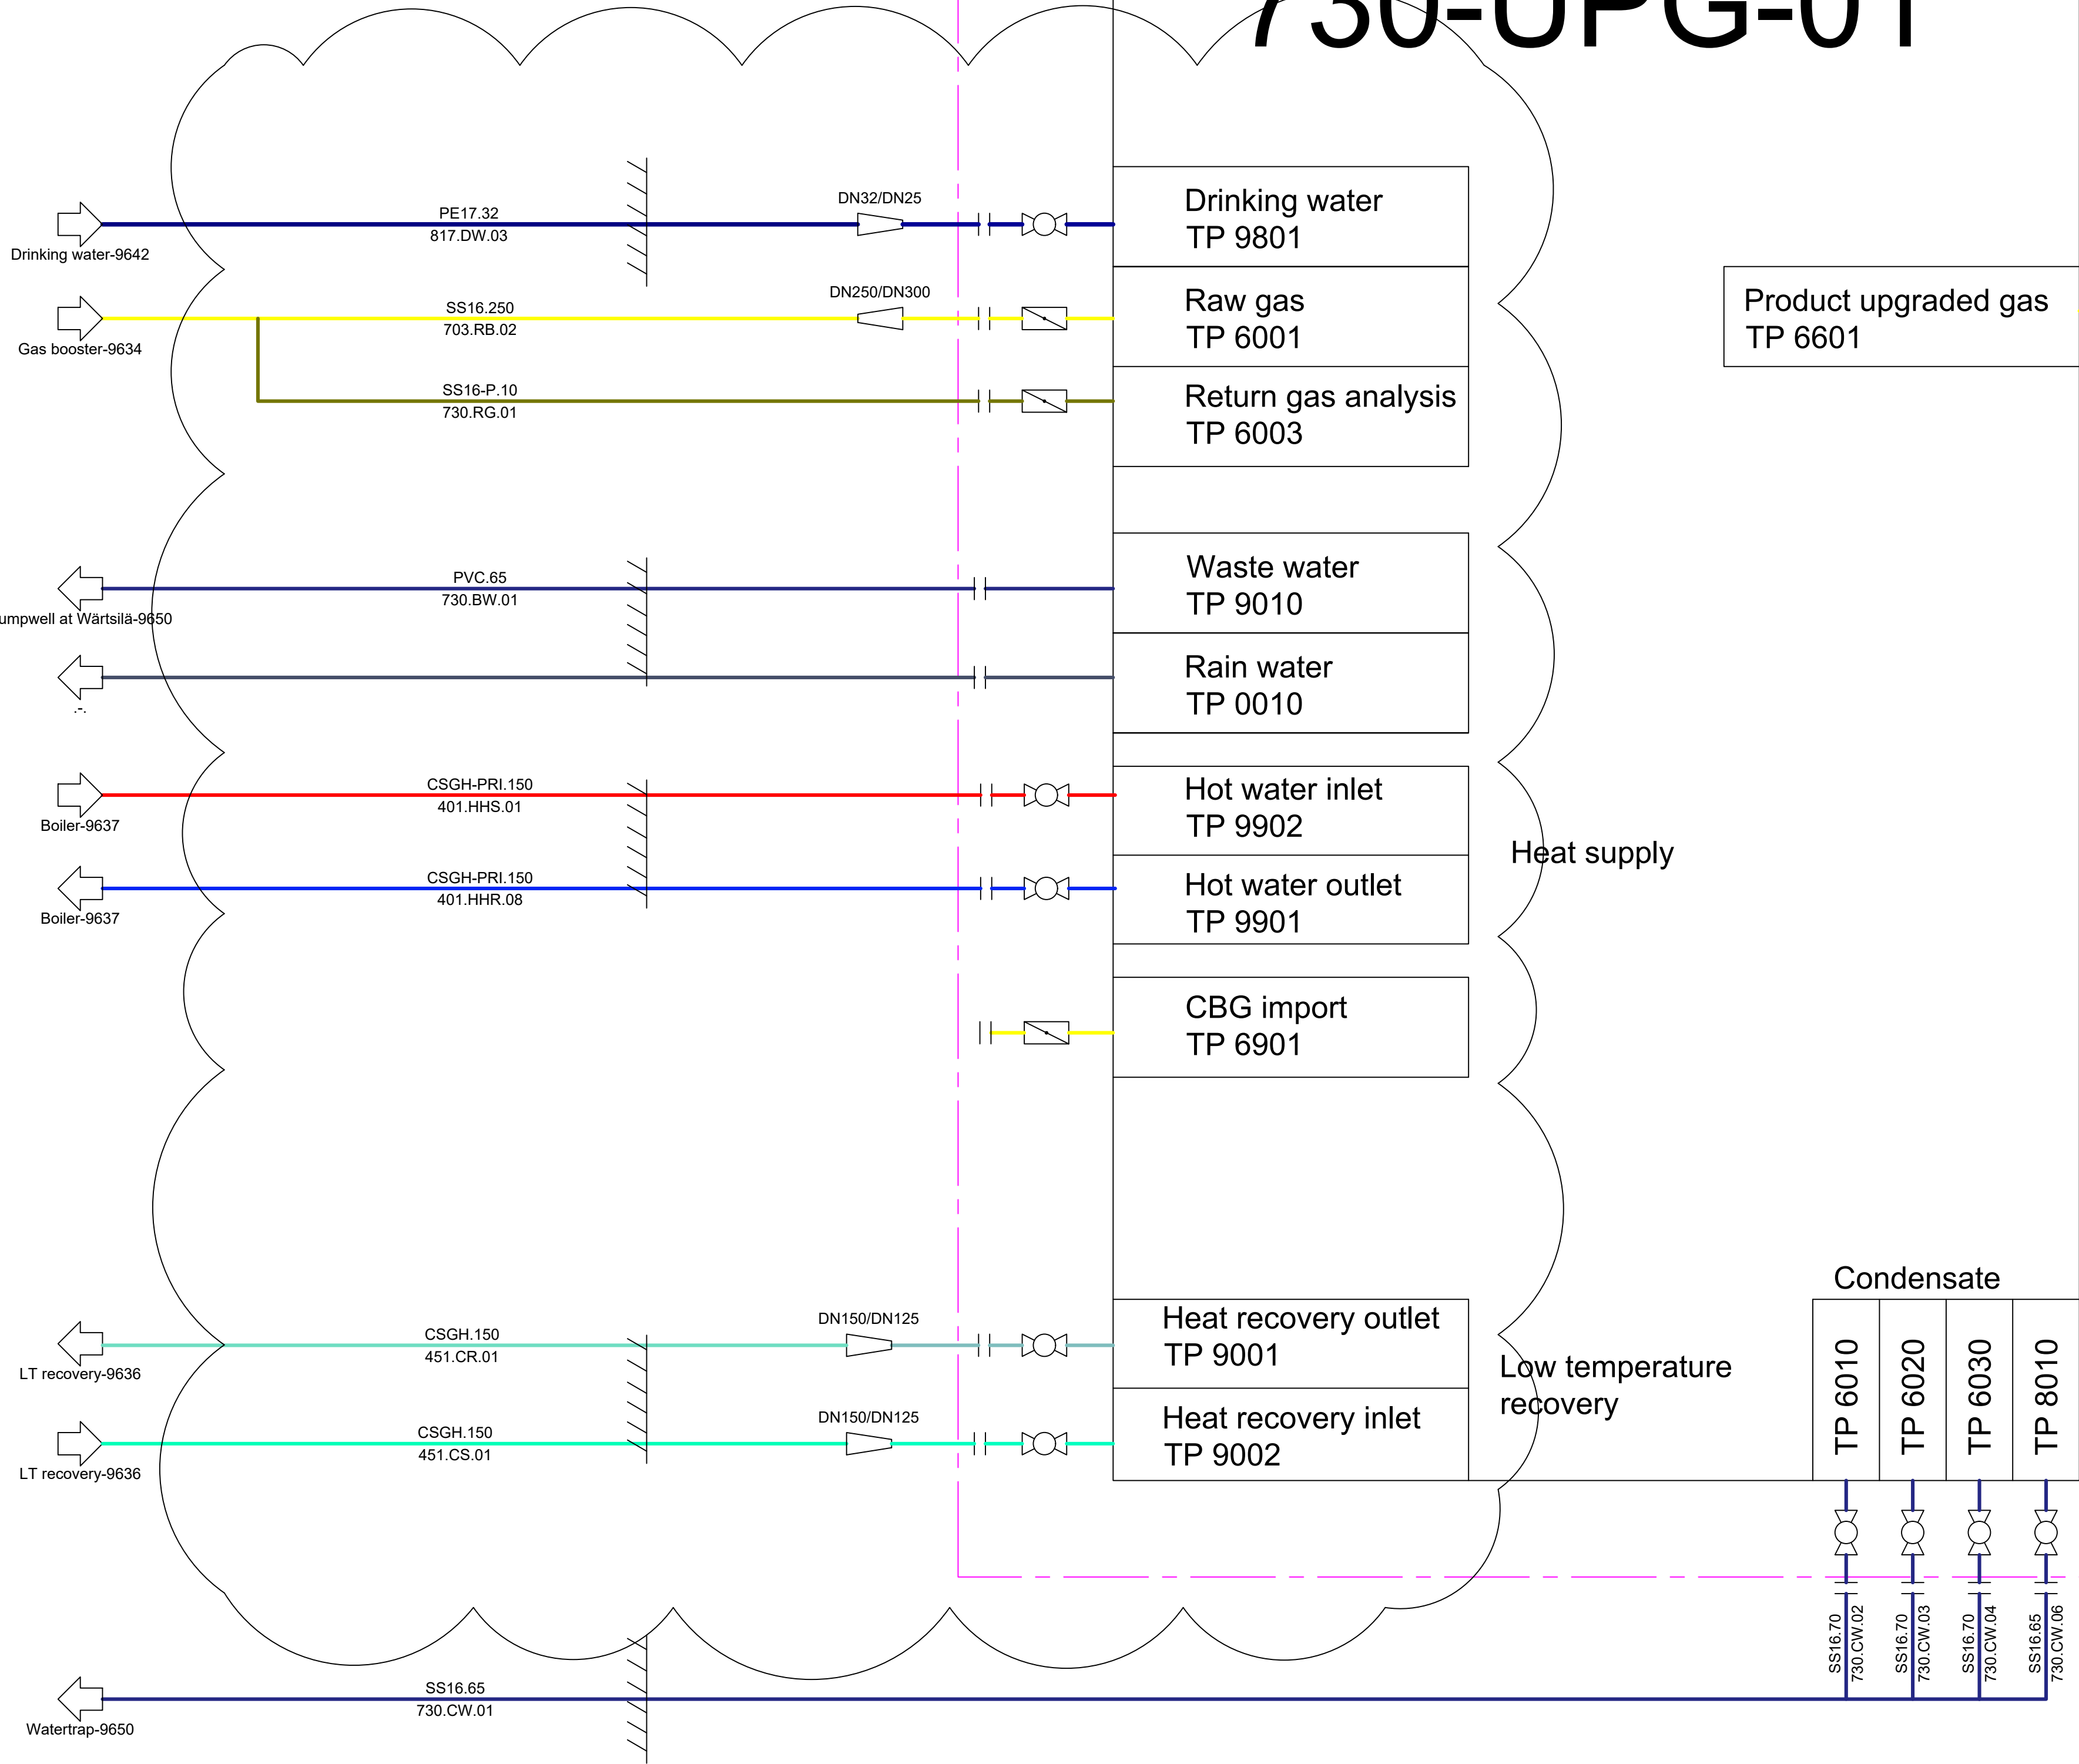


Product upgraded gas
TP 6601

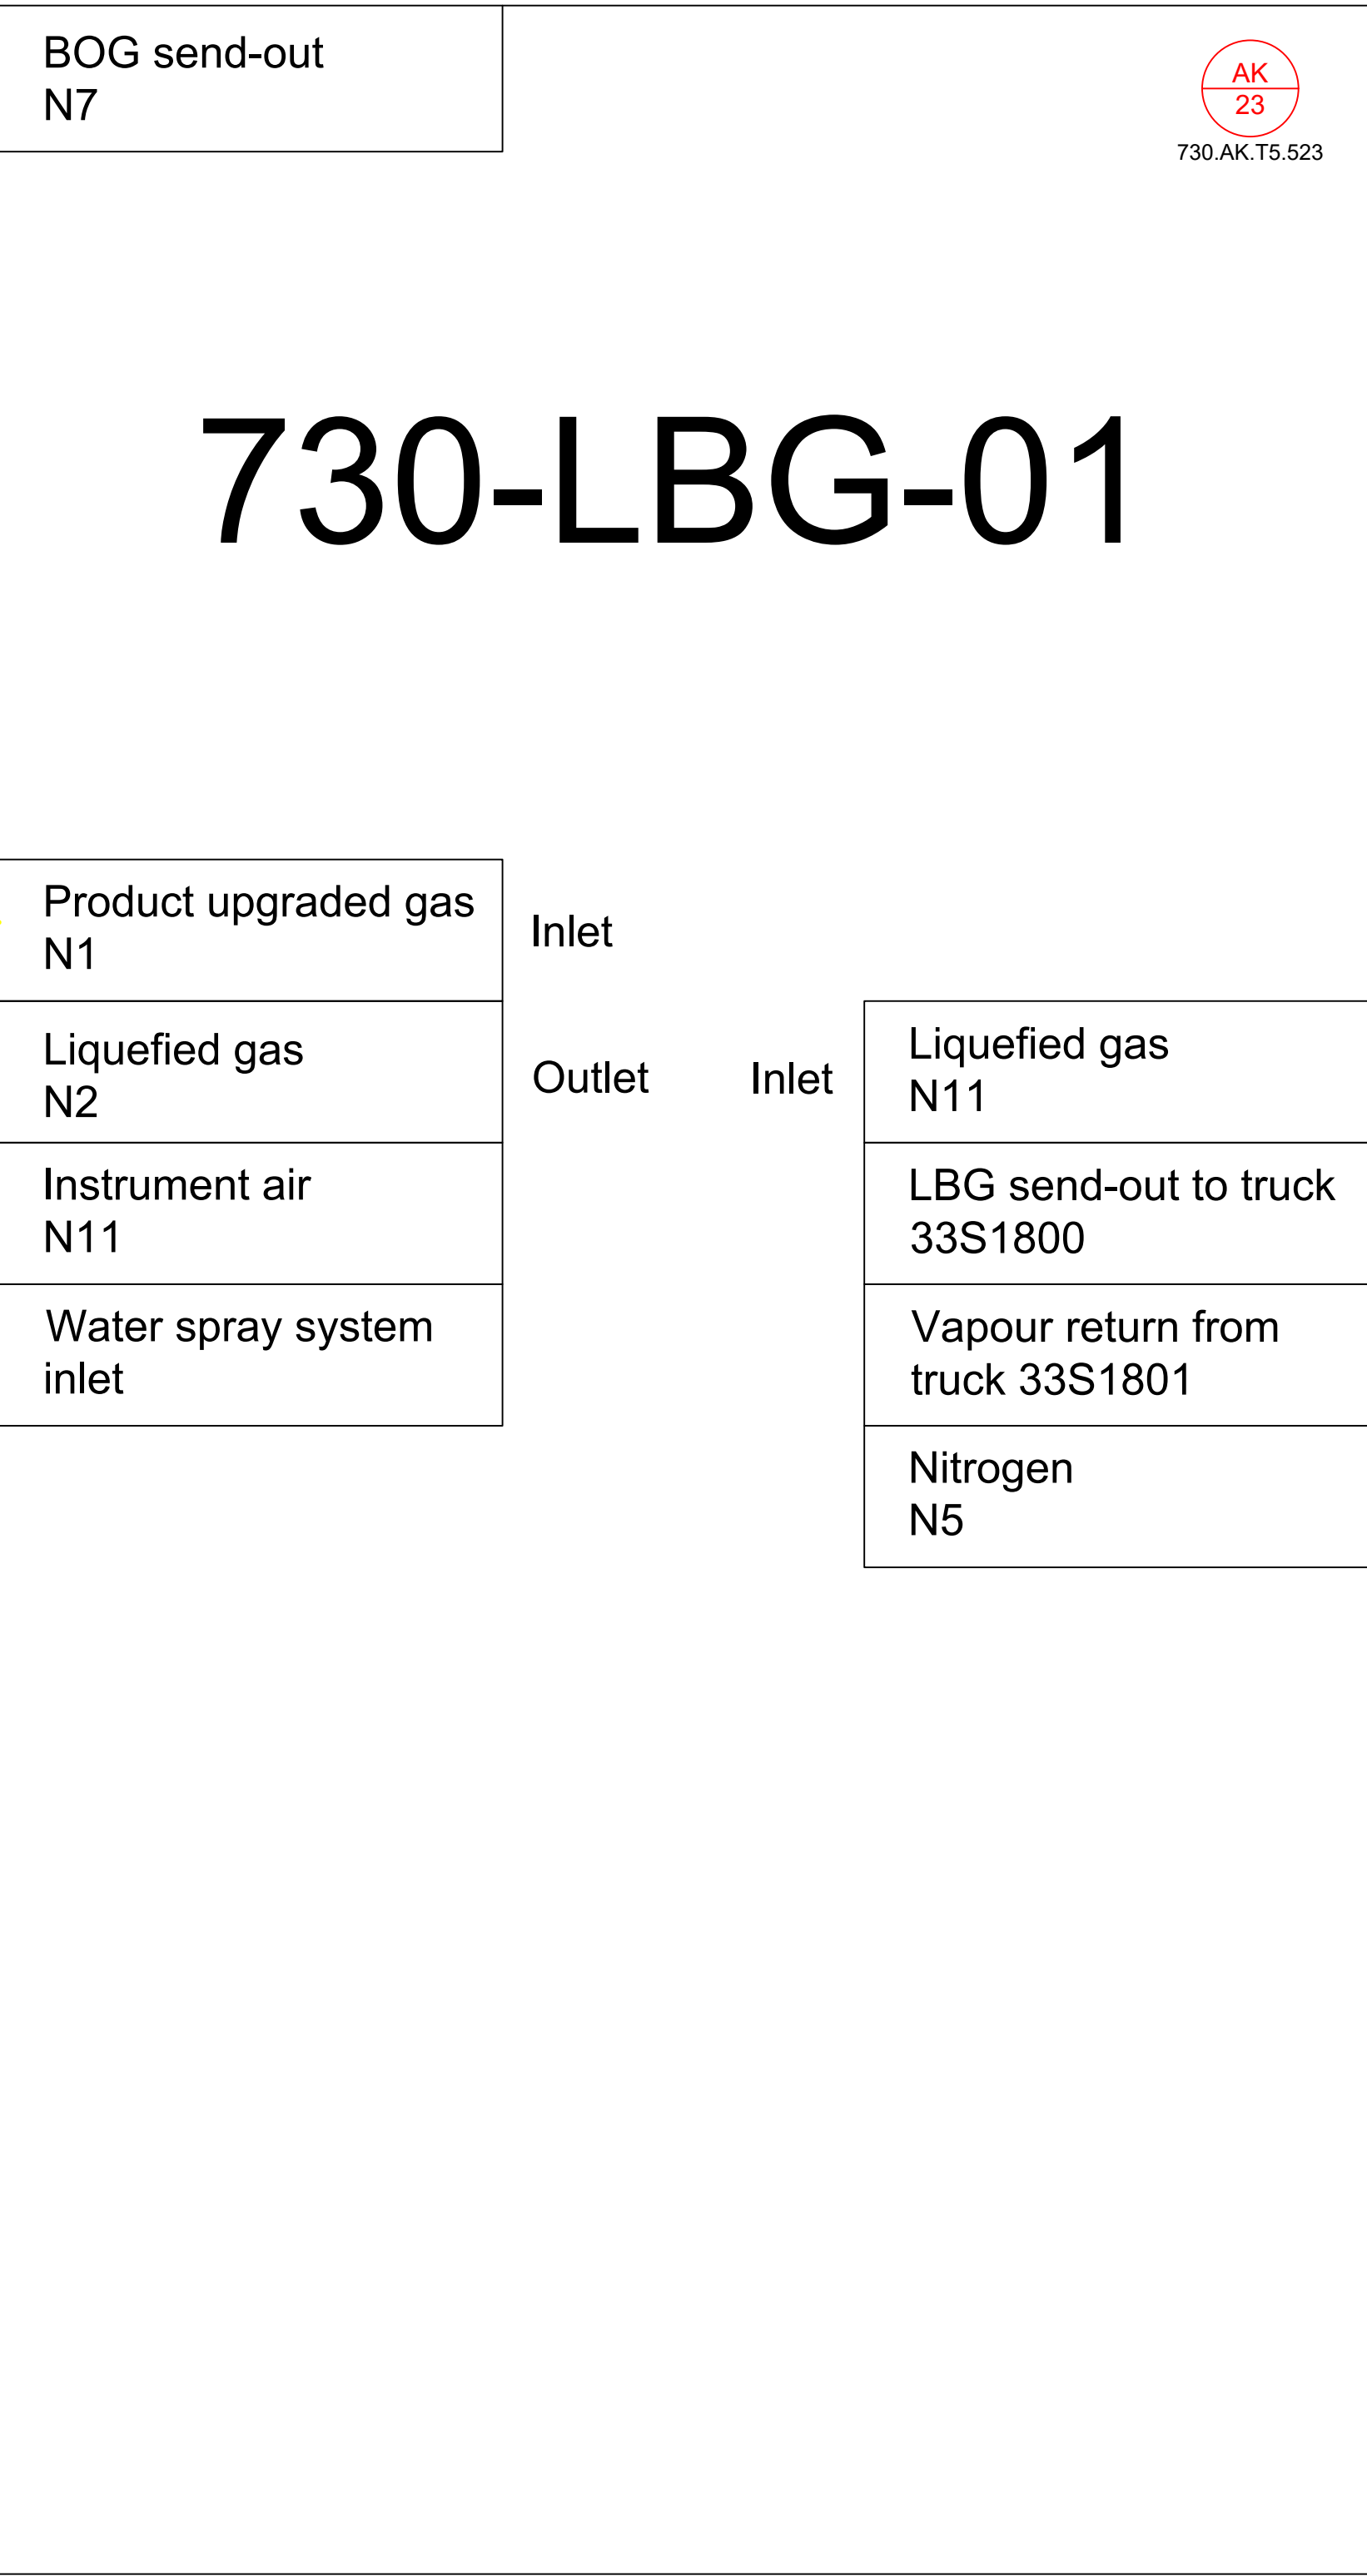


Rev. Nr.:	Rev. Dato:	Rev. Description:
Builder:	ST1	
Project:	SLK	
Subject:	Upgrade	
	Rev. 6	
Int.:MDC	QC.CM	APP.:
		Date: 15-10-2025
LUNDSBY RENEWABLE SOLUTIONS		
Lundby Renewable Solutions A/S, Hjarbækvej 65, 8831 Lægstrup Tlf.: +45 96 49 43 00 Info@lundby.dk This Drawing is subject to copyright and may not be reproduced without permission from Lundby Renewable Solutions A/S		
Project nr...:1768 Drawing nr...: 9635		FORMAT: A1

Technology building

Heat pump scope

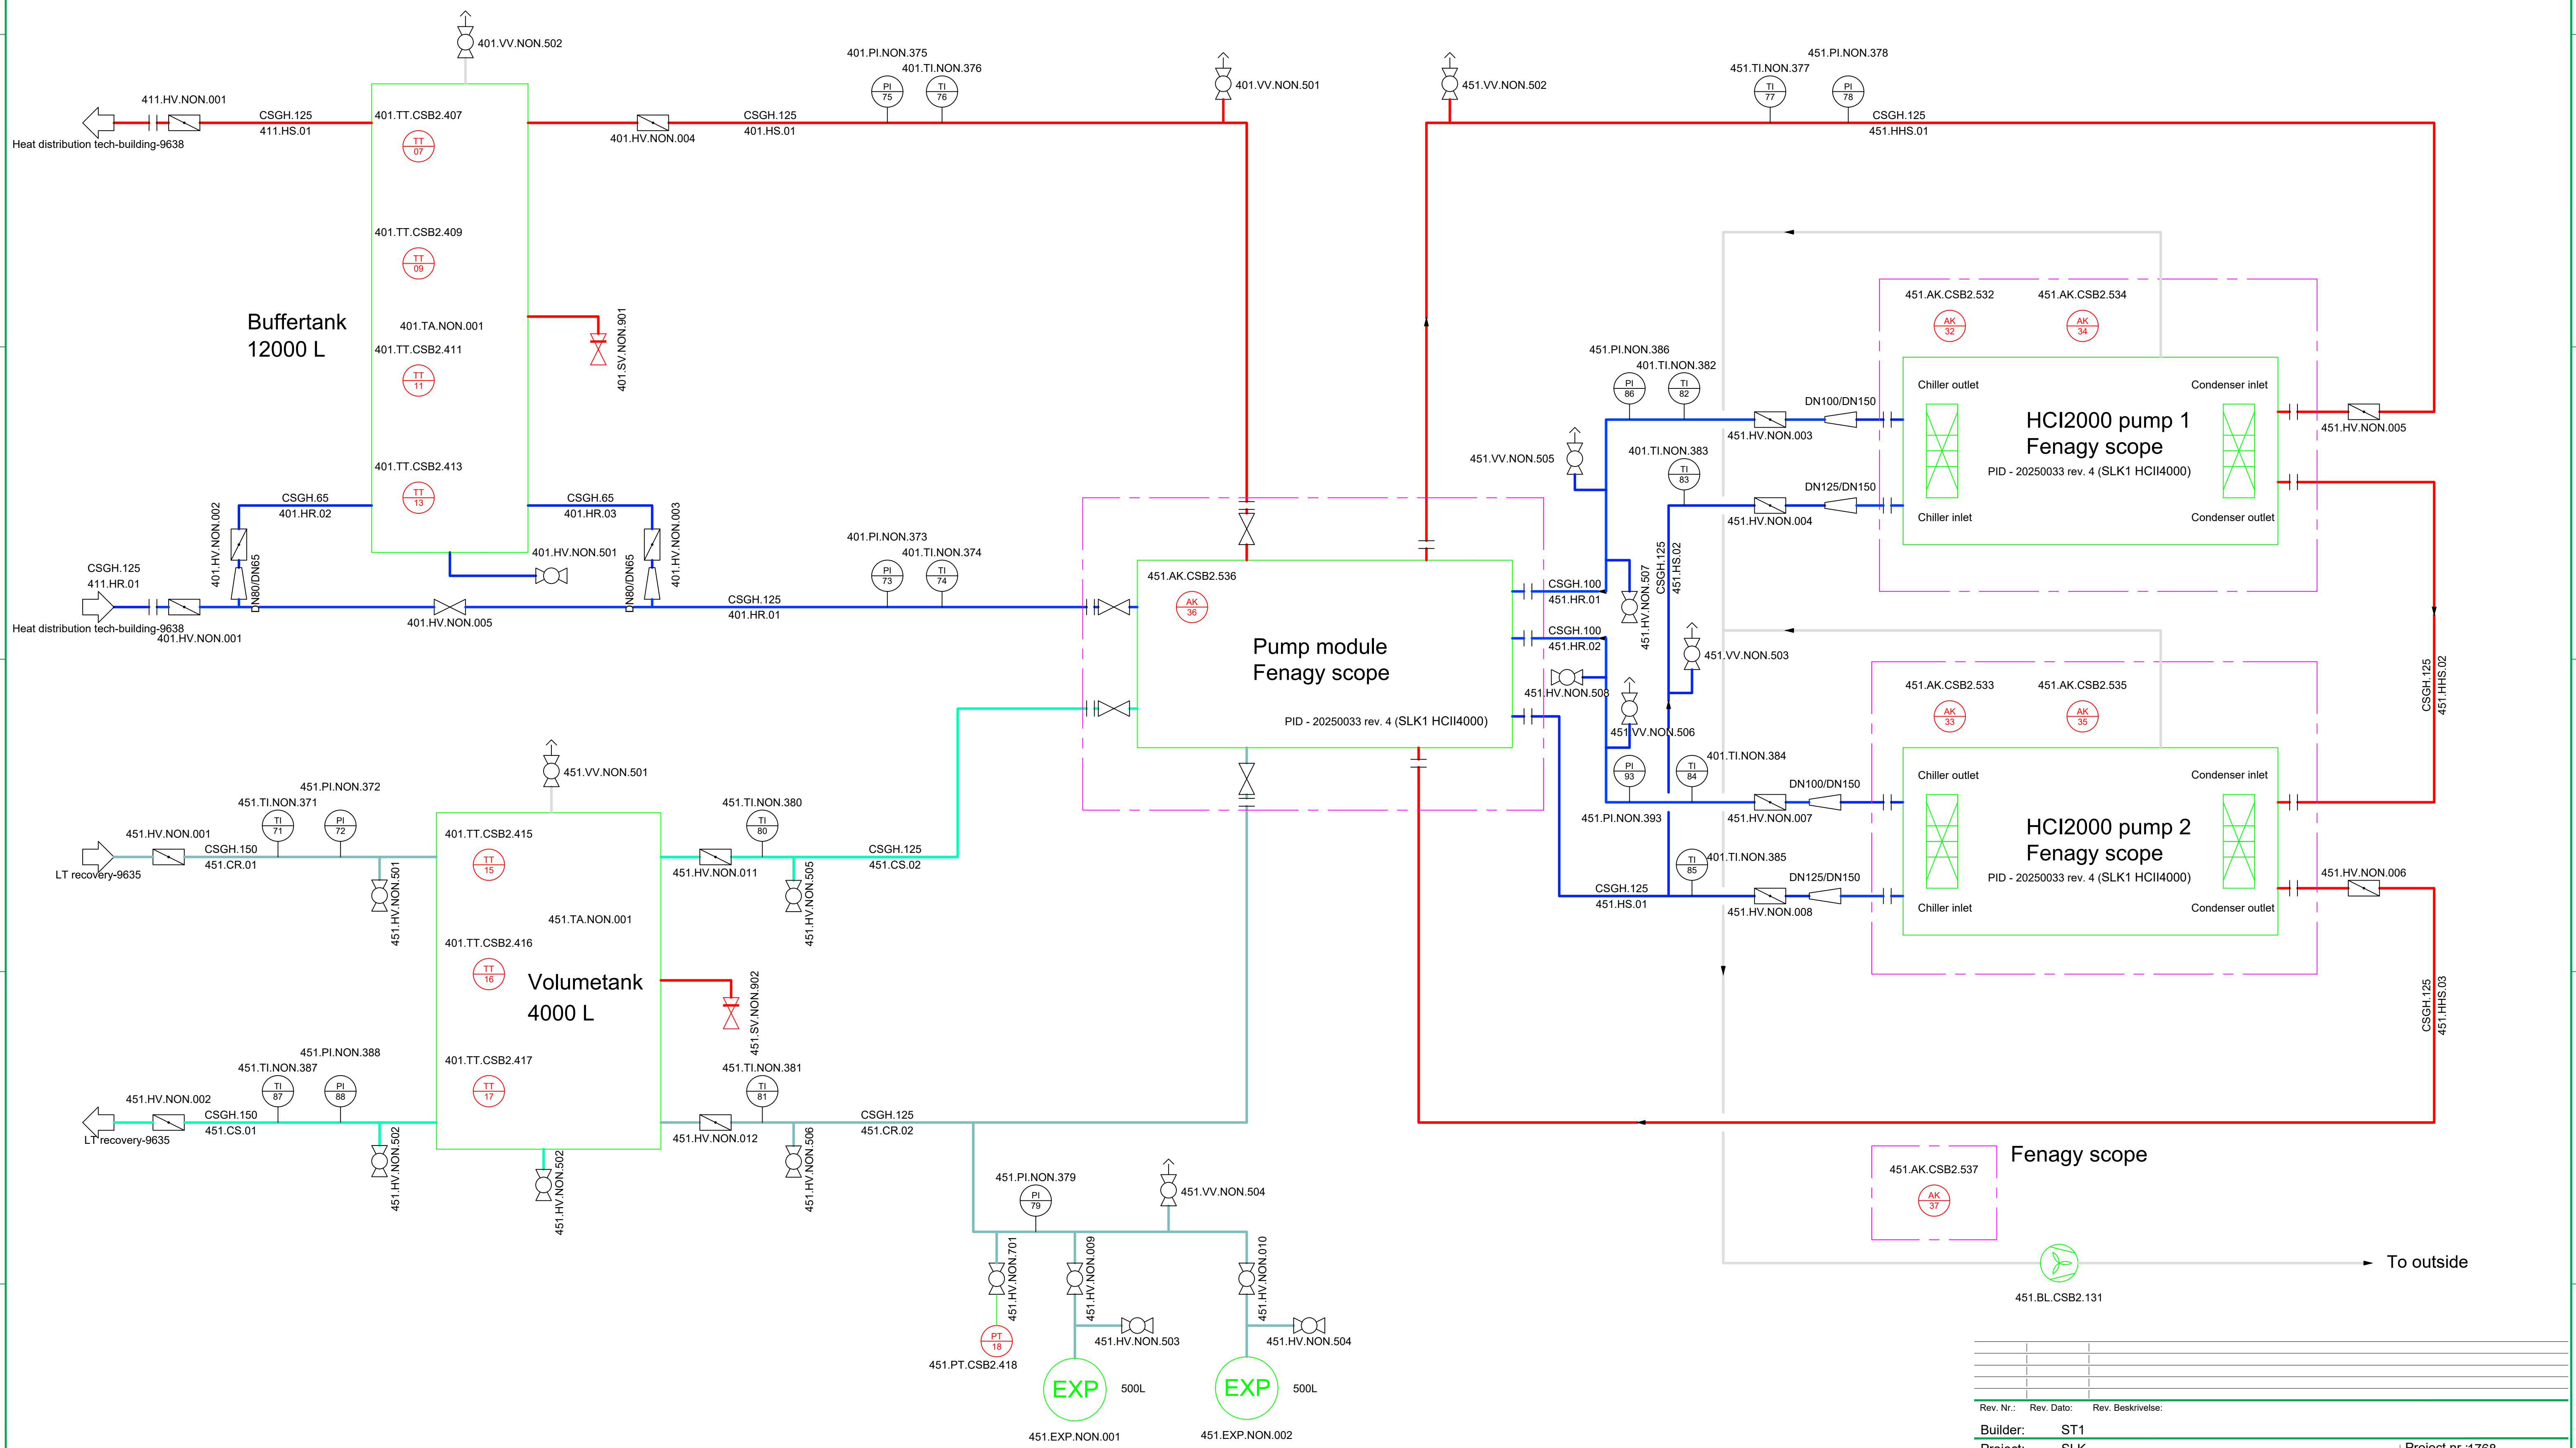

Rev. Nr.:	Rev. Dato:	Rev. Beskrivelse:	
Builder:	ST1		
Project:	SLK		
Subject:	Heat pumps		
Rev.:	6		
Int.:MDC	QC: CM	APP.:	Date: 15-10-2025
LUNDSBY RENEWABLE SOLUTIONS			Lundsby Biogas A/S, Hjarbækvej 65, 8831 Løgstrup Tlf.: +45 96 49 43 00 info@lundsbybiogas.dk Denne tegning er underlagt copyright og må ikke reproducere uden tilladelse fra Lundsbybiogas A/S
Project nr.:1768 Drawing nr.: 9636			FORMAT: A1

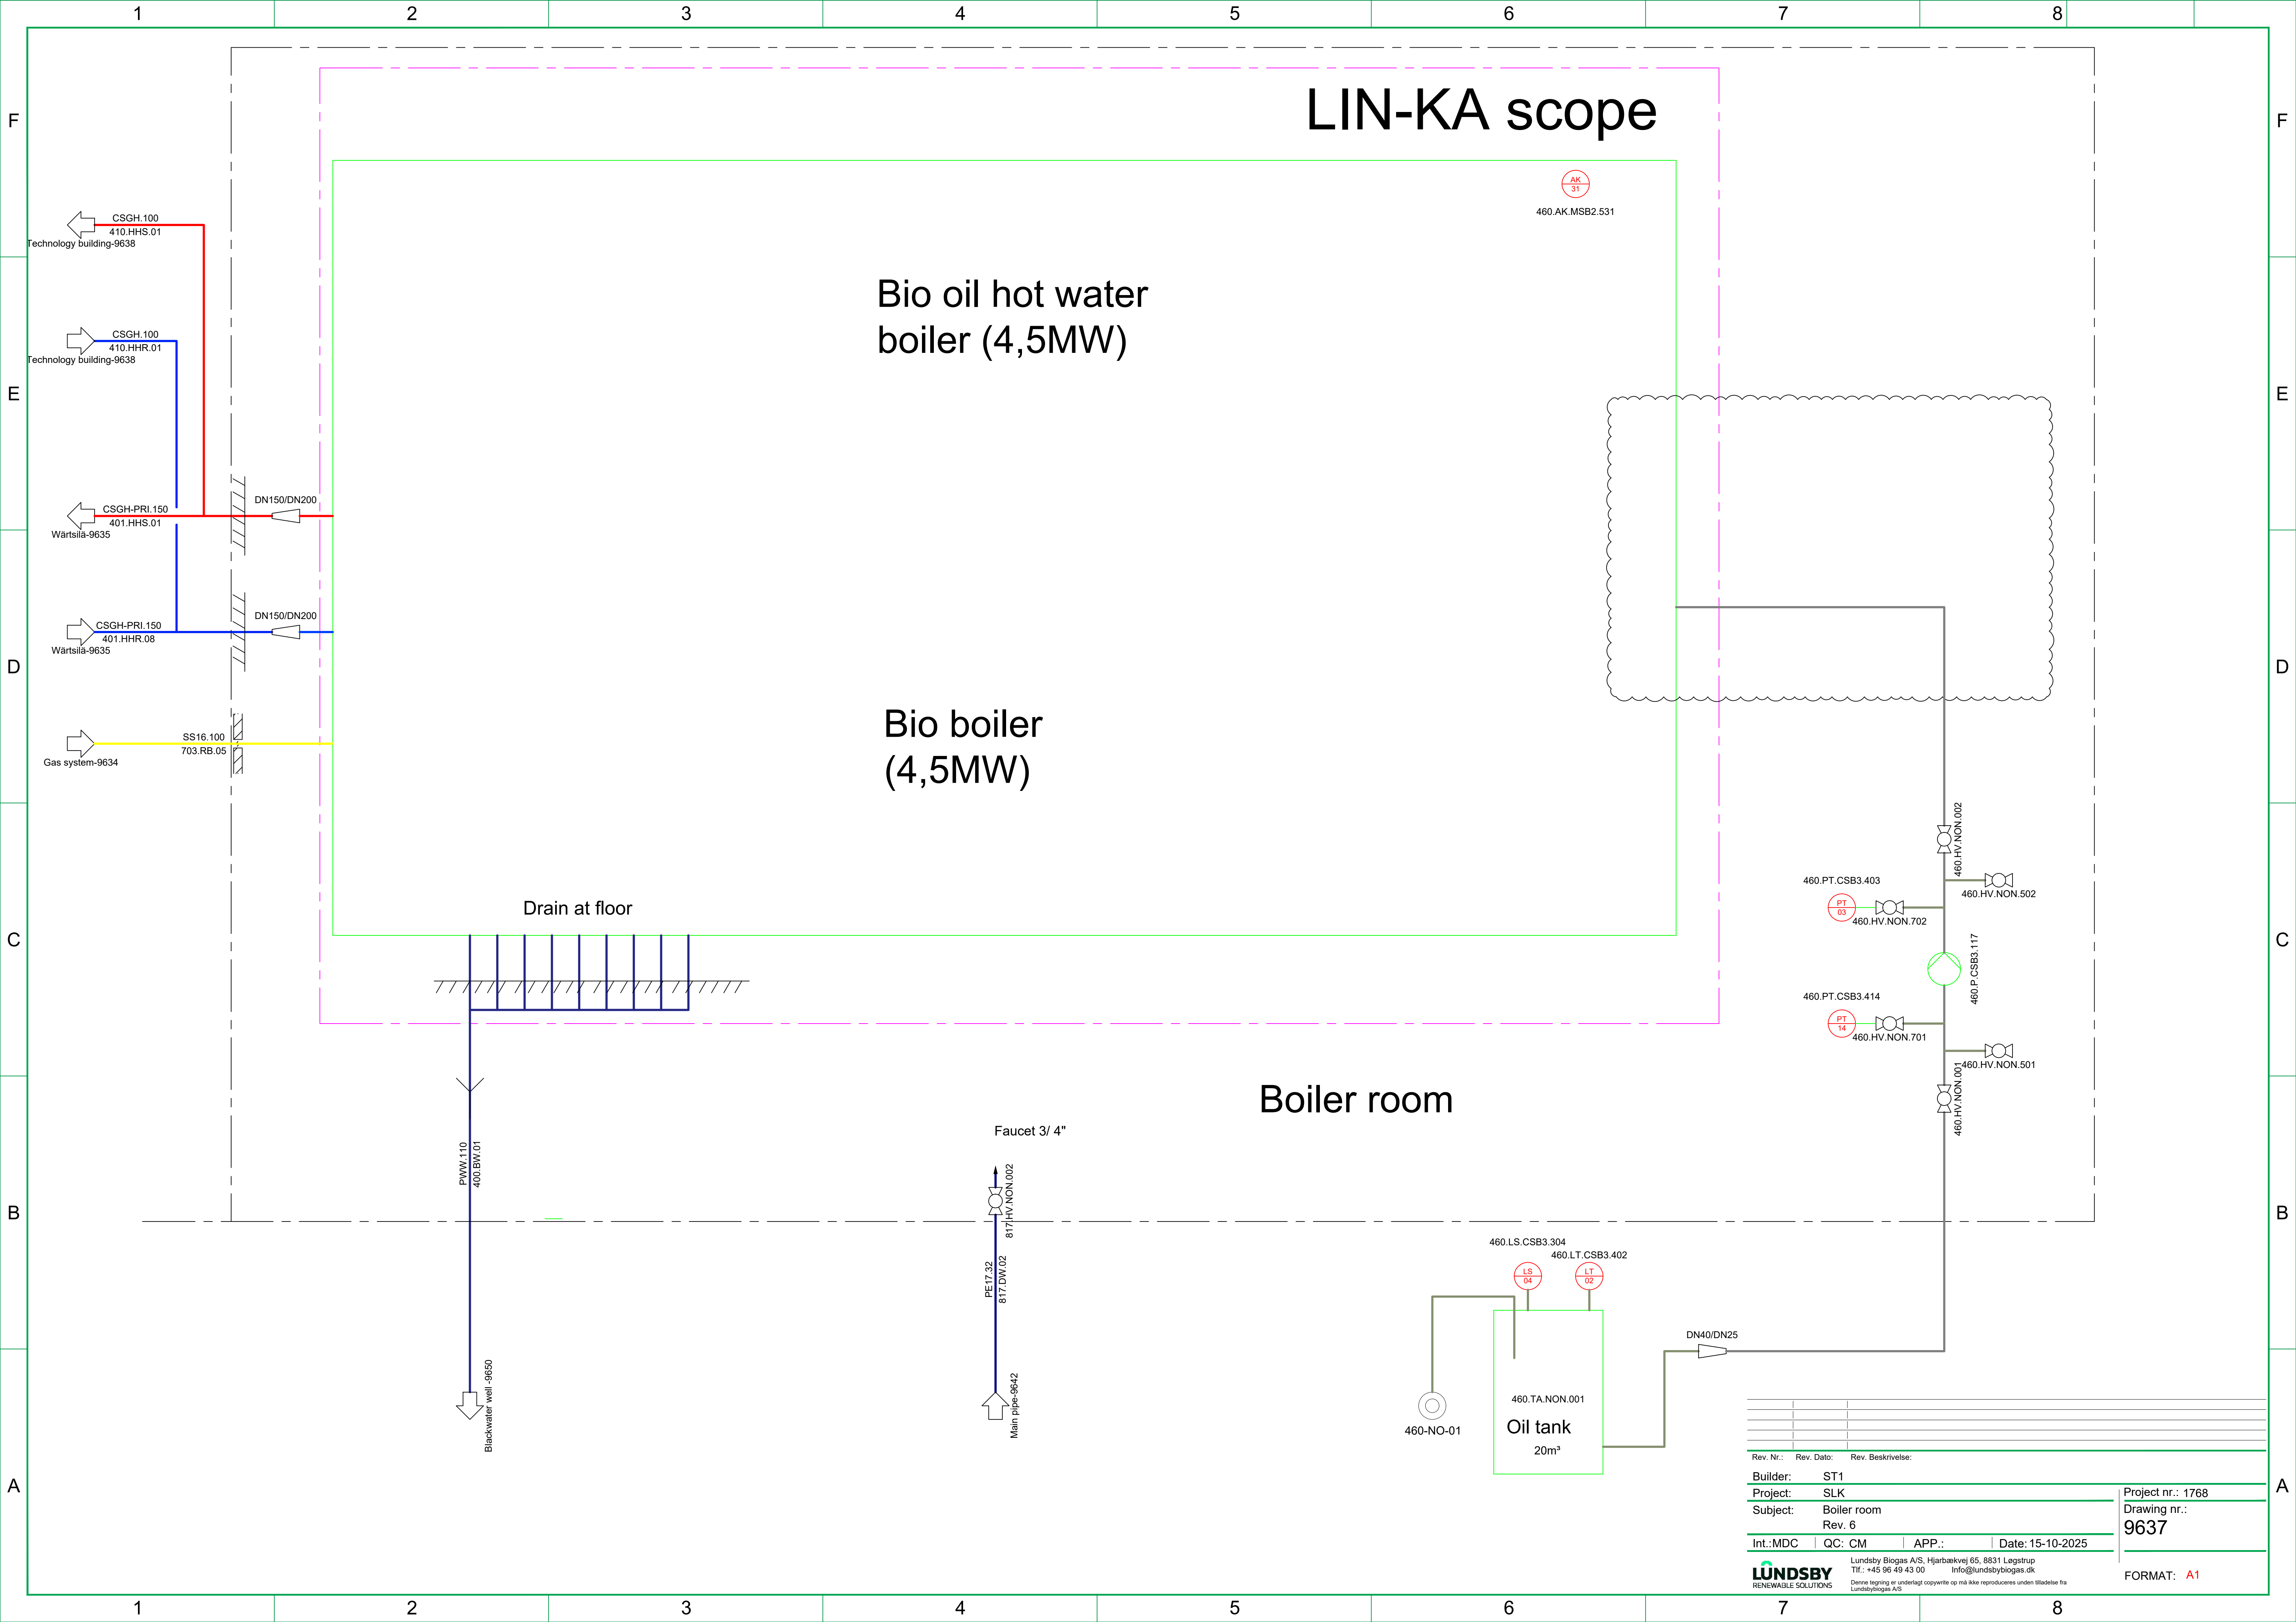

LIN-KA scope

Bio oil hot water boiler (4,5MW)

Bio boiler (4,5MW)

Boiler room

AK 31
460.AK.MSB2.531


Drain at floor

Faucet 3/ 4"

460.LS.CSB3.304
460.LT.CSB3.402

460.TA.NON.001
Oil tank
20m³

Rev. Nr.:	Rev. Dato:	Rev. Beskrivelse:	
Builder:	ST1		
Project:	SLK		
Subject:	Boiler room		
Rev. 6			
Int.:MDC	QC: CM	APP.:	Date: 15-10-2025
LUNDSBY RENEWABLE SOLUTIONS			Lundsby Biogas A/S, Hjarbækvej 65, 8831 Løgstrup Tlf.: +45 96 49 43 00 info@lundsbybiogas.dk Denne tegning er underlagt copyright og må ikke reproduceres uden tilladelse fra Lundsbybiogas A/S
			Project nr.: 1768 Drawing nr.: 9637 FORMAT: A1

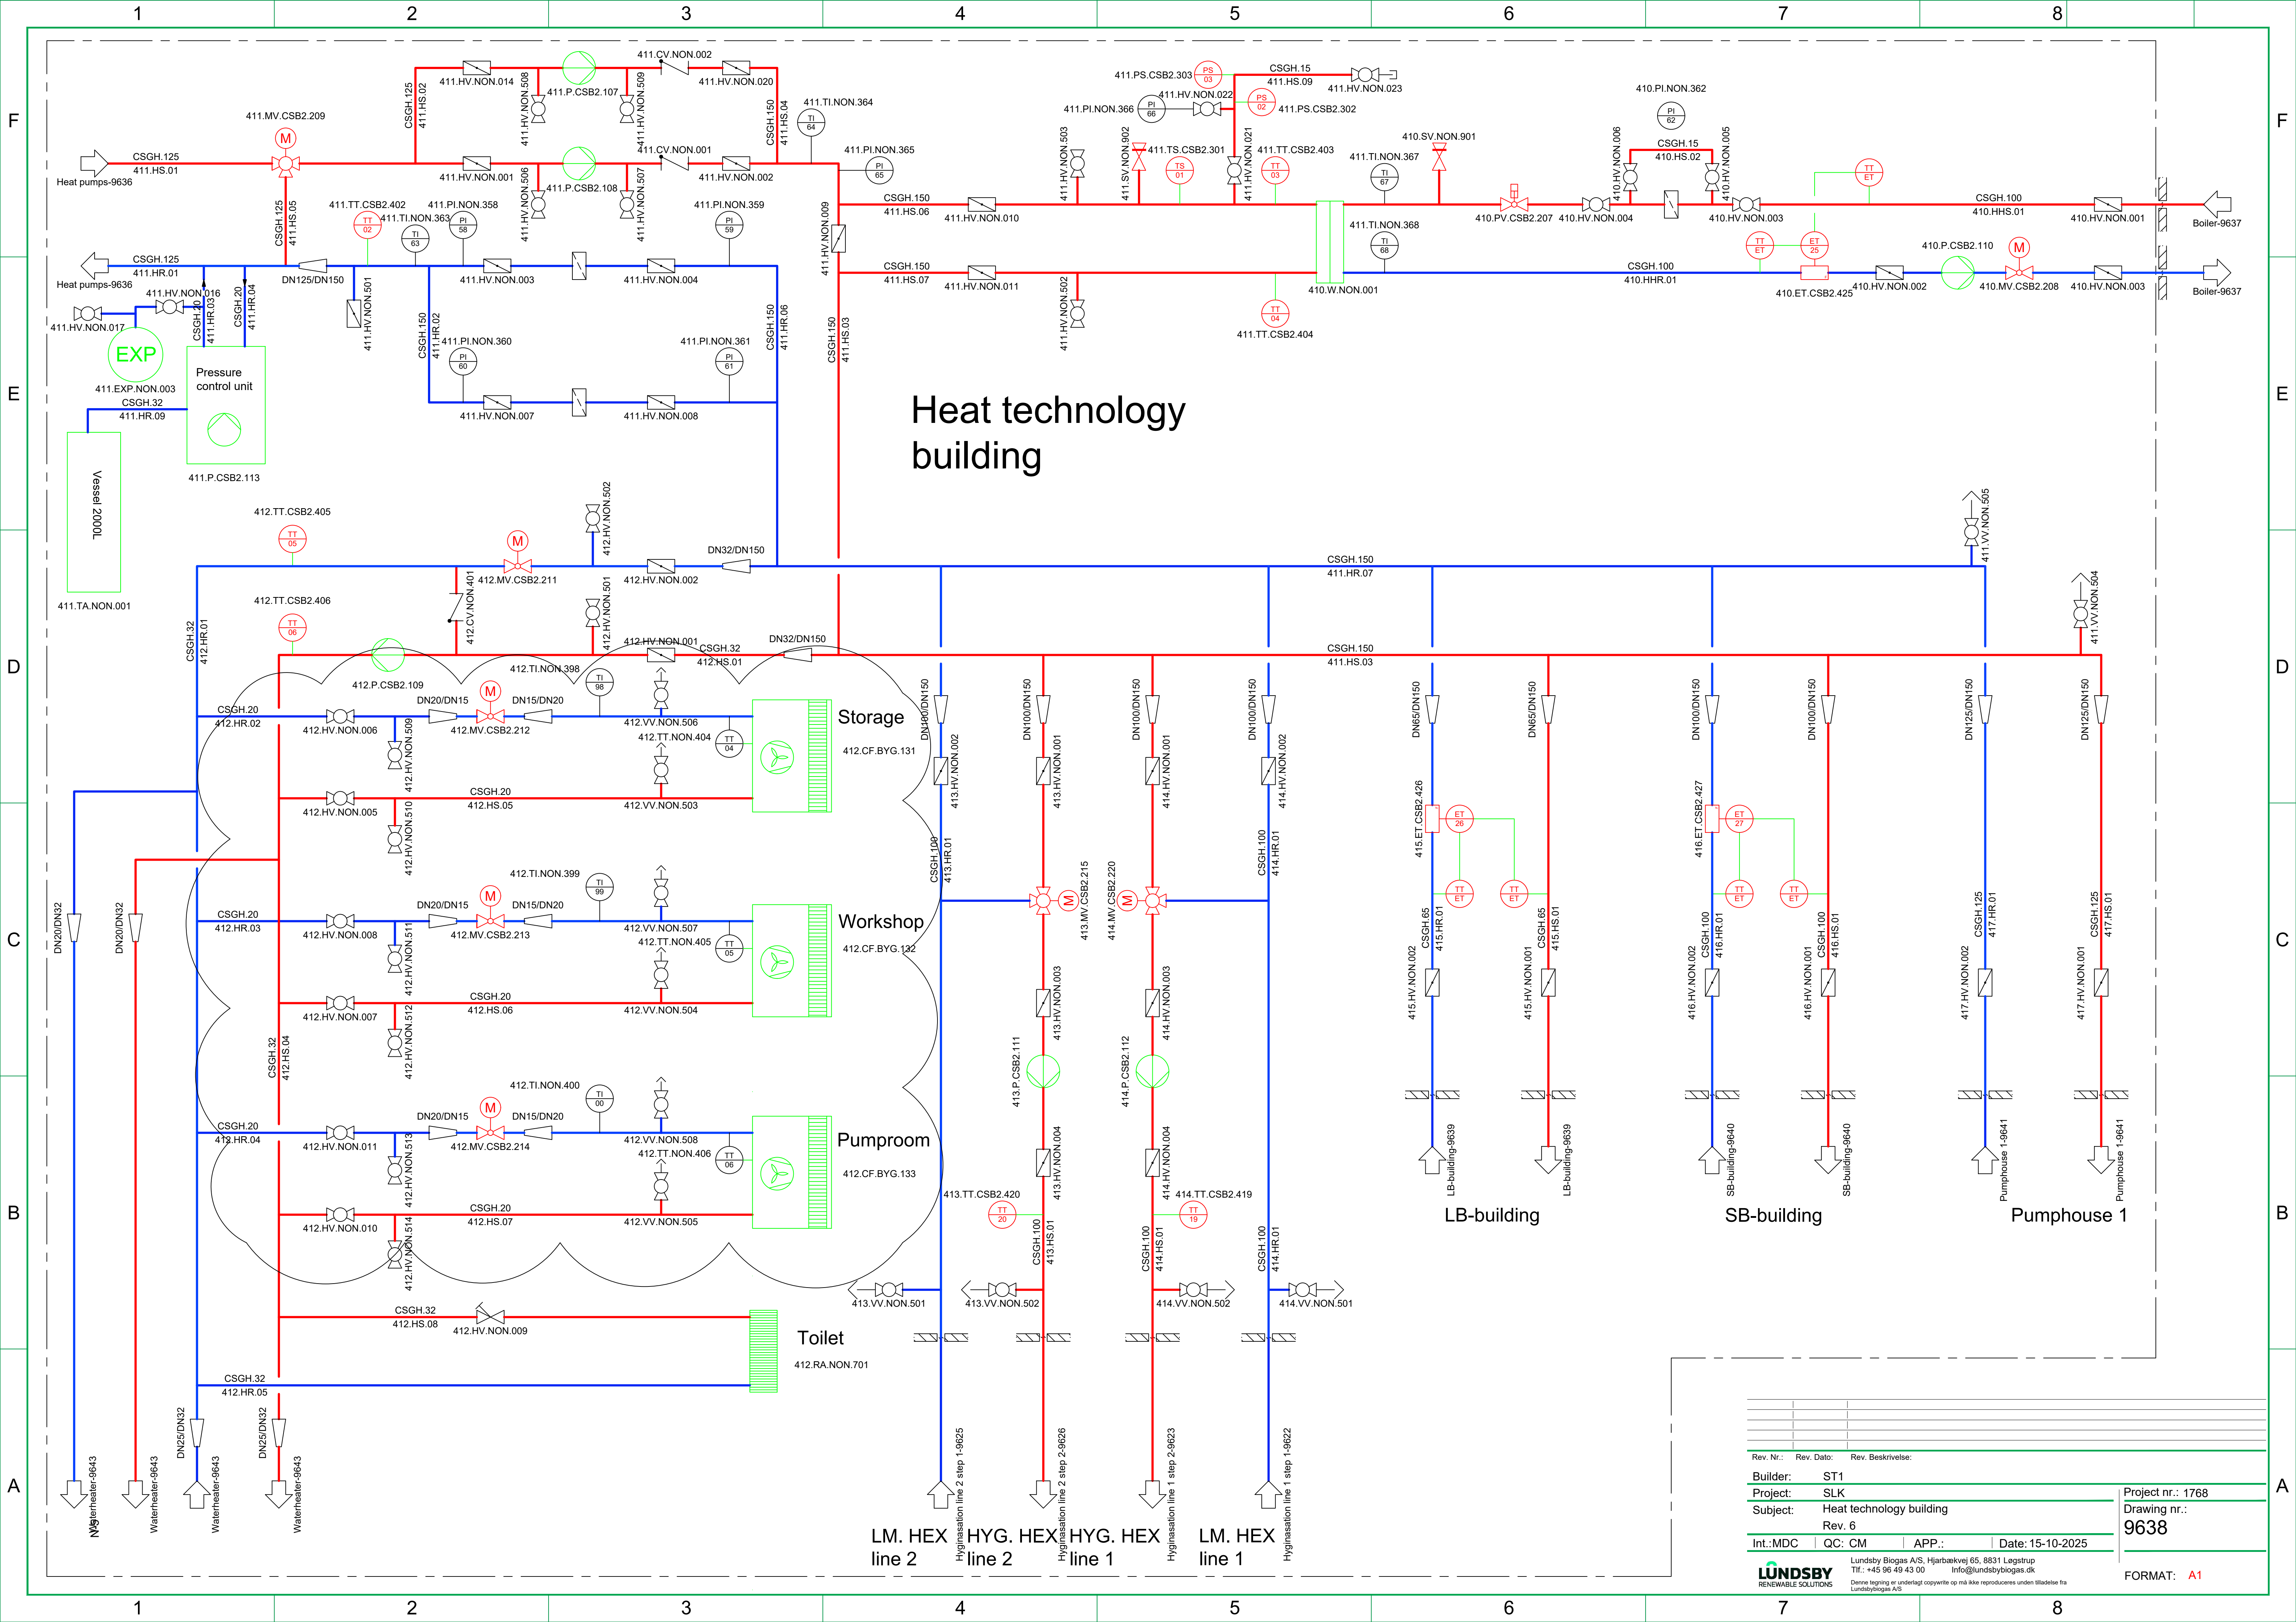

Heat technology building

Storage

Workshop

Pumproom

Toilet

LB-building

SB-building

Pumphouse 1

Rev. Nr.:	Rev. Dato:	Rev. Beskrivelse:
Builder:	ST1	
Project:	SLK	
Subject:	Heat technology building	
Rev. 6		
Int.:MDC	QC: CM	APP.: Date: 15-10-2025

Project nr.: 1768
Drawing nr.: 9638


LUNDSBY
RENEWABLE SOLUTIONS

Lundsby Biogas A/S, Hjarbækvej 65, 8831 Løgstrup
Tlf.: +45 96 49 43 00
info@lundsbybiogas.dk

Denne tegning er underlagt copyright og må ikke reproducere uden tilladelse fra Lundsbybiogas A/S


FORMAT: A1

LB-Building

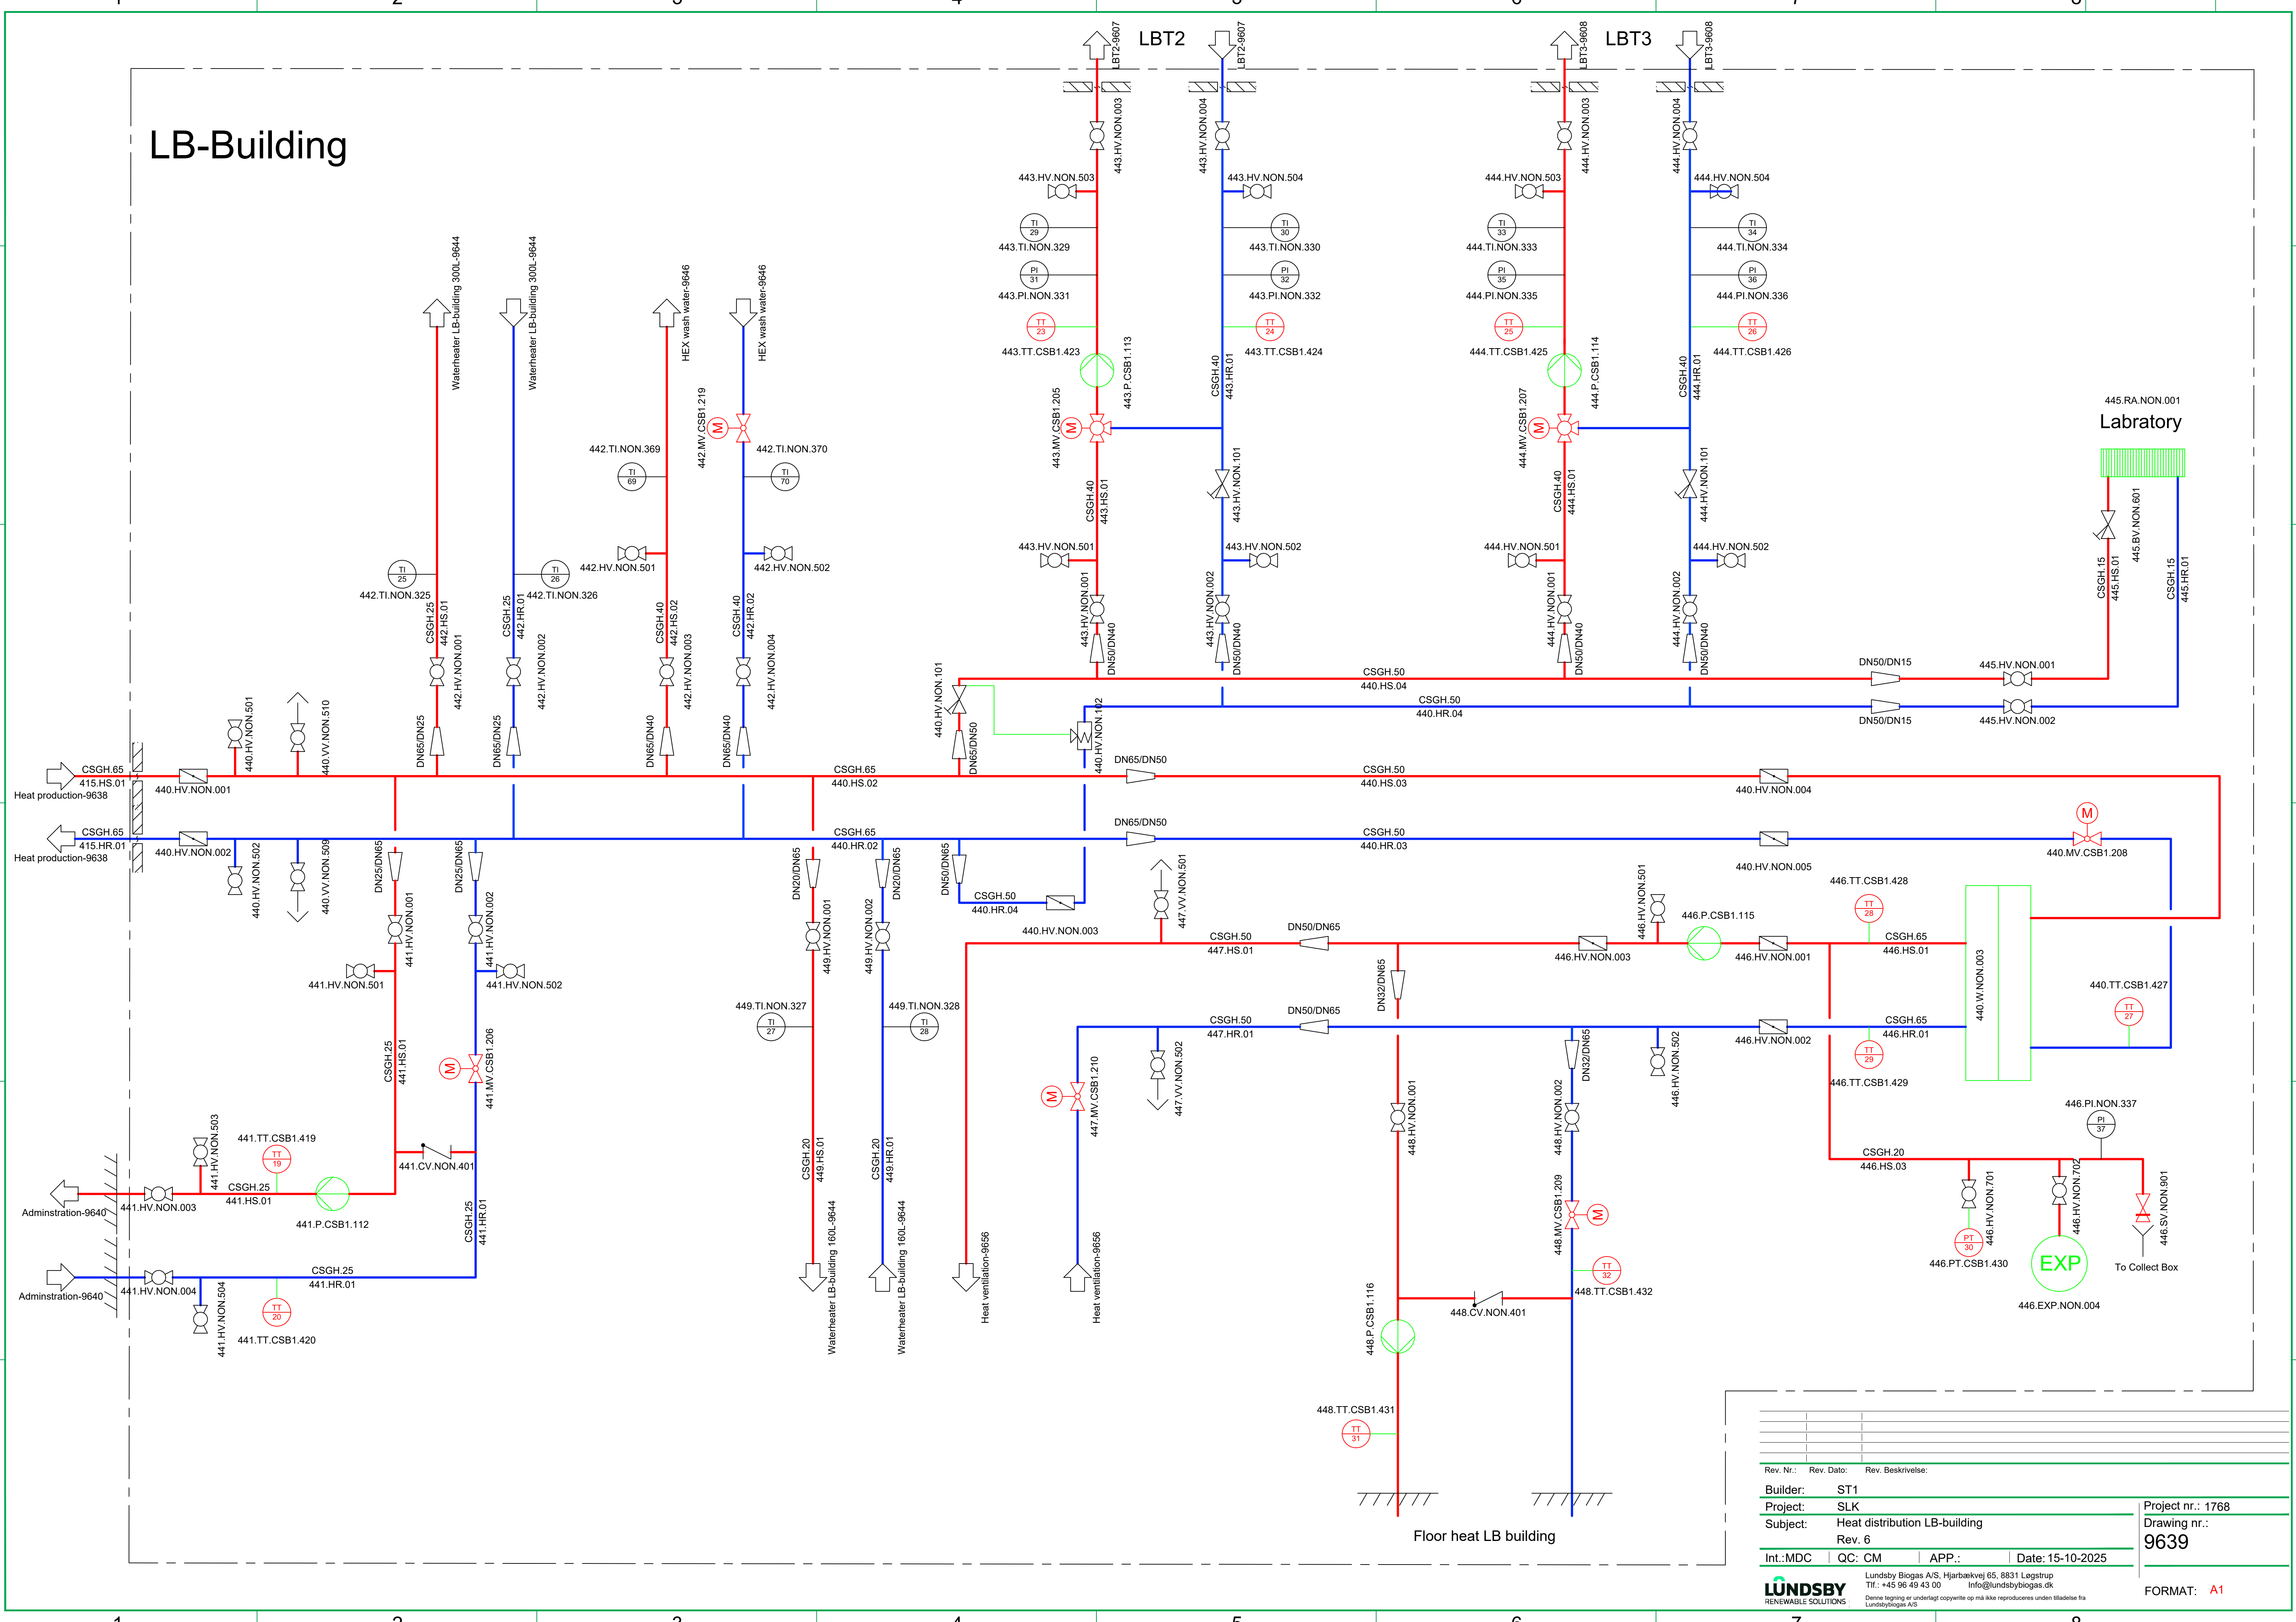


Rev. Nr.:	Rev. Dato:	Rev. Beskrivelse:
Builder:	ST1	
Project:	SLK	
Subject:	Heat distribution LB-building	
Rev. 6		
Int.:MDC	QC: CM	APP.: Date: 15-10-2025
LUNDSBY RENEWABLE SOLUTIONS		
Lundsby Biogas A/S, Hjarbækvej 65, 8831 Løgstrup Tlf.: +45 96 49 43 00 info@lundsbybiogas.dk		
Denne tegning er underlagt copyright og må ikke reproduceres uden tilladelse fra Lundsbybiogas A/S		
Project nr.: 1768 Drawing nr.: 9639		FORMAT: A1

SB-Building

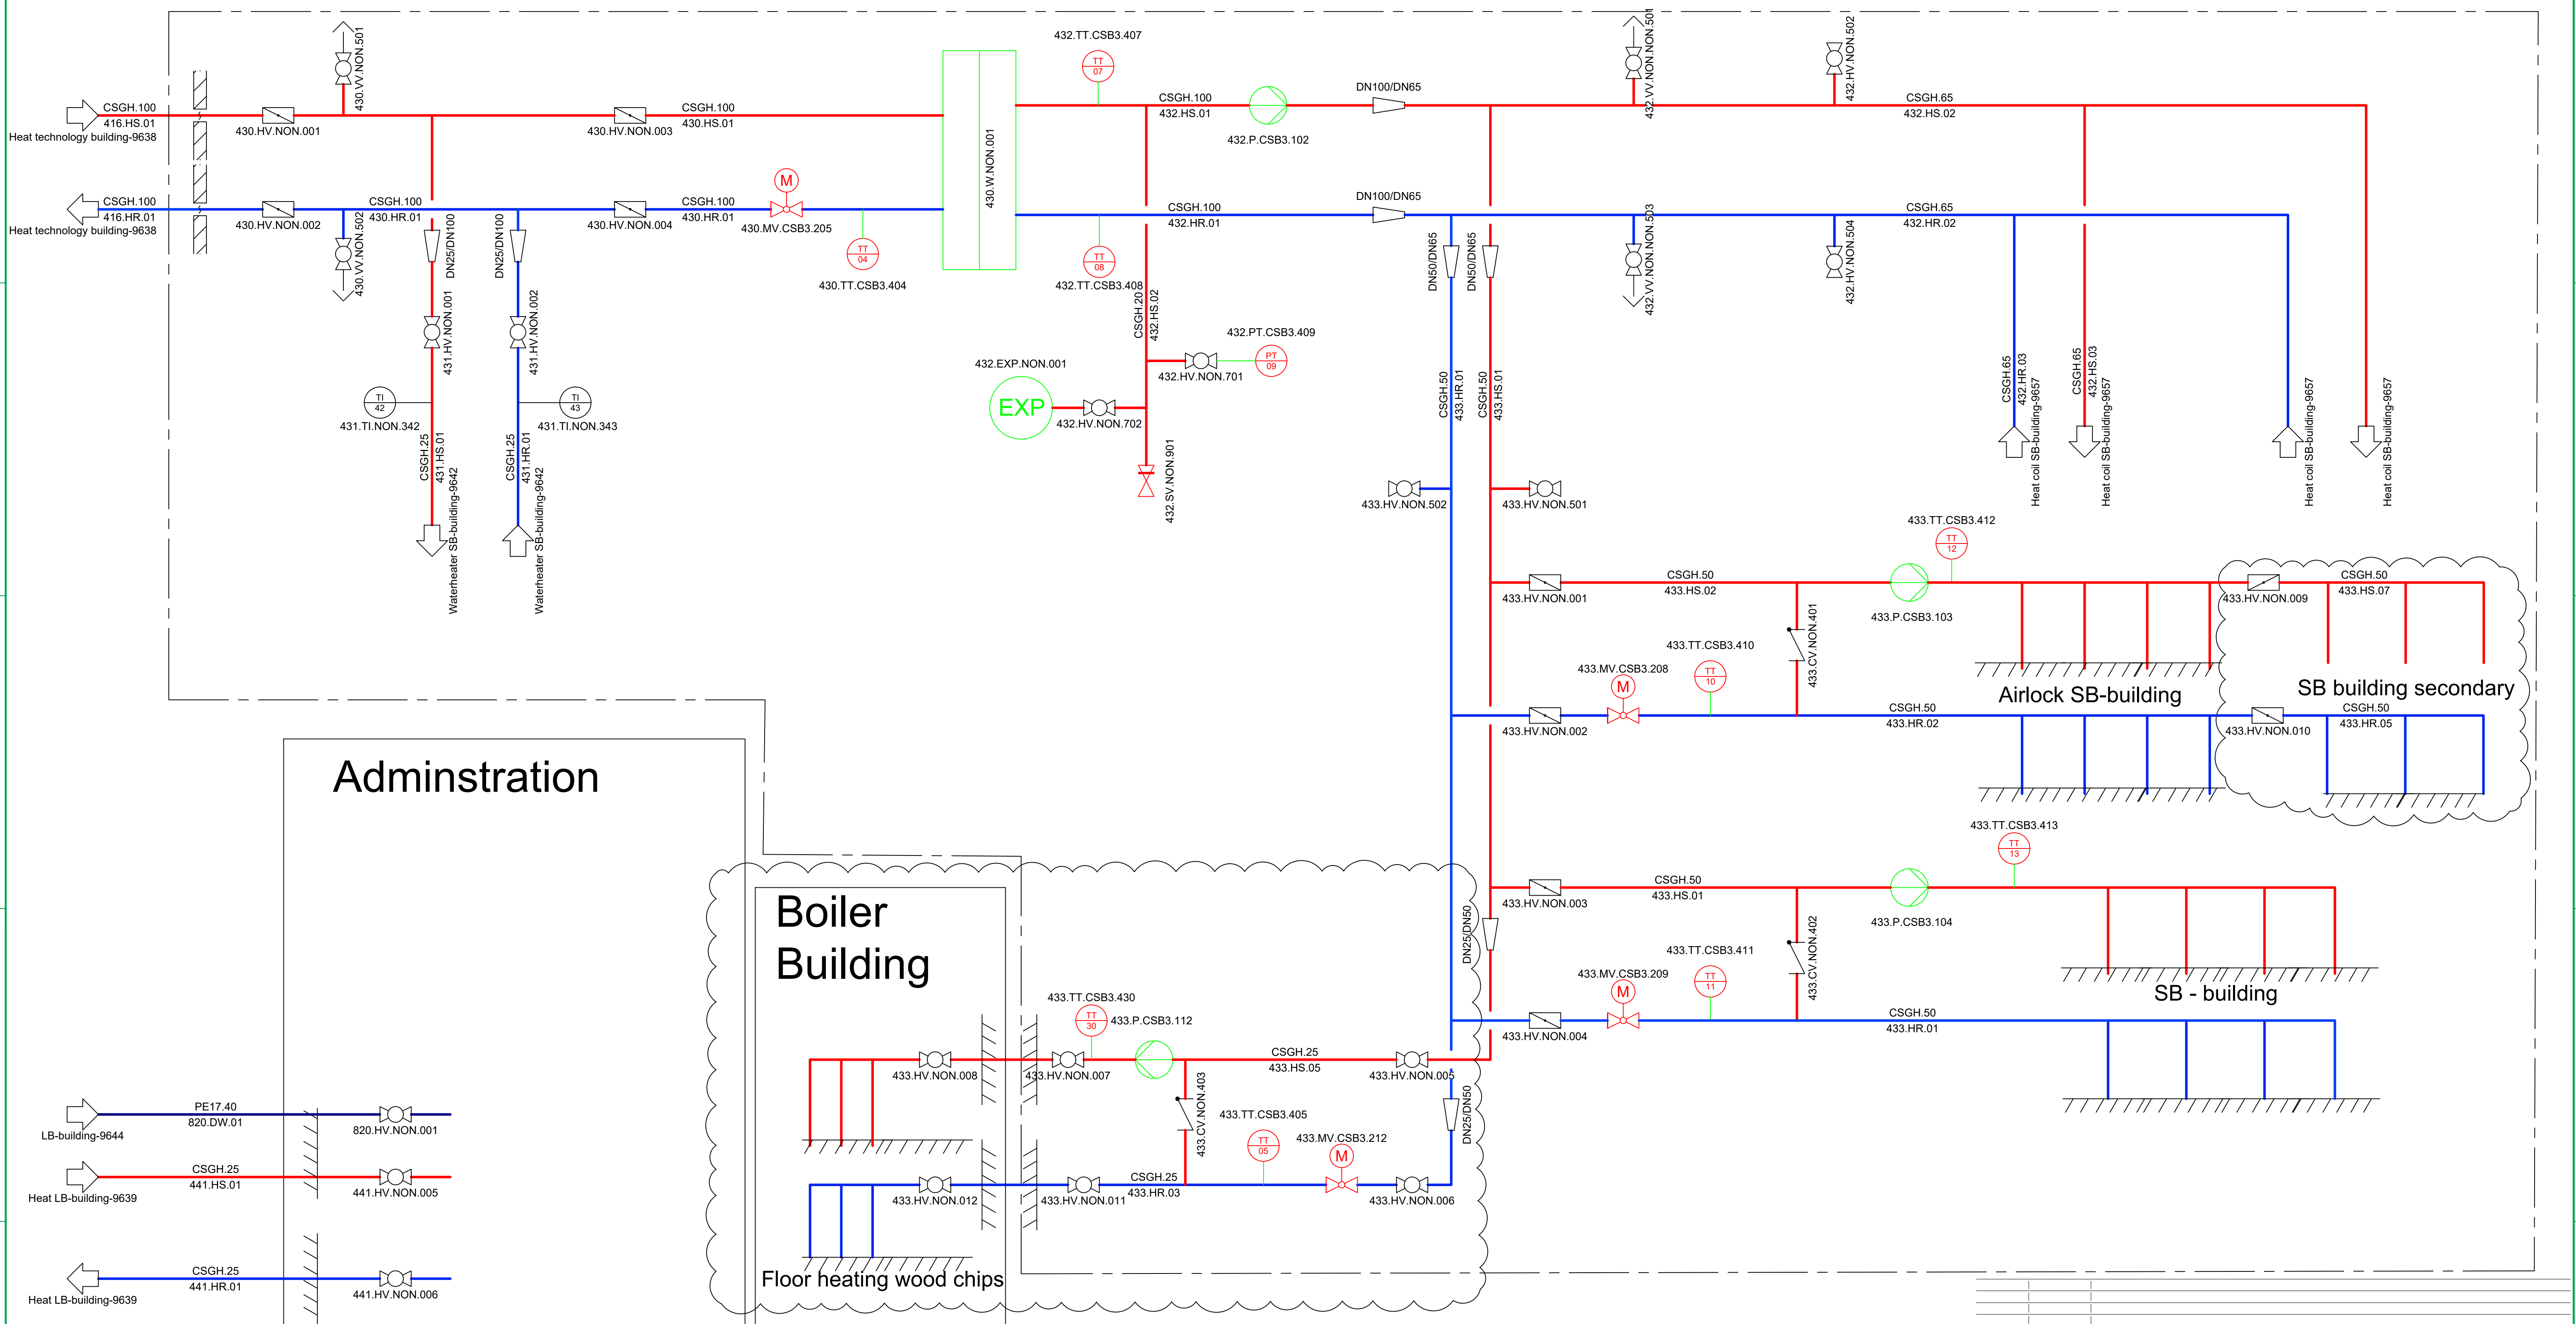


Rev. Nr.:	Rev. Dato:	Rev. Beskrivelse:	
Builder:	ST1		
Project:	SLK		
Subject:	Heat distribution SB-building		
	Rev. 6		
Int.:MDC	QC: CM	APP.:	Date: 15-10-2025
 Lundsby Biogas A/S, Hjarbækvej 65, 8831 Legstrup Tlf.: +45 96 49 43 00 Info@lundsbybiogas.dk Denne tegning er udelagt copyright og må ikke reproduceres uden tilladelse fra Lundsby Biogas A/S			Project nr.: 1768 Drawing nr.: 9640 FORMAT: A1

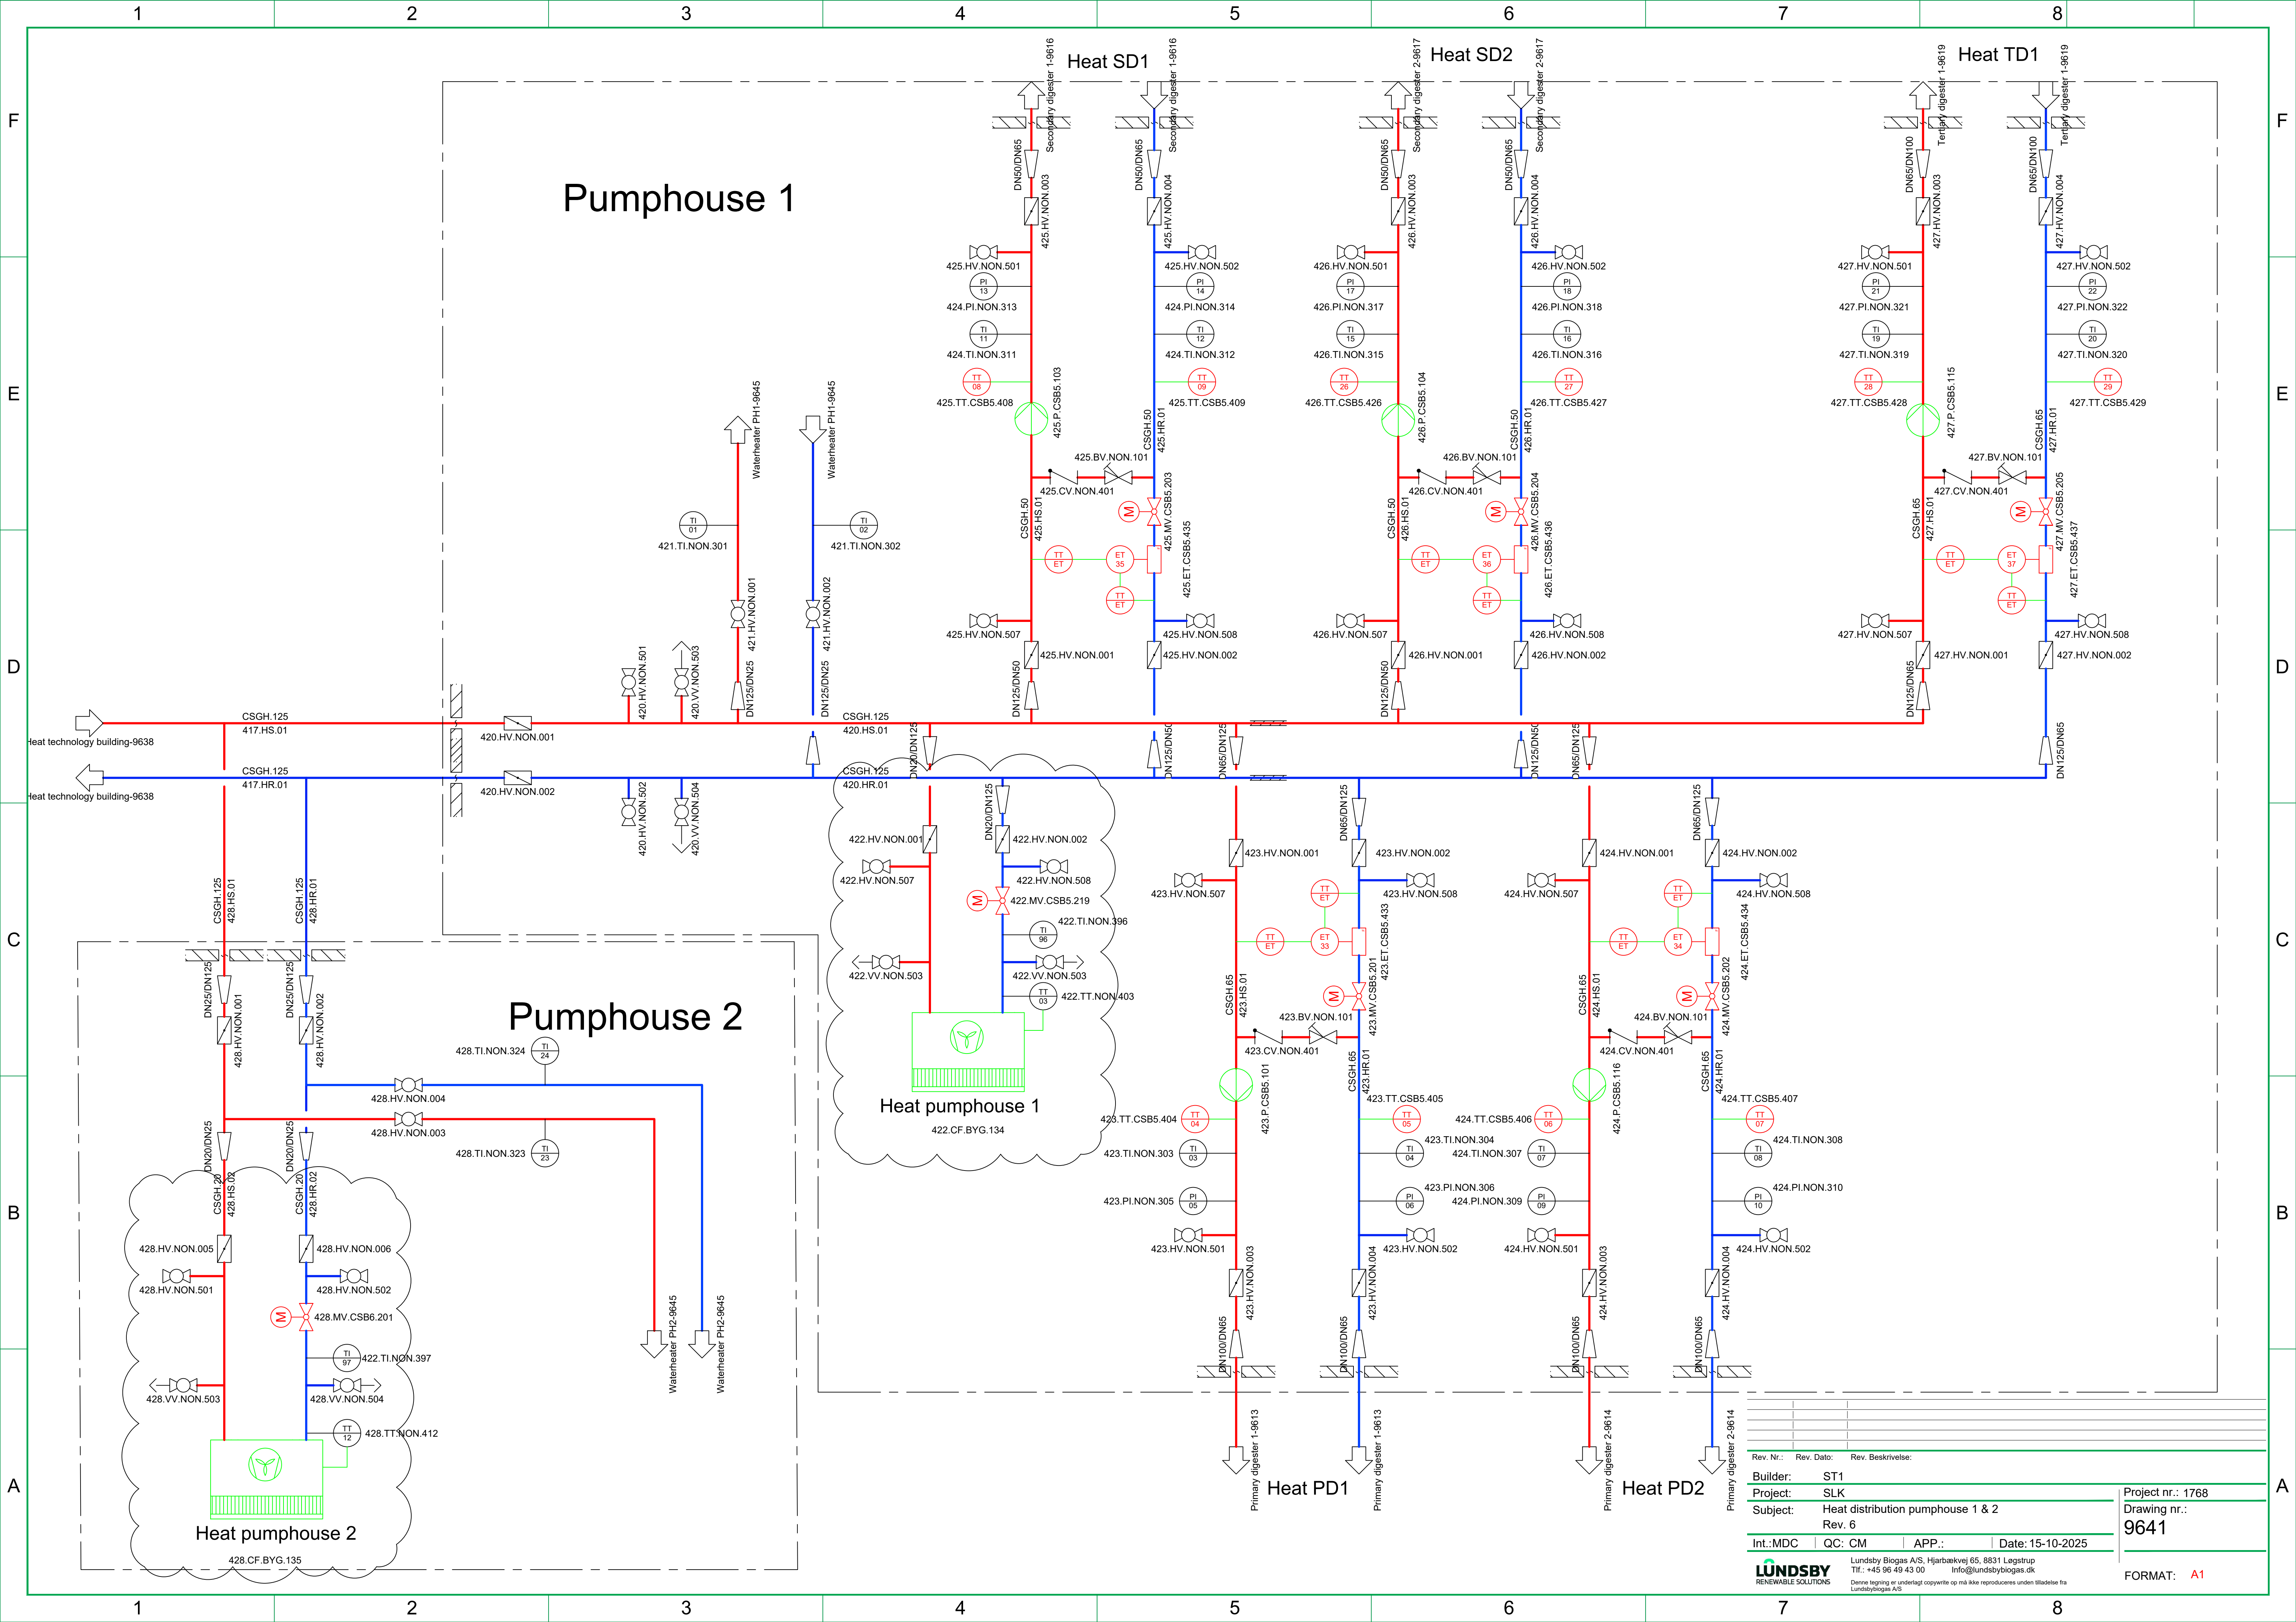


Rev. Nr.: Rev. Dato: Rev. Beskrivelse:					
Builder:		ST1			
Project:		SLK			
Subject:		Heat distribution pumphouse 1 & 2			
		Rev. 6			
Int.:MDC		QC: CM	APP.:	Date: 15-10-2025	
 LUNDSBY RENEWABLE SOLUTIONS Lundsby Biogas A/S, Hjarbækvej 65, 8831 Løgstrup Tlf.: +45 96 49 43 00 Info@lundsbybiogas.dk Denne tegning er underlagt copyright op på ikke reproduceres uden tilladelse fra Lundsbybiogas A/S					
				Project nr.: 1768	
				Drawing nr.: 9641	
				FORMAT: A1	

SB-Building

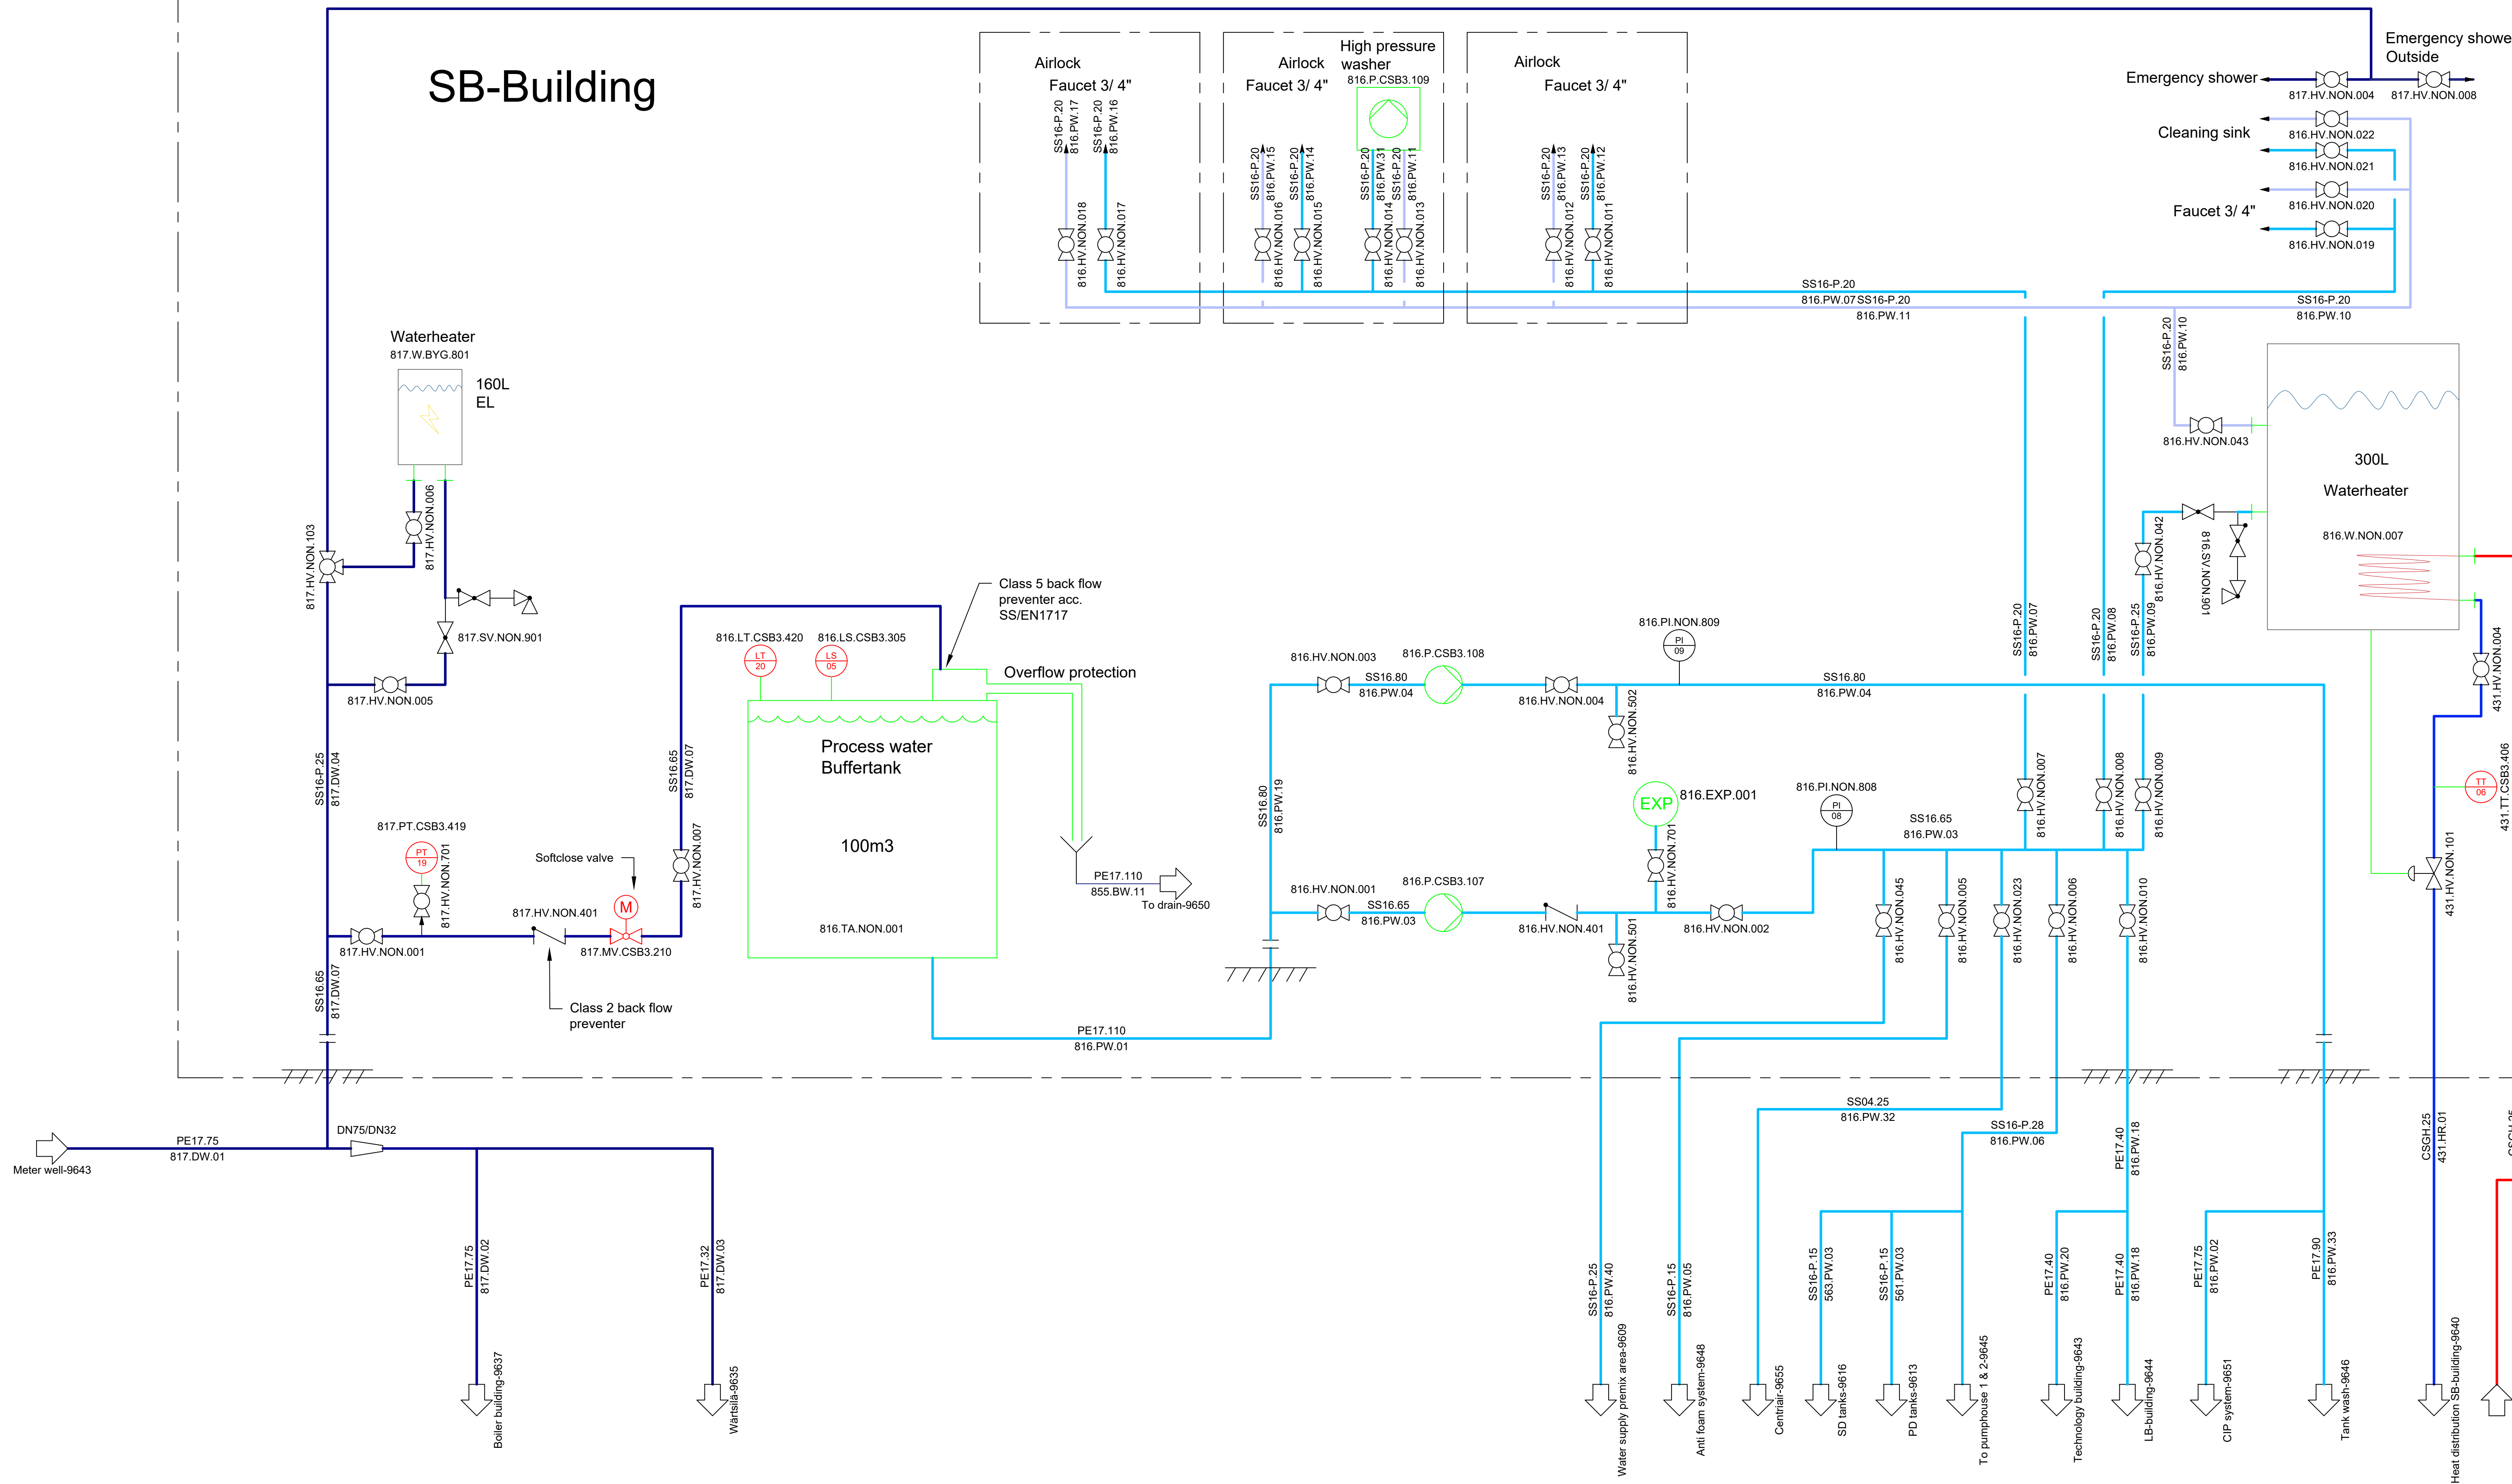


Rev. Nr.:	Rev. Dato:	Rev. Beskrivelse:
Builder:	ST1	
Project:	SLK	
Subject:	Water distribution SB-building	
Rev. 6		
Int.:MDC	QC:CM	APP.:
		Date: 15-10-2025
LUNDSBY RENEWABLE SOLUTIONS		
Lundsby Biogas A/S, Hjarbækvej 65, 8831 Løgstrup Tlf.: +45 96 49 43 00 info@lundsbybiogas.dk		
Denne tegning er underlagt copyright op på ikke reproduceres uden tilladelse fra Lundsbybiogas A/S		
Project nr.: 1768 Drawing nr.: 9642		FORMAT: A1


Technology building

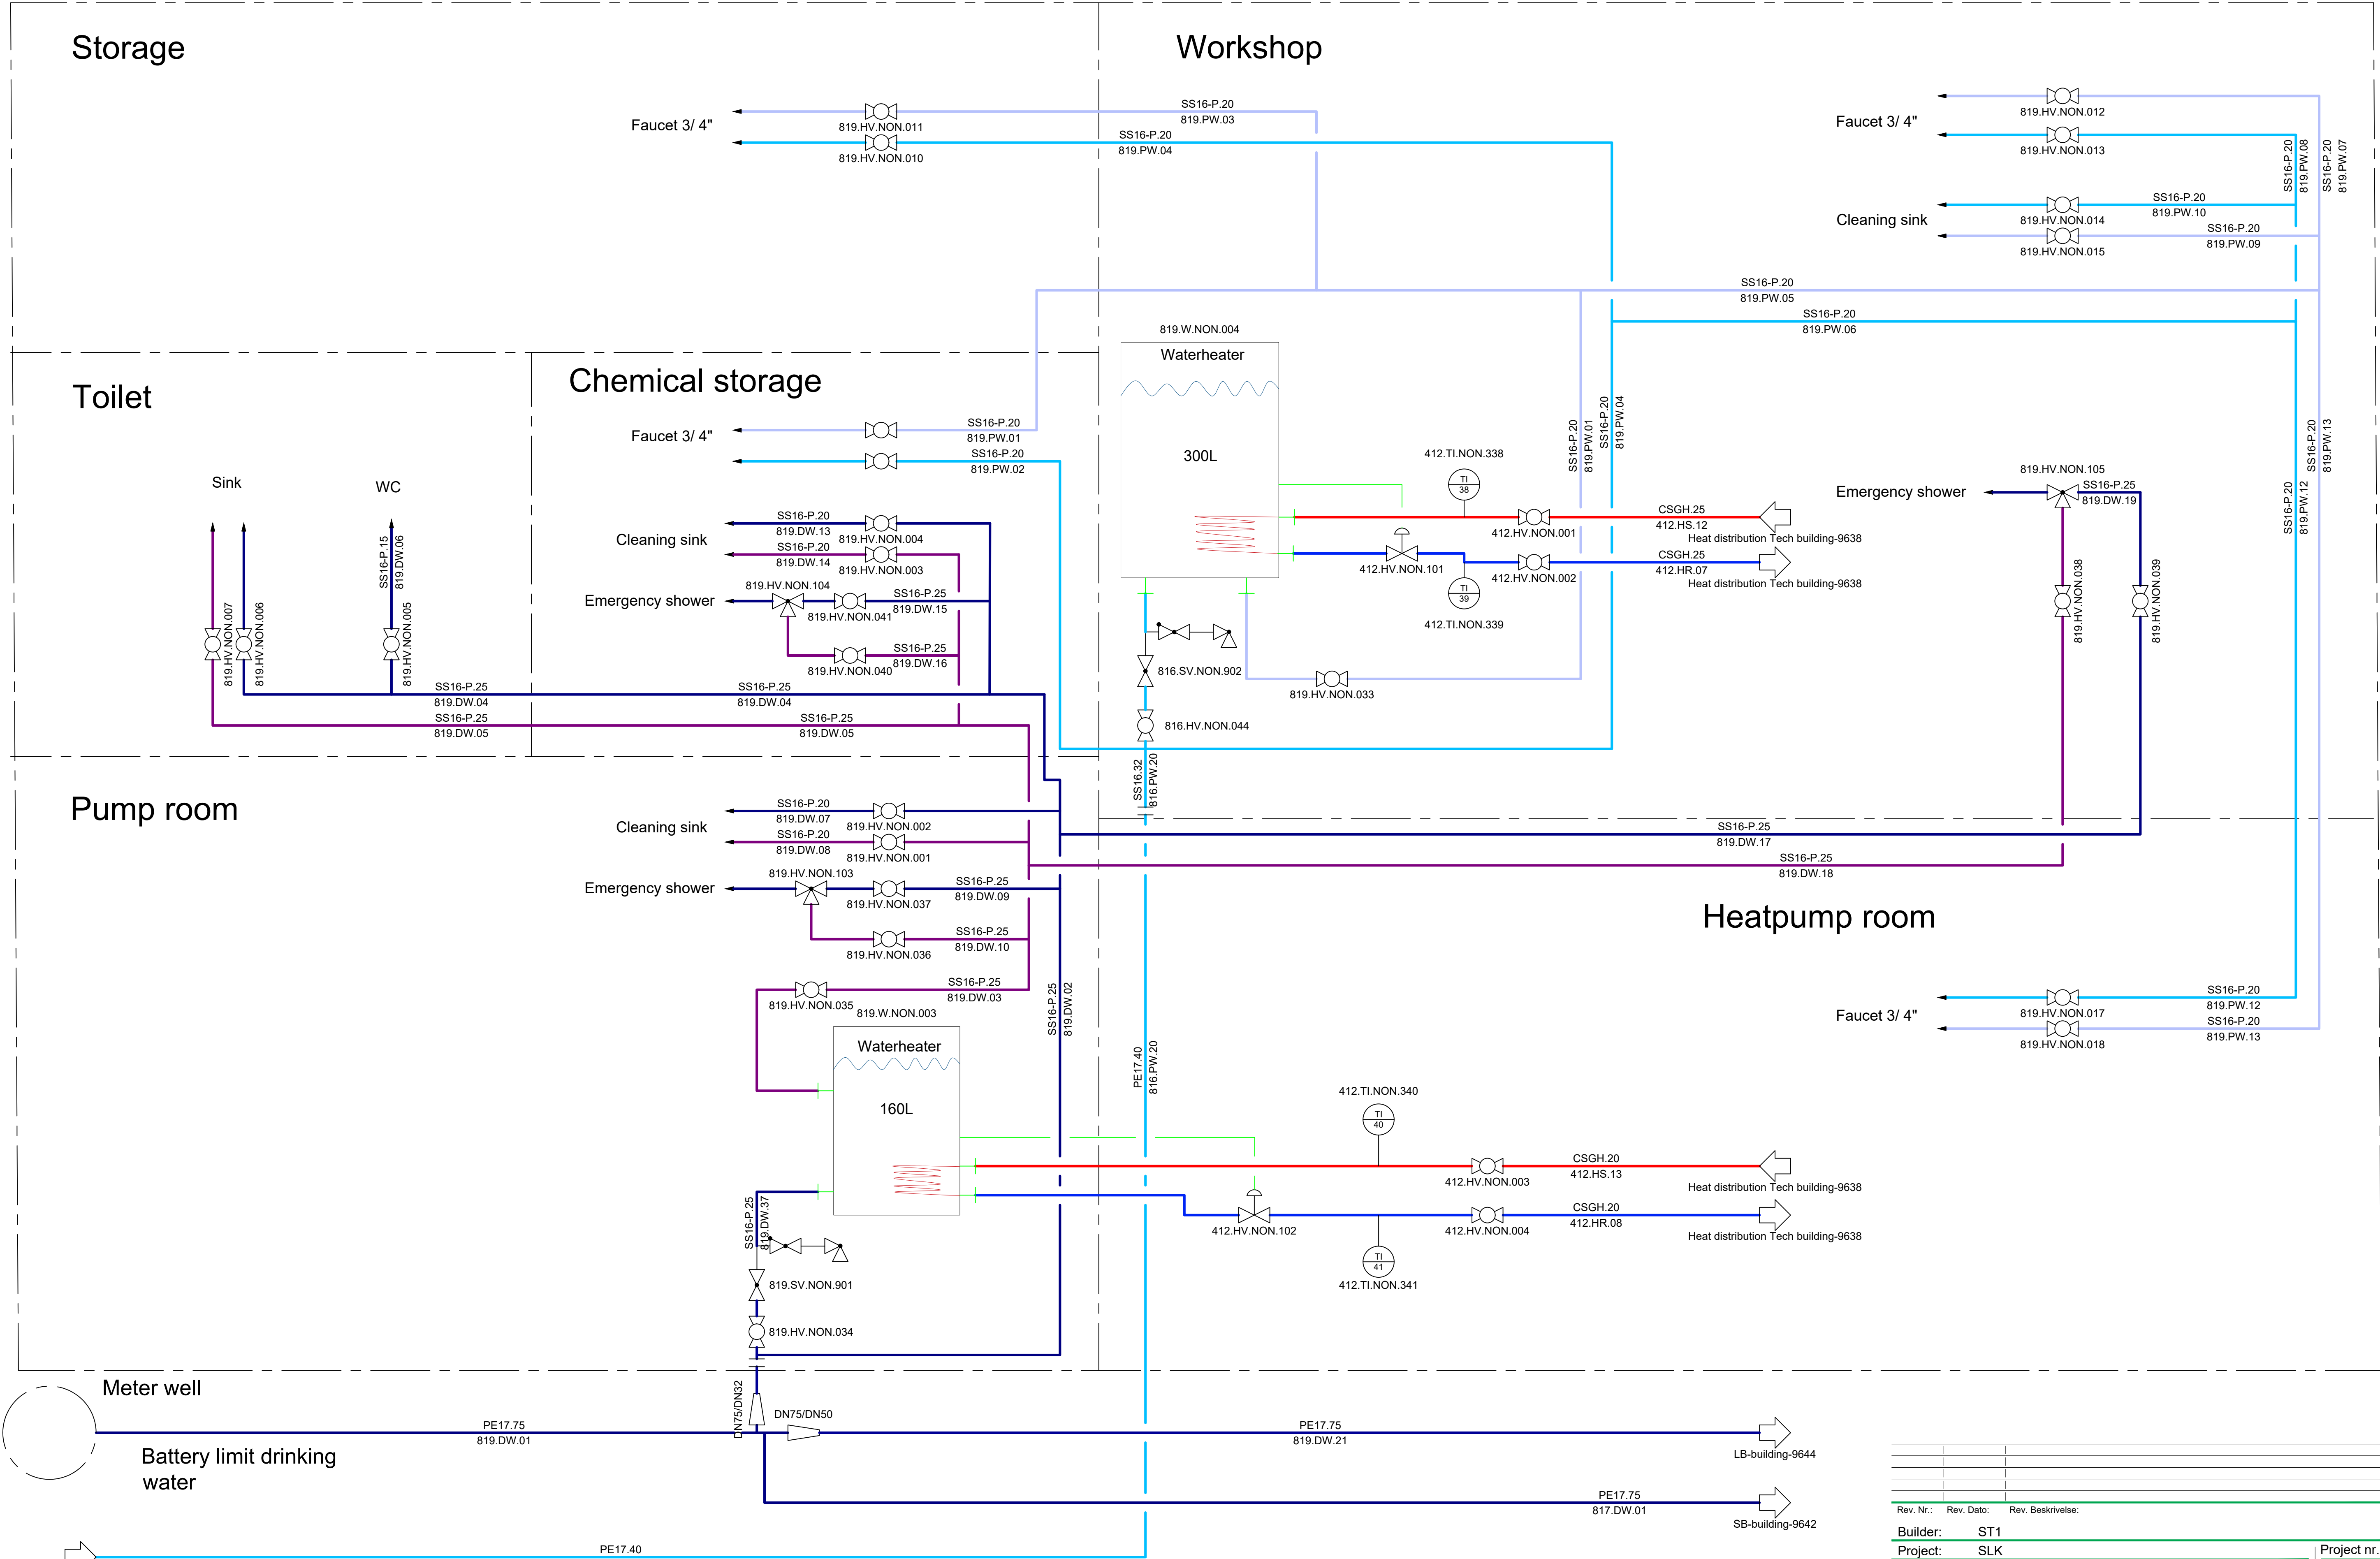

Rev. Nr.:	Rev. Dato:	Rev. Beskrivelse:
Builder:	ST1	
Project:	SLK	
Subject:	Water distribution Tech building	
Rev. 6		
Int.:MDC	QC:CM	APP.:
		Date: 15-10-2025
LUNDSBY RENEWABLE SOLUTIONS		
Lundsby Biogas A/S, Hjarbækvej 65, 8831 Løgstrup Tlf.: +45 96 49 43 00 info@lundsbybiogas.dk		
Denne tegning er underlagt copyright og må ikke reproduceres uden tilladelse fra Lundsbybiogas A/S		
Project nr.: 1768 Drawing nr.: 9643		FORMAT: A1

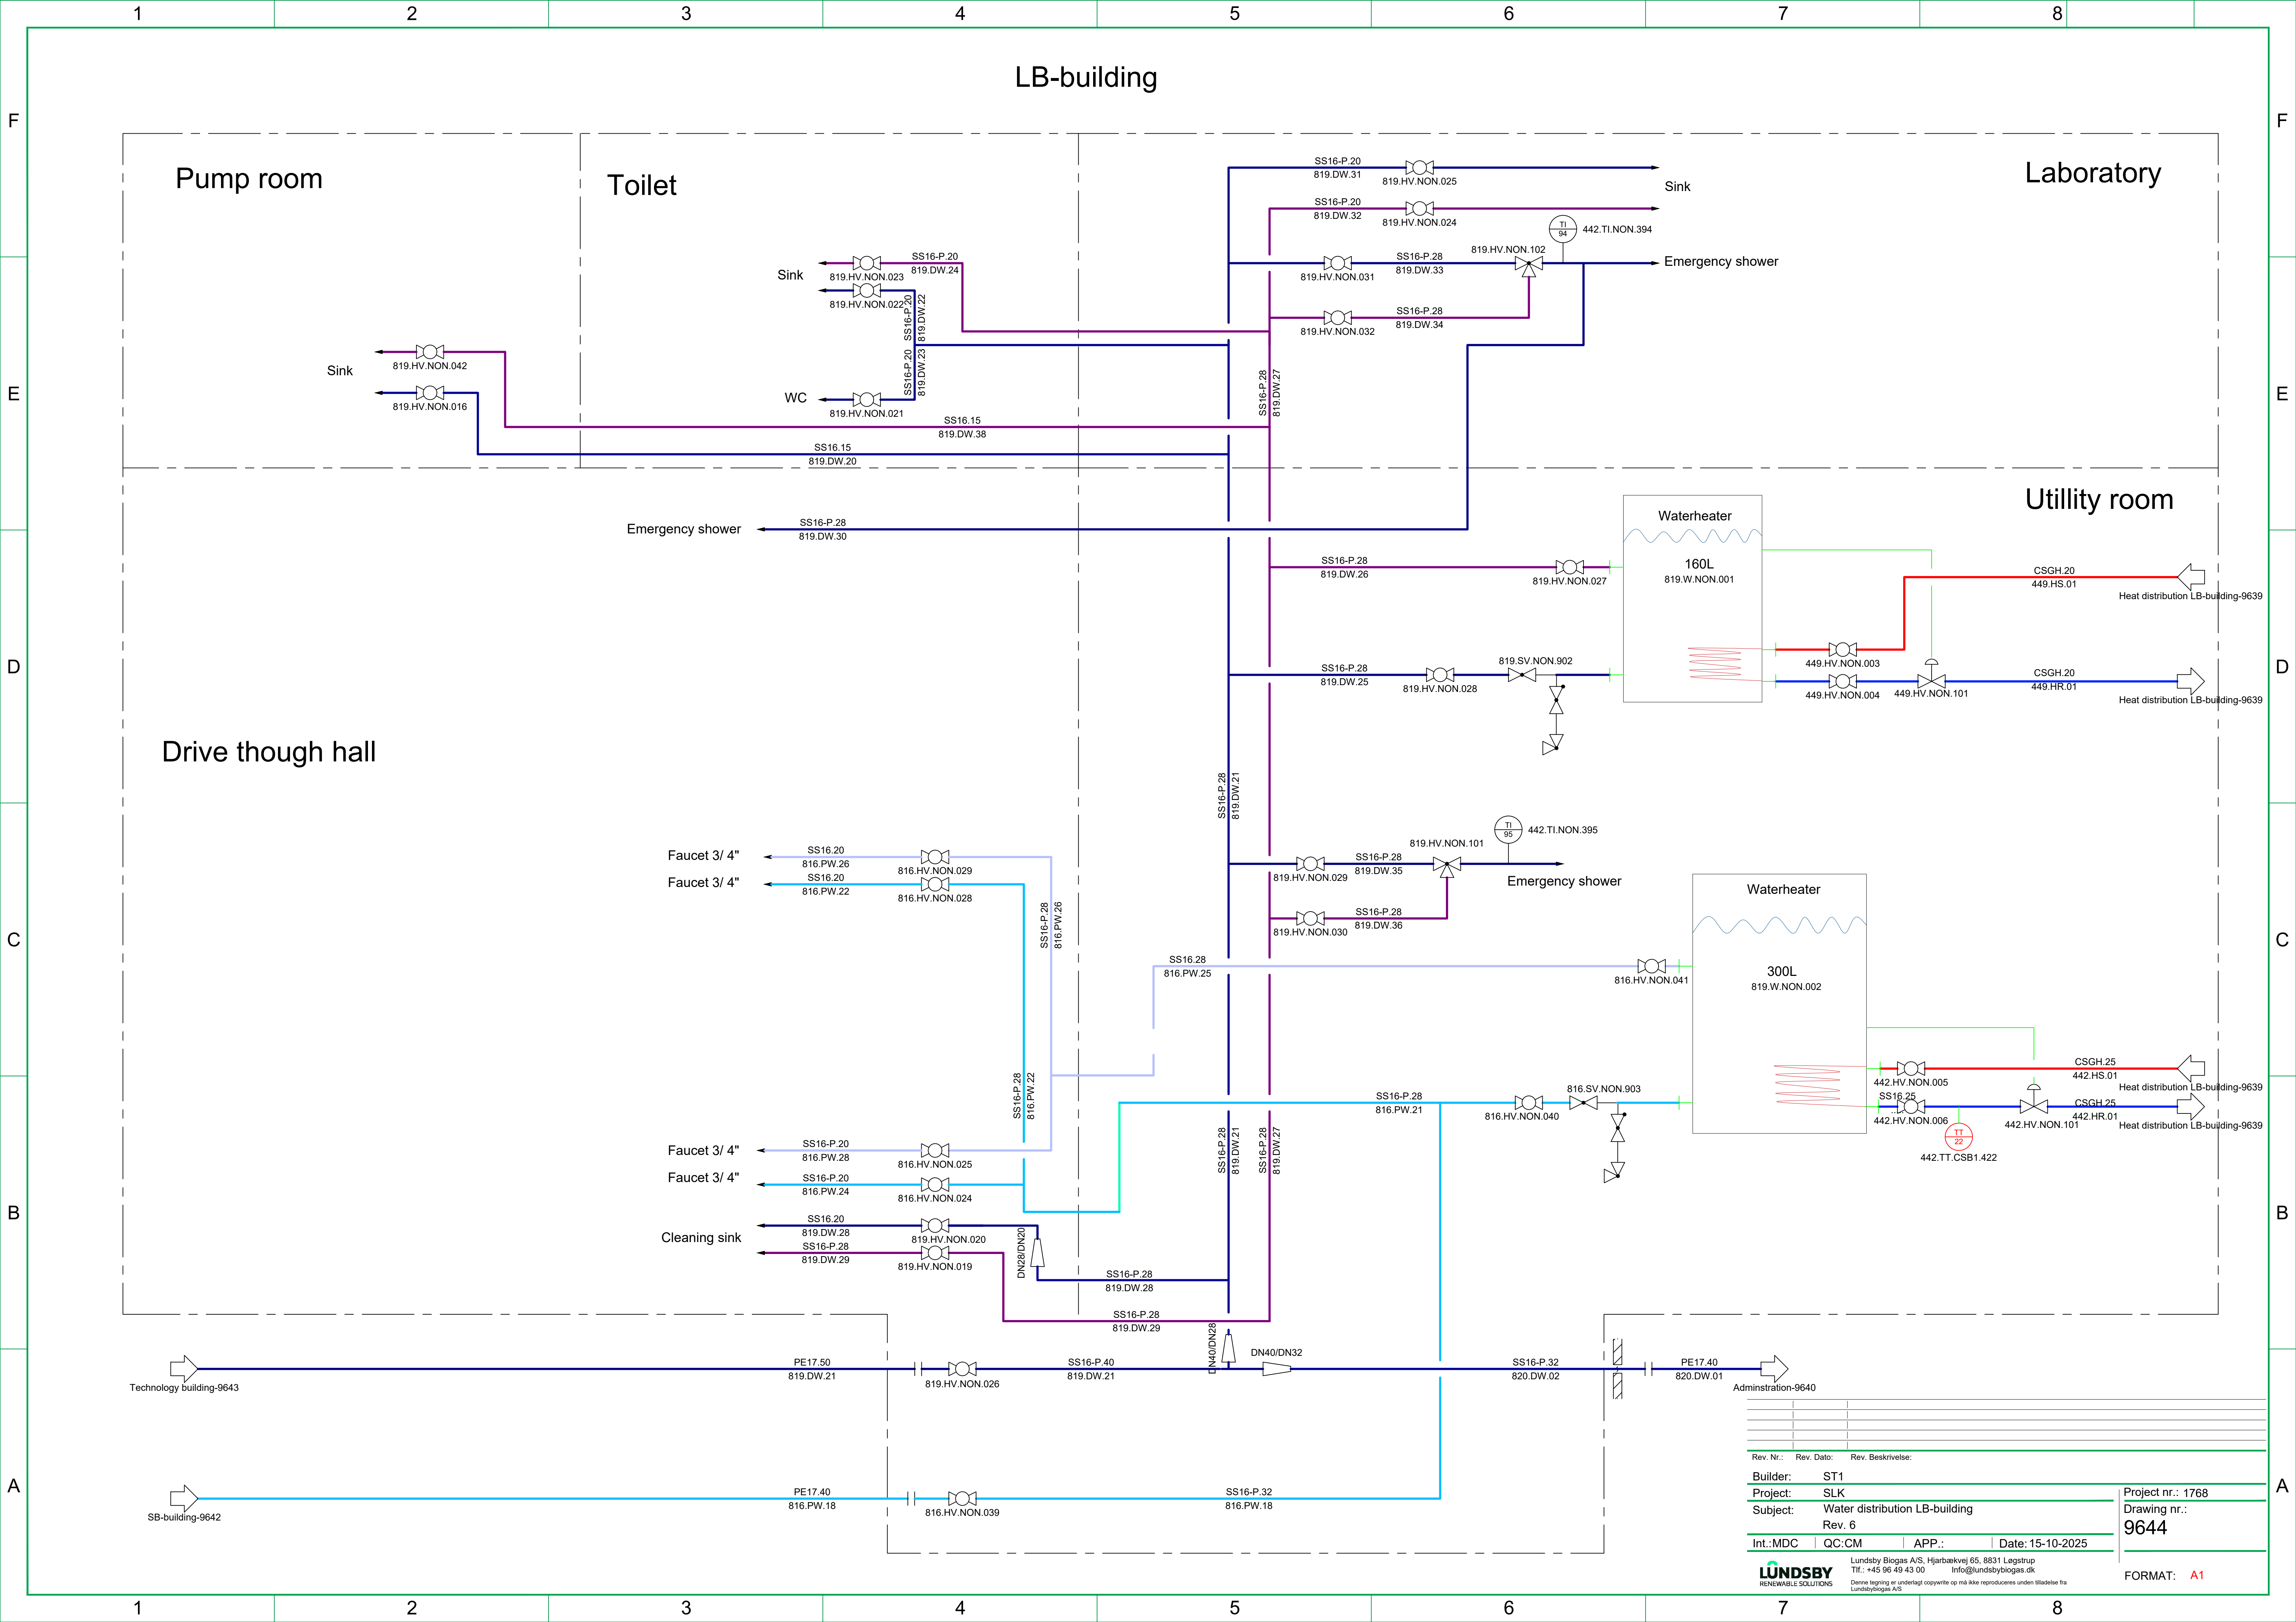

Pumphouse 1

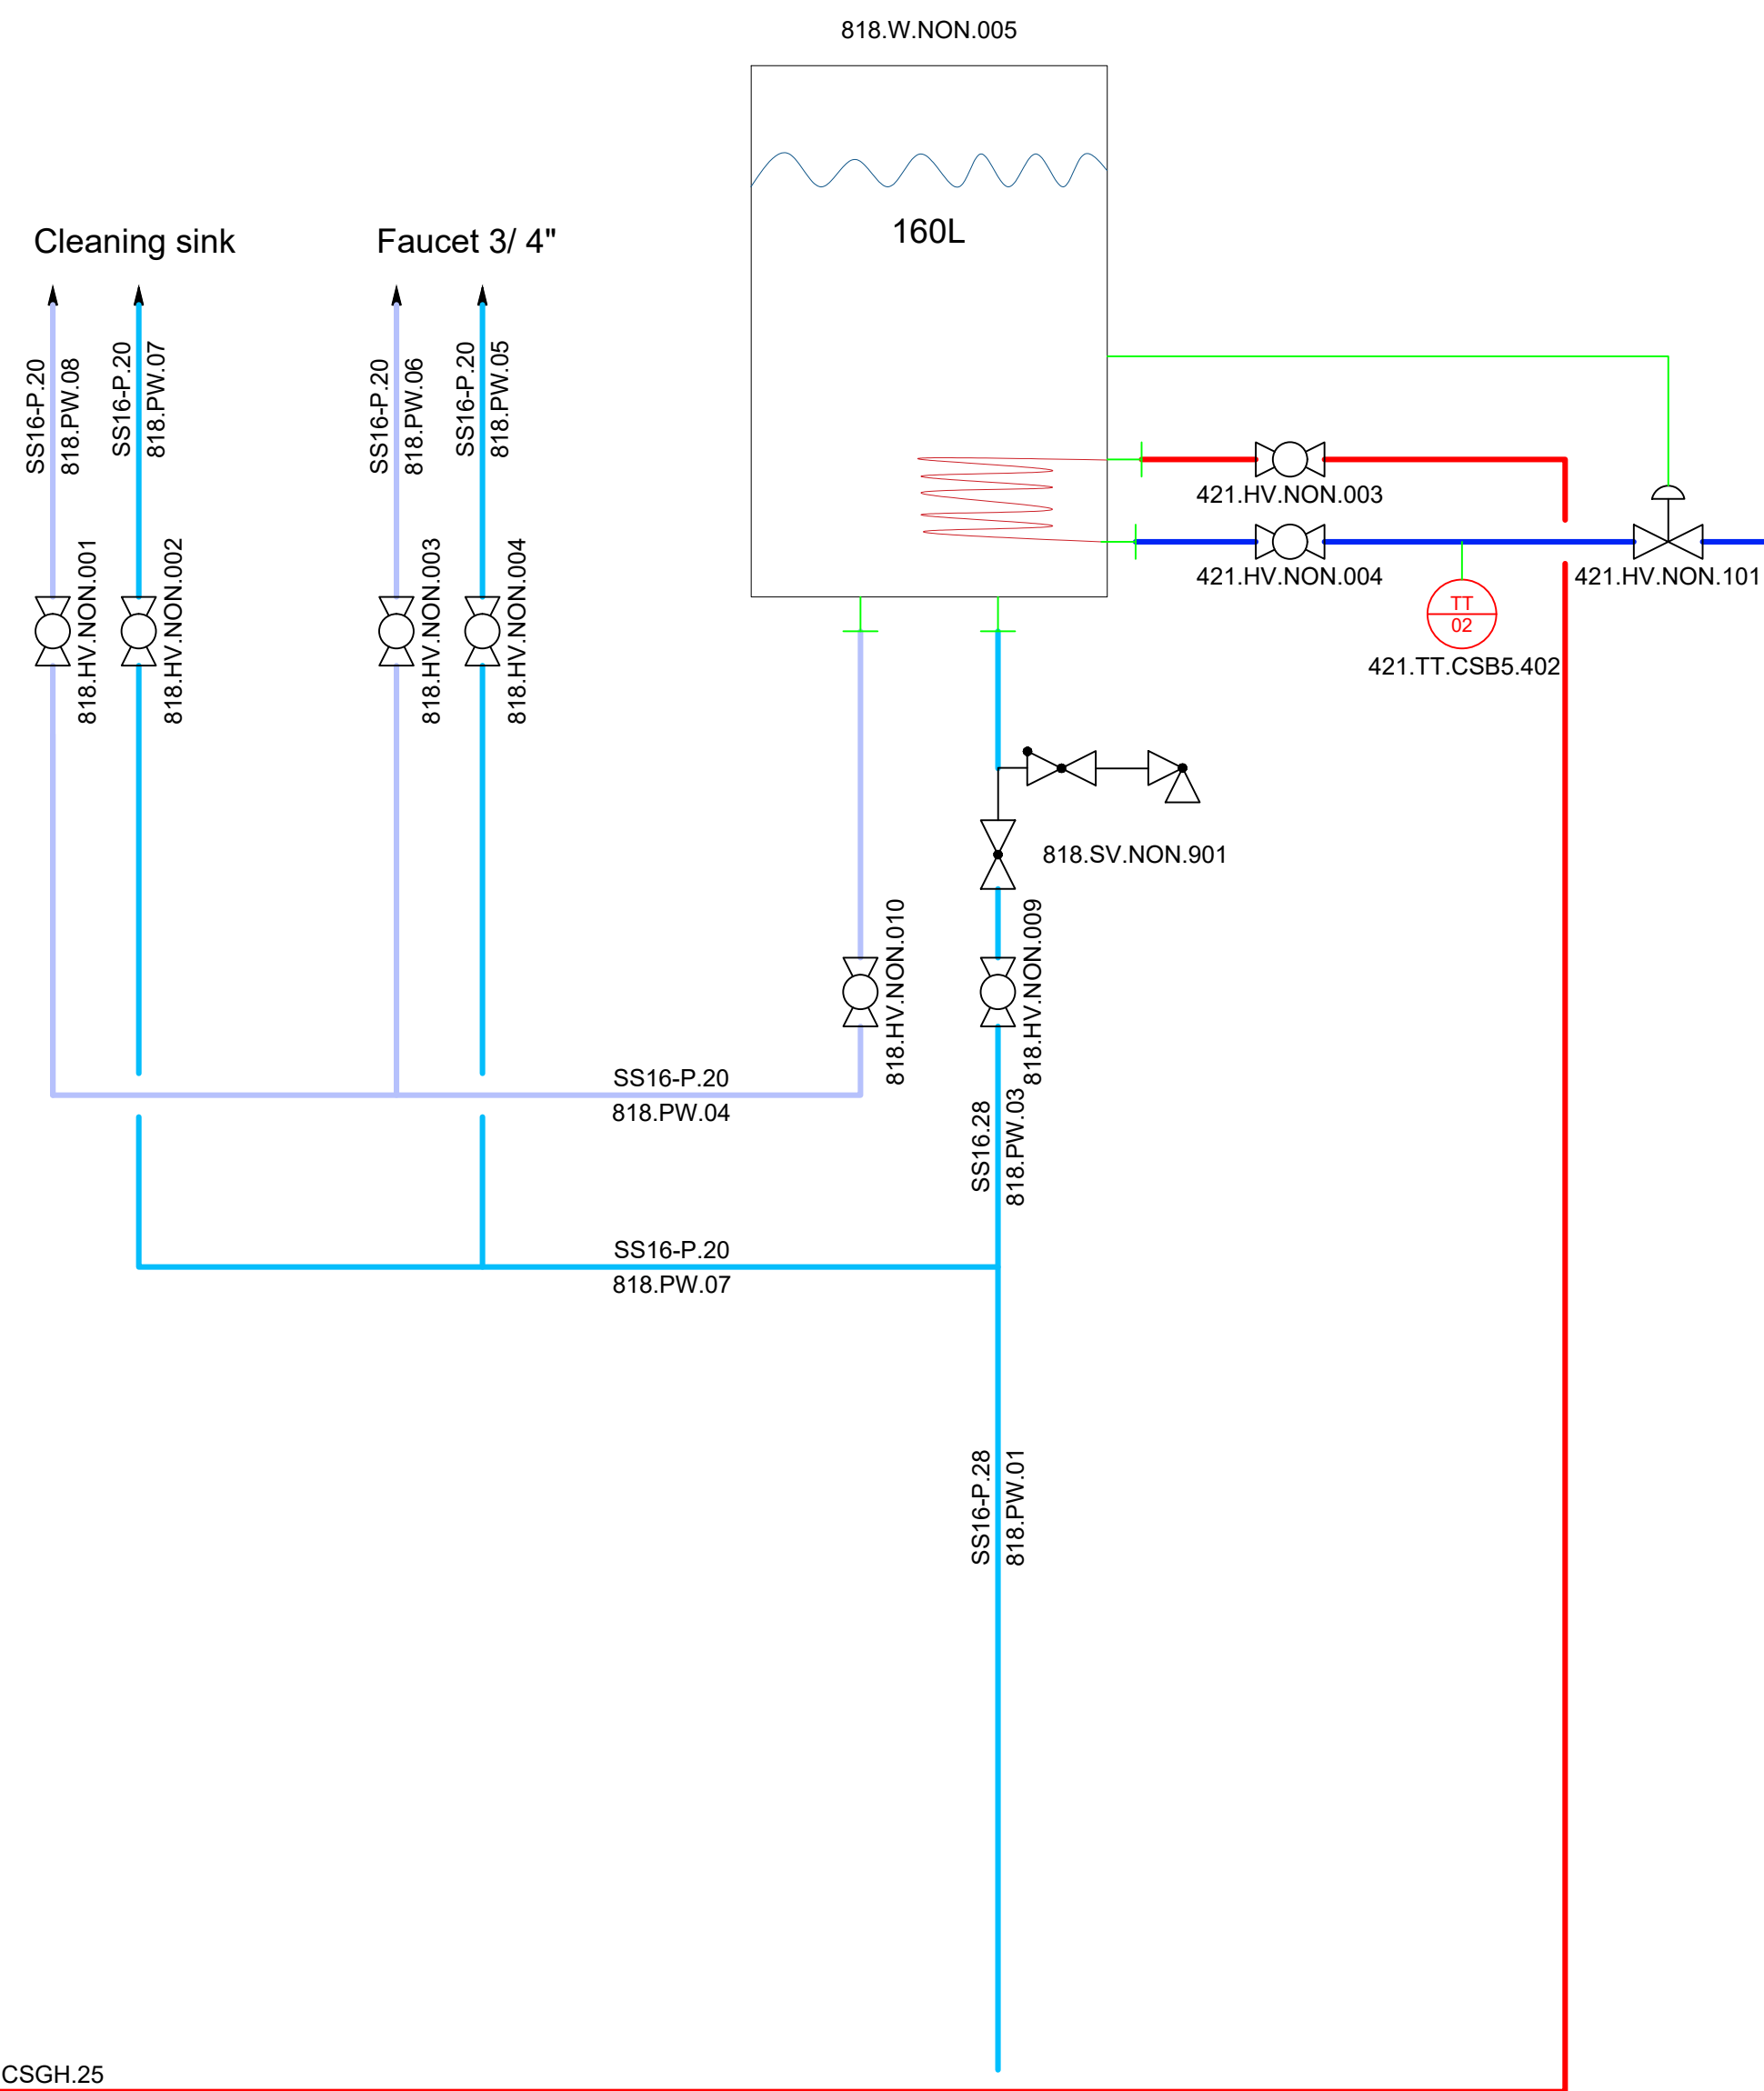


Heat distribution PH1-9641
CSGH.25
421.HS.01

Heat distribution PH1-9641
CSGH.25
421.HR.01

SB-building-9642
SS16-P.28
816.PW.06

Pumphouse 2

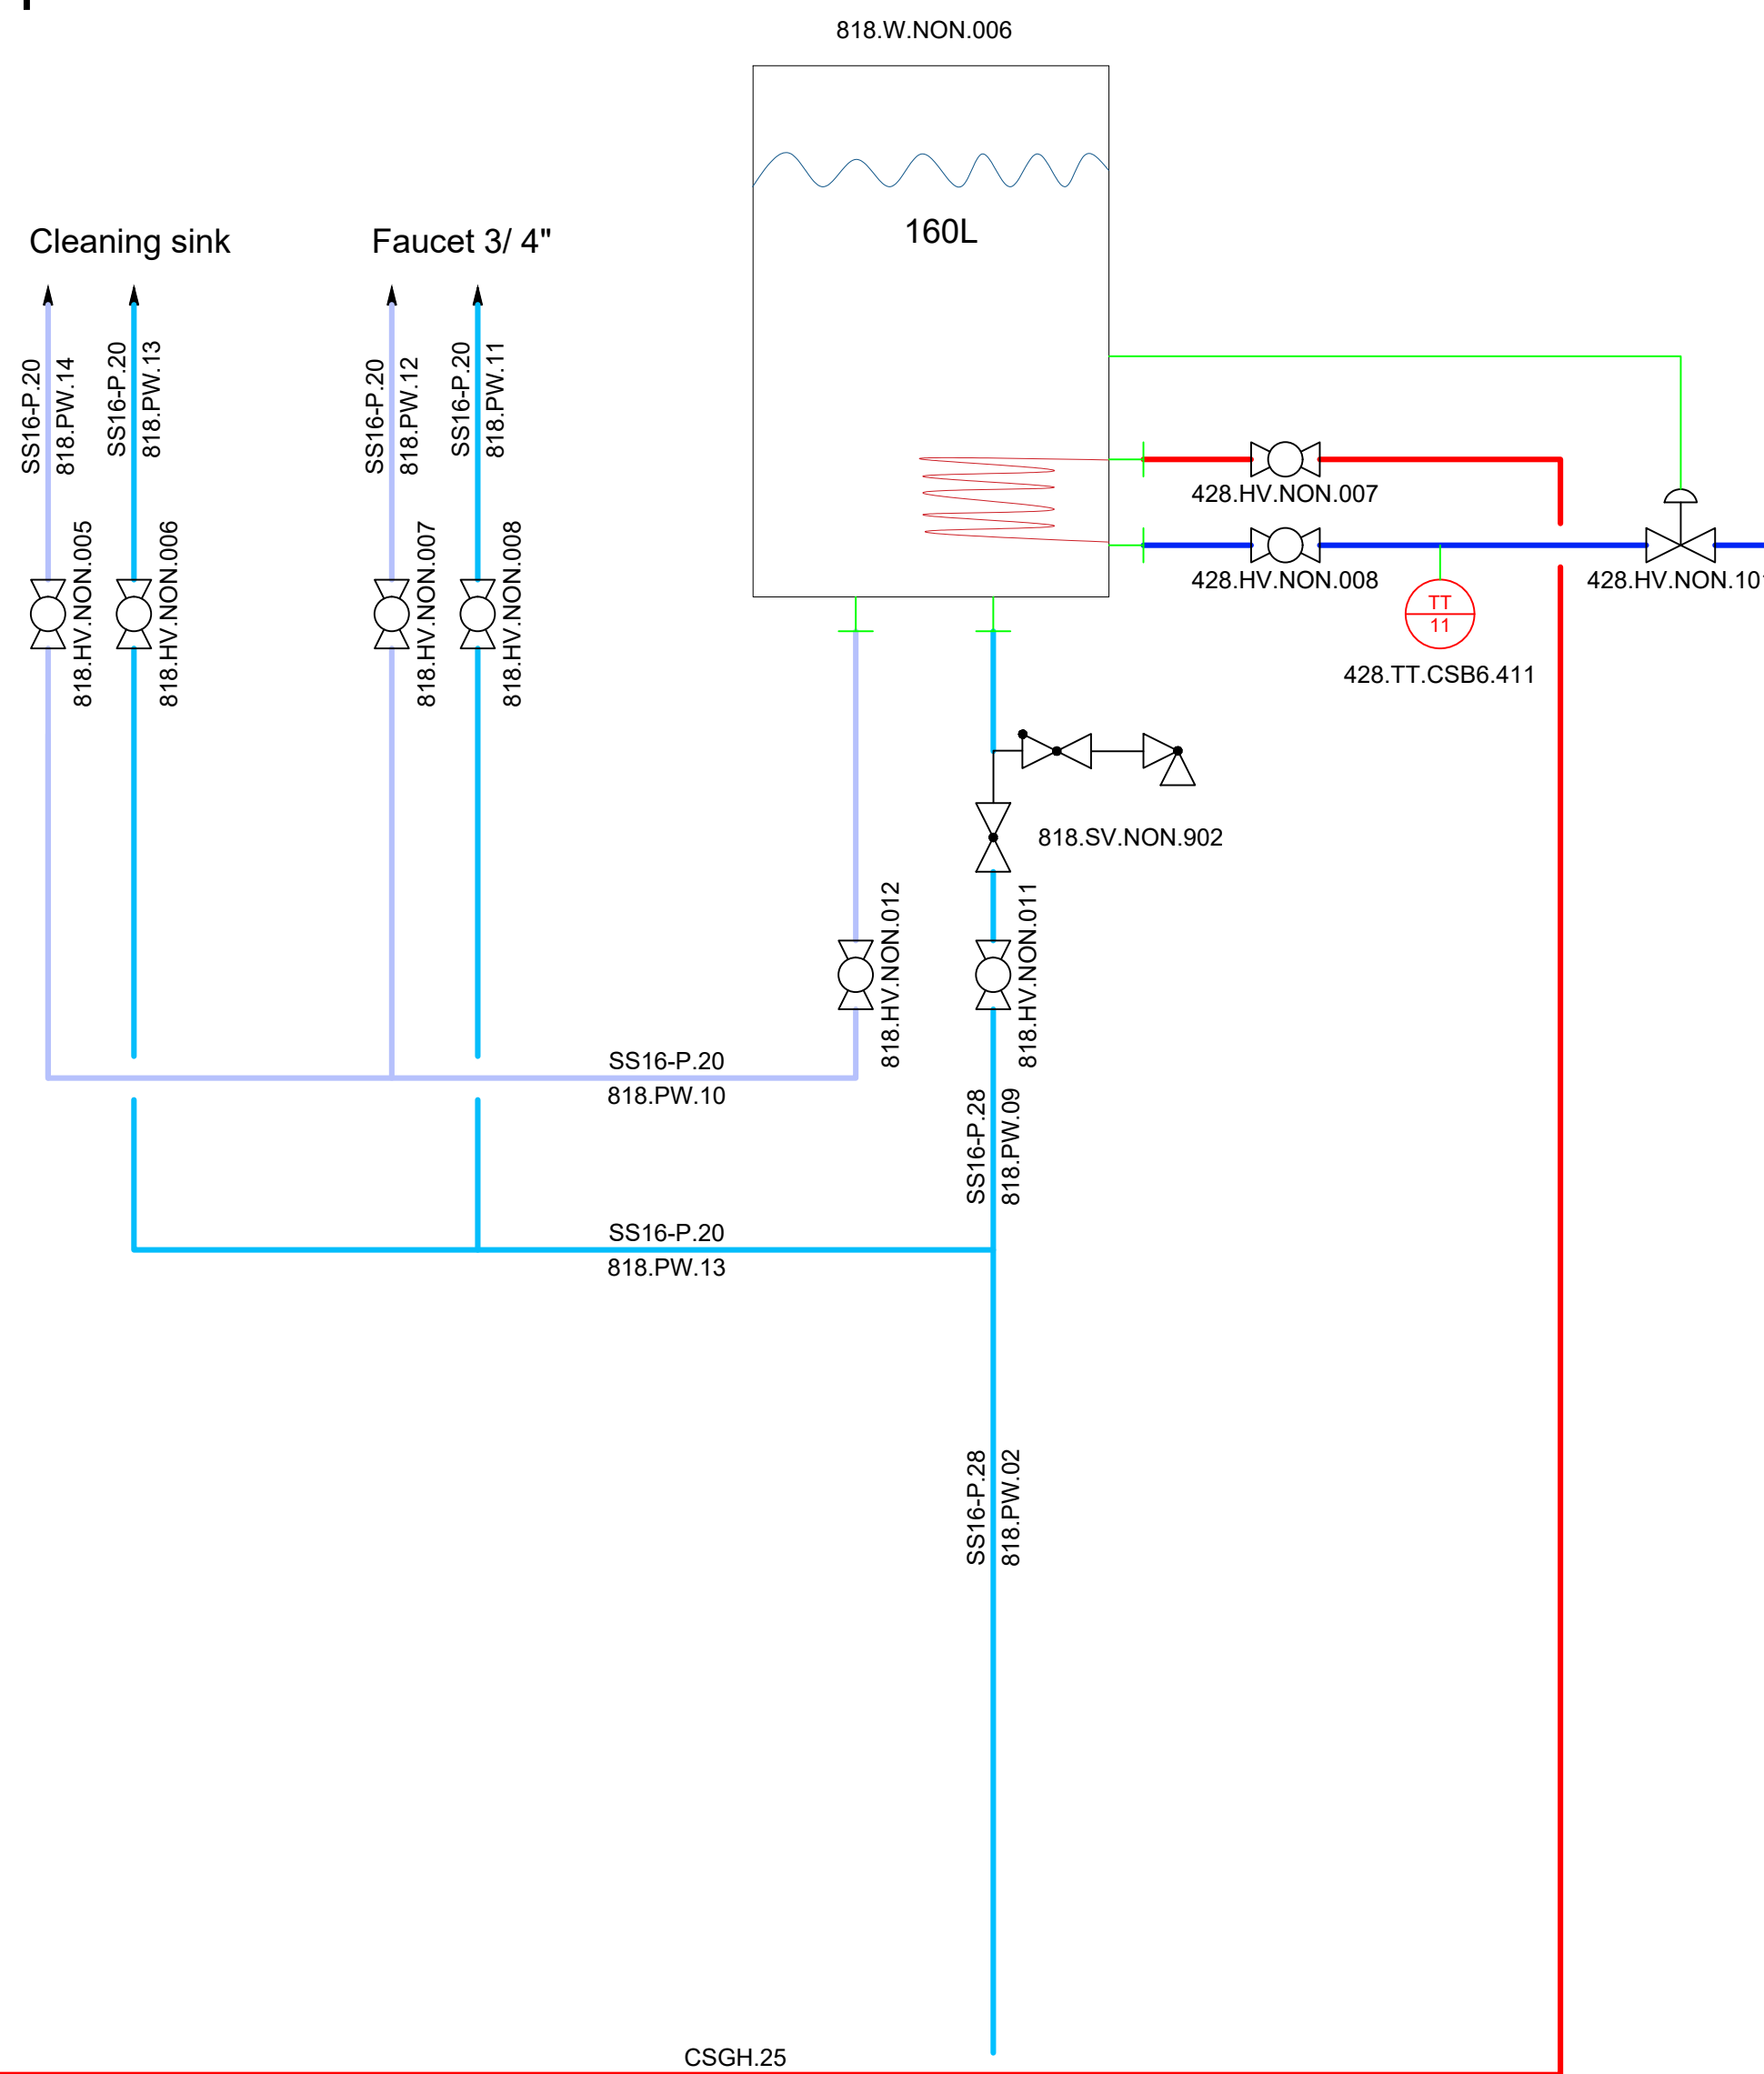

Heat distribution PH2-9641
CSGH.25
428.HS.01


Heat distribution PH2-9641
CSGH.25
428.HR.01

SS16-P.28
816.PW.06


Rev. Nr.:	Rev. Dato:	Rev. Beskrivelse:
Builder:	ST1	
Project:	SLK	
Subject:	Water distribution pumphouse 1 & 2	
Int.:MDC	QC:CM	APP.:
Date:	15-10-2025	
Project nr.:	1768	
Drawing nr.:	9645	
FORMAT:	A1	

LUNDSBY
RENEWABLE SOLUTIONS

Lundsby Biogas A/S, Hjarbækvej 65, 8831 Løgstrup
Tlf.: +45 96 49 43 00
info@lundsbybiogas.dk
Denne tegning er underlagt copyright og må ikke reproduceres uden tilladelse fra Lundsbybiogas A/S

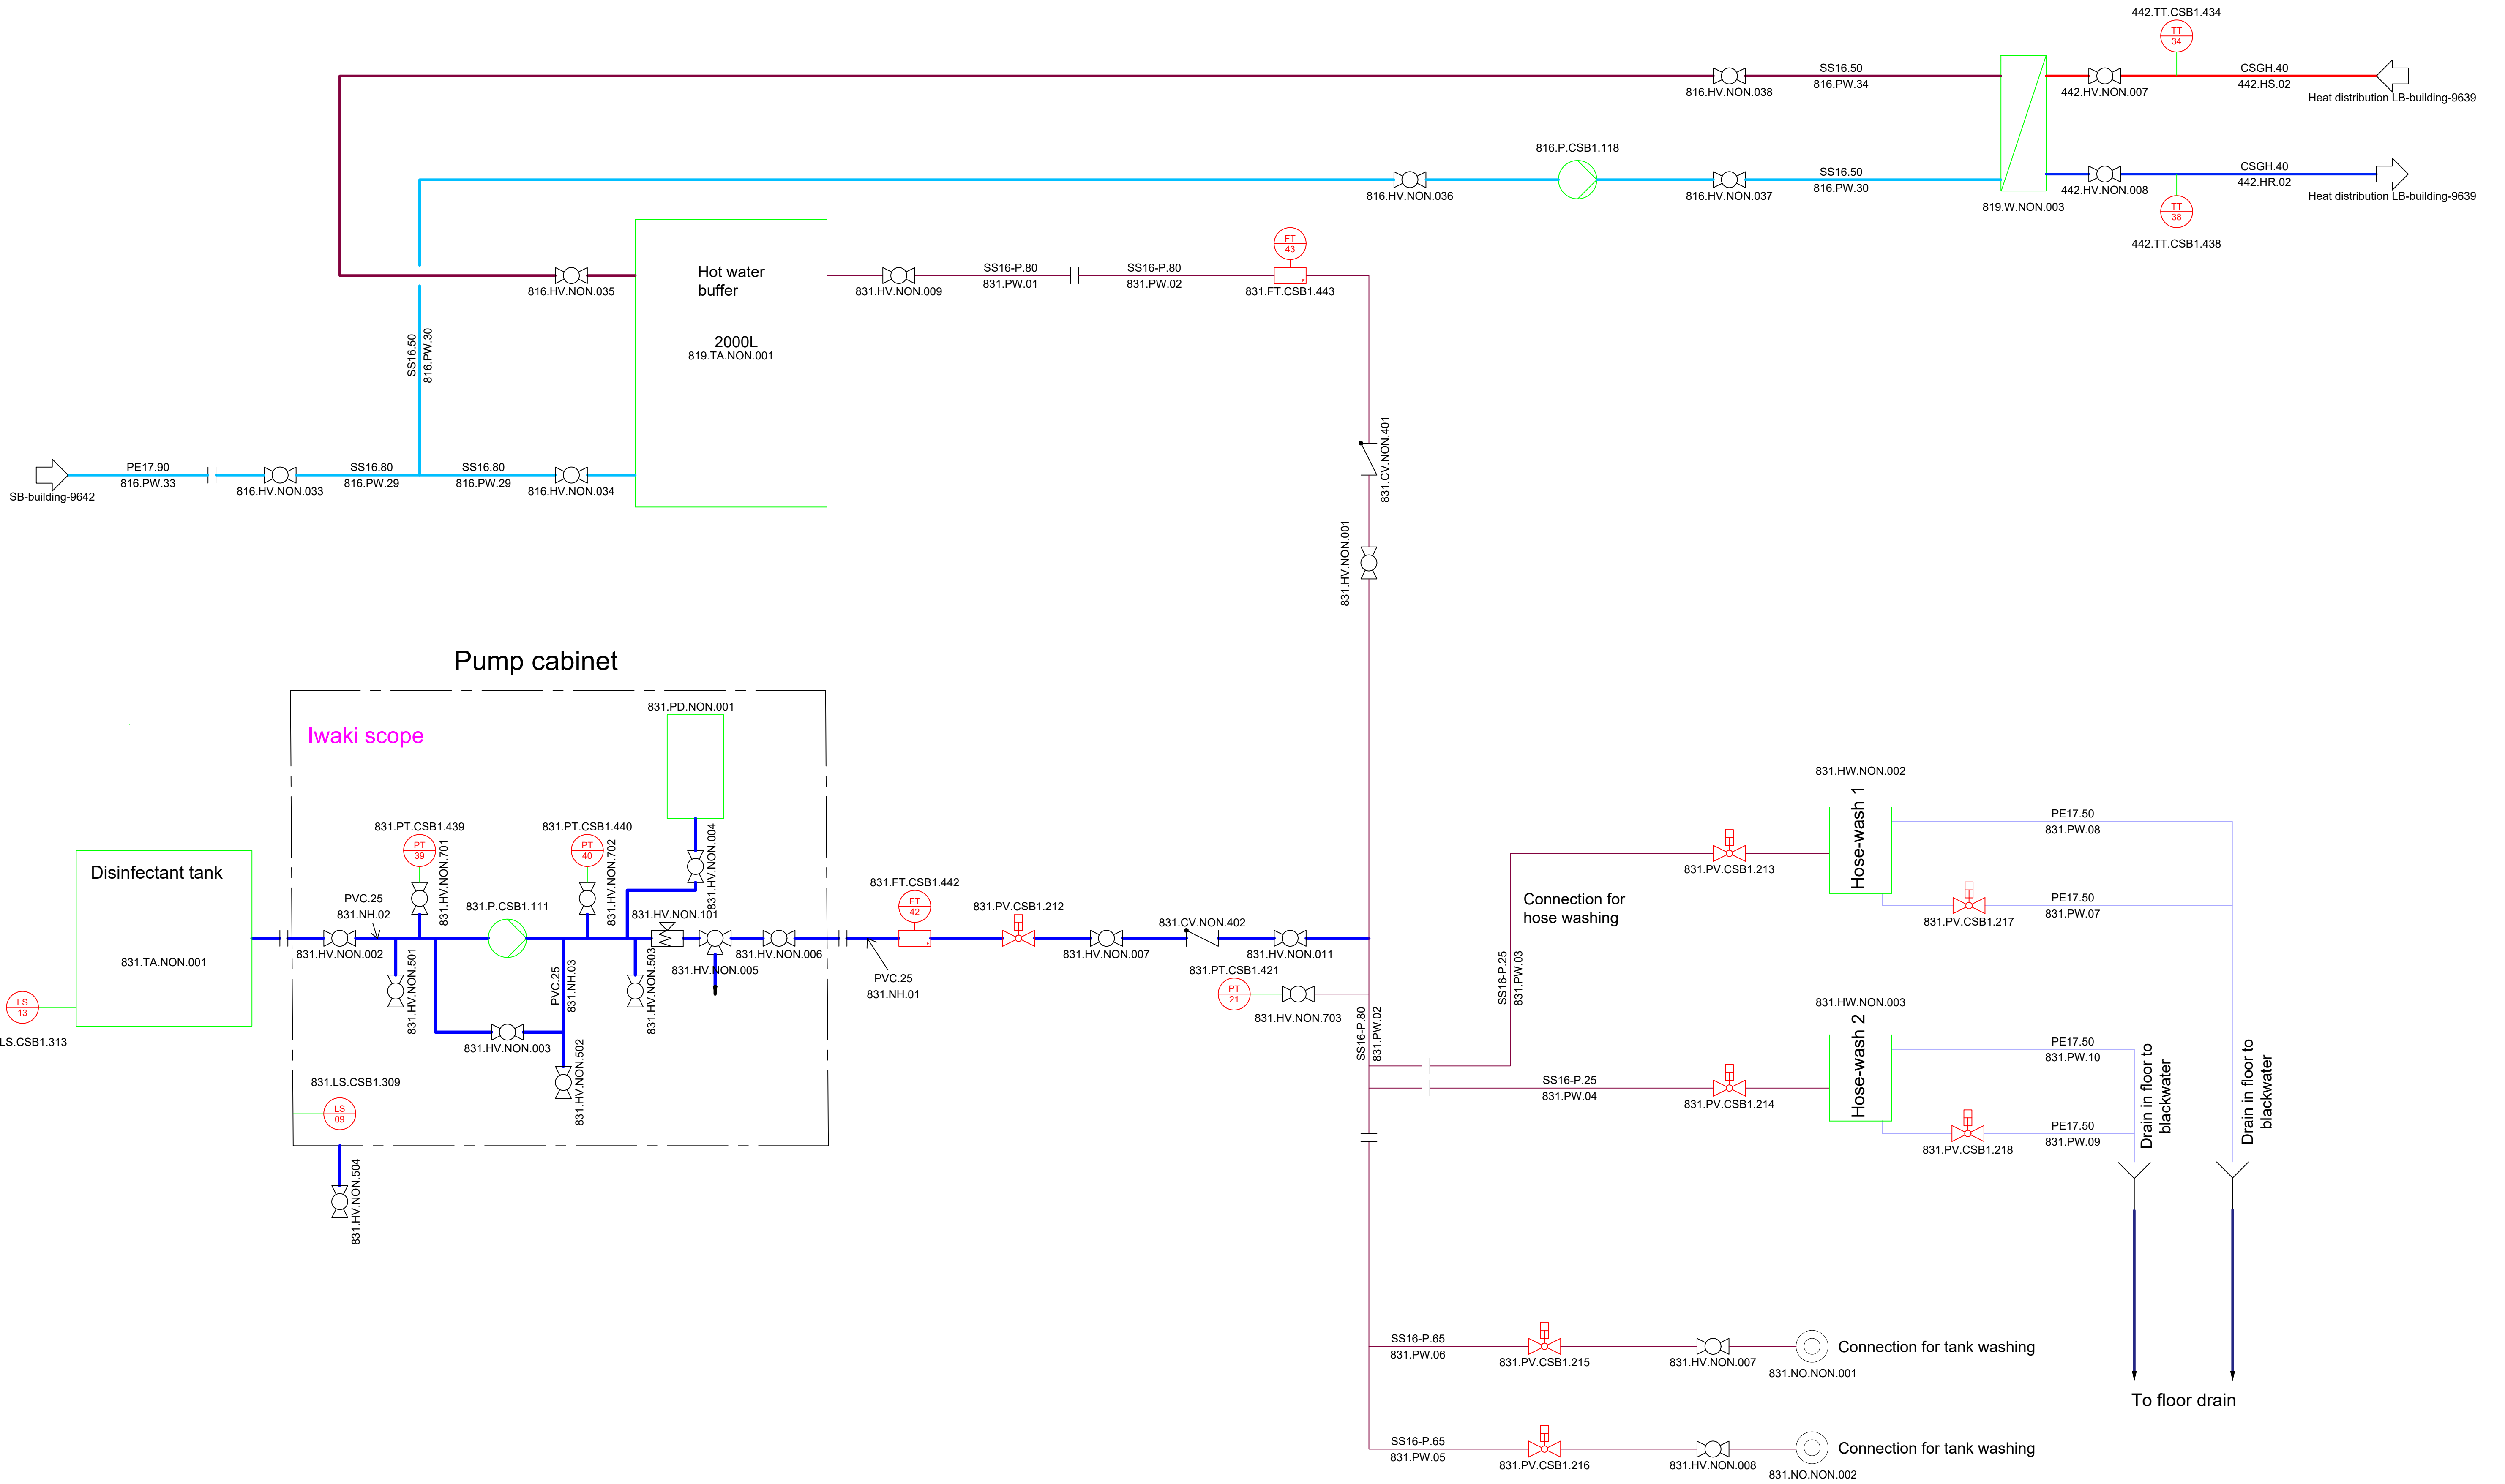

Rev. Nr.:	Rev. Dato:	Rev. Beskrivelse:	
Builder:	ST1		
Project:	SLK		
Subject:	Wash system		
Rev. 6			
Int.:MDC	QC: CM	APP.:	Date: 15-10-2025
LUNDSBY RENEWABLE SOLUTIONS			Lundsby Biogas A/S, Hjarbækvej 65, 8831 Løgstrup Tlf.: +45 96 49 43 00 info@lundsbybiogas.dk Denne tegning er underlagt copyright op på ikke reproduceres uden tilladelse fra Lundsbybiogas A/S
			Sags nr.: 1768 Tegn. nr.: 9646 FORMAT: A1

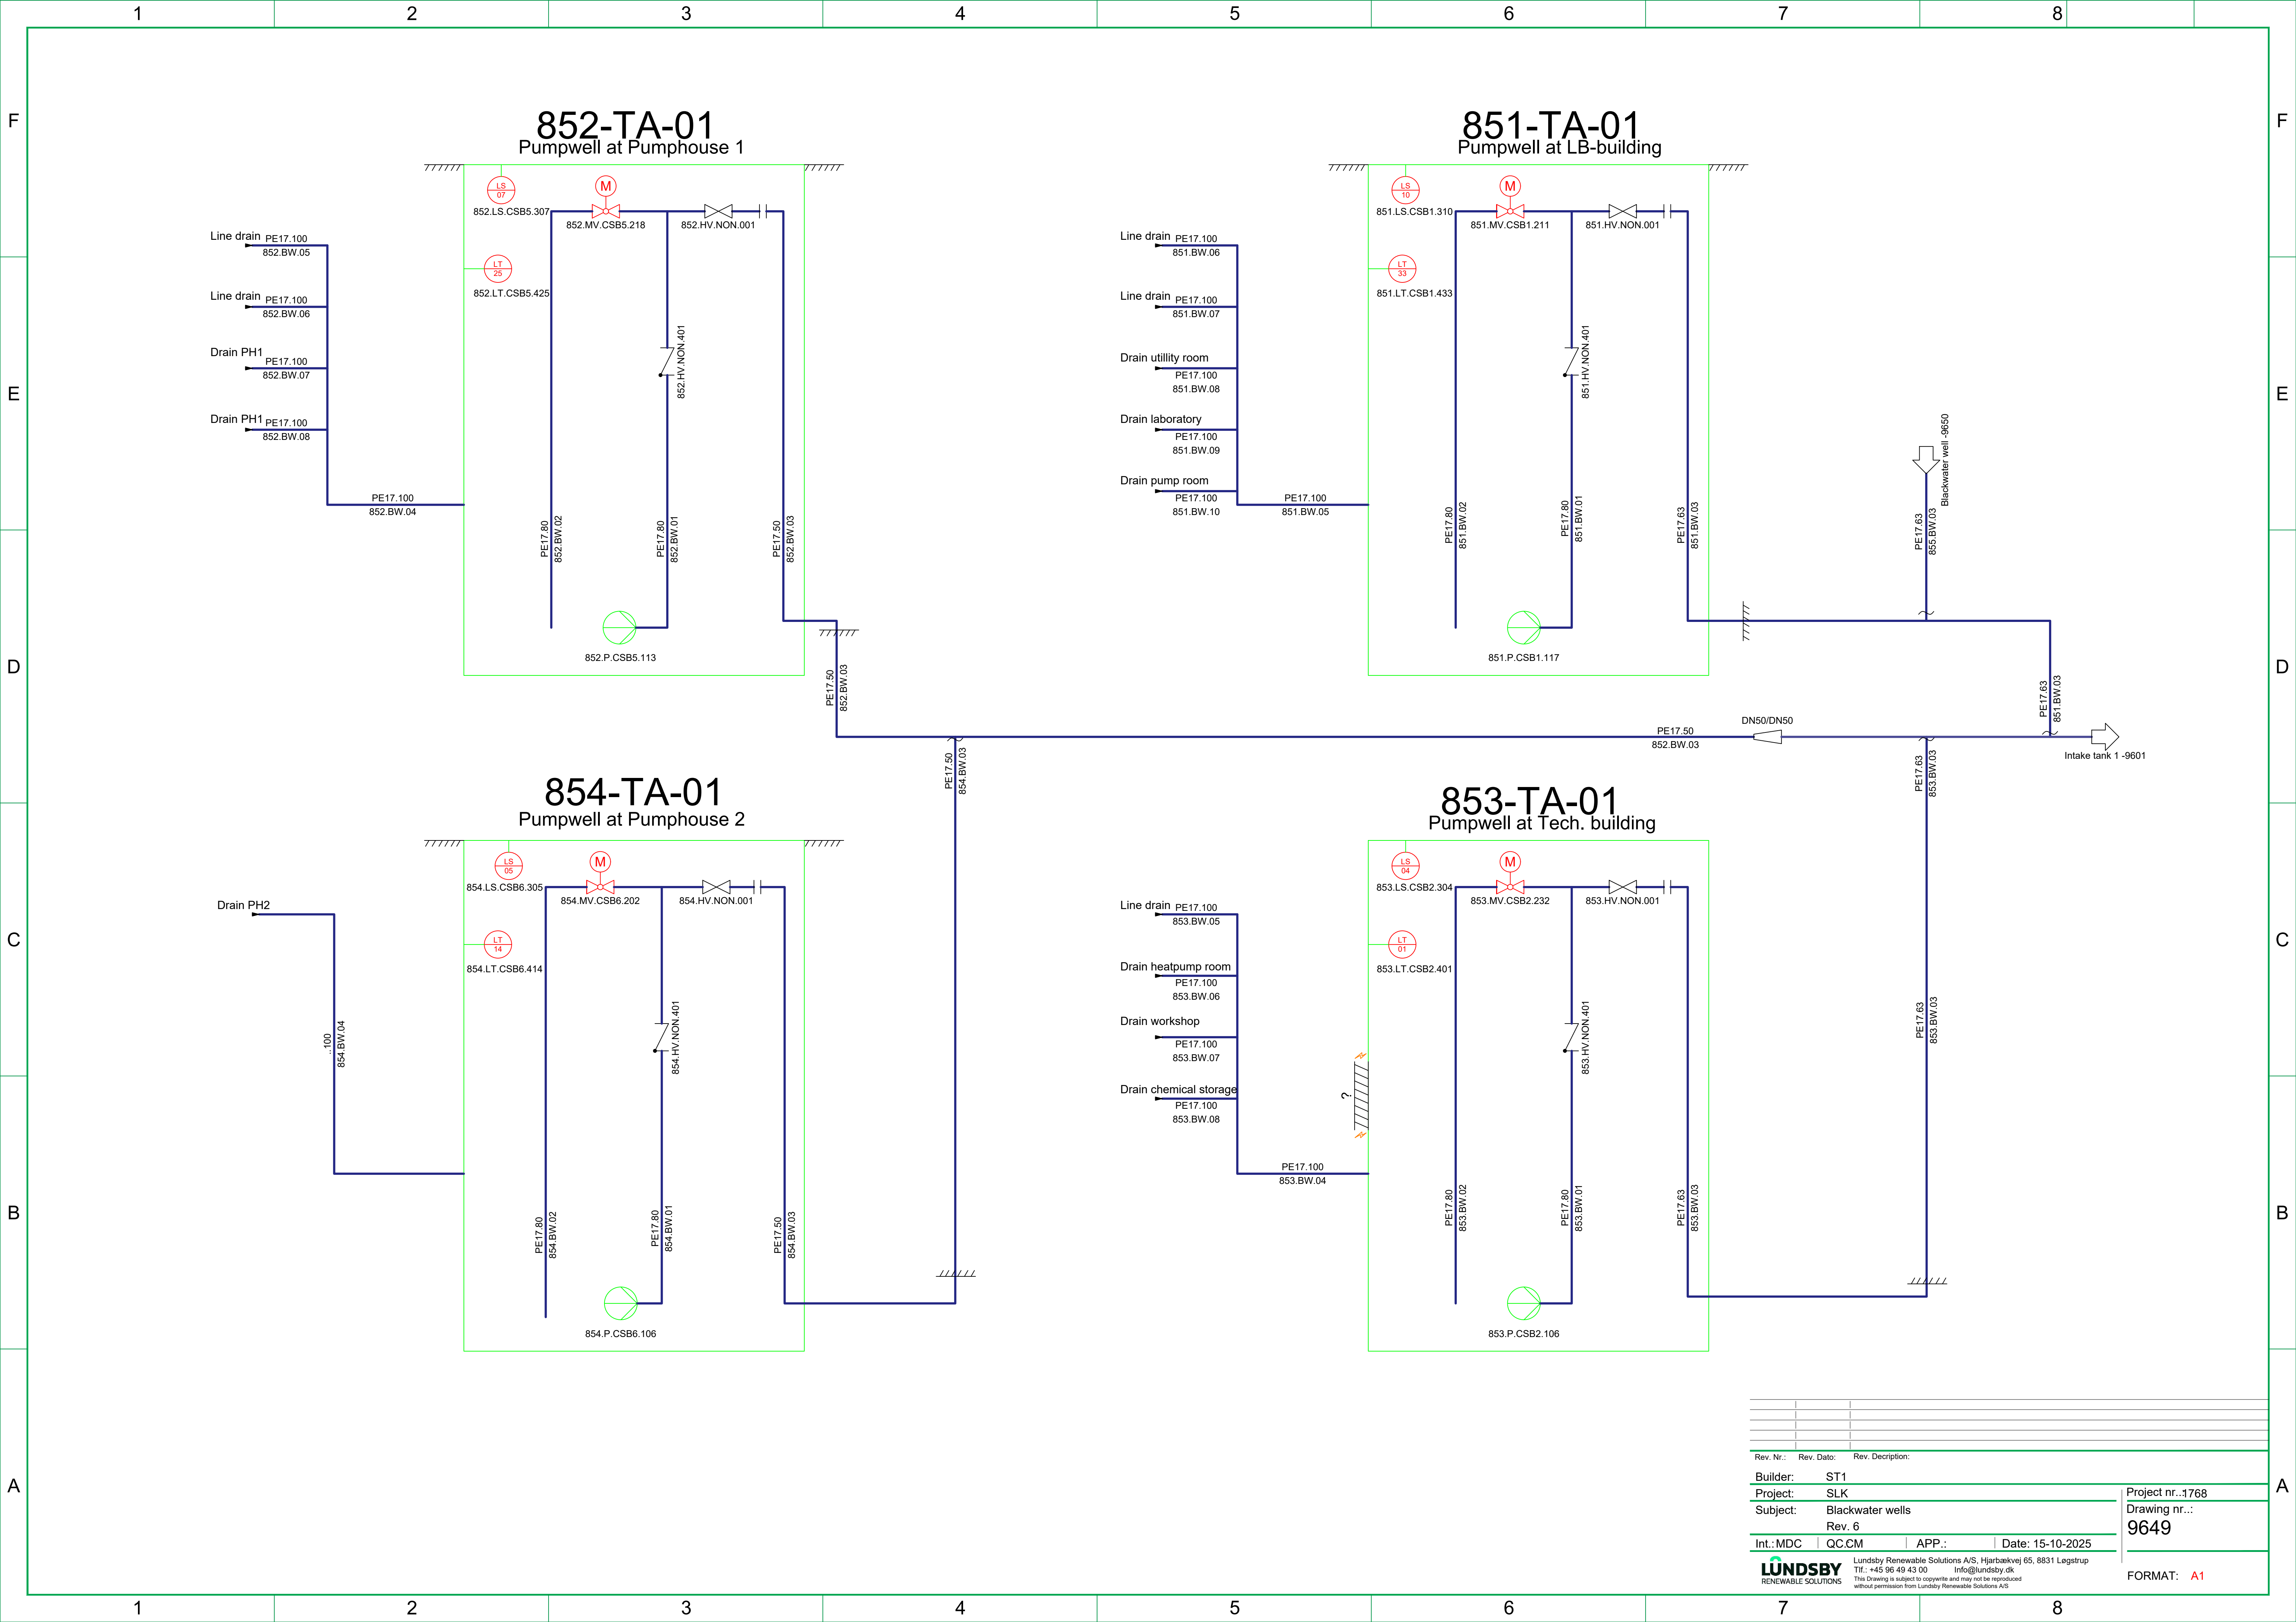

852-TA-01

Pumpwell at Pumphouse 1

851-TA-01

Pumpwell at LB-building


854-TA-01

Pumpwell at Pumphouse 2

853-TA-01


Pumpwell at Tech. building

Rev. Nr.:	Rev. Dato:	Rev. Description:	
Builder:	ST1		
Project:	SLK		
Subject:	Blackwater wells		
	Rev. 6		
Int.:MDC	QC:CM	APP.:	Date: 15-10-2025
LUNDSBY RENEWABLE SOLUTIONS			Lundsby Renewable Solutions A/S, Hjarbækvej 65, 8831 Løgstrup Tlf.: +45 96 49 43 00 Info@lundsby.dk This Drawing is subject to copyright and may not be reproduced without permission from Lundsby Renewable Solutions A/S
			Project nr.:1768 Drawing nr.: 9649
			FORMAT: A1

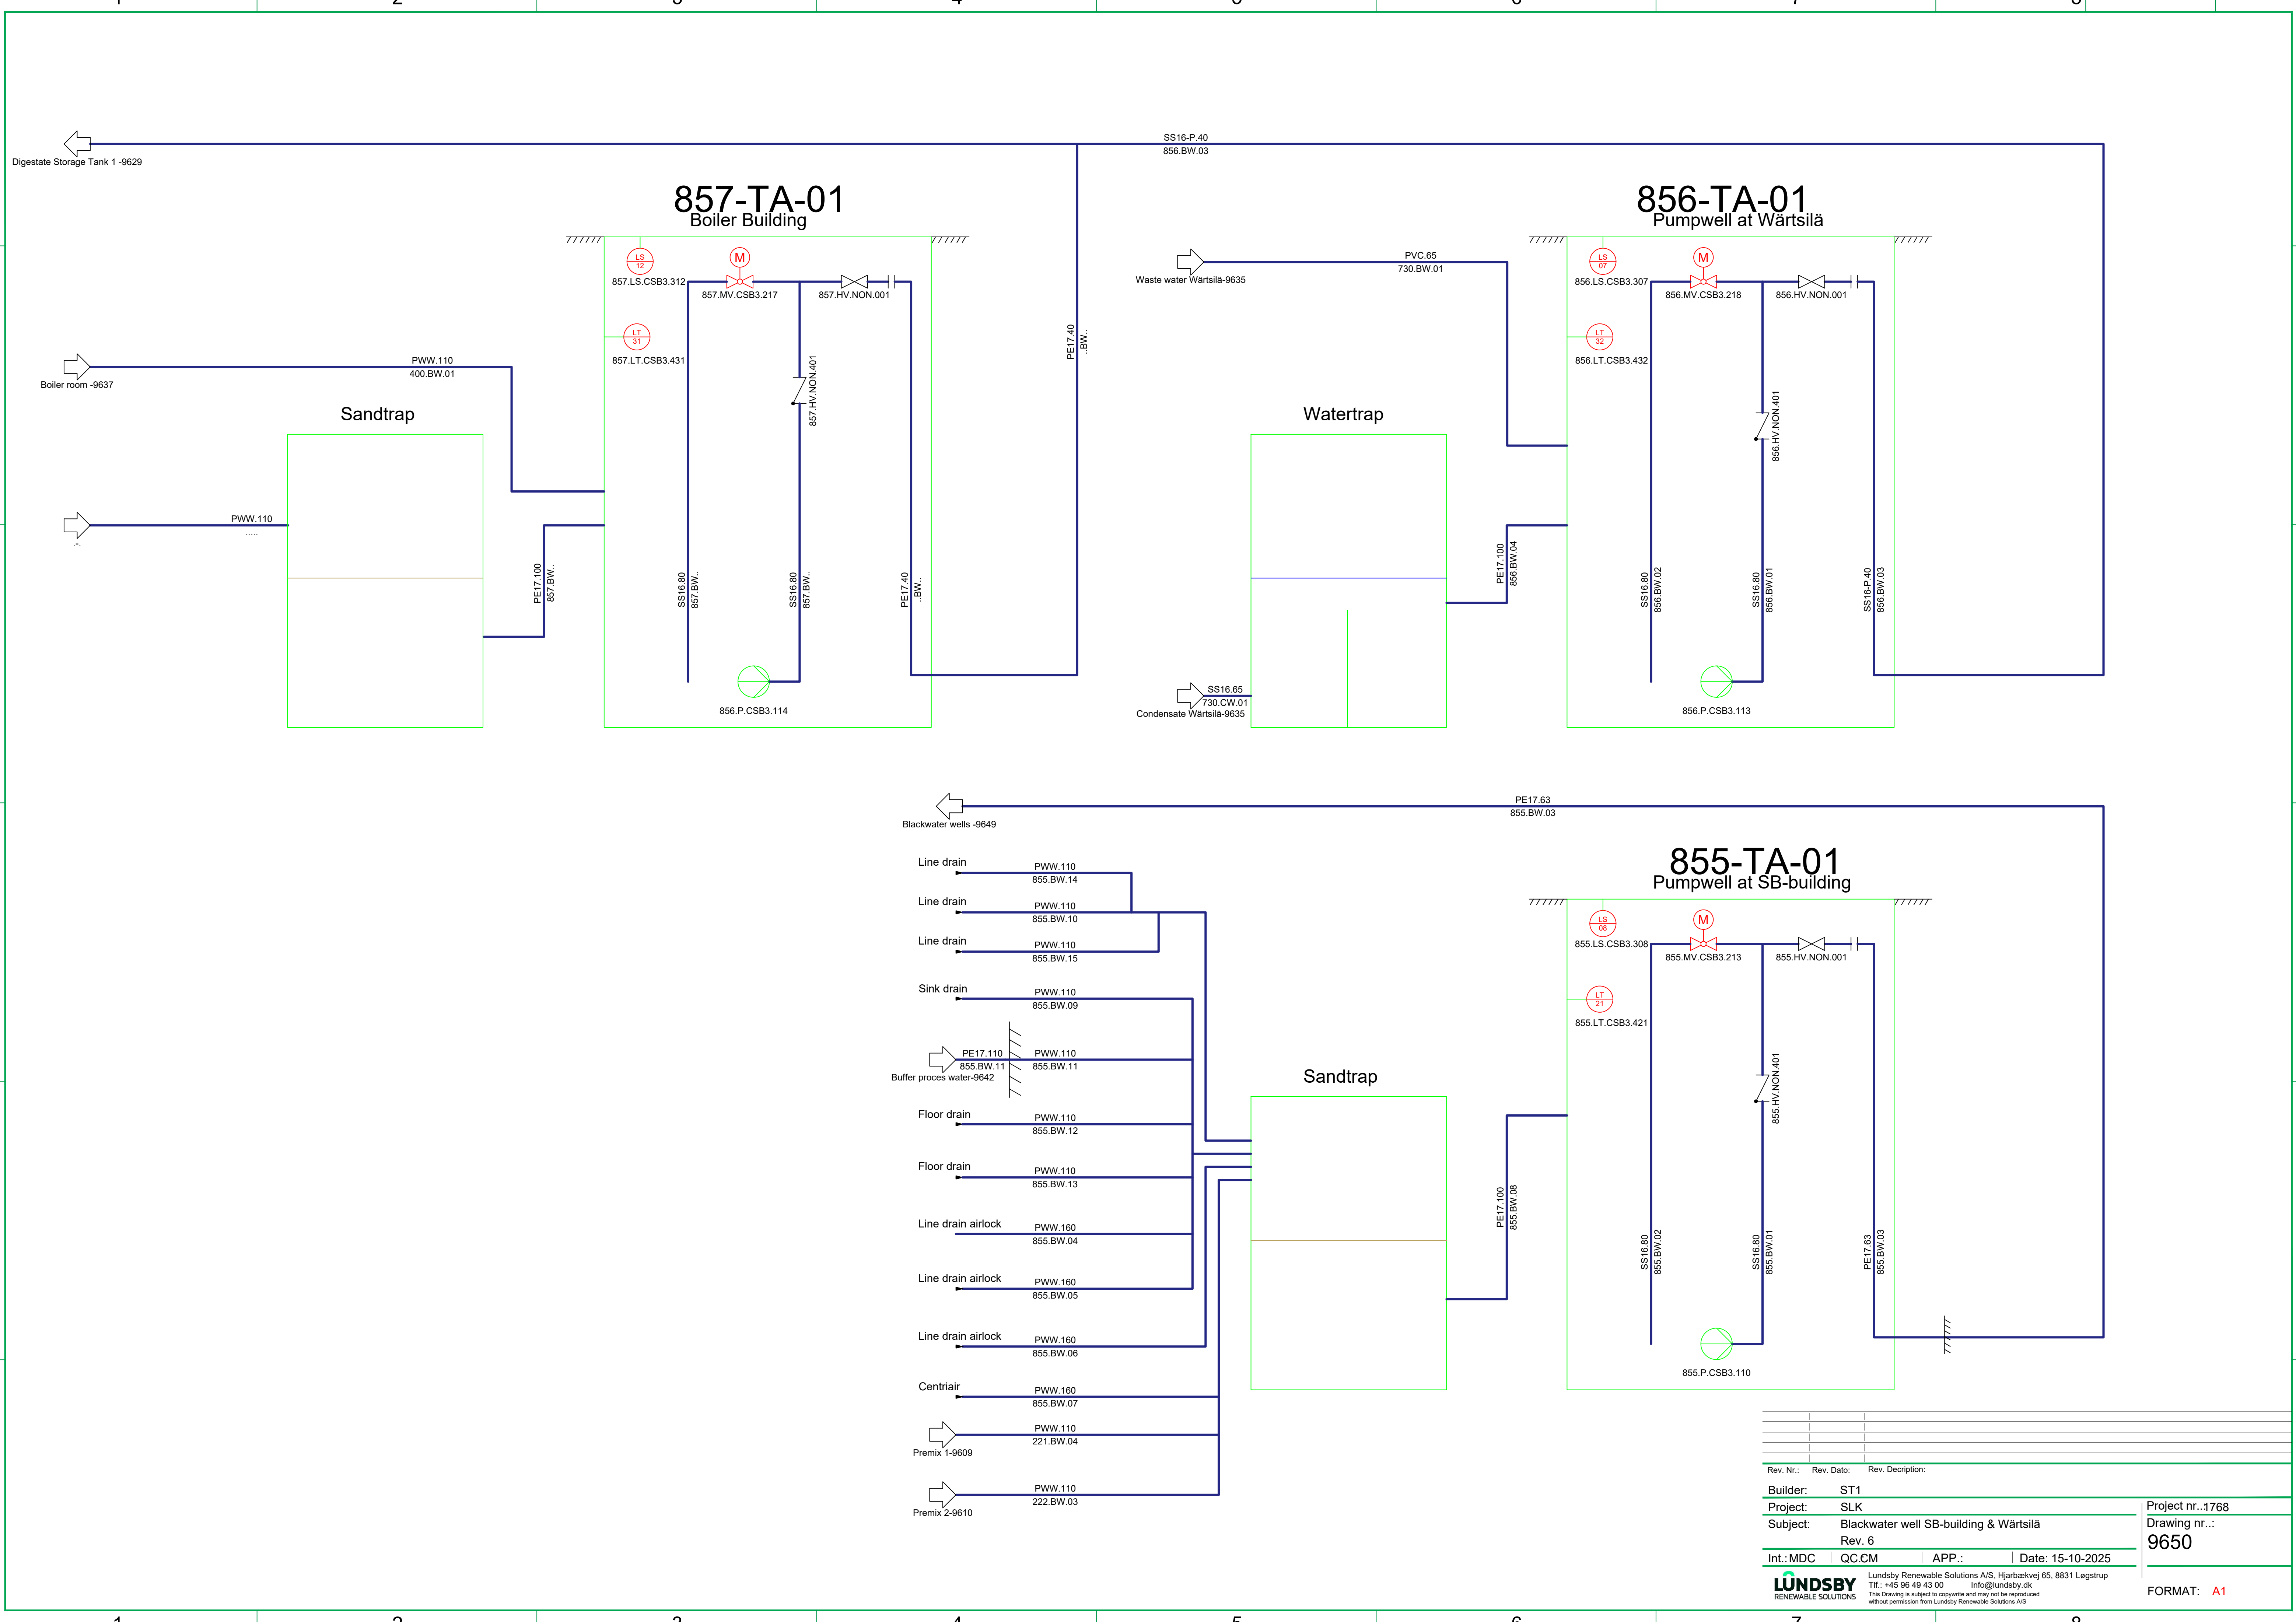


Rev. Nr.:	Rev. Dato:	Rev. Description:
Builder:	ST1	
Project:	SLK	
Subject:	Blackwater well SB-building & Wärtsilä	
Rev.	6	
Int.:MDC	QC:CM	APP.:
Date:	15-10-2025	
LUNDSBYRENEWABLE SOLUTIONS Lundsby Renewable Solutions A/S, Hjarbækvej 65, 8831 Løgstrup Tlf.: +45 96 49 43 00 Info@lundsby.dk This Drawing is subject to copyright and may not be reproduced without permission from Lundsby Renewable Solutions A/S		
Project nr.:1768		Drawing nr.:9650
FORMAT:		A1


Pumphouse 1
JA Trykluft scope

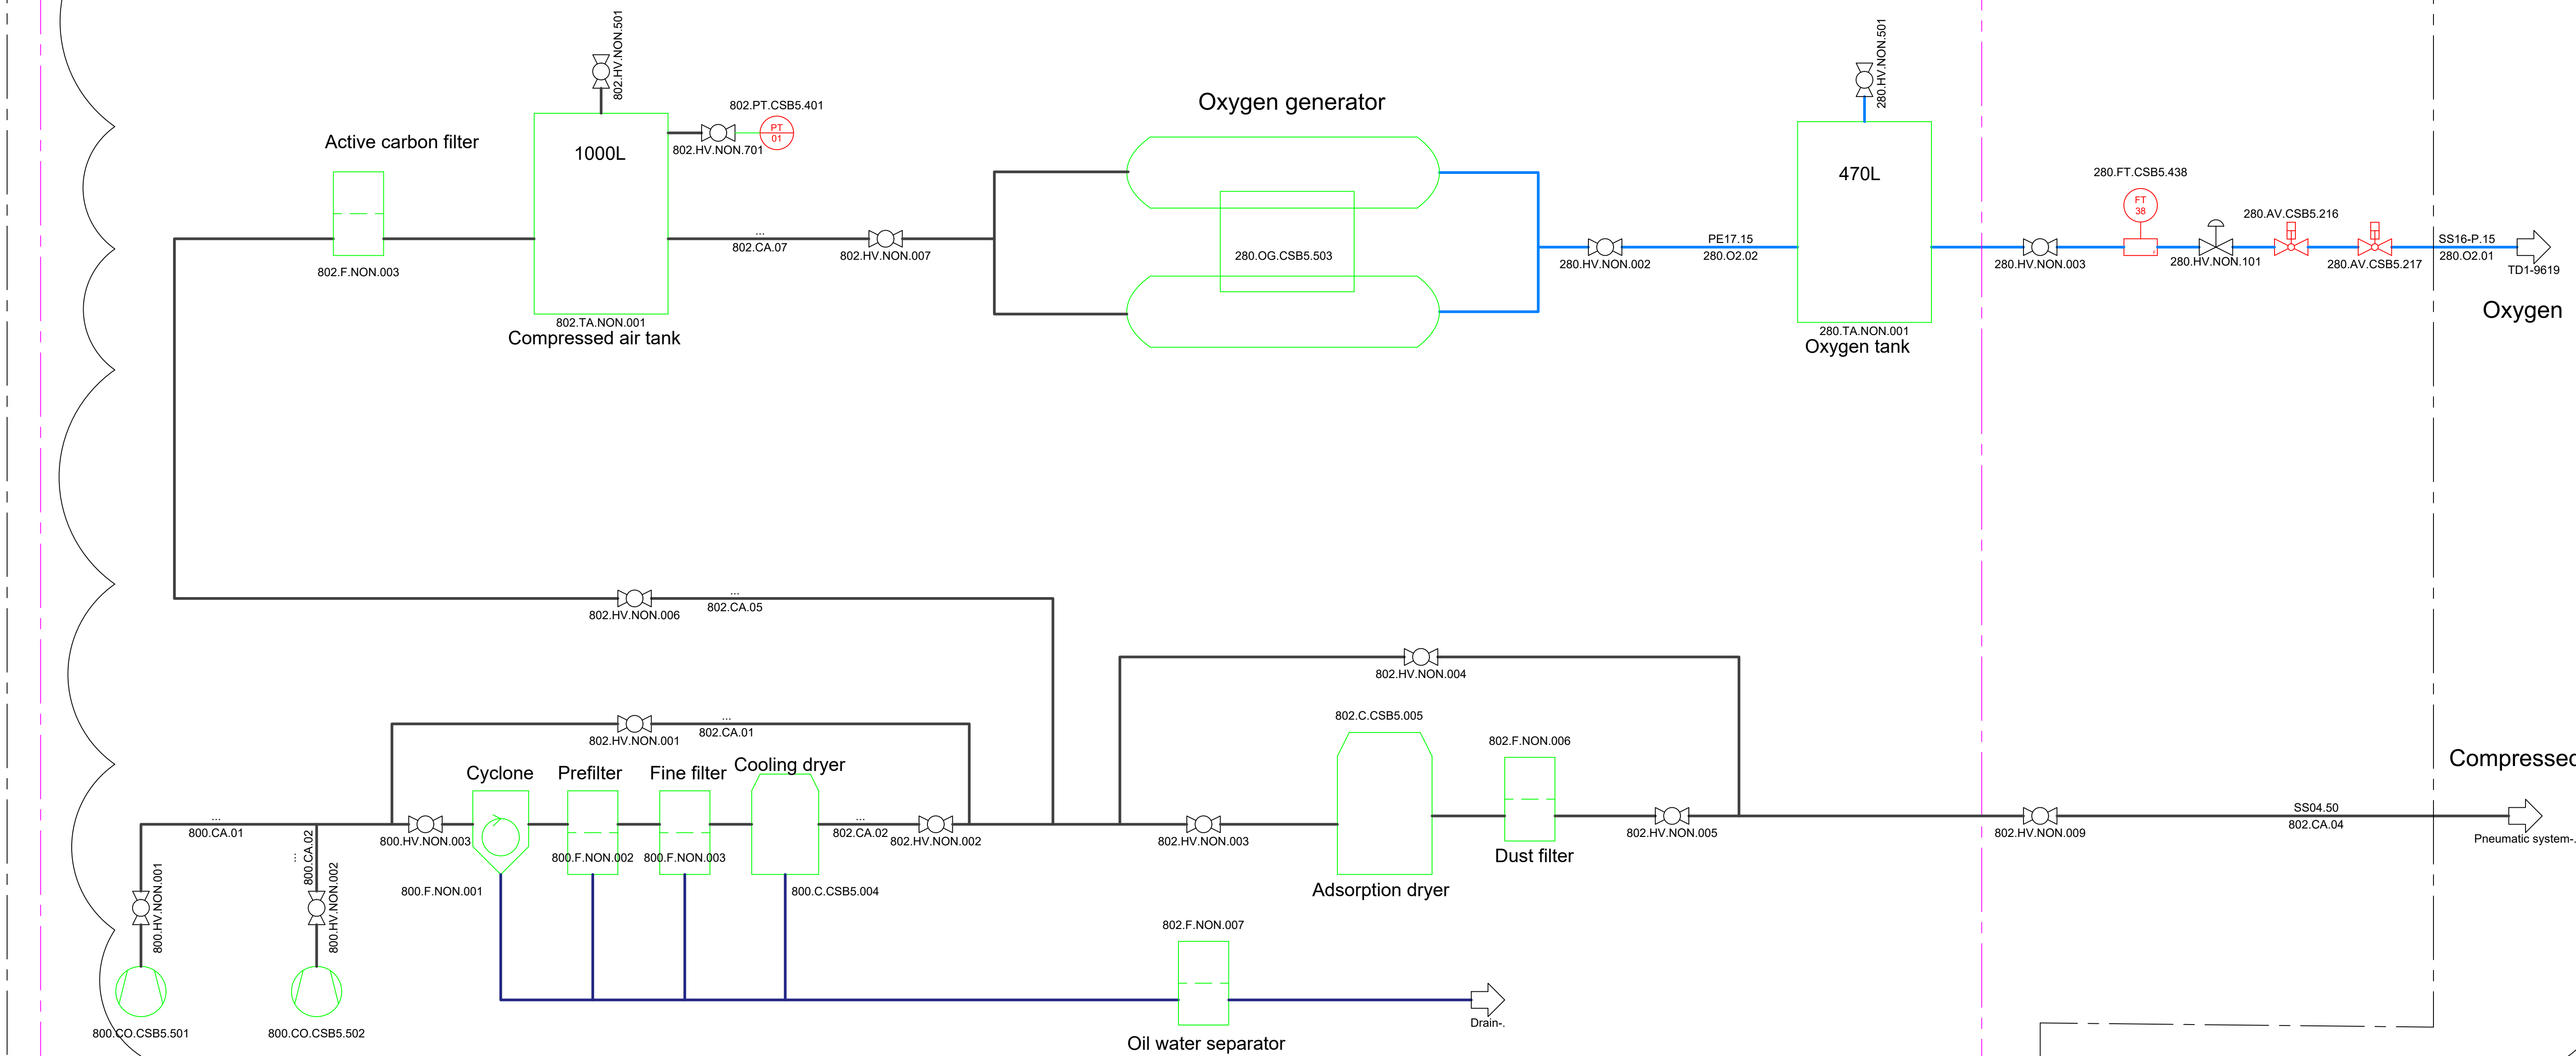


Rev. Nr.:	Rev. Dato:	Rev. Description:	
Builder:	ST1		
Project:	SLK		
Subject:	Compressed air & Oxygen		
Rev. 6			
Int.:MDC	QC:CM	APP.:	Date: 15-10-2025
LUNDSBY RENEWABLE SOLUTIONS			Lundsby Renewable Solutions A/S, Hjarbækvej 65, 8831 Løgstrup Tlf.: +45 96 49 43 00 Info@lundsby.dk This drawing is subject to copyright and may not be reproduced without permission from Lundsby Renewable Solutions A/S
Project nr.:1768 Drawing nr.: 9652			FORMAT: A1

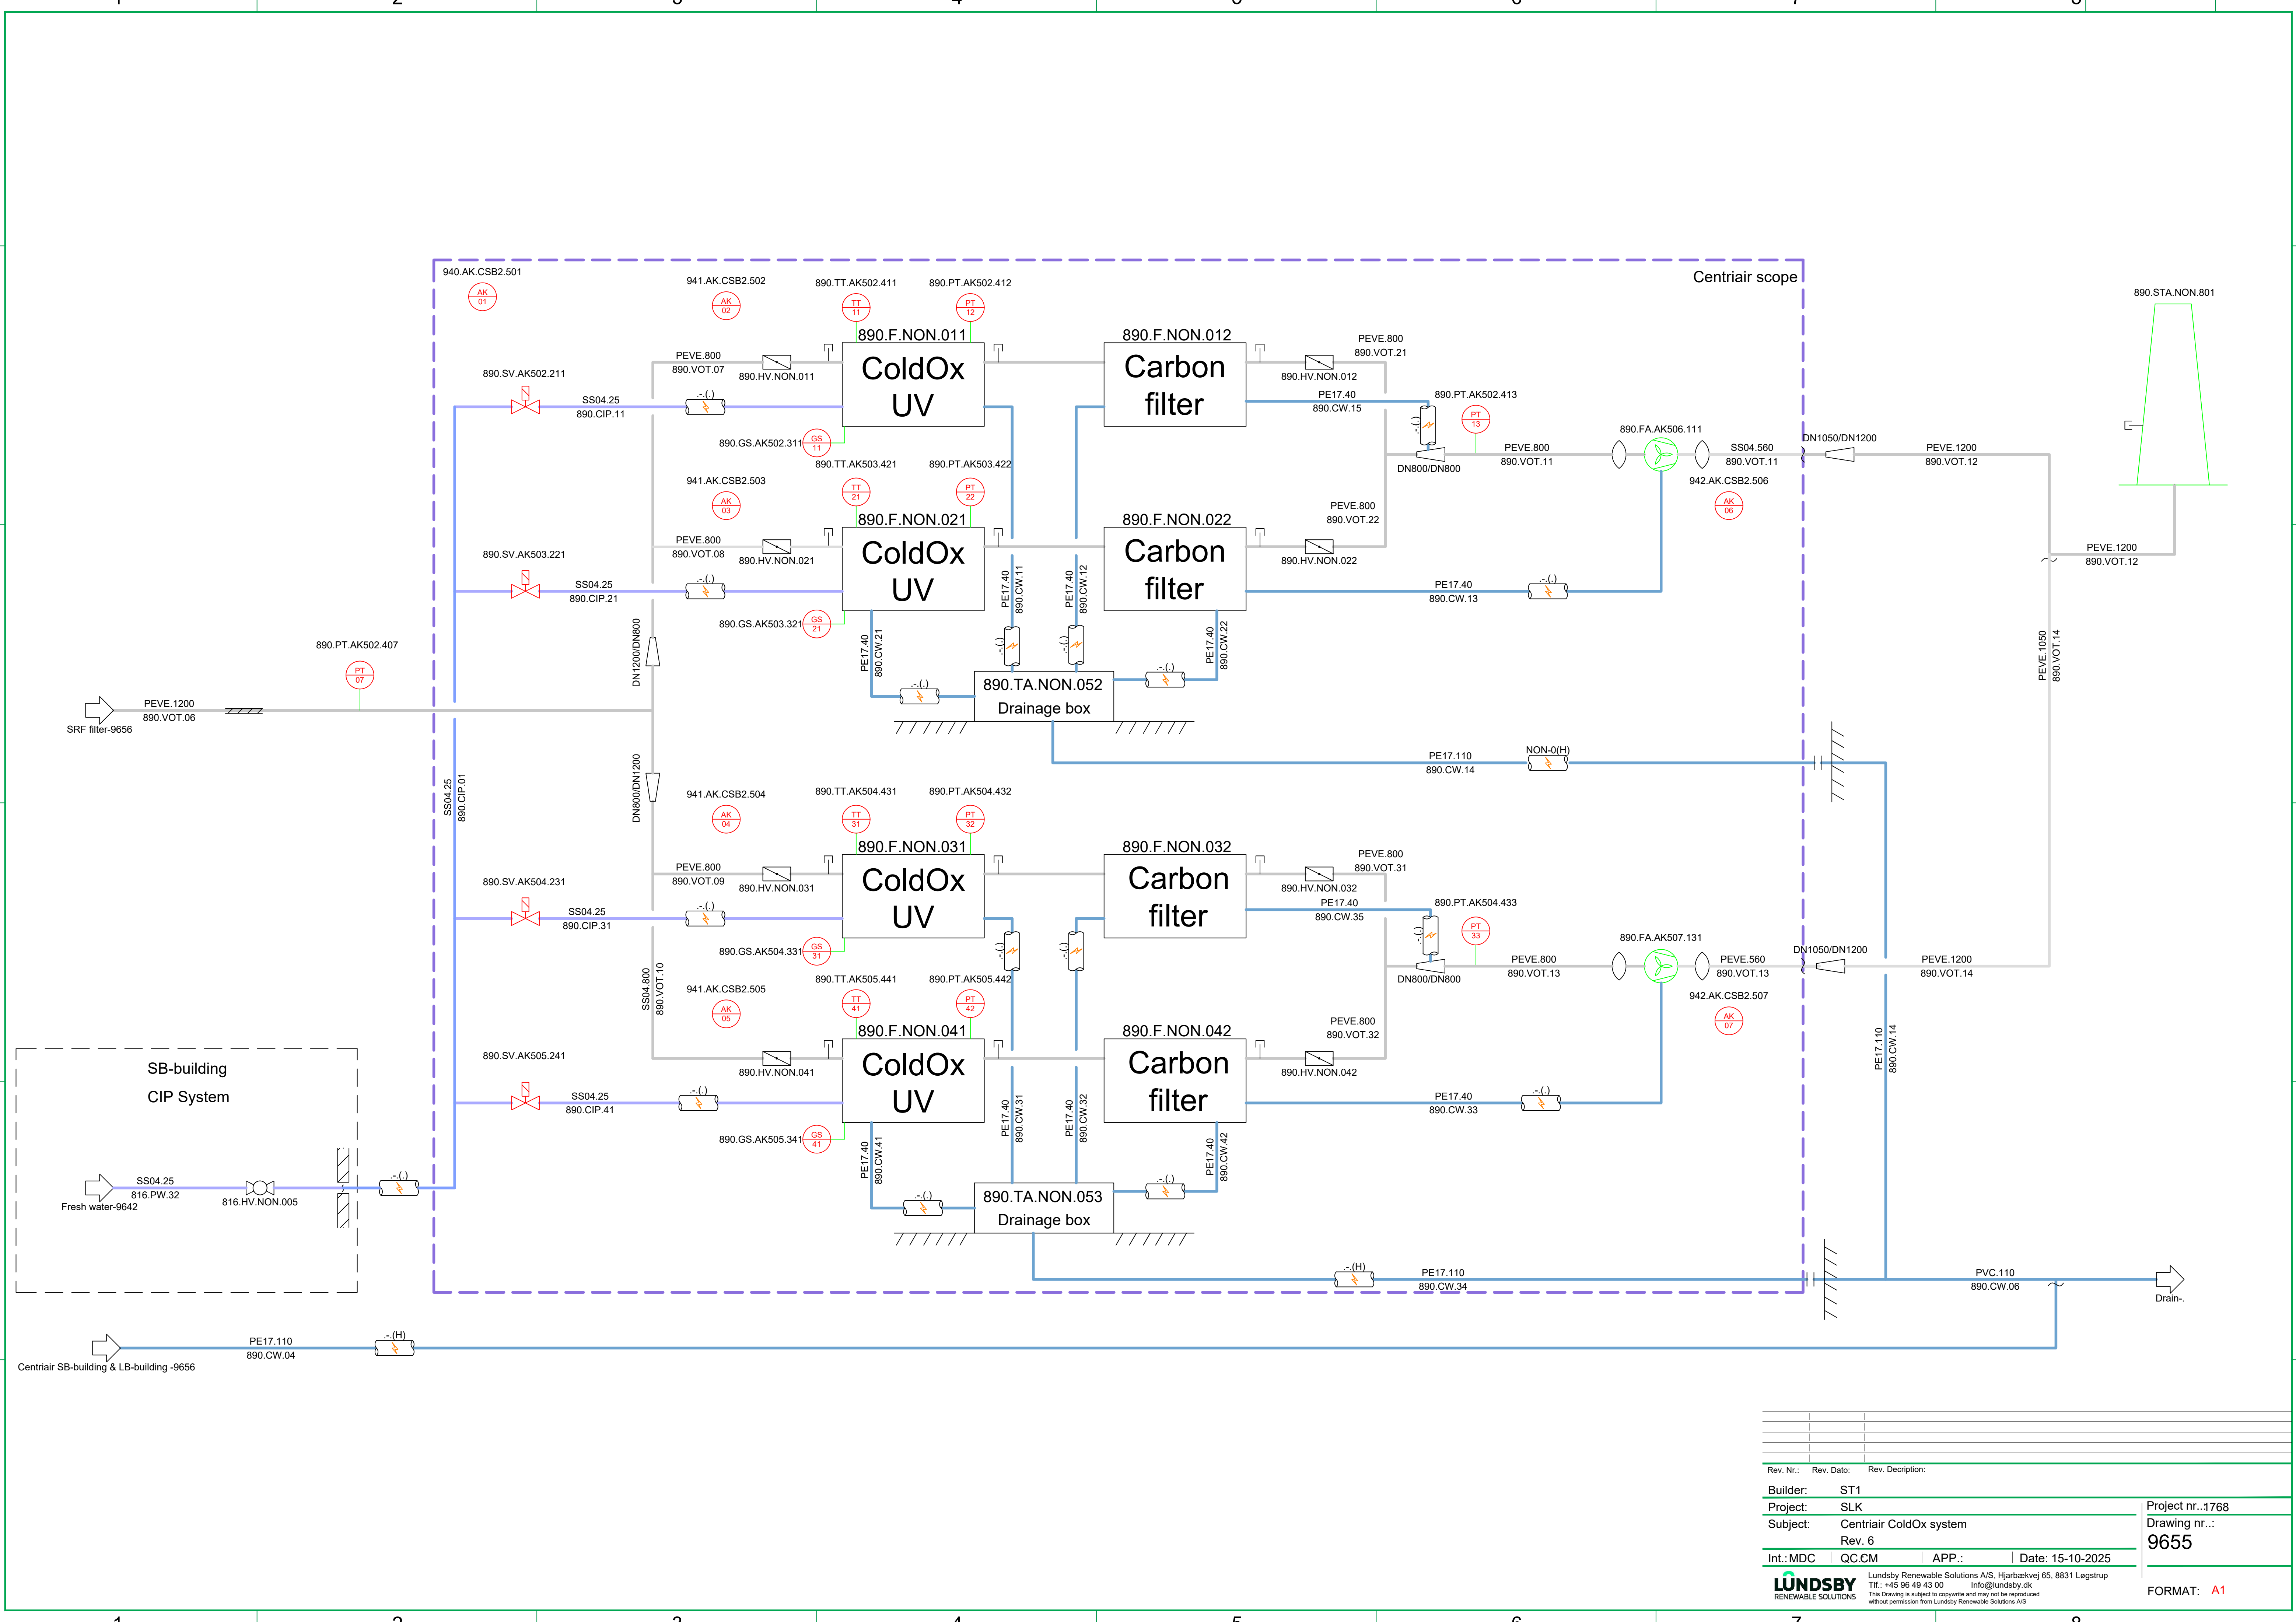

Rev. Nr.:	Rev. Dato:	Rev. Description:
Builder:	ST1	
Project:	SLK	
Subject:	Centriair ColdOx system	
Rev. 6		
Int.:MDC	QC:CM	APP.:
Date:	15-10-2025	
LUNDSBY RENEWABLE SOLUTIONS		
Lundsby Renewable Solutions A/S, Hjarbækvej 65, 8831 Løgstrup Tlf.: +45 96 49 43 00 info@lundsby.dk This drawing is subject to copyright and may not be reproduced without permission from Lundsby Renewable Solutions A/S		
Project nr.:1768 Drawing nr.: 9655		FORMAT: A1

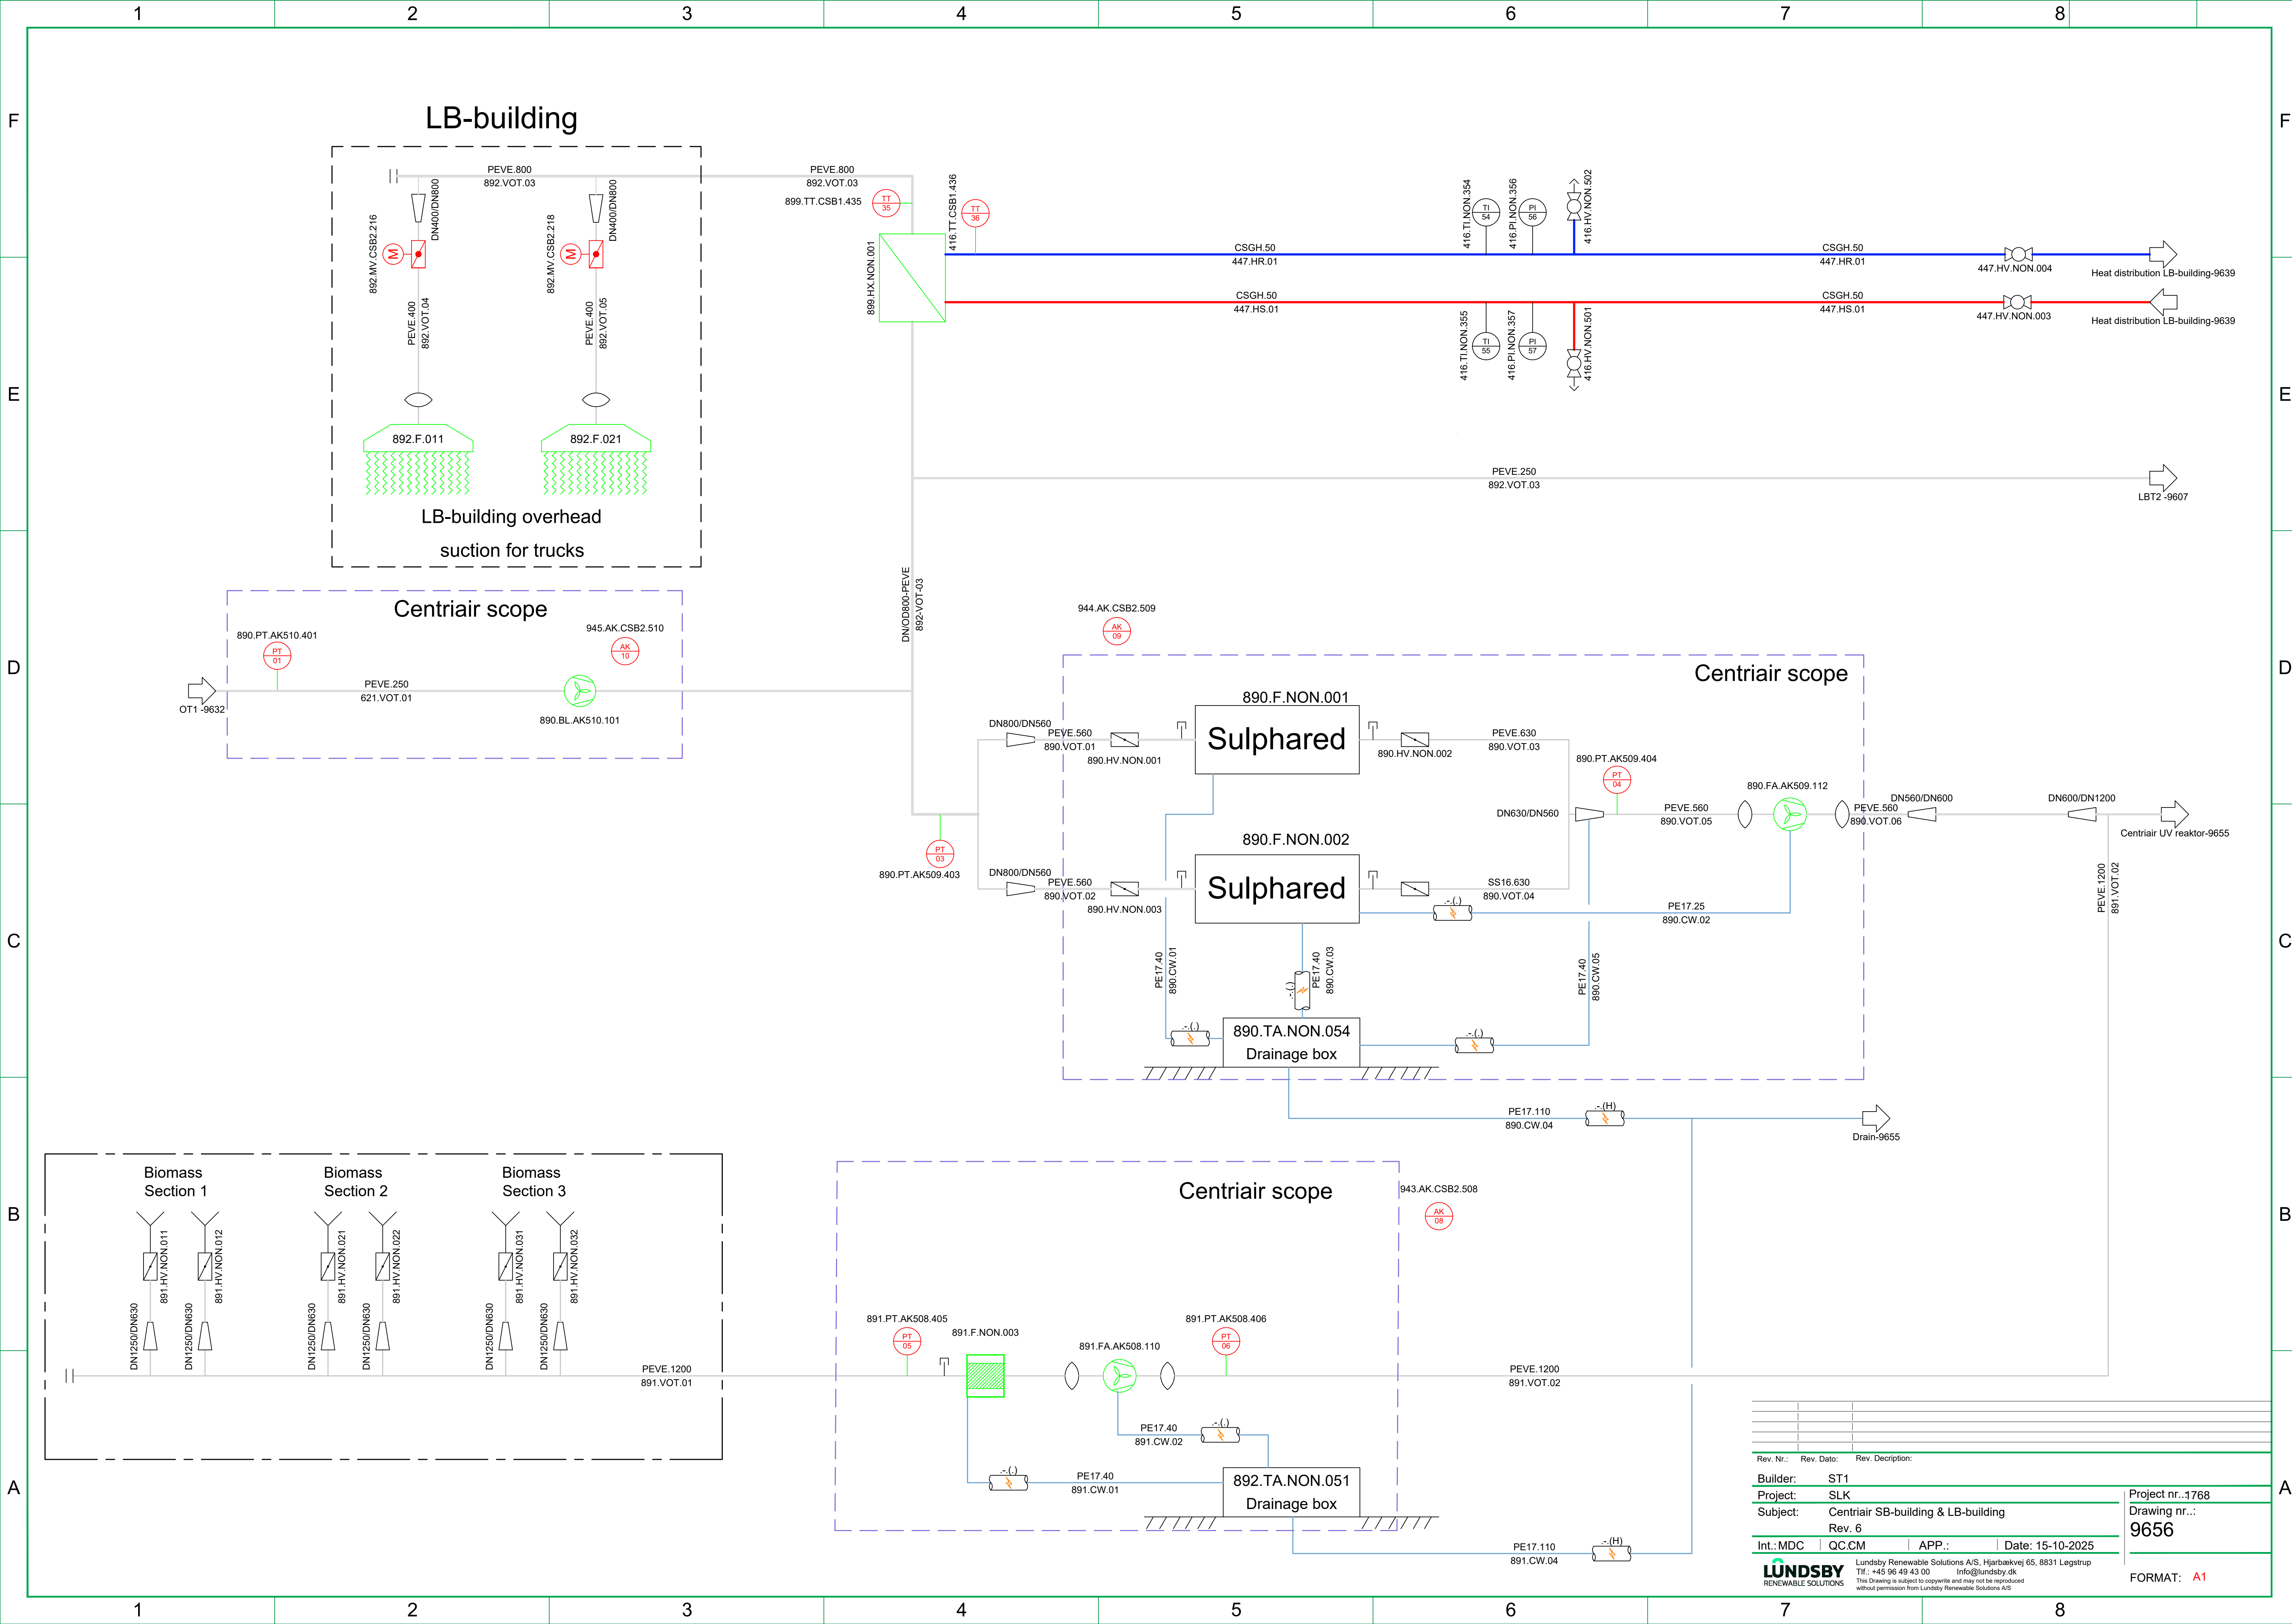

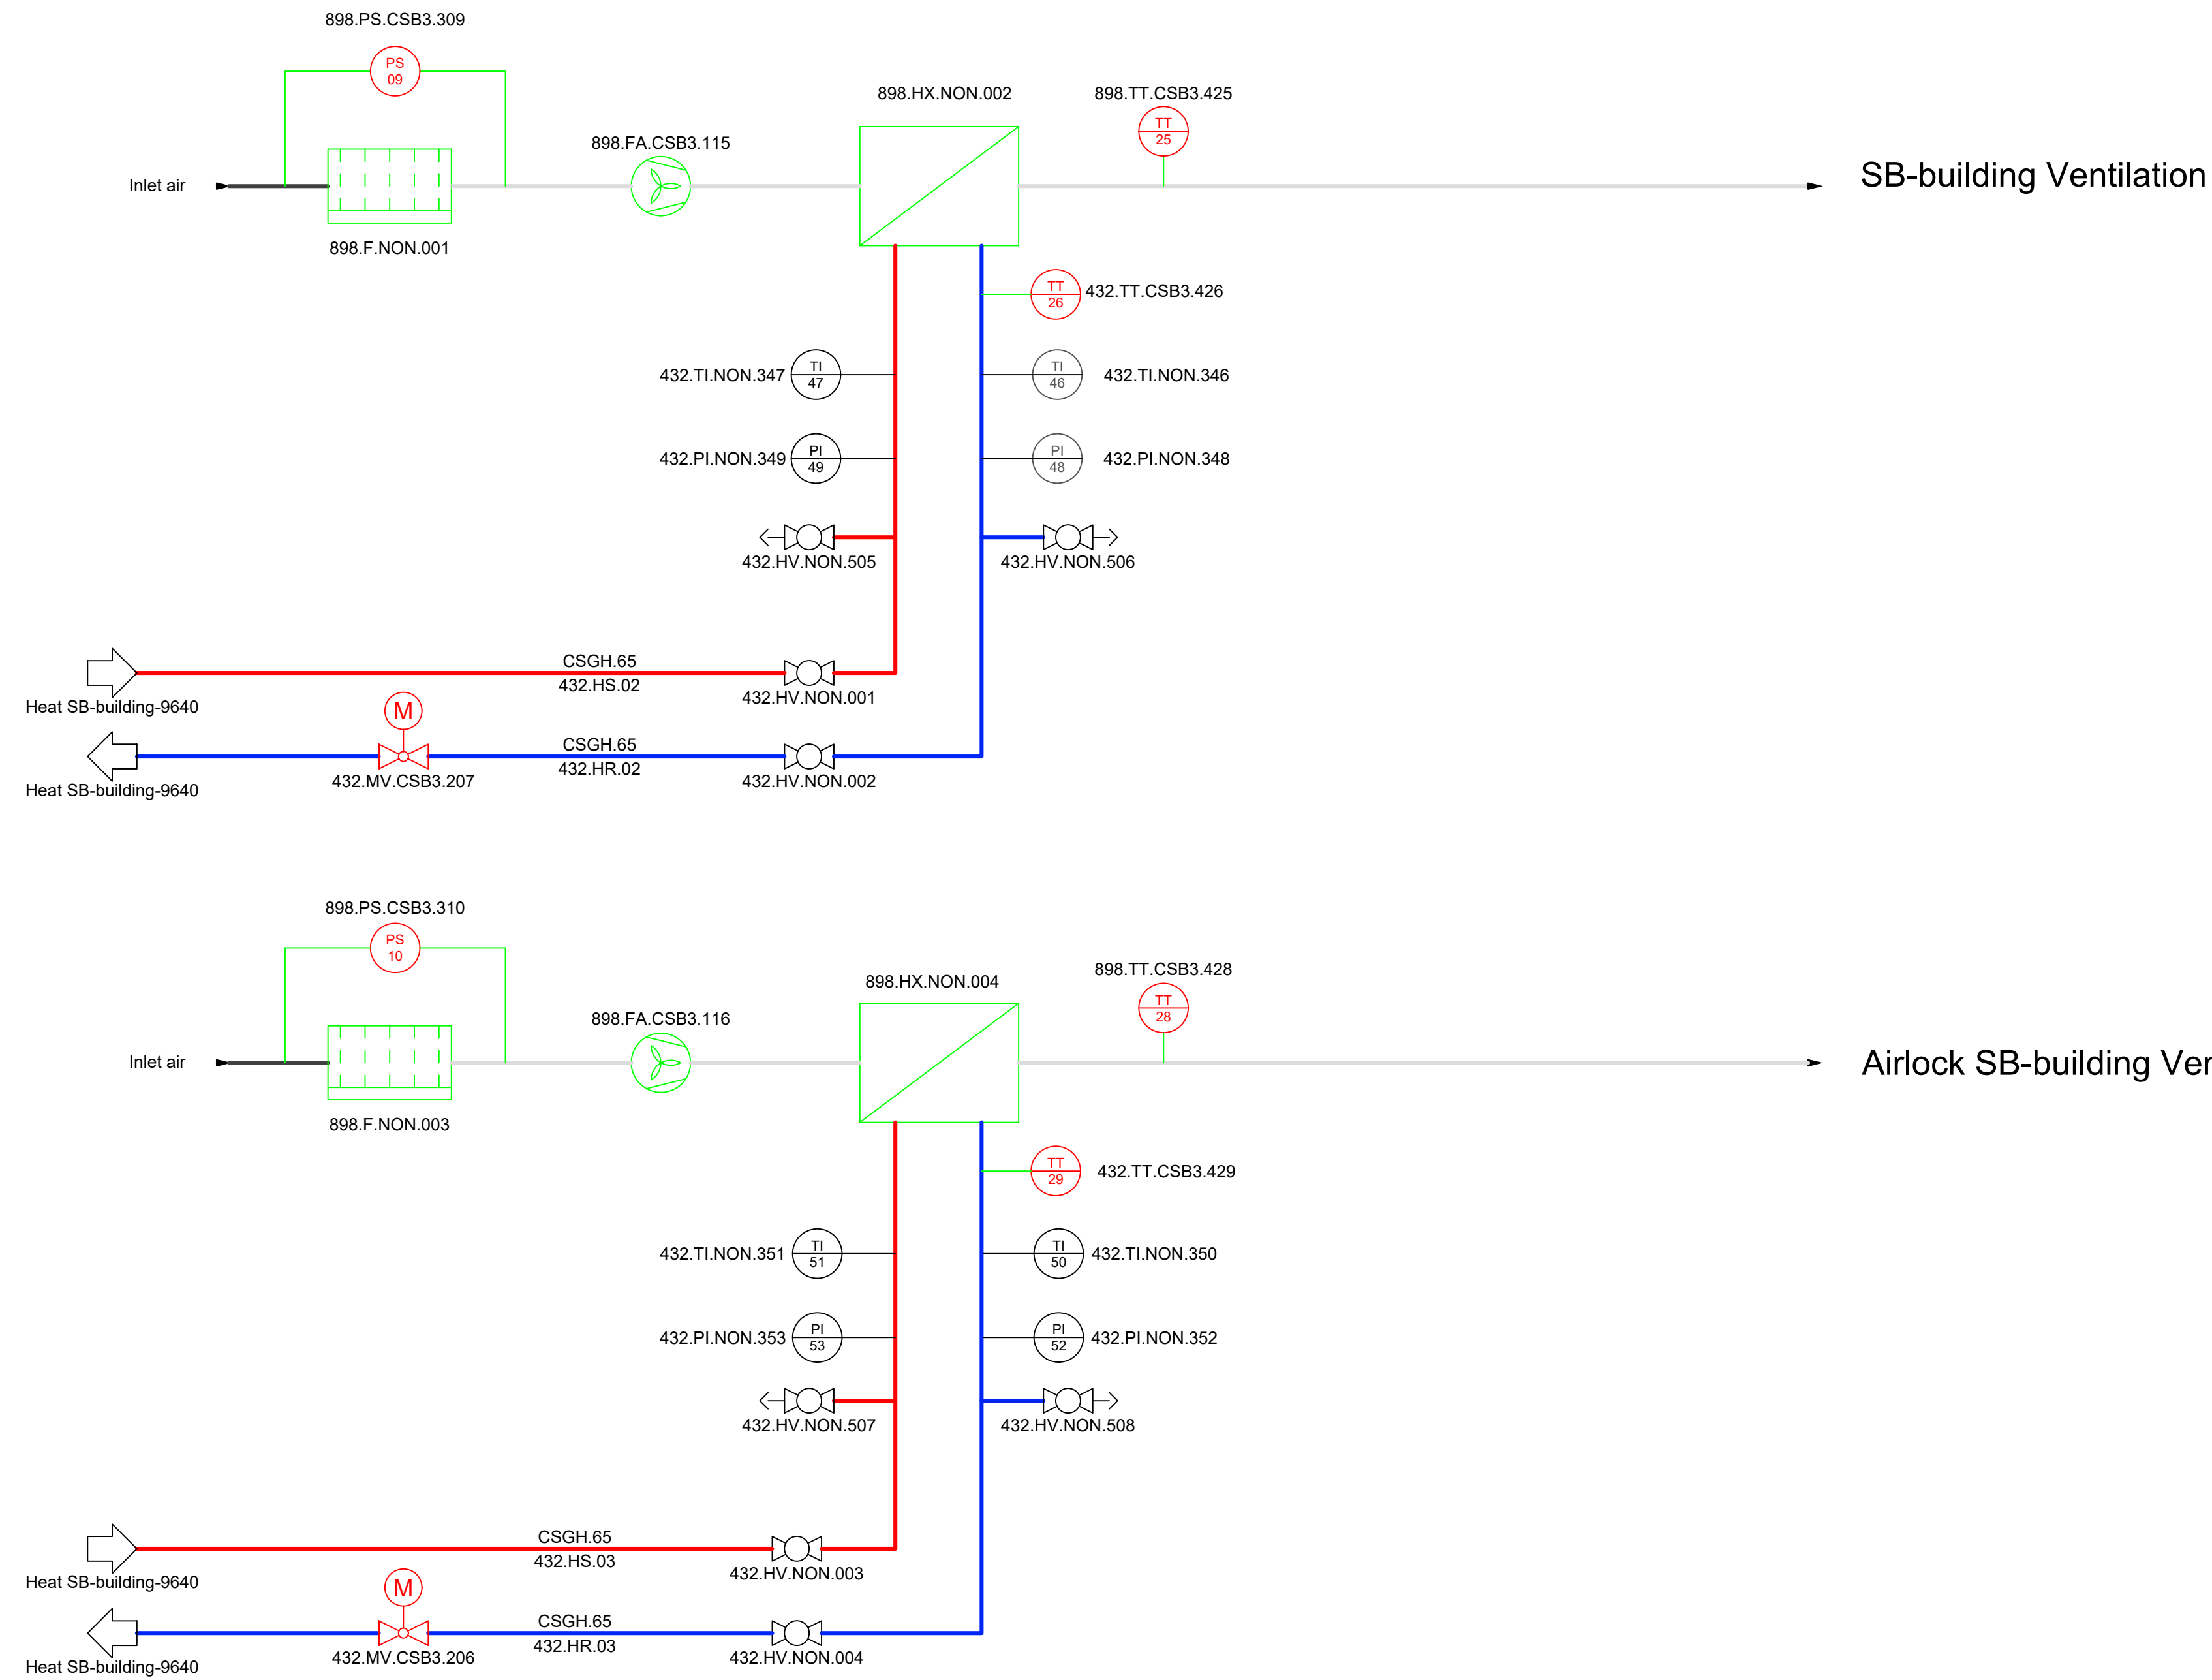

Rev. Nr.:	Rev. Dato:	Rev. Description:	
Builder:	ST1		
Project:	SLK		
Subject:	Ventilation SB-building		
Rev. 6			
Int.:MDC	QC.: CM	APP.:	Date: 15-10-2025
LUNDSBY RENEWABLE SOLUTIONS			Lundsby Renewable Solutions A/S, Hjarbækvej 65, 8831 Løgstrup Tlf.: +45 96 49 43 00 Info@lundsby.dk This Drawing is subject to copyright and may not be reproduced without permission from Lundsby Renewable Solutions A/S
Project nr.: 1768 Drawing nr.: 9657			FORMAT: A1