






Structure of the tagging system

Structure of the component tagging

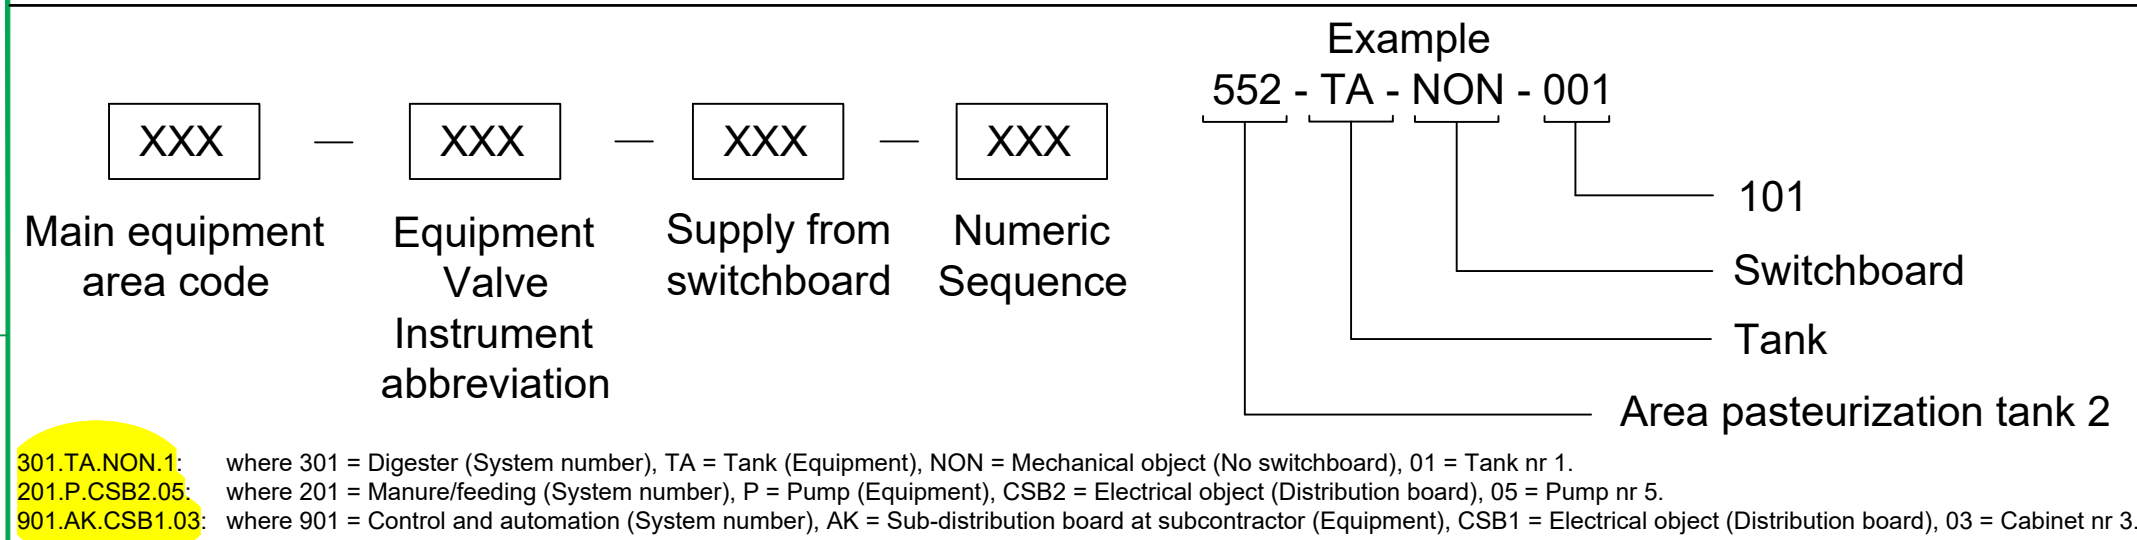

301 TA.NON.1: where 301 = Digester (System number), TA = Tank (Equipment), NON = Mechanical object (No switchboard), 01 = Tank nr 1.
201 P.CSB2.05: where 201 = Manure/feeding (System number), P = Pump (Equipment), CSB2 = Electrical object (Distribution board), 05 = Pump nr 5.
901 AK.CSB1.03: where 901 = Control and automation (System number), AK = Sub-distribution board at subcontractor (Equipment), CSB1 = Electrical object (Distribution board), 03 = Cabinet nr 3.

Lines

 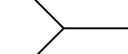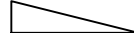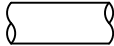Description	Symbol
Subcontractor scope	
Boundary line	
Page connector	
Start pipe - Not linked to page	
End pipe - Not linked to page	
Fald/ Slope	
Insulation	
Electrical Heat tracing	

Building/Area/Tank


Description	Code
Primary digester	PD
Secondary digester	SD
Digester storage	DST
Liquid manure tank	LMT
Liquid biomass tank	LBT
Outlet tank	OT
Blackwater tank	BWT
Tech building	TB
Admin building	ADB
Solid biomass building	SBB
Liquid biomass building	LBB
Plansilo	PS
Pump house	PH
Hygienization tanks	HYG
Flare	FLA
Stack	STA
Odour treatment facility	OD
Upgrade facility	UPG
Liquifaction facility	LIQ
Oil boiler	OB
Wood boiler	WB
Transformer	TR

Media code

Media	Pipe color	RBG color	Code
Heat Return		0,37,245	HR
Heat Supply		255,0,0	HS
Heat Hot Return		255,223,127	HHR
Heat Hot Supply		238,129,129	HHS
Cooling Supply		0,255,183	CS
Cooling Return		126,189,189	CR
Black Water		36,39,132	BW
CIP		253,53,223	CIP
Process Water		170,170,255	PW
Technical Water		69,78,104	TW
Drinking Water		0,0,129	DW
Drinking Water Hot		0,127,255	DWH
Condensate		108,163,208	CW
Steam		255,82,82	ST
Steam Condensate		189,0,0	STC
Liquid Manure (Slurry)		240,130,40	LM
Liquid Biomass (Substrat)		128,0,255	LB
Process Biomass		165,103,82	PB
Hygienized Biomass		169,130,0	HB
Recirculated Biomass		165,103,82	RCB
Ferric Chloride FeCl		145,255,71	FeCl
Ventilation Odour Treatment		199,199,199	VOT
Ventilation Fresh Air		199,199,199	VFA
Compressed Air		64,64,64	CA
Oxygen		0,128,255	O2
Raw Biogas		255,255,0	RB
Return/reject Gas		116,118,4	RG
Nature Gas		0,255,127	NG
Instrument Leader		Green	N/A

Structure of the pipeline tagging system

The pipetag consists of various information about the pipe
Full pipeline tag as shown below

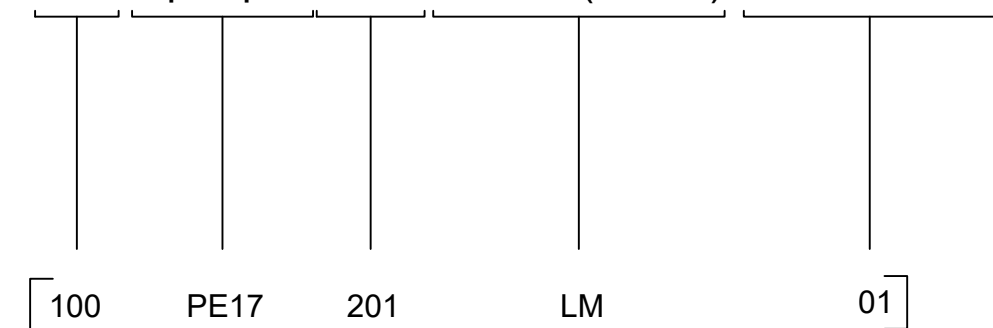

Example

Two (2) digits. Starts with 01
[01]

- Two (2) to four (4) characters (letters)
- [LM - Liquid manure]

Three (3) digits
[201 - Manure feeding in tank 1]

Pipe Spec name
[PE17 - PE100 SDR17]

Pipe size
DN indication for Metric pipes
OD indication for PE-pipe
[This example is OD 100 mm]

The pipe tag will be shown on the P&ID as follows:

PipeSpec-Size
Area-Service-Serialnumber

Example of line tag notation on P&ID: PE17-110
201-LM-01

Line color corresponding to table above.
The part below the pipeline is the Unique Line Tag.
Unique Line Tag is generated automatically when creating complete Line Tag.
Unique Line Tag is used by the P3D system when designing pipes in the 3D model and when generating Isometrics.

Rev. Nr.:	Rev. Dato:	Rev. Description:
Builder:	ST1	
Project:	SLK	
Subject:	PID Legend	
	Rev. 6	
Int.: MDC	QC.: CM	APP.: Date: 15-10-2025




Lundbys
RENEWABLE SOLUTIONS

Lundbys Renewable Solutions A/S, Hjarbakvej 65, 8831 Logstrup
Tlf.: +45 96 49 43 00 Info@lundbs.dk
This Drawing is subject to copyright and may not be reproduced
without permission from Lundbys Renewable Solutions A/S


Project nr.: 1768

Drawing nr.:
PID Legend


FORMAT: A1

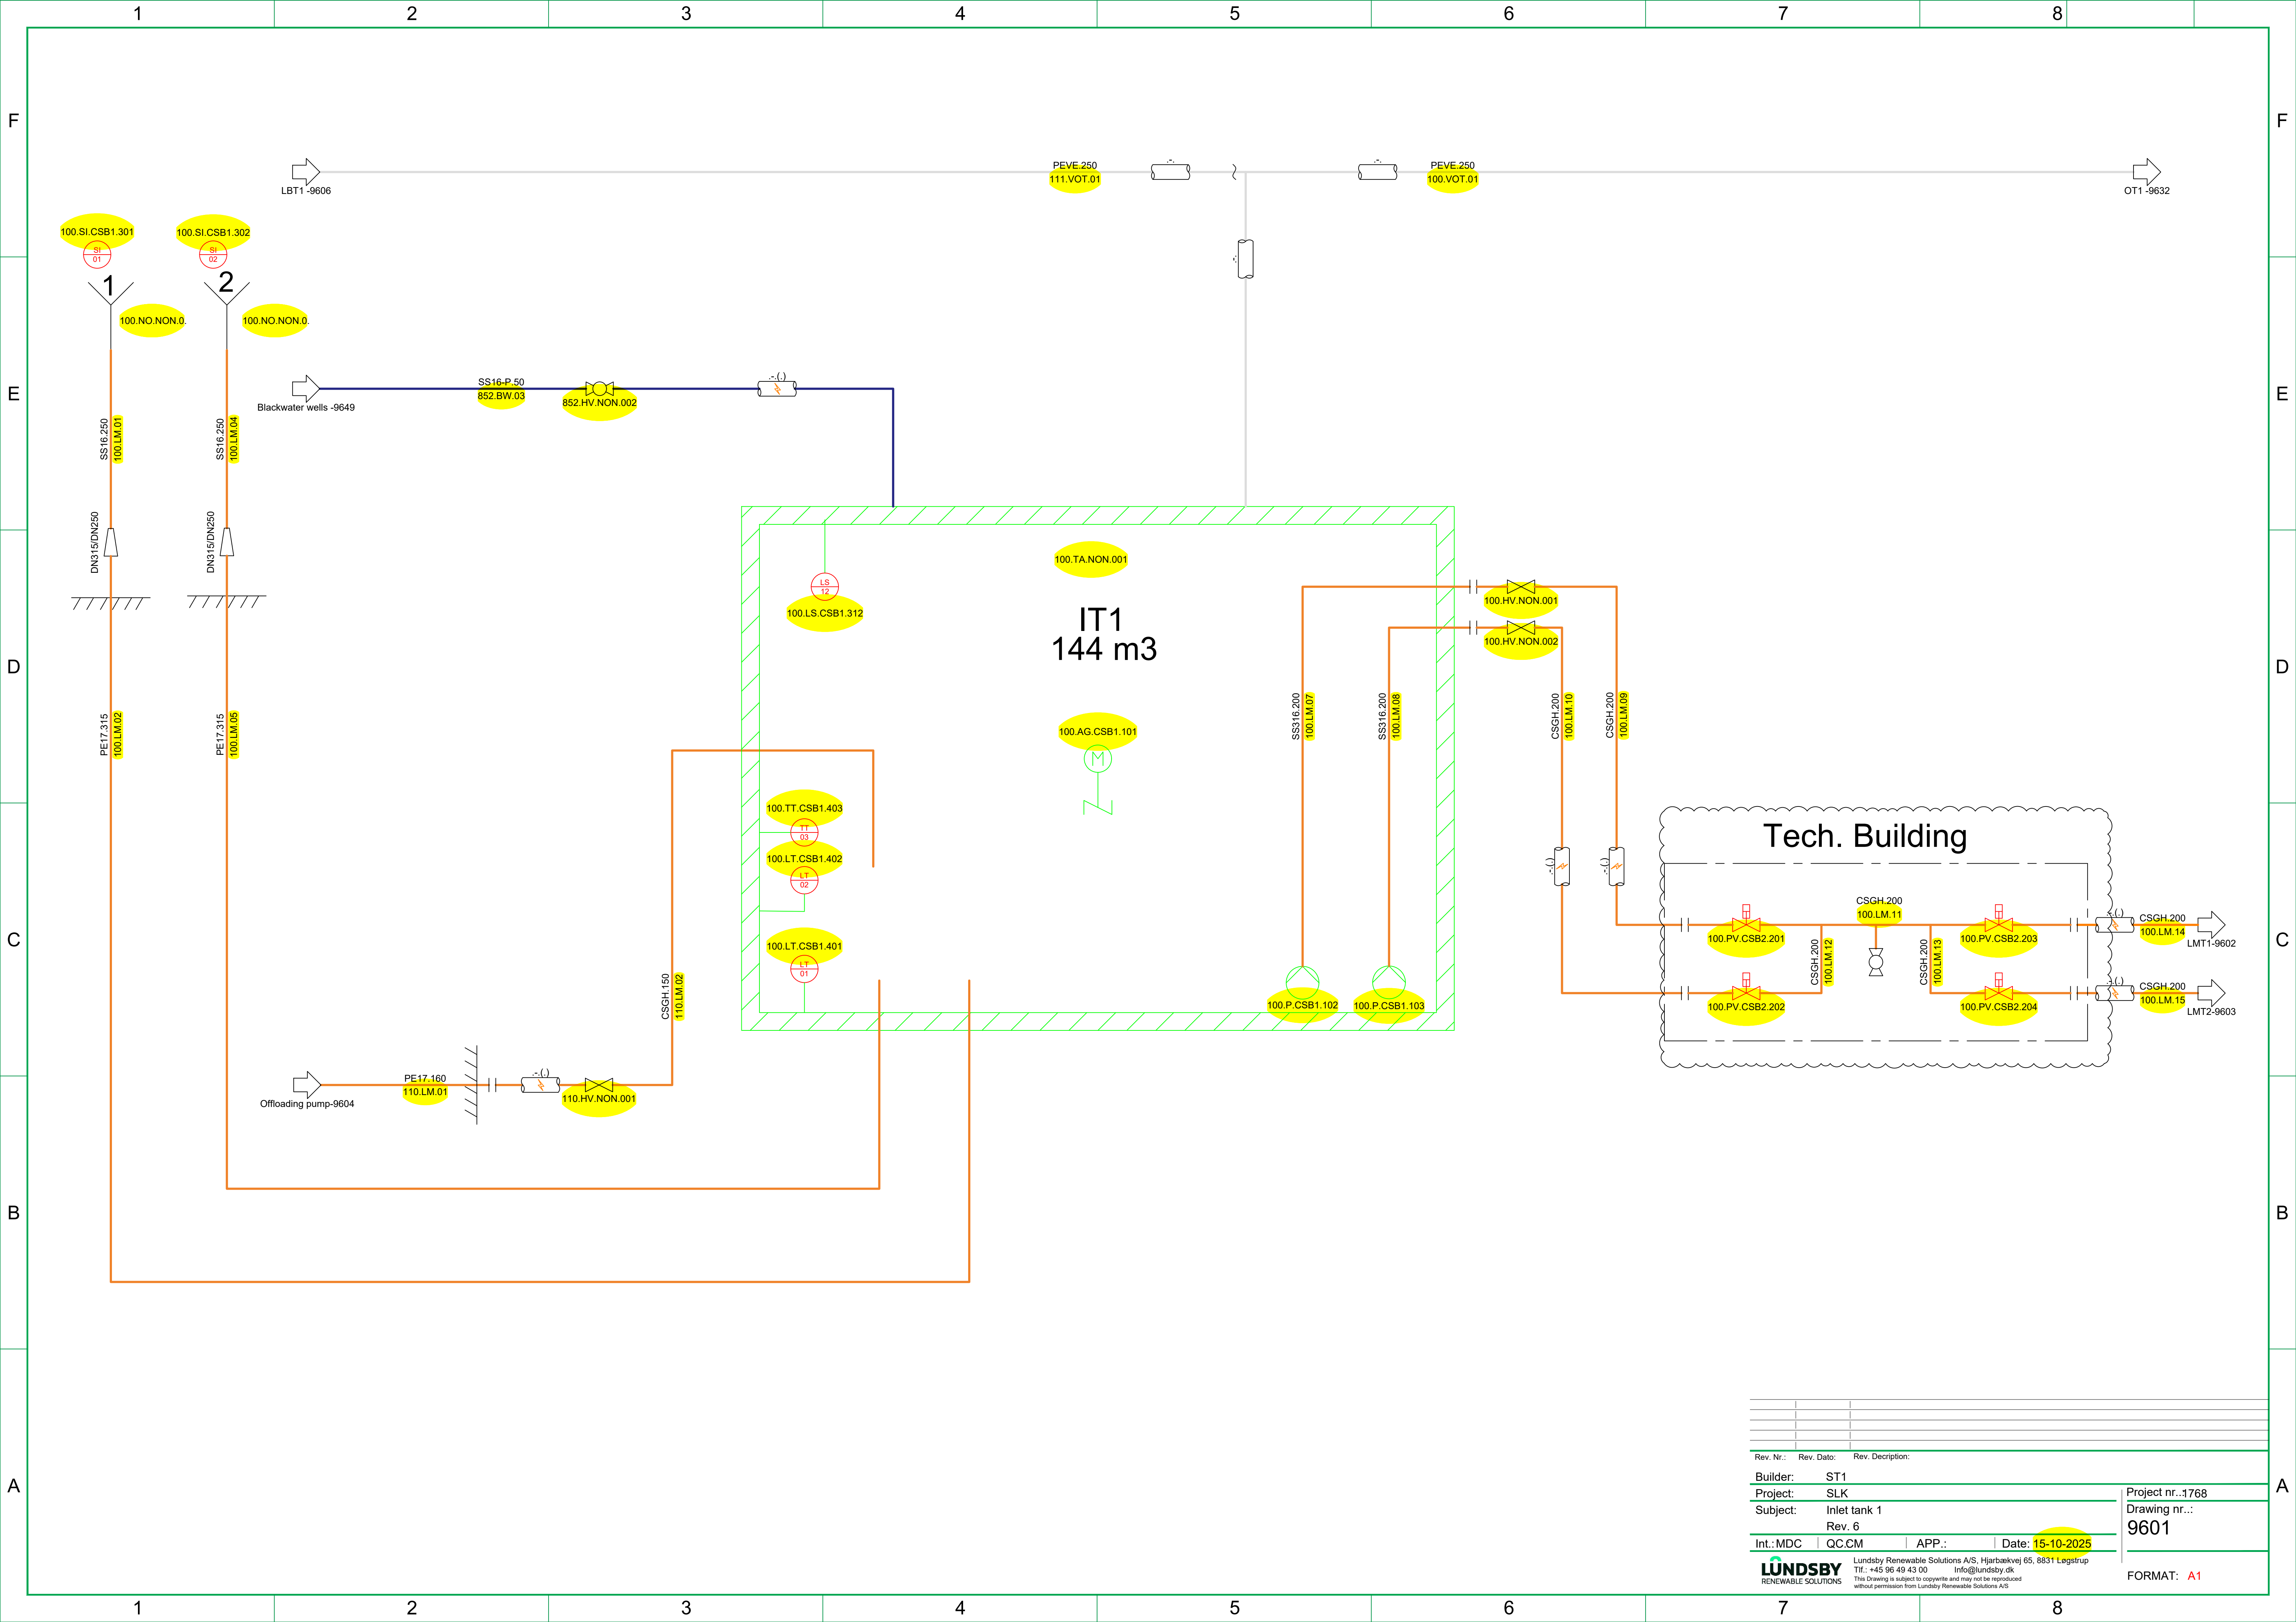


Rev. Nr.:	Rev. Dato:	Rev. Description:
Builder:	ST1	
Project:	SLK	
Subject:	Inlet tank 1	
Rev. 6		
Int.:MDC	QC:CM	APP.:
Date:	15-10-2025	
LUNDSBY RENEWABLE SOLUTIONS	Lundsby Renewable Solutions A/S, Hjarbækvej 65, 8831 Løgstrup Tlf.: +45 96 49 43 00 Info@lundsby.dk This drawing is subject to copyright and may not be reproduced without permission from Lundsby Renewable Solutions A/S	
Project nr.:1768		Drawing nr.: 9601
FORMAT: A1		

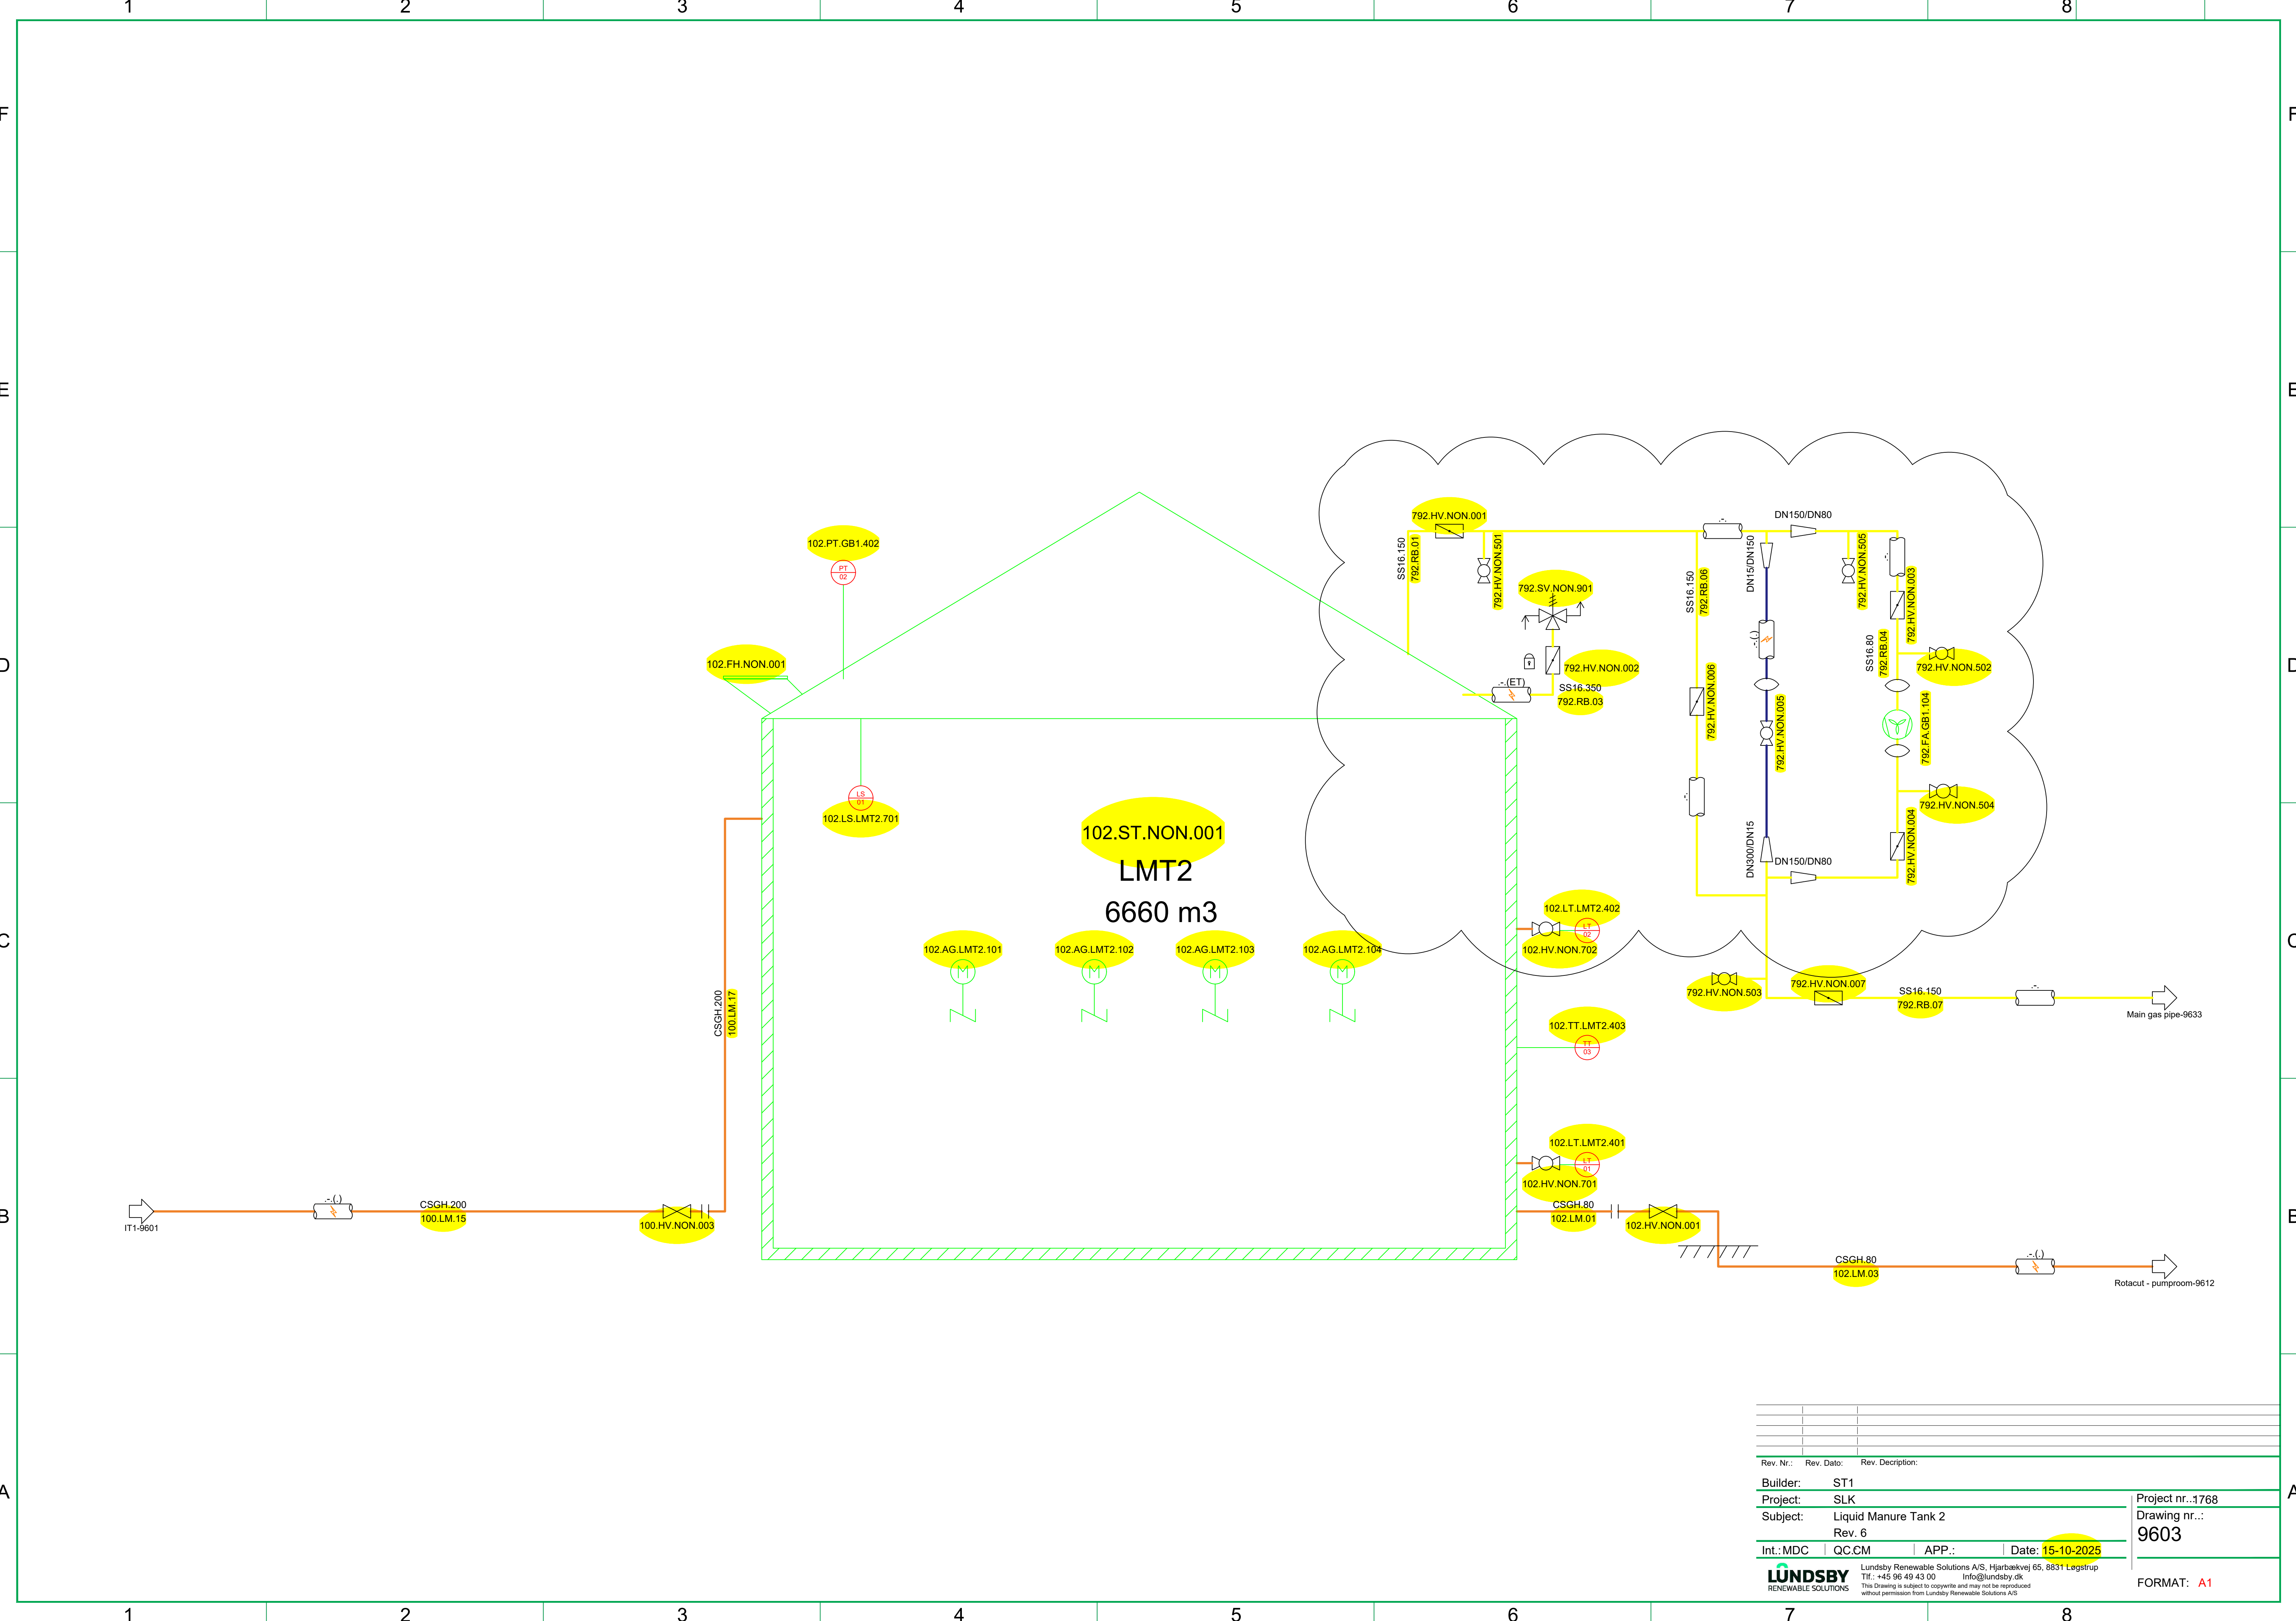


Rev. Nr.:	Rev. Dato:	Rev. Description:
Builder:	ST1	
Project:	SLK	
Subject:	Liquid Manure Tank 2	
Rev. 6		
Int.:MDC	QC:CM	APP.:
Date:	15-10-2025	
LUNDSBY RENEWABLE SOLUTIONS		
Lundsby Renewable Solutions A/S, Hjarbækvej 65, 8831 Løgstrup Tlf.: +45 96 49 43 00 Info@lundsby.dk This Drawing is subject to copyright and may not be reproduced without permission from Lundsby Renewable Solutions A/S		
Project nr.:1768		Drawing nr.: 9603
FORMAT: A1		

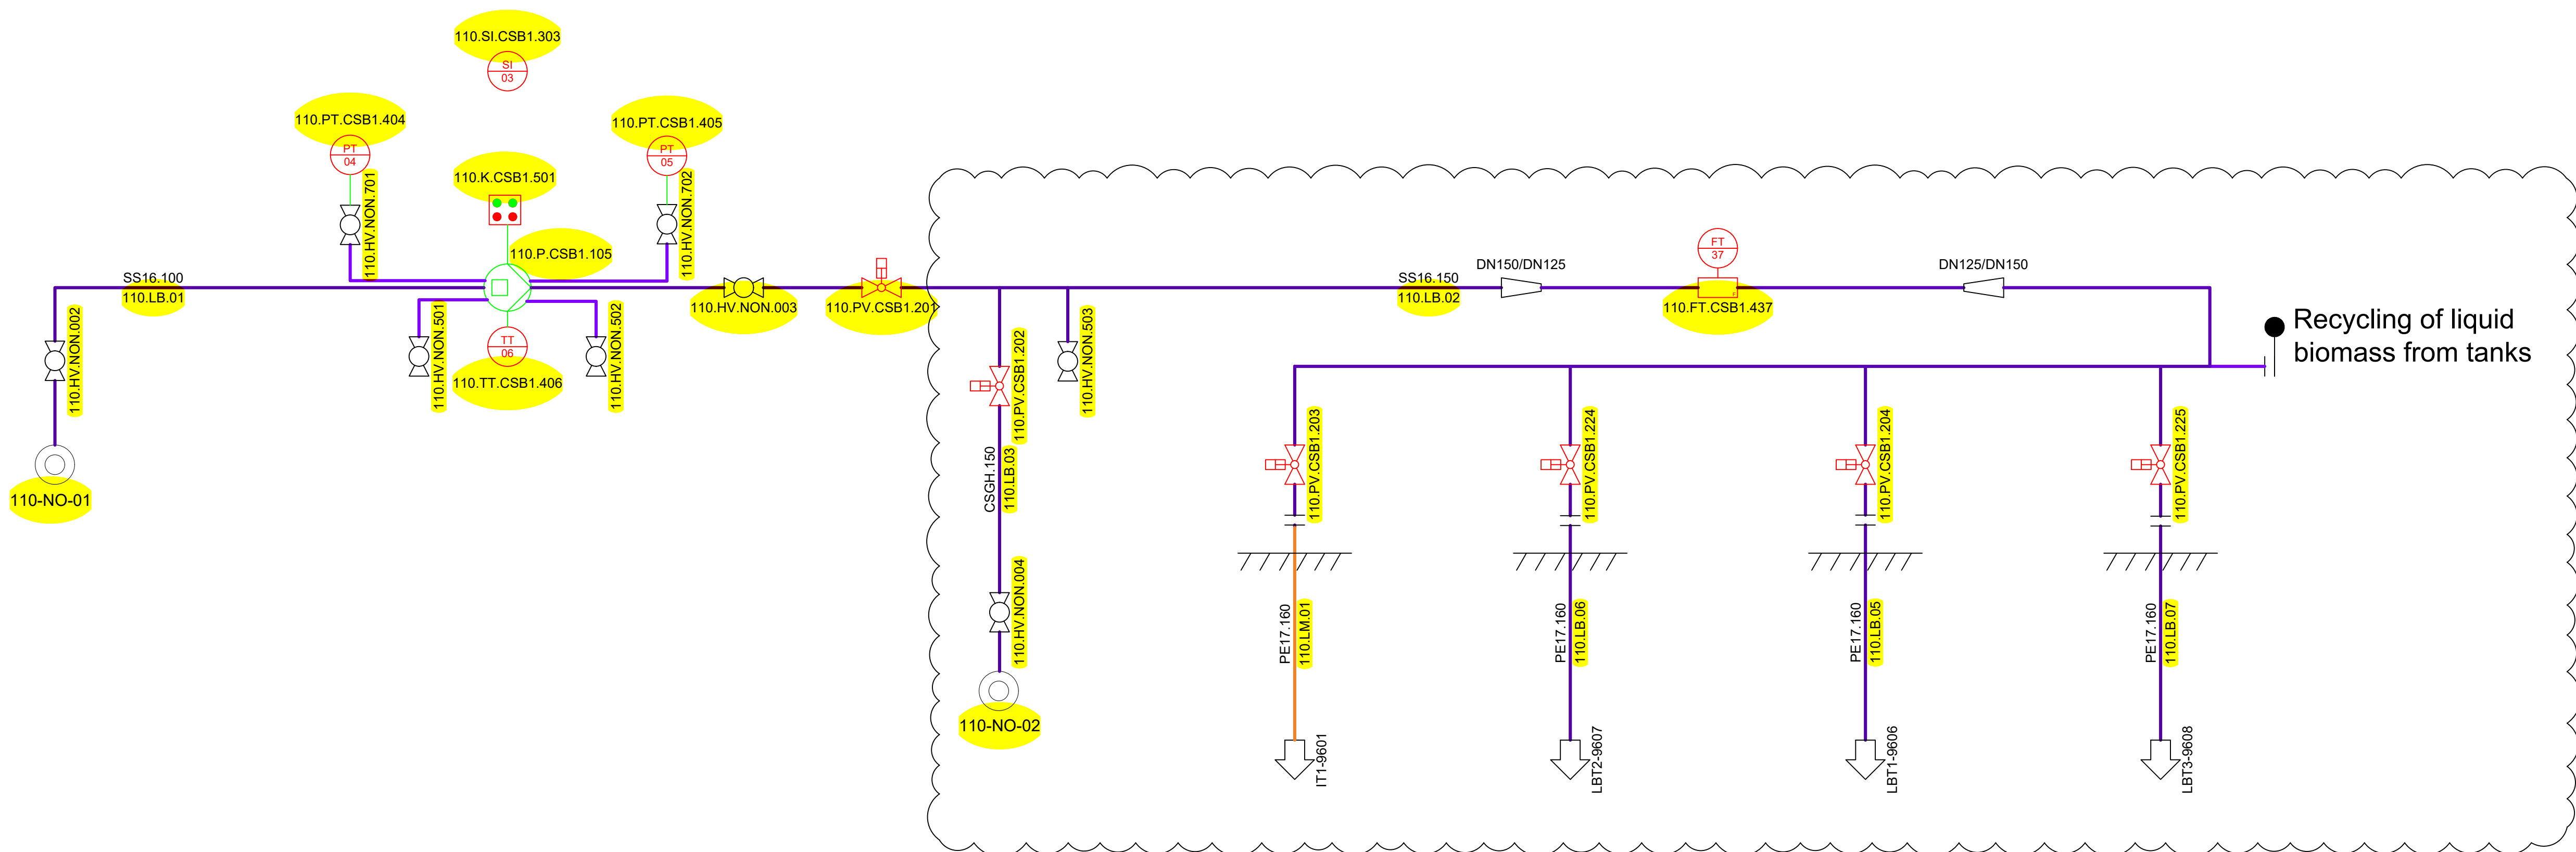


Rev. Nr.:	Rev. Dato:	Rev. Description:	
Builder:	ST1		
Project:	SLK		
Subject:	Liquid biomass delivery pump		
Rev. 6			
Int.:MDC	QC.CM	APP.:	Date: 15-10-2025
LUNDSBY RENEWABLE SOLUTIONS			Lundsby Renewable Solutions A/S, Hjarbækvej 65, 8831 Løgstrup Tlf.: +45 96 49 43 00 Info@lundsby.dk This Drawing is subject to copyright and may not be reproduced without permission from Lundsby Renewable Solutions A/S
Project nr.:1768 Drawing nr.: 9604			FORMAT: A1

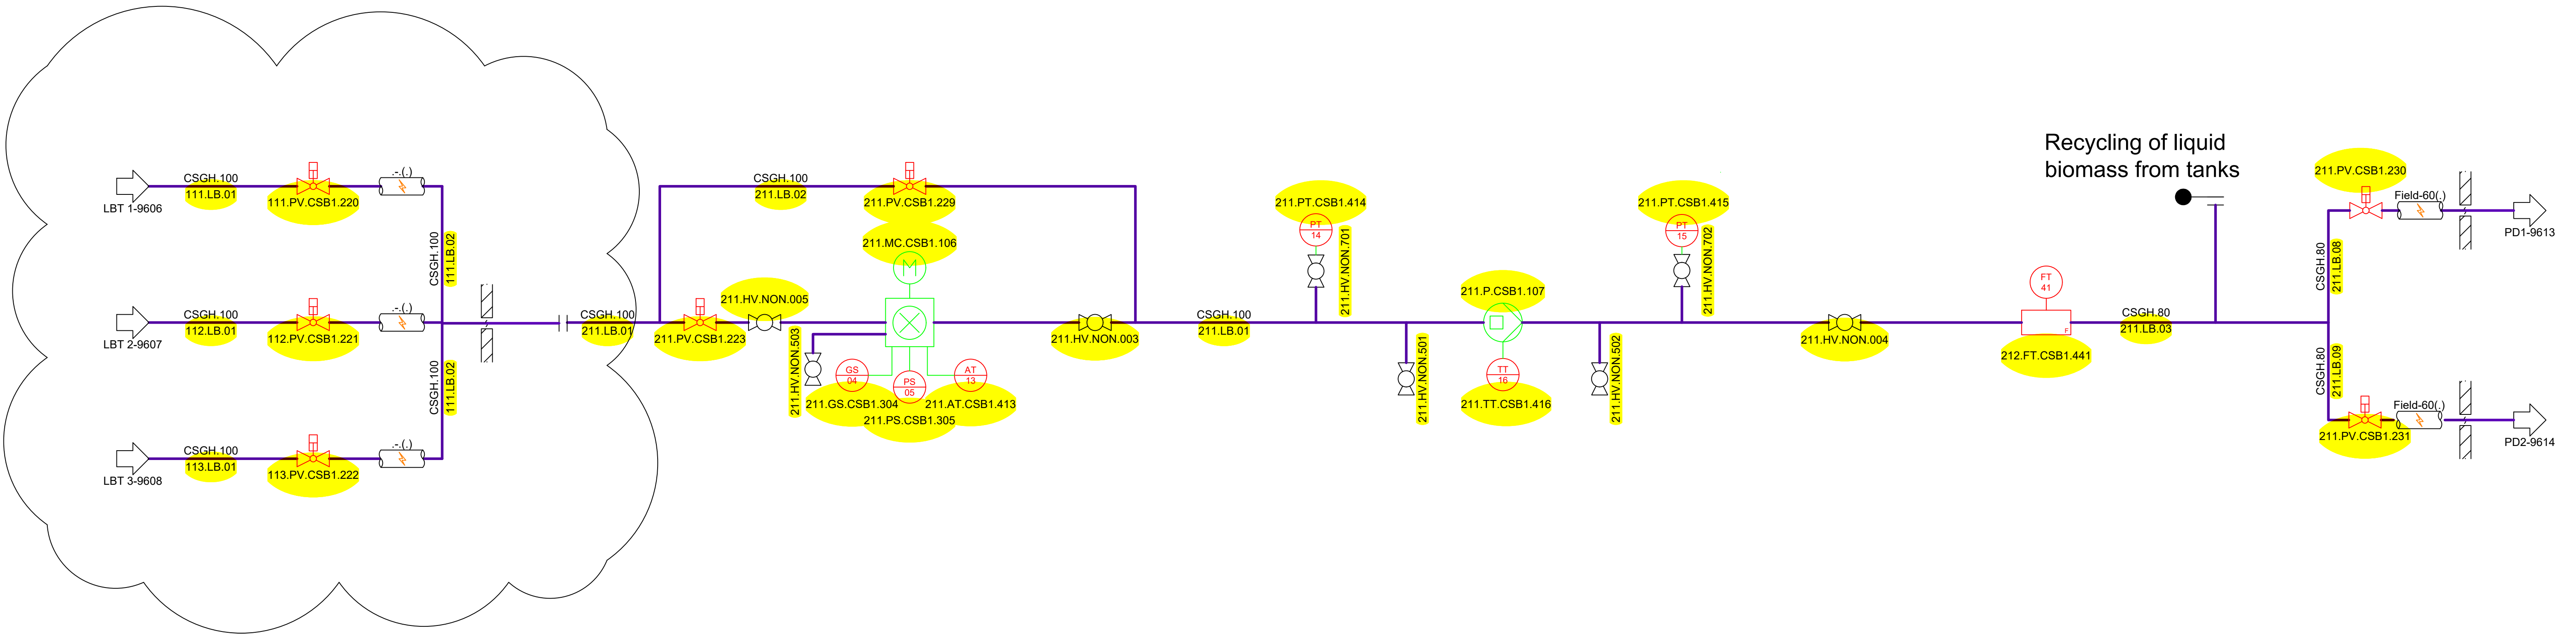


Rev. Nr.:	Rev. Dato:	Rev. Description:
Builder:	ST1	
Project:	SLK	
Subject:	Liquid biomass pump 1	
Rev. 6		
Int.:MDC	QC.CM	APP.:
Date:	15-10-2025	
LUNDSBY RENEWABLE SOLUTIONS		
Lundsby Renewable Solutions A/S, Hjarbækvej 65, 8831 Løgstrup Tlf.: +45 96 49 43 00 Info@lundsby.dk This Drawing is subject to copyright and may not be reproduced without permission from Lundsby Renewable Solutions A/S		
Project nr.:1768 Drawing nr.: 9605		FORMAT: A1

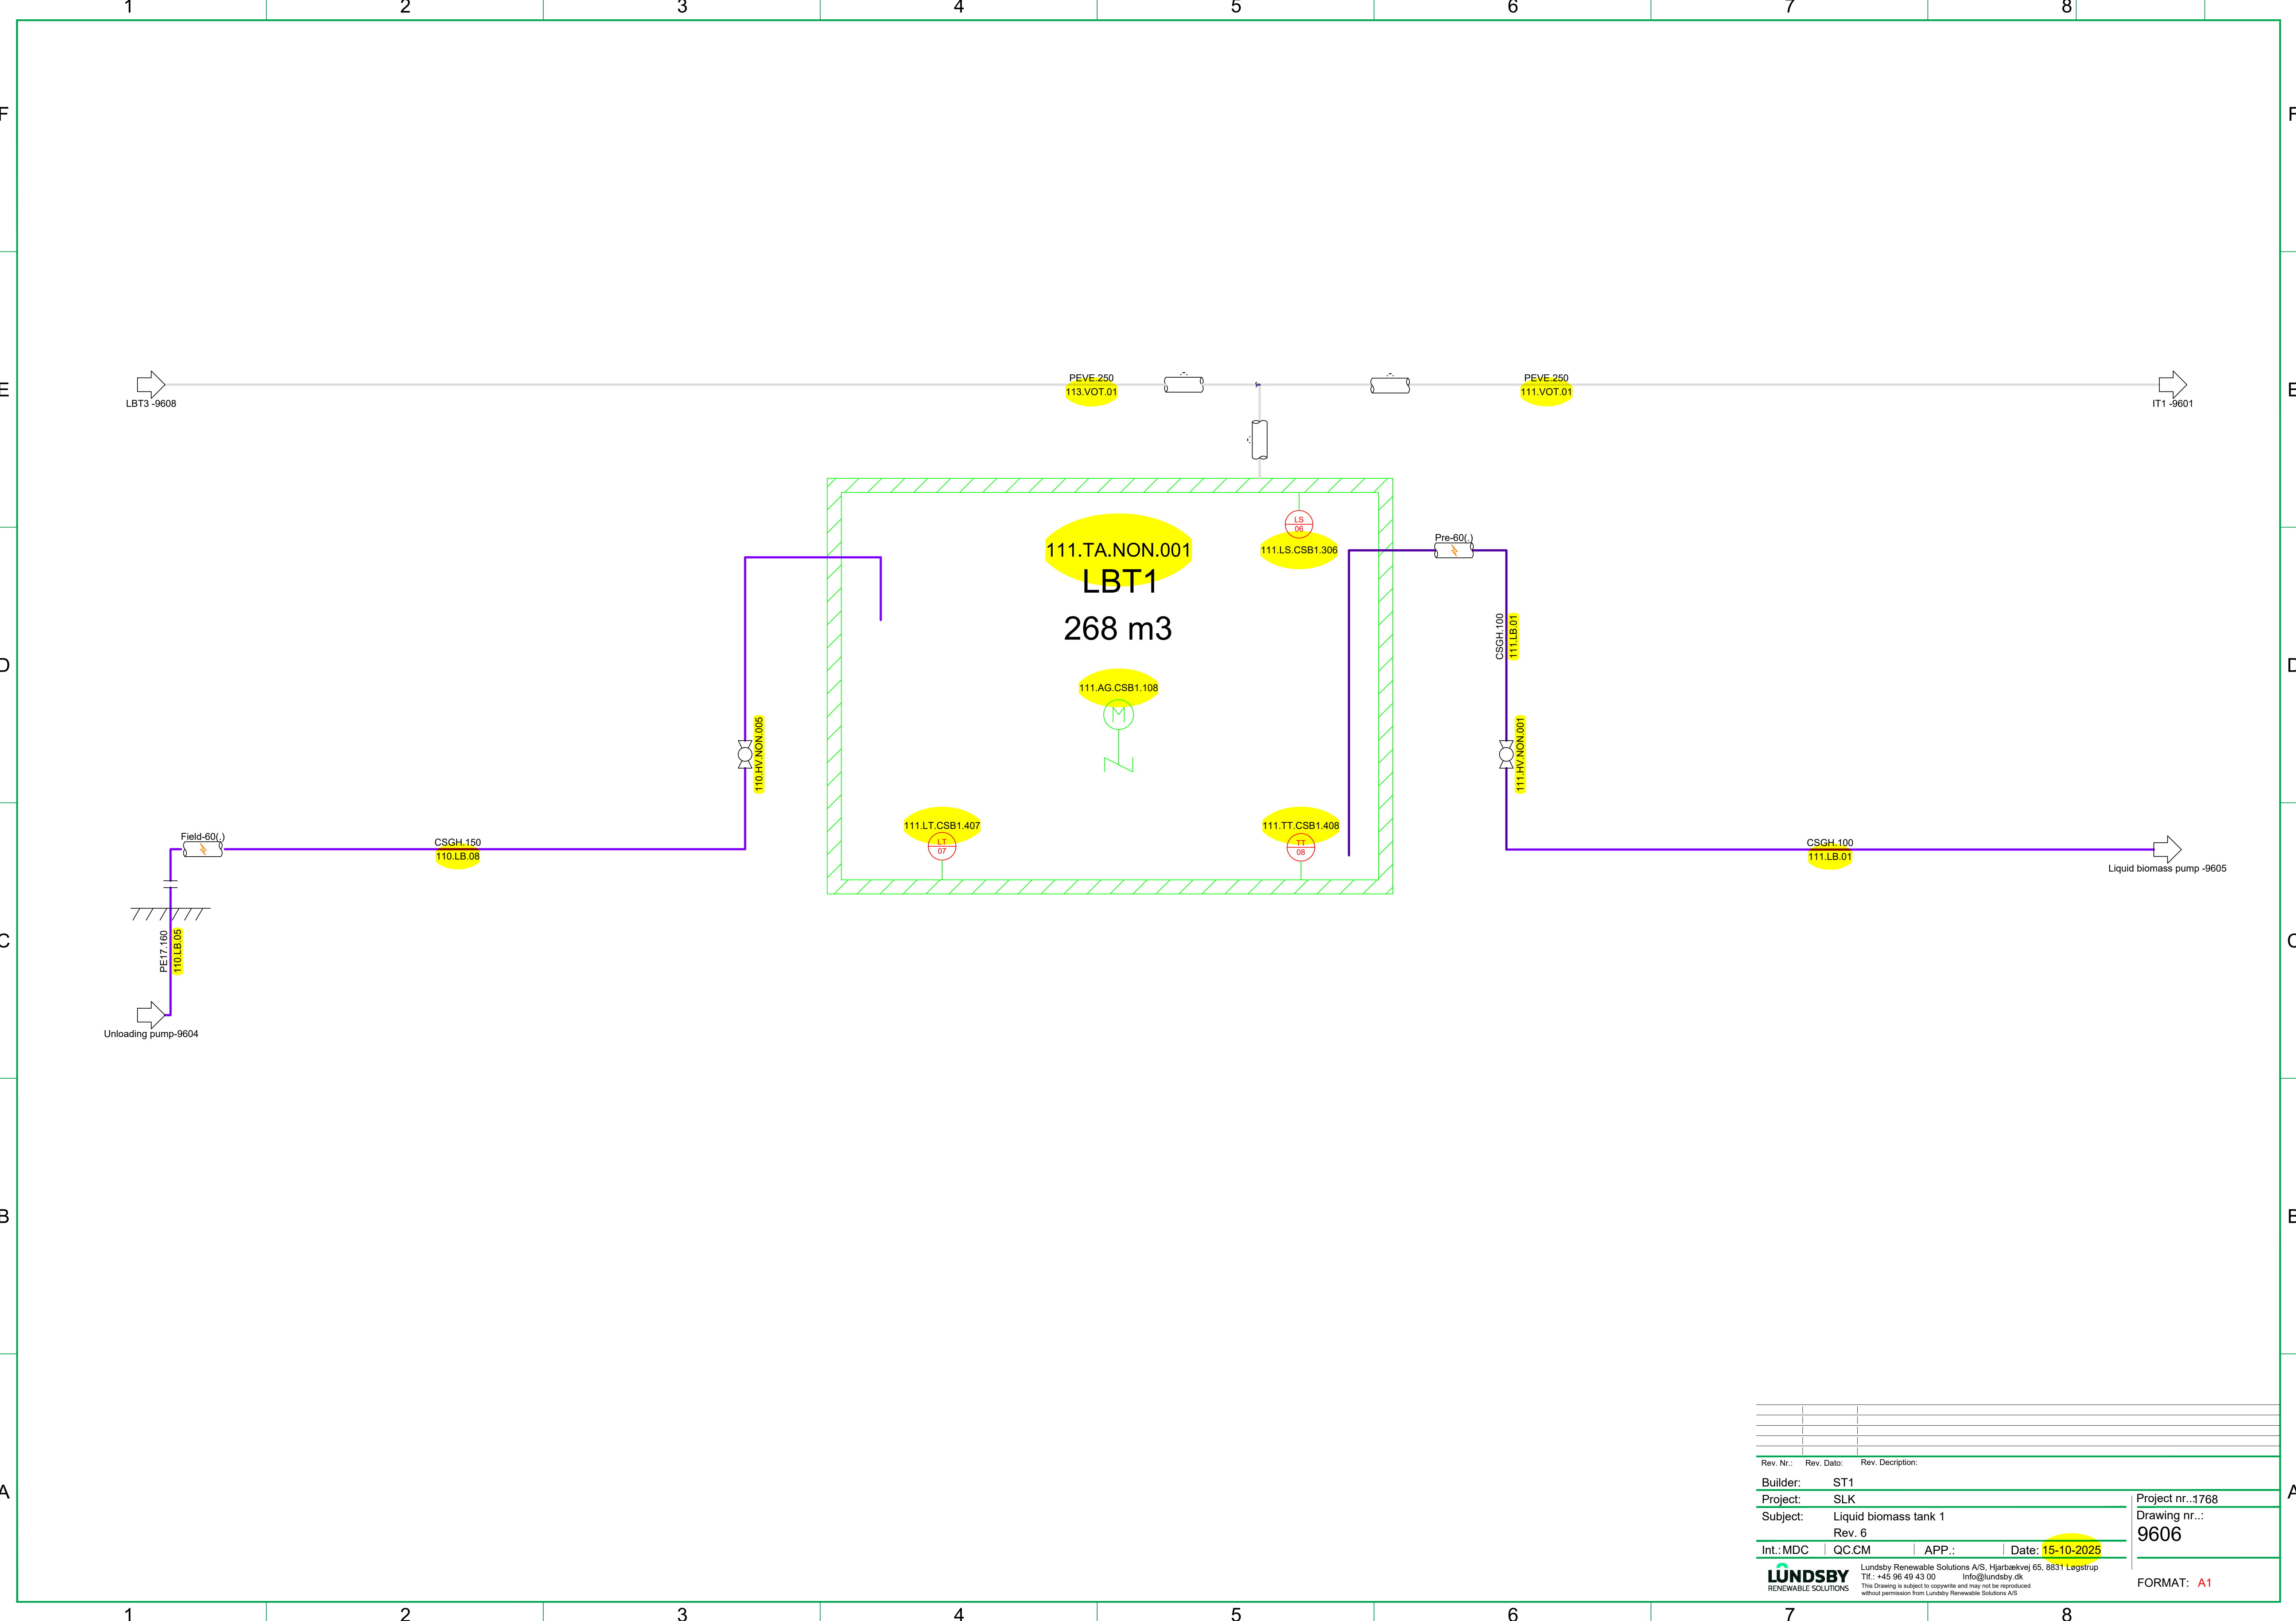


Rev. Nr.:	Rev. Dato:	Rev. Description:	
Builder:	ST1		
Project:	SLK		
Subject:	Liquid biomass tank 1		
	Rev. 6		
Int.:MDC	QC.CM	APP.:	Date: 15-10-2025
LUNDSBY RENEWABLE SOLUTIONS			Lundsby Renewable Solutions A/S, Hjarbækvej 65, 8831 Løgstrup Tlf.: +45 96 49 43 00 Info@lundsby.dk This Drawing is subject to copyright and may not be reproduced without permission from Lundsby Renewable Solutions A/S
			Project nr...1768 Drawing nr...: 9606 FORMAT: A1

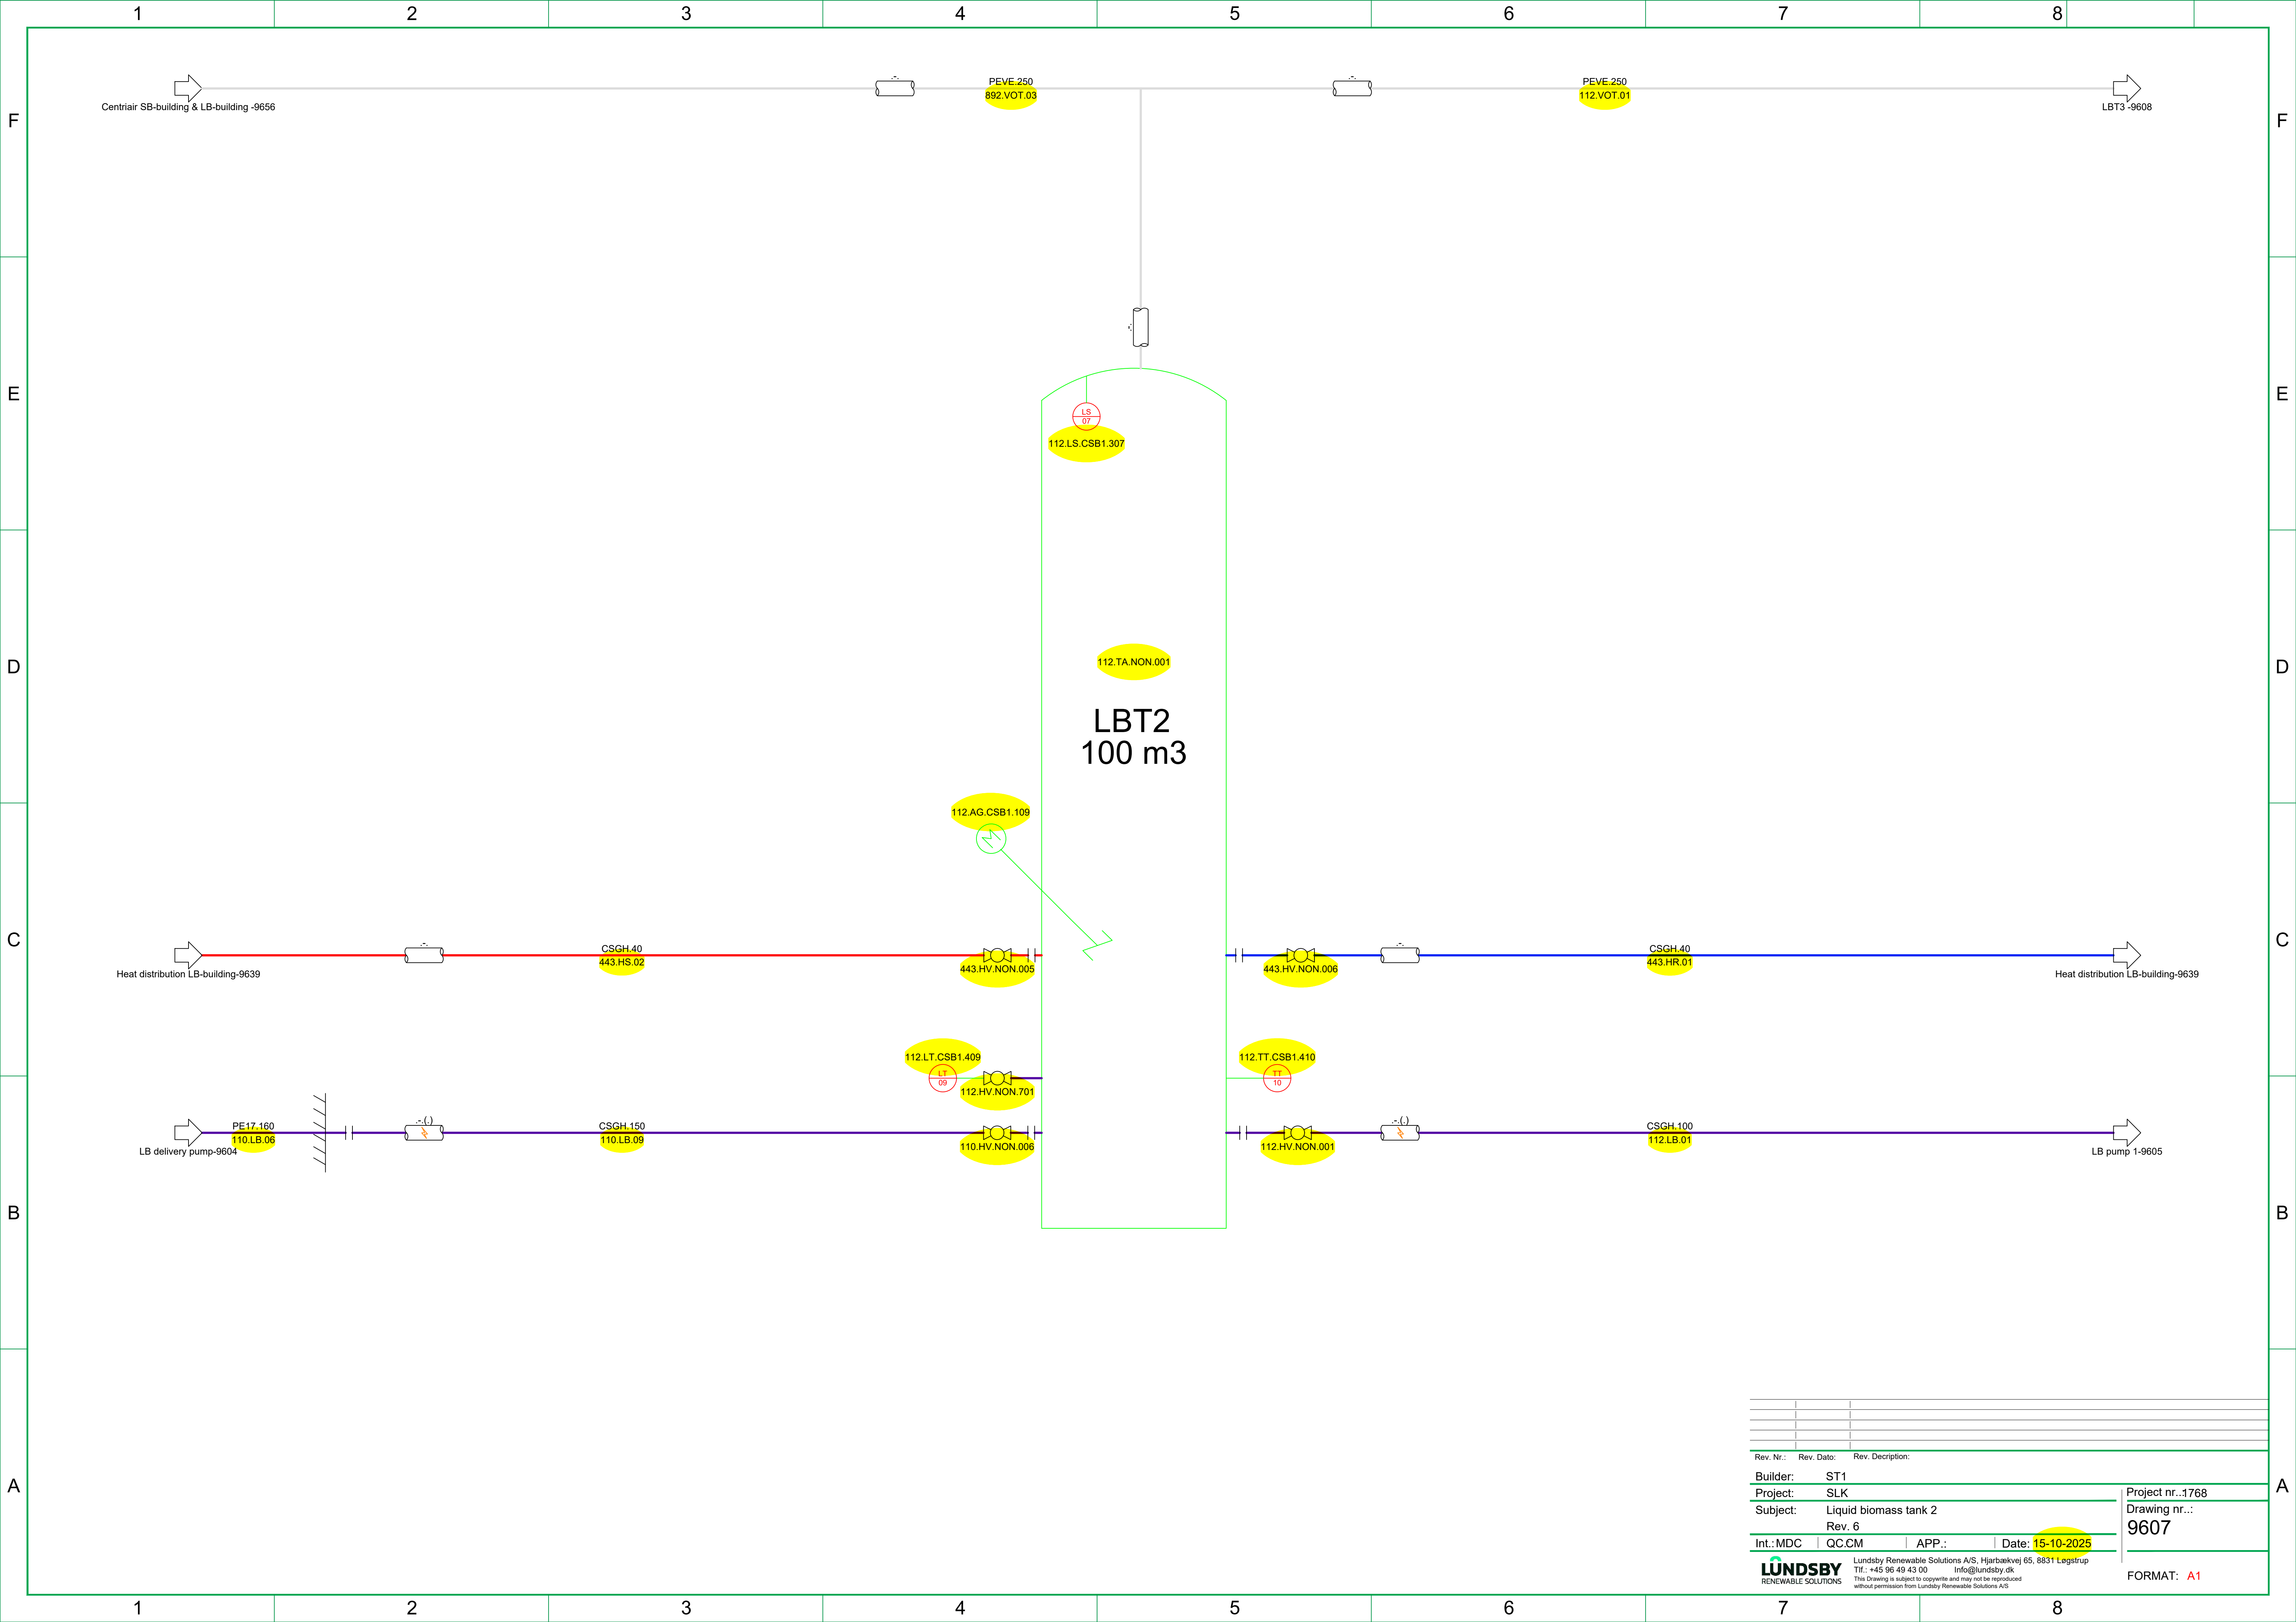


Rev. Nr.:	Rev. Dato:	Rev. Description:	
Builder:	ST1		
Project:	SLK		
Subject:	Liquid biomass tank 2		
	Rev. 6		
Int.:MDC	QC:CM	APP.:	Date: 15-10-2025
LUNDSBY RENEWABLE SOLUTIONS			Lundsby Renewable Solutions A/S, Hjarbækvej 65, 8831 Løgstrup Tlf.: +45 96 49 43 00 Info@lundsby.dk This Drawing is subject to copyright and may not be reproduced without permission from Lundsby Renewable Solutions A/S
			Project nr...1768 Drawing nr...: 9607
			FORMAT: A1

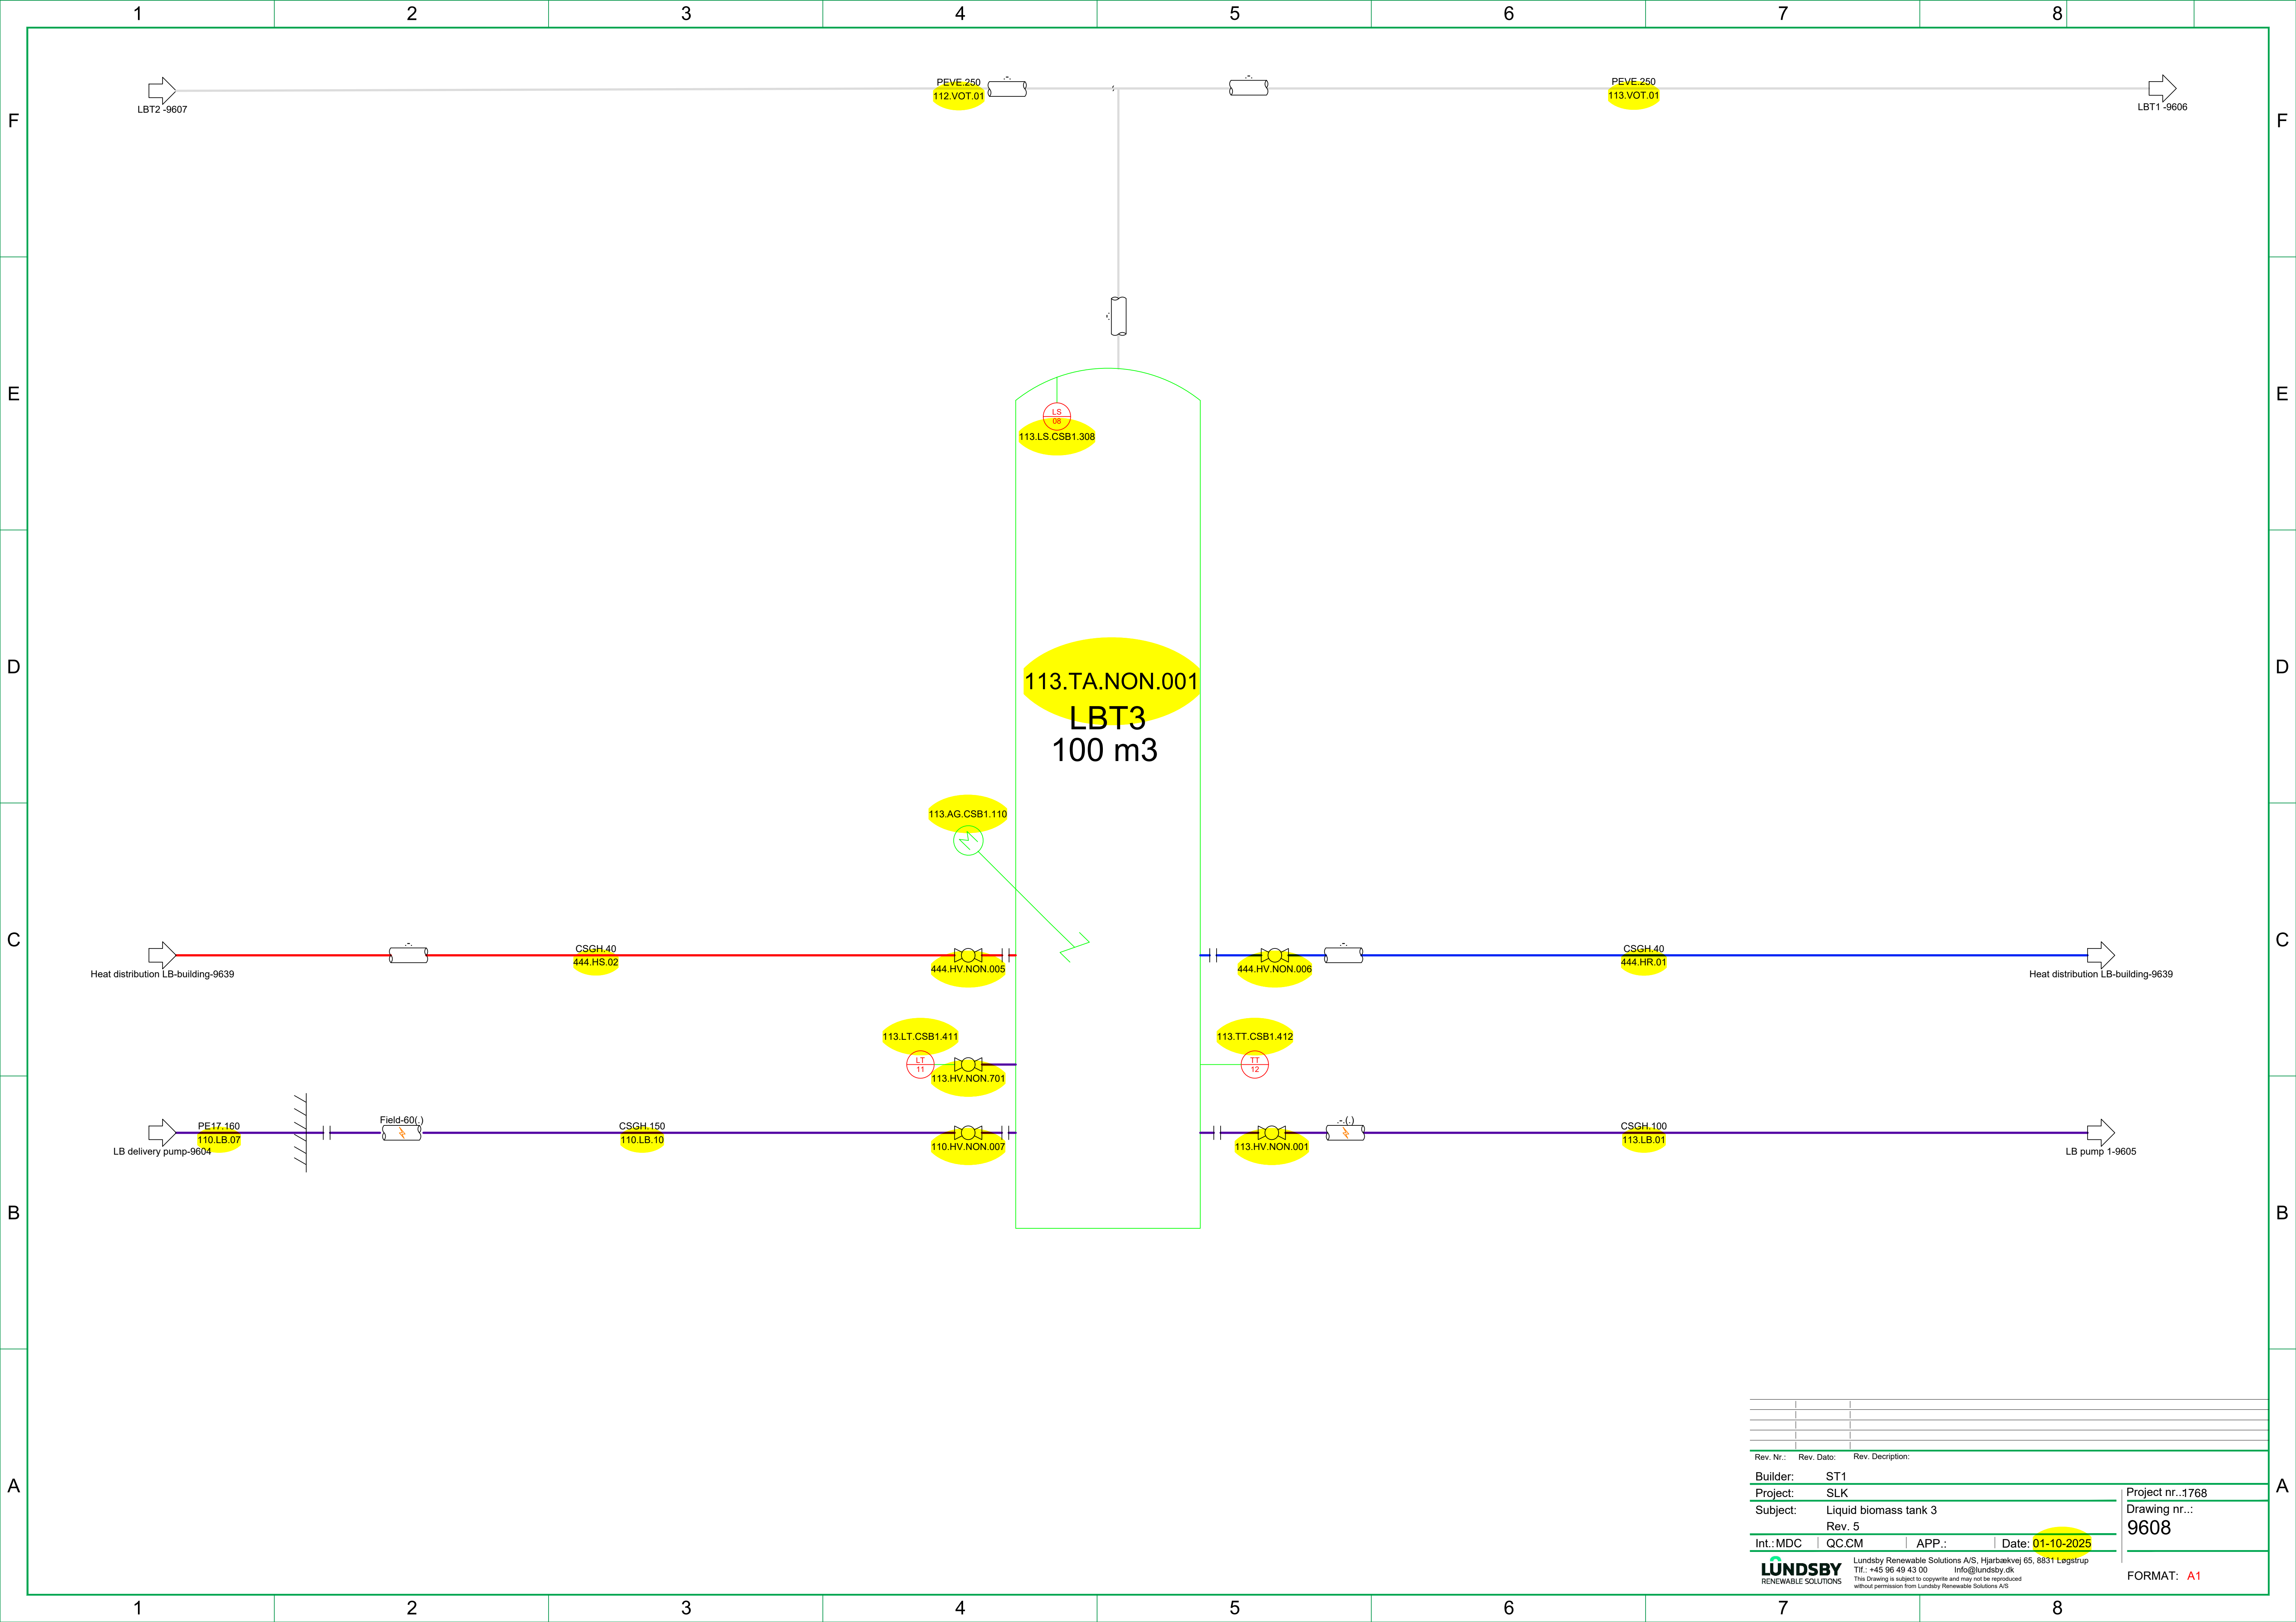

Rev. Nr.:	Rev. Dato:	Rev. Description:
Builder:	ST1	
Project:	SLK	
Subject:	Liquid biomass tank 3	
Rev. 5		
Int.:MDC	QC:CM	APP.:
Date:	01-10-2025	
LUNDSBY RENEWABLE SOLUTIONS		
Lundsby Renewable Solutions A/S, Hjarbækvej 65, 8831 Løgstrup Tlf.: +45 96 49 43 00 Info@lundsby.dk This Drawing is subject to copyright and may not be reproduced without permission from Lundsby Renewable Solutions A/S		
Project nr.:1768 Drawing nr.: 9608		FORMAT: A1

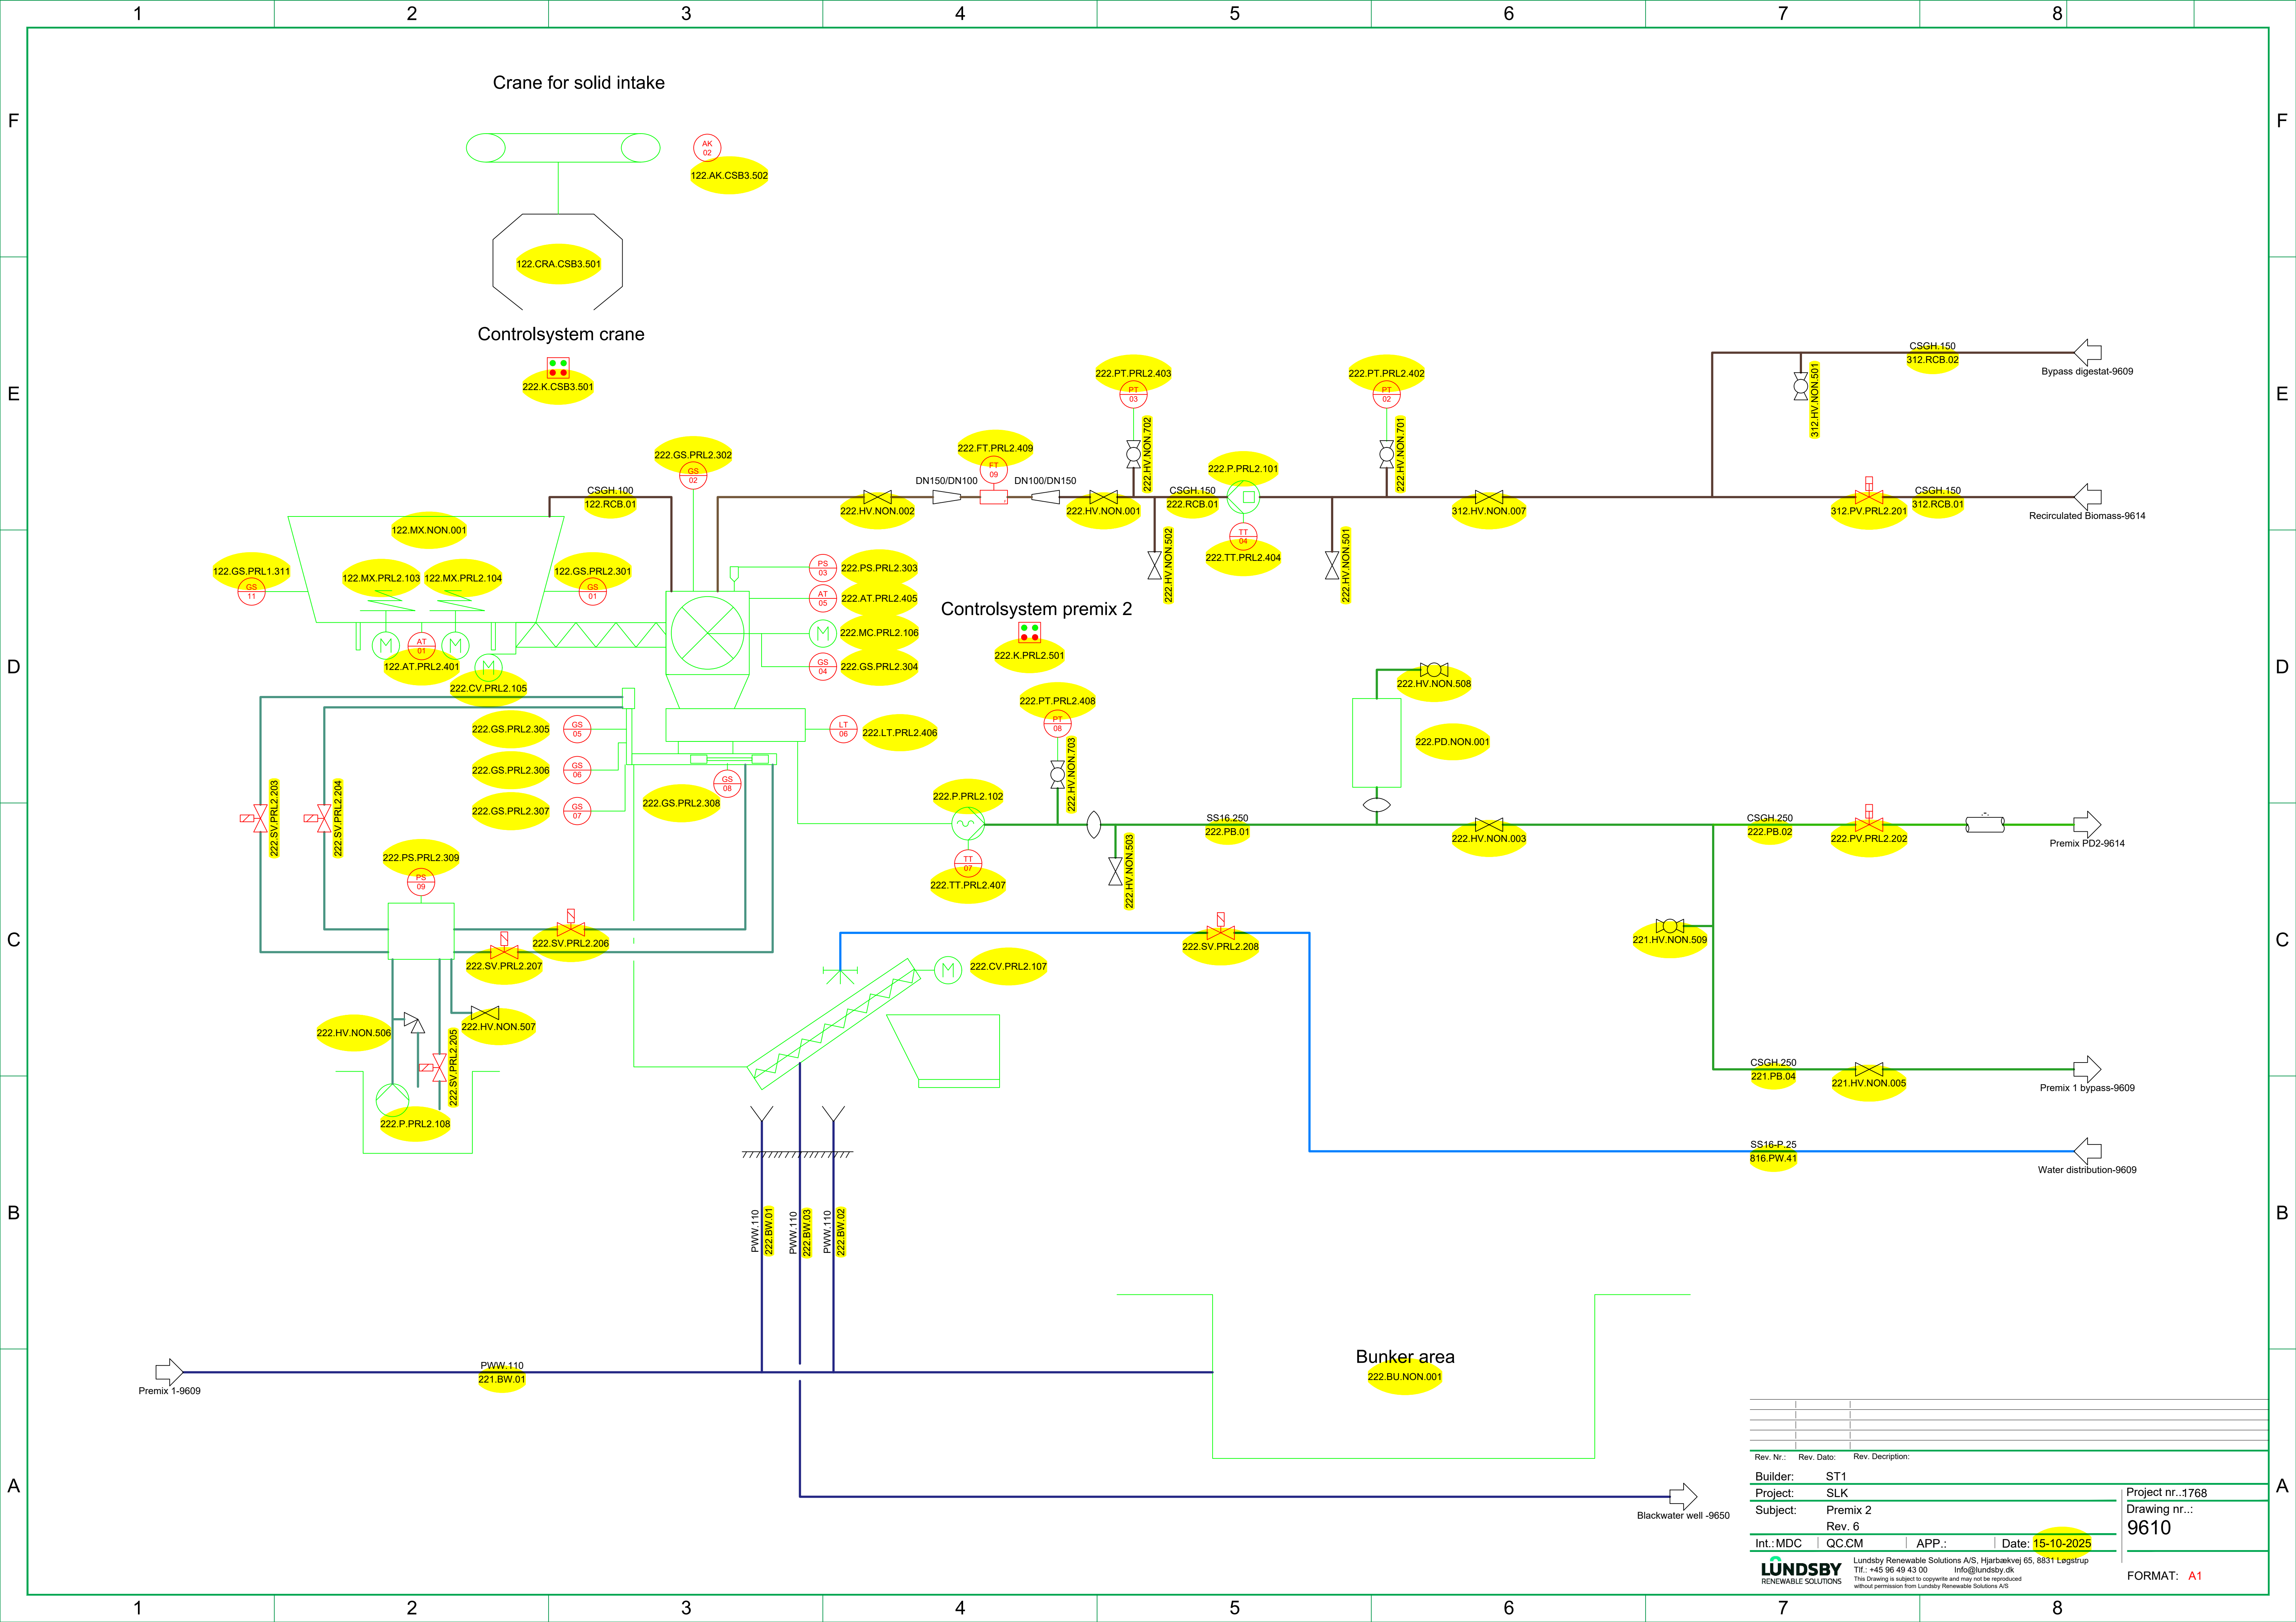

Rev. Nr.:	Rev. Dato:	Rev. Description:
Builder:	ST1	
Project:	SLK	
Subject:	Premix 2	
Int.:MDC	QC.CM	APP.:
Date:	15-10-2025	
LUNDSBY RENEWABLE SOLUTIONS		
Lundsby Renewable Solutions A/S, Hjarbækvej 65, 8831 Løgstrup Tlf.: +45 96 49 43 00 Info@lundsby.dk This Drawing is subject to copyright and may not be reproduced without permission from Lundsby Renewable Solutions A/S		
Project nr.:1768 Drawing nr.: 9610		FORMAT: A1

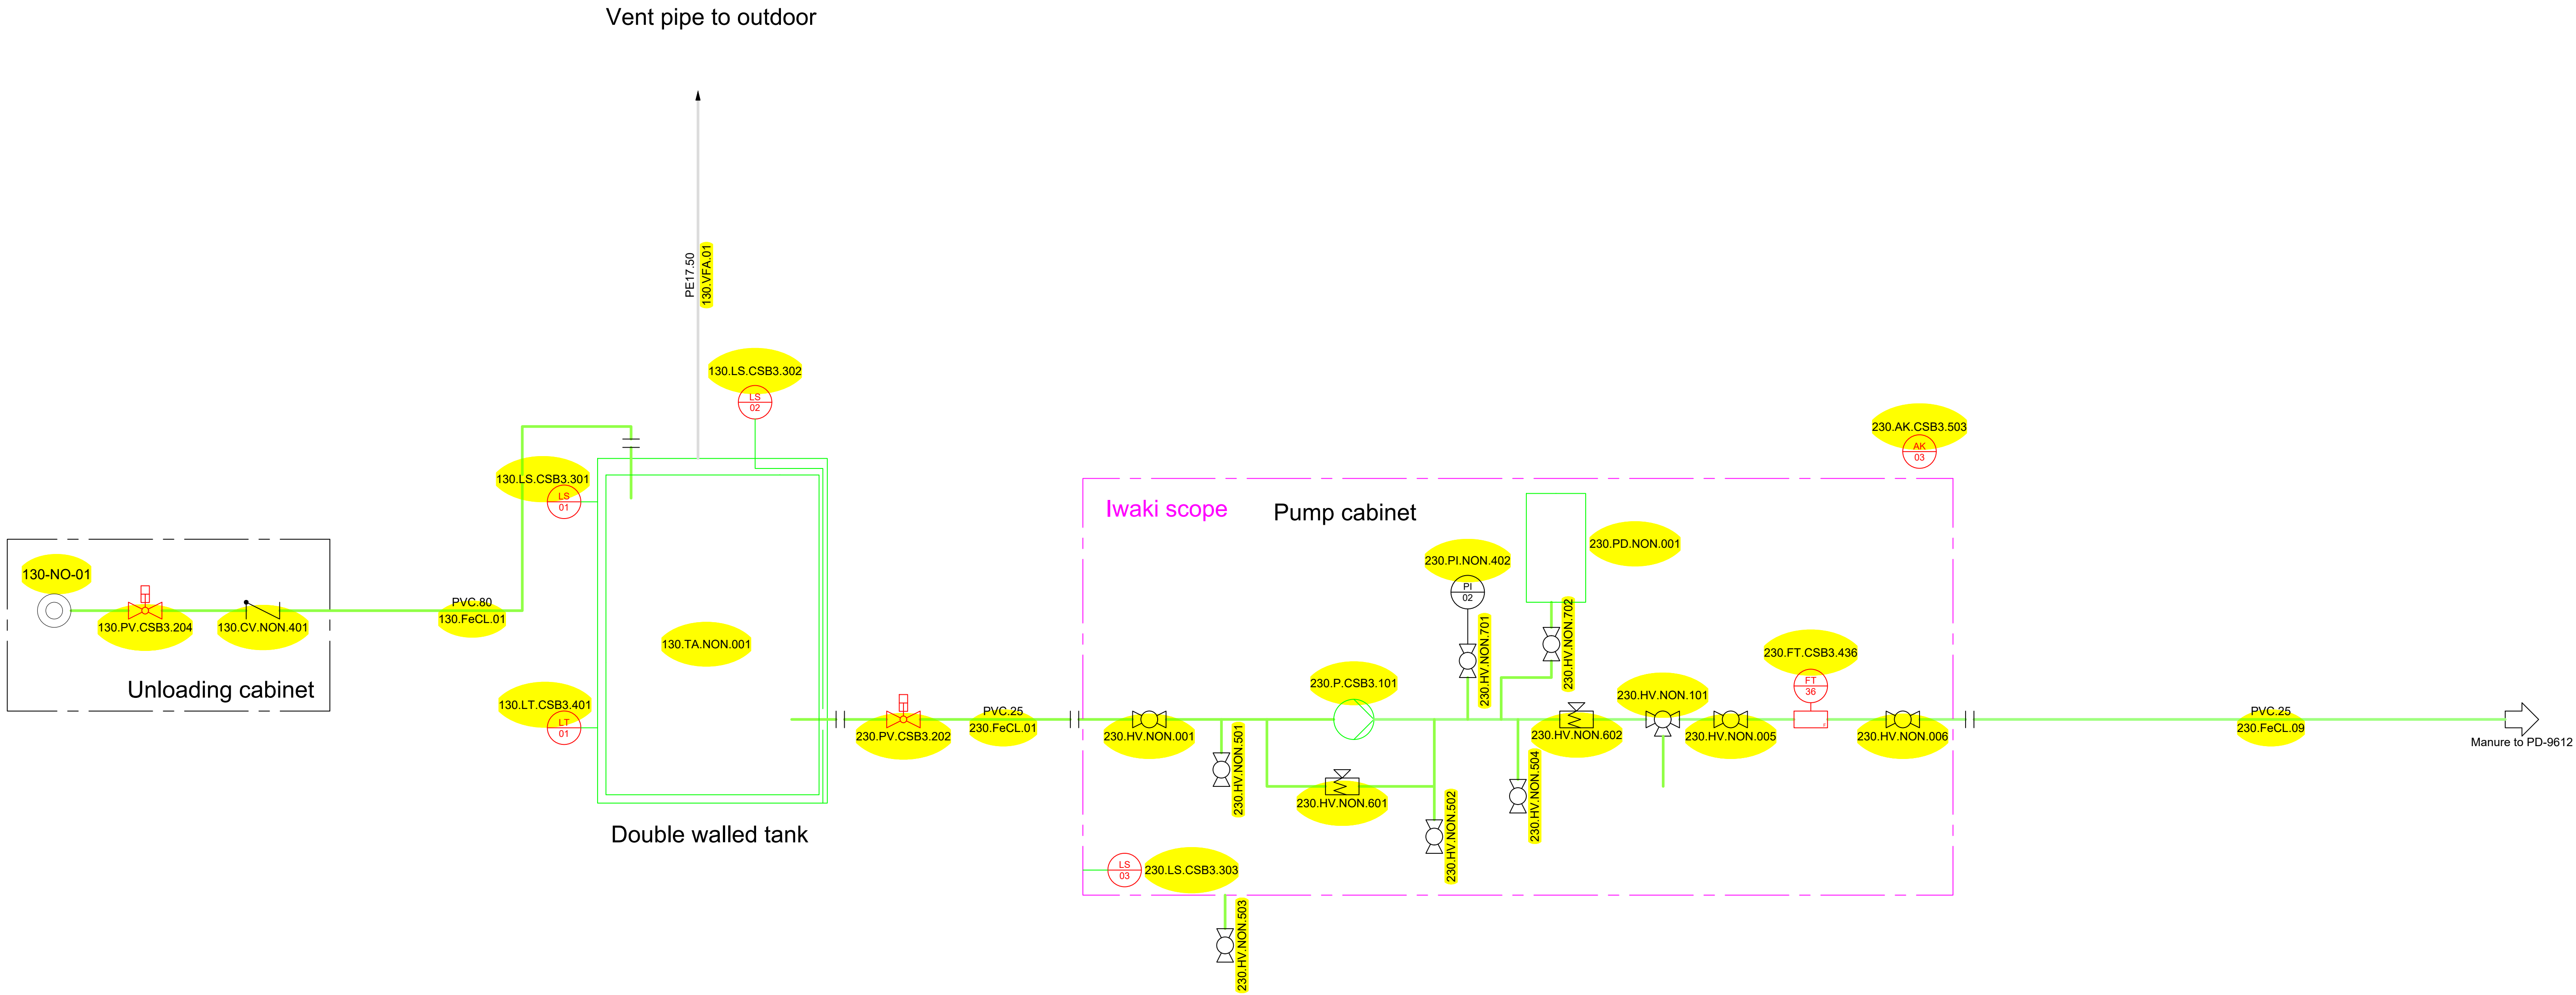

Rev. Nr.: Rev. Dato: Rev. Description:					
Builder:		ST1			
Project:		SLK			
Subject:		FECL system			
		Rev. 6			
Int.: MDC		QC.CM	APP.:	Date: 15-10-2025	
Lundsby Renewable Solutions A/S, Hjarbækvej 65, 8831 Løgstrup Tlf.: +45 96 49 43 00 Info@lundsby.dk This Drawing is subject to copyright and may not be reproduced without permission from Lundsby Renewable Solutions A/S					


Project nr.:1768

Drawing nr...:

9611


FORMAT: A1

Pumphouse 2

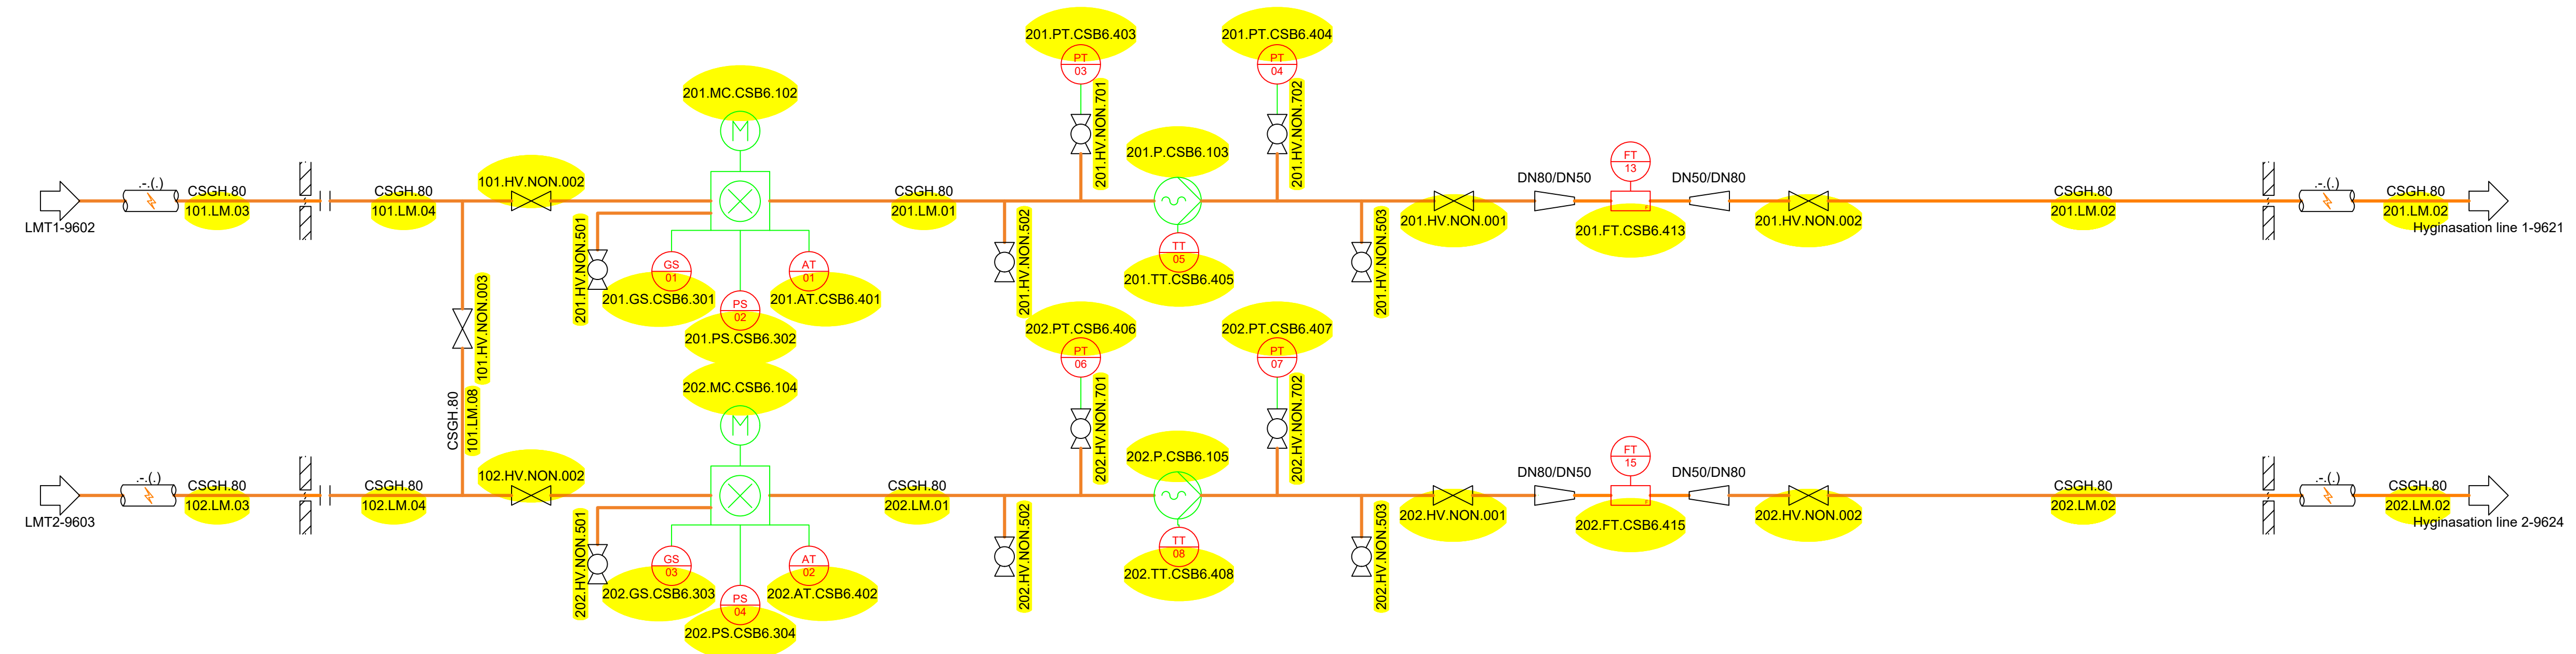


Tech
building


SB-building

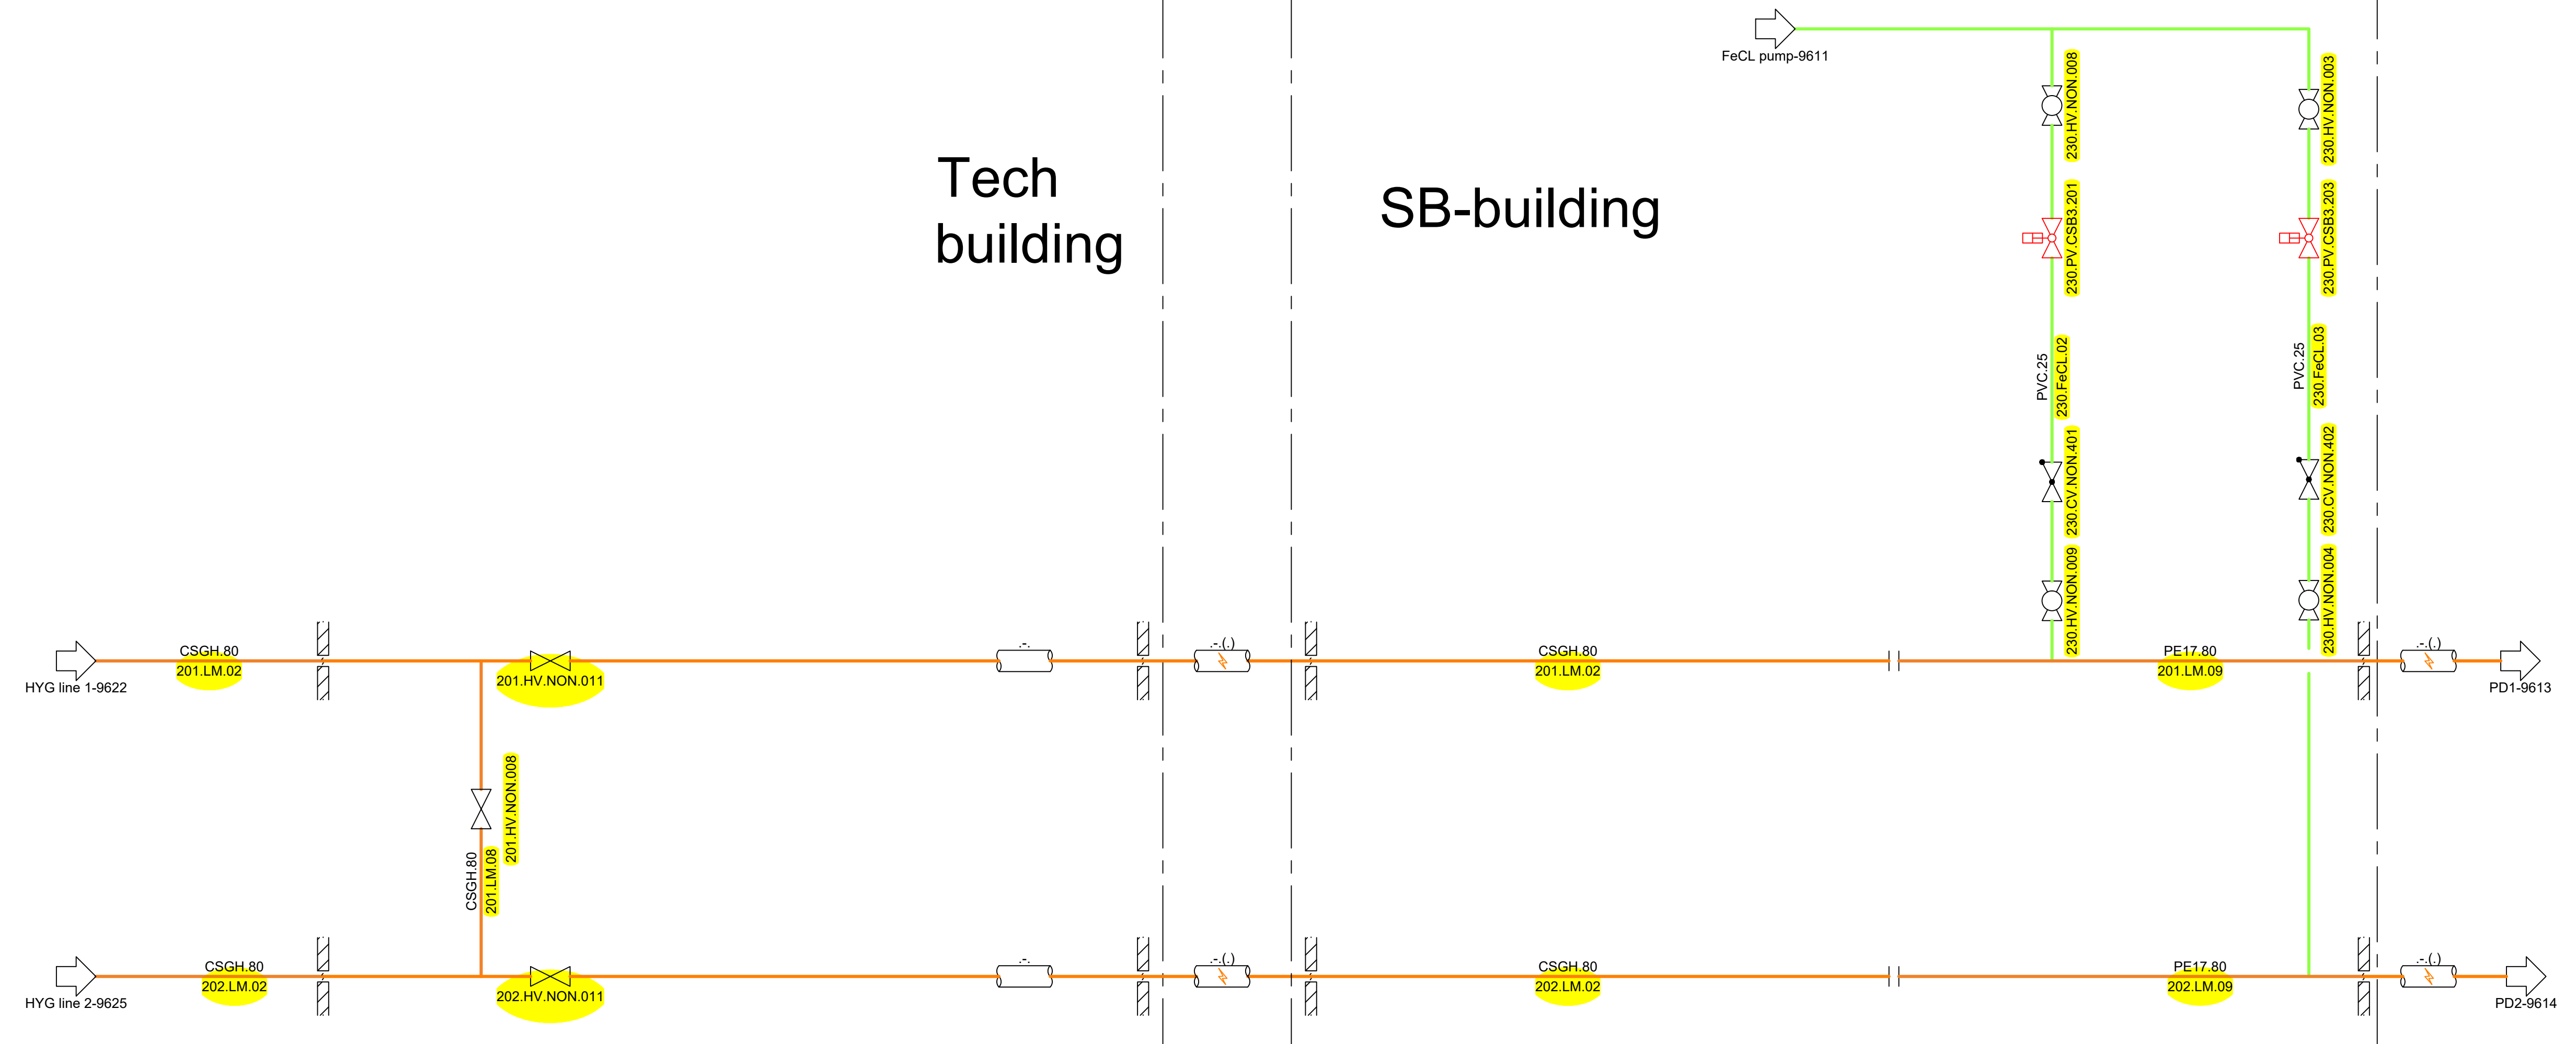


Rev. Nr.:	Rev. Dato:	Rev. Description:
Builder:	ST1	
Project:	SLK	
Subject:	Liquid manure pump	
Rev. 6		
Int.: MDC	QC.CM	APP.:
Date:	15-10-2025	
LUNDSBY RENEWABLE SOLUTIONS		
Lundsby Renewable Solutions A/S, Hjarbækvej 65, 8831 Løgstør Tlf.: +45 96 49 43 00 info@lundsby.dk This Drawing is subject to copyright and may not be reproduced without permission from Lundsby Renewable Solutions A/S		
Project nr.: 1768		Drawing nr.: 9612
FORMAT: A1		

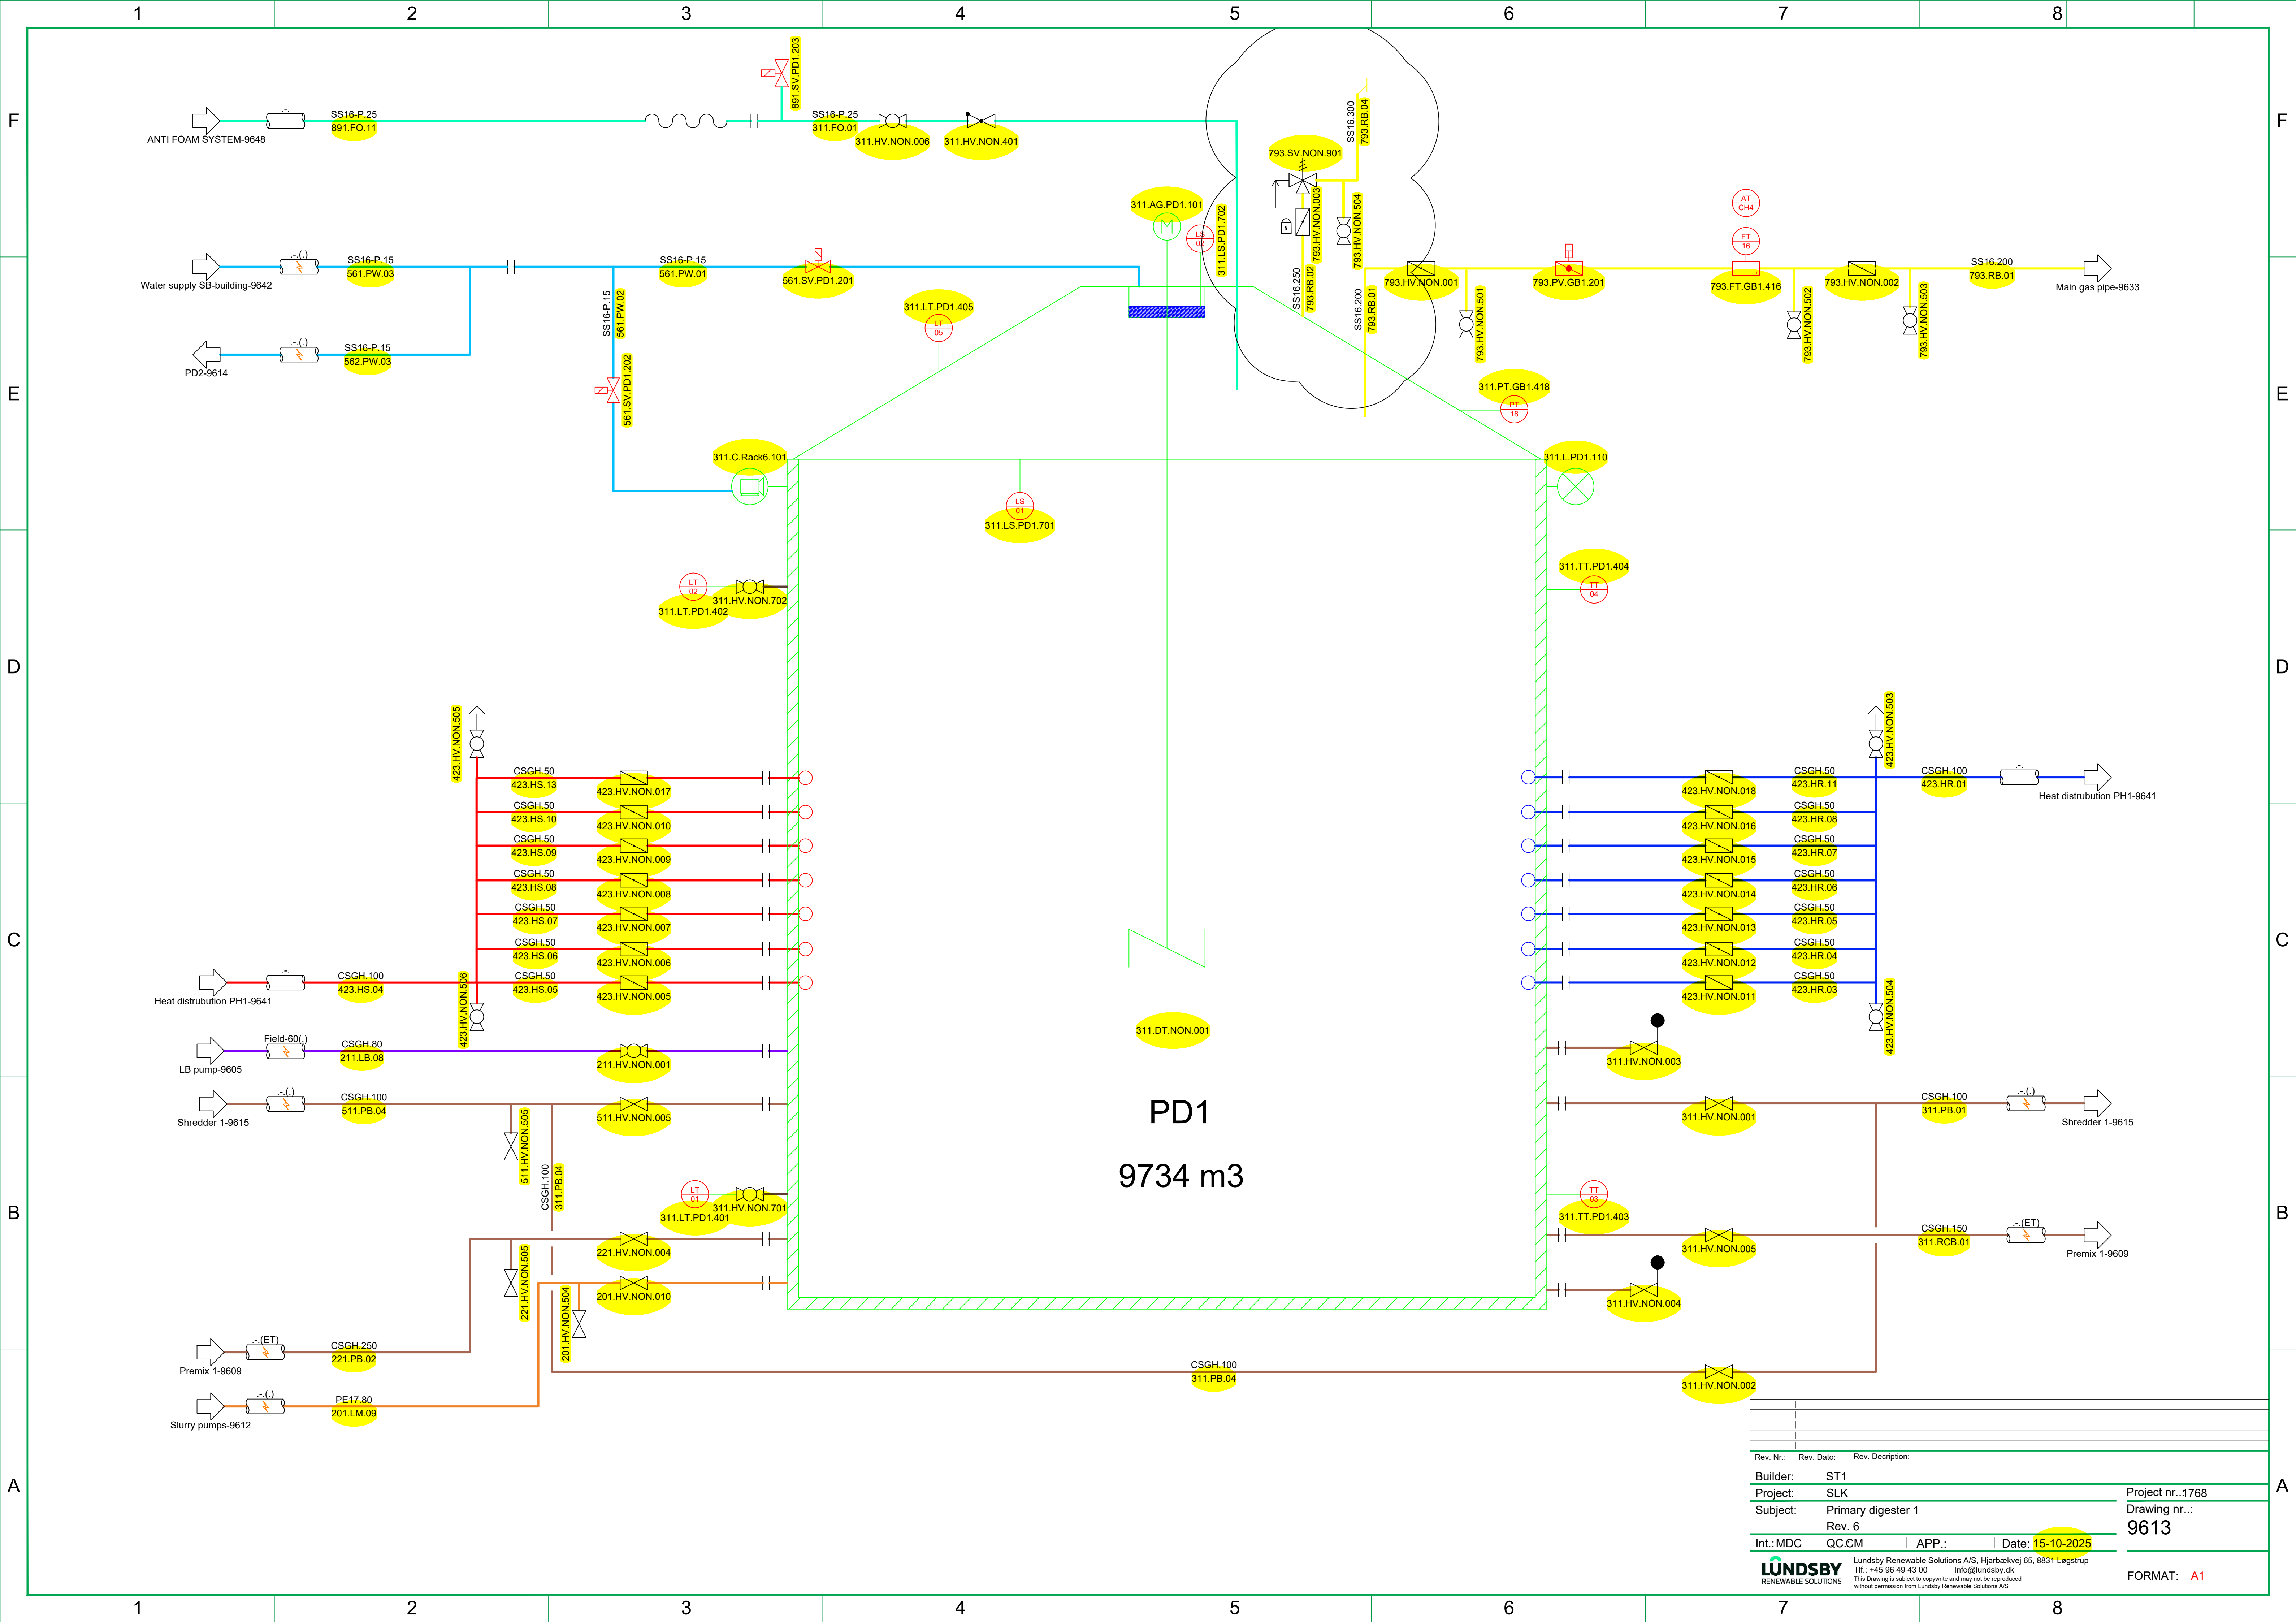


Rev. Nr.:	Rev. Dato:	Rev. Description:
Builder:	ST1	
Project:	SLK	
Subject:	Primary digester 1	
Rev. 6		
Int.:MDC	QC:CM	APP.:
Date:	15-10-2025	
LUNDSBY RENEWABLE SOLUTIONS		
Lundsby Renewable Solutions A/S, Hjarbrækvej 65, 8831 Løgstrup Tlf.: +45 96 49 43 00 Info@lundsby.dk This drawing is subject to copyright and may not be reproduced without permission from Lundsby Renewable Solutions A/S		
Project nr.:1768		Drawing nr.: 9613
FORMAT: A1		

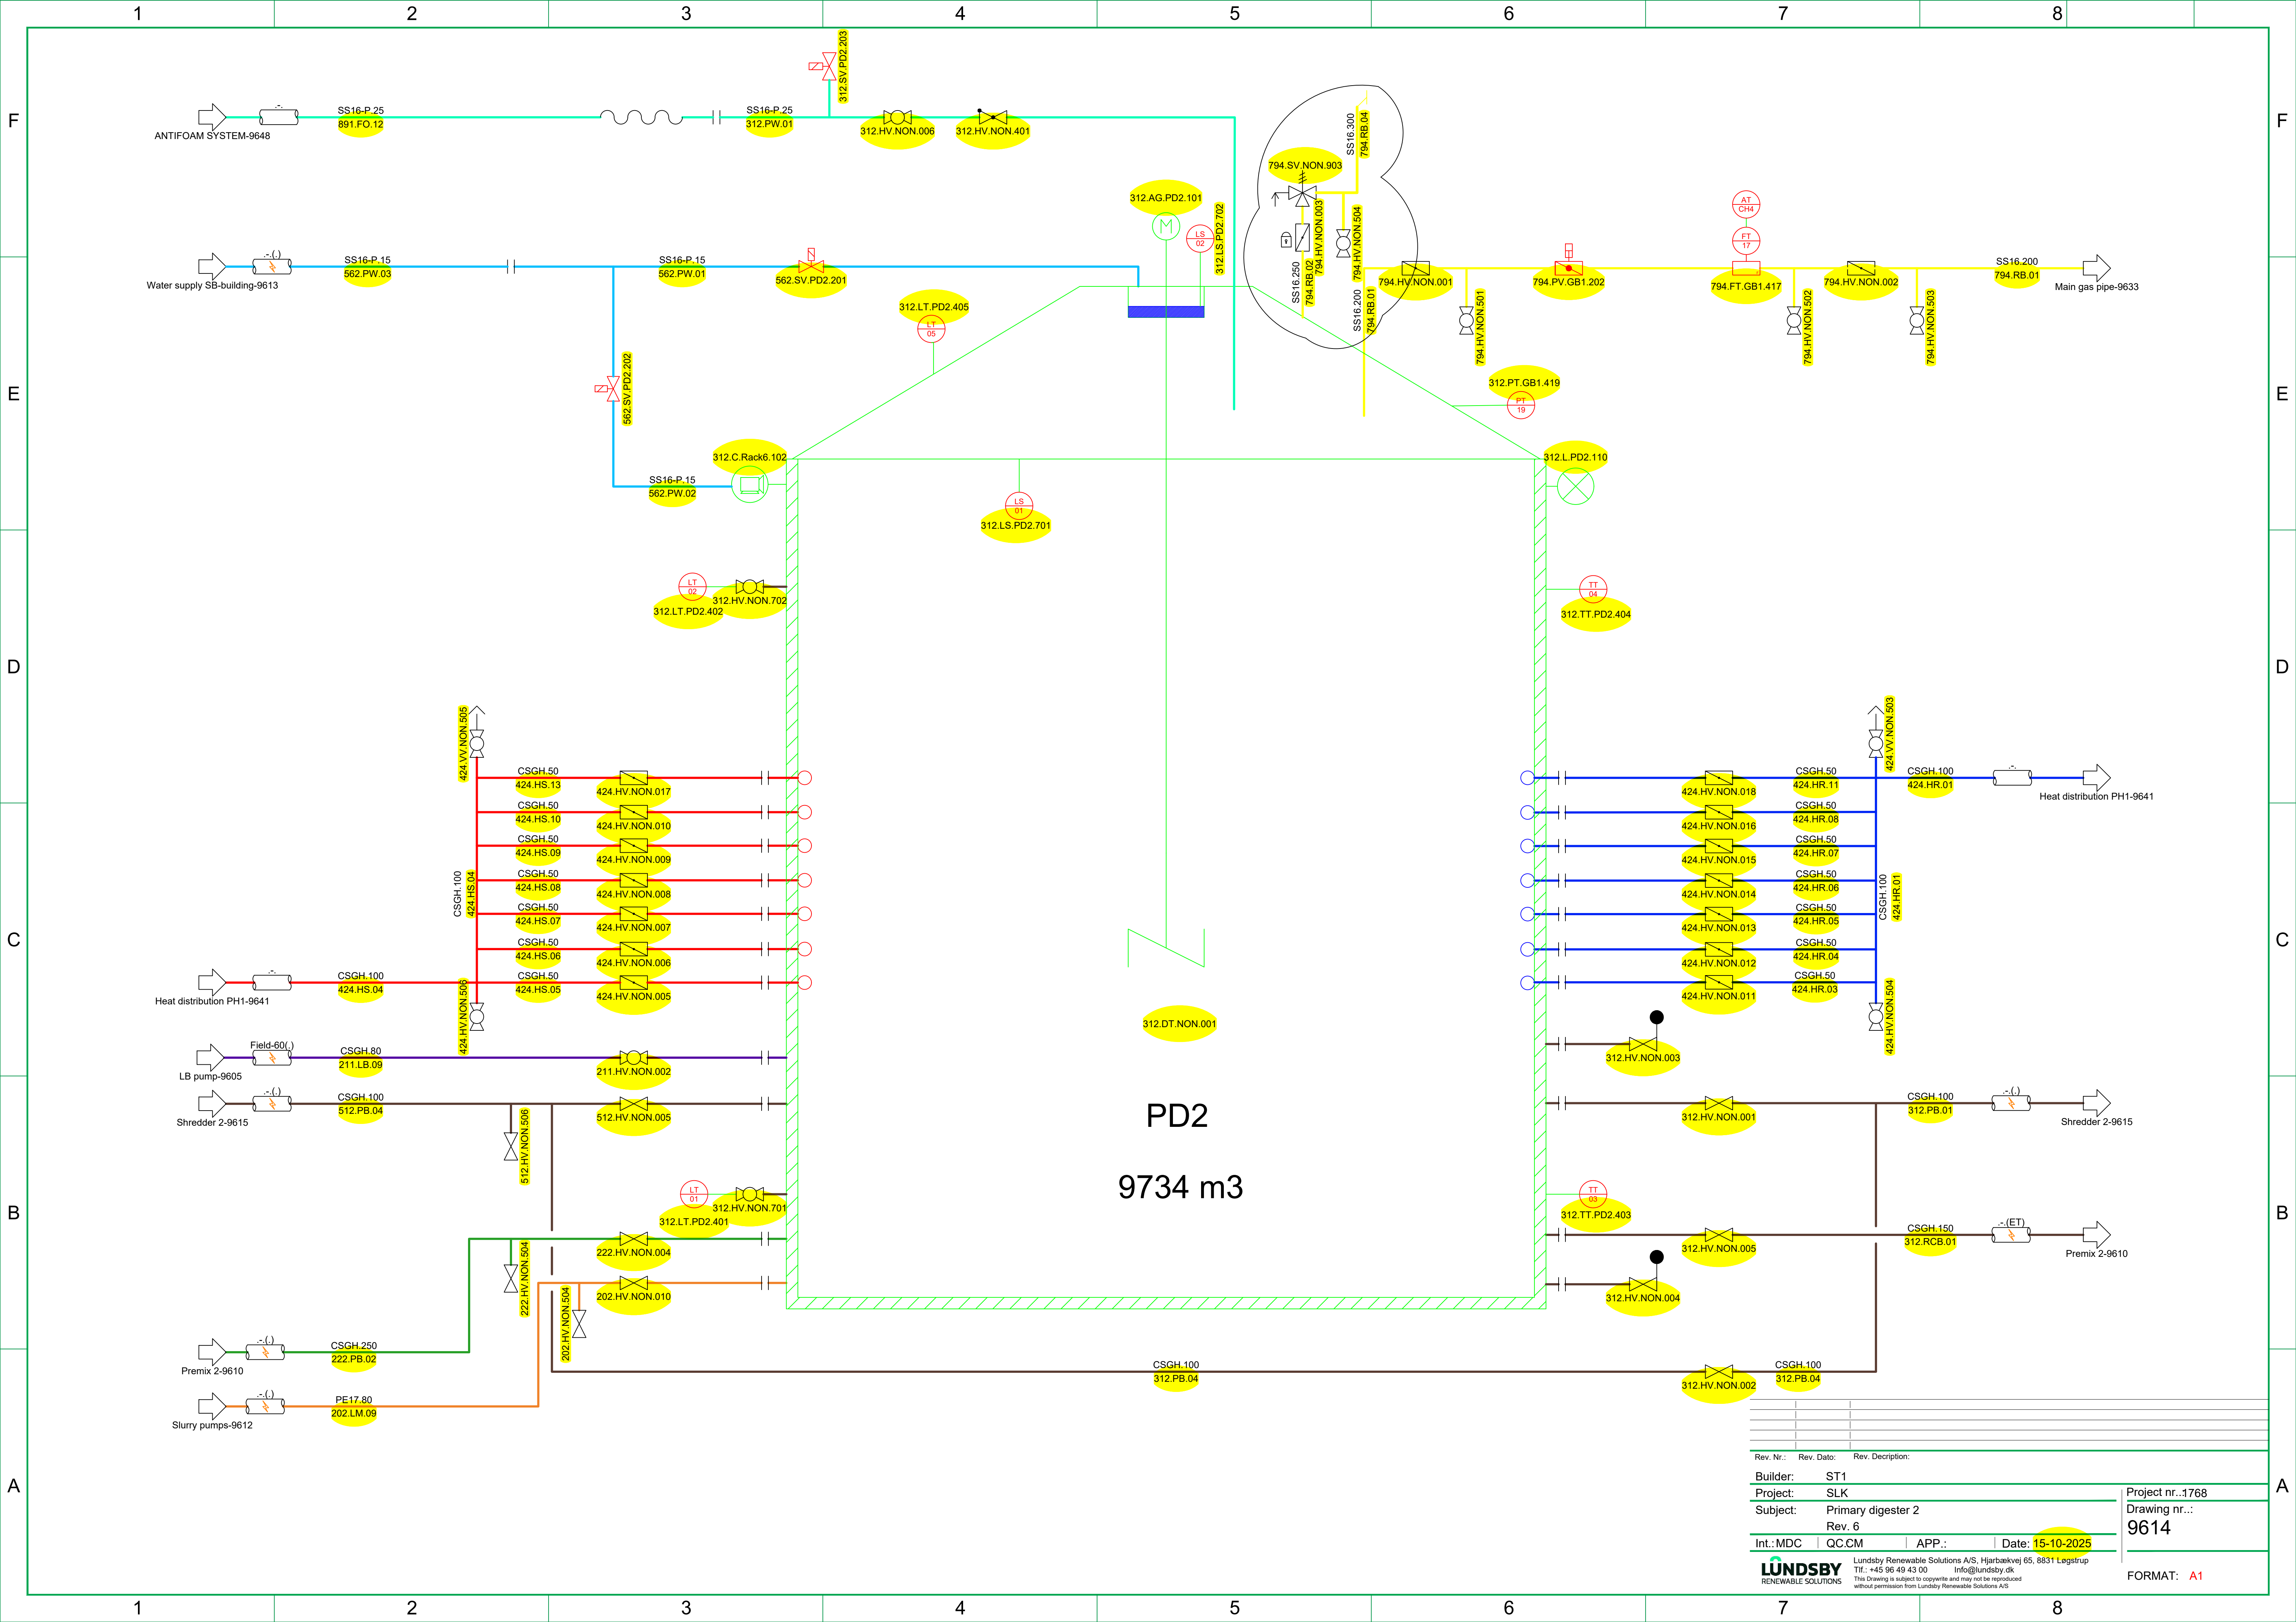


Rev. Nr.:	Rev. Dato:	Rev. Description:
Builder:	ST1	
Project:	SLK	
Subject:	Primary digester 2	
Rev. 6		
Int.:MDC	QC:CM	APP.:
Date:	15-10-2025	
LUNDSBY RENEWABLE SOLUTIONS Lundsby Renewable Solutions A/S, Hjarbrækvej 65, 8831 Løgstrup Tlf.: +45 96 49 43 00 Info@lundsby.dk This drawing is subject to copyright and may not be reproduced without permission from Lundsby Renewable Solutions A/S		
Project nr.:1768		Drawing nr.: 9614
FORMAT: A1		

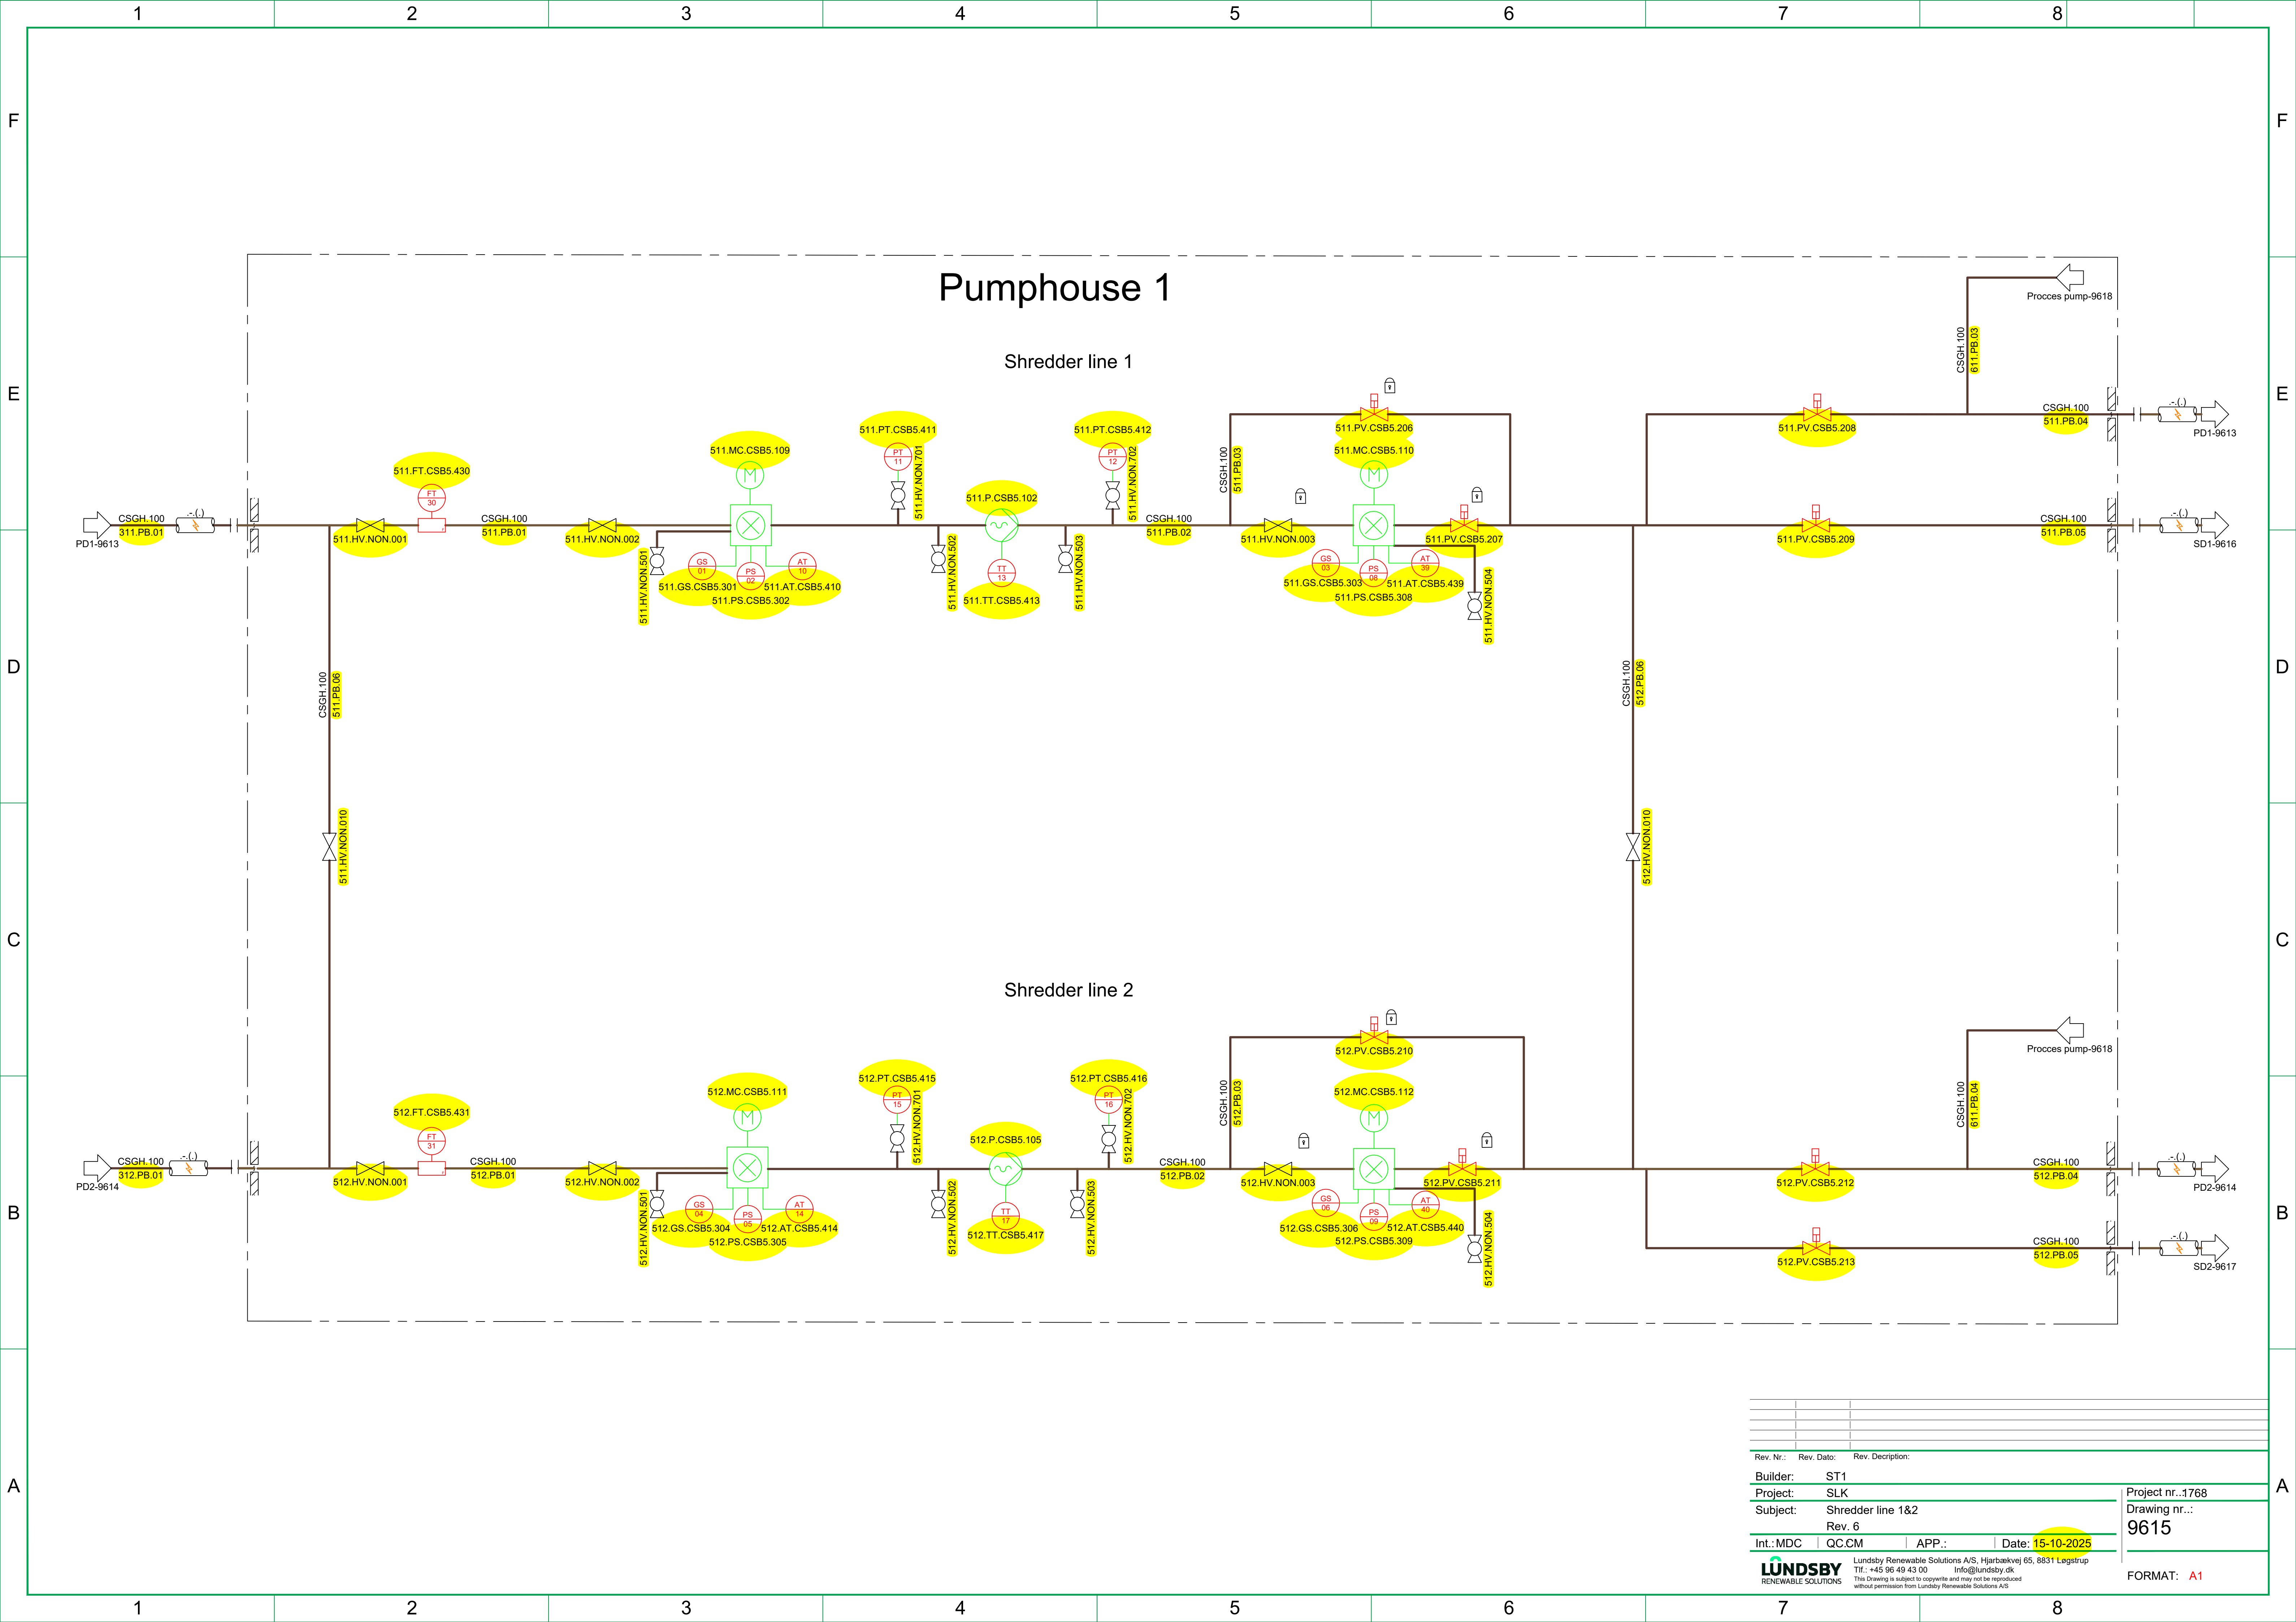


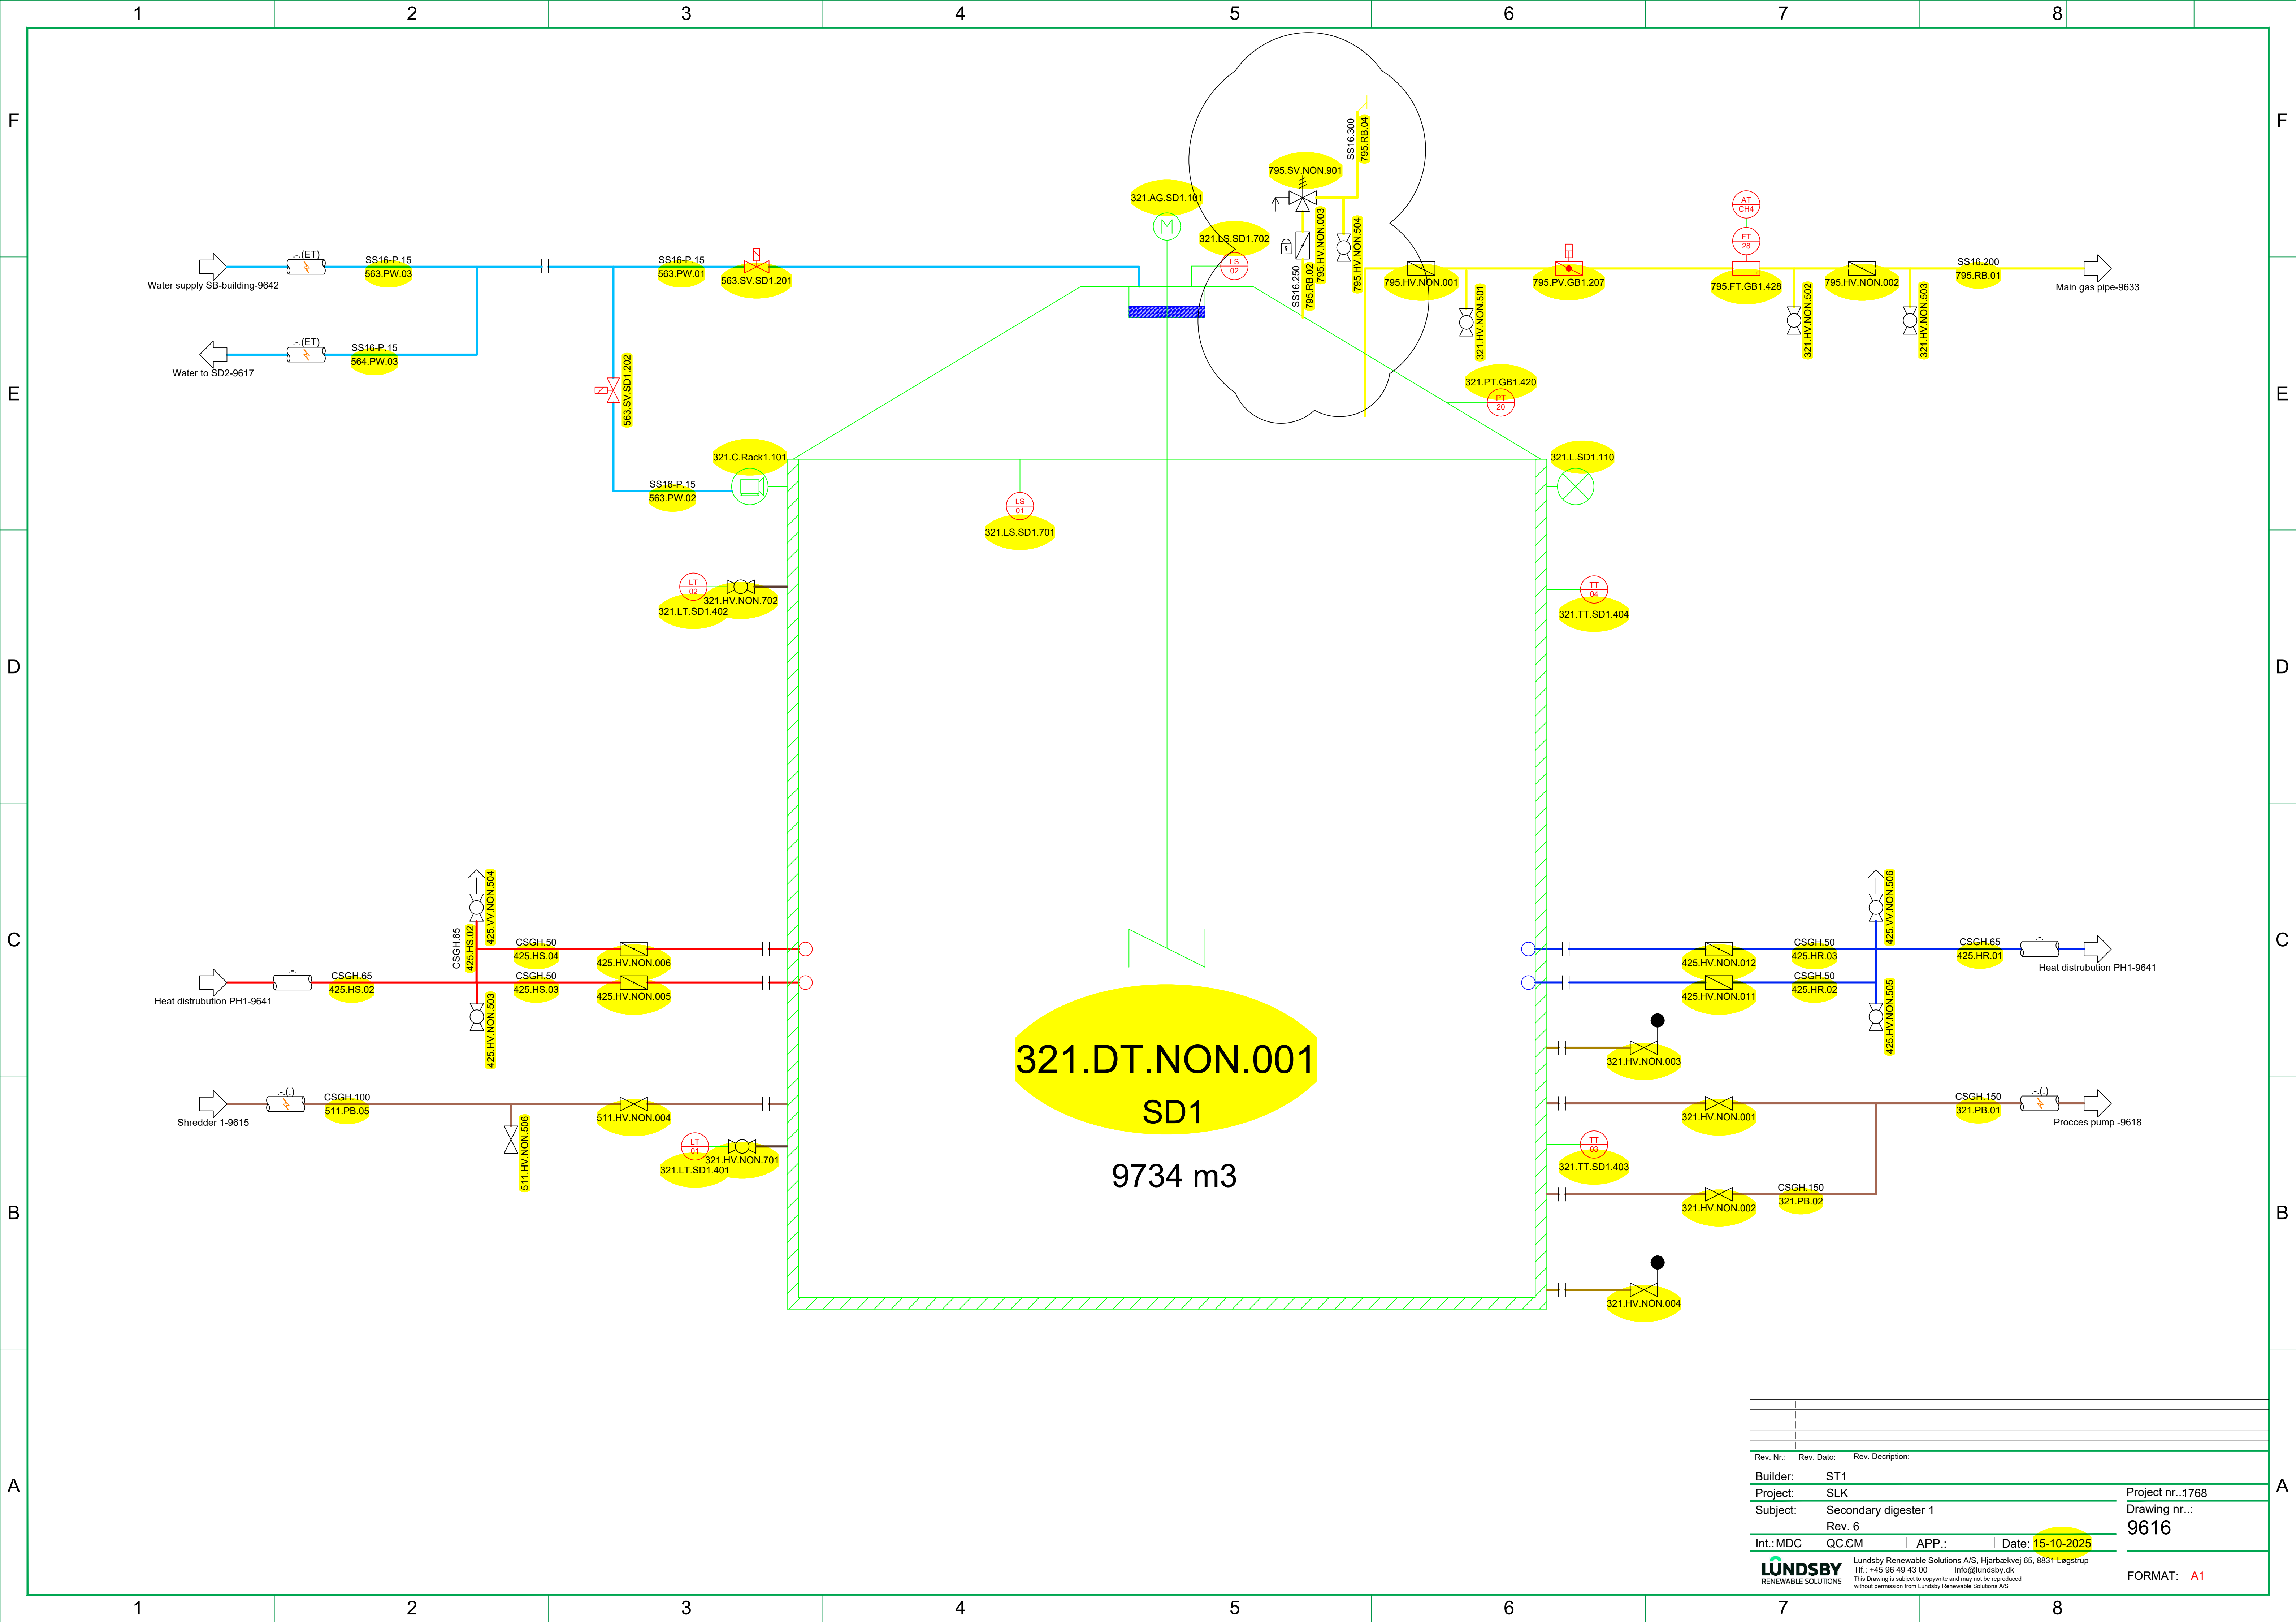


Rev. Nr.:	Rev. Dato:	Rev. Description:	
Builder:	ST1		
Project:	SLK		
Subject:	Secondary digester 1		
Rev. 6			
Int.:MDC	QC:CM	APP.:	Date: 15-10-2025
LUNDSBY RENEWABLE SOLUTIONS			Lundsgby Renewable Solutions A/S, Hjarbækvej 65, 8831 Løgstrup Tlf.: +45 96 49 43 00 Info@lundsgby.dk This drawing is subject to copyright and may not be reproduced without permission from Lundsgby Renewable Solutions A/S
Project nr.:1768 Drawing nr.: 9616			FORMAT: A1

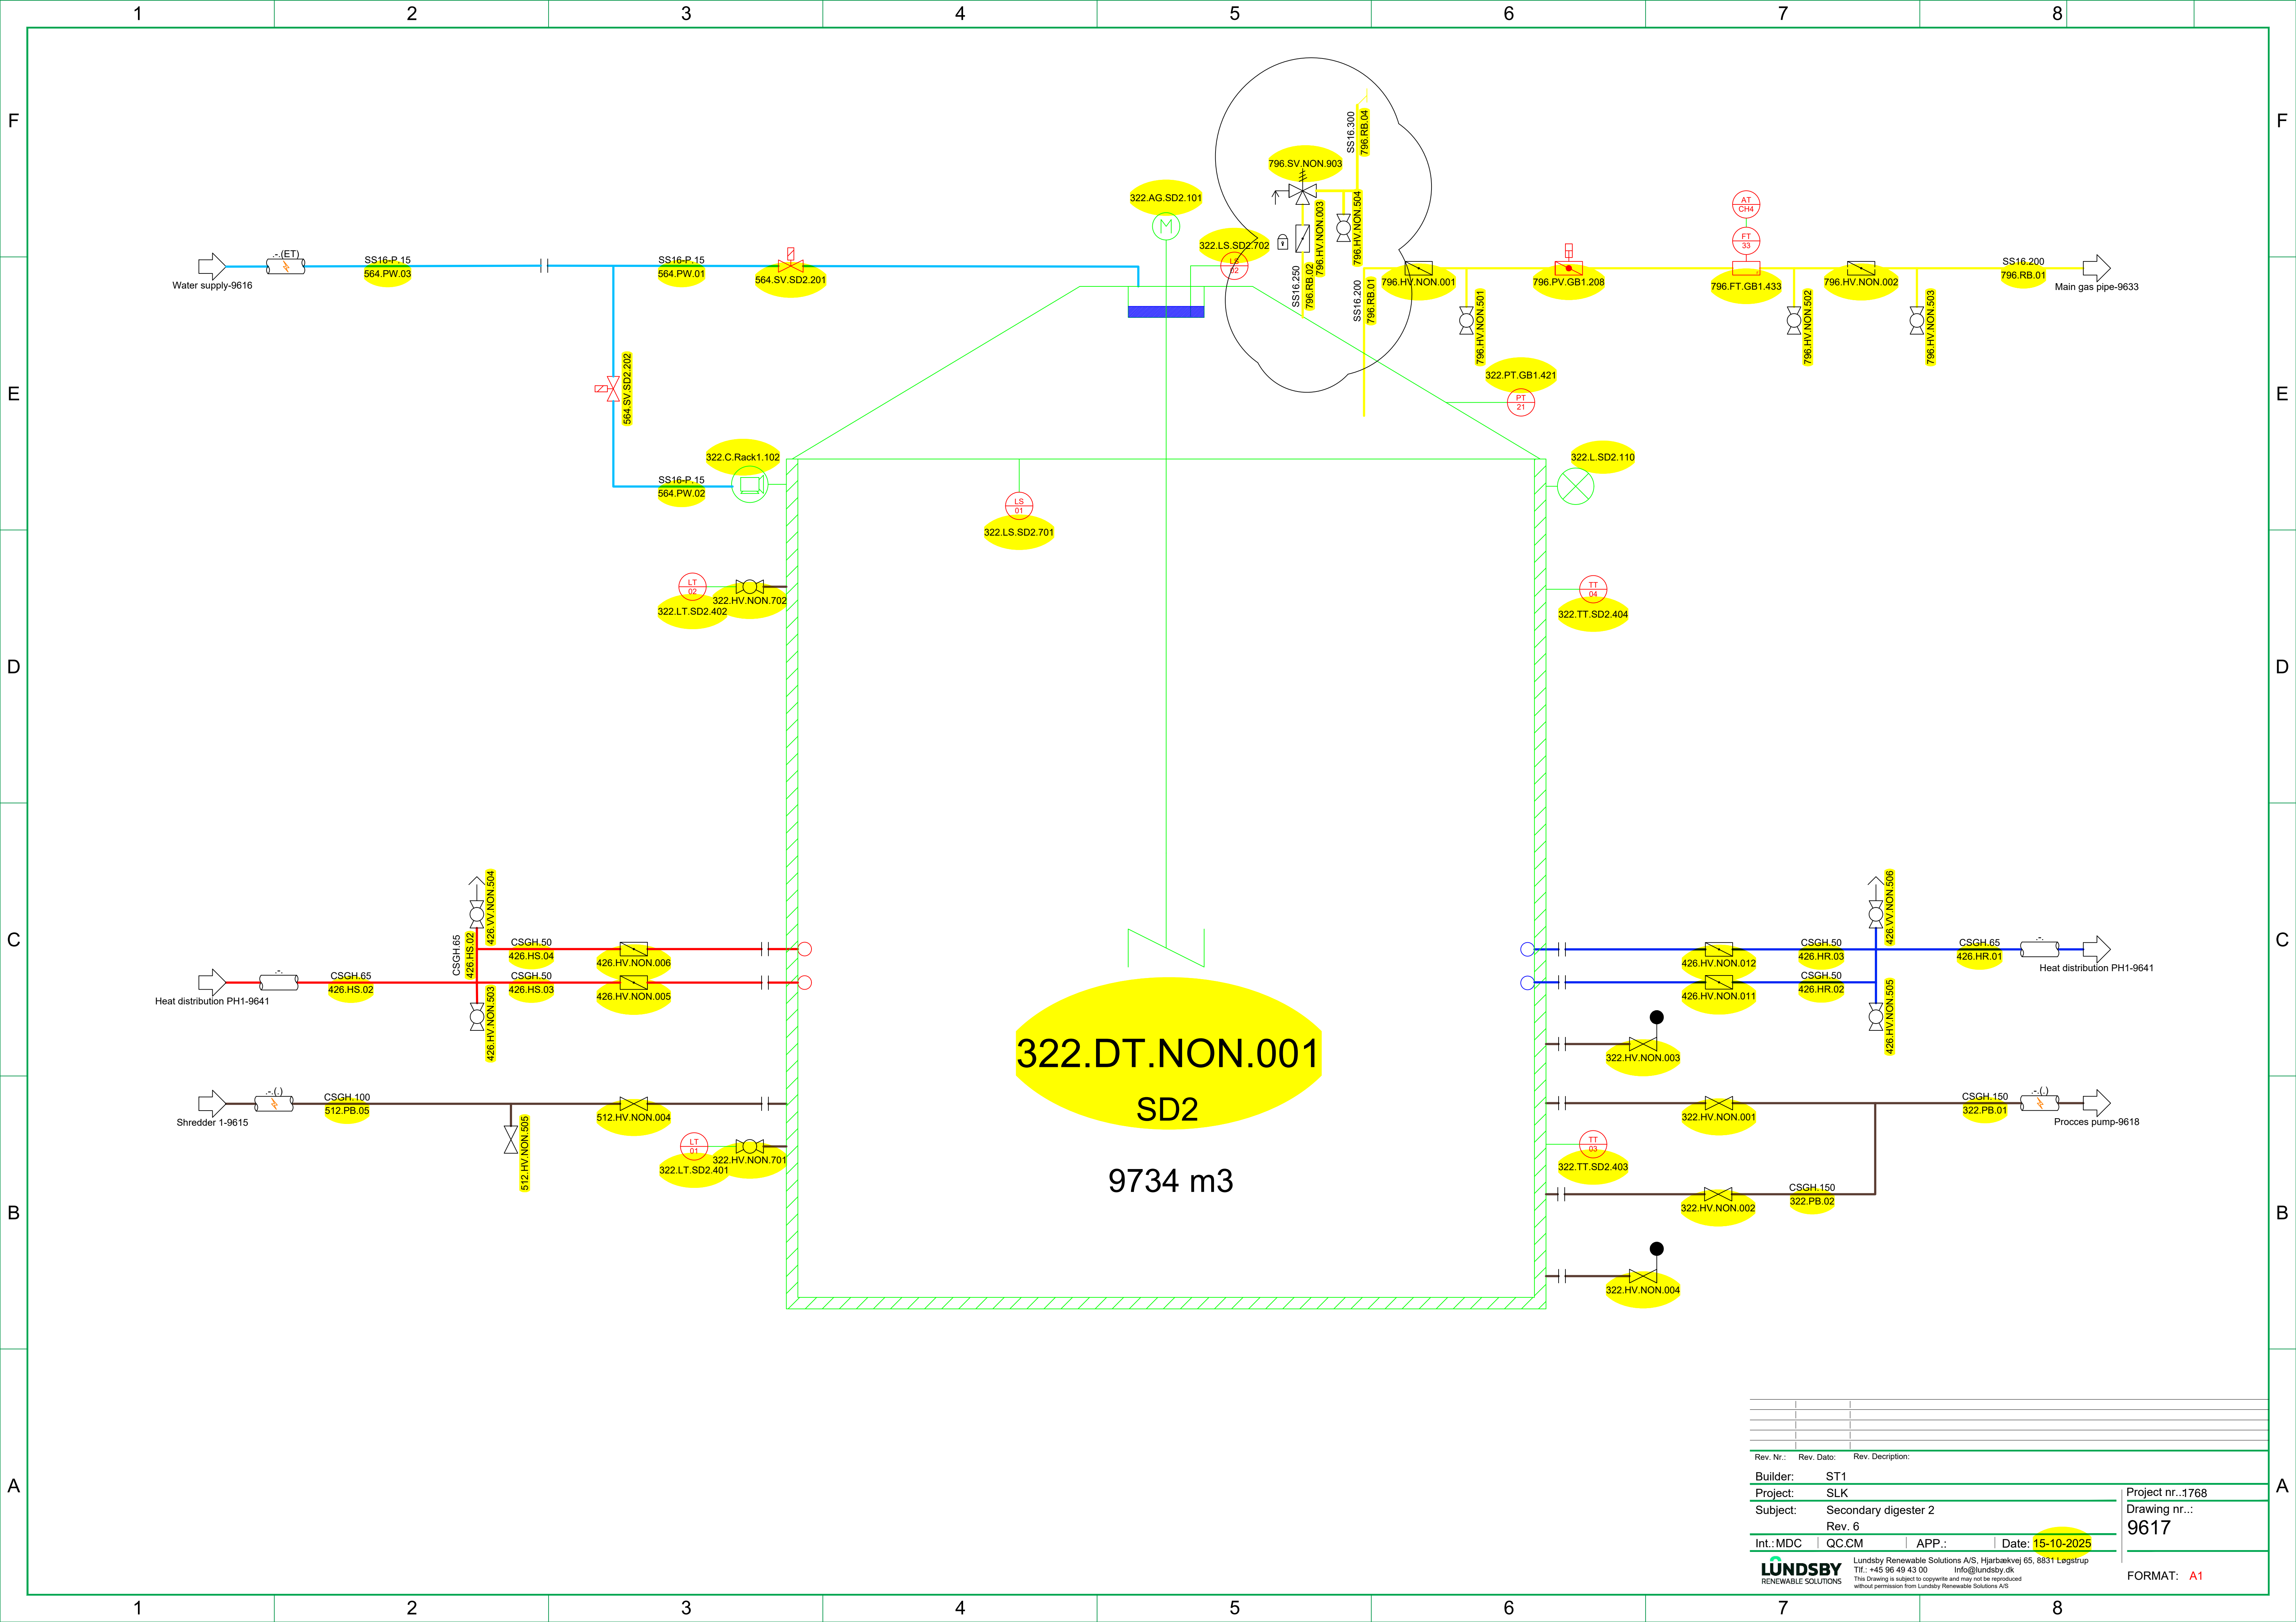

Rev. Nr.:	Rev. Dato:	Rev. Description:	
Builder:	ST1		
Project:	SLK		
Subject:	Secondary digester 2		
Rev. 6			
Int.:MDC	QC:CM	APP.:	Date: 15-10-2025
LUNDSBY RENEWABLE SOLUTIONS			Lundsgby Renewable Solutions A/S, Hjarbrækvej 65, 8831 Løgstrup Tlf.: +45 96 49 43 00 Info@lundsgby.dk This Drawing is subject to copyright and may not be reproduced without permission from Lundsgby Renewable Solutions A/S
Project nr.:1768 Drawing nr.: 9617			FORMAT: A1

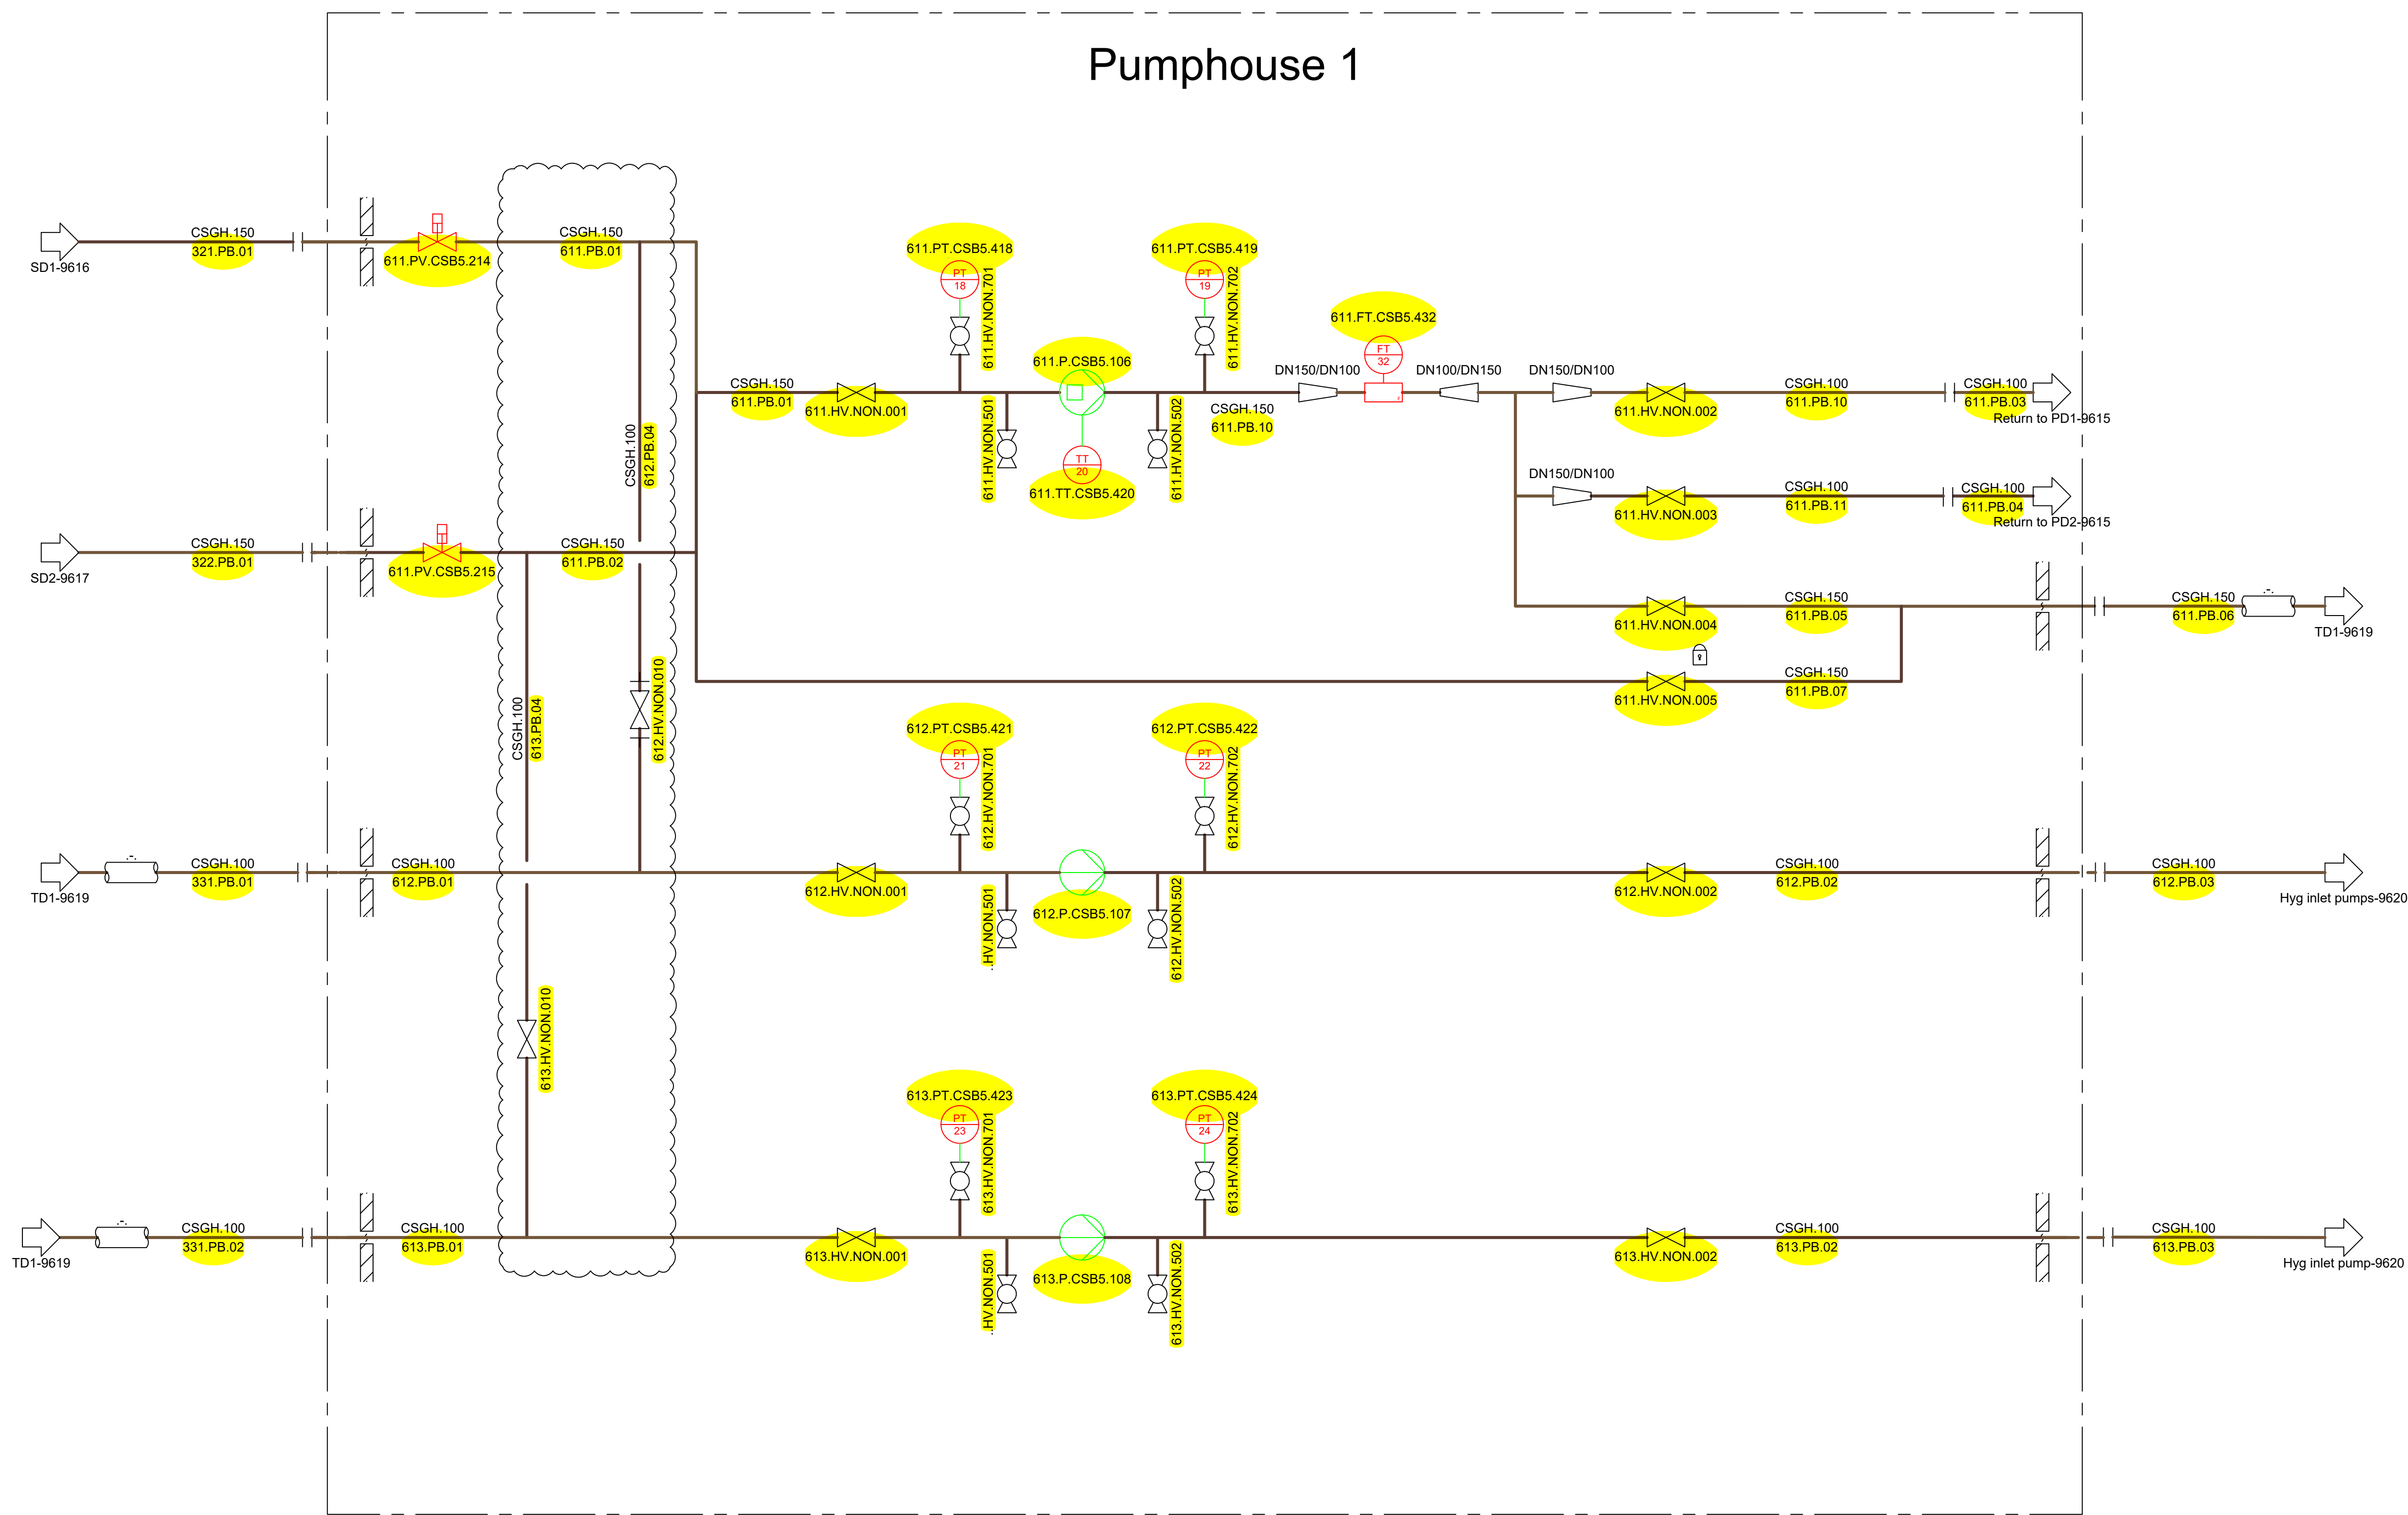


Rev. Nr.:	Rev. Dato:	Rev. Description:
Builder:	ST1	
Project:	SLK	
Subject:	Procces pumps	
Rev. 6		
Int.:MDC	QC:CM	APP.:
Date:	15-10-2025	
LUNDSBY RENEWABLE SOLUTIONS		
Lundsby Renewable Solutions A/S, Hjarbækvej 65, 8831 Løgstrup Tlf.: +45 96 49 43 00 Info@lundsby.dk This Drawing is subject to copyright and may not be reproduced without permission from Lundsby Renewable Solutions A/S		
Project nr.:1768 Drawing nr.: 9618		FORMAT: A1

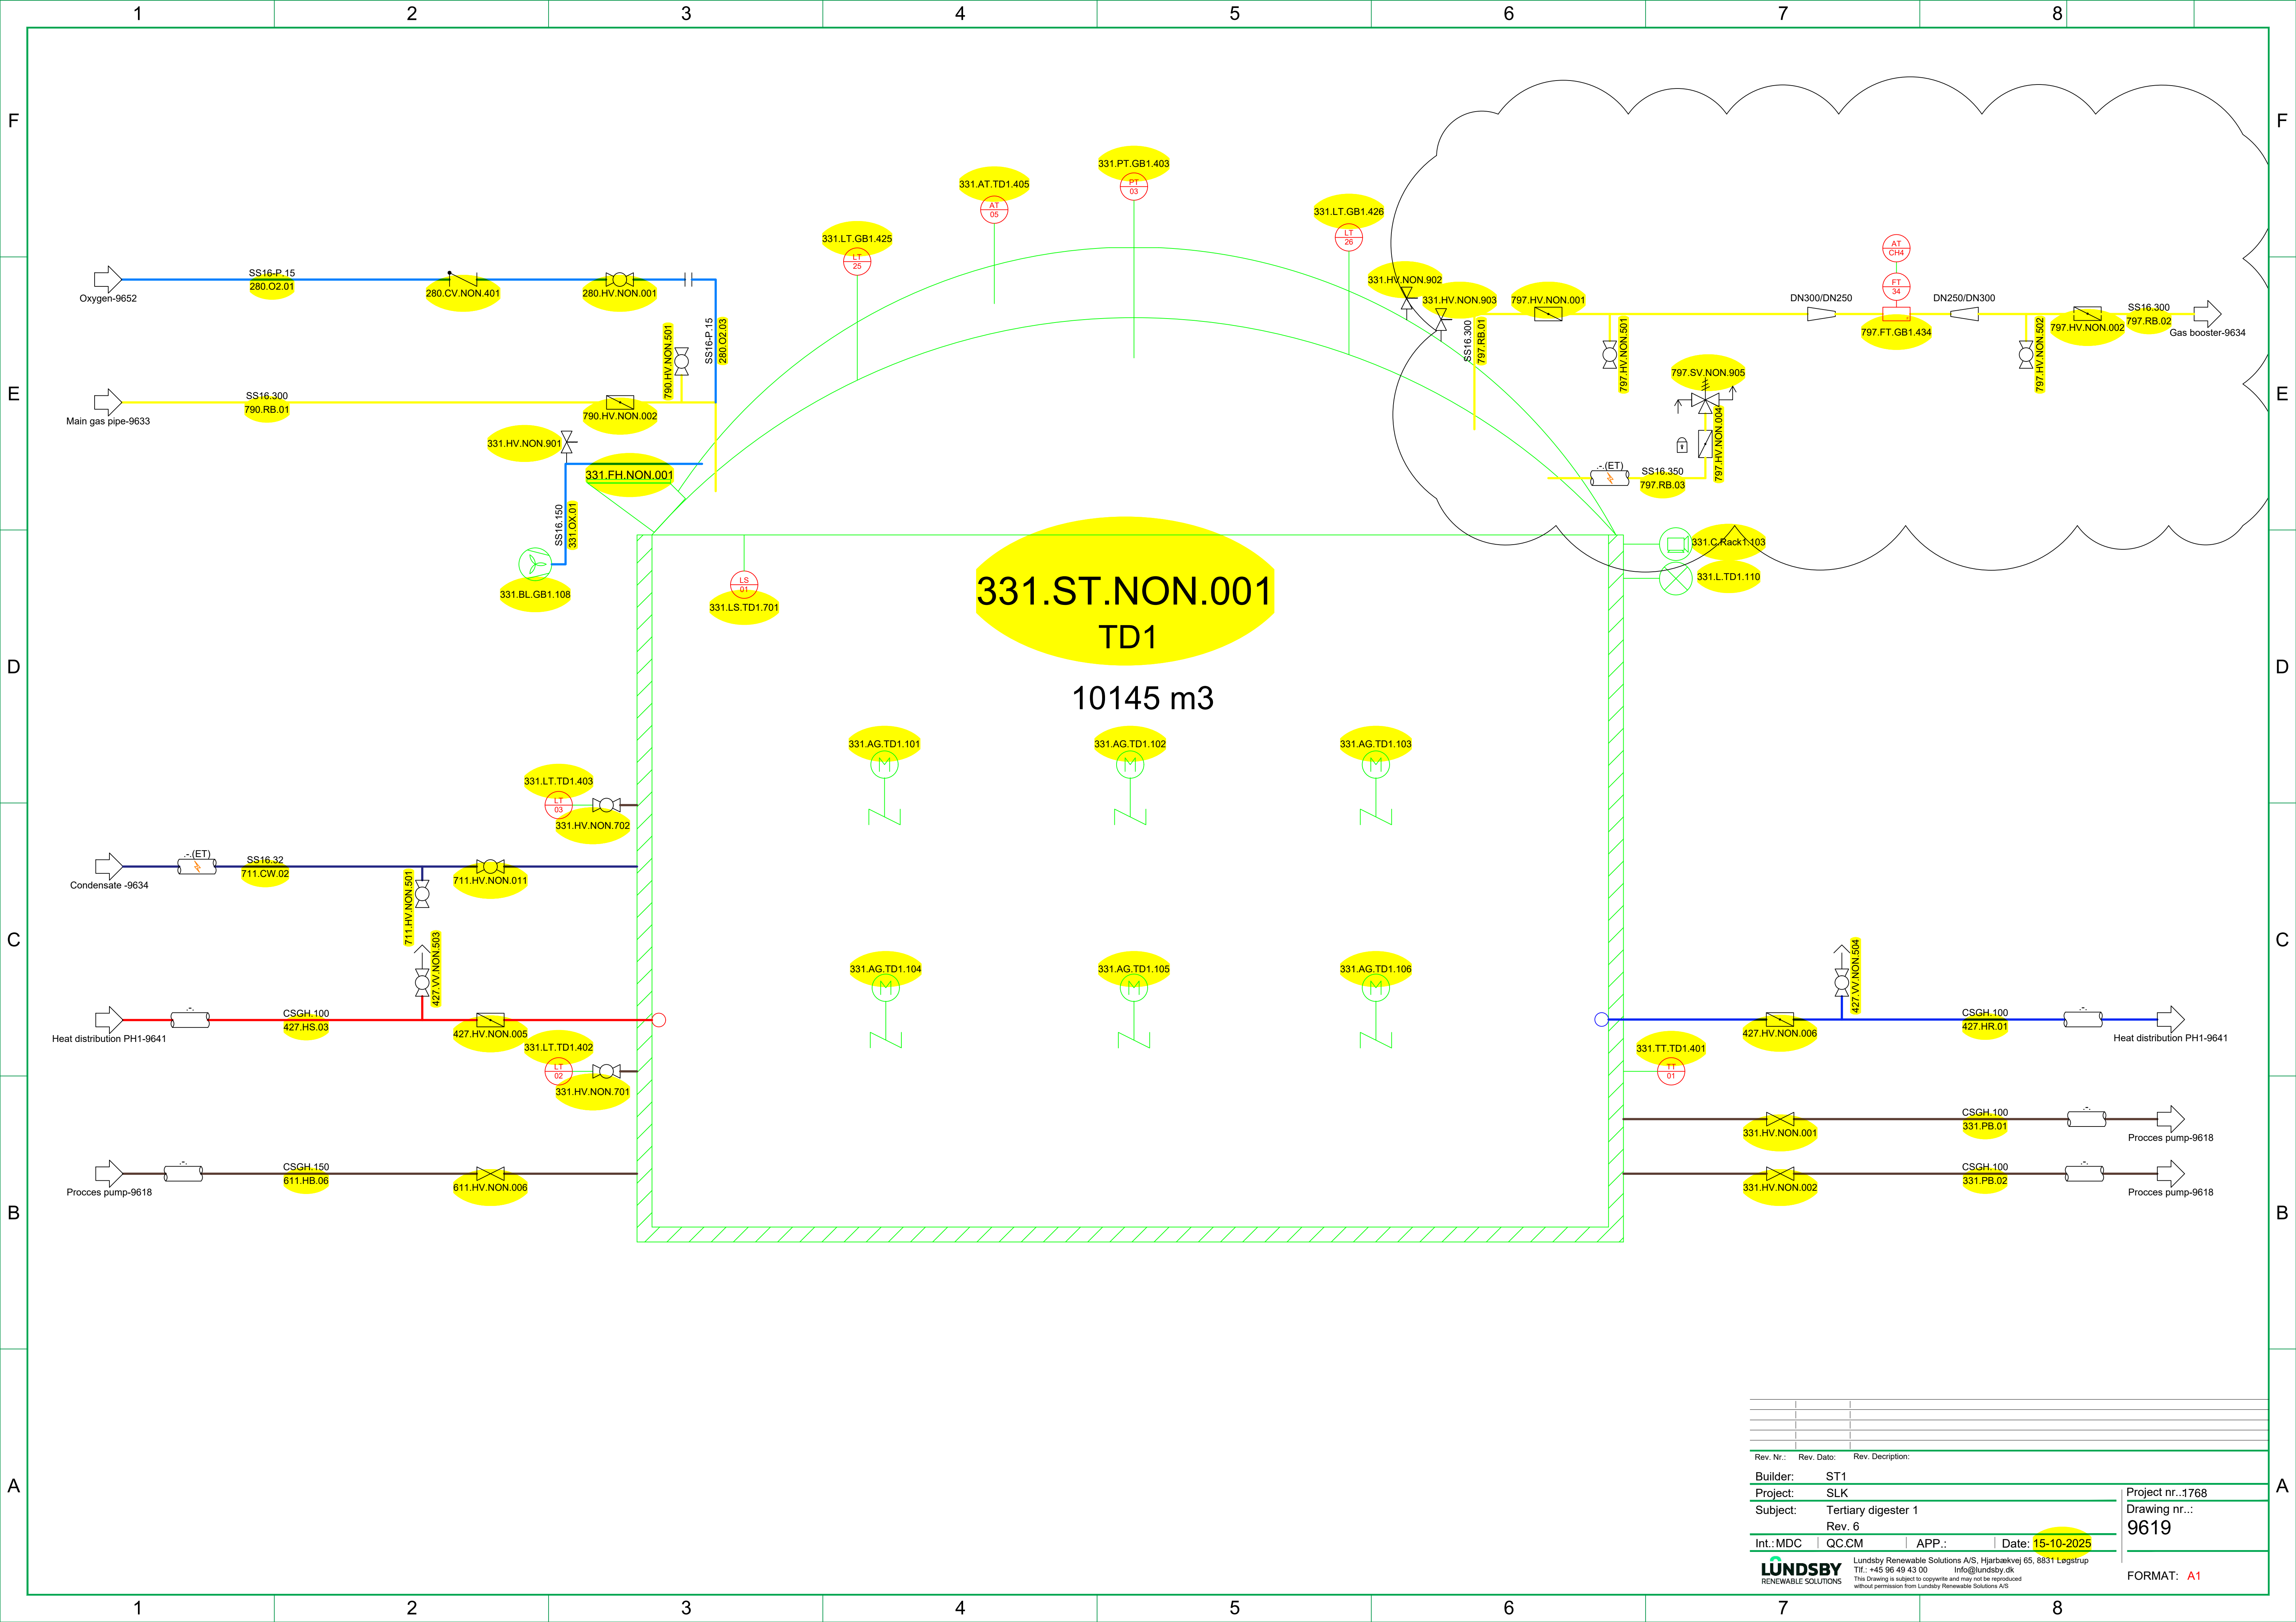


	</
--	--	----

Tech Building


Inlet pumps

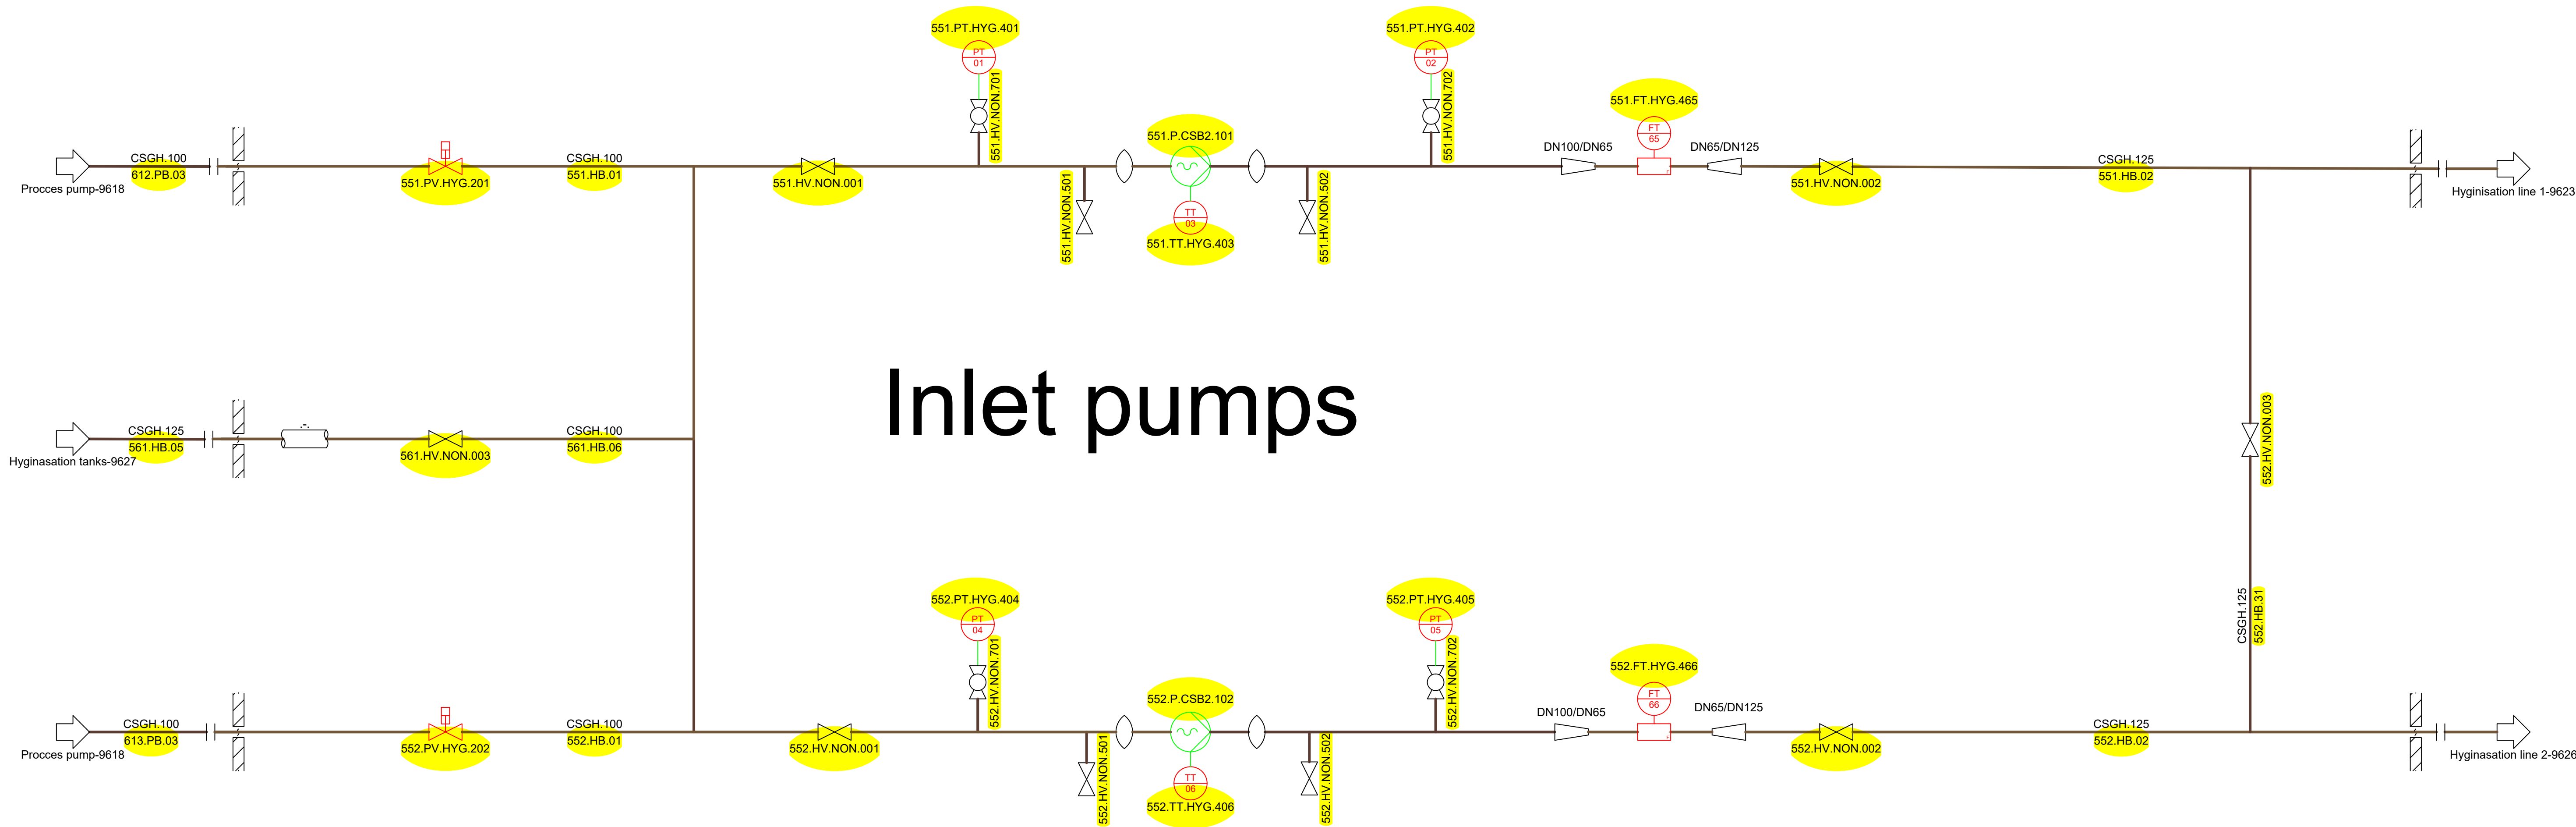



Rev. Nr.:	Rev. Dato:	Rev. Description:	
Builder:	ST1		
Project:	SLK		
Subject:	Hyginisation inlet pumps		
	Rev. 6		
Int.:MDC	QC:CM	APP.:	Date: 15-10-2025
LUNDSBY RENEWABLE SOLUTIONS			Lundsby Renewable Solutions A/S, Hjarbrækvej 65, 8831 Løgstrup Tlf.: +45 96 49 43 00 Info@lundsby.dk This Drawing is subject to copyright and may not be reproduced without permission from Lundsby Renewable Solutions A/S
			Project nr.:1768 Drawing nr.: 9620 FORMAT: A1

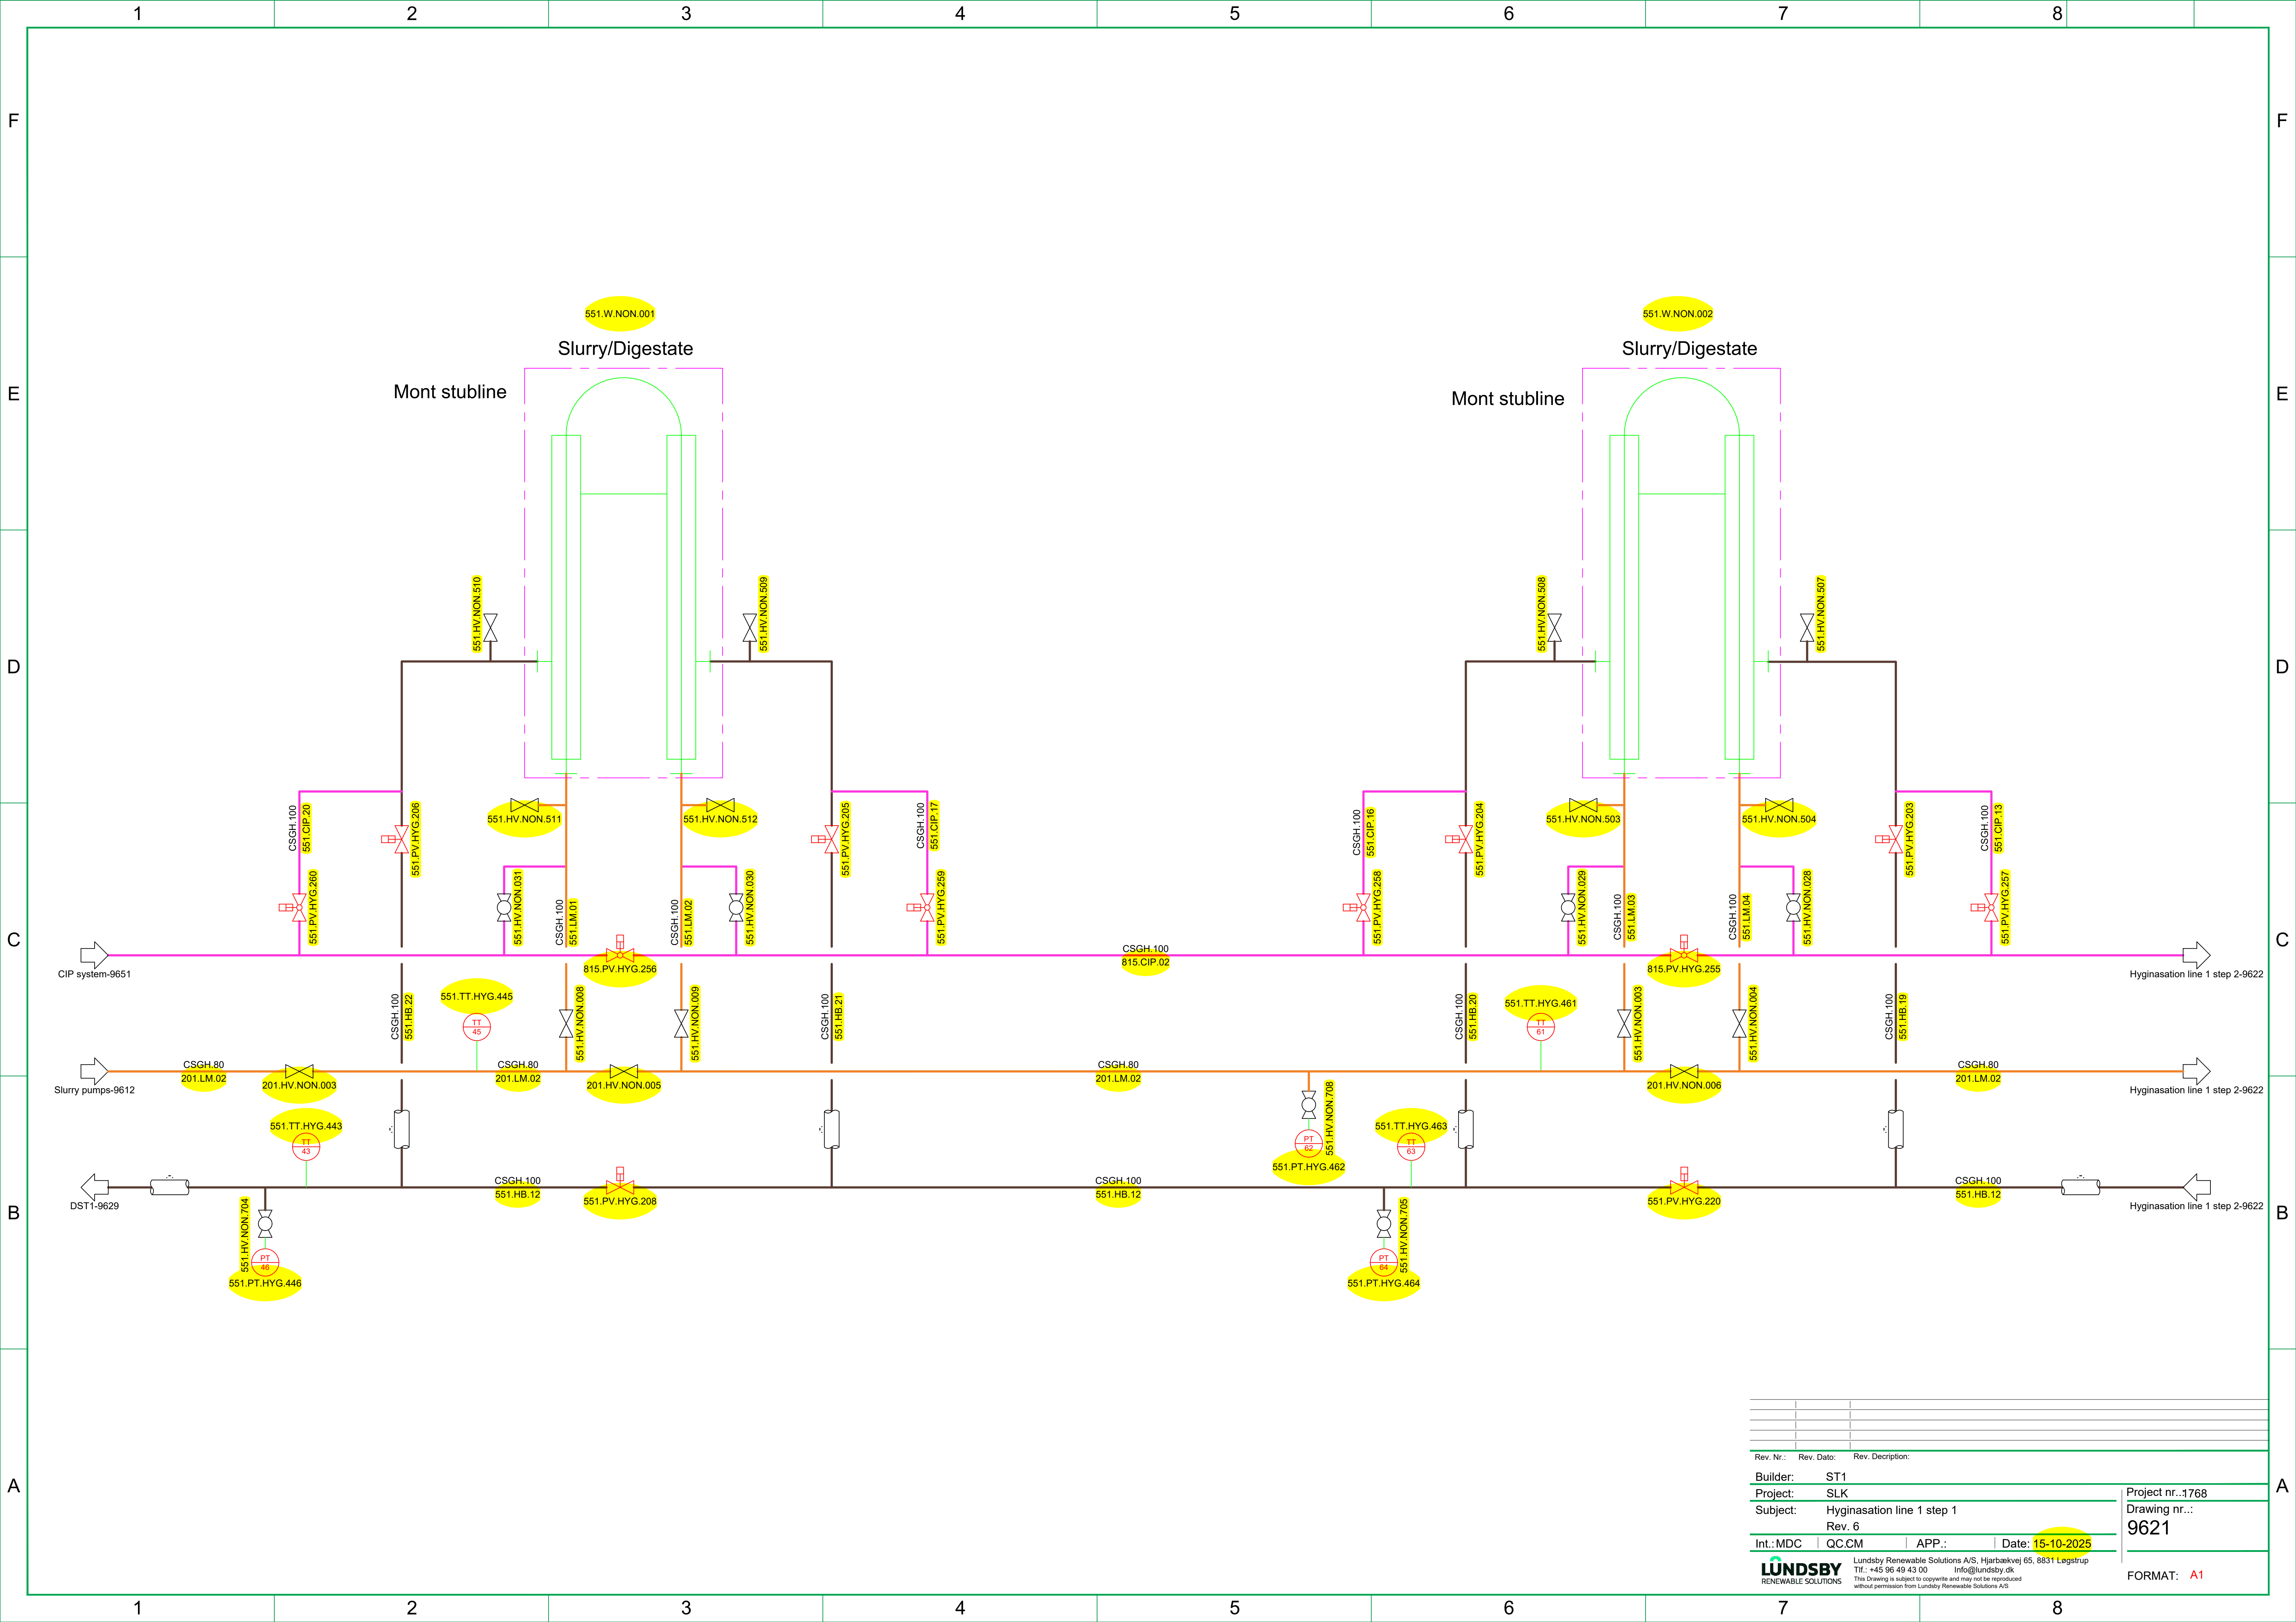


Rev. Nr.:	Rev. Dato:	Rev. Description:
Builder:	ST1	
Project:	SLK	
Subject:	Hyginasation line 1 step 1	
Rev. 6		
Int.: MDC	QC: CM	APP.: Date: 15-10-2025
LUNDSBY RENEWABLE SOLUTIONS		
Lundsby Renewable Solutions A/S, Hjarbækvej 65, 8831 Løgstrup Tlf.: +45 96 49 43 00 Info@lundsby.dk This Drawing is subject to copyright and may not be reproduced without permission from Lundsby Renewable Solutions A/S		
Project nr.: 1768 Drawing nr.: 9621		FORMAT: A1

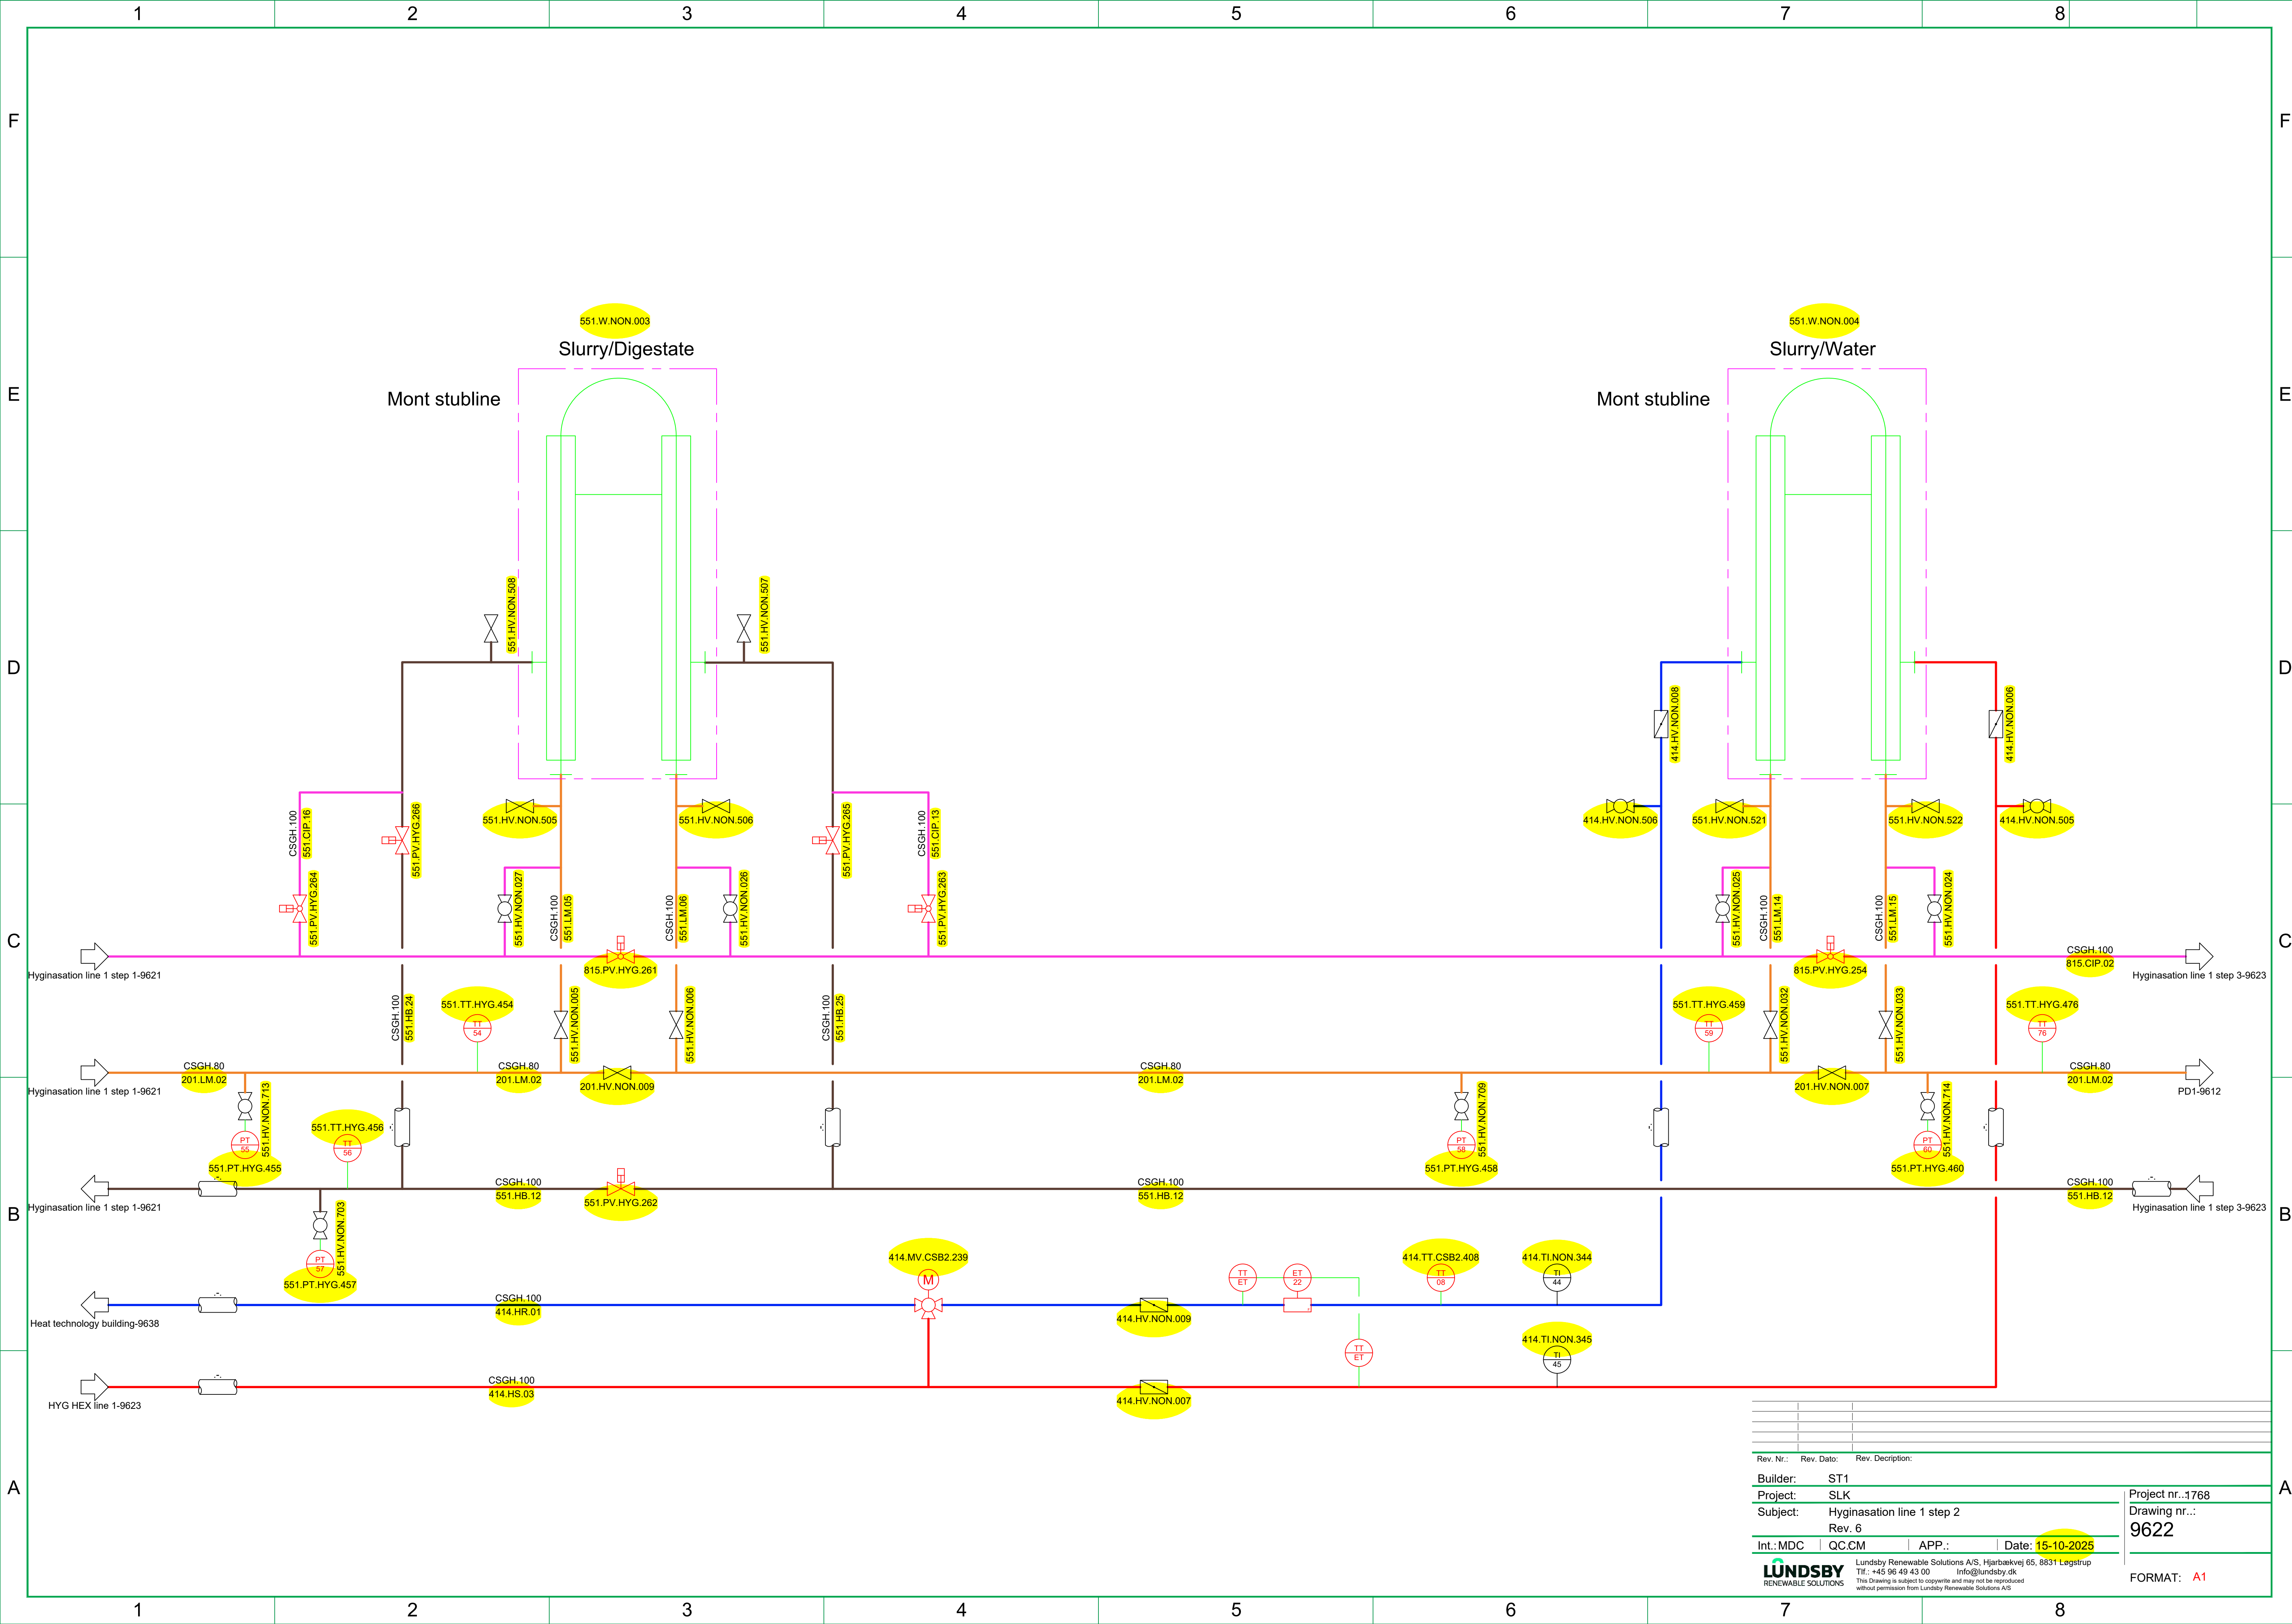


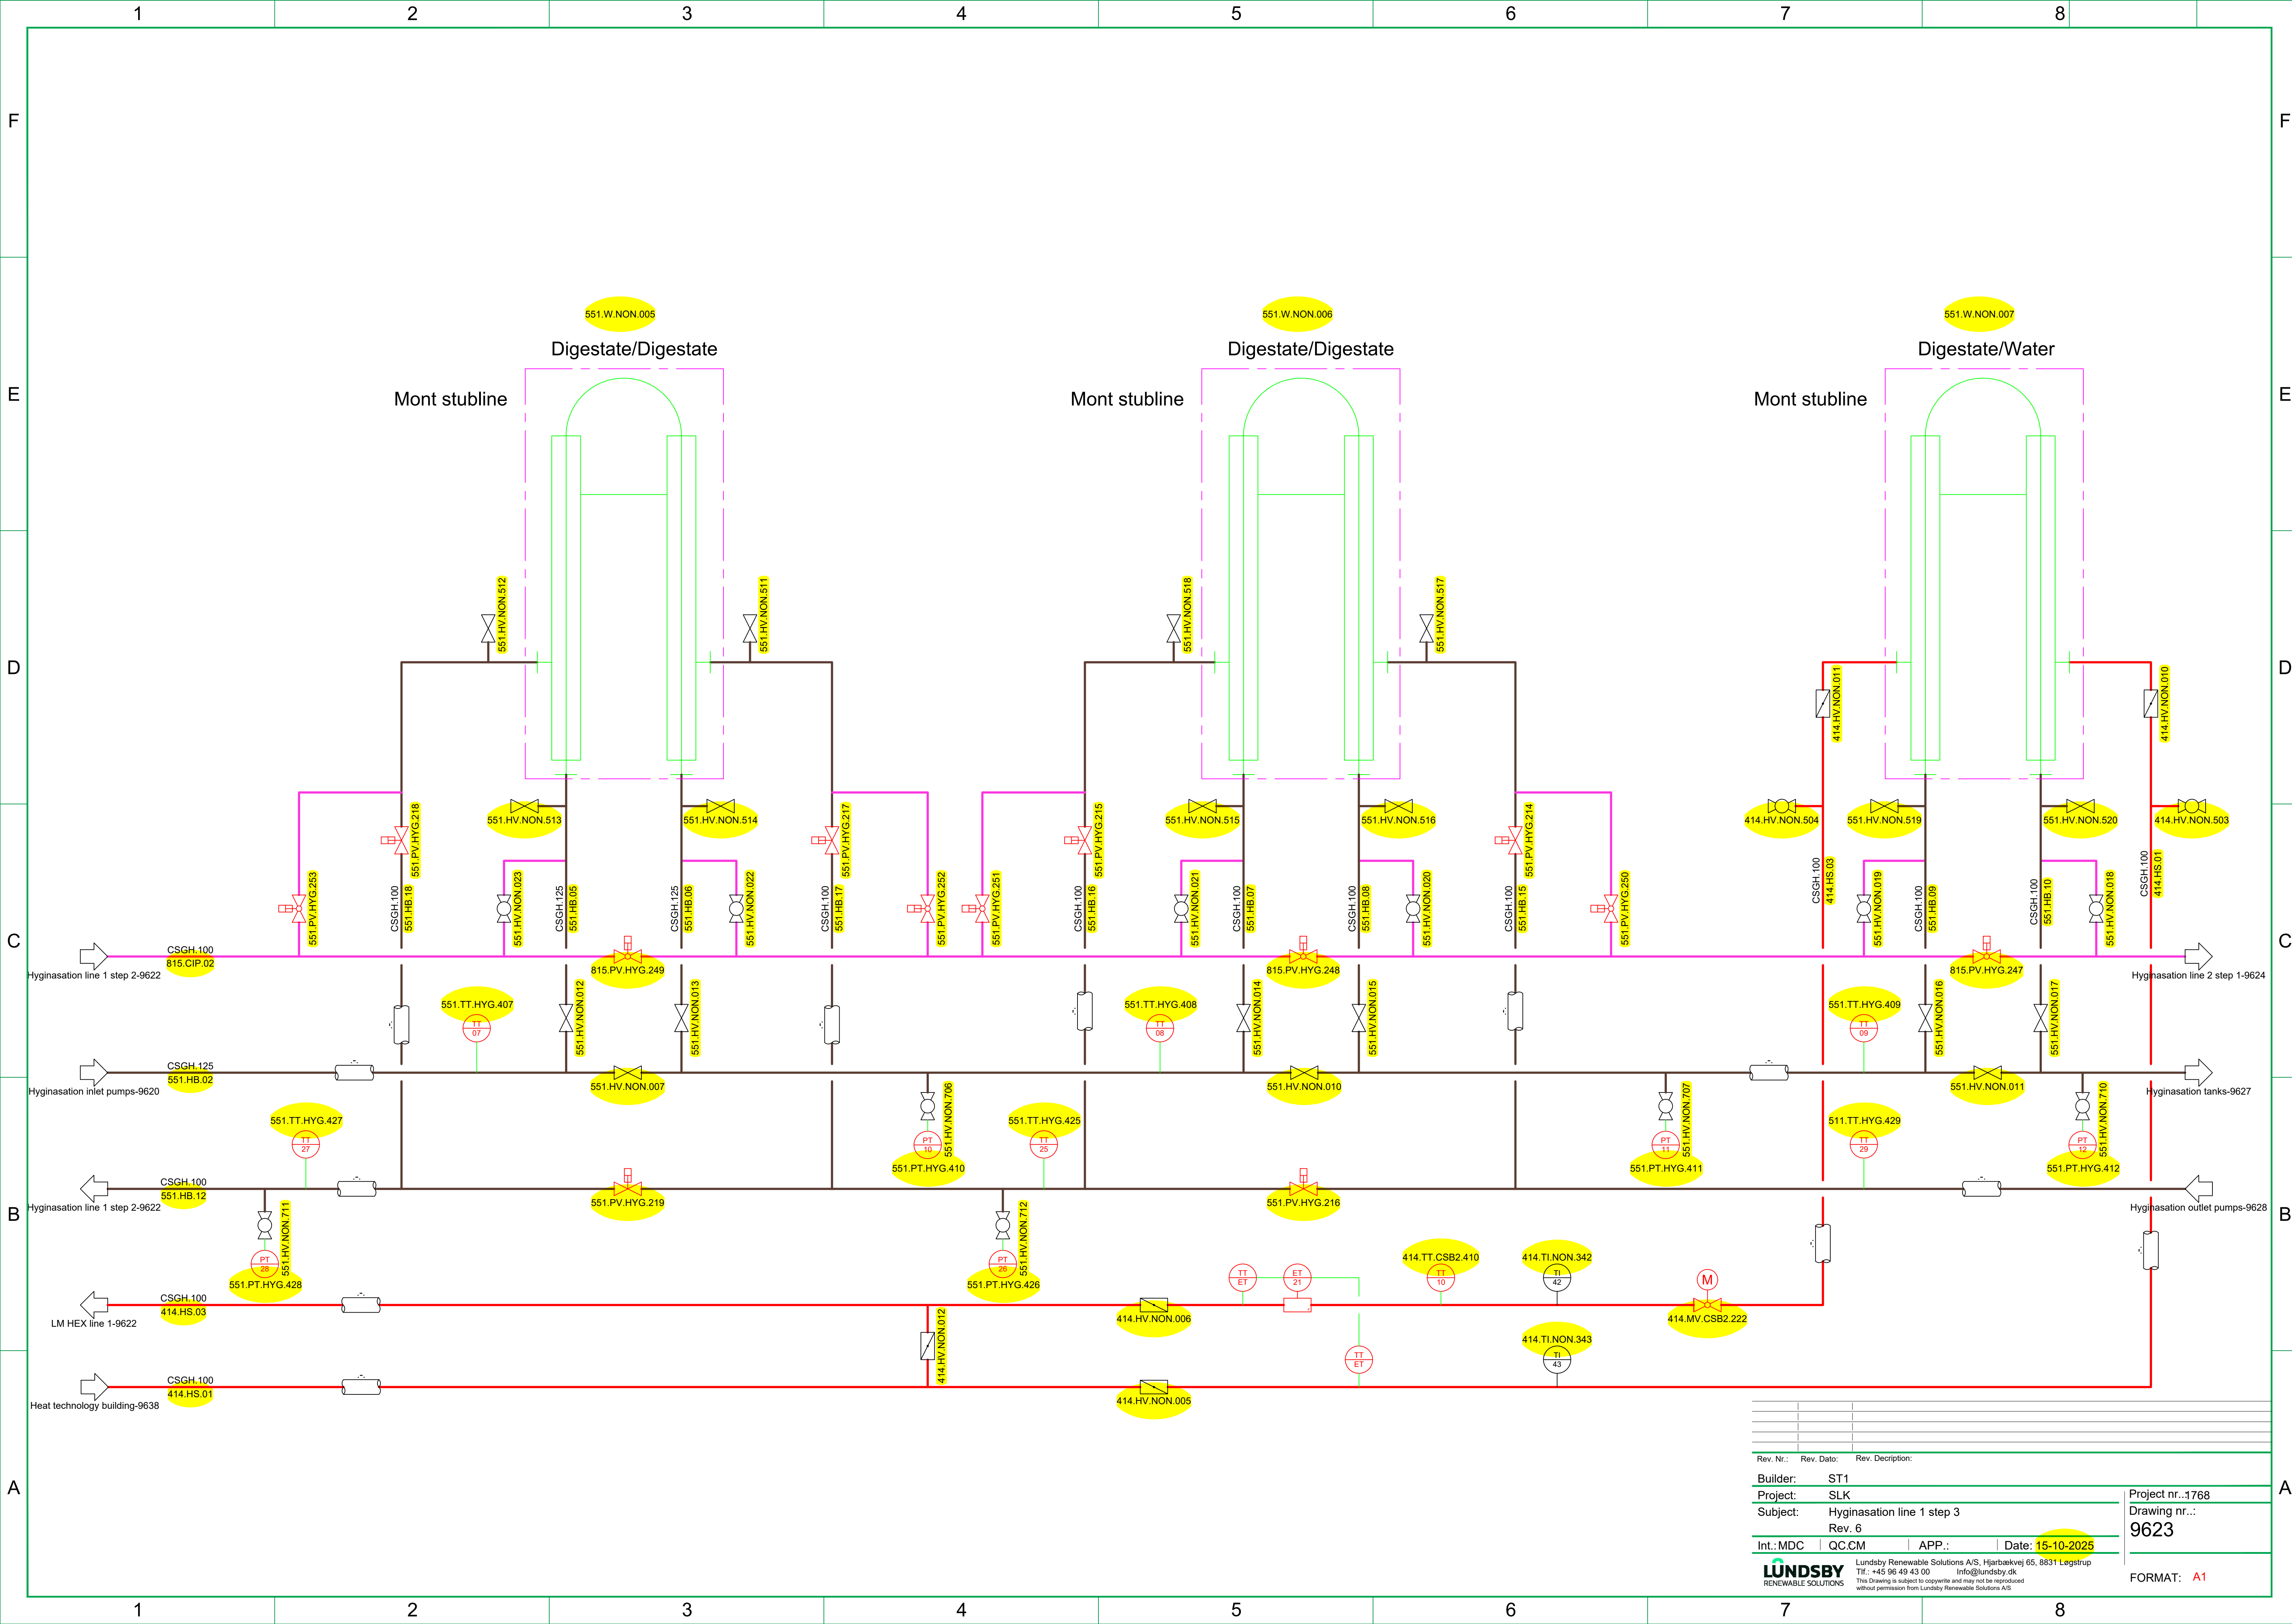


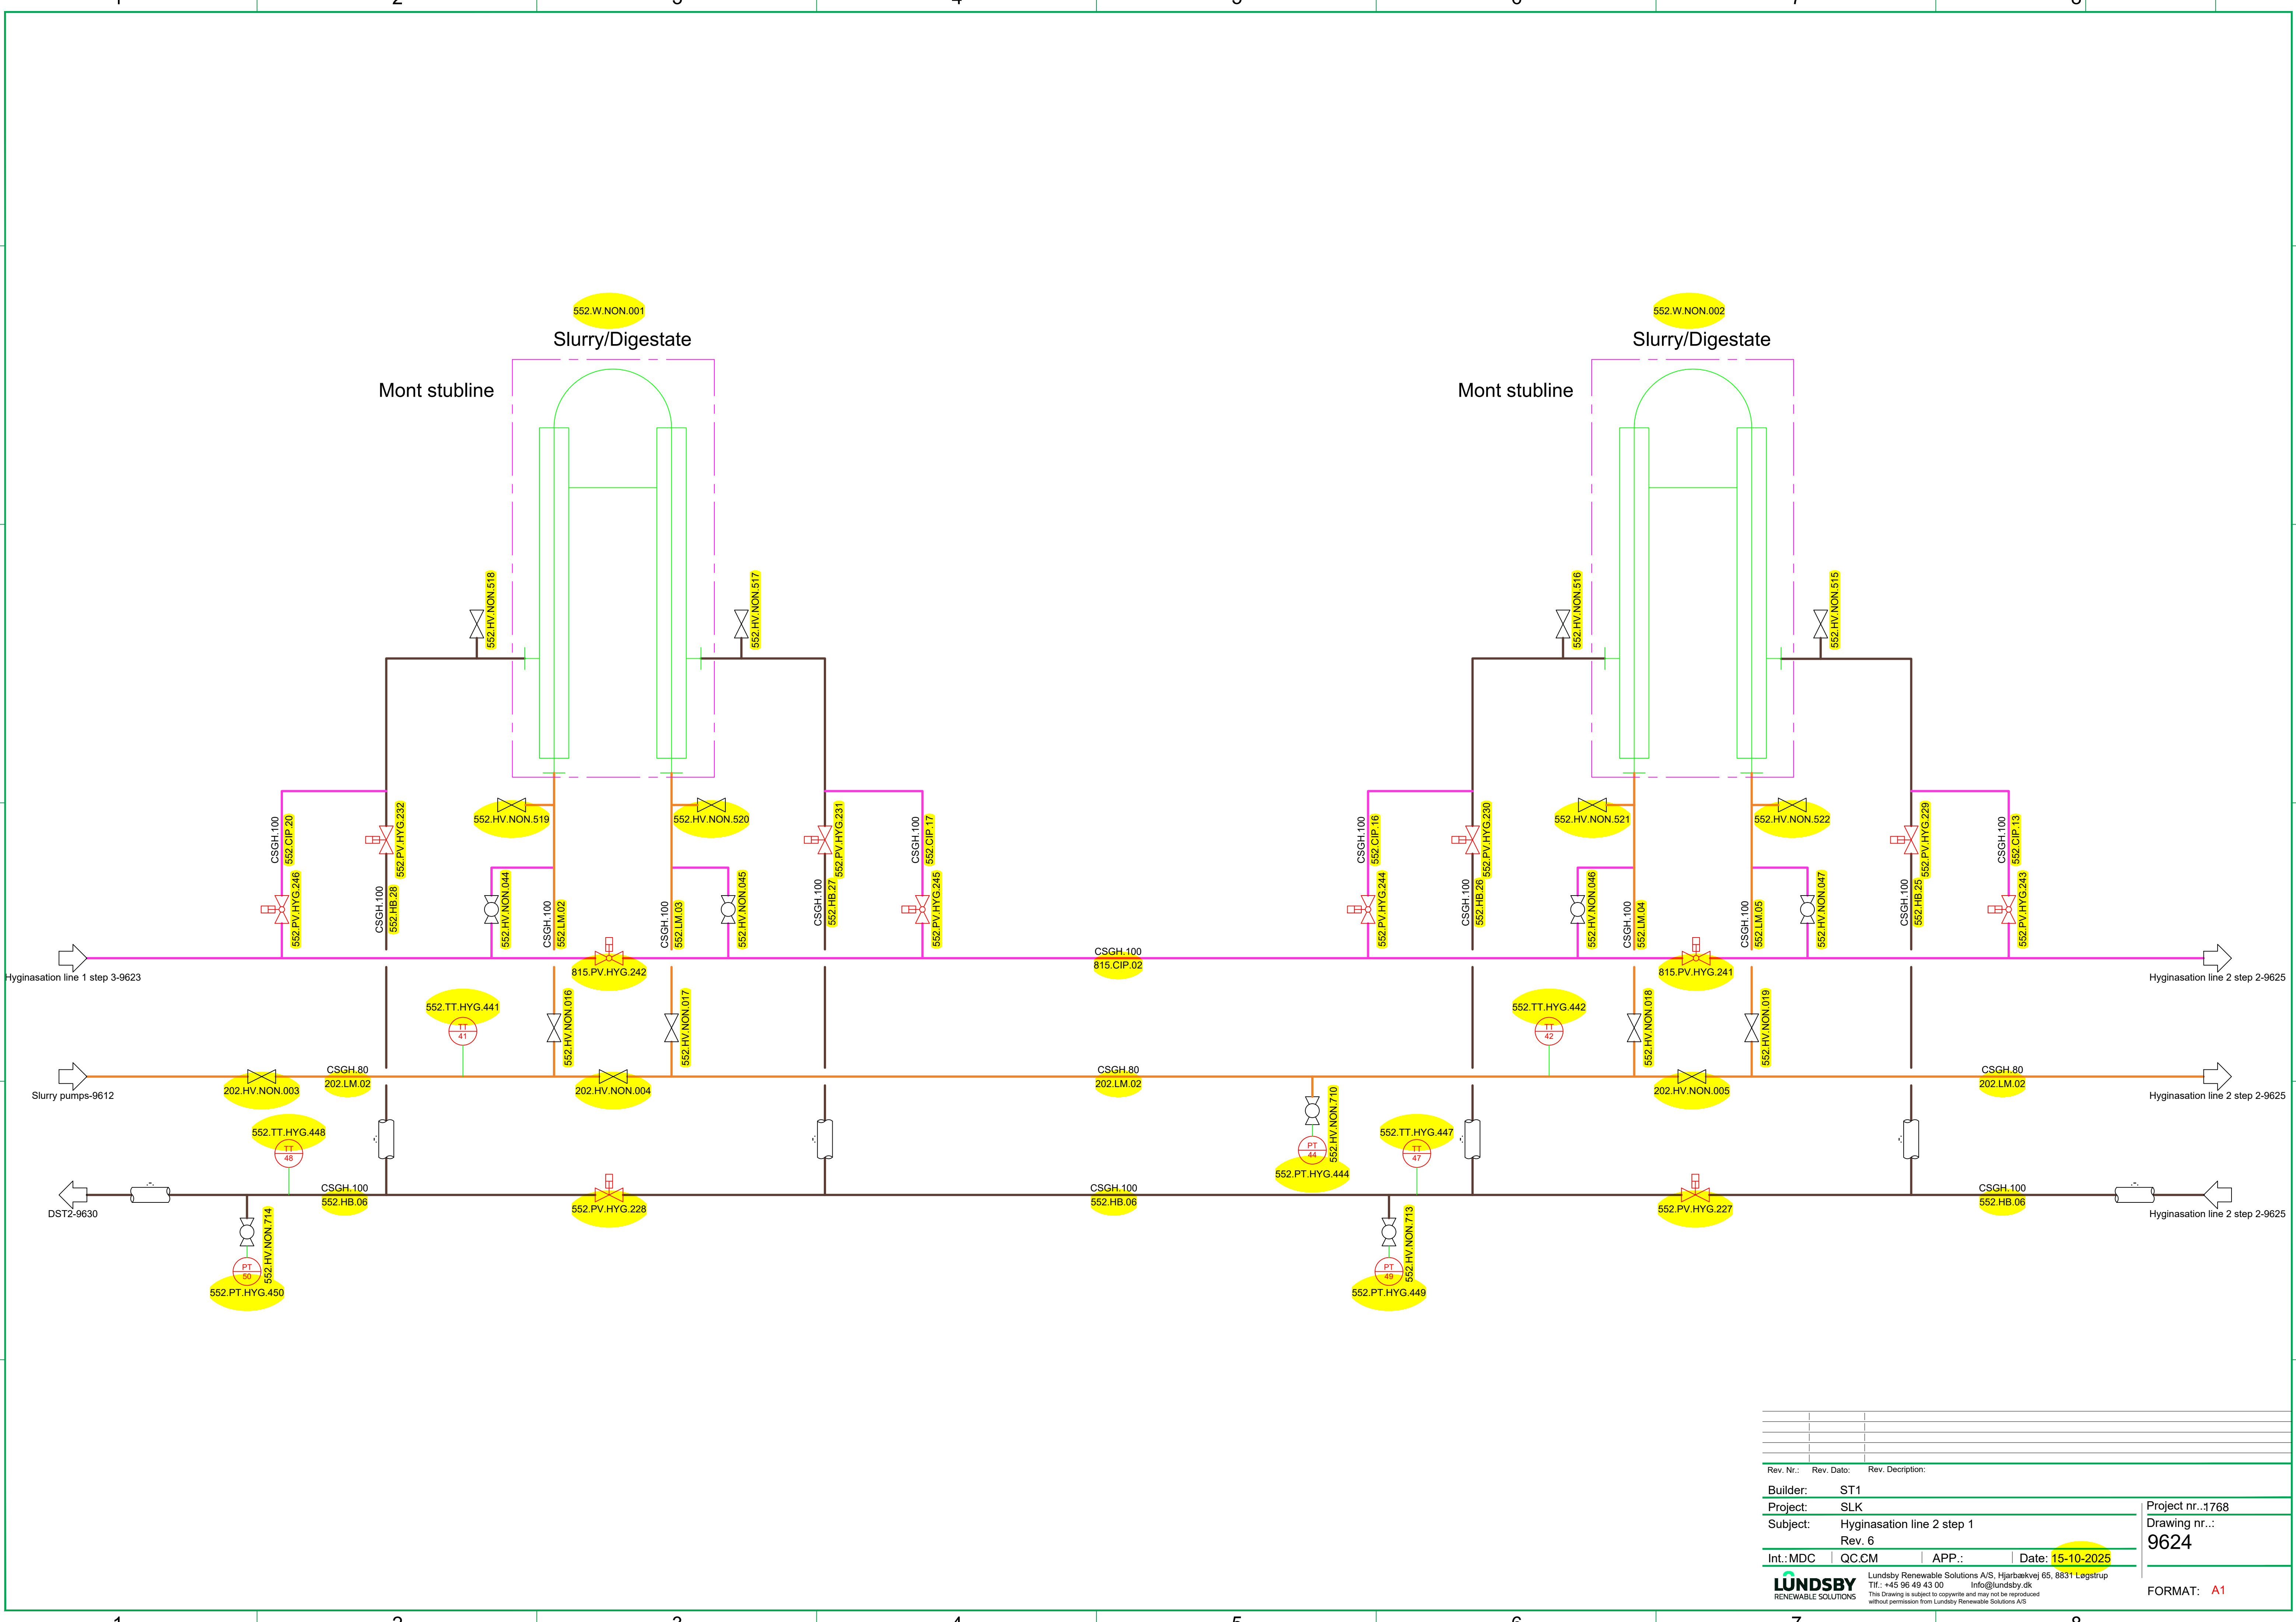

Rev. Nr.:	Rev. Dato:	Rev. Description:
Builder:	ST1	
Project:	SLK	
Subject:	Hyginasation line 2 step 1	
Rev. 6		
Int.:MDC	QC:CM	APP.:
Date:	15-10-2025	
LUNDSBY RENEWABLE SOLUTIONS		
Lundsby Renewable Solutions A/S, Hjarbækvej 65, 8831 Løgstrup Tlf.: +45 96 49 43 00 Info@lundsby.dk This Drawing is subject to copyright and may not be reproduced without permission from Lundsby Renewable Solutions A/S		
Project nr.:1768 Drawing nr.: 9624		FORMAT: A1

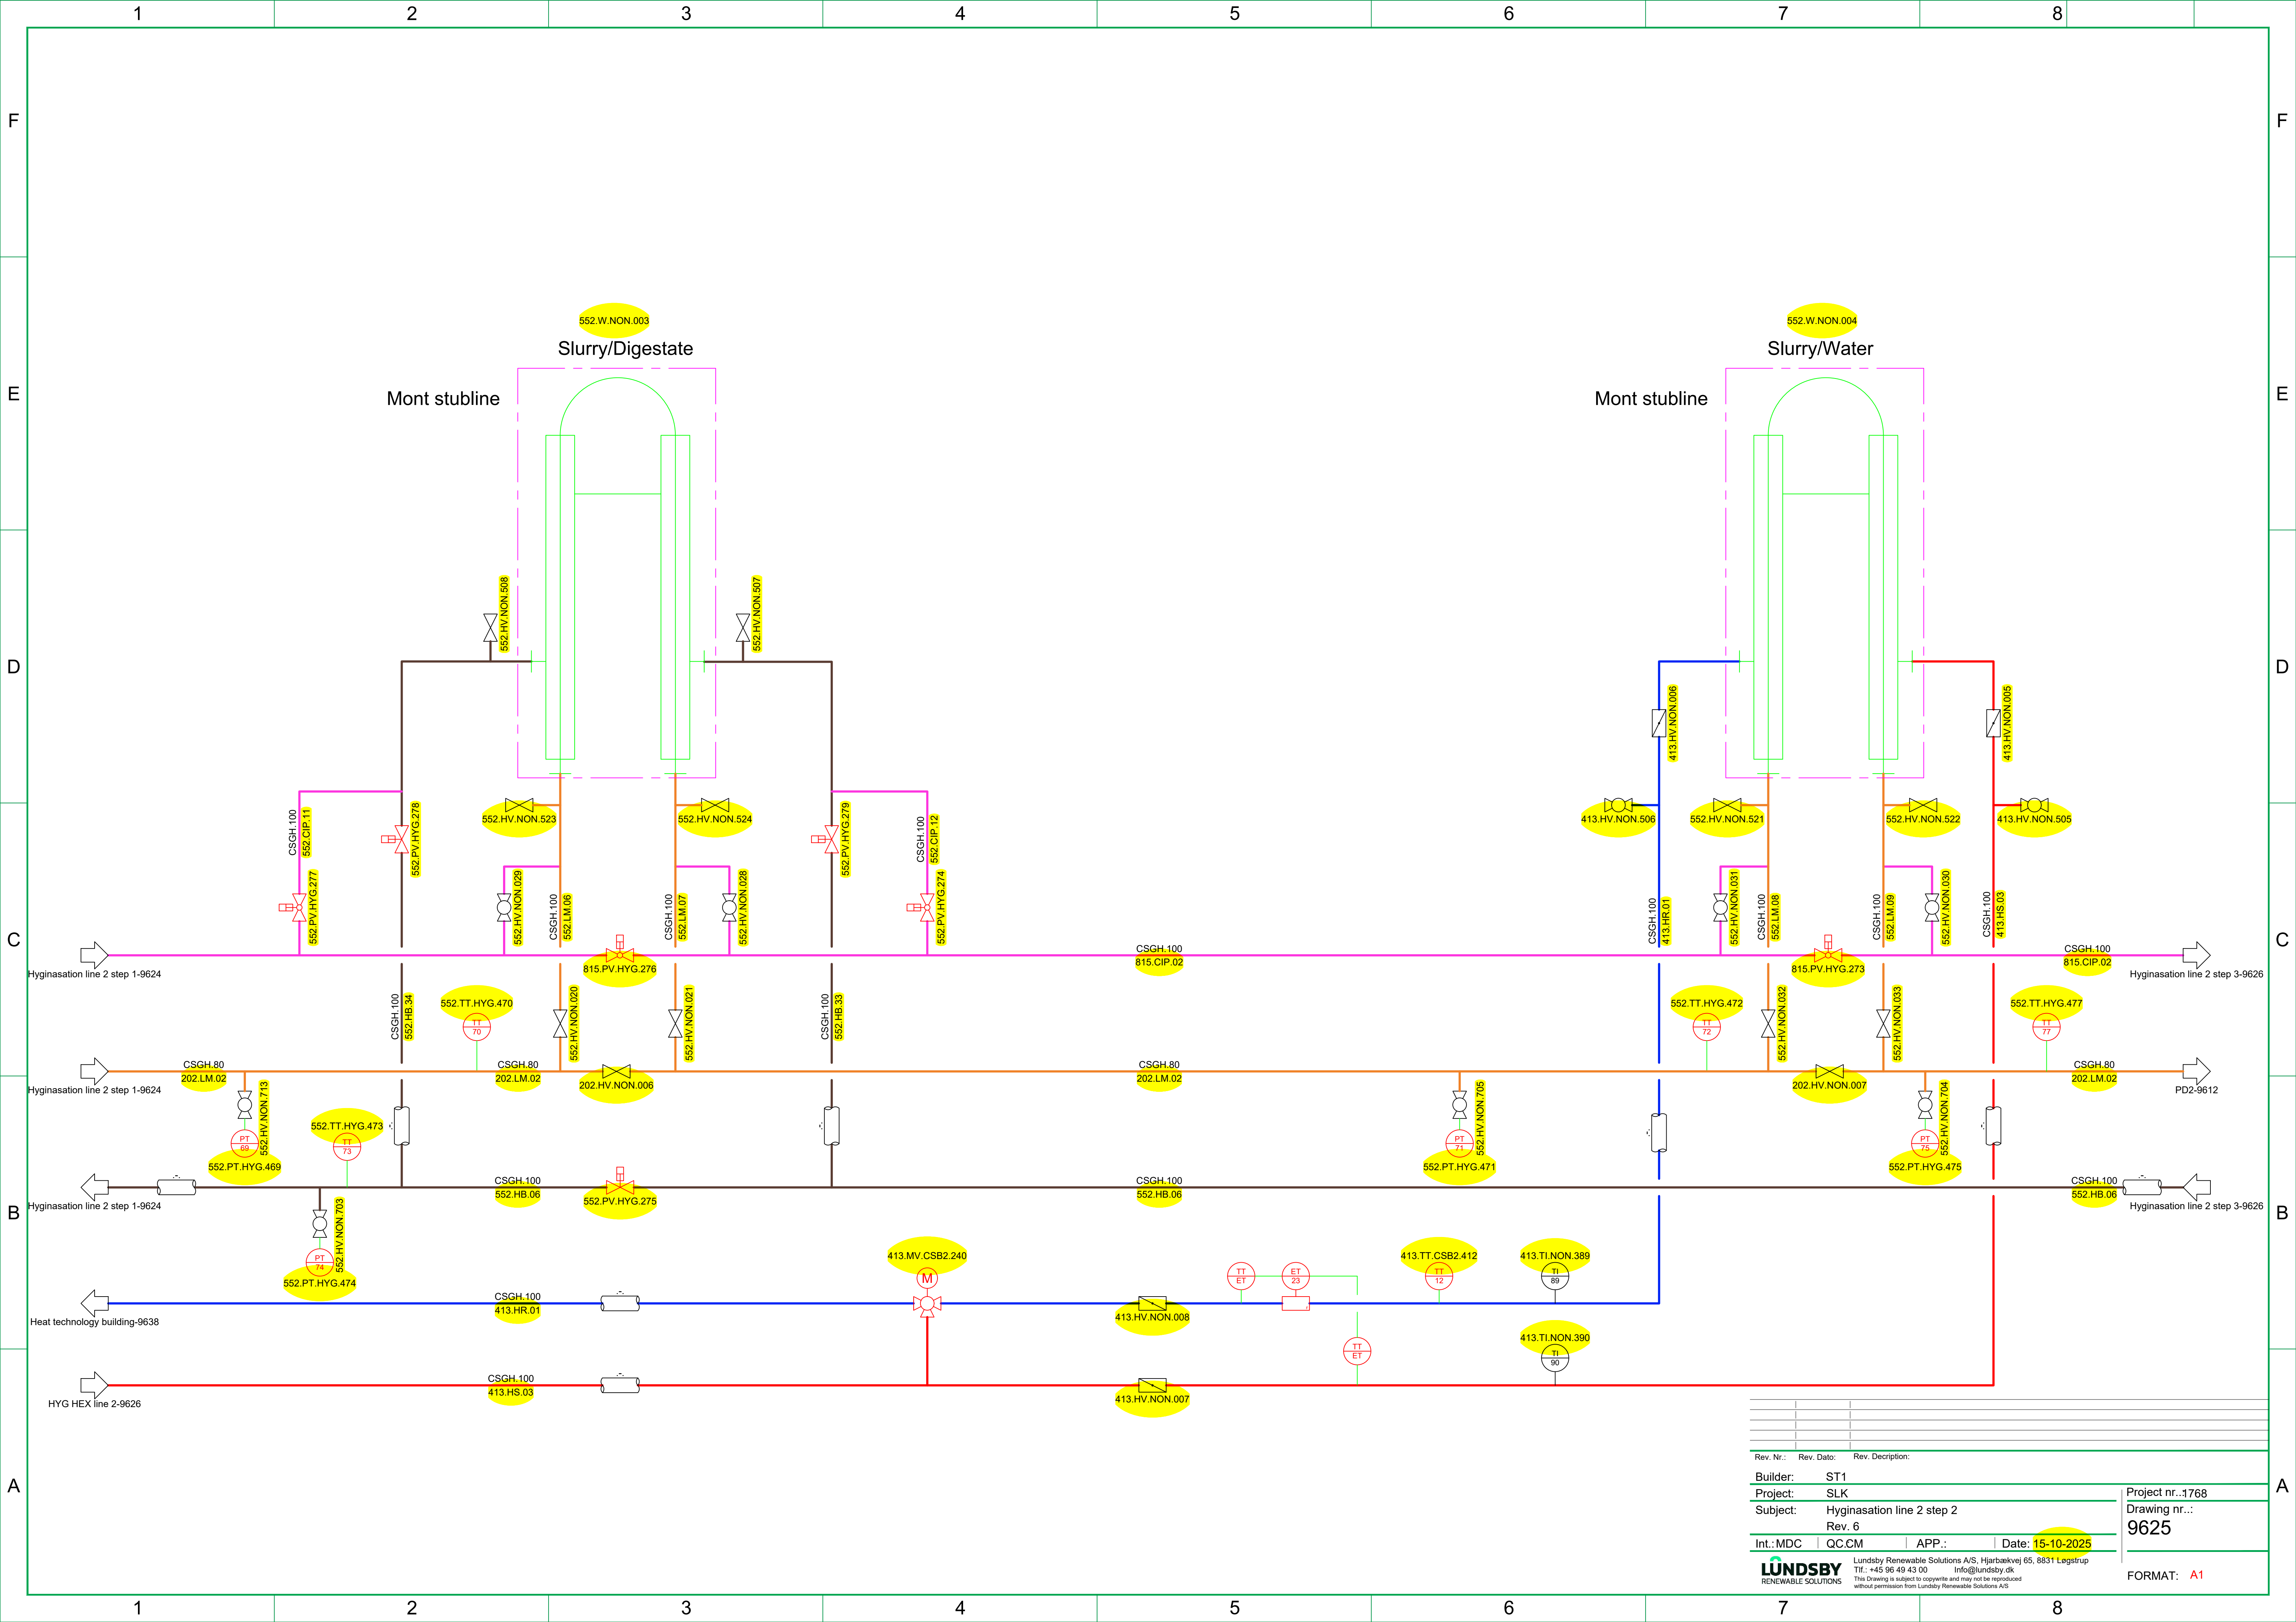

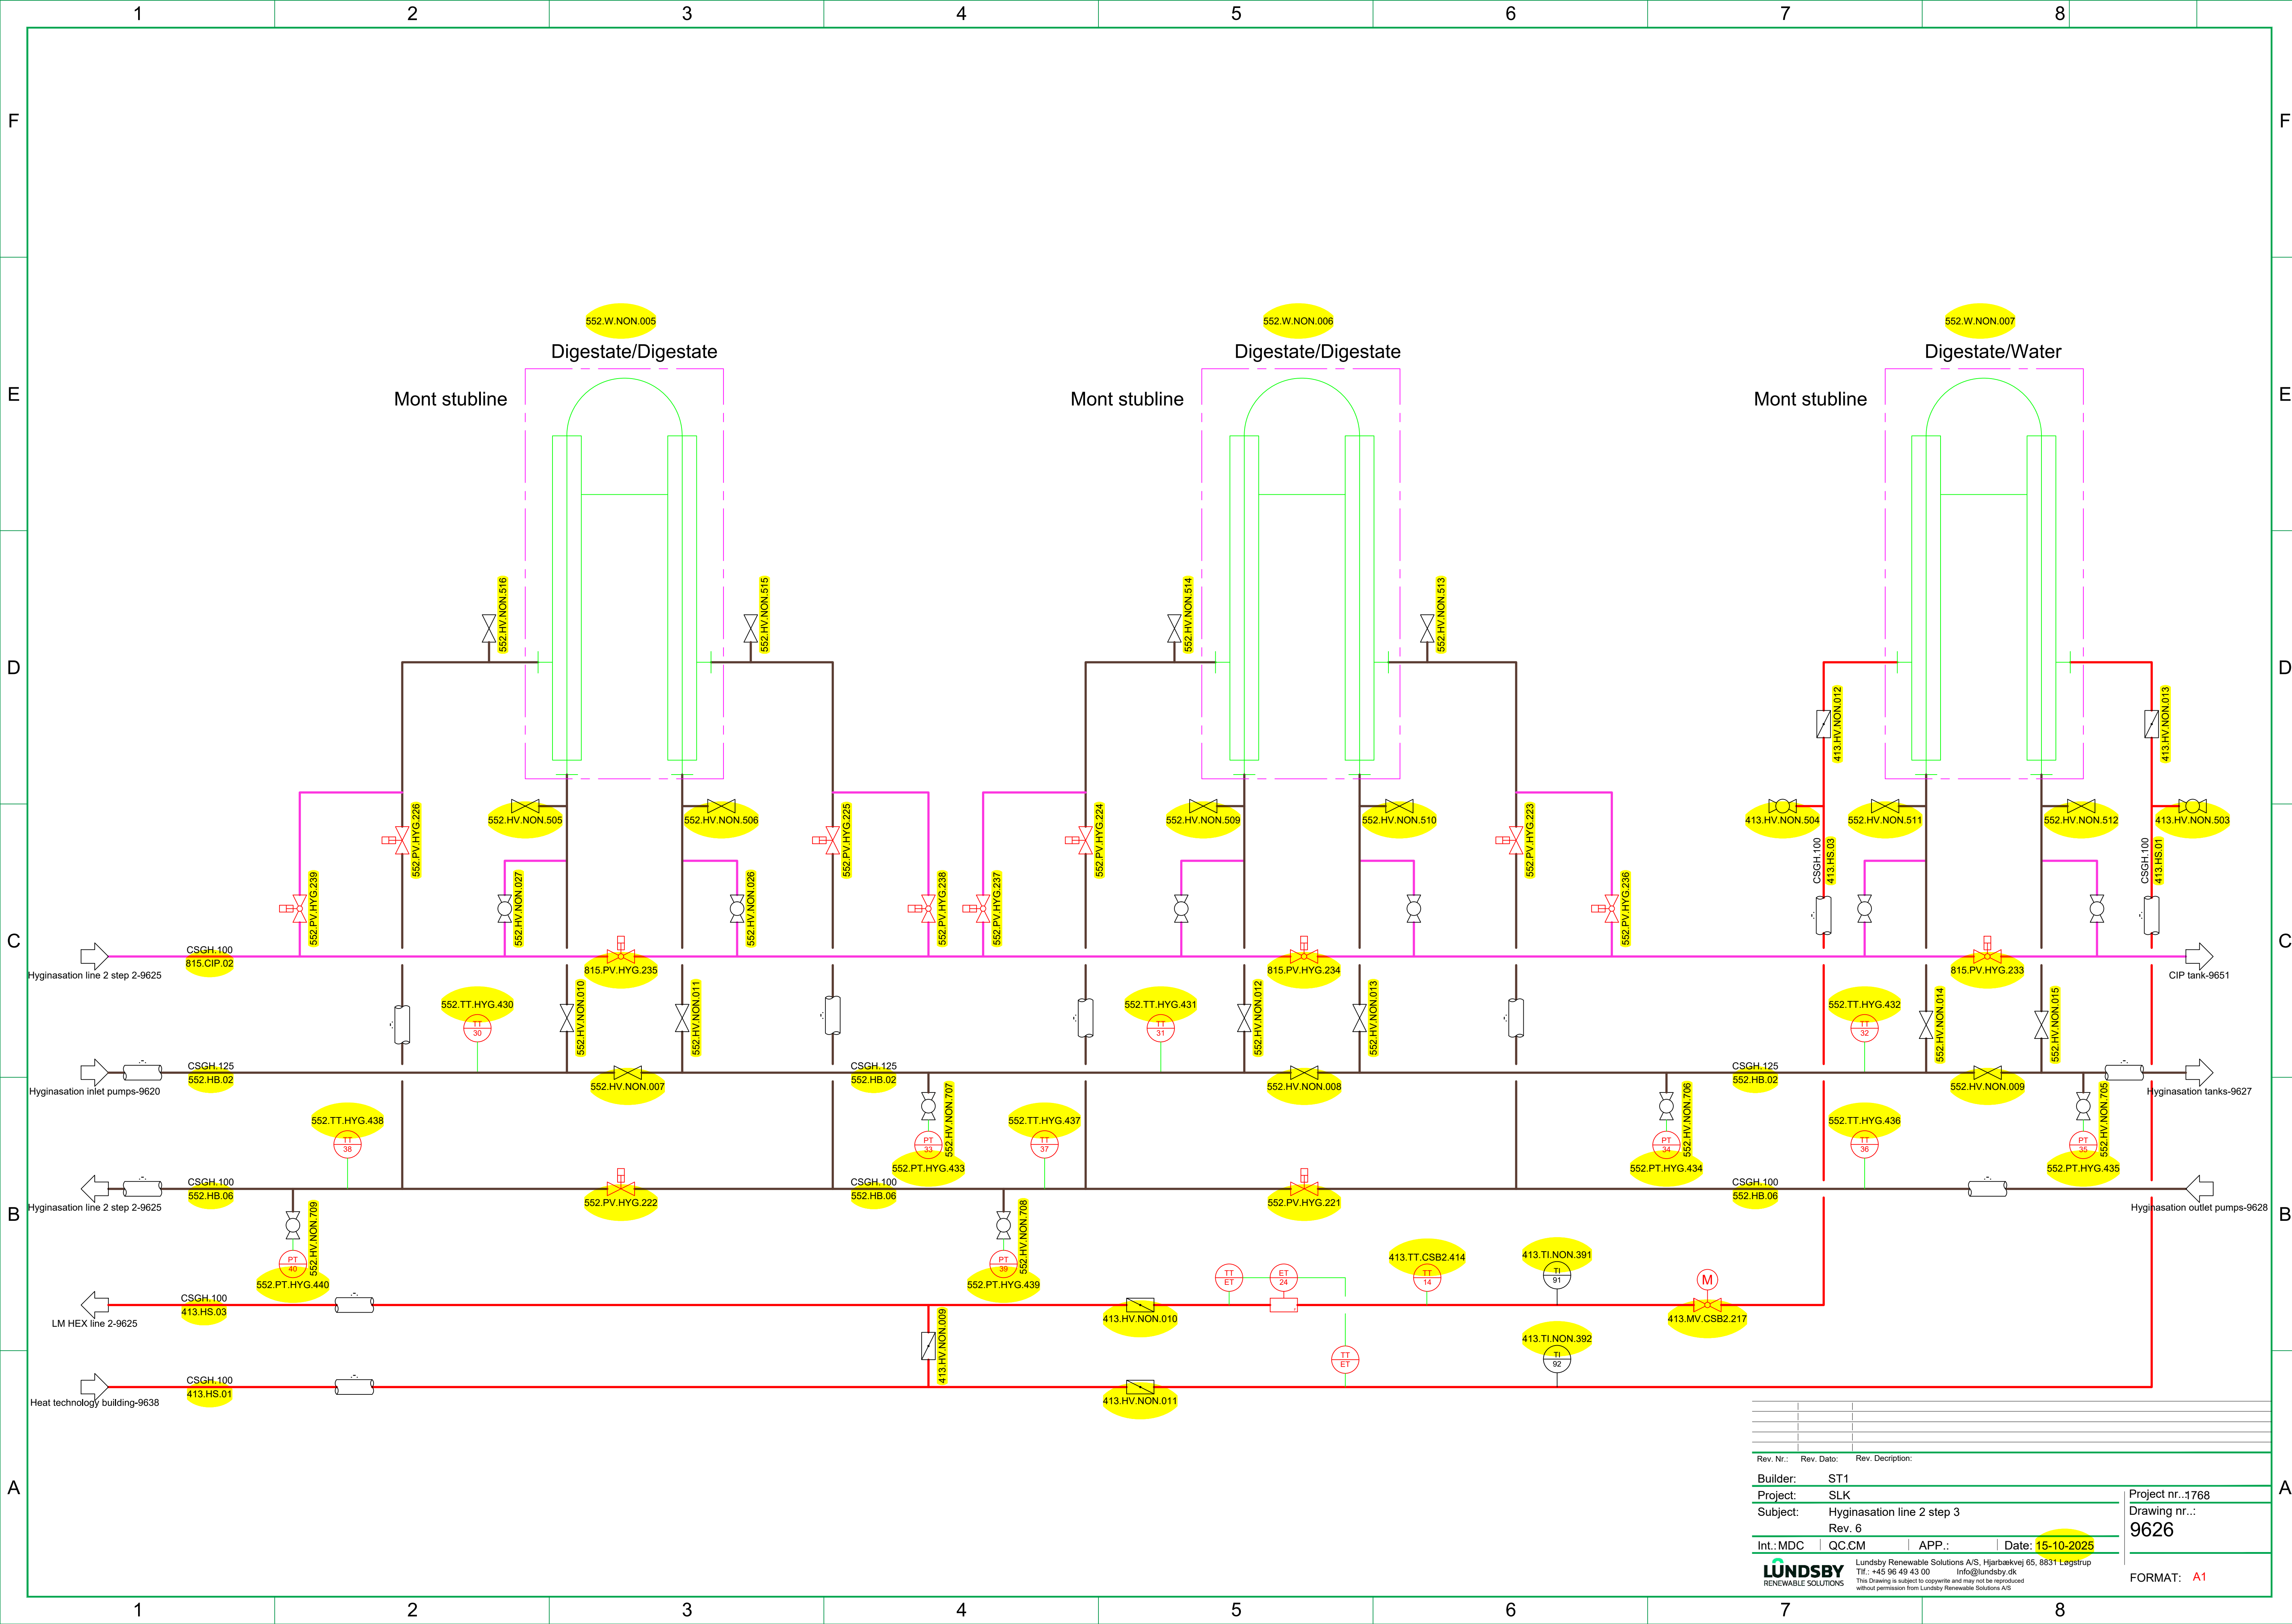


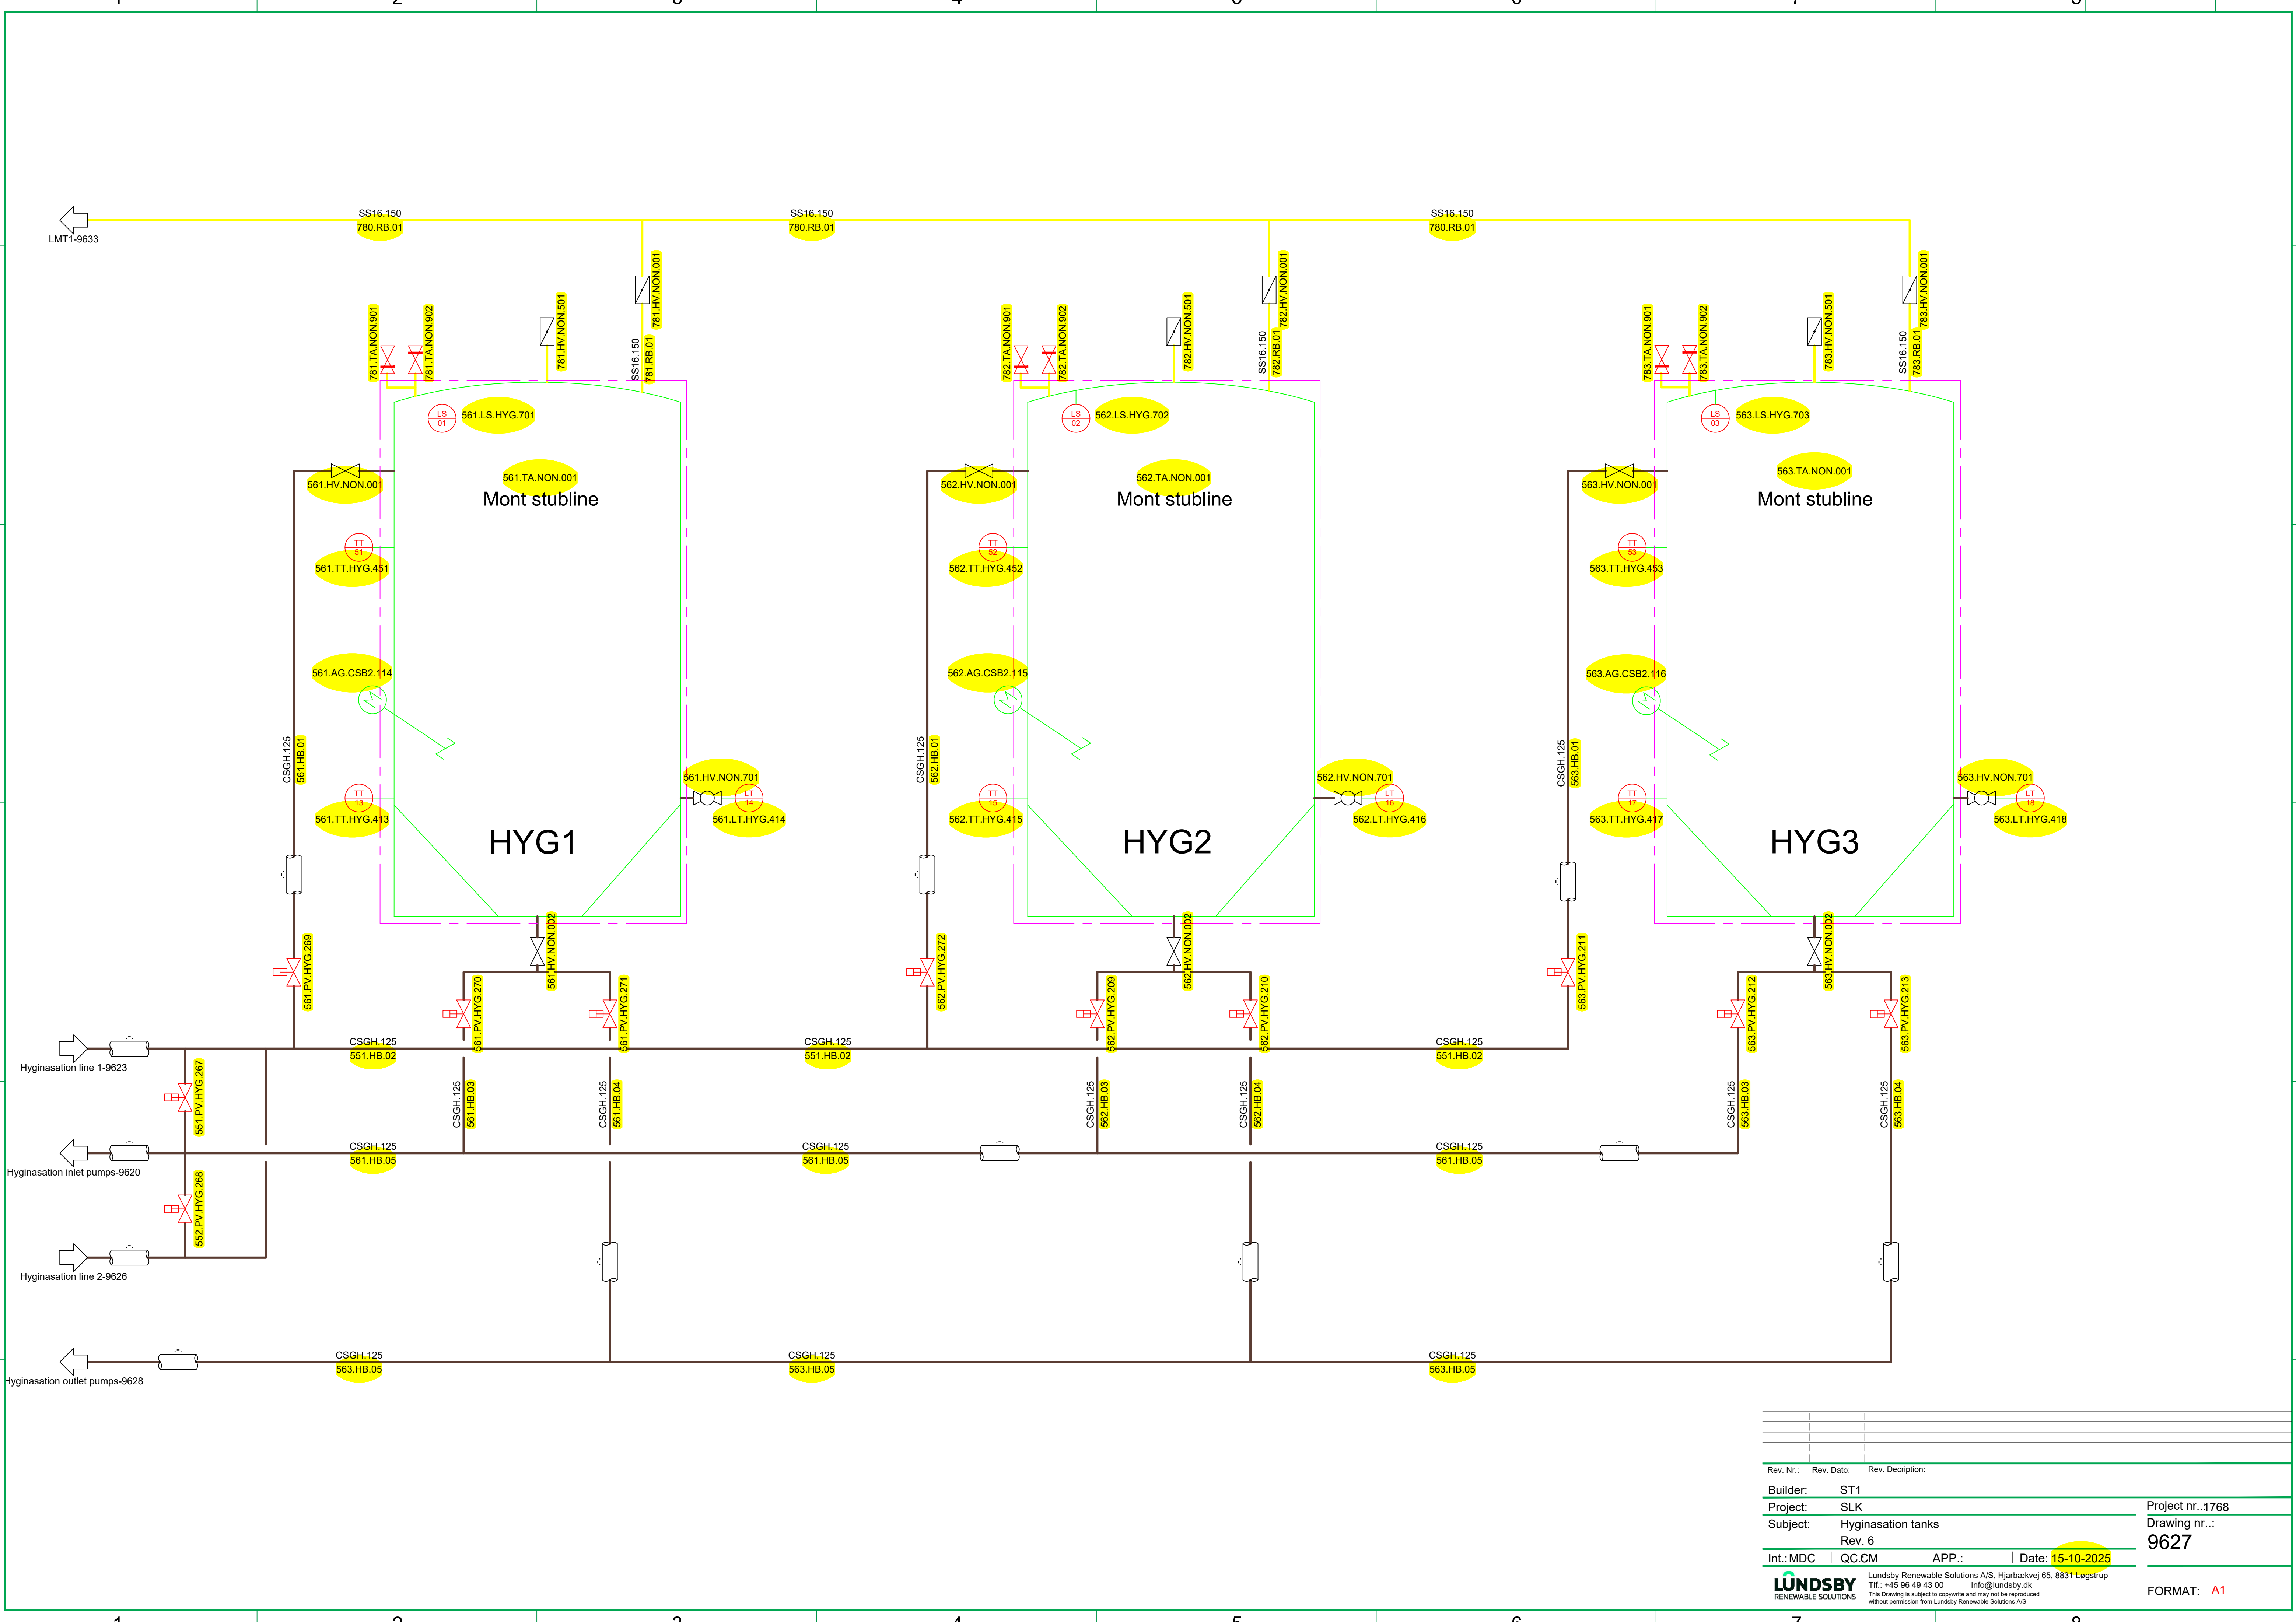


Rev. Nr.: Rev. Dato: Rev. Description:			
Builder: ST1			
Project: SLK			
Subject: Hyginasation tanks			
Rev. 6			
Int.: MDC	QC.CM	APP.:	Date: 15-10-2025
LUNDSBY RENEWABLE SOLUTIONS			
Lundsby Renewable Solutions A/S, Hjarbækvej 65, 8831 Løgstrup Tlf.: +45 96 49 43 00 Info@lundsby.dk This Drawing is subject to copyright and may not be reproduced without permission from Lundsby Renewable Solutions A/S			
Project nr.: 1768 Drawing nr.: 9627			FORMAT: A1

Tech Building


Outlet pumps

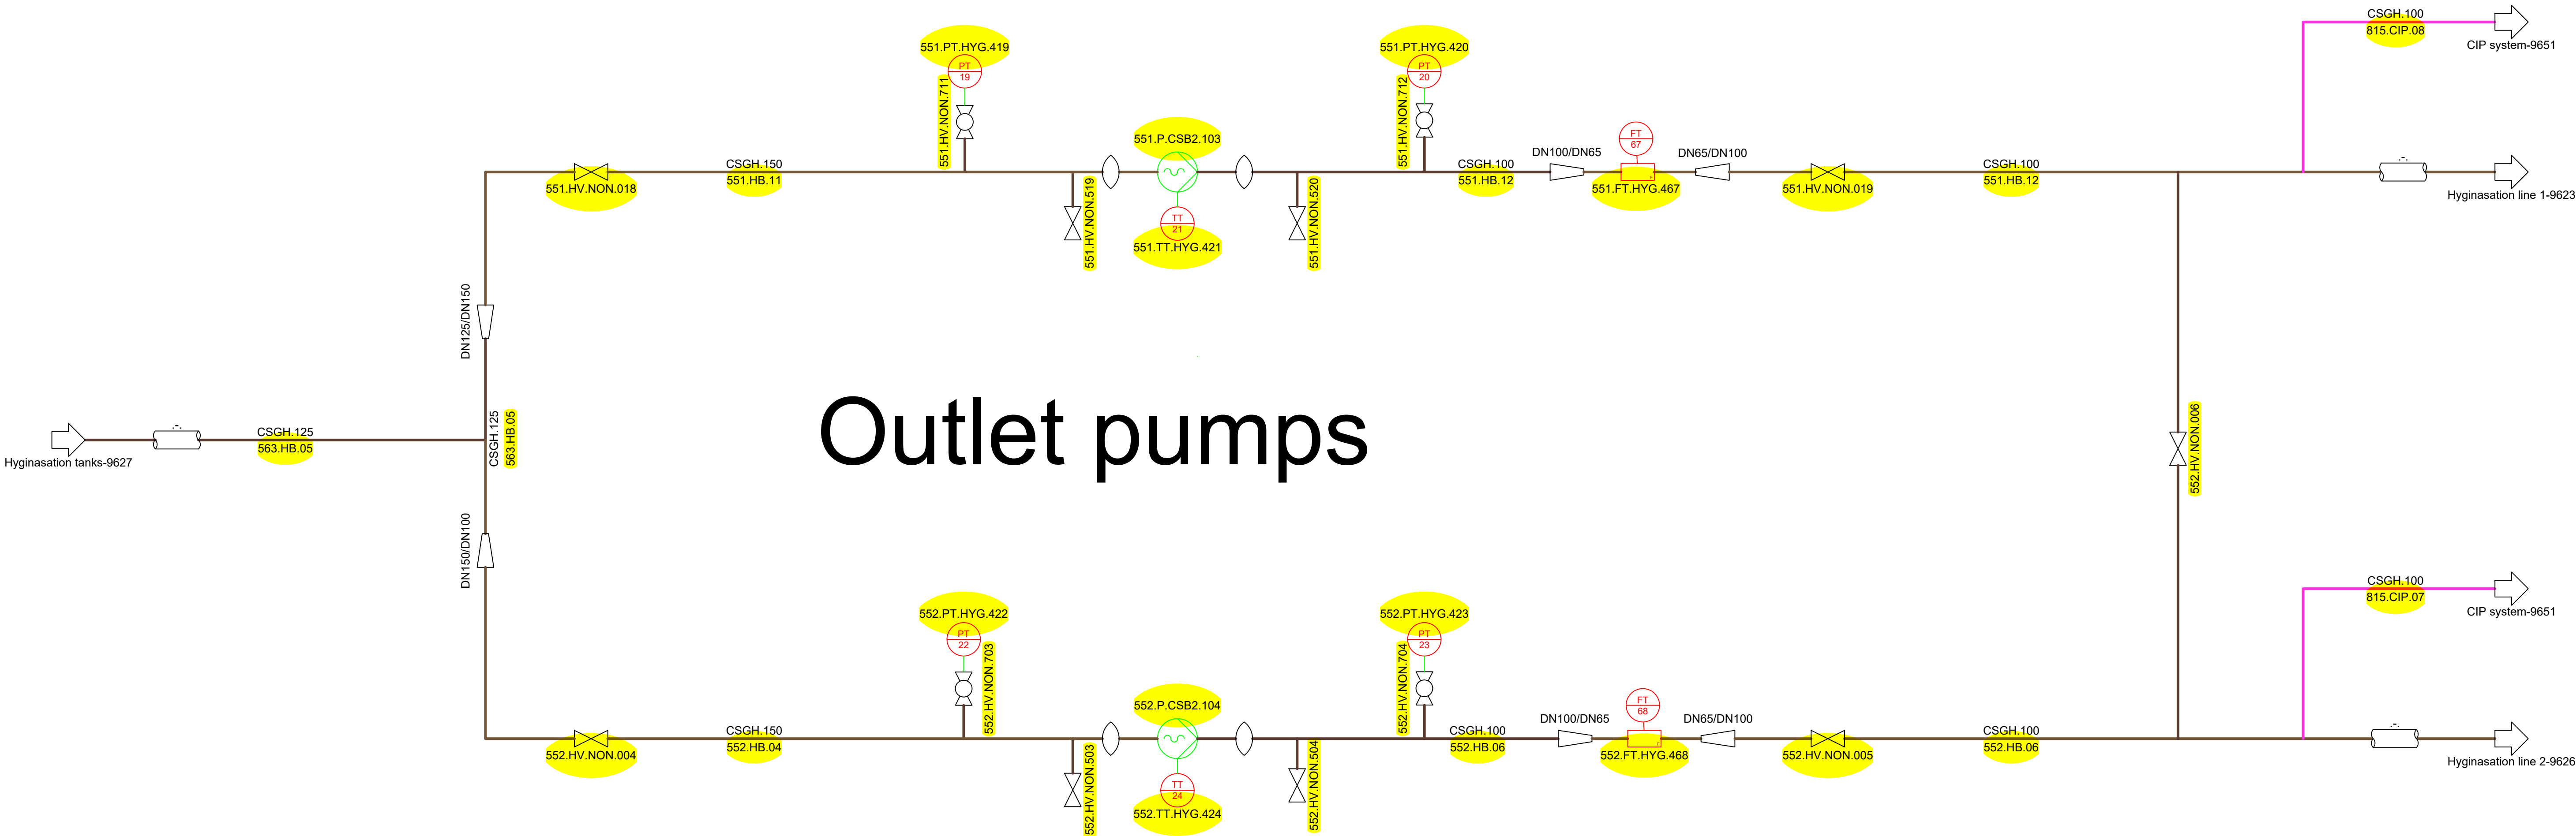


Rev. Nr.:	Rev. Dato:	Rev. Description:	Project nr.:1768
Builder:	ST1		Drawing nr.:9628
Project:	SLK		
Subject:	Hyginasation outlet pumps		
Rev. 6			
Int.:MDC	QC:CM	APP.:	Date:15-10-2025
LUNDSBY RENEWABLE SOLUTIONS			FORMAT: A1

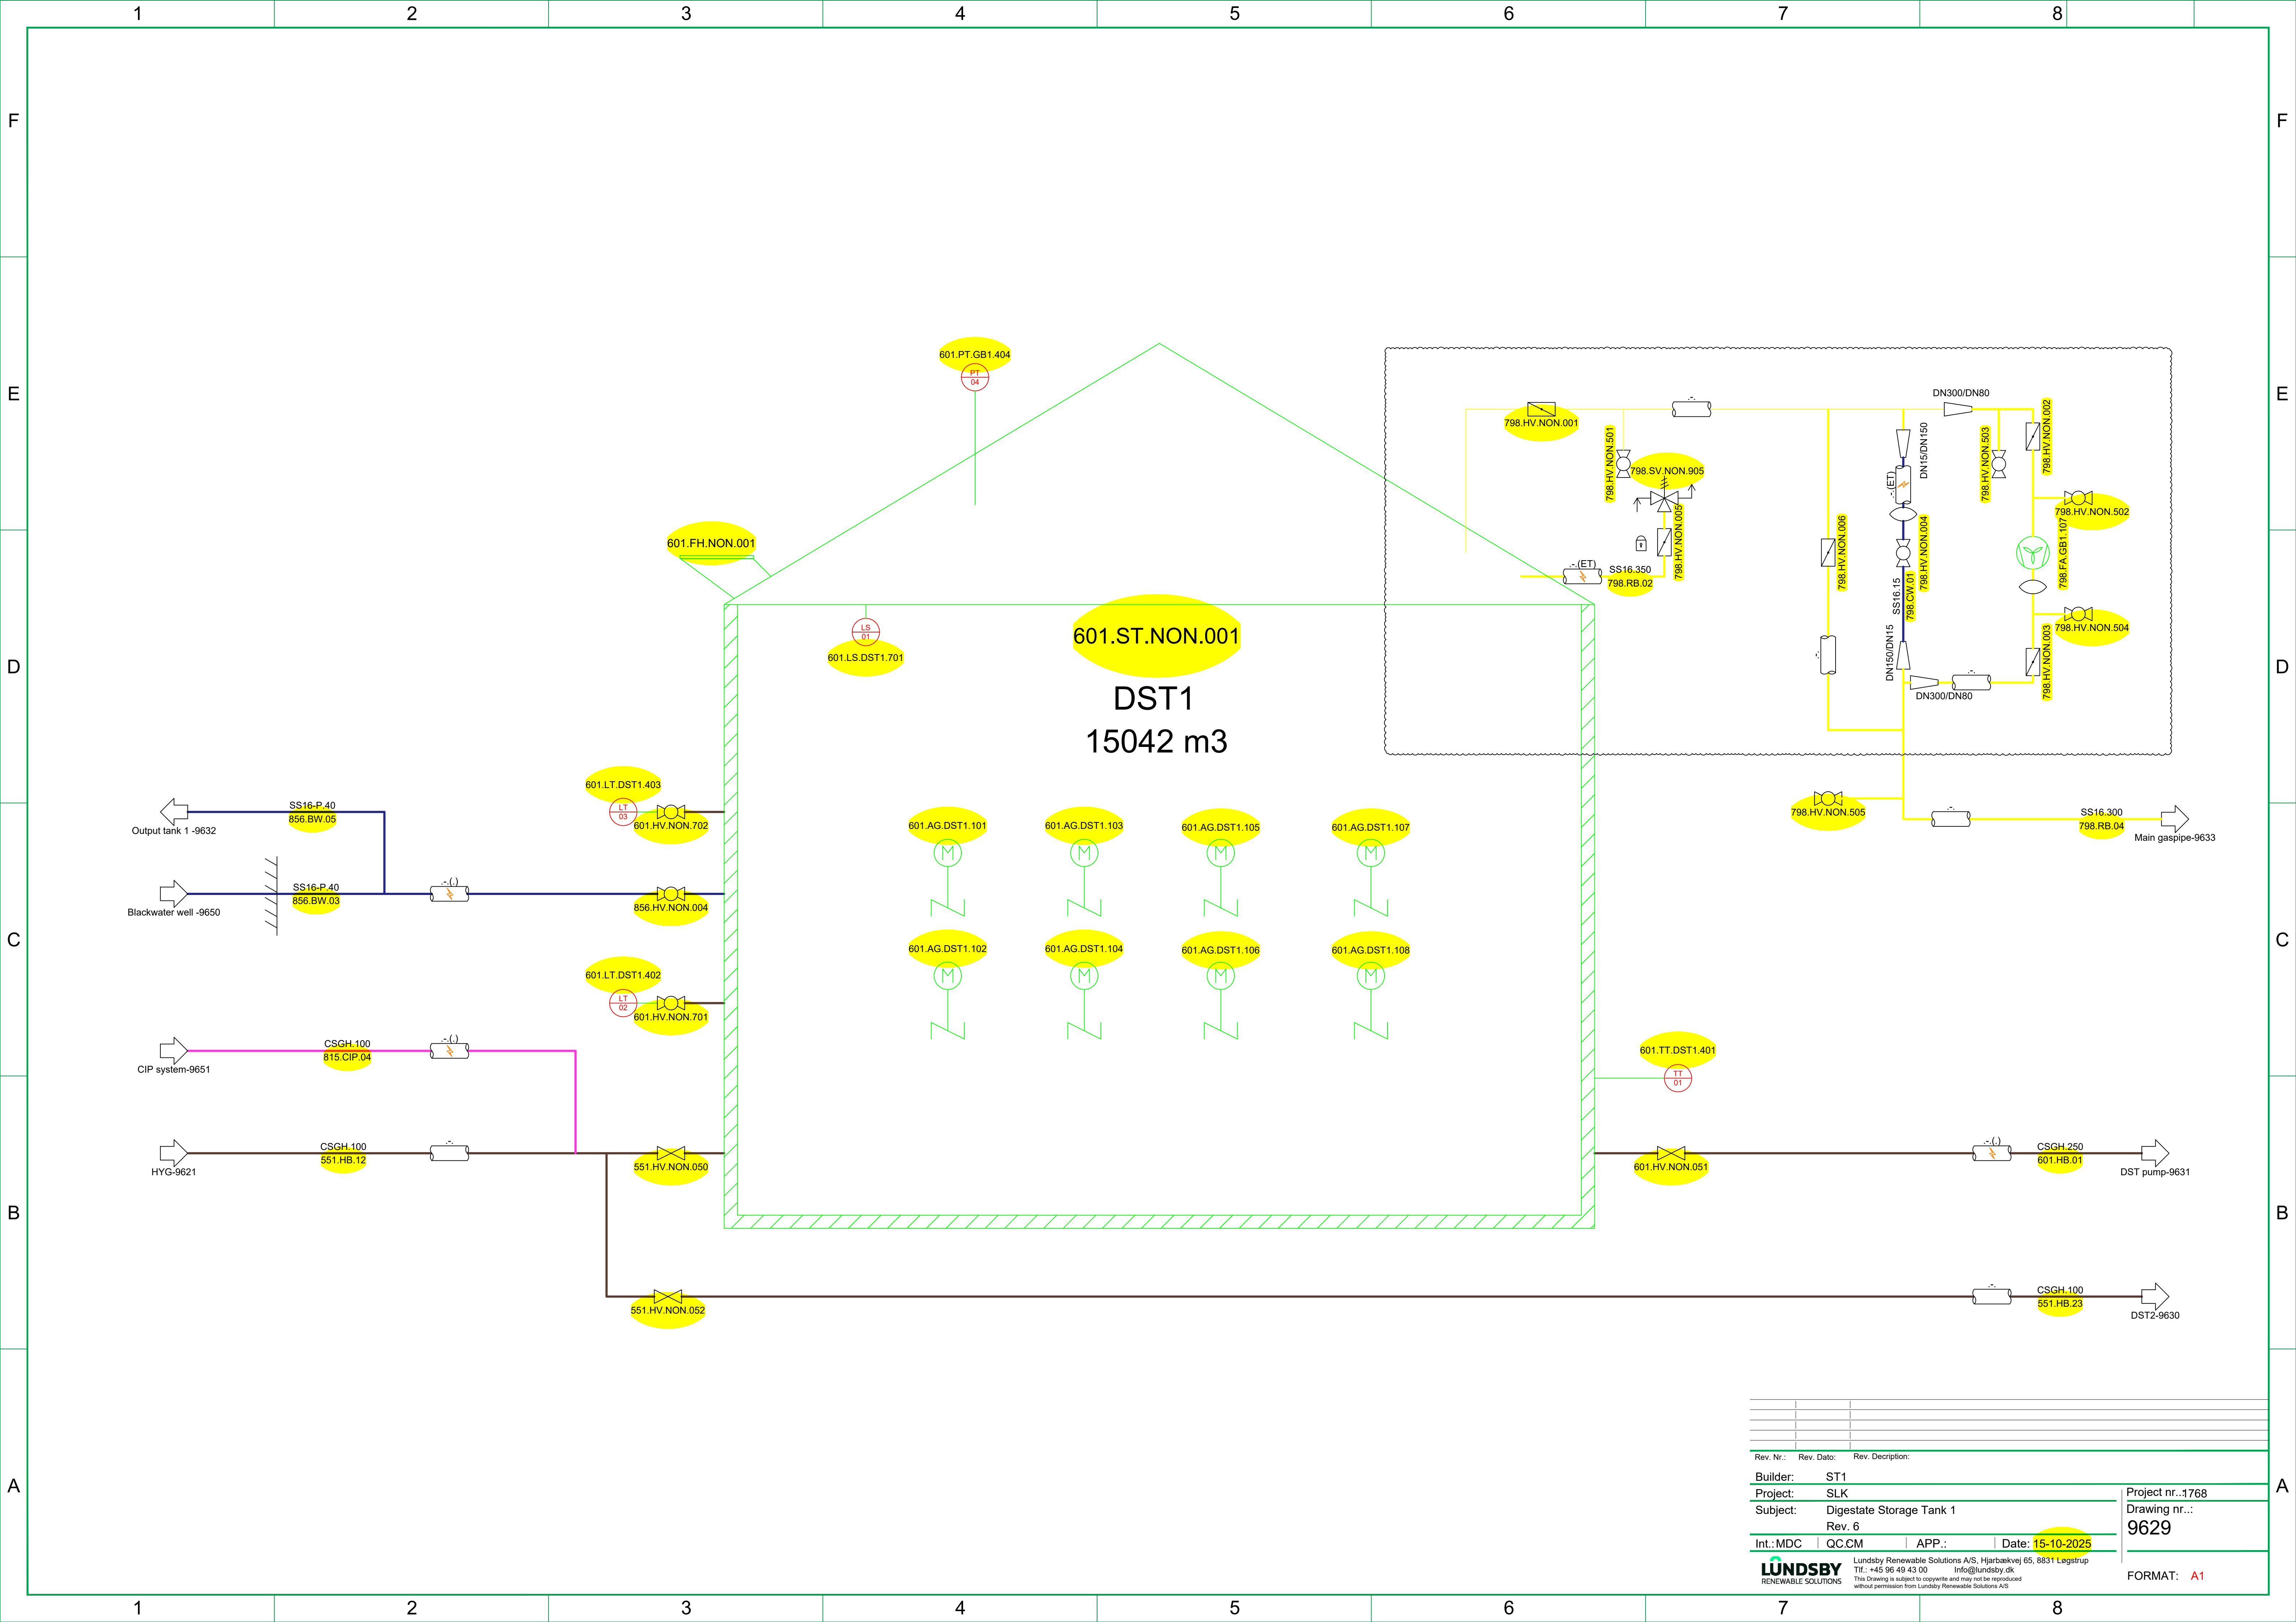


Rev. Nr.:	Rev. Dato:	Rev. Description:
Builder:	ST1	
Project:	SLK	
Subject:	Digestate Storage Tank 1	
Int.:MDC	QC&M	APP.:
Date:	15-10-2025	
LUNDSBY RENEWABLE SOLUTIONS		
Lundsby Renewable Solutions A/S, Hjarbrækvej 65, 8831 Løgstrup Tlf.: +45 96 49 43 00 Info@lundsby.dk This drawing is subject to copyright and may not be reproduced without permission from Lundsby Renewable Solutions A/S		
Project nr.:1768		
Drawing nr.: 9629		
FORMAT: A1		

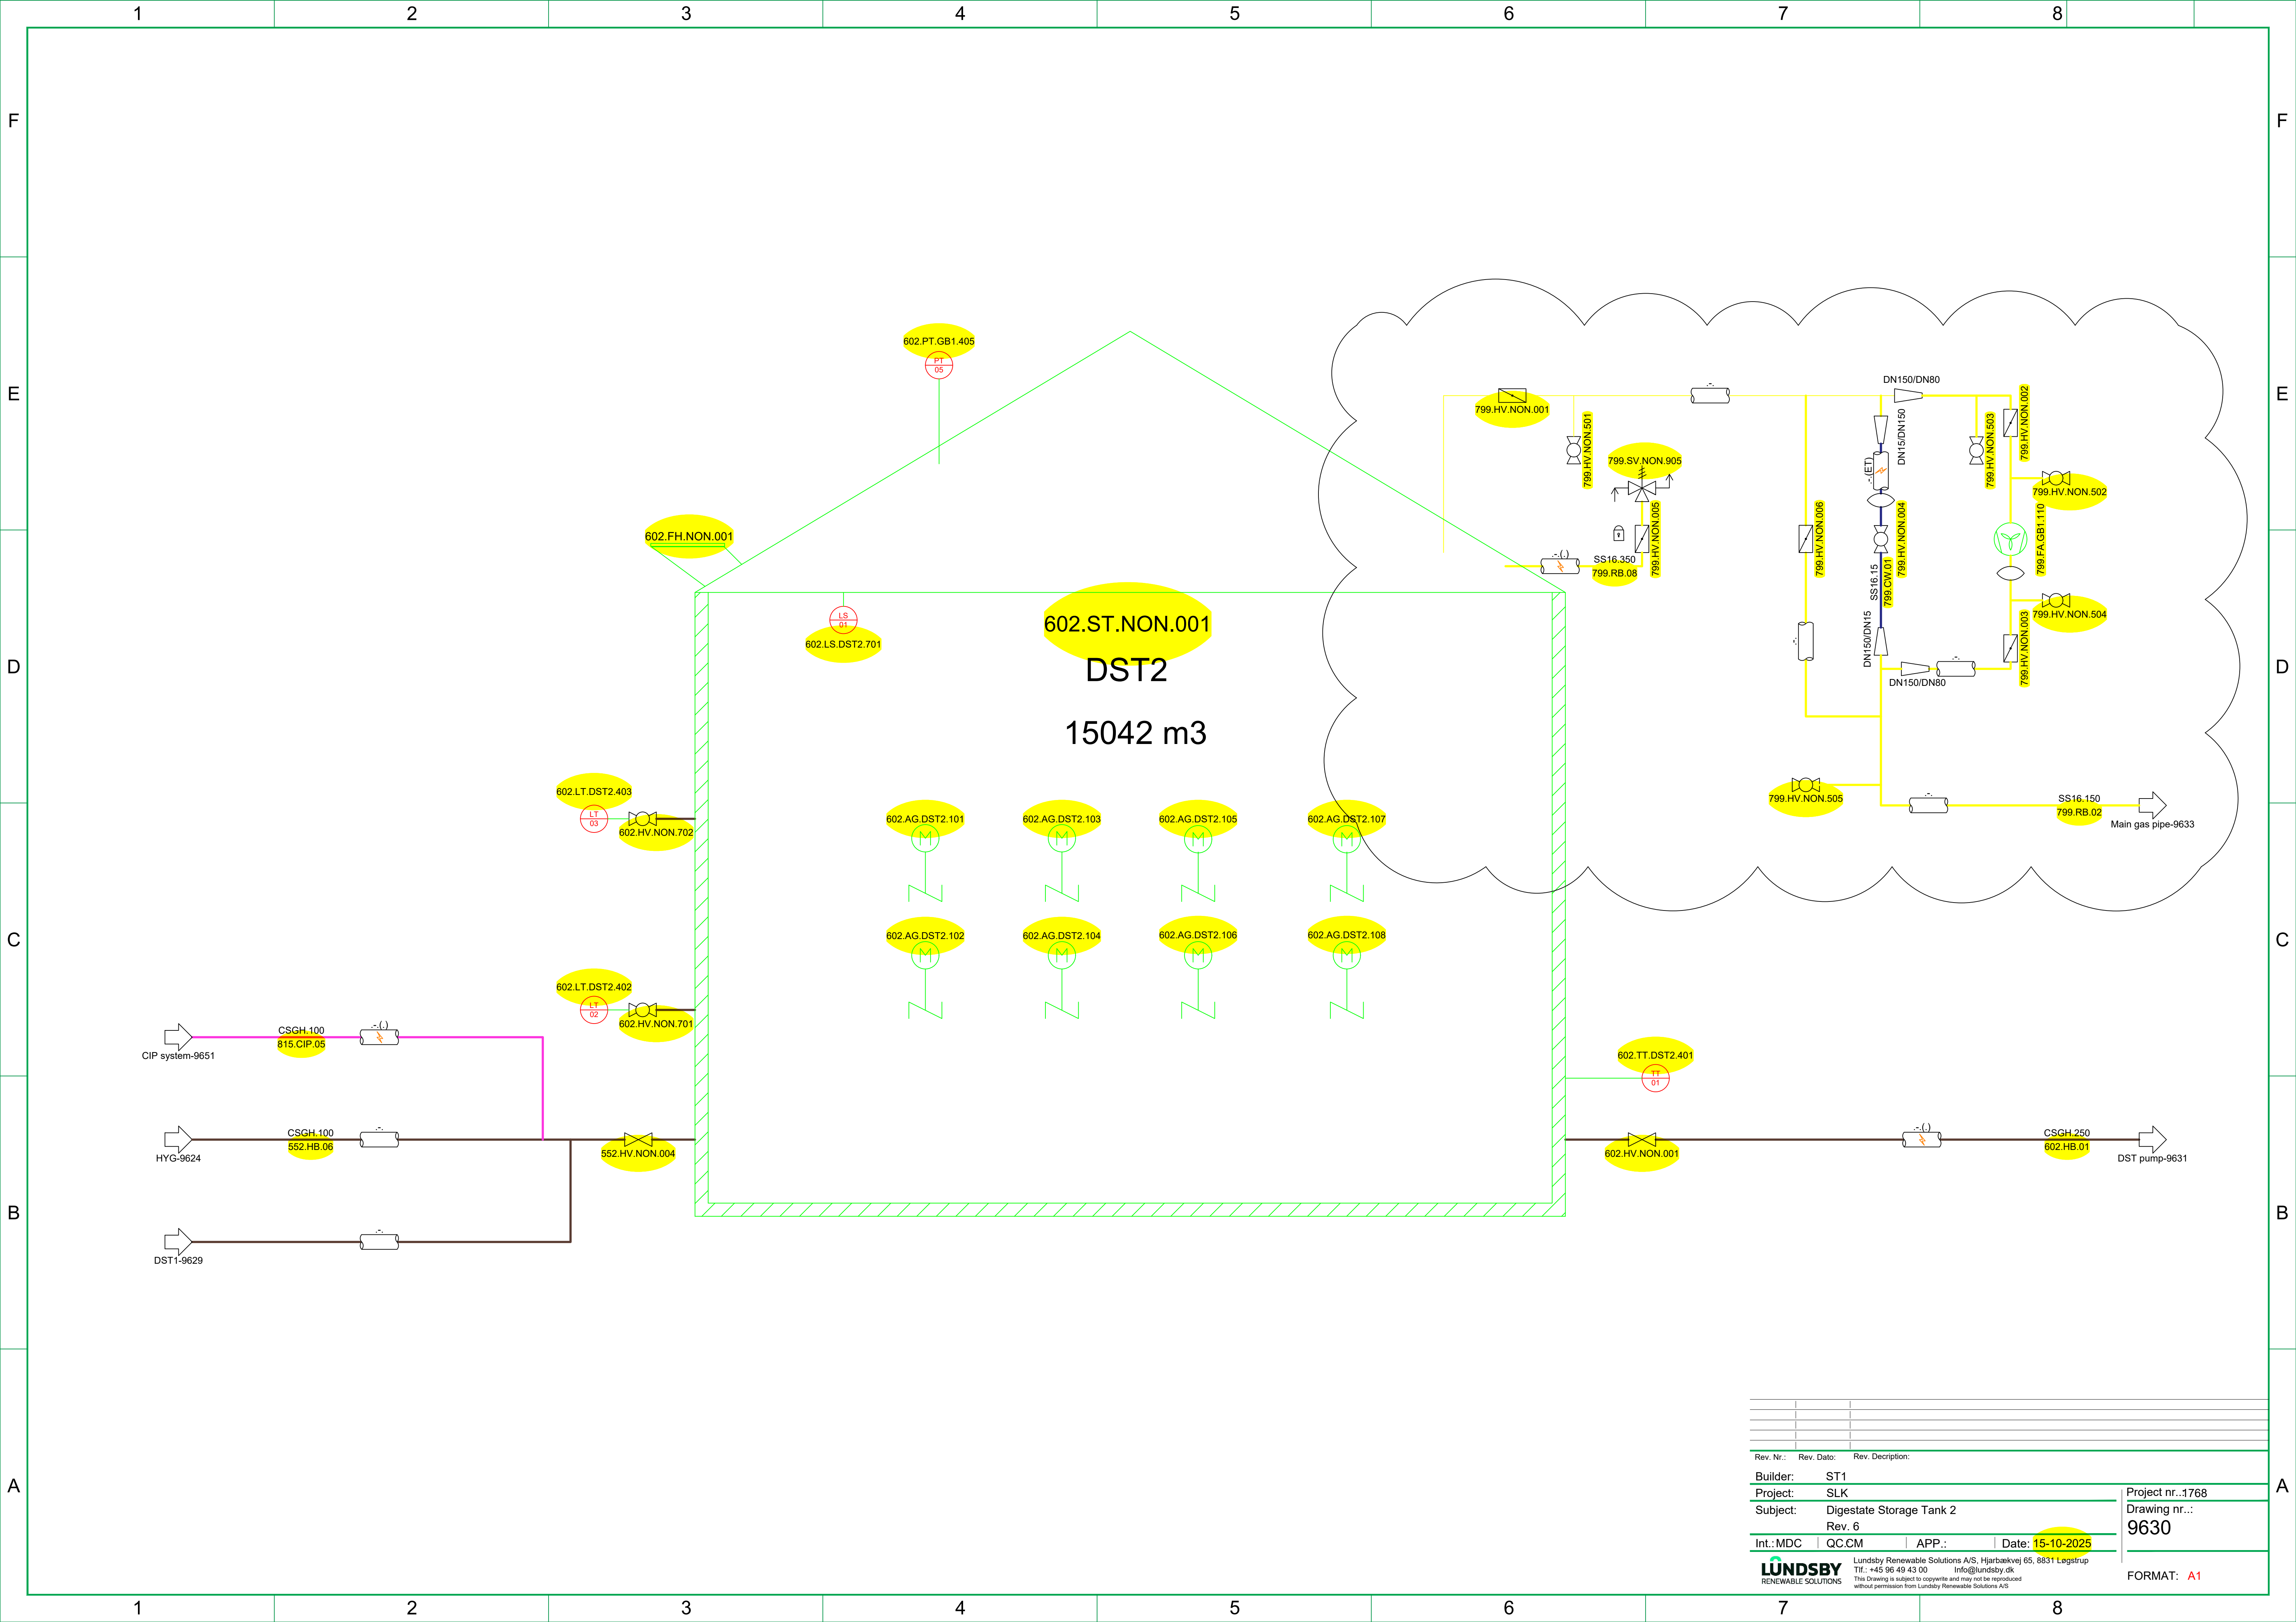


Rev. Nr.:	Rev. Dato:	Rev. Description:		
Builder:	ST1			
Project:	SLK			
Subject:	Digestate Storage Tank 2			
	Rev. 6			
Int.:MDC	QC:CM	APP.:	Date:	15-10-2025
LUNDSBY RENEWABLE SOLUTIONS		Lundby Renewable Solutions A/S, Hjarbrækvej 65, 8831 Løgstrup Tlf.: +45 96 49 43 00 Info@lundby.dk This Drawing is subject to copyright and may not be reproduced without permission from Lundby Renewable Solutions A/S		
		Project nr.:1768 Drawing nr.: 9630 FORMAT: A1		

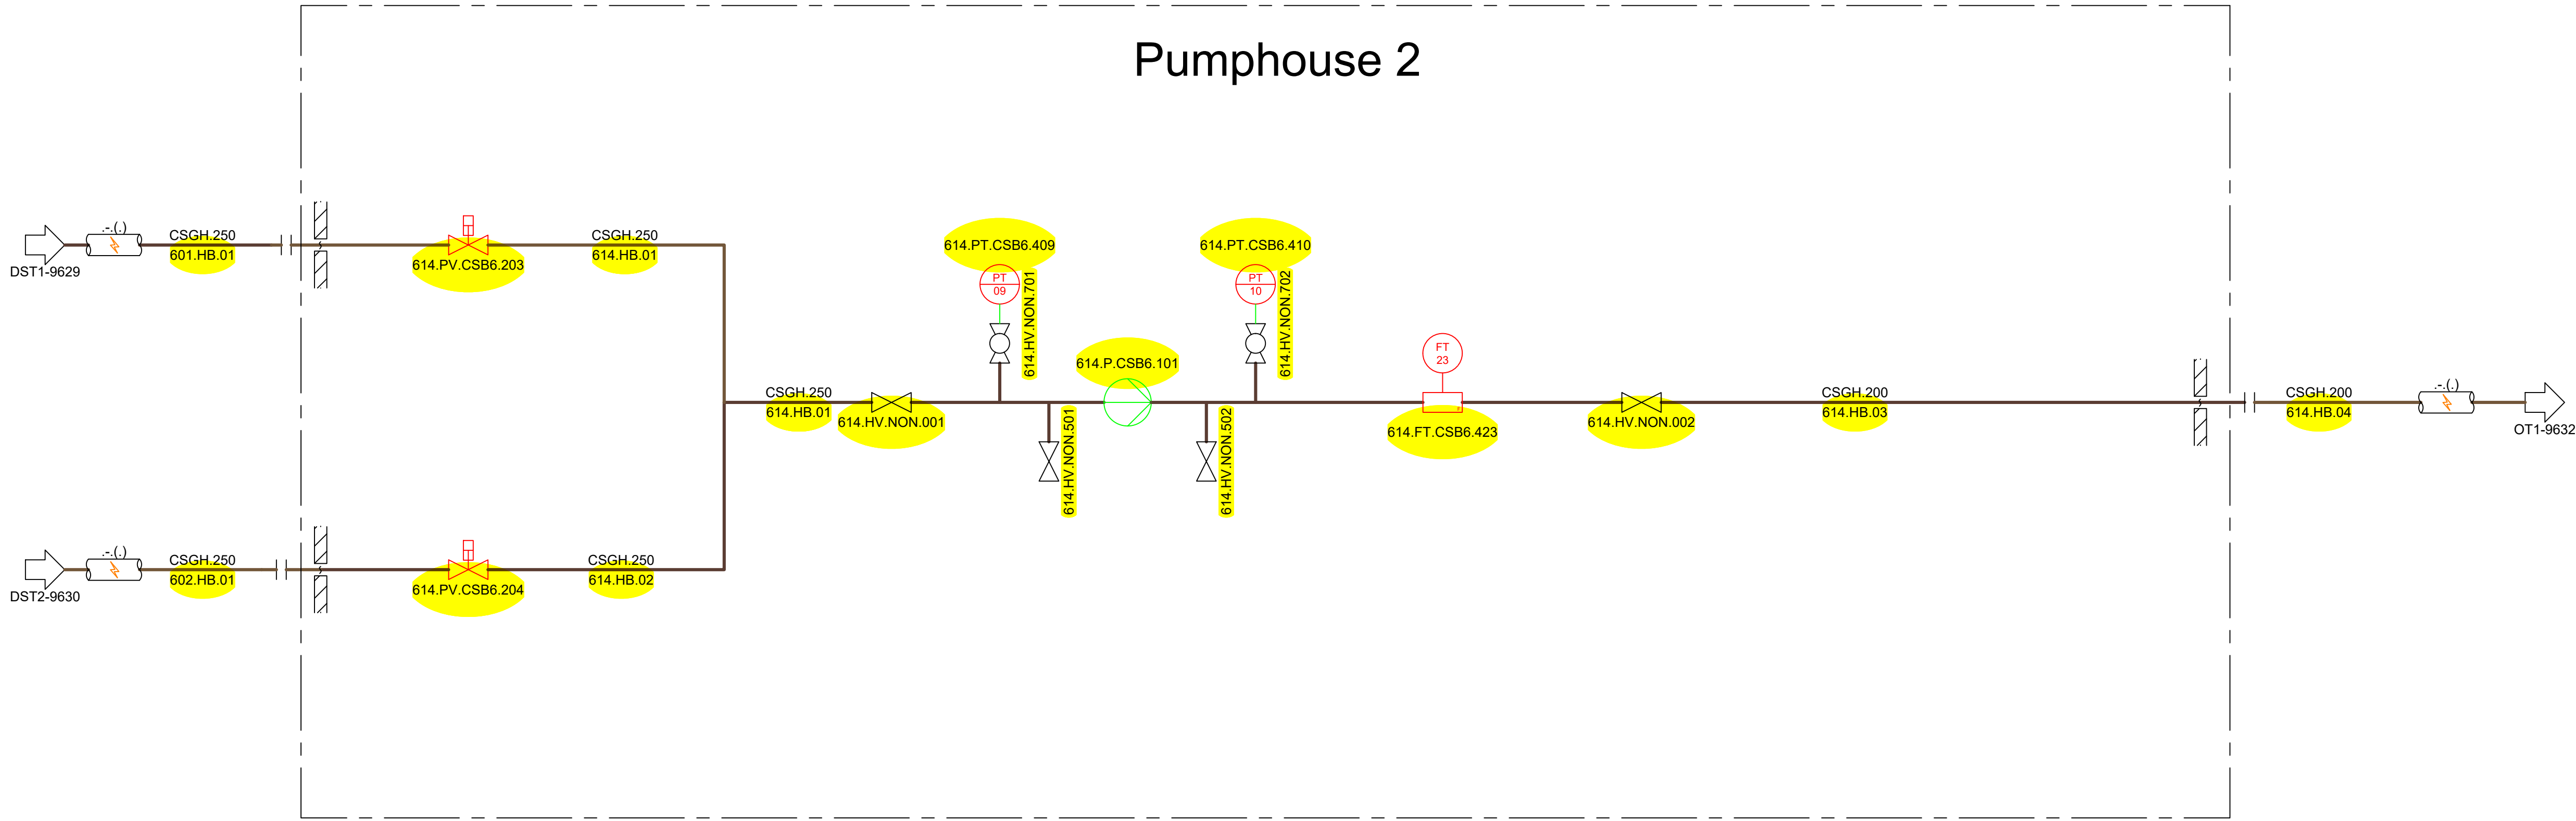

Rev. Nr.:	Rev. Dato:	Rev. Description:	Project nr.:1768
Builder:	ST1		Drawing nr...:
Project:	SLK		9631
Subject:	DST pump		
	Rev. 6		
Int.:MDC	QC.CM	APP.:	Date: 15-10-2025
LUNDSBY RENEWABLE SOLUTIONS		Lundsby Renewable Solutions A/S, Hjarbækvej 65, 8831 Løgstrup Tlf.: +45 96 49 43 00 Info@lundsby.dk This Drawing is subject to copyright and may not be reproduced without permission from Lundsby Renewable Solutions A/S	
		FORMAT: A1	

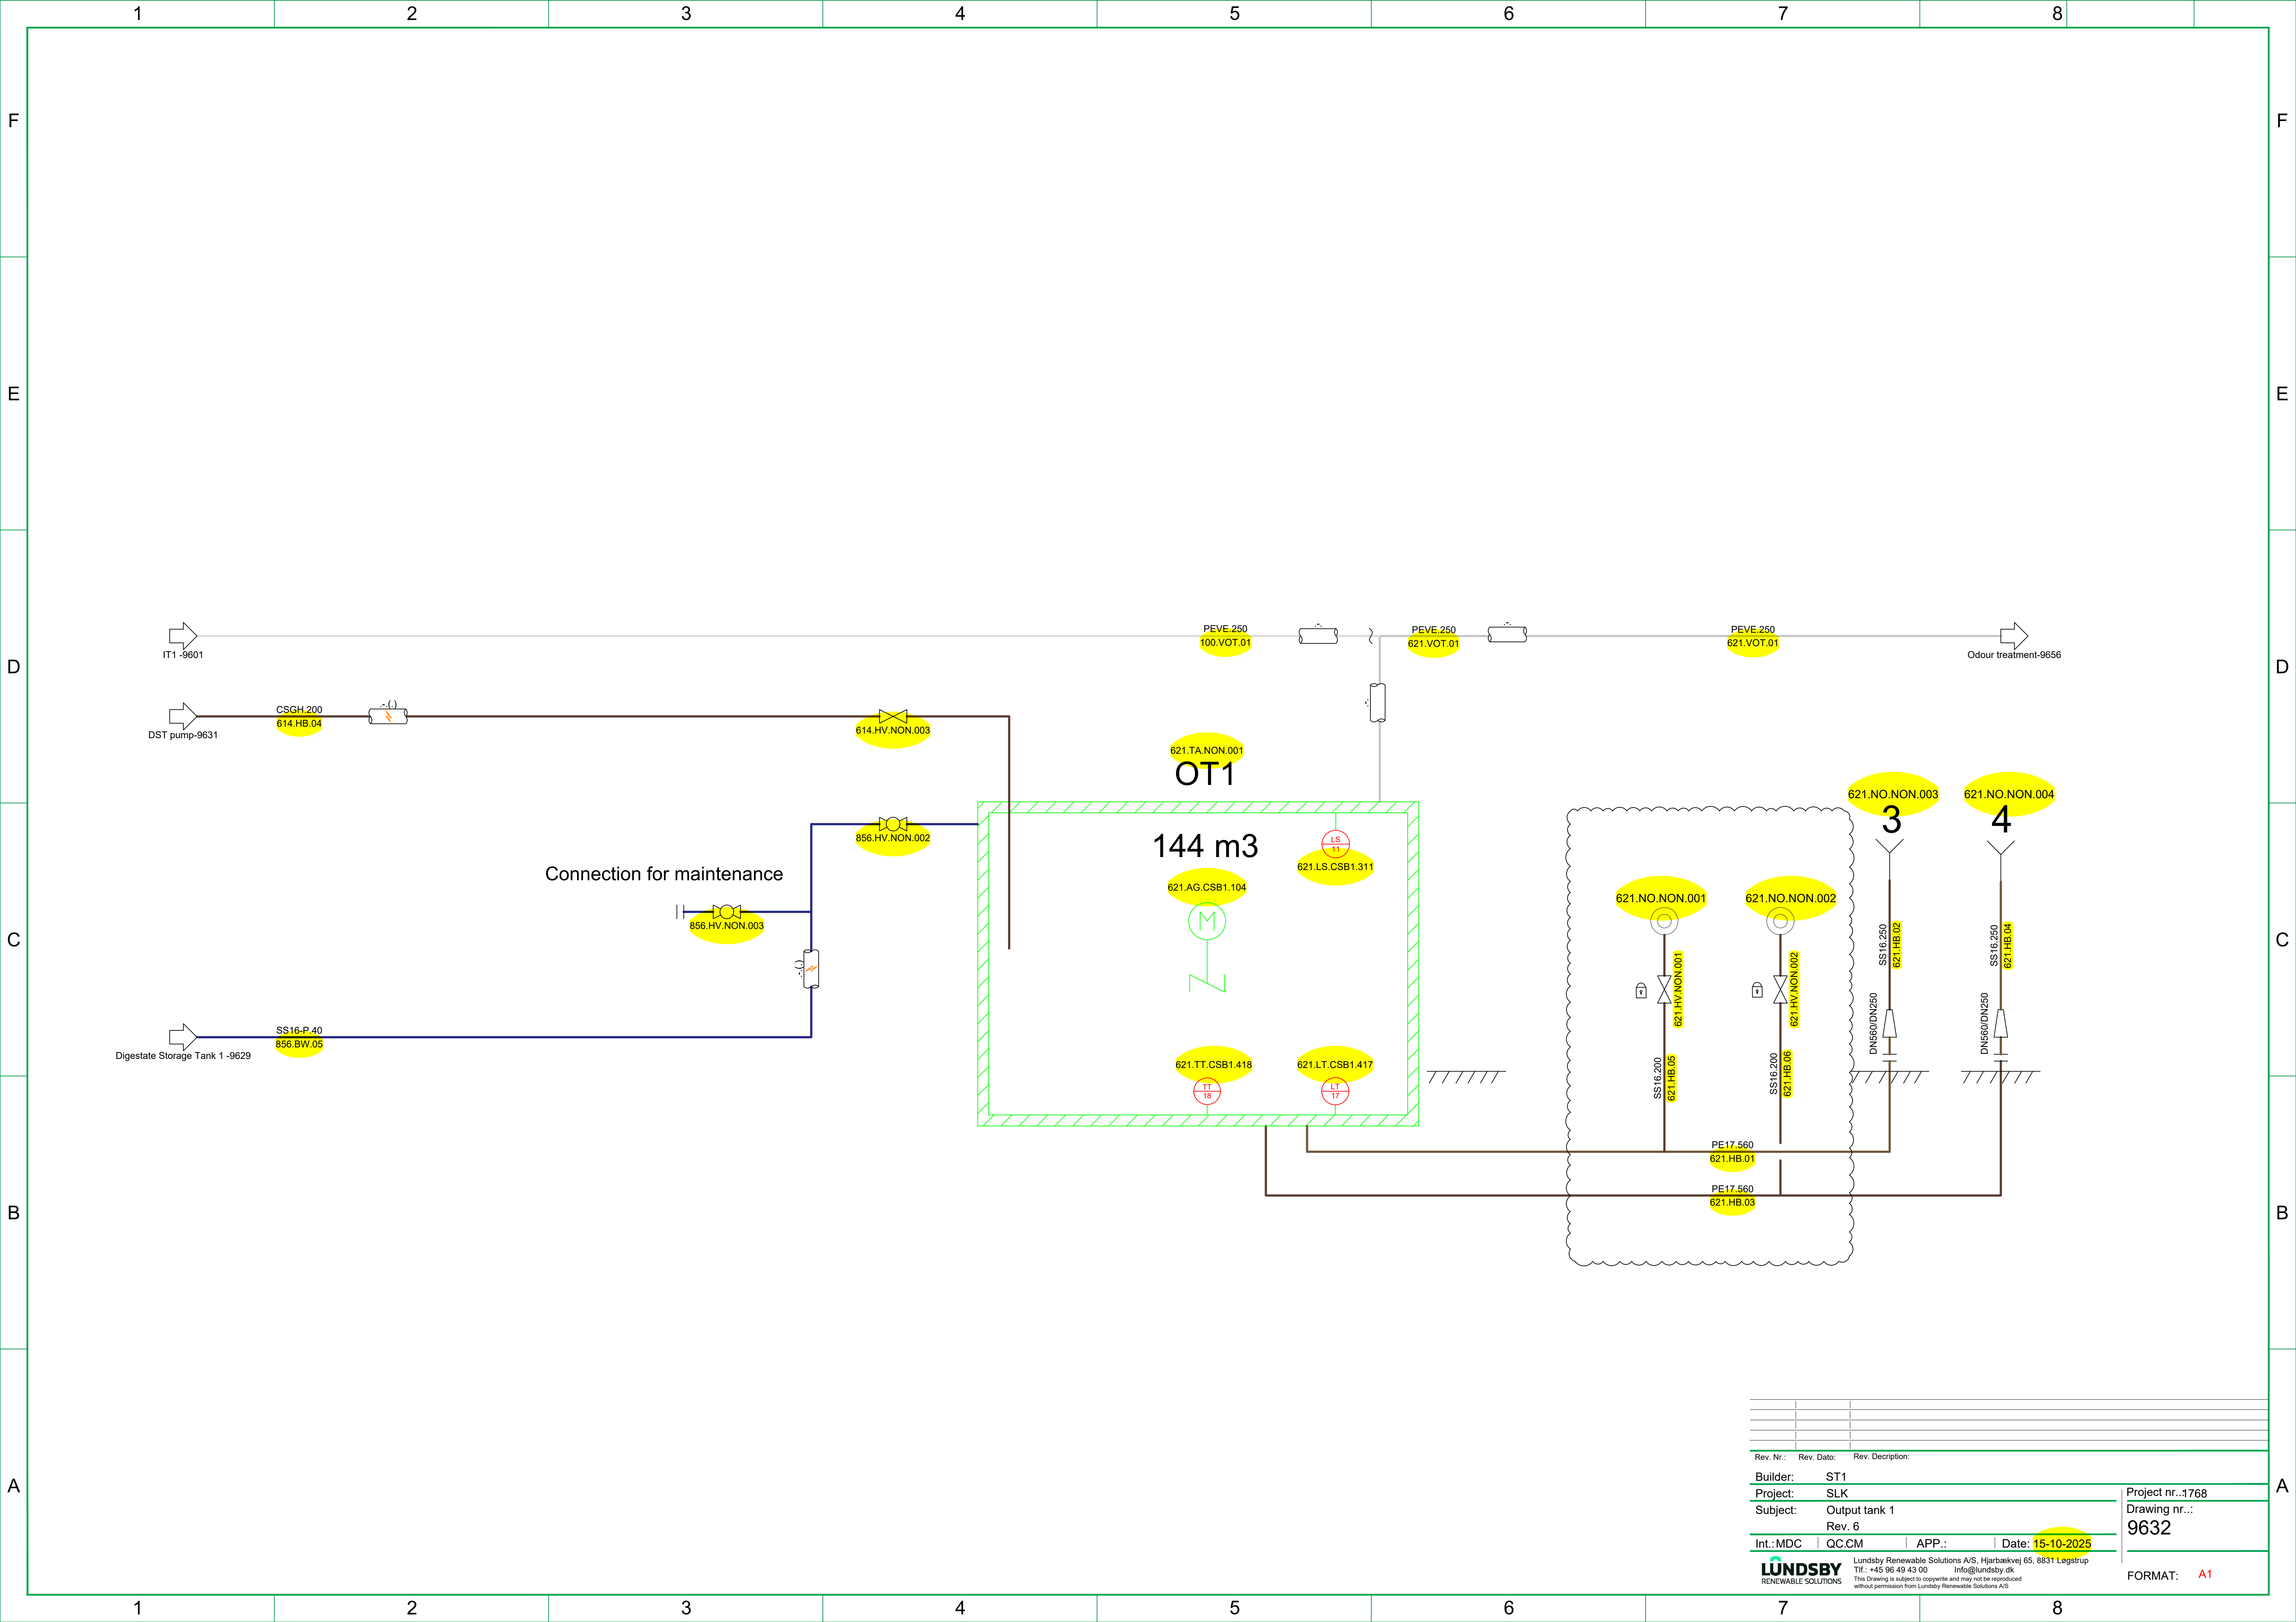


Rev. Nr.:	Rev. Dato:	Rev. Description:	Project nr...1768
Builder:	ST1		Drawing nr...: 9632
Project:	SLK		
Subject:	Output tank 1		
Rev. 6			
Int.: MDC	QC.CM	APP.:	Date: 15-10-2025
LUNDSBY RENEWABLE SOLUTIONS			Format: A1

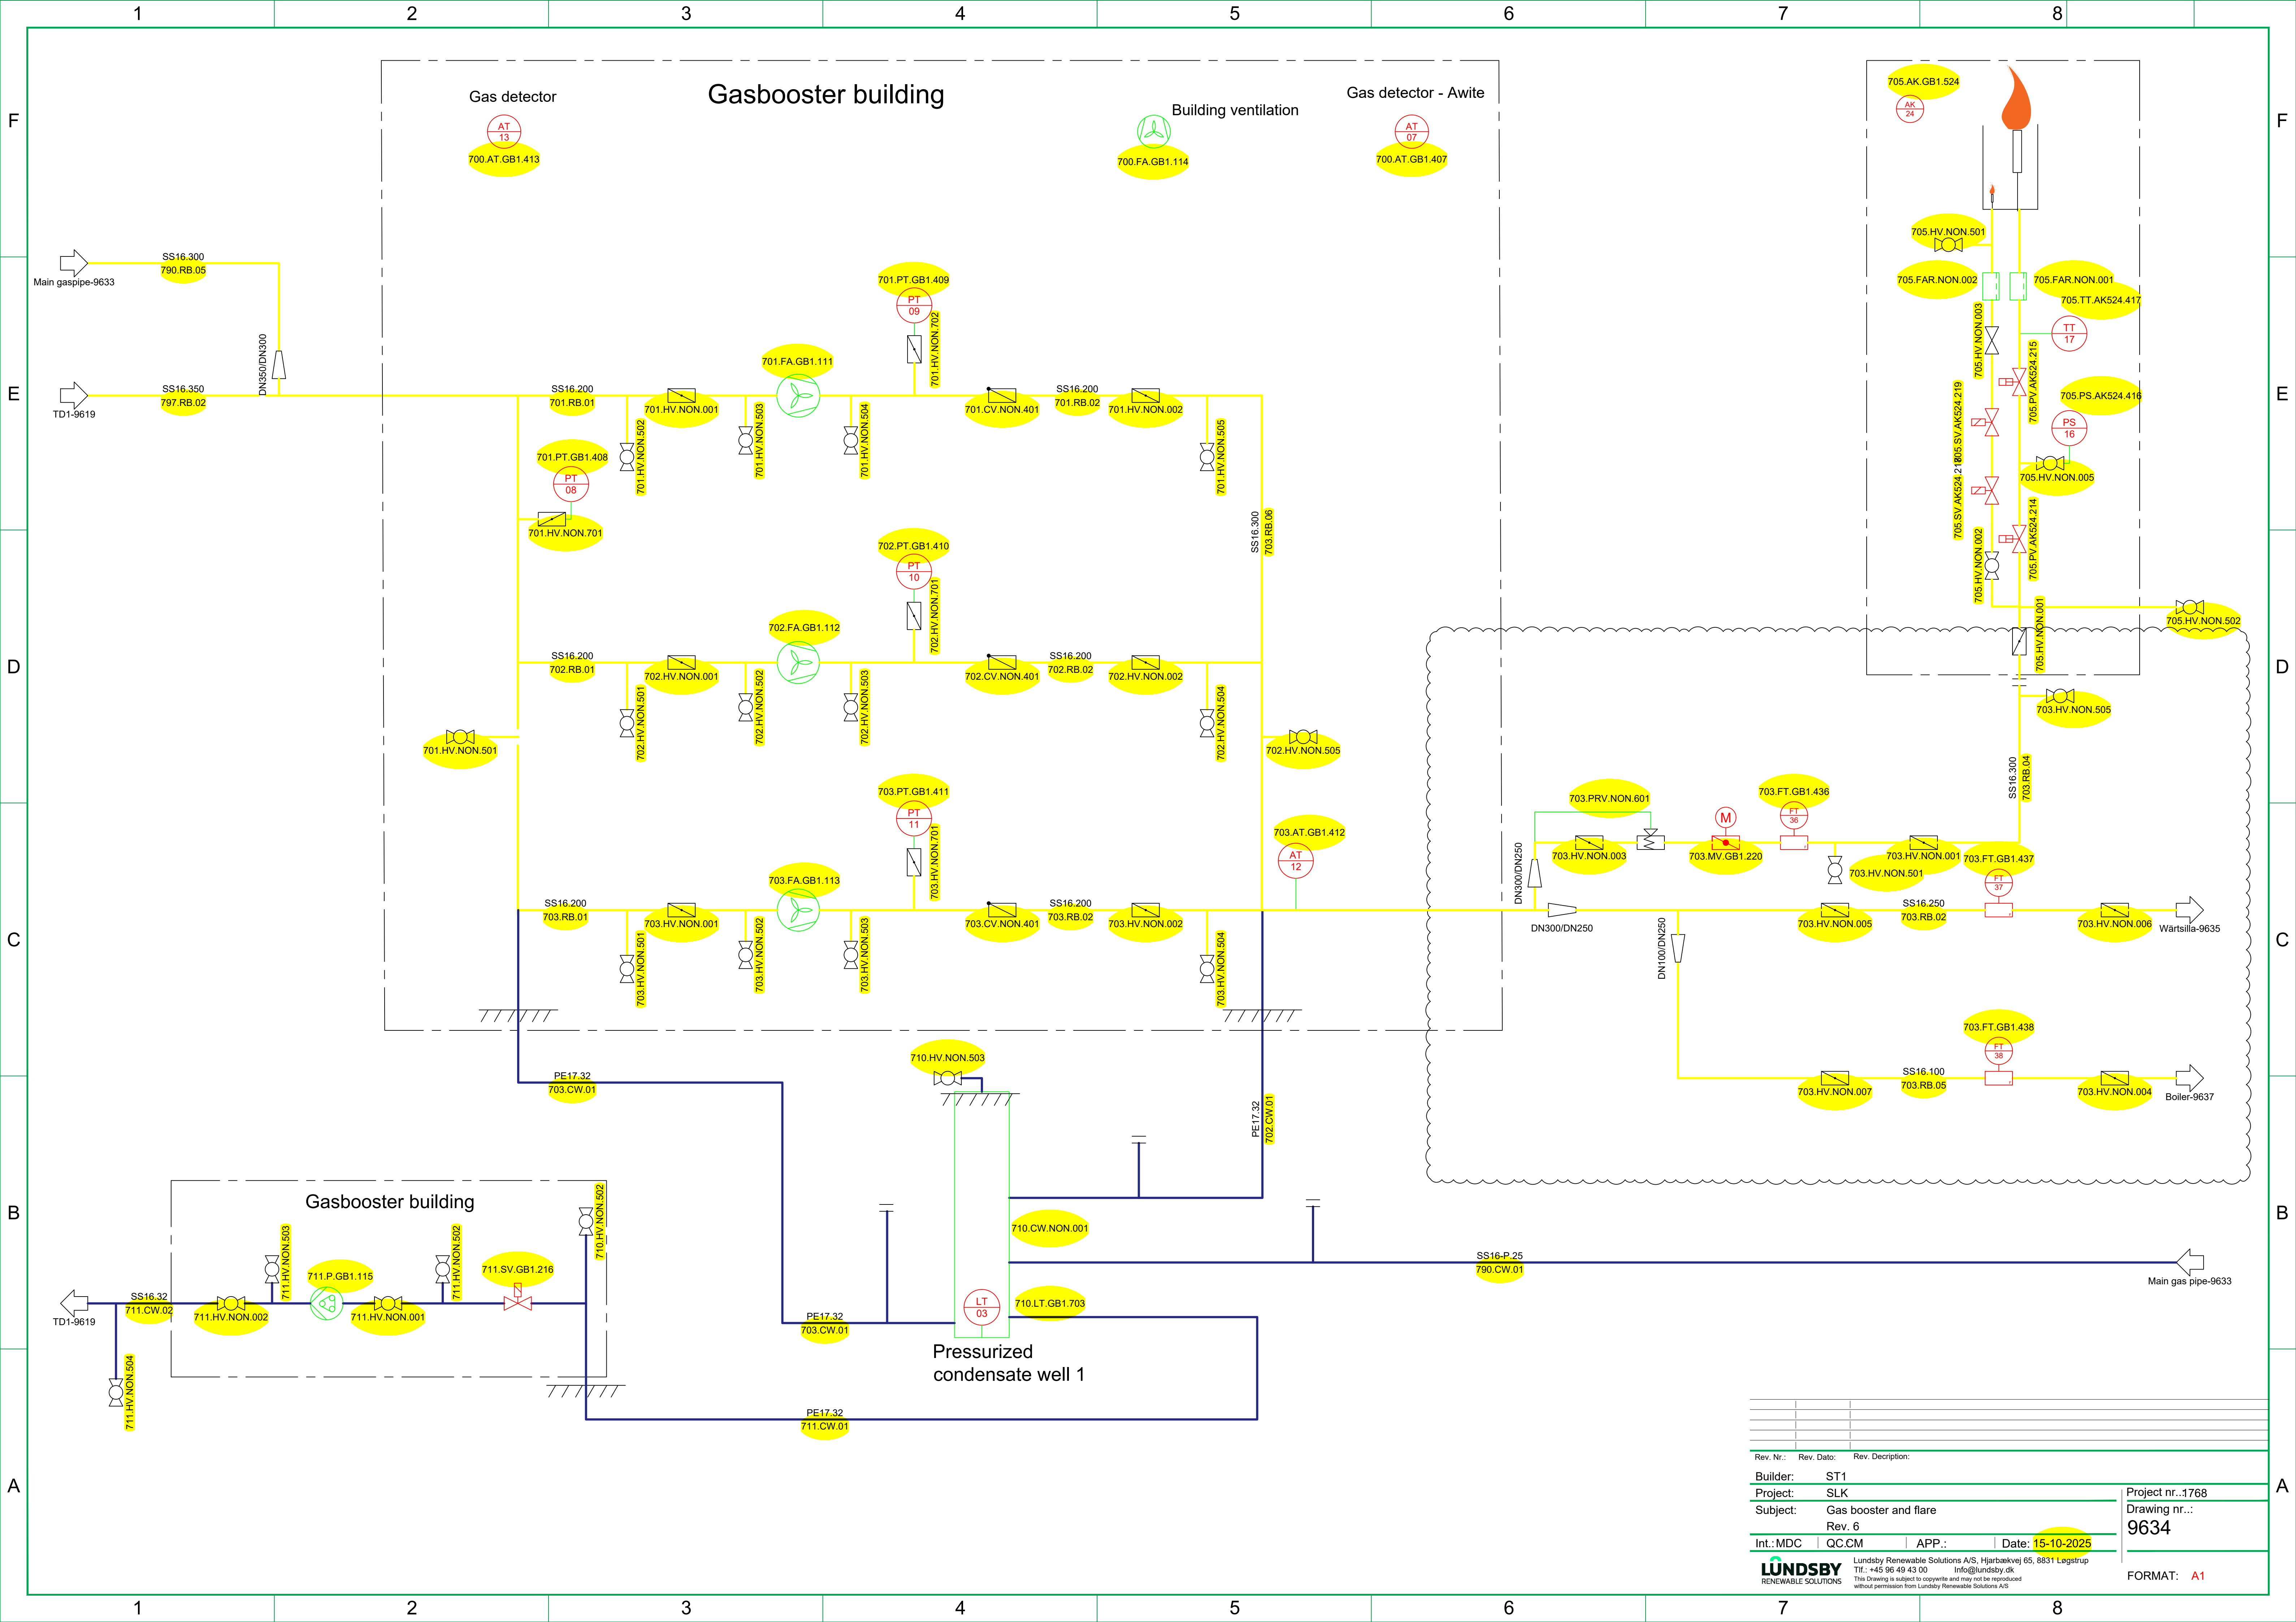

Wärtsillä

730-UPG-01


730-LBG-01

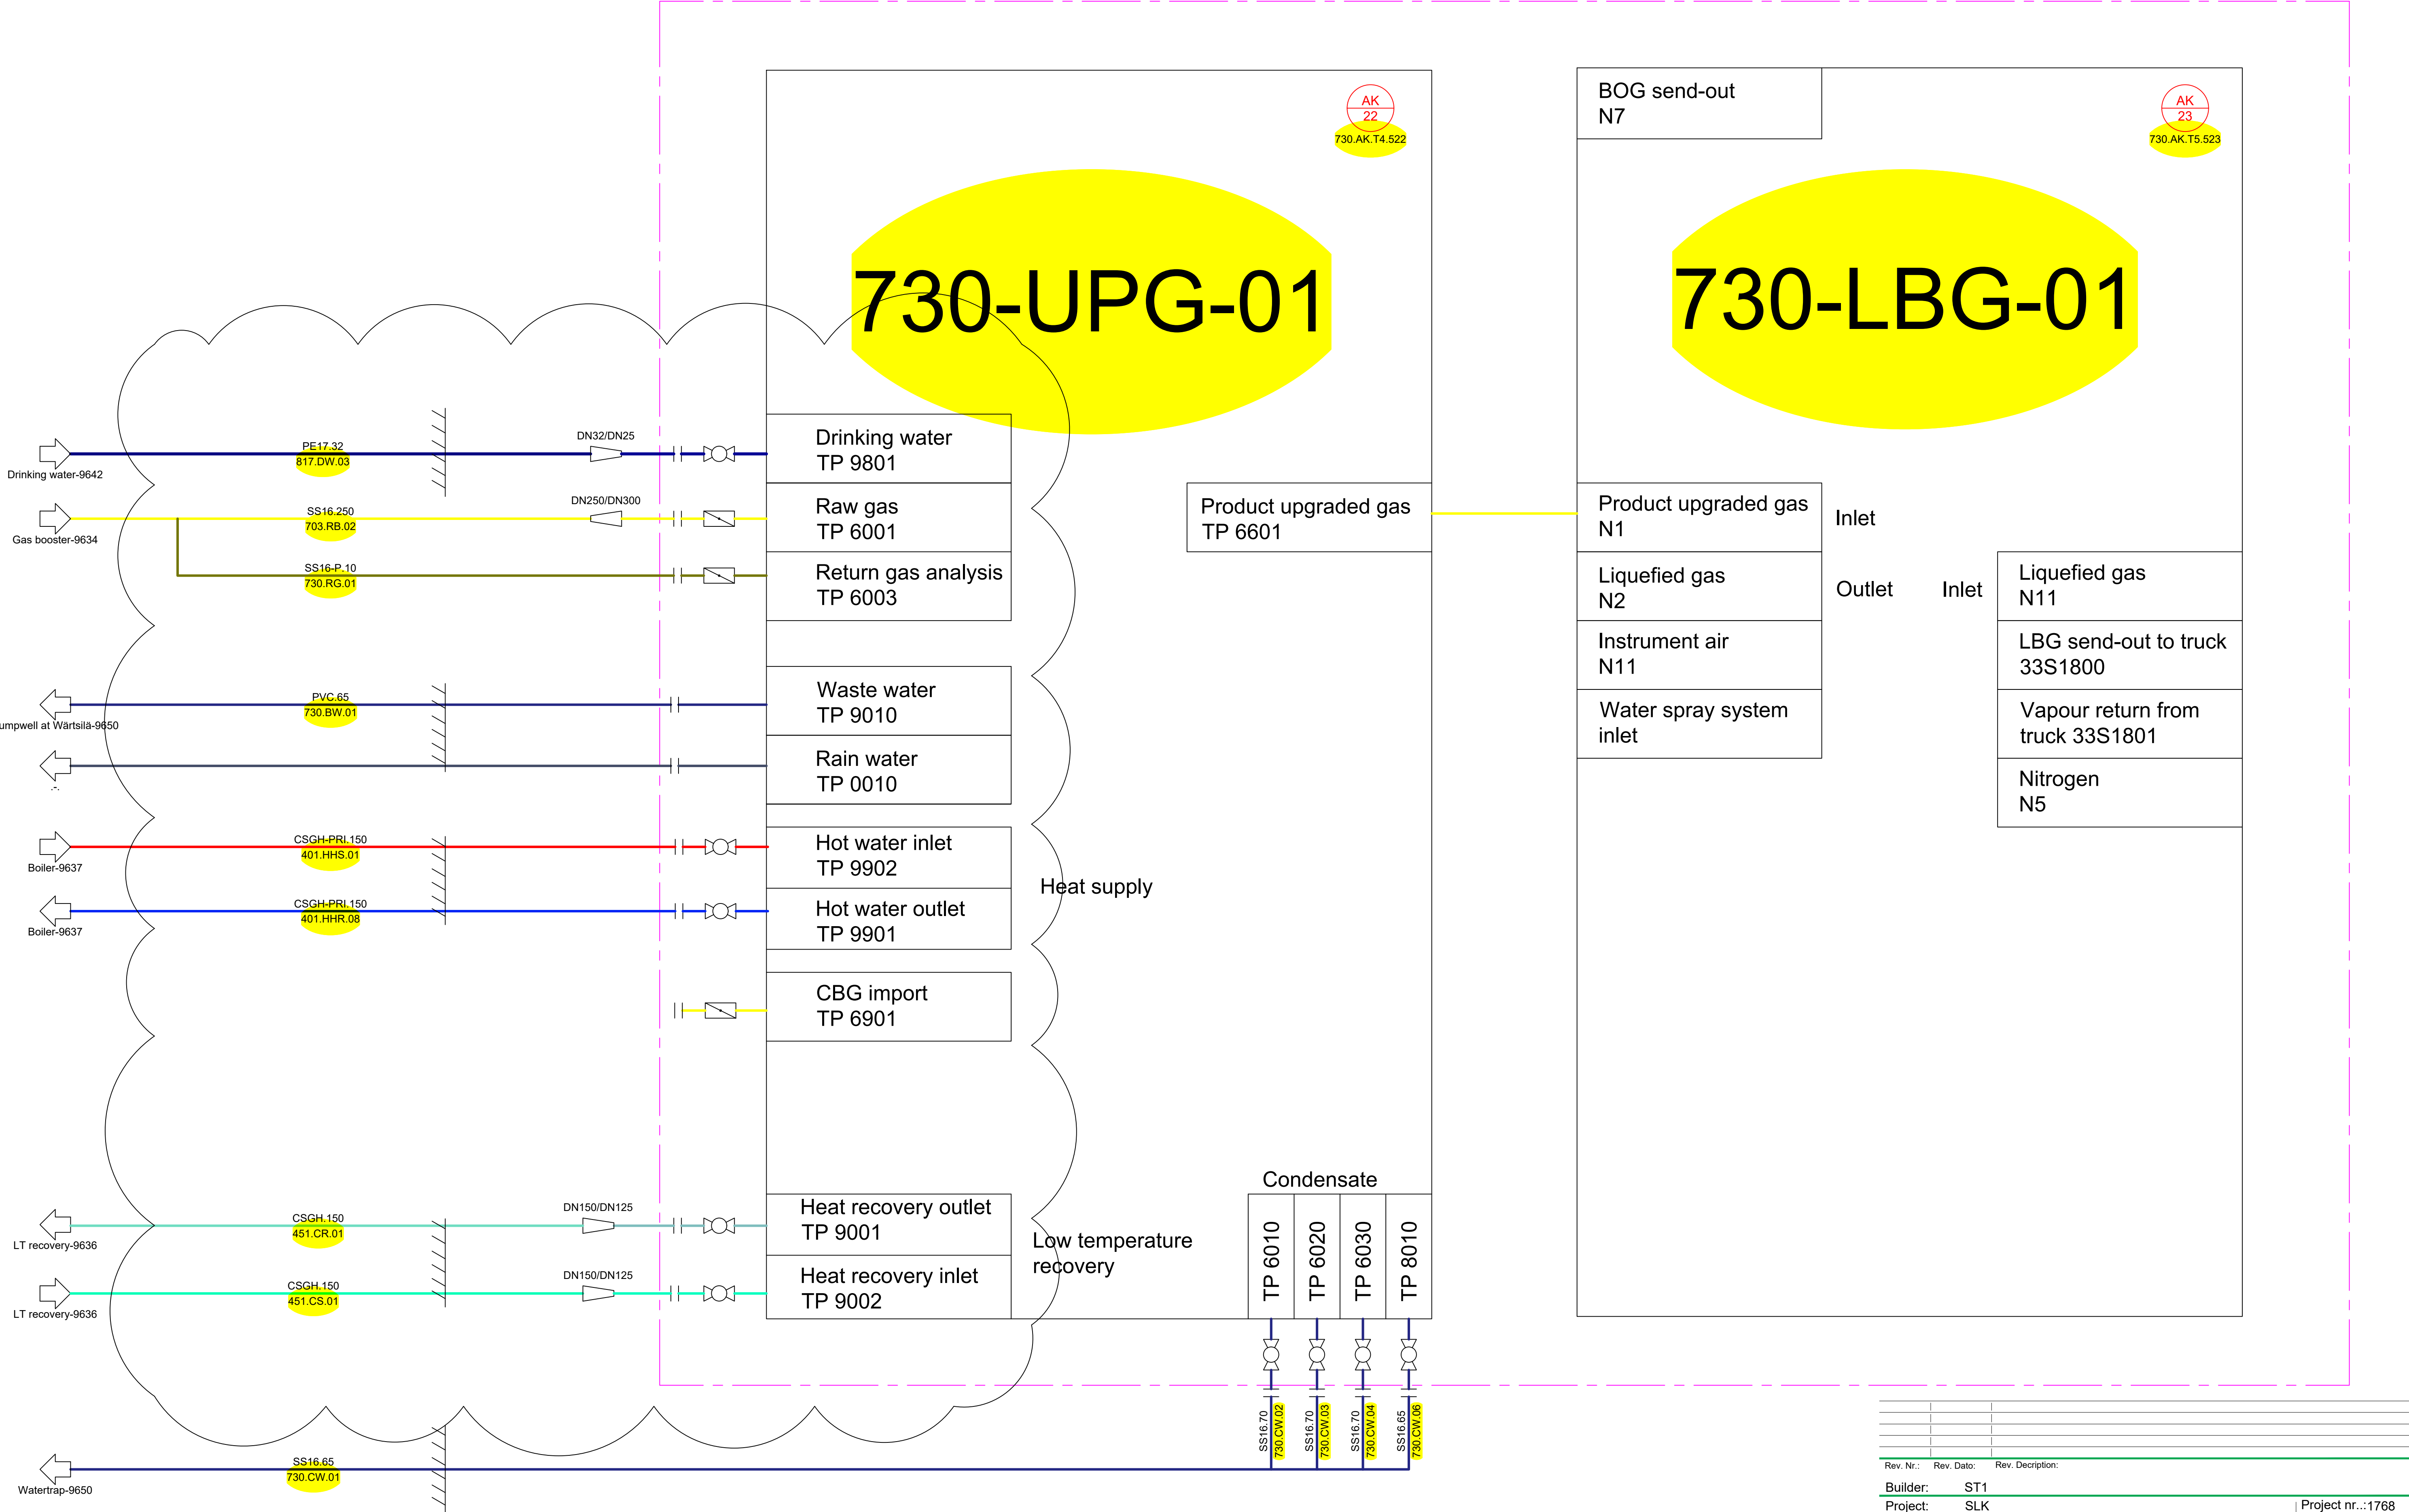


Rev. Nr.:	Rev. Dato:	Rev. Description:	
Builder:	ST1		
Project:	SLK		
Subject:	Upgrade		
	Rev. 6		
Int.:MDC	QC.CM	APP.:	Date: 15-10-2025
LUNDSBY RENEWABLE SOLUTIONS			Lundby Renewable Solutions A/S, Hjarbækvej 65, 8831 Løgstrup Tlf.: +45 96 49 43 00 Info@lundby.dk This Drawing is subject to copyright and may not be reproduced without permission from Lundby Renewable Solutions A/S
Project nr...:1768 Drawing nr...: 9635			FORMAT: A1

Technology building


Heat pump scope

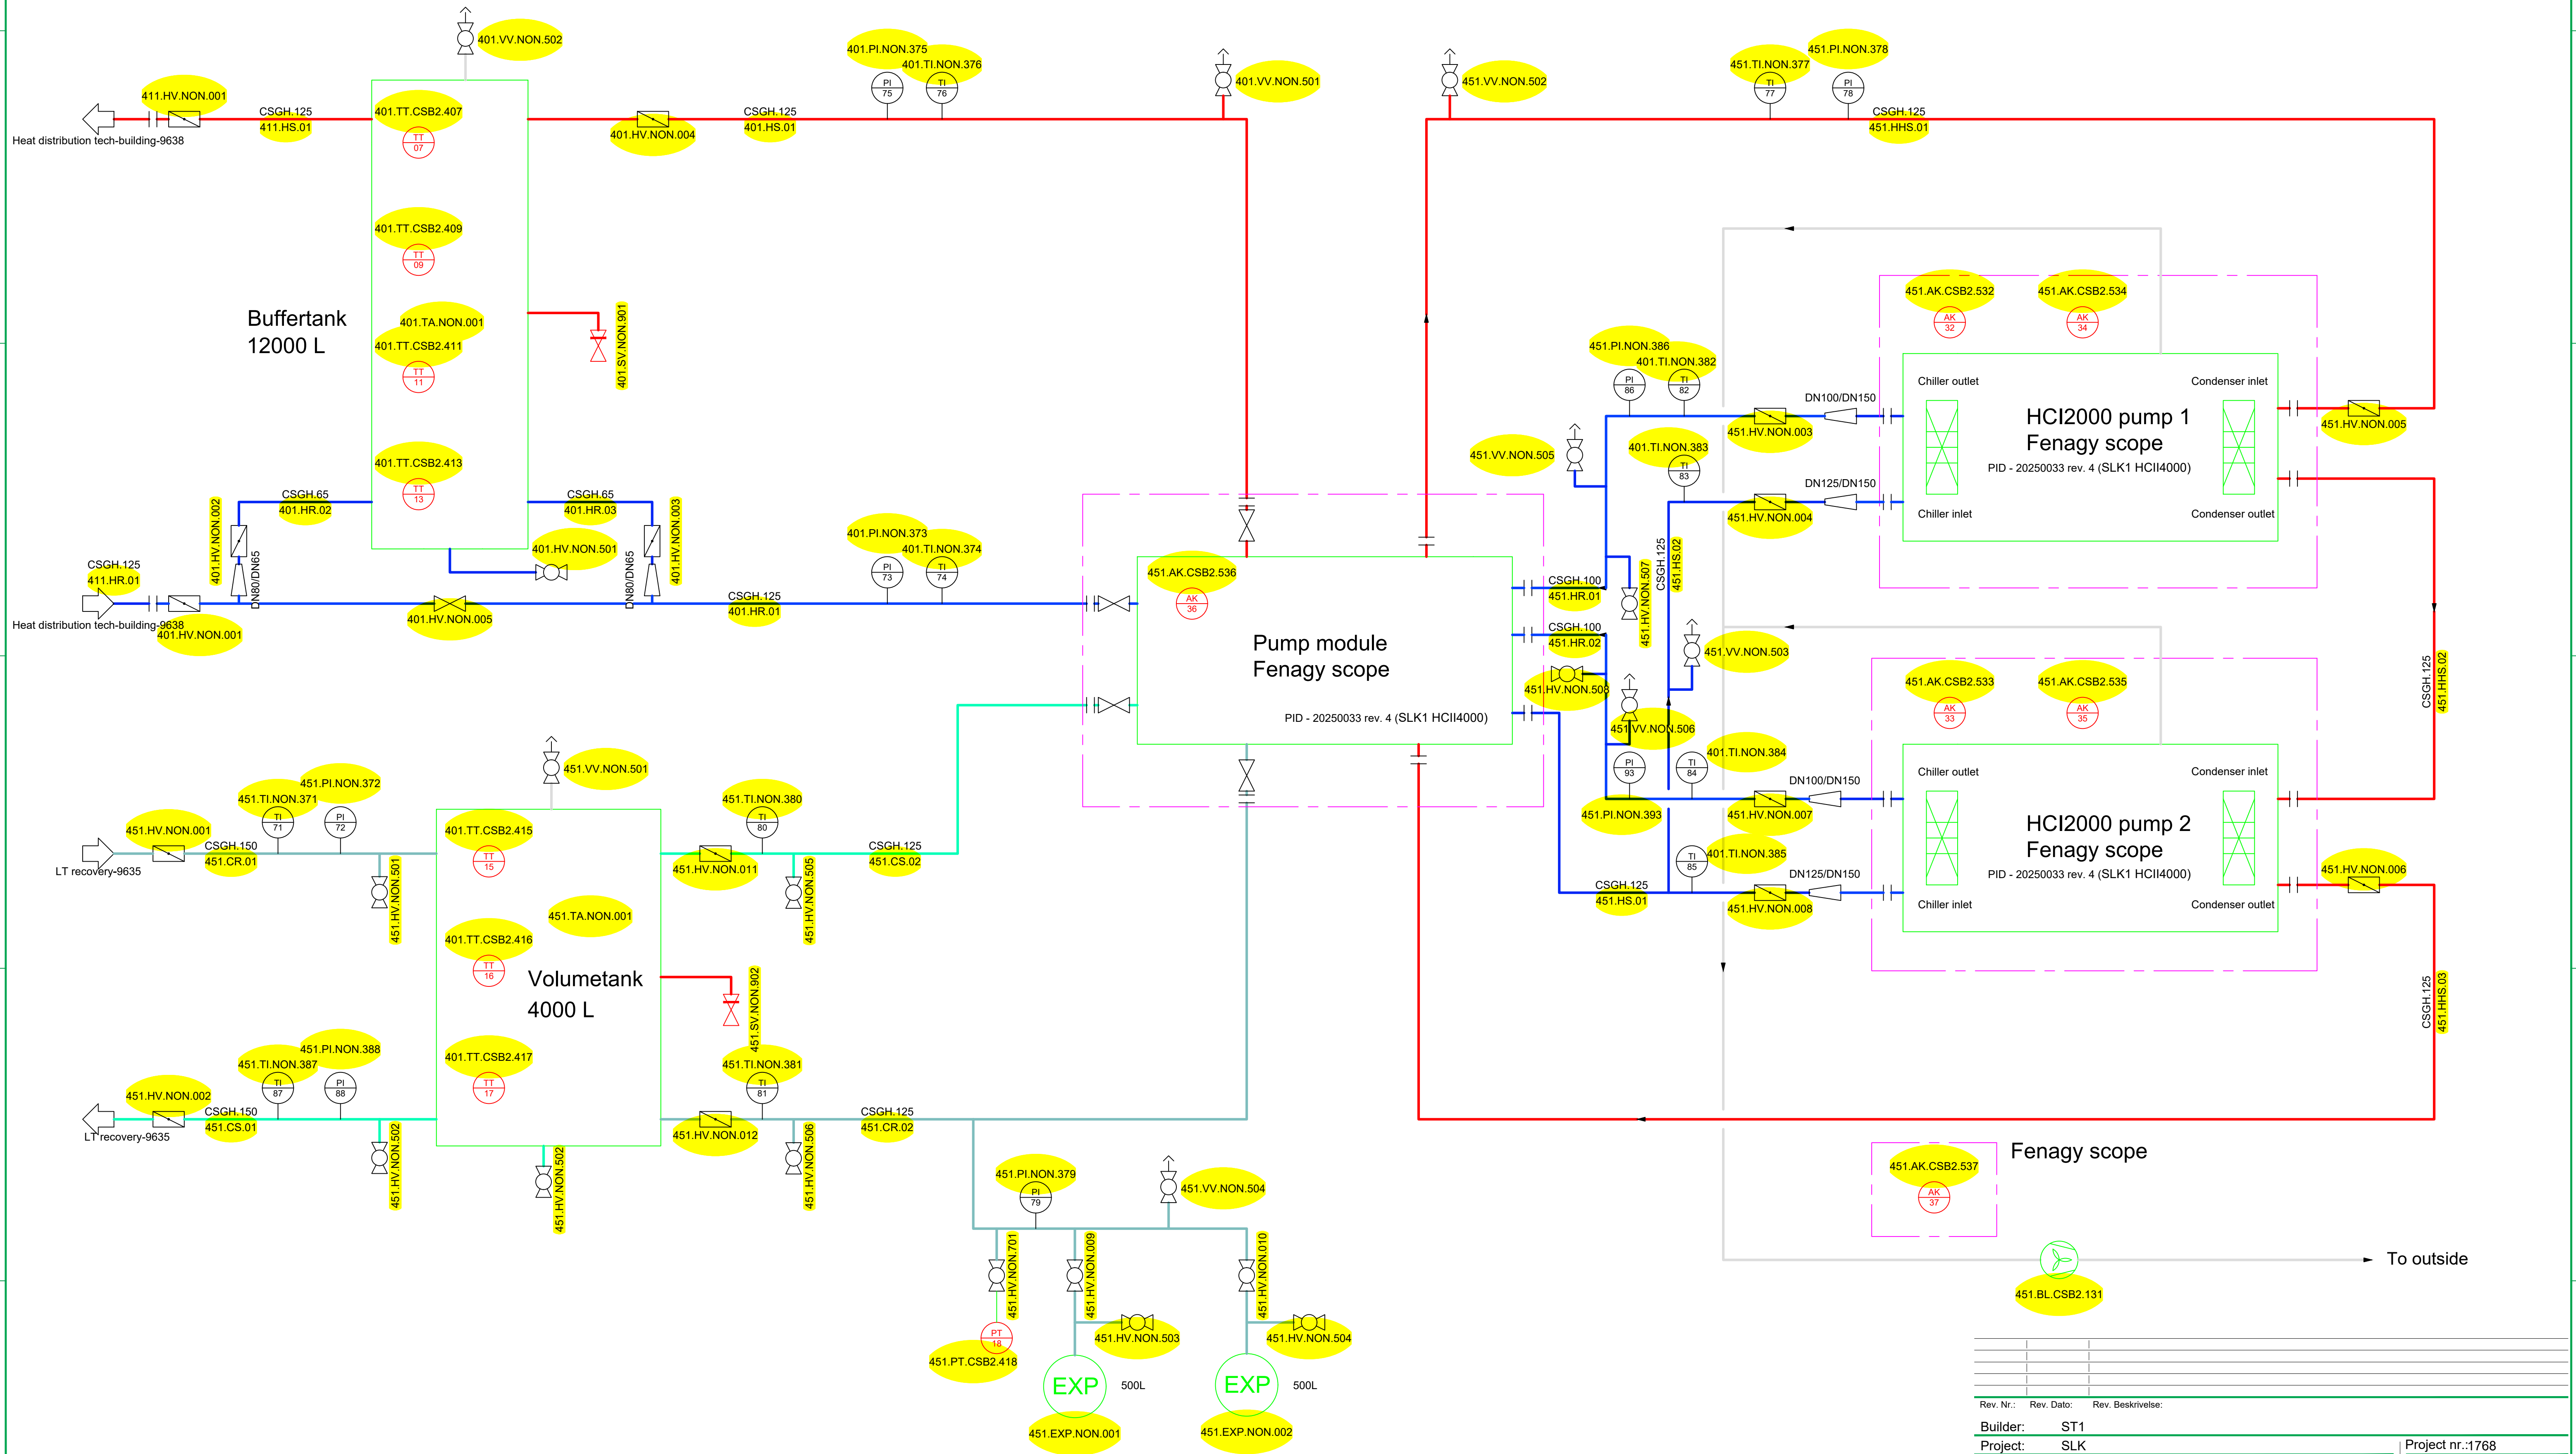


Rev. Nr.:	Rev. Dato:	Rev. Beskrivelse:	
Builder:	ST1		
Project:	SLK		
Subject:	Heat pumps		
Rev.:	6		
Int.:MDC	QC:CM	APP.:	Date: 15-10-2025
LUNDSBY RENEWABLE SOLUTIONS			Lundsby Biogas A/S, Hjarbækvej 65, 8831 Løgstrup Tlf.: +45 96 49 43 00 info@lundsbybiogas.dk Denne tegning er underlagt copywrite og må ikke reproduceres uden tilladelse fra Lundsbybiogas A/S
Project nr.:1768 Drawing nr.: 9636			FORMAT: A1

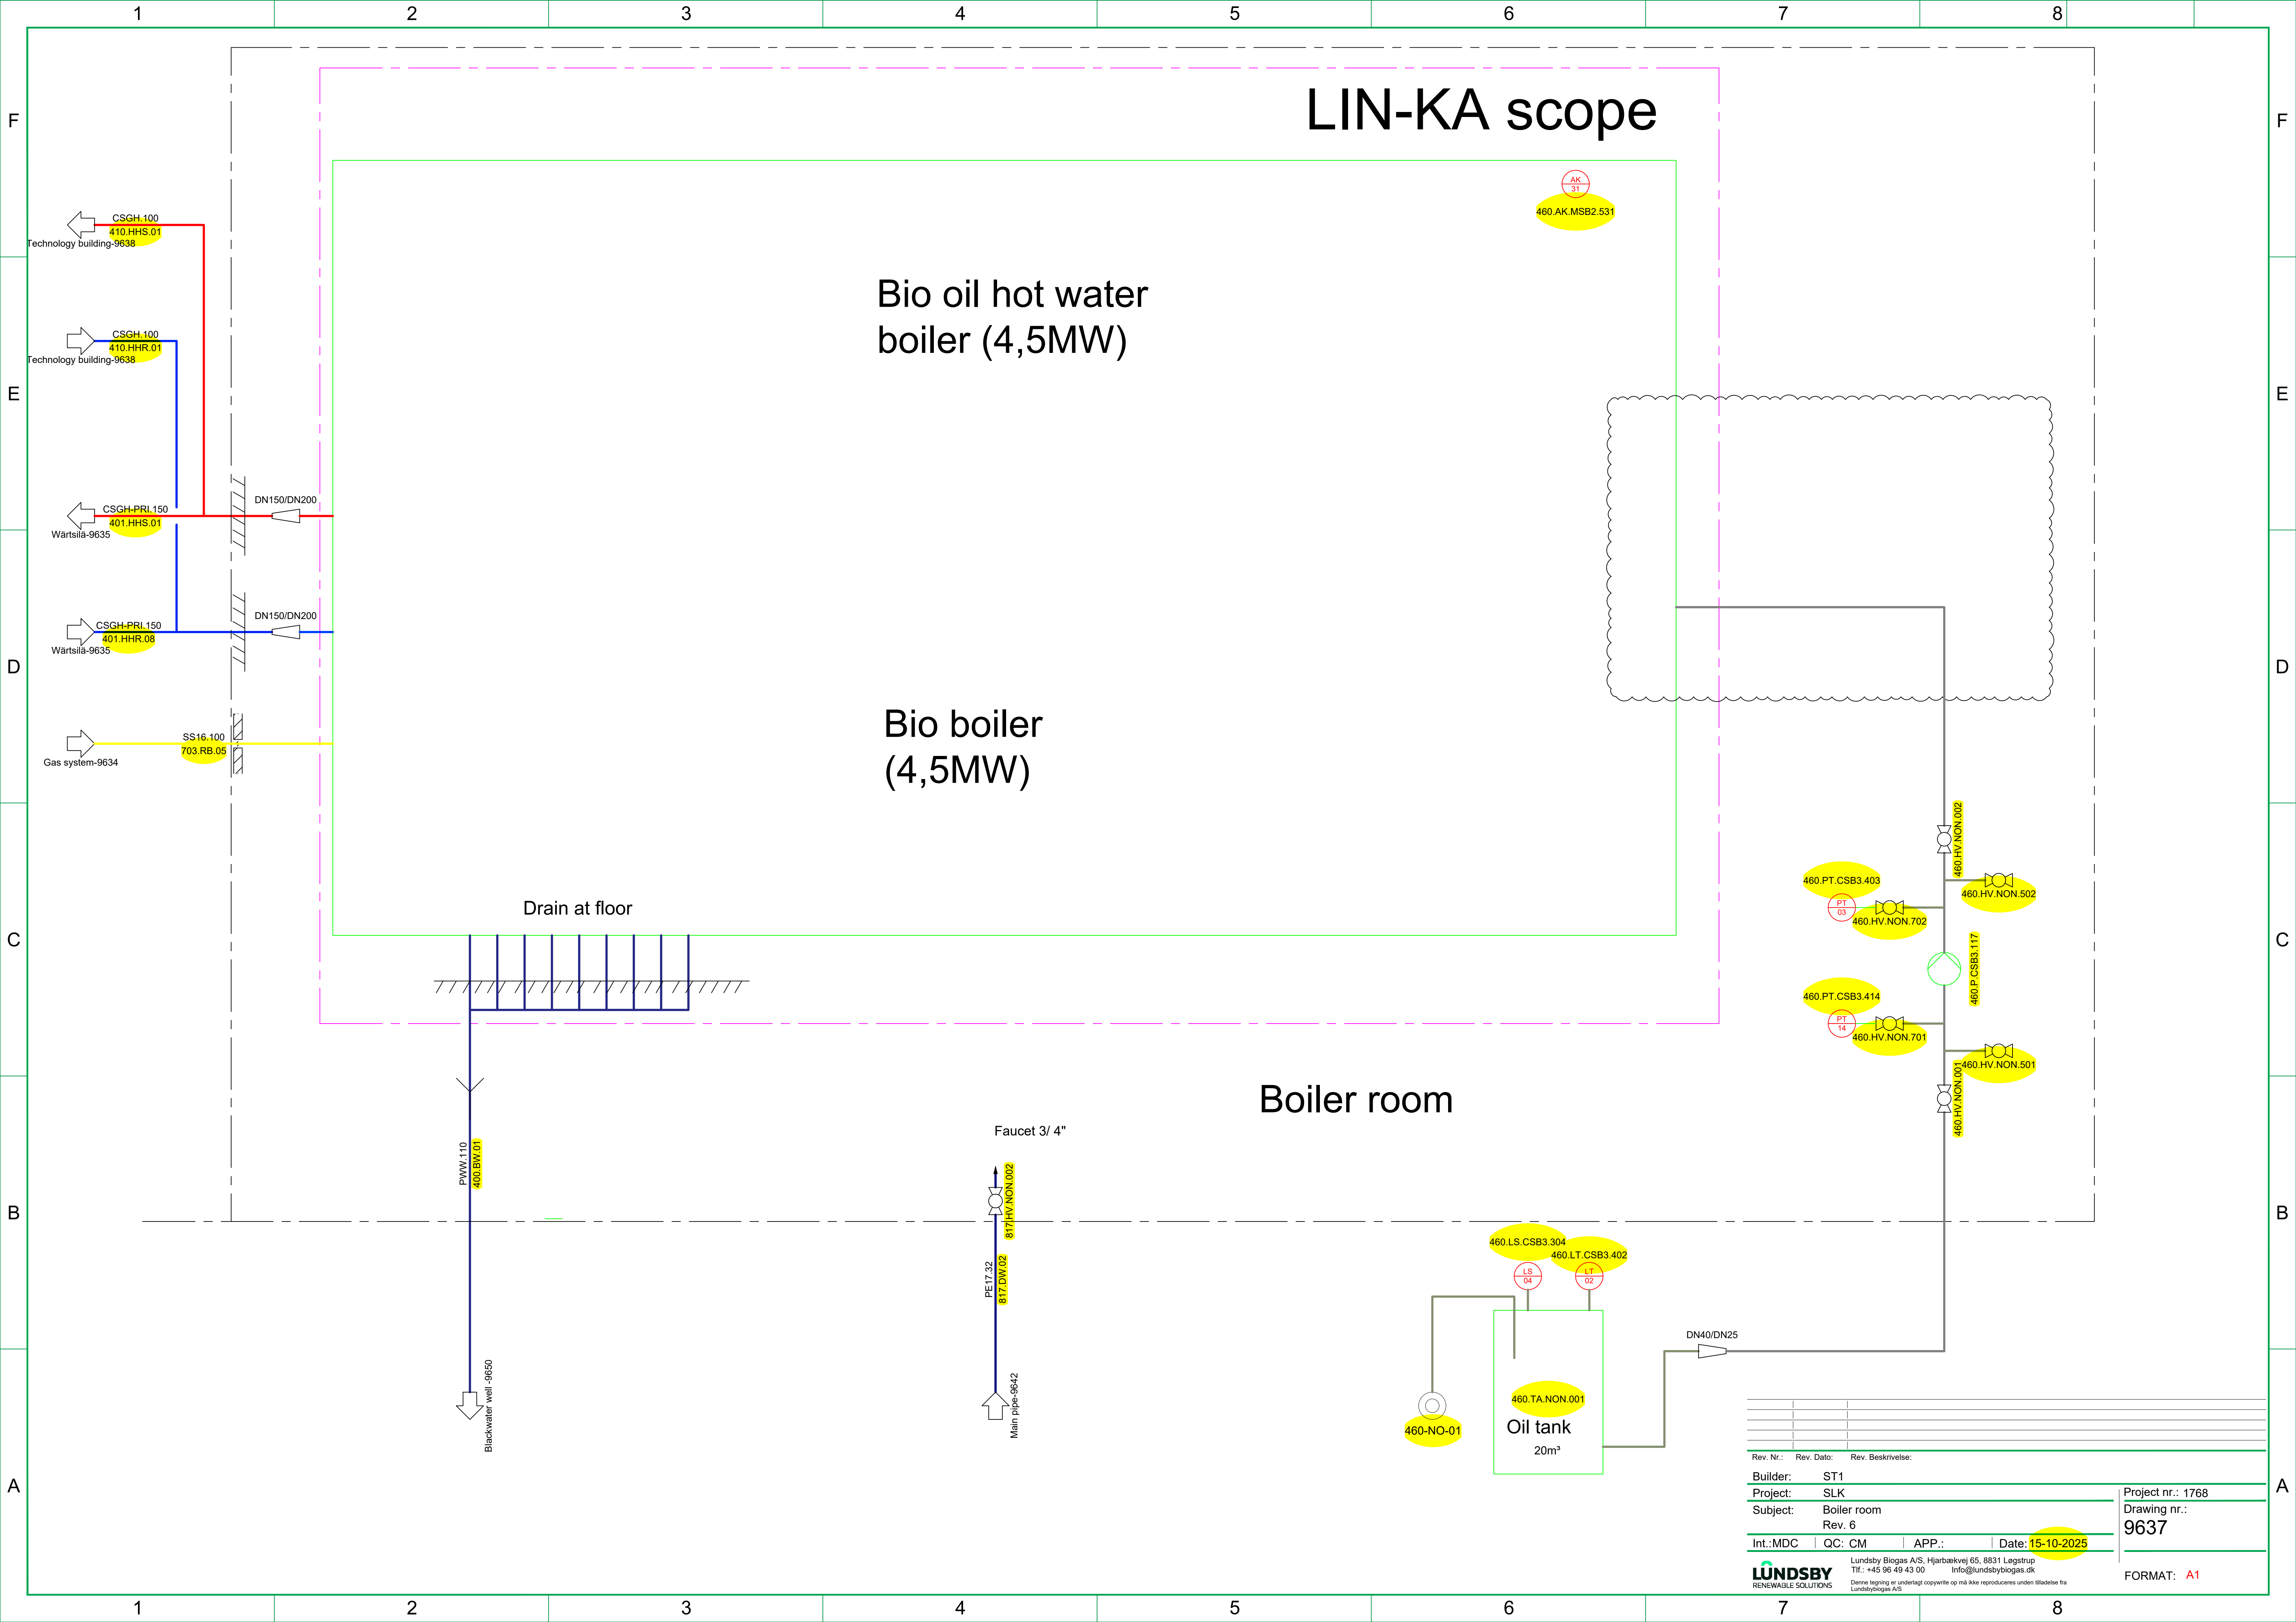

Rev. Nr.:	Rev. Dato:	Rev. Beskrivelse:	
Builder:	ST1		
Project:	SLK		
Subject:	Boiler room		
Rev. 6			
Int.:MDC	QC: CM	APP.:	Date: 15-10-2025
LUNDSBY RENEWABLE SOLUTIONS			Lundsby Biogas A/S, Hjarbækvej 65, 8831 Løgstrup Tlf.: +45 96 49 43 00 Info@lundsbybiogas.dk Denne tegning er underlagt copyright og må ikke reproduceres uden tilladelse fra Lundsbybiogas A/S
Project nr.: 1768 Drawing nr.: 9637			FORMAT: A1

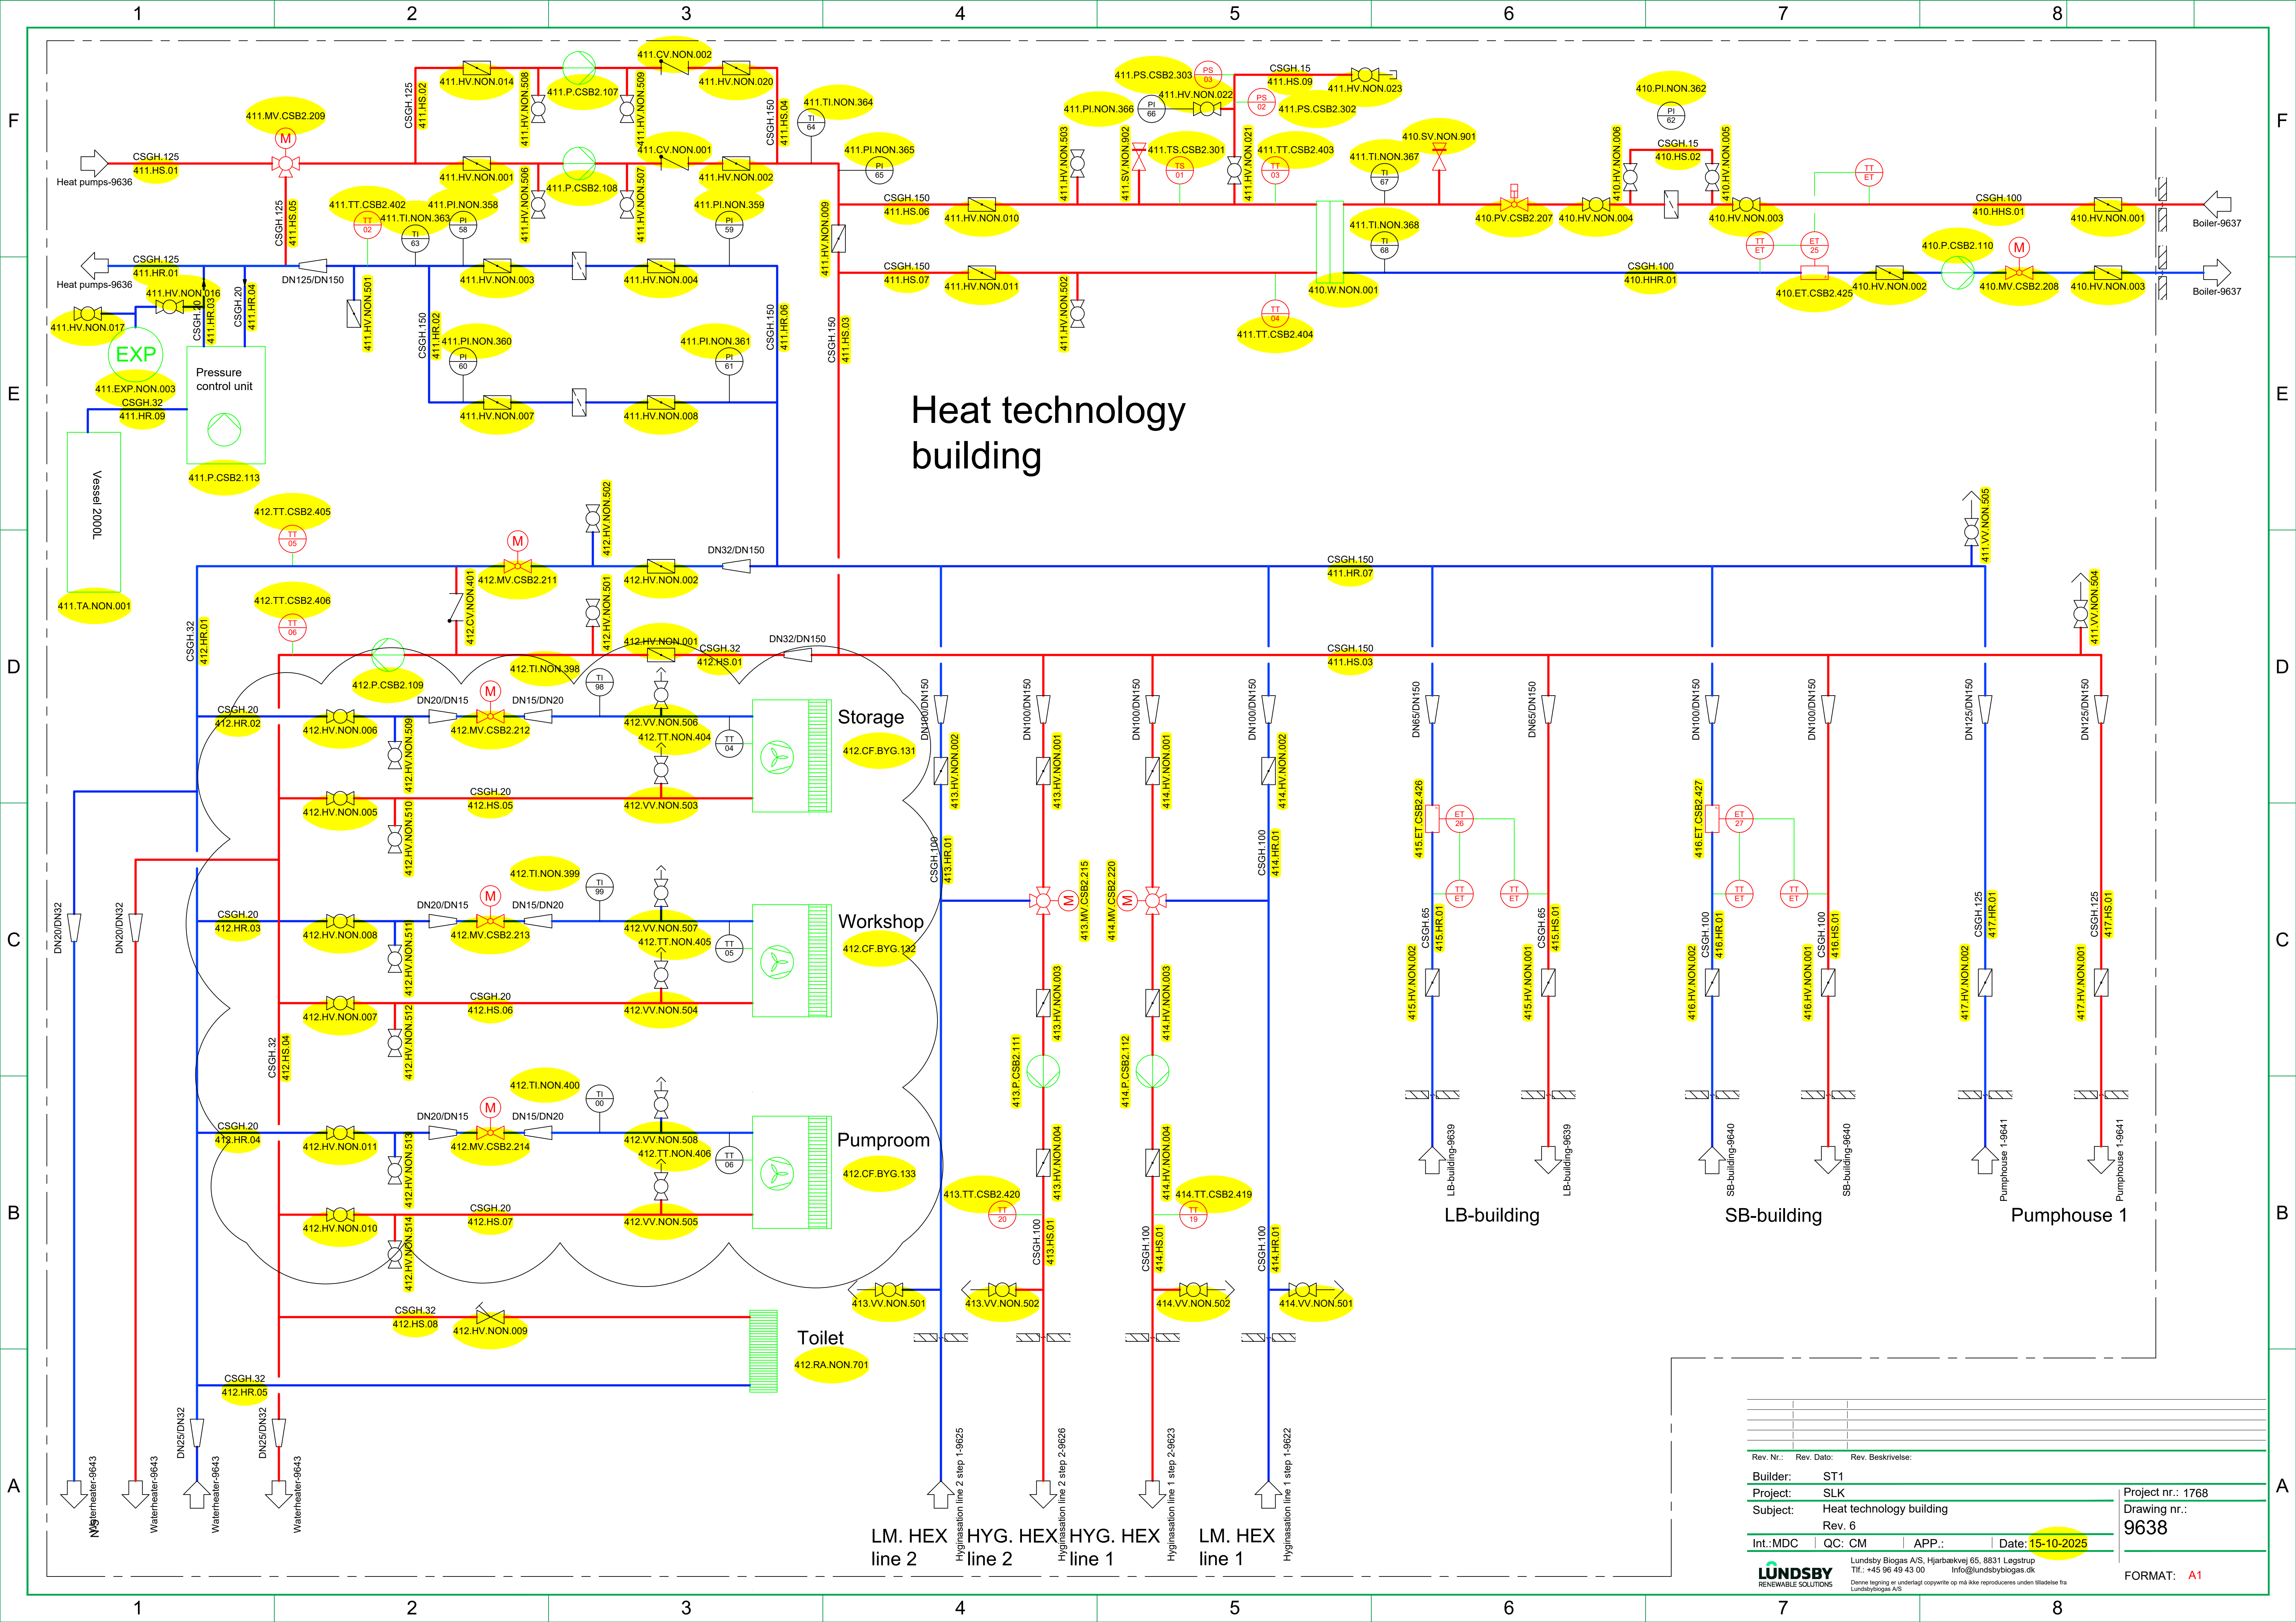

LB-Building

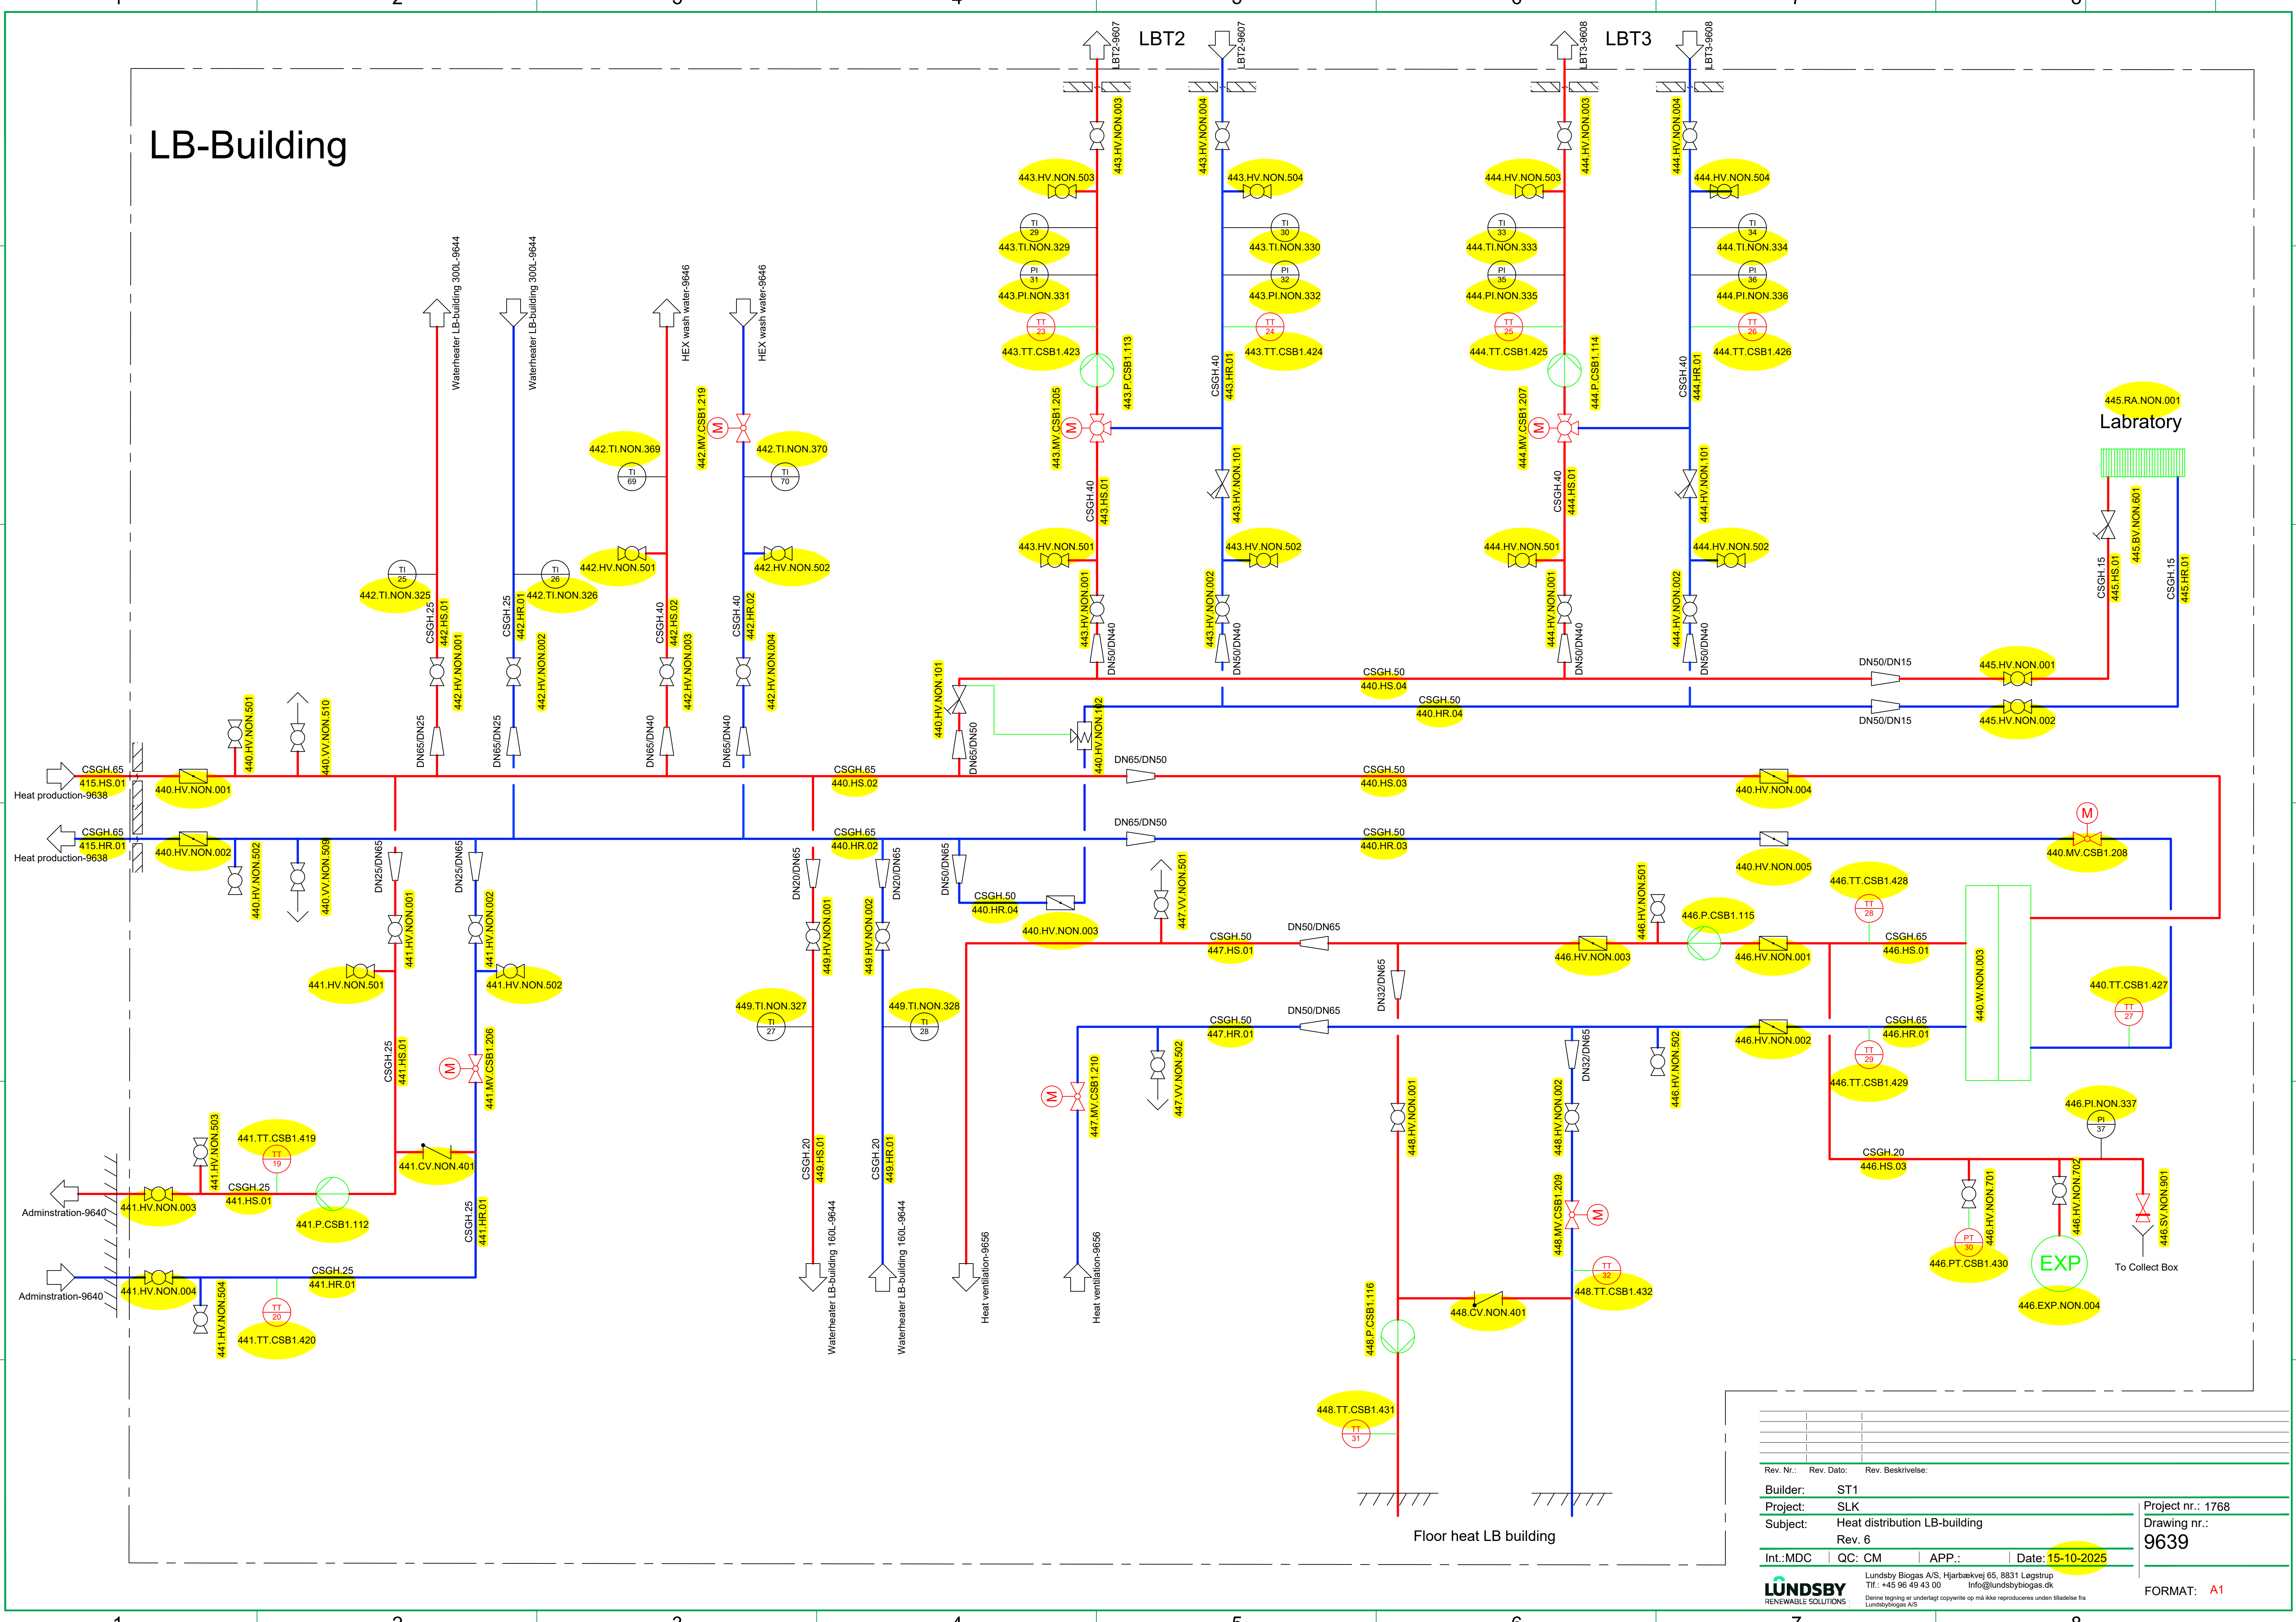


Rev. Nr.:	Rev. Dato:	Rev. Beskrivelse:


Builder:	ST1		
Project:	SLK		
Subject:	Heat distribution LB-building		
Rev. 6			
Int.:MDC	QC: CM	APP.:	Date: 15-10-2025

LUNDSBY
RENEWABLE SOLUTIONS

Lundsby Biogas A/S, Hjarbækvej 65, 8831 Løgstrup
Tlf.: +45 96 49 43 00
info@lundsbybiogas.dk
Denne tegning er underlagt copyright op på ikke reproduceres uden tilladelse fra Lundsbybiogas A/S

Project nr.: 1768
Drawing nr.: 9639
FORMAT: A1

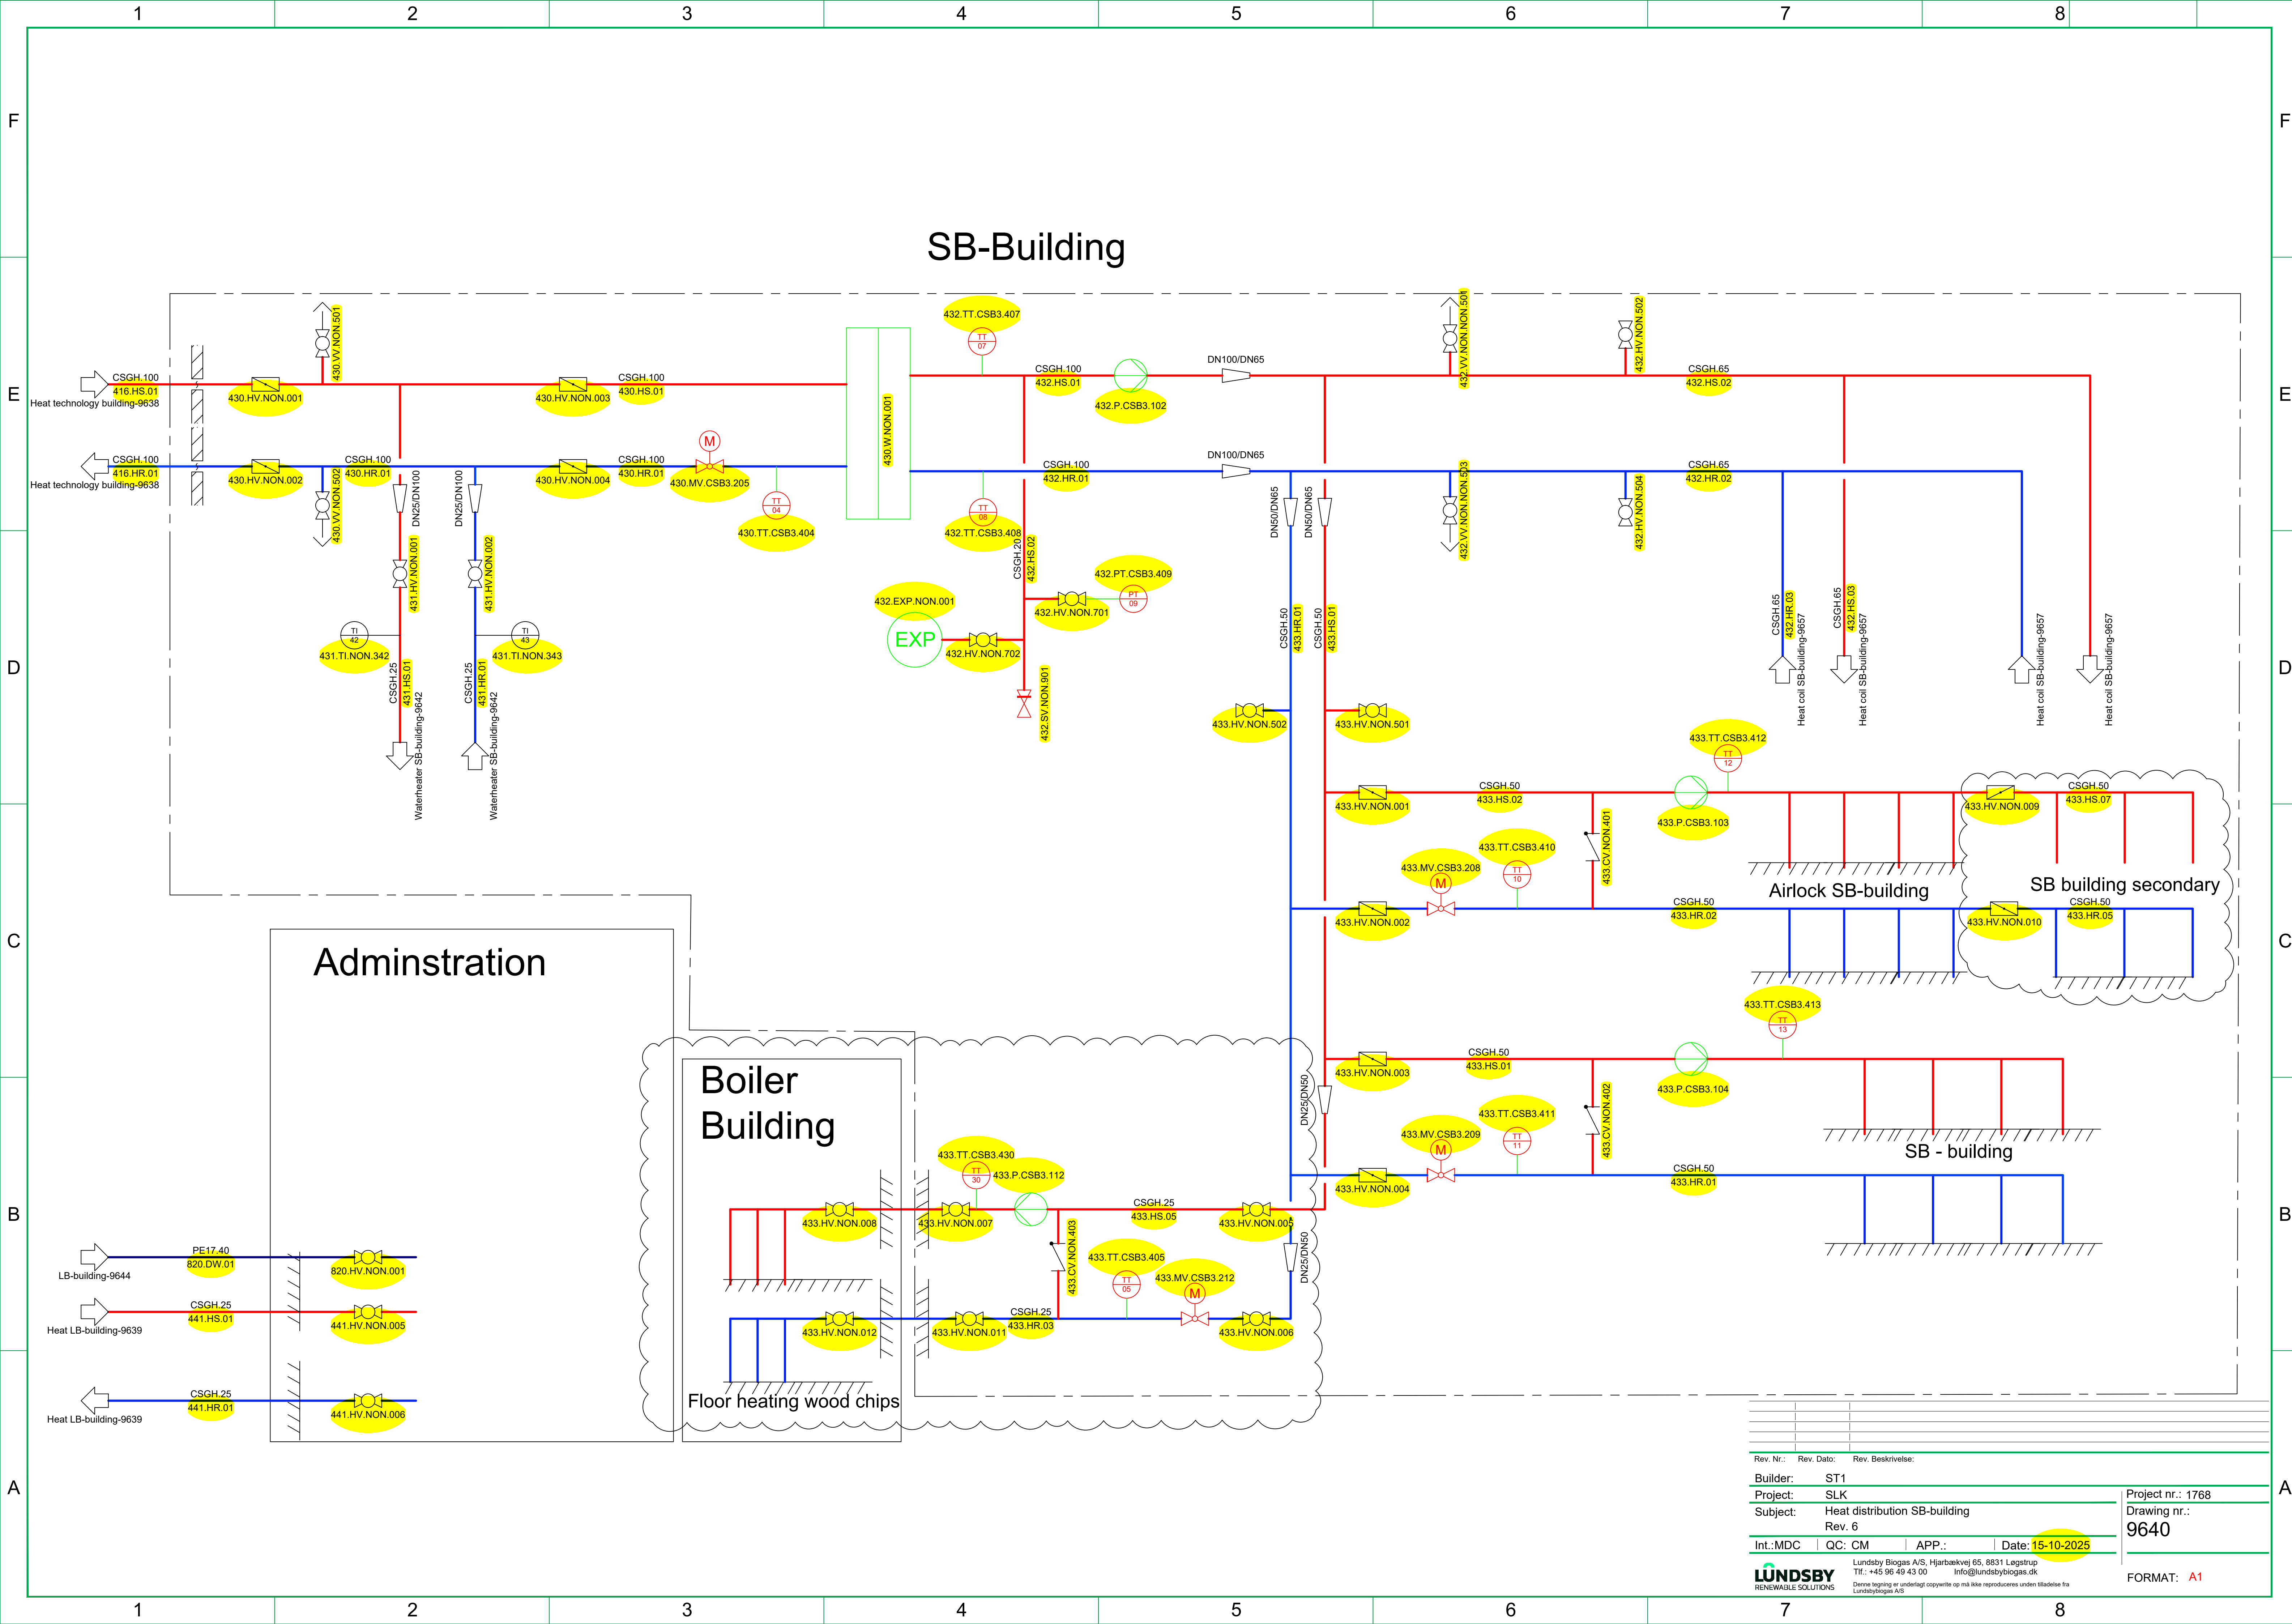

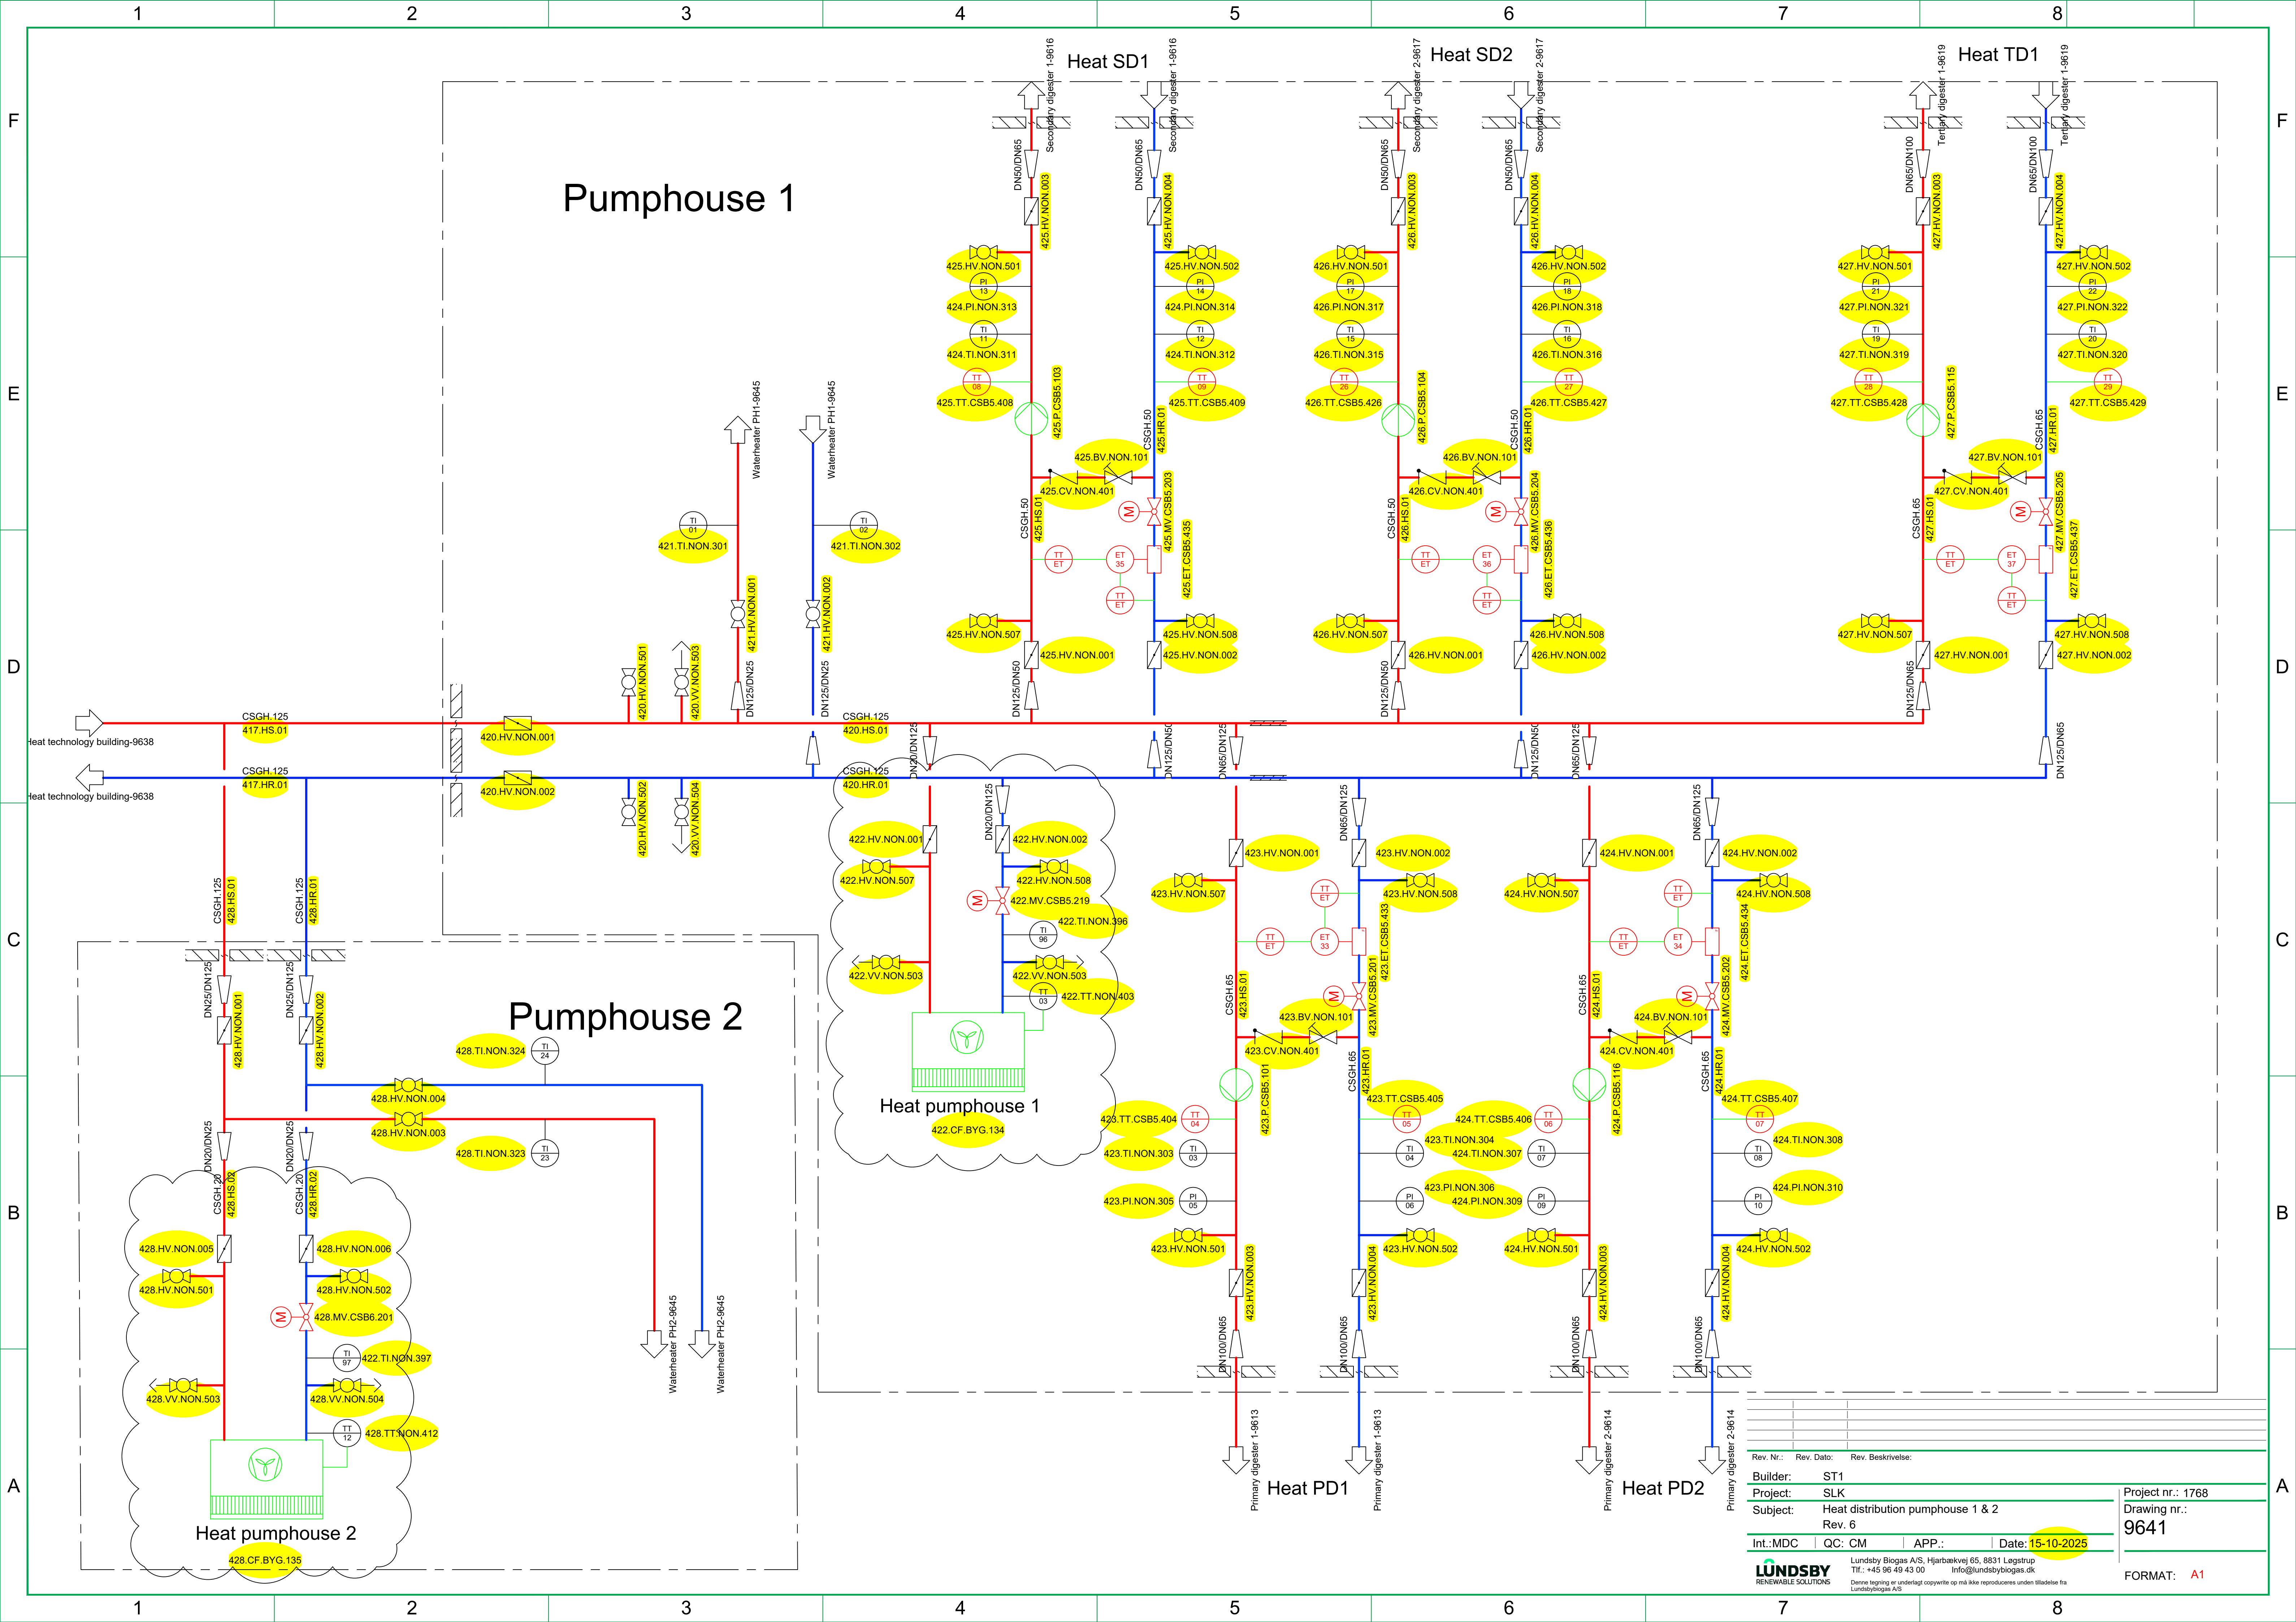


Rev. Nr.:	Rev. Dato:	Rev. Beskrivelse:
Builder:	ST1	
Project:	SLK	
Subject:	Heat distribution pumphouse 1 & 2	
Int.:MDC	QC: CM	APP.:
Date:	15-10-2025	
Project nr.:	1768	
Drawing nr.:	9641	
FORMAT:	A1	

LUNDSBY
RENEWABLE SOLUTIONS


Lundsby Biogas A/S, Hjarbækvej 65, 8831 Løgstrup
Tlf.: +45 96 49 43 00
info@lundsbybiogas.dk
Denne tegning er underlagt copyright op på ikke reproduceres uden tilladelse fra Lundsbybiogas A/S

SB-Building

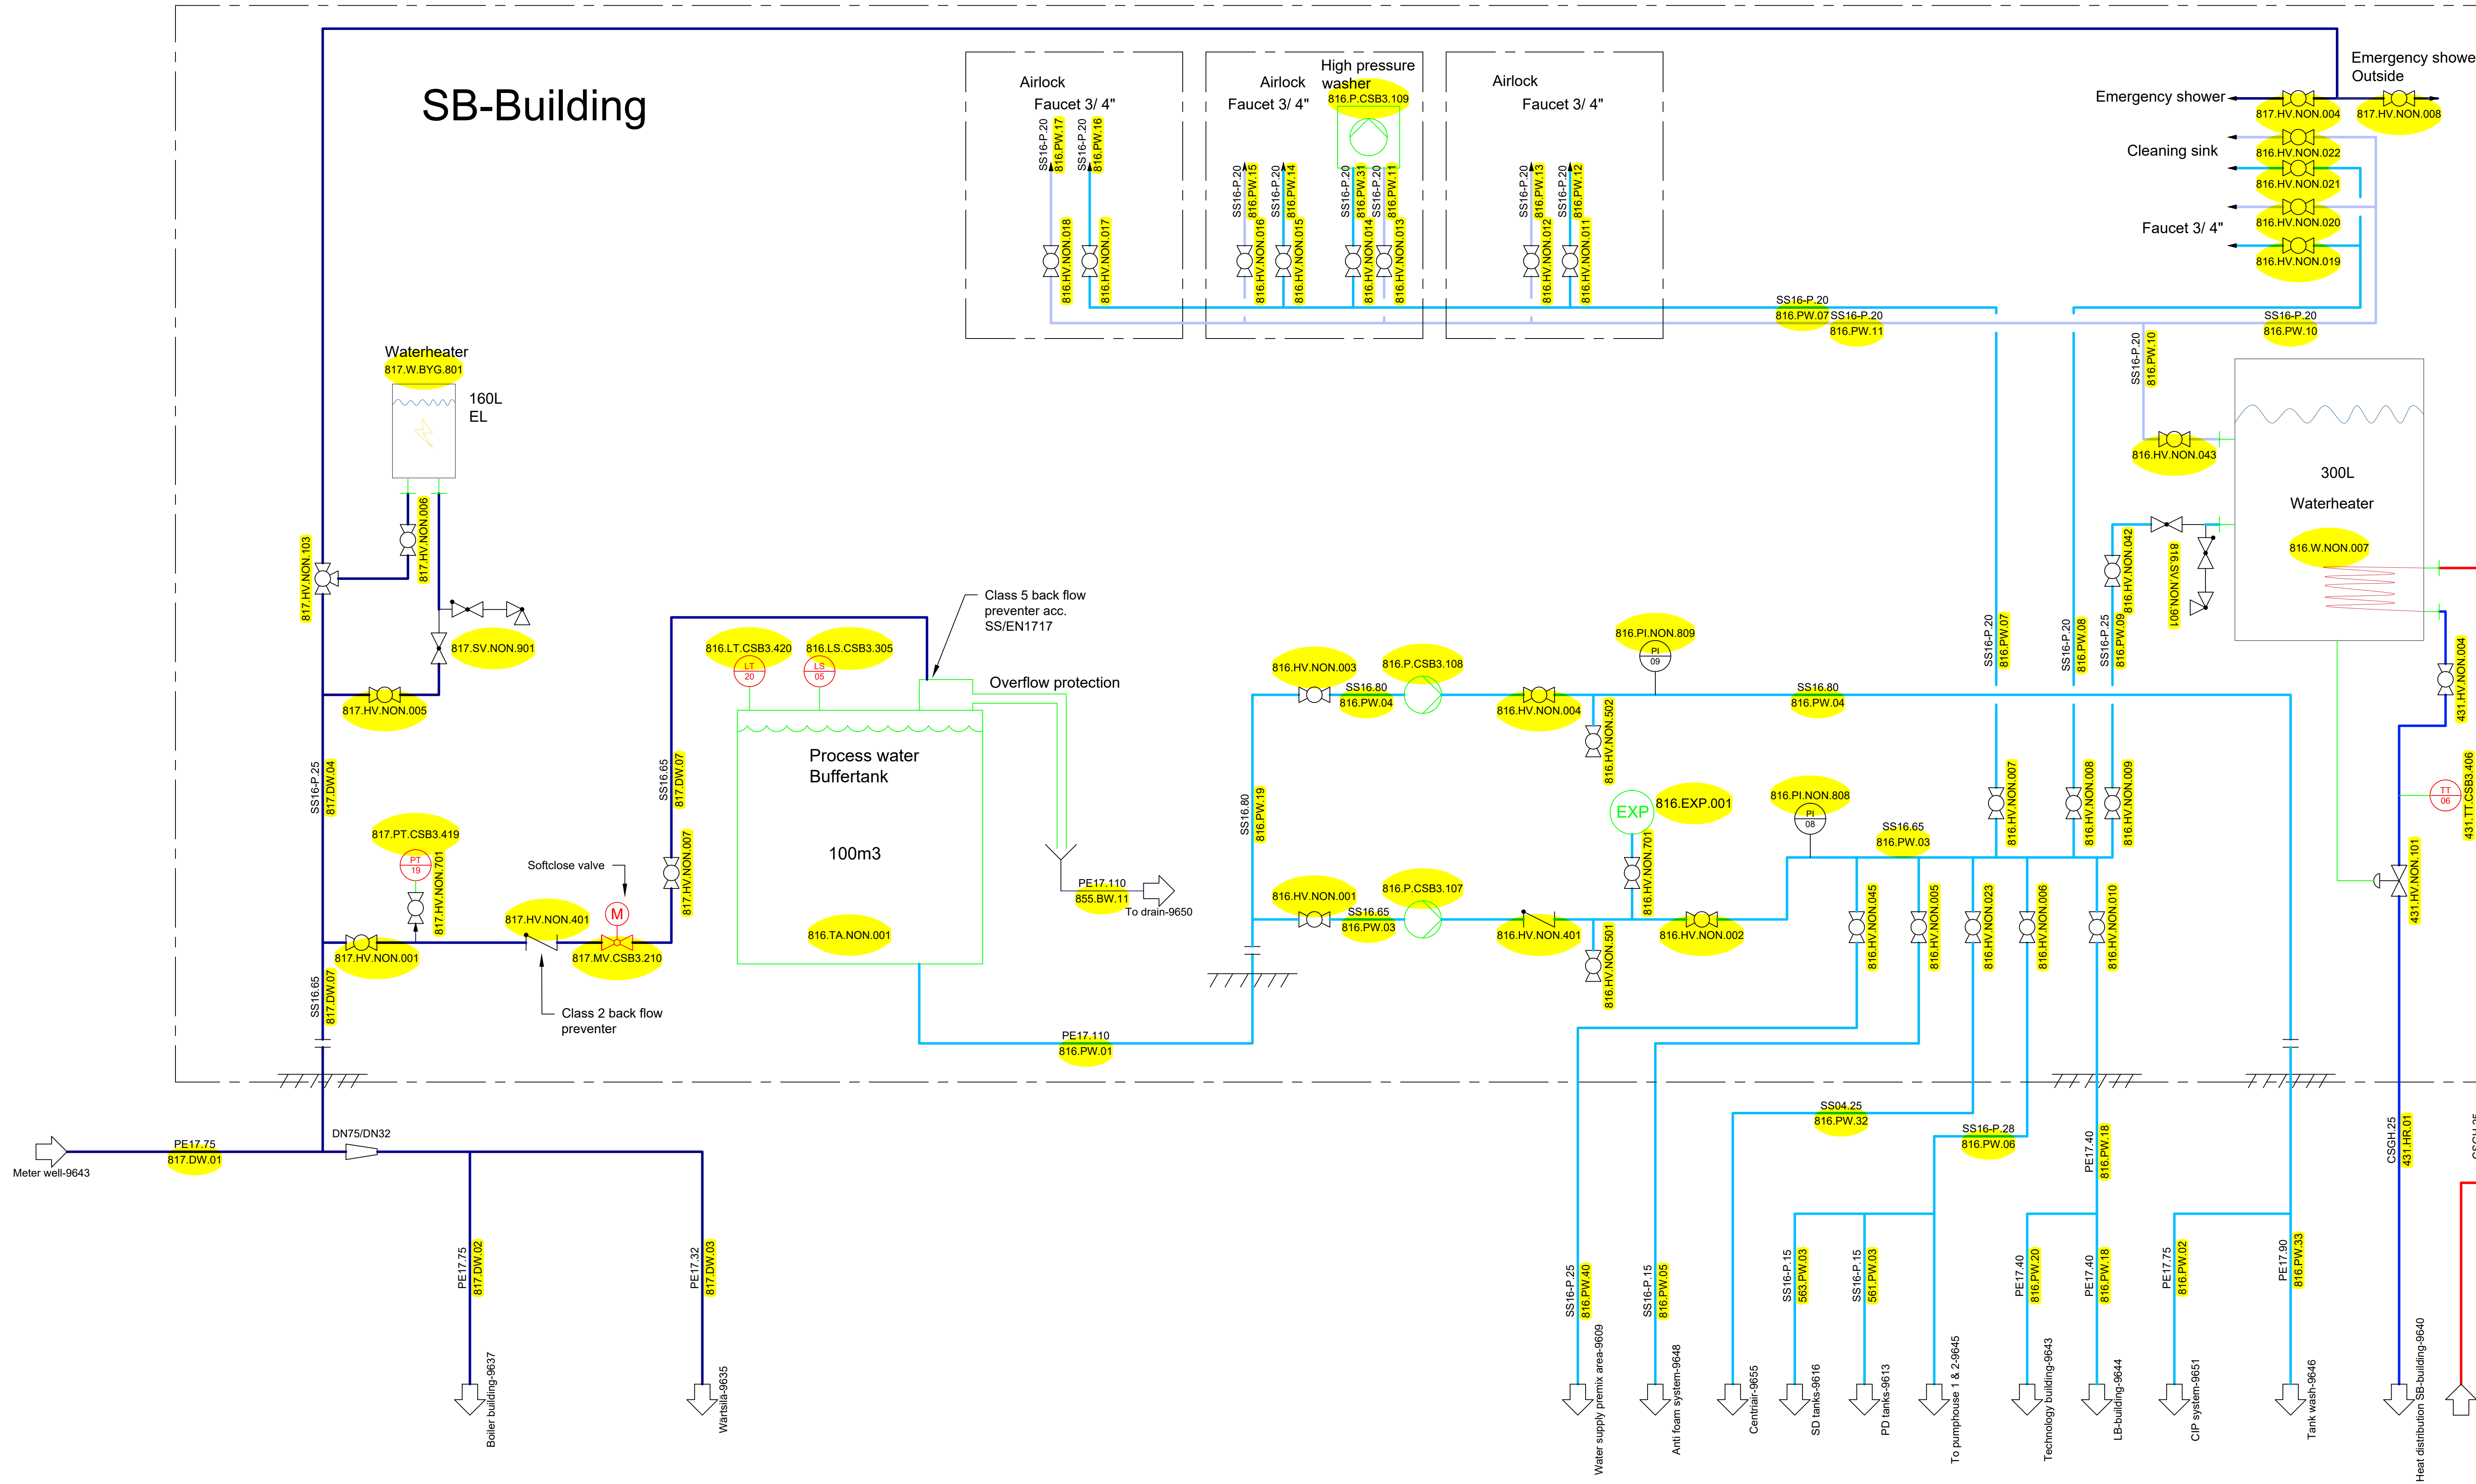


Rev. Nr.:	Rev. Dato:	Rev. Beskrivelse:
Builder:	ST1	
Project:	SLK	
Subject:	Water distribution SB-building	
Rev. 6		
Int.:MDC	QC:CM	APP.:
Date:	15-10-2025	
LUNDSBY RENEWABLE SOLUTIONS		
Lundsby Biogas A/S, Hjarbækvej 65, 8831 Løgstrup Tlf.: +45 96 49 43 00 info@lundsbybiogas.dk		
Denne tegning er underlagt copyright op på ikke reproduceres uden tilladelse fra Lundsbybiogas A/S		
Project nr.: 1768		Drawing nr.: 9642
FORMAT:		A1

Technology building

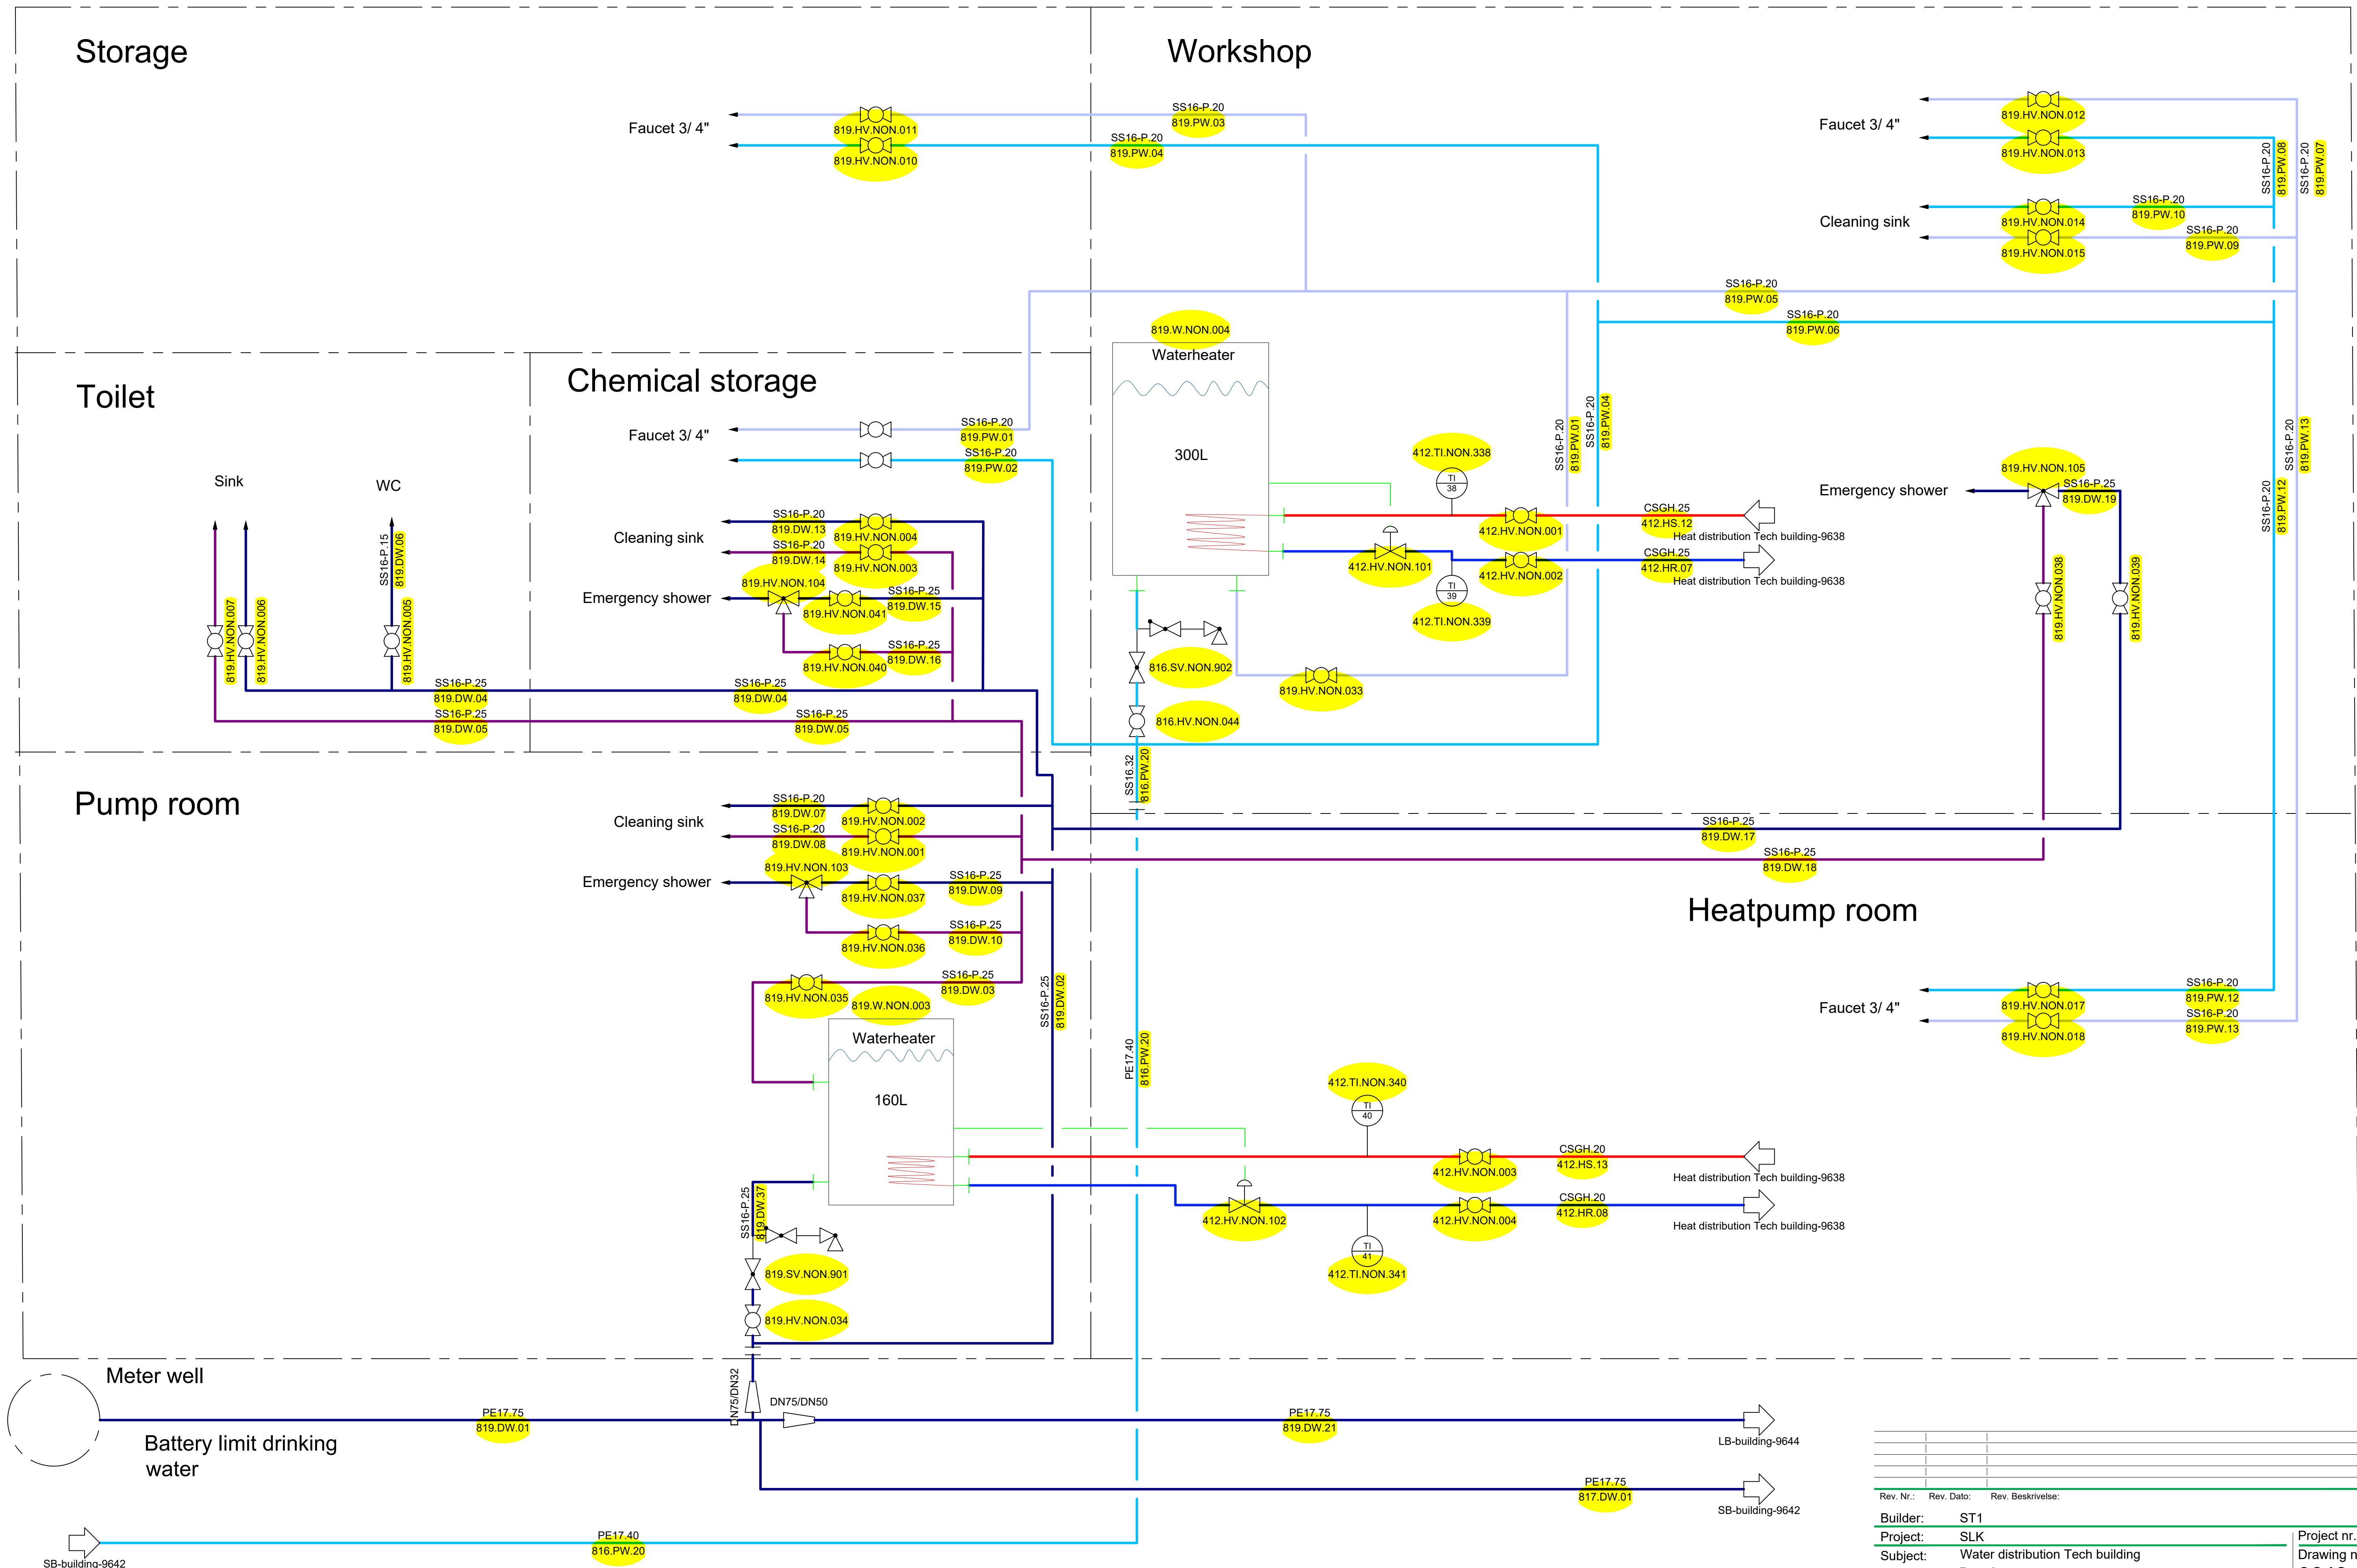


Rev. Nr.:	Rev. Dato:	Rev. Beskrivelse:
Builder:	ST1	
Project:	SLK	
Subject:	Water distribution Tech building	
Rev. 6		
Int.:MDC	QC:CM	APP.:
Date:	15-10-2025	
LUNDSBY RENEWABLE SOLUTIONS		
Lundsby Biogas A/S, Hjarbækvej 65, 8831 Løgstrup Tlf.: +45 96 49 43 00 info@lundsbybiogas.dk		
Denne tegning er underlagt copyright og må ikke reproduceres uden tilladelse fra Lundsbybiogas A/S		
Project nr.:	1768	
Drawing nr.:	9643	
FORMAT:	A1	

LB-building

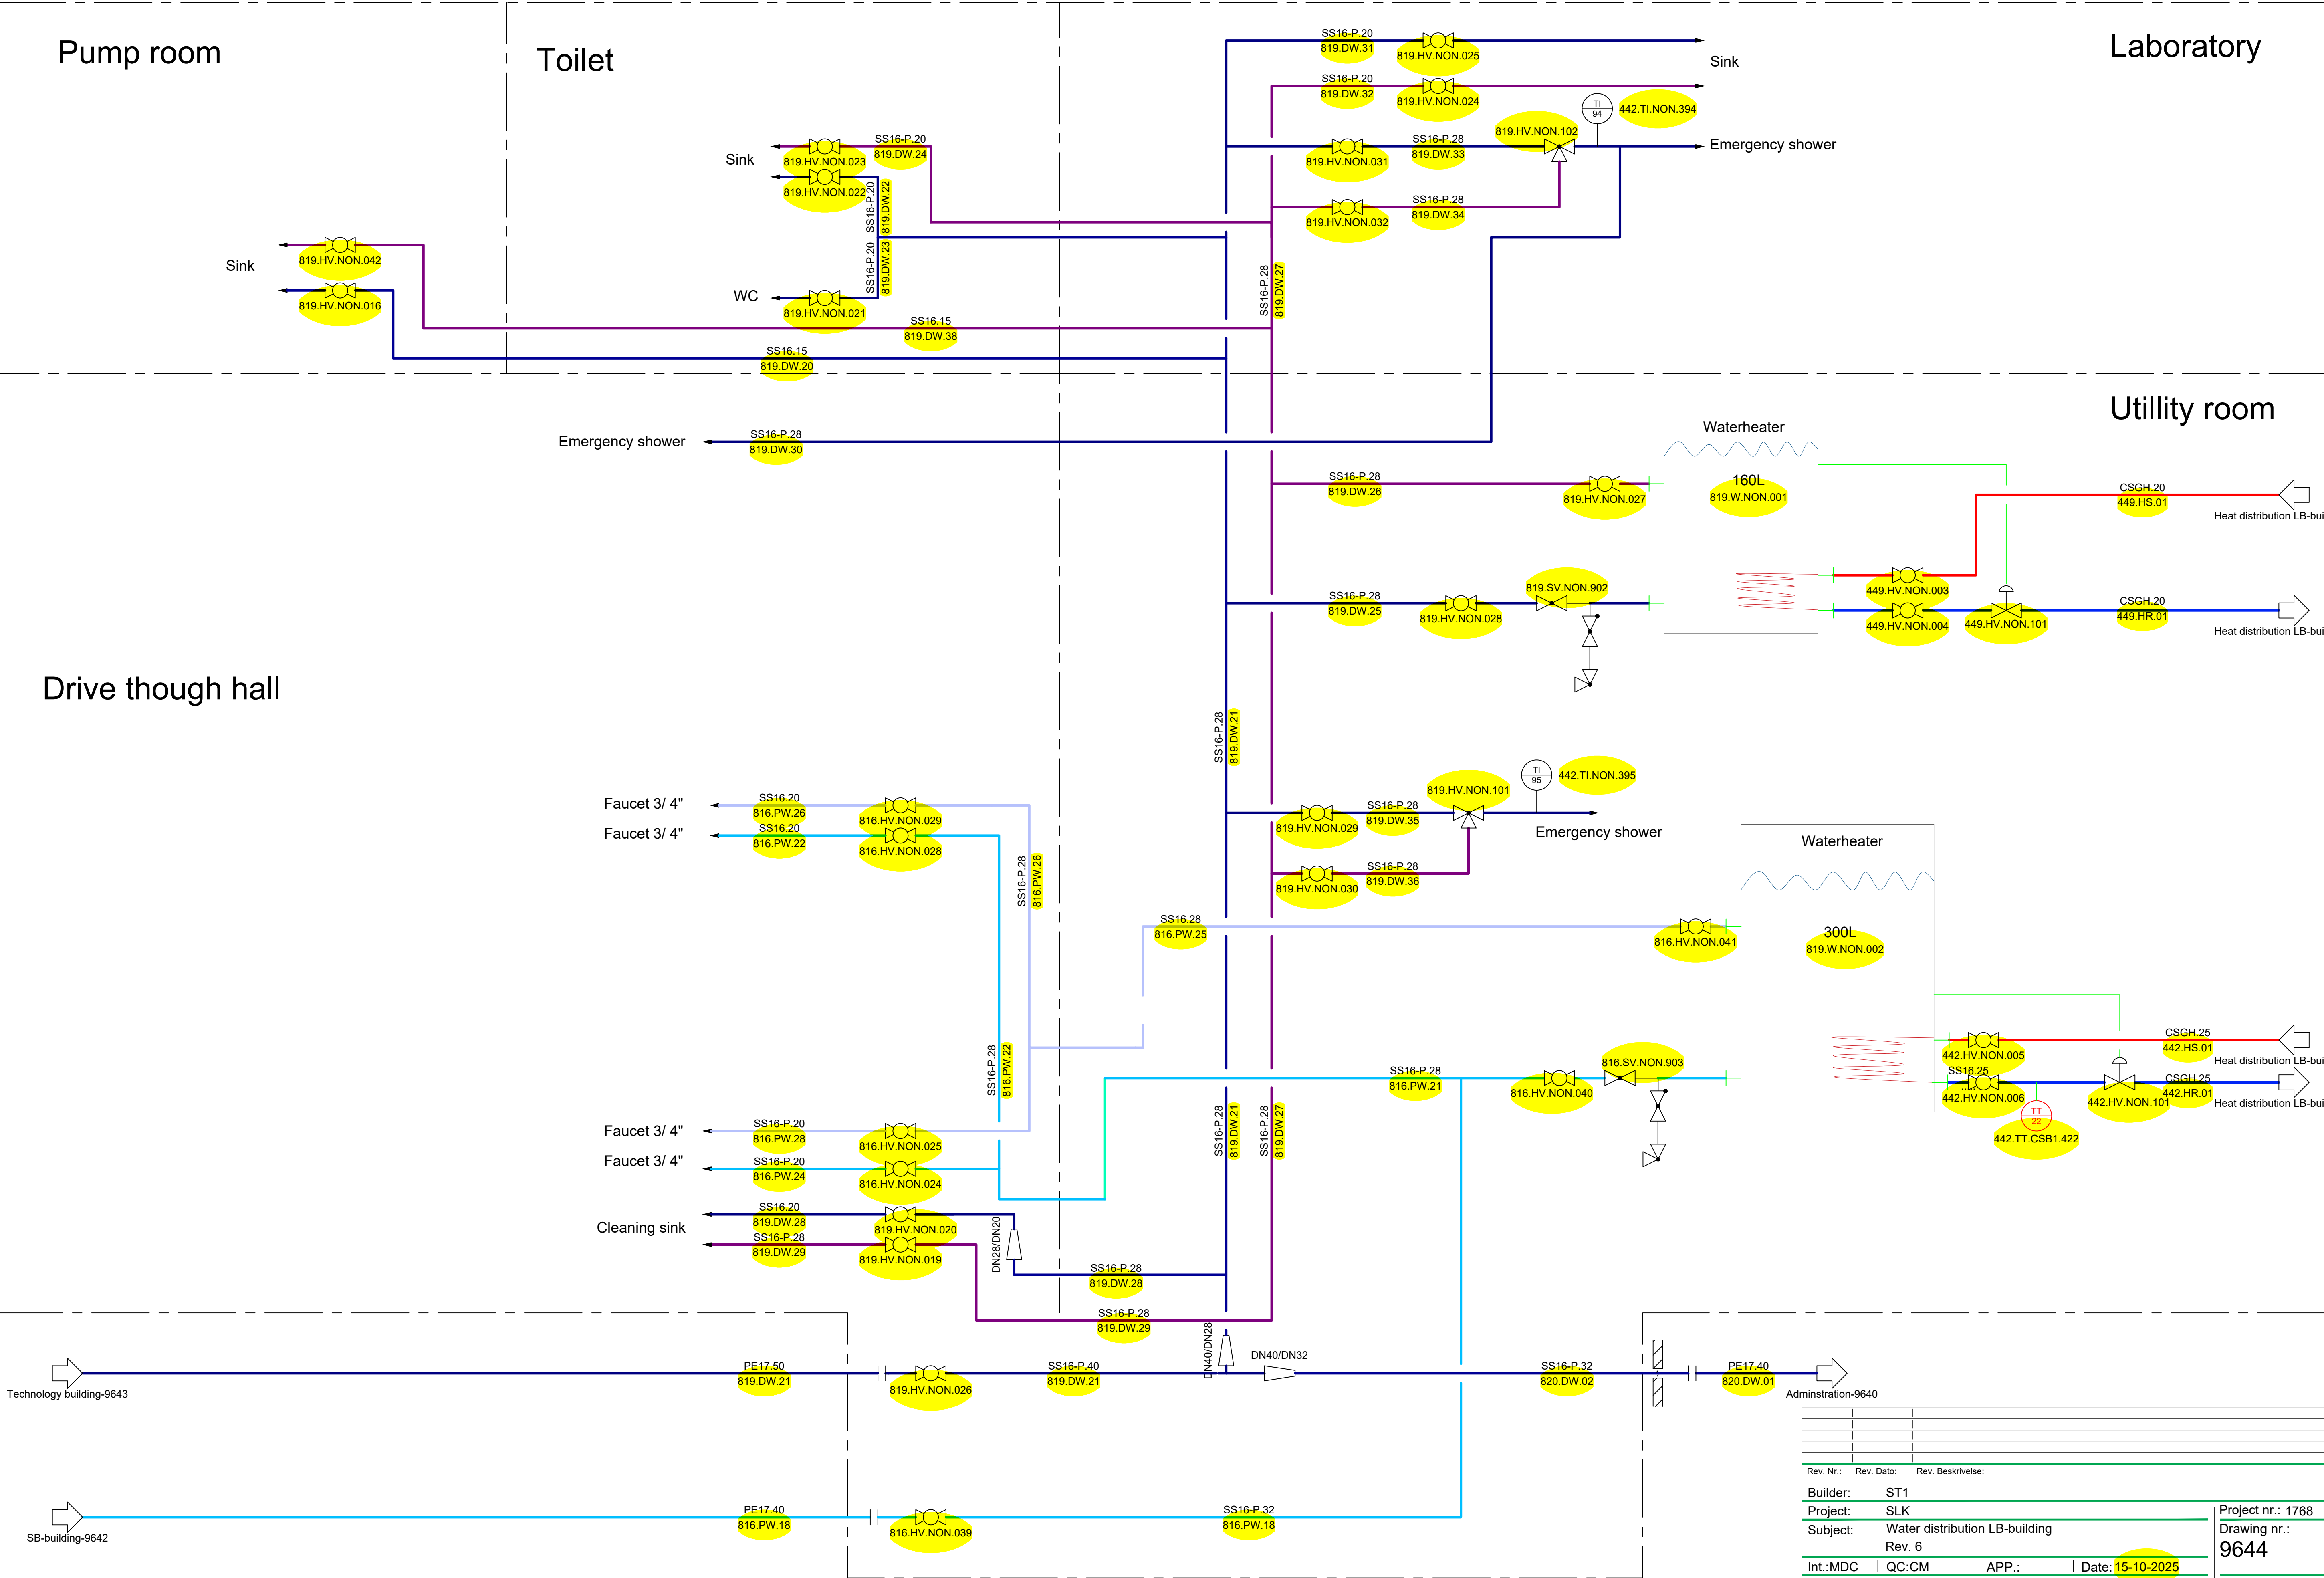


Rev. Nr.:	Rev. Dato:	Rev. Beskrivelse:
Builder:	ST1	
Project:	SLK	
Subject:	Water distribution LB-building	
	Rev. 6	
Int.:MDC	QC:CM	APP.:
		Date: 15-10-2025
LUNDSBY RENEWABLE SOLUTIONS Lundsby Biogas A/S, Hjarbækvej 65, 8831 Løgstrup Tlf.: +45 96 49 43 00 info@lundsbybiogas.dk Denne tegning er underlagt copyright op må ikke reproduceres uden tilladelse fra Lundsbybiogas A/S		
Project nr.: 1768 Drawing nr.: 9644 FORMAT: A1		


Pumphouse 1

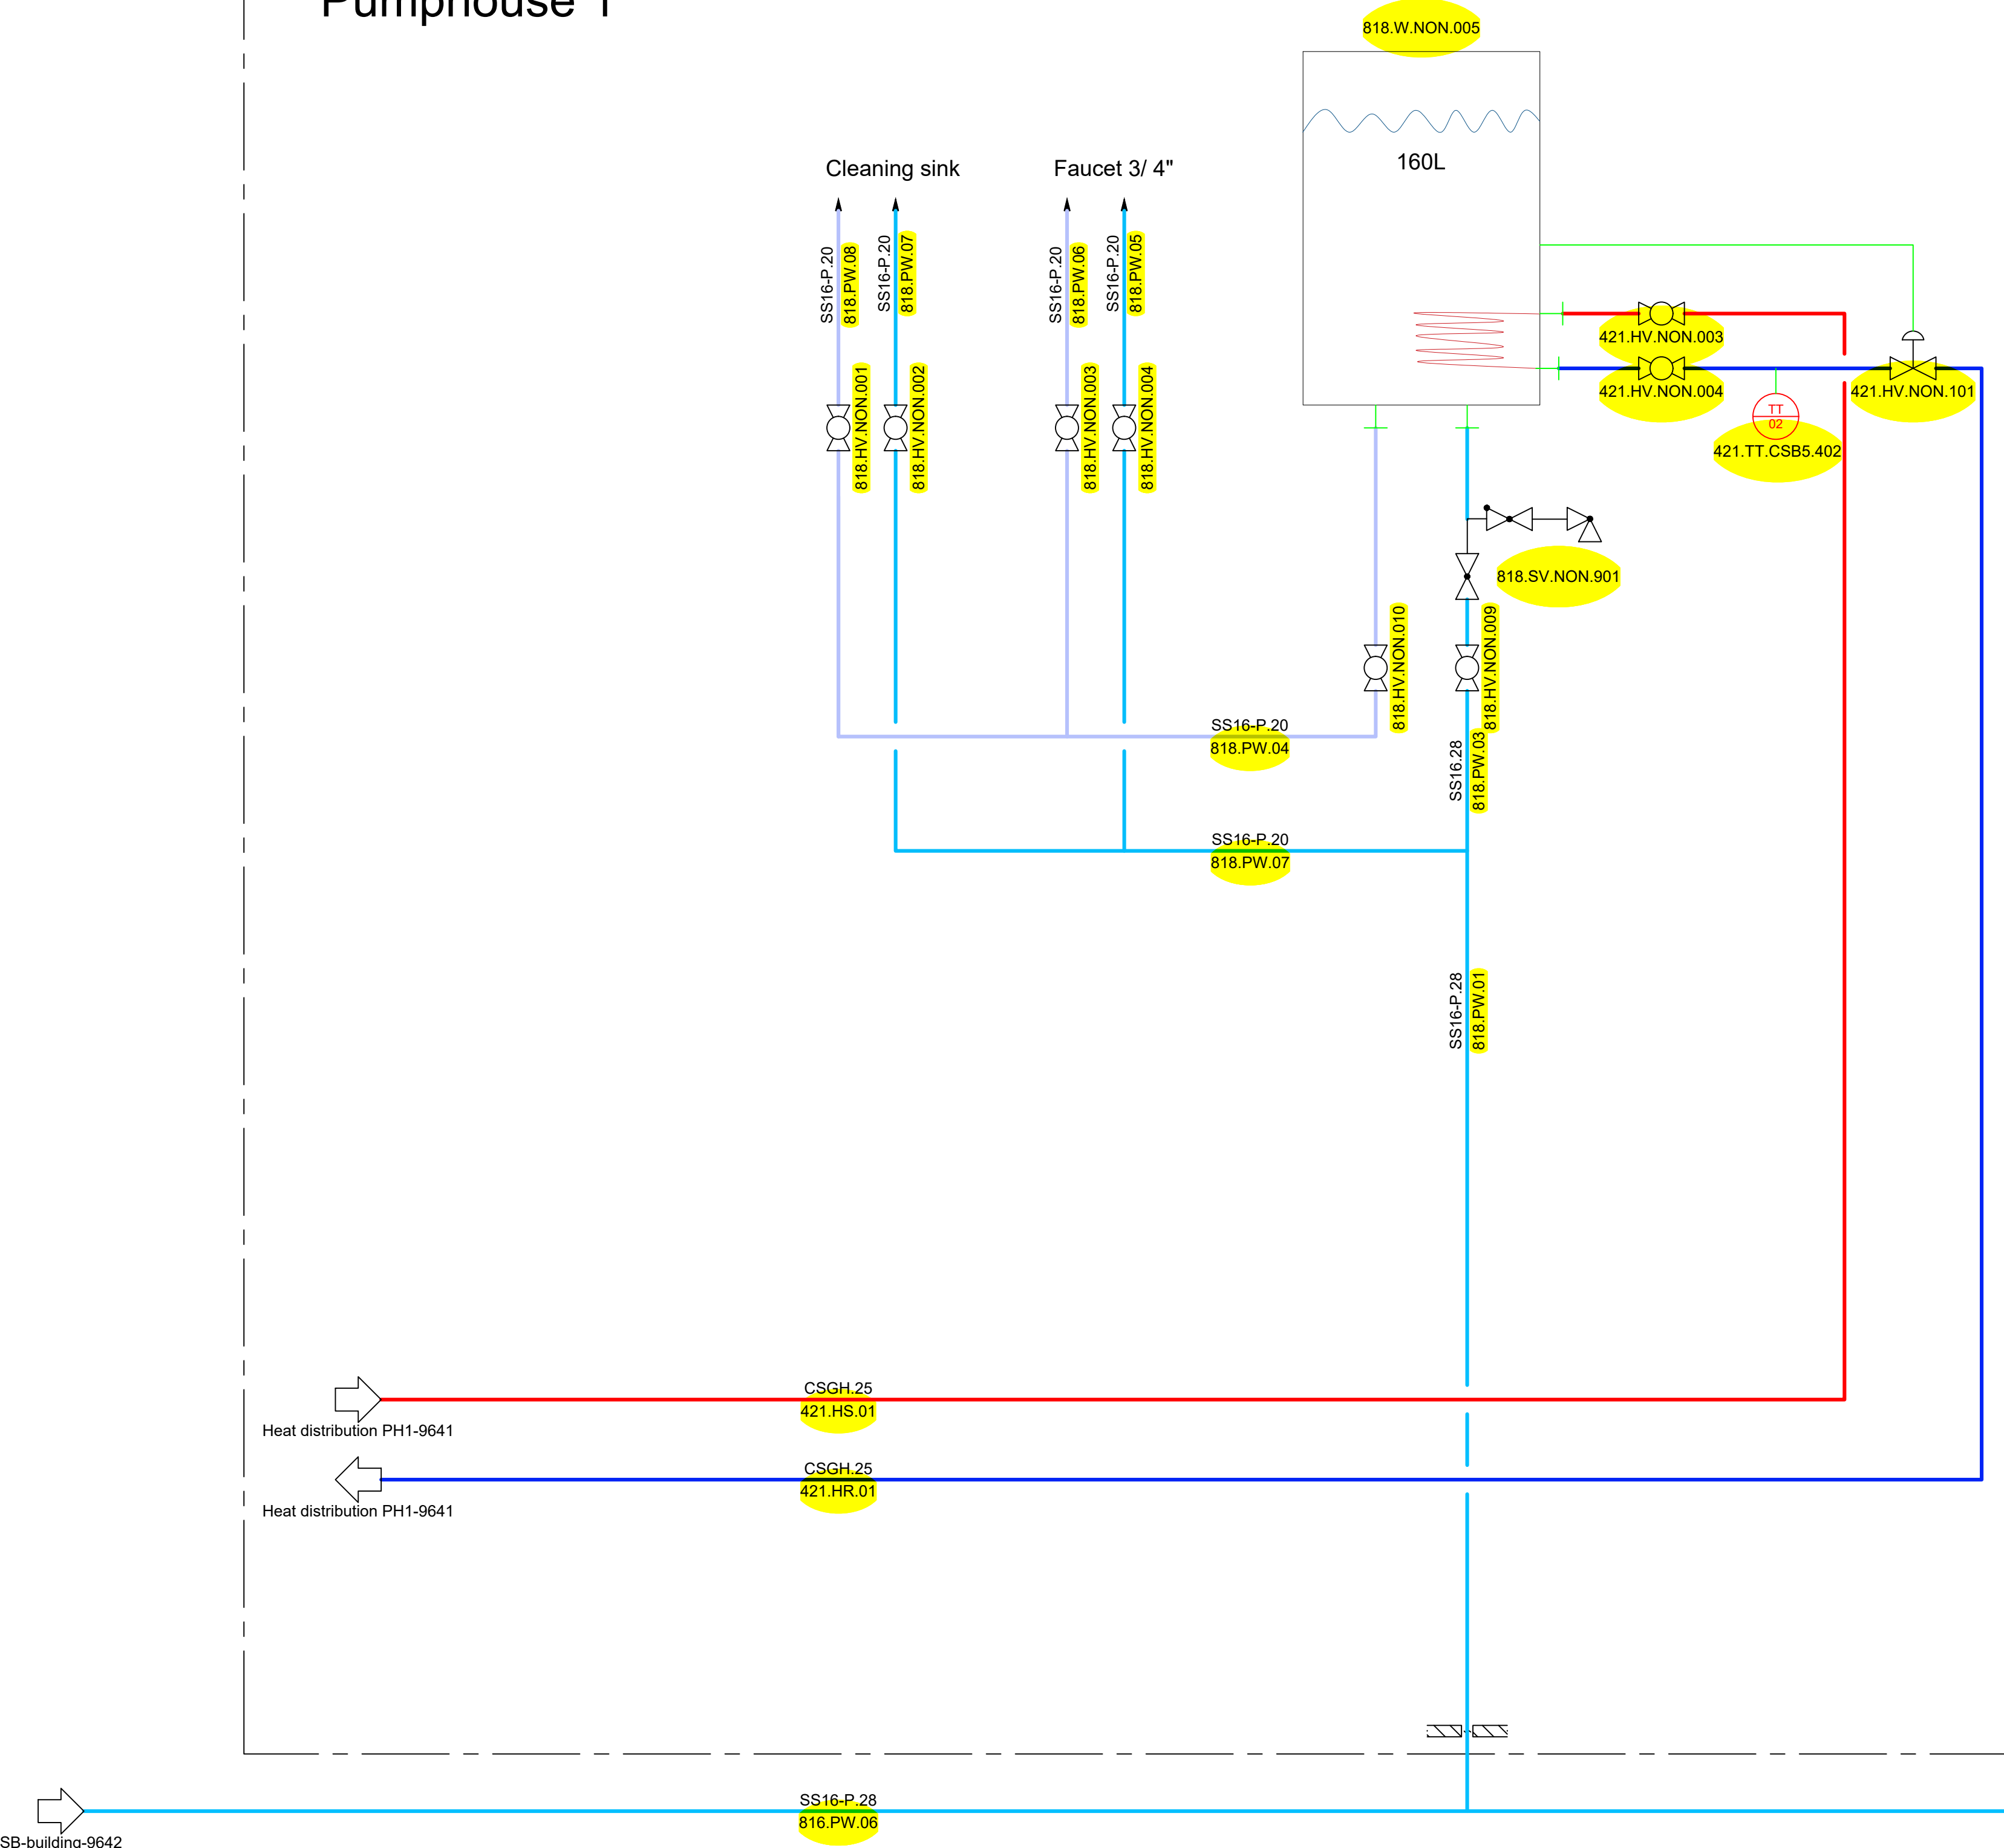


Pumphouse 2

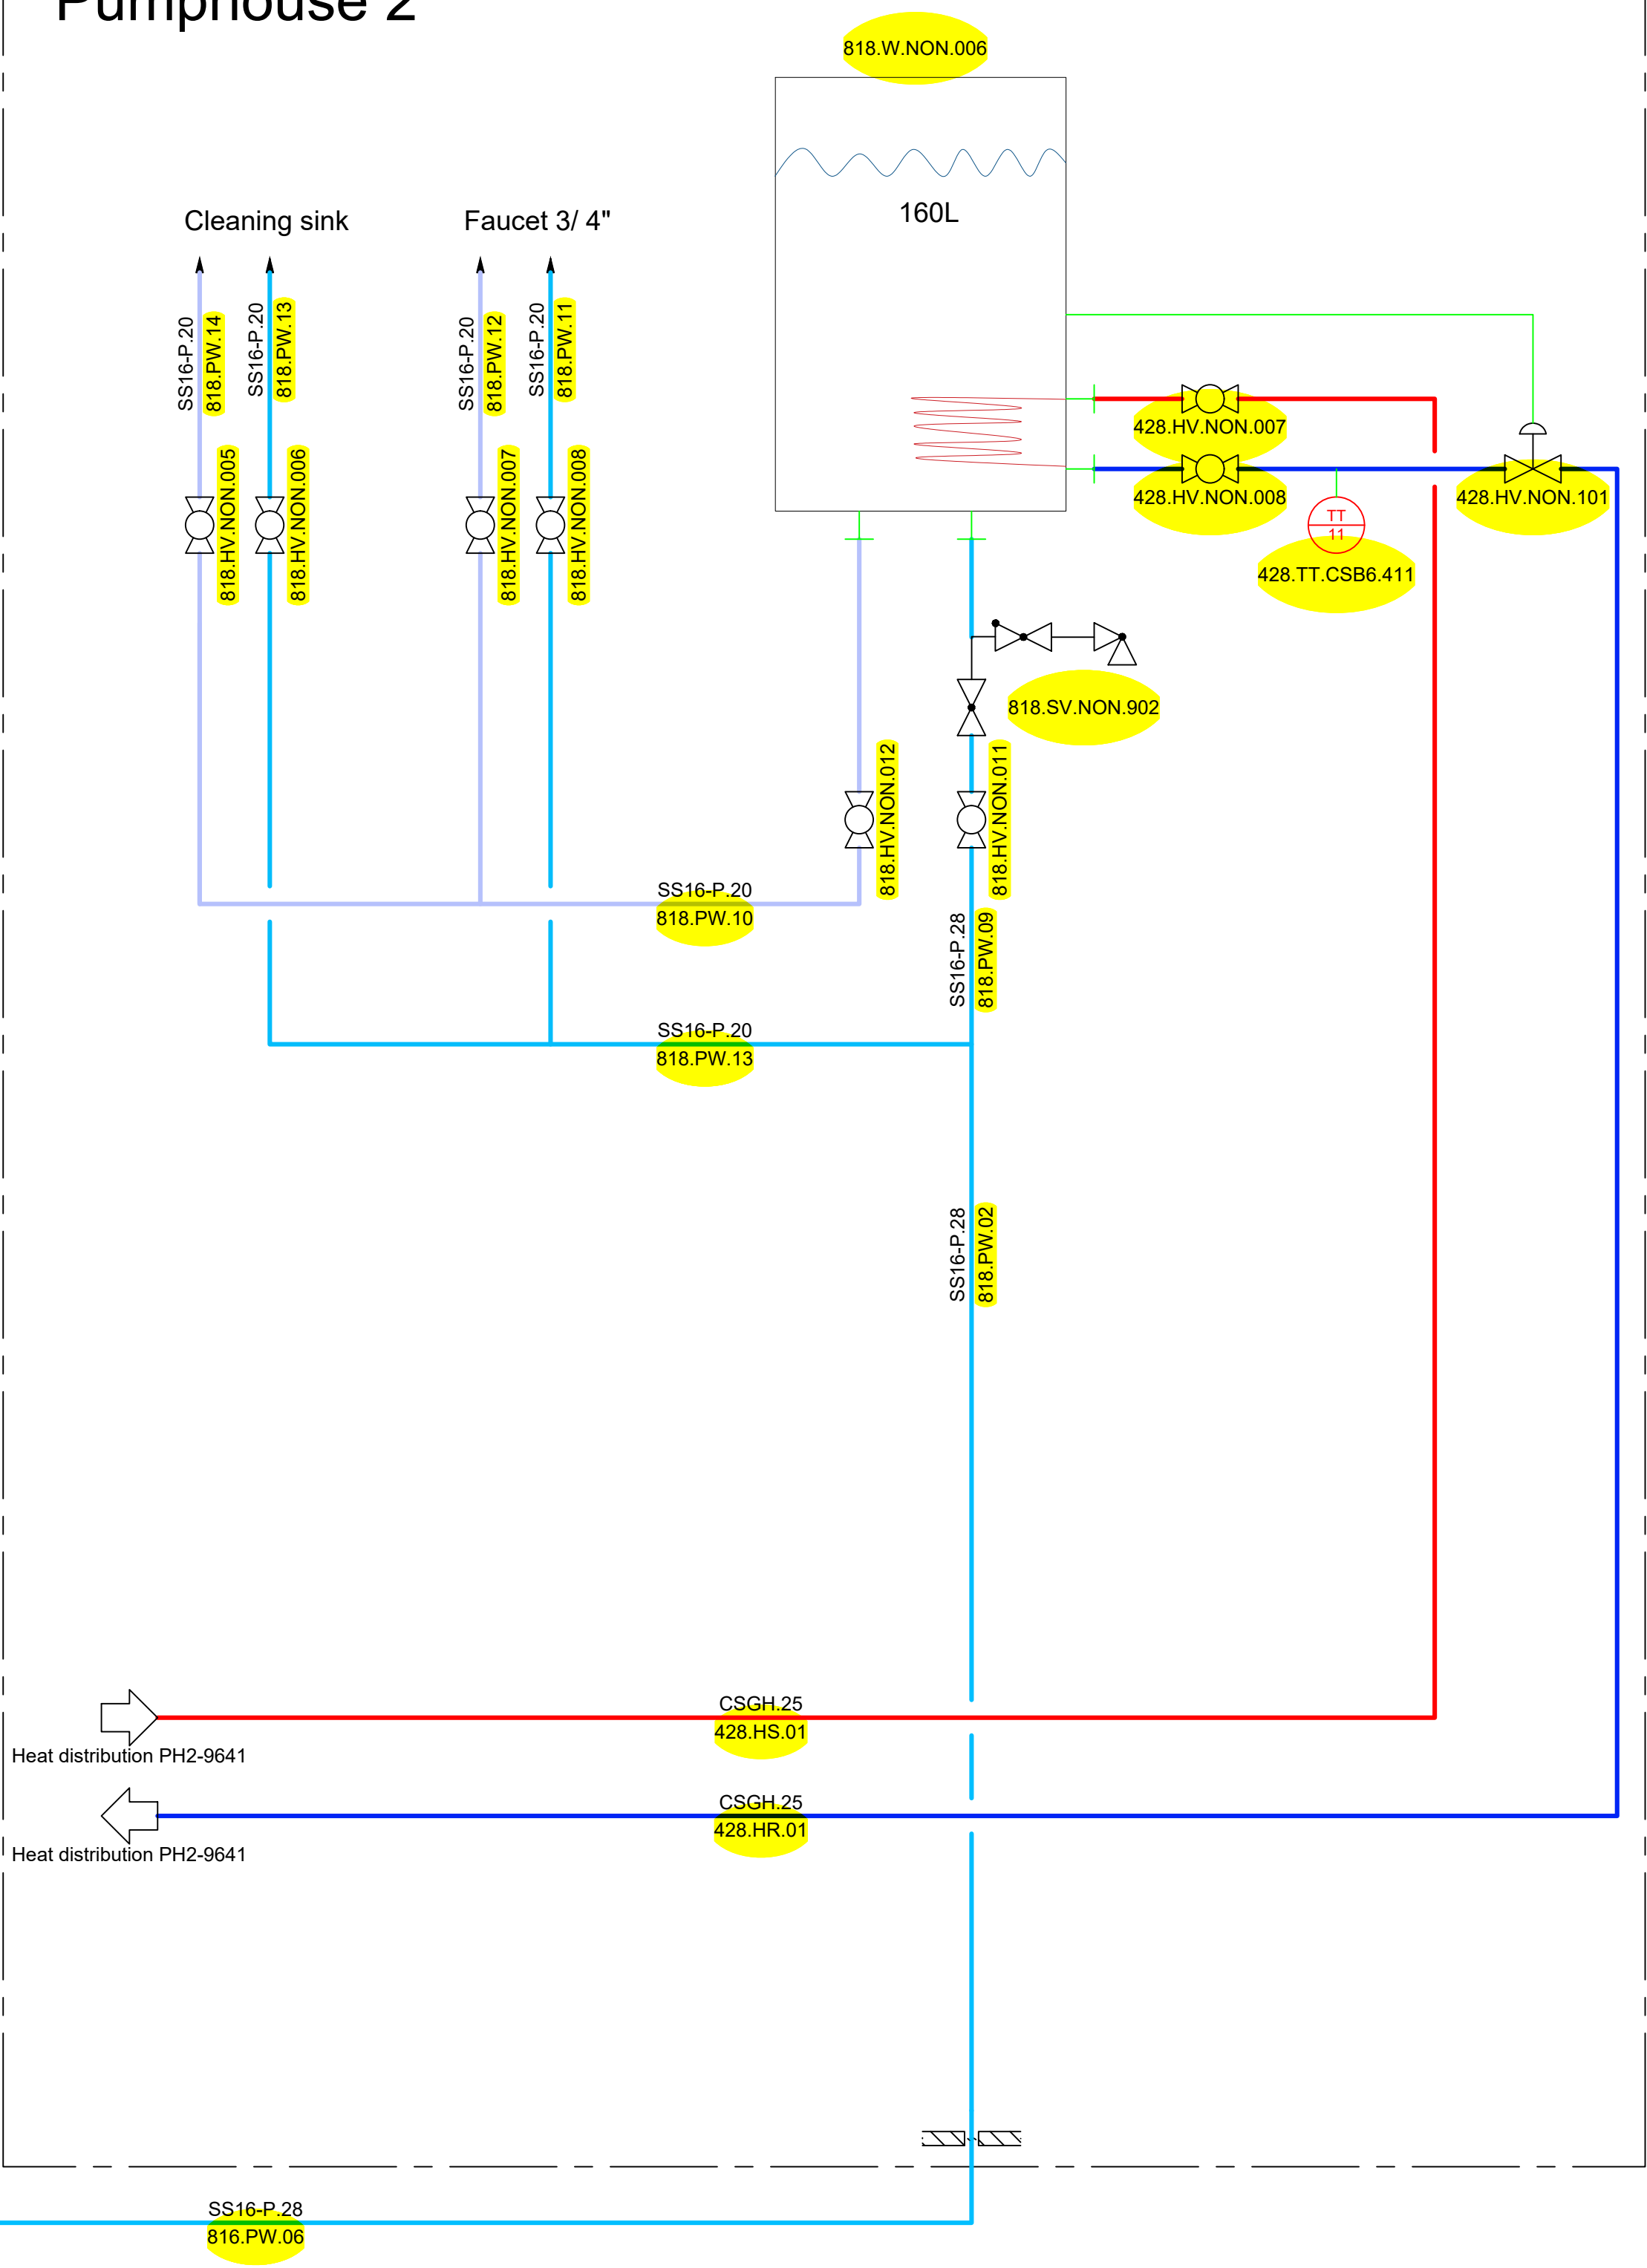

Rev. Nr.:	Rev. Dato:	Rev. Beskrivelse:
Builder:	ST1	
Project:	SLK	
Subject:	Water distribution pumphouse 1 & 2	
Rev. 6		
Int.:MDC	QC:CM	APP.:
Date:	15-10-2025	
LUNDSBY RENEWABLE SOLUTIONS		
Lundsby Biogas A/S, Hjarbækvej 65, 8831 Løgstrup Tlf.: +45 96 49 43 00 info@lundsbybiogas.dk		
Denne tegning er underlagt copyright og må ikke reproducere uden tilladelse fra Lundsbybiogas A/S		
Project nr.: 1768		
Drawing nr.: 9645		
FORMAT: A1		

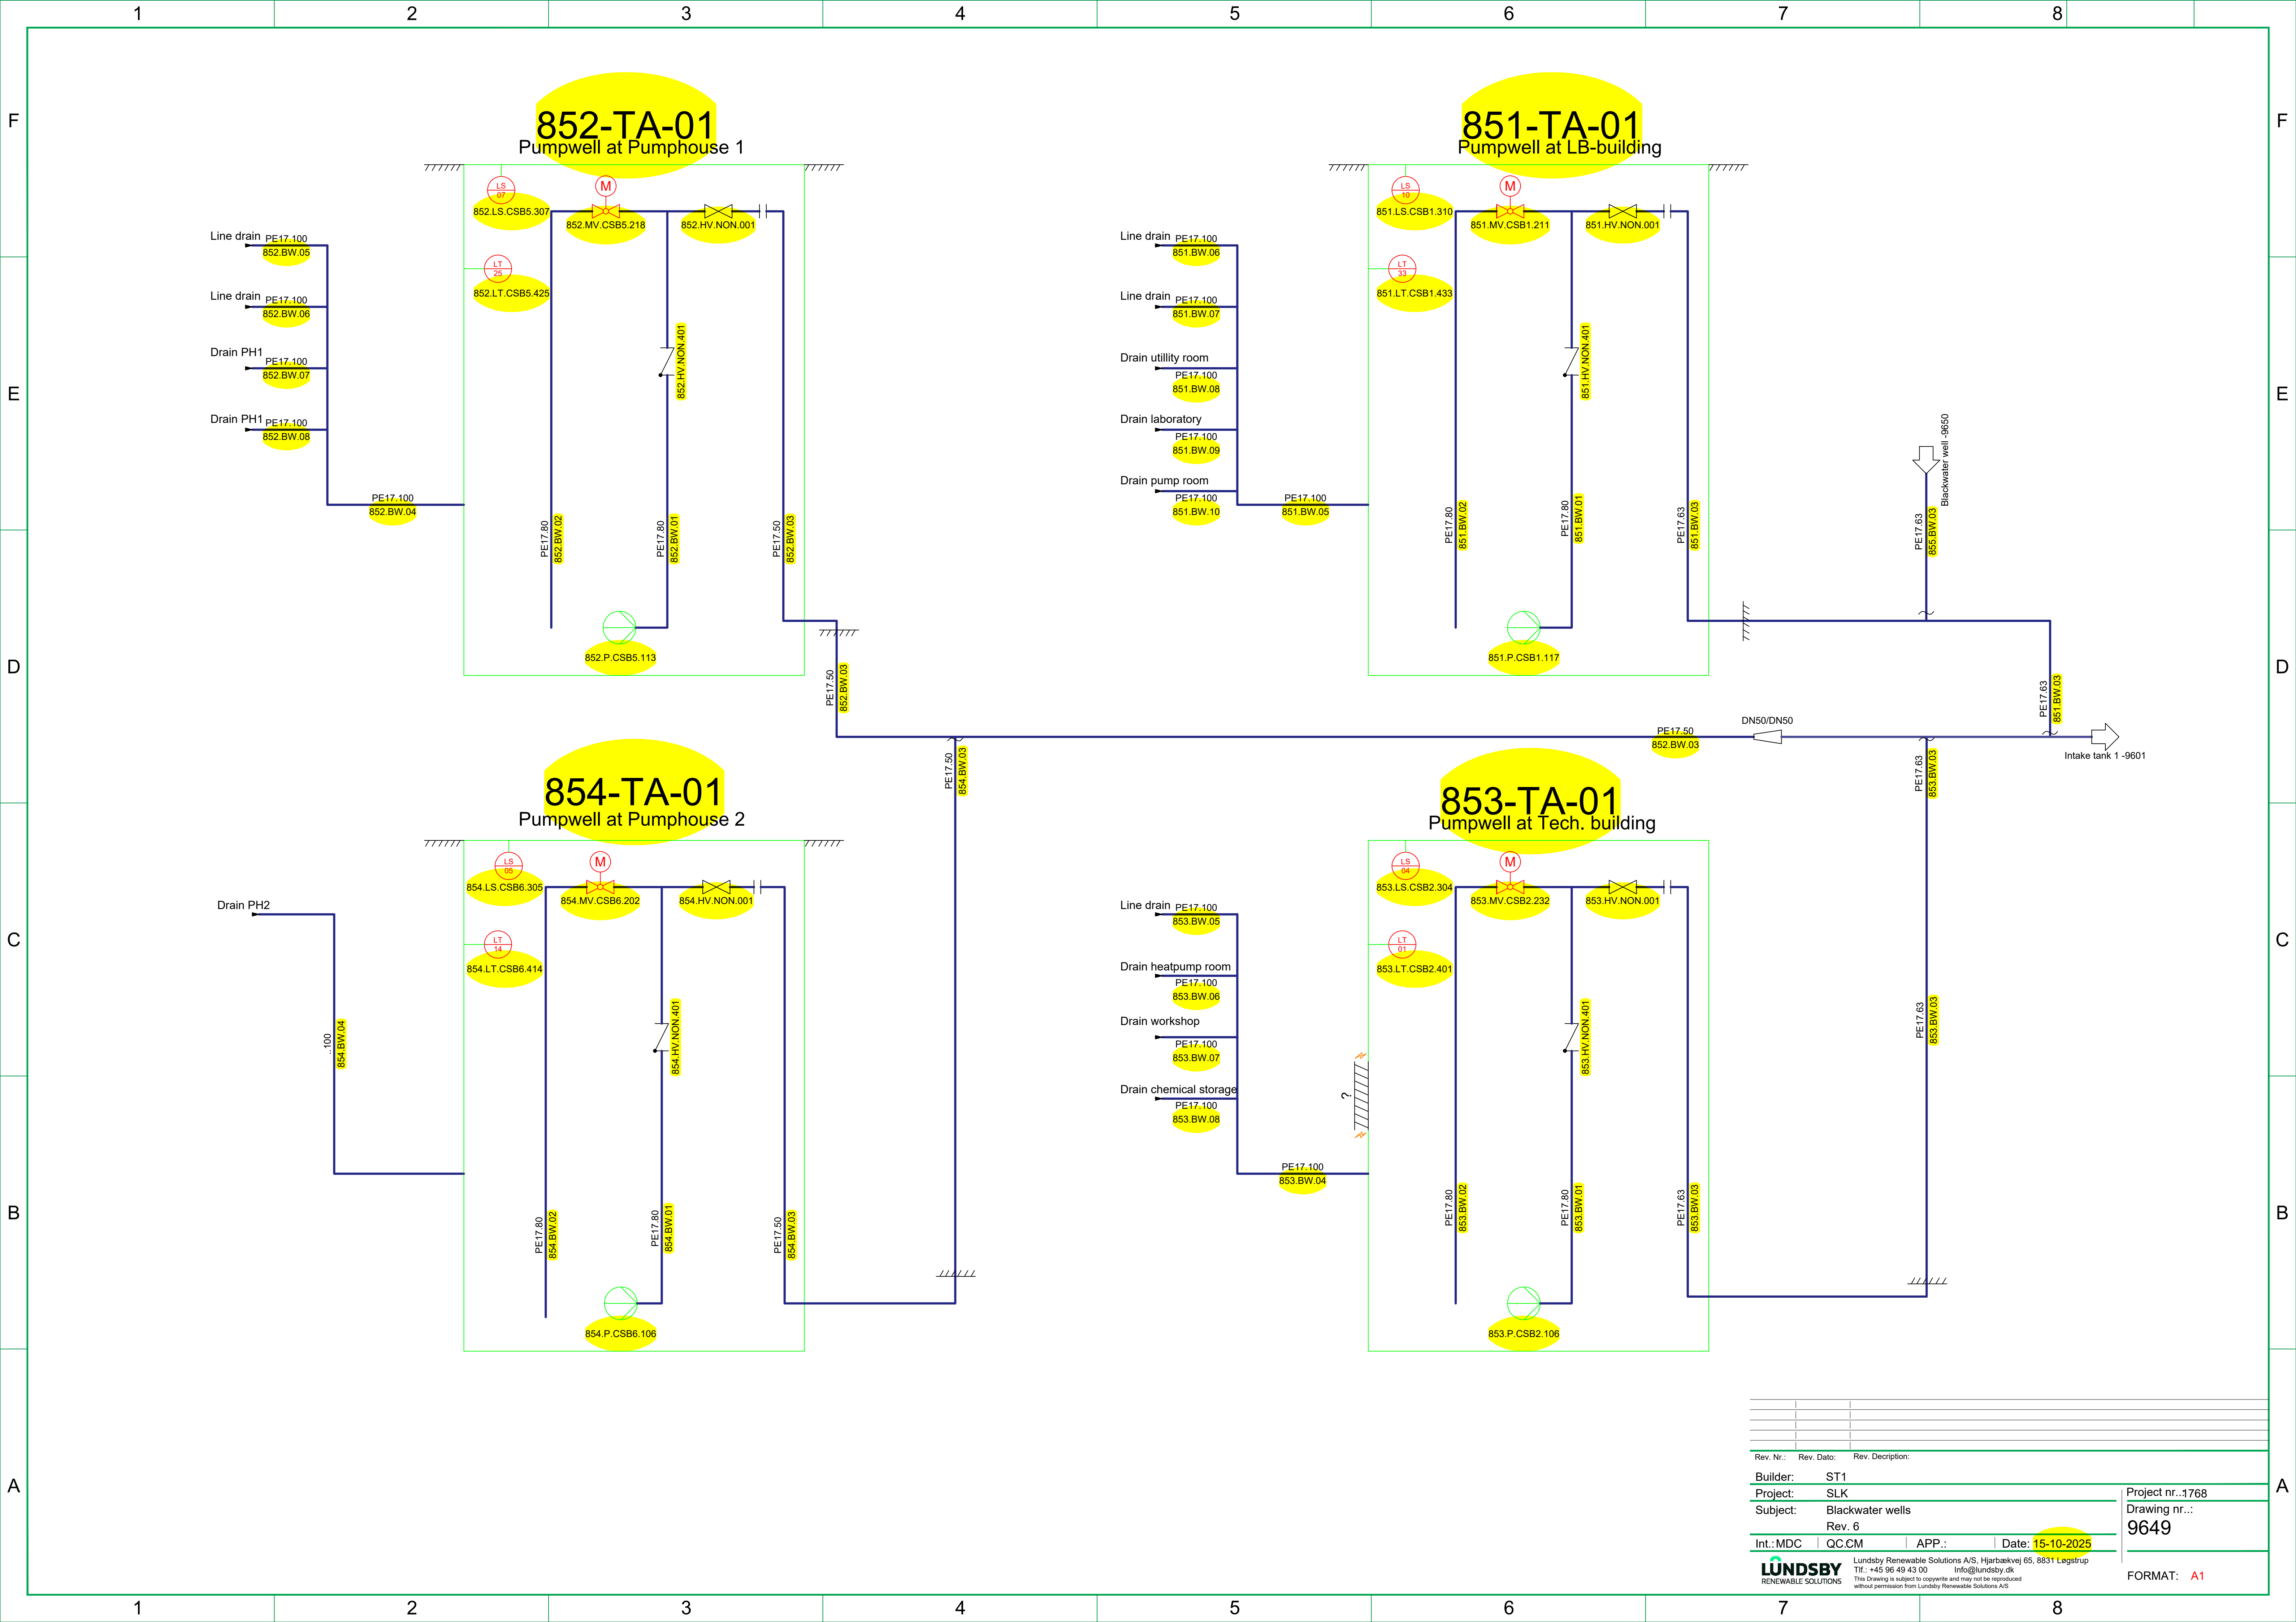


Rev. Nr.:	Rev. Dato:	Rev. Description:	Project nr.:1768
Builder:	ST1		Drawing nr.: 9649
Project:	SLK		
Subject:	Blackwater wells		
Rev. 6			
Int.:MDC	QC.CM	APP.:	Date: 15-10-2025
LUNDSBY RENEWABLE SOLUTIONS			FORMAT: A1

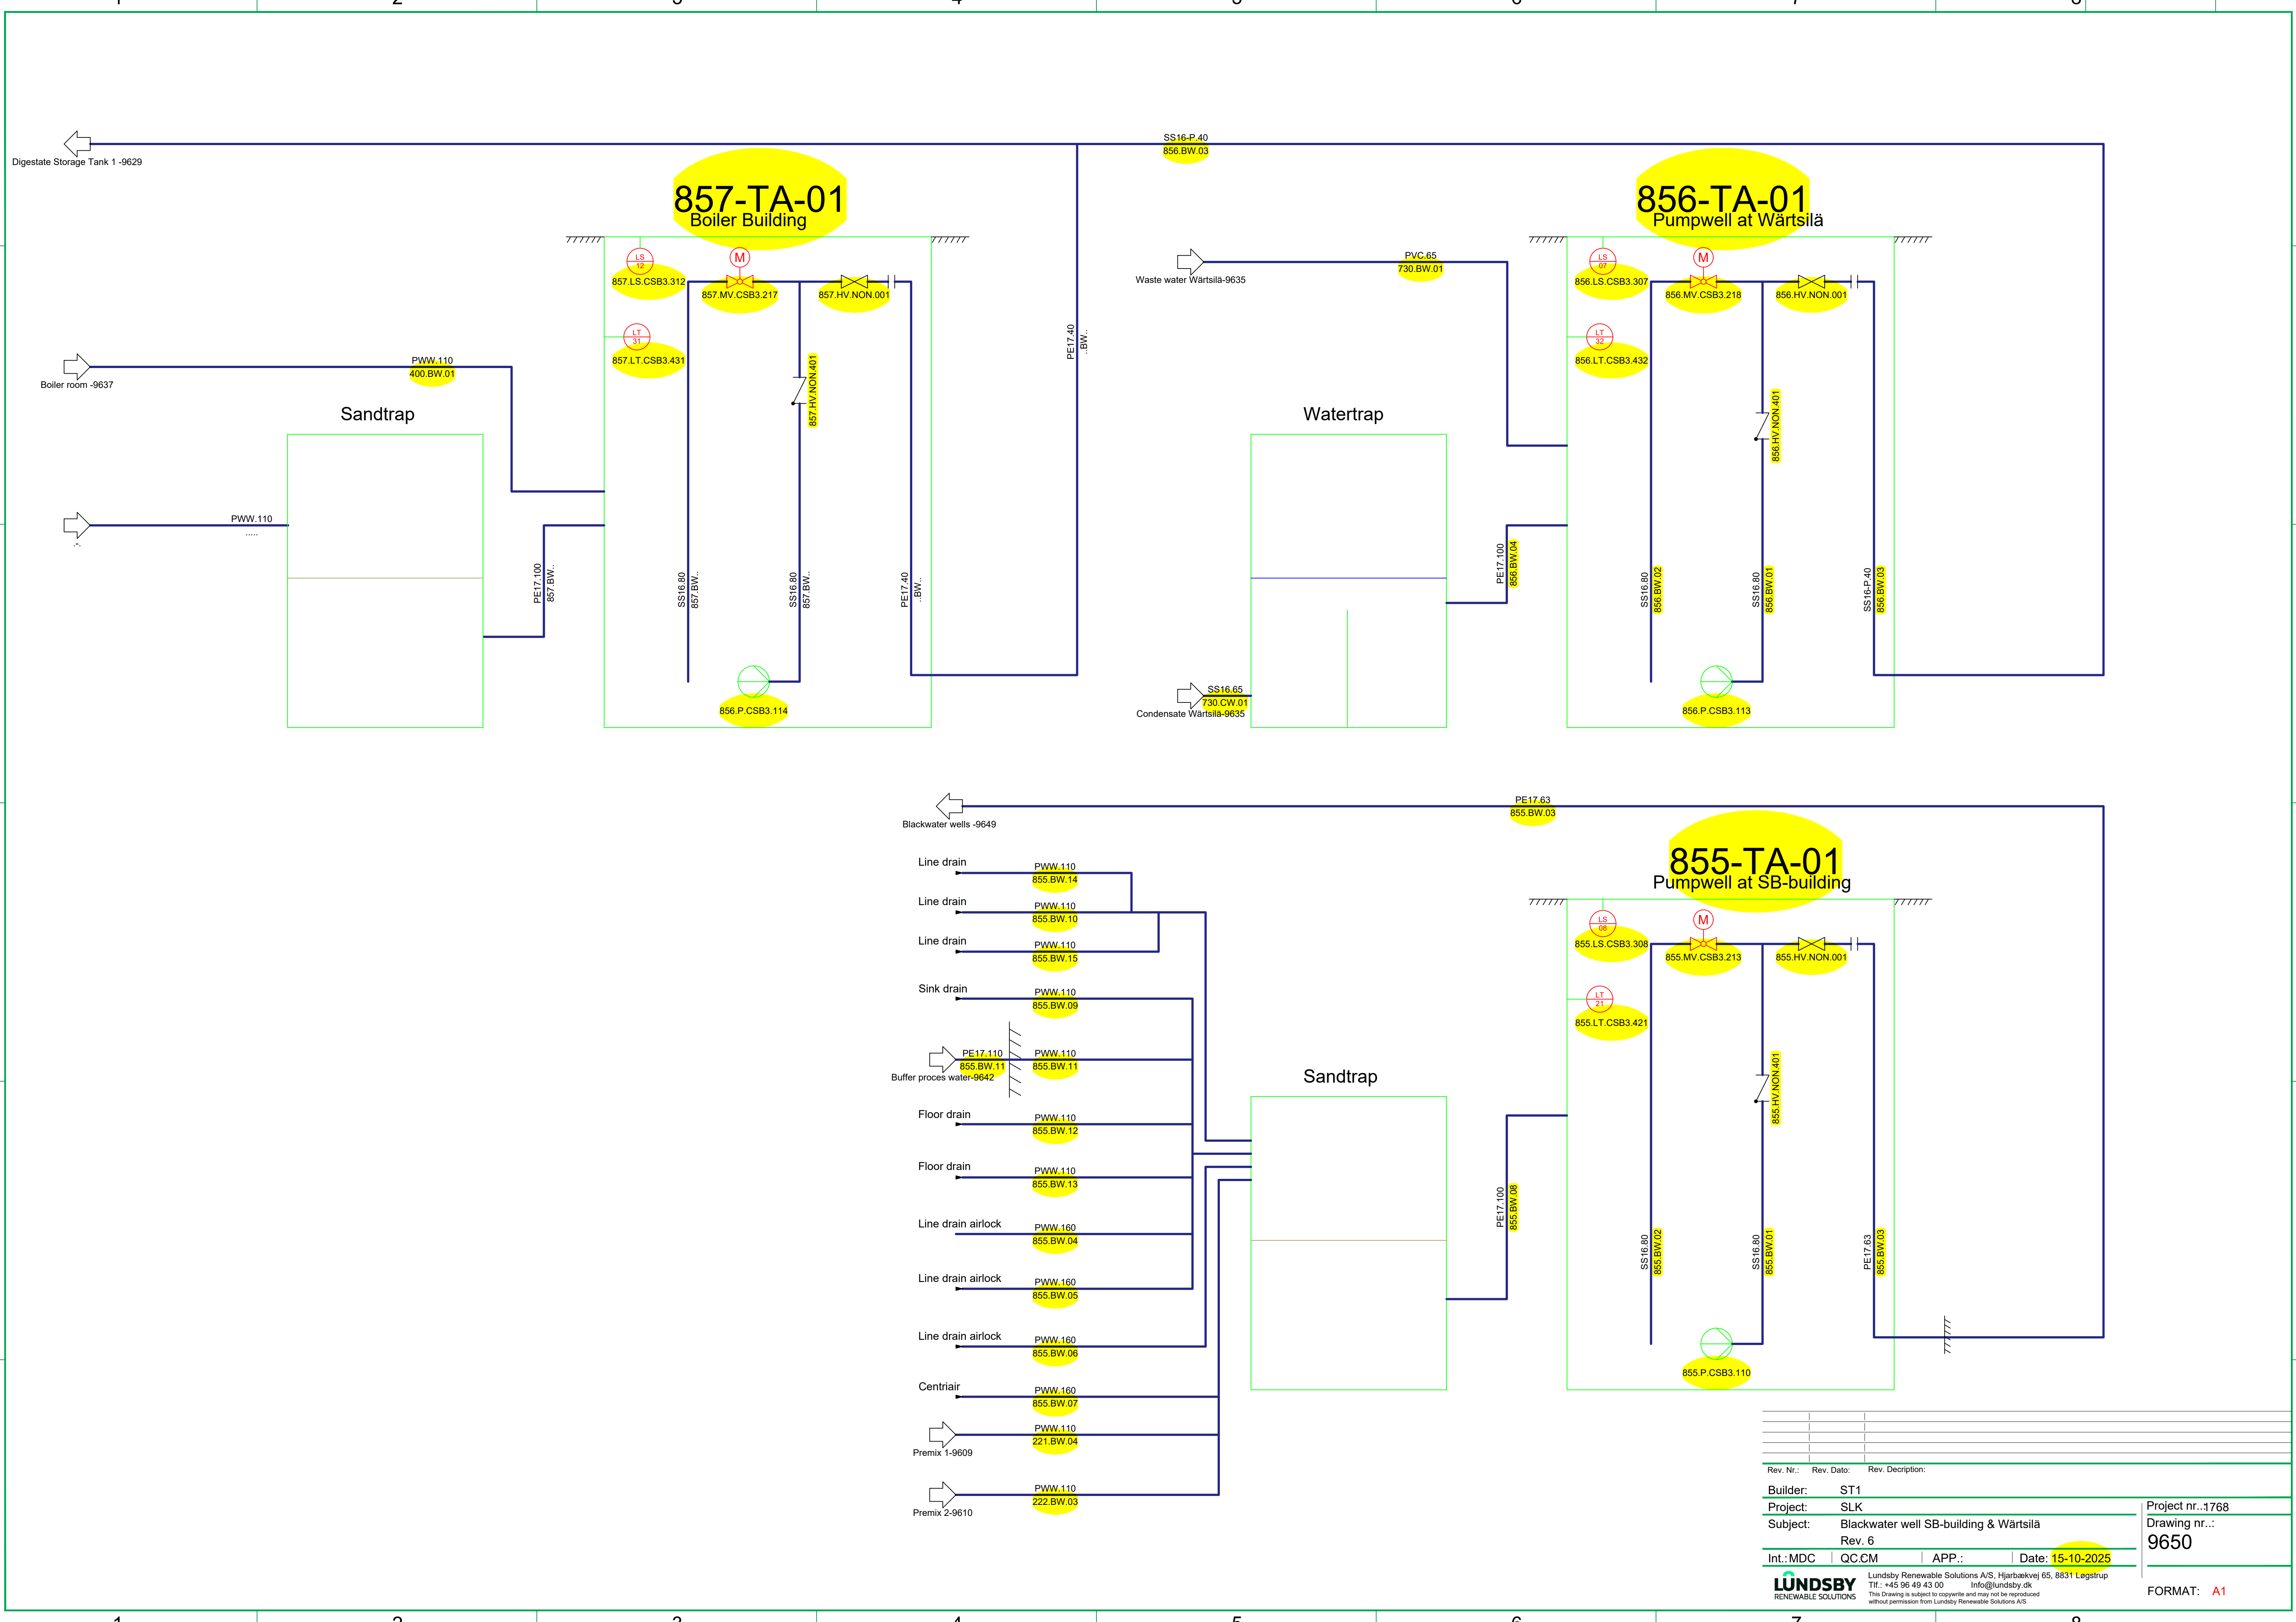



Rev. Nr.:	Rev. Date:	Rev. Description:
Builder:	ST1	
Project:	SLK	
Subject:	Blackwater well SB-building & Wärtsilä	
Rev. 6		
Int.:MDC	QC.CM	APP.:
Date:	15-10-2025	
LUNDSBY RENEWABLE SOLUTIONS		
Lundsby Renewable Solutions A/S, Hjarbækvej 65, 8831 Løgstrup Tlf.: +45 96 49 43 00 Info@lundsby.dk This Drawing is subject to copyright and may not be reproduced without permission from Lundsby Renewable Solutions A/S		
Project nr.:1768		Drawing nr.: 9650
FORMAT: A1		

Pumphouse 1
JA Trykluft scope

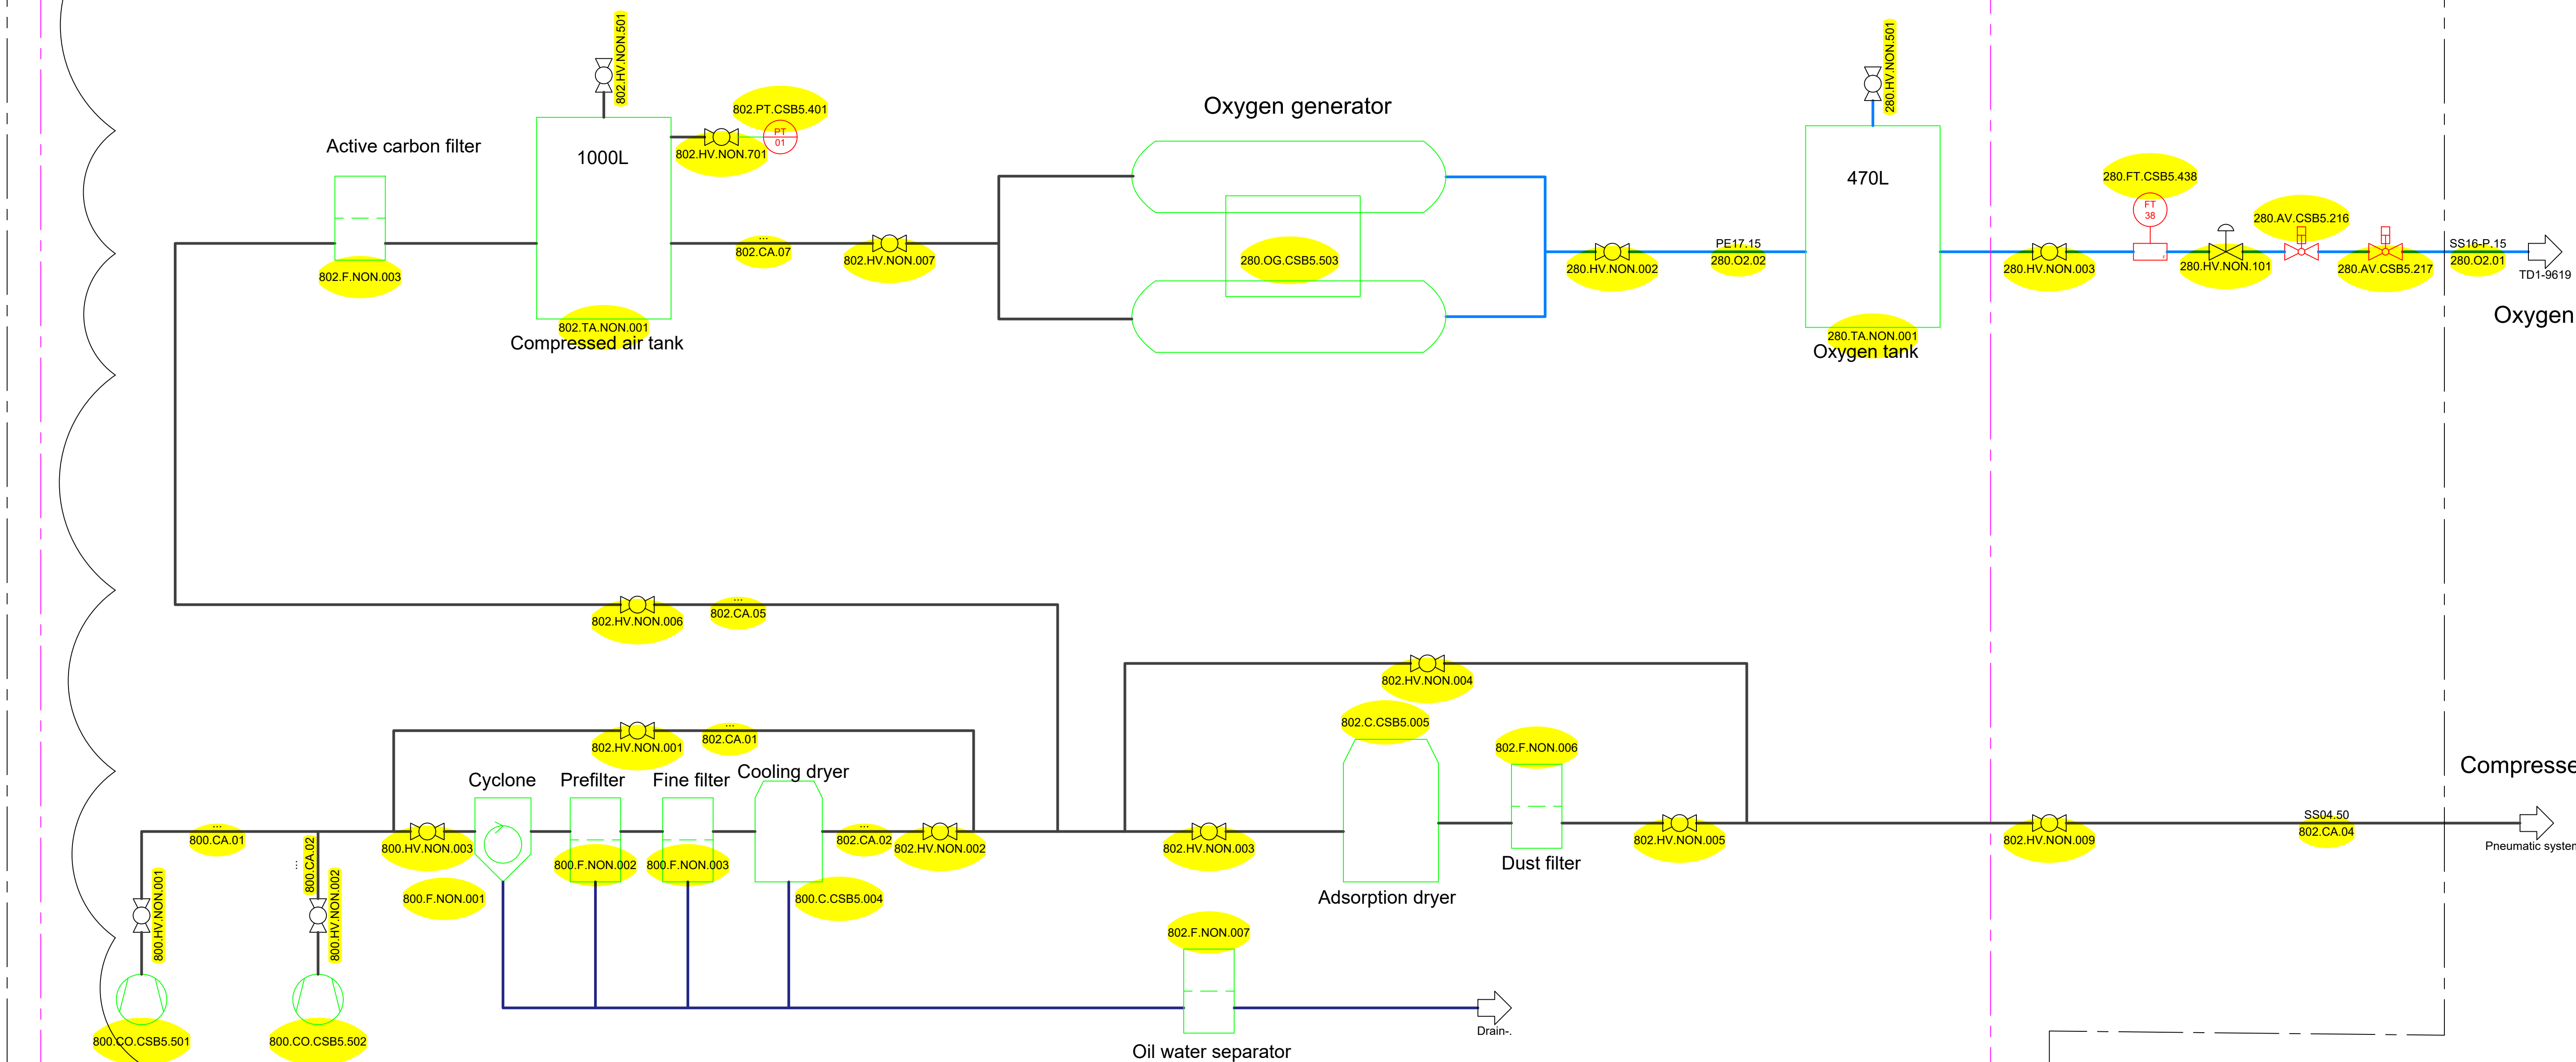


Rev. Nr.:	Rev. Dato:	Rev. Description:	
Builder:	ST1		
Project:	SLK		
Subject:	Compressed air & Oxygen		
Rev. 6			
Int.:MDC	QC:CM	APP.:	Date: 15-10-2025
LUNDSBY RENEWABLE SOLUTIONS			Lundsby Renewable Solutions A/S, Hjarbrækvej 65, 8831 Løgstrup Tlf.: +45 96 49 43 00 Info@lundsby.dk This drawing is subject to copyright and may not be reproduced without permission from Lundsby Renewable Solutions A/S
Project nr.:1768 Drawing nr.: 9652			FORMAT: A1

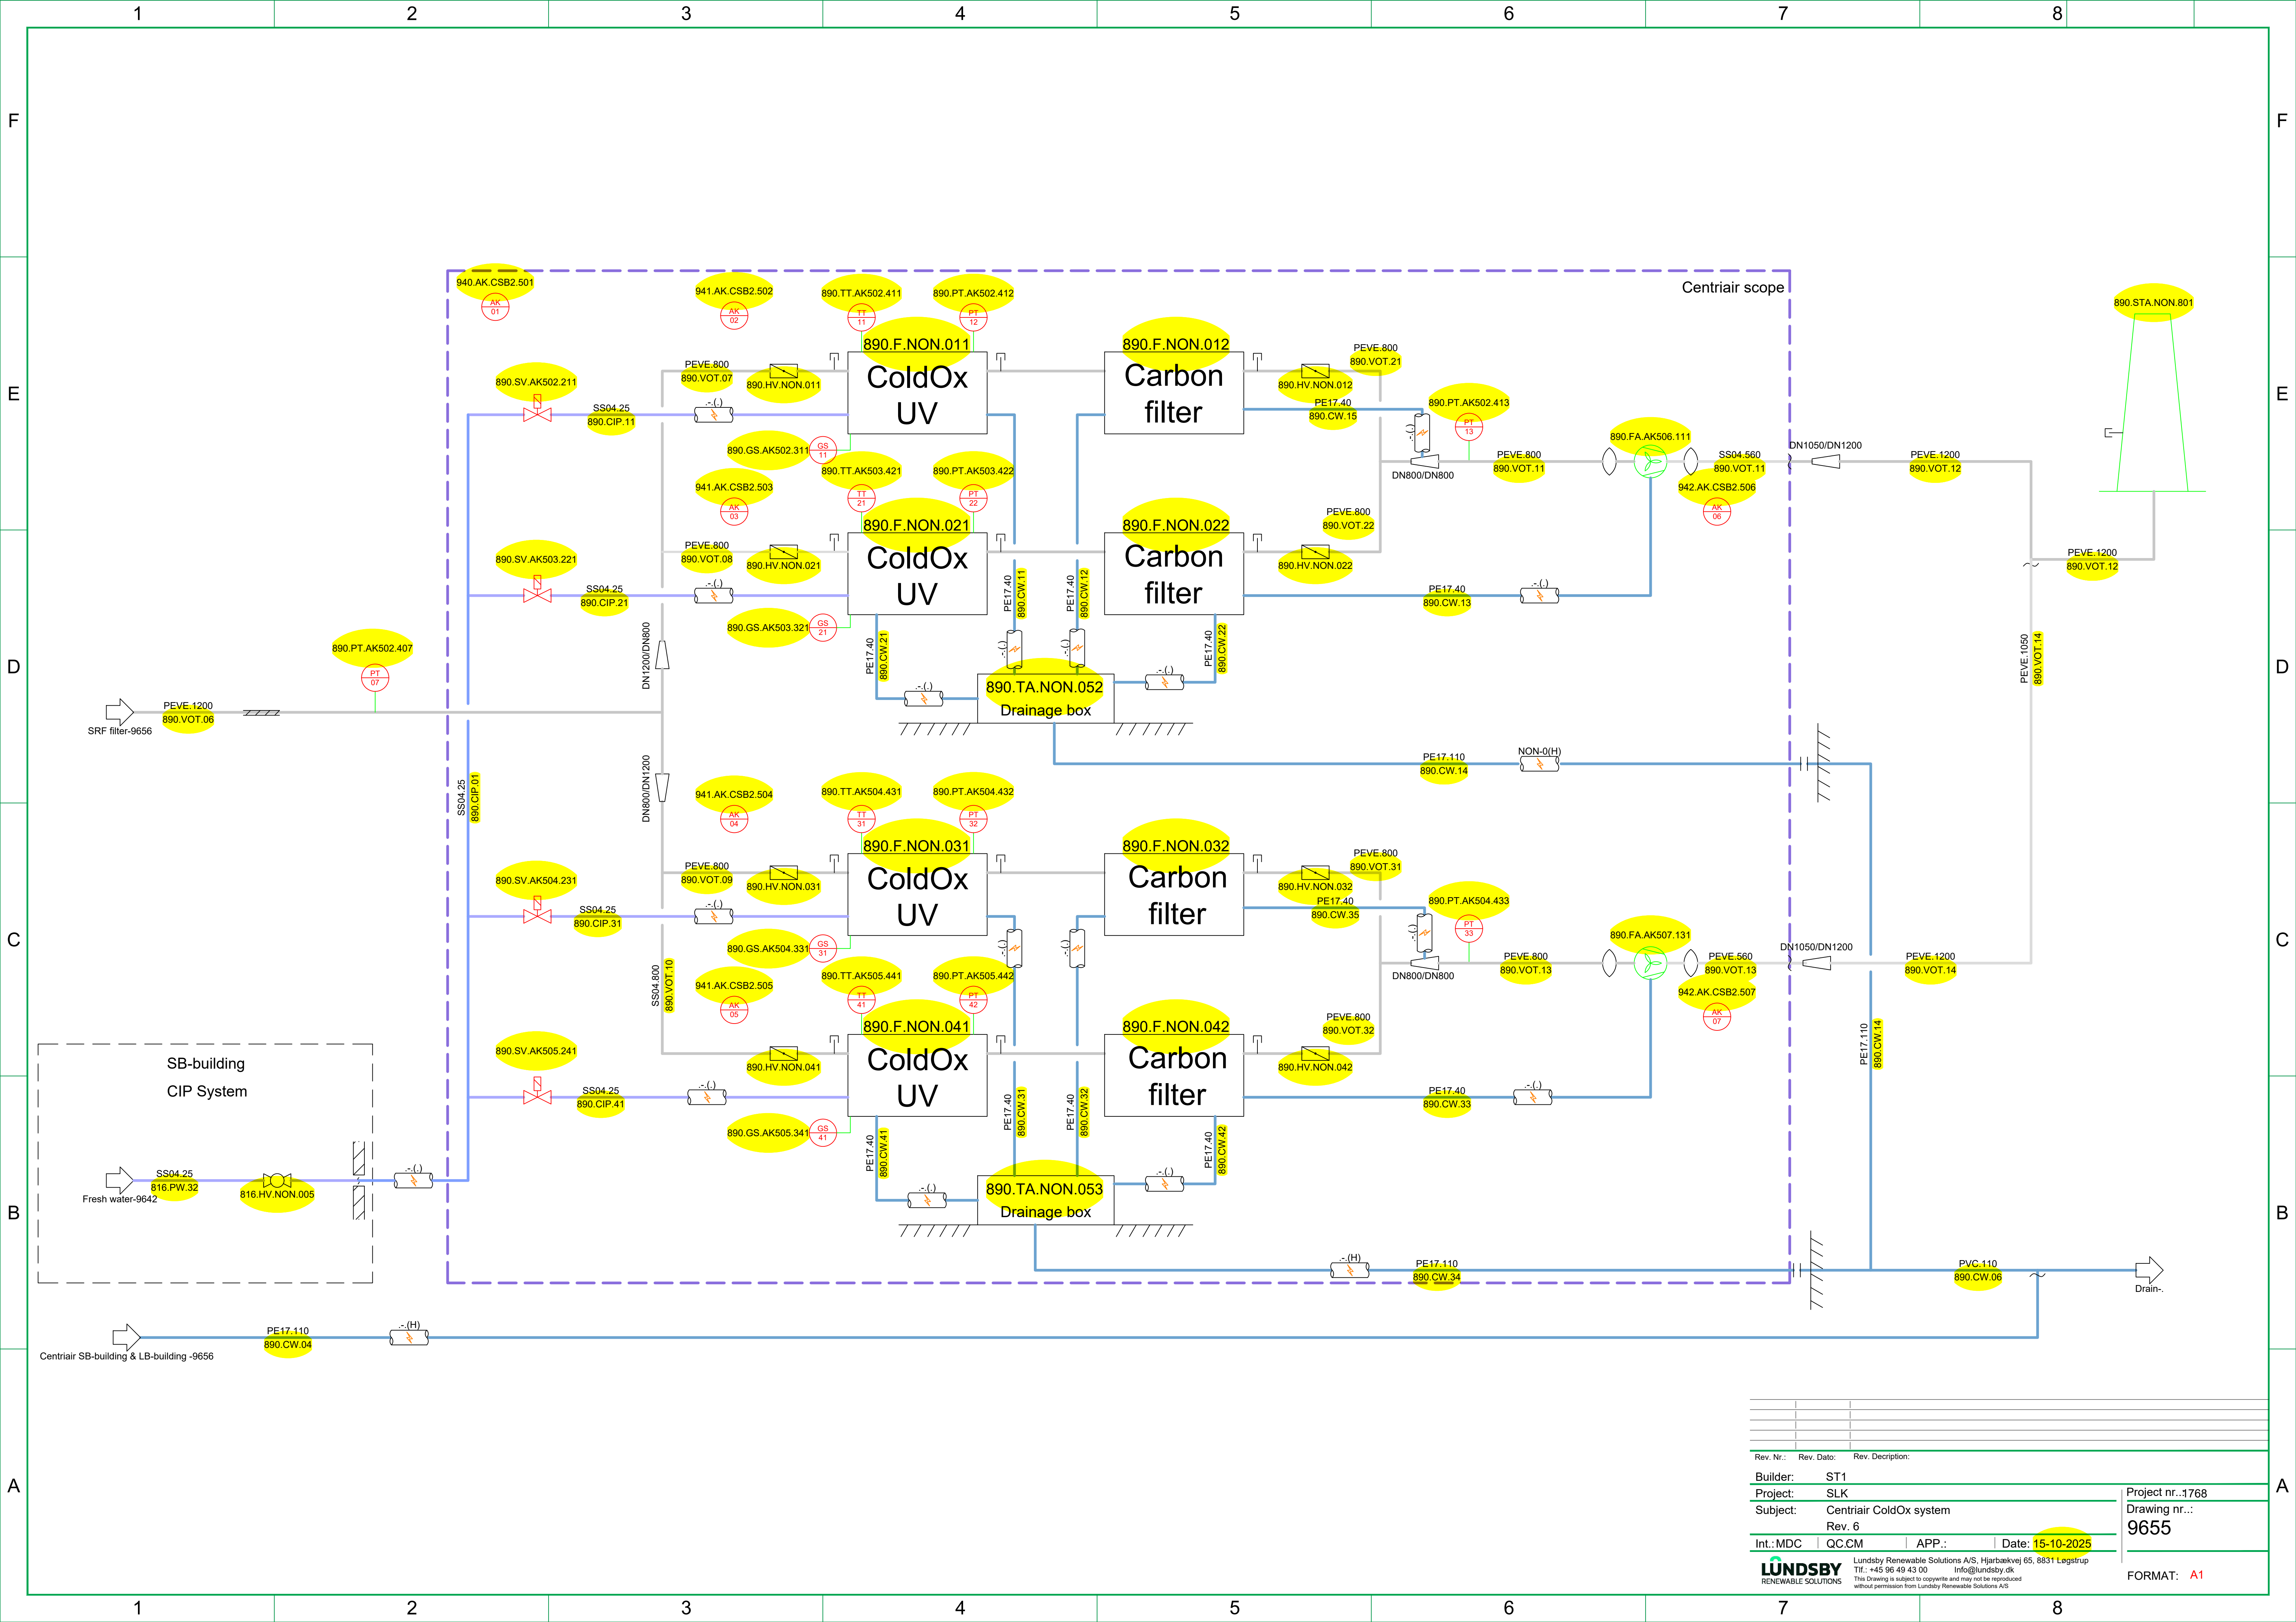

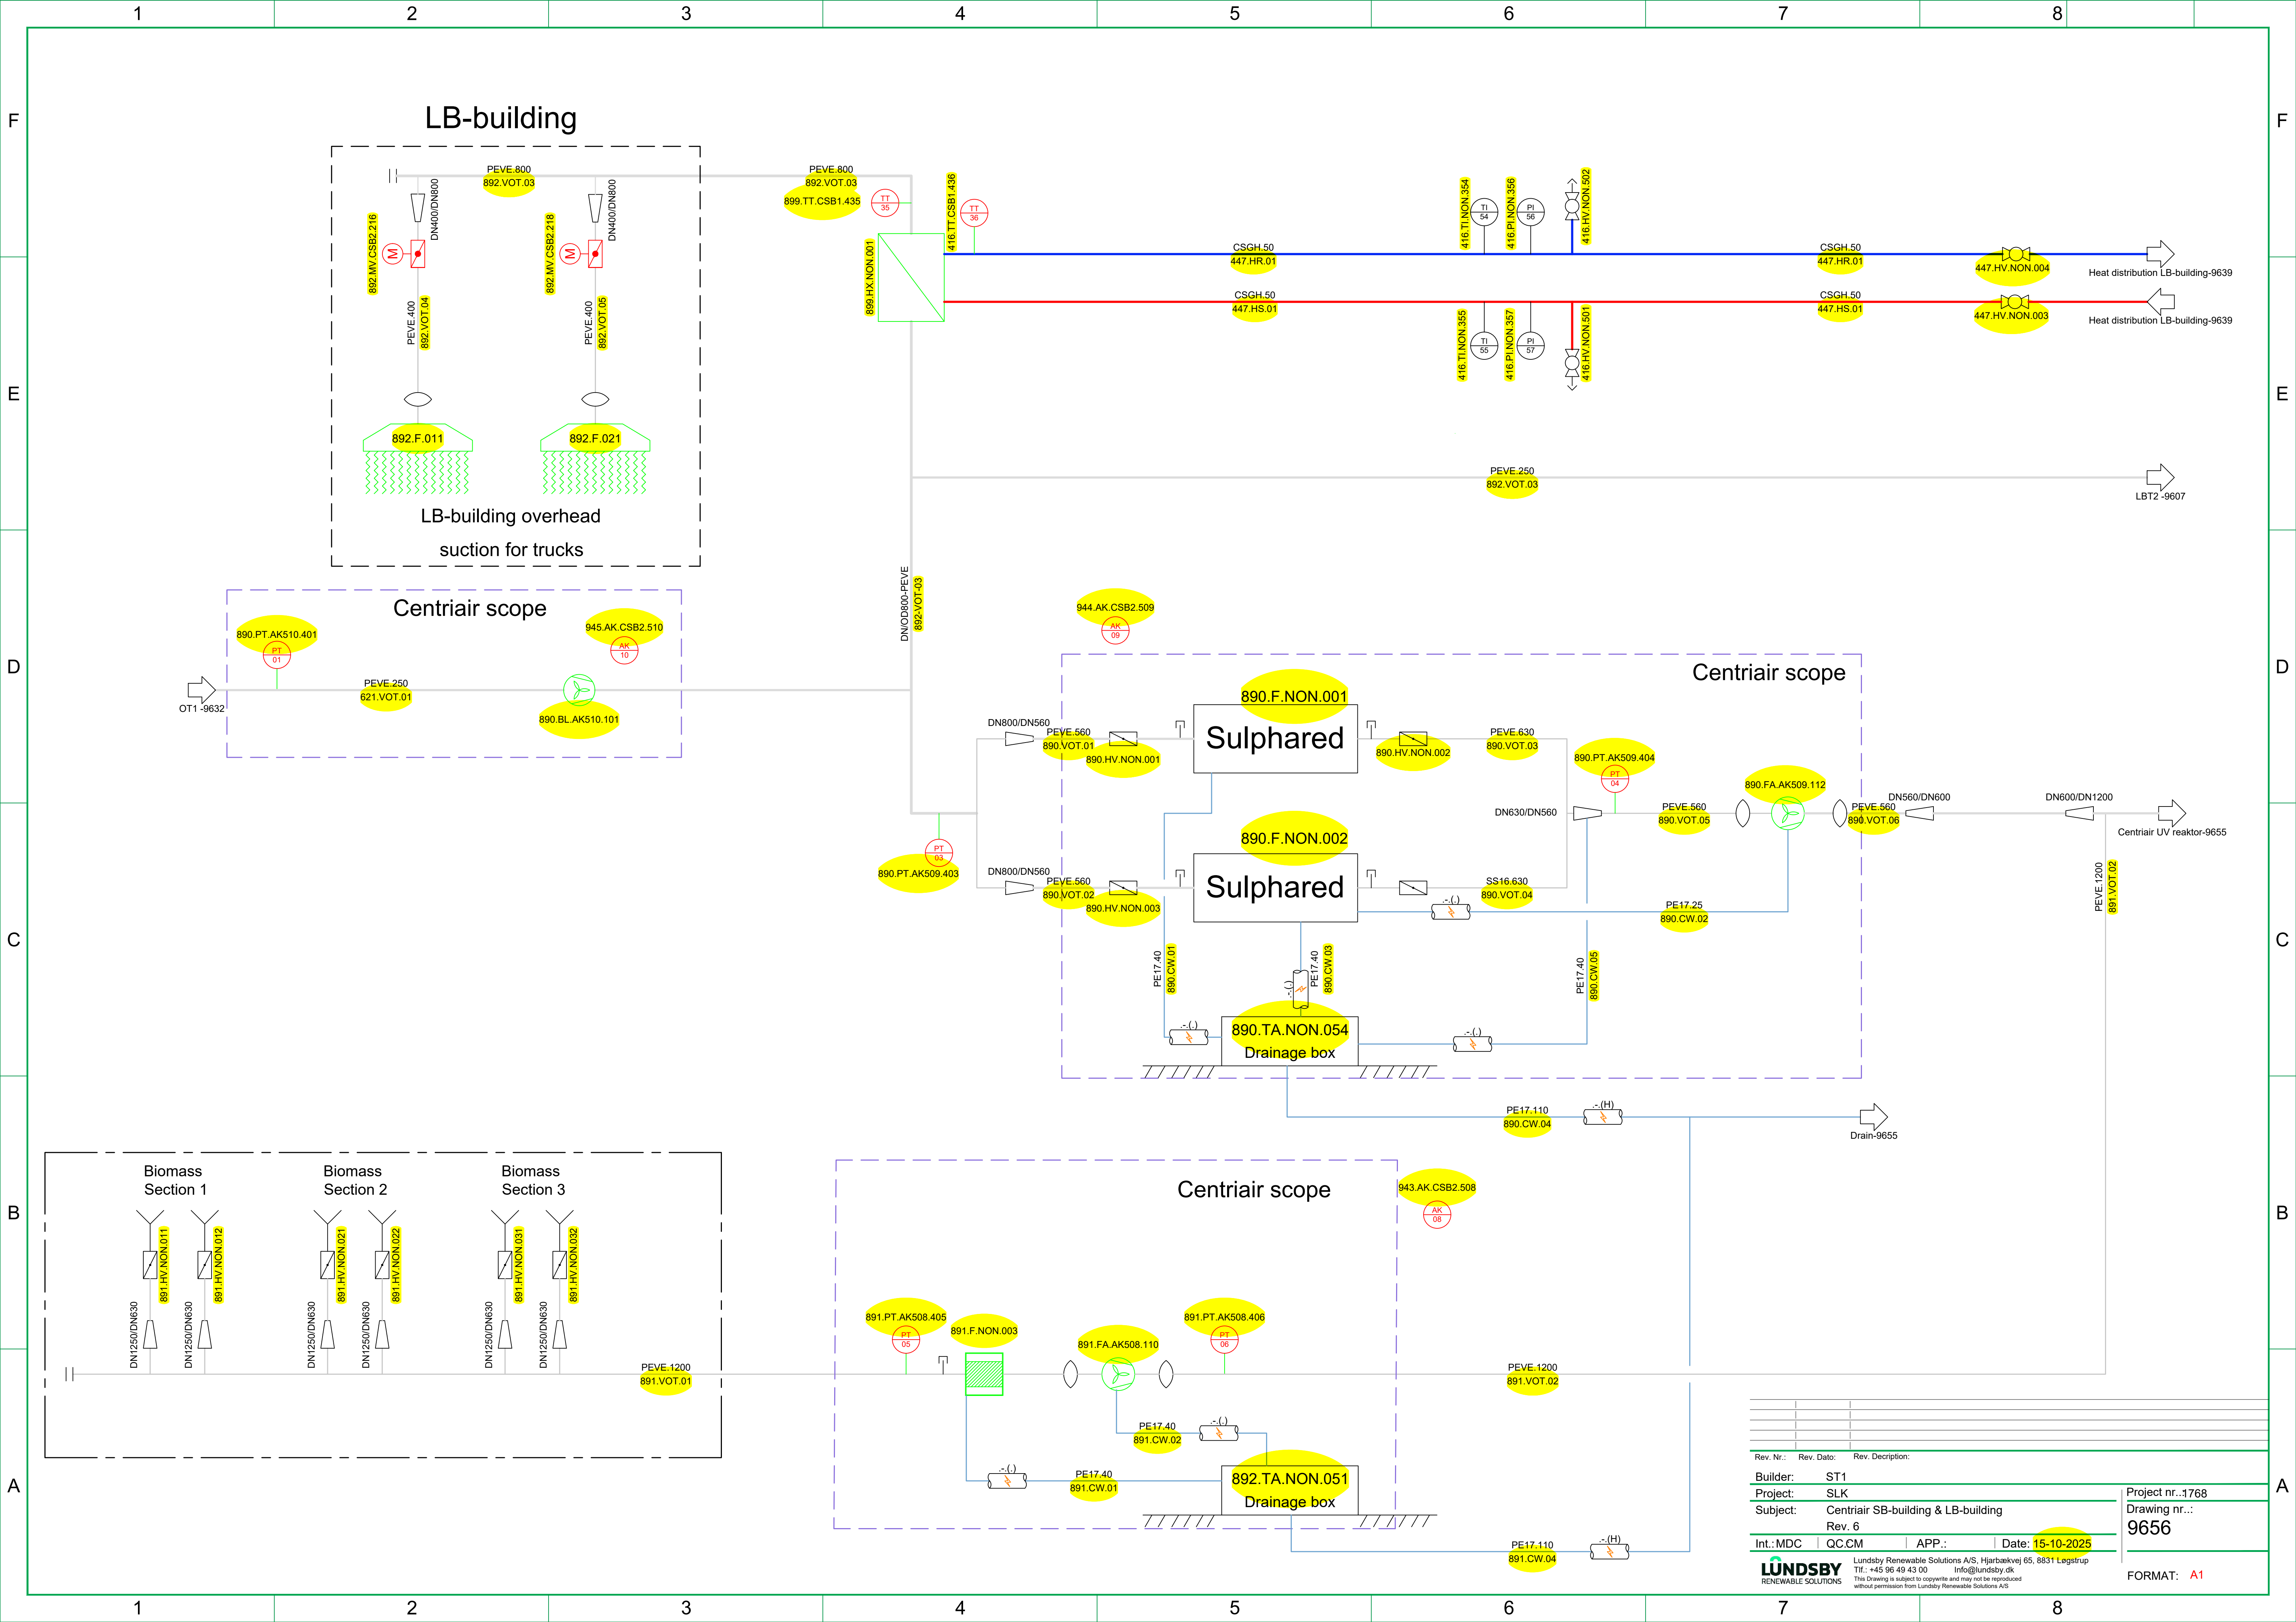

Rev. Nr.:	Rev. Dato:	Rev. Description:
Builder:	ST1	
Project:	SLK	
Subject:	Centriair SB-building & LB-building	
Rev. 6		
Int.:MDC	QC.CM	APP.:
Date:	15-10-2025	
LUNDSBY RENEWABLE SOLUTIONS		
Lundsby Renewable Solutions A/S, Hjarbækvej 65, 8831 Løgstrup Tlf.: +45 96 49 43 00 Info@lundsby.dk This drawing is subject to copyright and may not be reproduced without permission from Lundsby Renewable Solutions A/S		
Project nr...1768	Drawing nr...: 9656	FORMAT: A1

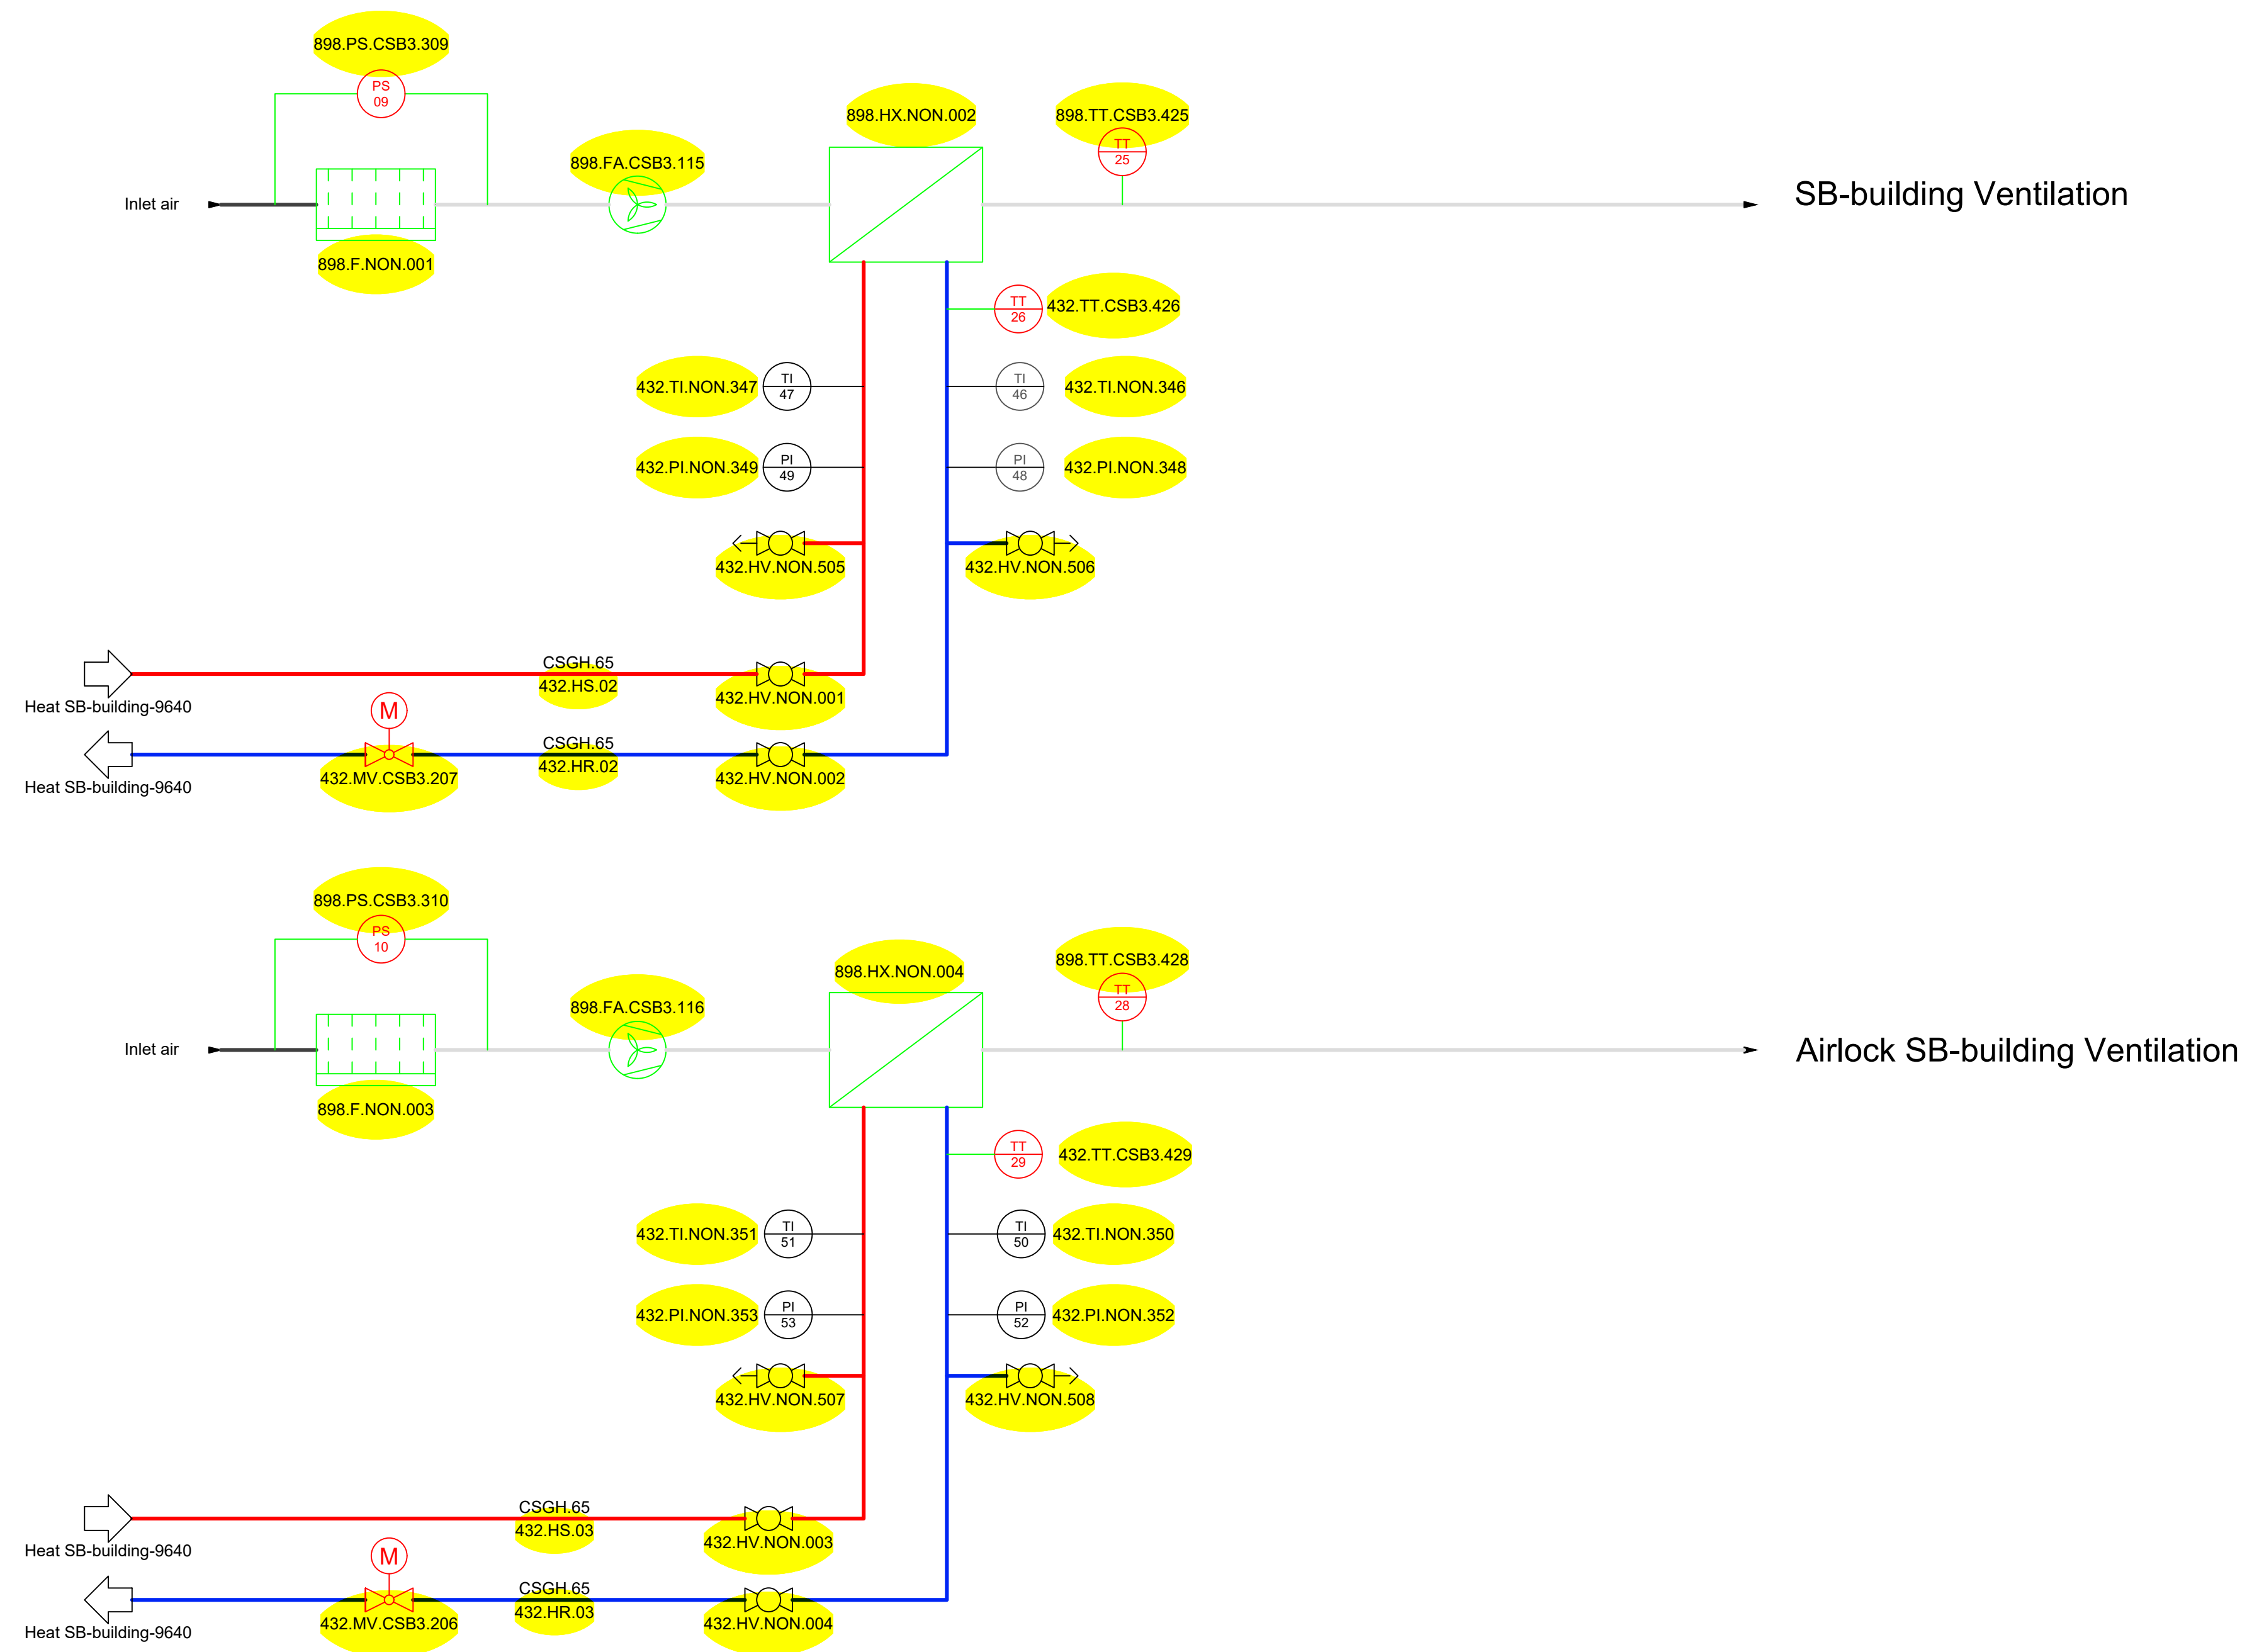

Rev. Nr.:	Rev. Dato:	Rev. Description:	Project nr.:
Builder:	ST1		1768
Project:	SLK		Drawing nr.:
Subject:	Ventilation SB-building		9657
Rev. 6			
Int.:MDC	QC.:CM	APP.:	Date: 15-10-2025
LUNDSBY RENEWABLE SOLUTIONS			Format: A1