






Structure of the tagging system

Structure of the component tagging

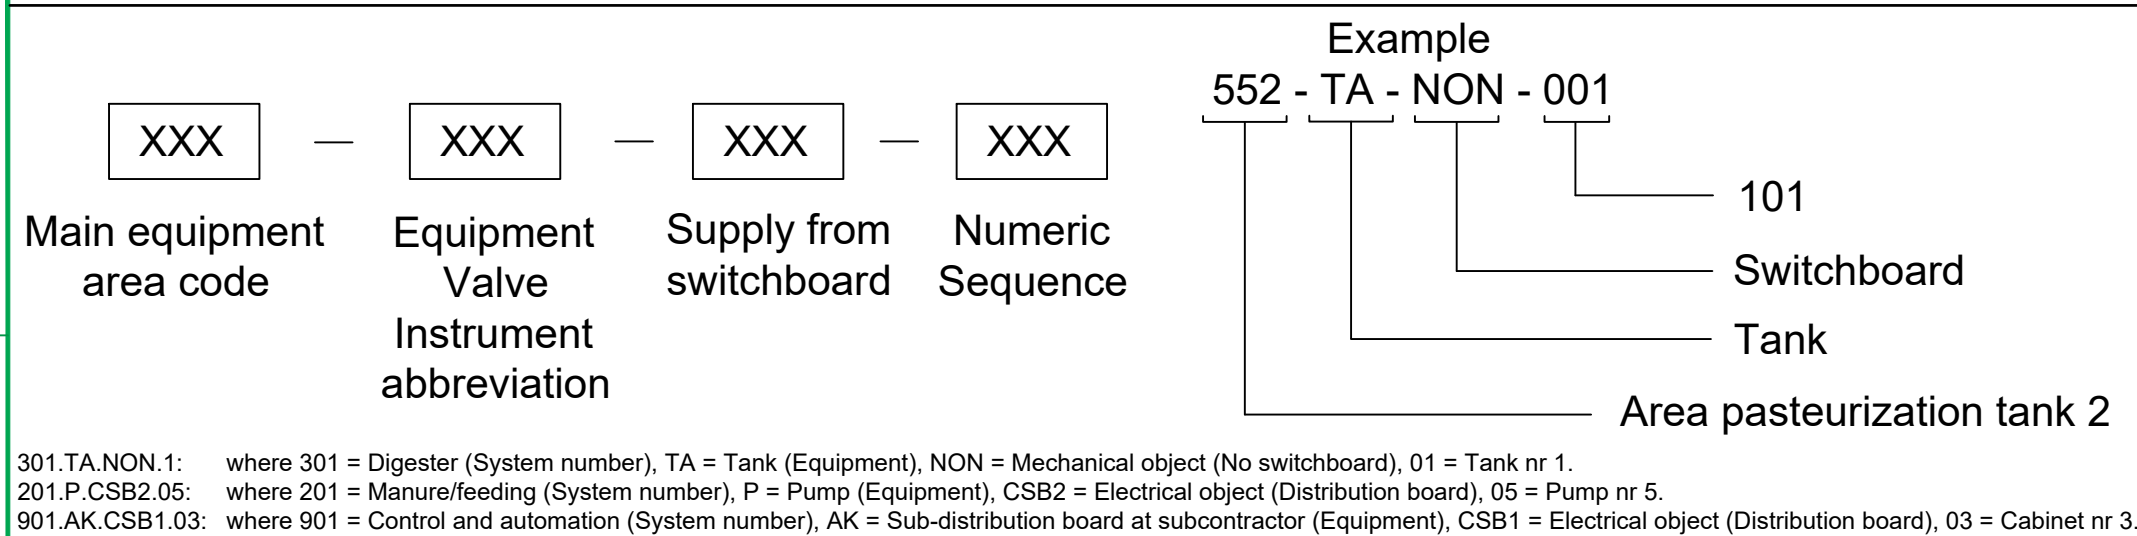

301.TA.NON.1: where 301 = Digester (System number), TA = Tank (Equipment), NON = Mechanical object (No switchboard), 01 = Tank nr 1.
201.P.CSB2.05: where 201 = Manure/feeding (System number), P = Pump (Equipment), CSB2 = Electrical object (Distribution board), 05 = Pump nr 5.
901.AK.CSB1.03: where 901 = Control and automation (System number), AK = Sub-distribution board at subcontractor (Equipment), CSB1 = Electrical object (Distribution board), 03 = Cabinet nr 3.

Lines

 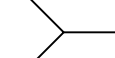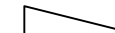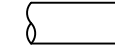Description	Symbol
Subcontractor scope	
Boundary line	
Page connector	
Start pipe - Not linked to page	
End pipe - Not linked to page	
Fald/ Slope	
Insulation	
Electrical Heat tracing	

Building/Area/Tank


Description	Code
Primary digester	PD
Secondary digester	SD
Digester storage	DST
Liquid manure tank	LMT
Liquid biomass tank	LBT
Outlet tank	OT
Blackwater tank	BWT
Tech building	TB
Admin building	ADB
Solid biomass building	SBB
Liquid biomass building	LBB
Plansilo	PS
Pump house	PH
Hygienization tanks	HYG
Flare	FLA
Stack	STA
Odour treatment facility	OD
Upgrade facility	UPG
Liquifaction facility	LIQ
Oil boiler	OB
Wood boiler	WB
Transformer	TR

Media code

Media	Pipe color	RBG color	Code
Heat Return		0,37,245	HR
Heat Supply		255,0,0	HS
Heat Hot Return		255,223,127	HHR
Heat Hot Supply		238,129,129	HHS
Cooling Supply		0,255,183	CS
Cooling Return		126,189,189	CR
Black Water		36,39,132	BW
CIP		253,53,223	CIP
Process Water		170,170,255	PW
Technical Water		69,78,104	TW
Drinking Water		0,0,129	DW
Drinking Water Hot		0,127,255	DWH
Condensate		108,163,208	CW
Steam		255,82,82	ST
Steam Condensate		189,0,0	STC
Liquid Manure (Slurry)		240,130,40	LM
Liquid Biomass (Substrat)		128,0,255	LB
Process Biomass		165,103,82	PB
Hygienized Biomass		169,130,0	HB
Recirculated Biomass		165,103,82	RCB
Ferric Chloride FeCl		145,255,71	FeCl
Ventilation Odour Treatment		199,199,199	VOT
Ventilation Fresh Air		199,199,199	VFA
Compressed Air		64,64,64	CA
Oxygen		0,128,255	O2
Raw Biogas		255,255,0	RB
Return/reject Gas		116,118,4	RG
Nature Gas		0,255,127	NG
Instrument Leader		Green	N/A

Structure of the pipeline tagging system

The pipetag consists of various information about the pipe
Full pipeline tag as shown below

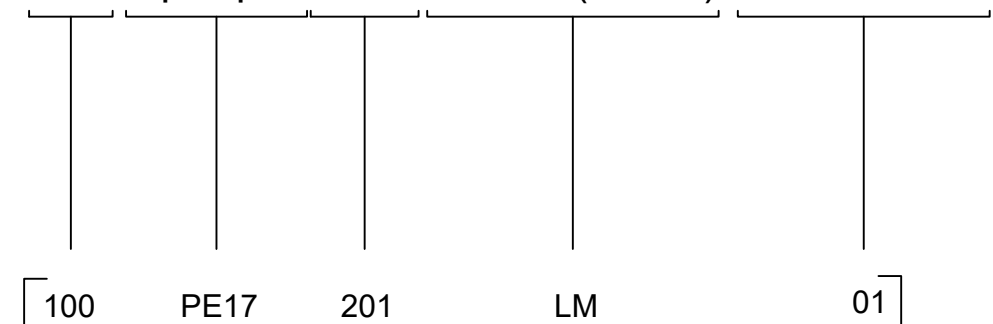

Example

Two (2) digits. Starts with 01
[01]

- Two (2) to four (4) characters (letters)
- [LM - Liquid manure]

Three (3) digits
[201 - Manure feeding in tank 1]

Pipe Spec name
[PE17 - PE100 SDR17]

Pipe size
DN indication for Metric pipes
OD indication for PE-pipe
[This example is OD 100 mm]

The pipe tag will be shown on the P&ID as follows:

	PipeSpec-Size
	Area-Service-Serialnumber

Example of line tag notation on P&ID: PE17-110
201-LM-01

Line color corresponding to table above.
The part below the pipeline is the Unique Line Tag.
Unique Line Tag is generated automatically when creating complete Line Tag.
Unique Line Tag is used by the P3D system when designing pipes in the 3D model and when generating Isometrics.

Rev. Nr.:	Rev. Dato:	Rev. Description:
Builder:	ST1	
Project:	SLK	
Subject:	PID Legend	
	Rev. 6	
Int.: MDC	QC.: CM	APP.: Date: 15-10-2025


Lundsby Renewable Solutions A/S, Hjarbakvej 65, 8831 Løgstrup
Tlf.: +45 96 49 43 00 Info@lundsby.dk

This Drawing is subject to copyright and may not be reproduced without permission of Lundsby Renewable Solutions A/S.


Project nr.: 1768
 Drawing nr.:
PID Legend

FORMAT: A1


1	2	3	4	5	6	7	8																																						
Valves		Equipment			Piping		Instruments																																						
Hand valves			Pumps / Compressors / Blowers			Piping symbols		Description																																					
Symbols	Code	Description	Symbols	Code	Description	Symbols	Code	Description																																					
	HV	General valve		P	Pump (General)		N/A	Offpage connector	Instruments will be tagged XXX - XX - XXX - XXX Main area code Letter code Switchboard Numeric sequence First letter XX Succeeding letter XX Numeric sequence Description Example Field instrument Temperature indication Instrument with connection to control Level switch Instruments with succeeding letter T is an analog signal. Instruments with succeeding letter S is a digital signal. <table><tr><th>Instruments</th><th>Abbreviation</th></tr><tr><td>Analyze Indicator</td><td>AI</td></tr><tr><td>Analyse Transmitter</td><td>AT</td></tr><tr><td>Energi Transmitter</td><td>ET</td></tr><tr><td>Flow Indicator</td><td>FI</td></tr><tr><td>Flow Transmitter</td><td>FT</td></tr><tr><td>Flow Switch</td><td>FS</td></tr><tr><td>Flow Transmitter</td><td>FT</td></tr><tr><td>General Switch</td><td>GS</td></tr><tr><td>Level Switch</td><td>LS</td></tr><tr><td>Level Indicator</td><td>LI</td></tr><tr><td>Level Transmitter</td><td>LT</td></tr><tr><td>Pressure Indicator</td><td>PI</td></tr><tr><td>Pressure Switch</td><td>PS</td></tr><tr><td>Pressure Transmitter</td><td>PT</td></tr><tr><td>Thermometer</td><td>TI</td></tr><tr><td>Temperature Transmitter</td><td>TT</td></tr><tr><td>Weight Transmitter</td><td>WT</td></tr></table>	Instruments	Abbreviation	Analyze Indicator	AI	Analyse Transmitter	AT	Energi Transmitter	ET	Flow Indicator	FI	Flow Transmitter	FT	Flow Switch	FS	Flow Transmitter	FT	General Switch	GS	Level Switch	LS	Level Indicator	LI	Level Transmitter	LT	Pressure Indicator	PI	Pressure Switch	PS	Pressure Transmitter	PT	Thermometer	TI	Temperature Transmitter	TT	Weight Transmitter	WT
Instruments	Abbreviation	
Analyze Indicator	AI	
Analyse Transmitter	AT	
Energi Transmitter	ET	
Flow Indicator	FI	
Flow Transmitter	FT	
Flow Switch	FS	
Flow Transmitter	FT	
General Switch	GS	
Level Switch	LS	
Level Indicator	LI	
Level Transmitter	LT	
Pressure Indicator	PI	
Pressure Switch	PS	
Pressure Transmitter	PT	
Thermometer	TI	
Temperature Transmitter	TT	
Weight Transmitter	WT	
	HV	Ball valve		P	Positive displacement pump		N/A	Flange connection																																					
	HV	Butterfly valve		P	Helical rotor pump		N/A	Blind flange																																					
	HV	Globe valve		P	Centrifugal pump		NO	Truck nozzle																																					
	HV	Three way valve		P	Peristaltic pump		NO	Funnel/Drain																																					
	HV	Ground covered valve		MC	Rotacut		AS	Expansion joint																																					
	BV	Balancing valve		MC	Shredder		SN	Strainer																																					
Actuated valves / Regulating valves			Heating and Cooling				N/A	Going into the ground / Coming up from																																					
	MV/RV	Motor ball valve		HX	Heat exchanger - Shell & tube		AJ	Concentric reducer																																					
	MV/RV	Motor butterfly valve		HX	Heat exchanger - plate		AJ	Eccentric reducer																																					
	AV/RV	Pneumatic ball valve		HX	Heat exchanger - double pipe		AX	Sample point																																					
	AV/RV	Pneumatic valve		HX	Heating coil (in tank)		BS	Inline silencer																																					
	AV	Solenoid valve		HS	Heatpump		BU	Electrical heat tracing																																					
Safety valves			Tank equipment				N/A	Going though wall																																					
	SV	Exhaust valve covers		AG	ISO Agitator - Propeller	<table><tr><th>Category</th><th>Numbers</th></tr><tr><td>Manual valves</td><td>001-099</td></tr><tr><td>Manual regulation valves</td><td>101-199</td></tr><tr><td>Pneumatic, electrical, solenoid</td><td>201-299</td></tr><tr><td>-</td><td>301-399</td></tr><tr><td>Check, Non-return valves</td><td>401-499</td></tr><tr><td>Drain, venting valves</td><td>501-599</td></tr><tr><td>Self-regulating valves (thermal/liquid)</td><td>601-699</td></tr><tr><td>Instrument valves</td><td>701-799</td></tr><tr><td>-</td><td>801-899</td></tr><tr><td>Safety valves</td><td>901-999</td></tr></table>	Category	Numbers	Manual valves	001-099	Manual regulation valves	101-199	Pneumatic, electrical, solenoid	201-299	-	301-399	Check, Non-return valves	401-499	Drain, venting valves	501-599	Self-regulating valves (thermal/liquid)	601-699	Instrument valves	701-799	-	801-899	Safety valves	901-999																	
Category	Numbers	
Manual valves	001-099	
Manual regulation valves	101-199	
Pneumatic, electrical, solenoid	201-299	
-	301-399	
Check, Non-return valves	401-499	
Drain, venting valves	501-599	
Self-regulating valves (thermal/liquid)	601-699	
Instrument valves	701-799	
-	801-899	
Safety valves	901-999	
	SV	Safety valve		AG	Agitator		DT	Digester tank																																					
	SV	Breather valve		LA	Light			ST	Storage tank																																				
Mechanical valves				CA	Camera			DT/ST	Storage tank with cover																																				
	PV	Pressure holding valve		FH	Foam hatch			HT	Gas/Hyginisation tank																																				
	CV	Check valve	Filters and Vessels					TA	Buried tank																																				
	VV	Venting valve		AT	General filter / Forfilter			EXP	Expansion tank																																				
Miscellaneous additional valve symbols				AT	General liquid	
				AT	Drier - General	
		Operator lock mechanism		F	Suction hood	
				EXP	Expansion tank	
Equipment			Equipment			Revision clouds																																							
Symbols	Code	Description	Symbols	Code	Description	Instruments will be tagged																																							
	MX	Bio mixer		MC	Premix	Instruments will be tagged XXX - XX - XXX - XXX Main area code Letter code Switchboard Numeric sequence																																							
	CV	Debris lift unit		CV	Screw conveyor	Description	Example																																						
	CV	Belt conveyor		CRA	Crane	Field instrument	Temperature indication																																						
	CH	ISO Stack - Chimney		FL	Flare	Instrument with connection to control	Level switch																																						
	PD	Pulsation damper		SP	Screw press	Instruments with succeeding letter T is an analog signal. Instruments with succeeding letter S is a digital signal.																																							
Safety valves		Tank equipment			Various instruments	
	SV	Exhaust valve covers		AG	ISO Agitator - Propeller		FT	Flow transmitter																																					
	SV	Safety valve		AG	Agitator		EM	Energy meter																																					
	SV	Breather valve		LA	Light		SI	Siren																																					
Mechanical valves		Filters and Vessels			<table> <tr> <td>Rev. Nr.:</td> <td>Rev. Dato:</td> <td>Rev. Beskrivelse:</td> <td></td> </tr> <tr> <td>Builder:</td> <td>ST1</td> <td></td> <td></td> </tr> <tr> <td>Project:</td> <td>SLK</td> <td></td> <td></td> </tr> <tr> <td>Subject:</td> <td>PID legend 2</td> <td></td> <td></td> </tr> <tr> <td>Int.:MDC</td> <td>QC: CM</td> <td>APP.:</td> <td>Date: 15-10-2025</td> </tr> </table>				Rev. Nr.:	Rev. Dato:	Rev. Beskrivelse:		Builder:	ST1			Project:	SLK			Subject:	PID legend 2			Int.:MDC	QC: CM	APP.:	Date: 15-10-2025																	
Rev. Nr.:	Rev. Dato:	Rev. Beskrivelse:	
Builder:	ST1	
Project:	SLK	
Subject:	PID legend 2	
Int.:MDC	QC: CM	APP.:	Date: 15-10-2025	
	PV	Pressure holding valve		AT	General filter / Forfilter	Project nr.: 1768 Drawing nr.: PID legend 2																																							
	CV	Check valve		AT	General liquid	FORMAT: A1																																							
	VV	Venting valve		AT	Drier - General	
Miscellaneous additional valve symbols			F	Suction hood	
		Operator lock mechanism		EXP	Expansion tank	
Equipment		Equipment			Various instruments	
Symbols	Code	Description	Symbols	Code	Description	Instruments will be tagged																																							
	MX	Bio mixer		MC	Premix	Instruments will be tagged XXX - XX - XXX - XXX Main area code Letter code Switchboard Numeric sequence																																							
	CV	Debris lift unit	


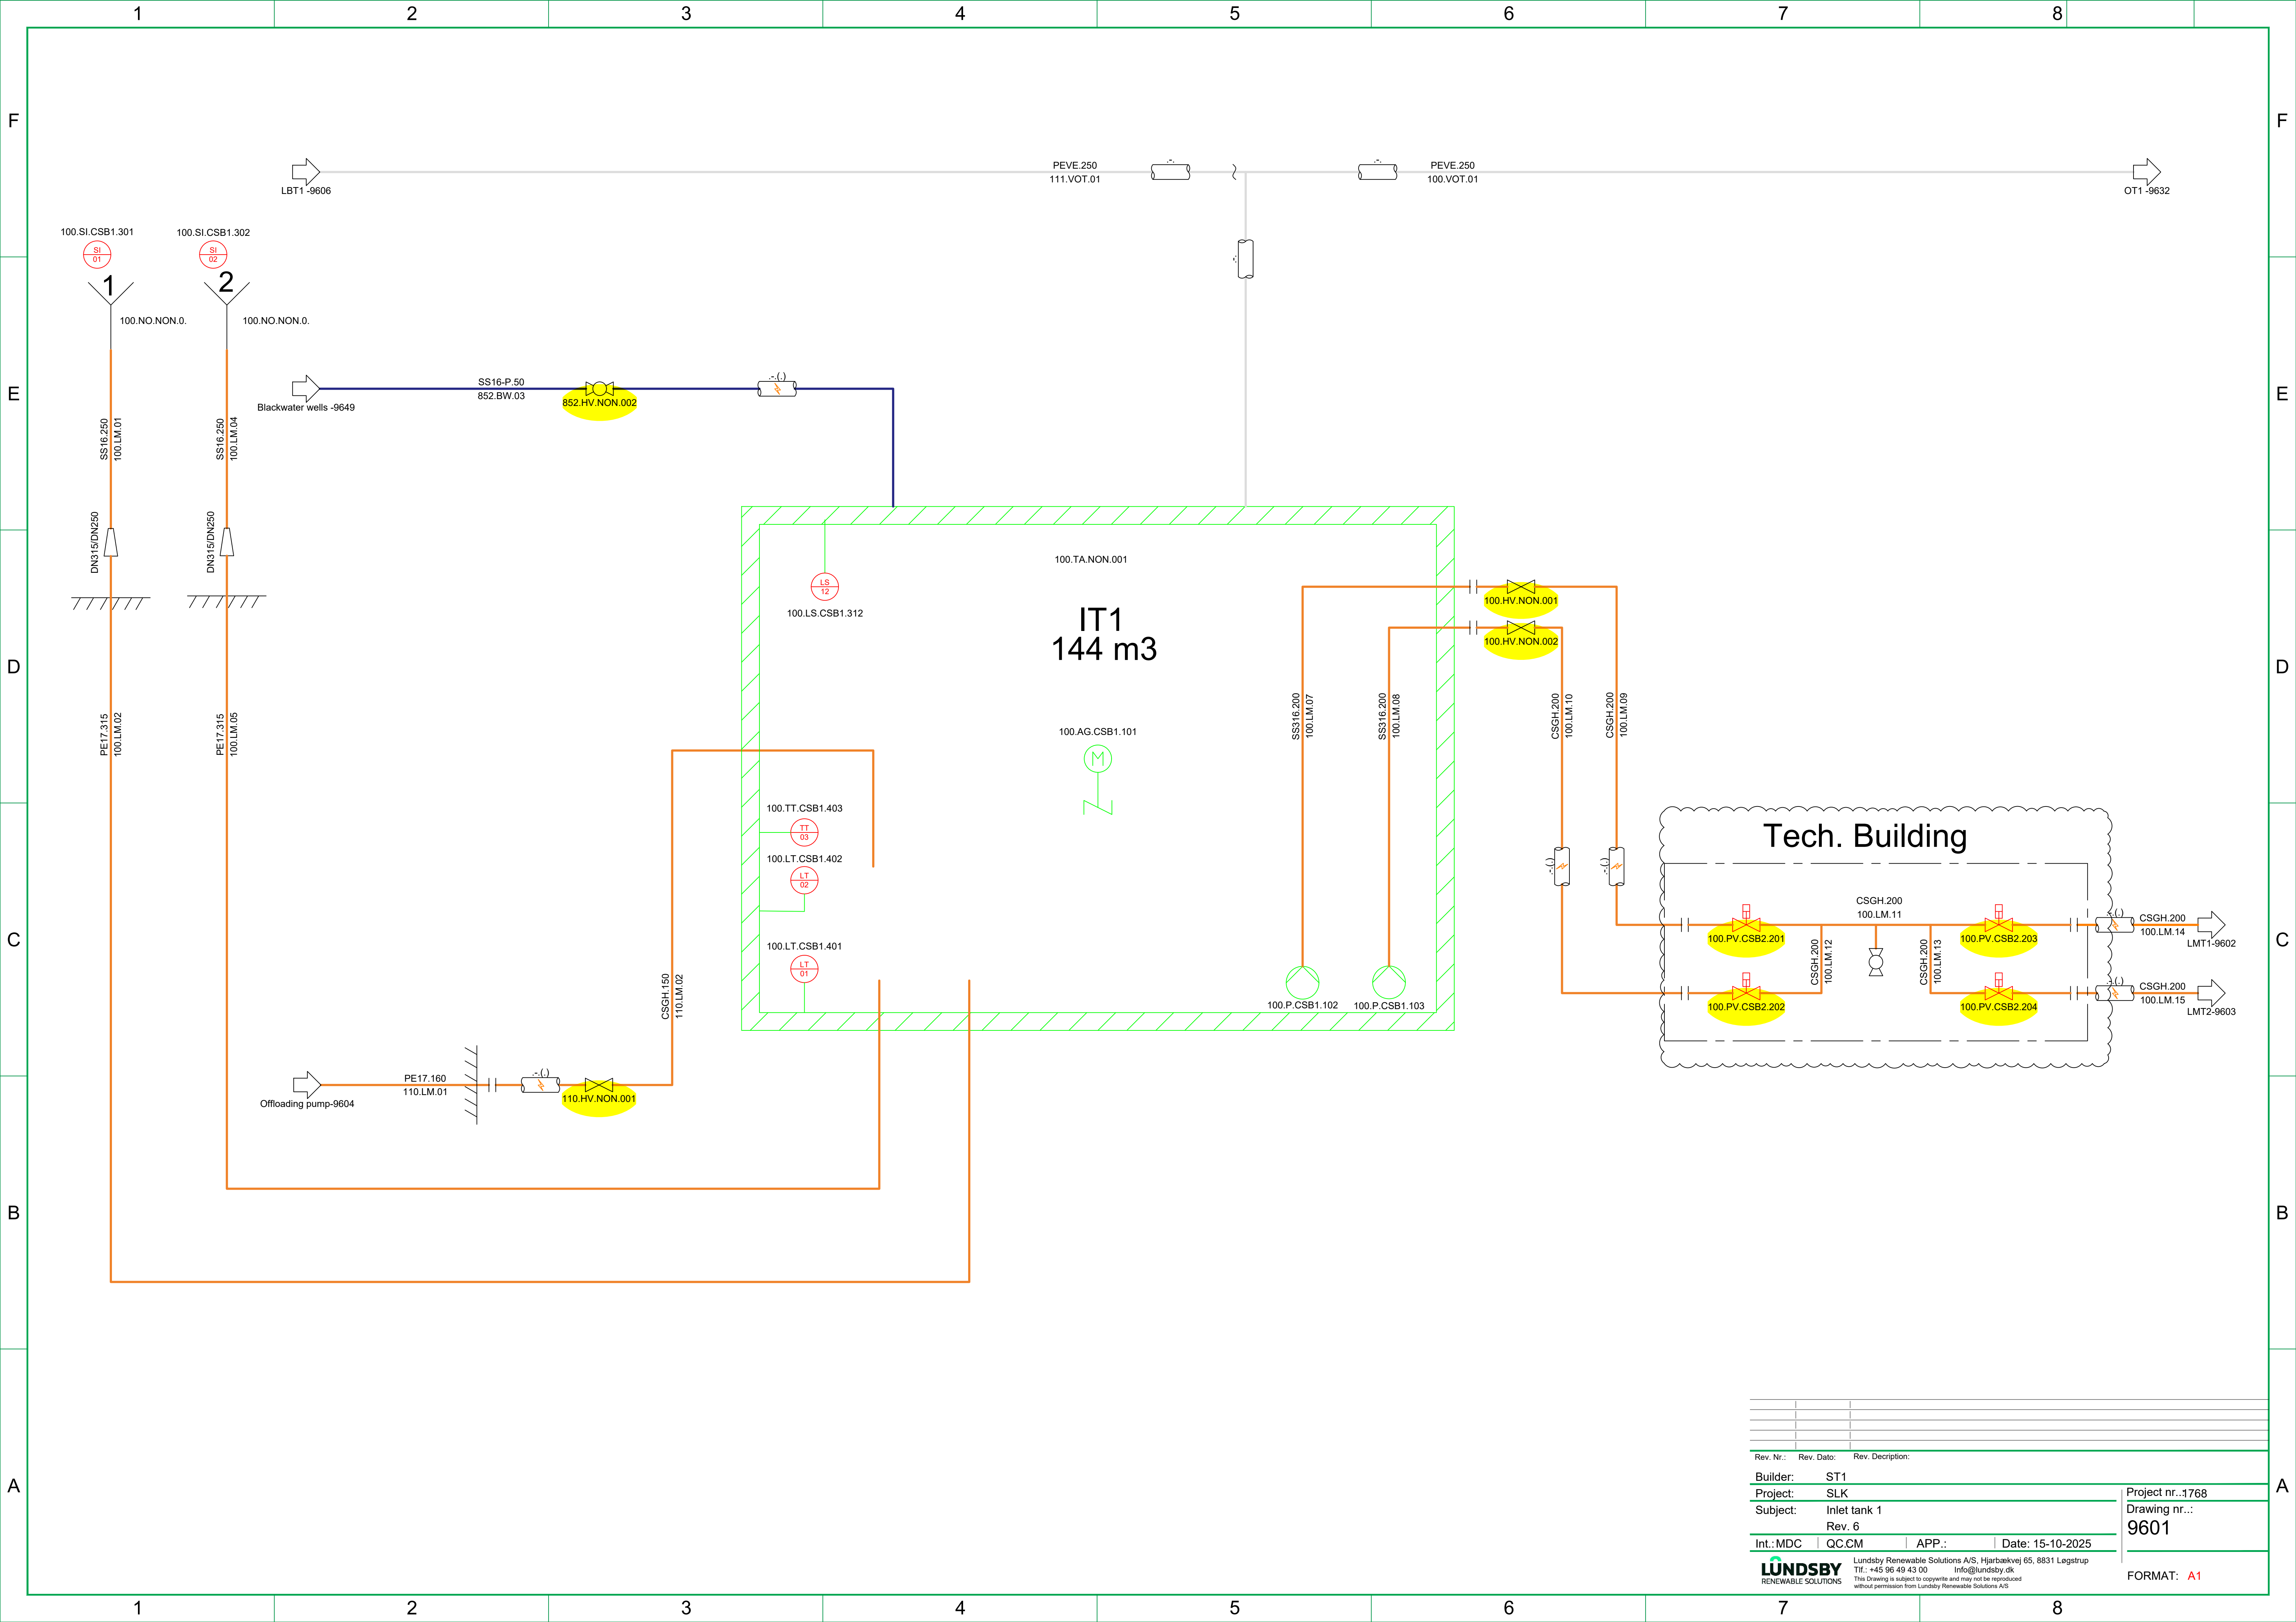


Rev. Nr.:	Rev. Dato:	Rev. Description:			
Builder:	ST1				
Project:	SLK				
Subject:	Inlet tank 1				
	Rev. 6				
Int.: MDC	QC:CM	APP.:	Date: 15-10-2025		
LUNDSBY RENEWABLE SOLUTIONS Lundsby Renewable Solutions A/S, Hjarbækvej 65, 8831 Løgstrup Tlf.: +45 96 49 43 00 Info@lundsby.dk This Drawing is subject to copyright and may not be reproduced without permission from Lundsby Renewable Solutions A/S					
Project nr.:1768					
Drawing nr.: 9601					
FORMAT: A1					

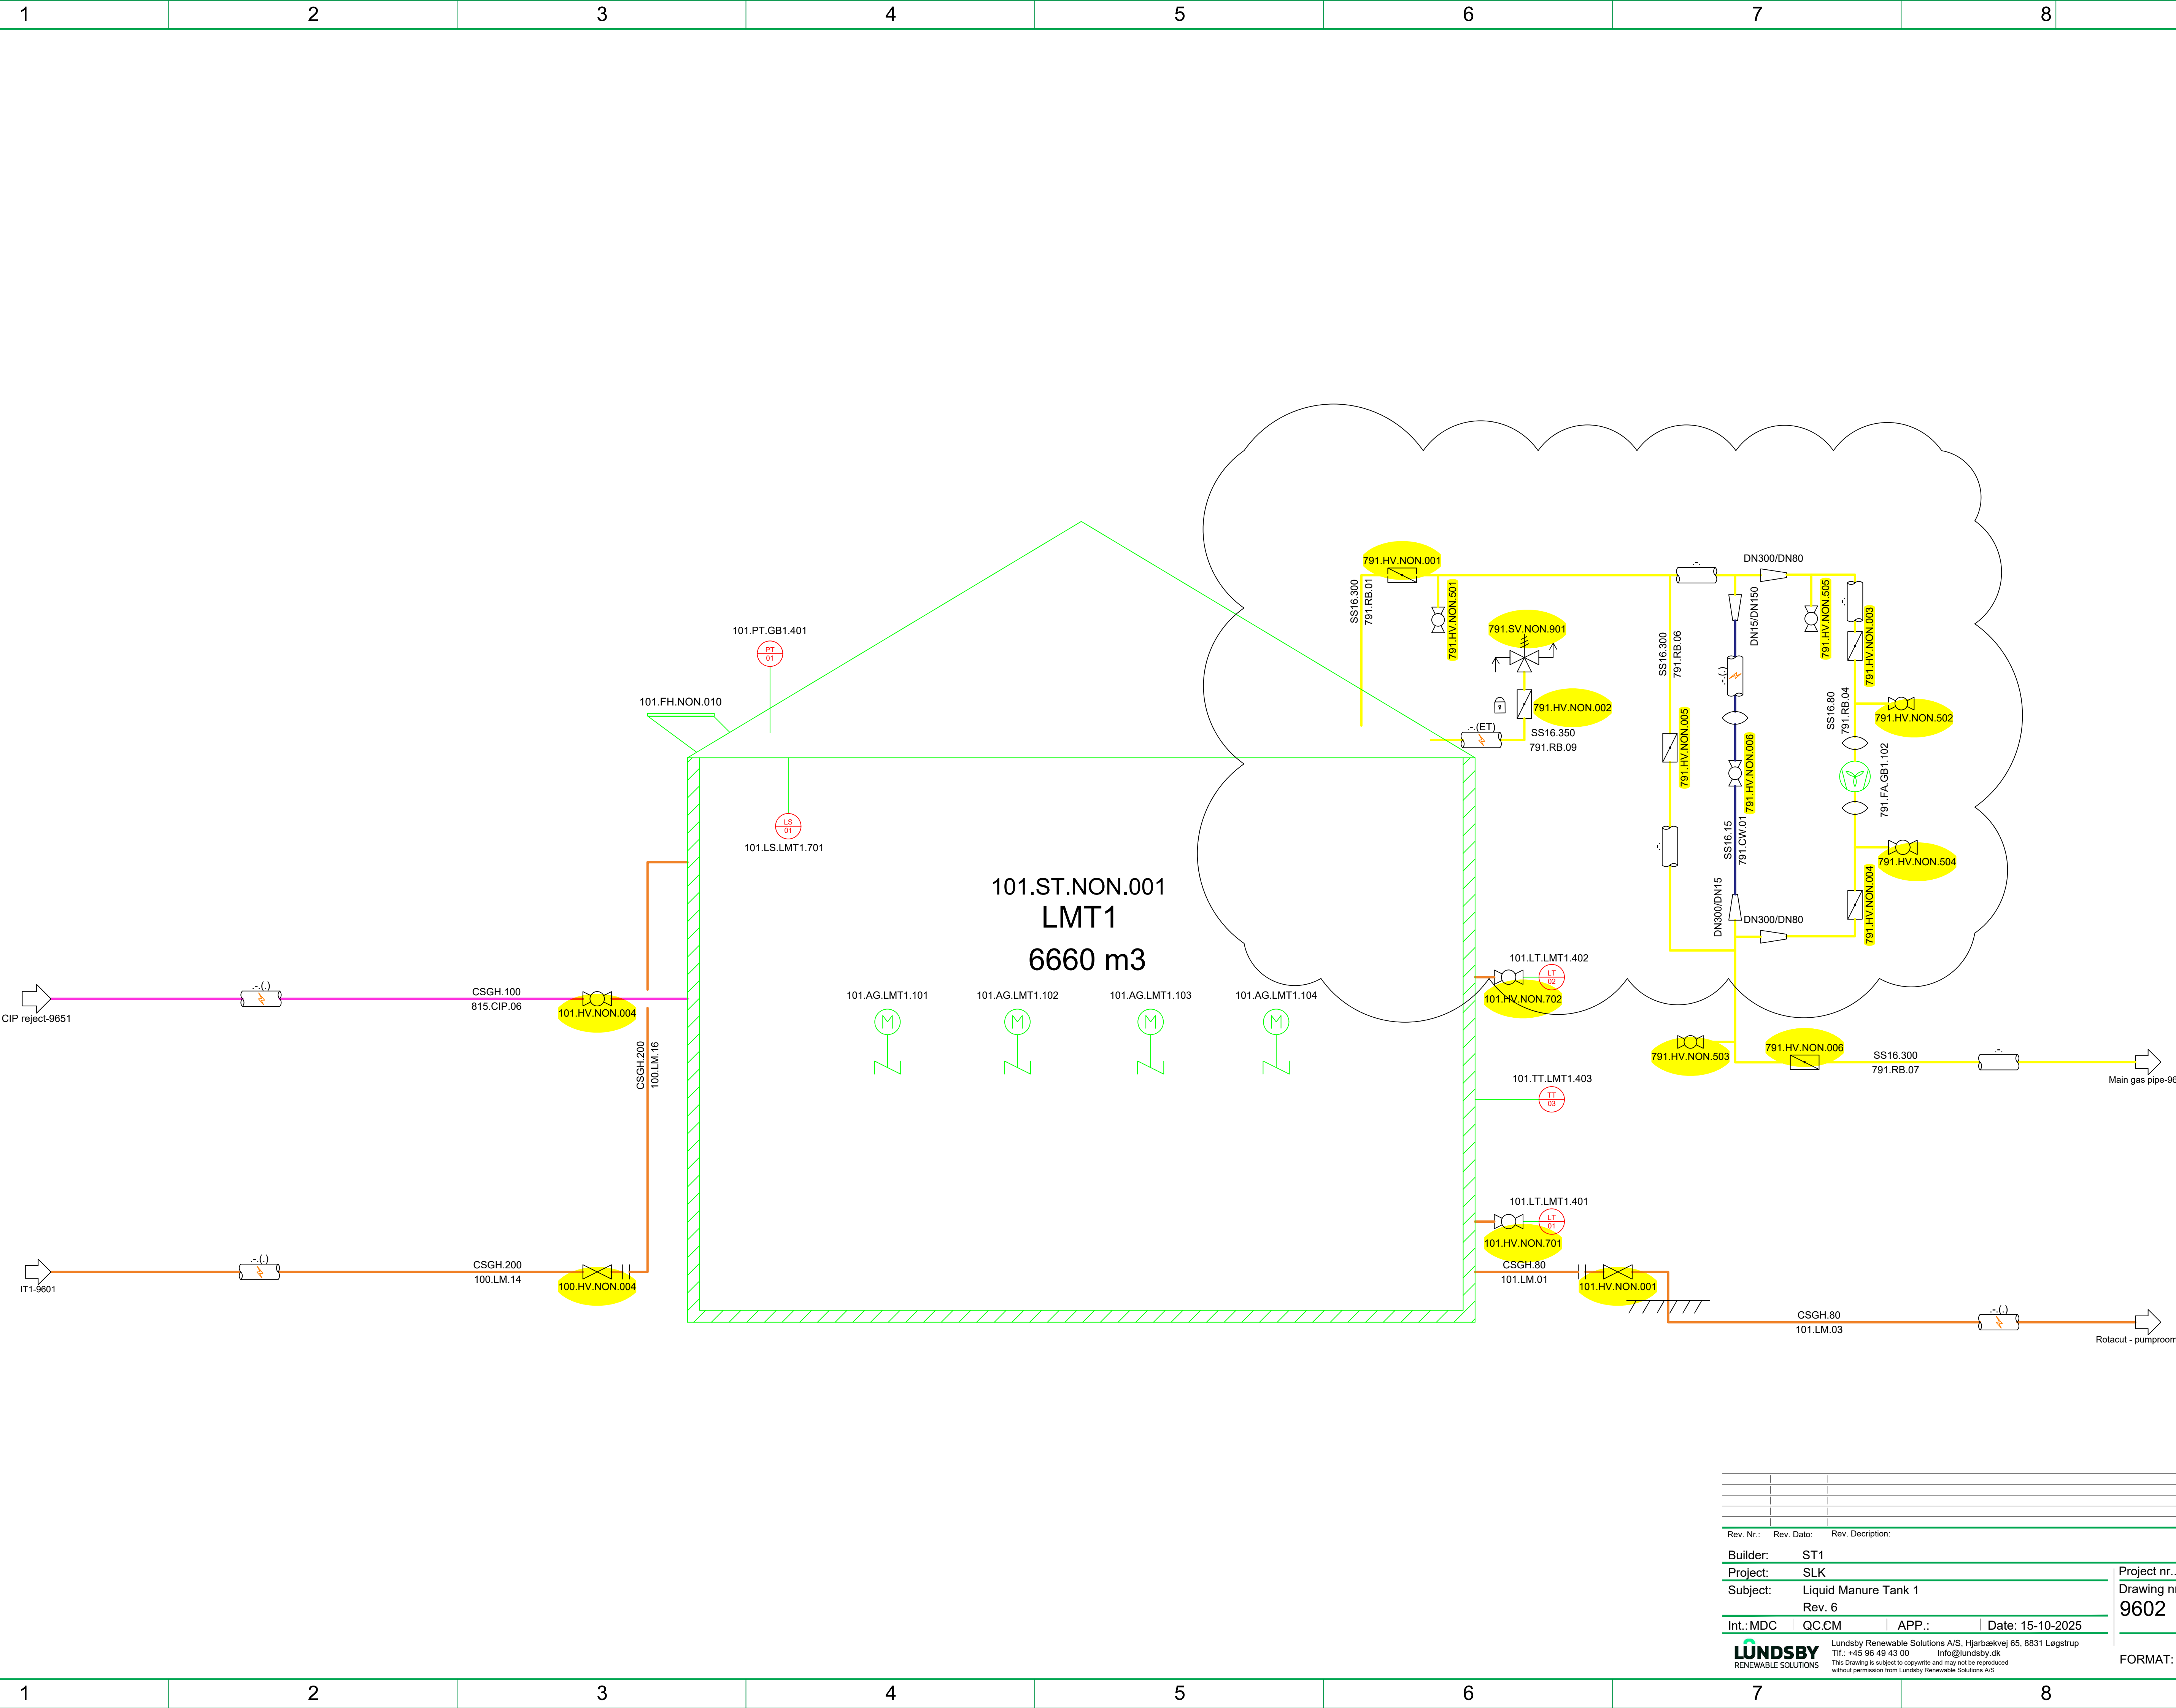


Rev. Nr.:		Rev. Dato:	Rev. Description:
Builder:		ST1	
Project:		SLK	
Subject:		Liquid Manure Tank 1	
		Rev. 6	
Int.: MDC		QC: CM	APP.: Date: 15-10-2025
LUNDSBY		Lundsby Renewable Solutions A/S, Hjarbækvej 65, 8831 Lægstrup	
RENEWABLE SOLUTIONS		Tlf.: +45 96 49 43 00 Info@lundsby.dk	
		This Drawing is subject to copyright and may not be reproduced without permission from Lundsby Renewable Solutions A/S	
		Project nr.: 1768	
		Drawing nr.: 9602	
		FORMAT: A1	

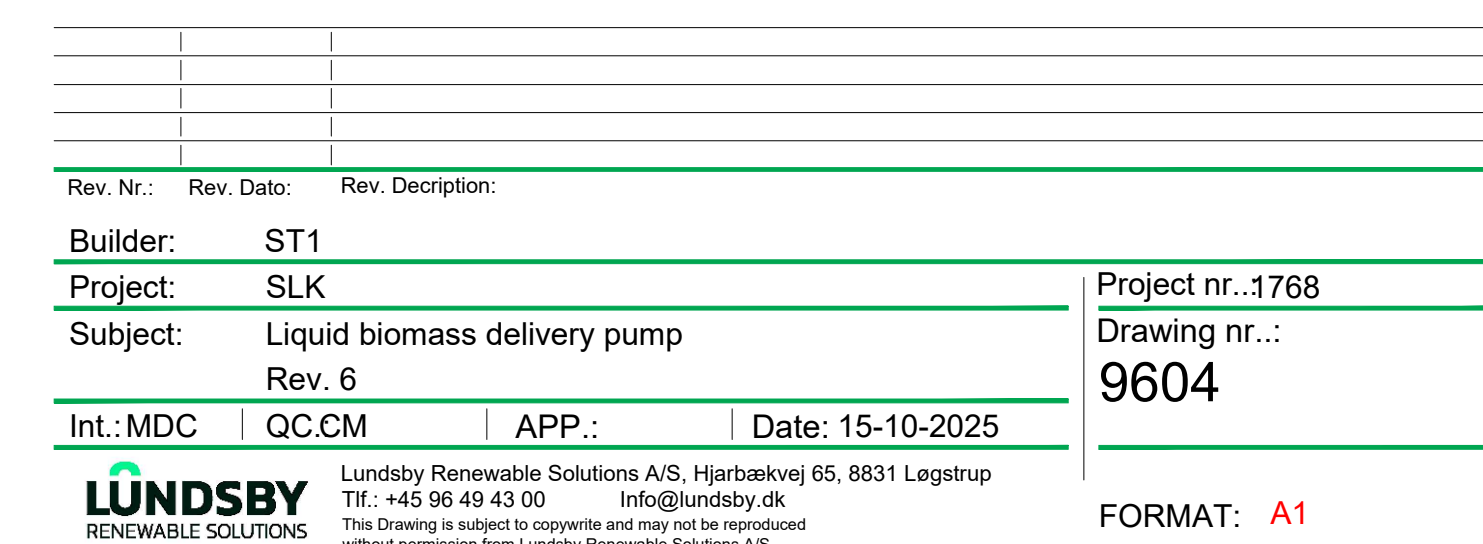


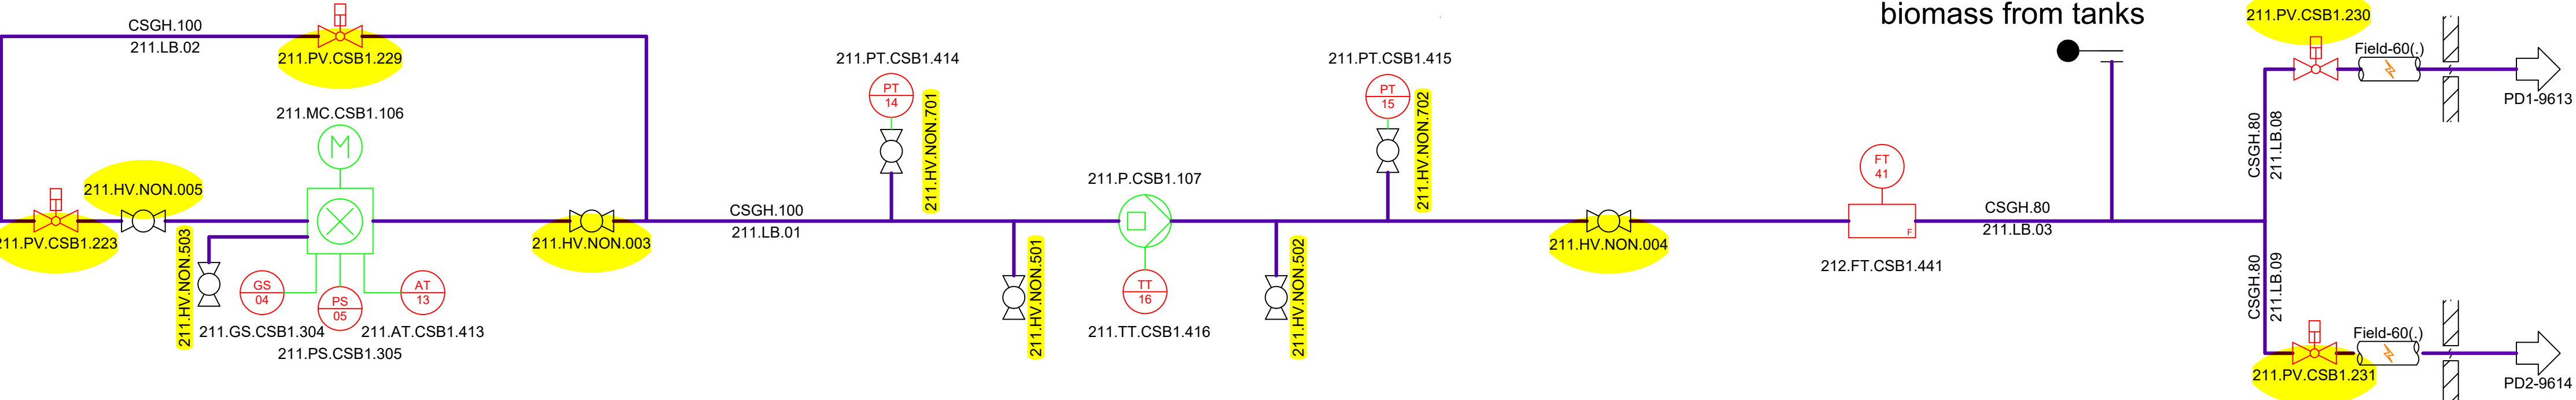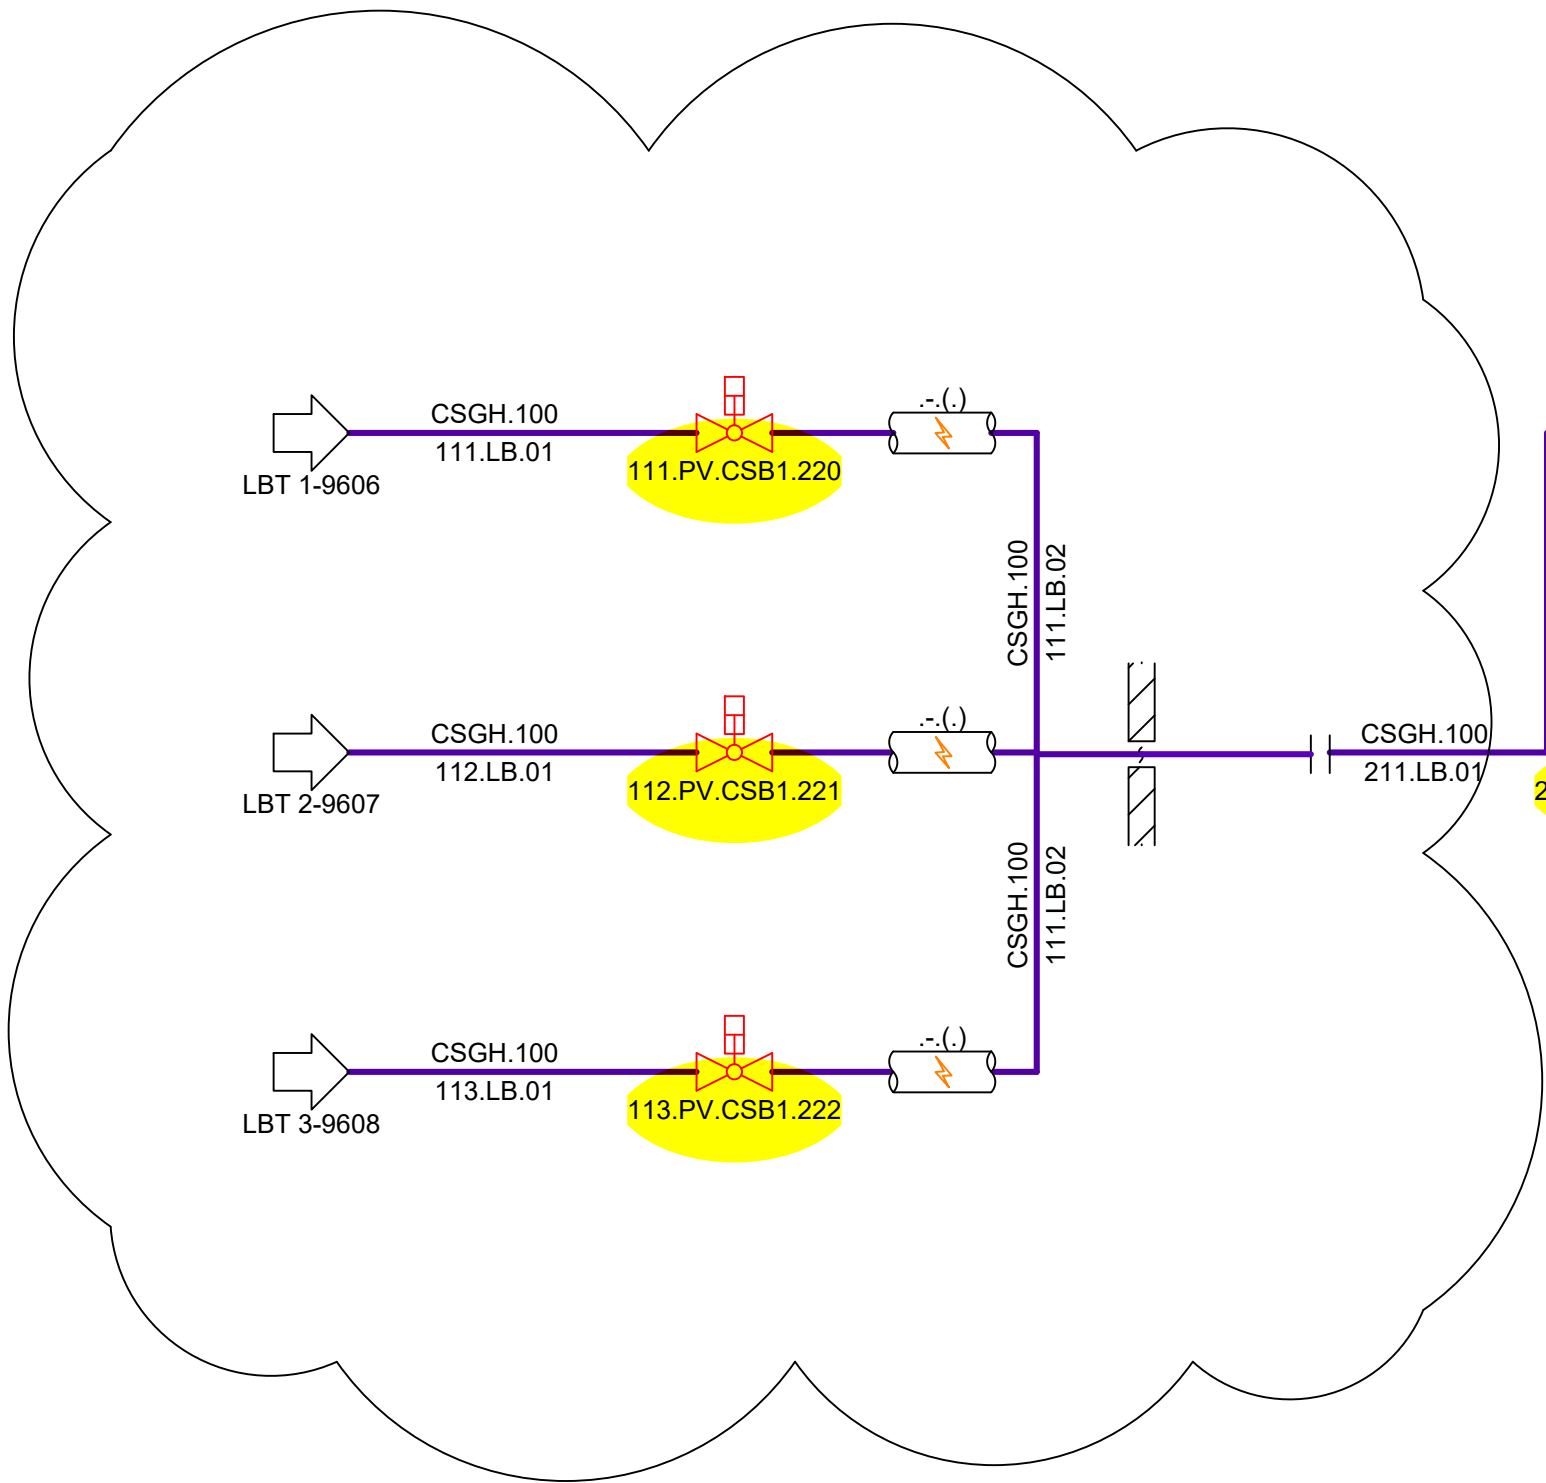


Rev. Nr.:	Rev. Dato:	Rev. Description:
Builder:	ST1	
Project:	SLK	
Subject:	Liquid biomass pump 1	
Rev. 6		
Int.:MDC	QC:CM	APP.: Date: 15-10-2025
LUNDSBY RENEWABLE SOLUTIONS		
Lundsby Renewable Solutions A/S, Hjarbækvej 65, 8831 Løgstrup Tlf.: +45 96 49 43 00 Info@lundsby.dk This Drawing is subject to copyright and may not be reproduced without permission from Lundsby Renewable Solutions A/S		
Project nr.:1768 Drawing nr.: 9605		FORMAT: A1

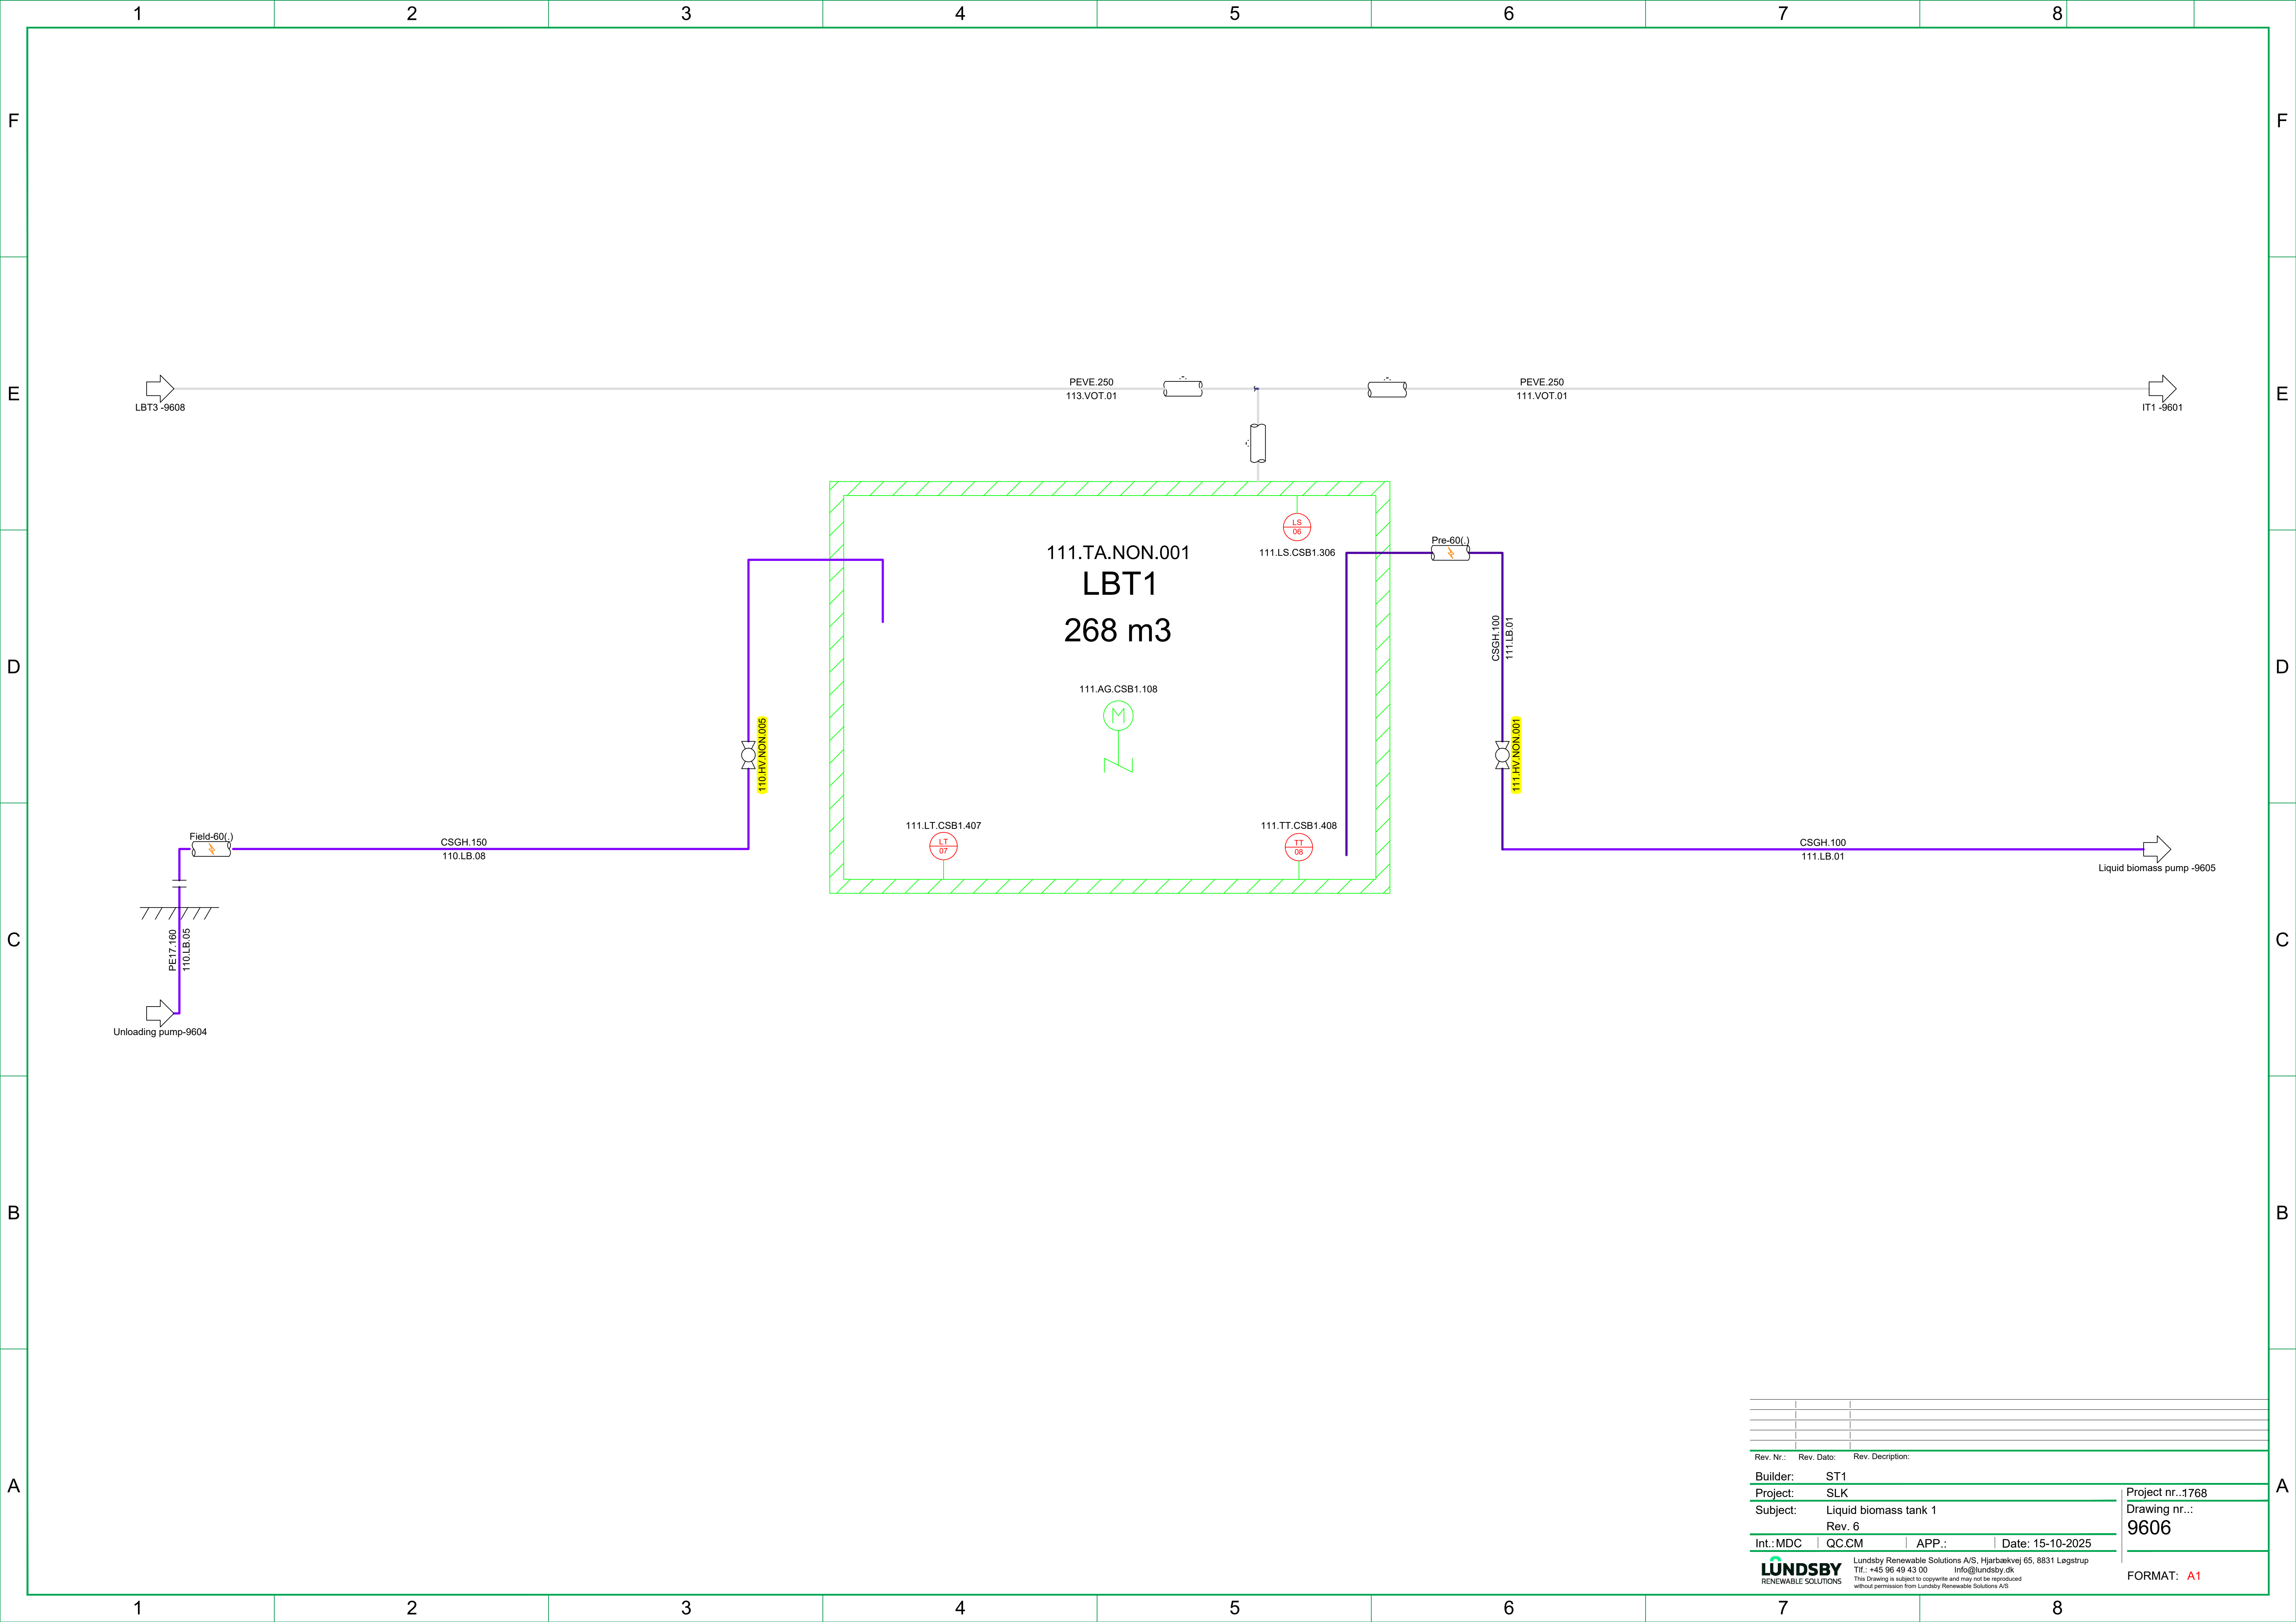


Rev. Nr.:	Rev. Dato:	Rev. Description:	Project nr...1768
Builder:	ST1		Drawing nr...: 9606
Project:	SLK		
Subject:	Liquid biomass tank 1		
	Rev. 6		
Int.:MDC	QC.CM	APP.:	Date: 15-10-2025
LUNDSBY RENEWABLE SOLUTIONS			FORMAT: A1

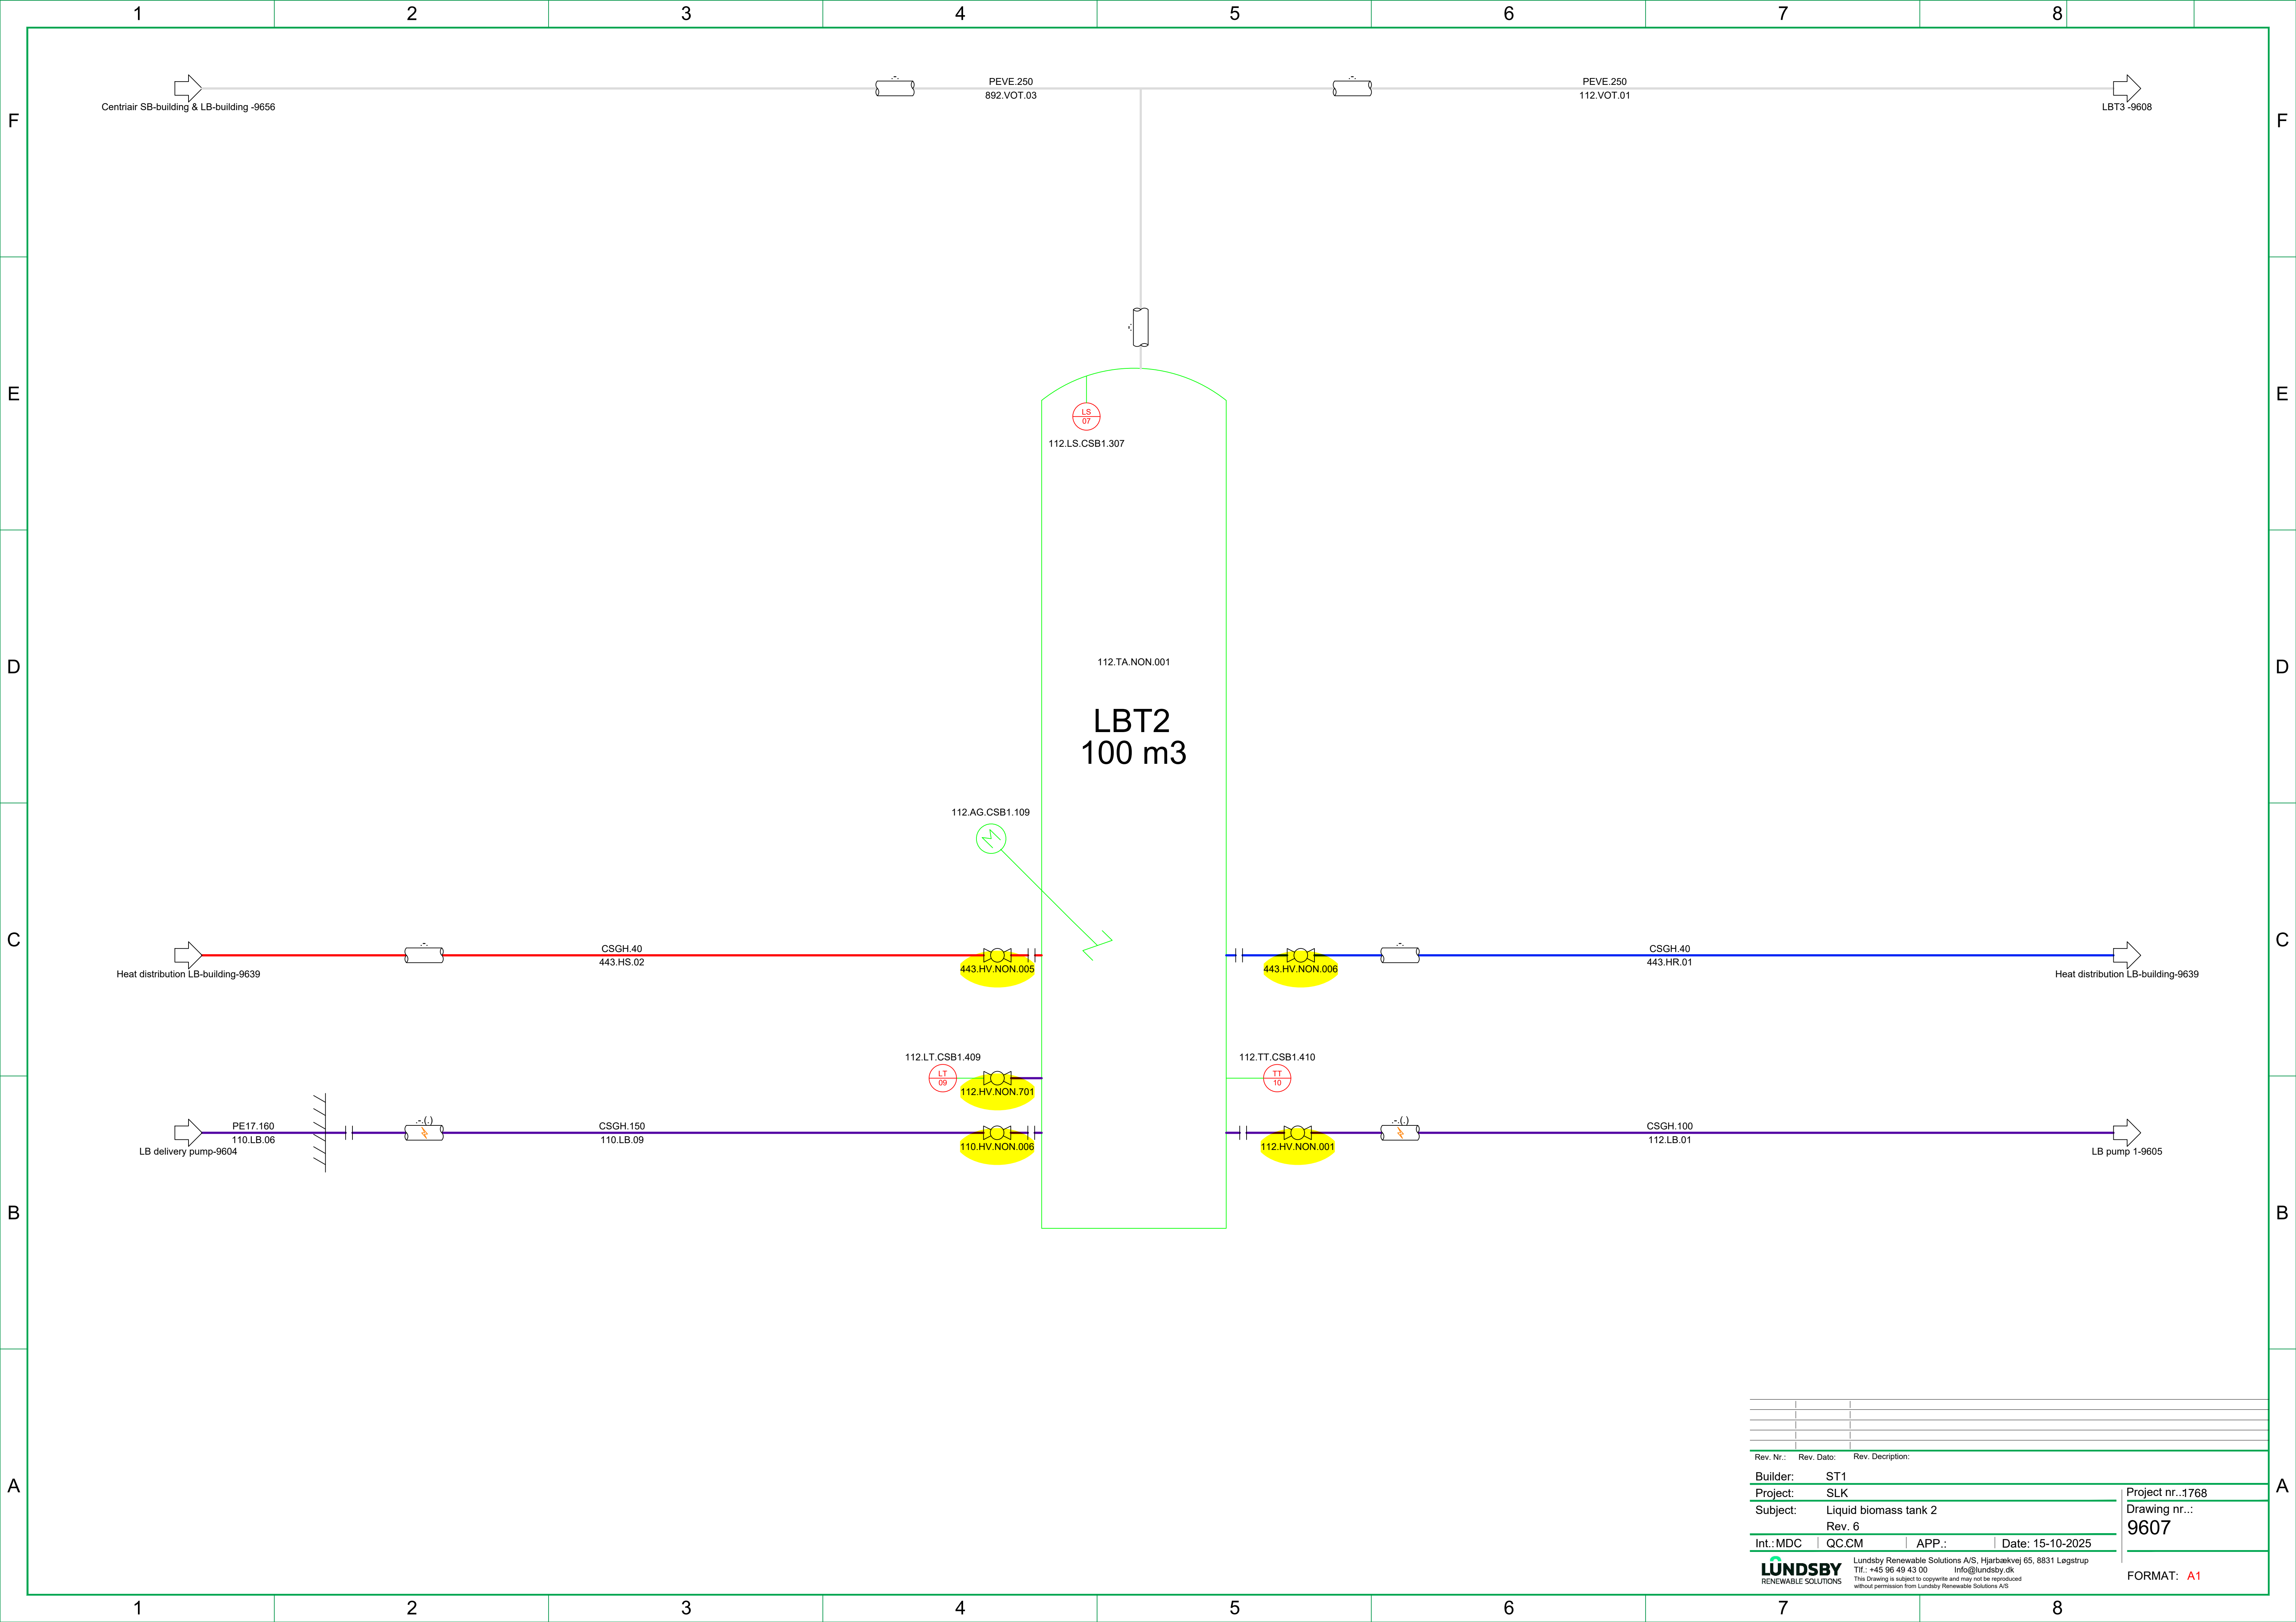


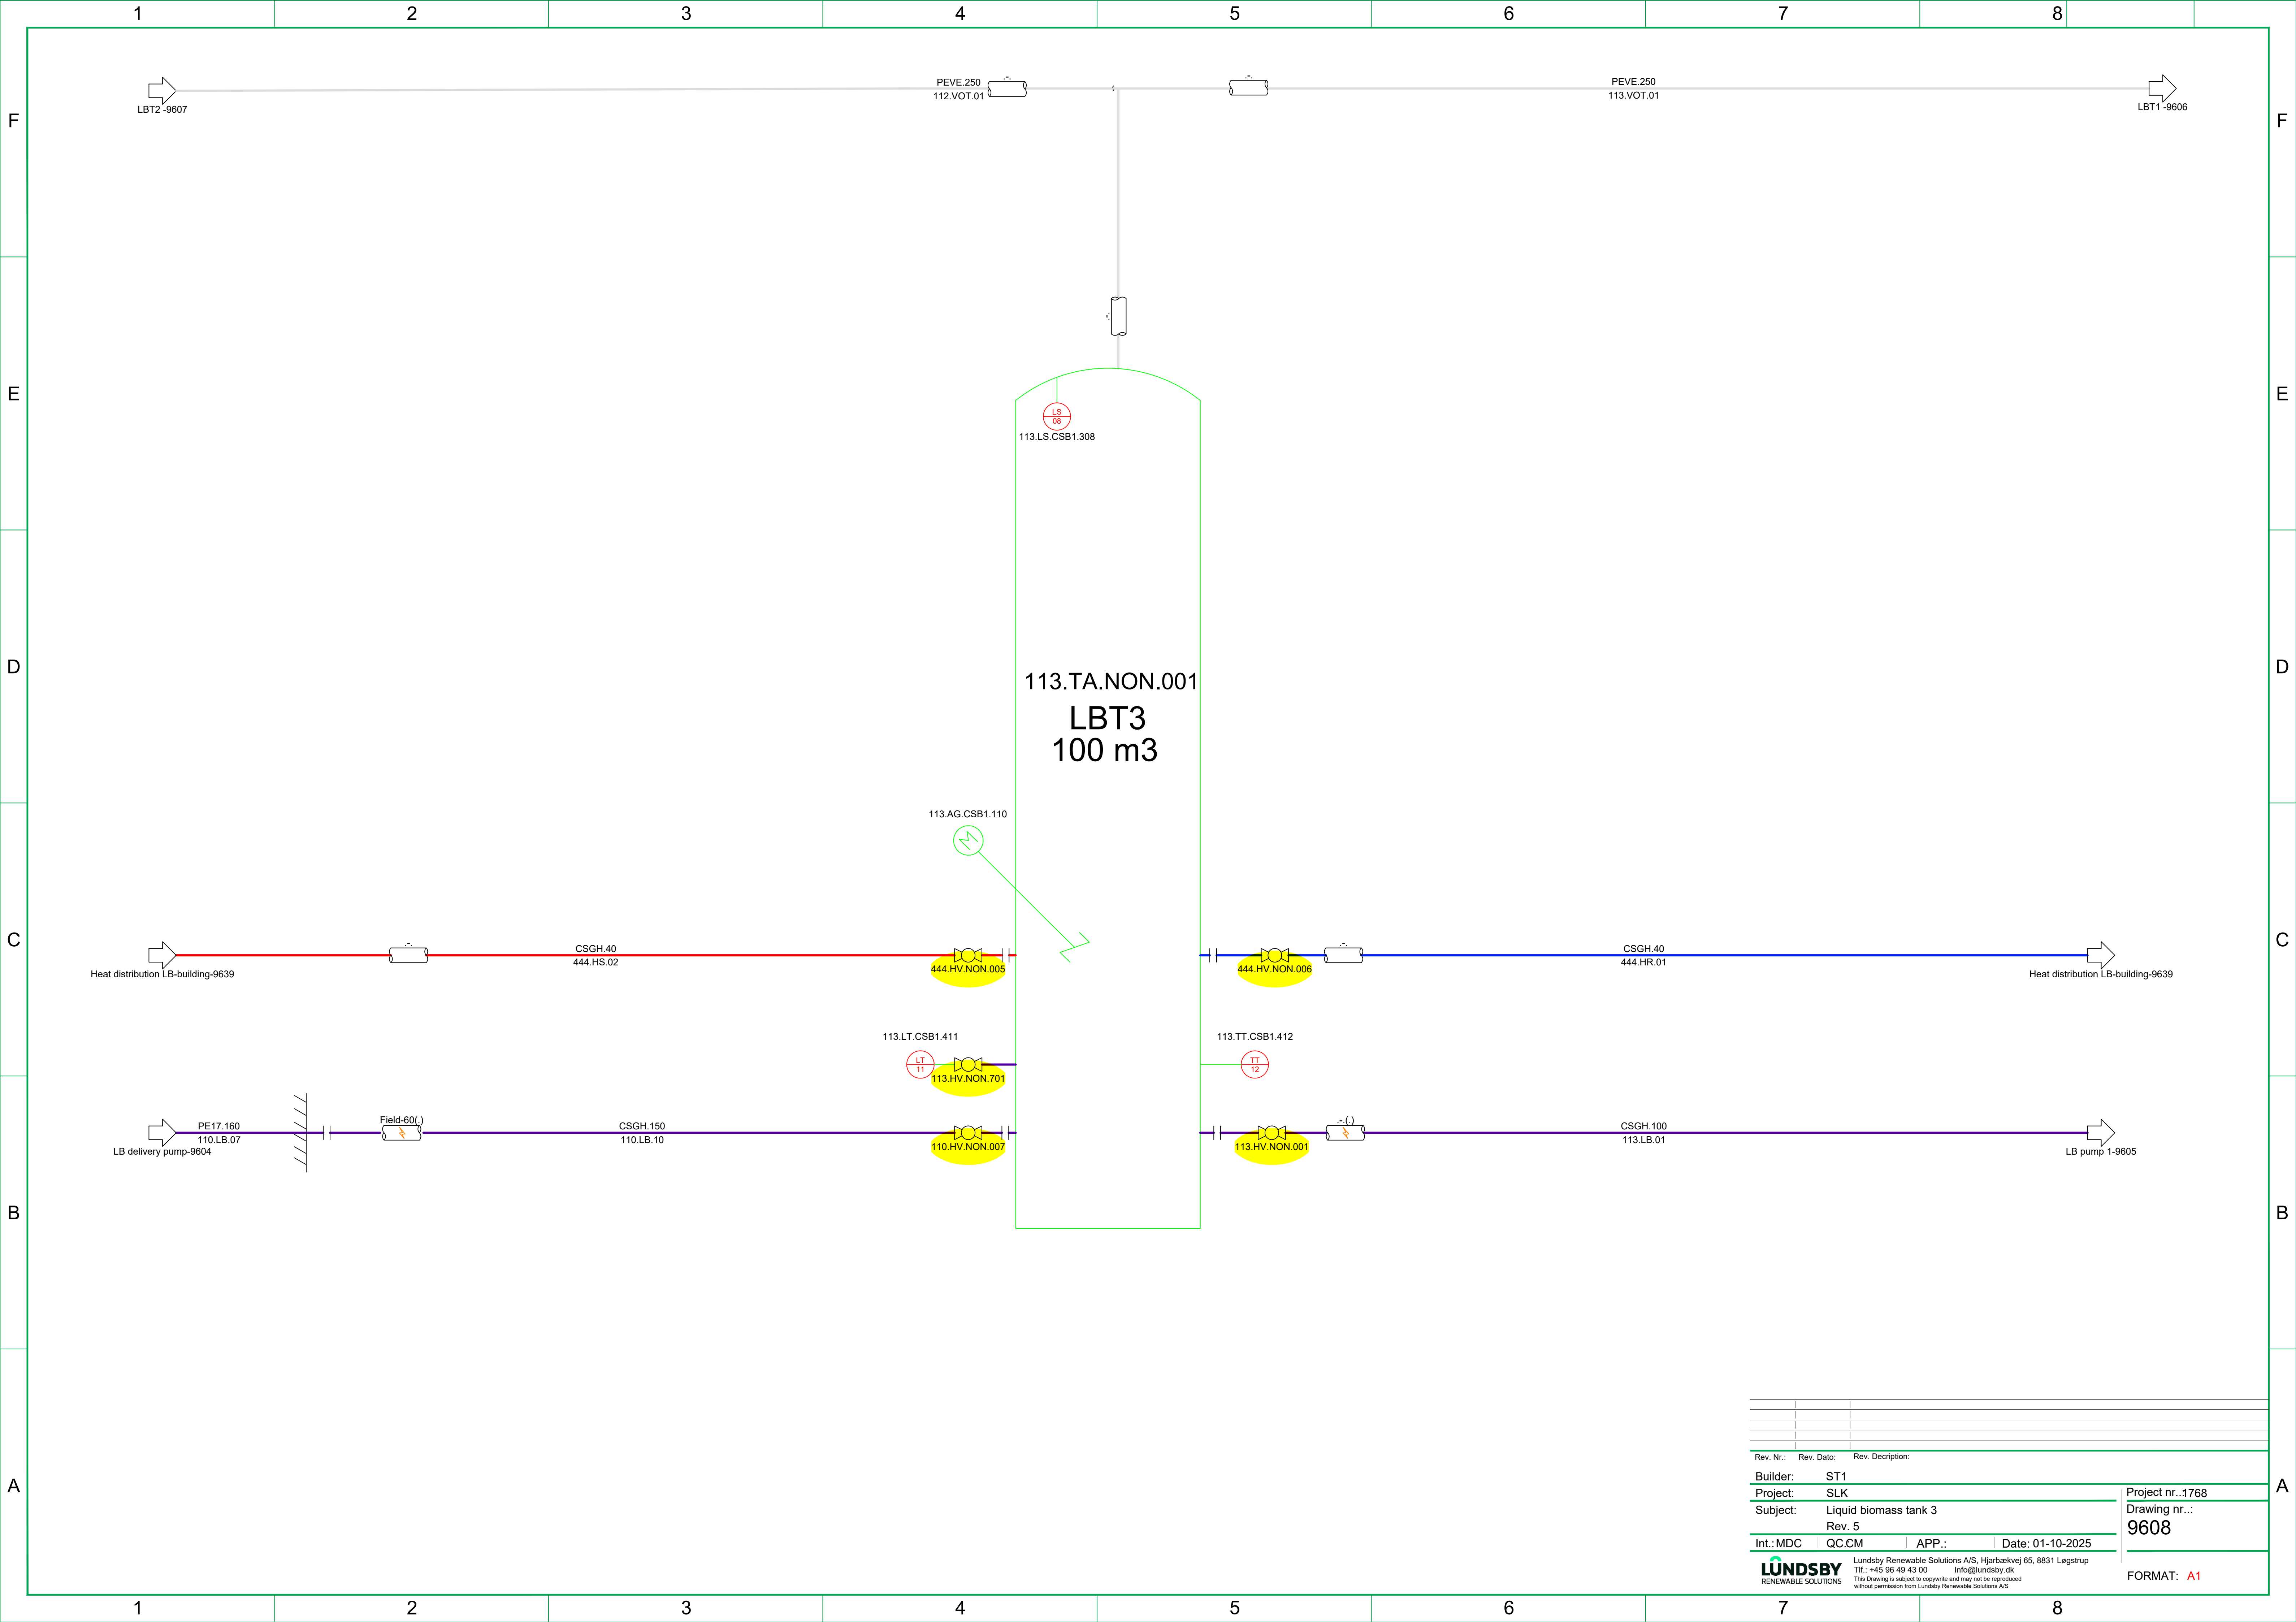


Rev. Nr.:	Rev. Dato:	Rev. Description:
Builder:	ST1	
Project:	SLK	
Subject:	Liquid biomass tank 3	
Rev. 5		
Int.:MDC	QC:CM	APP.: Date: 01-10-2025
LUNDSBY RENEWABLE SOLUTIONS		
Lundsby Renewable Solutions A/S, Hjarbækvej 65, 8831 Løgstrup Tlf.: +45 96 49 43 00 Info@lundsby.dk This Drawing is subject to copyright and may not be reproduced without permission from Lundsby Renewable Solutions A/S		
Project nr.:1768		Drawing nr.: 9608
FORMAT: A1		

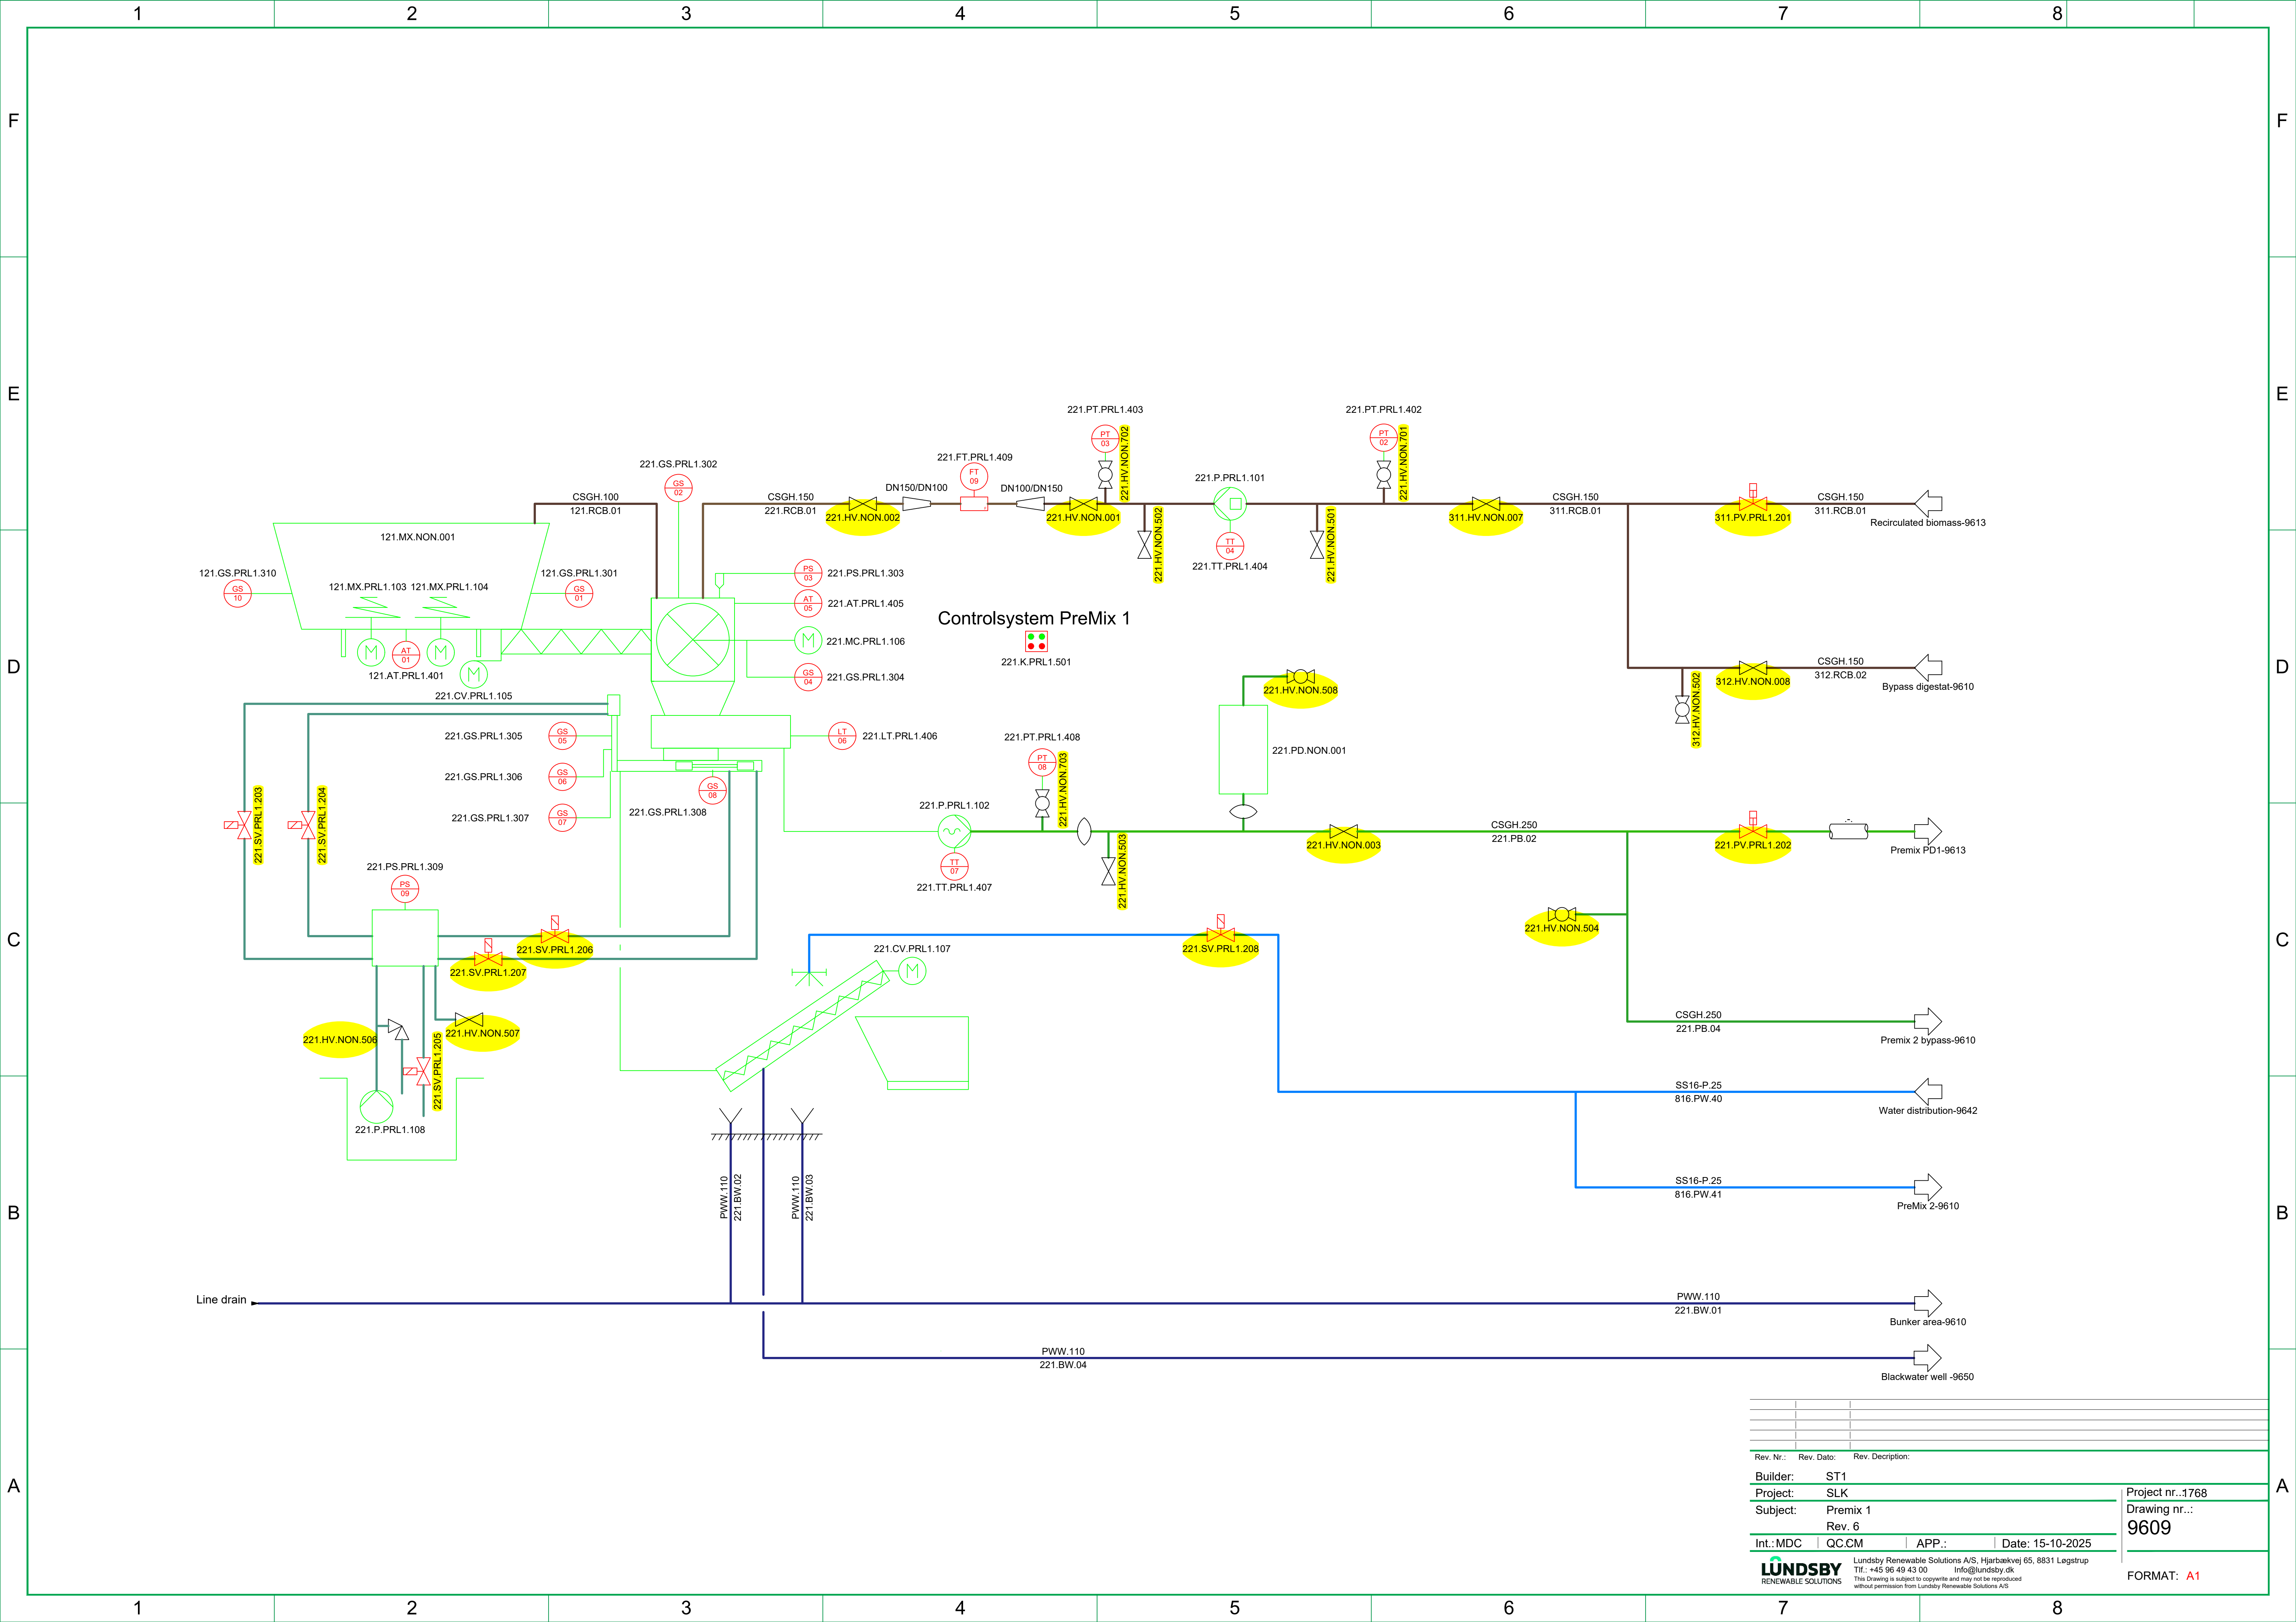

Rev. Nr.:	Rev. Dato:	Rev. Description:	
Builder:	ST1		
Project:	SLK		
Subject:	Premix 1		
	Rev. 6		
Int.: MDC	QC.CM	APP.:	Date: 15-10-2025
LUNDSBY RENEWABLE SOLUTIONS			Lundsby Renewable Solutions A/S, Hjarbækvej 65, 8831 Løgstrup Tlf.: +45 96 49 43 00 Info@lundsby.dk This drawing is subject to copyright and may not be reproduced without permission from Lundsby Renewable Solutions A/S
Project nr.: 1768 Drawing nr.: 9609			FORMAT: A1

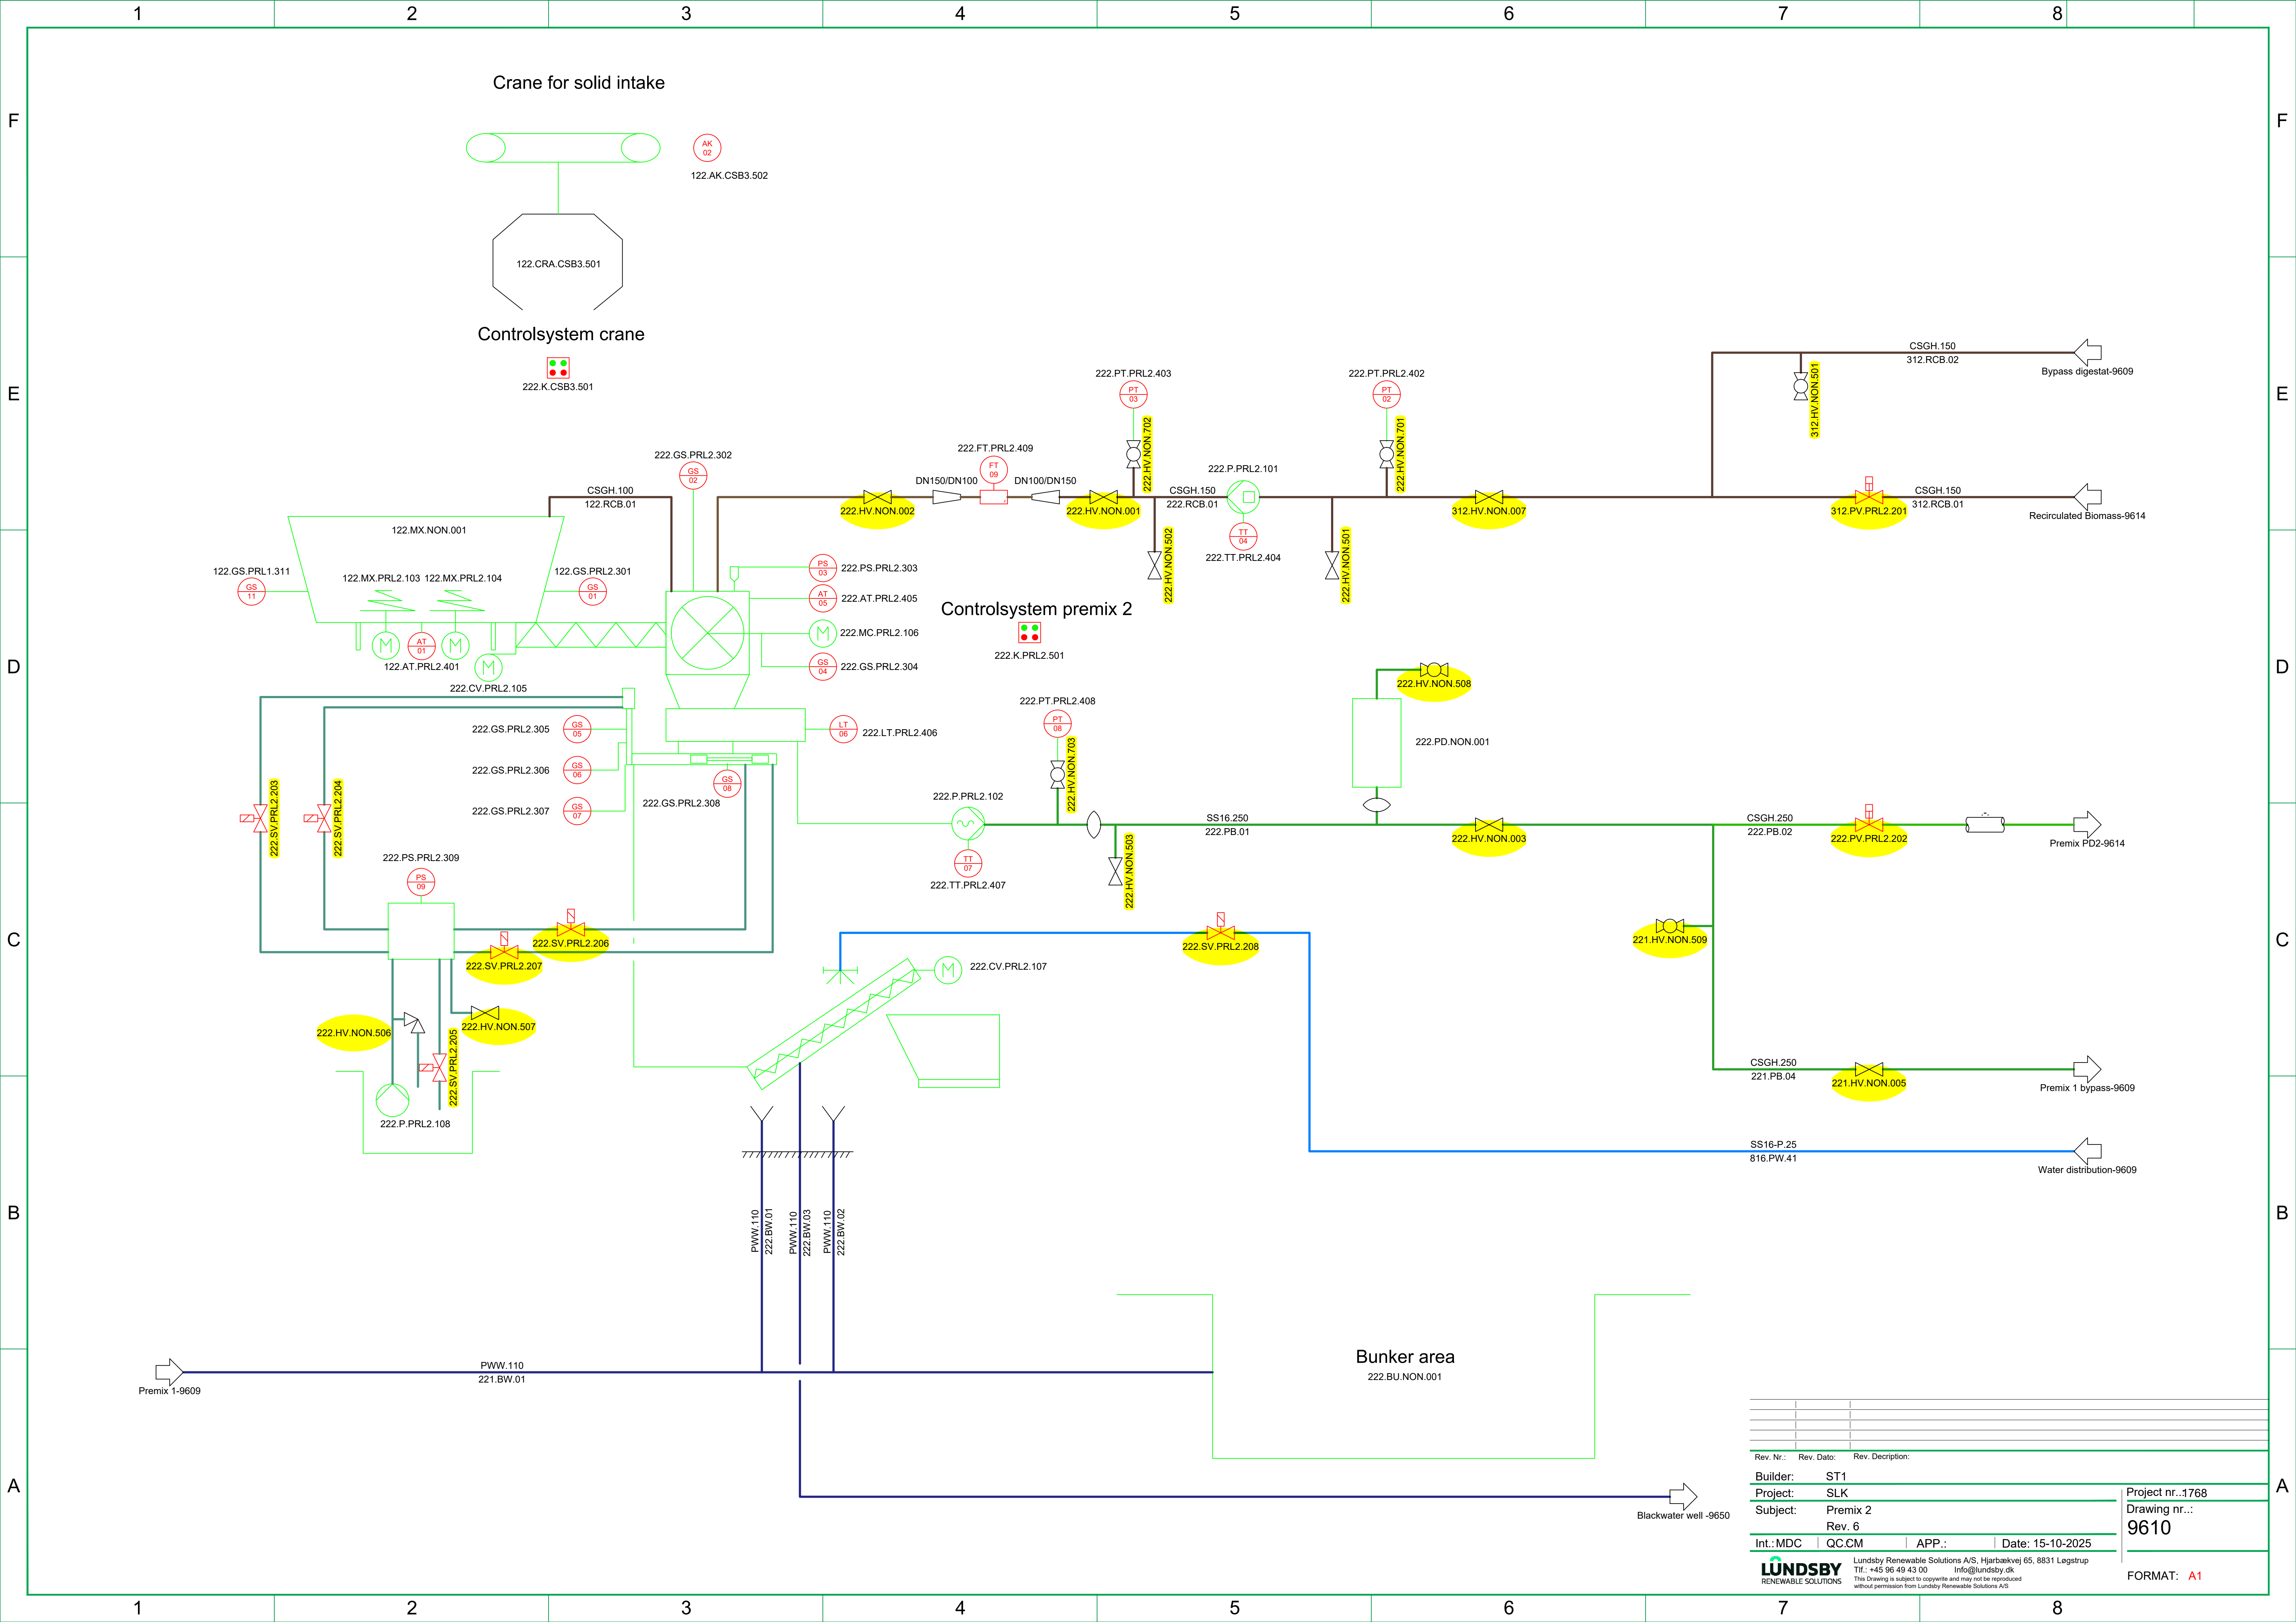


Rev. Nr.:	Rev. Dato:	Rev. Description:
Builder:	ST1	
Project:	SLK	
Subject:	Premix 2	
	Rev. 6	
Int.:MDC	QC:CM	APP.:
		Date: 15-10-2025
LUNDSBY RENEWABLE SOLUTIONS		
Lundsby Renewable Solutions A/S, Hjarbækvej 65, 8831 Løgstrup Tlf.: +45 96 49 43 00 Info@lundsby.dk This Drawing is subject to copyright and may not be reproduced without permission from Lundsby Renewable Solutions A/S		
Project nr.:1768 Drawing nr.: 9610		FORMAT: A1

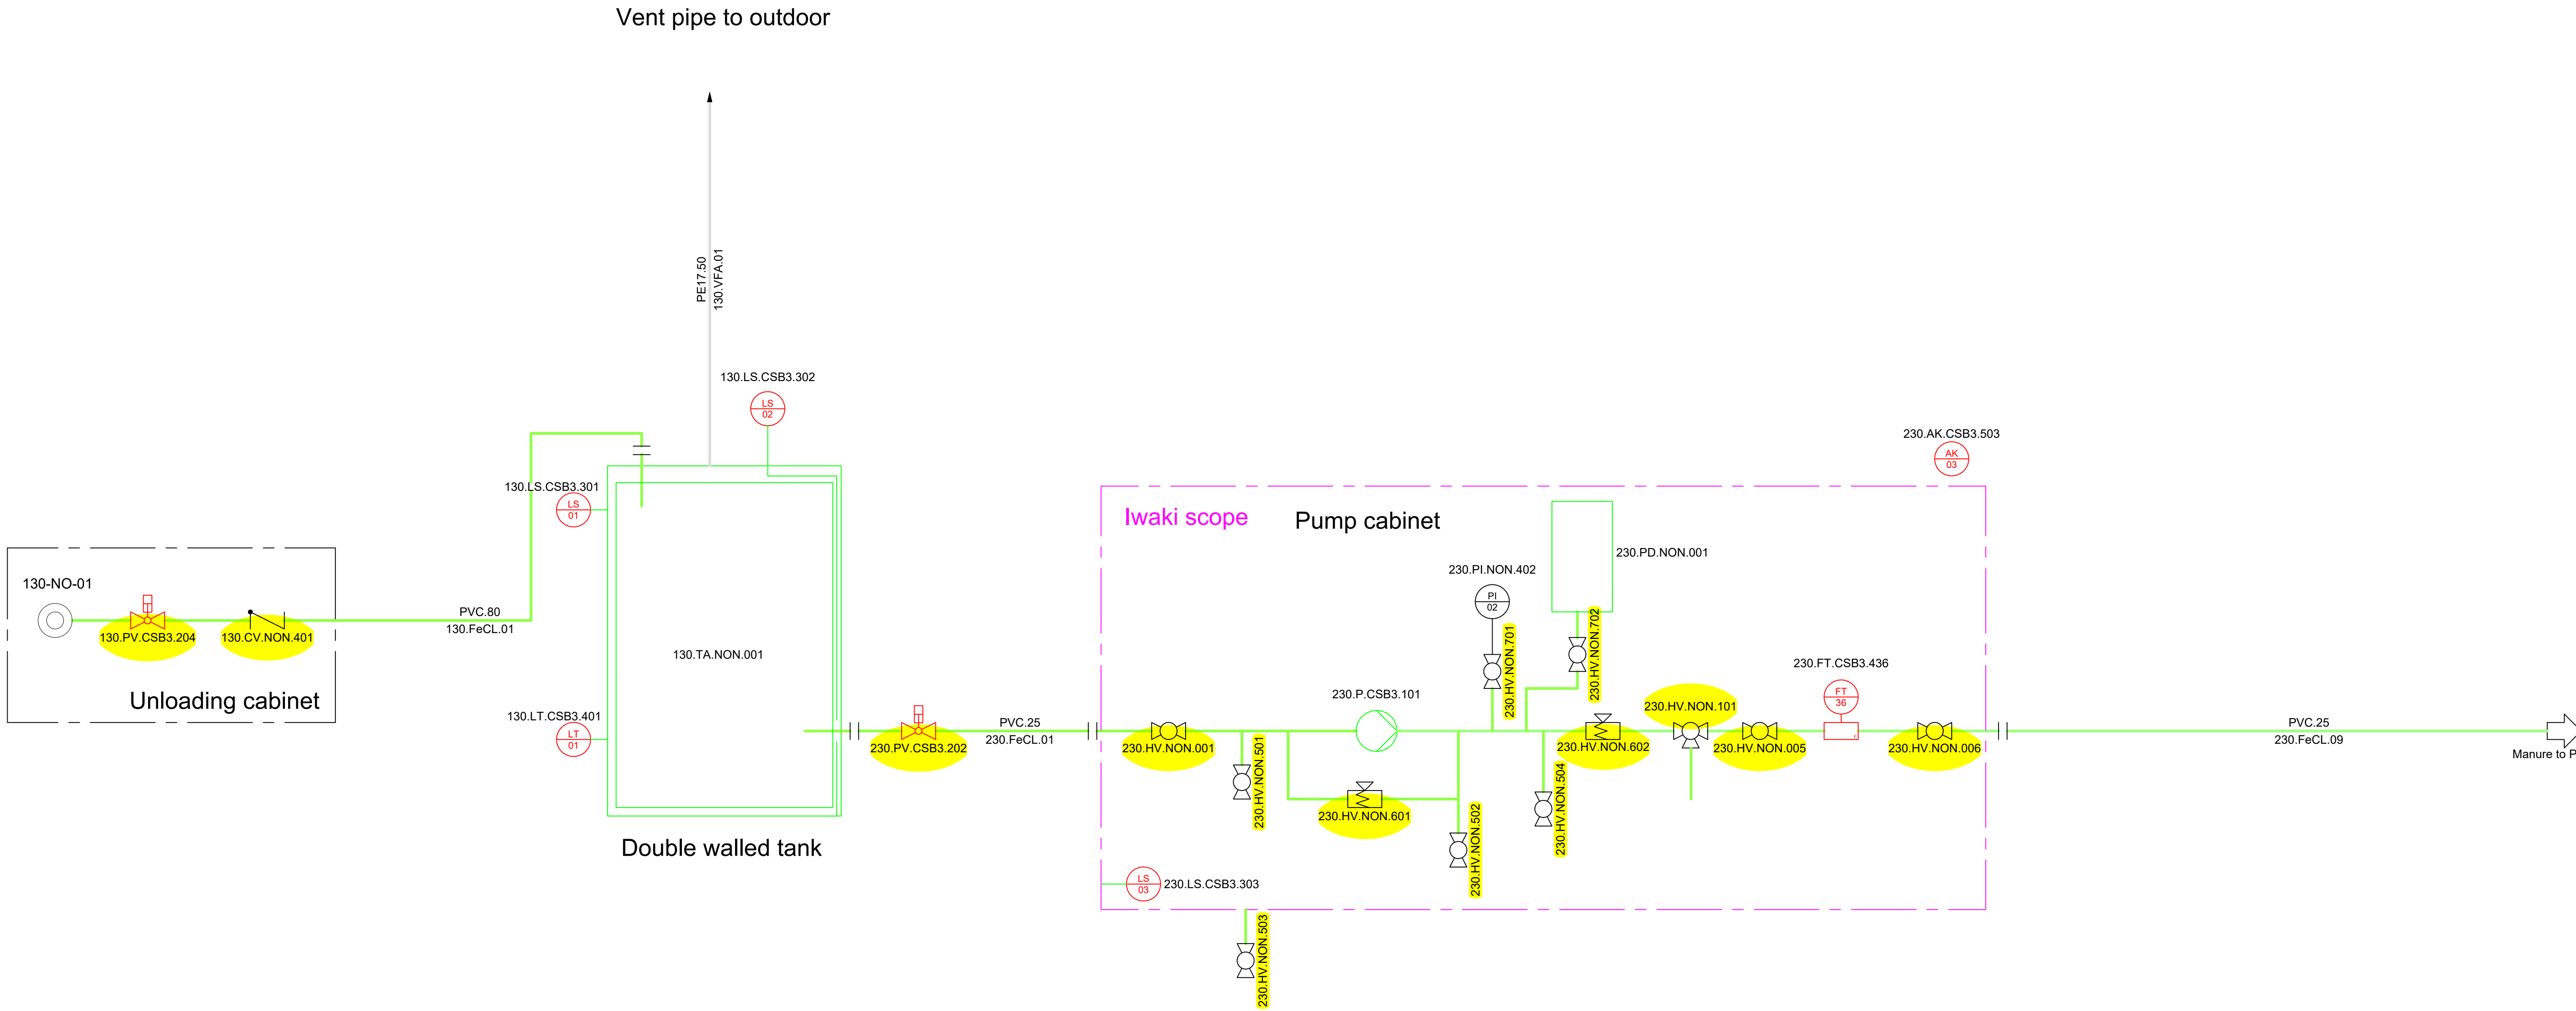


Rev. Nr.: Rev. Dato: Rev. Description:					
Builder:		ST1			
Project:		SLK			
Subject:		FECL system			
		Rev. 6			
Int.: MDC		QC:CM		APP.: Date: 15-10-2025	
		Lundsby Renewable Solutions A/S, Hjarbækvej 65, 8831 Løgstrup Tlf.: +45 96 49 43 00 Info@lundsby.dk This Drawing is subject to copyright and may not be reproduced without permission from Lundsby Renewable Solutions A/S			
		Project nr.:1768 Drawing nr.: 9611			
		FORMAT: A1			

Pumphouse 2

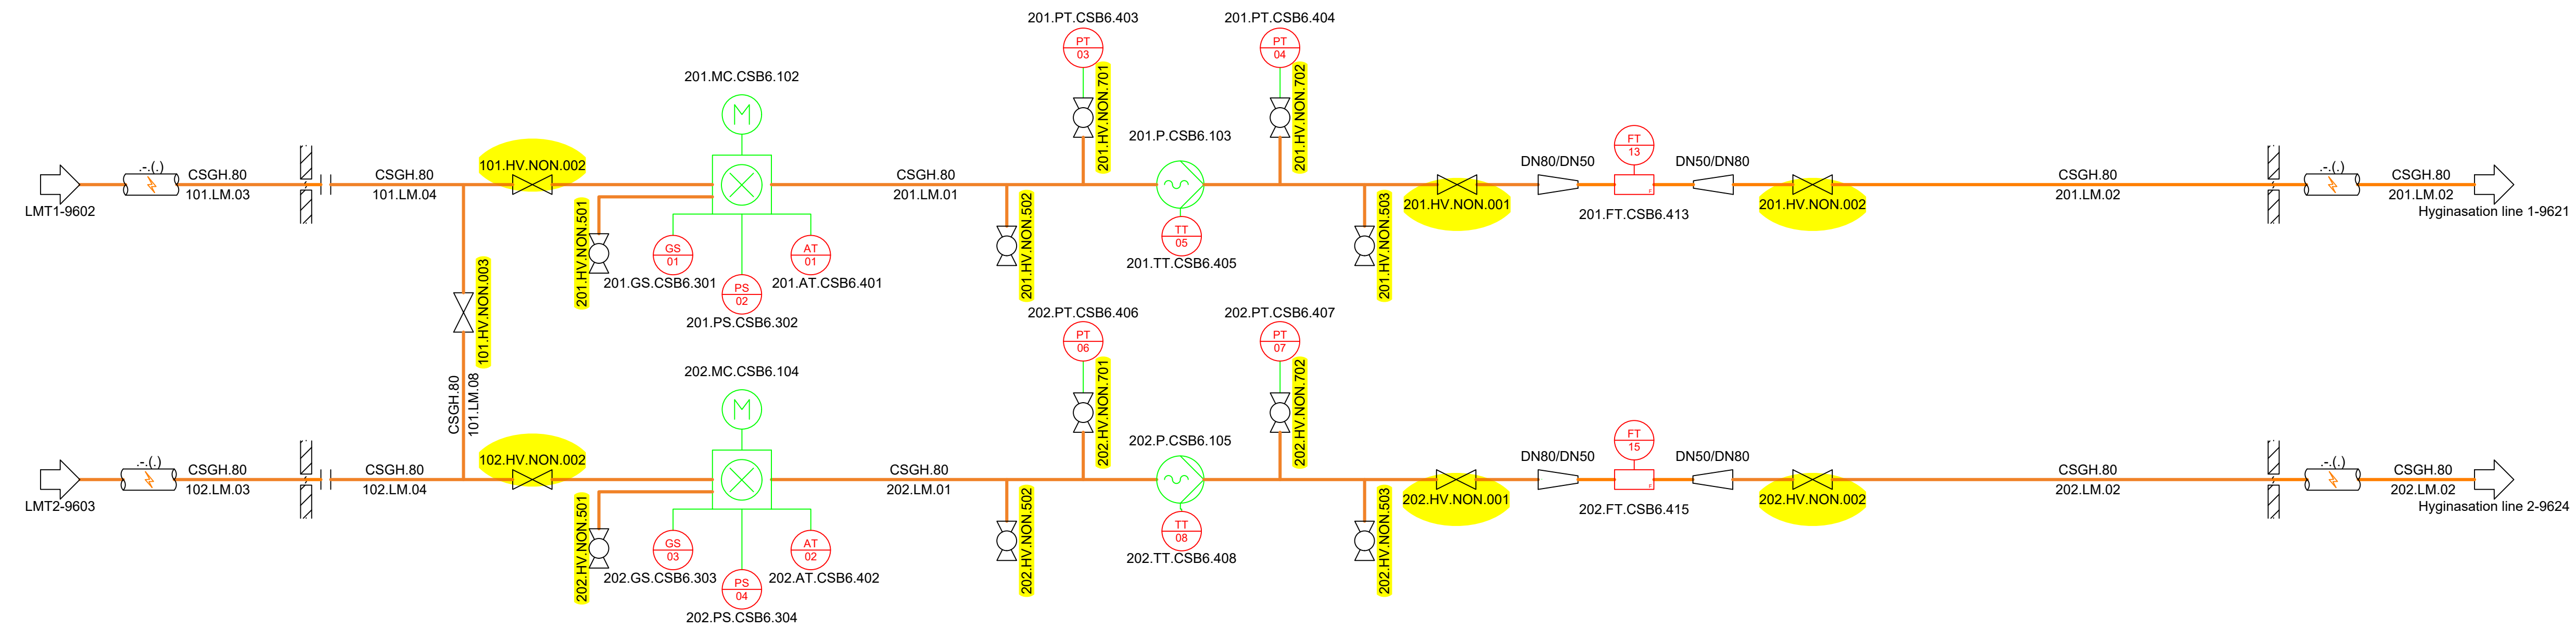



Tech
building


SB-building

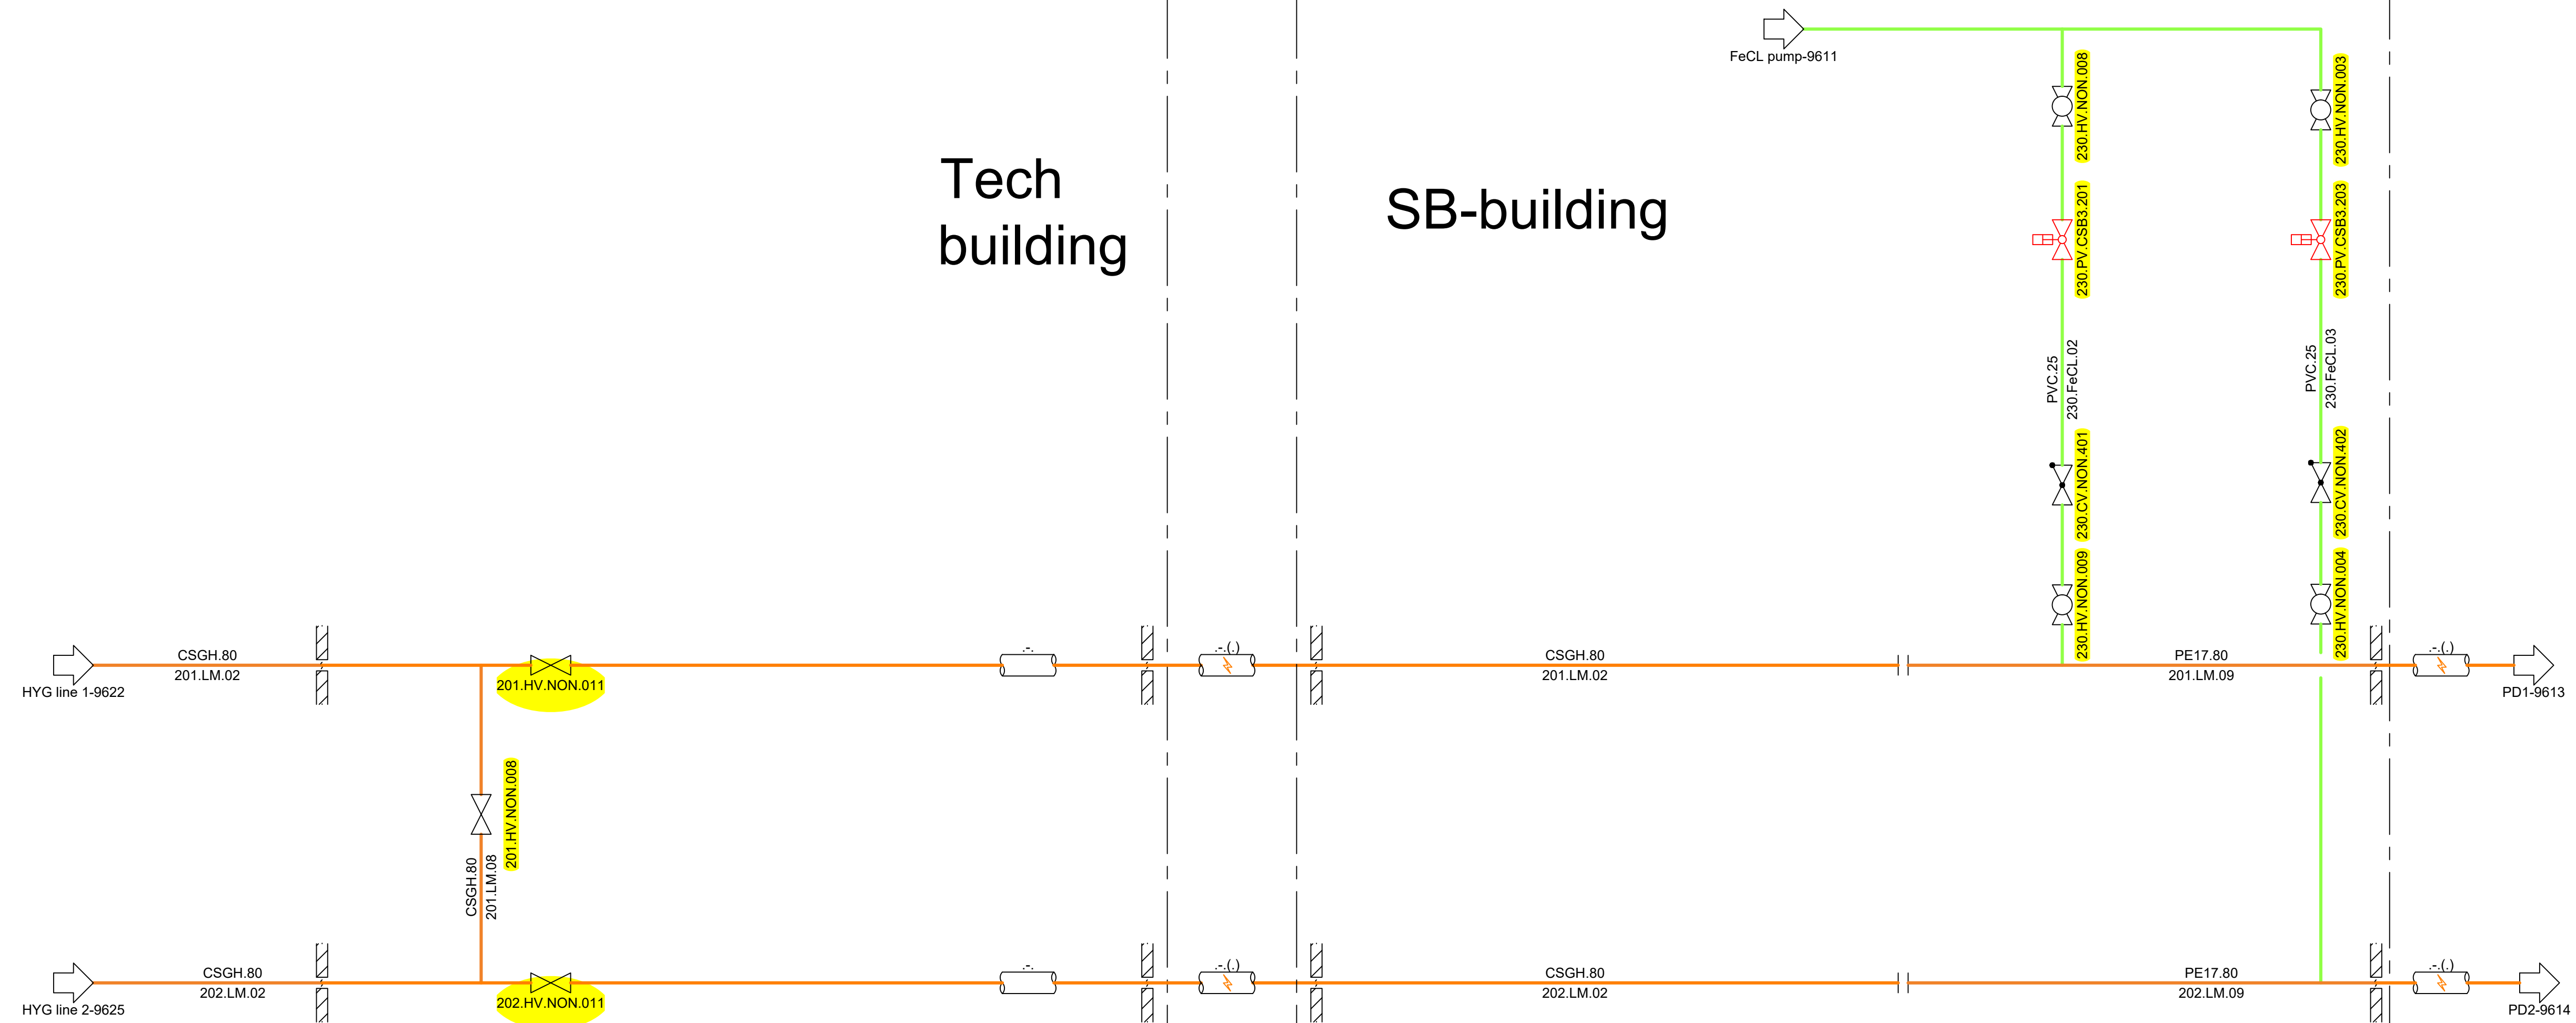


Rev. Nr.:	Rev. Dato:	Rev. Description:	
Builder:	ST1		
Project:	SLK		
Subject:	Liquid manure pump		
Rev. 6			
Int.: MDC	QC.CM	APP.:	Date: 15-10-2025
LUNDSBY RENEWABLE SOLUTIONS			Lundsby Renewable Solutions A/S, Hjarbækvej 65, 8831 Lægstrup Tlf.: +45 96 49 43 00 Info@lundsby.dk This Drawing is subject to copyright and may not be reproduced without permission from Lundsby Renewable Solutions A/S
Project nr.: 1768 Drawing nr.: 9612			FORMAT: A1

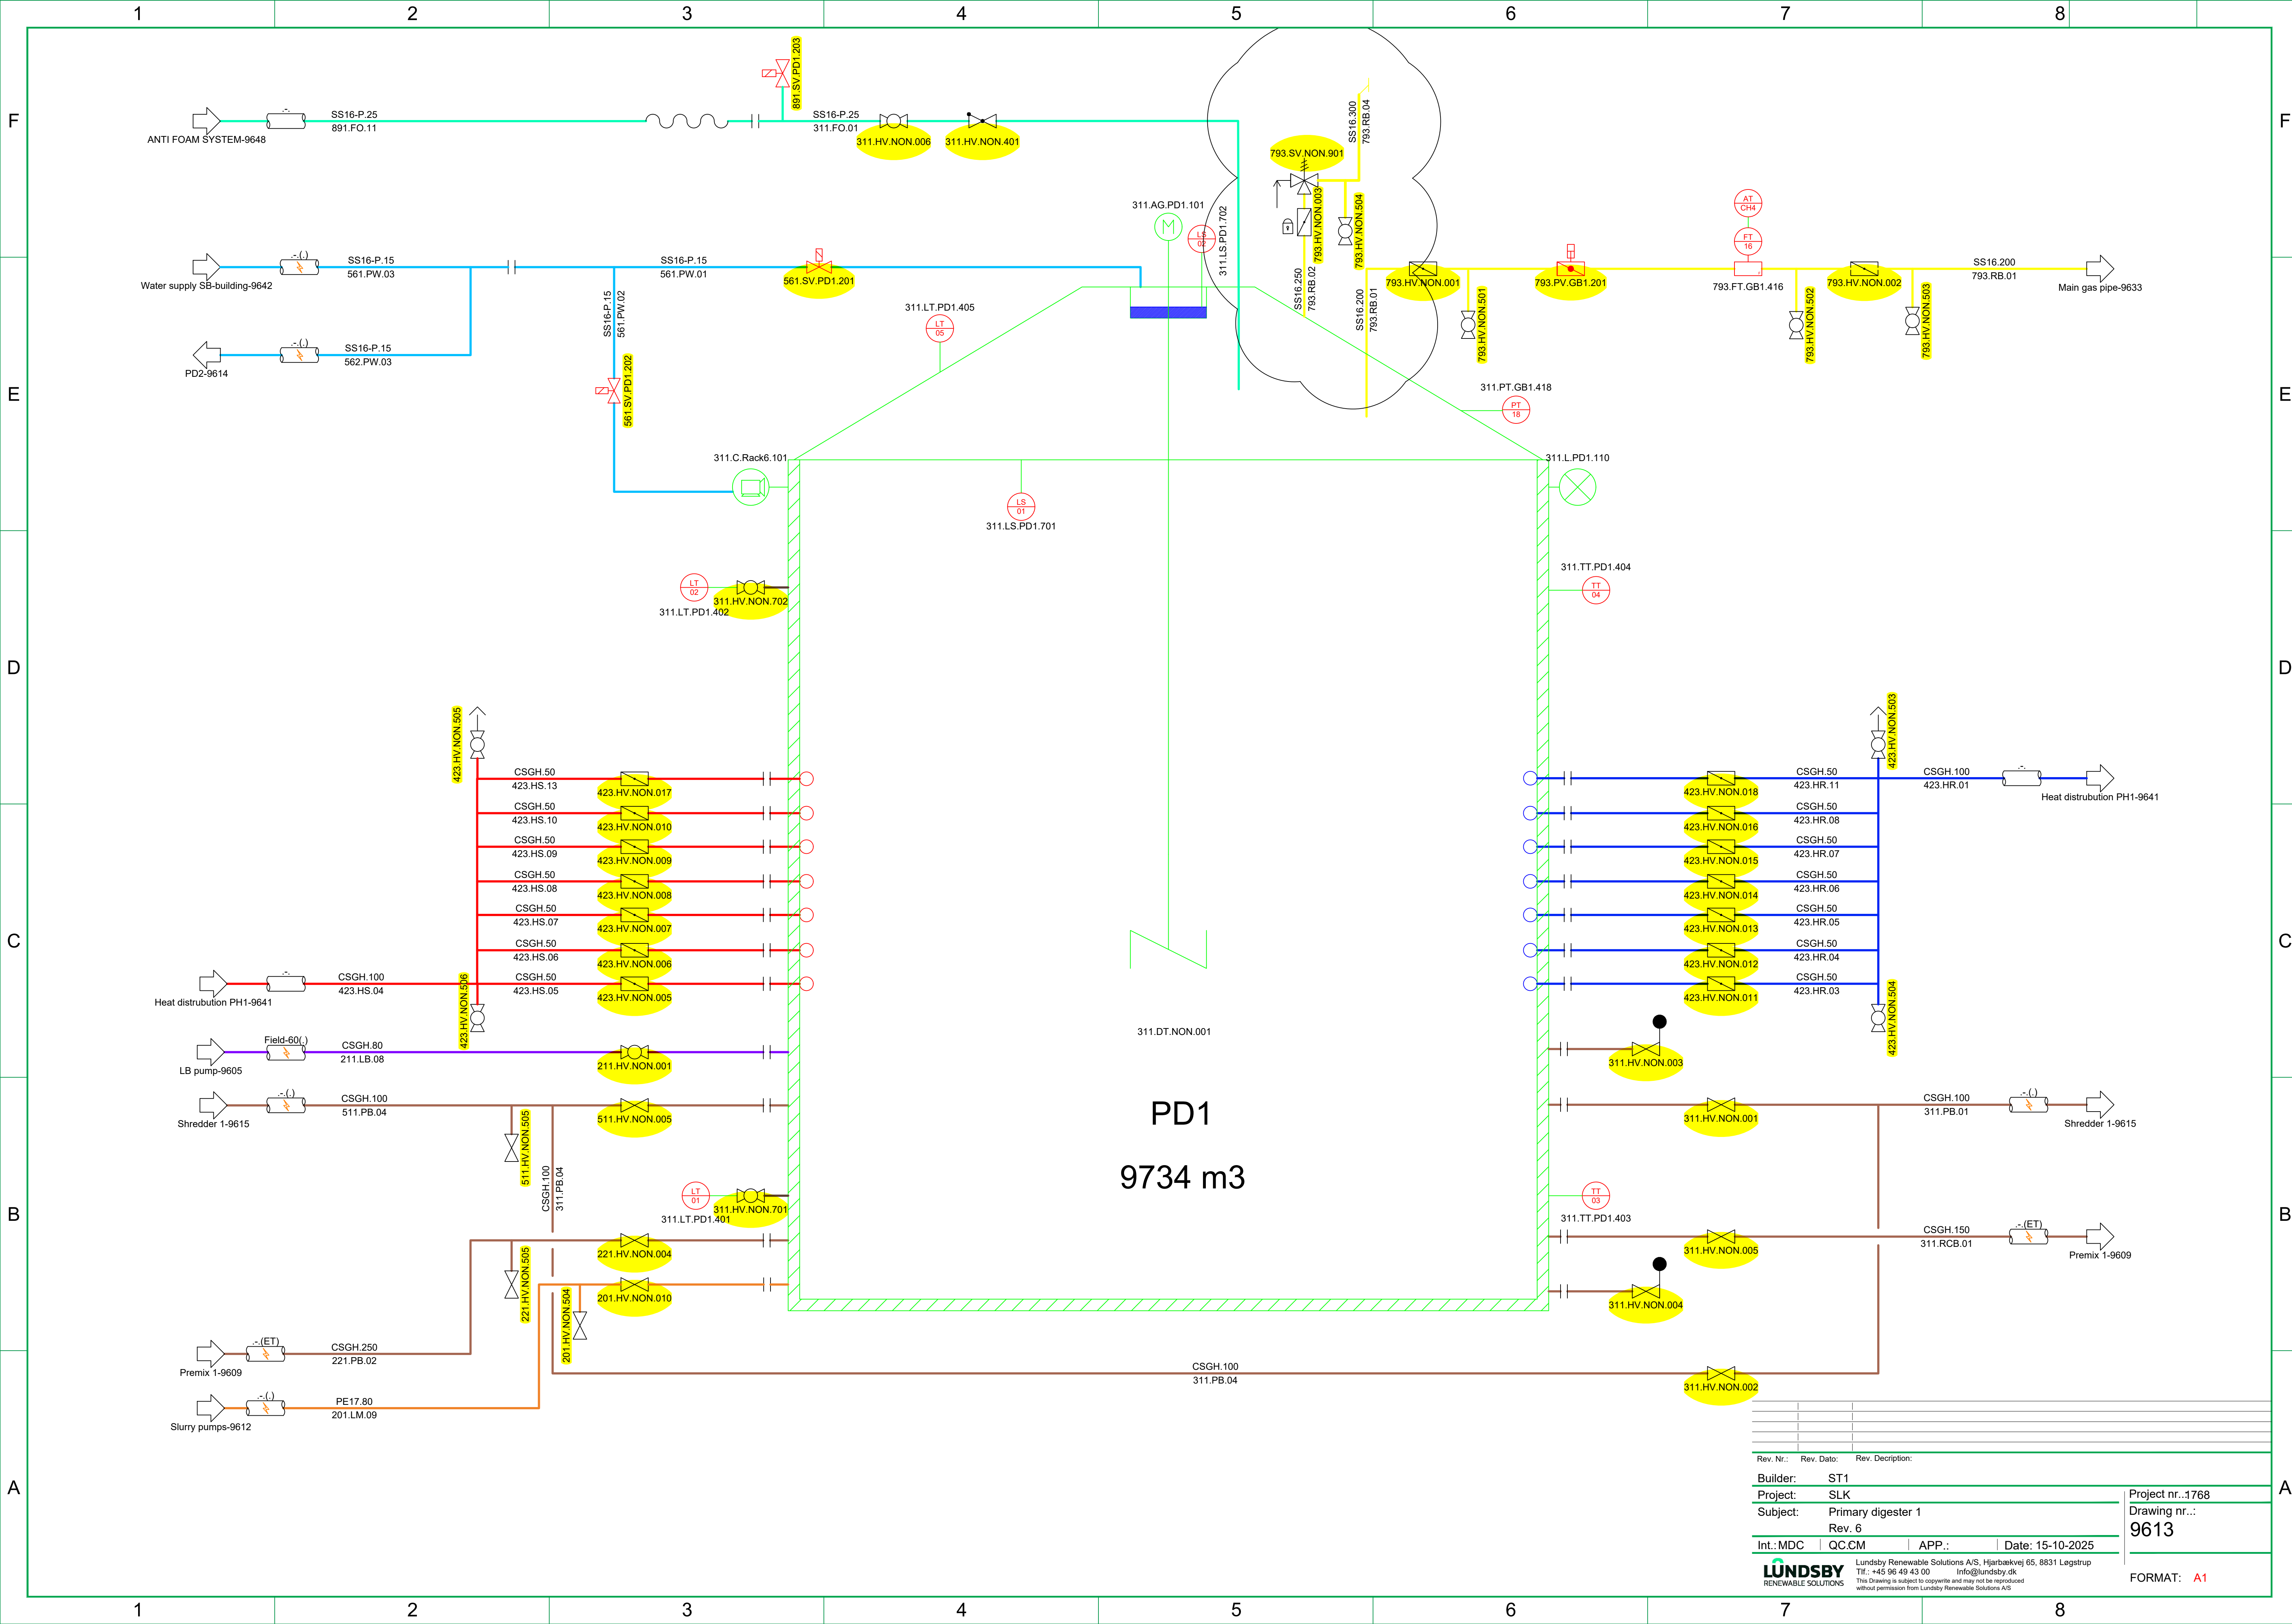

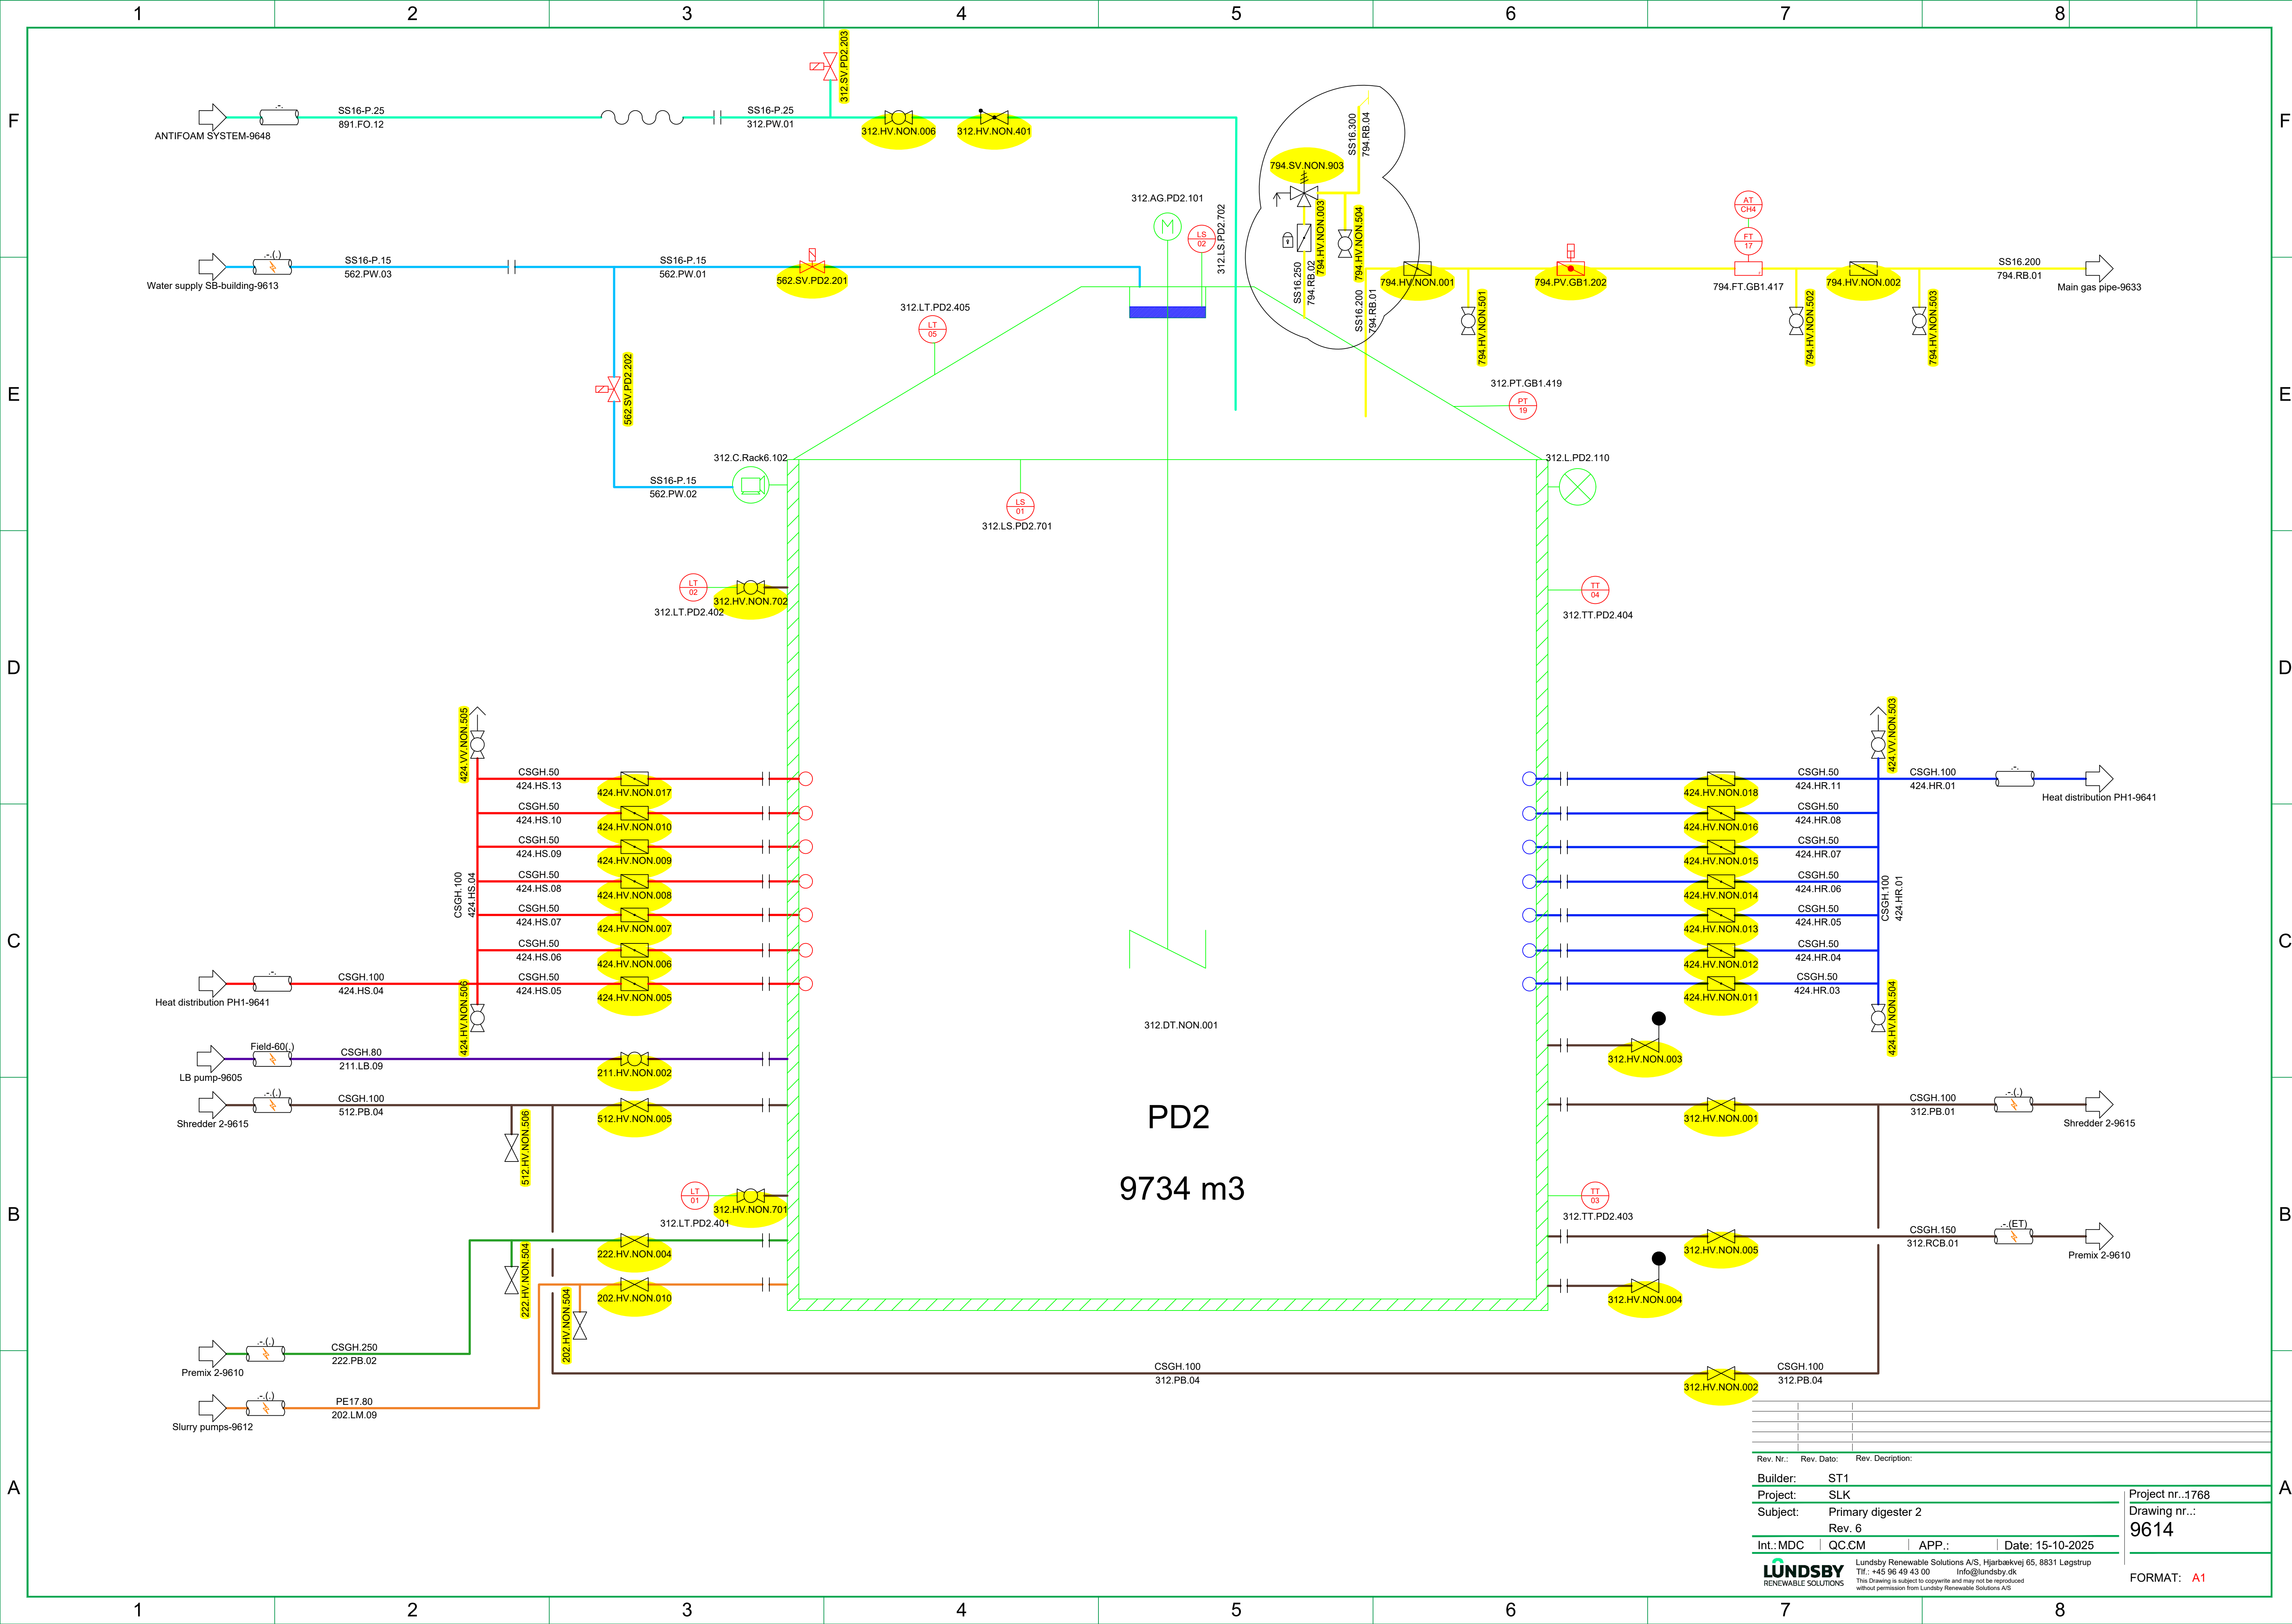


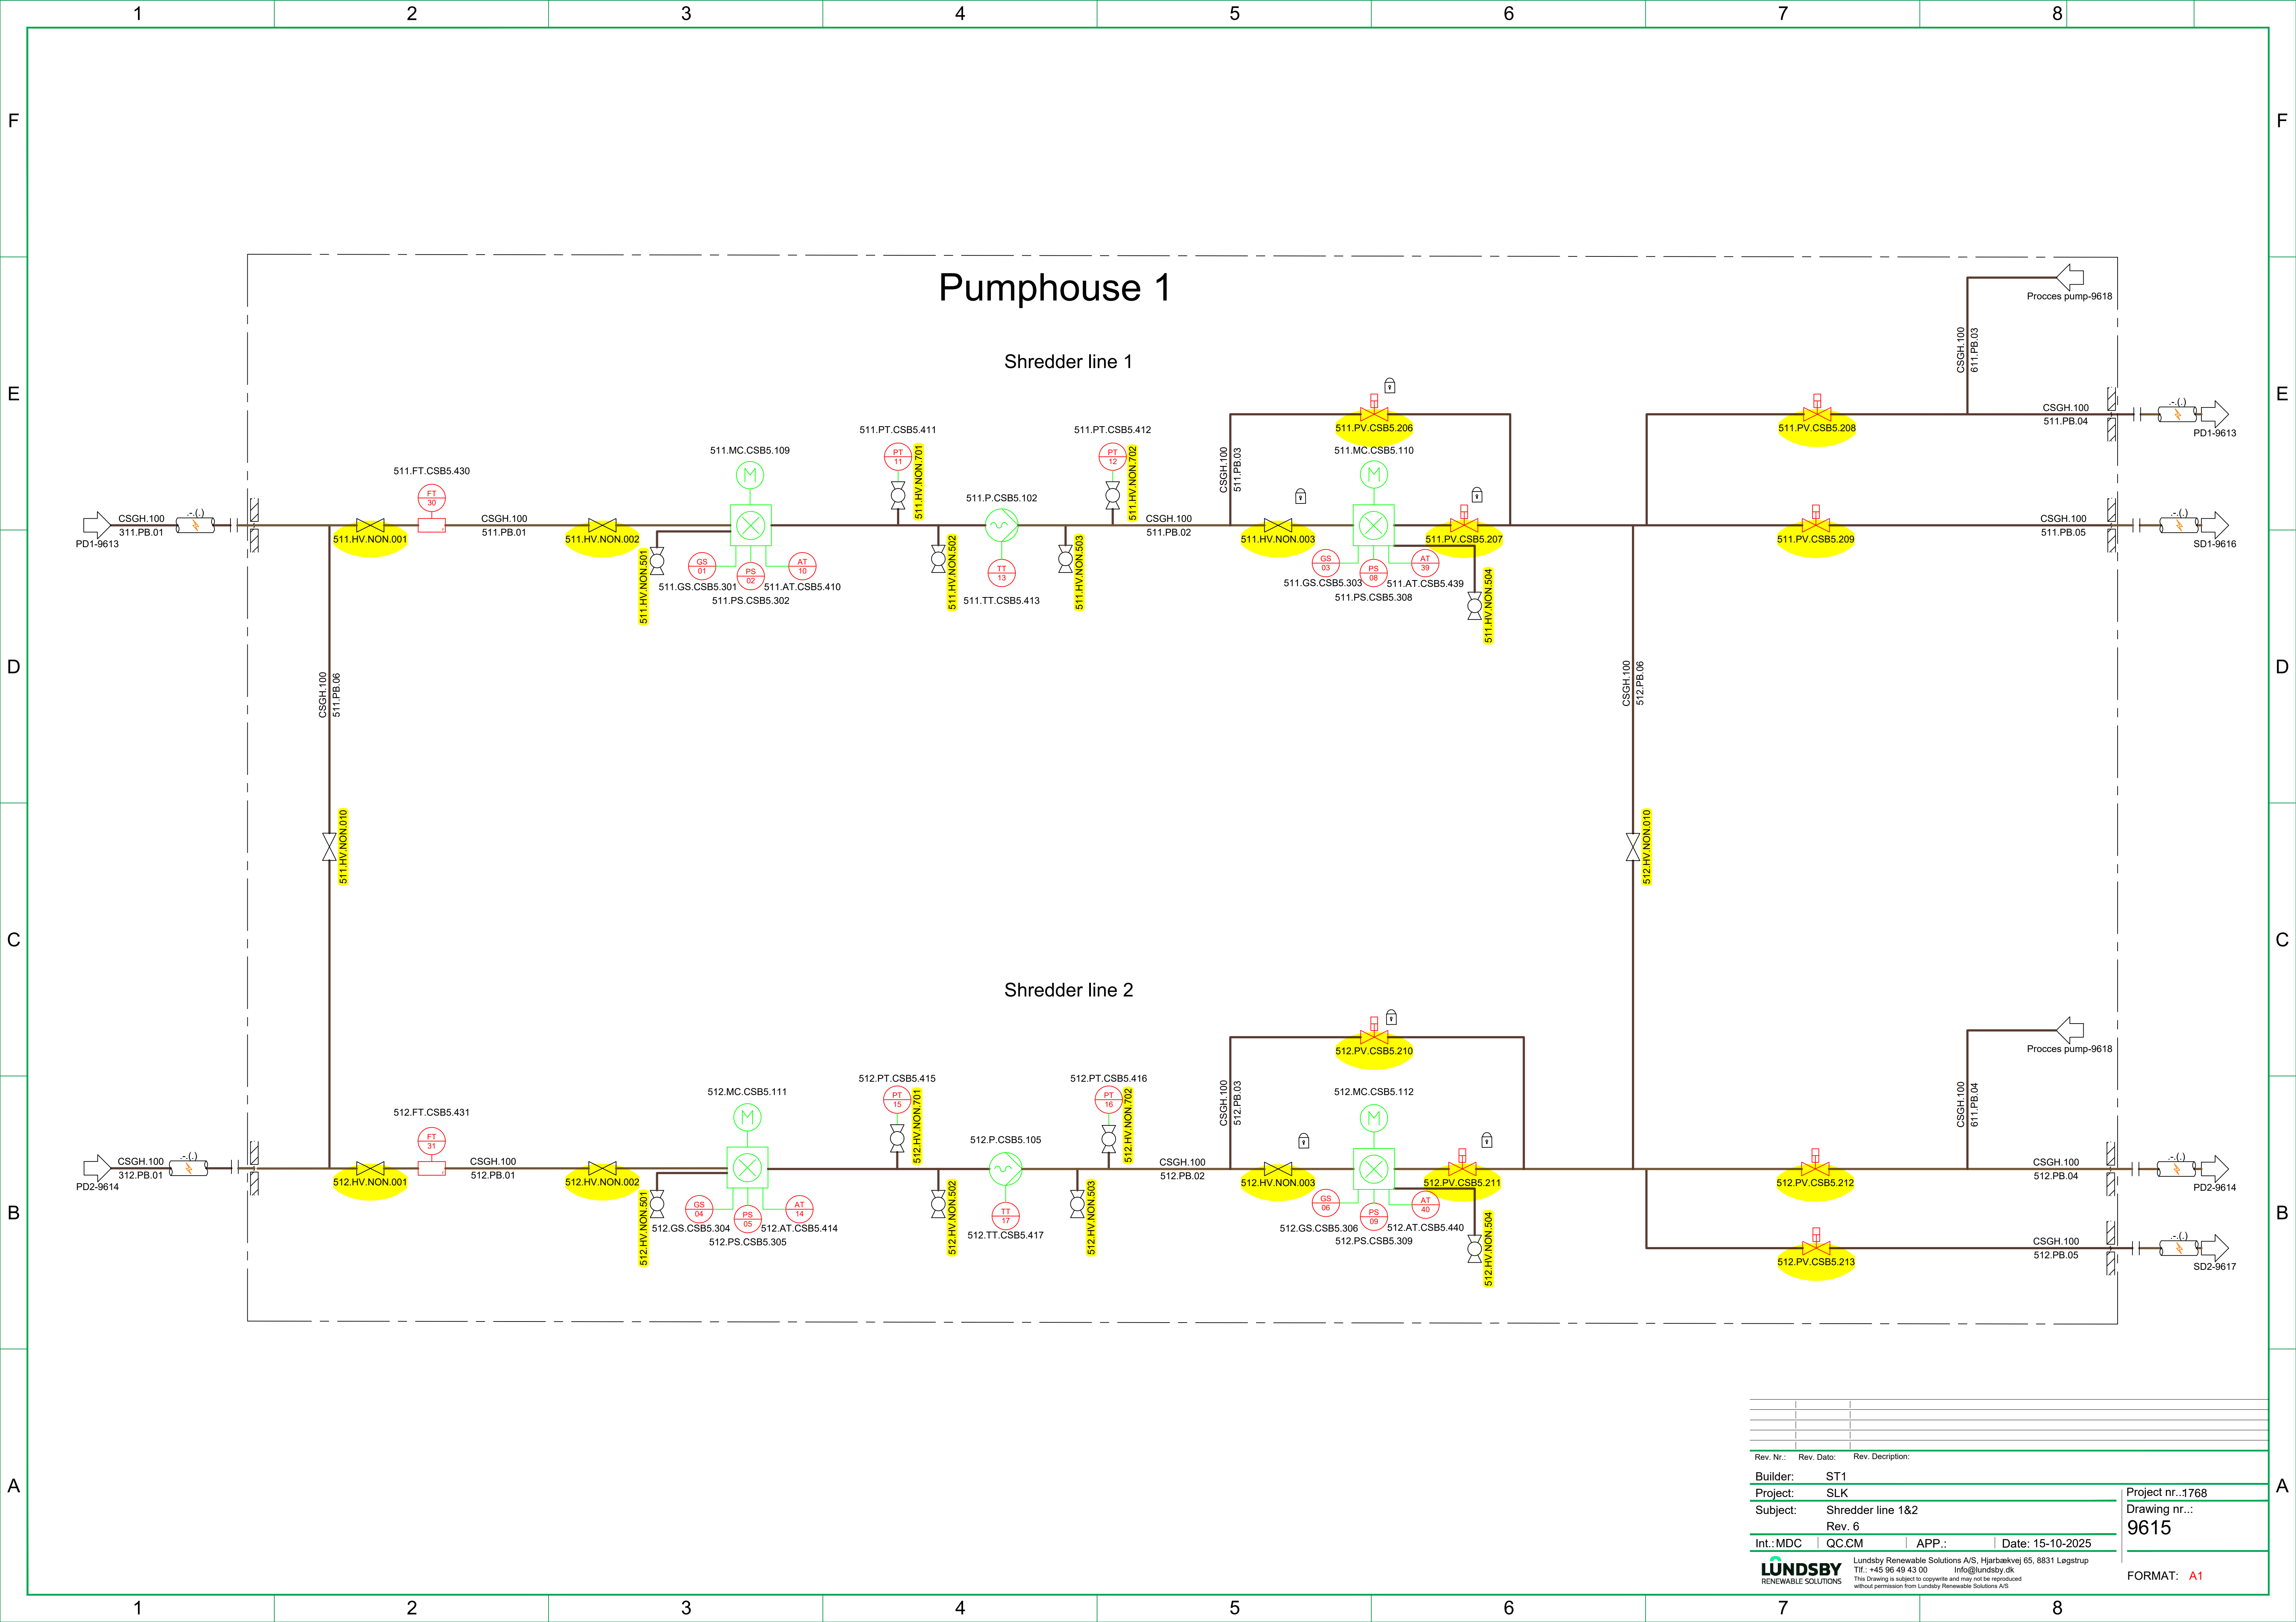


Rev. Nr.:	Rev. Dato:	Rev. Description:
Builder:	ST1	
Project:	SLK	
Subject:	Shredder line 1&2	
Rev. 6		
Int.:MDC	QC:CM	APP.:Date: 15-10-2025
LUNDSBY RENEWABLE SOLUTIONS		
Lundsby Renewable Solutions A/S, Hjarbækvej 65, 8831 Lægstrup Tlf.: +45 96 49 43 00 Info@lundsby.dk This Drawing is subject to copyright and may not be reproduced without permission from Lundsby Renewable Solutions A/S		
Project nr.:1768 Drawing nr.: 9615		FORMAT: A1

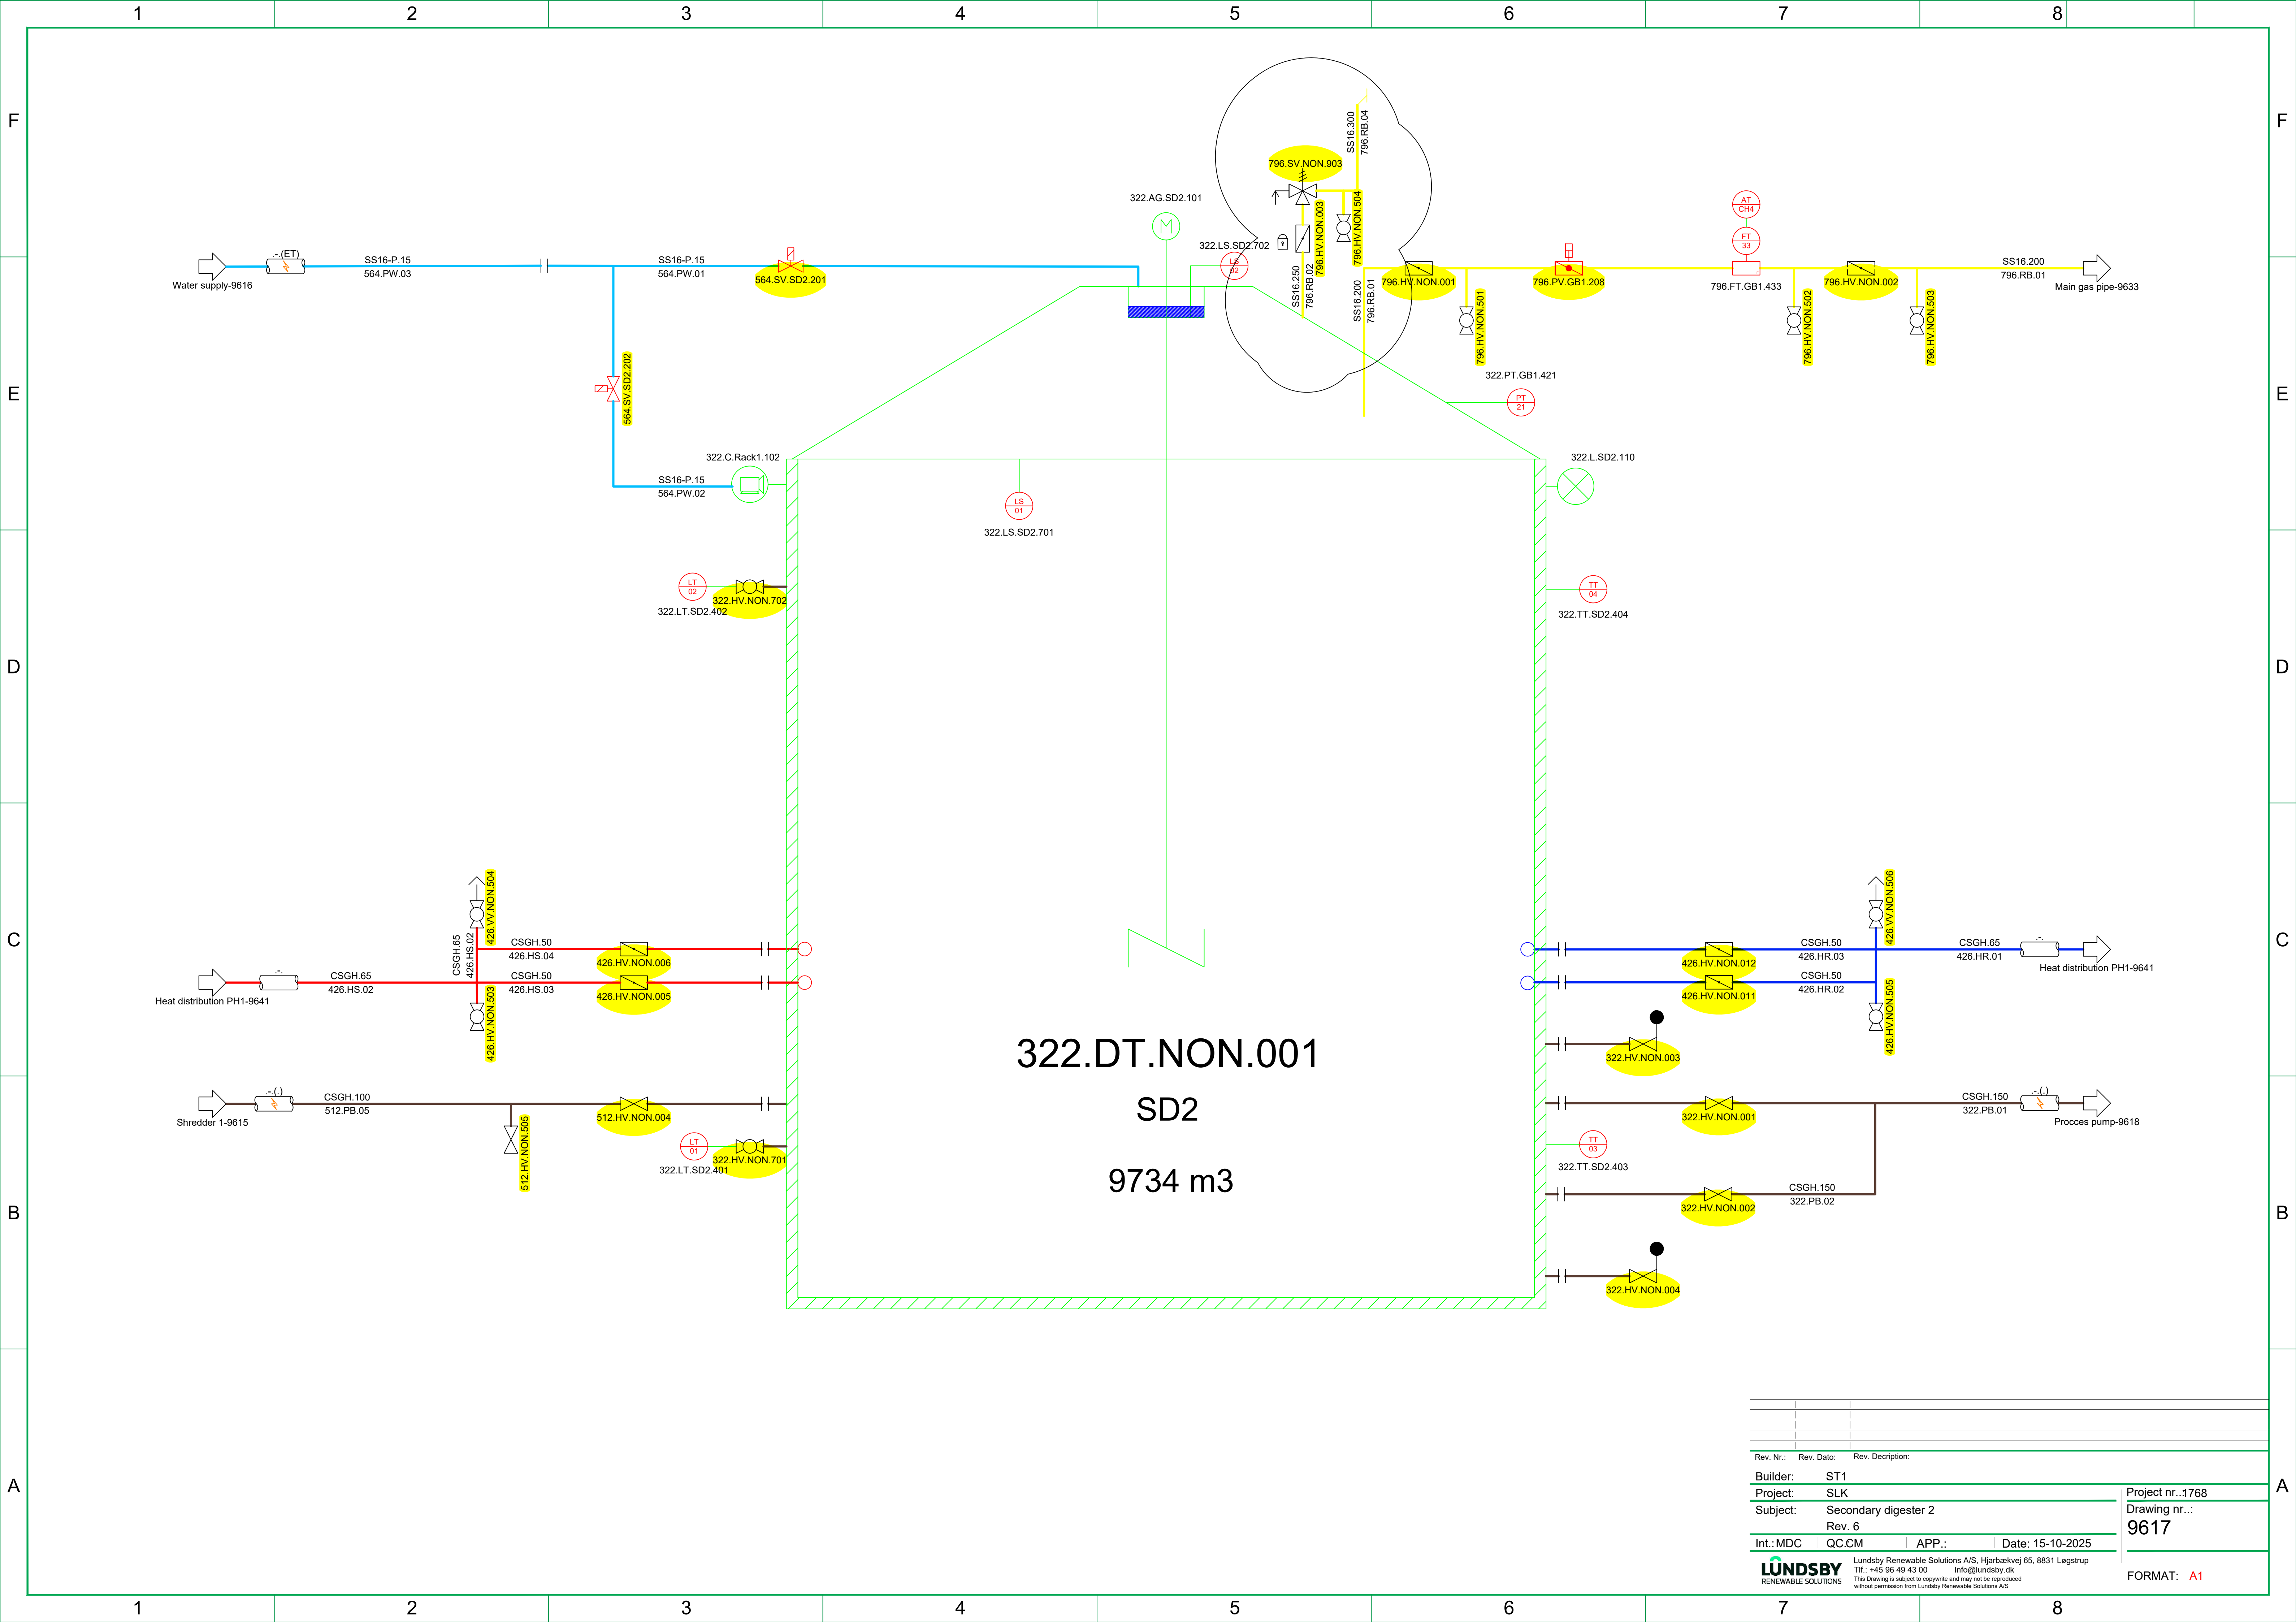

Rev. Nr.:	Rev. Dato:	Rev. Description:
Builder:	ST1	
Project:	SLK	
Subject:	Secondary digester 2	
Rev. 6		
Int.:MDC	QC:CM	APP.:Date: 15-10-2025
LUNDSBY RENEWABLE SOLUTIONS		
Lundsgby Renewable Solutions A/S, Hjarbrækvej 65, 8831 Lægstrup Tlf.: +45 96 49 43 00 Info@lundsgby.dk This Drawing is subject to copyright and may not be reproduced without permission from Lundsgby Renewable Solutions A/S		
Project nr.:1768 Drawing nr.: 9617		FORMAT: A1

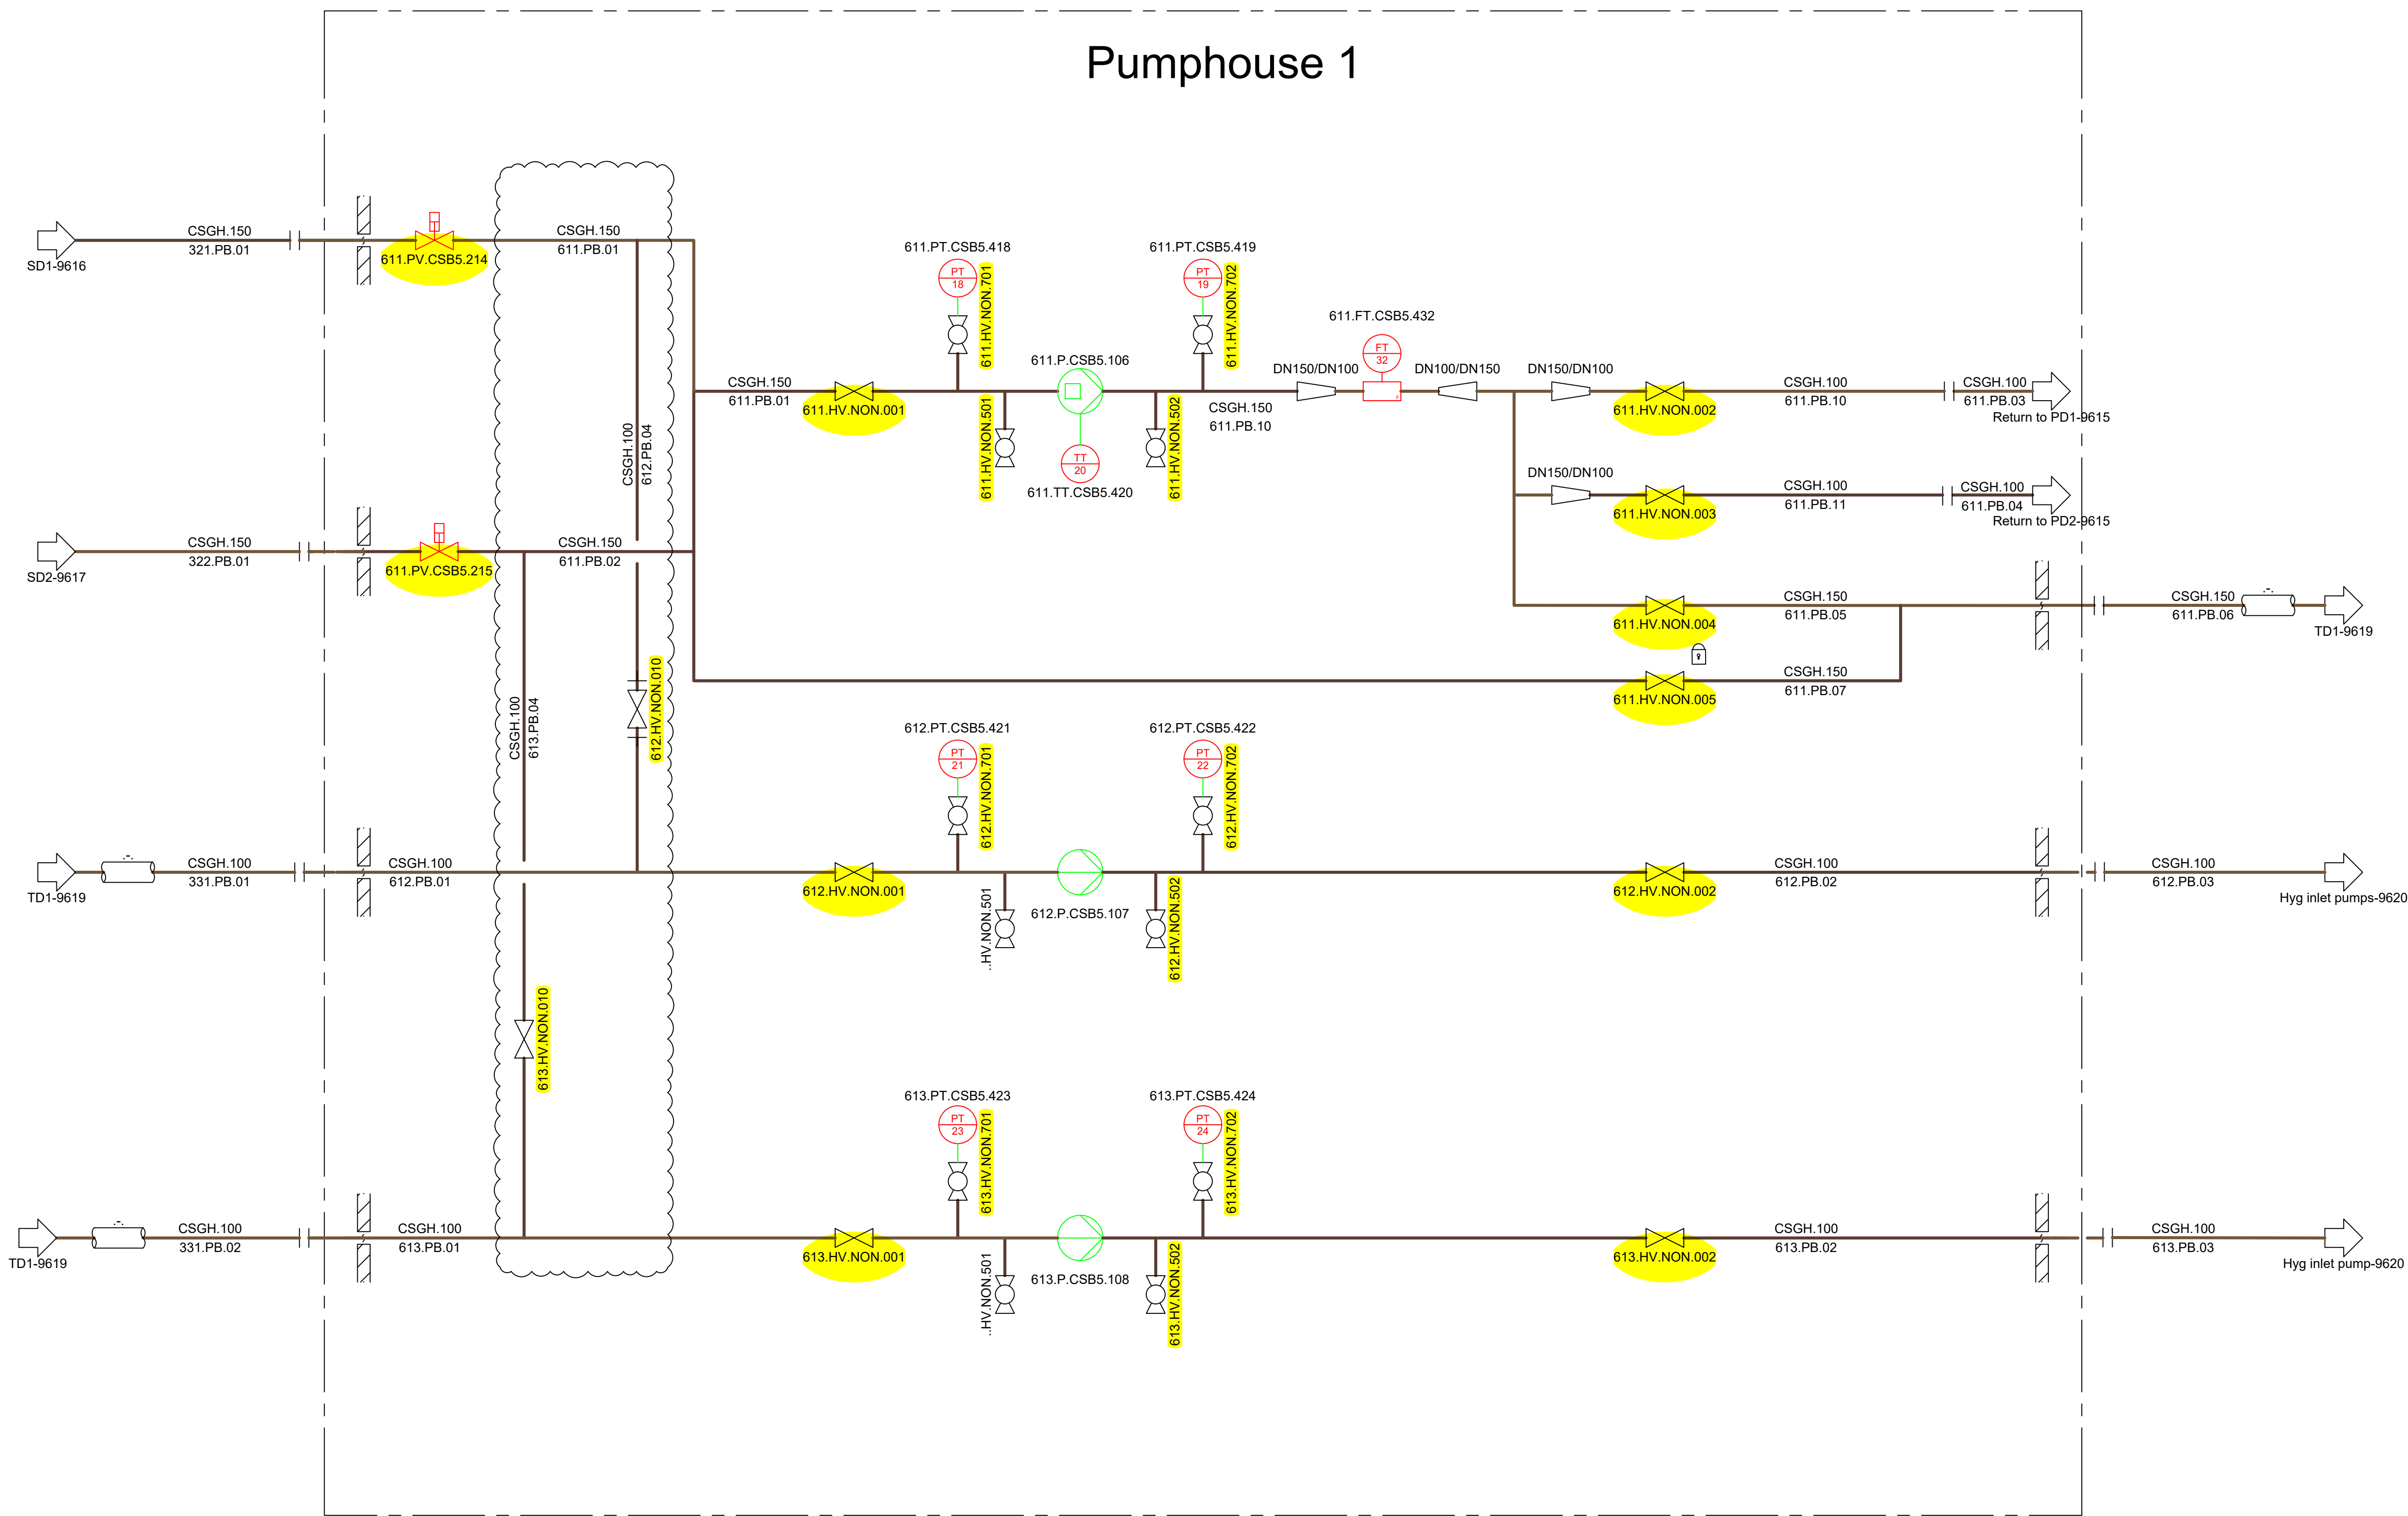


Rev. Nr.:	Rev. Dato:	Rev. Description:	
Builder:	ST1		
Project:	SLK		
Subject:	Procces pumps		
	Rev. 6		
Int.:MDC	QC.CM	APP.:	Date: 15-10-2025
LUNDSBY RENEWABLE SOLUTIONS			Lundsby Renewable Solutions A/S, Hjarbækvej 65, 8831 Løgstrup Tlf.: +45 96 49 43 00 Info@lundsby.dk This Drawing is subject to copyright and may not be reproduced without permission from Lundsby Renewable Solutions A/S
Project nr.:1768 Drawing nr.: 9618			FORMAT: A1

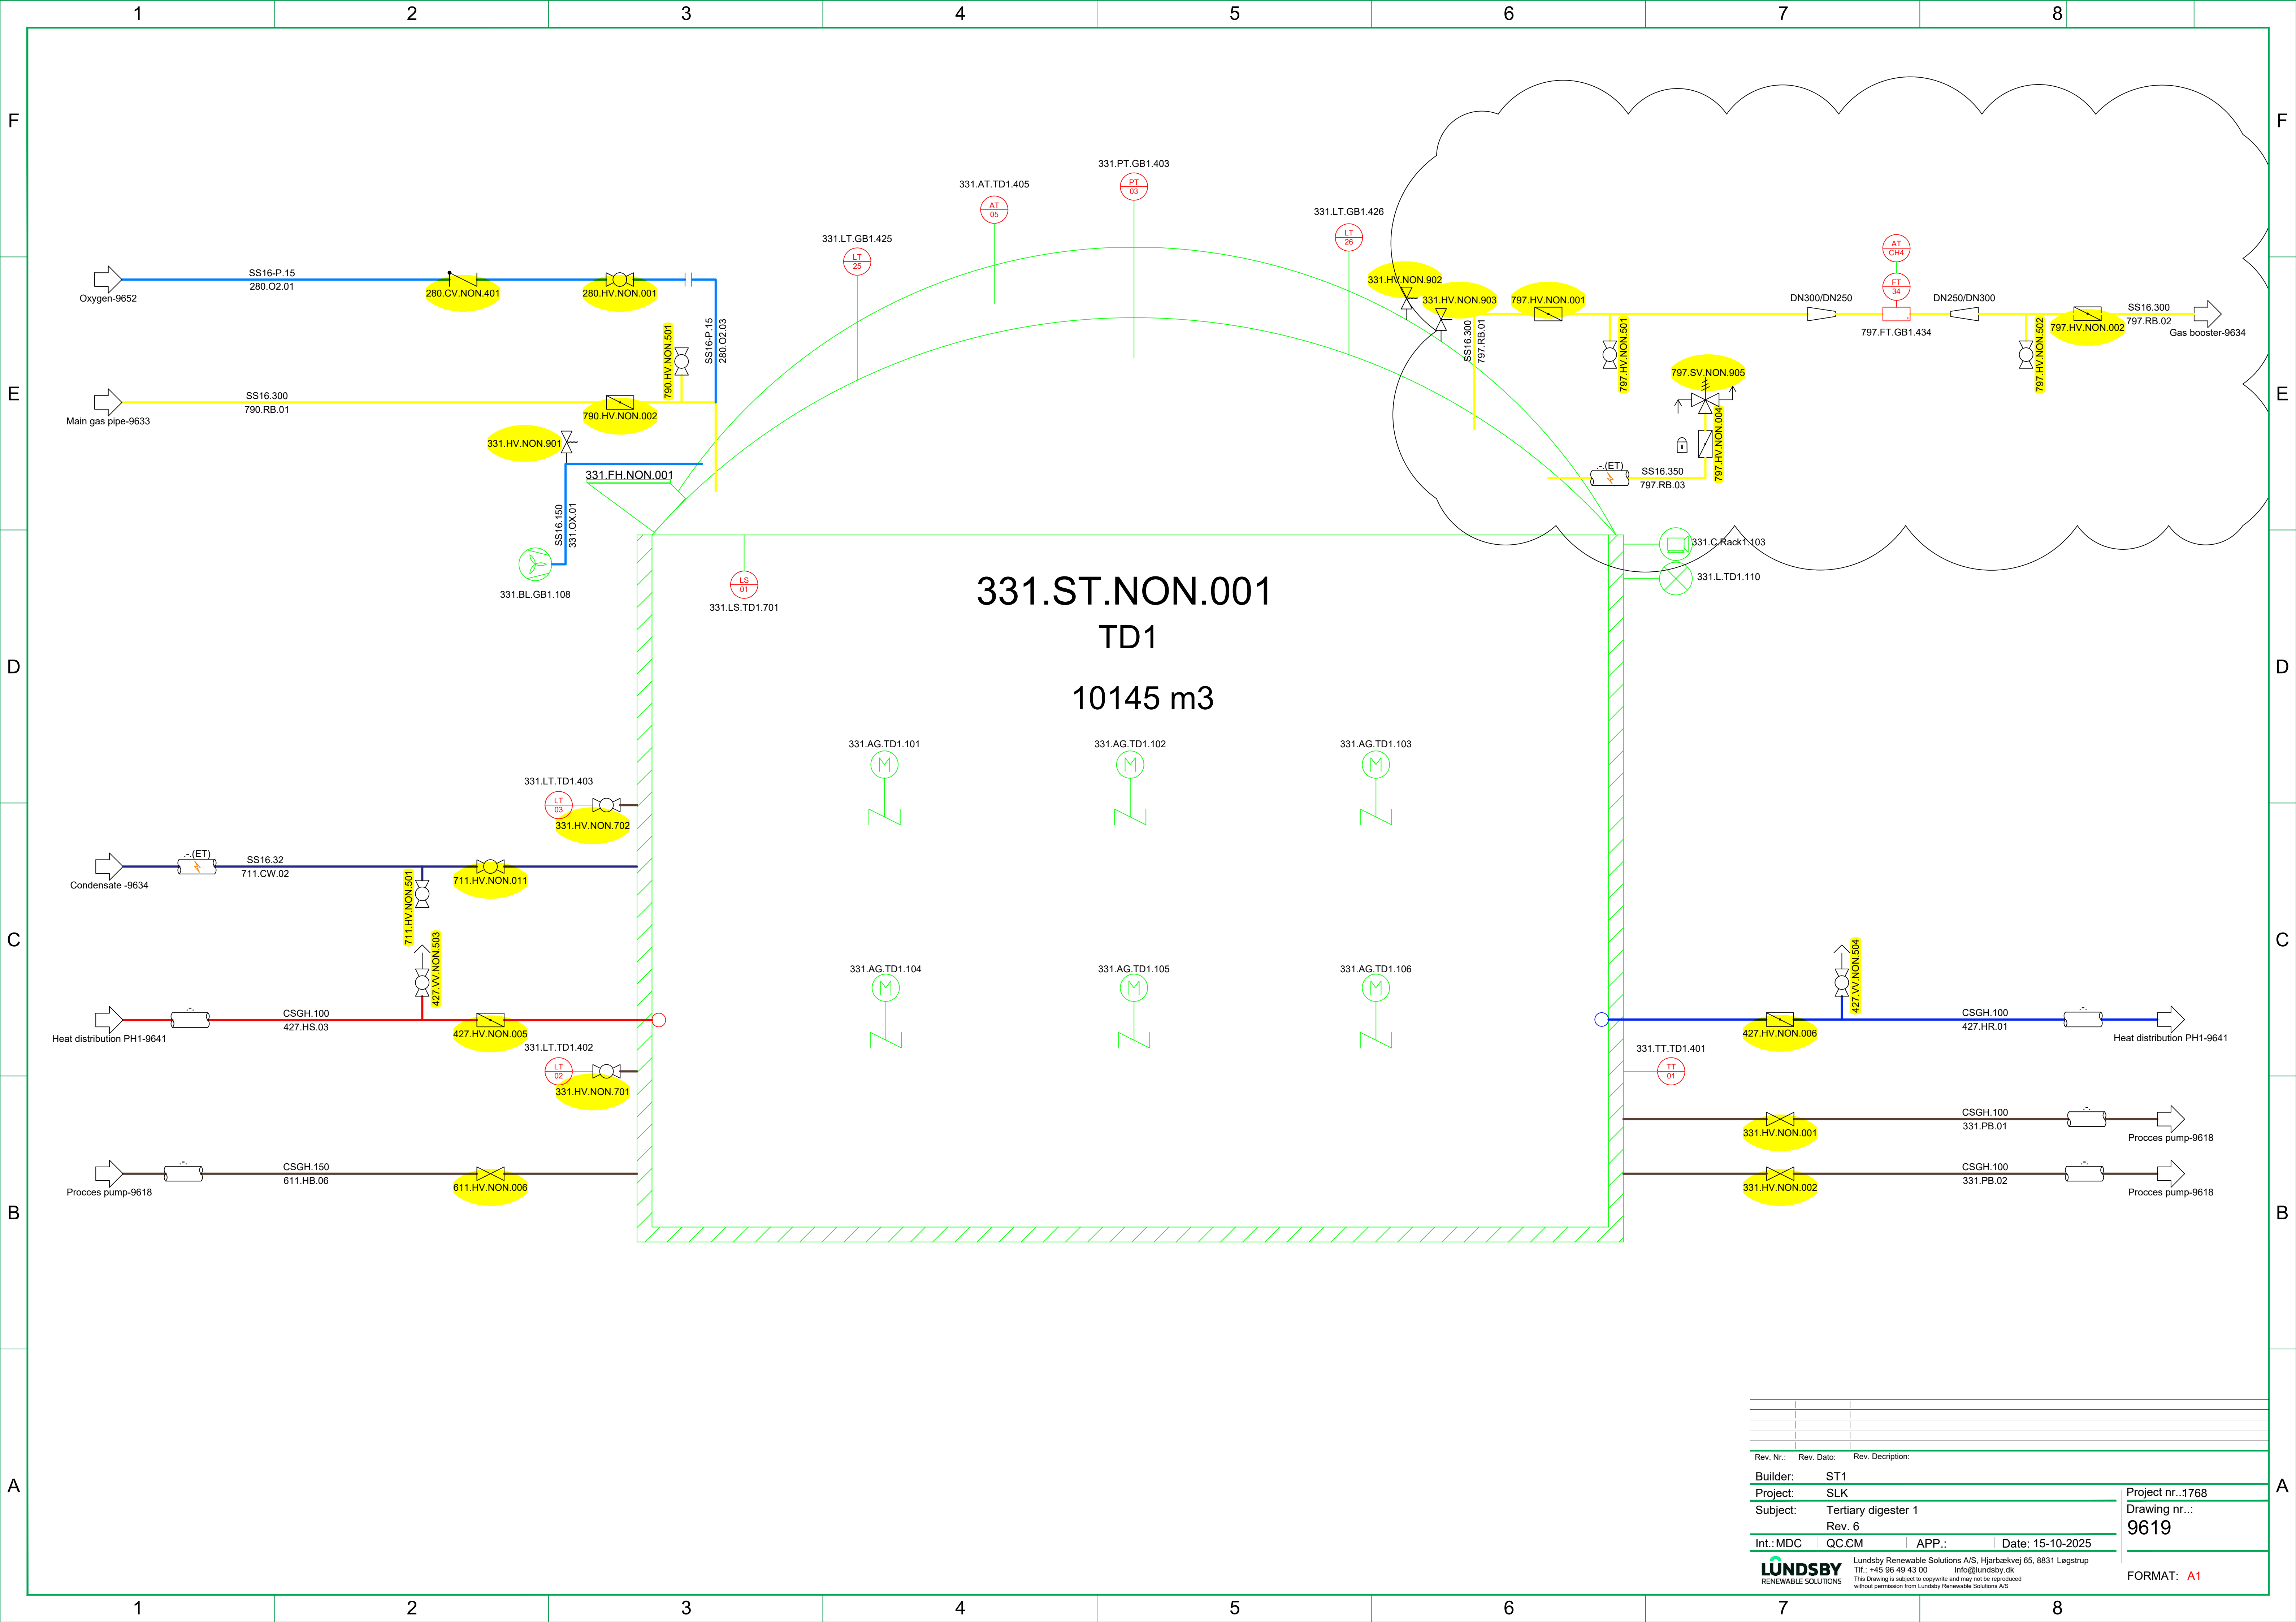


Rev. Nr.:	Rev. Dato:	Rev. Description:			
Builder:	ST1				
Project:	SLK				
Subject:	Tertiary digester 1				
	Rev. 6				
Int.: MDC	QC.M	APP.:		Date: 15-10-2025	
		Lundsby Renewable Solutions A/S, Hjarbækvej 65, 8831 Løgstrup Tlf.: +45 96 49 43 00 info@lundsby.dk This Drawing is subject to copyright and may not be reproduced without permission from Lundsby Renewable Solutions A/S			
		Project nr.: 1768		Drawing nr.: 9619	
		FORMAT: A1			

Tech Building


Inlet pumps

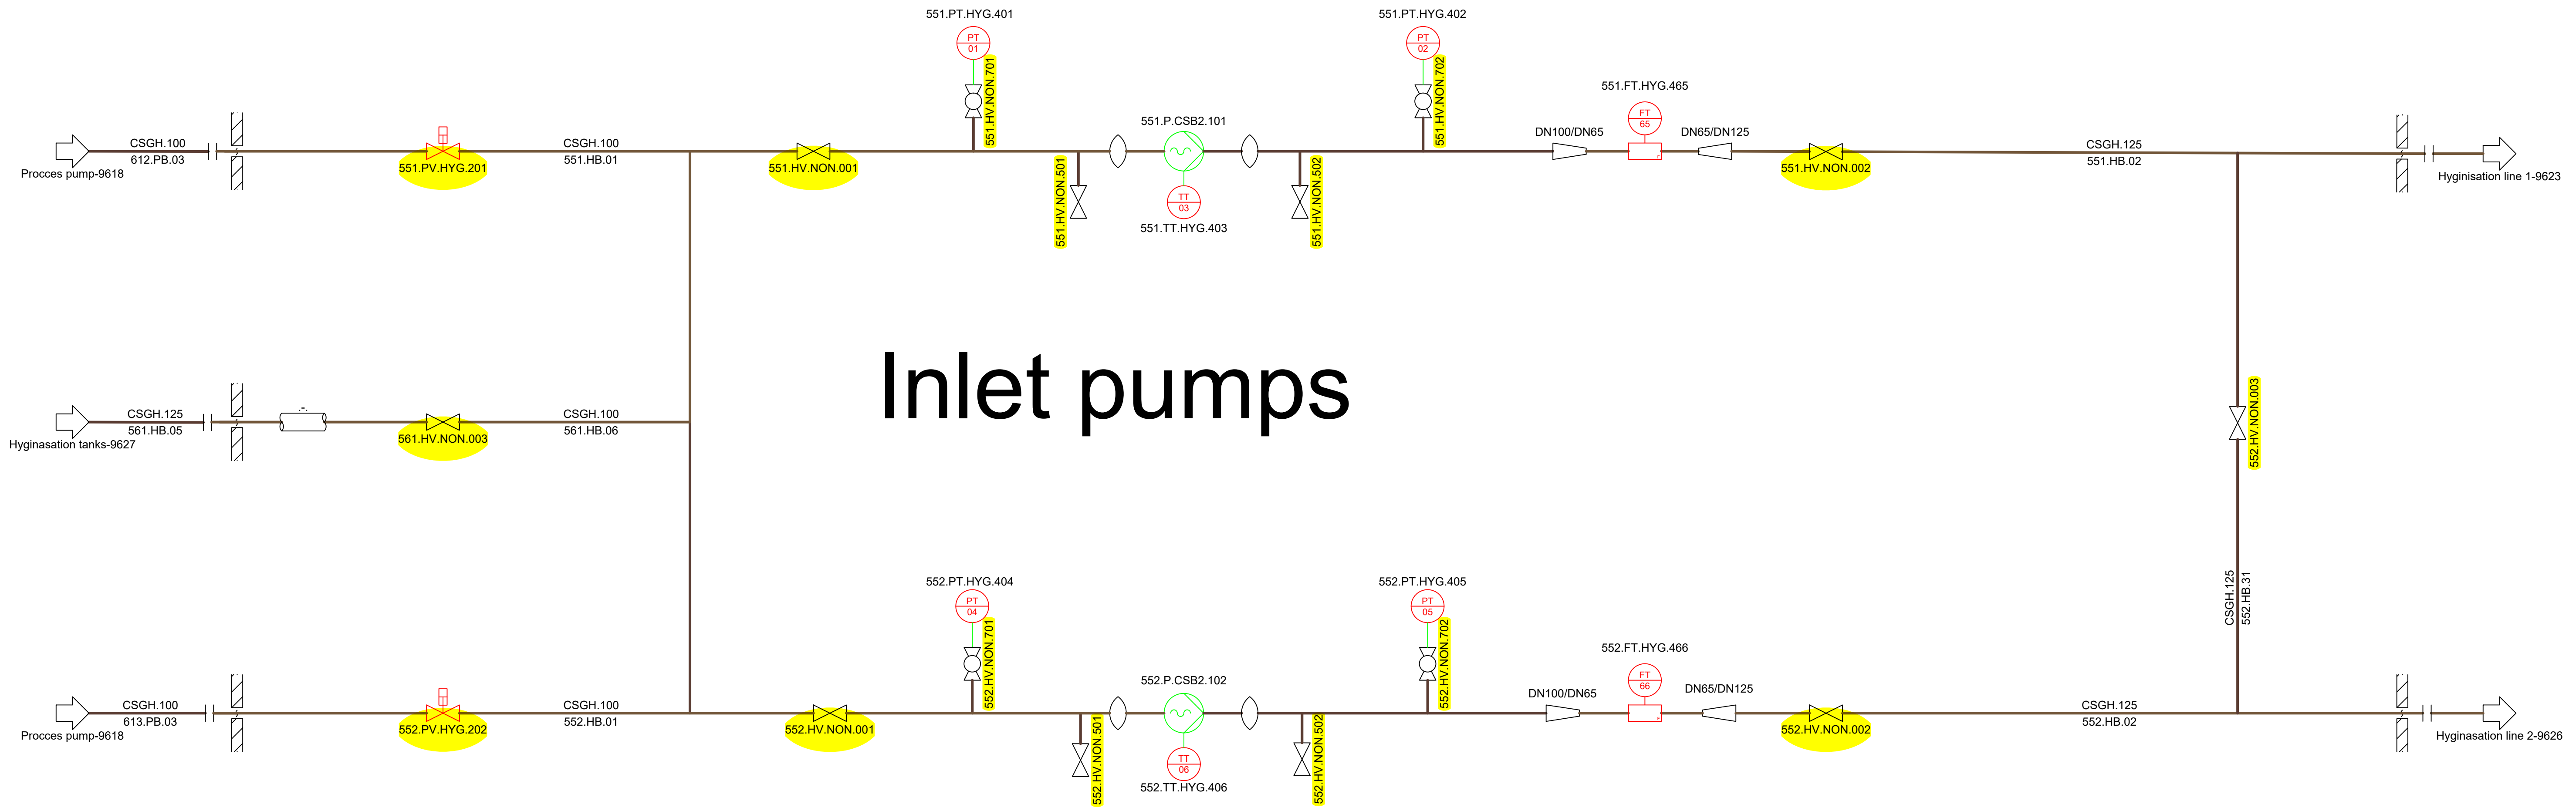


Rev. Nr.:	Rev. Dato:	Rev. Description:	
Builder:	ST1		
Project:	SLK		
Subject:	Hyginisation inlet pumps		
	Rev. 6		
Int.:MDC	QC:CM	APP.:	Date: 15-10-2025
LUNDSBY RENEWABLE SOLUTIONS			Lundsby Renewable Solutions A/S, Hjarbækvej 65, 8831 Lægstrup Tlf.: +45 96 49 43 00 Info@lundsby.dk This Drawing is subject to copyright and may not be reproduced without permission from Lundsby Renewable Solutions A/S
			Project nr.:1768 Drawing nr.: 9620 FORMAT: A1

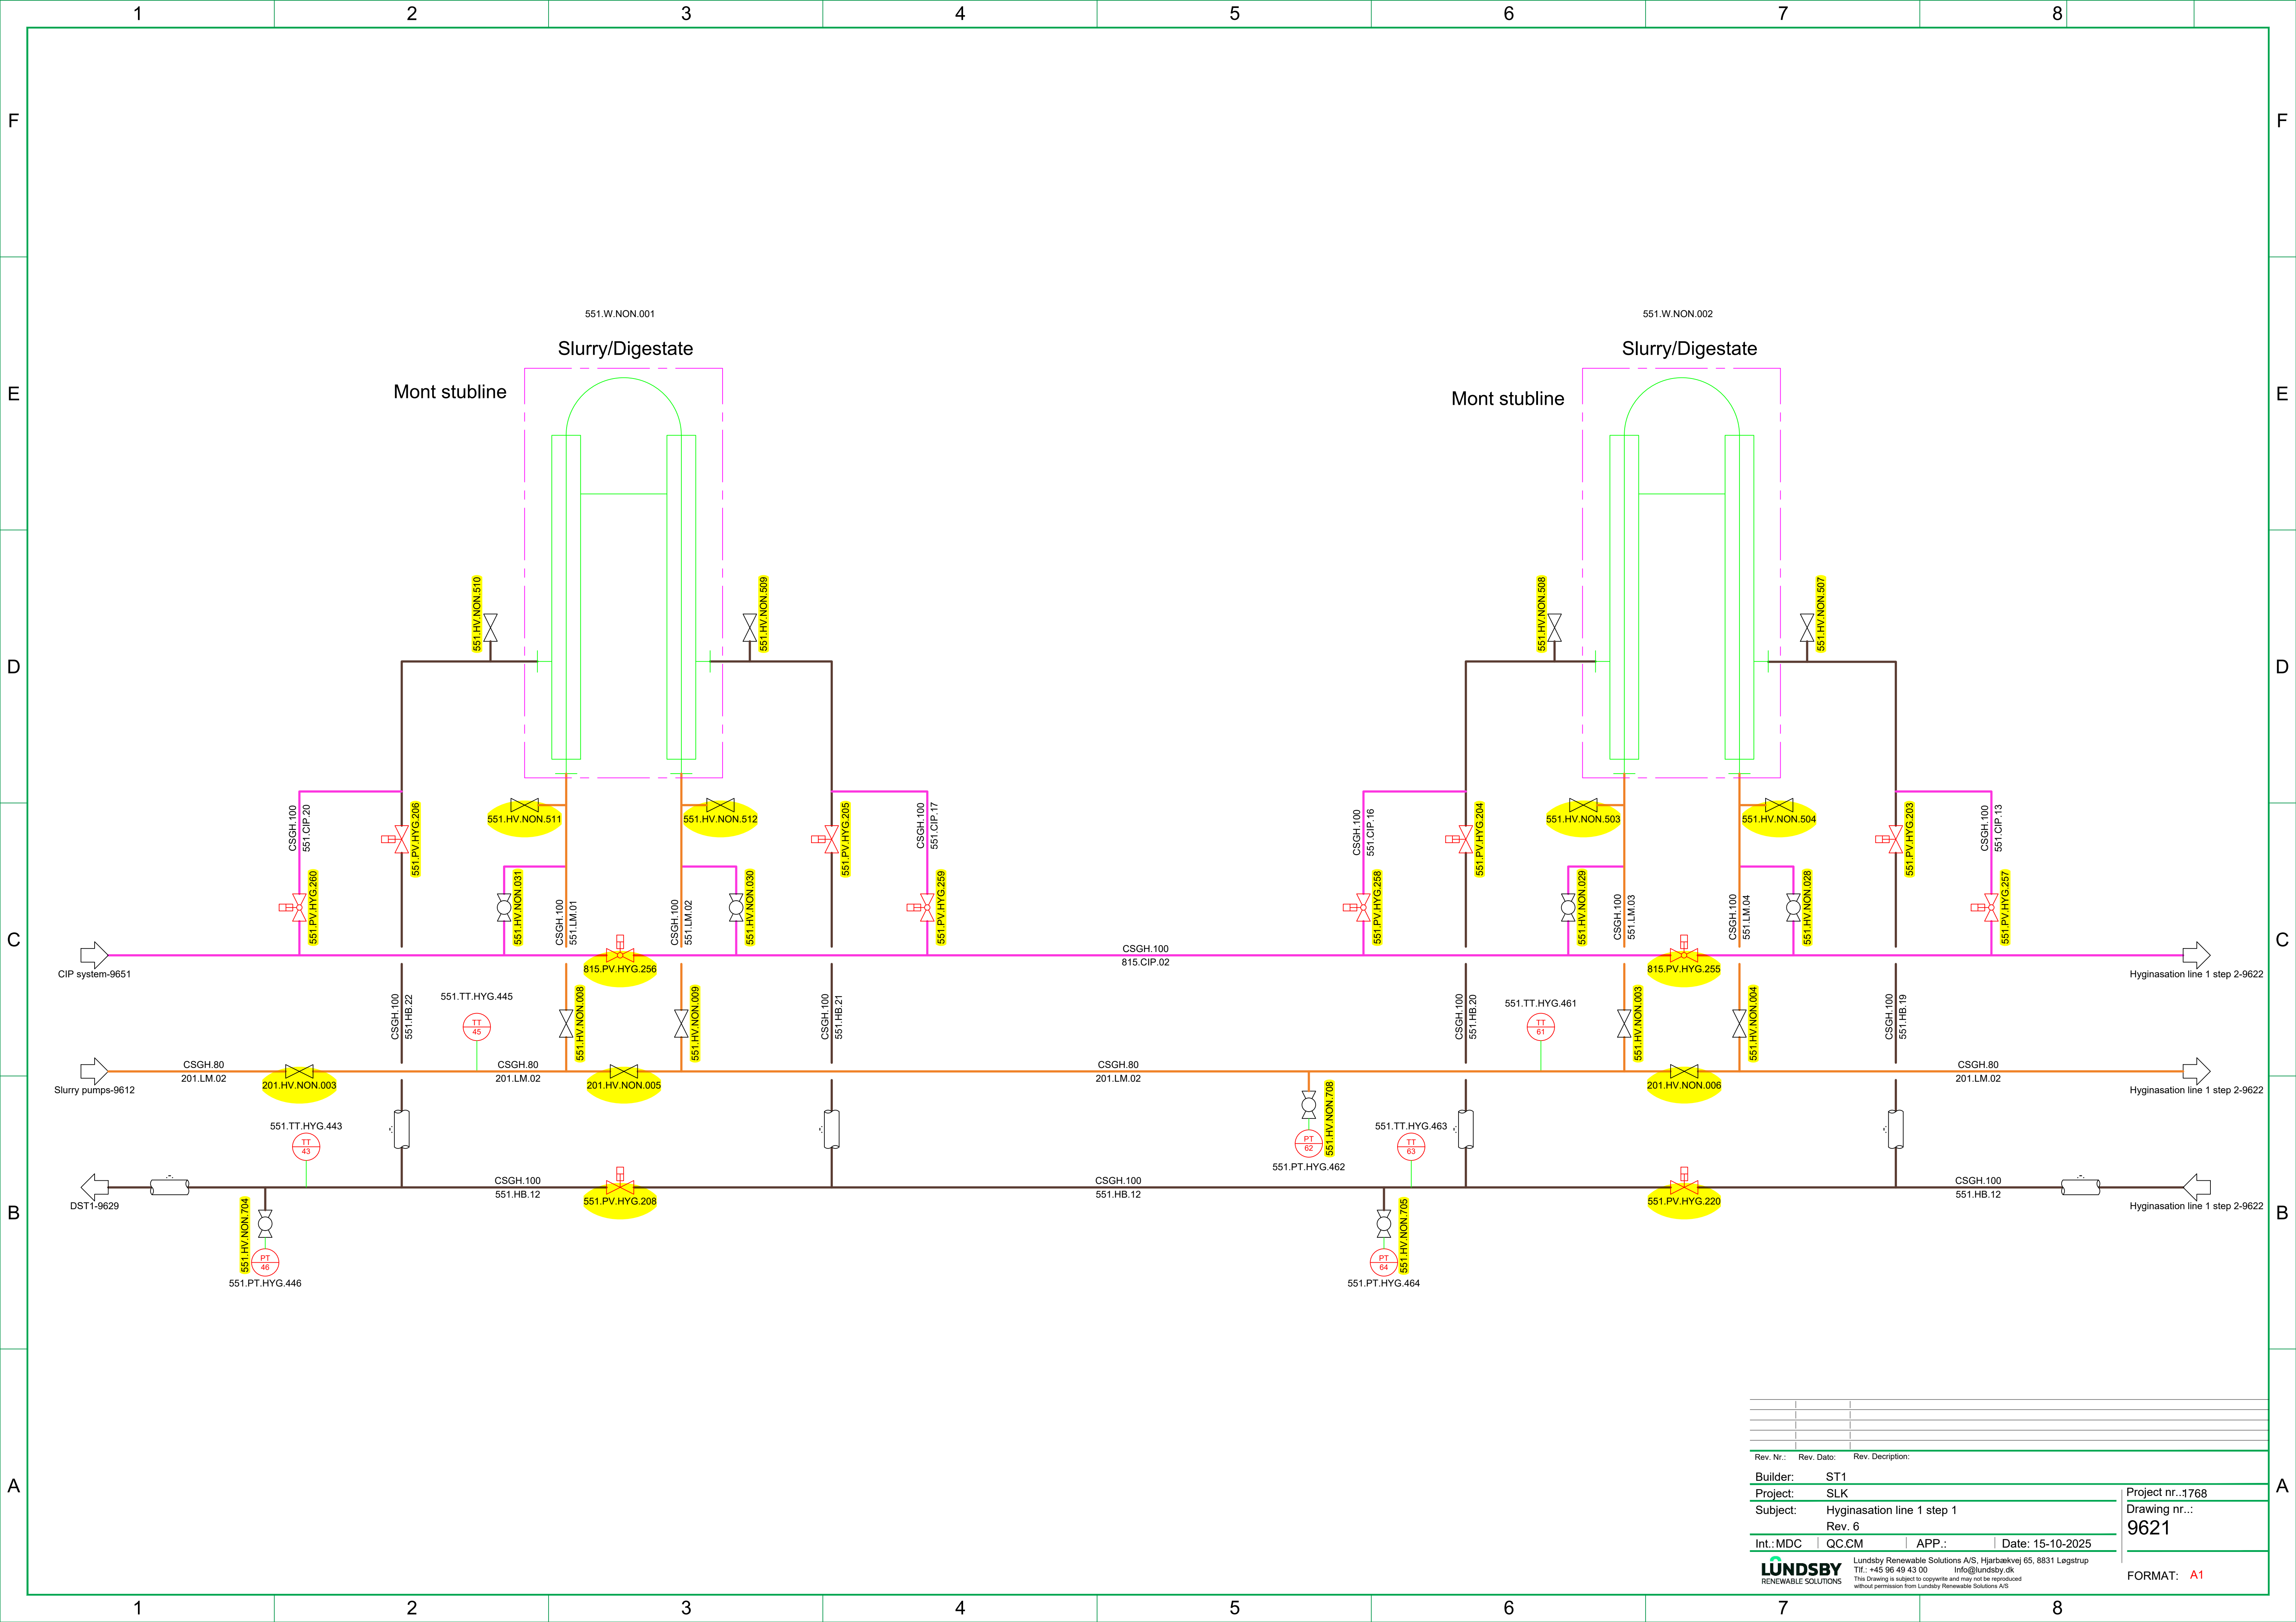


Rev. Nr.:	Rev. Dato:	Rev. Description:
Builder:	ST1	
Project:	SLK	
Subject:	Hyginasation line 1 step 1	
Rev. 6		
Int.:MDC	QC:CM	APP.:
Date:	15-10-2025	
LUNDSBY RENEWABLE SOLUTIONS		
Lundsby Renewable Solutions A/S, Hjarbækvej 65, 8831 Løgstrup Tlf.: +45 96 49 43 00 Info@lundsby.dk This Drawing is subject to copyright and may not be reproduced without permission from Lundsby Renewable Solutions A/S		
Project nr.:1768 Drawing nr.: 9621		FORMAT: A1

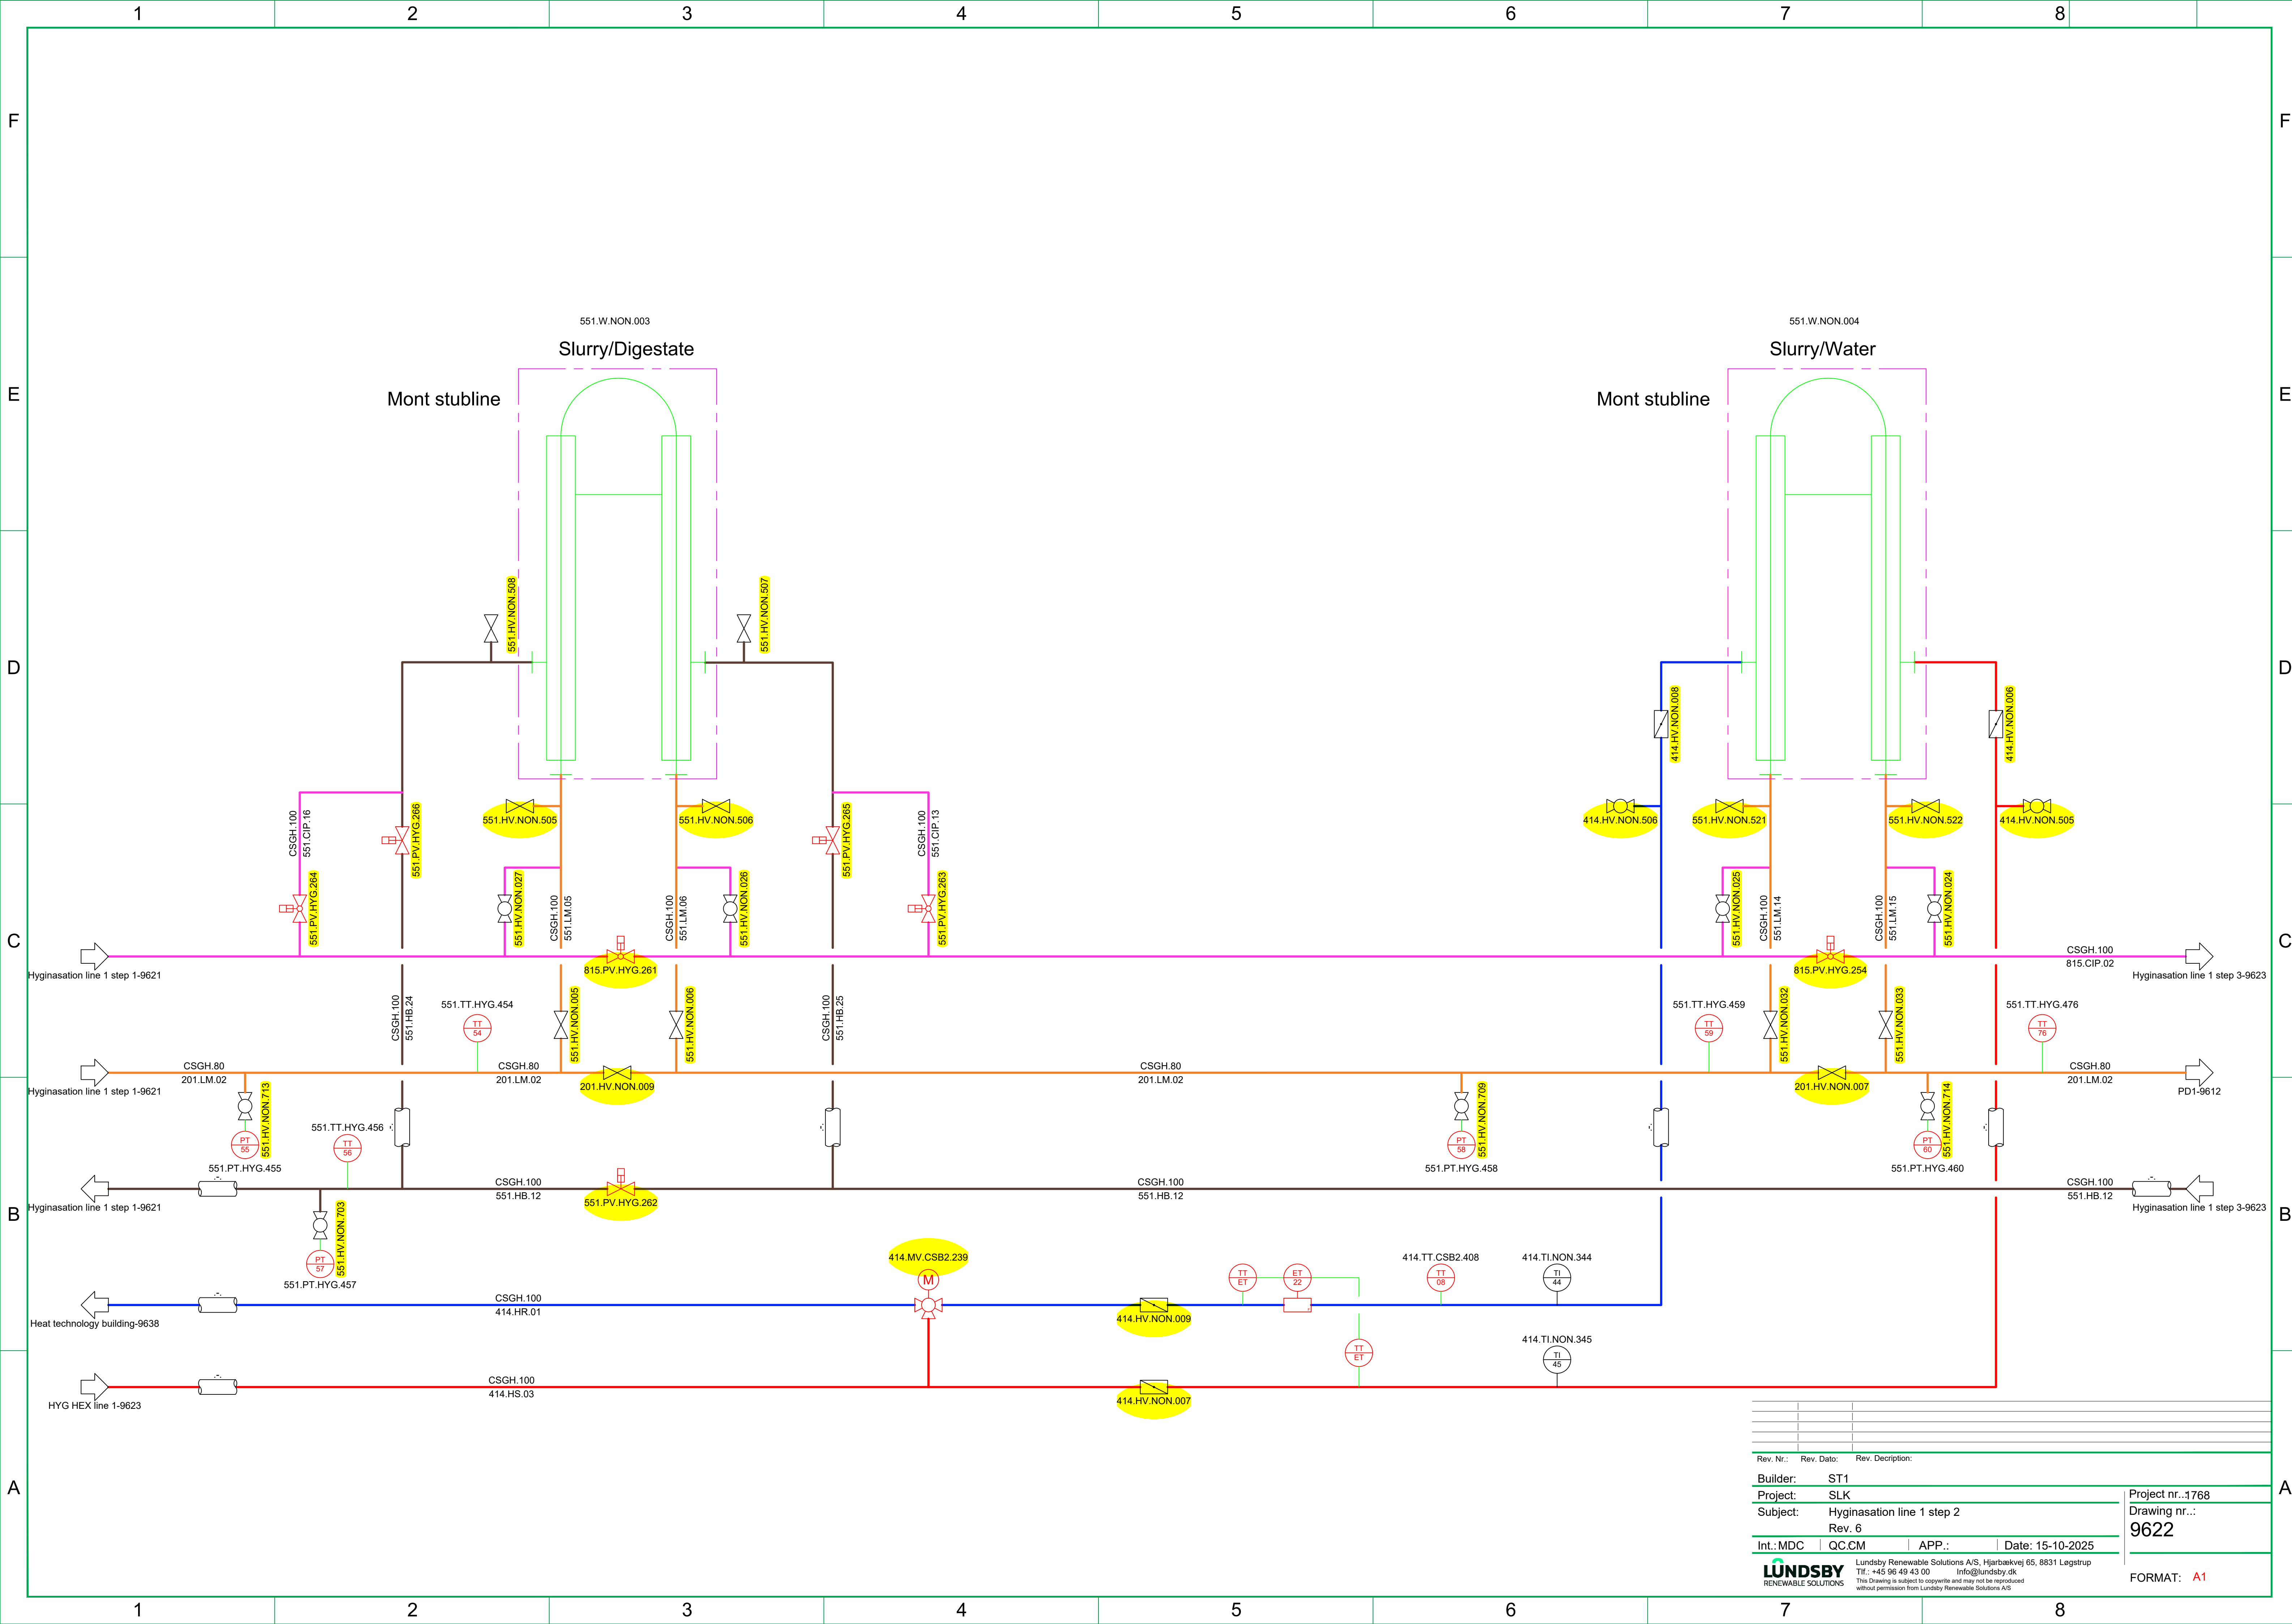

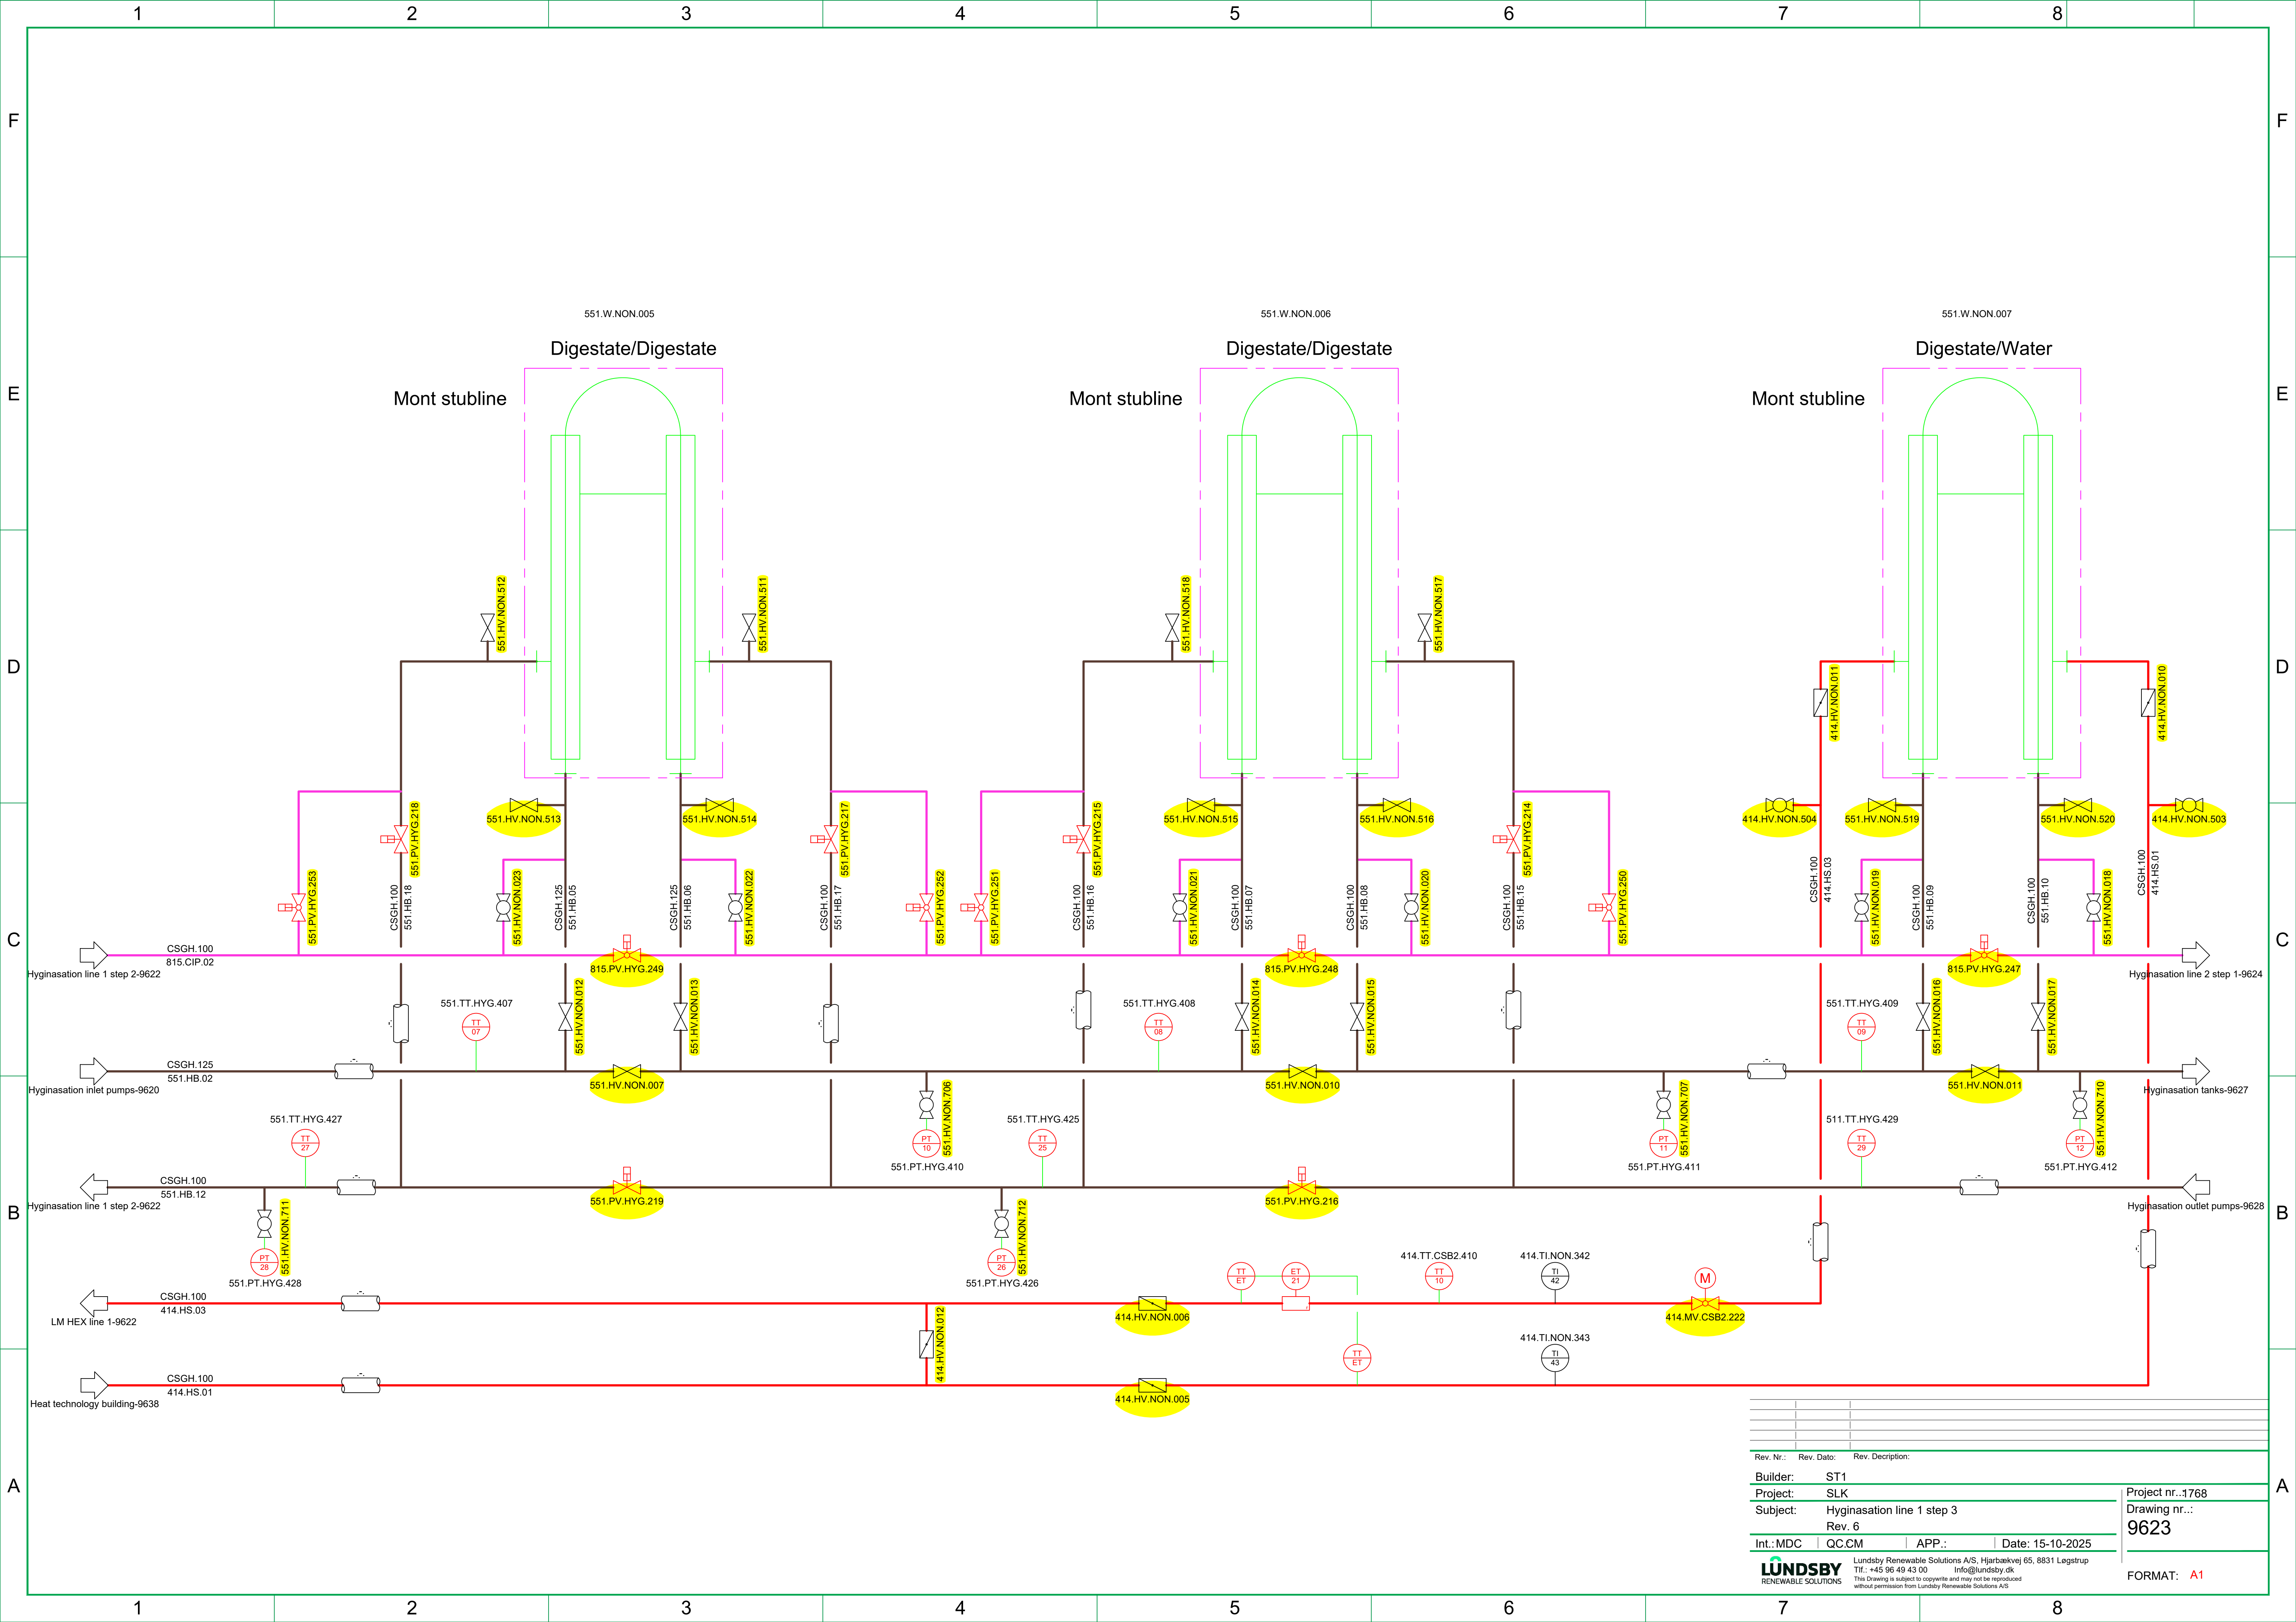

Rev. Nr.:	Rev. Dato:	Rev. Description:
Builder:	ST1	
Project:	SLK	
Subject:	Hyginasation line 1 step 3	
Rev. 6		
Int.:MDC	QC:CM	APP.: Date: 15-10-2025
LUNDSBY RENEWABLE SOLUTIONS		
Lundby Renewable Solutions A/S, Hjarbrækvej 65, 8831 Lægstrup Tlf.: +45 96 49 43 00 Info@lundby.dk This drawing is subject to copyright and may not be reproduced without permission from Lundby Renewable Solutions A/S		
Project nr.:1768 Drawing nr.: 9623		FORMAT: A1

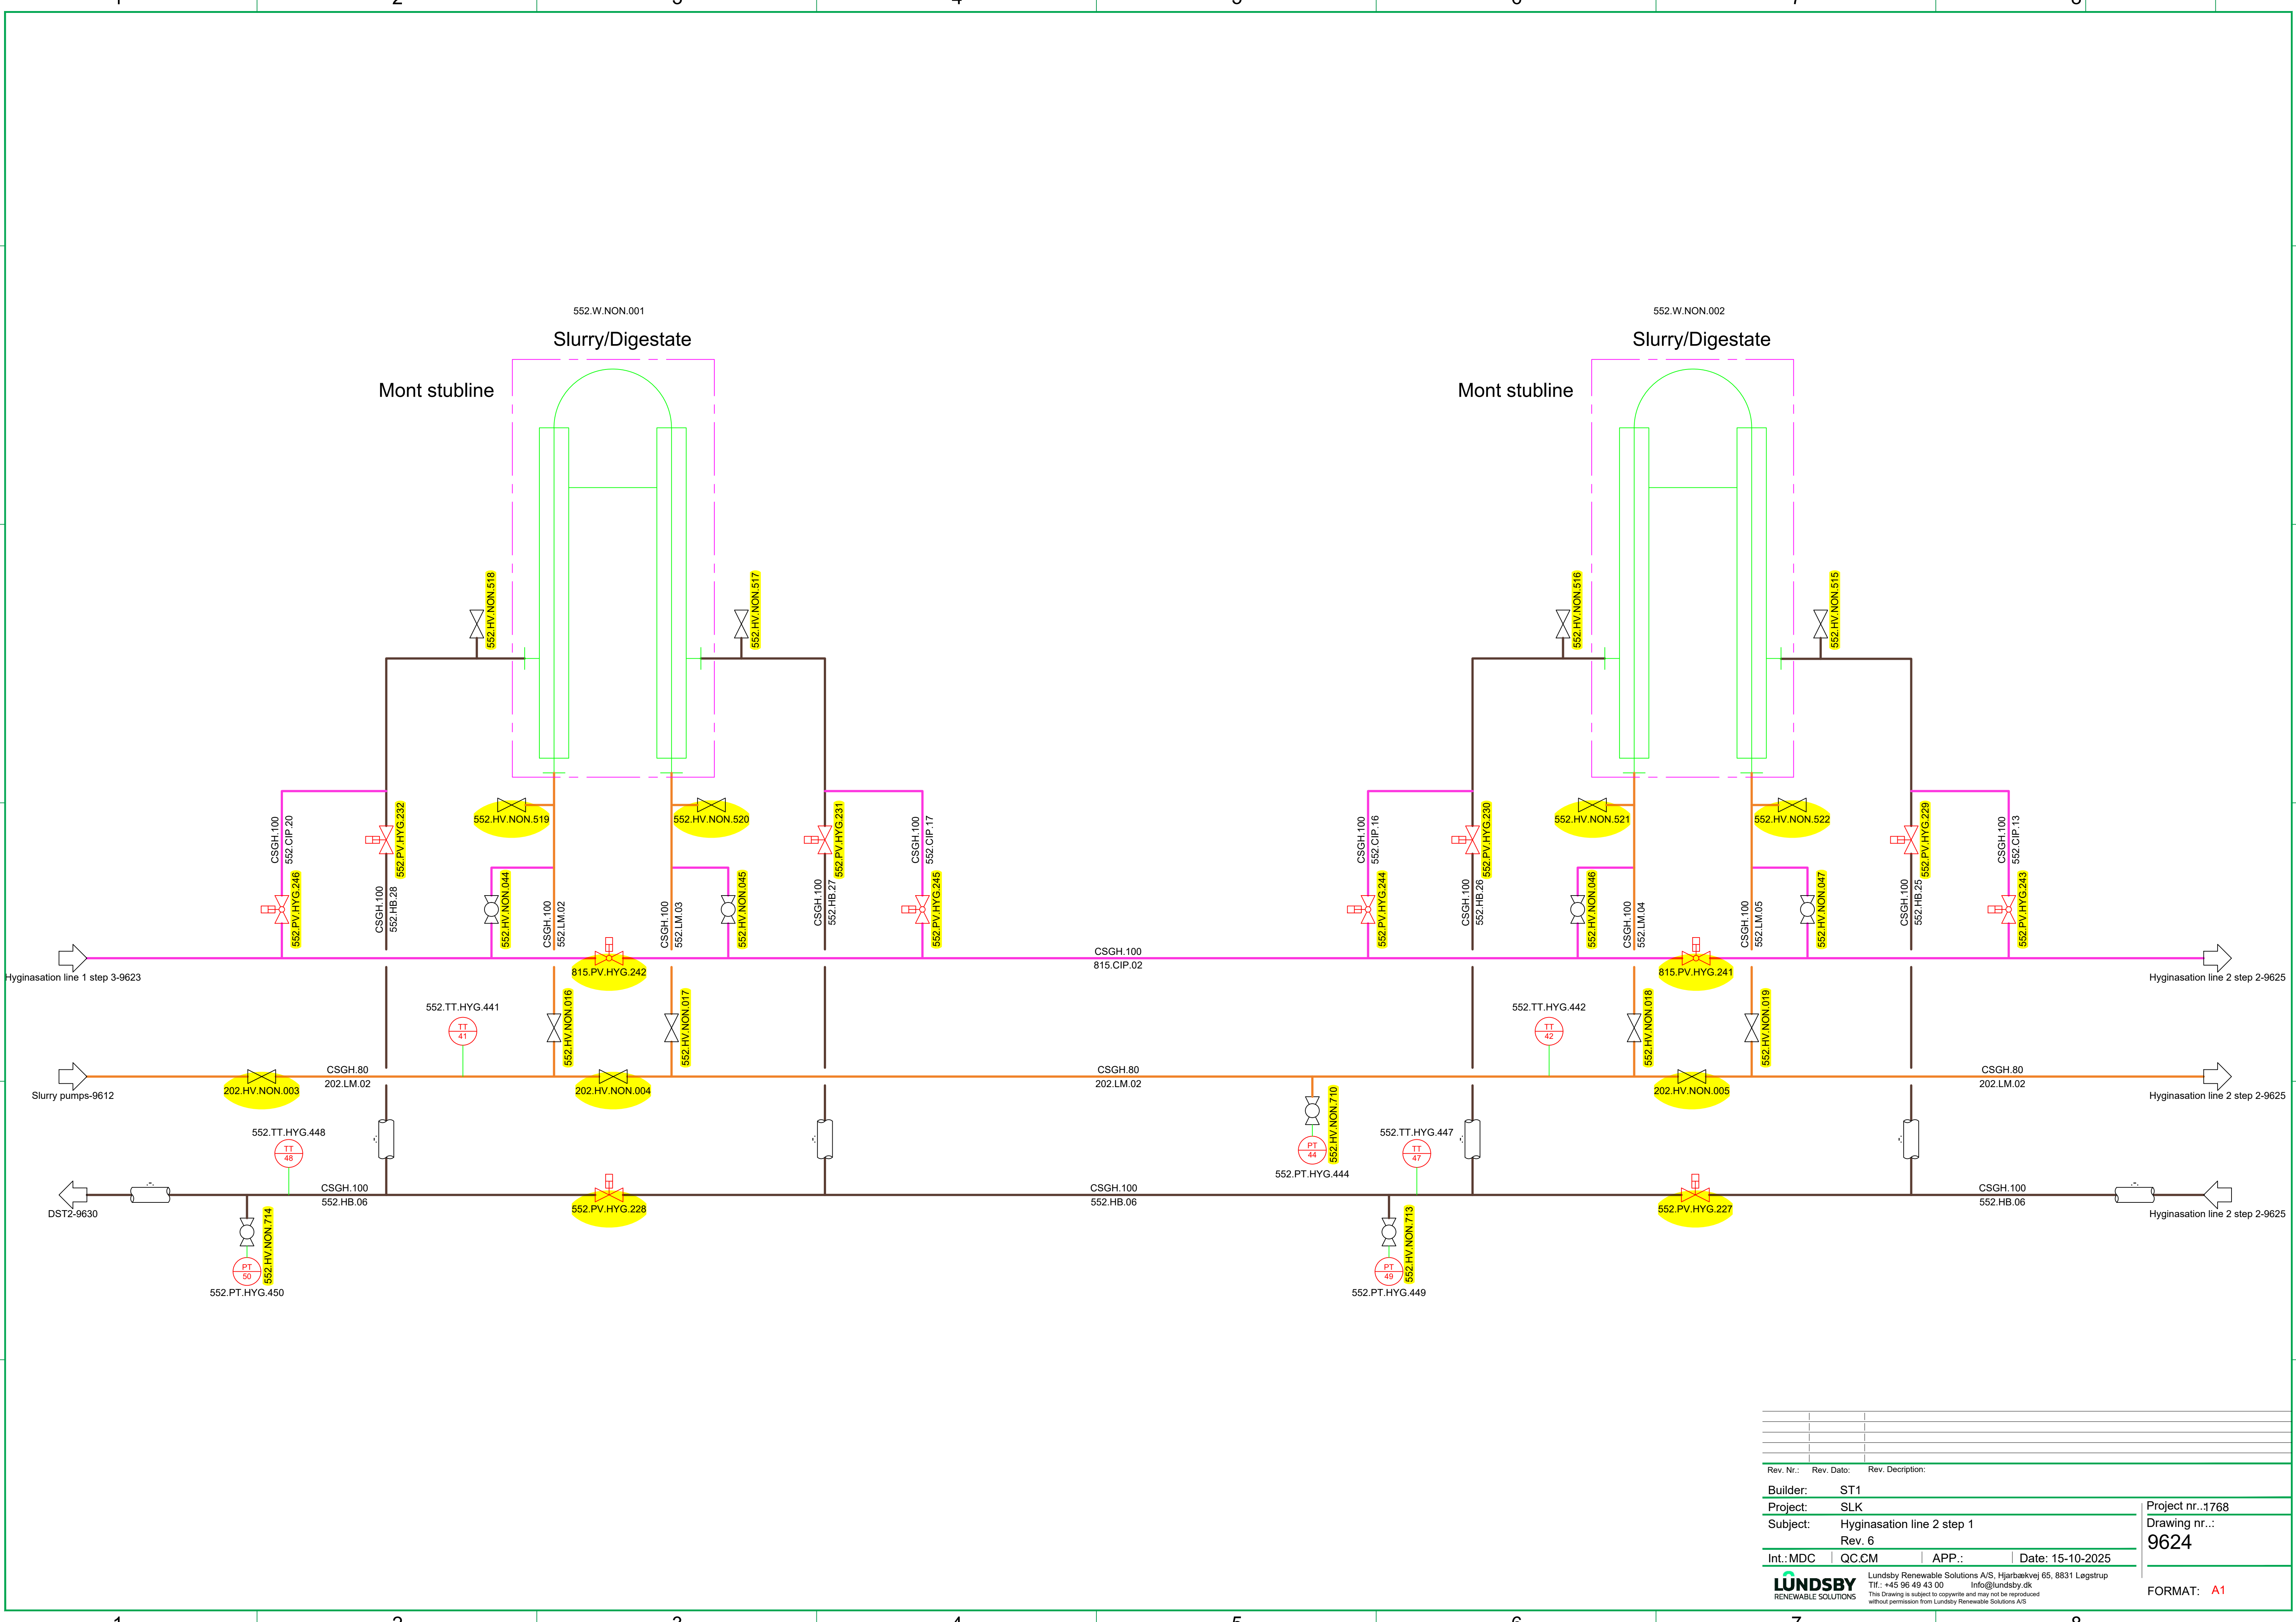

Rev. Nr.:	Rev. Dato:	Rev. Description:

Builder:	ST1
Project:	SLK
Subject:	Hyginasation line 2 step 1
Rev. 6	


Int.:MDC	QC:CM	APP.:	Date: 15-10-2025
----------	-------	-------	------------------

LUNDSBY
RENEWABLE SOLUTIONS


Lundsby Renewable Solutions A/S, Hjarbækvej 65, 8831 Løgstrup
Tlf.: +45 96 49 43 00 info@lundsby.dk
This Drawing is subject to copyright and may not be reproduced without permission from Lundsby Renewable Solutions A/S


Project nr.:1768
Drawing nr.:
9624

FORMAT: **A1**

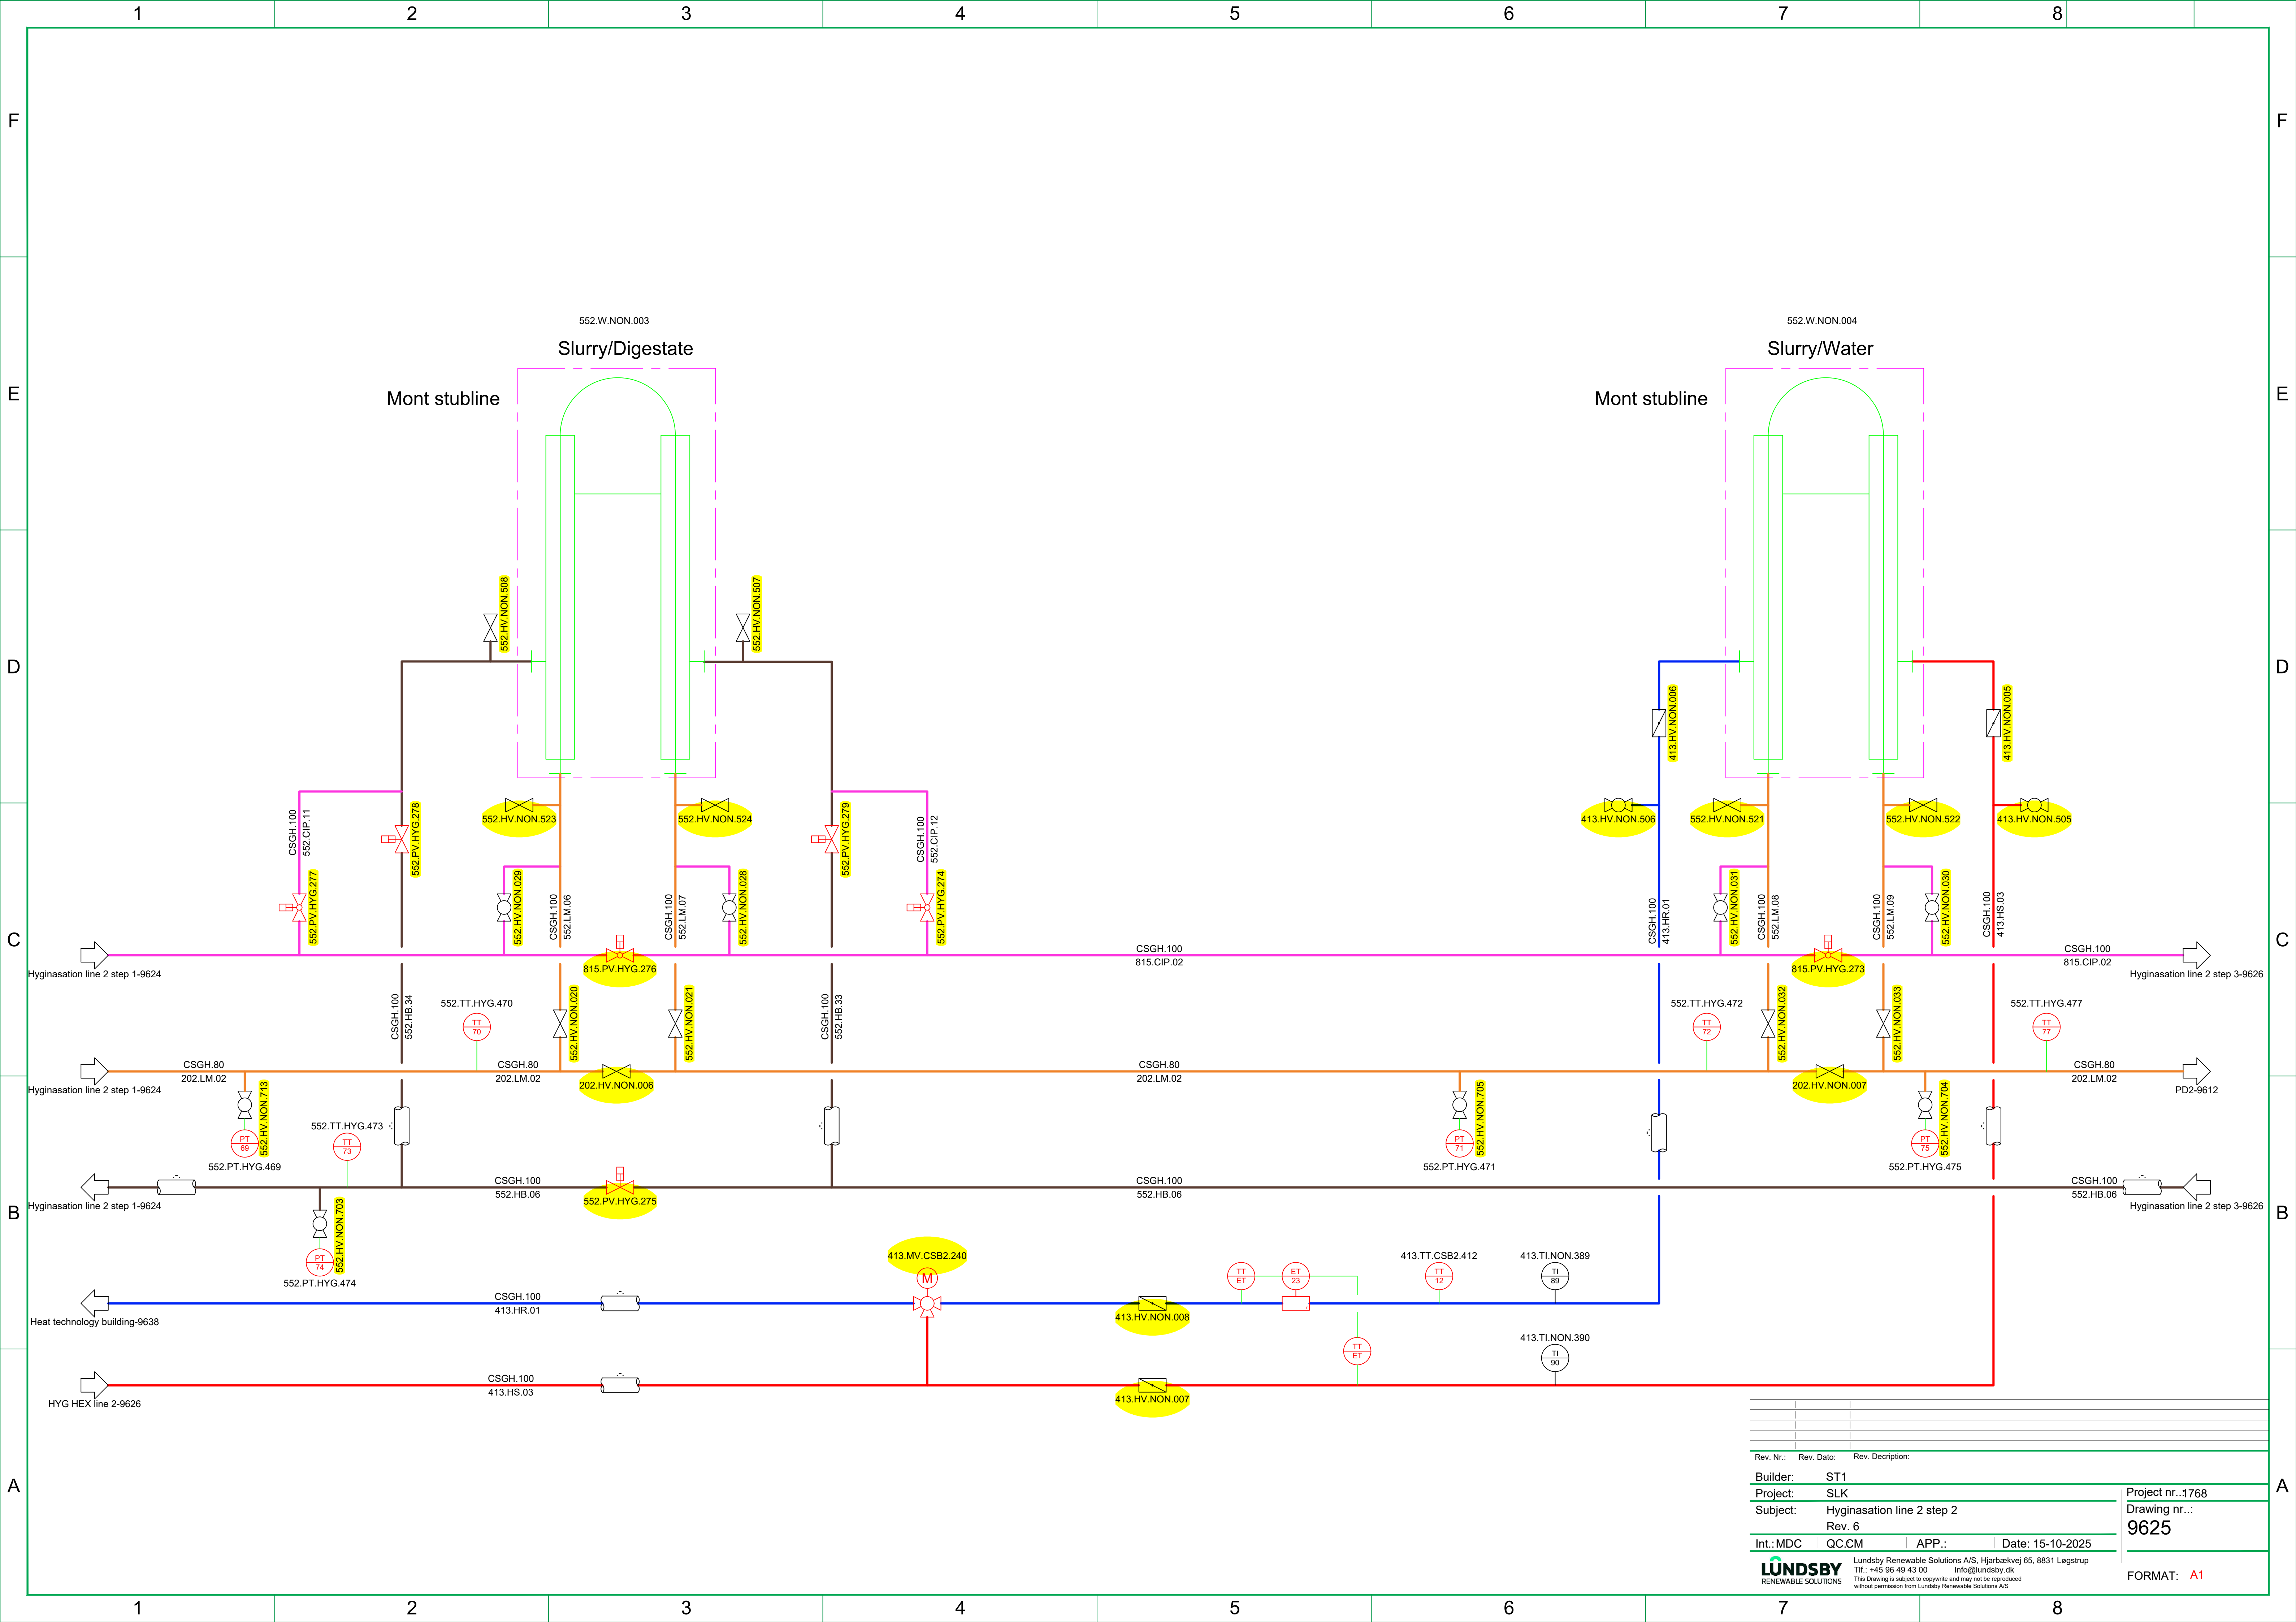

Rev. Nr.:	Rev. Dato:	Rev. Description:
Builder:	ST1	
Project:	SLK	
Subject:	Hyginasation line 2 step 2	
	Rev. 6	
Int.:MDC	QC:CM	APP.:
		Date: 15-10-2025
LUNDSBY RENEWABLE SOLUTIONS Lundsby Renewable Solutions A/S, Hjarbækvej 65, 8831 Løgstrup Tlf.: +45 96 49 43 00 Info@lundsby.dk This drawing is subject to copyright and may not be reproduced without permission from Lundsby Renewable Solutions A/S		
Project nr.:1768		Drawing nr.:9625
FORMAT: A1		

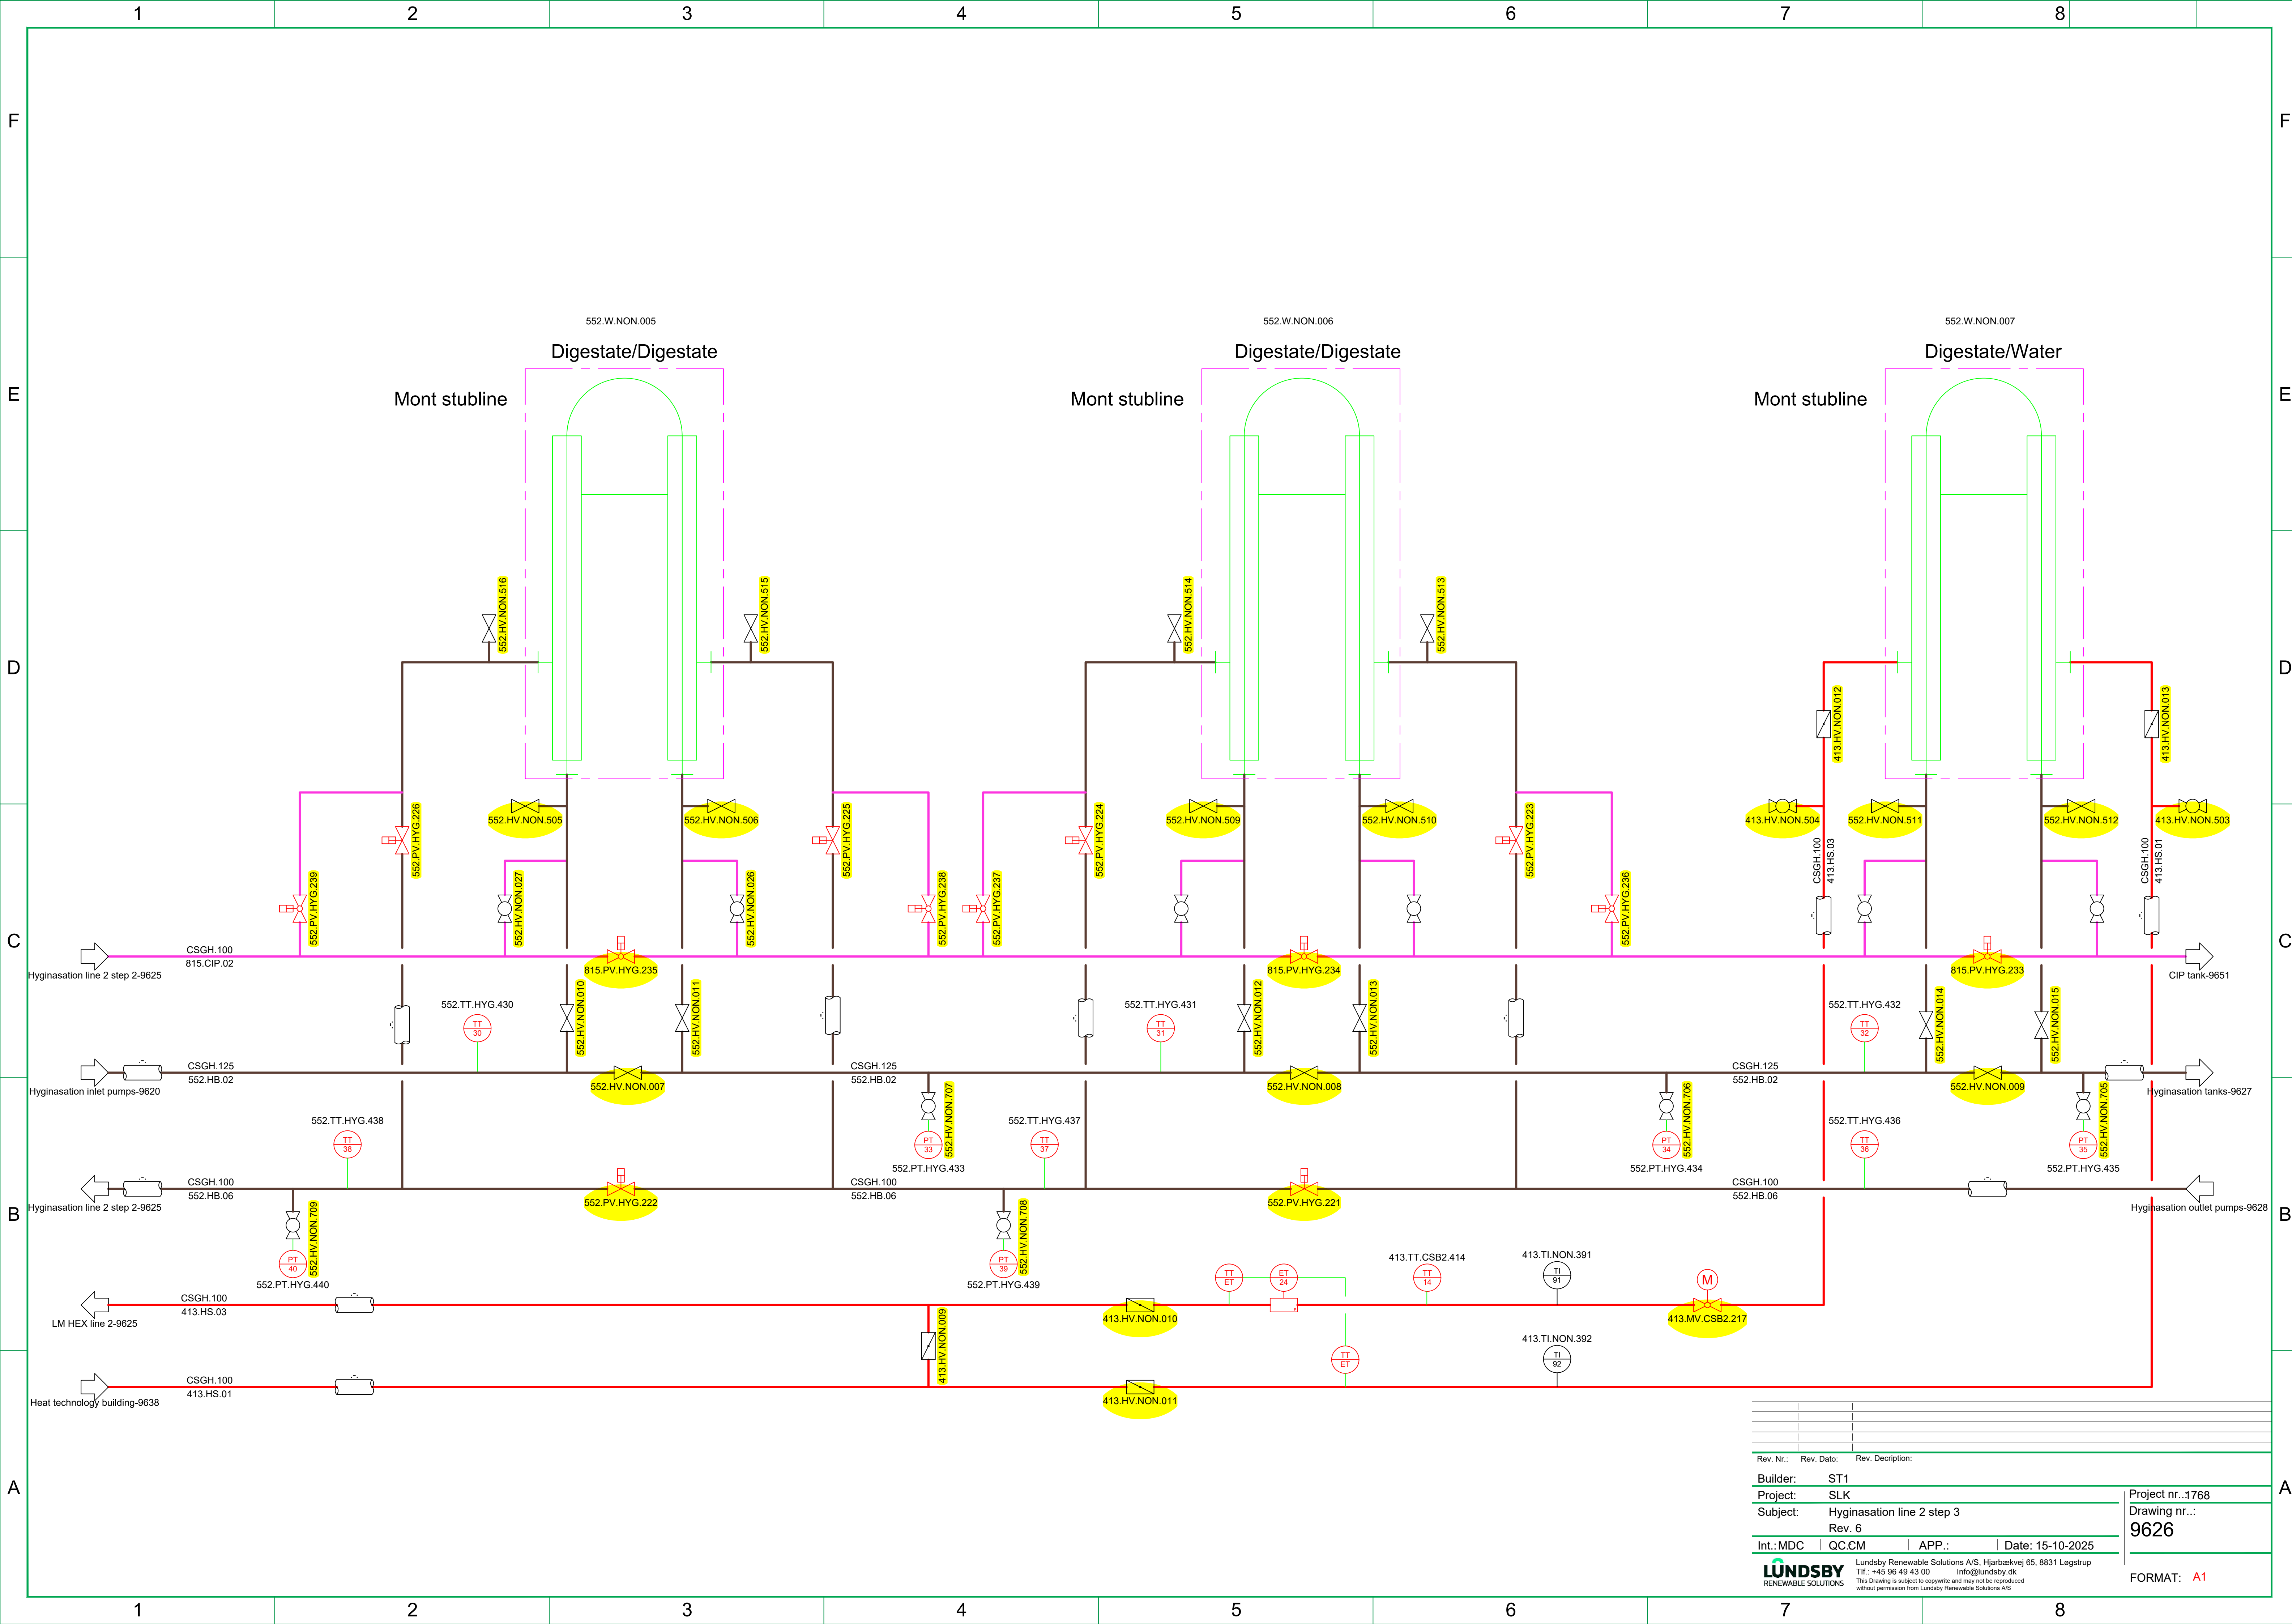

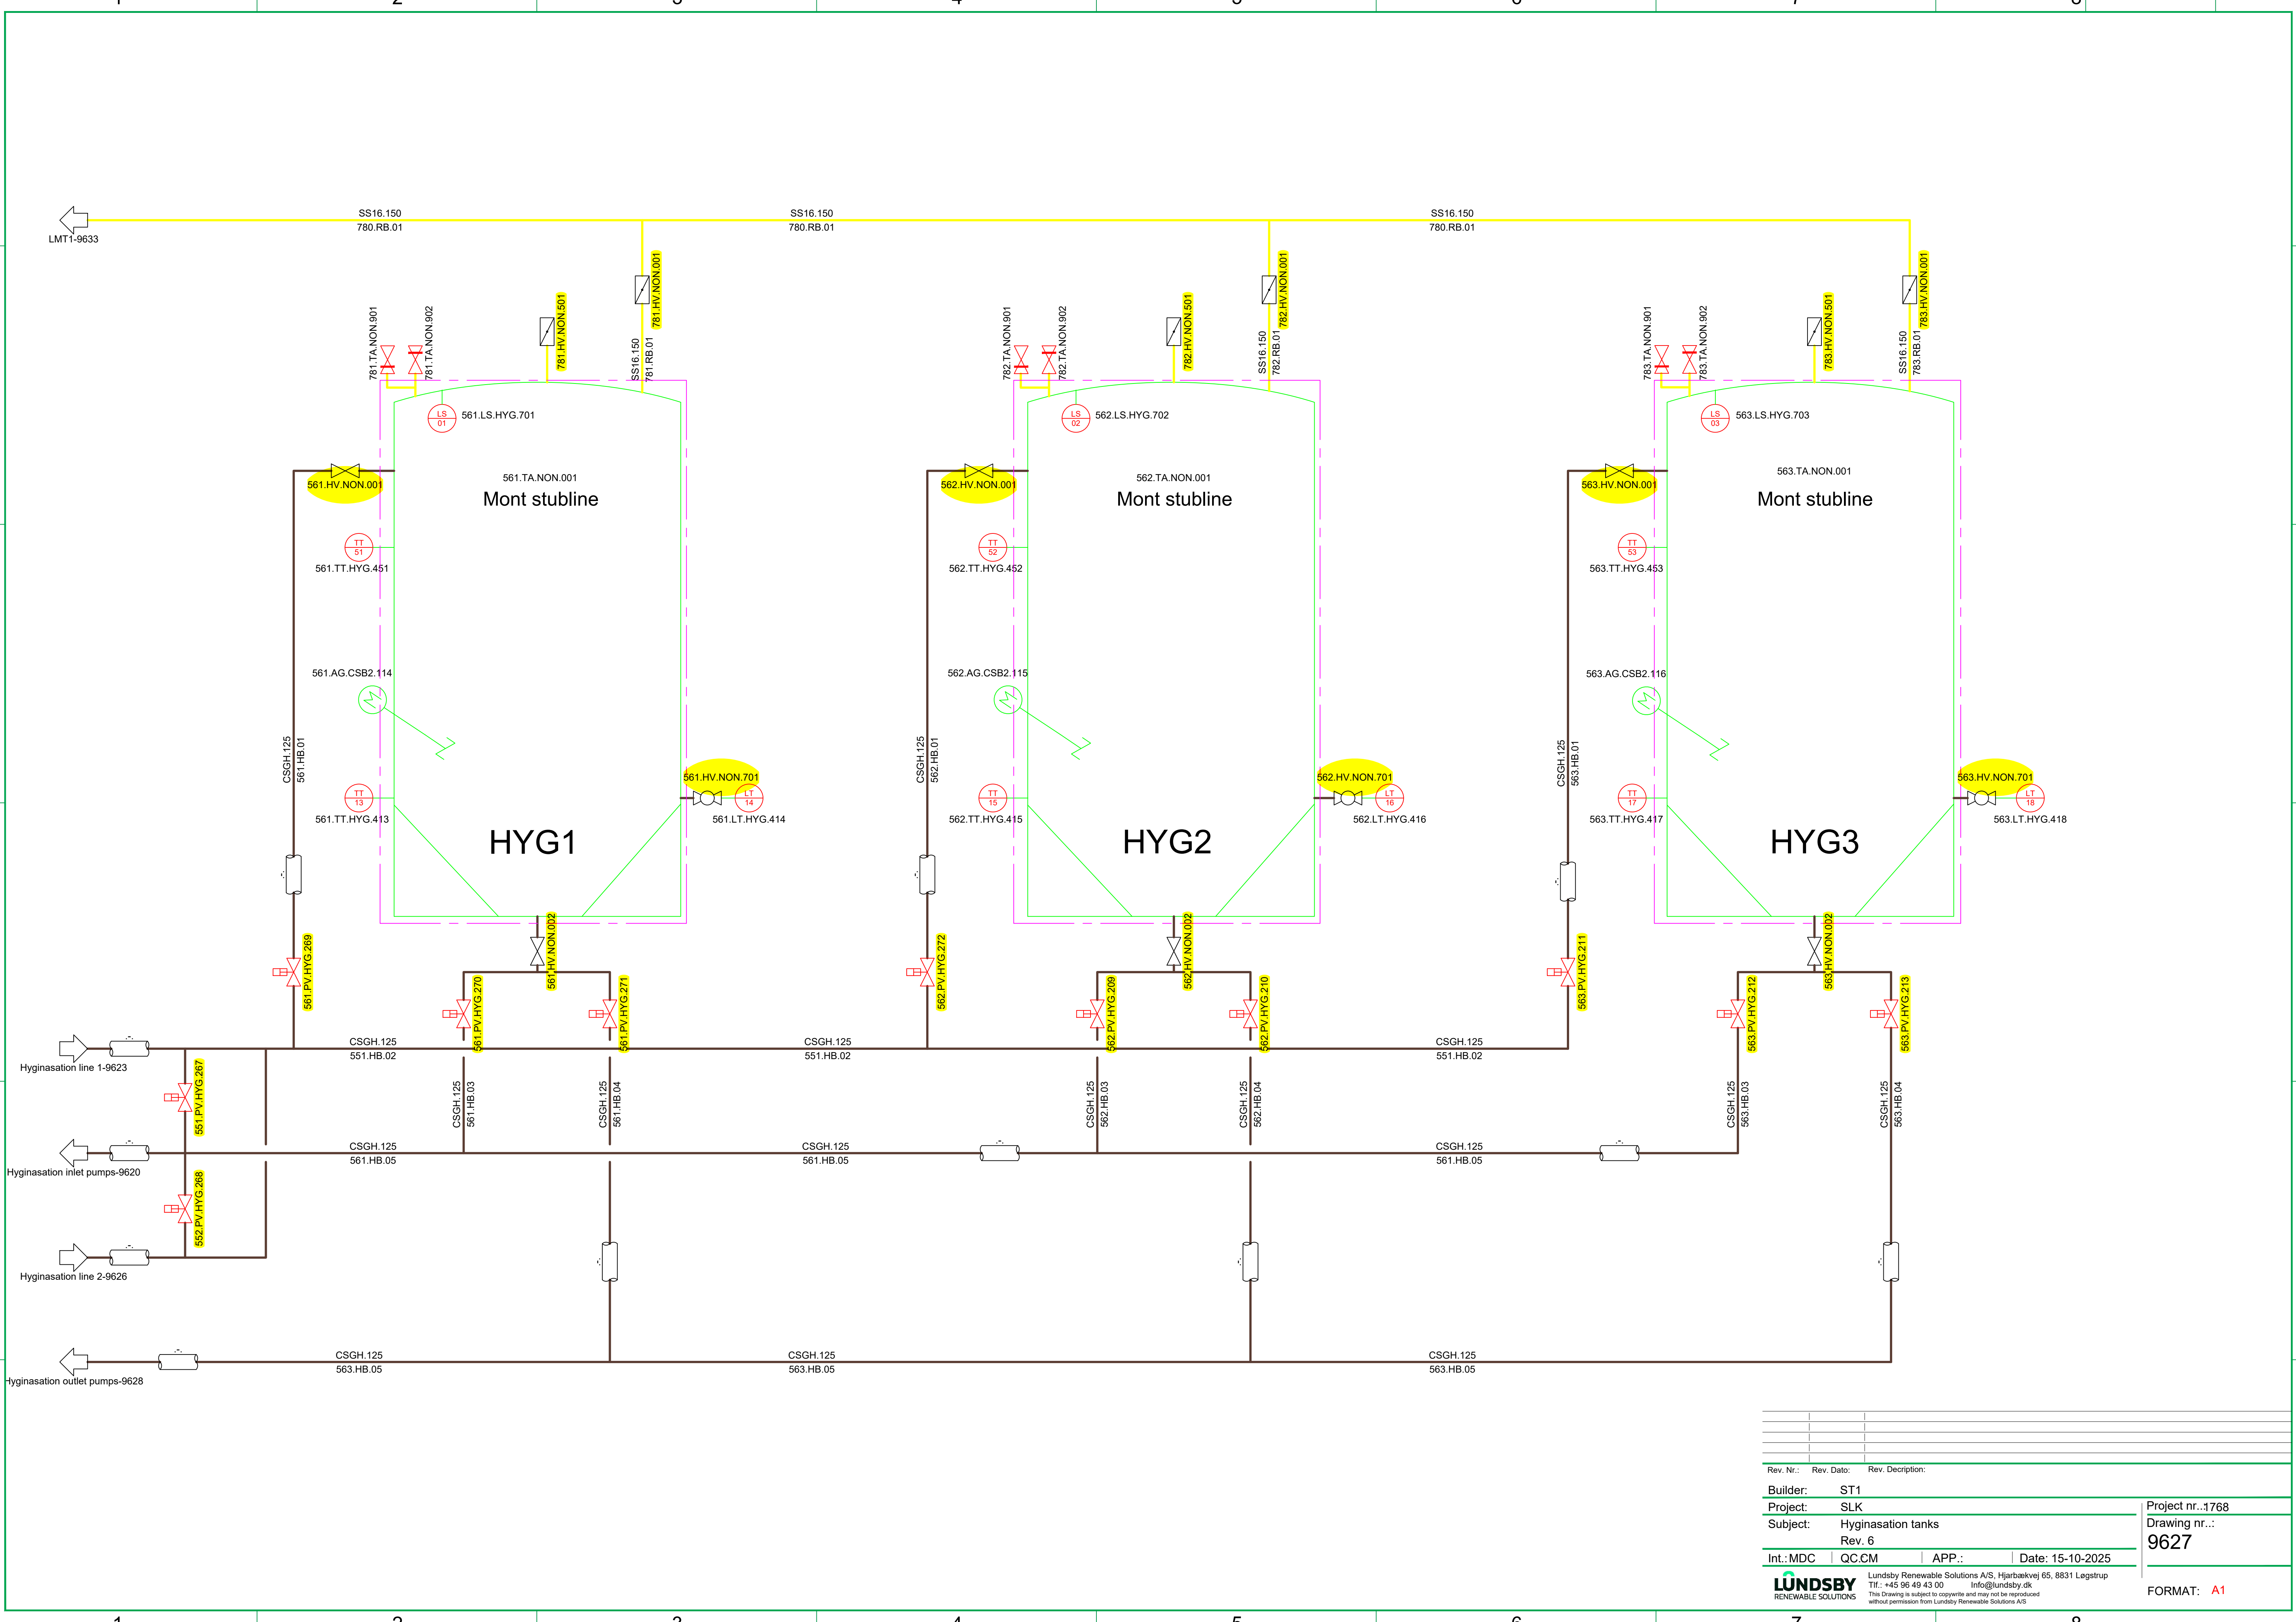

Rev. Nr.:	Rev. Dato:	Rev. Description:
Builder:	ST1	
Project:	SLK	
Subject:	Hyginasation tanks	
Rev. 6		
Int.: MDC	QC.CM	APP.:
Date: 15-10-2025		
LUNDSBY RENEWABLE SOLUTIONS		
Lundsby Renewable Solutions A/S, Hjarbrækvej 65, 8831 Løgstrup Tlf.: +45 96 49 43 00 Info@lundsby.dk This Drawing is subject to copyright and may not be reproduced without permission from Lundsby Renewable Solutions A/S		
Project nr.: 1768 Drawing nr.: 9627		FORMAT: A1

1 2 3 4 5 6 7 8

F

E

D

C

B

A

1 2 3 4 5 6 7 8

Tech Building

Outlet pumps

Hyginasation tanks-9627

CSGH.125 563.HB.05

DN125/DN150

DN150/DN100

551.HV.NON.018

CSGH.150 551.HB.11

551.PT.HYG.419

551.HV.NON.711

551.HV.NON.519

551.P.CSB2.103

551.TT.HYG.421

551.HV.NON.520

551.PT.HYG.420

551.HV.NON.712

CSGH.100 551.HB.12

DN100/DN65

551.FT.HYG.467

DN65/DN100

551.HV.NON.019

CSGH.100 551.HB.12

Hyginasation line 1-9623

815.CIP.08

CIP system-9651

552.HV.NON.004

CSGH.150 552.HB.04

552.PT.HYG.422

552.HV.NON.703

552.HV.NON.503

552.P.CSB2.104

552.TT.HYG.424

552.HV.NON.504

552.PT.HYG.423

552.HV.NON.704

CSGH.100 552.HB.06

DN100/DN65

552.FT.HYG.468

DN65/DN100

552.HV.NON.005

CSGH.100 552.HB.06

Hyginasation line 2-9626

815.CIP.07

CIP system-9651

552.HV.NON.006

Rev. Nr.	Rev. Dato	Rev. Description

Builder:	ST1	Project nr.:1768	
Project:	SLK		
Subject:	Hyginasation outlet pumps		
Rev.	6	Drawing nr.: 9628	
Int.:MDC	QC:CM	APP.:	Date: 15-10-2025

LUNDSBY
RENEWABLE SOLUTIONS

Lundsby Renewable Solutions A/S, Hjarbrækvej 65, 8831 Lægstrup
Tlf.: +45 96 49 43 00
Info@lundsby.dk

This Drawing is subject to copyright and may not be reproduced without permission from Lundsby Renewable Solutions A/S

FORMAT: A1

1 2 3 4 5 6 7 8

F

E

D

C

B

A

1 2 3 4 5 6 7 8

Tech Building

Outlet pumps

Hyginasation tanks-9627

CSGH.125
563.HB.05

DN125/DN150

DN150/DN100

551.HV.NON.018

CSGH.150
551.HB.11

551.PT.HYG.419
PT 19

551.HV.NON.711

551.HV.NON.519

551.P.CSB2.103

551.TT.HYG.421
TT 21

551.HV.NON.520

551.PT.HYG.420
PT 20

551.HV.NON.712

CSGH.100
551.HB.12

DN100/DN65

551.FT.HYG.467
FT 67

DN65/DN100

551.HV.NON.019

CSGH.100
551.HB.12

CSGH.100
815.CIP.08

CIP system-9651

Hyginasation line 1-9623

552.HV.NON.004

CSGH.150
552.HB.04

552.PT.HYG.422
PT 22

552.HV.NON.703

552.HV.NON.503

552.P.CSB2.104

552.TT.HYG.424
TT 24

552.HV.NON.504

552.PT.HYG.423
PT 23

552.HV.NON.704

CSGH.100
552.HB.06

DN100/DN65

552.FT.HYG.468
FT 68

DN65/DN100

552.HV.NON.005

CSGH.100
552.HB.06

CSGH.100
815.CIP.07

CIP system-9651

Hyginasation line 2-9626

552.HV.NON.006


Rev. Nr.:	Rev. Dato:	Rev. Description:


Builder:	ST1	Project nr.:1768
Project:	SLK	
Subject:	Hyginasation outlet pumps	
Rev. 6		Drawing nr.: 9628
Int.:MDC	QC:CM	APP.: Date: 15-10-2025

LUNDSBY
RENEWABLE SOLUTIONS


Lundsby Renewable Solutions A/S, Hjarbækvej 65, 8831 Løgstrup
Tlf.: +45 96 49 43 00 Info@lundsby.dk
This Drawing is subject to copyright and may not be reproduced
without permission from Lundsby Renewable Solutions A/S

FORMAT: **A1**

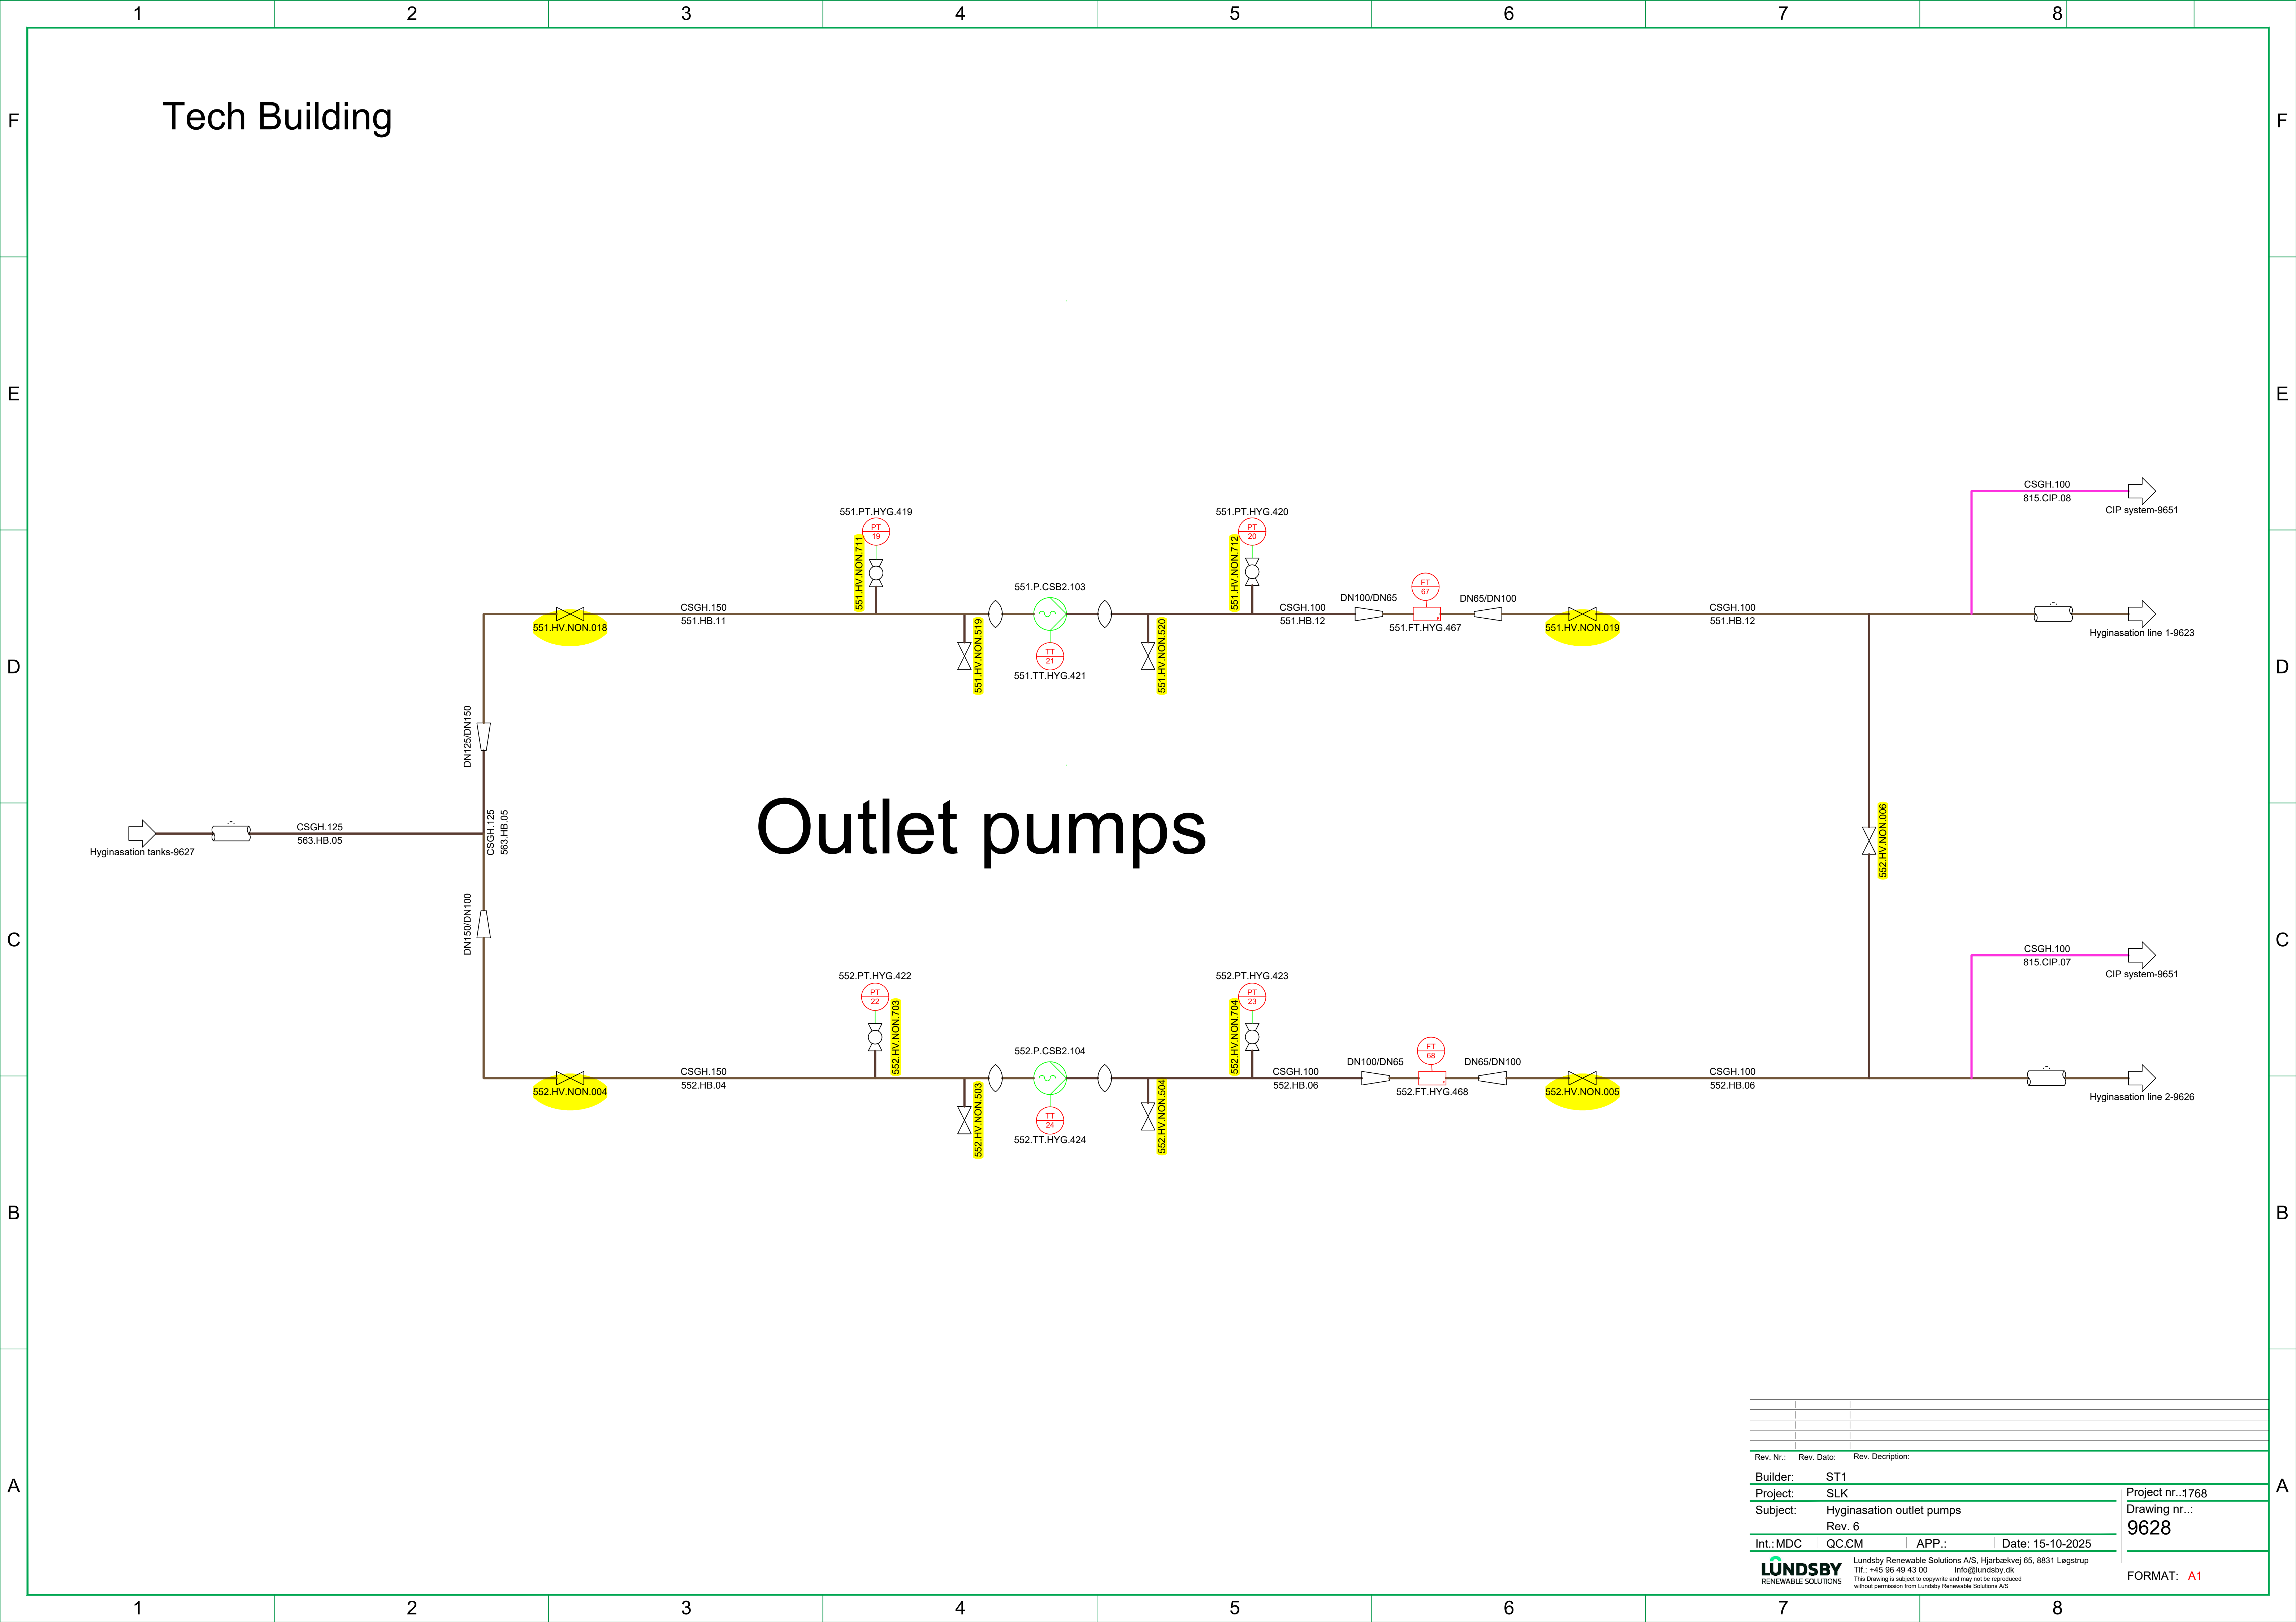
[illegible]

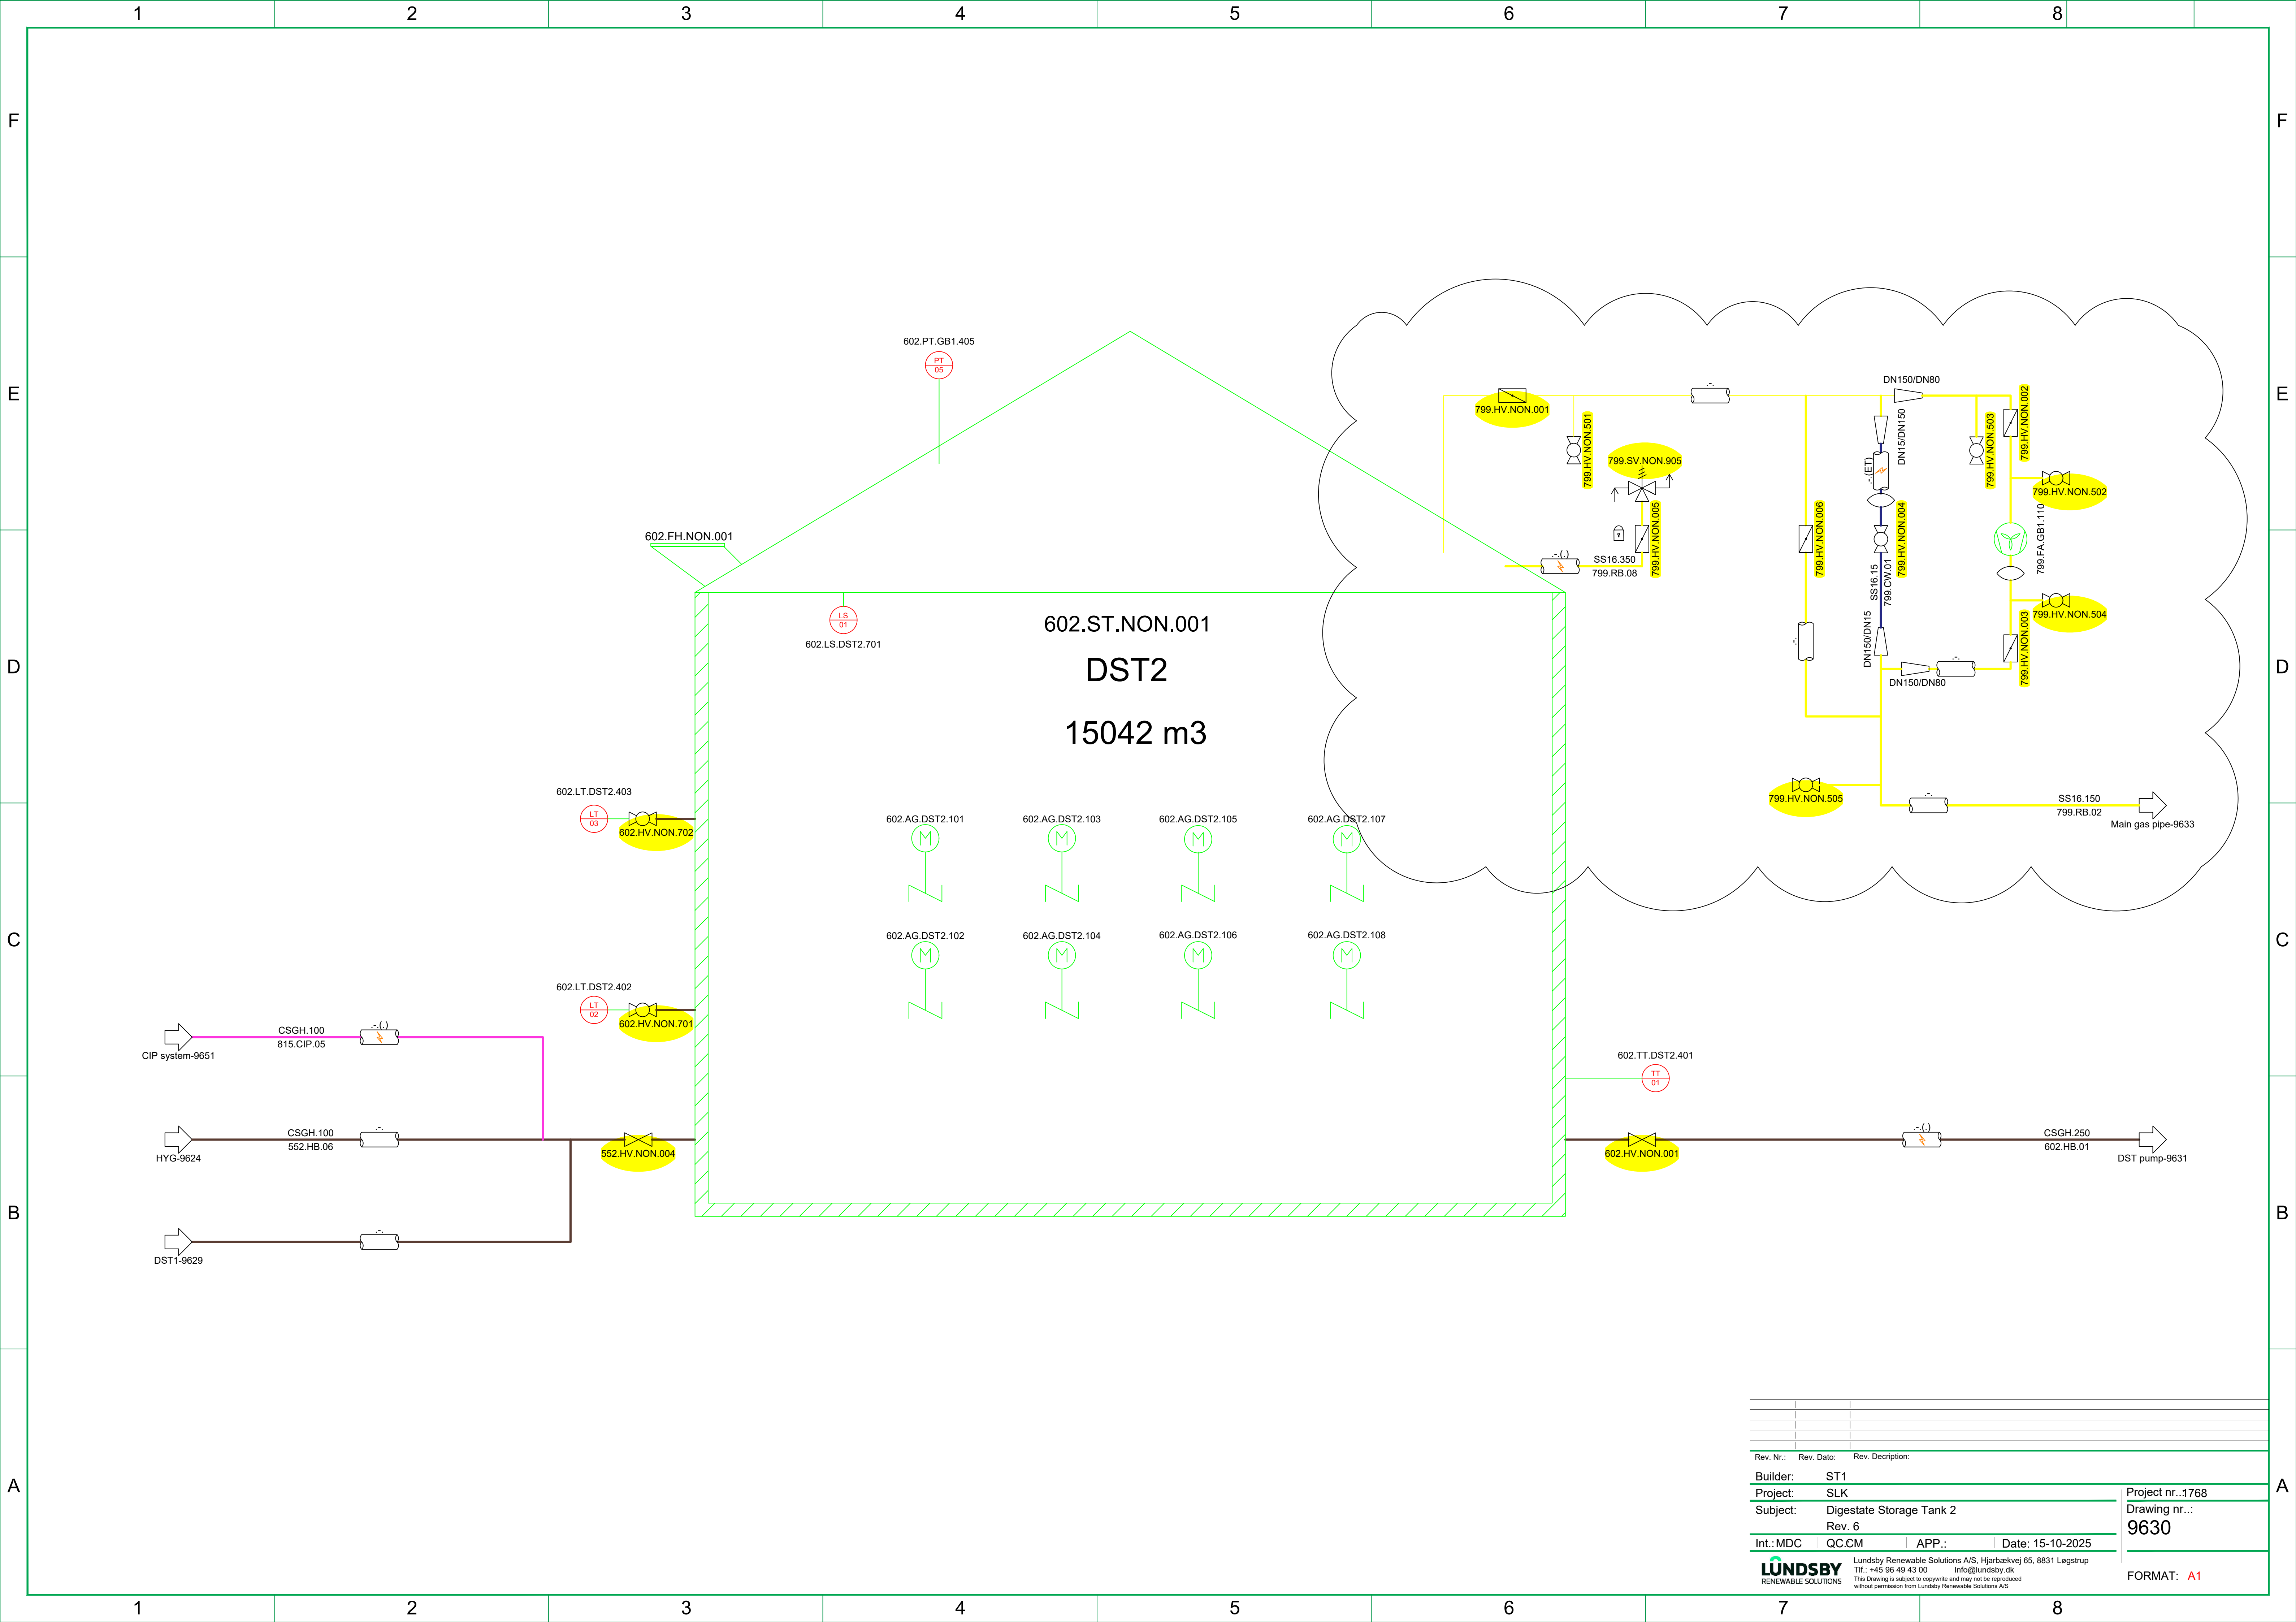


Rev. Nr.: Rev. Dato: Rev. Description:			Project nr.:1768	
Builder: ST1			Drawing nr.: 9630	
Project: SLK			Date: 15-10-2025	
Subject: Digestate Storage Tank 2			Format: A1	
Rev. 6			LUNDSBY RENEWABLE SOLUTIONS	
Int.:MDC QC:CM APP.:			Lundsby Renewable Solutions A/S, Hjarbrækvej 65, 8831 Løgstrup Tlf.: +45 96 49 43 00 Info@lundsby.dk This Drawing is subject to copyright and may not be reproduced without permission from Lundsby Renewable Solutions A/S	

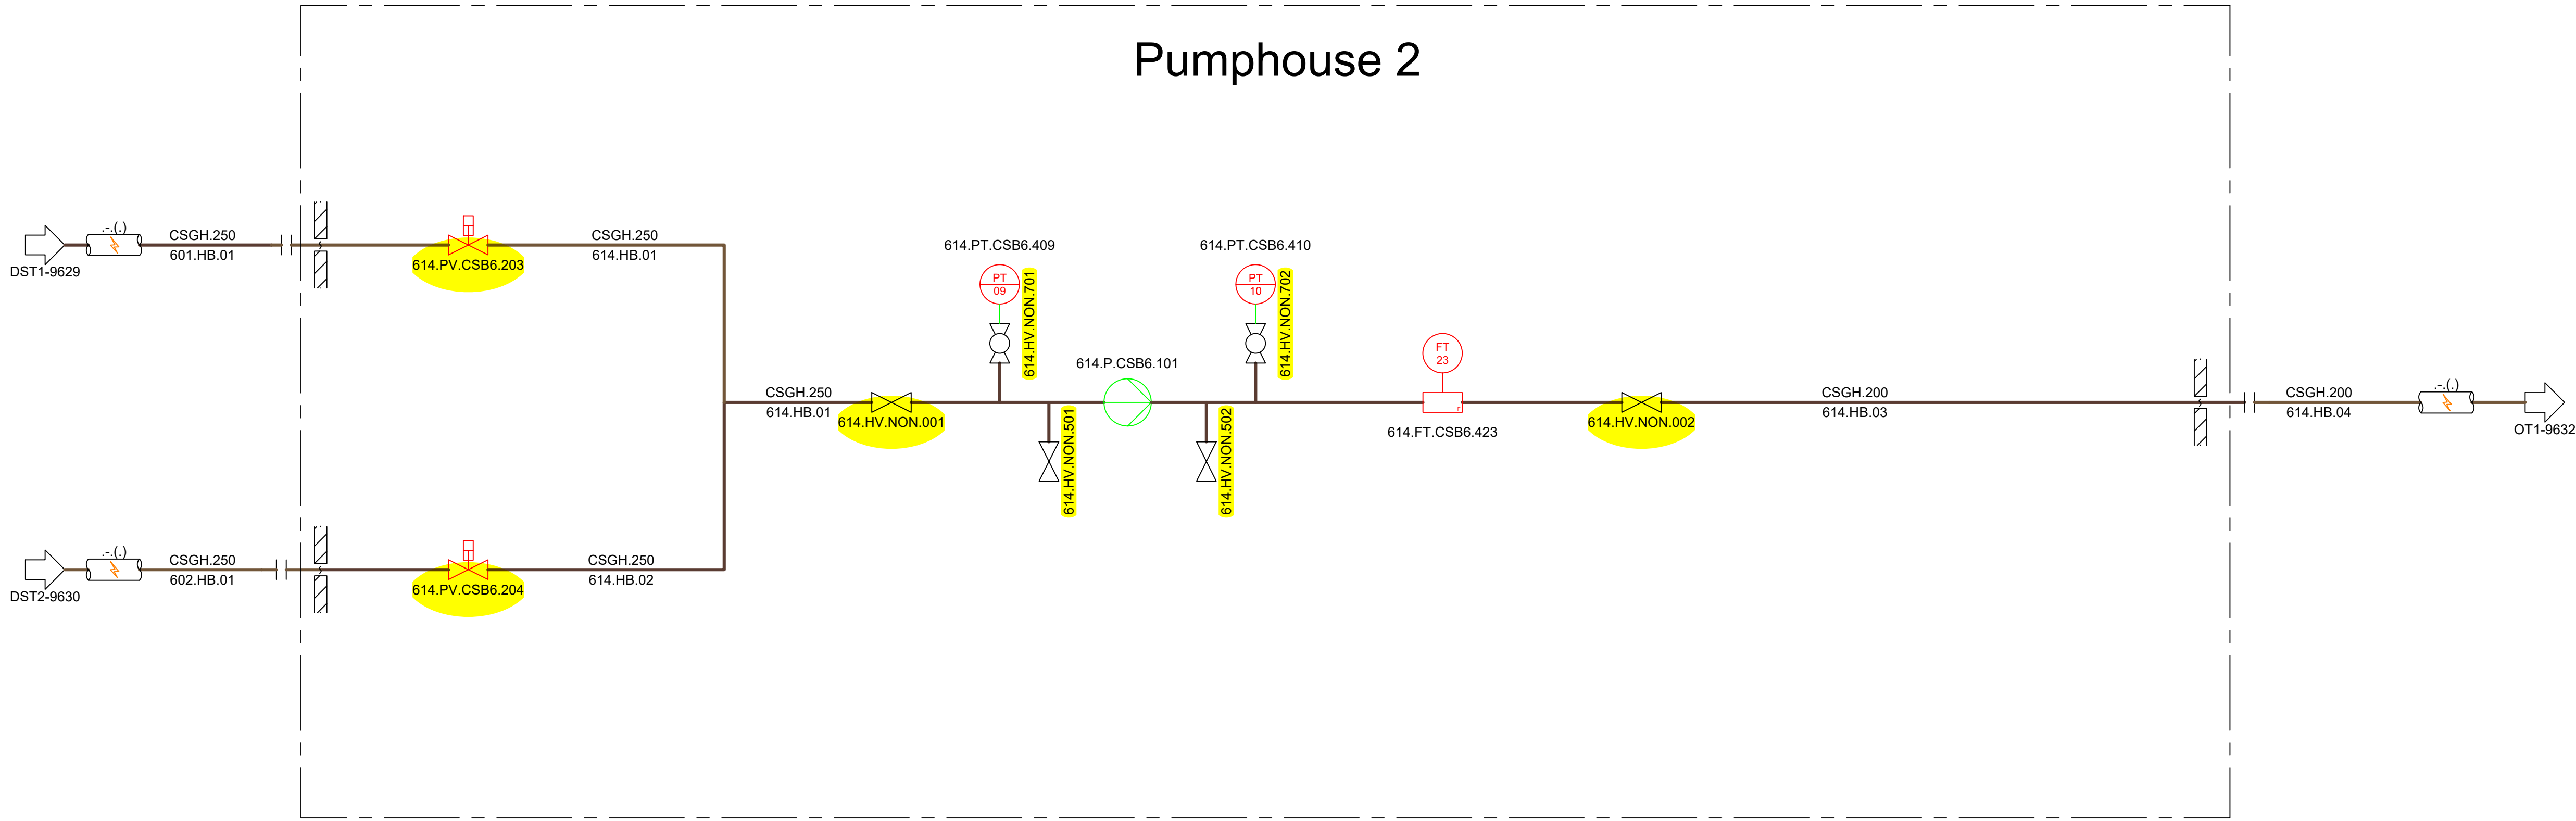


Rev. Nr.:	Rev. Dato:	Rev. Description:	
Builder:	ST1		
Project:	SLK		
Subject:	DST pump		
	Rev. 6		
Int.:MDC	QC:CM	APP.:	Date: 15-10-2025
LUNDSBY RENEWABLE SOLUTIONS			Lundsby Renewable Solutions A/S, Hjarbækvej 65, 8831 Løgstrup Tlf.: +45 96 49 43 00 Info@lundsby.dk This Drawing is subject to copyright and may not be reproduced without permission from Lundsby Renewable Solutions A/S
			Project nr.:1768 Drawing nr.: 9631 FORMAT: A1

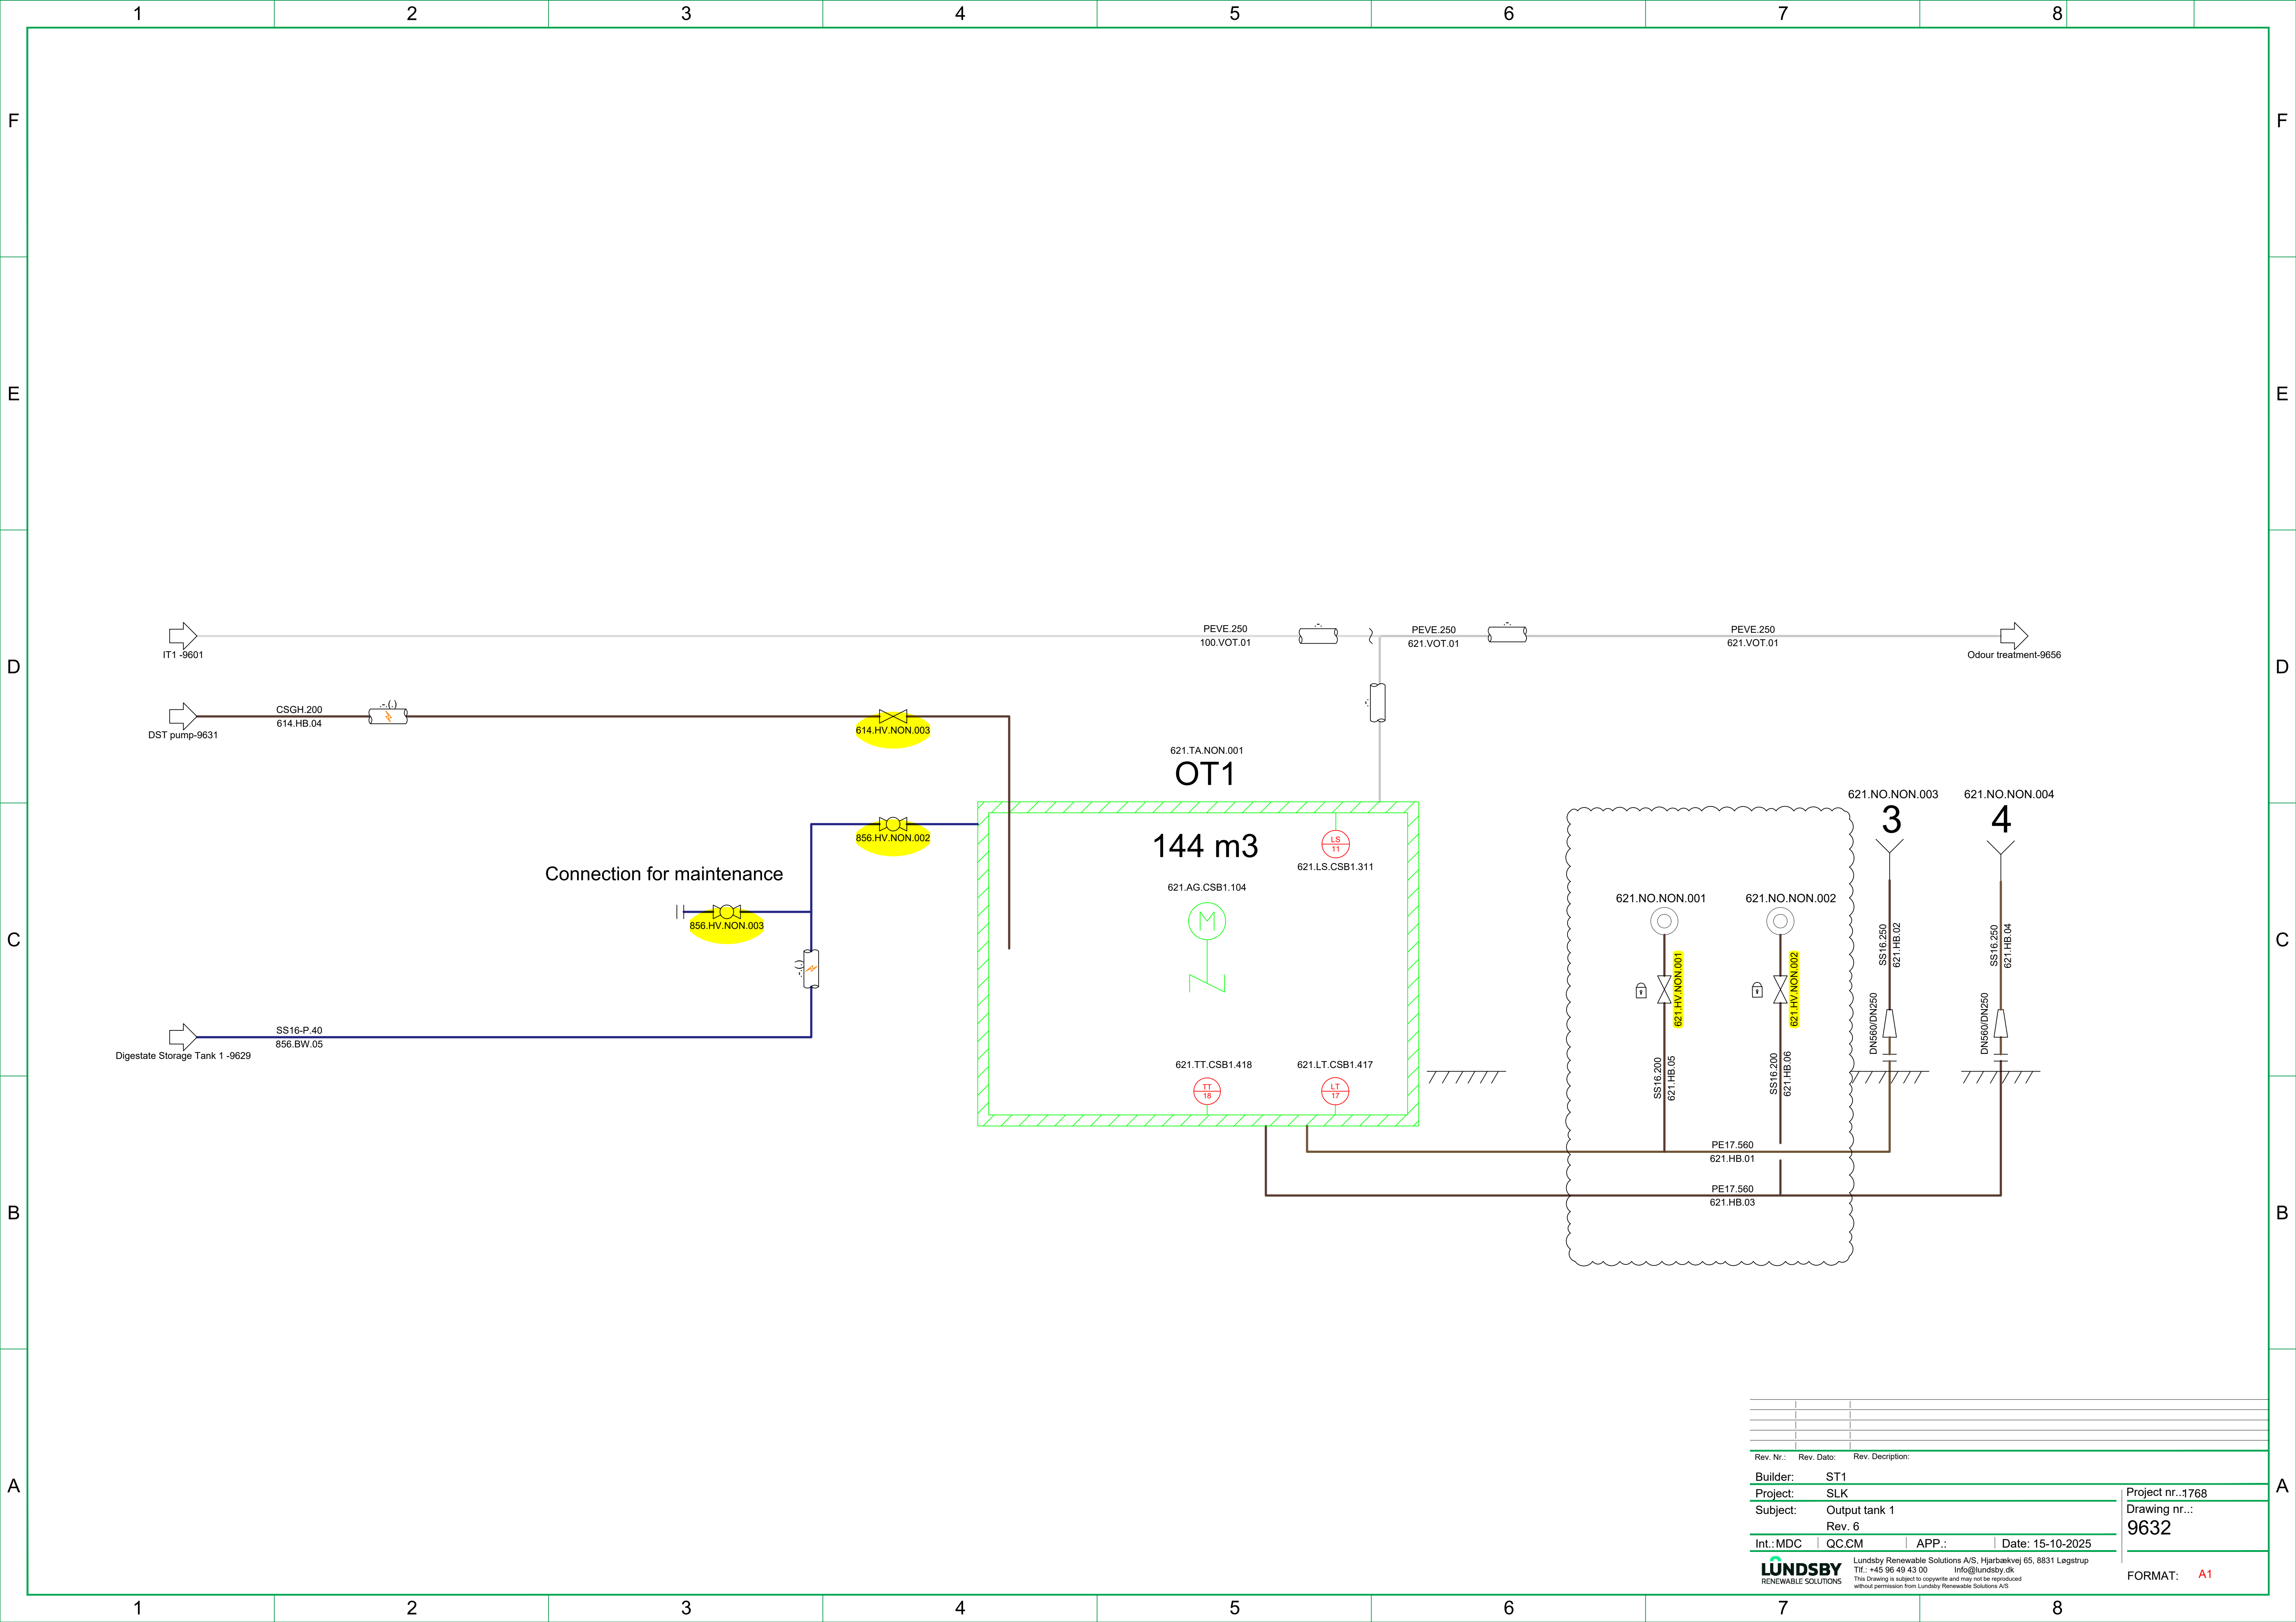

Rev. Nr.:	Rev. Dato:	Rev. Description:
Builder:	ST1	
Project:	SLK	
Subject:	Output tank 1	
Rev. 6		
Int.:MDC	QC:CM	APP.:
Date: 15-10-2025		
LUNDSBY RENEWABLE SOLUTIONS		
Lundsgby Renewable Solutions A/S, Hjarbrækvej 65, 8831 Lægstrup Tlf.: +45 96 49 43 00 Info@lundsgby.dk This Drawing is subject to copyright and may not be reproduced without permission from Lundsgby Renewable Solutions A/S		
Project nr.:1768 Drawing nr.: 9632		FORMAT: A1

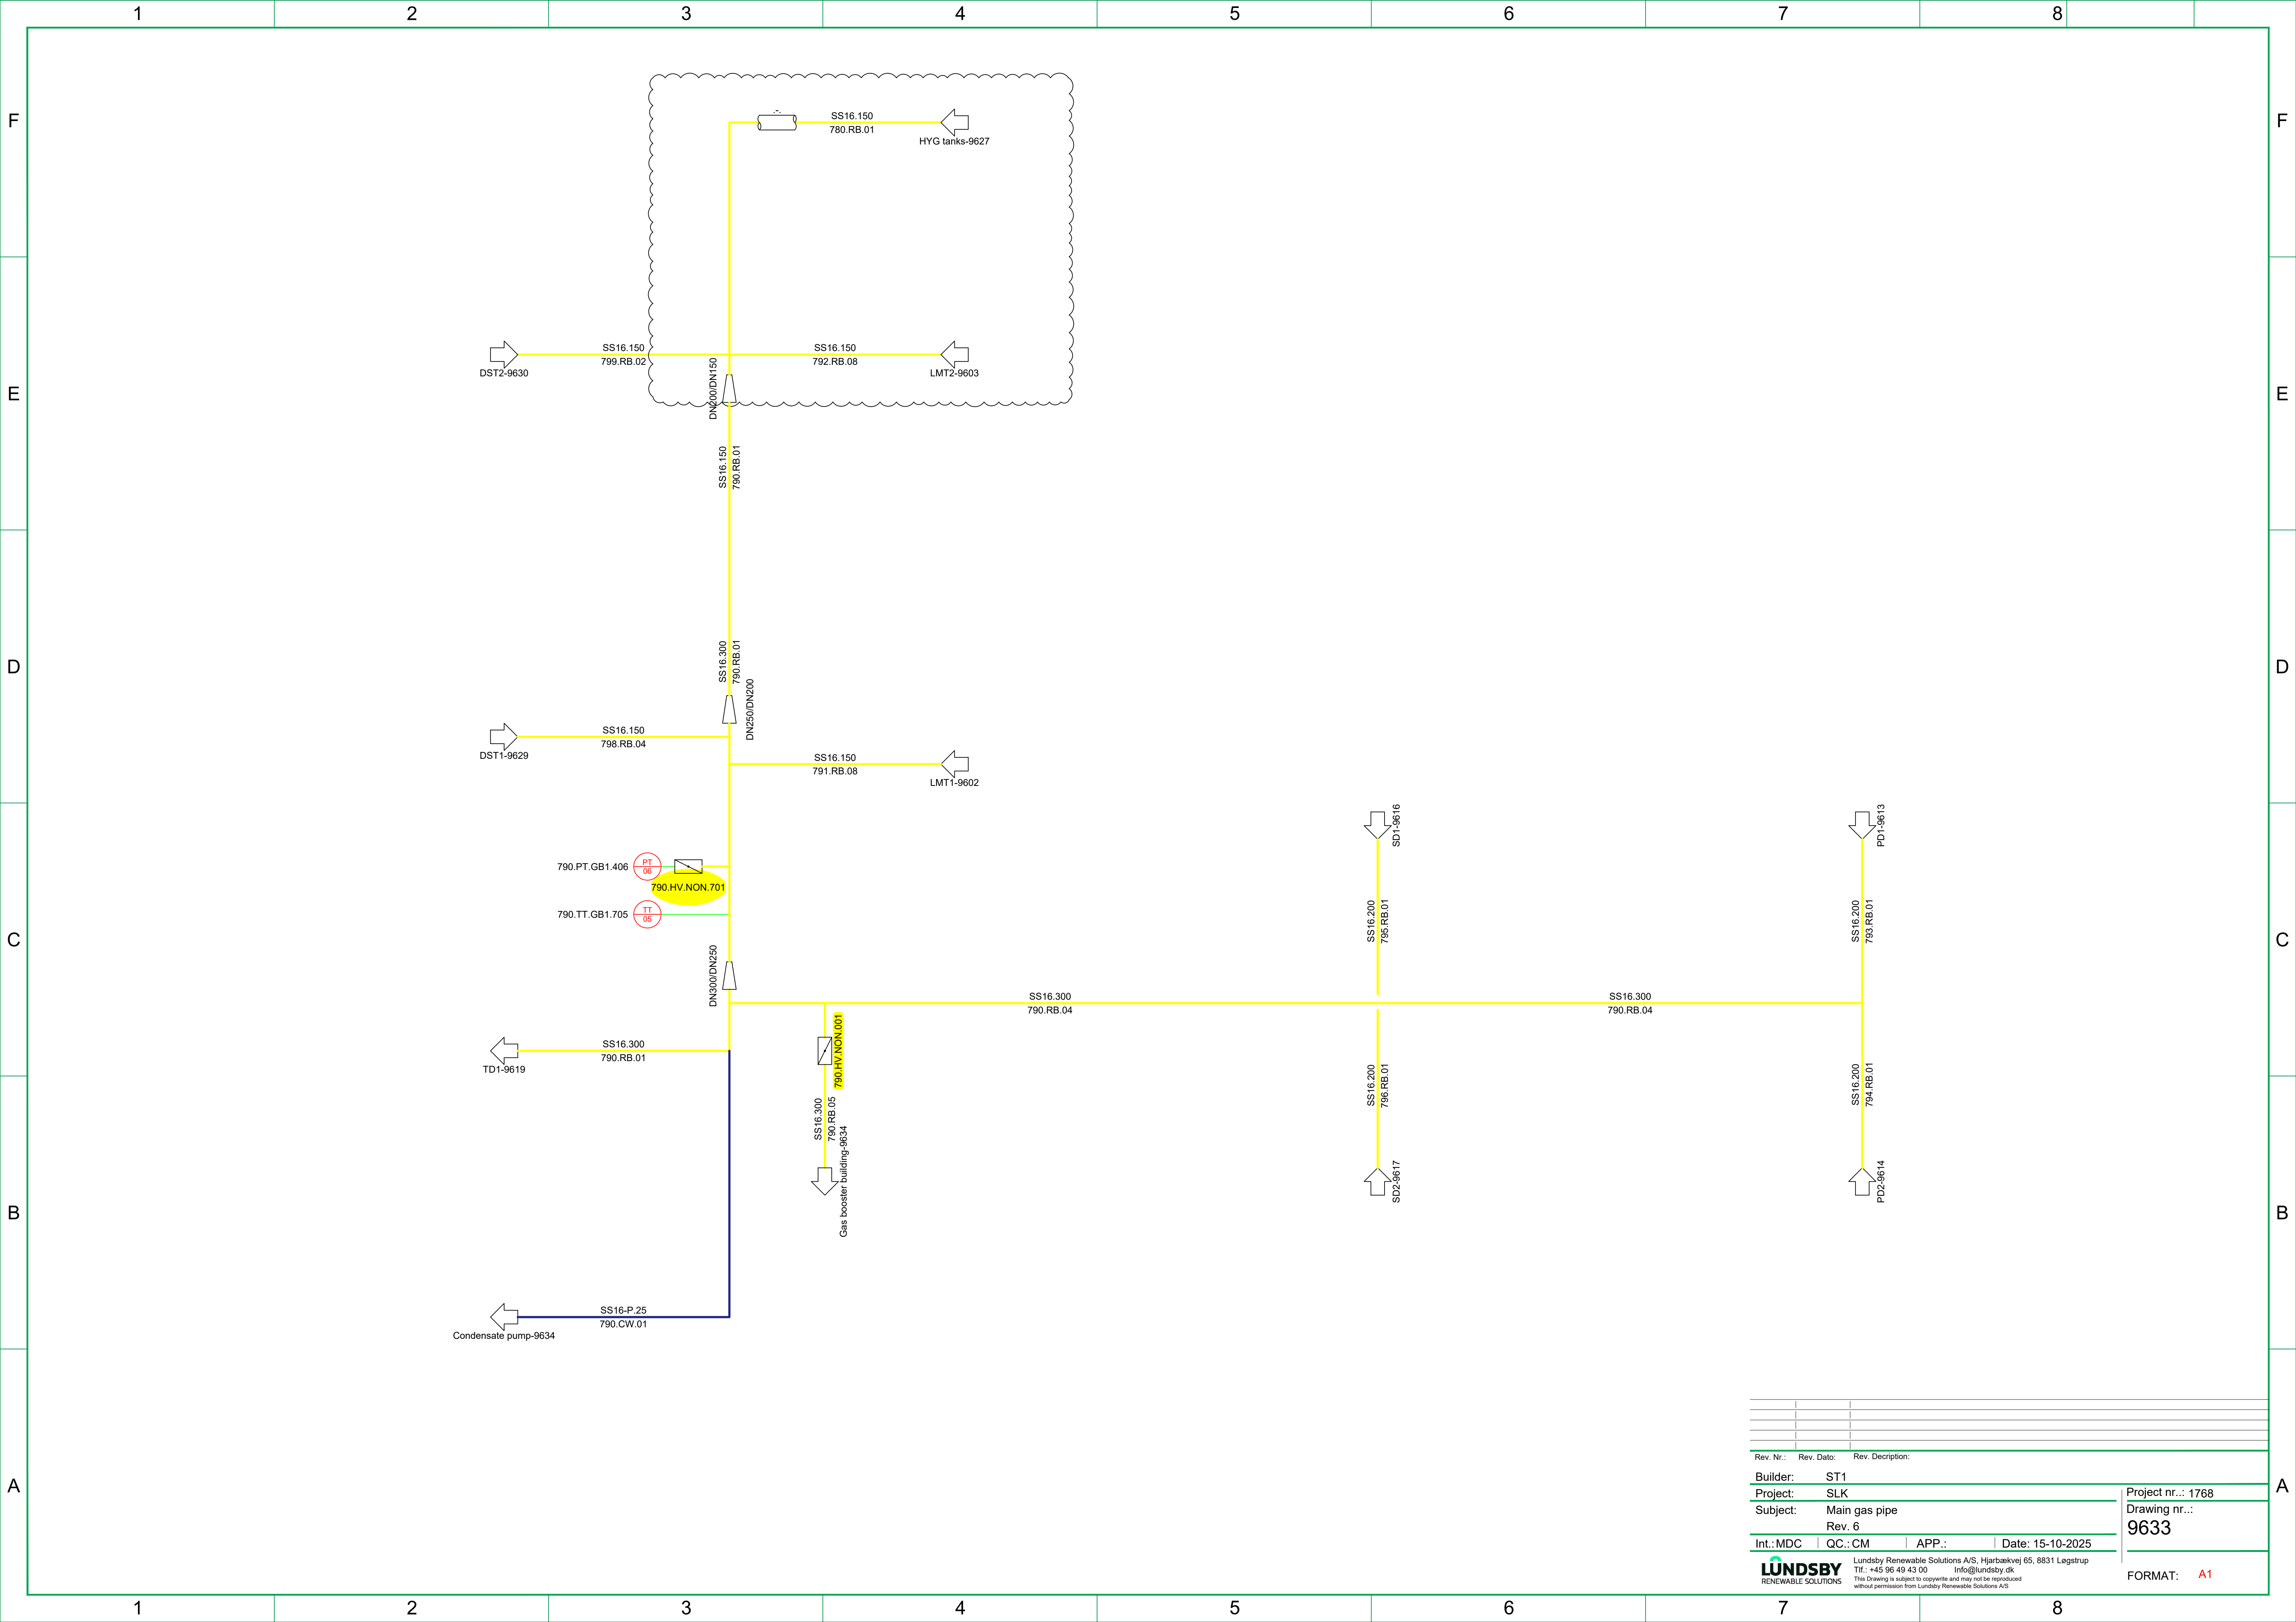


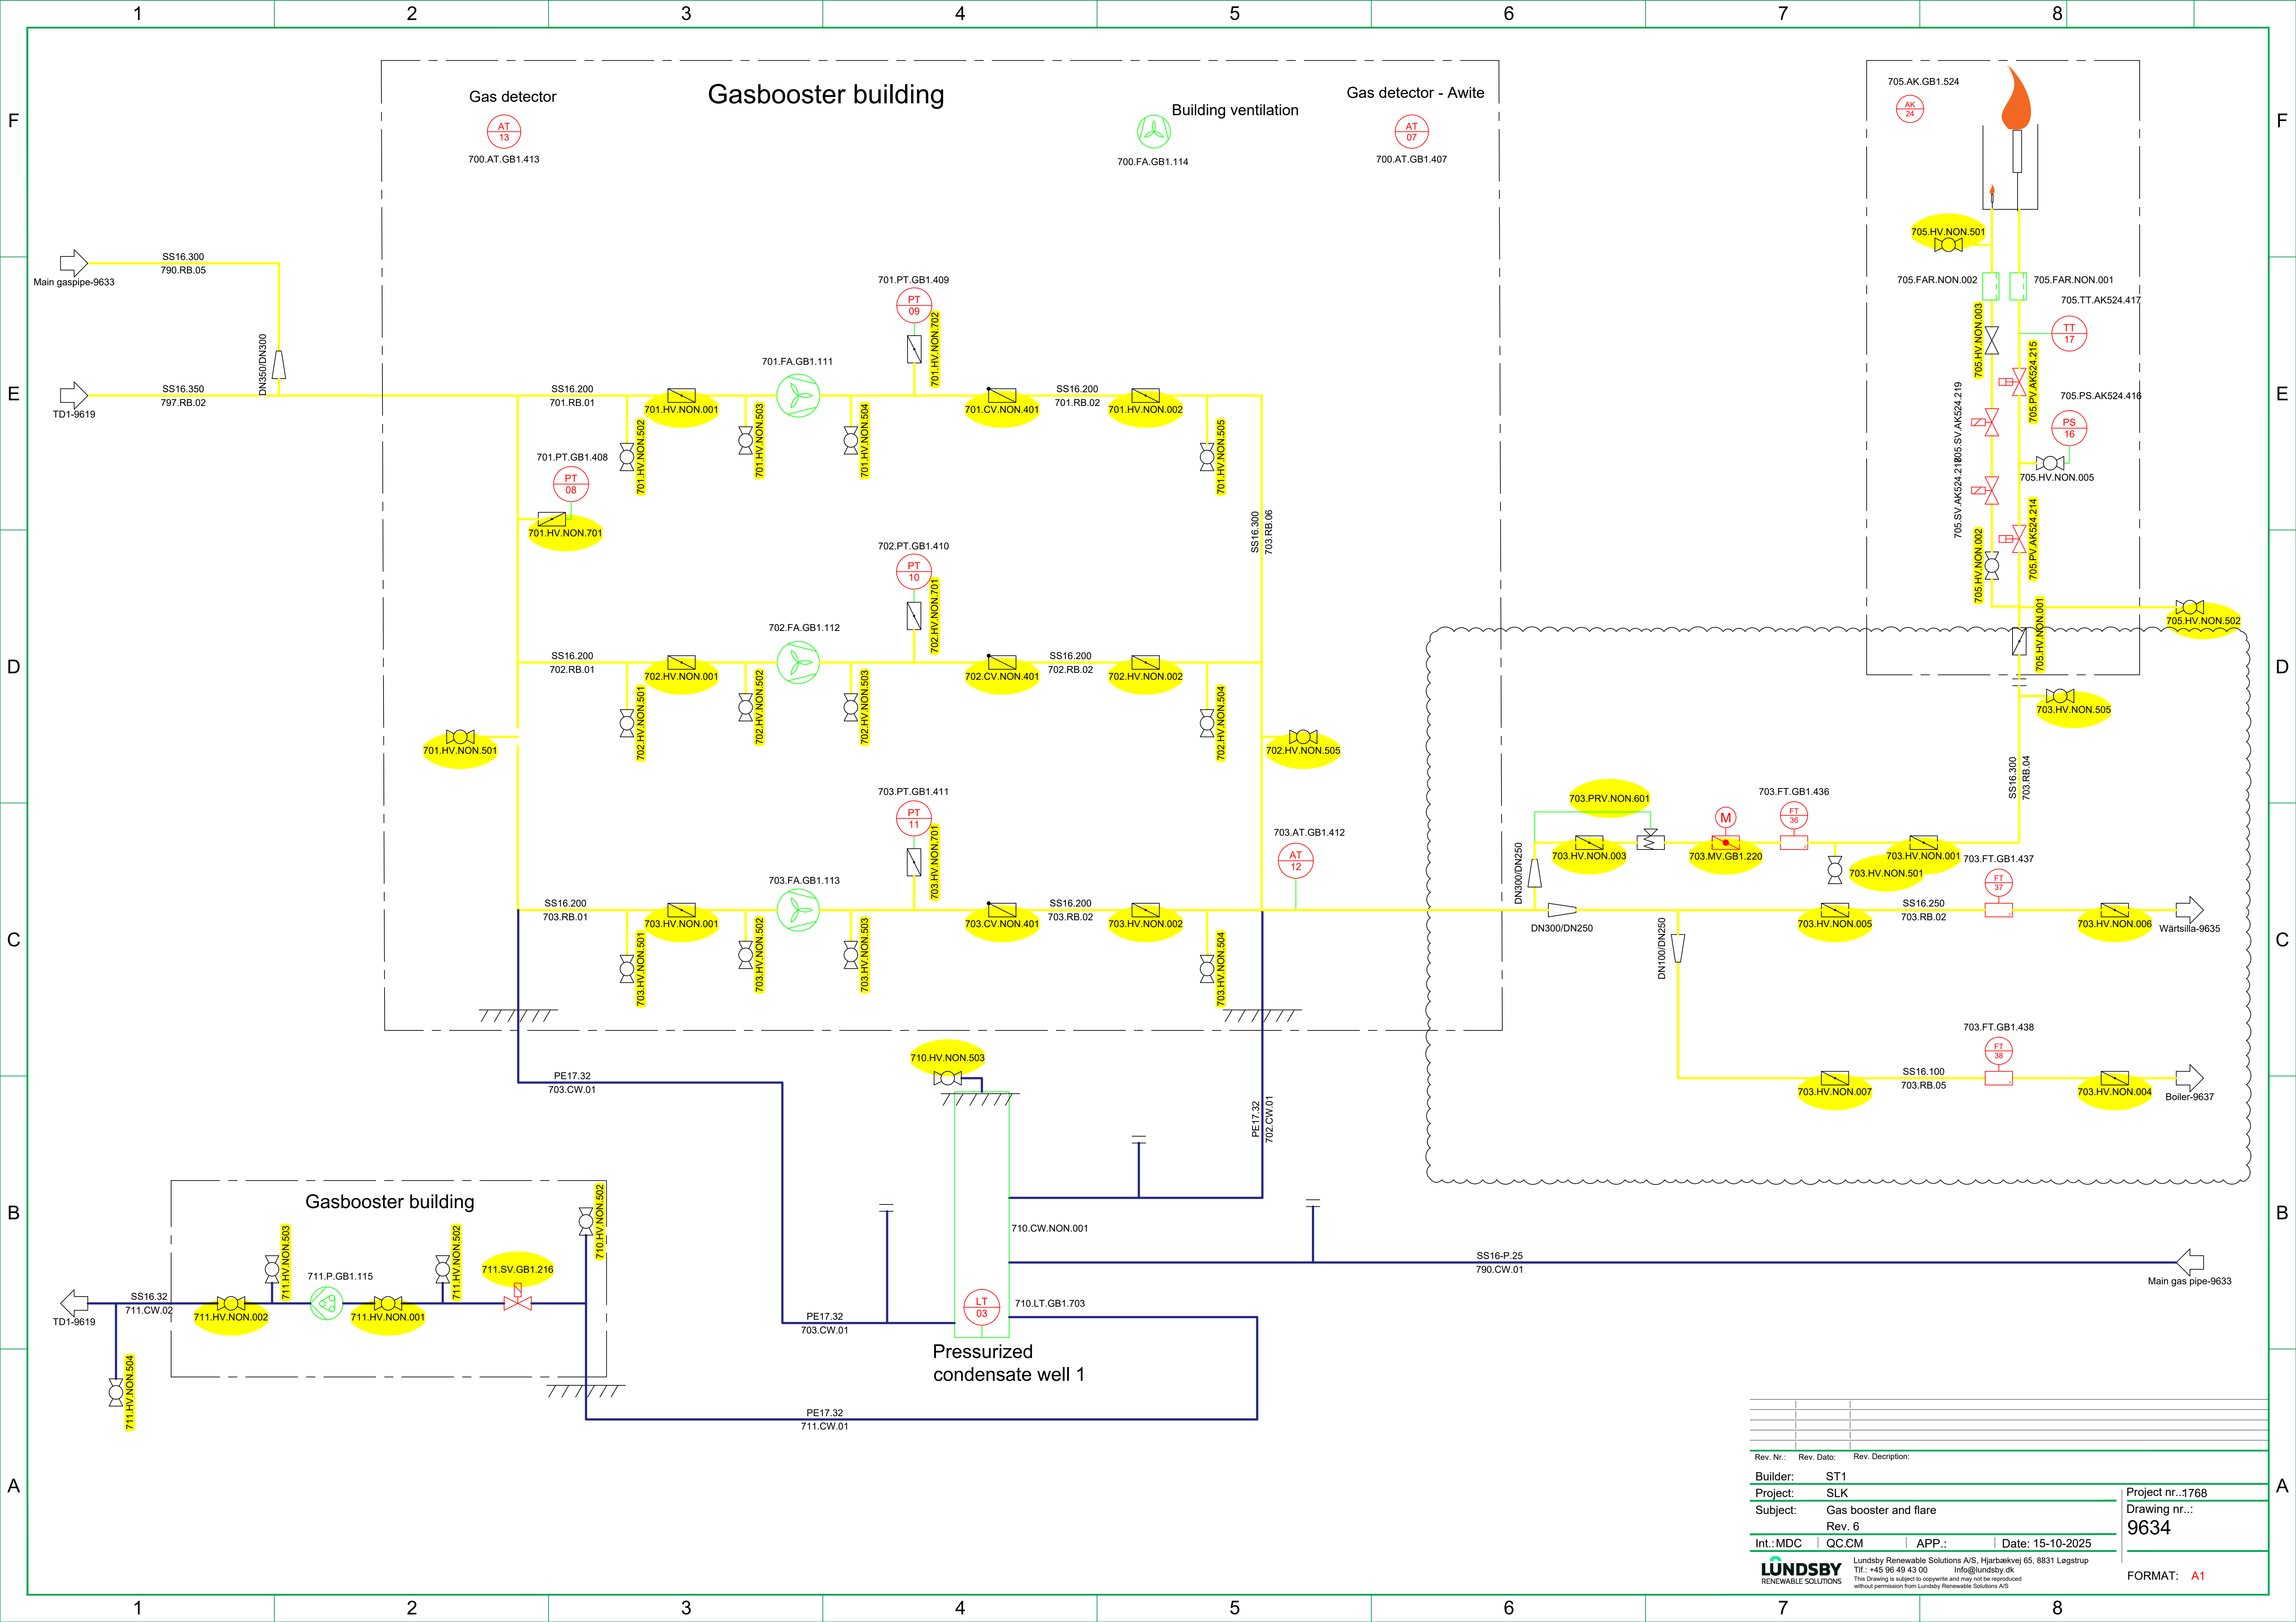


Rev. Nr.:	Rev. Dato:	Rev. Description:
Builder:	ST1	
Project:	SLK	
Subject:	Gas booster and flare	
Rev. 6		
Int.:MDC	QC:CM	APP.:
Date:	15-10-2025	
LUNDSBY RENEWABLE SOLUTIONS		
Lundsby Renewable Solutions A/S, Hjarbækvej 65, 8831 Lægstrup Tlf.: +45 96 49 43 00 info@lundsby.dk This Drawing is subject to copyright and may not be reproduced without permission from Lundsby Renewable Solutions A/S		
Project nr.:1768 Drawing nr.: 9634		FORMAT: A1

Wärtsillä

730-UPG-01


730-LBG-01

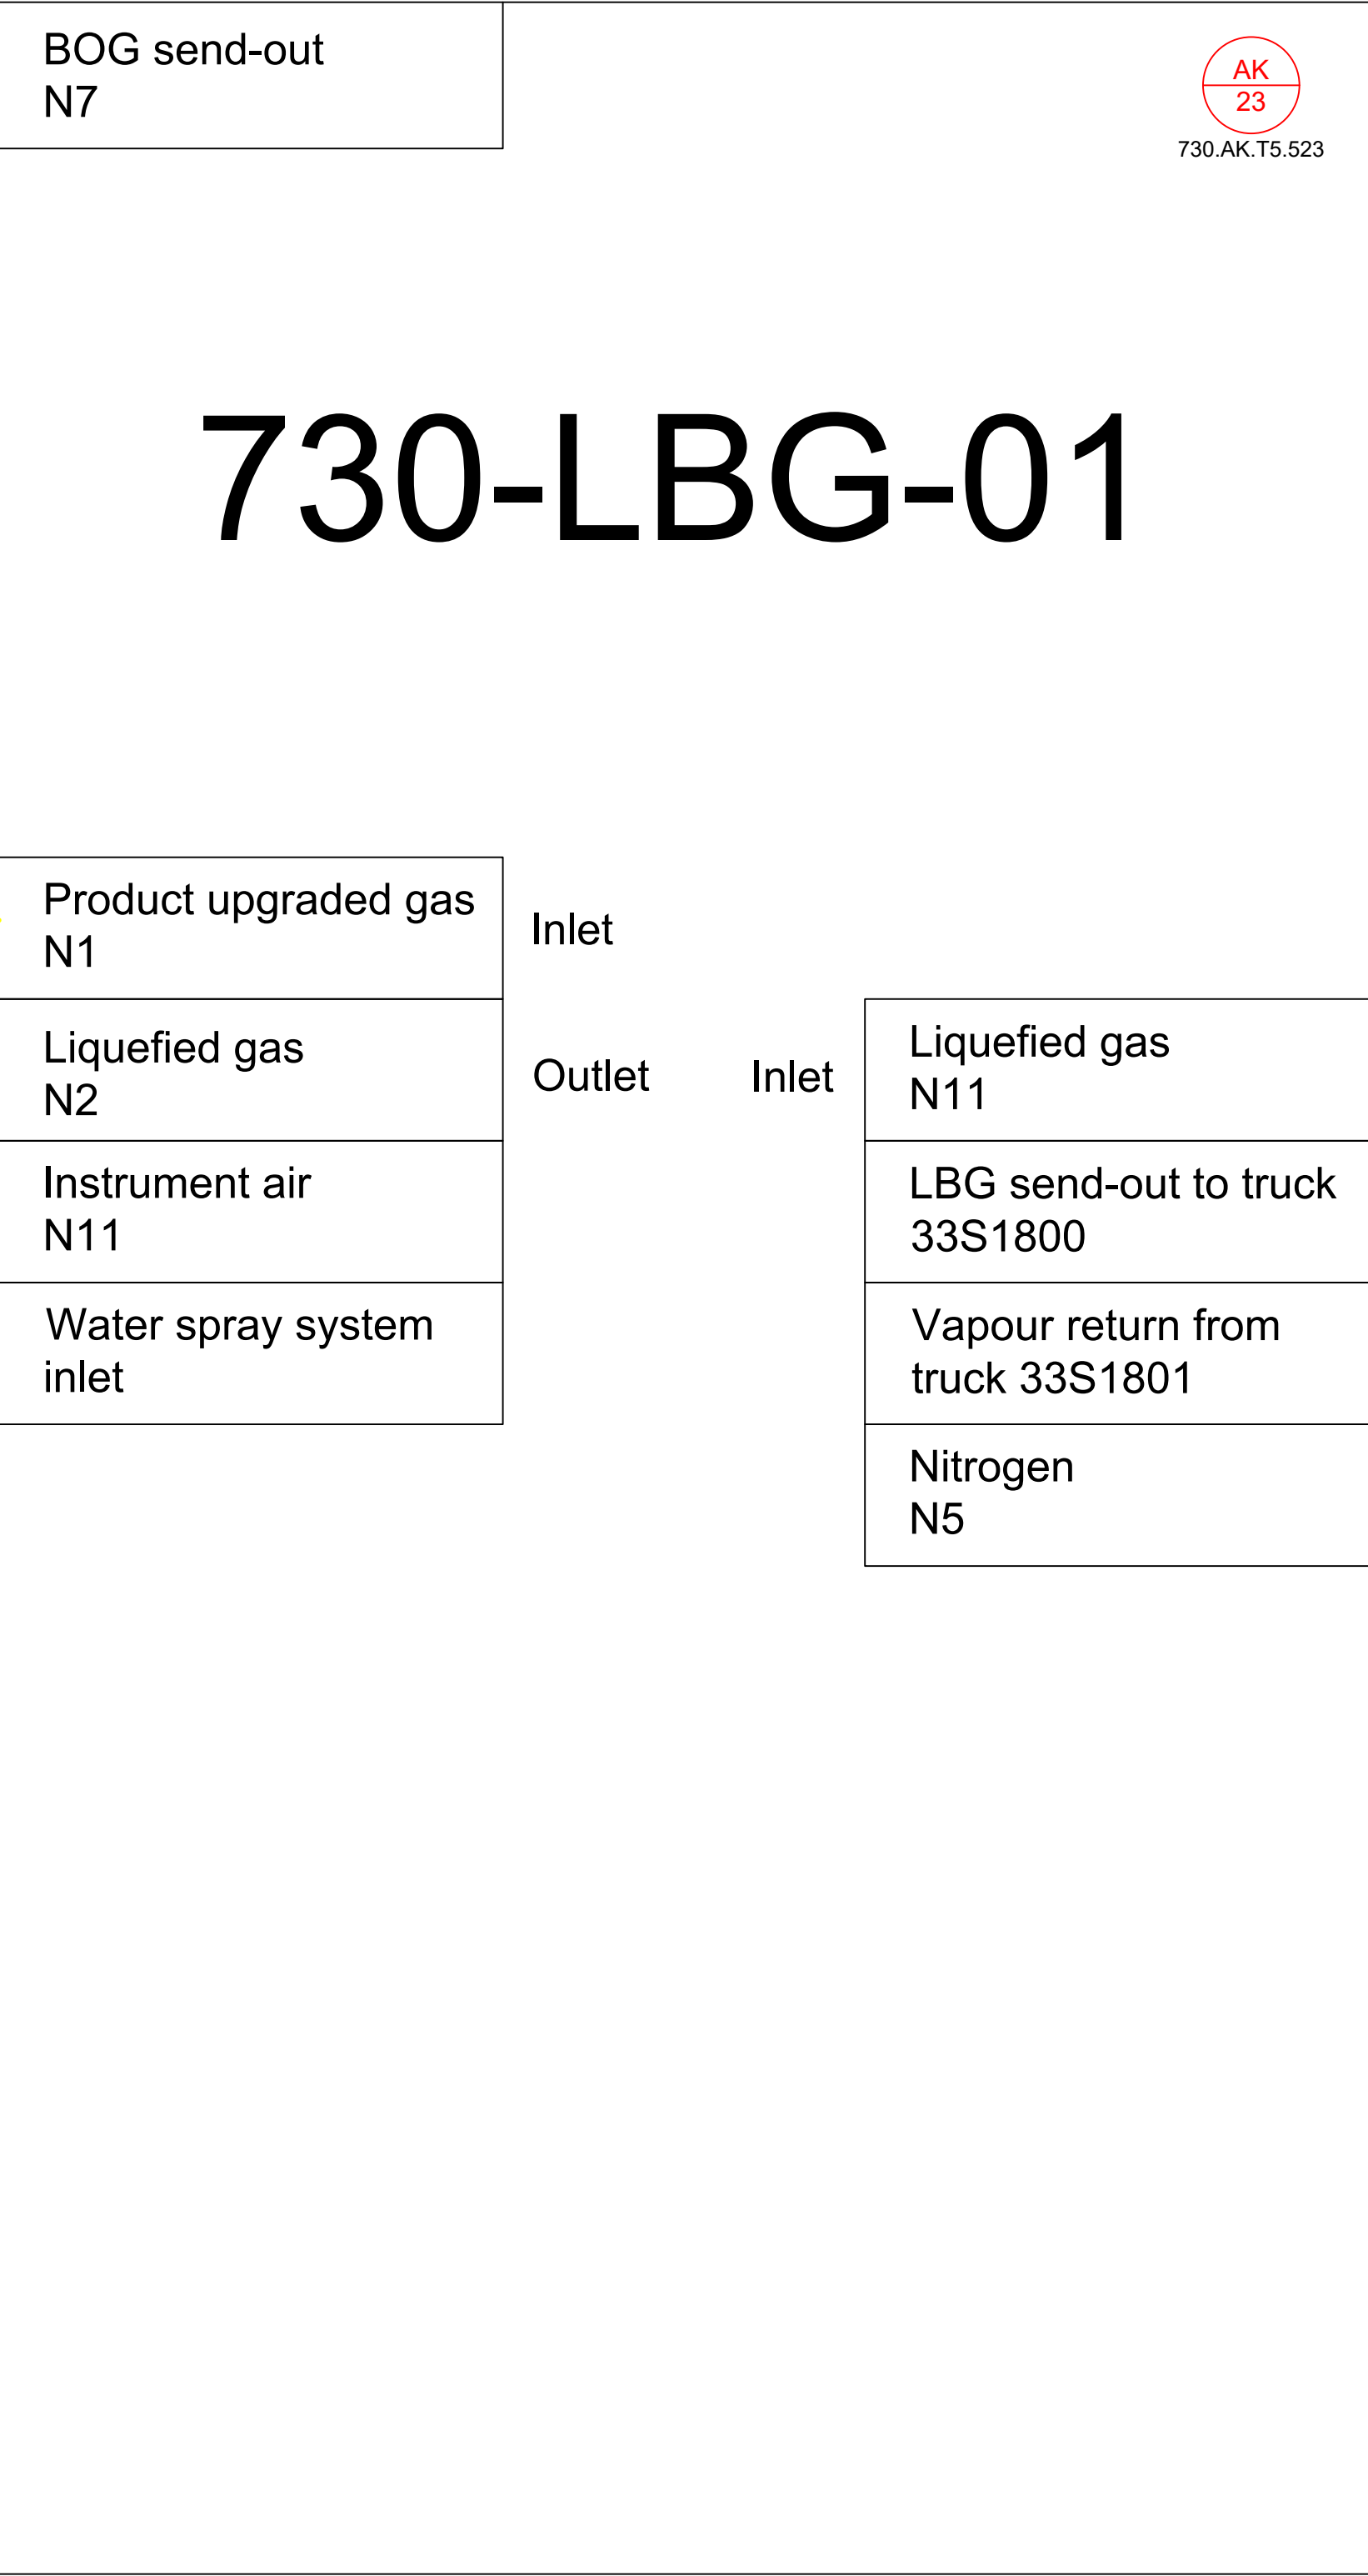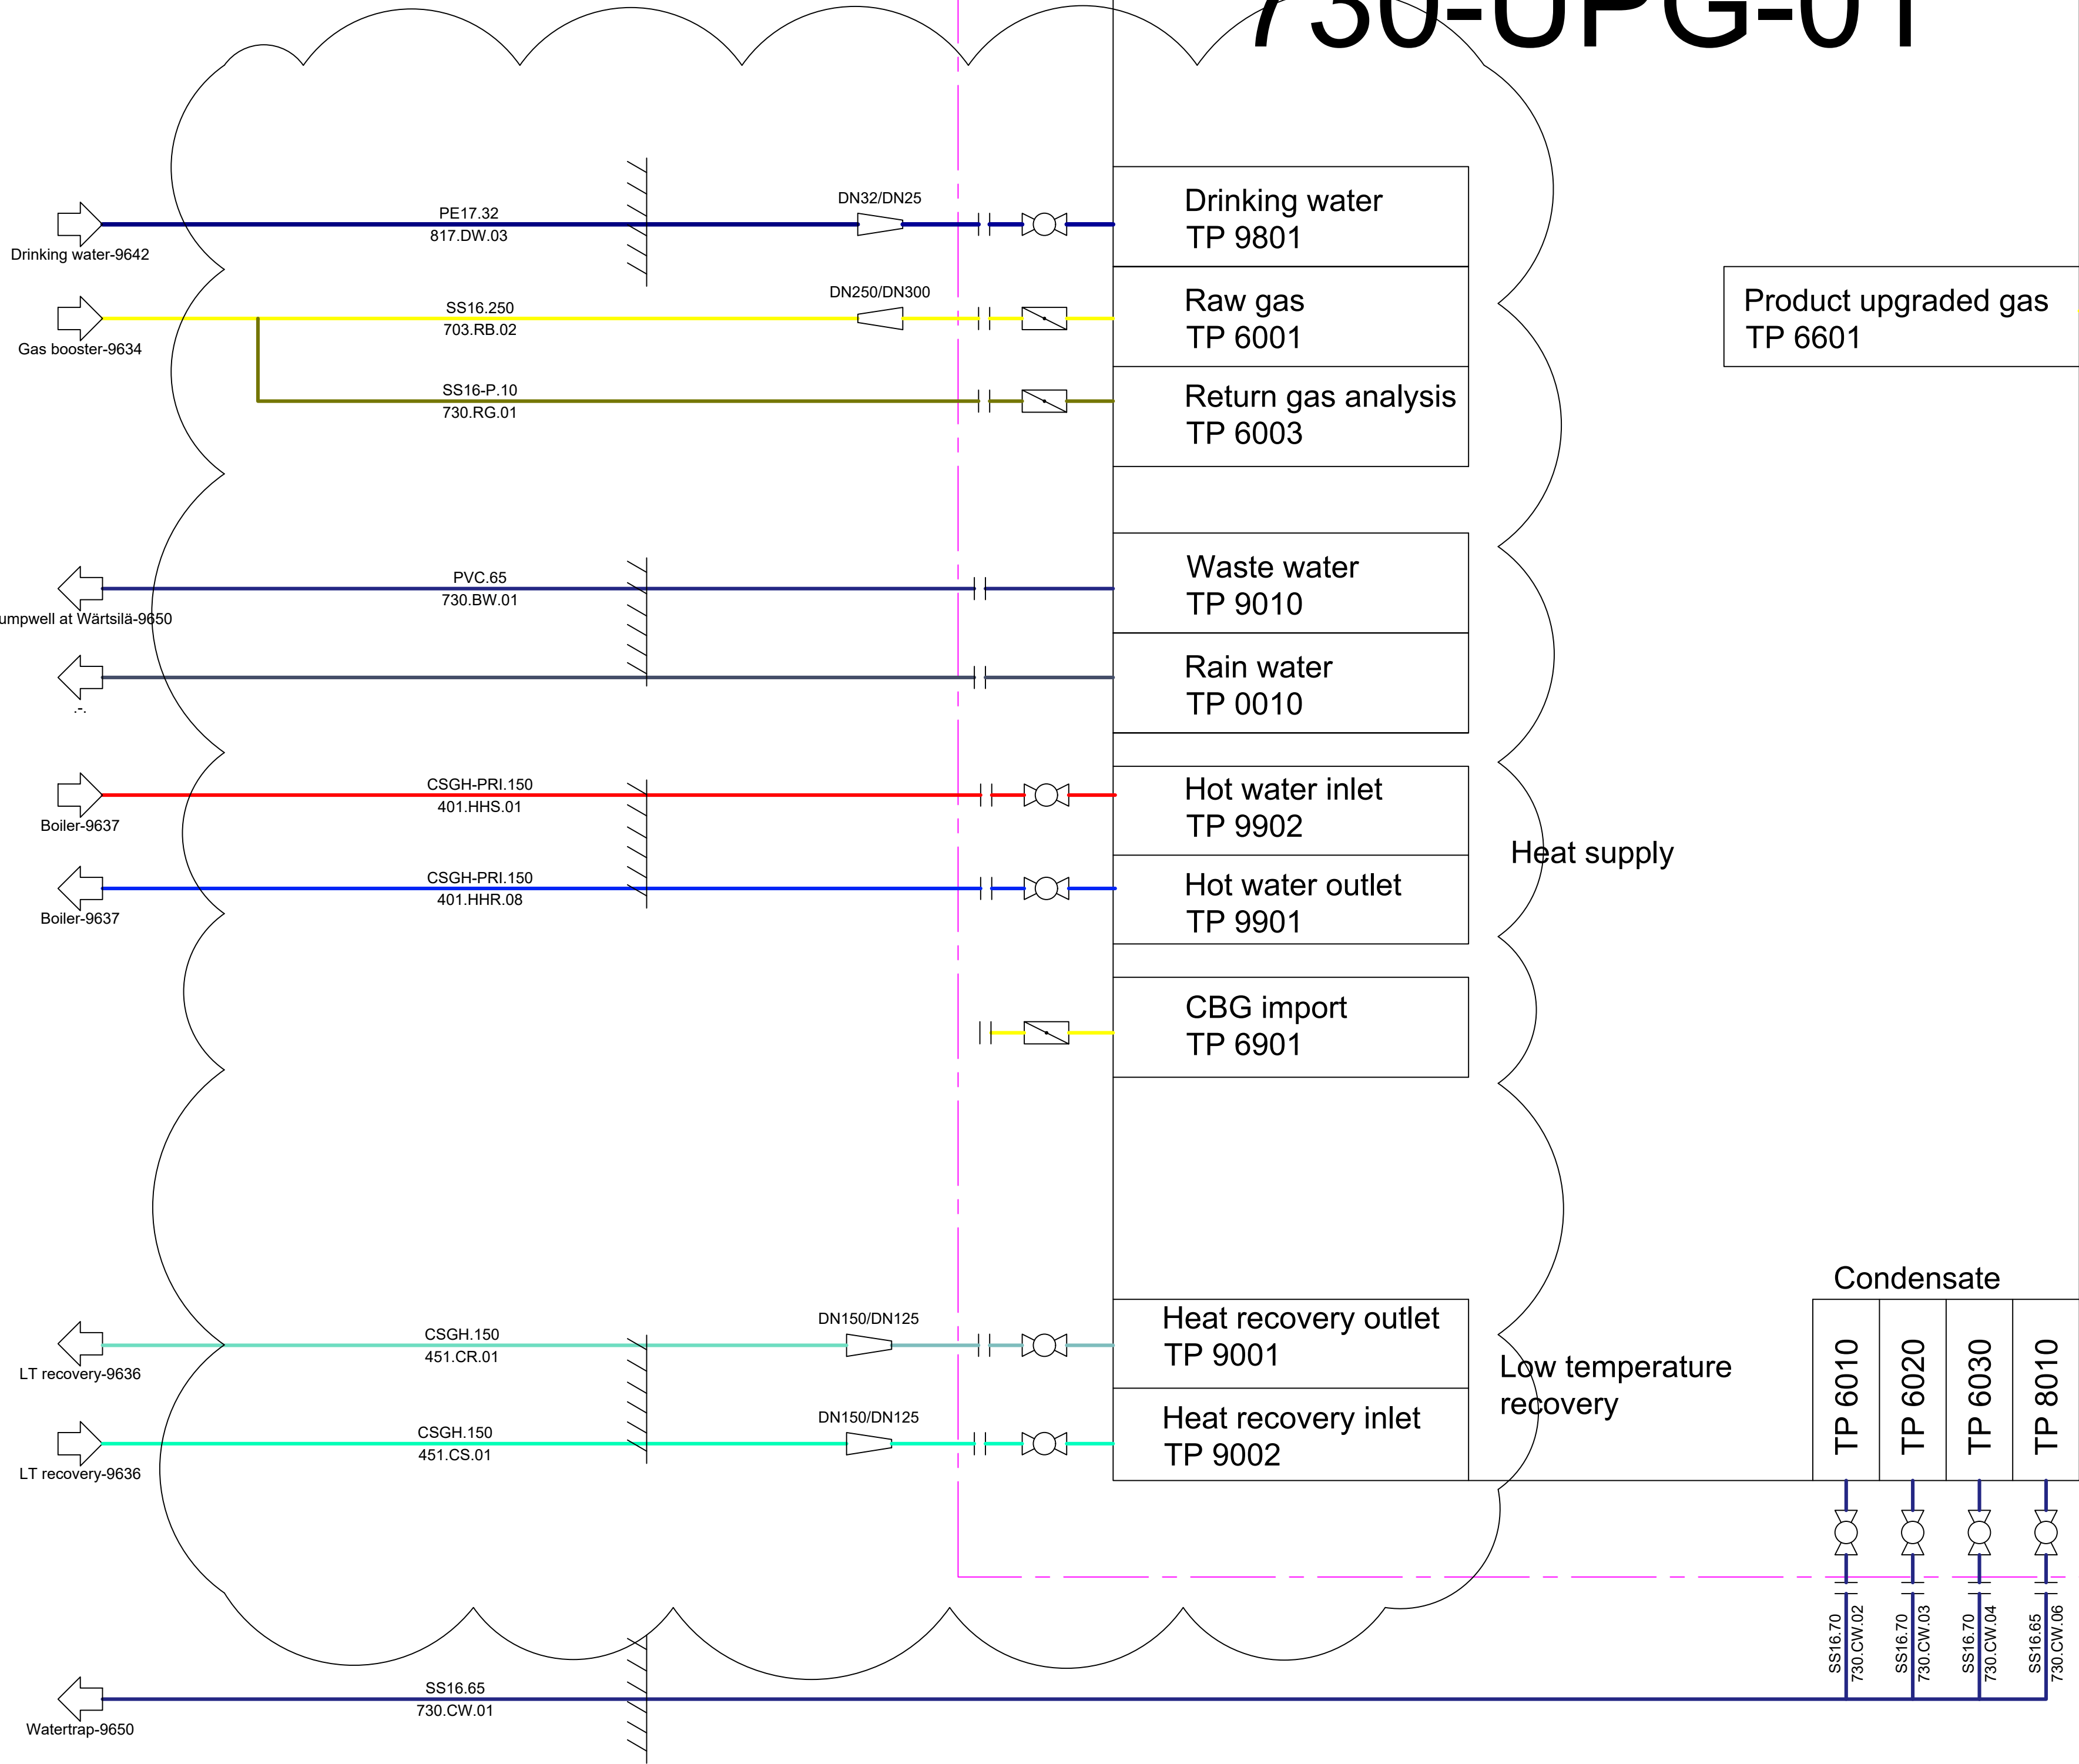


Rev. Nr.:	Rev. Dato:	Rev. Description:	
Builder:	ST1		
Project:	SLK		
Subject:	Upgrade		
	Rev. 6		
Int.:MDC	QC.CM	APP.:	Date: 15-10-2025
LUNDSBY RENEWABLE SOLUTIONS			Lundsbys Renewable Solutions A/S, Hjarbækvej 65, 8831 Løgstrup Tlf.: +45 96 49 43 00 Info@lundsbys.dk This Drawing is subject to copyright and may not be reproduced without permission from Lundsbys Renewable Solutions A/S
Project nr...:1768 Drawing nr...: 9635			FORMAT: A1

Technology building


Heat pump scope

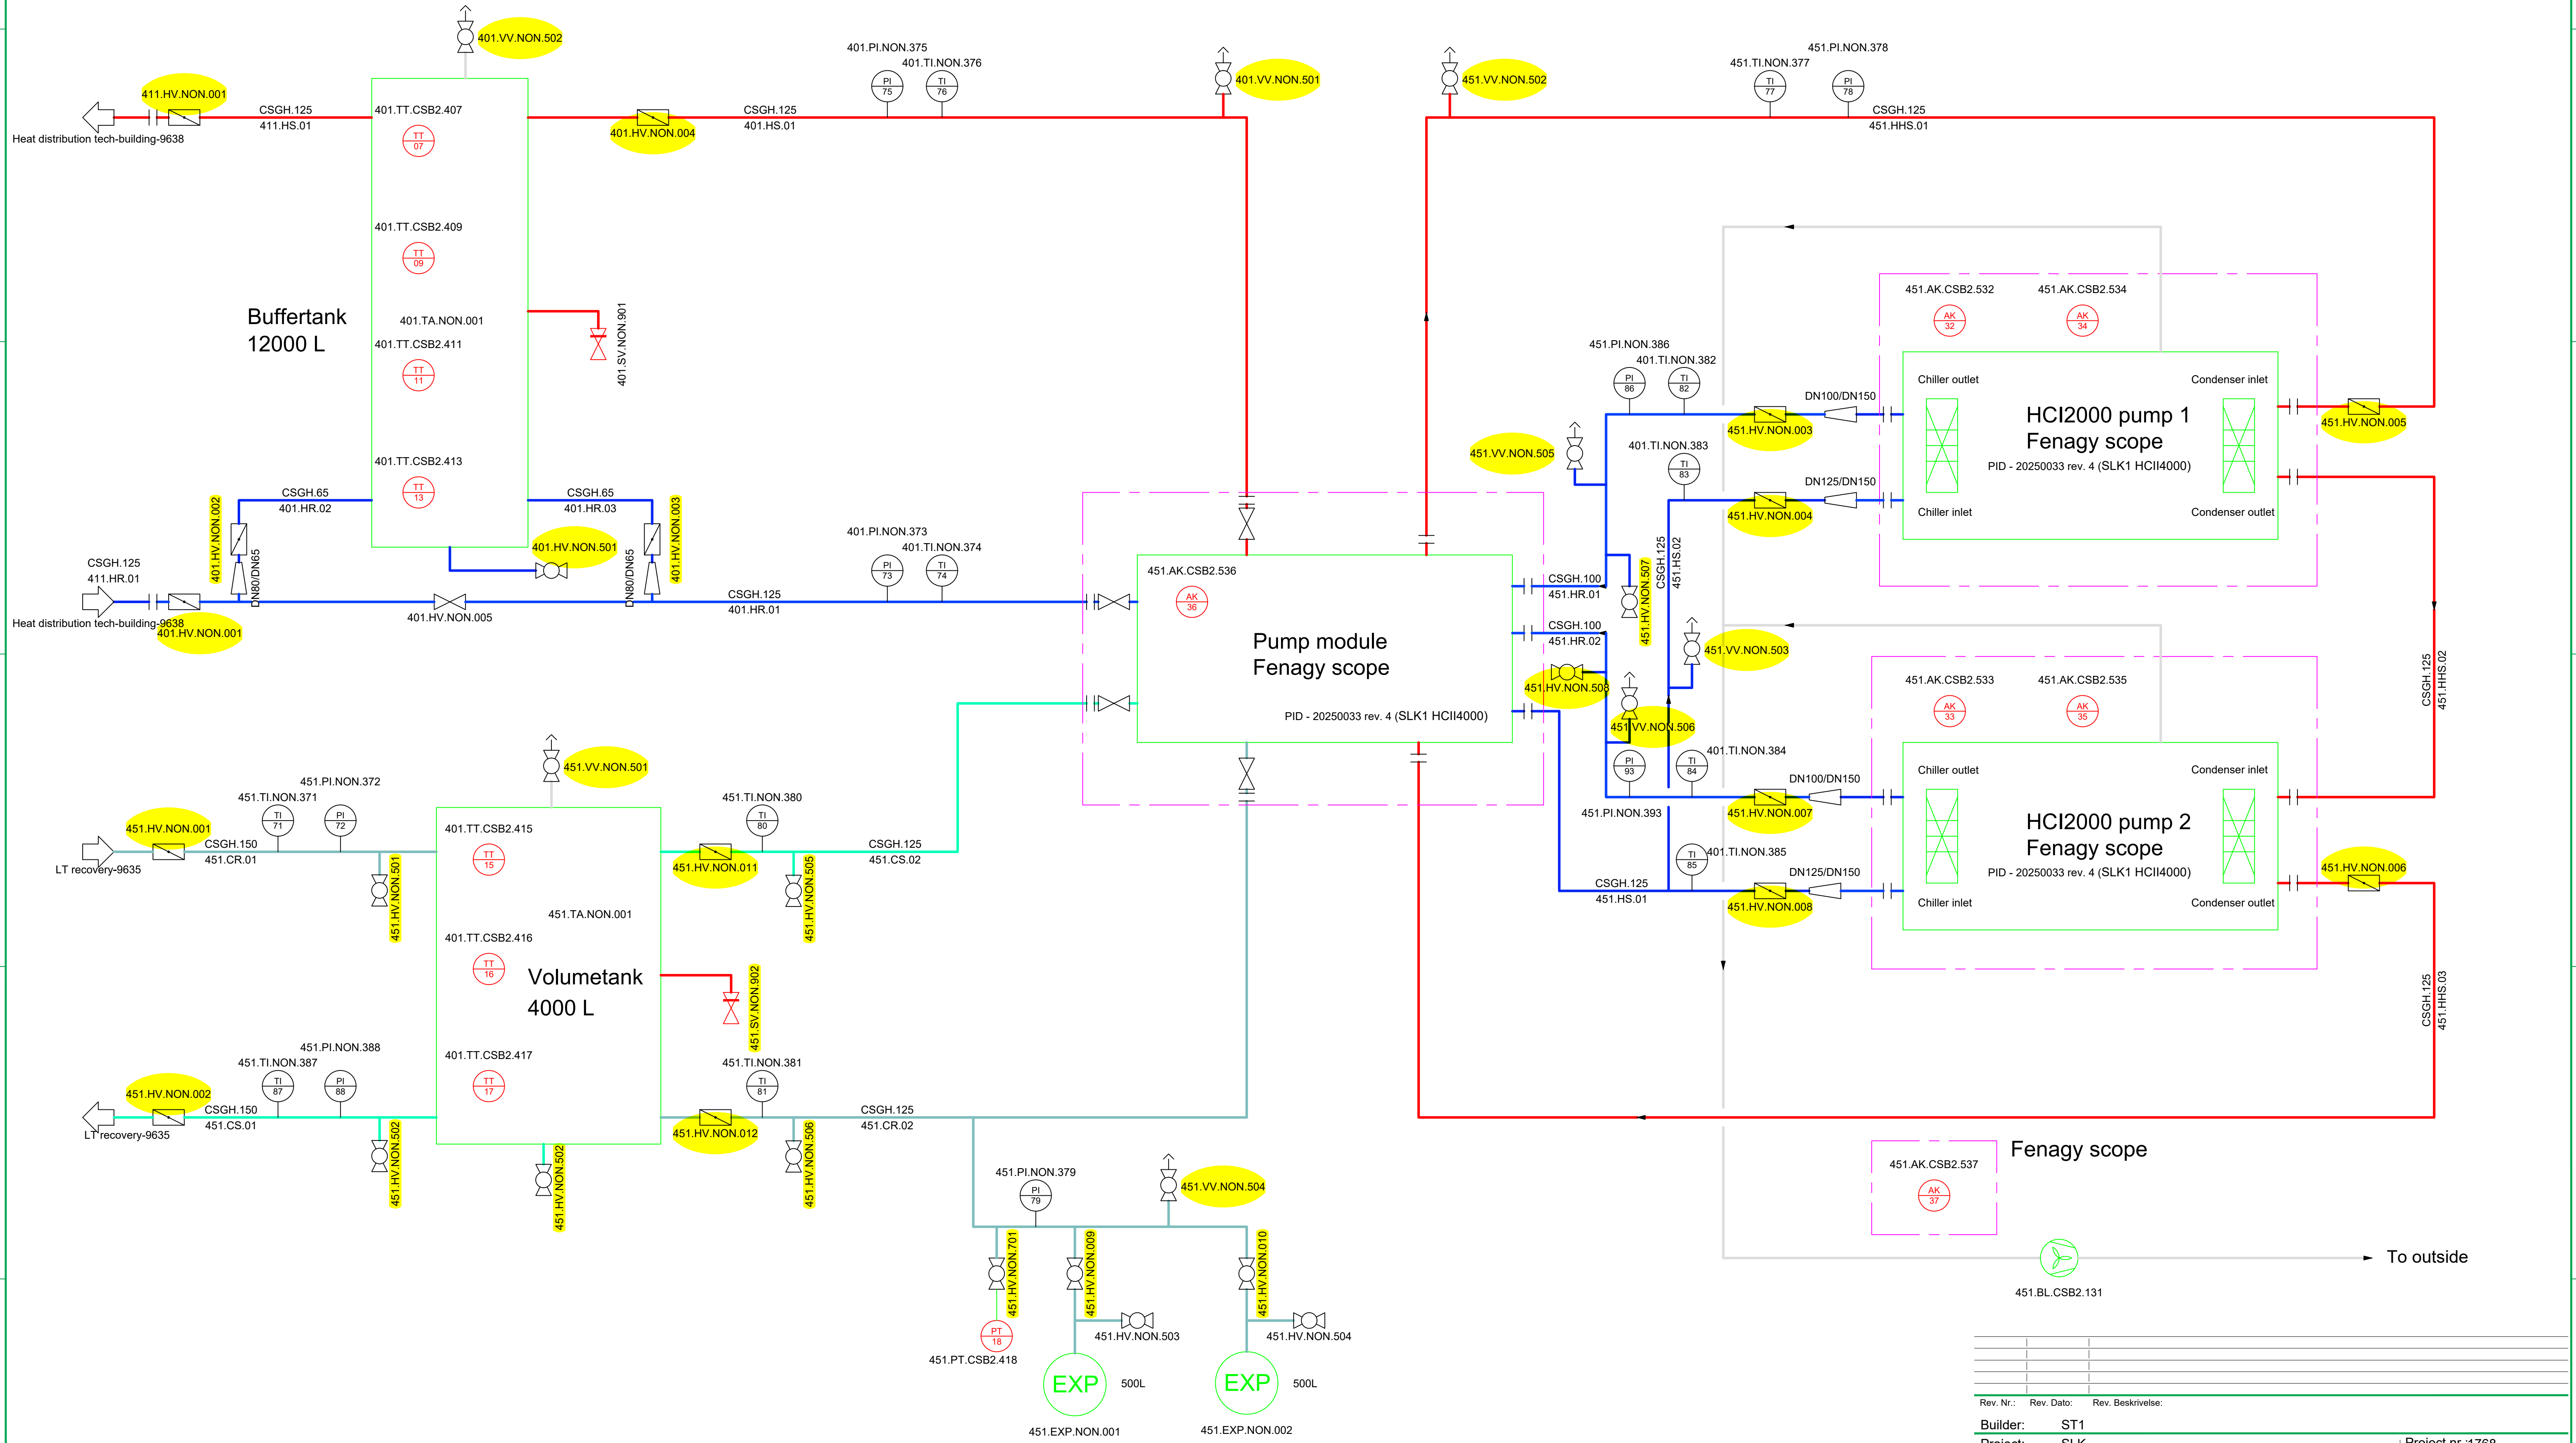

Rev. Nr.:	Rev. Dato:	Rev. Beskrivelse:
Builder:	ST1	
Project:	SLK	
Subject:	Heat pumps	
Rev.:	6	
Int.:MDC	QC:CM	APP.:Date: 15-10-2025
LUNDSBY RENEWABLE SOLUTIONS		
Lundsby Biogas A/S, Hjarbækvej 65, 8831 Løgstrup Tlf.: +45 96 49 43 00 info@lundsbybiogas.dk		
Denne tegning er underlagt copywrite op på ikke reproduceres uden tilladelse fra Lundsbybiogas A/S		
Project nr.:1768 Drawing nr.: 9636		FORMAT: A1

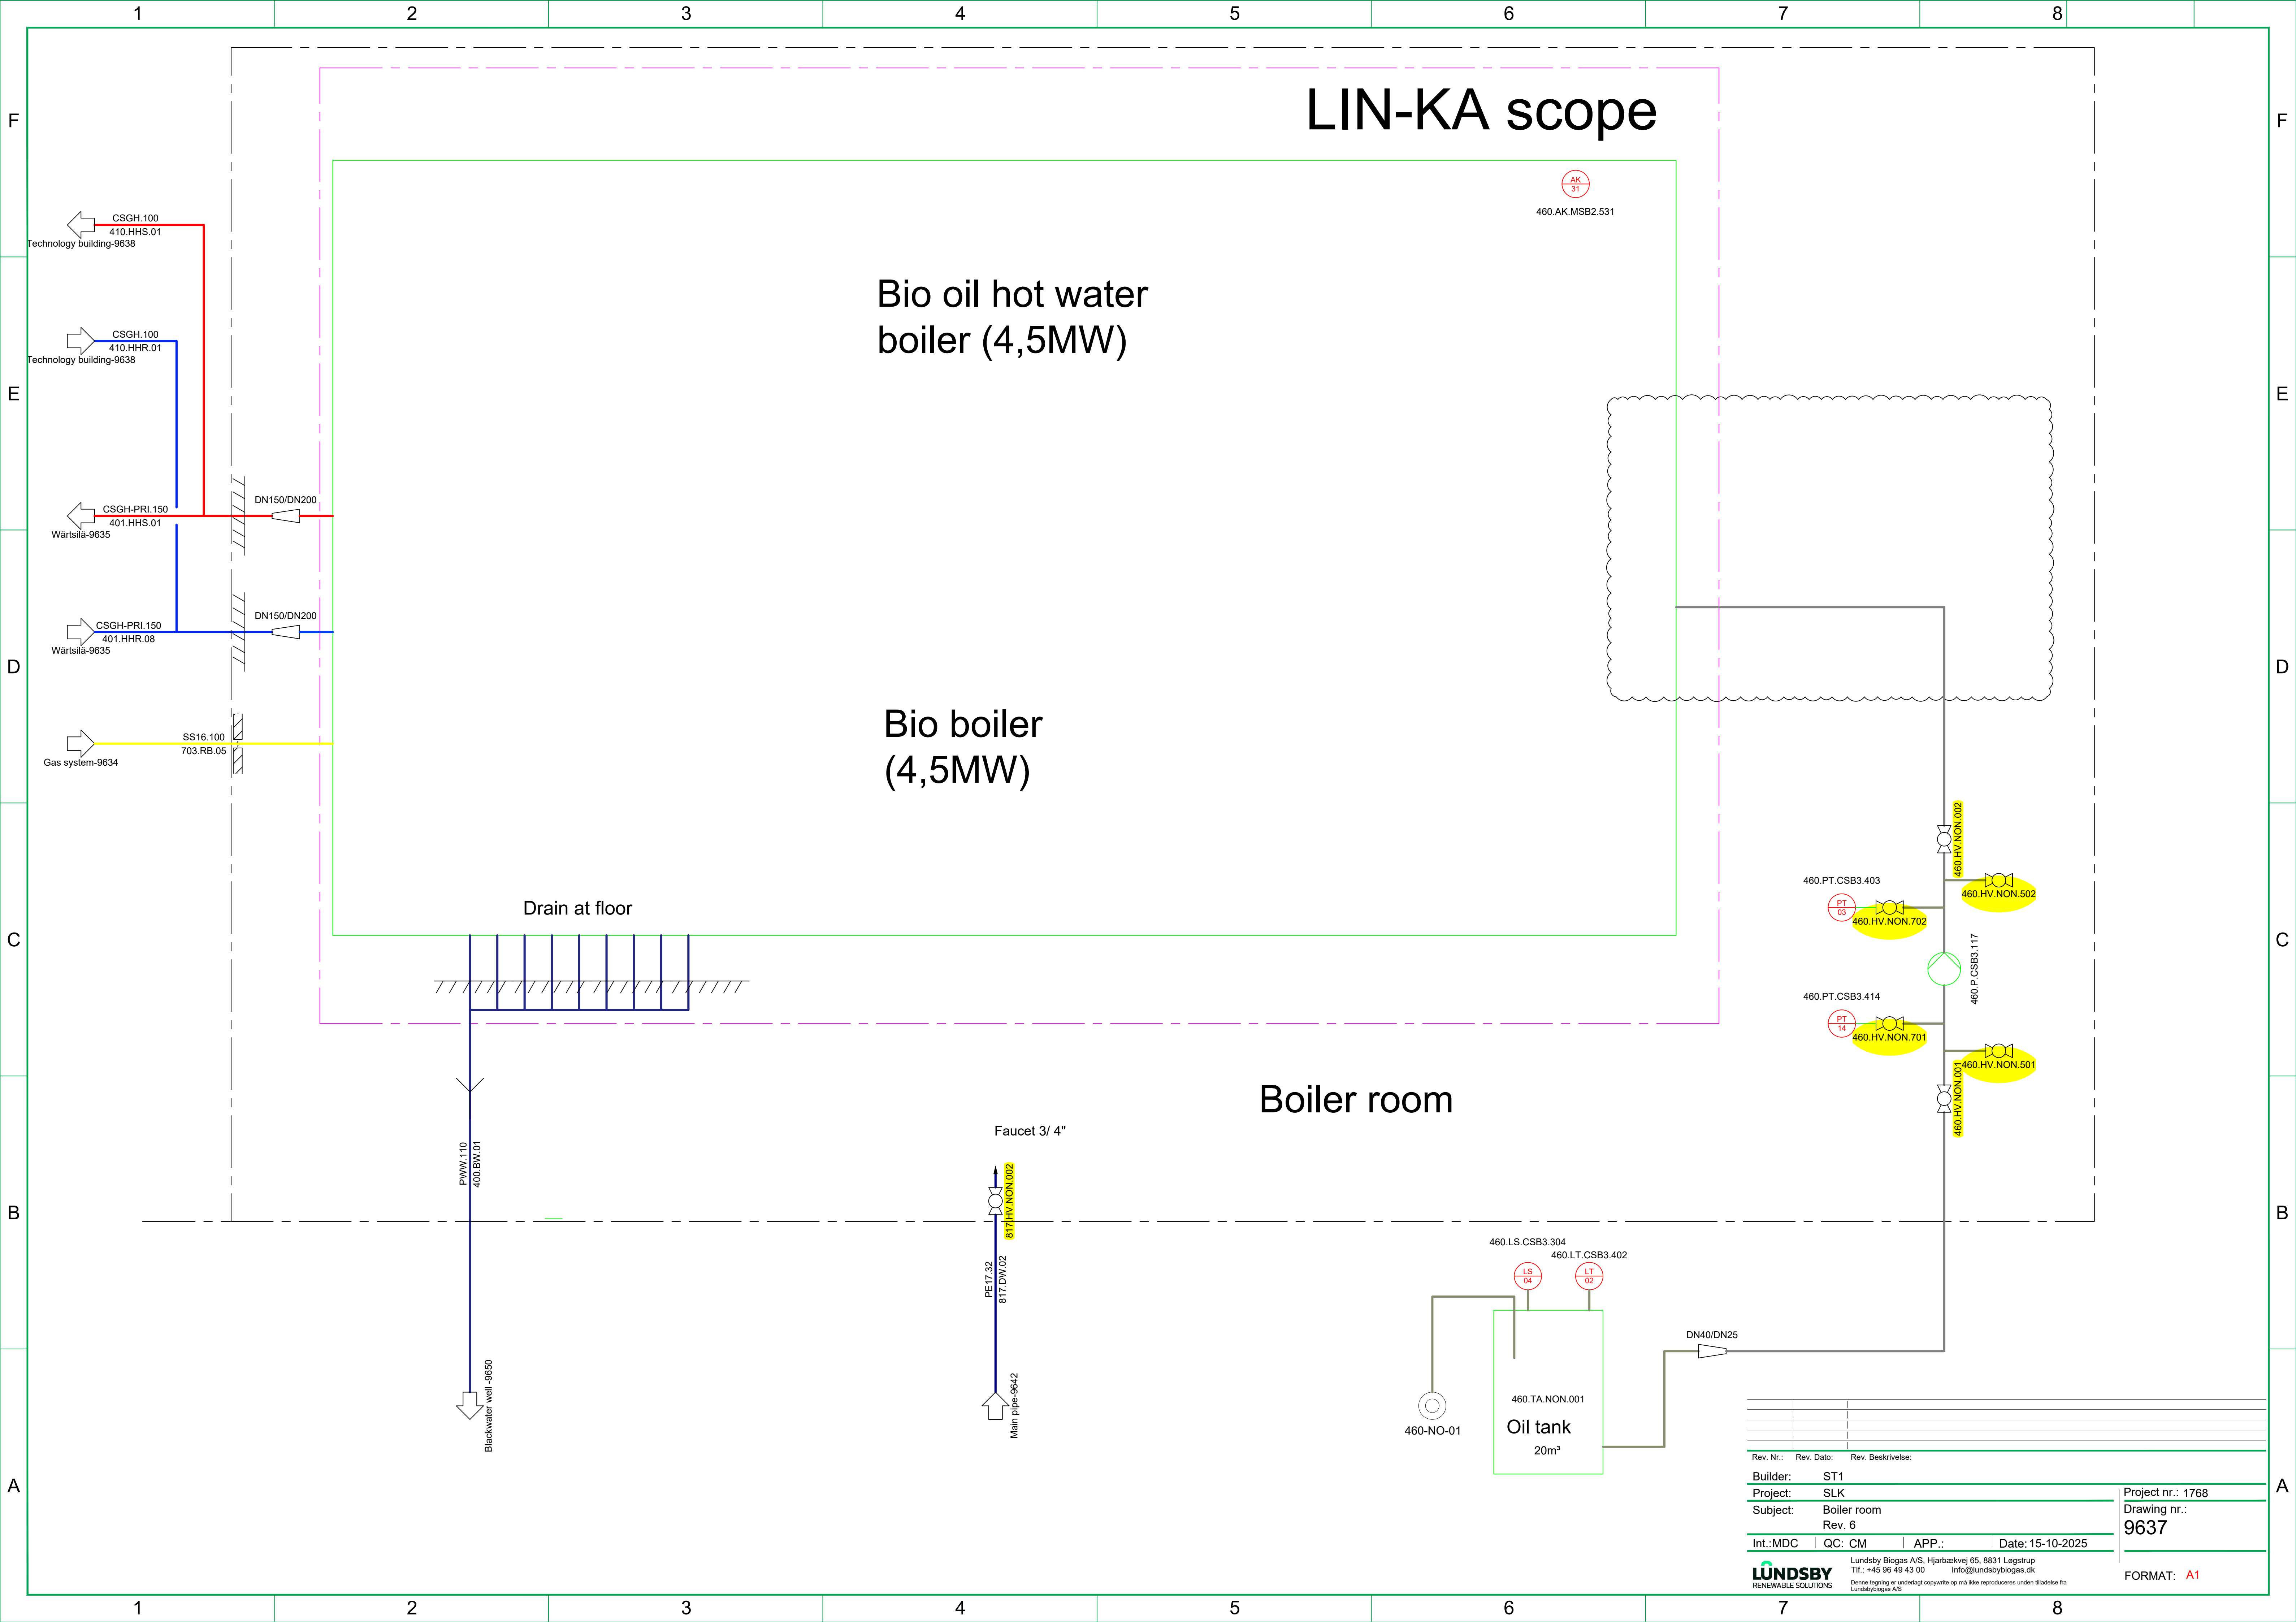


Rev. Nr.:	Rev. Dato:	Rev. Beskrivelse:	
Builder:	ST1		
Project:	SLK		
Subject:	Boiler room		
Rev. 6			
Int.:MDC	QC: CM	APP.:	Date: 15-10-2025
LUNDSBY RENEWABLE SOLUTIONS			Lundsby Biogas A/S, Hjarbækvej 65, 8831 Løgstrup Tlf.: +45 96 49 43 00 Info@lundsbybiogas.dk Denne tegning er underlagt copyright og må ikke reproduceres uden tilladelse fra Lundsbybiogas A/S
Project nr.: 1768 Drawing nr.: 9637			FORMAT: A1

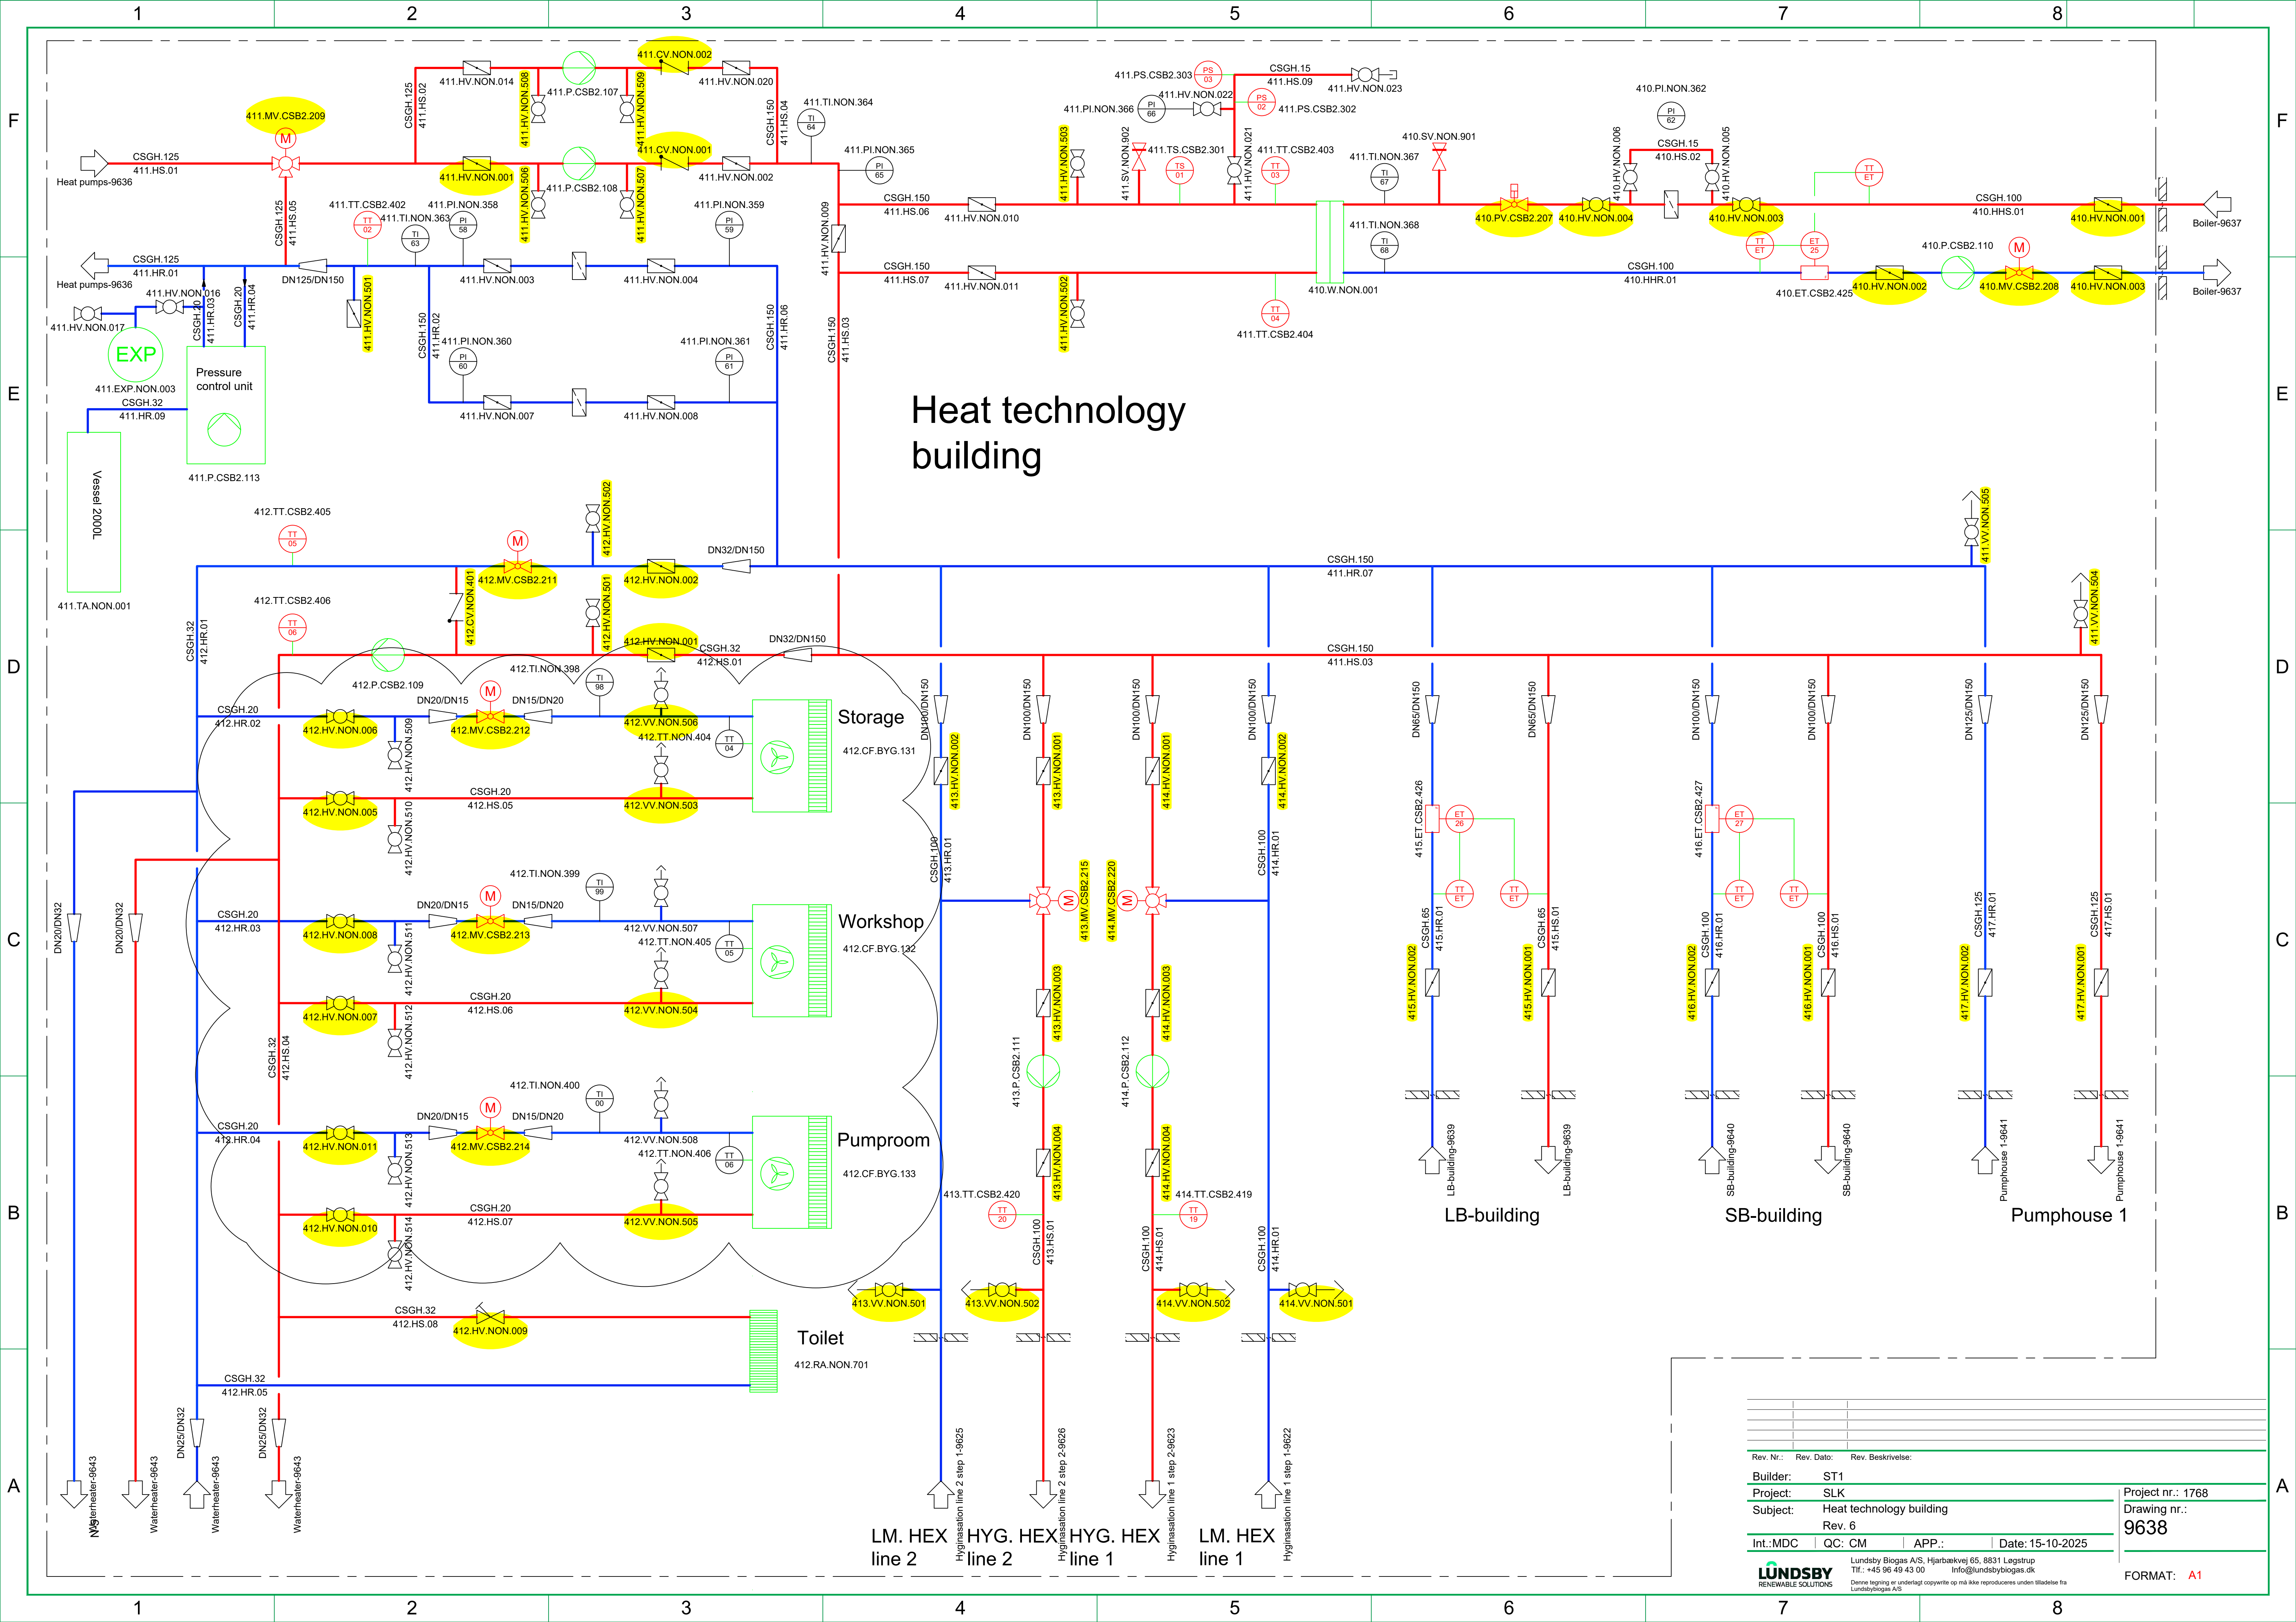


Rev. Nr.:	Rev. Dato:	Rev. Beskrivelse:
Builder:	ST1	
Project:	SLK	
Subject:	Heat technology building	
Rev. 6		
Int.:MDC	QC: CM	APP.: Date: 15-10-2025
LUNDSBY RENEWABLE SOLUTIONS		
Lundsby Biogas A/S, Hjarbækvej 65, 8831 Løgstrup Tlf.: +45 96 49 43 00 info@lundsbybiogas.dk Denne tegning er underlagt copyright og må ikke reproduceres uden tilladelse fra Lundsbybiogas A/S		
Project nr.: 1768		Drawing nr.: 9638
FORMAT: A1		


LB-Building

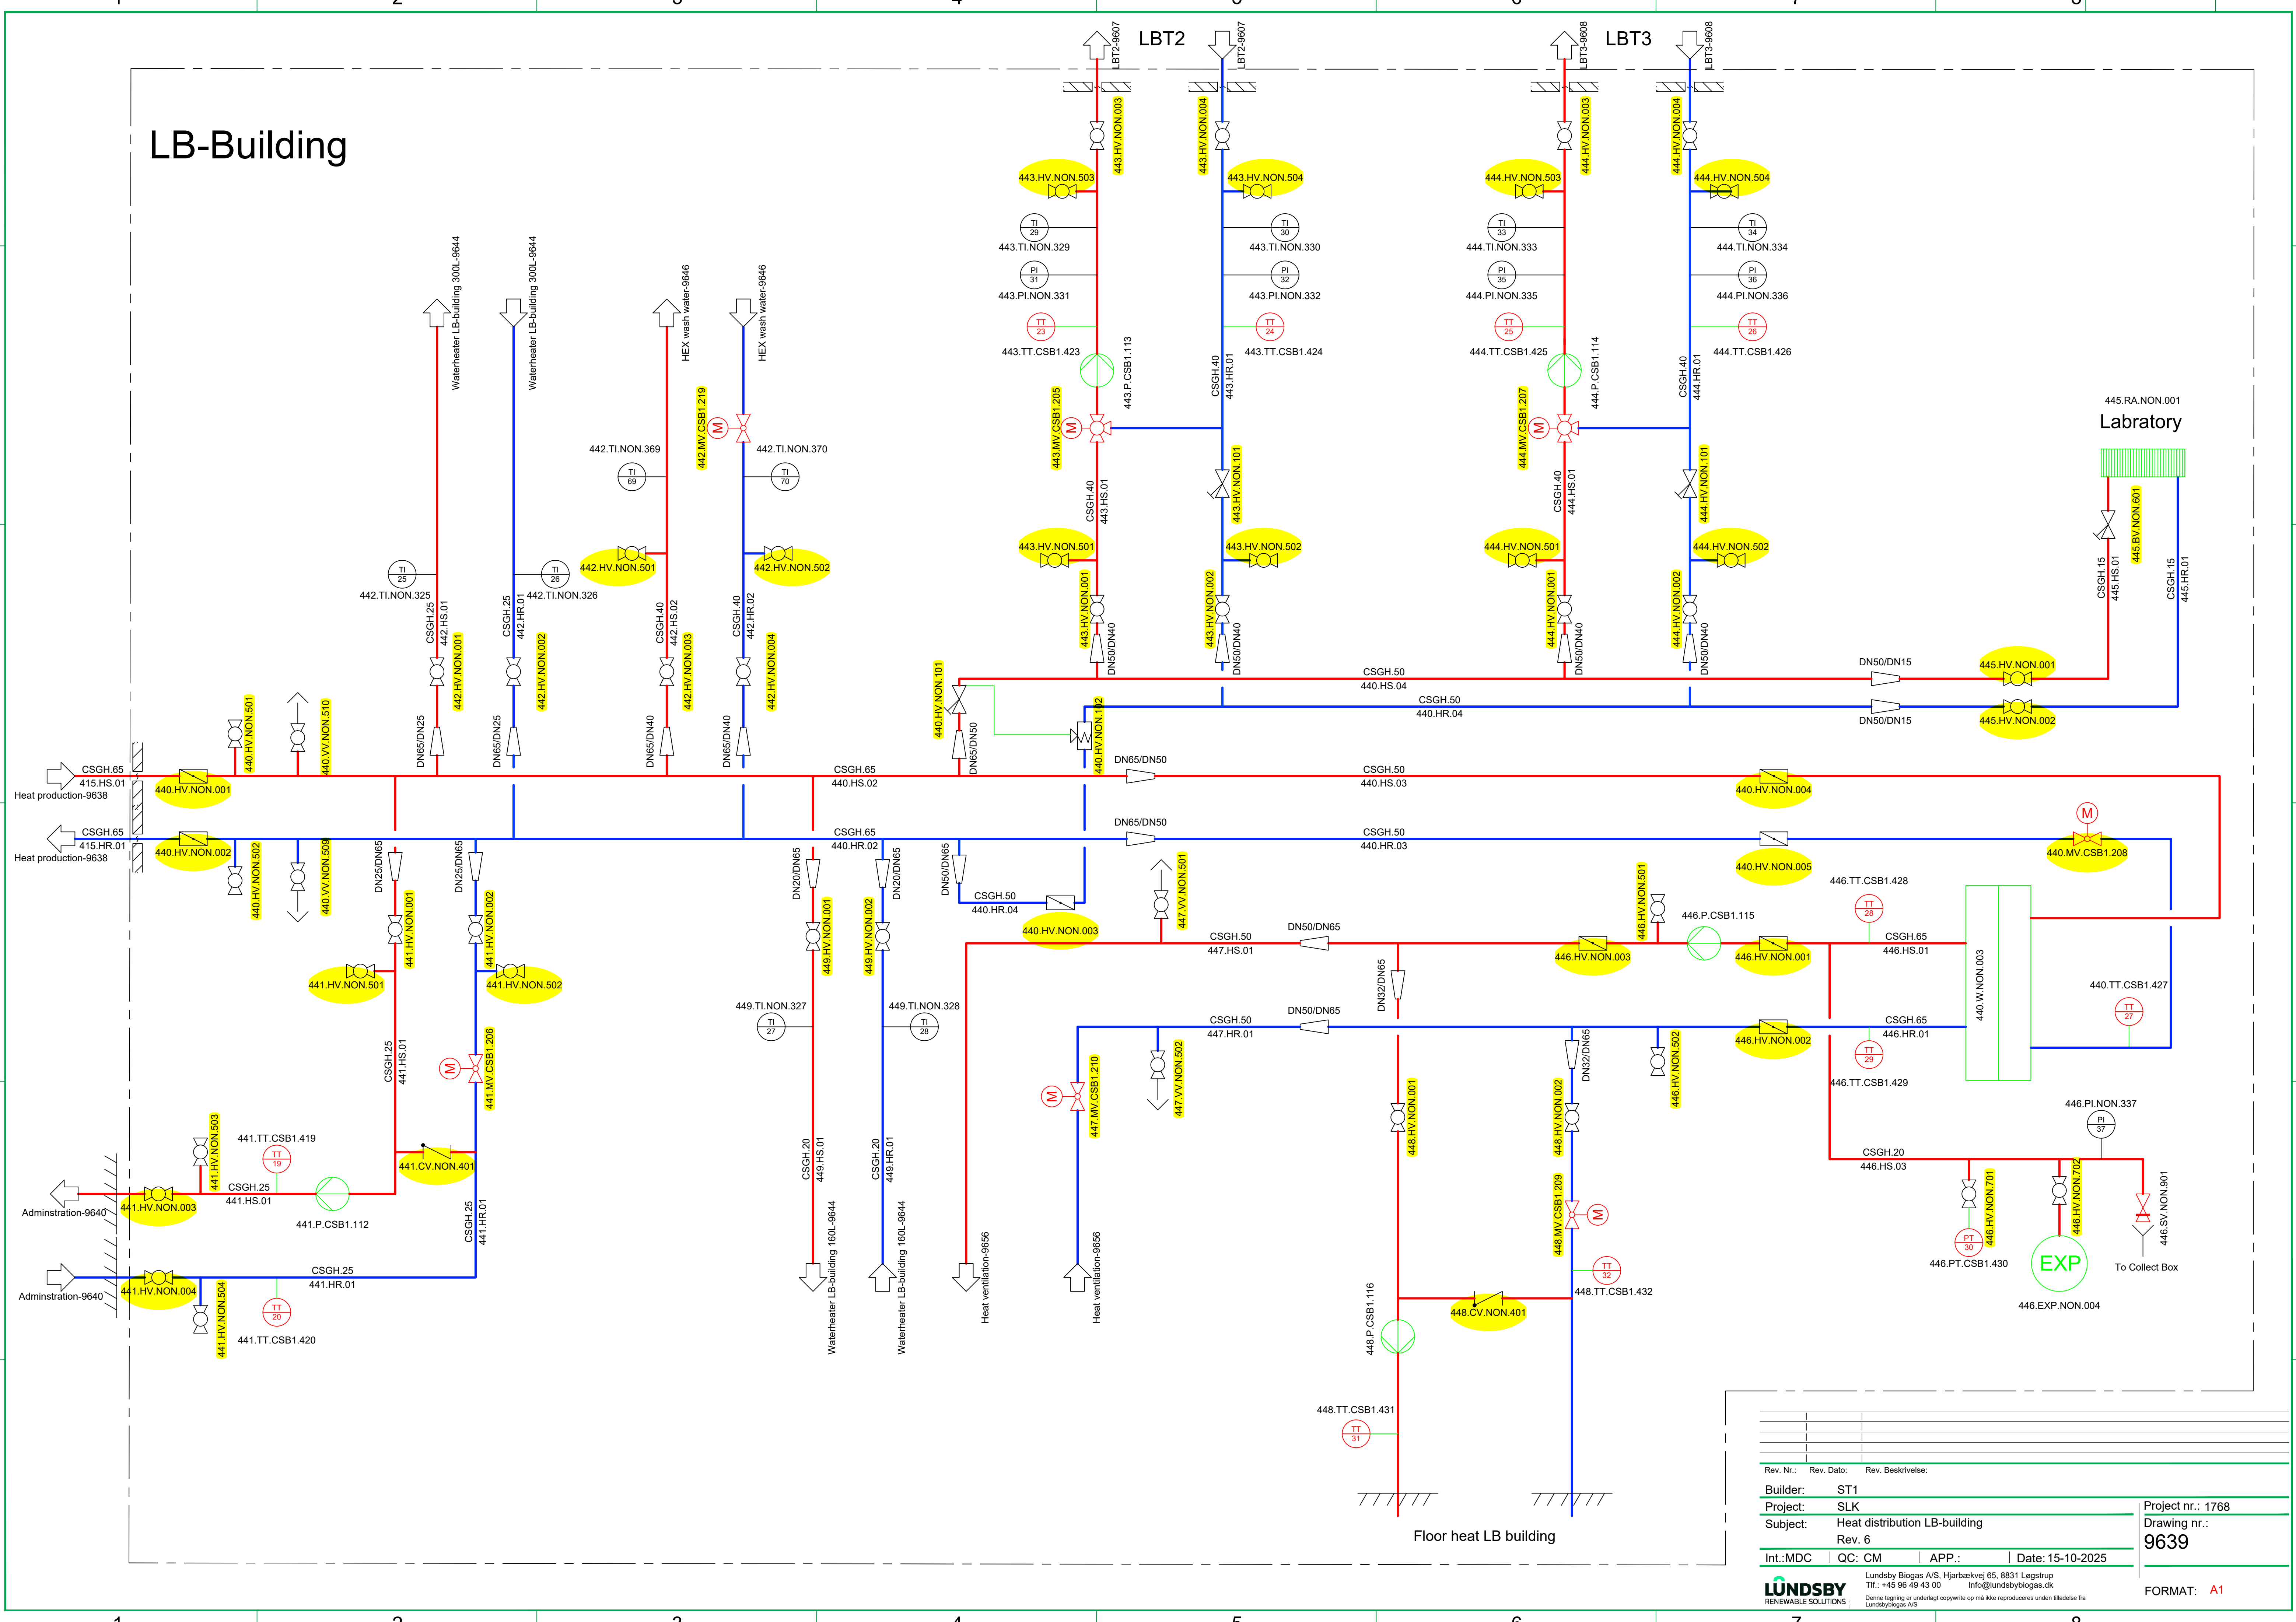

Rev. Nr.:	Rev. Dato:	Rev. Beskrivelse:
Builder:	ST1	
Project:	SLK	
Subject:	Heat distribution LB-building	
Rev. 6		
Int.:MDC	QC: CM	APP.: Date: 15-10-2025
LUNDSBY RENEWABLE SOLUTIONS		
Lundsby Biogas A/S, Hjarbækvej 65, 8831 Løgstrup Tlf.: +45 96 49 43 00 info@lundsbybiogas.dk		
Denne tegning er underlagt copyright op på ikke reproduceres uden tilladelse fra Lundsbybiogas A/S		
Project nr.: 1768 Drawing nr.: 9639		FORMAT: A1

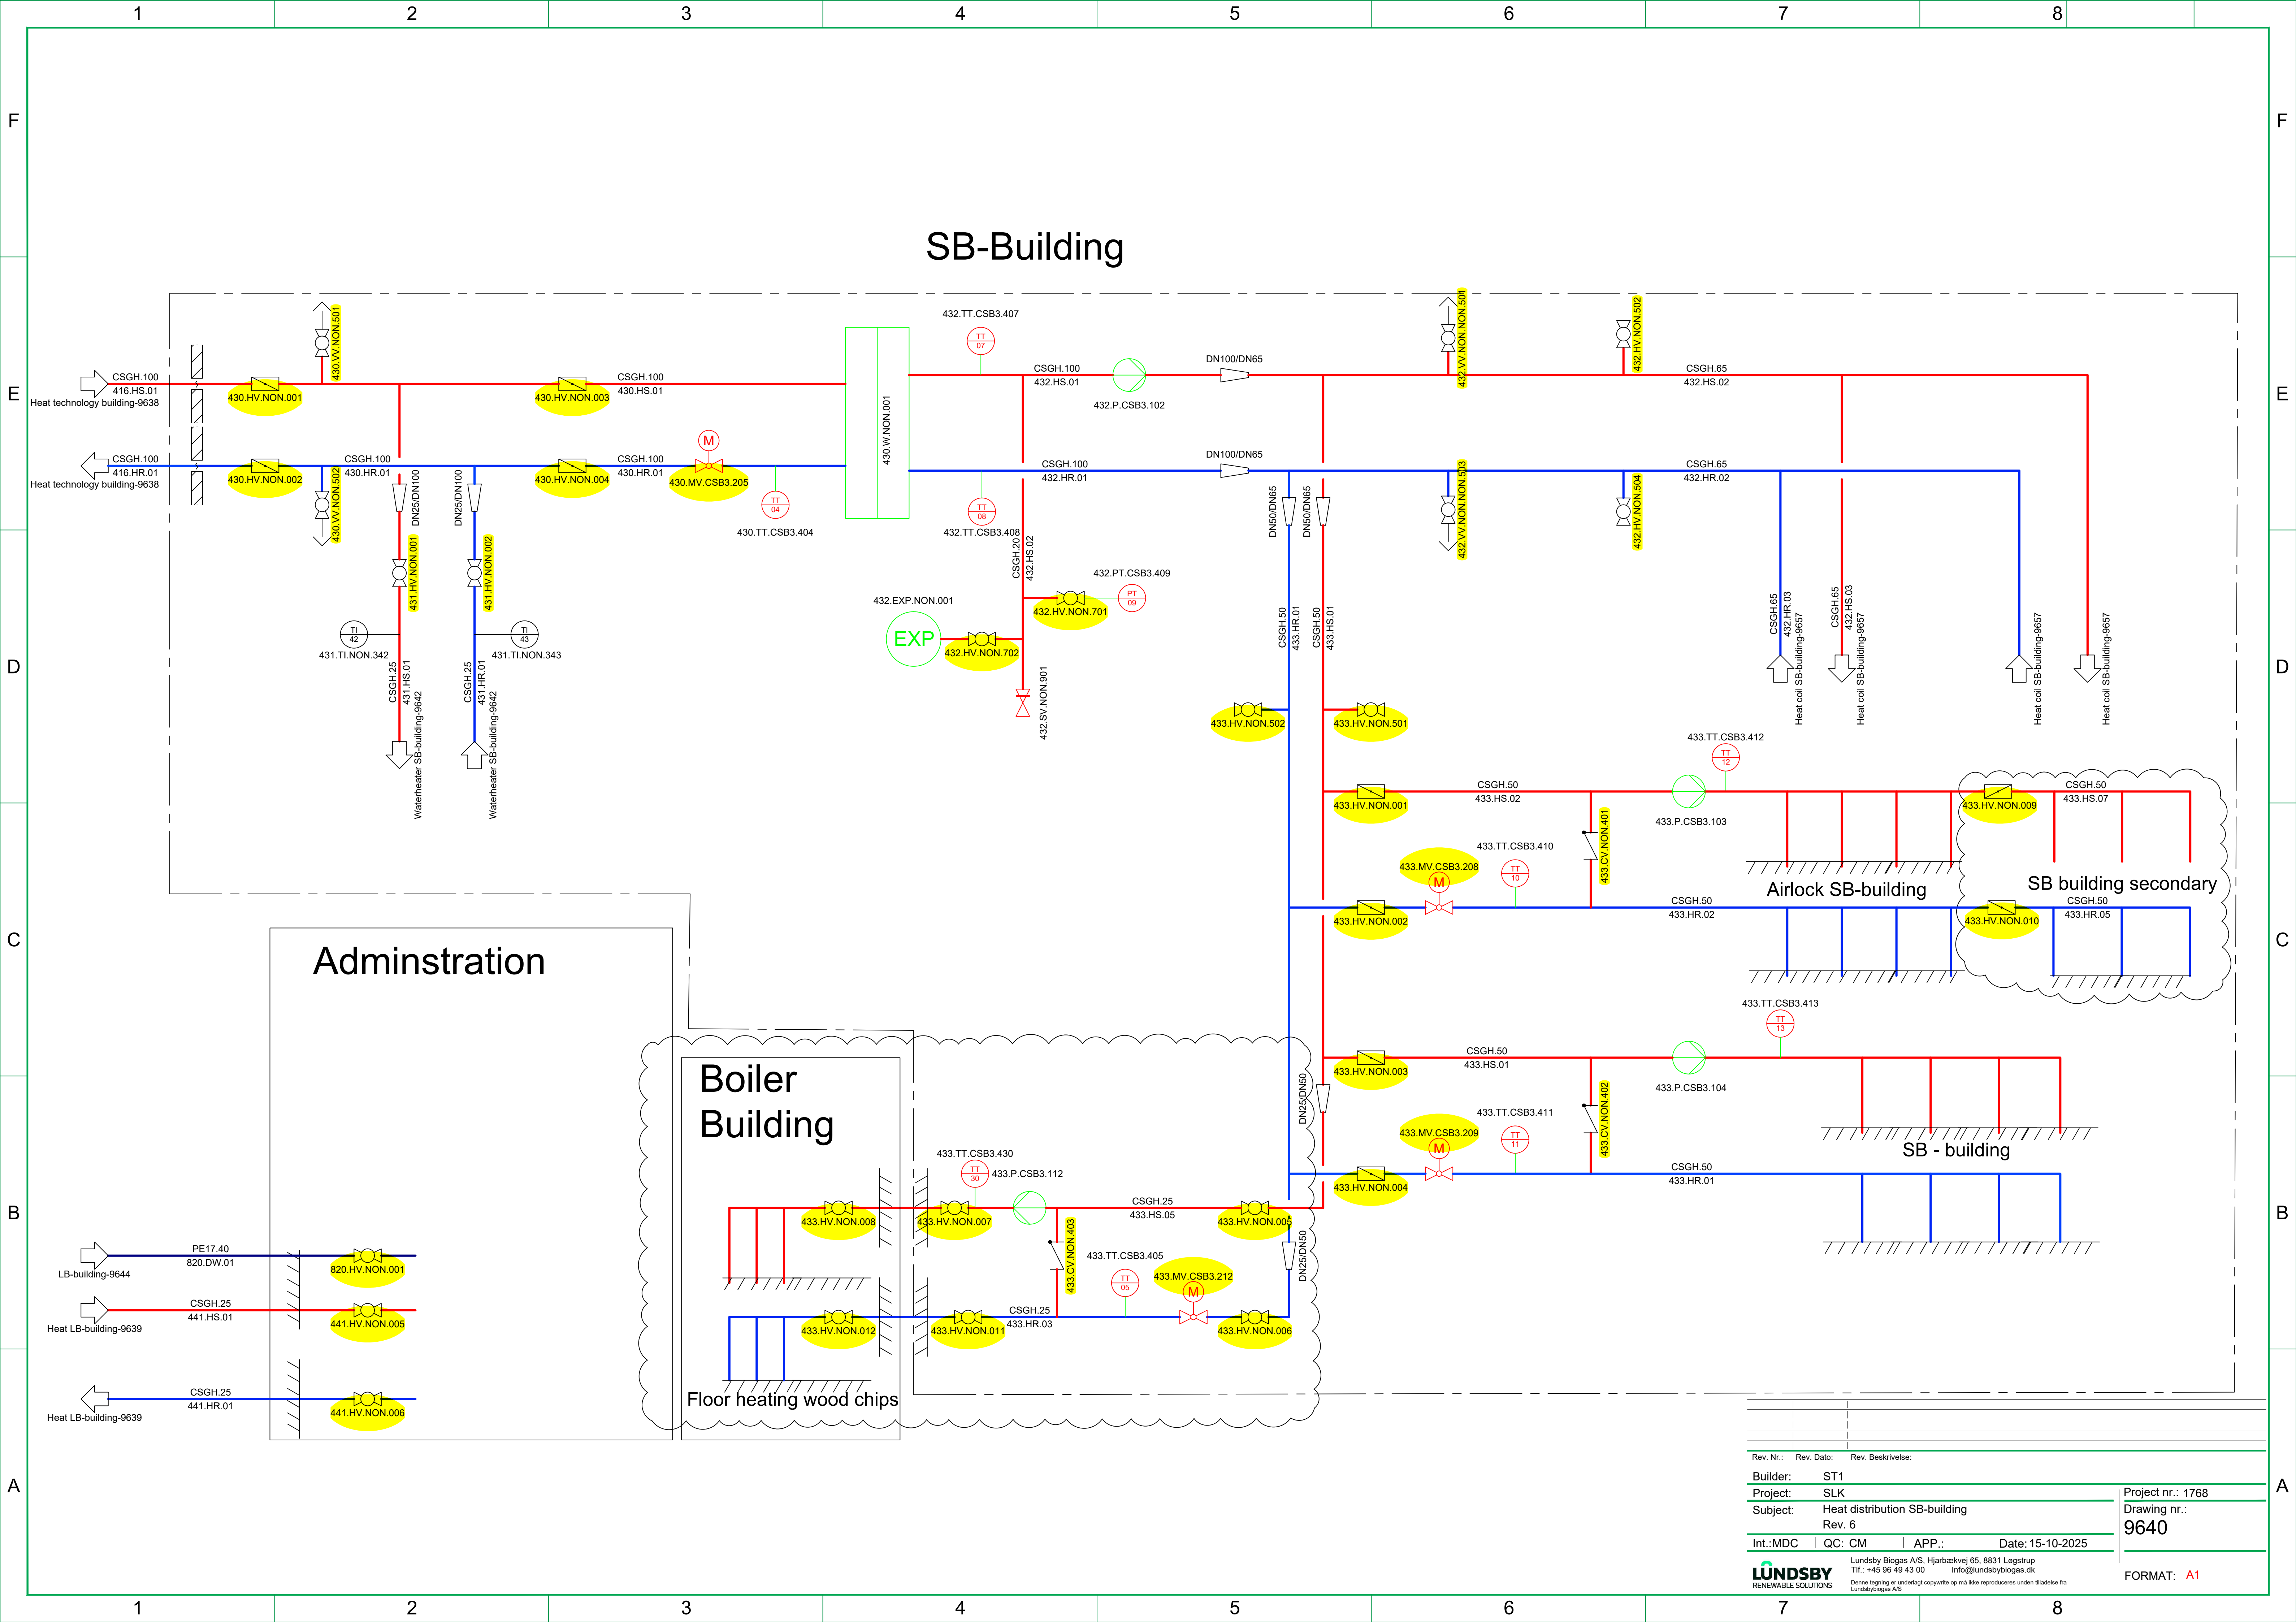


Rev. Nr.:	Rev. Dato:	Rev. Beskrivelse:	
Builder:	ST1		
Project:	SLK		
Subject:	Heat distribution SB-building		
Rev. 6			
Int.:MDC	QC: CM	APP.:	Date: 15-10-2025
LUNDSBY RENEWABLE SOLUTIONS			Lundsby Biogas A/S, Hjarbækvej 65, 8831 Løgstrup Tlf.: +45 96 49 43 00 info@lundsbybiogas.dk Denne tegning er underlagt copyright og må ikke reproduceres uden tilladelse fra Lundsbybiogas A/S
Project nr.: 1768 Drawing nr.: 9640			FORMAT: A1

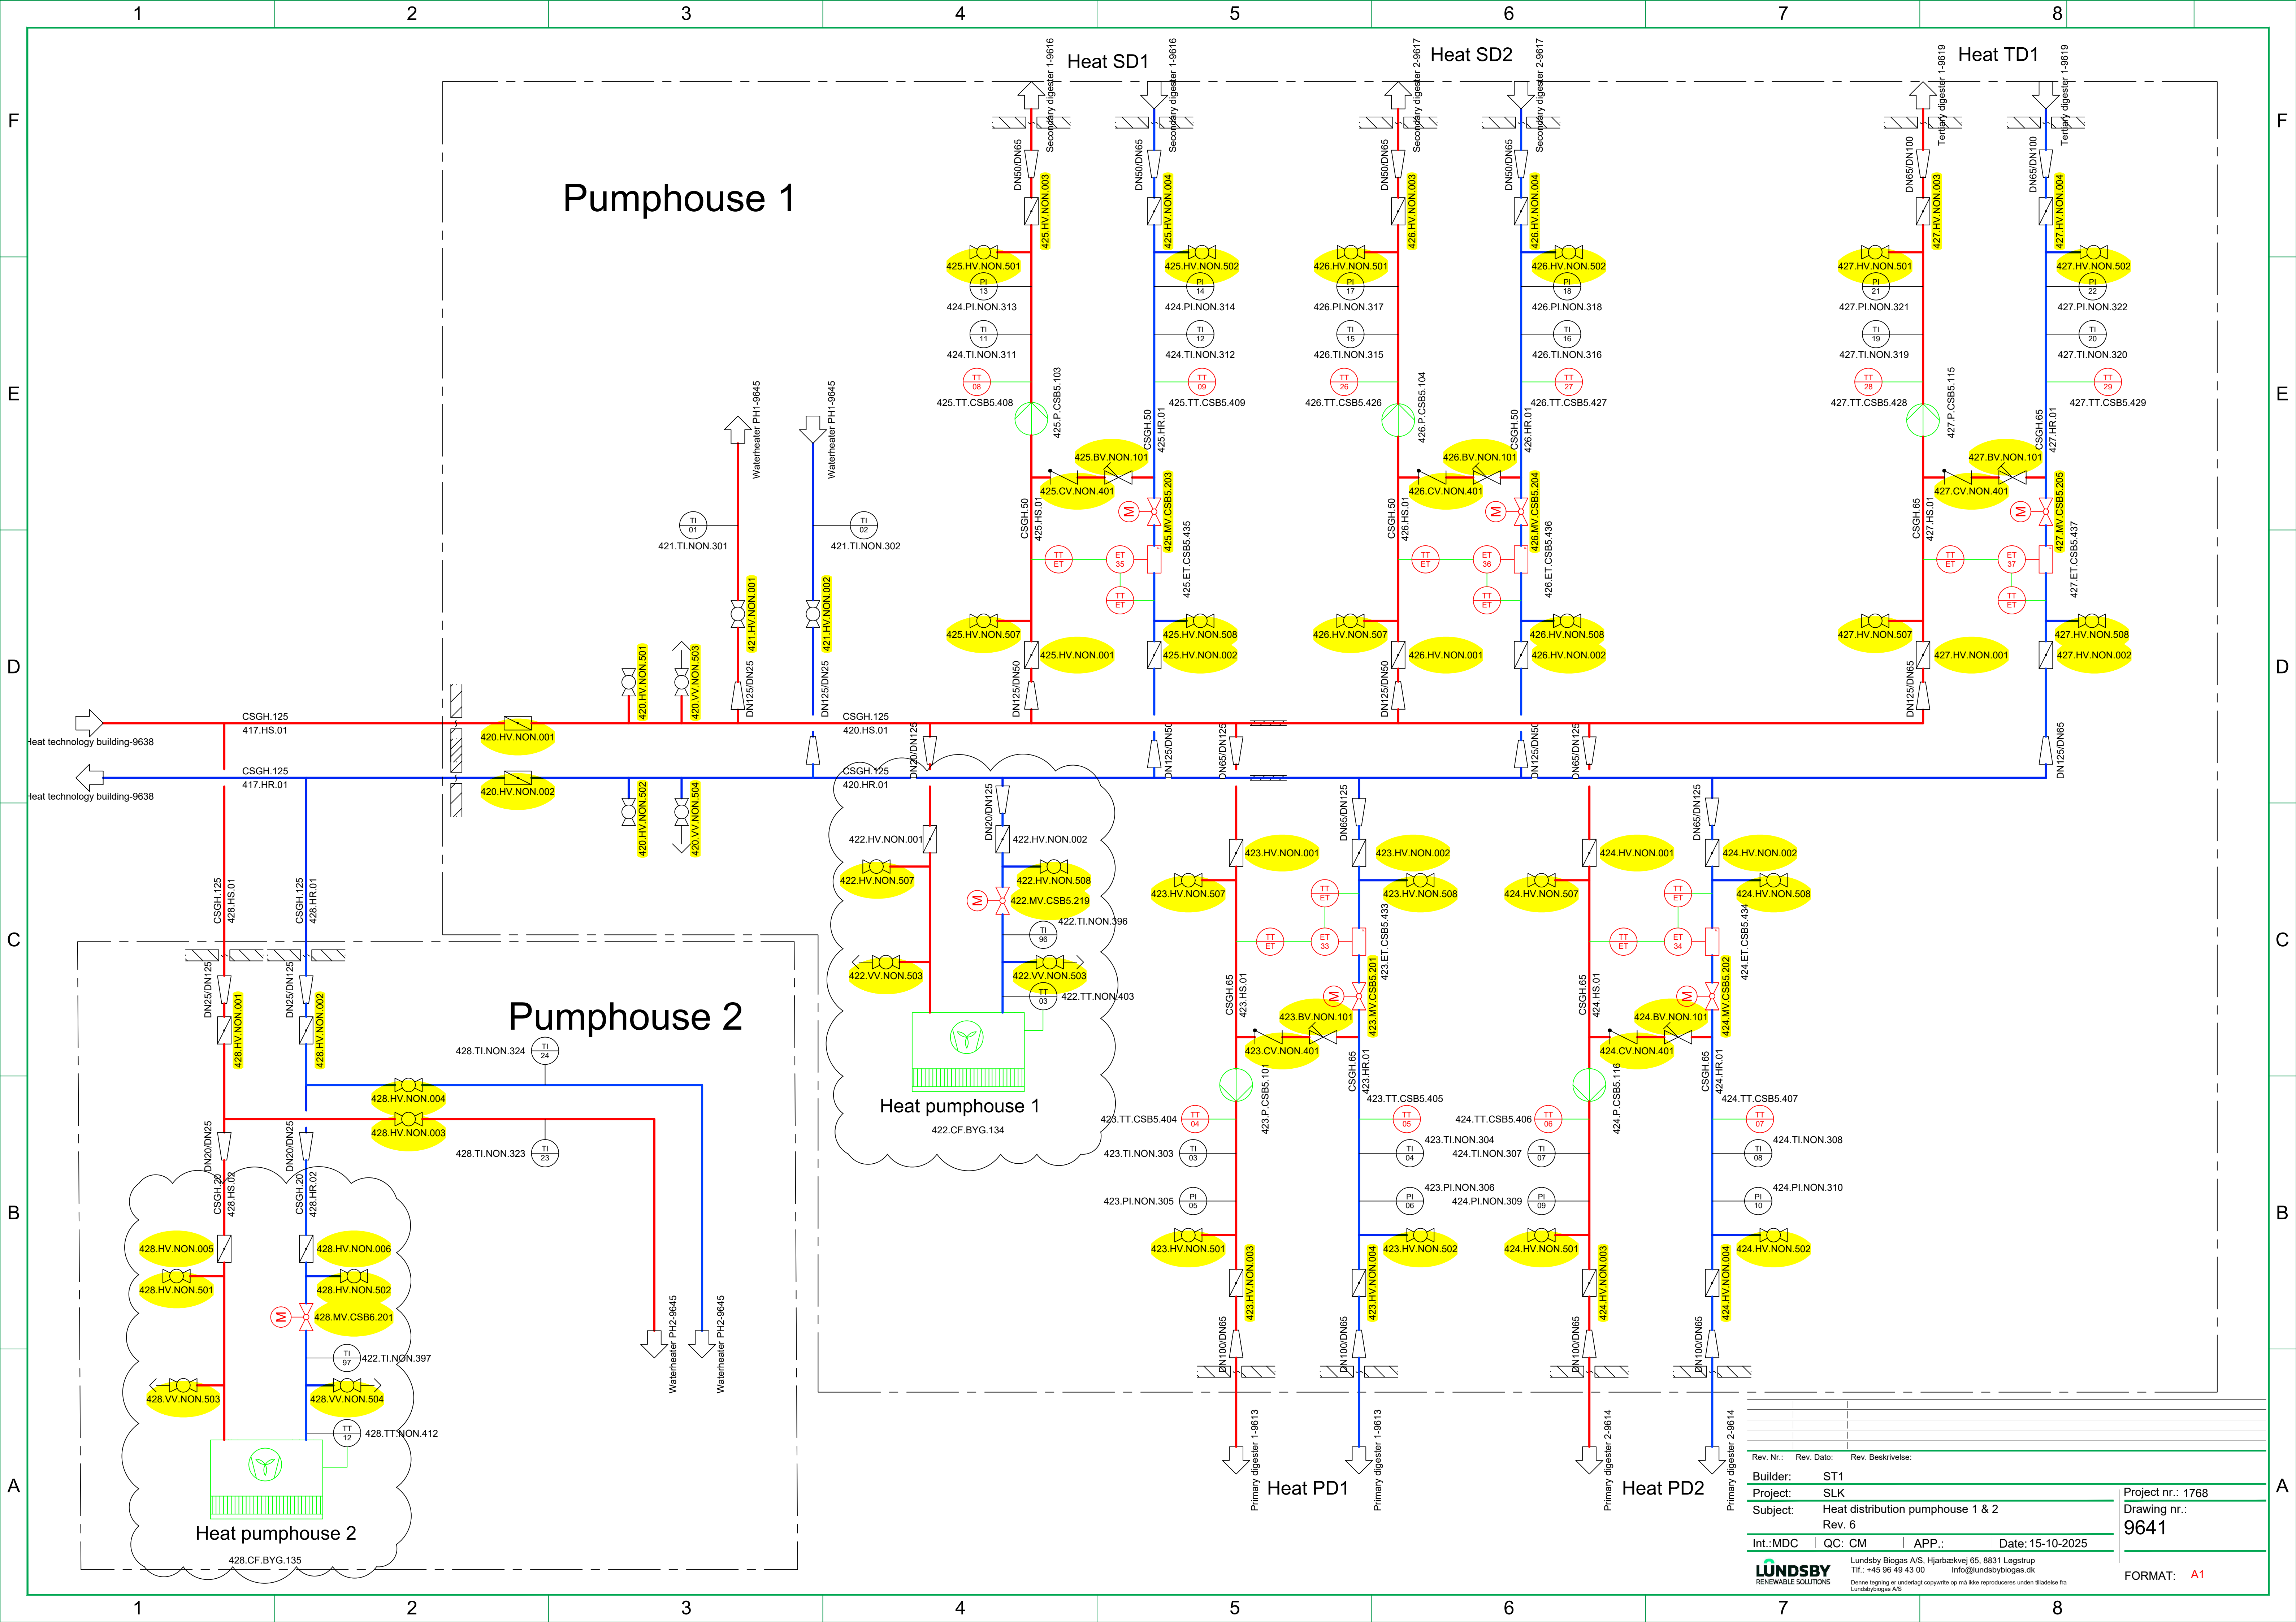


Rev. Nr.:	Rev. Dato:	Rev. Beskrivelse:
Builder:	ST1	
Project:	SLK	
Subject:	Heat distribution pumphouse 1 & 2	
Int.:MDC	QC: CM	APP.: Date: 15-10-2025
Project nr.: 1768		
Drawing nr.: 9641		
FORMAT: A1		

LUNDSBY
RENEWABLE SOLUTIONS

Lundsby Biogas A/S, Hjarbækvej 65, 8831 Løgstrup
Tlf.: +45 96 49 43 00
info@lundsbybiogas.dk
Denne tegning er underlagt copyright op på ikke reproduceres uden tilladelse fra Lundsbybiogas A/S

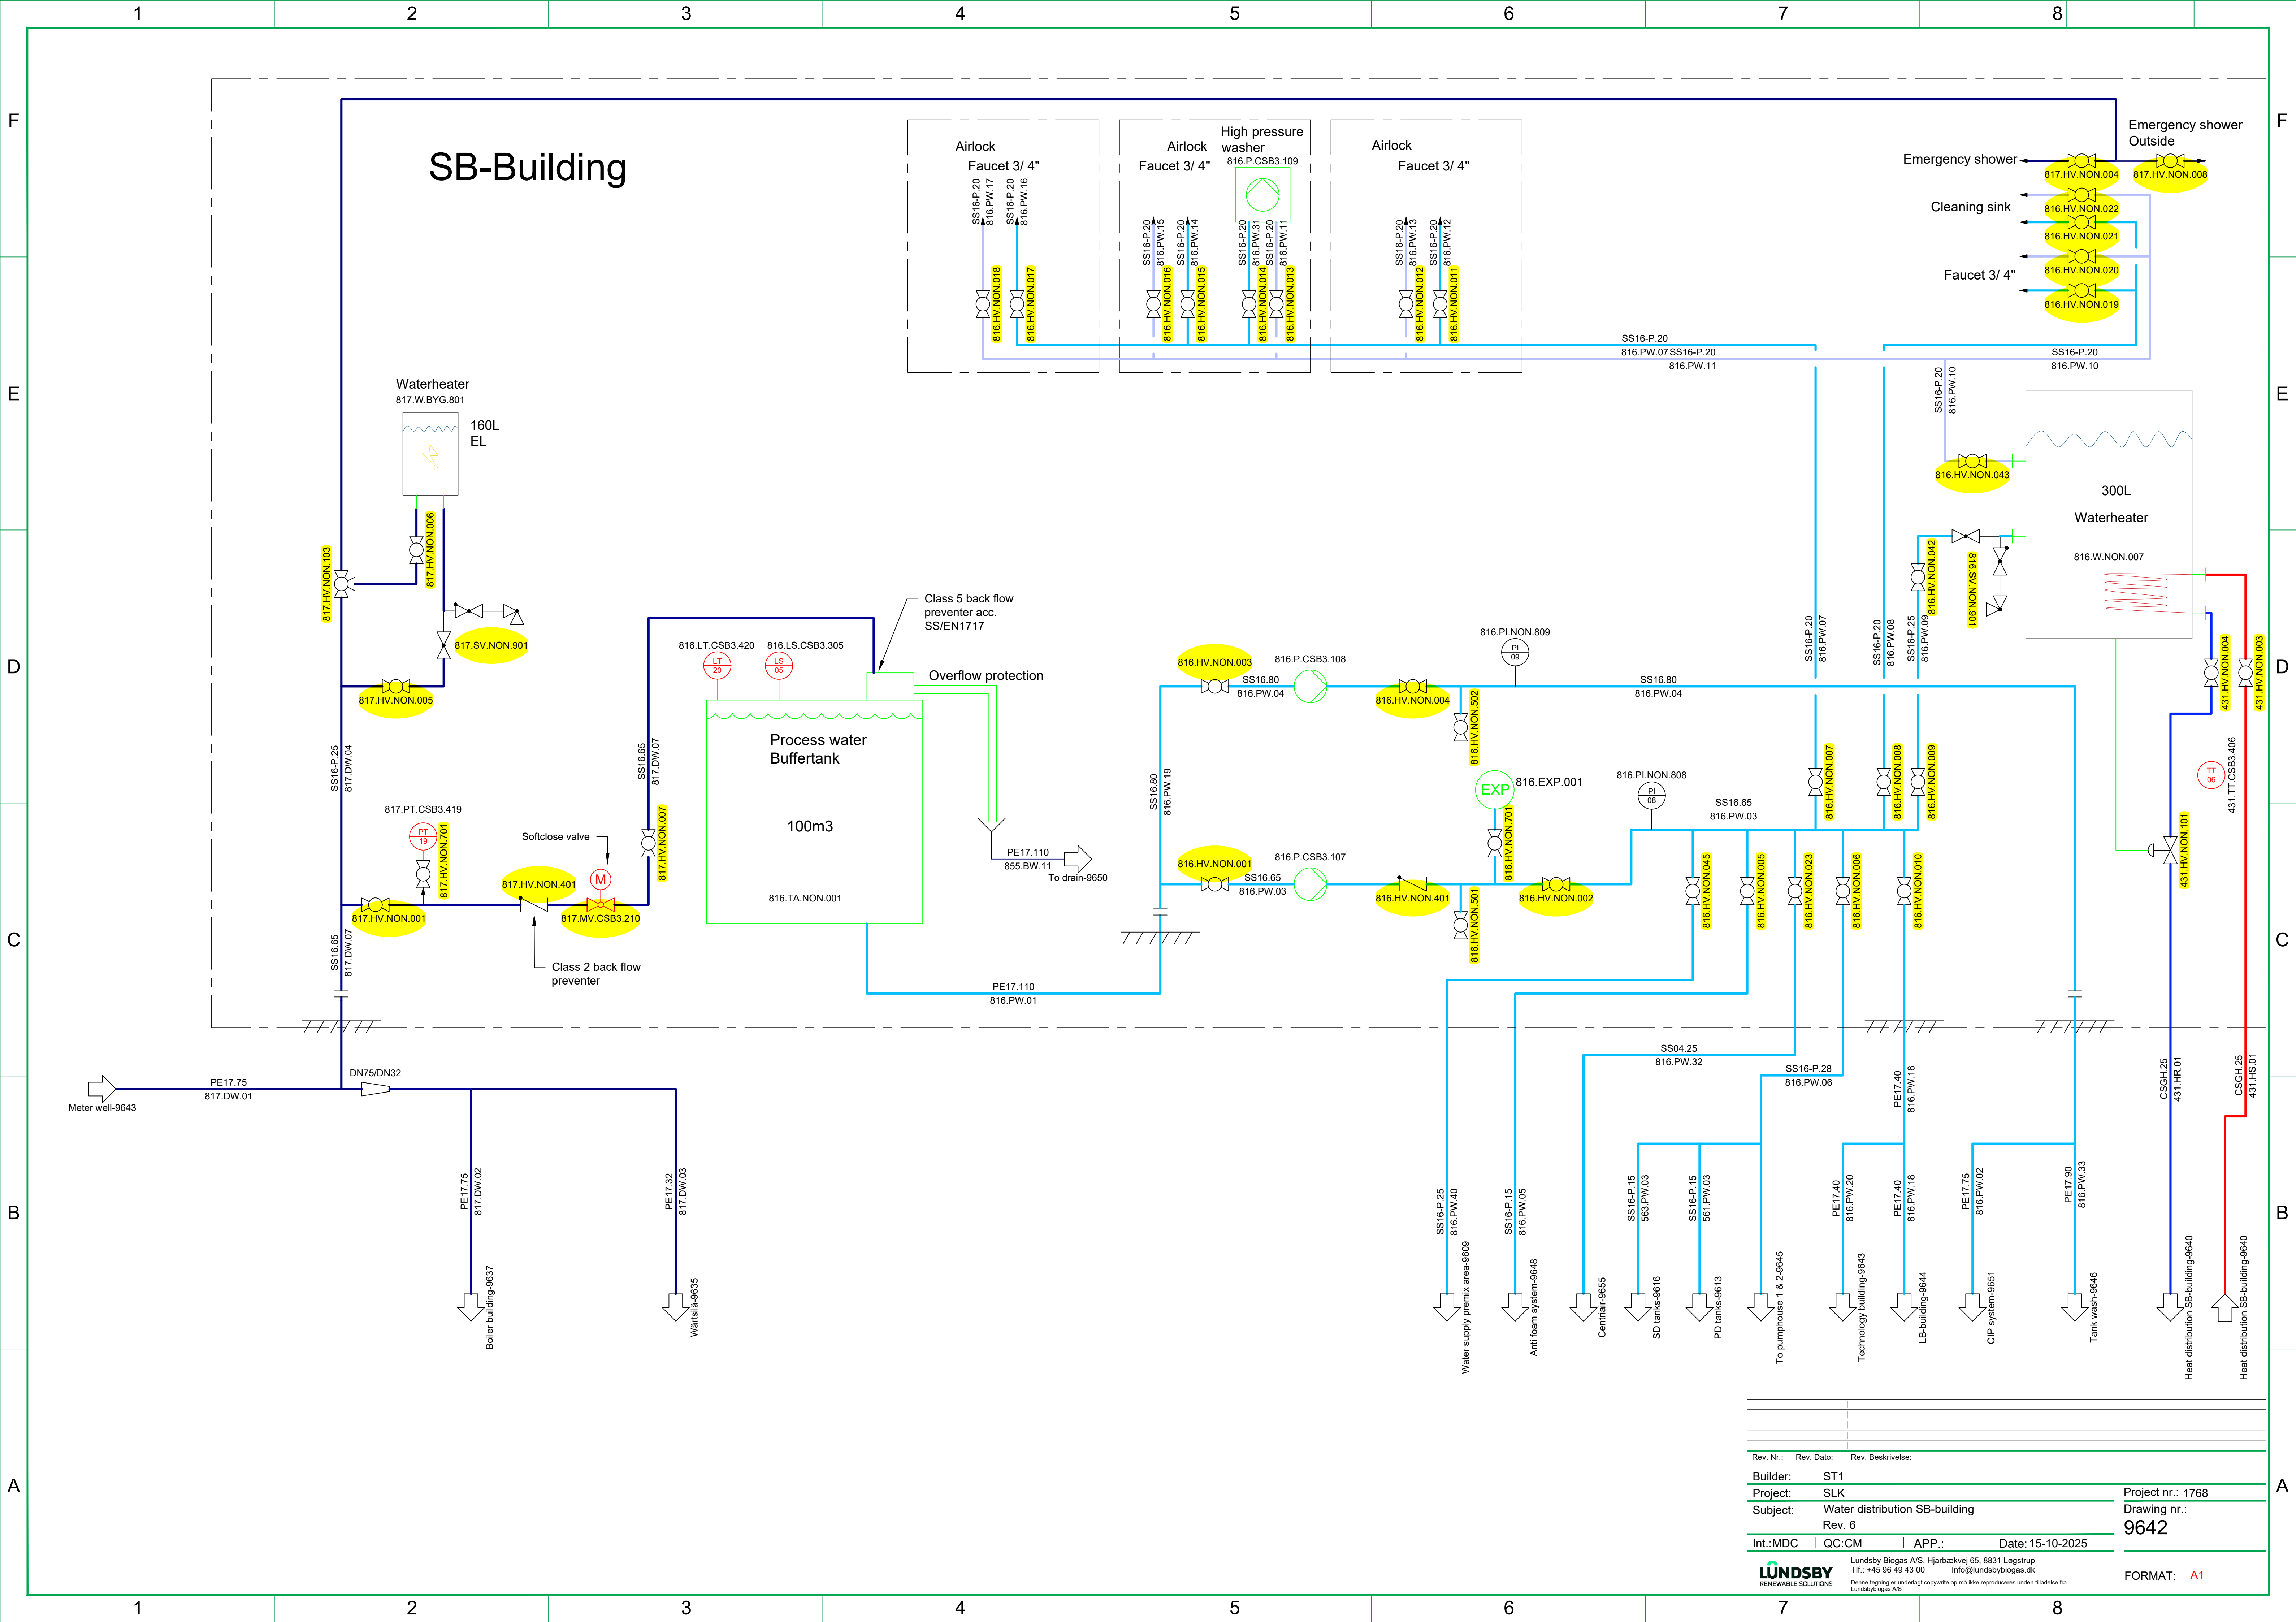


Technology building


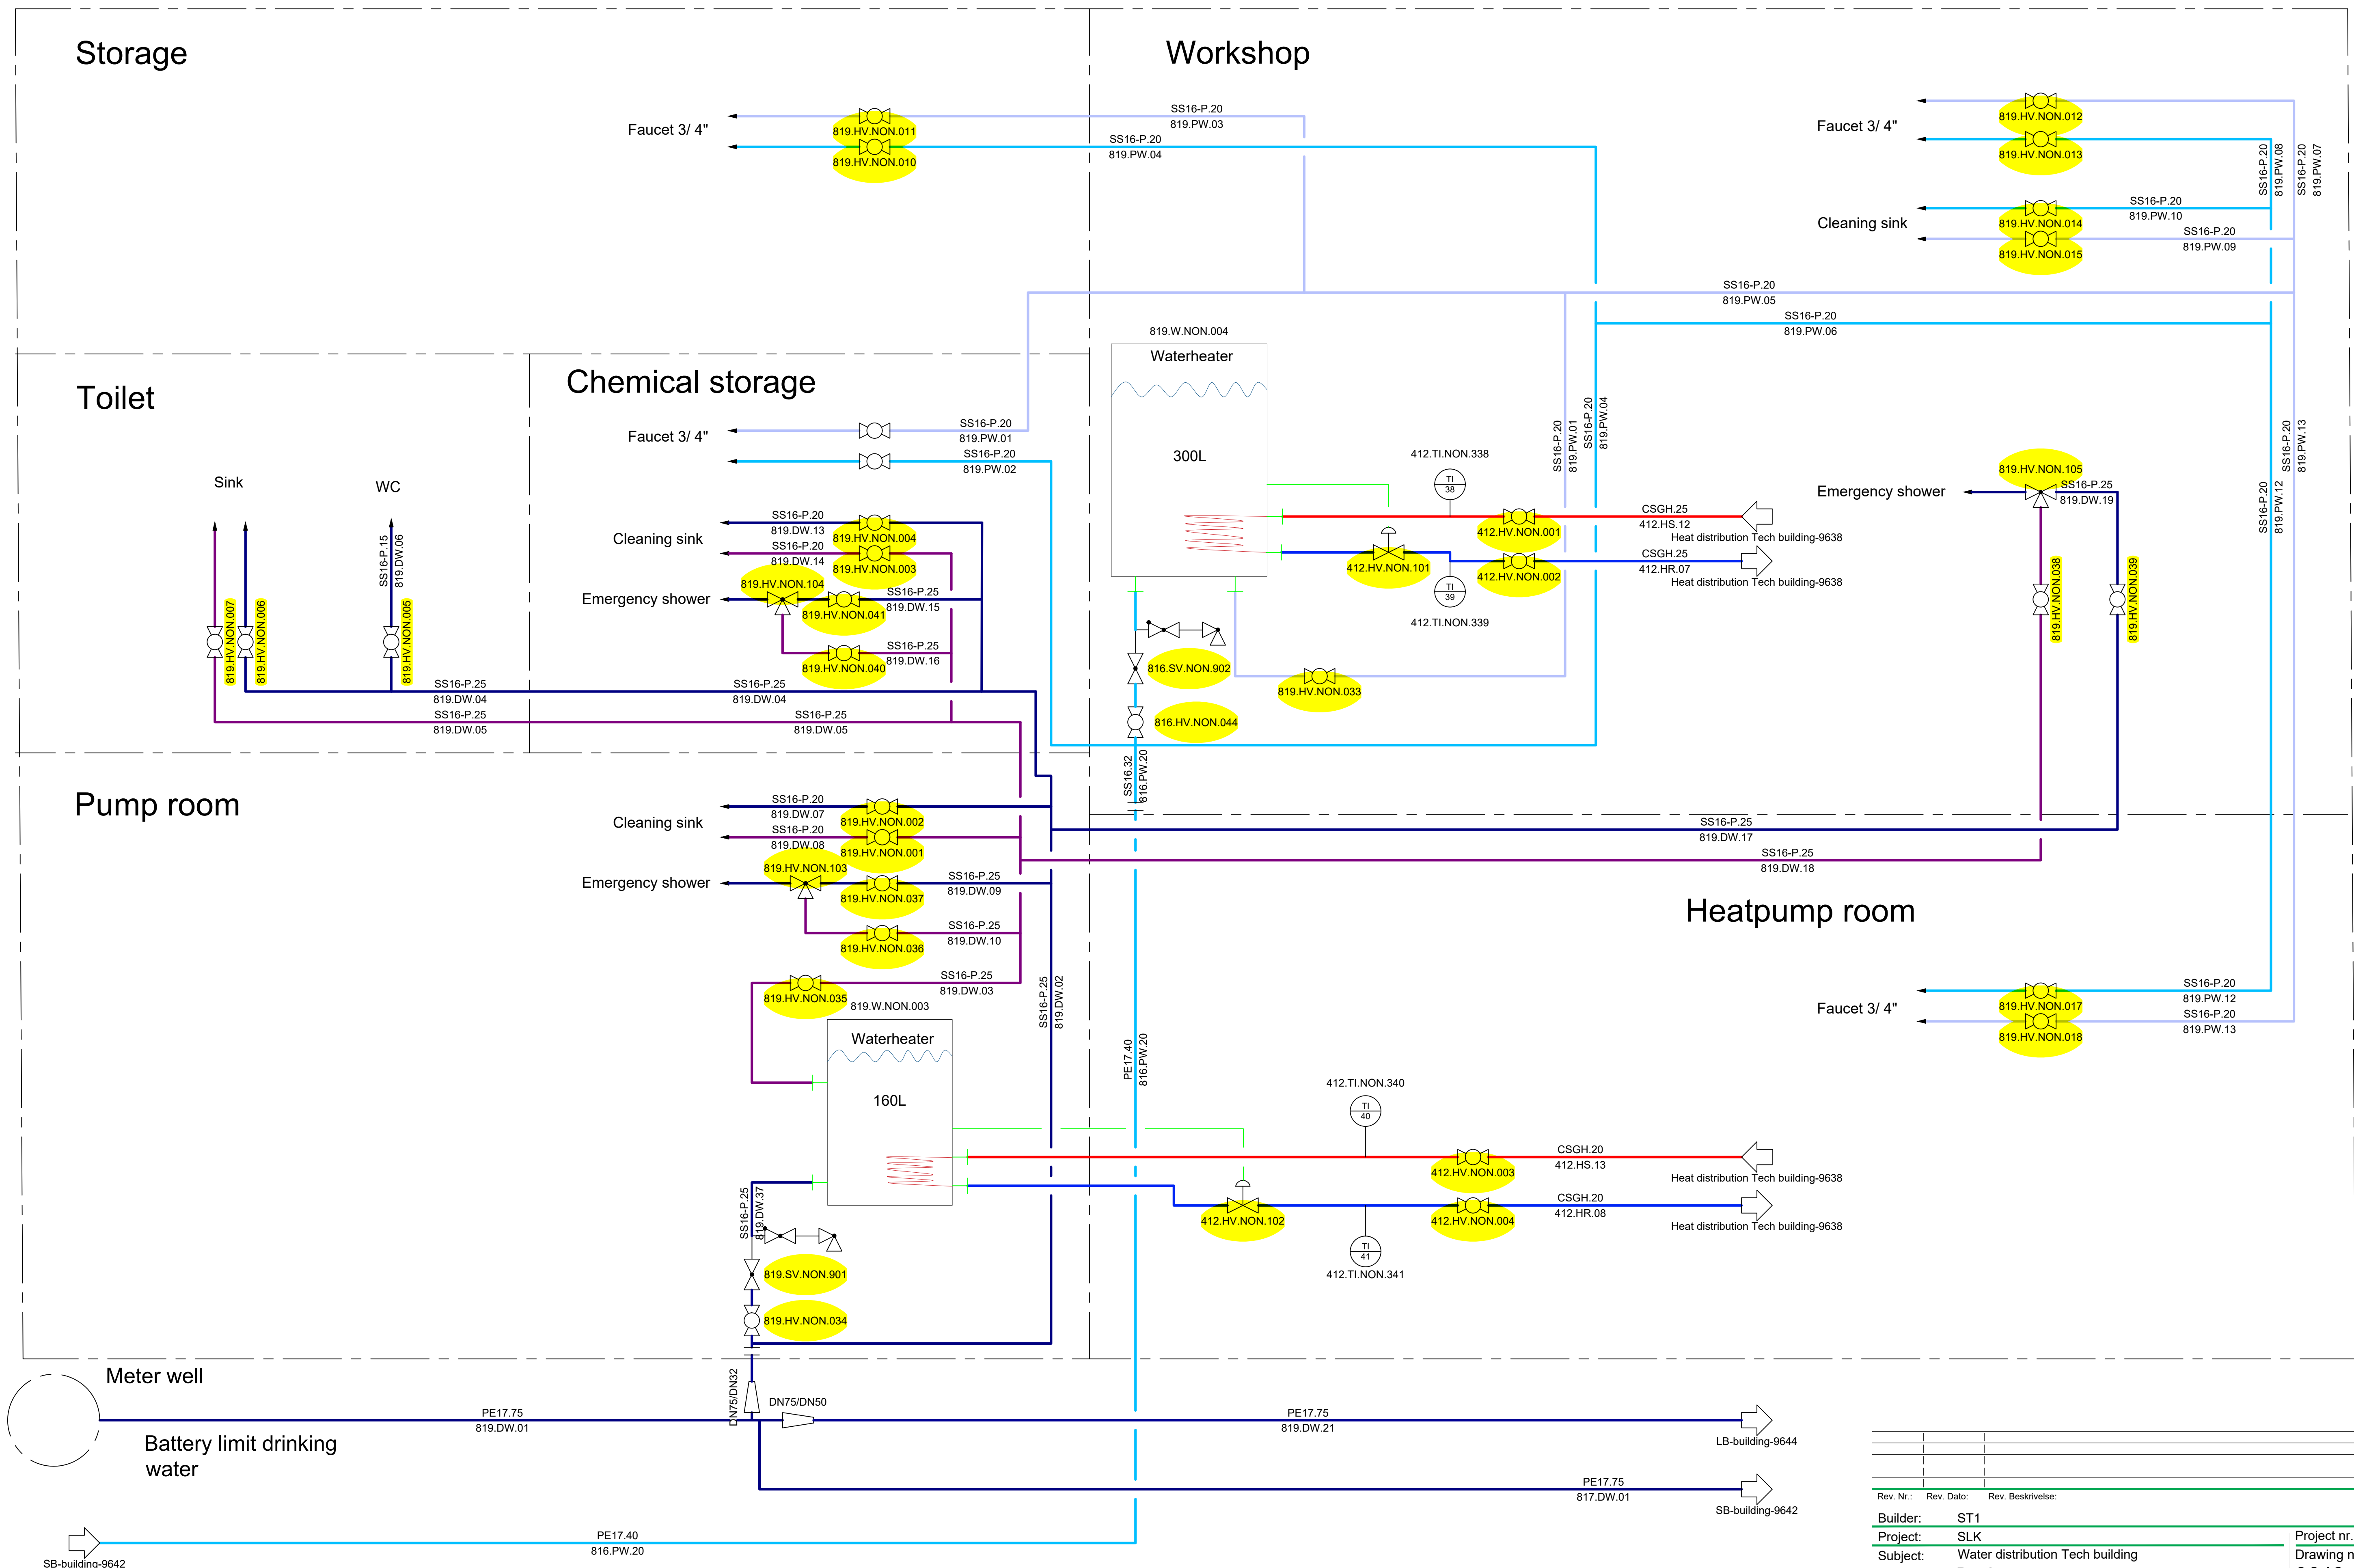



Rev. Nr.:	Rev. Dato:	Rev. Beskrivelse:
Builder:	ST1	
Project:	SLK	
Subject:	Water distribution Tech building	
Rev. 6		
Int.:MDC	QC:CM	APP.:
Date: 15-10-2025		
LUNDSBY RENEWABLE SOLUTIONS		
Lundsby Biogas A/S, Hjarbækvej 65, 8831 Løgstrup Tlf.: +45 96 49 43 00 info@lundsbybiogas.dk		
Denne tegning er underlagt copyright og må ikke reproduceres uden tilladelse fra Lundsbybiogas A/S		
Project nr.: 1768		Drawing nr.: 9643
FORMAT: A1		

LB-building

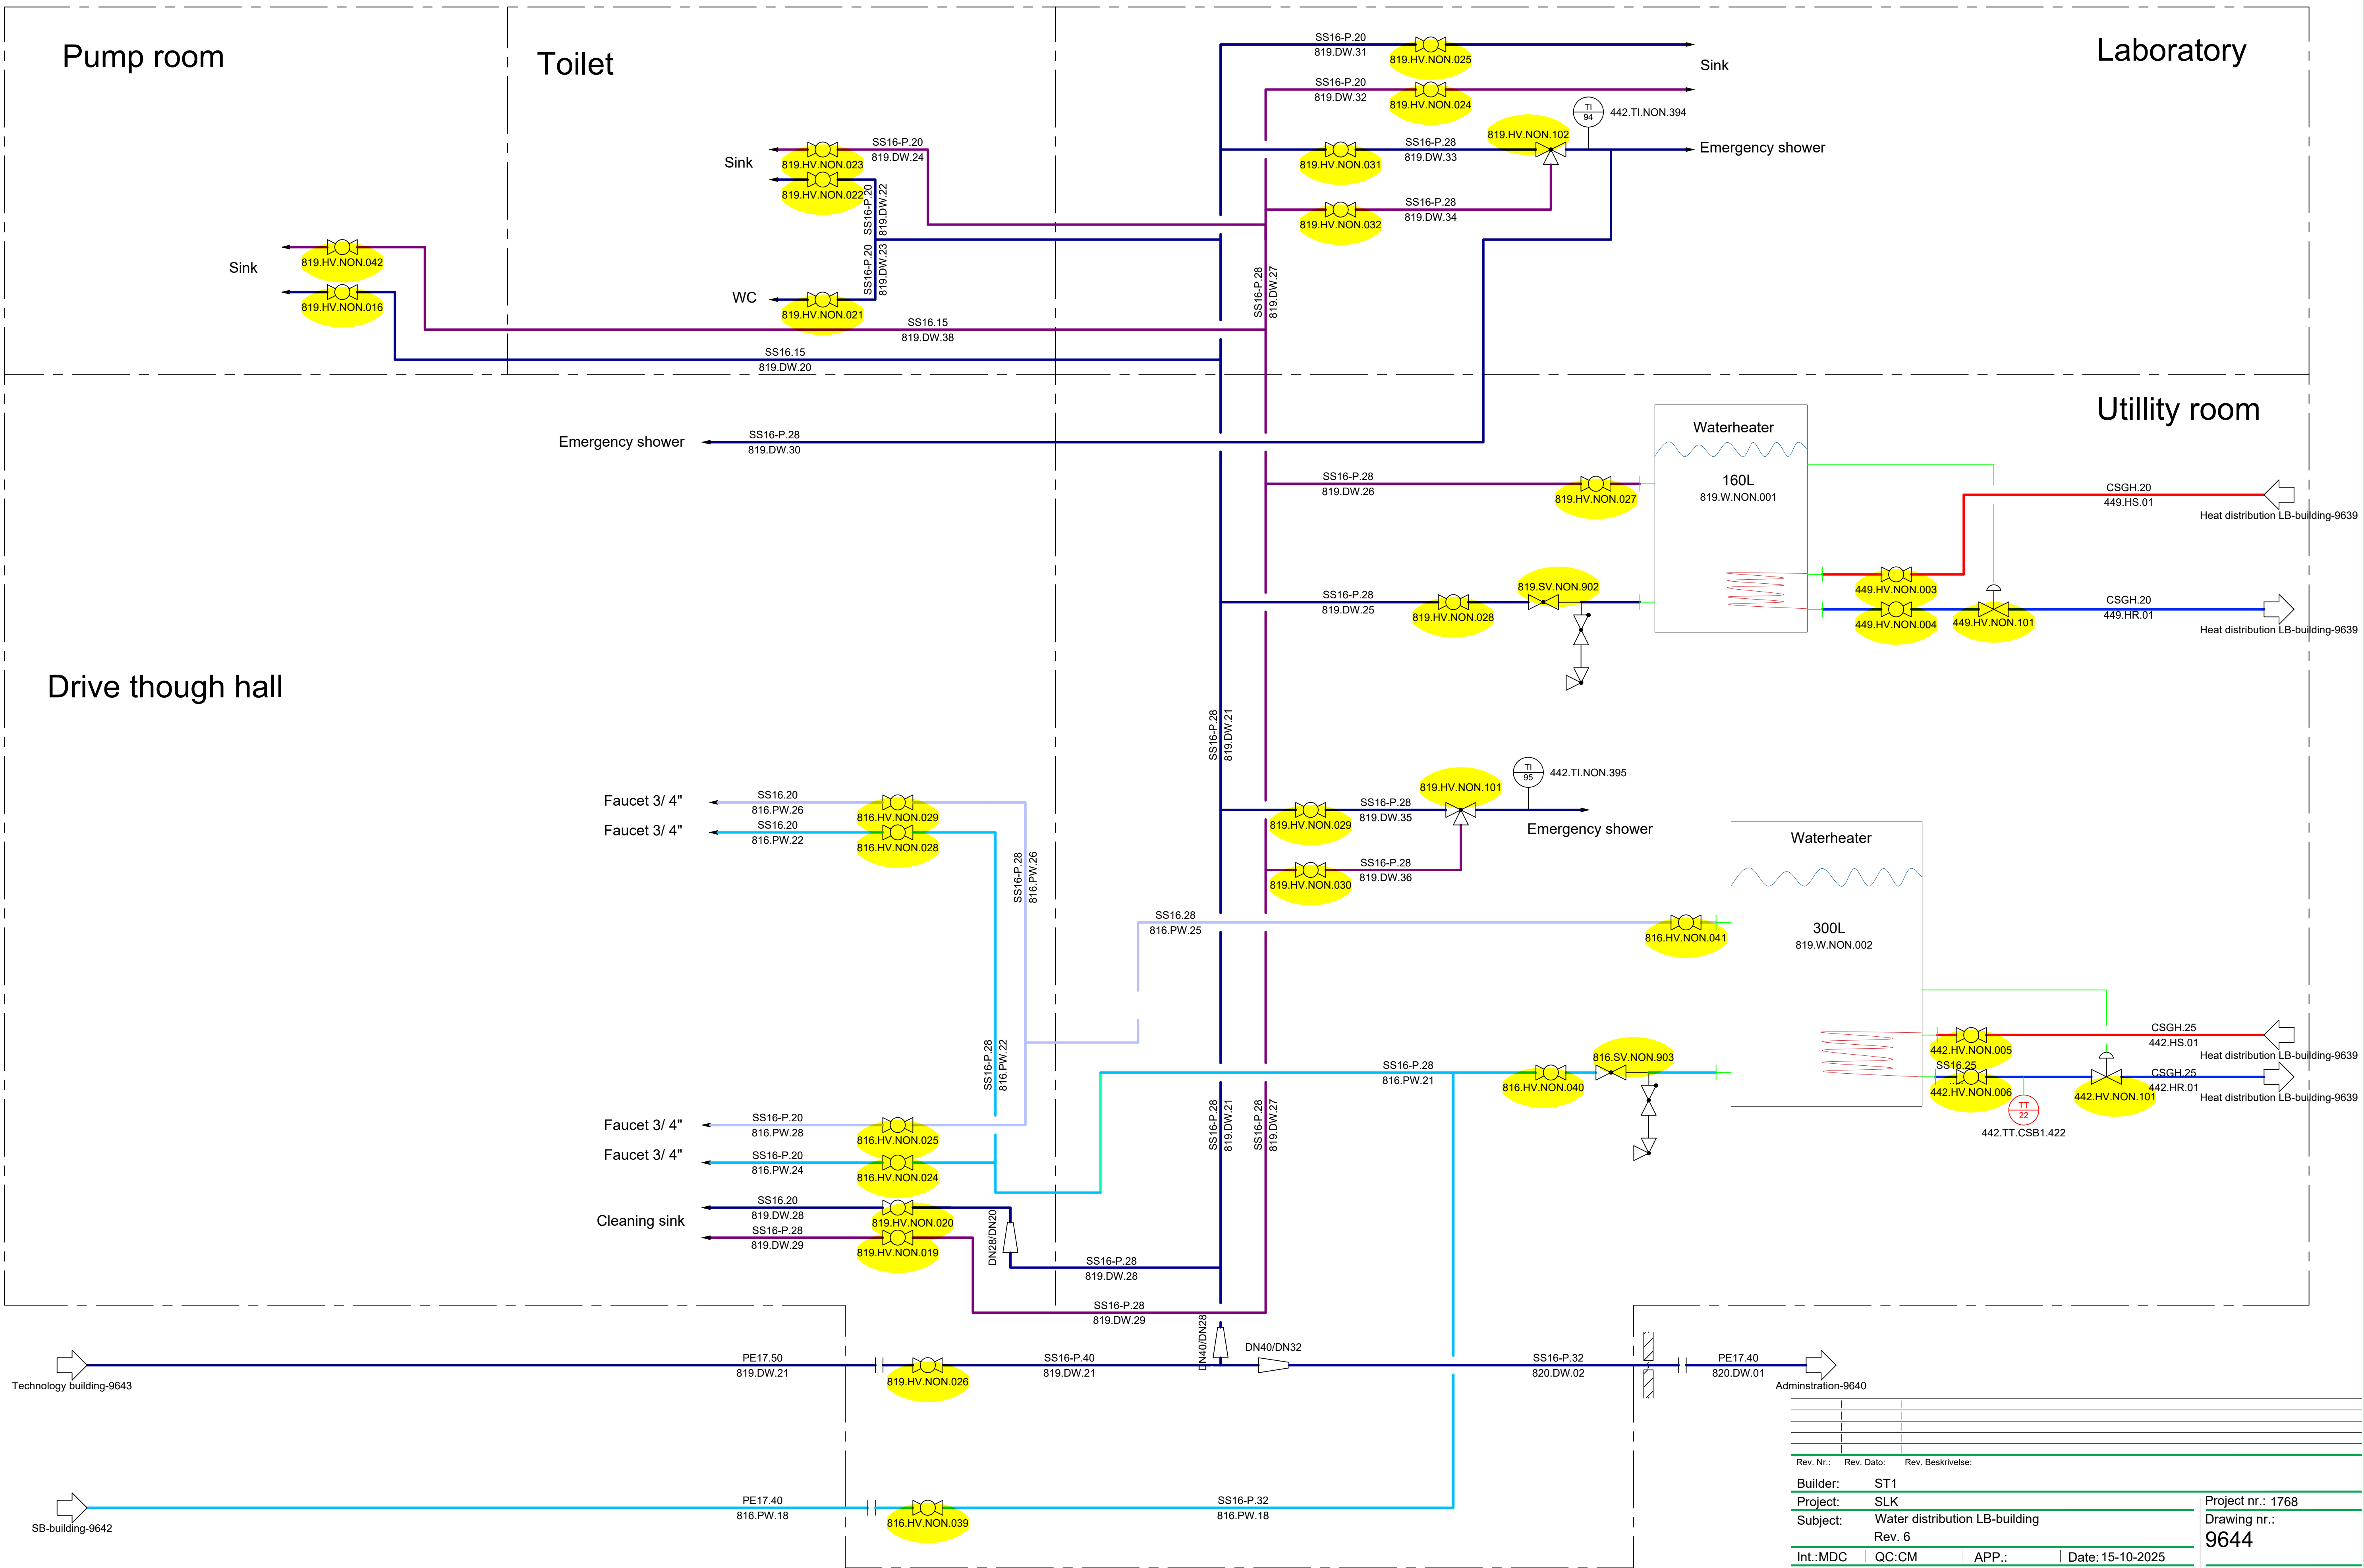


Rev. Nr.:	Rev. Dato:	Rev. Beskrivelse:
Builder:	ST1	
Project:	SLK	
Subject:	Water distribution LB-building	
Rev. 6		
Int.:MDC	QC:CM	APP.:
		Date: 15-10-2025
LUNDSBY RENEWABLE SOLUTIONS		
Lundsby Biogas A/S, Hjarbækvej 65, 8831 Løgstrup Tlf.: +45 96 49 43 00 Info@lundsbybiogas.dk Denne tegning er underlagt copyright og må ikke reproduceres uden tilladelse fra Lundsbybiogas A/S		
Project nr.: 1768 Drawing nr.: 9644		FORMAT: A1

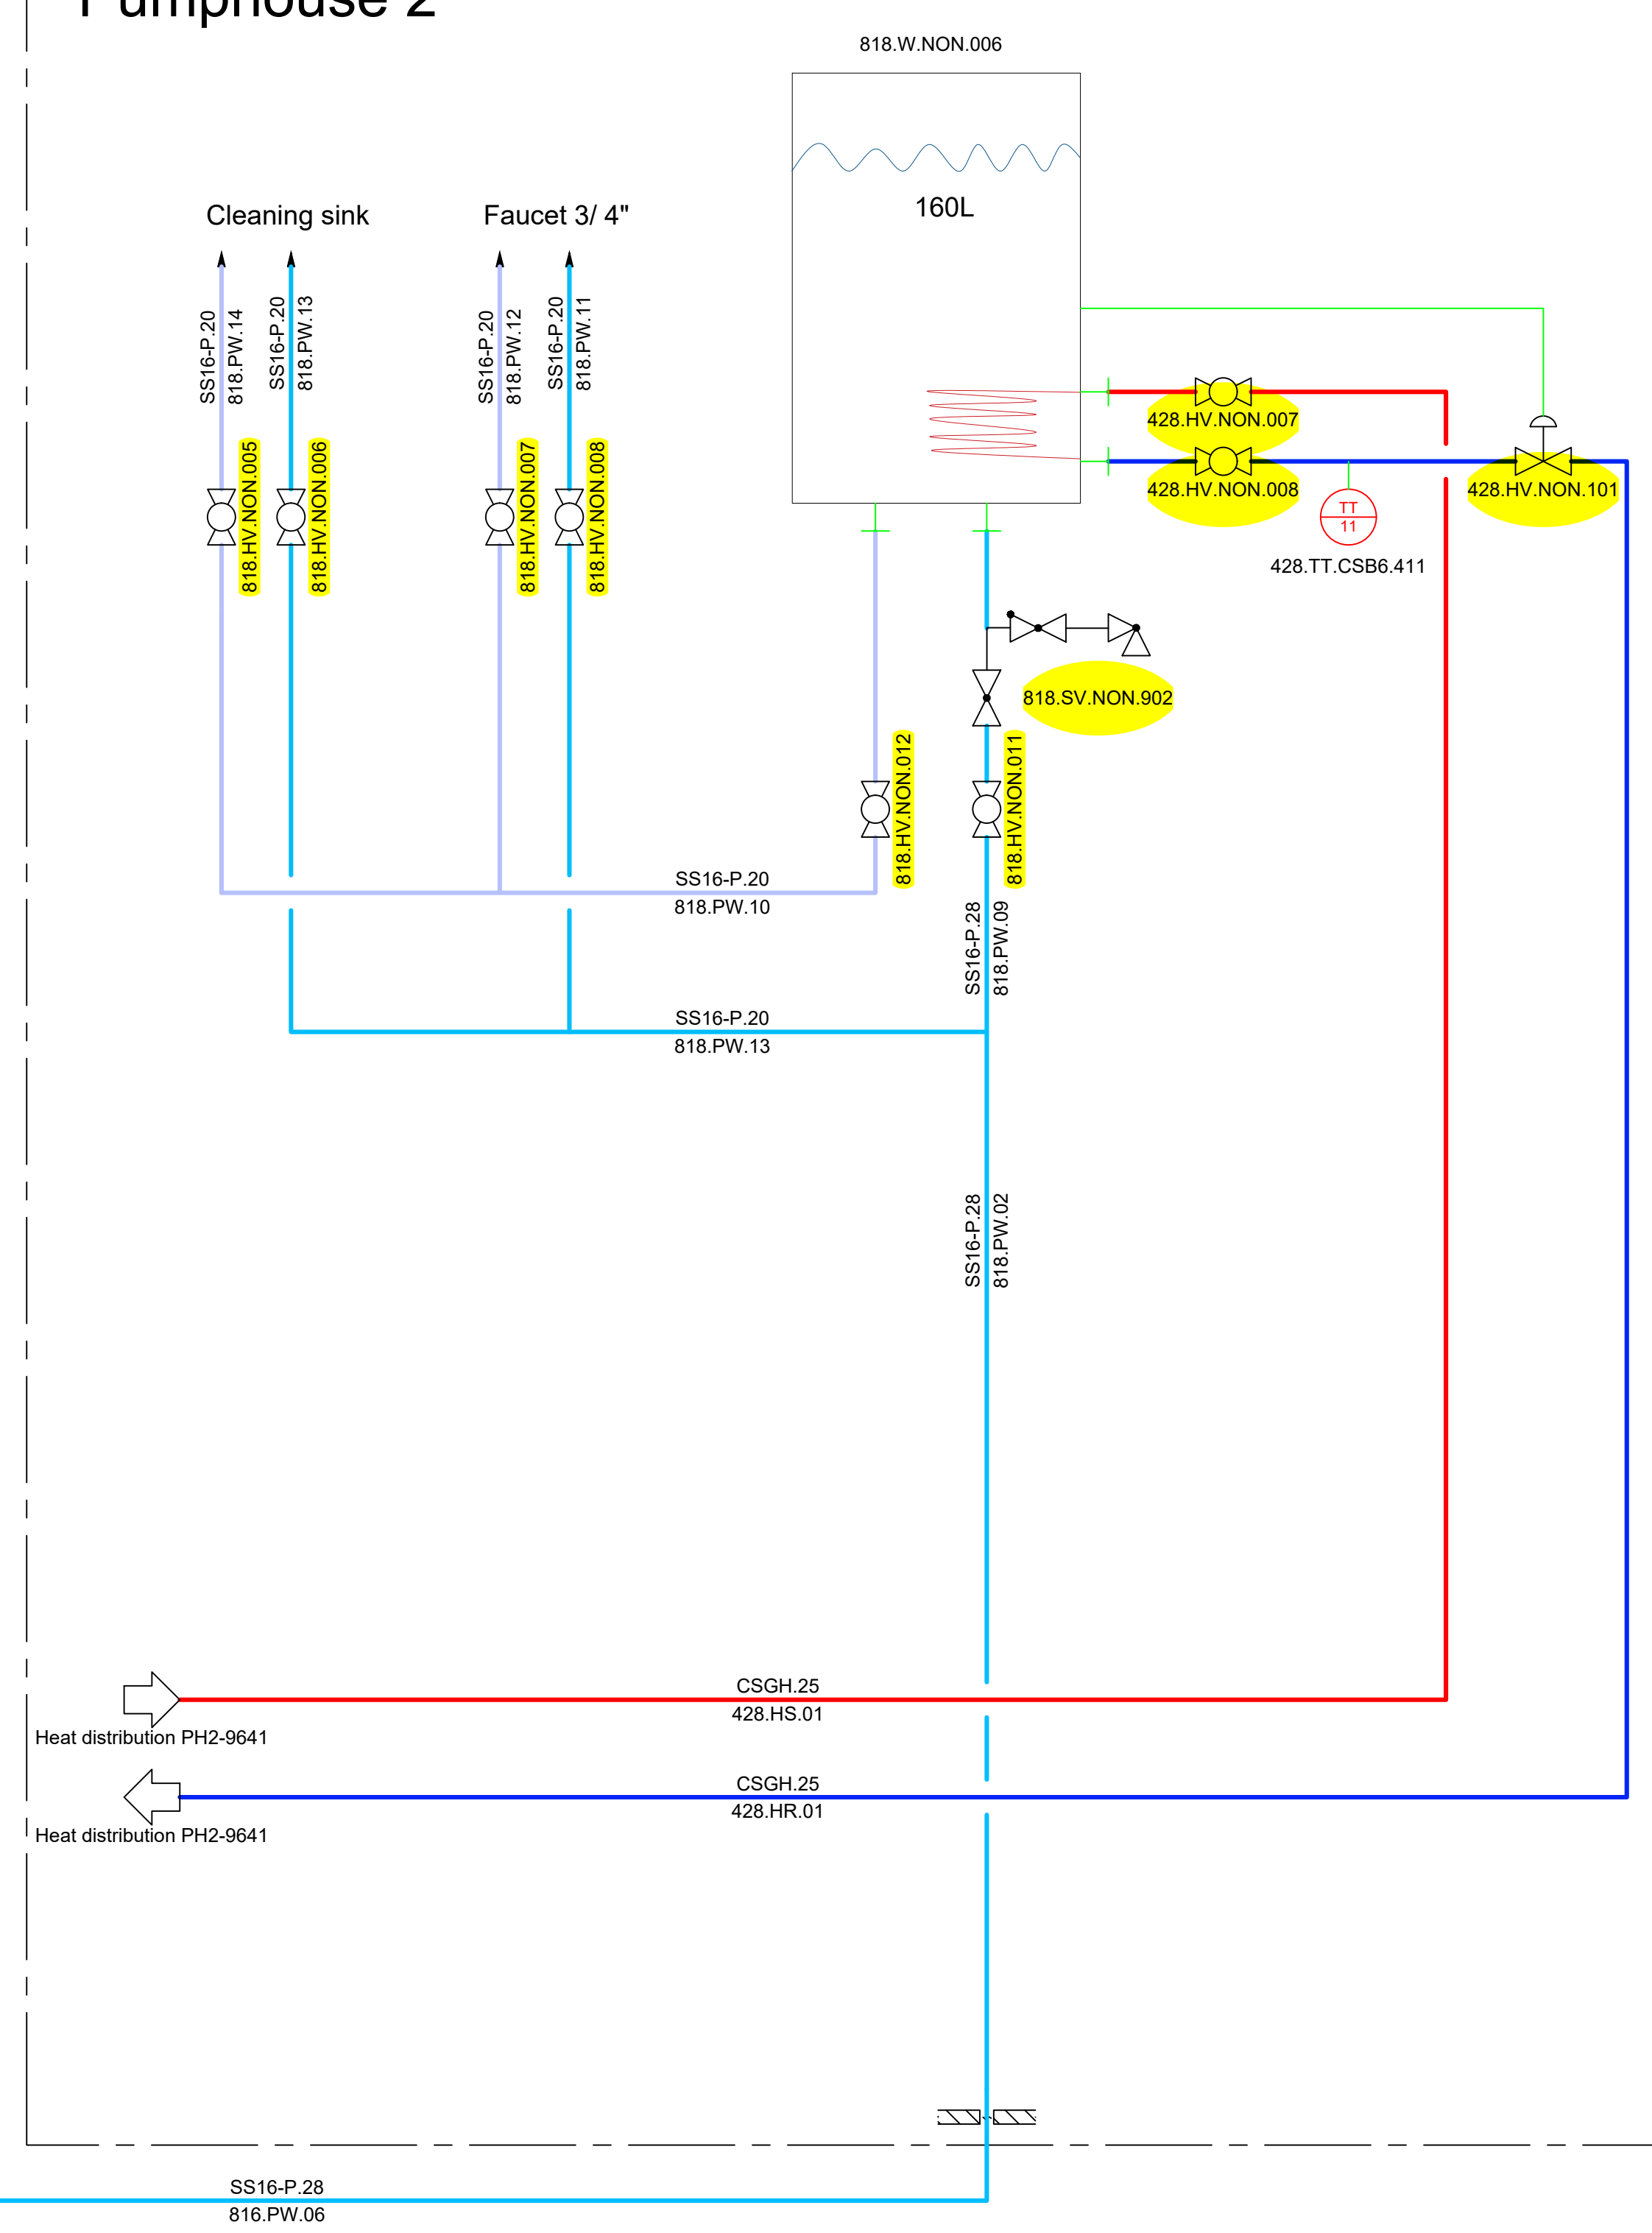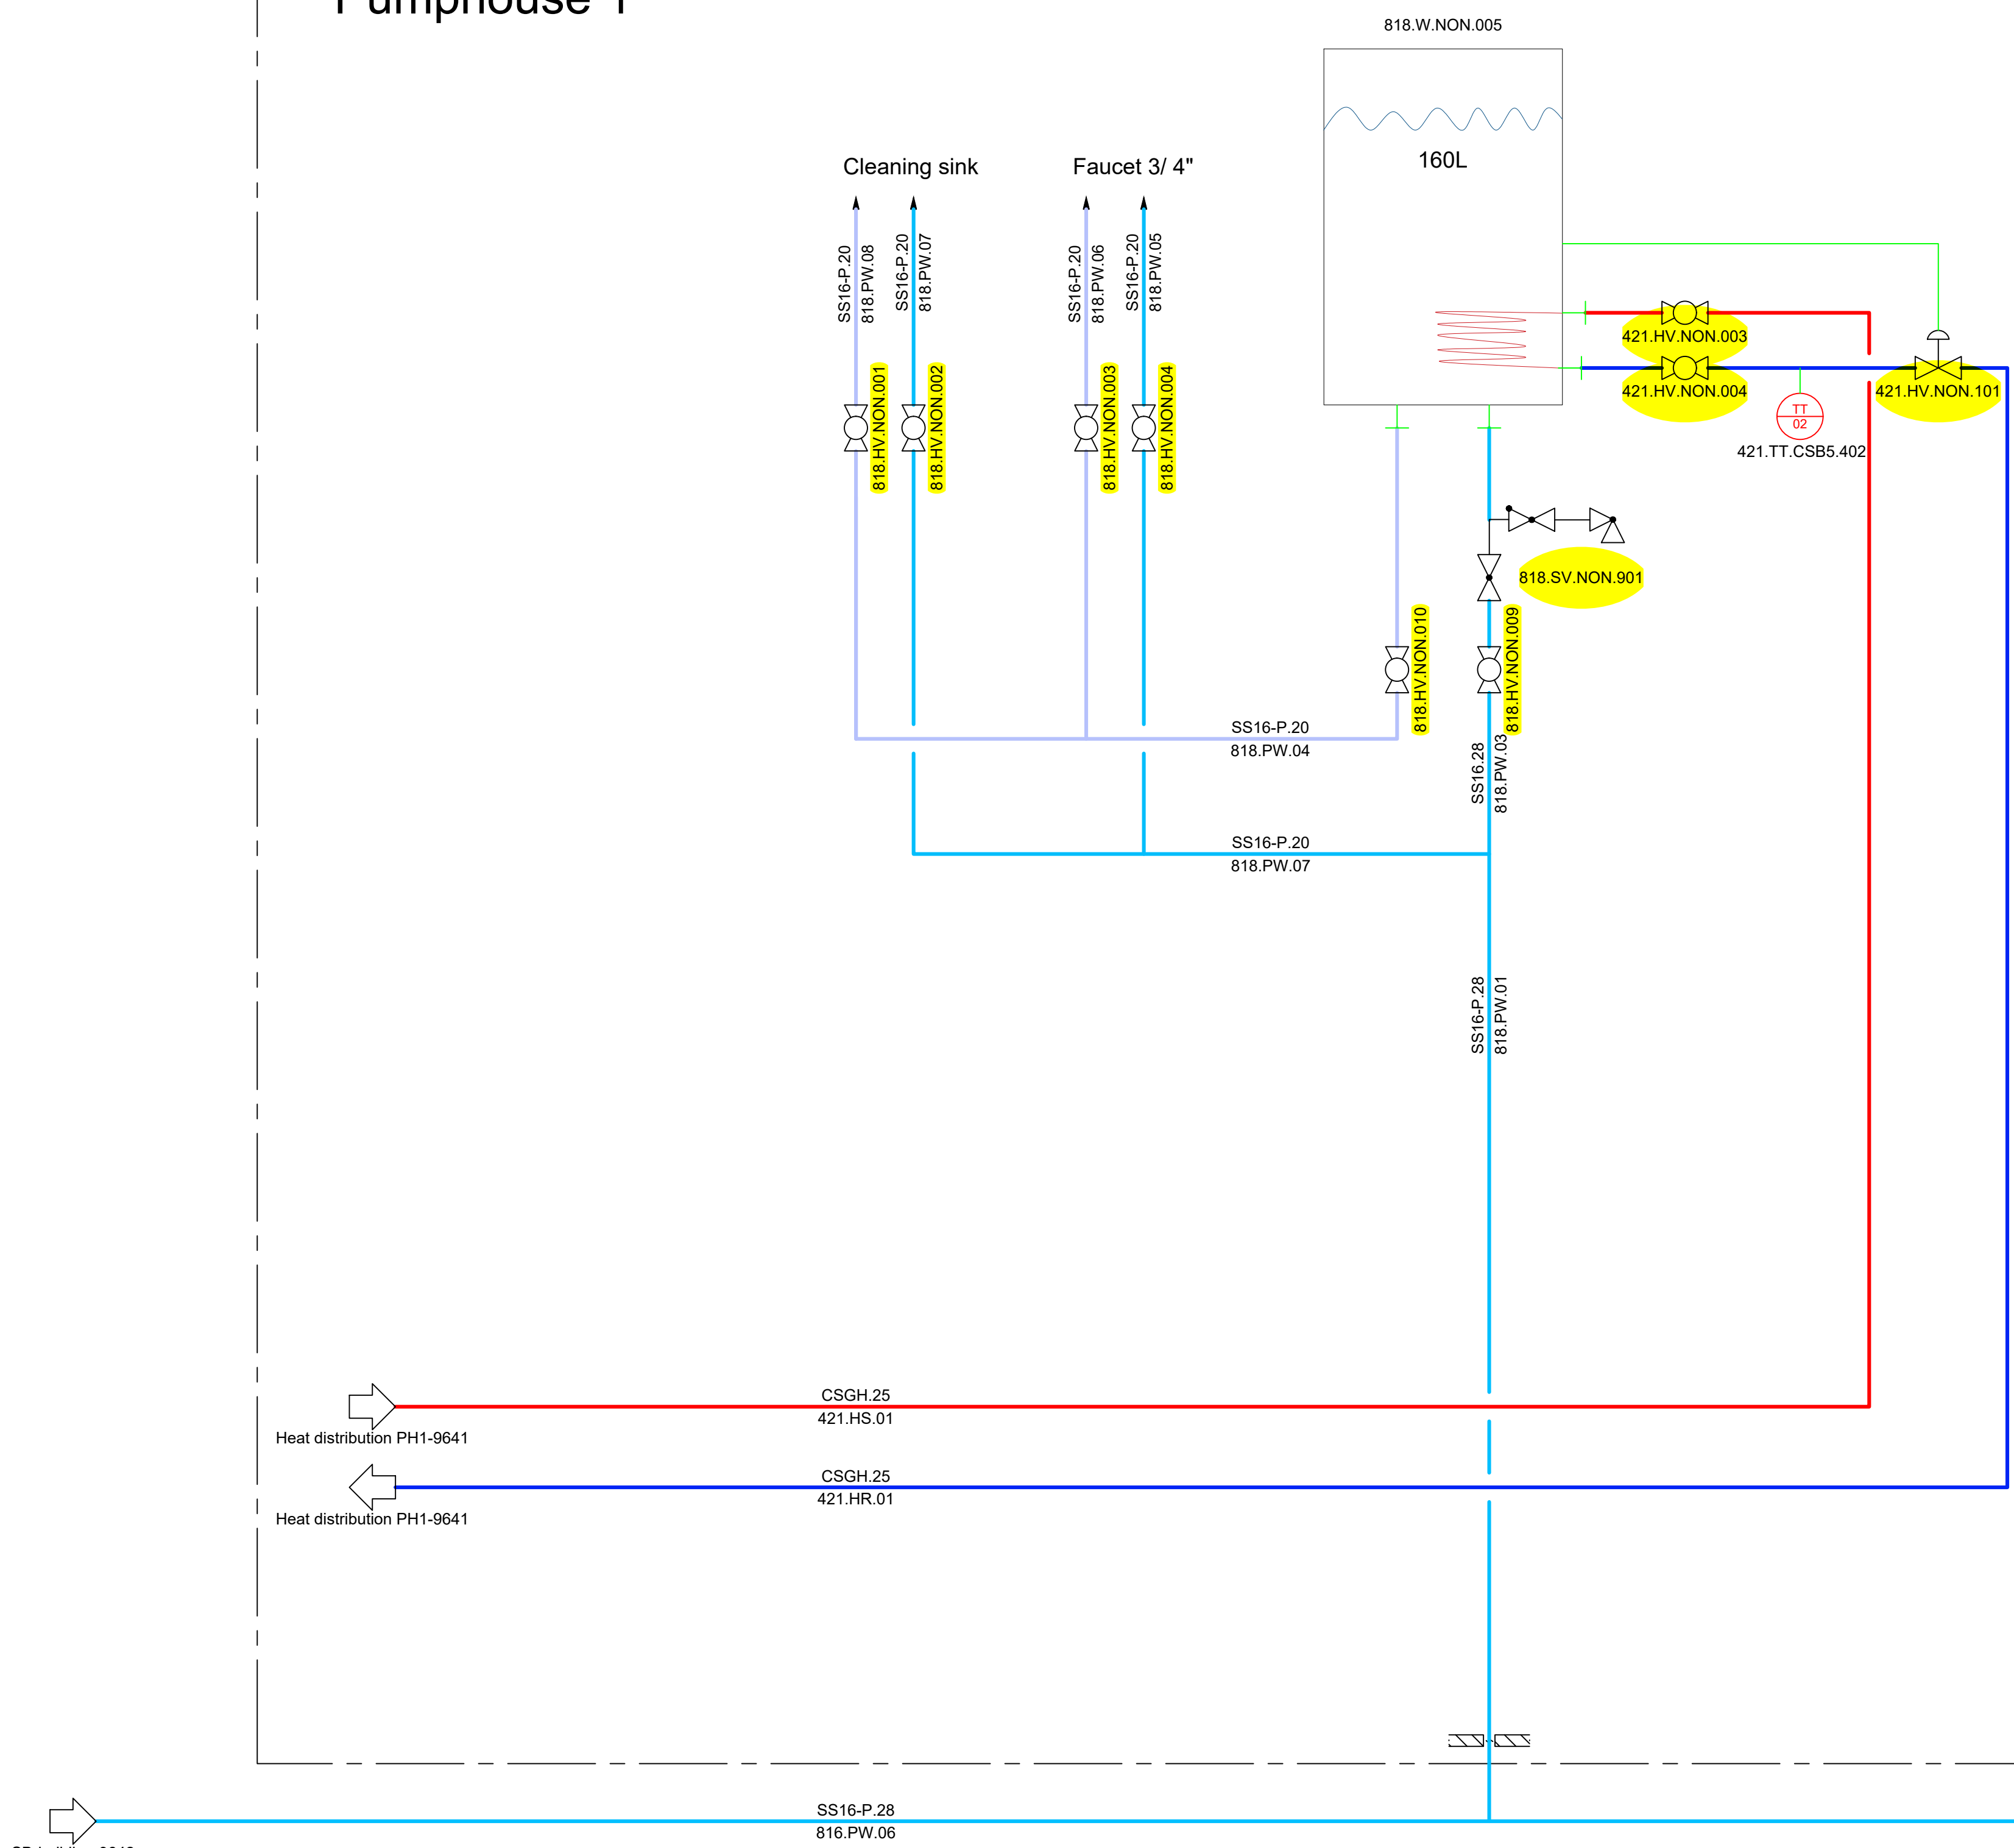
[illegible]

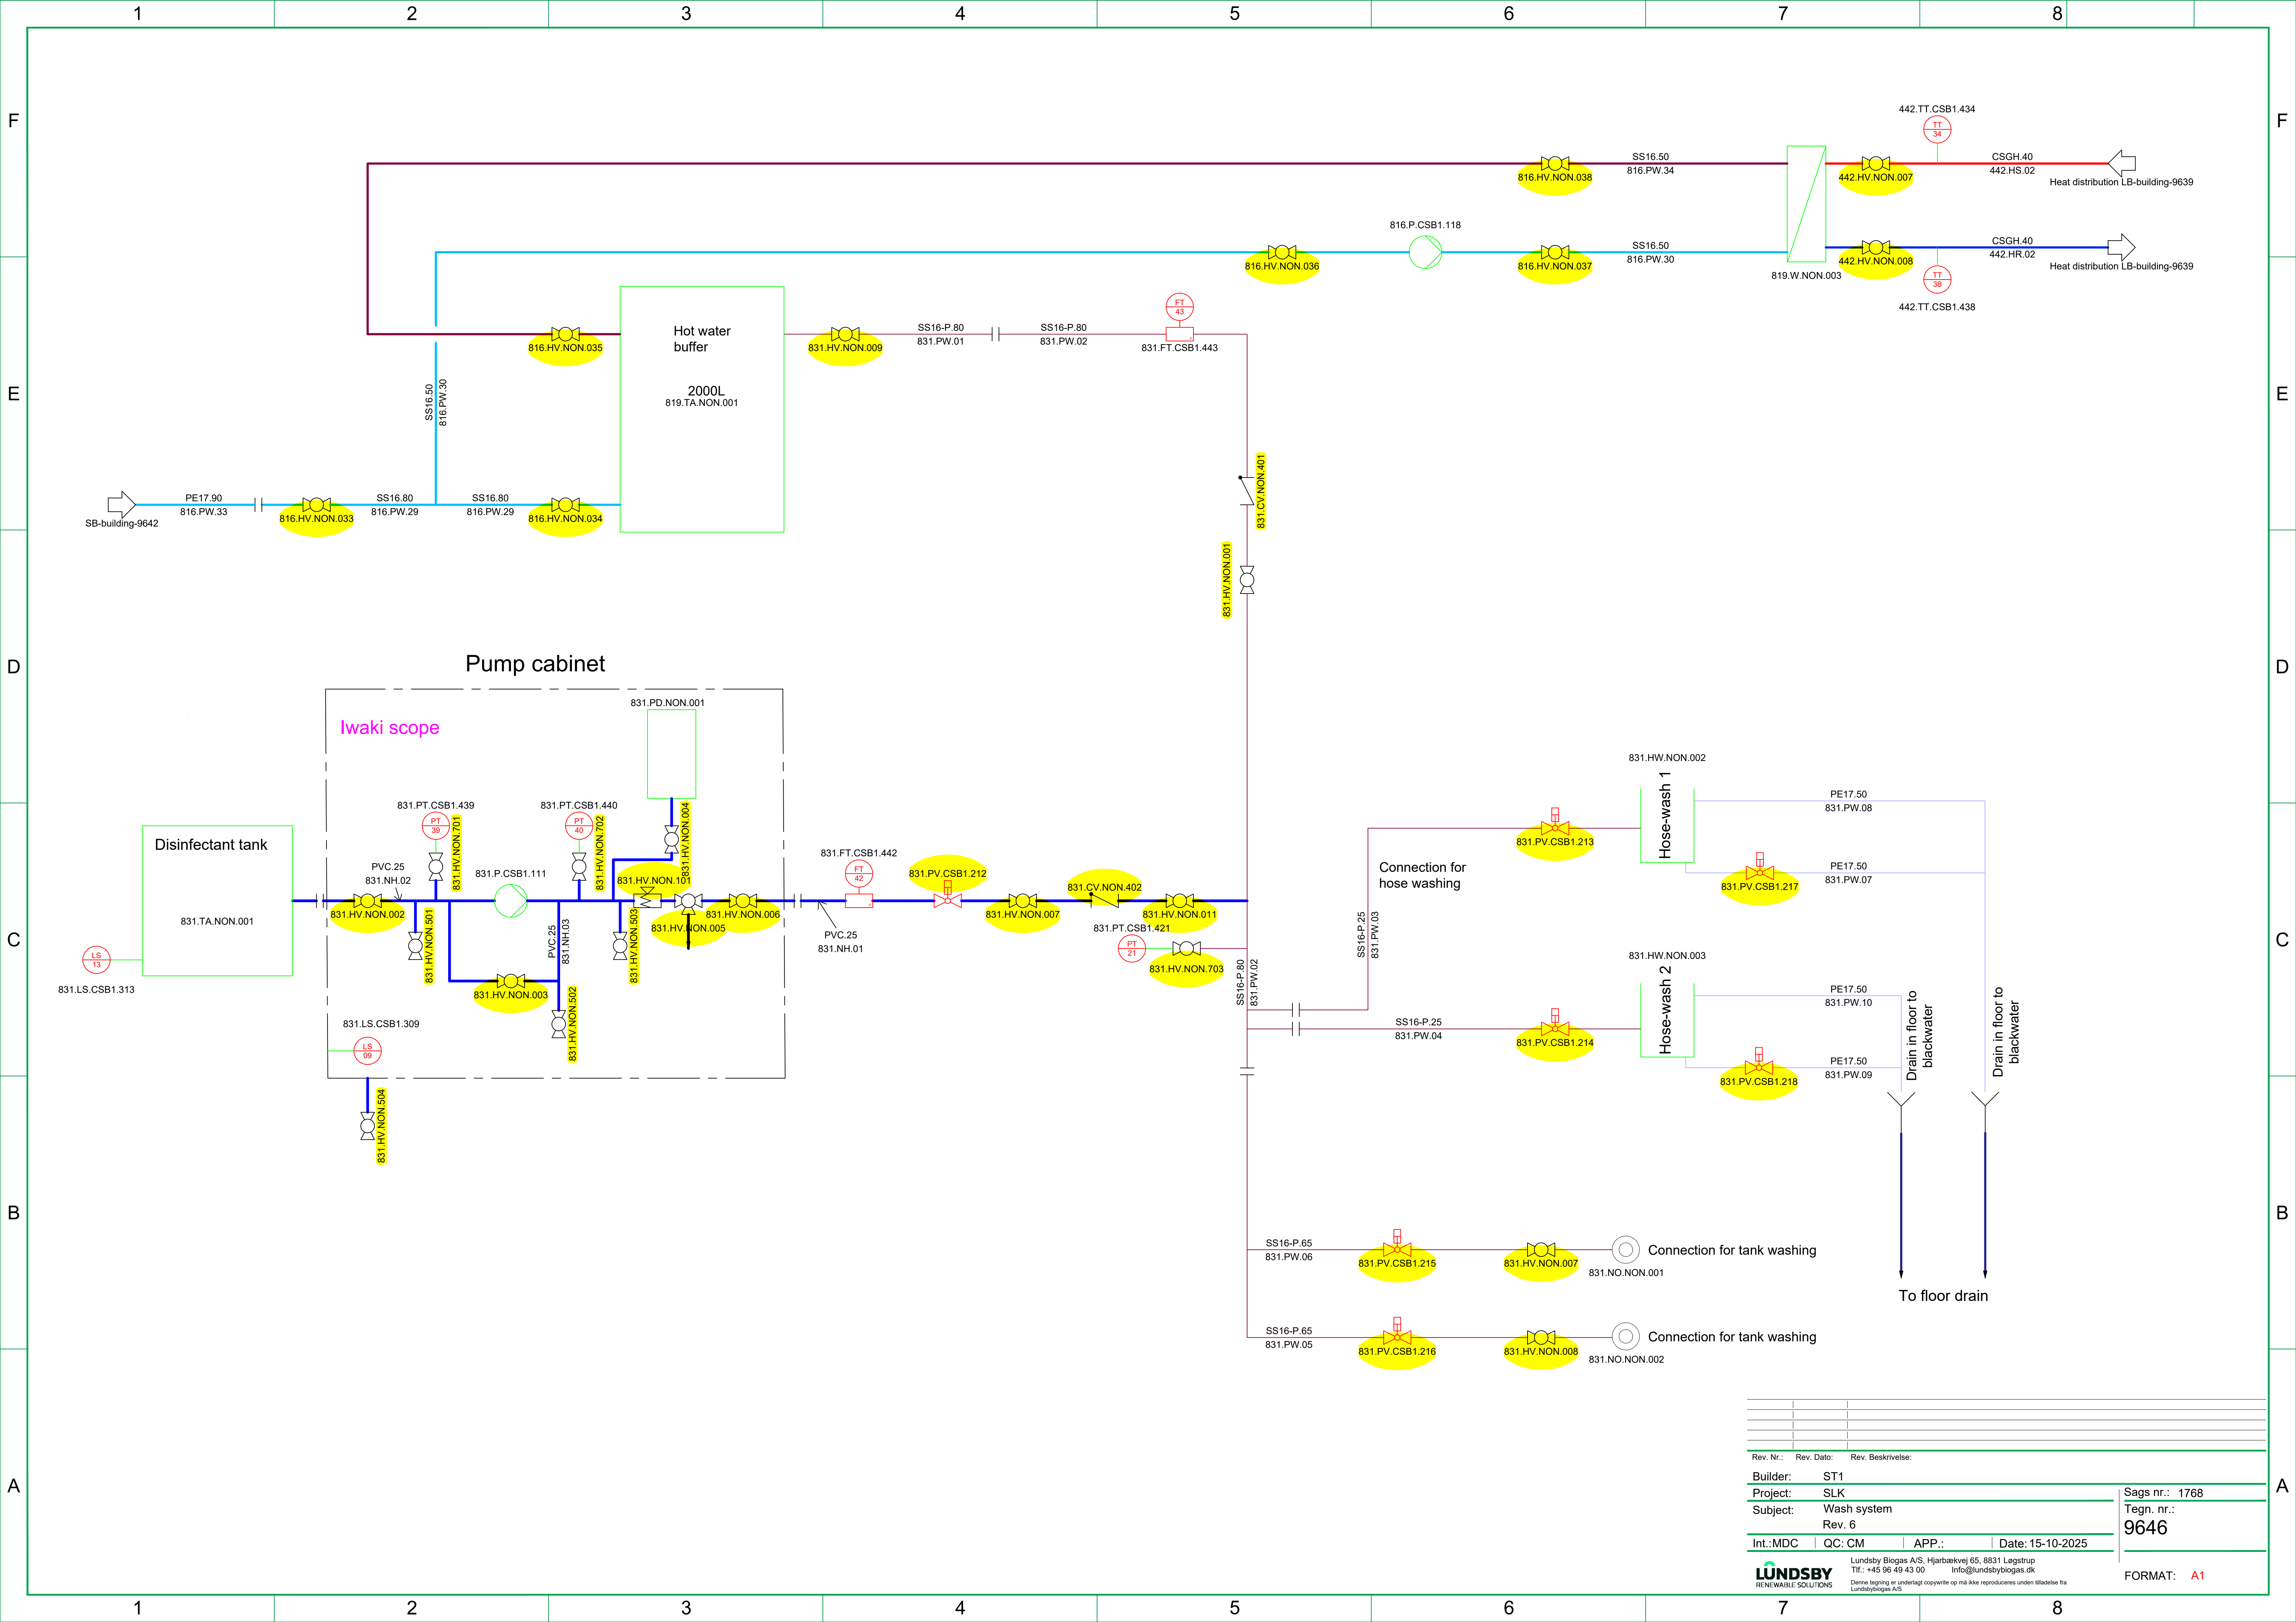

Rev. Nr.:	Rev. Dato:	Rev. Beskrivelse:	
Builder:	ST1		
Project:	SLK		
Subject:	Wash system		
Rev. 6			
Int.:MDC	QC: CM	APP.:	Date: 15-10-2025
LUNDSBY RENEWABLE SOLUTIONS			Lundsby Biogas A/S, Hjarbækvej 65, 8831 Løgstrup Tlf.: +45 96 49 43 00 info@lundsbybiogas.dk Denne tegning er underlagt copyright op på ikke reproduceres uden tilladelse fra Lundsbybiogas A/S
			Sags nr.: 1768 Tegn. nr.: 9646 FORMAT: A1

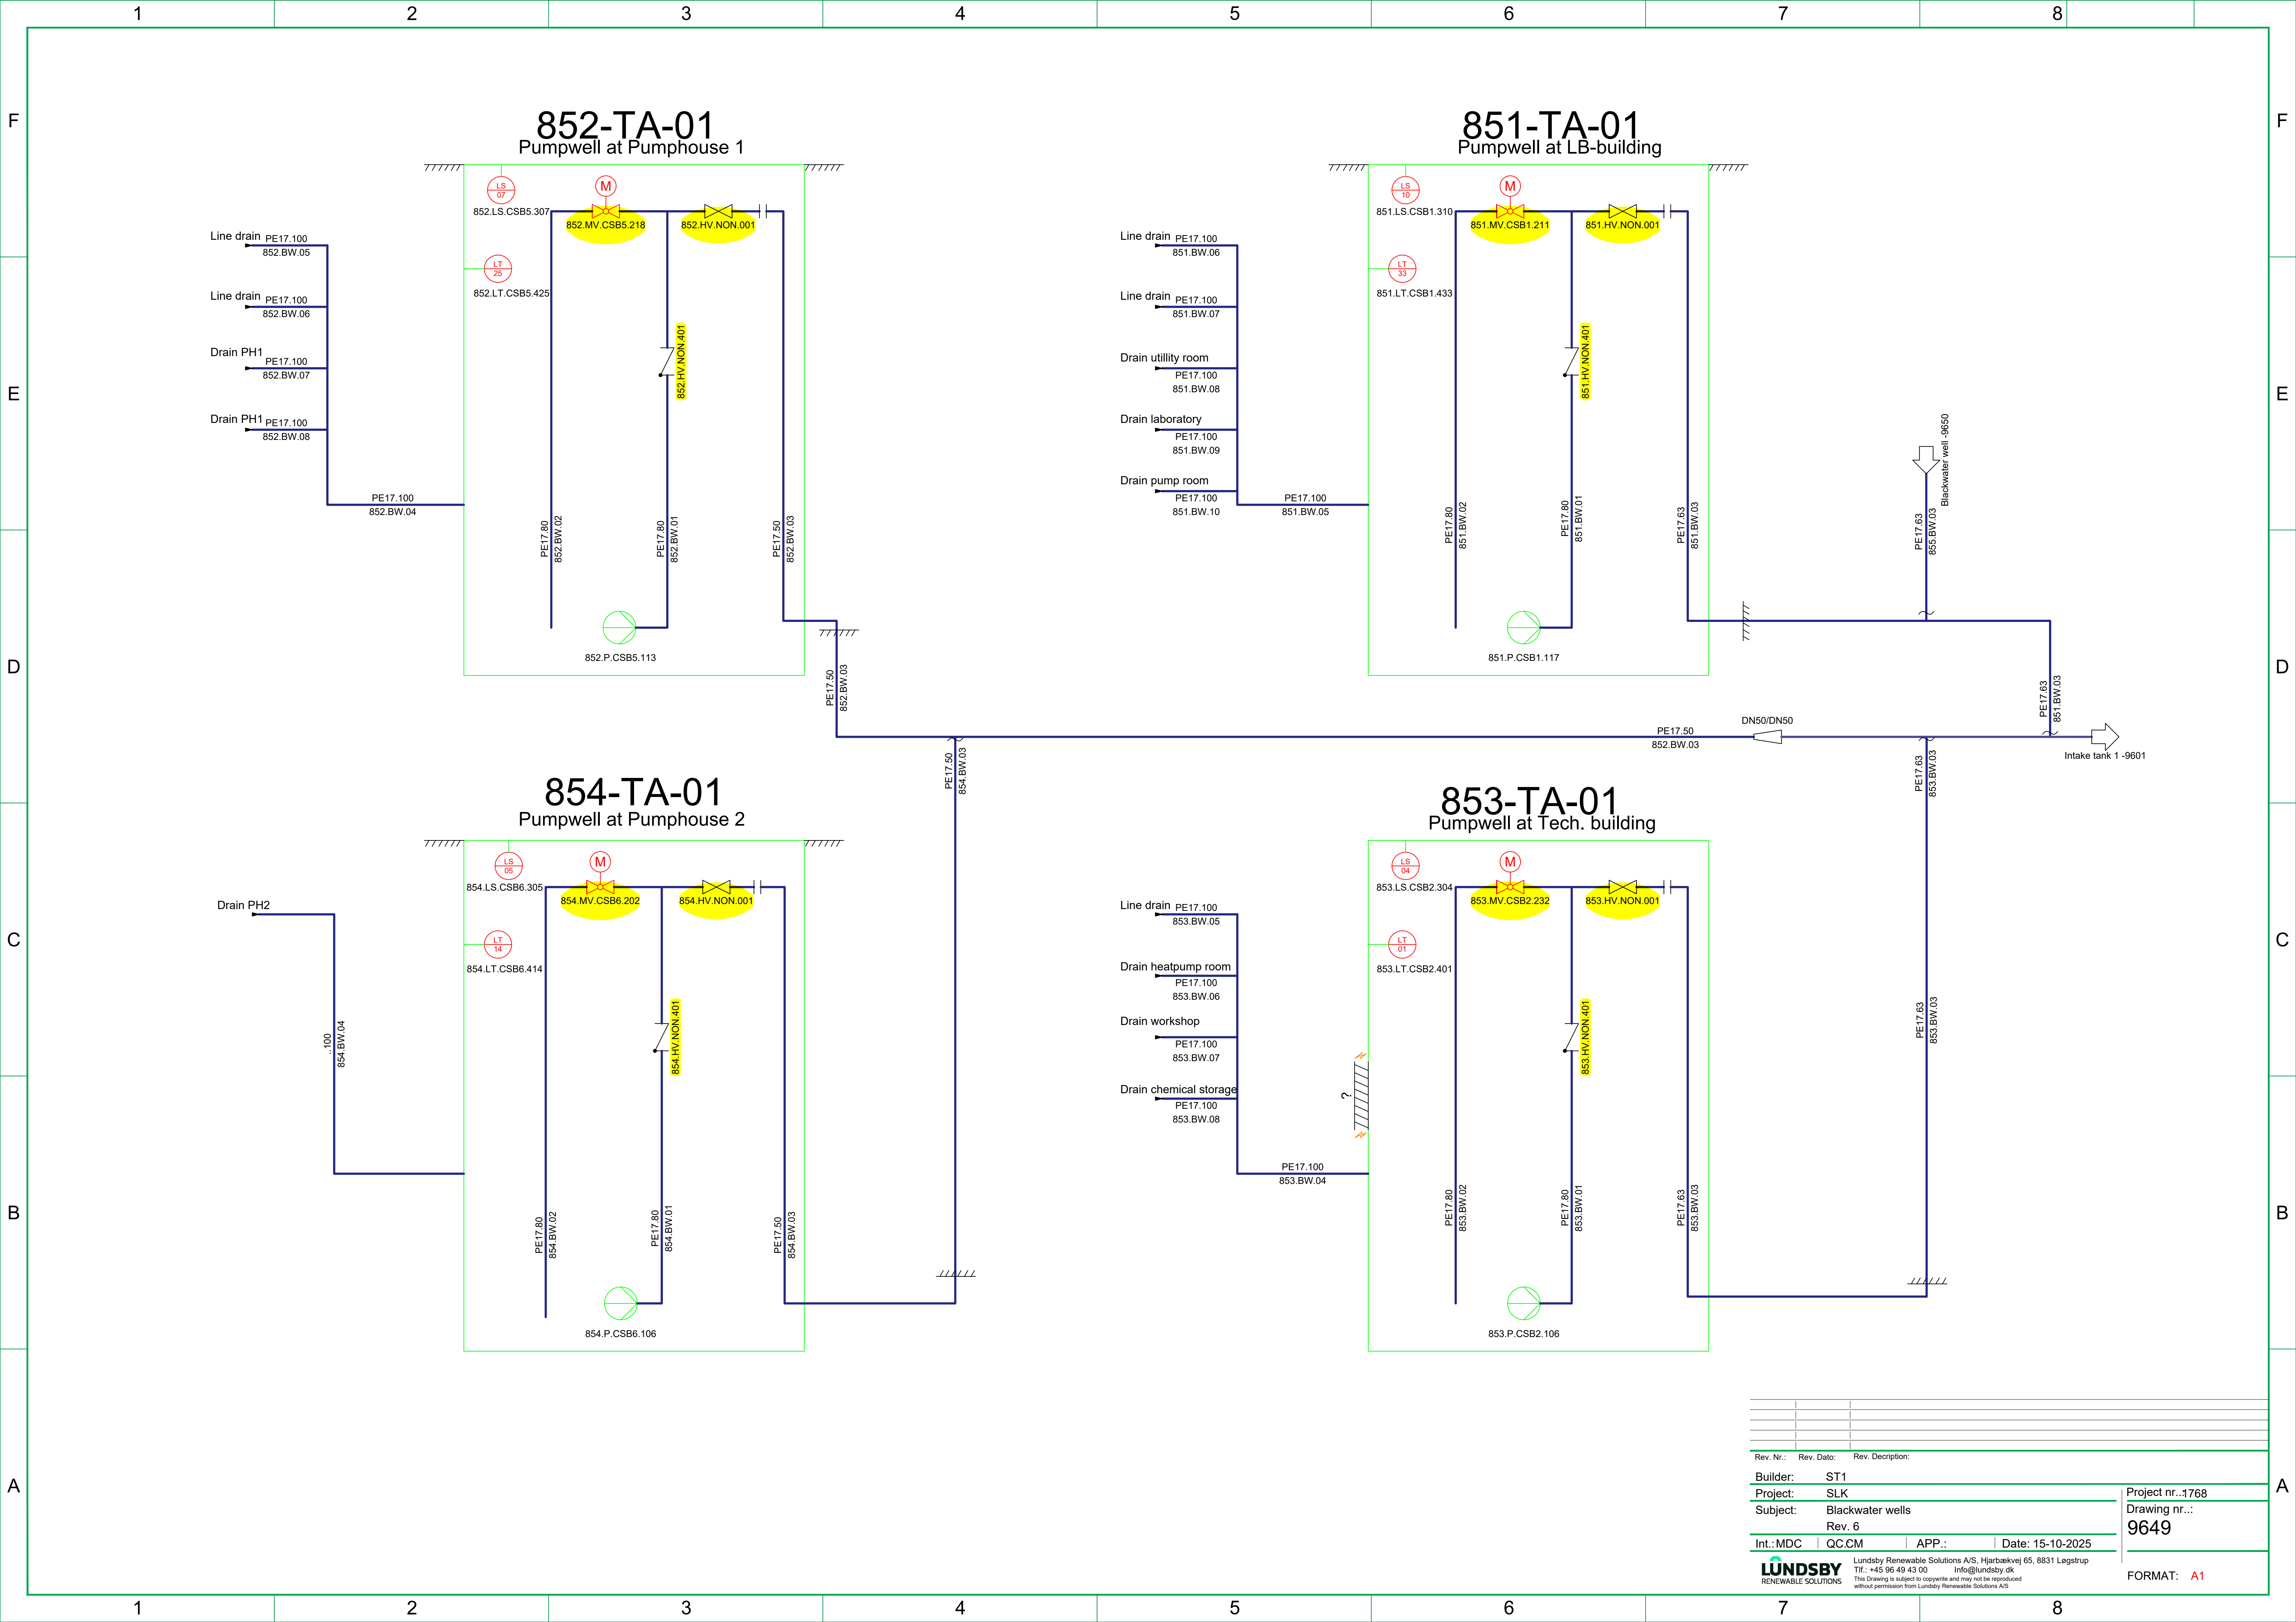


Rev. Nr.:	Rev. Dato:	Rev. Description:	
Builder:	ST1		
Project:	SLK		
Subject:	Blackwater wells		
Rev. 6			
Int.:MDC	QC:CM	APP.:	Date: 15-10-2025
LUNDSBY RENEWABLE SOLUTIONS			Lundsby Renewable Solutions A/S, Hjarbækvej 65, 8831 Løgstrup Tlf.: +45 96 49 43 00 Info@lundsby.dk This drawing is subject to copyright and may not be reproduced without permission from Lundsby Renewable Solutions A/S
Project nr.:1768 Drawing nr.: 9649			FORMAT: A1

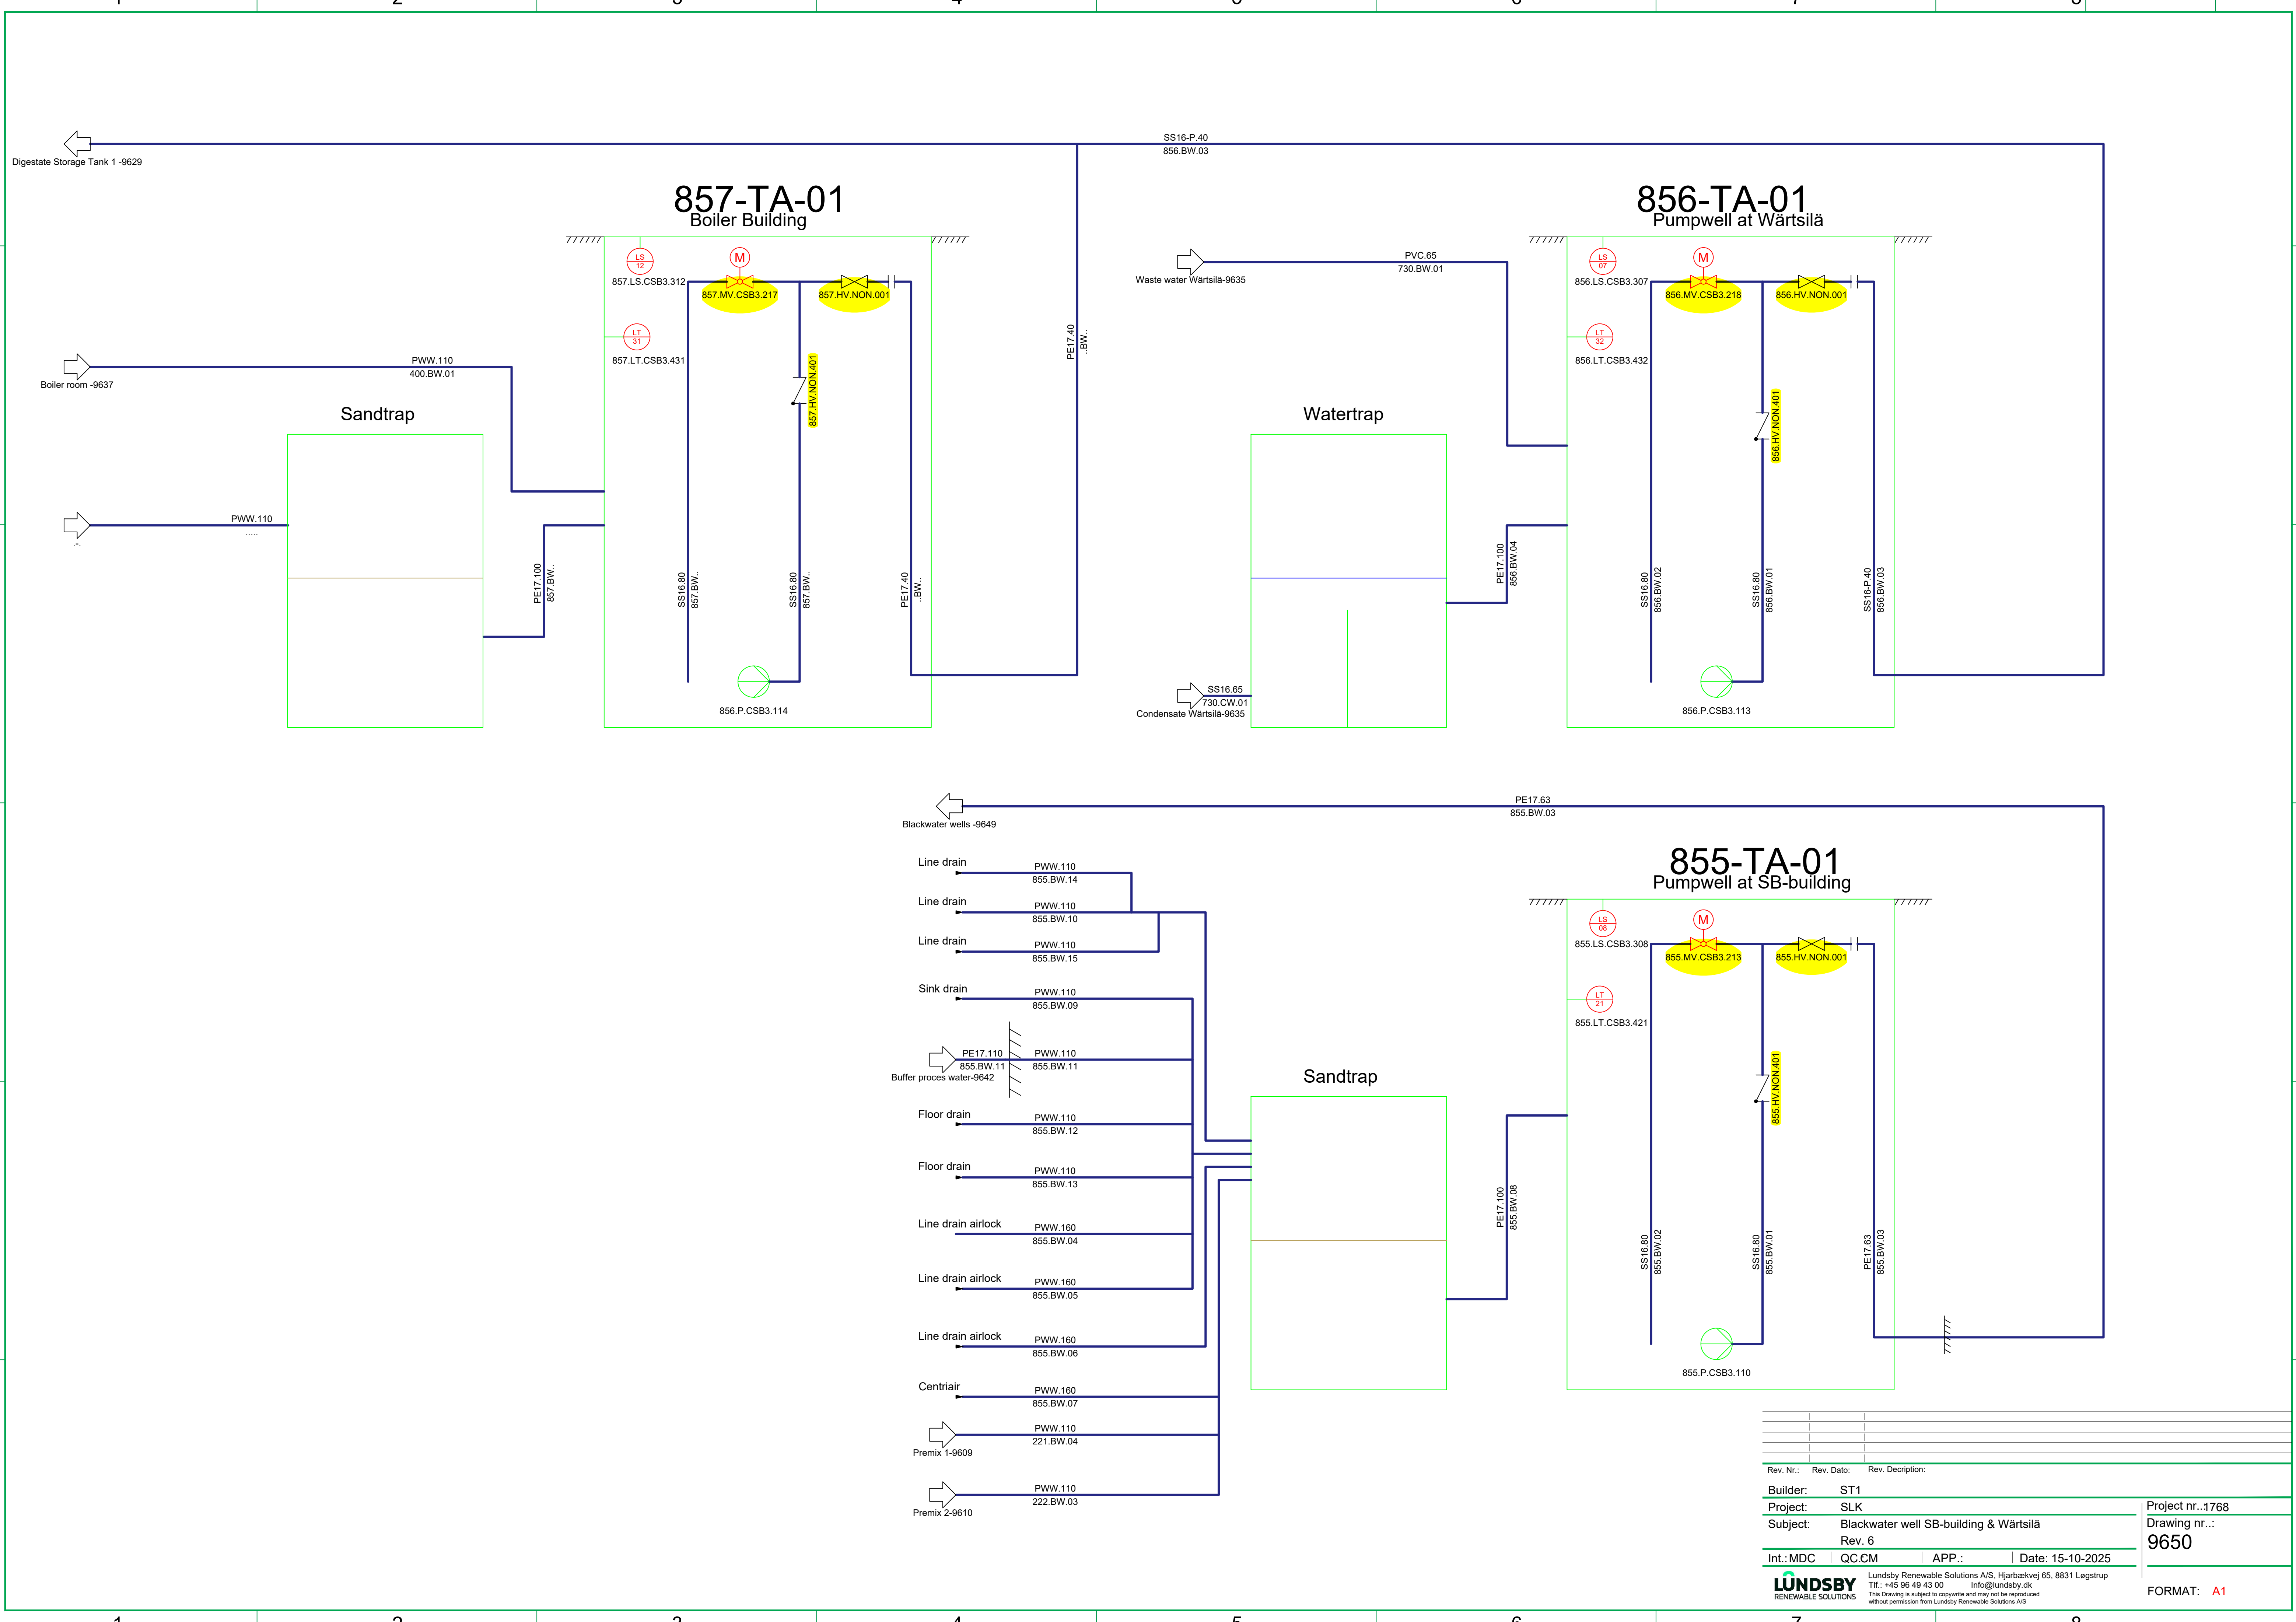

- Line drain PWW.110 855.BW.14
- Line drain PWW.110 855.BW.10
- Line drain PWW.110 855.BW.15
- Sink drain PWW.110 855.BW.09
- PE17.110 855.BW.11 PWW.110 855.BW.11
- Buffer proces water-9642
- Floor drain PWW.110 855.BW.12
- Floor drain PWW.110 855.BW.13
- Line drain airlock PWW.160 855.BW.04
- Line drain airlock PWW.160 855.BW.05
- Line drain airlock PWW.160 855.BW.06
- Centriair PWW.160 855.BW.07
- Premix 1-9609 PWW.110 221.BW.04
- Premix 2-9610 PWW.110 222.BW.03


Rev. Nr.:	Rev. Dato:	Rev. Description:
Builder:	ST1	
Project:	SLK	
Subject:	Blackwater well SB-building & Wärtsilä	
	Rev. 6	
Int.:MDC	QC:CM	APP.:
		Date: 15-10-2025
LUNDSBY RENEWABLE SOLUTIONS		
Lundsgby Renewable Solutions A/S, Hjarbrækvej 65, 8831 Løgstrup		
Tlf.: +45 96 49 43 00		
Info@lundsgby.dk		
This Drawing is subject to copyright and may not be reproduced without permission from Lundsgby Renewable Solutions A/S		
Project nr.:1768		Drawing nr.: 9650
FORMAT: A1		

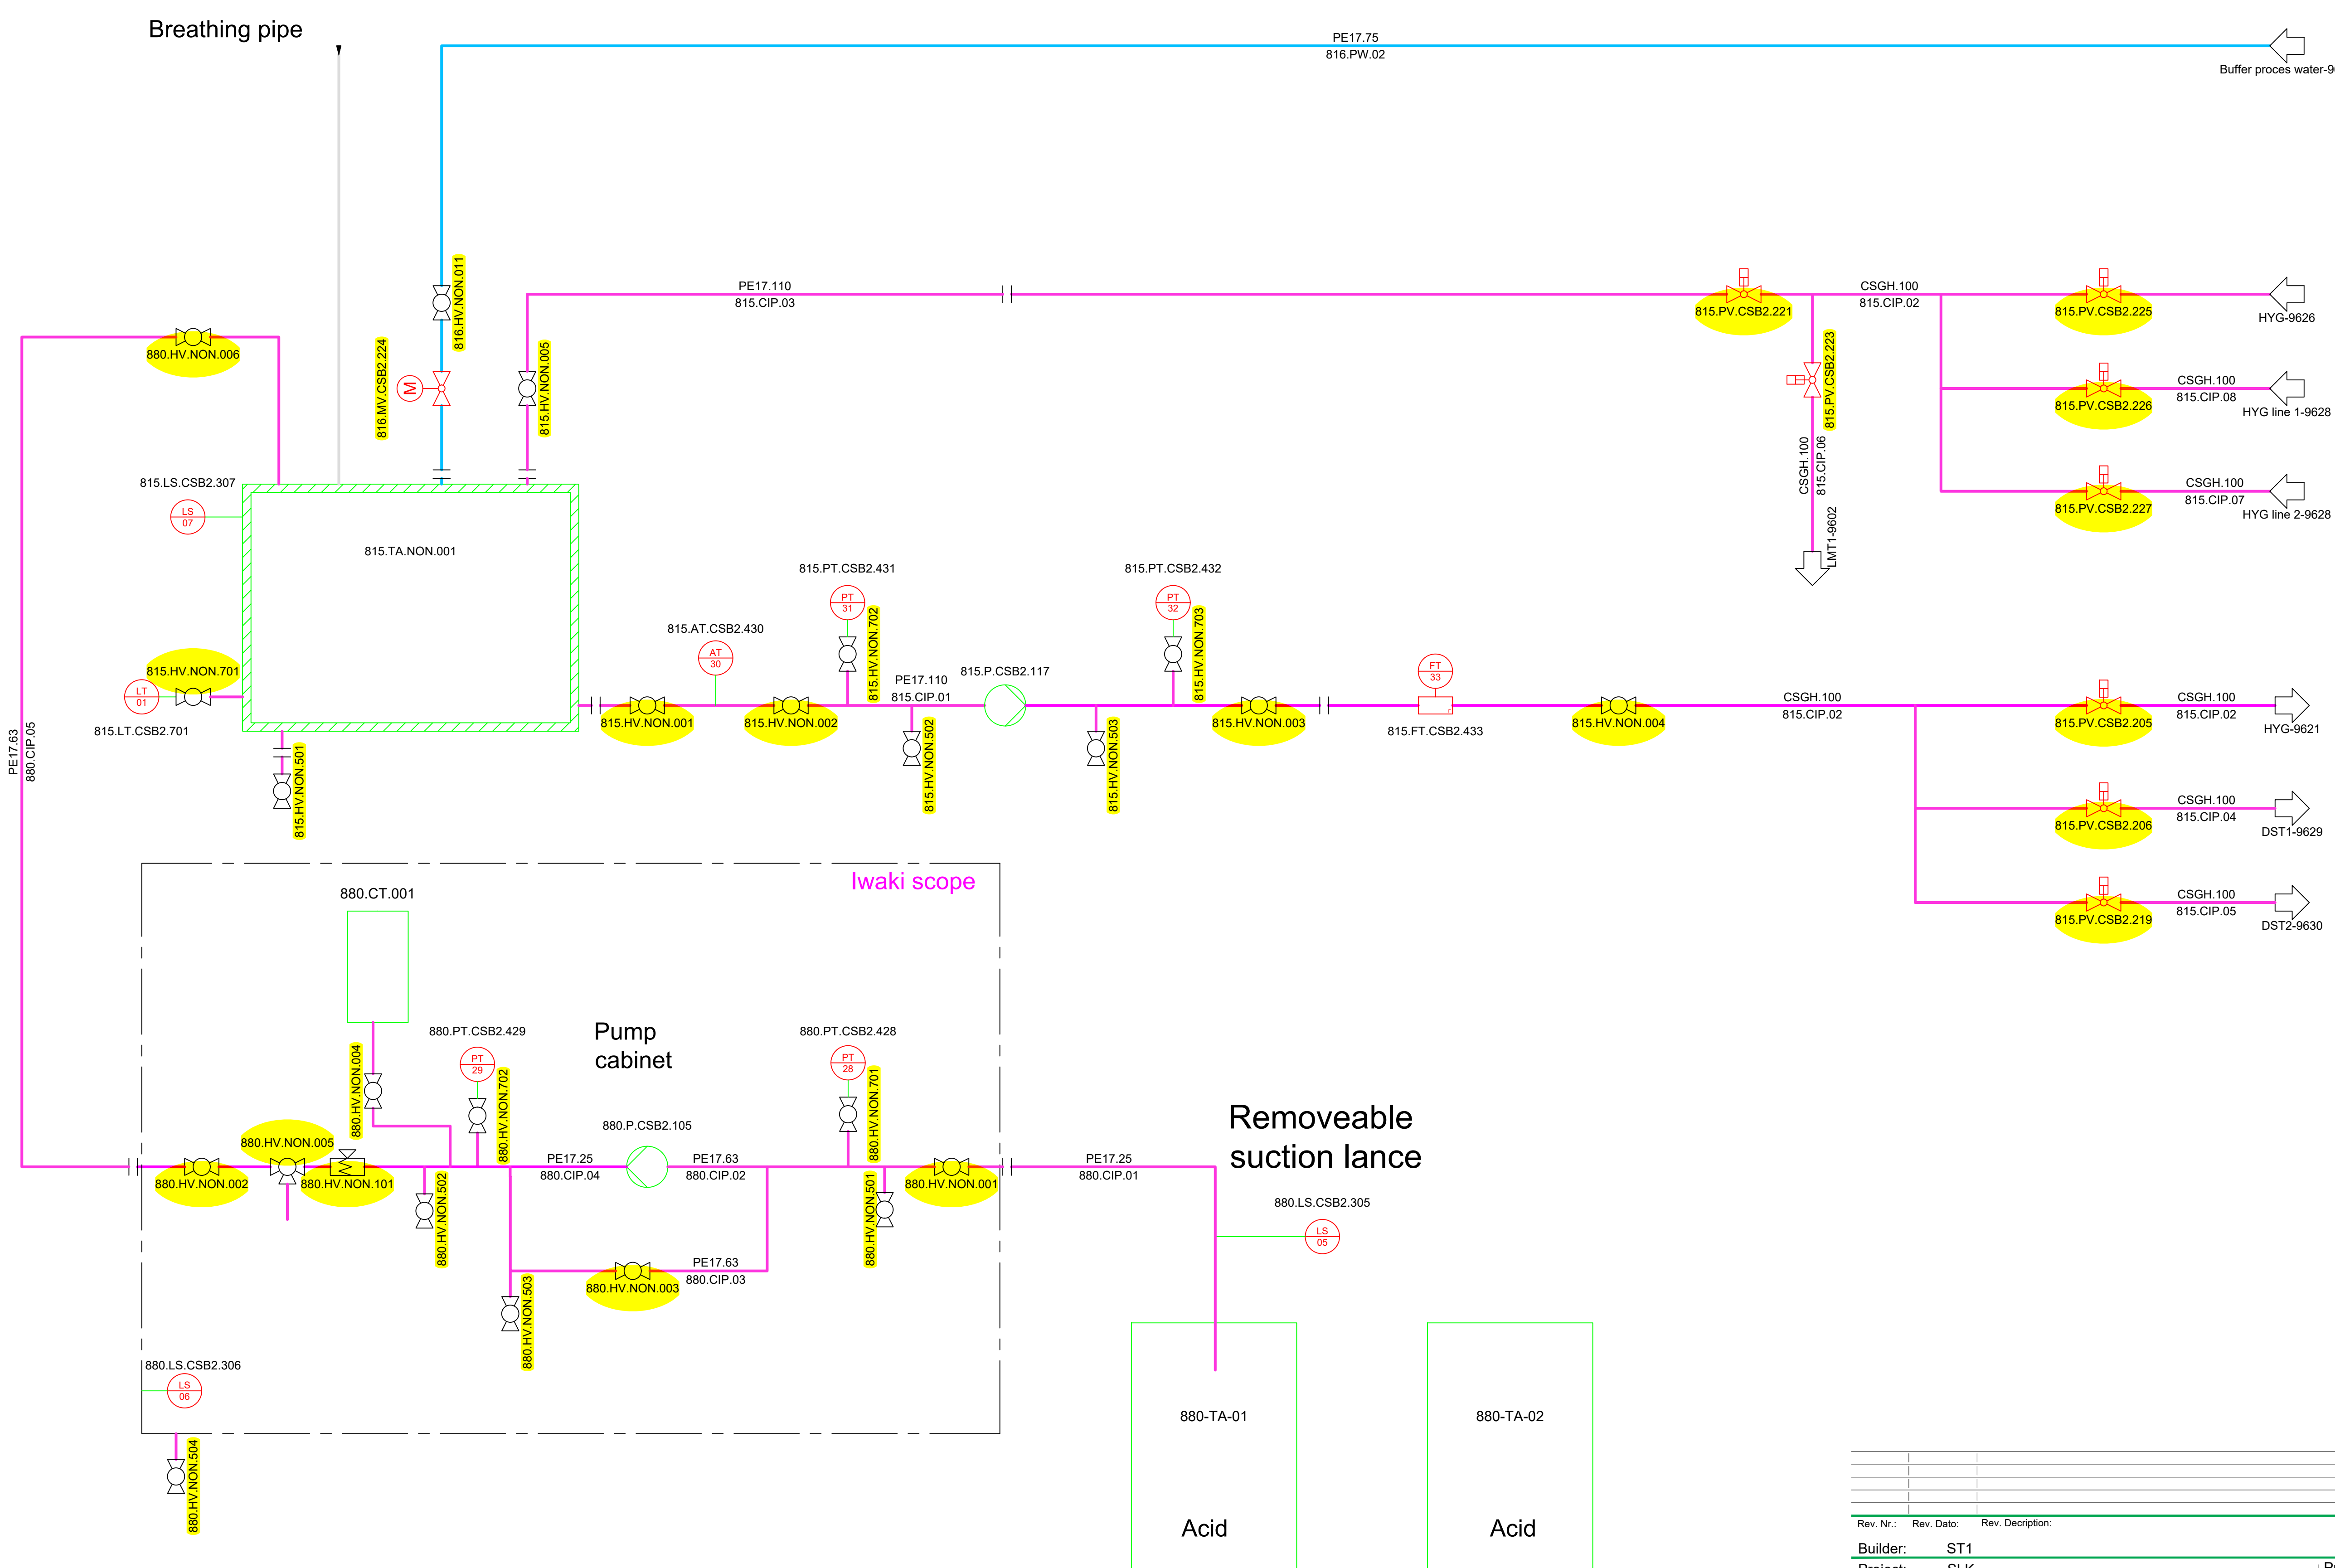


Rev. Nr.:	Rev. Dato:	Rev. Description:
Builder:	ST1	
Project:	SLK	
Subject:	CIP facility	
Rev. 6		
Int.:MDC	QC.CM	APP.:
Date:	15-10-2025	
LUNDSBY RENEWABLE SOLUTIONS		
Lundsby Renewable Solutions A/S, Hjarbrækvej 65, 8831 Lægstrup Tlf.: +45 96 49 43 00 info@lundsby.dk This Drawing is subject to copyright and may not be reproduced without permission from Lundsby Renewable Solutions A/S		
Project nr.:1768 Drawing nr.: 9651		FORMAT: A1


Pumphouse 1

~~JA Trykluft scope~~





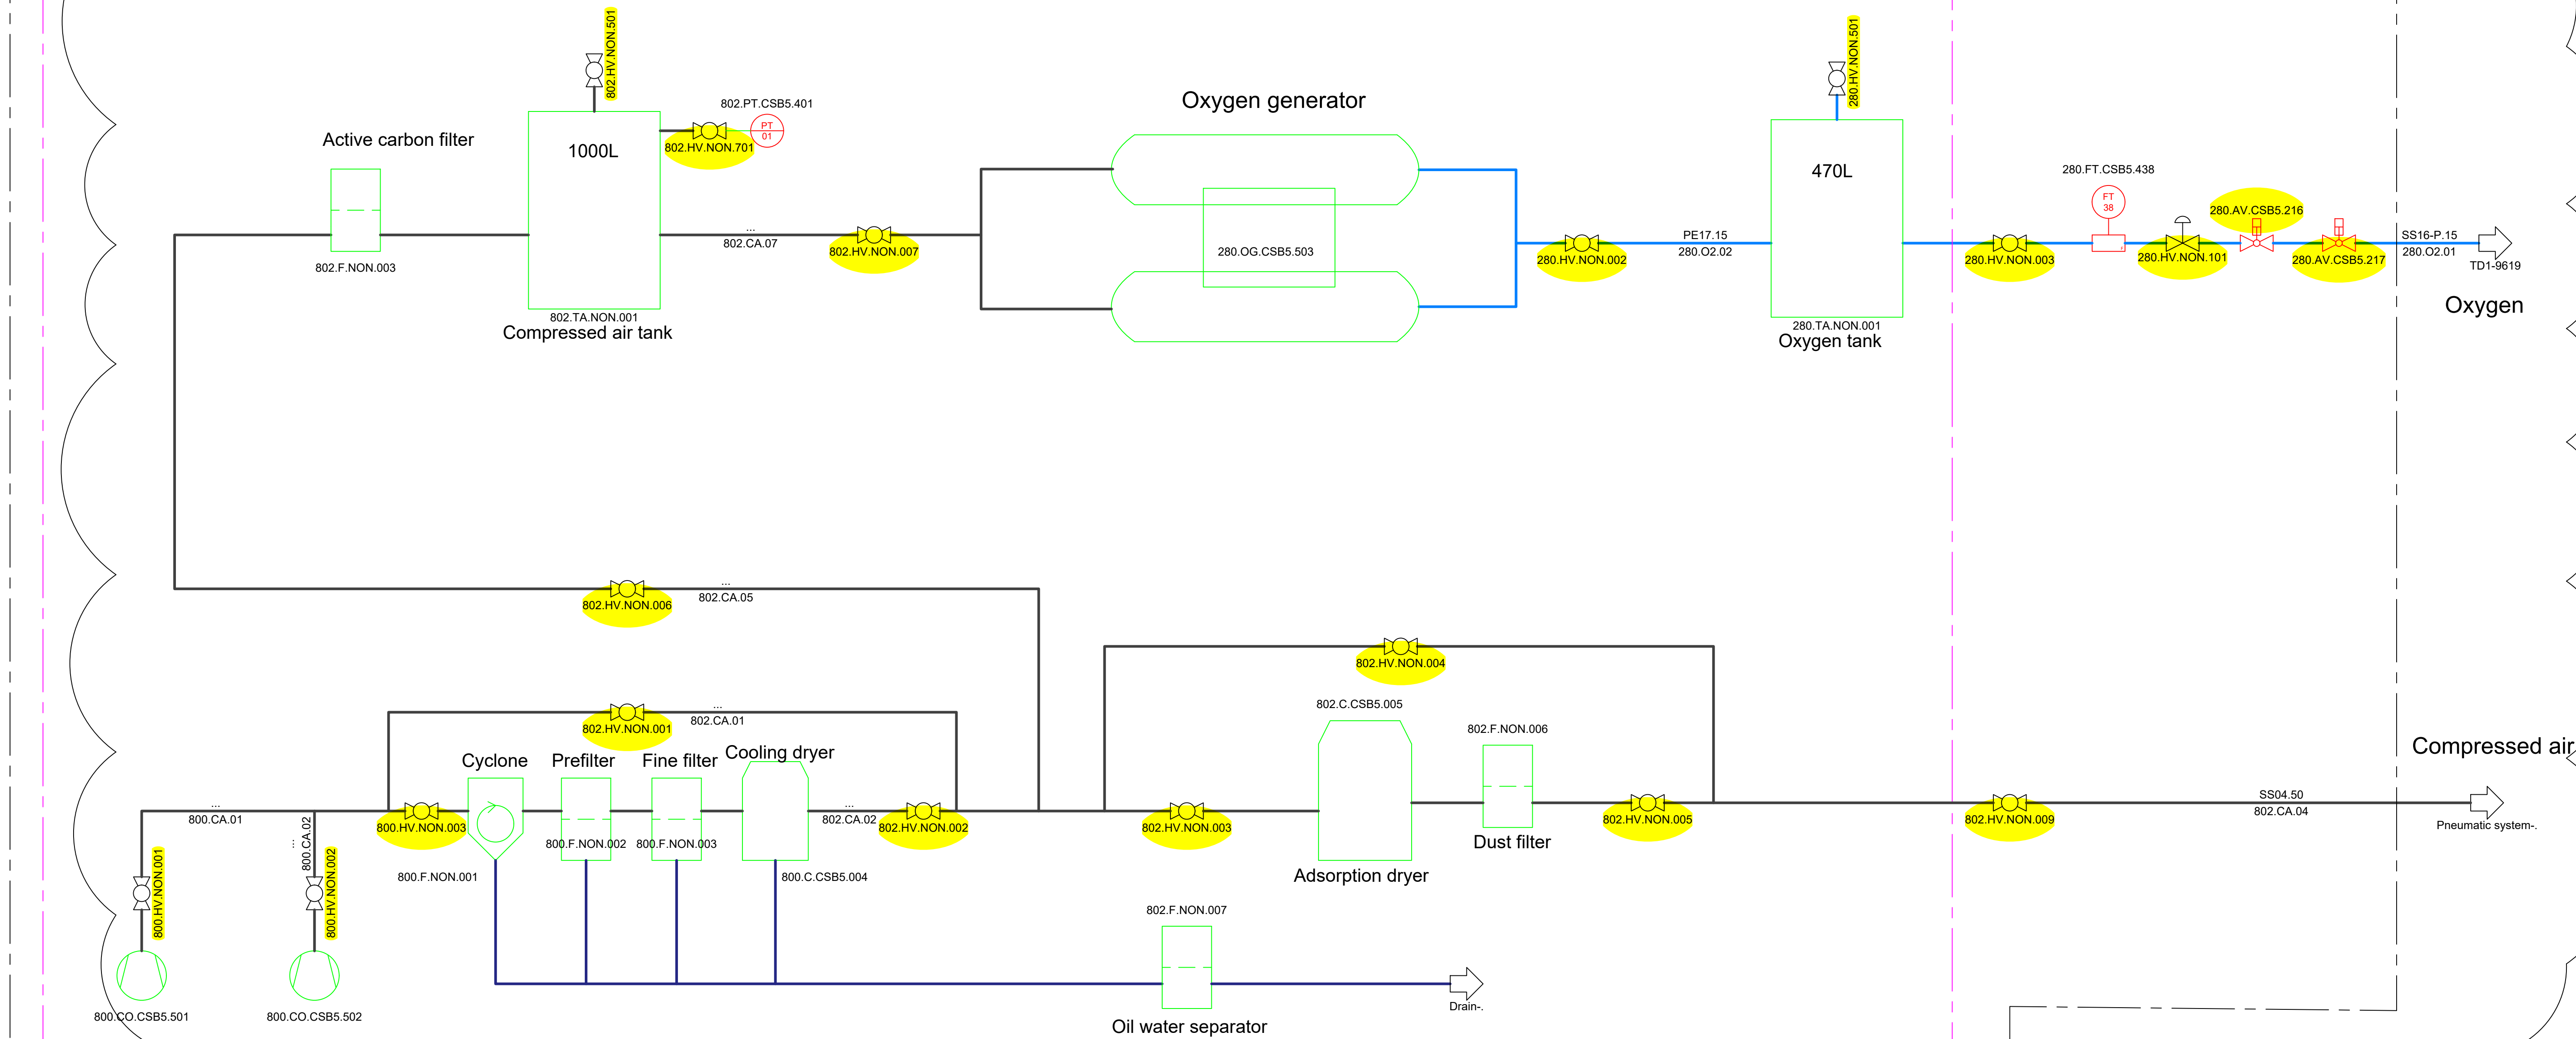
[illegible]

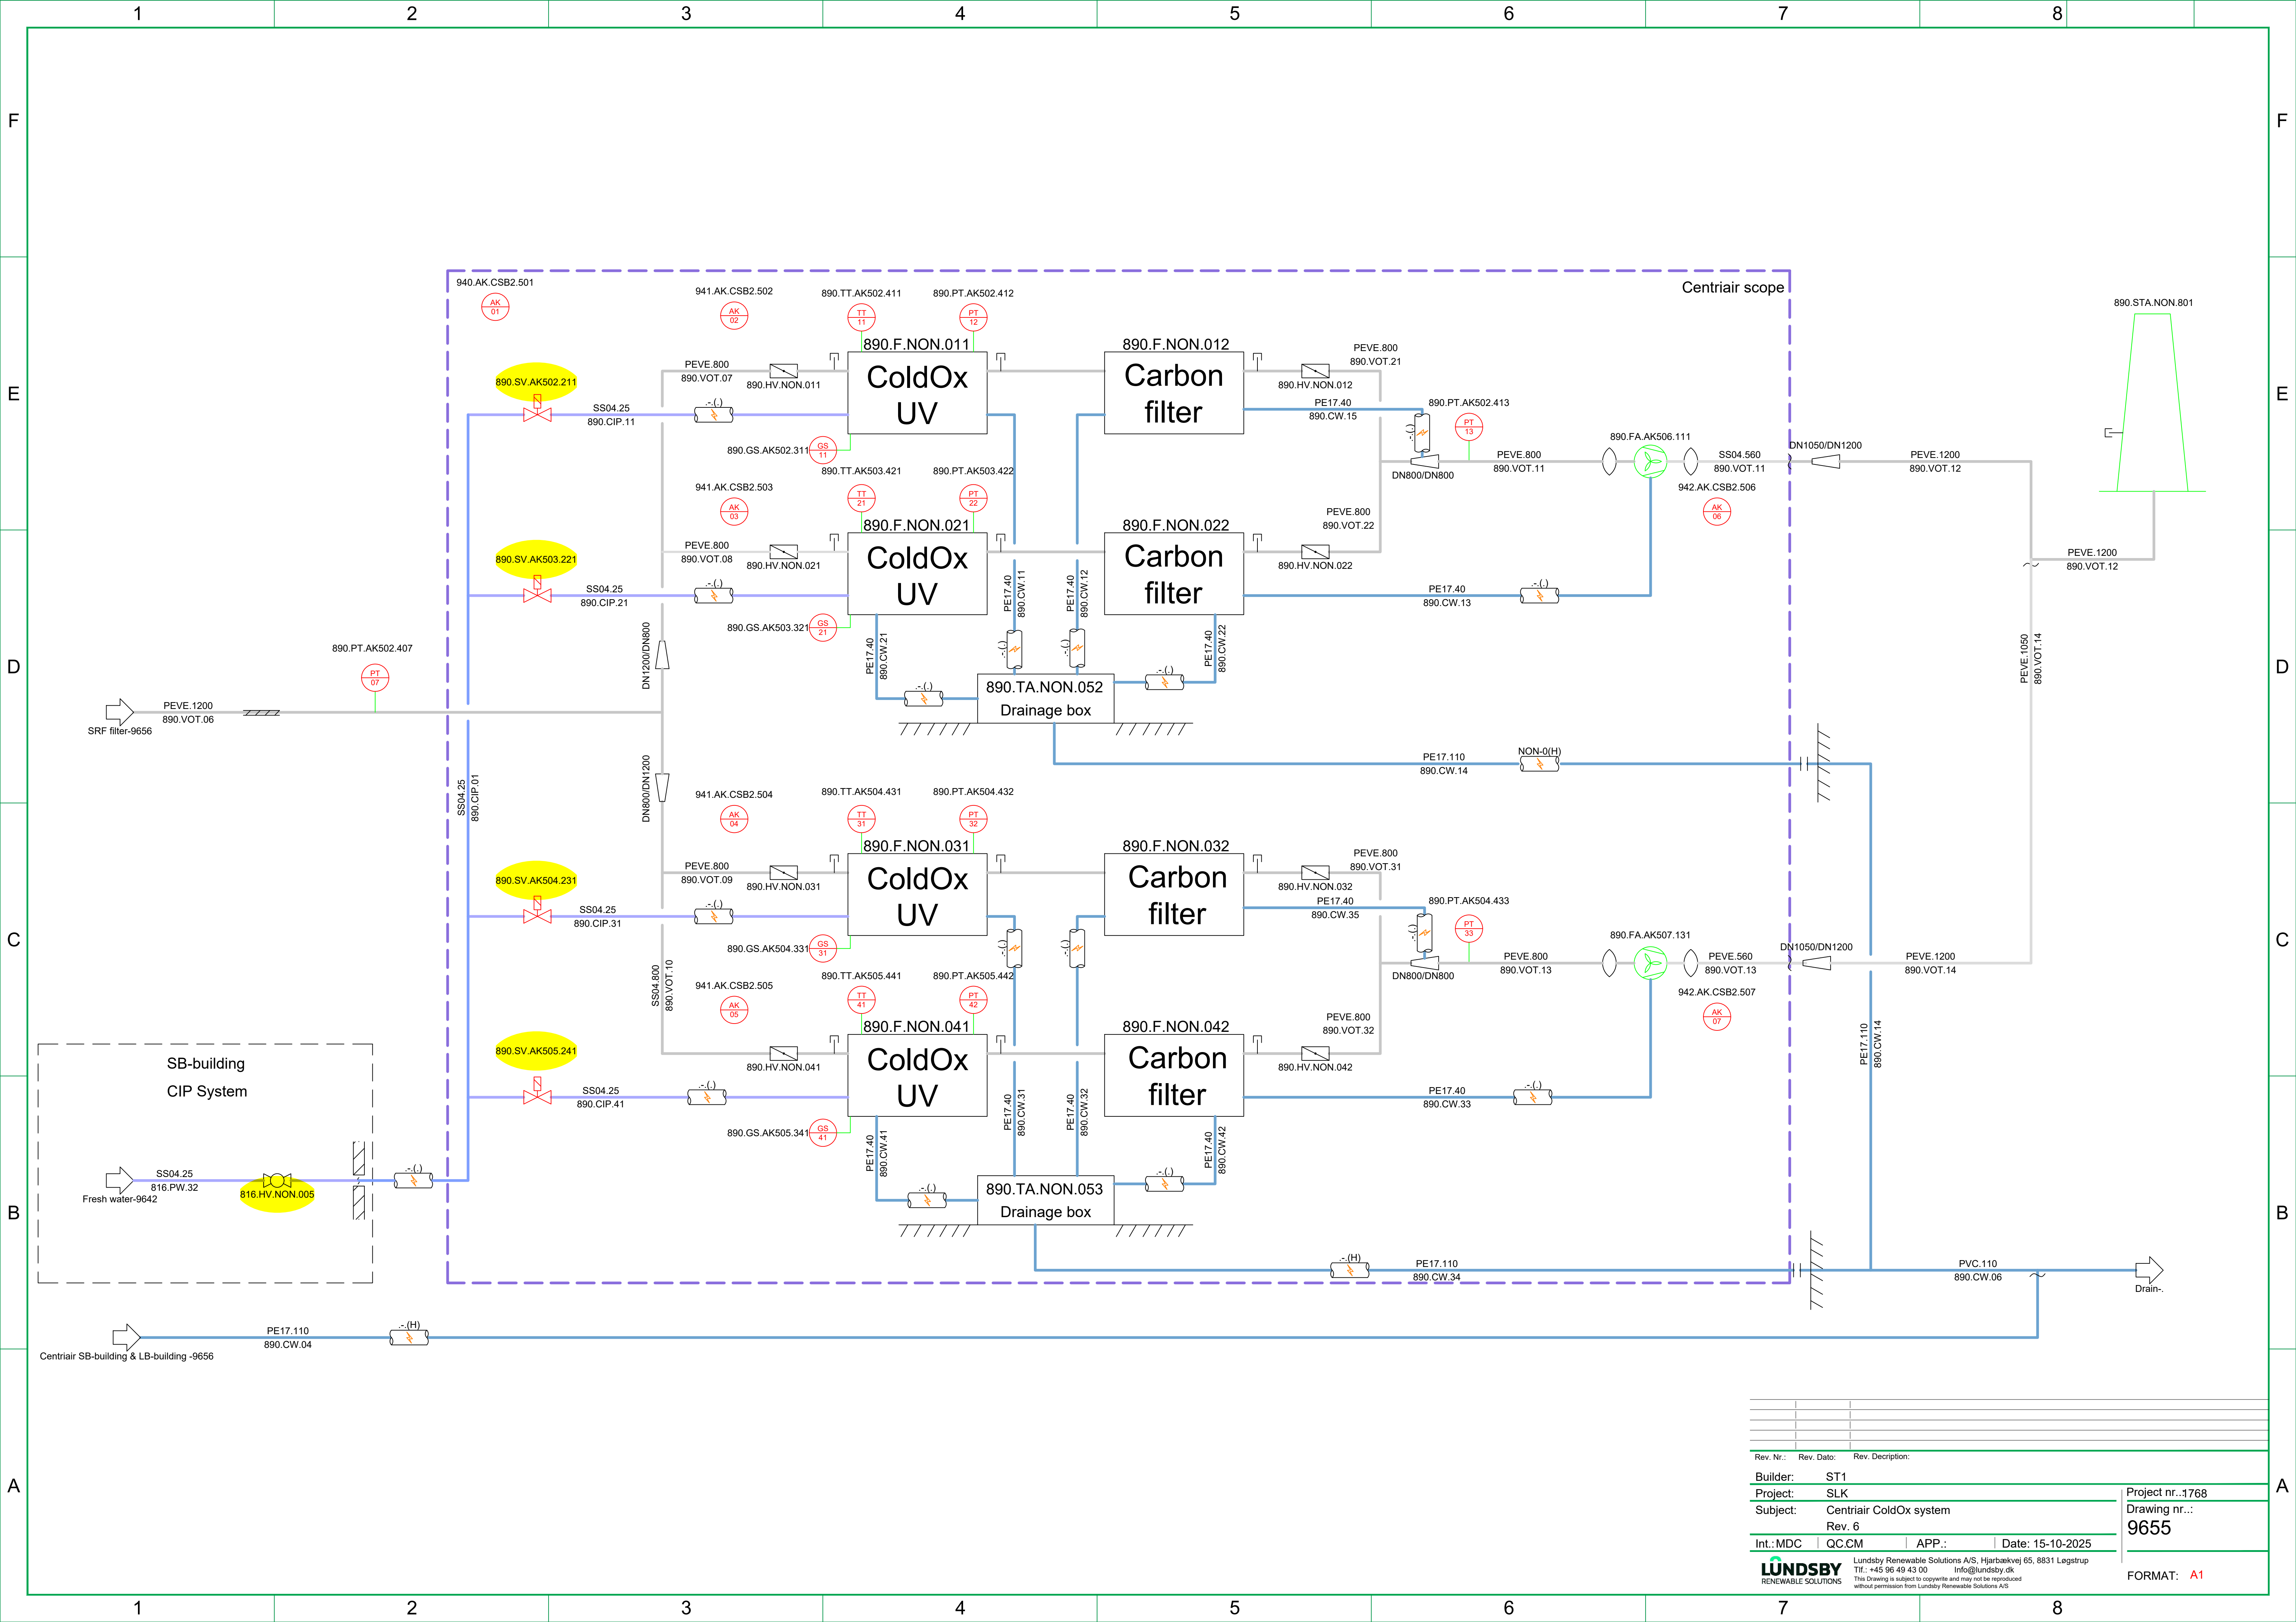

LB-building

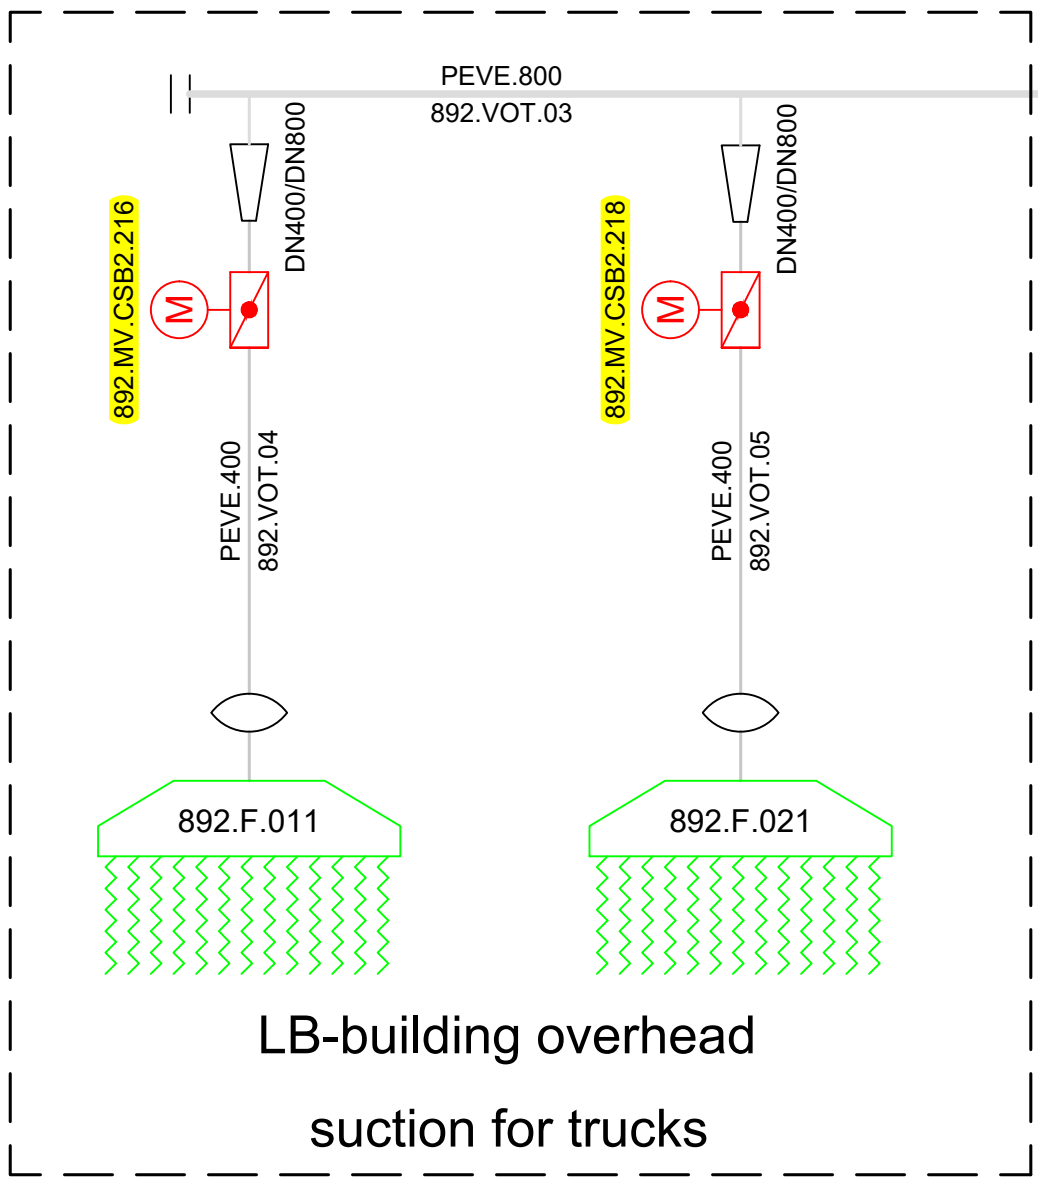

Centriair scope

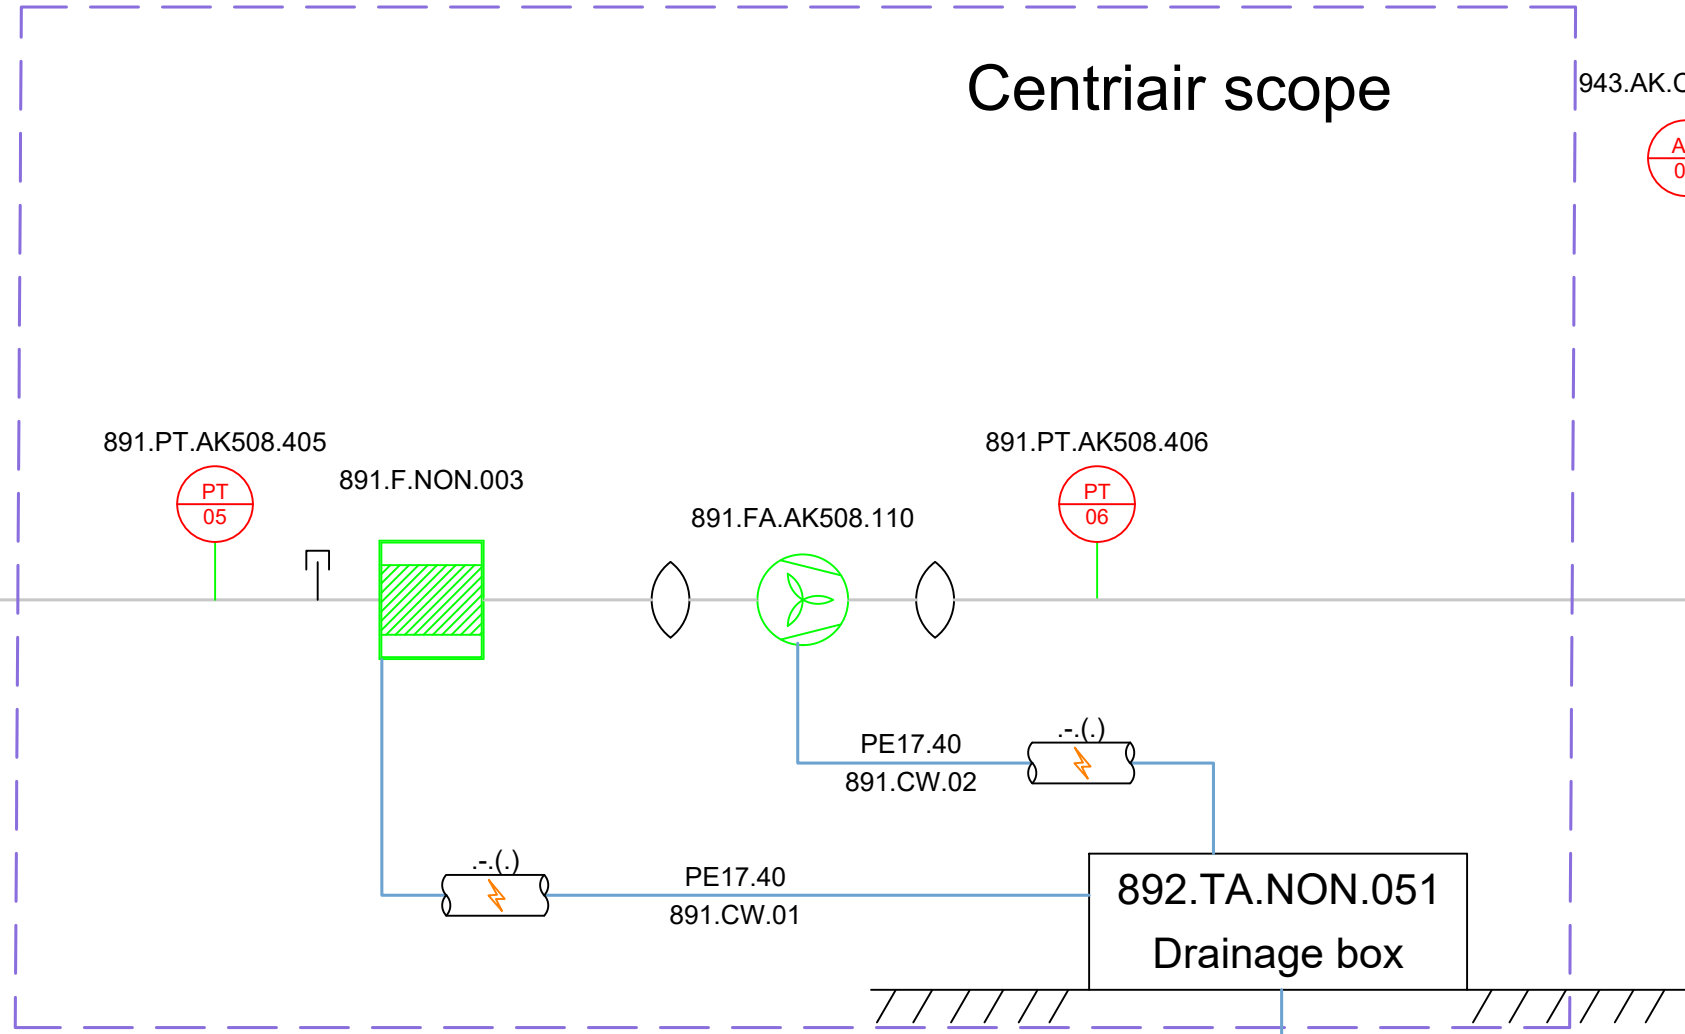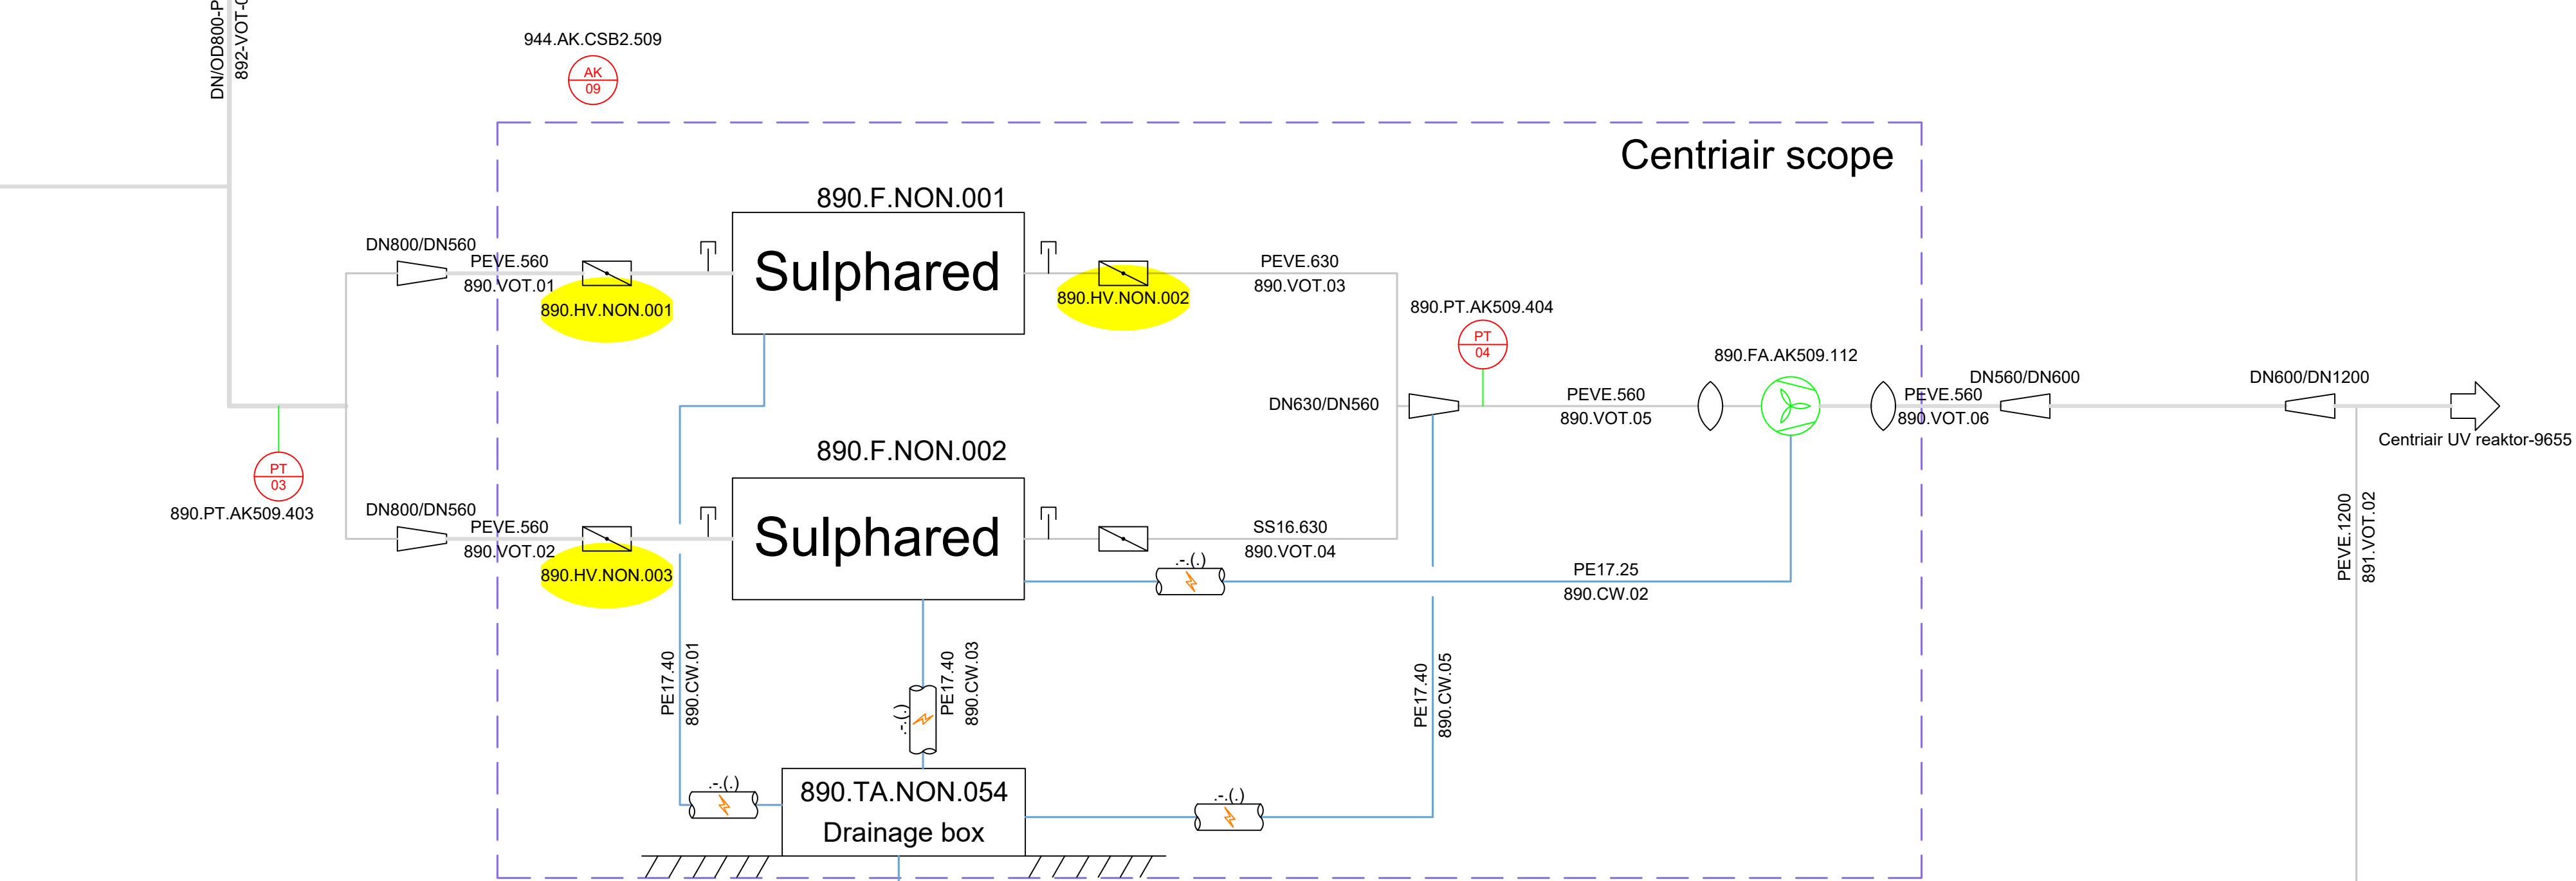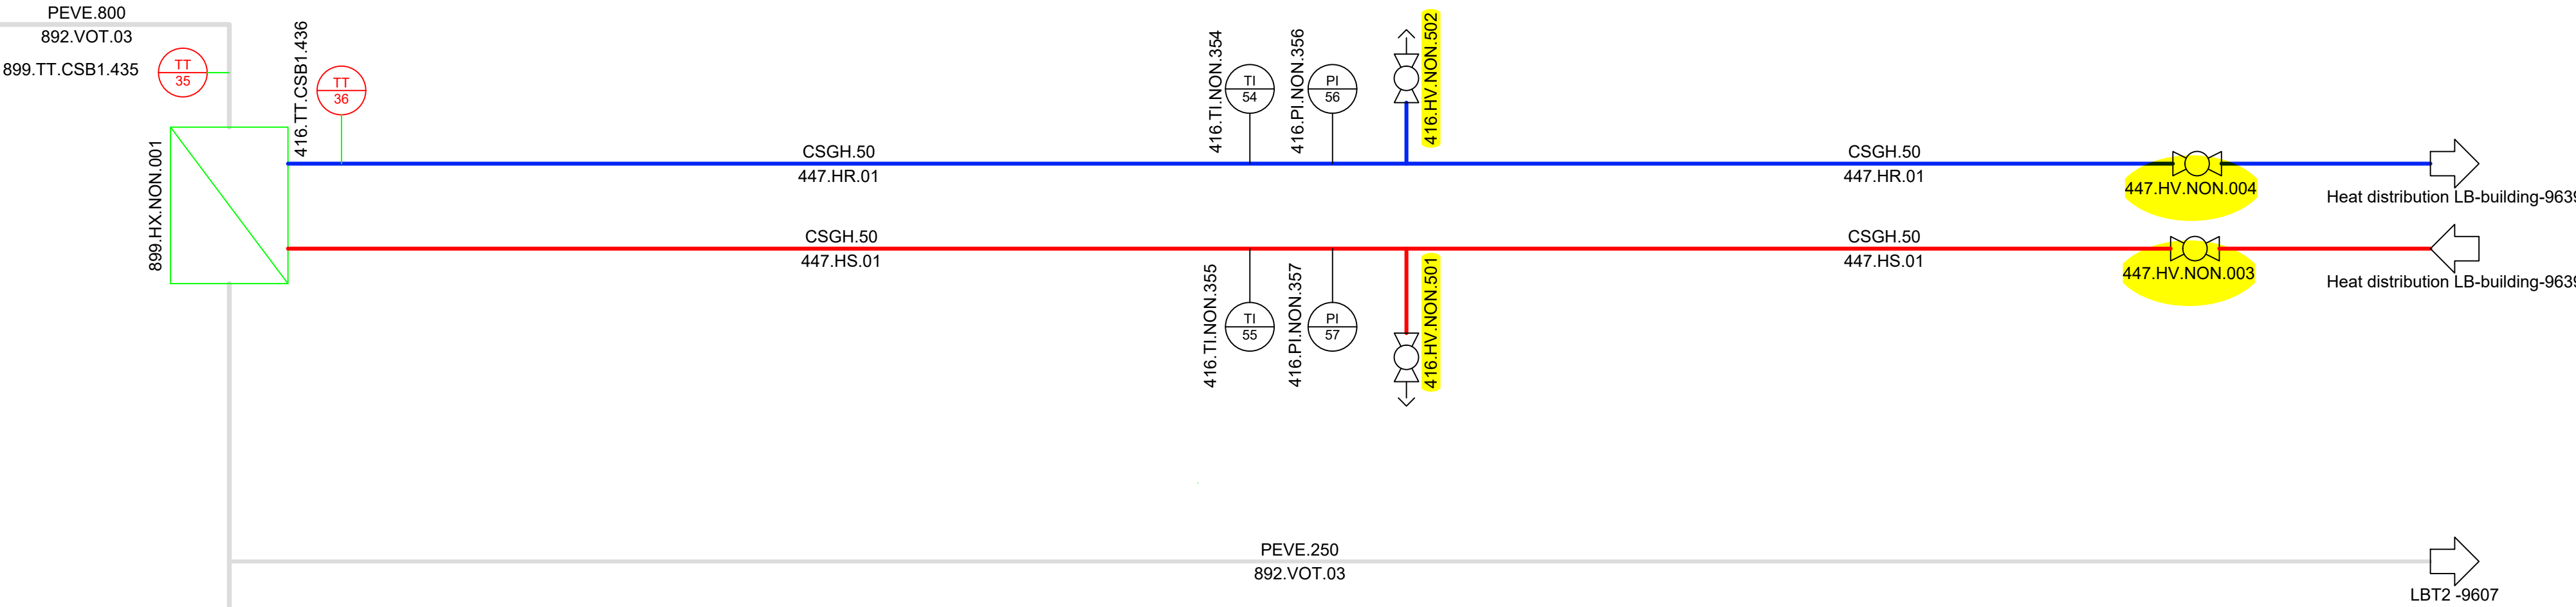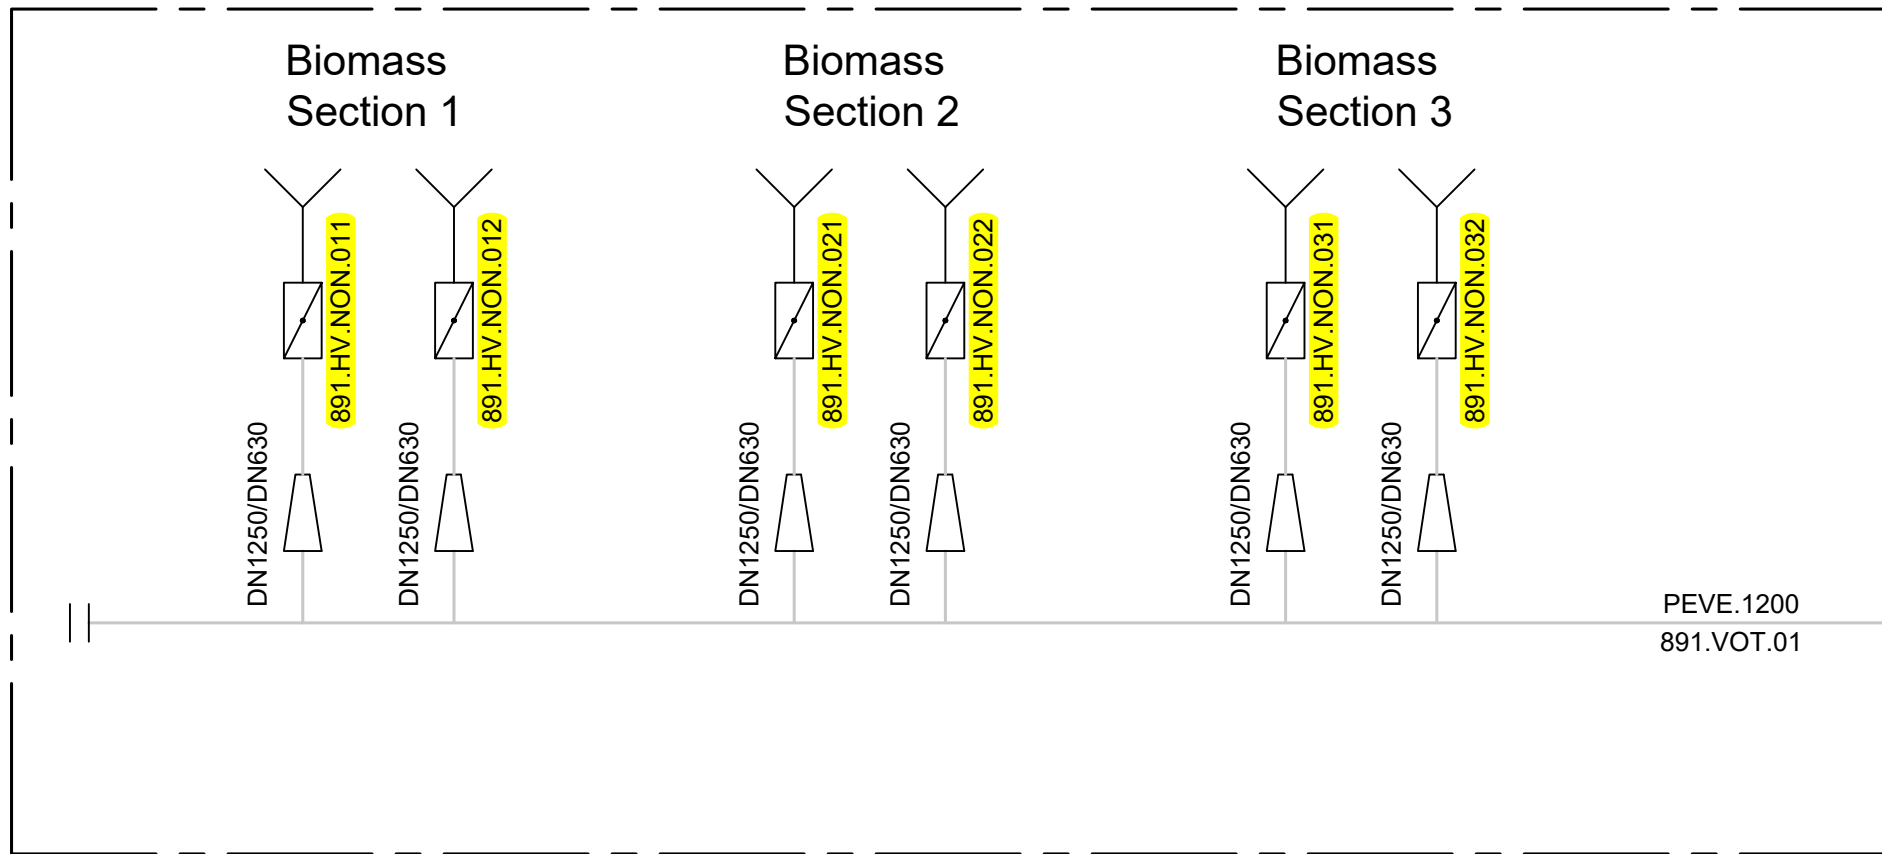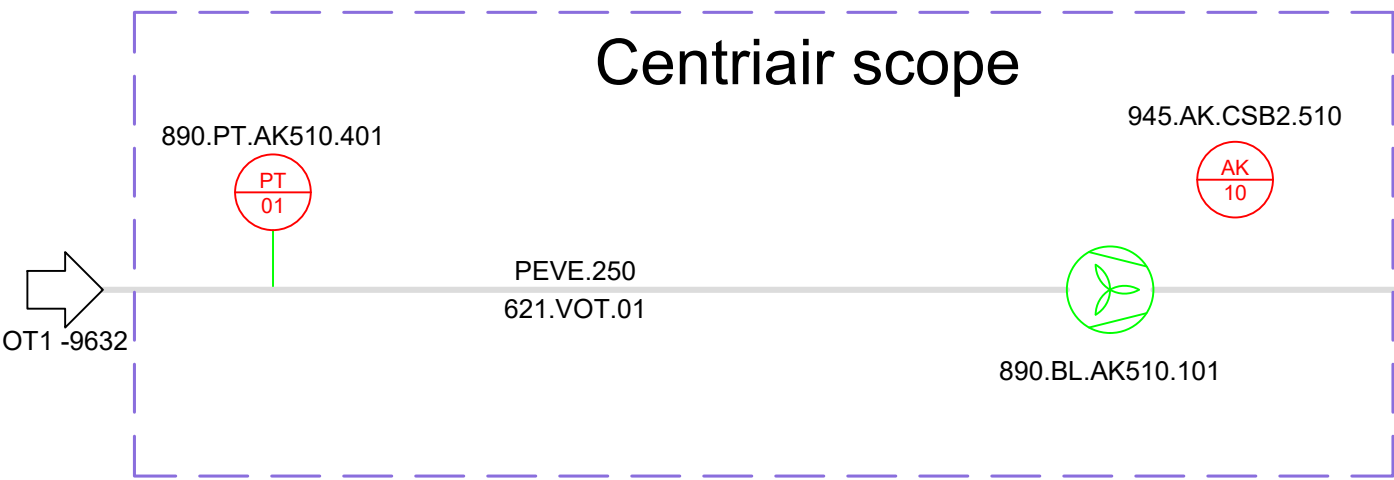

Rev. Nr.:	Rev. Dato:	Rev. Description:
Builder:	ST1	
Project:	SLK	
Subject:	Centriair SB-building & LB-building	
Rev. 6		
Int.:MDC	QC:CM	APP.:
Date: 15-10-2025		
LUNDSBY RENEWABLE SOLUTIONS		
Lundsby Renewable Solutions A/S, Hjarbækvej 65, 8831 Lægstrup Tlf.: +45 96 49 43 00 Info@lundsby.dk This Drawing is subject to copyright and may not be reproduced without permission from Lundsby Renewable Solutions A/S		
Project nr.:1768	Drawing nr.: 9656	FORMAT: A1

