

Structure of the tagging system

area code	Valve Instrument abbreviation	Sequence		Tank Area pasteurization tank 2
Anläggningsdel	Mottagning	Engelsk benämning Reception	Familjenummer 100-199	Komponentnummer
Gödselbrunn	Manure tank			100-109
Fetttank/tank för flytande substrat	Fat/Liquid Substrate tank			110-119
Fastinmatningsenhet	Dry Dosificator tank			120-129
FeCl-tank	FeCl tank			130-139
Glyceroltank	Glycerol tank			140-149
Spannmålssilo	Cereals silo			160-169
Vattentank	Water tank			170-179
Gasoltank	LPG tank			180-189
Betor och rotfrukter	Beets and root crops			190-191
Inmatning	Feeding in	200-299		
Gödselinmatning	Manure feeding			200-209
Fett-/flytande substratinmatning	Fat/Liquid Substrate feeding			210-219
Fastinmatning	Dry Dosificator			220-229
FeCL-inmatning	FeCl feeding			230-239
Glycerolinmatning	Glycerol feeding			240-249
Hygienisering på inmatningen	Pasteurization before digester			250
Spannmålsinmatning	Cereal feeding			260
Vatteninmatning	Water feeding			270
Syrgas/luft-dosering	Oxygen/air dozing			280
Blandningstank för inmatning	Mixing tank			290
rötkammare	Digester	300-399		
Rötkammare 1	Digester 1			301
Rötkammare 2	Digester 2			302
Rötkammare med "parallella linjer"	Linje X			3X0
Värmesystem	Heating system	400-499		
Värmesystem	Heating system			400-449
Kylsystem	Cooling system			450-459
Utmatning	Feeding out	500-599		
Pump	Pump			500 - 509
Hygienisering på utmatningen	Pasteurization after digester			550
Utlastning	Biofertilizer tank	600-699		
Brunn 1	Biofertilizer tank 1			601
Brunn 2	Biofertilizer tank 2			602
Separering	Separation			610 - 619
Gasbehandling	Gas treatment	700-799		
Fläktar, ventiler mm på allmän gasledning	Components on general gas pipe			700
Kondensbrunn 1	Condensate pit			710
Fackla	Flare			720
Uppgrad/CHP/panna	Upgrading unit/CHP/boiler			730
Stripperlufftförbränning i panna	Stripper air combustion			740
RTO	RTO			750
Högtryckskompressorstation	High pressure compressor station			760
LNG-anläggning	LNG plant			770
Propanisering	Propane dosing			780
Hjälpssystem	Support system	800-899		
Instrument luft	Instrument air			800
Hydraulsystem	Hydraulic system			805
Vatten	Water			810
Brutet vatten	Backflow protection system			815
Värmekabel	Heat tracing cable			820
Biltvätt	Car wash			830
Byggnad/Container	Building/container			840
Pumpbrunn	Pump tank			850
Oljearskiljare	Oil separator			860
"Generella givare"	General sensors			870
Doserutrustning	Dosing equipment			880
Luktreducering/-ventilationsutrustning	Odour contro/ventilation system			890
Styr och el	Electrical and Control	900-999		
Styrskåp	Control Cabinet			900-949
Server	Server			950
Elkraft	Switchgear			990-999

Start pipe - Not linked to page

End pipe - Not linked to page

Fald/ Slope

Insulation

Heat tracing

Page connector

Pipe Spec list

Code

Stainless steel pipes 1.4301
SS04

Stainless steel pipes 1.4304
SS16

Carbon steel P235TR1
CSTR

Carbon steel P235GH
CSGH

PE100 SDR17
PE17

PE100 SDR11
PE11

PE pipes for ventilation
PEVE

Structure of the pipeline tagging system

The pipetag consists of various information about the pipe Full pipeline tag as shown below

Size-PipeSpec-Area-Service (Medie)-Serial number

[DN/OD100 PE17 201 LM 01]

Example

Two (2) digits. Starts with 01 [01]

Two (2) to four (4) characters (letters) [LM - Liquid manure]

Three (3) digits [201 - Manure feeding in tank 1]

Pipe Spec name [PE17 - PE100 SDR17]

Pipe size DN indication for Metric pipes OD indication for PE-pipe [This example is OD 100 mm]

LMT

LBT

OT

BWT

TB

ADB

SBB

LBB

PS

PH

HYG

FLA

STA

OD

UPG

LIQ

OB

WB

TR

Liquid manure tank

Liquid biomass tank

Outlet tank

Blackwater tank

Tech building

Admin building

Solid biomass building

Liquid biomass building

Plansilo

Pump house

Hygienization tanks

Flare

Stack

Odour treatment facility

Upgrade facility

Liquifaction facility

Oil boiler

Wood boiler

Transformer

Heat Hot Supply

Cooling Supply

Cooling Return

Black Water

CIP

Process Water

Technical Water

Drinking Water

Drinking Water Hot

Condensate

Steam

Steam Condensate

Liquid Manure (Slurry)

Liquid Biomass (Substrat)

Process Biomass

Hygienized Biomass

Recirculated Biomass

Ferric Chloride FeCl

Ventilation Odour Treatment

Ventilation Fresh Air

Compressed Air

Oxygen

Raw Biogas

Return/reject Gas

Nature Gas

238,129,129

0,255,183

126,189,189

36,39,132

253,53,223

170,170,255

69,78,104

0,0,129

0,127,255

108,163,208

255,82,82

189,0,0

240,130,40

128,0,255

165,103,82

169,130,0

165,103,82

145,255,71

199,199,199

199,199,199

64,64,64

0,128,255

255,255,0

116,118,4

0,255,127

HHS

CS

CR

BW

CIP

PW

TW

DW

DWH

CW

ST

STC

LM

LB

PB

HB

RCB

FeCL

VOT

VFA

CA

O2

RB

RG

NG


N/A

The pipe tag will be shown on the P&ID as follows:


Example of line tag notation on P&ID:

Line color corresponding to table above.
The part below the pipeline is the Unique Line Tag.
Unique Line Tag is generated automatically when creating complete Line Tag.
Unique Line Tag is used by the P3D system when designing pipes


1	2	3	4	5	6	7	8	
Valves			Equipment			Piping		Instruments	
Hand valves			Pumps / Compressors / Blowers			Piping symbols		Description	
Symbols	Code	Description	Symbols	Code	Description	Symbols	Code	Description	
	HV	General valve		P	Pump (General)		N/A	Offpage connector	Instruments will be tagged XXX - XX - XX Main area code Letter code Numeric sequence XX First letter XX Succeeding letter XX Numeric sequence	
	HV	Ball valve		P	Positive displacement pump		N/A	Flange connection	
	HV	Butterfly valve		P	Helical rotor pump		N/A	Blind flange	
	HV	Globe valve		P	Centrifugal pump		NO	Truck nozzle	Description Field instrument Instrument with connection to control Example TI 01 Temperature indication LS 02 Level switch	
	HV	Three way valve		P	Peristaltic pump		NO	Funnel/Drain	
	HV	Ground covered valve		MC	Rotacut		AS	Expansion joint	
	BV	Balancing valve		MC	Disruptor		SN	Strainer	Instruments with succeeding letter T is an analog signal. Instruments with succeeding letter S is a digital signal. <table><tr><th>Givartyper</th><th>Engelsk översättning</th><th>Förkortning</th></tr><tr><td>Analysindikator</td><td>analyze indicator</td><td>AI</td></tr><tr><td>Analysgivare</td><td>Analyse transmitter</td><td>AT</td></tr><tr><td>Energimätare</td><td>Energi transmitter</td><td>ET</td></tr><tr><td>Flödesgivare</td><td>Flow indicator</td><td>FI</td></tr><tr><td>Flödesgivare</td><td>Flow transmitter</td><td>FT</td></tr><tr><td>Flödesvakt</td><td>Flow switch</td><td>FS</td></tr><tr><td>Flödesgivare</td><td>Flow transmitter</td><td>FT</td></tr><tr><td>Generell vakt</td><td>General Switch</td><td>GS</td></tr><tr><td>Nivåvakt</td><td>Level Switch</td><td>LS</td></tr><tr><td>Nivåindikator</td><td>Level indicator</td><td>LI</td></tr><tr><td>Nivågivare</td><td>Level Transmitter</td><td>LT</td></tr><tr><td>Tryckindikator/manometer</td><td>Pressure indicator</td><td>PI</td></tr><tr><td>Tryckvakt</td><td>Pressure switch</td><td>PS</td></tr><tr><td>Tryckgivare</td><td>Pressure transmitter</td><td>PT</td></tr><tr><td>Temperaturindikator</td><td>Thermometer</td><td>TI</td></tr><tr><td>Temperaturgivare</td><td>Temperature transmitter</td><td>TT</td></tr><tr><td>Viktgivare</td><td>Weight transmitter</td><td>WT</td></tr></table>	Givartyper	Engelsk översättning	Förkortning	Analysindikator	analyze indicator	AI	Analysgivare	Analyse transmitter	AT	Energimätare	Energi transmitter	ET	Flödesgivare	Flow indicator	FI	Flödesgivare	Flow transmitter	FT	Flödesvakt	Flow switch	FS	Flödesgivare	Flow transmitter	FT	Generell vakt	General Switch	GS	Nivåvakt	Level Switch	LS	Nivåindikator	Level indicator	LI	Nivågivare	Level Transmitter	LT	Tryckindikator/manometer	Pressure indicator	PI	Tryckvakt	Pressure switch	PS	Tryckgivare	Pressure transmitter	PT	Temperaturindikator	Thermometer	TI	Temperaturgivare	Temperature transmitter	TT	Viktgivare	Weight transmitter	WT
Givartyper	Engelsk översättning	Förkortning	
Analysindikator	analyze indicator	AI	
Analysgivare	Analyse transmitter	AT	
Energimätare	Energi transmitter	ET	
Flödesgivare	Flow indicator	FI	
Flödesgivare	Flow transmitter	FT	
Flödesvakt	Flow switch	FS	
Flödesgivare	Flow transmitter	FT	
Generell vakt	General Switch	GS	
Nivåvakt	Level Switch	LS	
Nivåindikator	Level indicator	LI	
Nivågivare	Level Transmitter	LT	
Tryckindikator/manometer	Pressure indicator	PI	
Tryckvakt	Pressure switch	PS	
Tryckgivare	Pressure transmitter	PT	
Temperaturindikator	Thermometer	TI	
Temperaturgivare	Temperature transmitter	TT	
Viktgivare	Weight transmitter	WT	
Actuated valves / Regulating valves			Heating and Cooling			Going into the ground / Coming up from Concentric reducer Eccentric reducer Sample point Inline silencer Electrical heat tracing	
	MV/RV	Motor ball valve		HX	Heat exchanger - Shell & tube	
	MV/RV	Motor butterfly valve		HX	Heat exchanger - plate	
	AV/RV	Pneumatic ball valve		HX	Heat exchanger - double pipe	
	AV/RV	Pneumatic valve		HX	Heating coil (in tank)	
	AV	Solenoid valve		HS	Heatpump	
Safety valves			Tank equipment	
	SV	Exhaust valve covers		AG	ISO Agitator - Propeller	
	SV	Safety valve		AG	Agitator	
	SV	Breather valve		LA	Light	
Mechanical valves			Filters and Vessels	
	PV	Pressure holding valve		AT	General filter / Forfilter	
	CV	Check valve		AT	General liquid	
	VV	Venting valve		AT	Drier - General	
				F	Suction hood	
				EXP	Expansion tank	

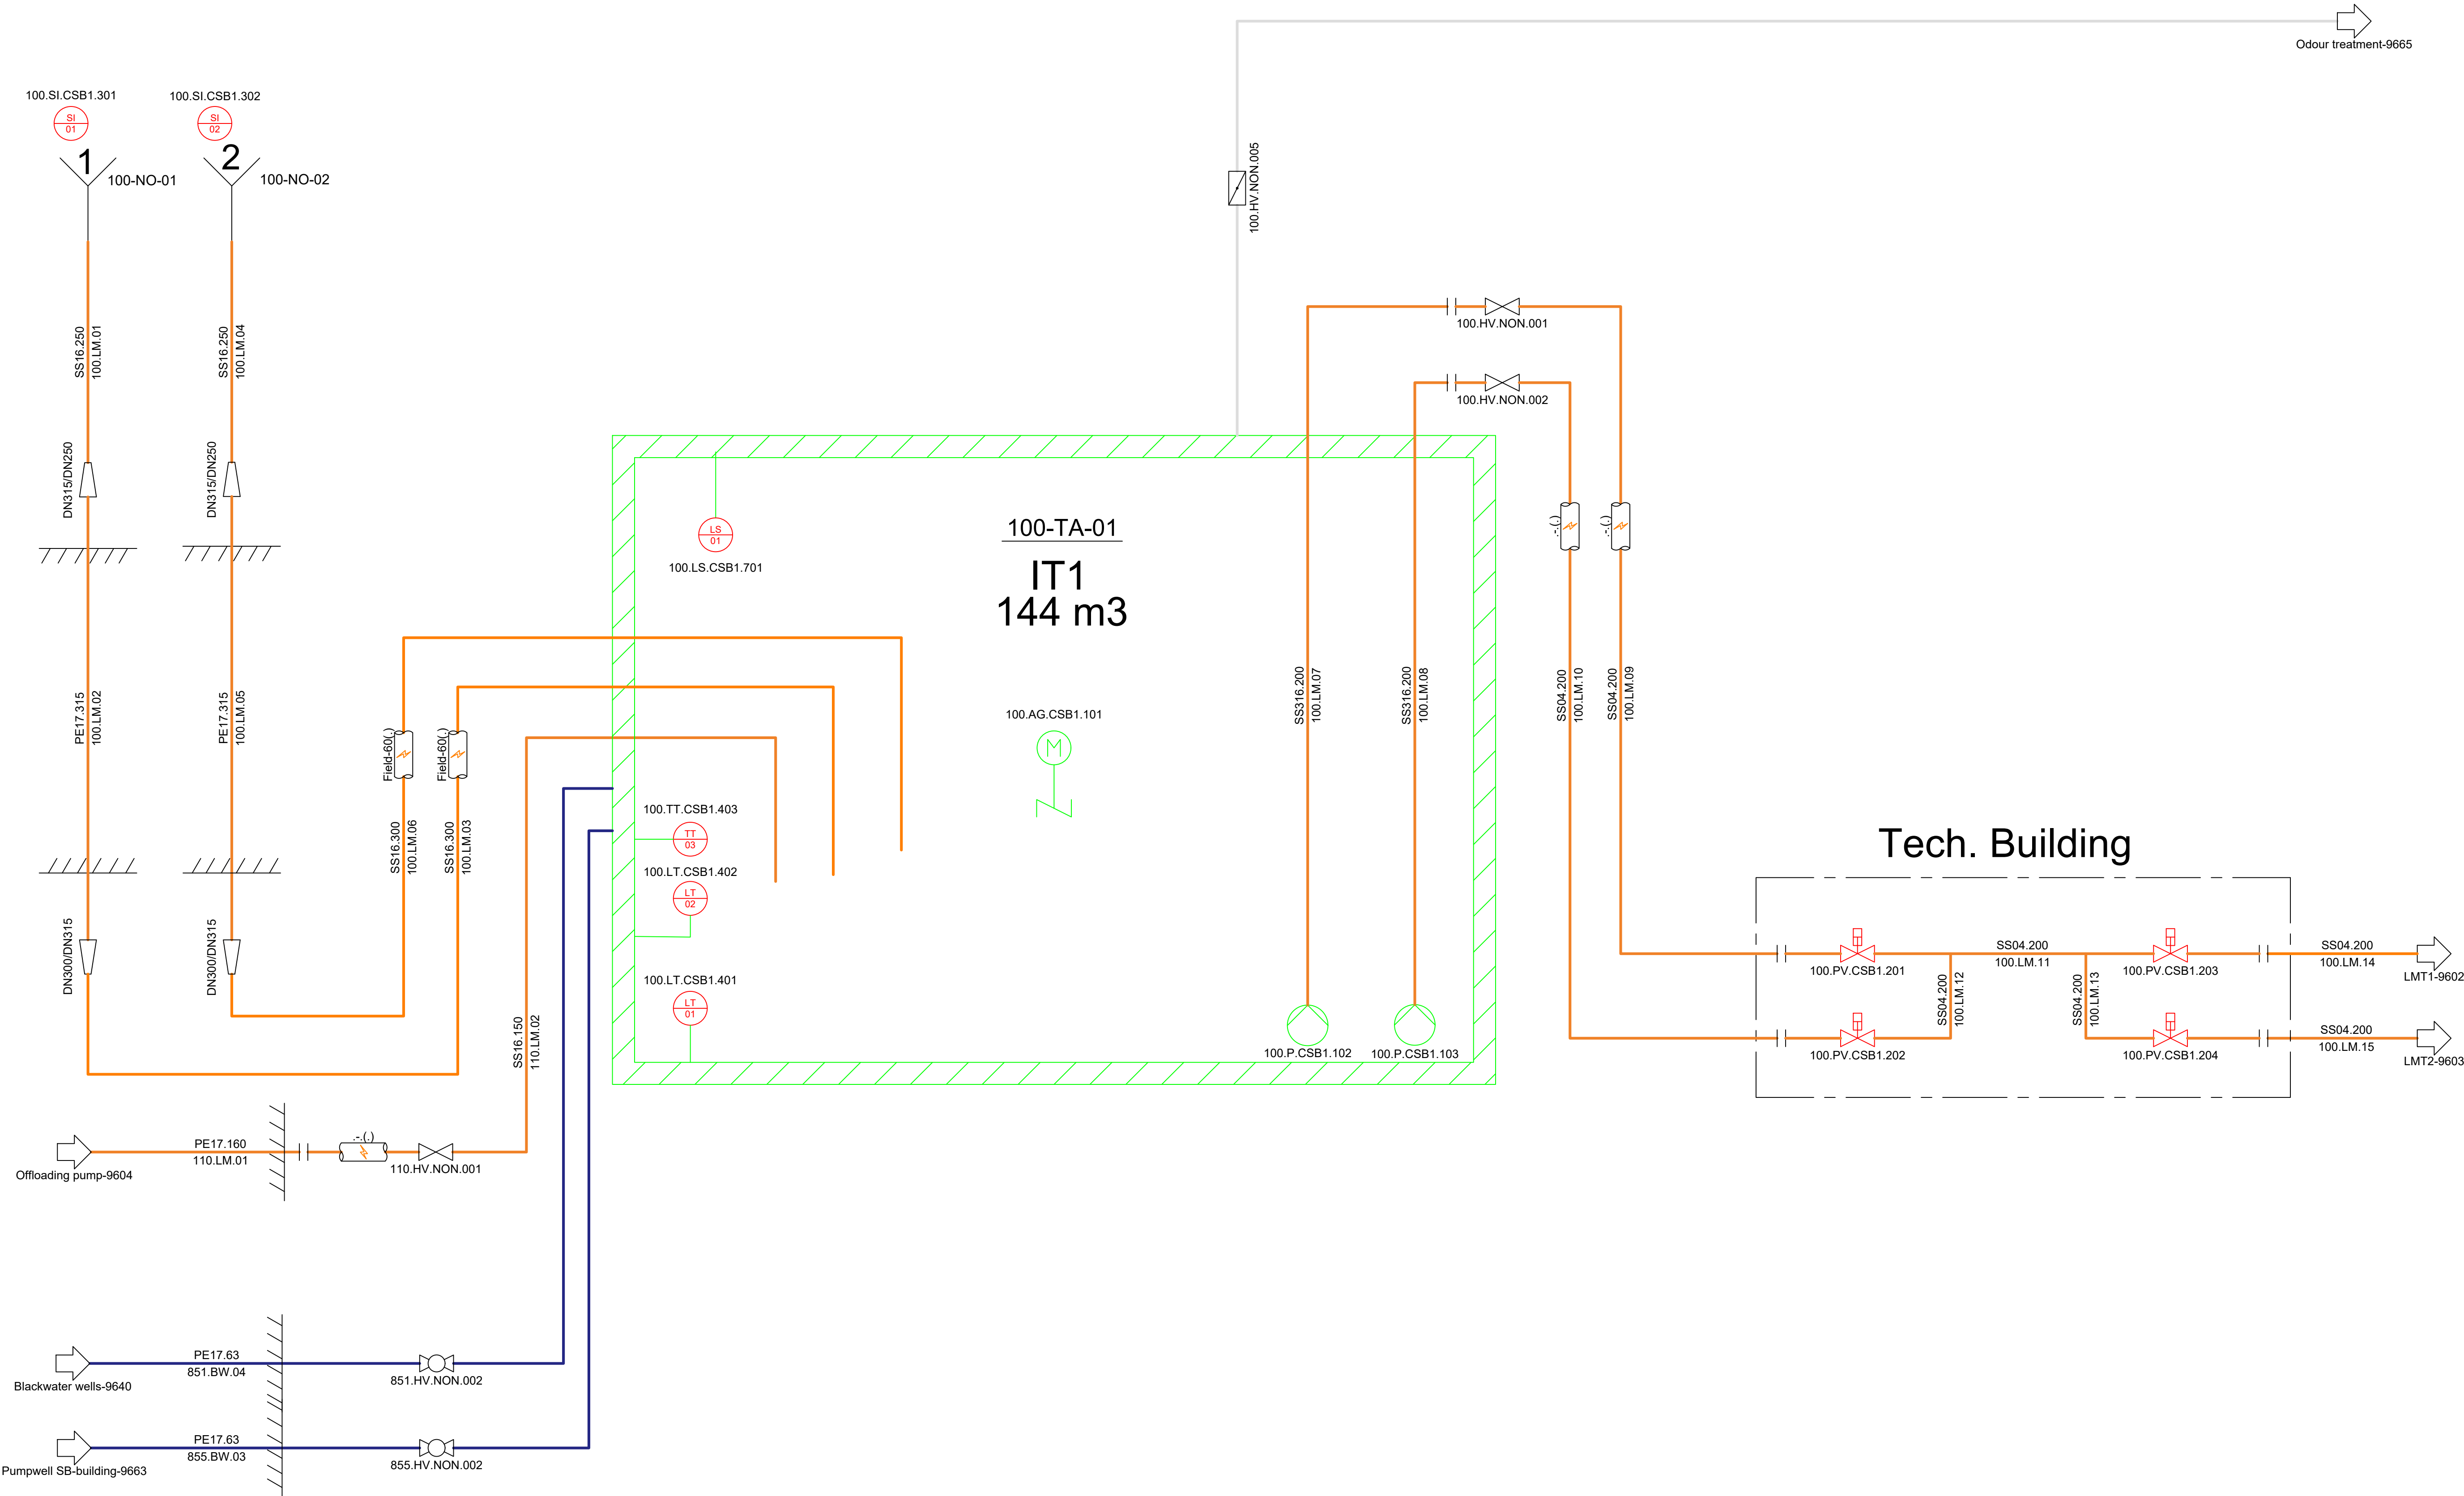


Rev. Nr.:	Rev. Dato:	Rev. Description:
Builder:	ST1	
Project:	SLK	
Subject:	Intake tank 1	
	Rev. 2	
Int.:MDC	QC:CM	APP.:
		Date: 26-06-2025
LUNDSBY RENEWABLE SOLUTIONS		
Lundsby Renewable Solutions A/S, Hjarbækvej 65, 8831 Løgstrup Tlf.: +45 96 49 43 00 Info@lundsby.dk This Drawing is subject to copyright and may not be reproduced without permission from Lundsby Renewable Solutions A/S		
Project nr.:1768 Drawing nr.: 9601		FORMAT: A1

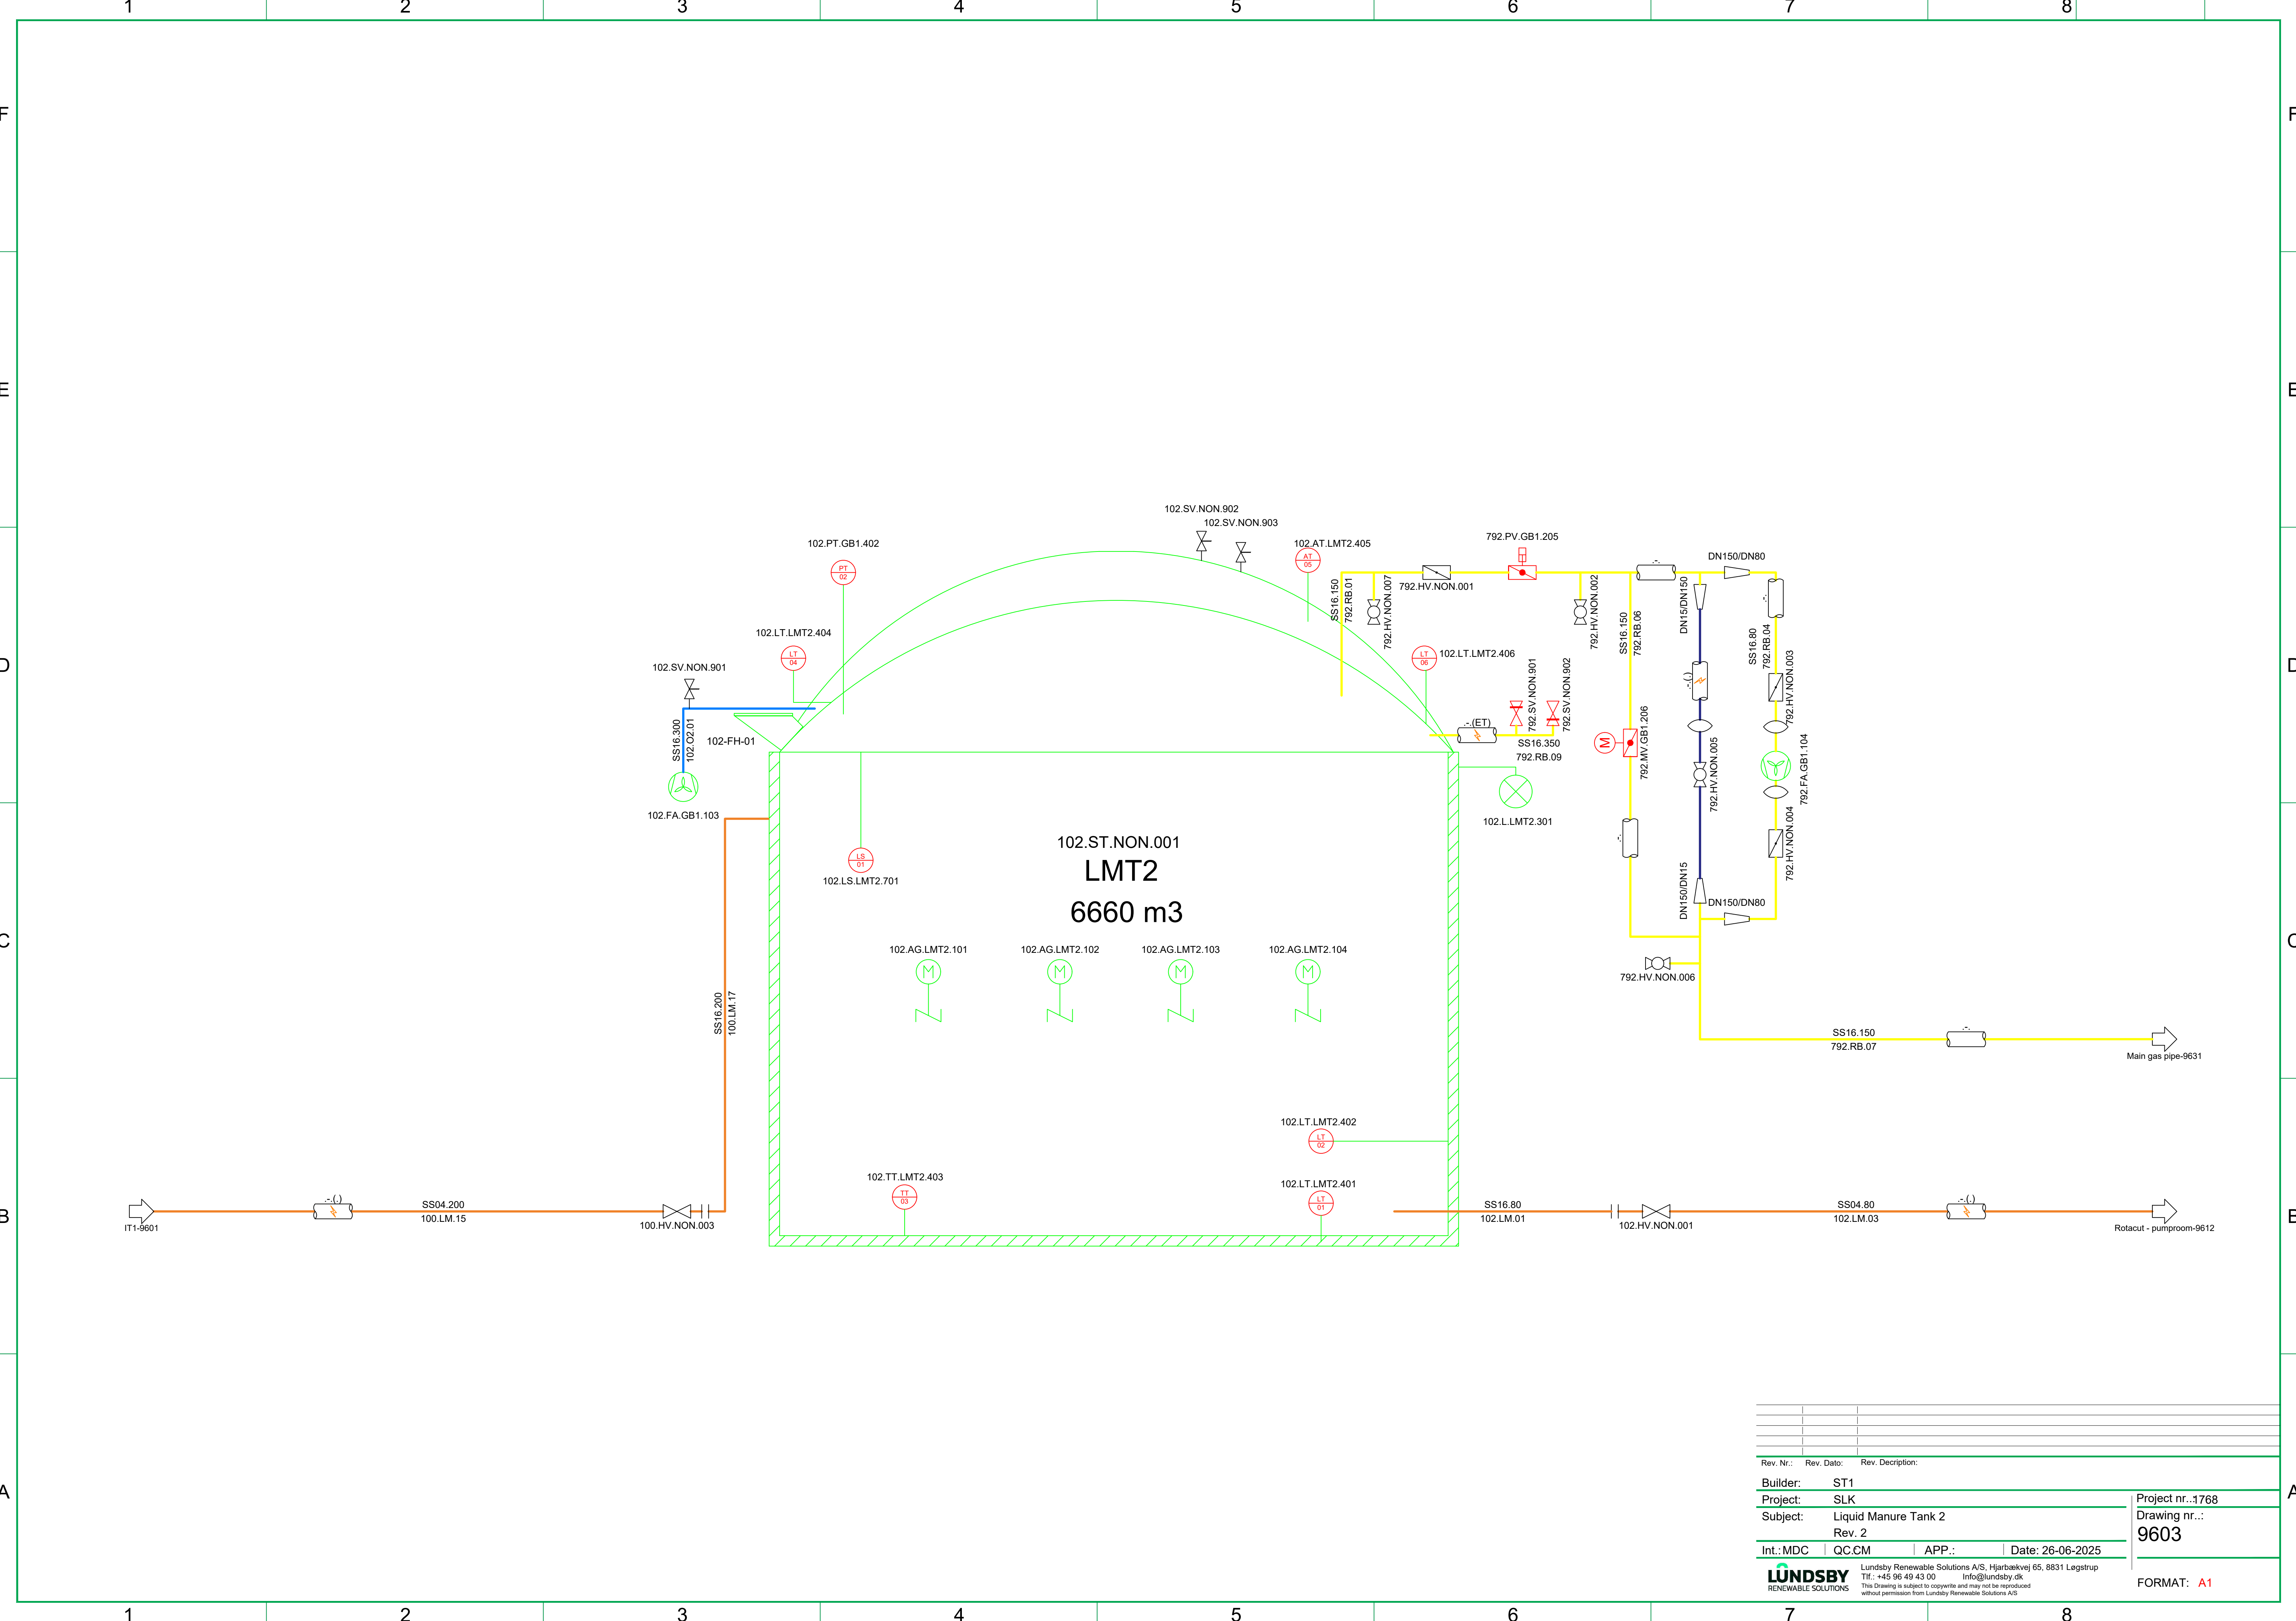


Rev. Nr.:	Rev. Dato:	Rev. Description:			
Builder:	ST1				
Project:	SLK				
Subject:	Liquid Manure Tank 2				
	Rev. 2				
Int.: MDC	QC: CM	APP.:	Date: 26-06-2025		
		Lundsby Renewable Solutions A/S, Hjarbækvej 65, 8831 Løgstrup Tlf.: +45 96 49 43 00 info@lundsby.dk This Drawing is subject to copyright and may not be reproduced without permission from Lundsby Renewable Solutions A/S			
				Project nr.:1768	
				Drawing nr.: 9603	
				FORMAT: A1	

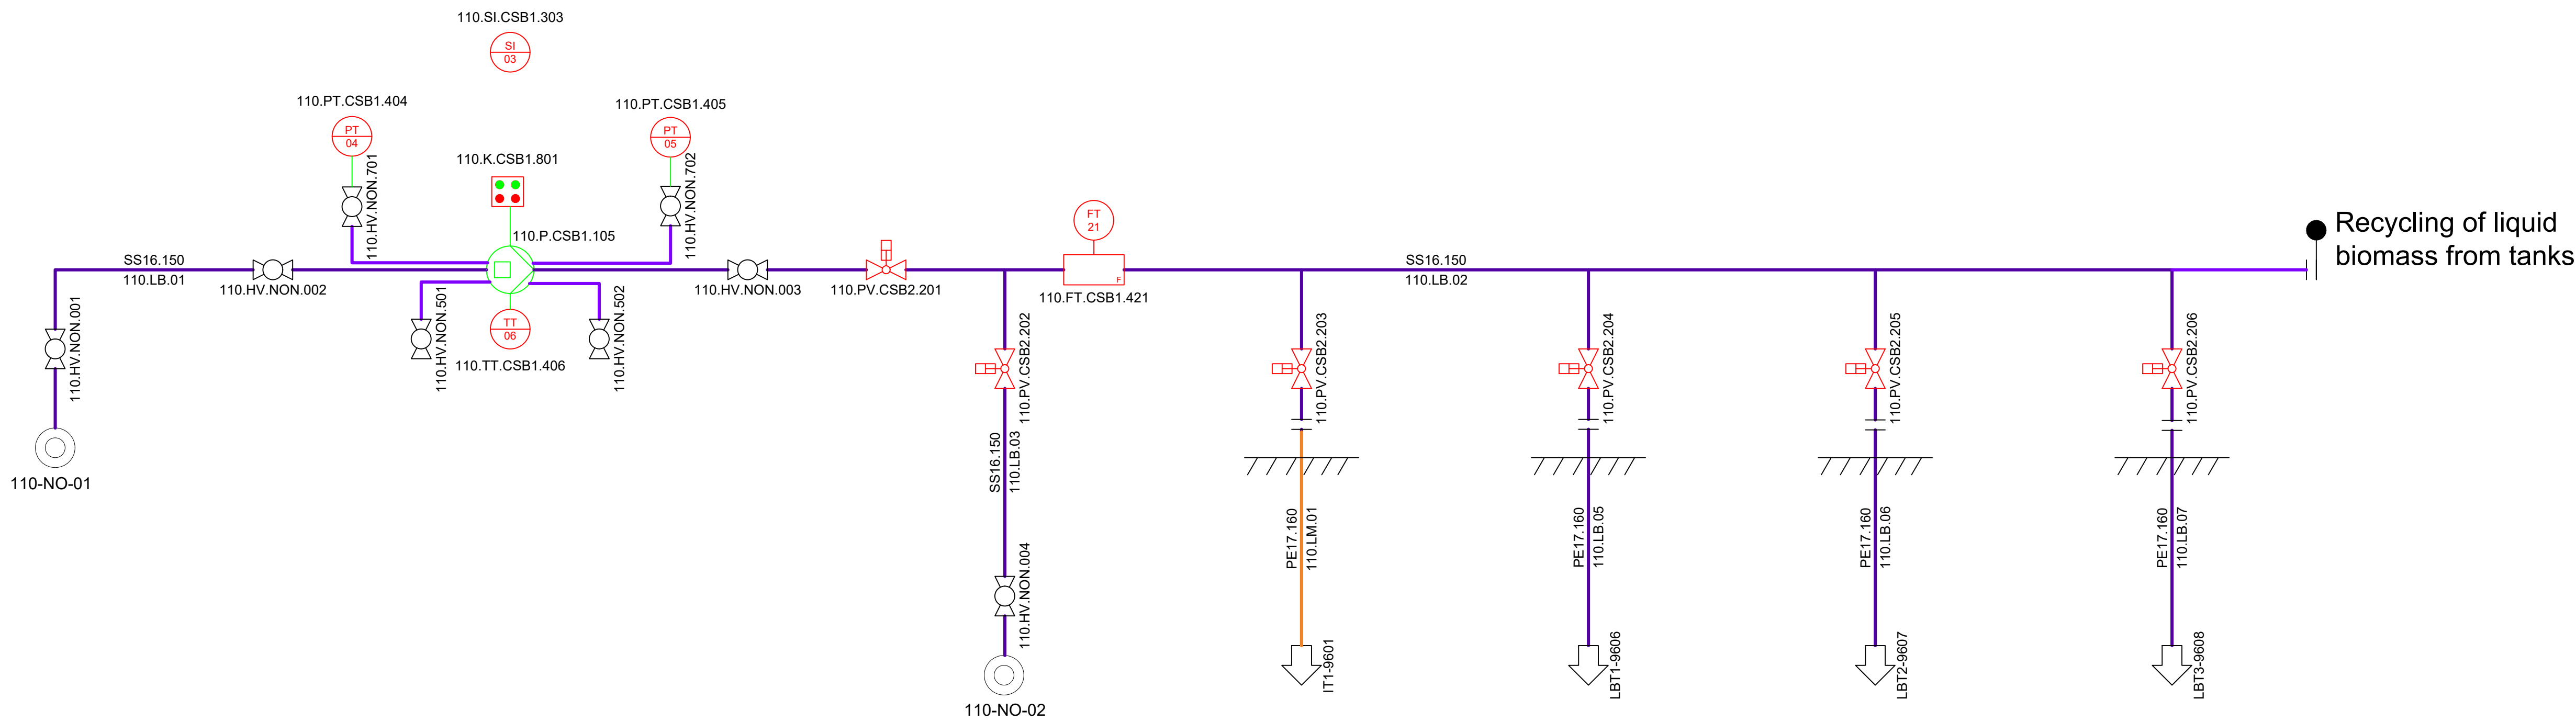


Rev. Nr.:	Rev. Dato:	Rev. Description:	
Builder:	ST1		
Project:	SLK		
Subject:	Liquid biomass delivery pump		
Rev. 2			
Int.:MDC	QC.CM	APP.:	Date: 26-06-2025
LUNDSBY RENEWABLE SOLUTIONS			Lundsby Renewable Solutions A/S, Hjarbækvej 65, 8831 Lægstrup Tlf.: +45 96 49 43 00 Info@lundsby.dk This Drawing is subject to copyright and may not be reproduced without permission from Lundsby Renewable Solutions A/S
Project nr...1768 Drawing nr...: 9604			FORMAT: A1

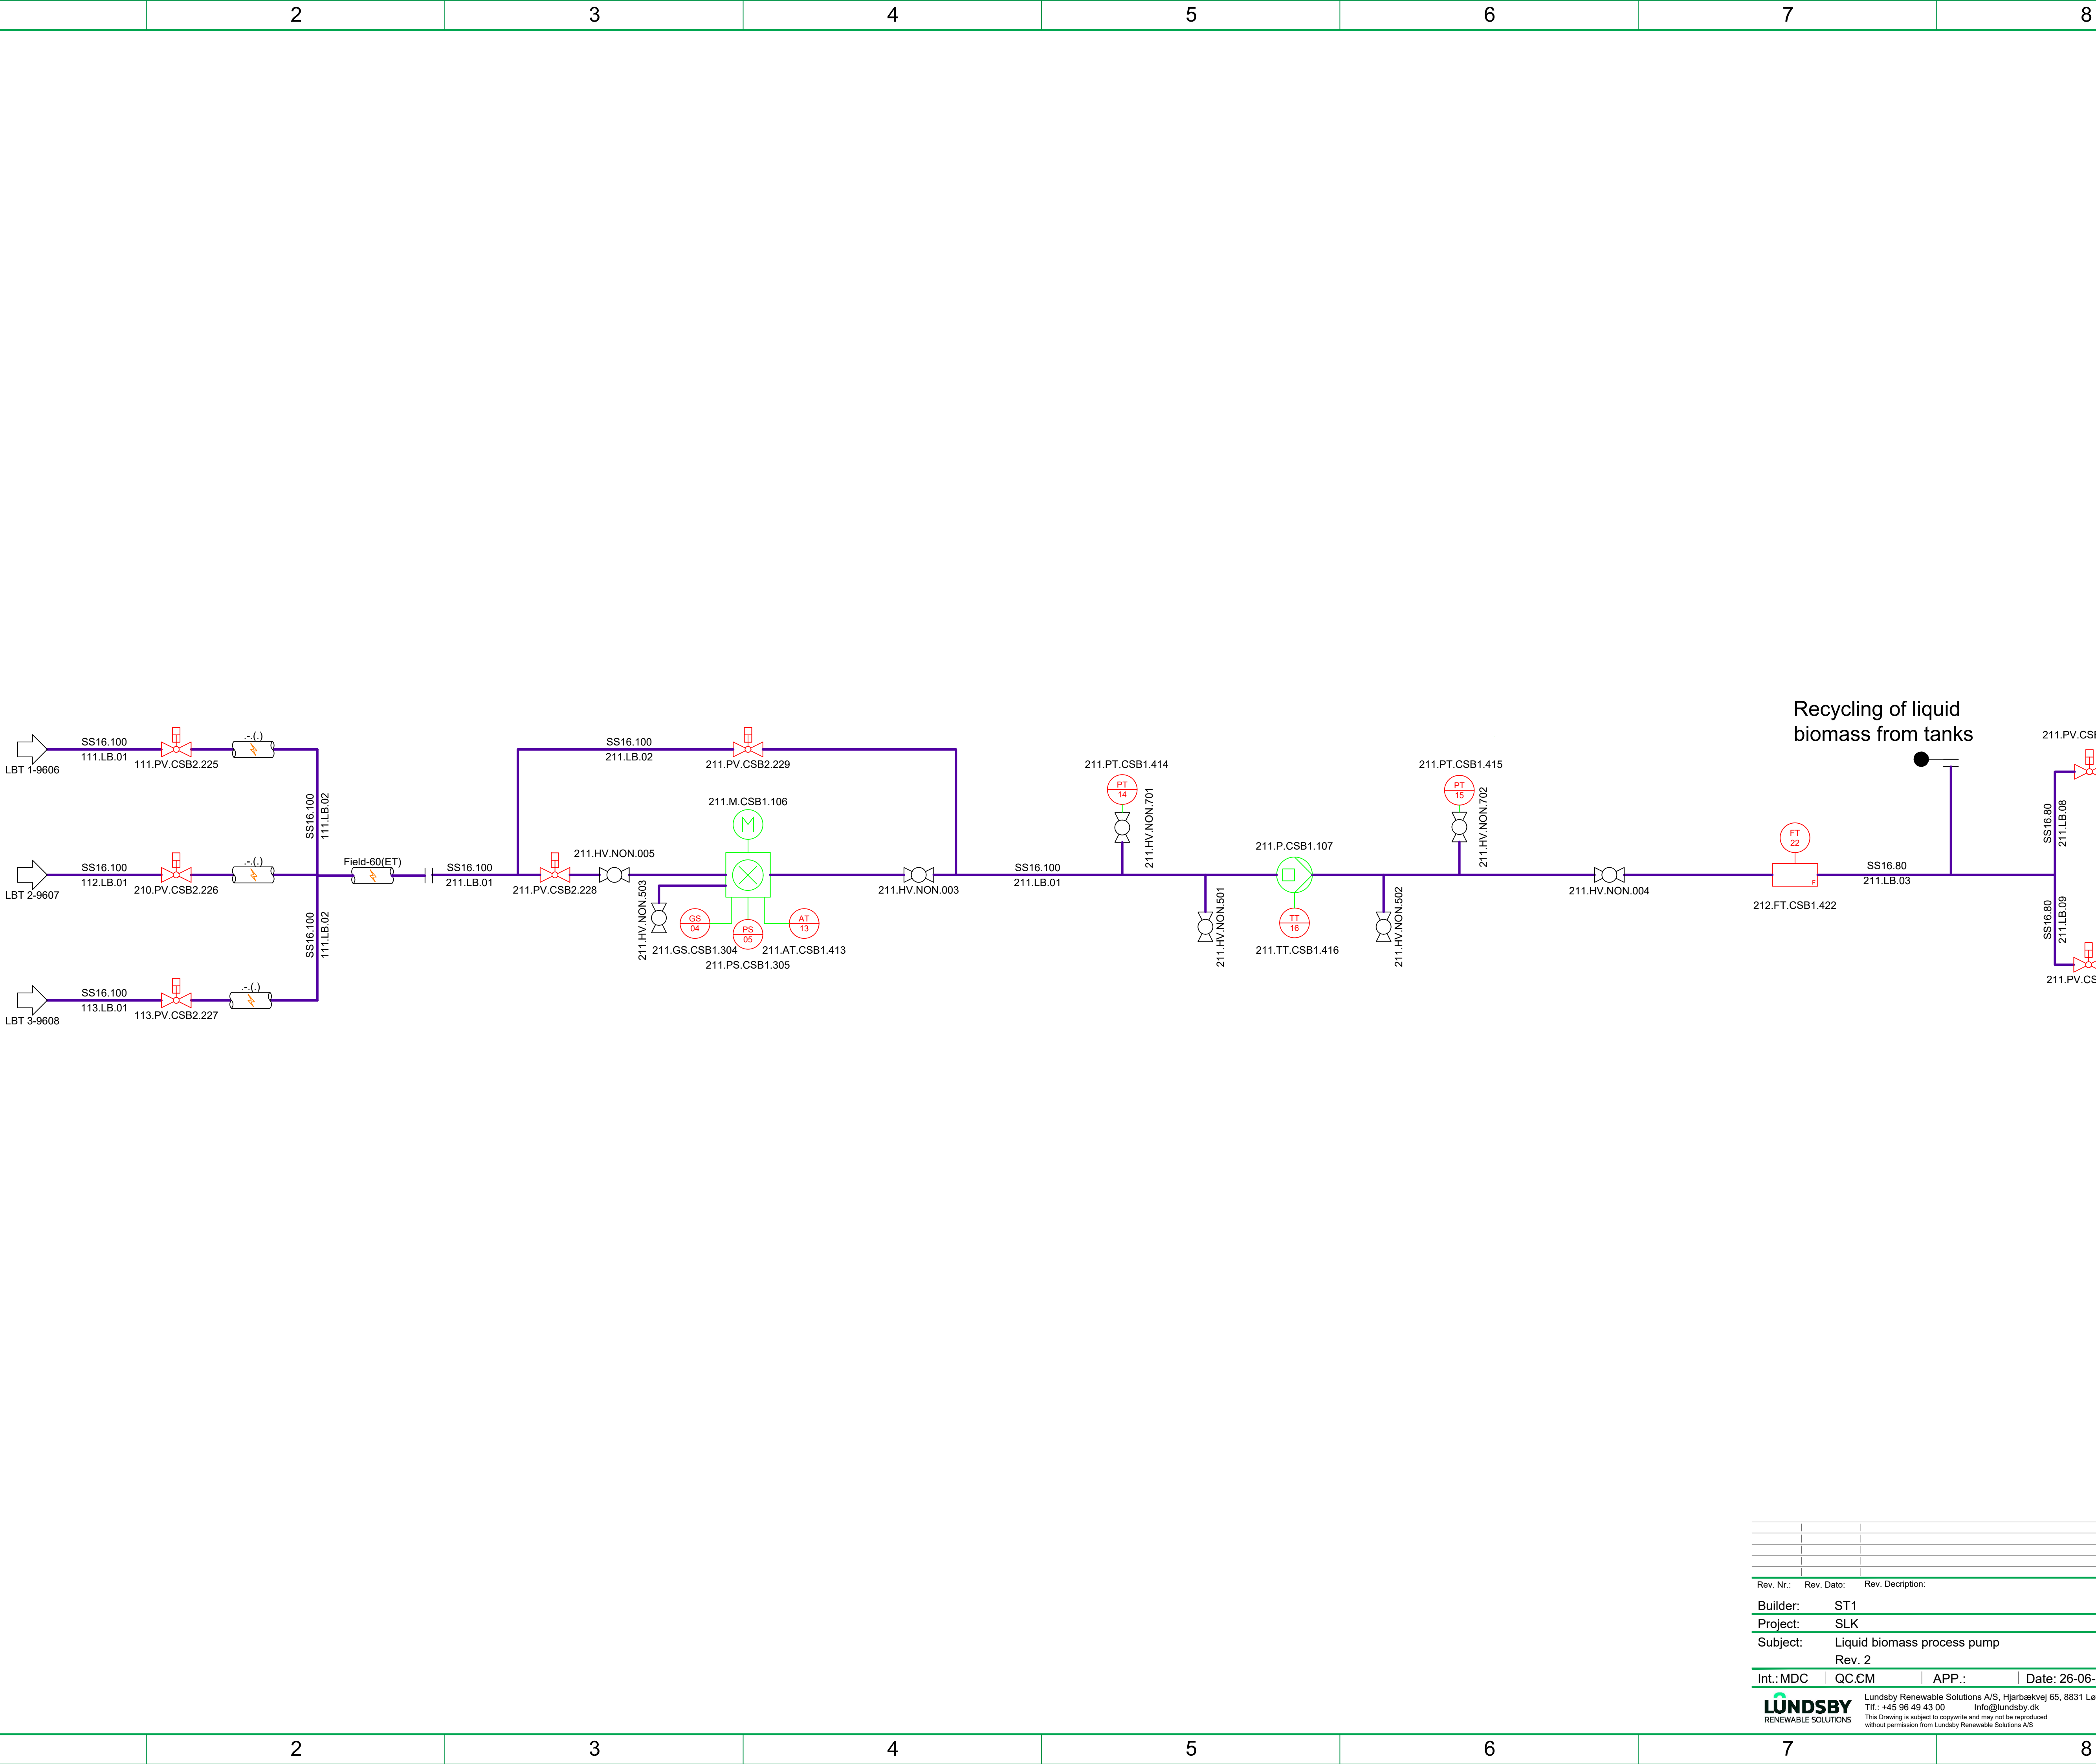


Rev. Nr.: Rev. Dato: Rev. Description:		
Builder: ST1		
Project: SLK		
Subject: Liquid biomass process pump		
Rev. 2		
Int.: MDC	QC: CM	APP.: Date: 26-06-2025
LUNDSBY RENEWABLE SOLUTIONS		
Lundsby Renewable Solutions A/S, Hjarbækvej 65, 8831 Løgstrup Tlf.: +45 96 49 43 00 Info@lundsby.dk This Drawing is subject to copyright and may not be reproduced without permission from Lundsby Renewable Solutions A/S		
Project nr.: 1768 Drawing nr.: 9605		FORMAT: A1

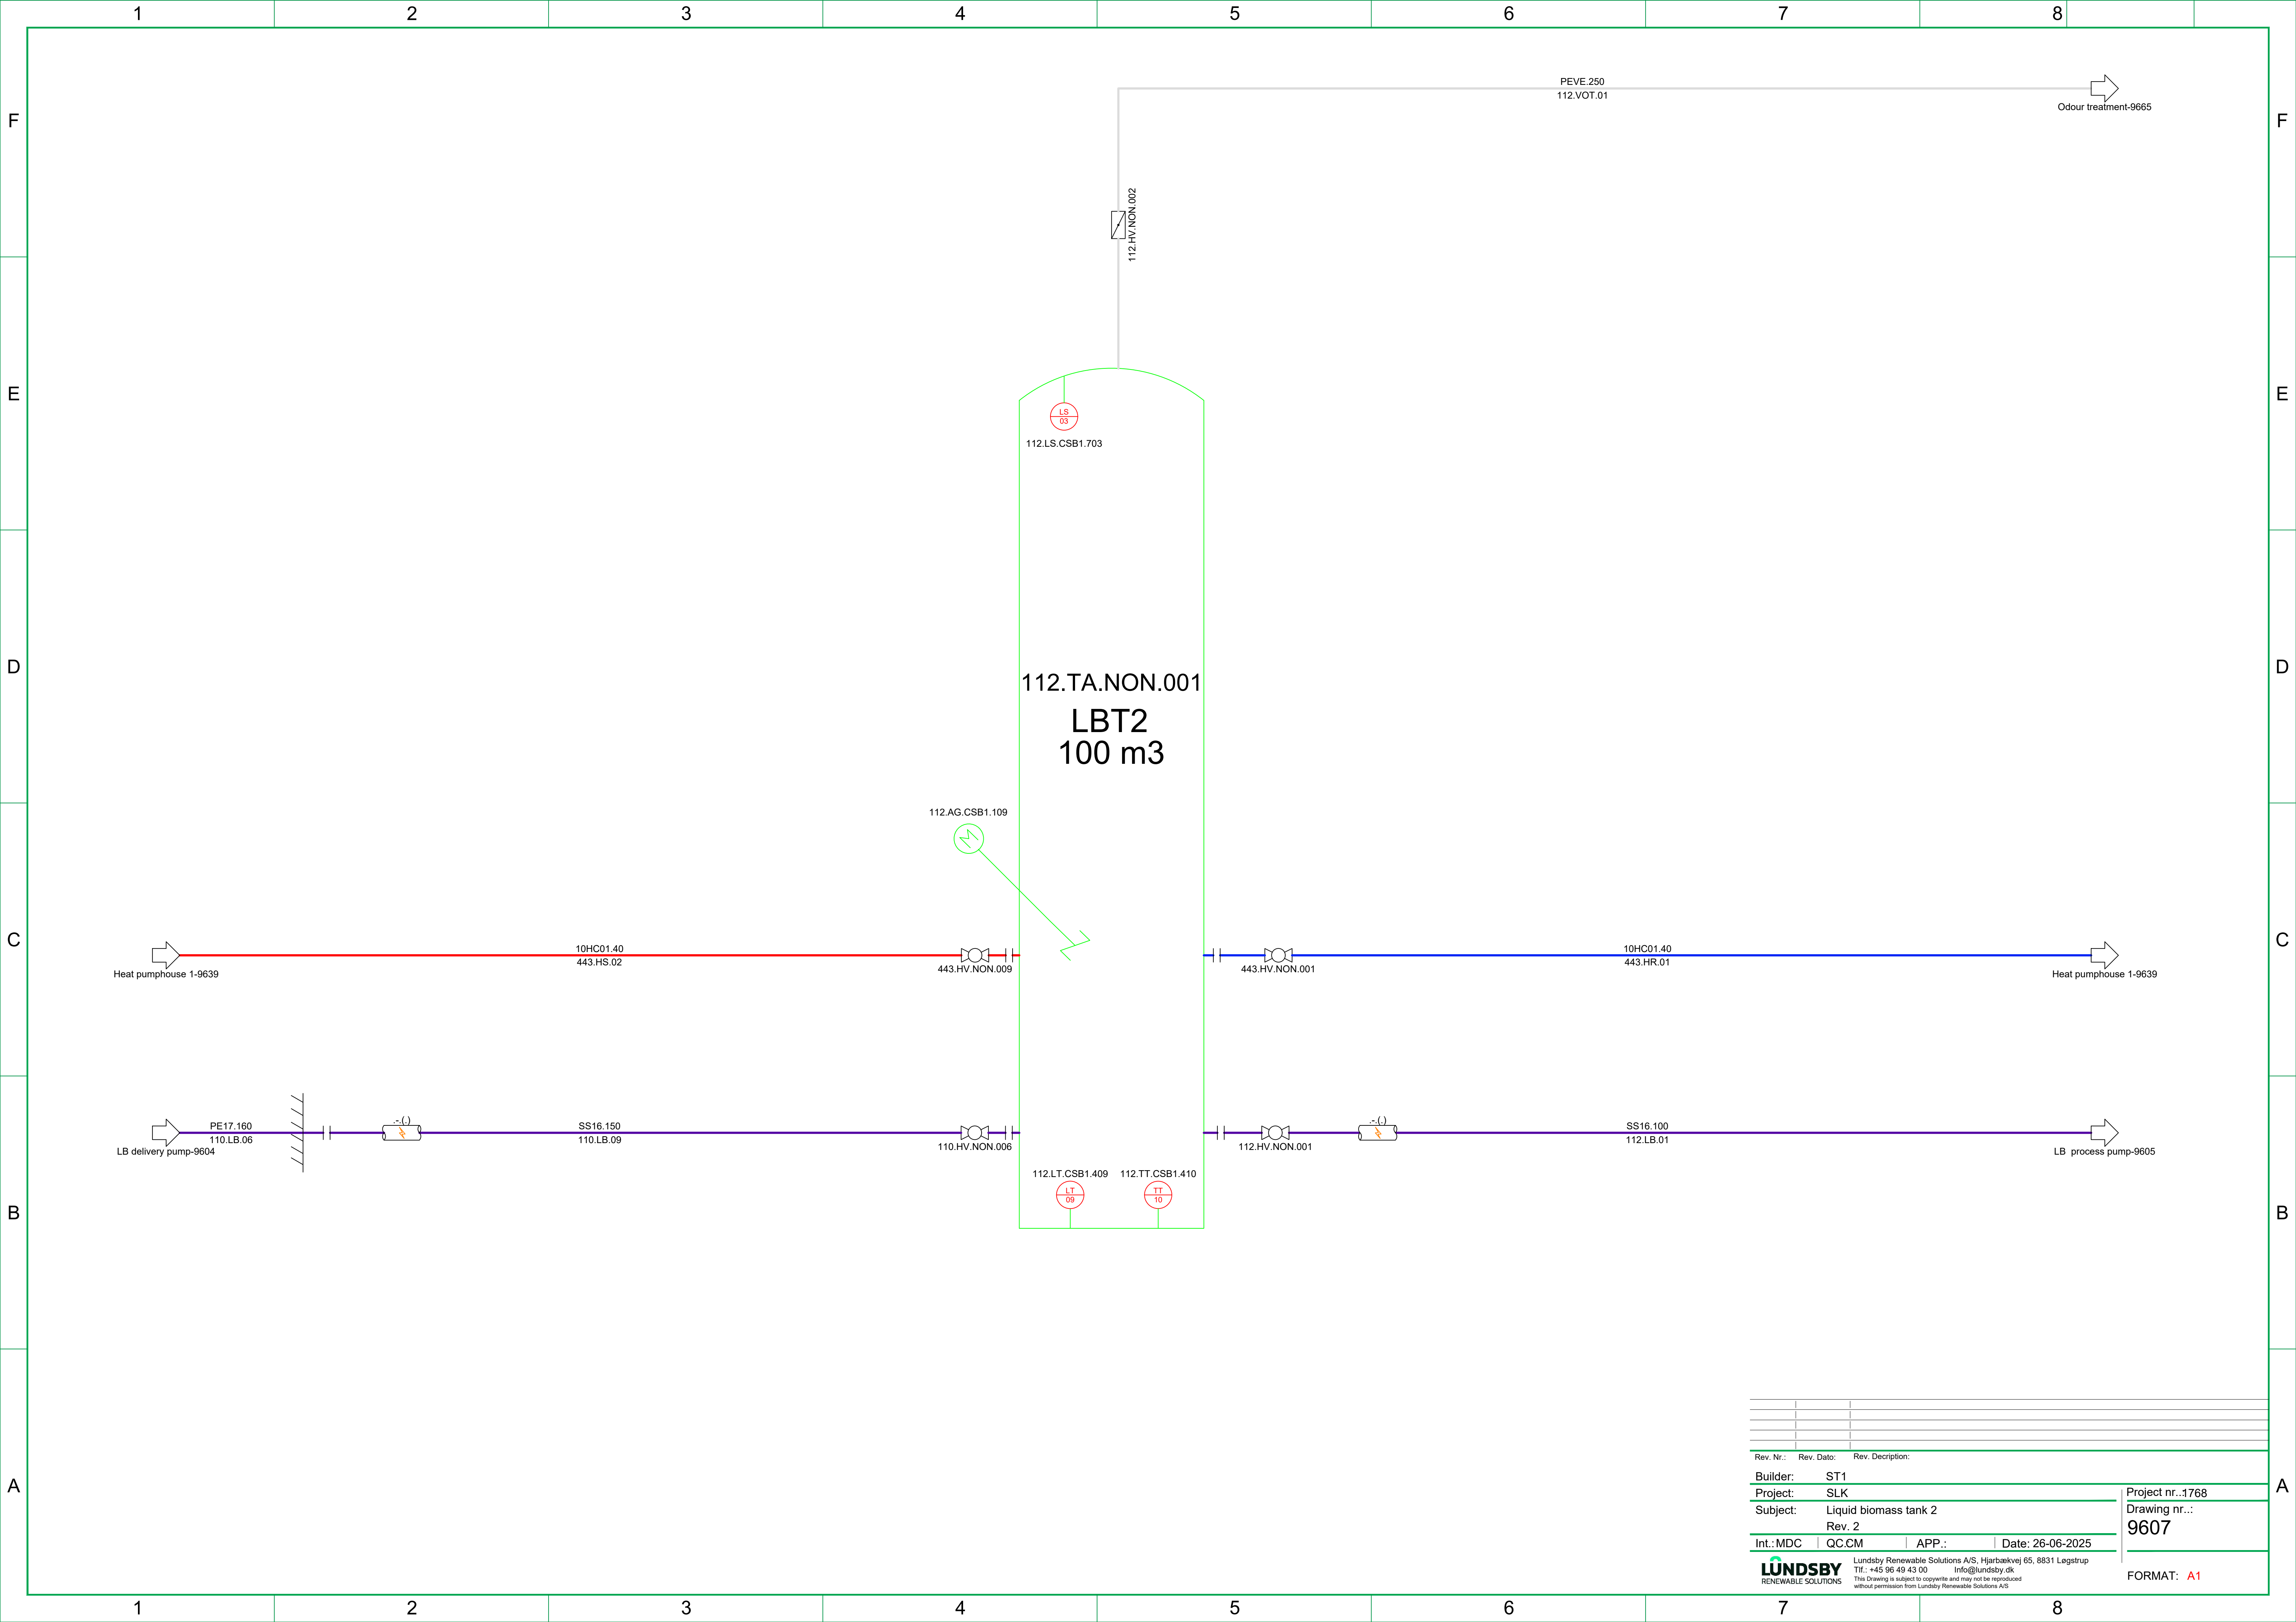


Rev. Nr.:	Rev. Dato:	Rev. Description:	
Builder:	ST1		
Project:	SLK		
Subject:	Liquid biomass tank 2		
Rev. 2			
Int.:MDC	QC:CM	APP.:	Date: 26-06-2025
LUNDSBY RENEWABLE SOLUTIONS			Lundsby Renewable Solutions A/S, Hjarbækvej 65, 8831 Løgstrup Tlf.: +45 96 49 43 00 Info@lundsby.dk This Drawing is subject to copyright and may not be reproduced without permission from Lundsby Renewable Solutions A/S
			Project nr...1768 Drawing nr...: 9607
			FORMAT: A1

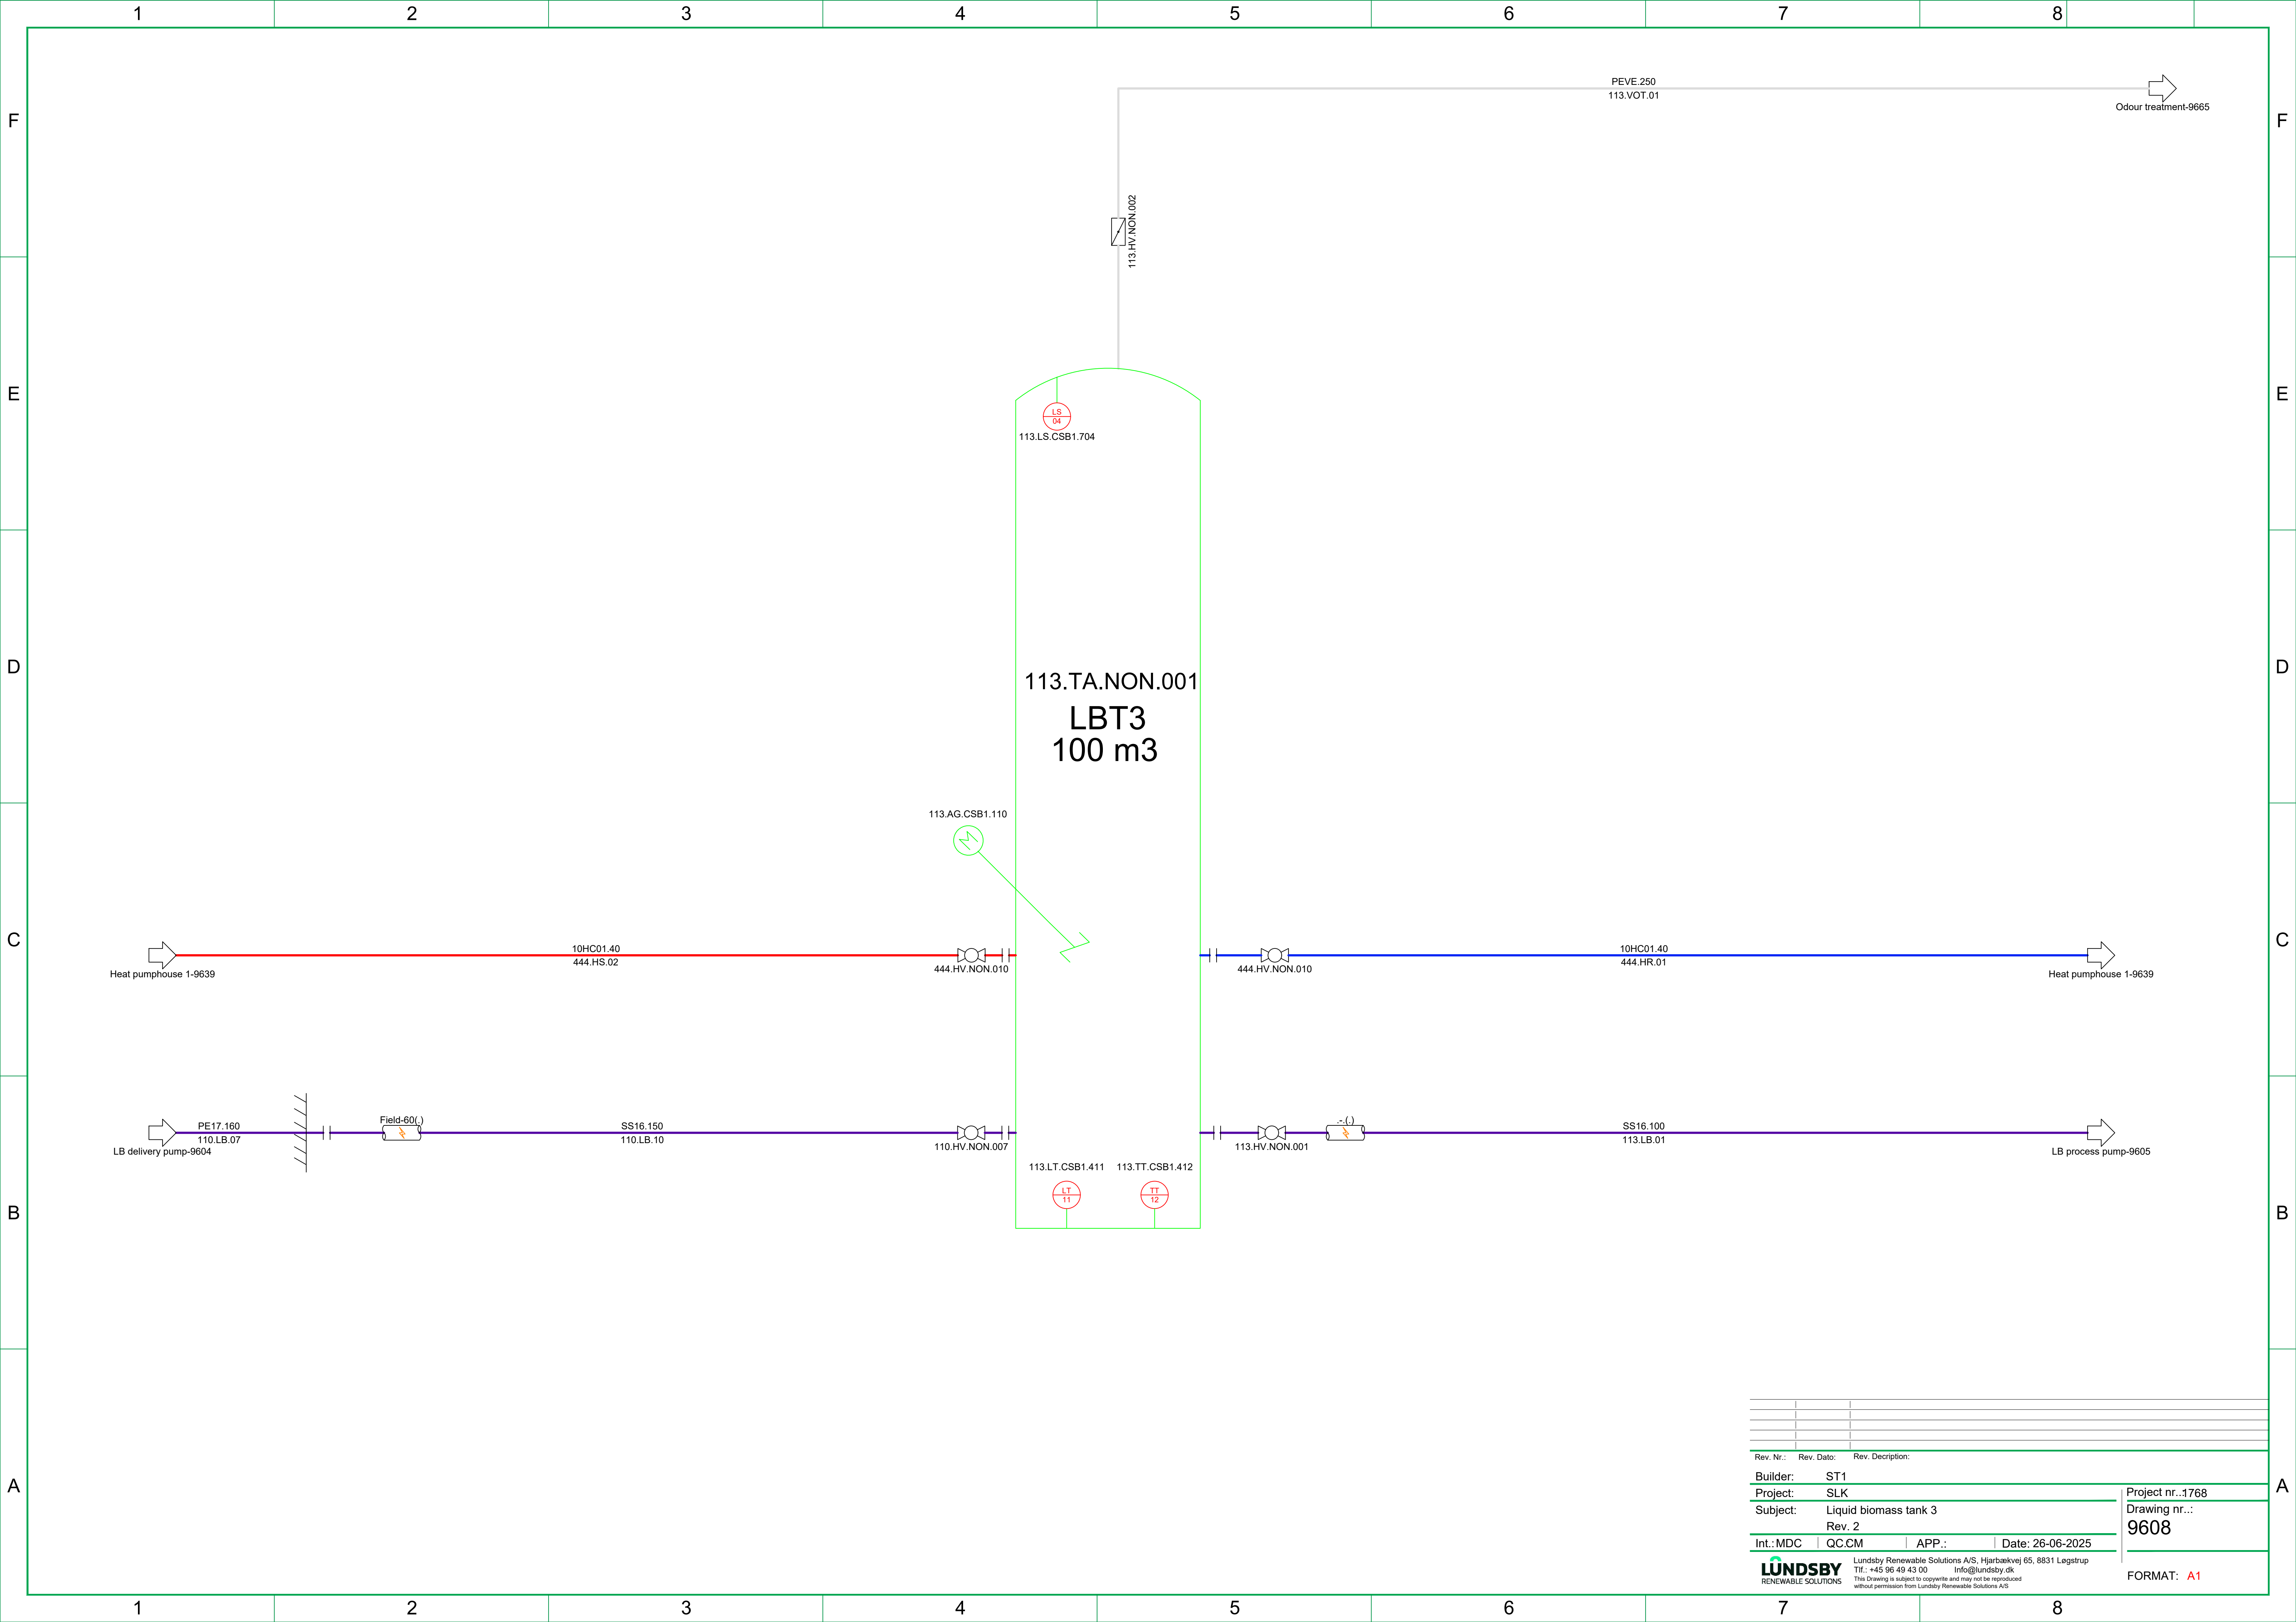

Rev. Nr.:	Rev. Dato:	Rev. Description:	
Builder:	ST1		
Project:	SLK		
Subject:	Liquid biomass tank 3		
Rev. 2			
Int.:MDC	QC:CM	APP.:	Date: 26-06-2025
LUNDSBY RENEWABLE SOLUTIONS			Lundsby Renewable Solutions A/S, Hjarbækvej 65, 8831 Løgstrup Tlf.: +45 96 49 43 00 Info@lundsby.dk This Drawing is subject to copyright and may not be reproduced without permission from Lundsby Renewable Solutions A/S
Project nr...1768 Drawing nr...: 9608			FORMAT: A1

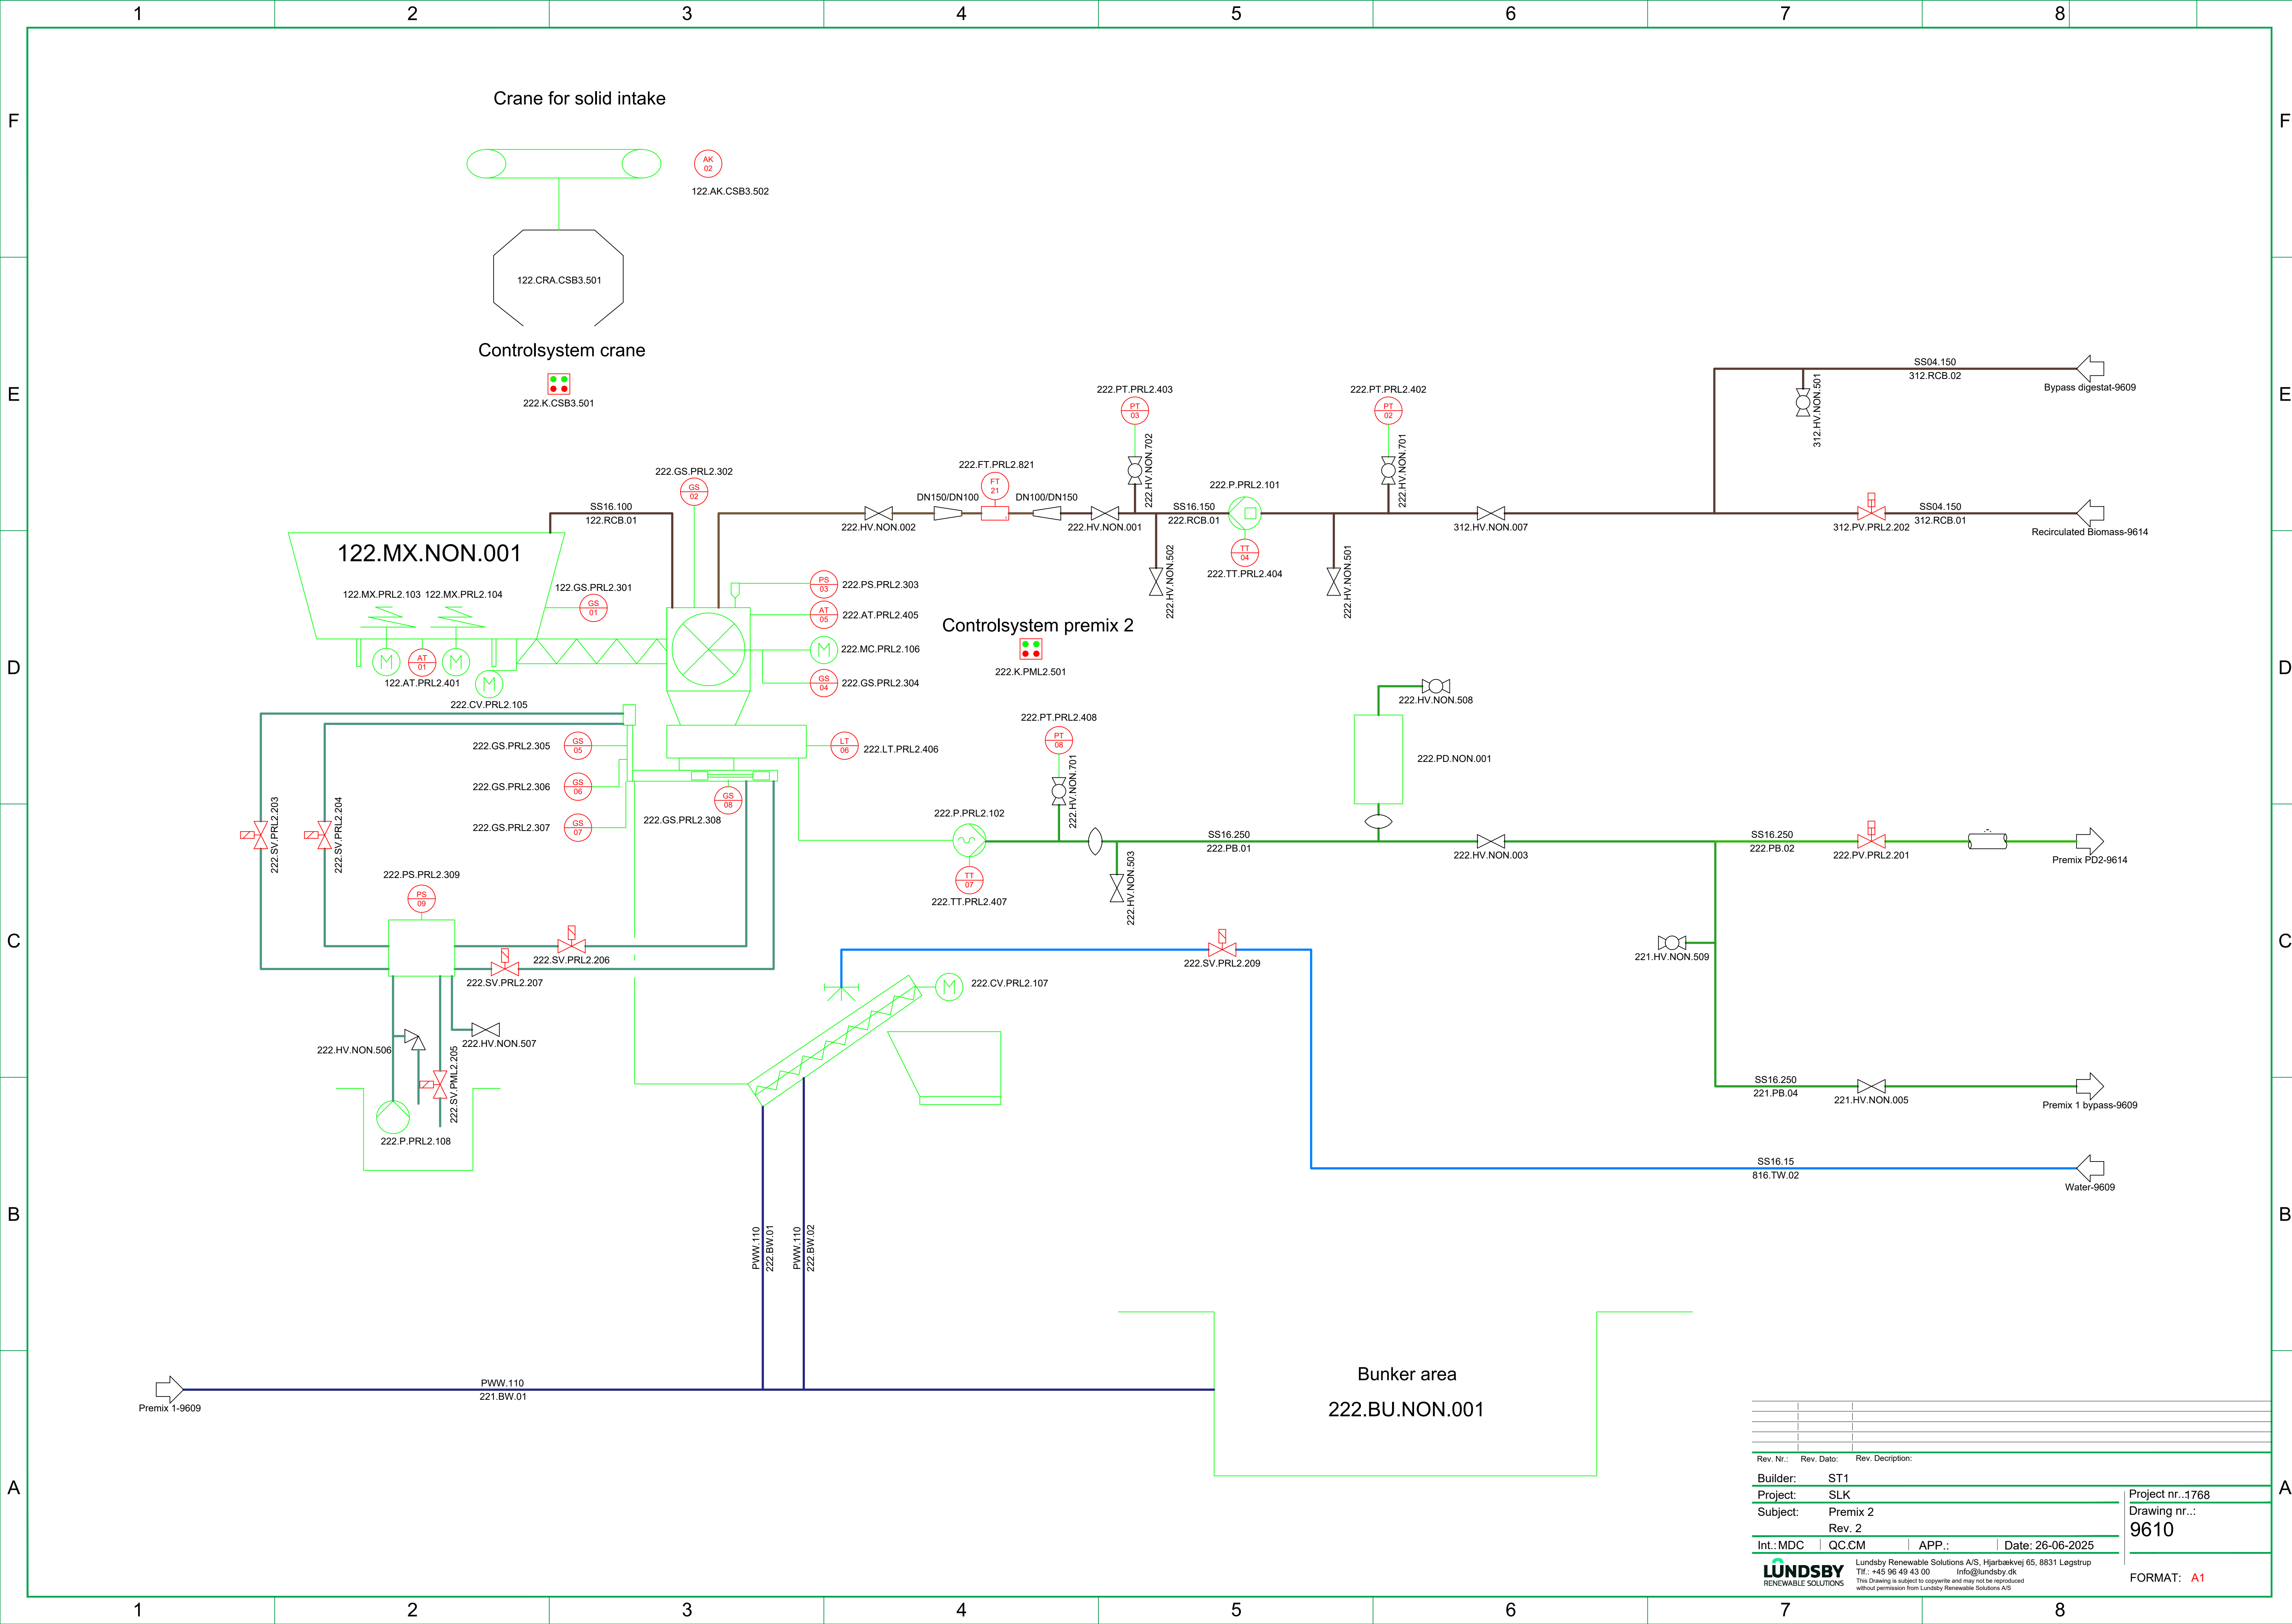


Pumphouse 2

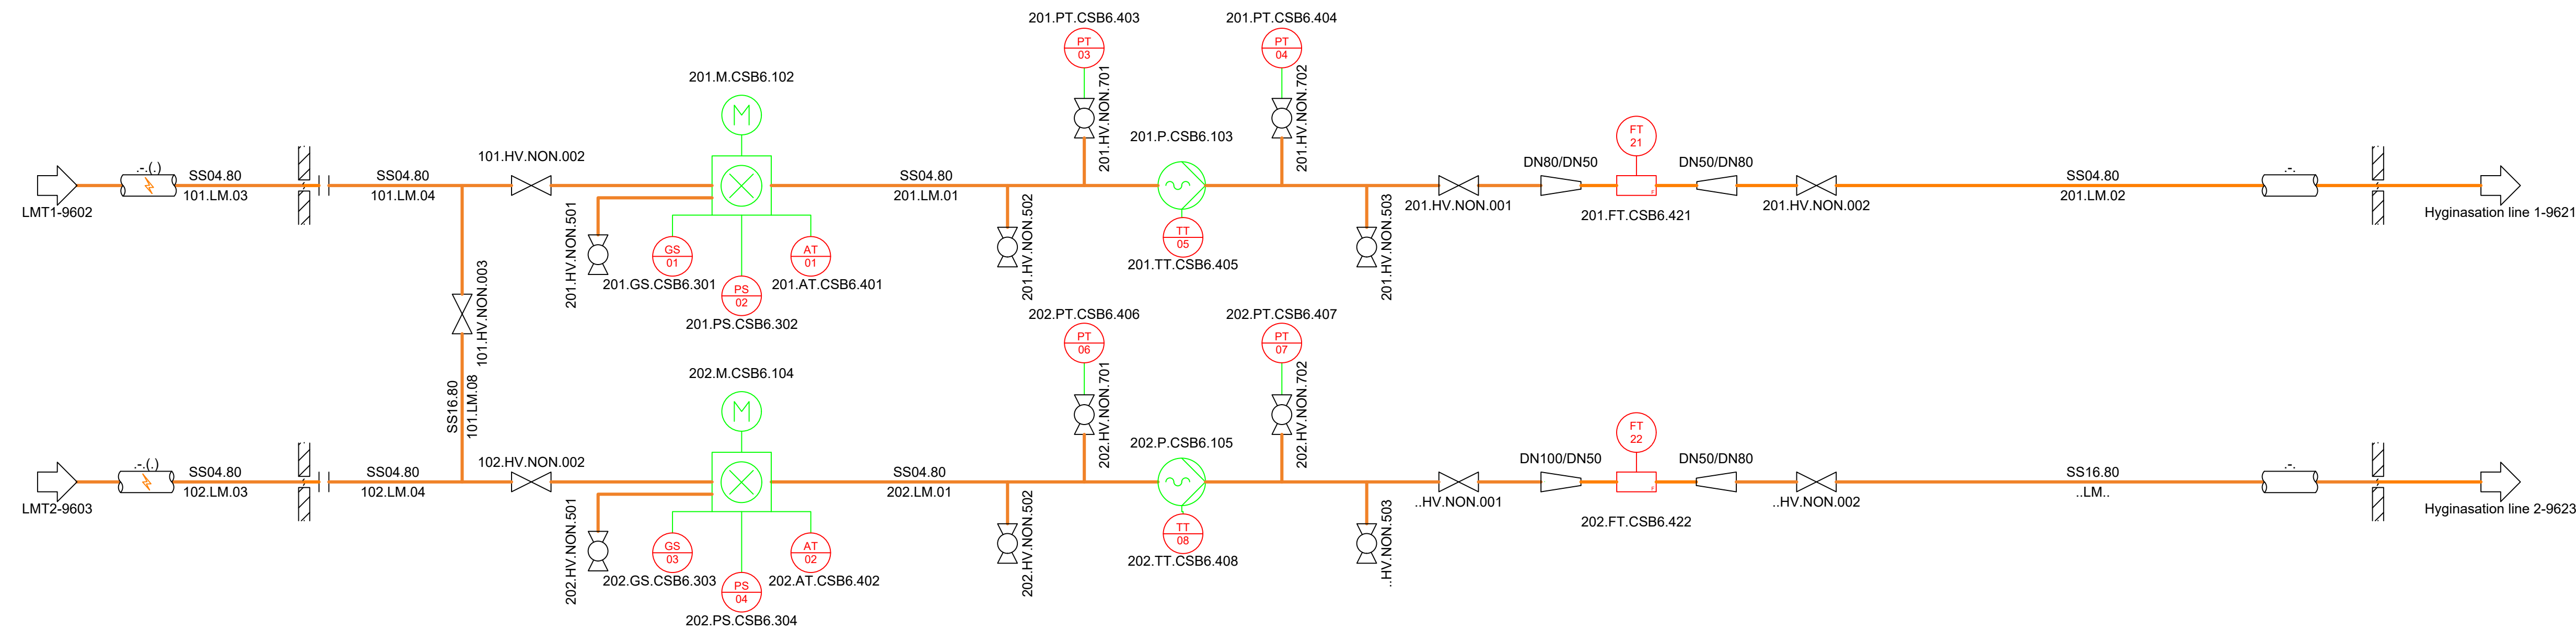


Tech
building


SB-building

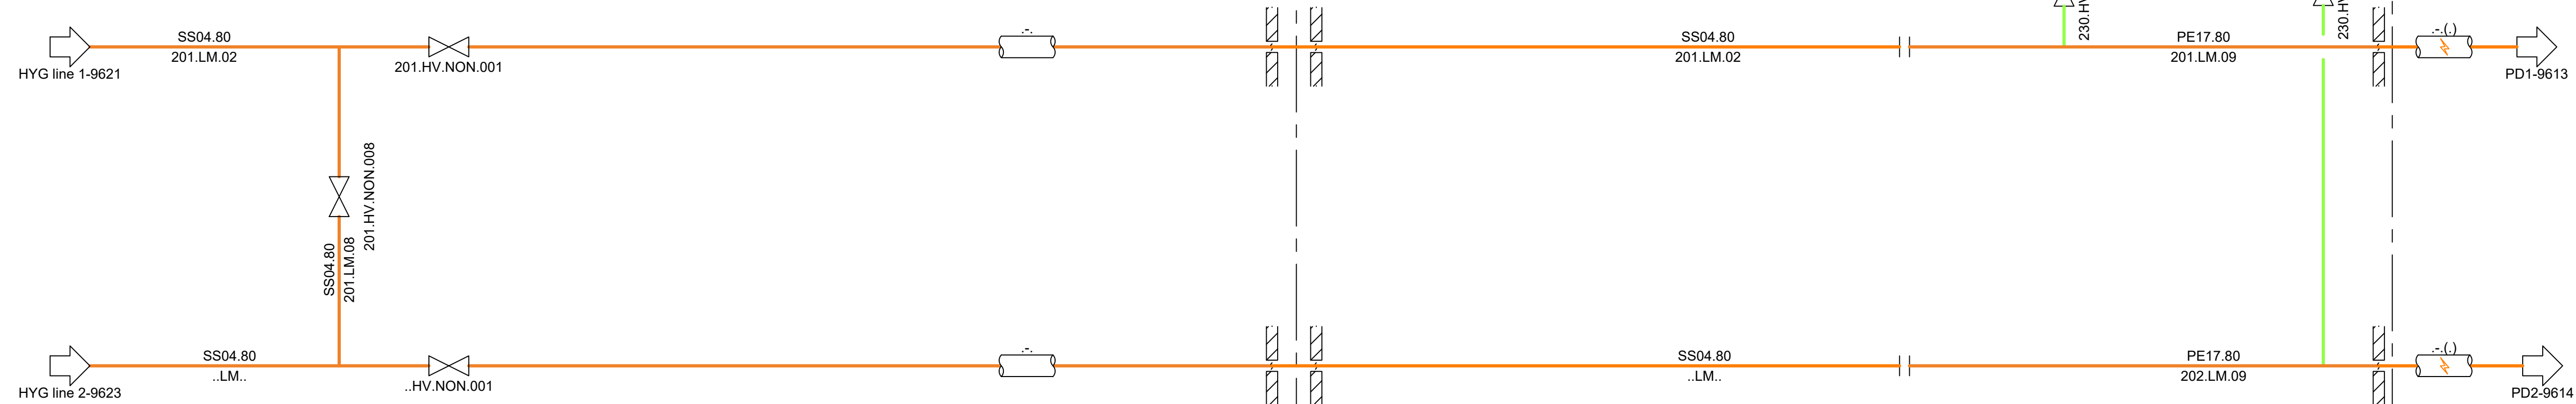

Rev. Nr.:	Rev. Dato:	Rev. Description:
Builder:	ST1	
Project:	SLK	
Subject:	Liquid manure pump	
Rev. 2		
Int.: MDC	QC.CM	APP.:
Date:	26-06-2025	
LUNDSBY RENEWABLE SOLUTIONS		
Lundsby Renewable Solutions A/S, Hjarbækvej 65, 8831 Lægstrup Tlf.: +45 96 49 43 00 Info@lundsby.dk This Drawing is subject to copyright and may not be reproduced without permission from Lundsby Renewable Solutions A/S		
Project nr.: 1768		Drawing nr.: 9612
FORMAT: A1		

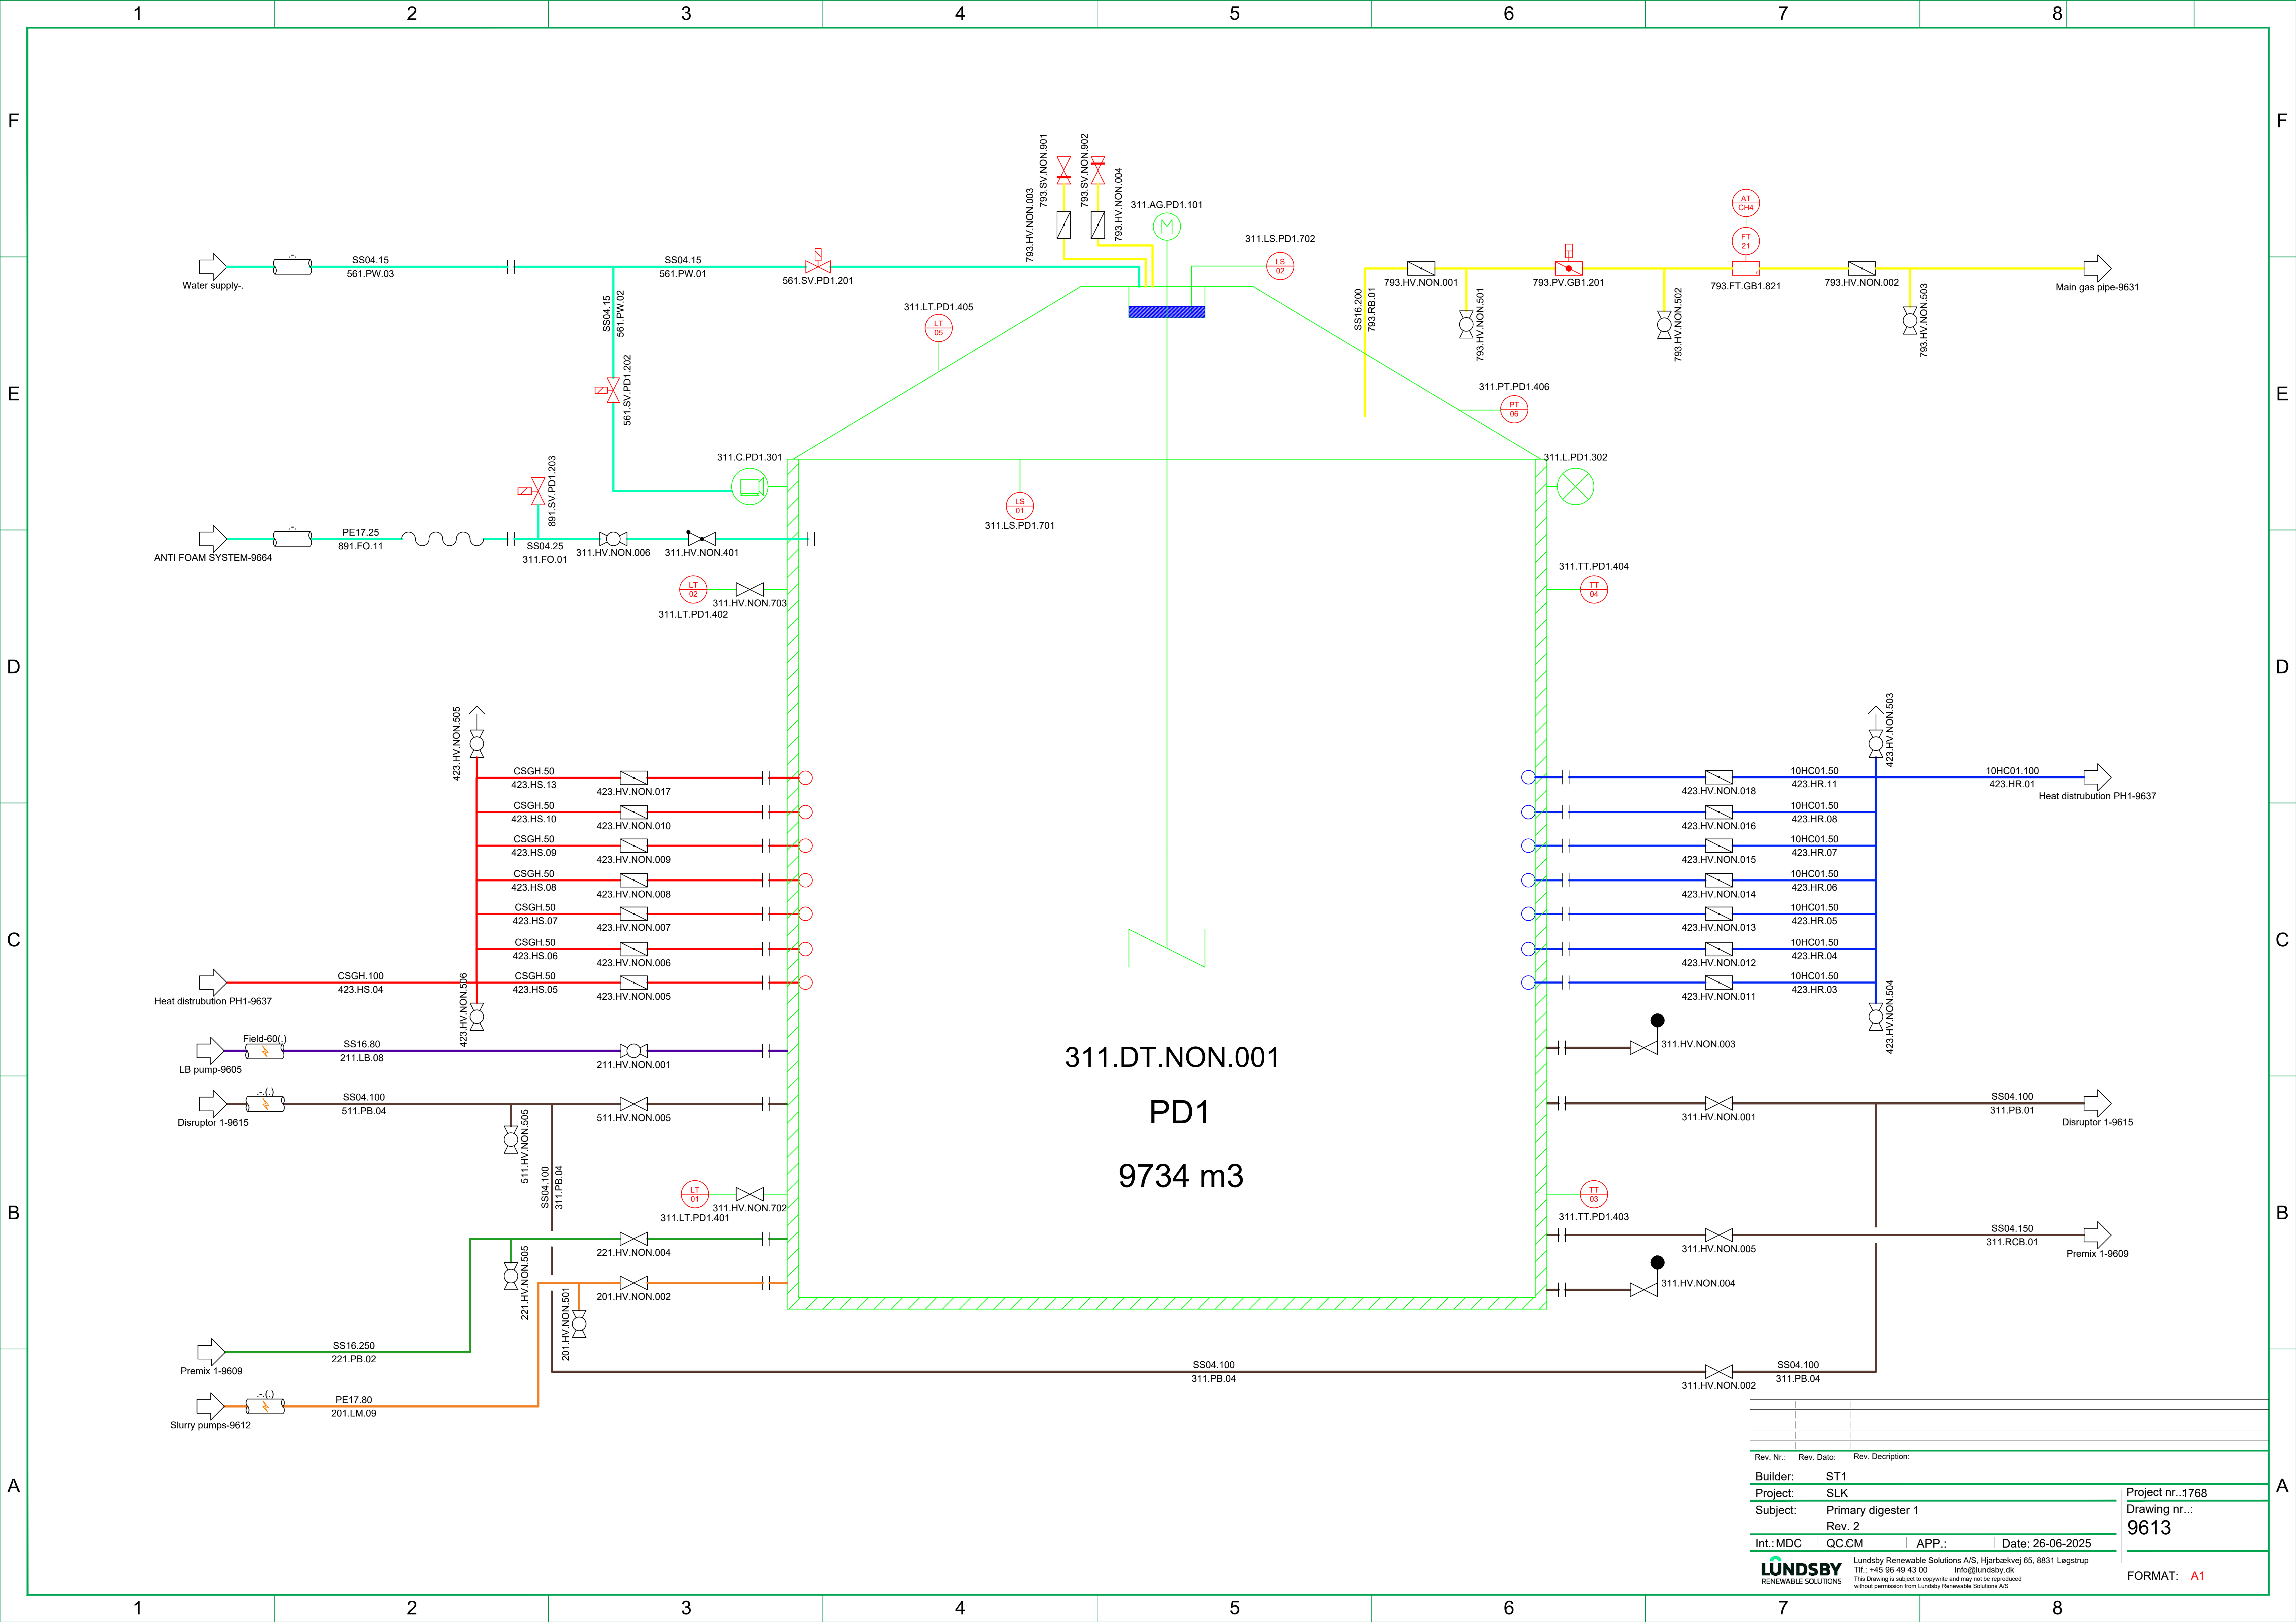


Rev. Nr.:	Rev. Dato:	Rev. Description:
Builder:	ST1	
Project:	SLK	
Subject:	Primary digester 1	
Rev. 2		
Int.:MDC	QC:CM	APP.:
Date:	26-06-2025	
LUNDSBY RENEWABLE SOLUTIONS		
Lundsby Renewable Solutions A/S, Hjarbækvej 65, 8831 Løgstrup Tlf.: +45 96 49 43 00 Info@lundsby.dk This drawing is subject to copyright and may not be reproduced without permission from Lundsby Renewable Solutions A/S		
Project nr.:1768 Drawing nr.: 9613		FORMAT: A1

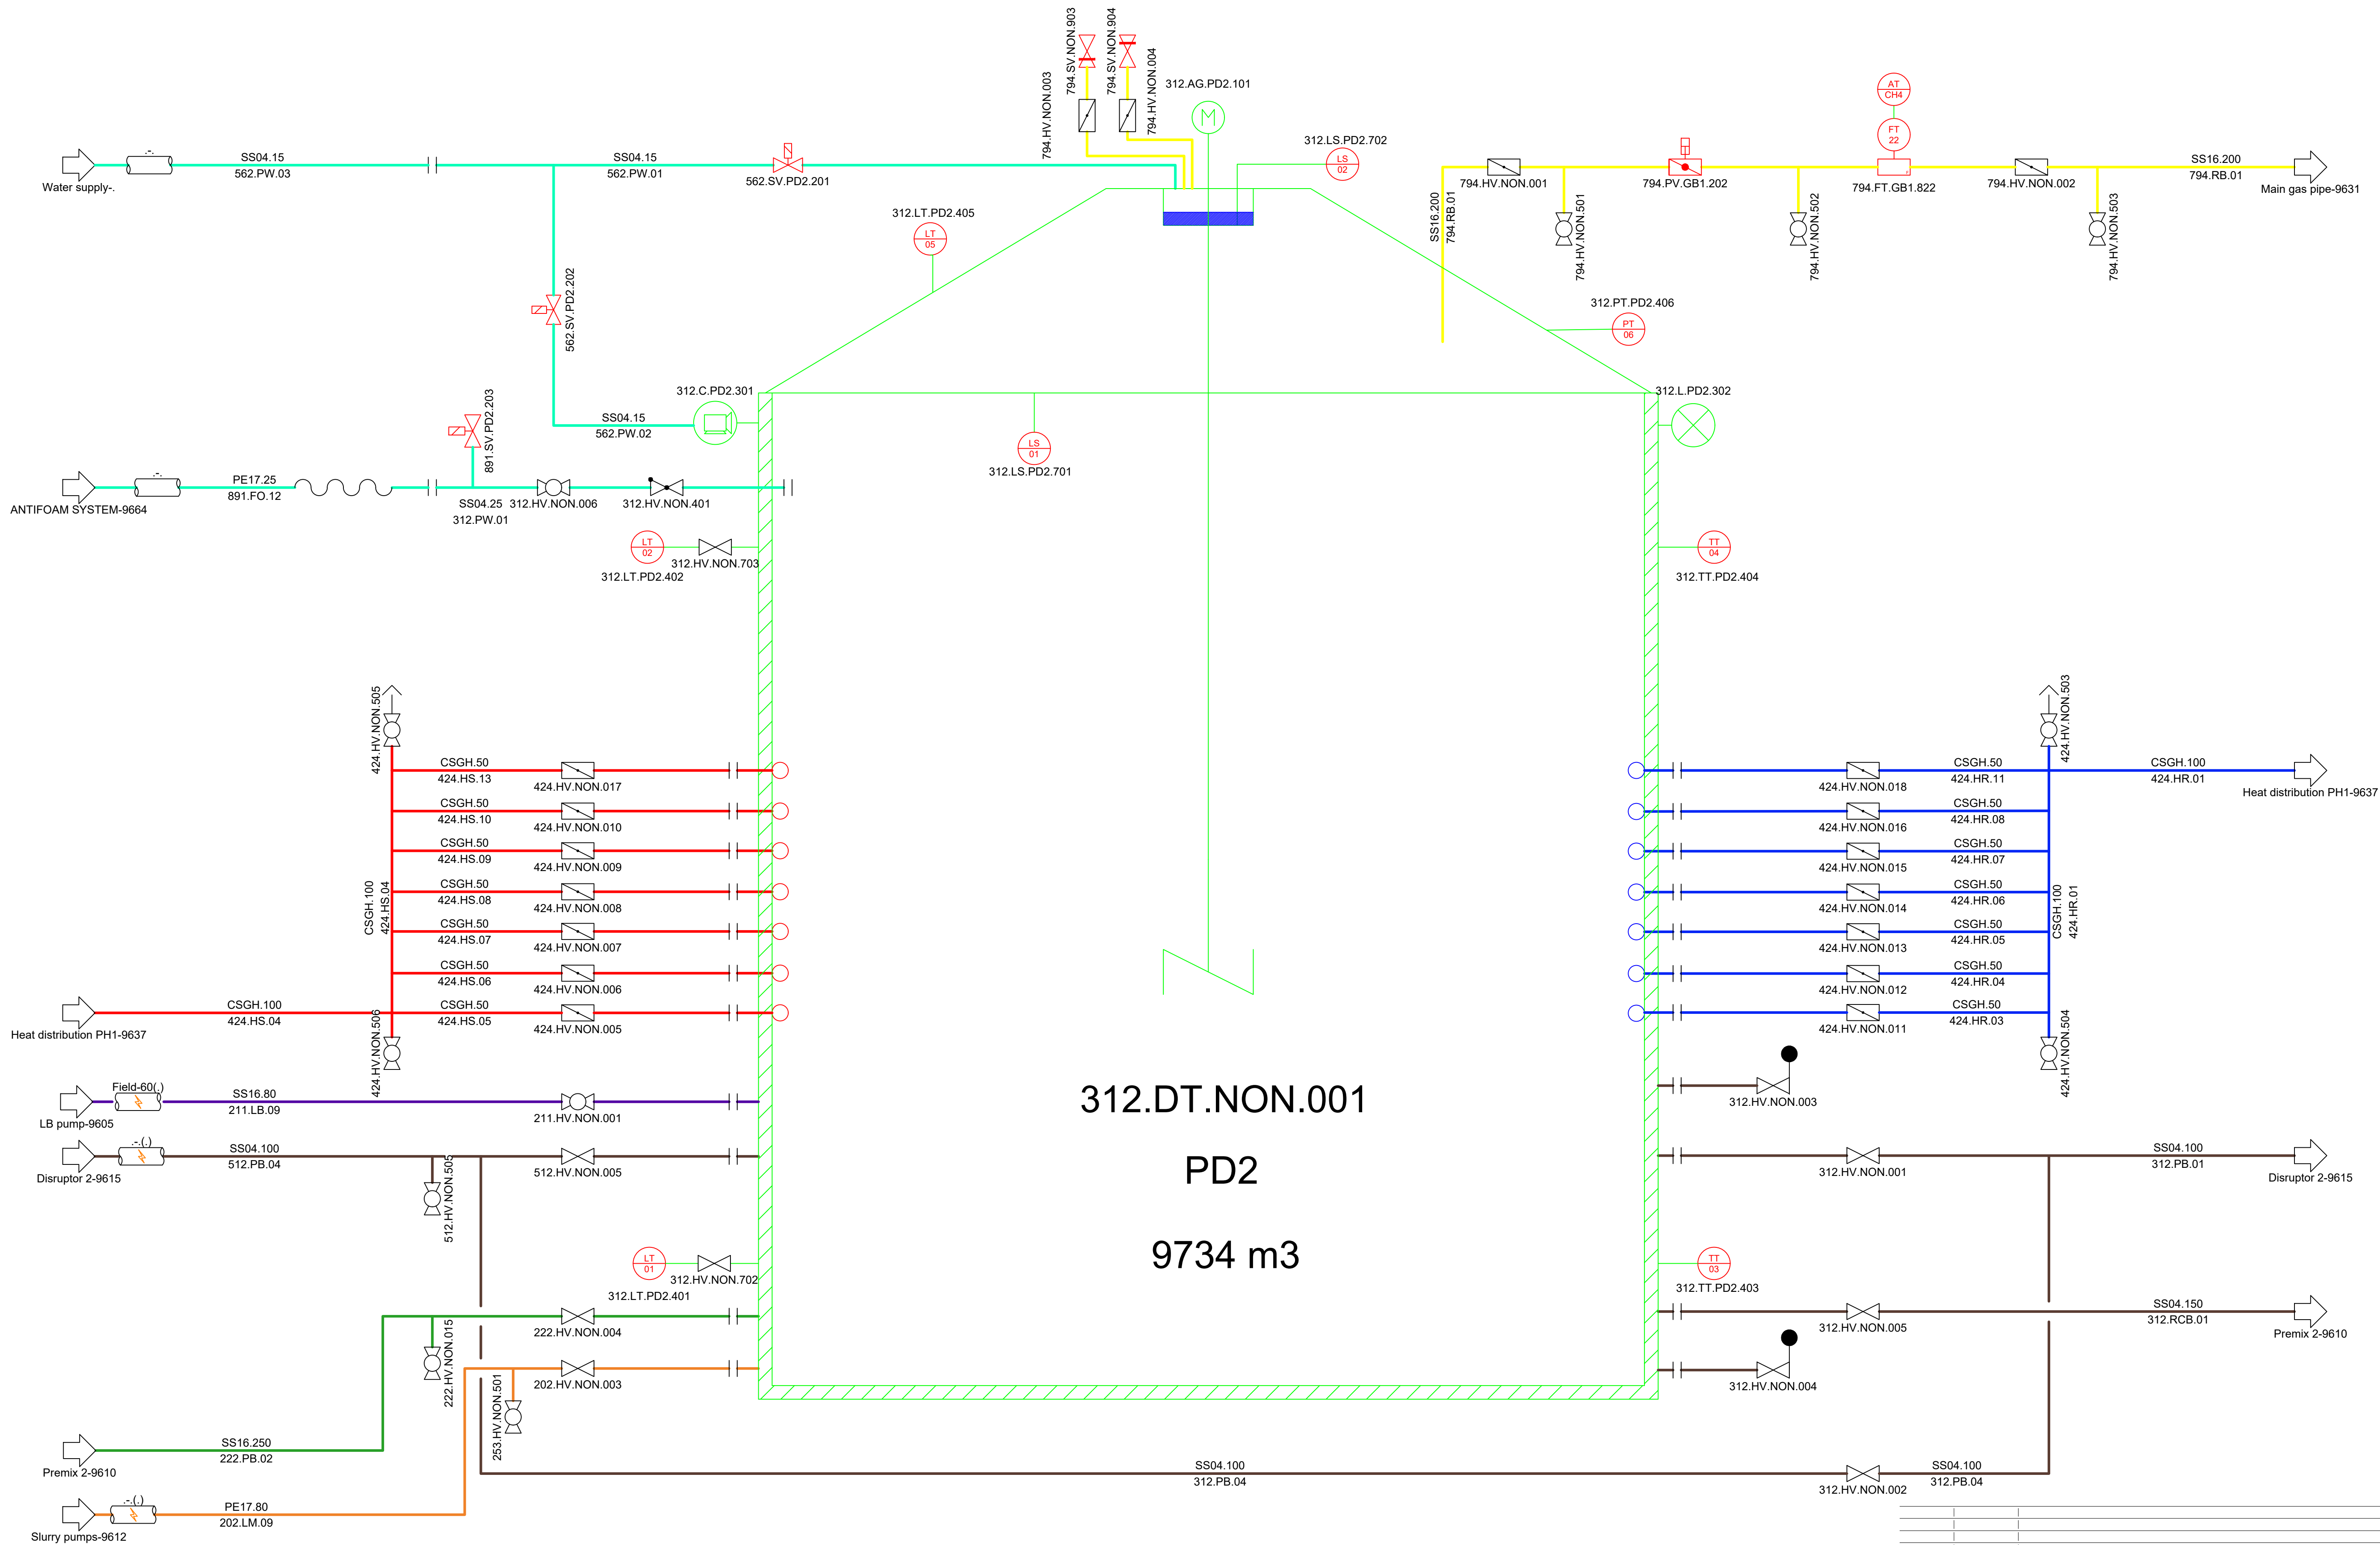


Rev. Nr.:	Rev. Dato:	Rev. Description:
Builder:	ST1	
Project:	SLK	
Subject:	Primary digester 2	
Rev. 2		
Int.:MDC	QC:CM	APP.:Date: 26-06-2025
LUNDSBY RENEWABLE SOLUTIONS		
Lundsby Renewable Solutions A/S, Hjarbækvej 65, 8831 Legstrup Tlf.: +45 96 49 43 00 Info@lundsby.dk This drawing is subject to copyright and may not be reproduced without permission from Lundsby Renewable Solutions A/S		
Project nr.:1768 Drawing nr.: 9614		FORMAT: A1

Pumphouse 1

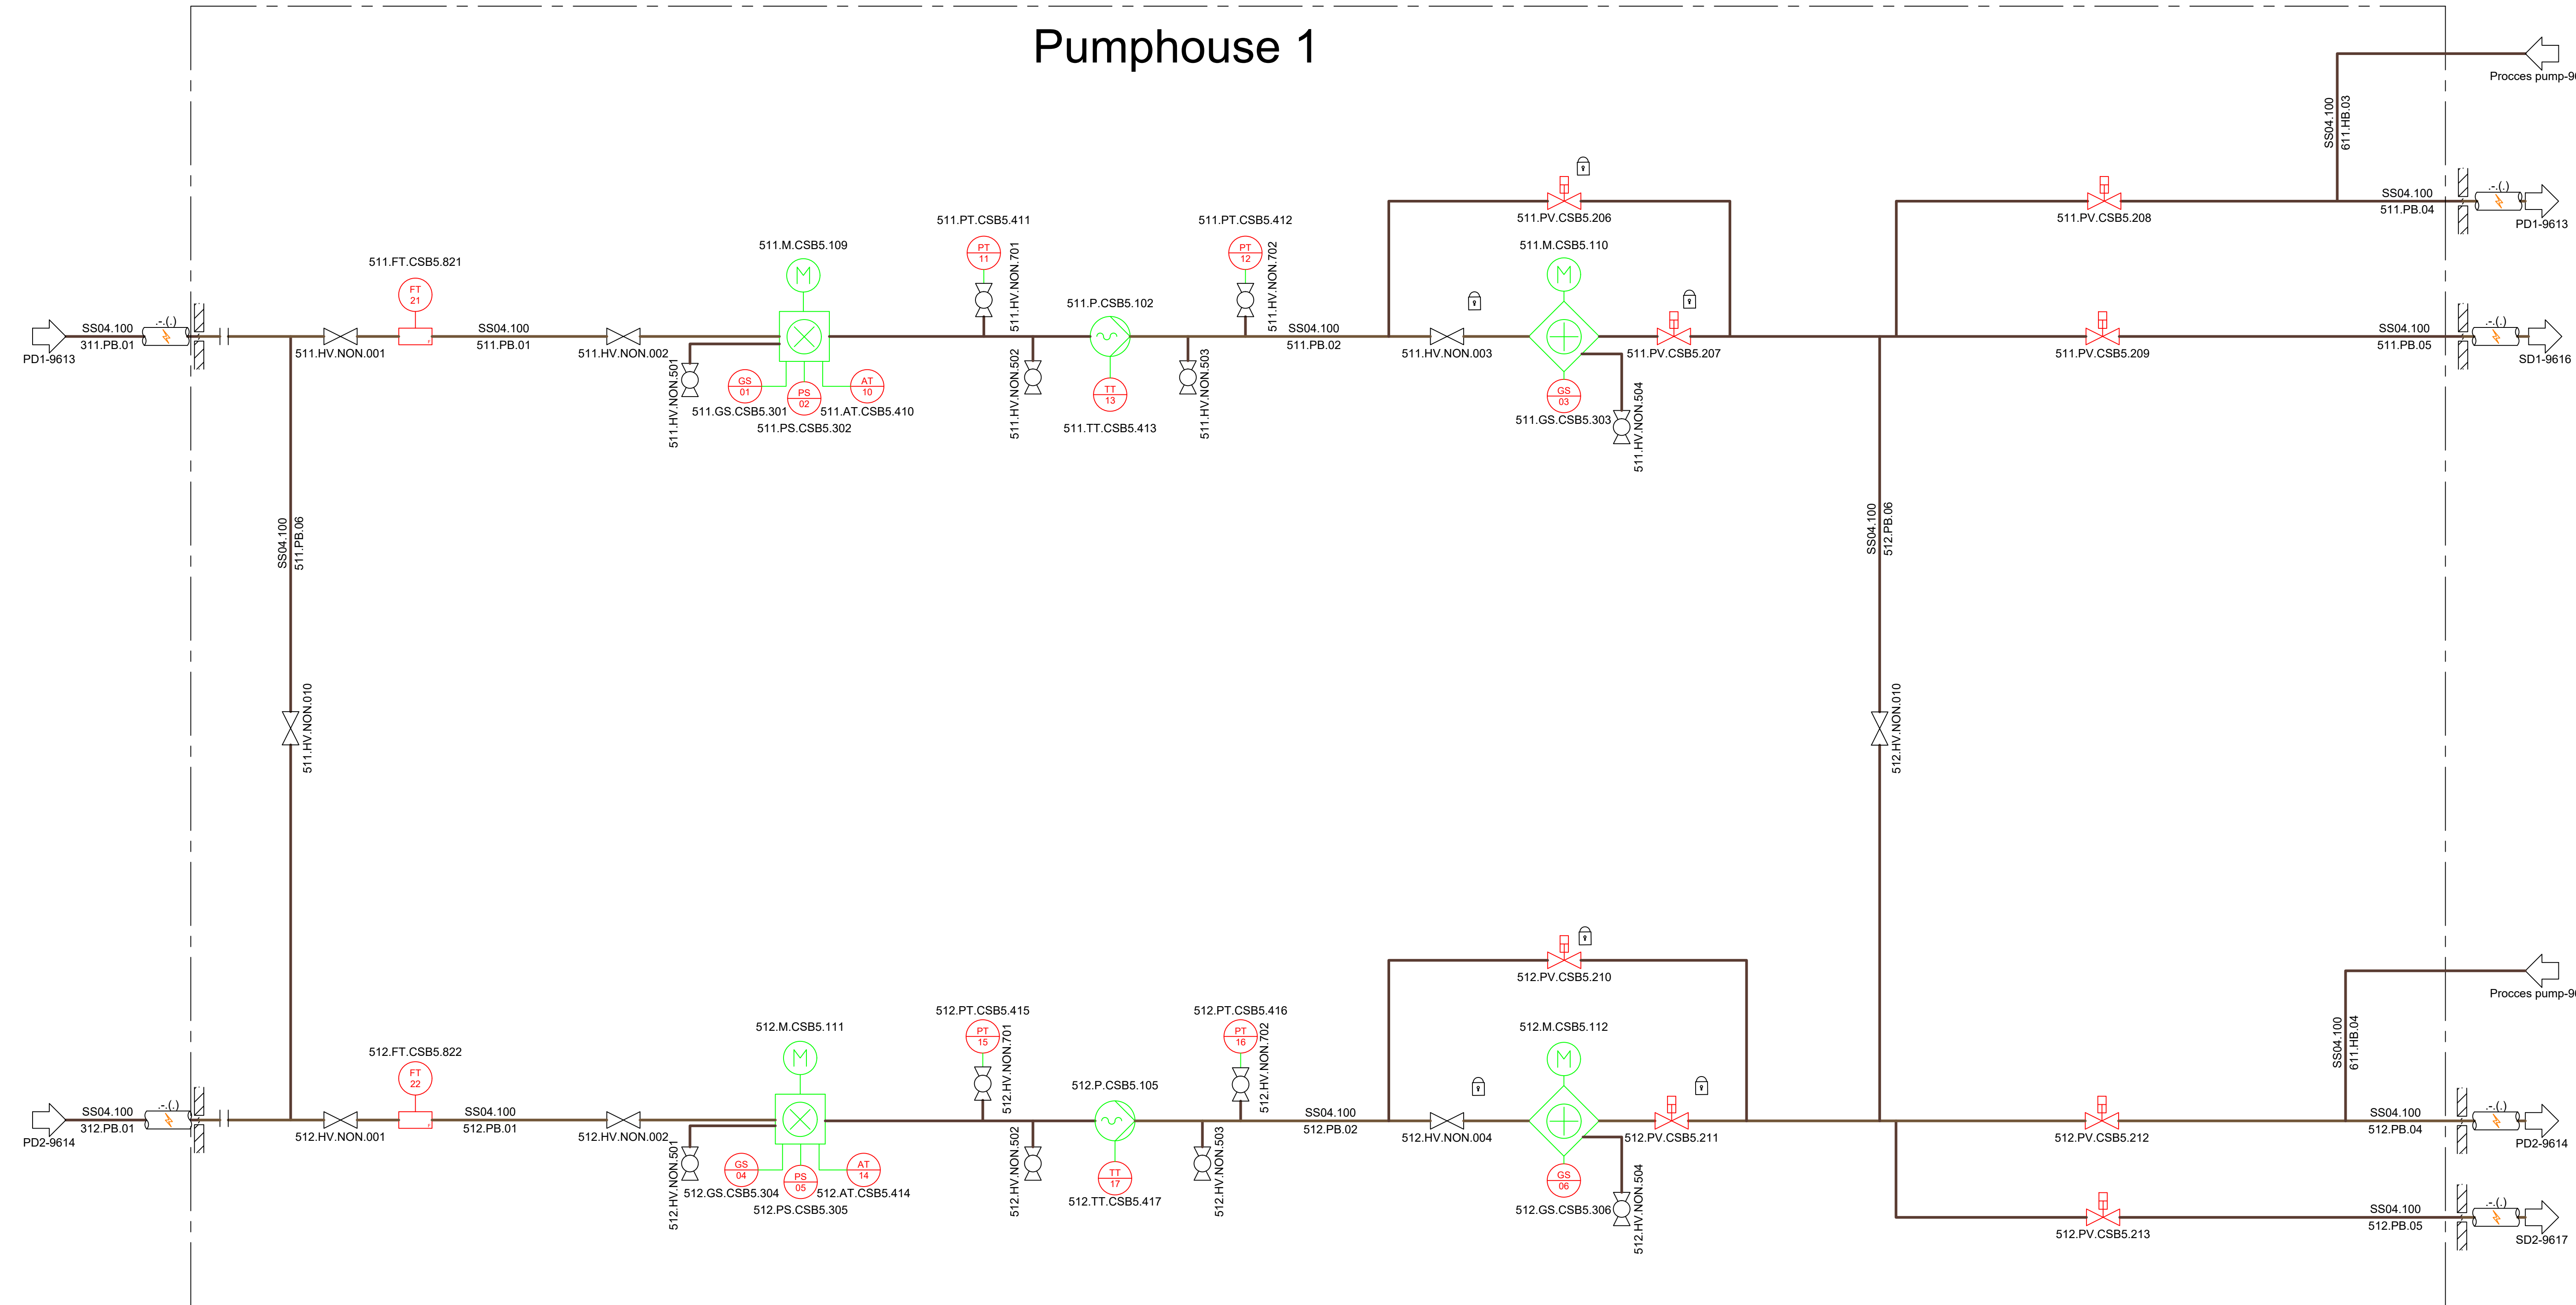


Rev. Nr.:	Rev. Dato:	Rev. Description:	
Builder:	ST1		
Project:	SLK		
Subject:	Disruptor 1 and 2		
	Rev. 2		
Int.: MDC	QC.CM	APP.:	Date: 26-06-2025
LUNDSBY RENEWABLE SOLUTIONS			Lundsby Renewable Solutions A/S, Hjarbækvej 65, 8831 Løgstrup Tlf.: +45 96 49 43 00 Info@lundsby.dk This Drawing is subject to copyright and may not be reproduced without permission from Lundsby Renewable Solutions A/S
Project nr.: 1768 Drawing nr.: 9615			FORMAT: A1

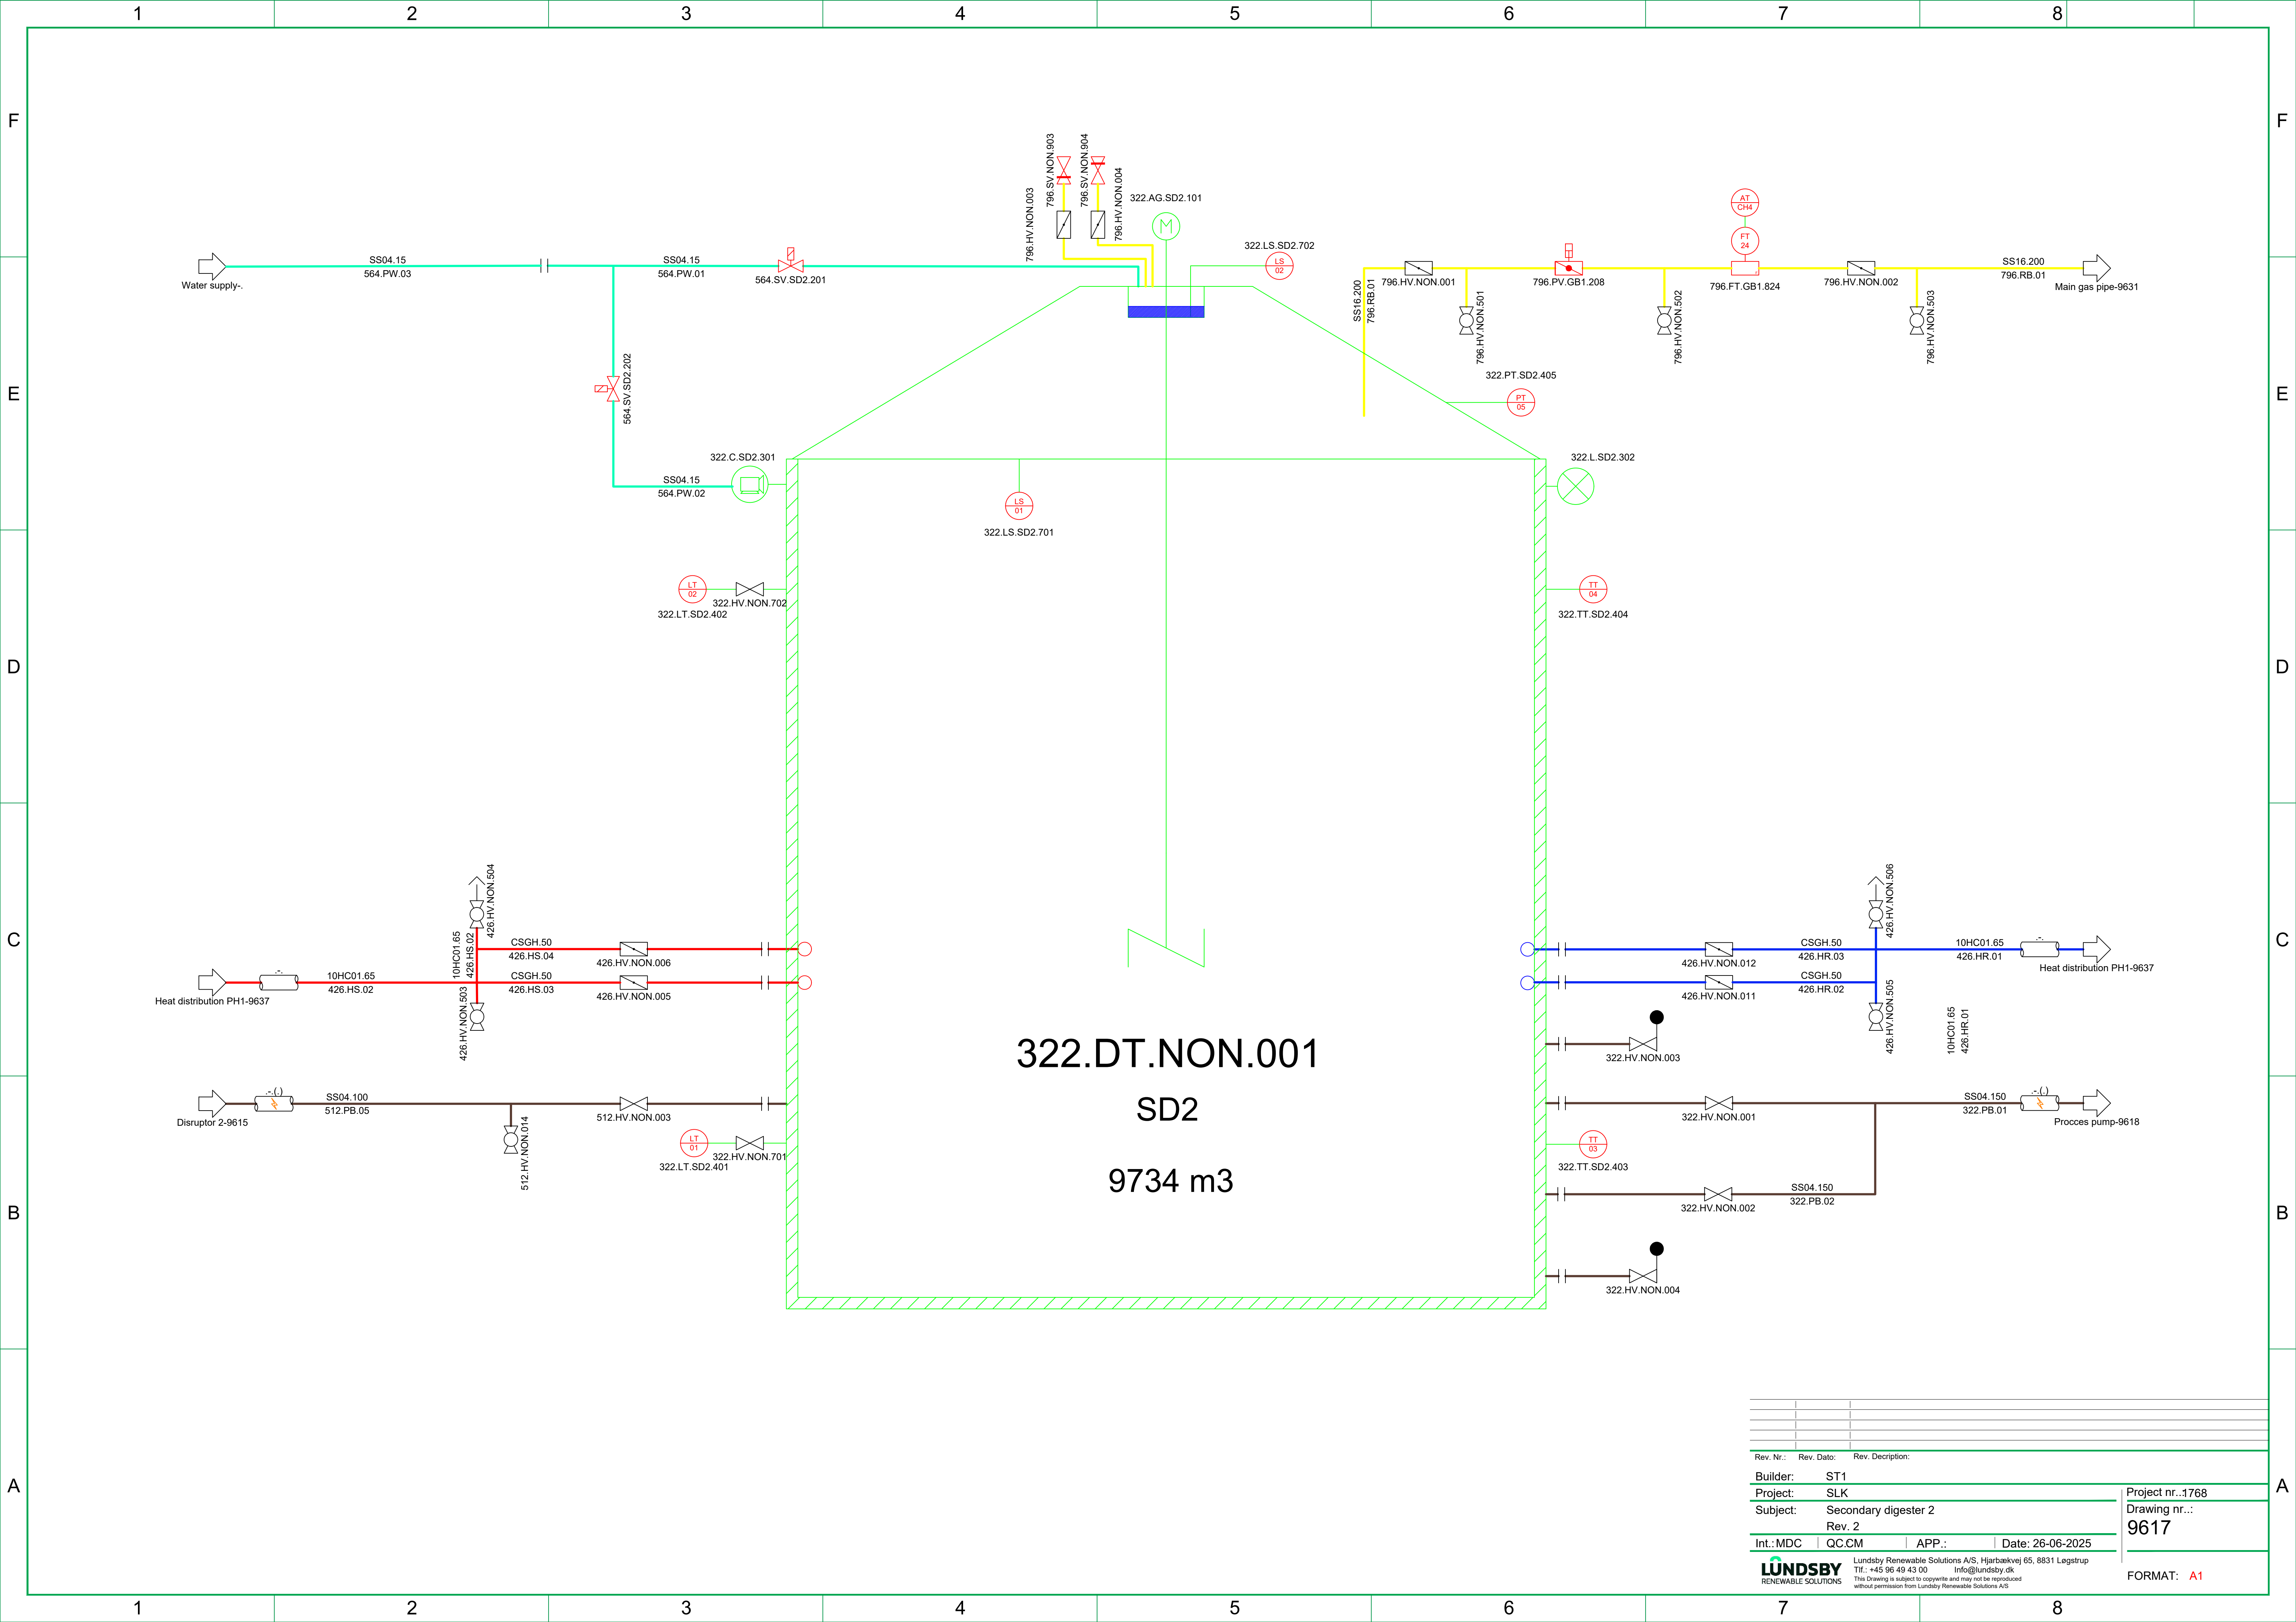


Rev. Nr.:	Rev. Dato:	Rev. Description:
Builder:	ST1	
Project:	SLK	
Subject:	Secondary digester 2	
Rev. 2		
Int.:MDC	QC:CM	APP.:Date: 26-06-2025
LUNDSBYRENEWABLE SOLUTIONS Lundsby Renewable Solutions A/S, Hjarbækvej 65, 8831 Løgstrup Tlf.: +45 96 49 43 00 info@lundsby.dk This drawing is subject to copyright and may not be reproduced without permission from Lundsby Renewable Solutions A/S		
Project nr.:1768 Drawing nr.: 9617		FORMAT: A1

Pumphouse 1

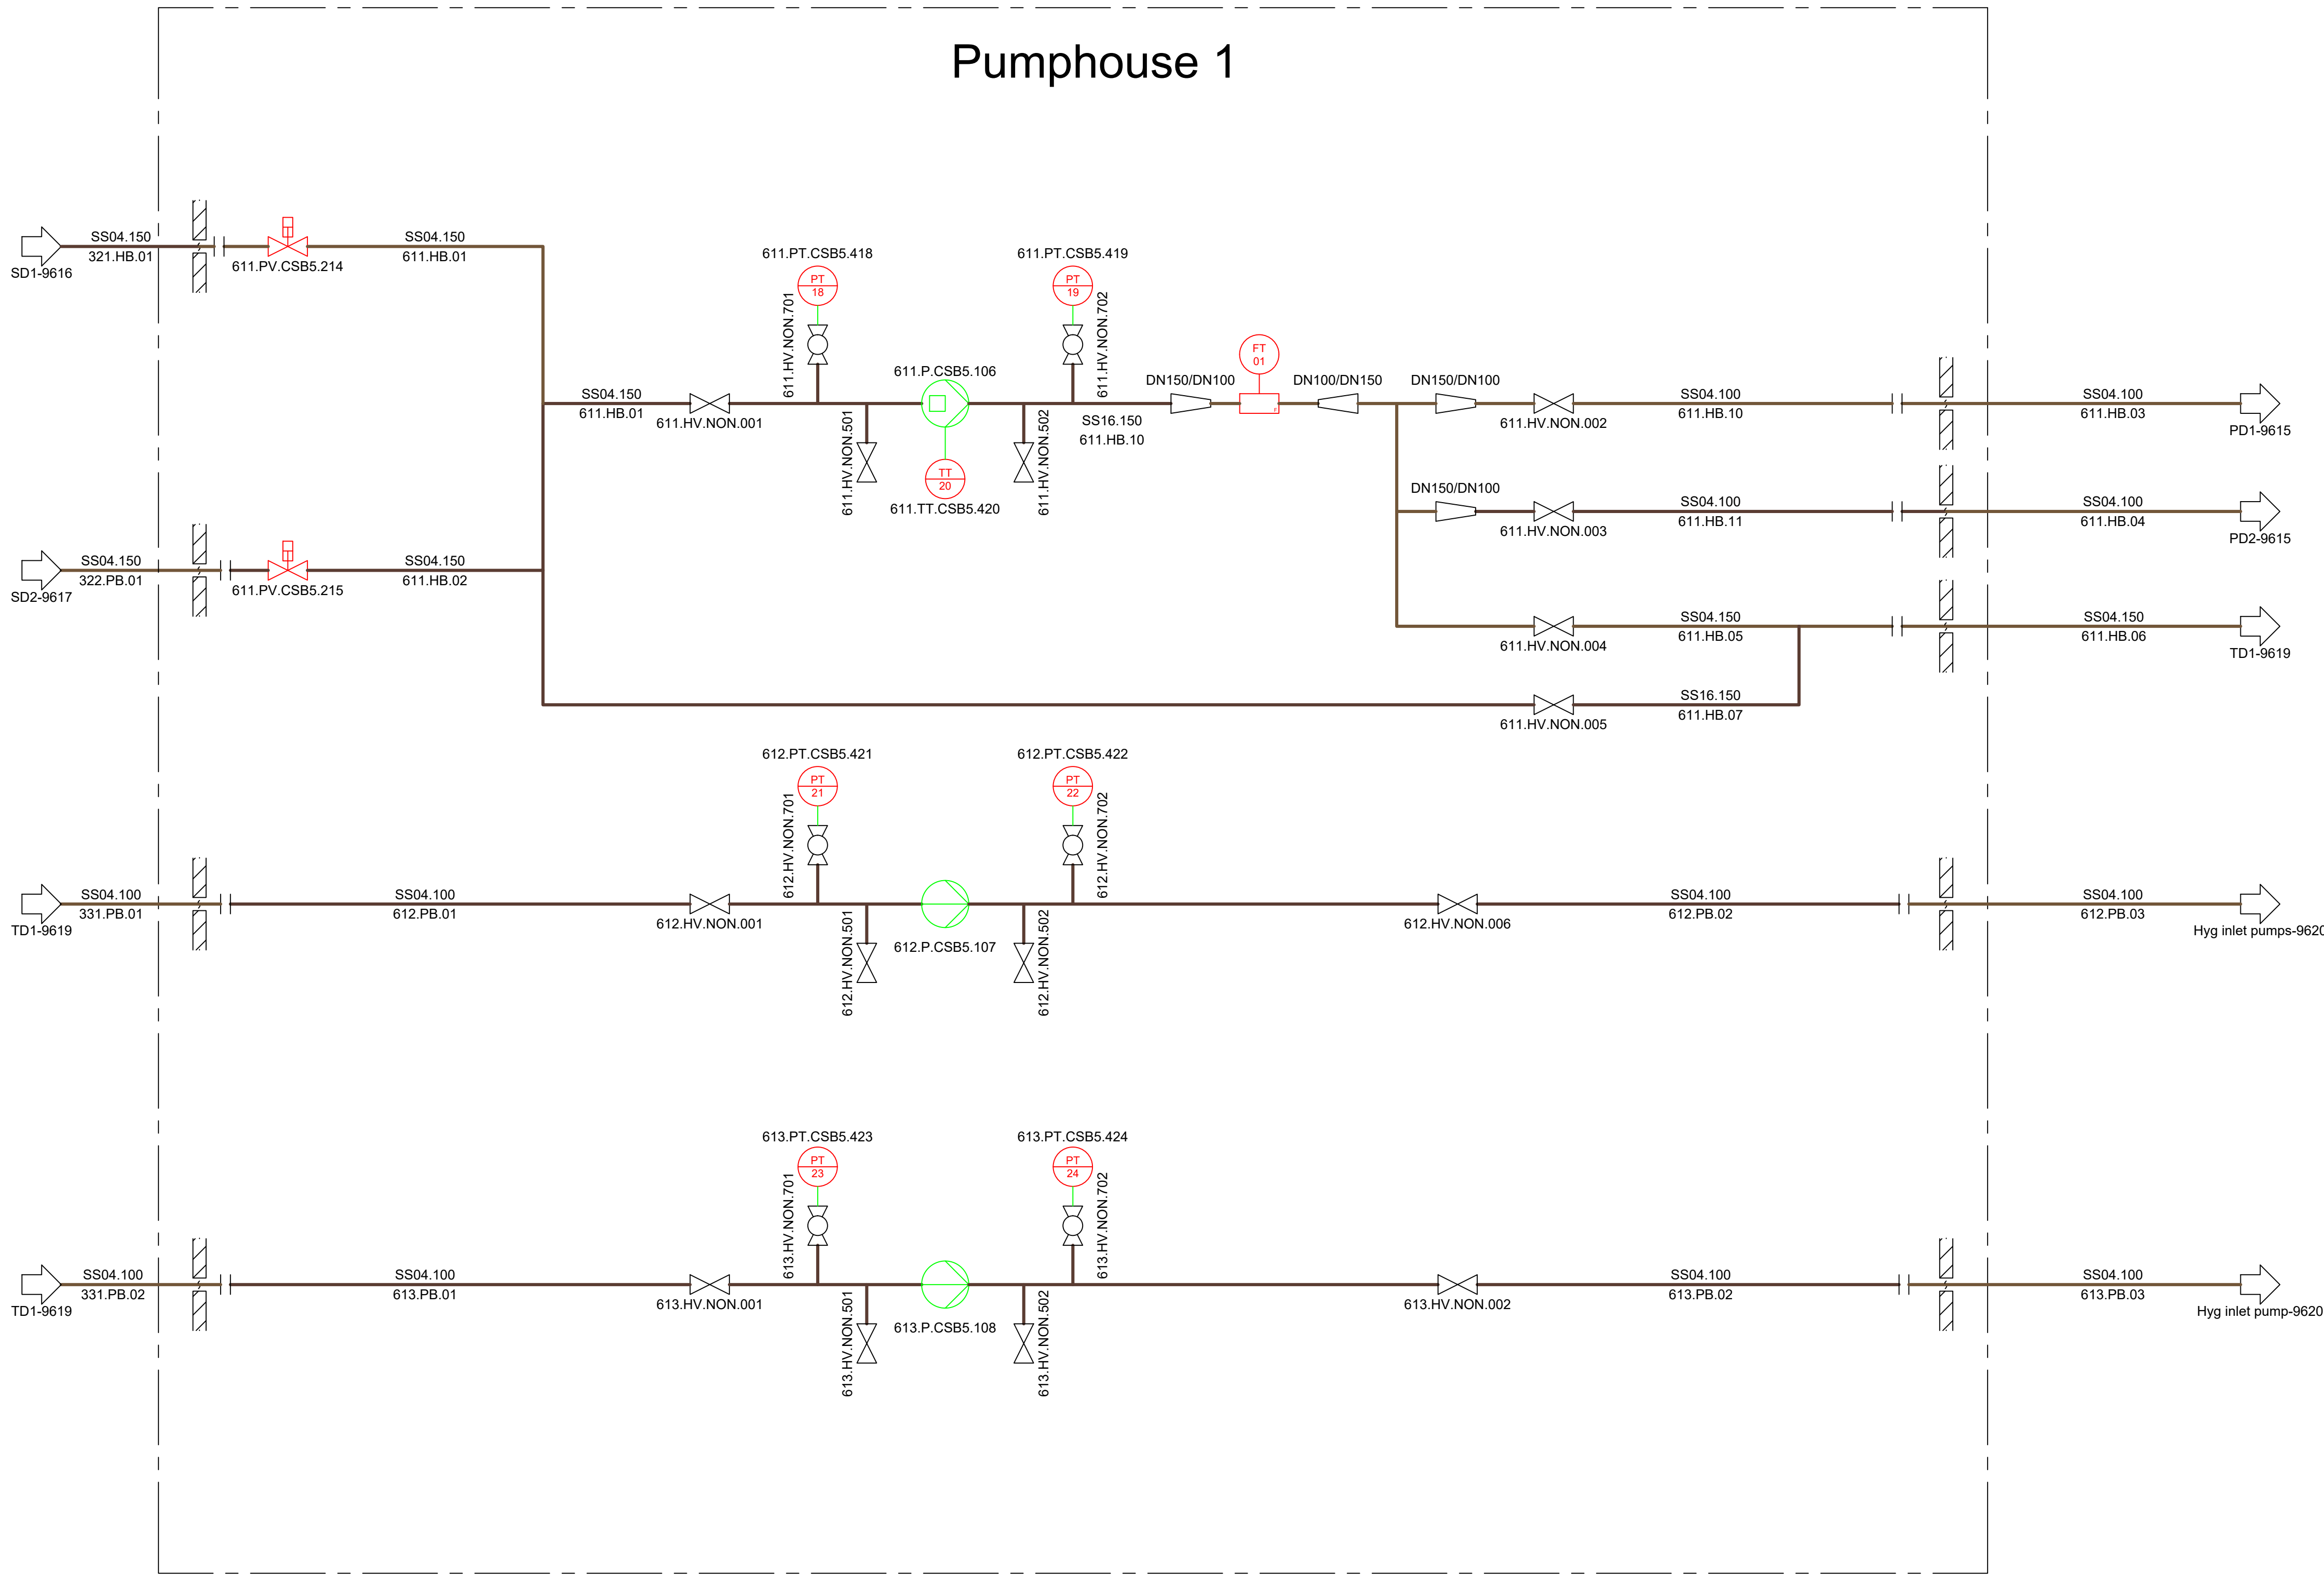


Rev. Nr.:		Rev. Dato:	Rev. Description:
Builder:		ST1	
Project:		SLK	
Subject:		Procces pumps	
Int.:MDC		QC.CM	APP.:
Date: 26-06-2025		Date: 26-06-2025	
LUNDSBY RENEWABLE SOLUTIONS		Lundsby Renewable Solutions A/S, Hjarbækvej 65, 8831 Løgstrup Tlf.: +45 96 49 43 00 Info@lundsby.dk This Drawing is subject to copyright and may not be reproduced without permission from Lundsby Renewable Solutions A/S	
Project nr...1768		Drawing nr...: 9618	
FORMAT: A1			

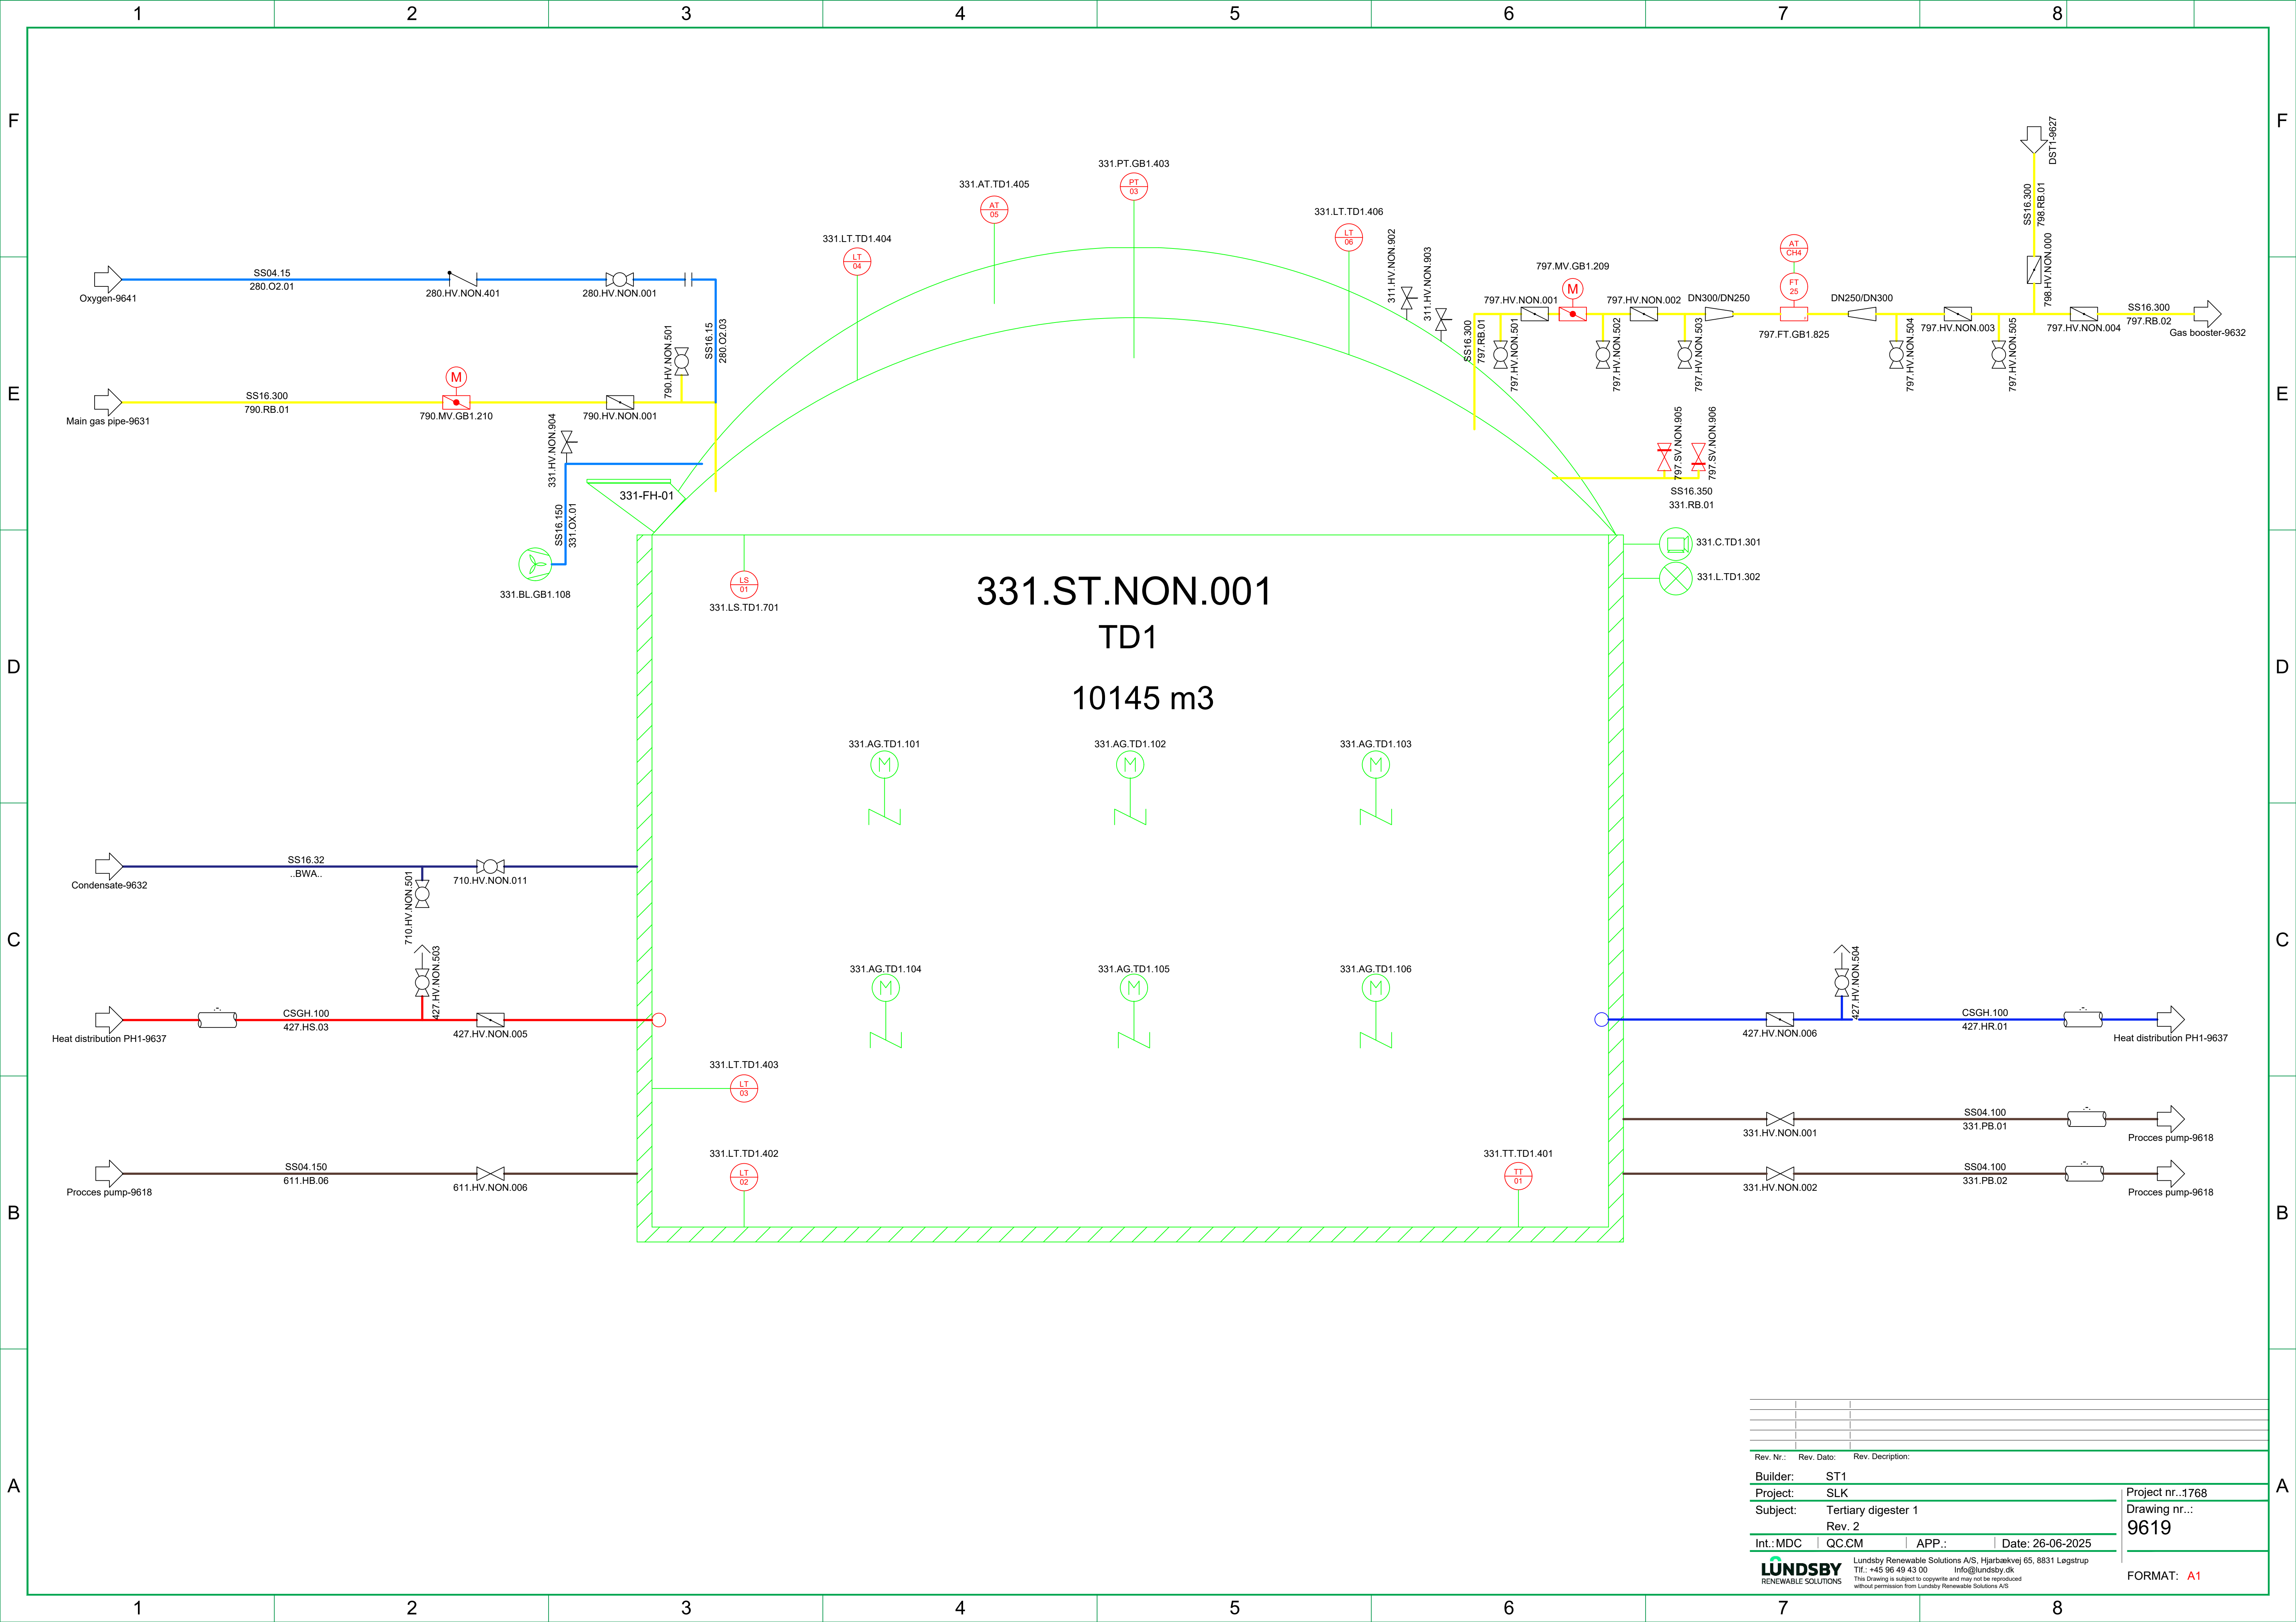

Rev. Nr.:	Rev. Dato:	Rev. Description:
Builder:	ST1	
Project:	SLK	
Subject:	Tertiary digester 1	
Rev. 2		
Int.:MDC	QC:CM	APP.:Date: 26-06-2025
LUNDSBY RENEWABLE SOLUTIONS		
Lundsby Renewable Solutions A/S, Hjarbrækvej 65, 8831 Lægstrup Tlf.: +45 96 49 43 00 Info@lundsby.dk This Drawing is subject to copyright and may not be reproduced without permission from Lundsby Renewable Solutions A/S		
Project nr.:1768 Drawing nr.: 9619		FORMAT: A1

Tech Building

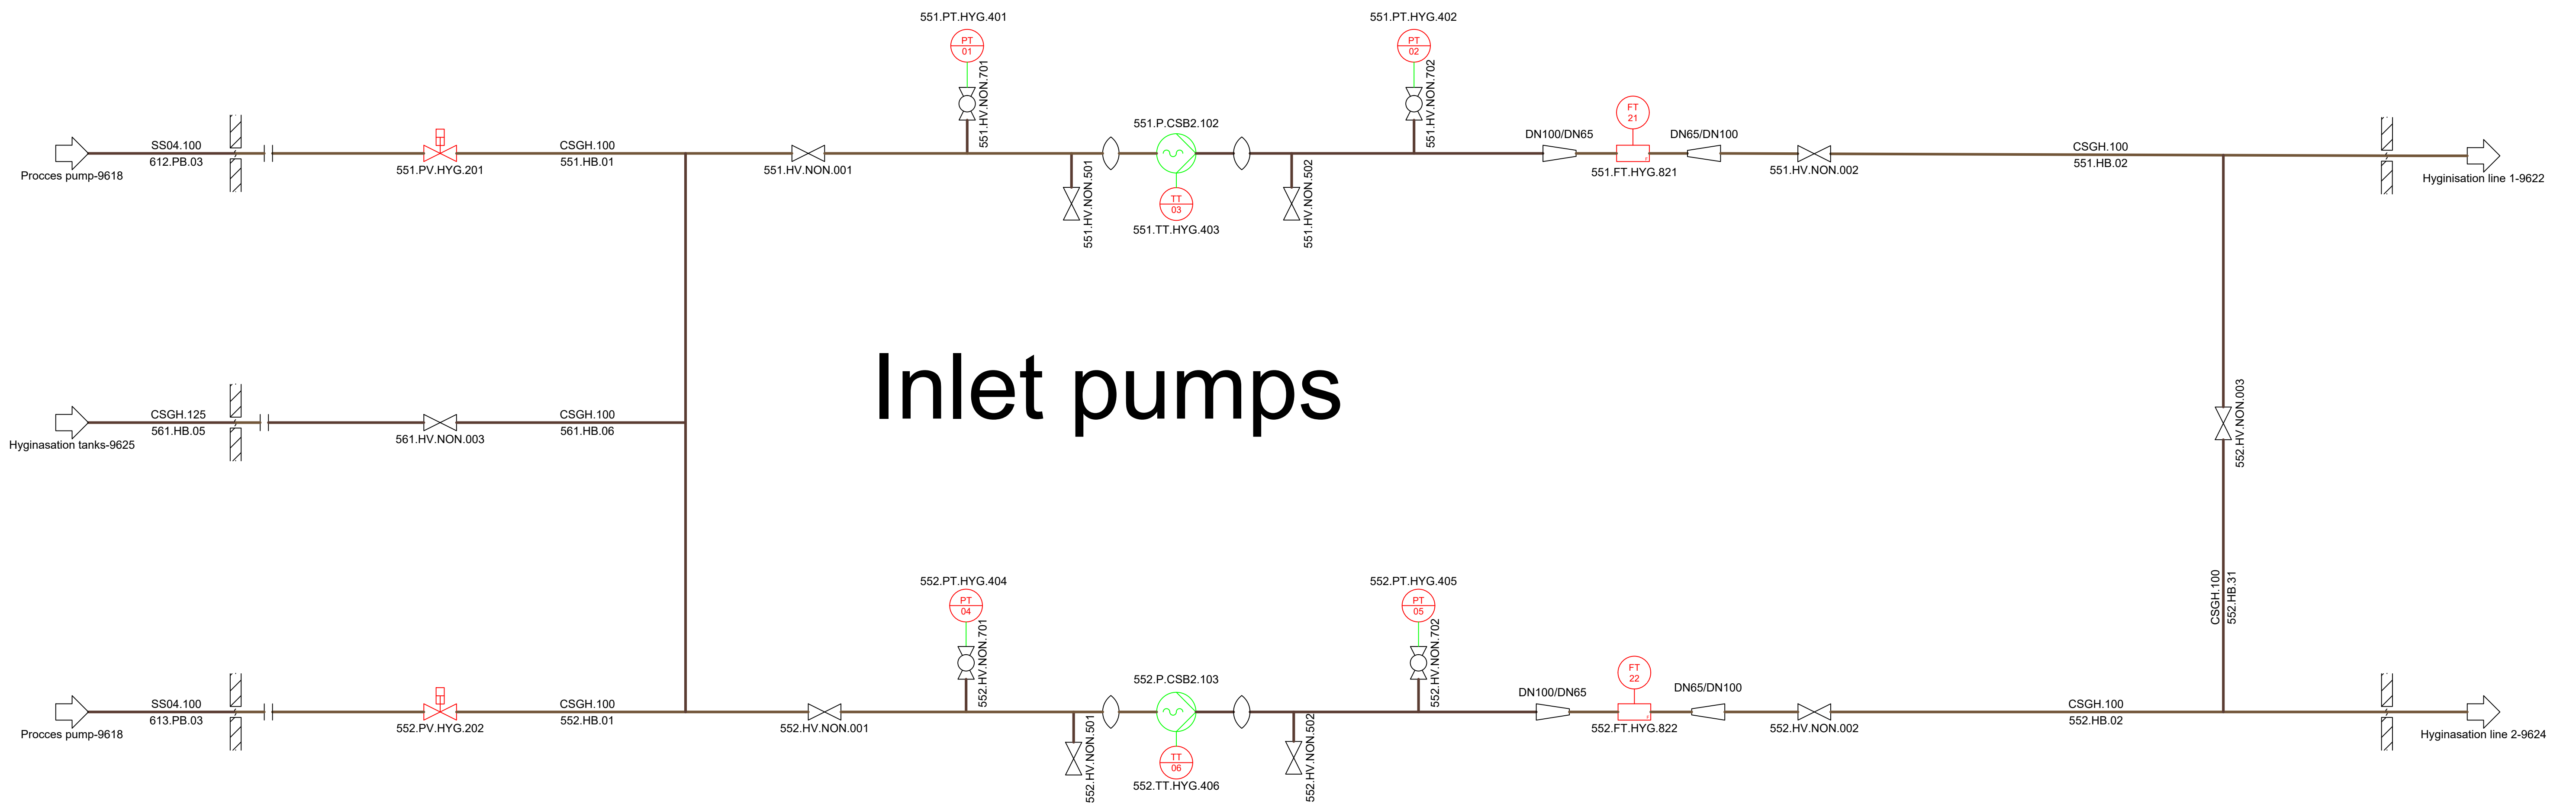


Rev. Nr.:	Rev. Dato:	Rev. Description:
Buider:	ST	
Project:	SLK	
Subject:	Hyginisation inlet pumps	
	Rev. 2	
Int.: MDC	QC.CM	Date: 26-06-2025

Lundsby Renewable Solutions A/S, Hjarbækvej 65, 8831 Legstrup
Tlf.: +45 96 49 43 00 info@lundsby.dk
This Drawing is subject to copyright and may not be reproduced without permission from Lundsbys Renewable Solutions ApS.

Project nr...1768

Drawing nr.:
9620

FORMAT: **A1**

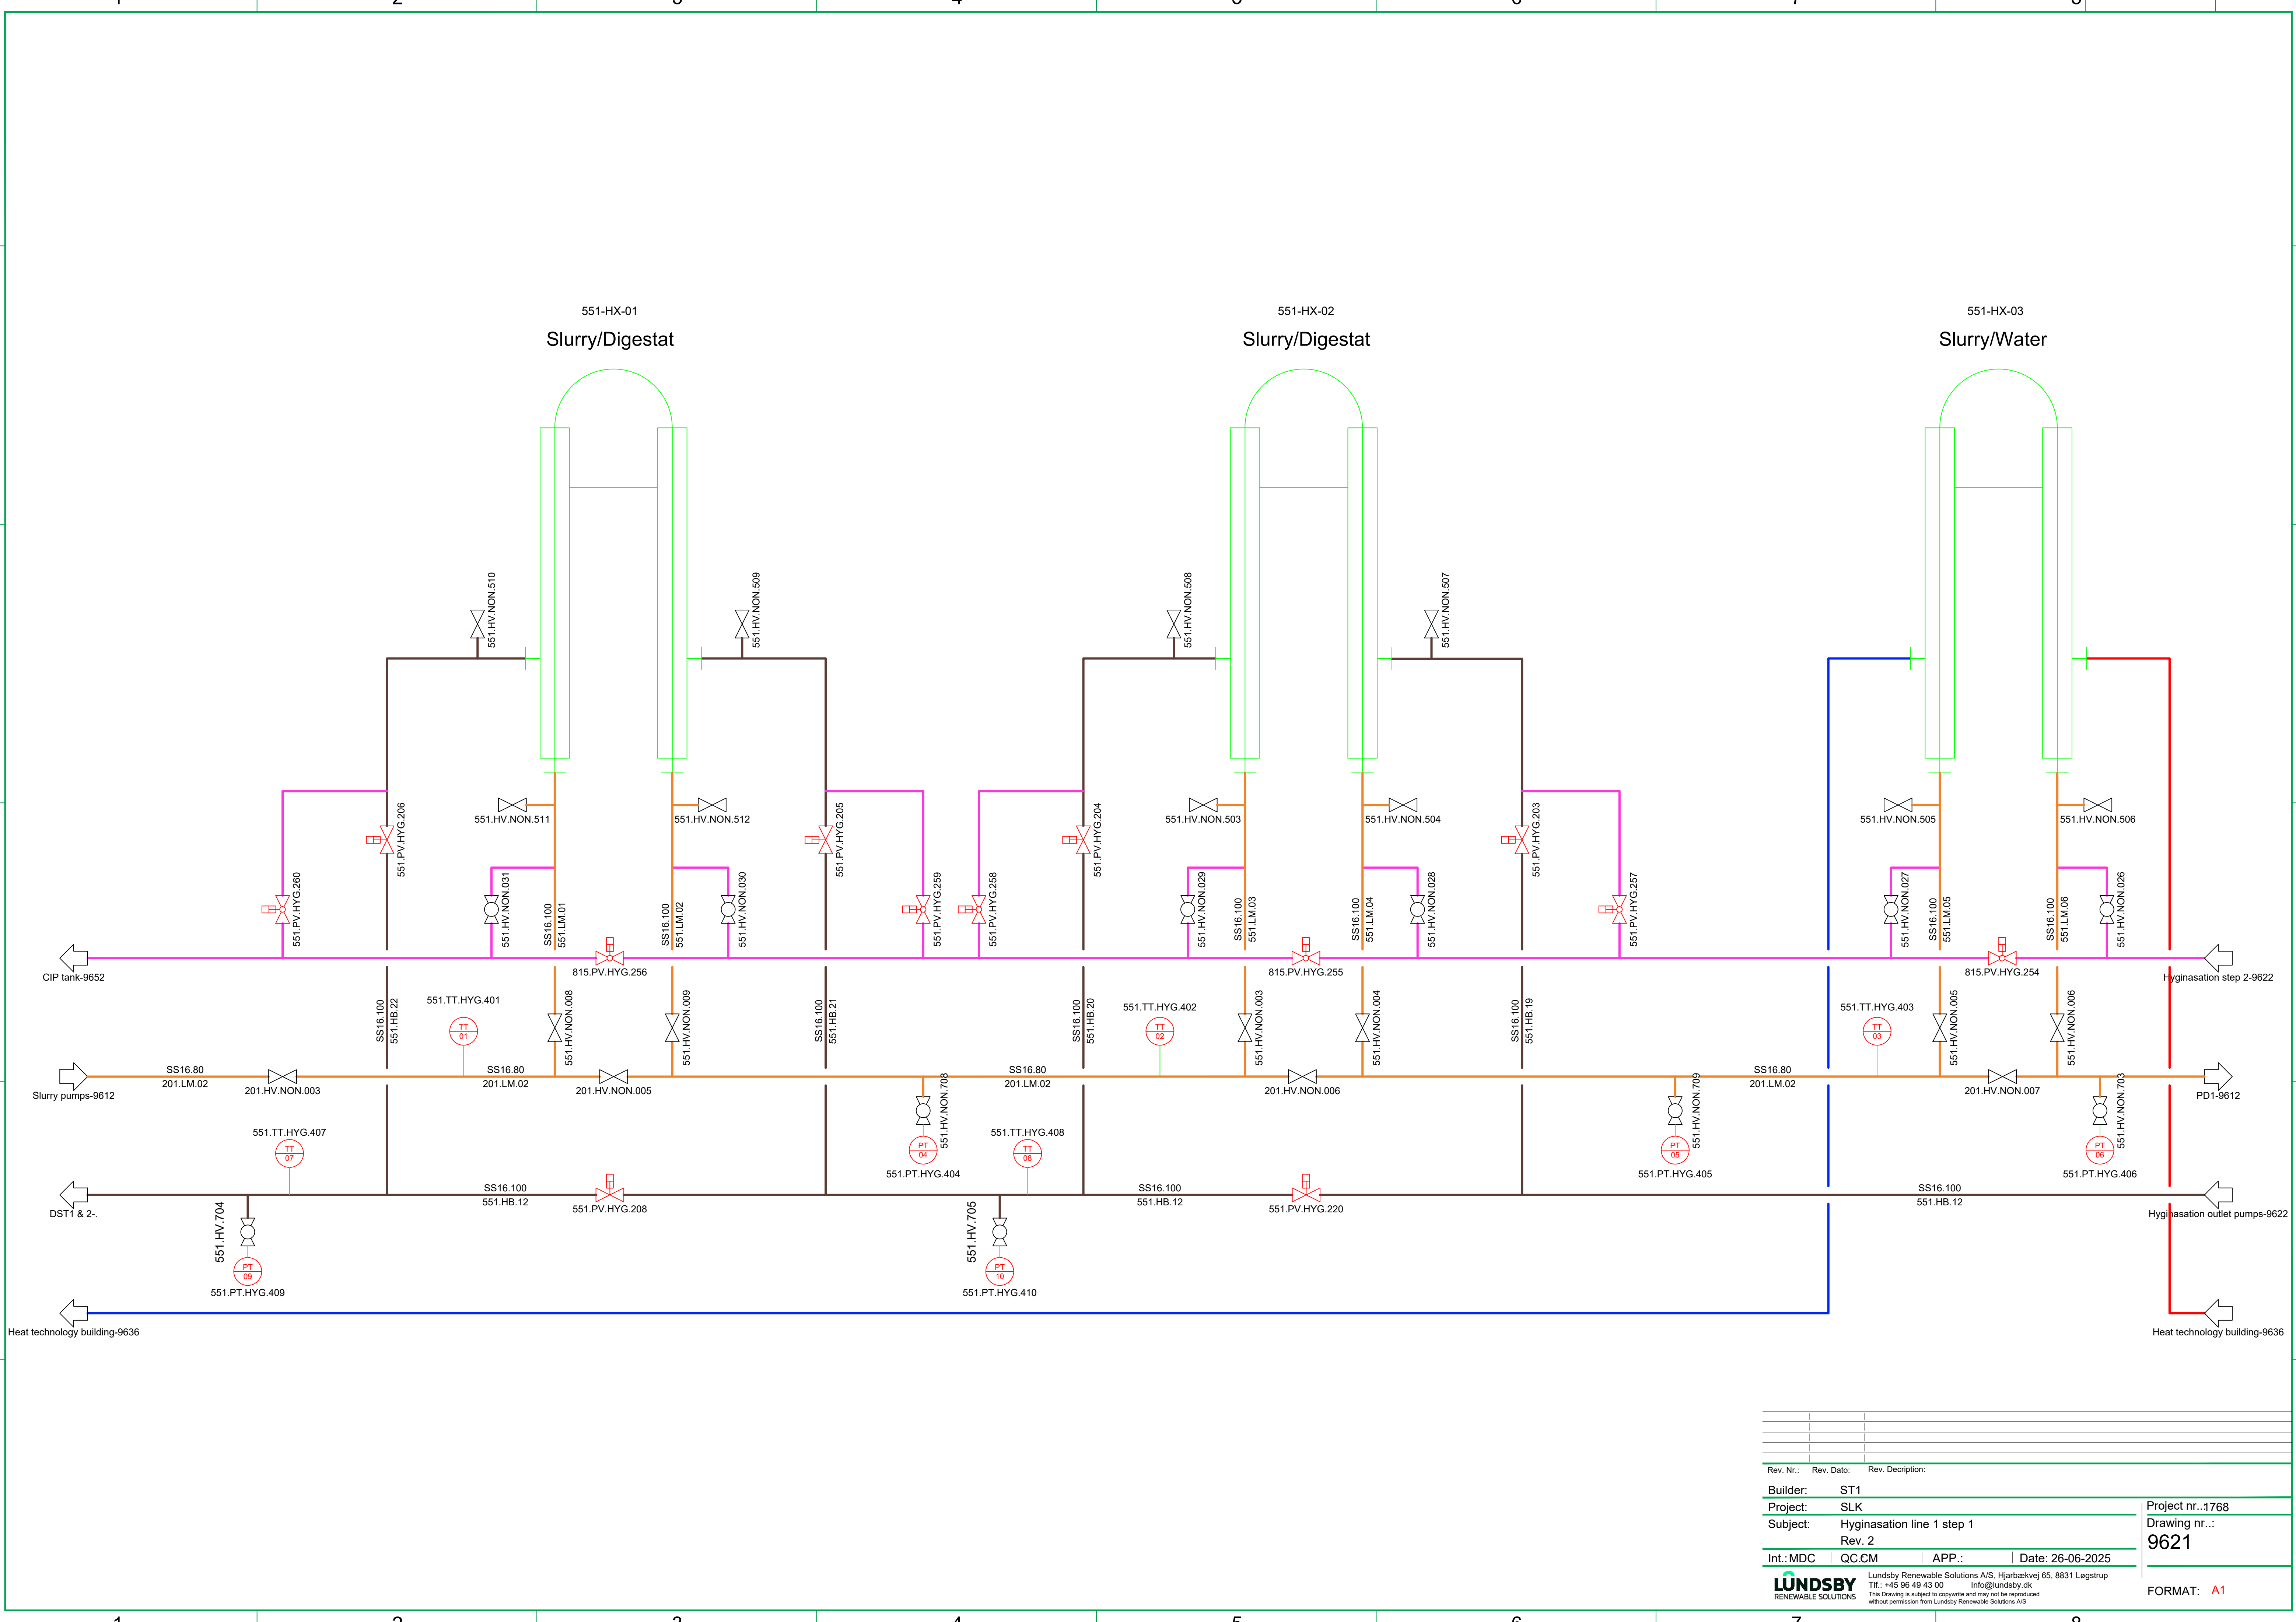


Rev. Nr.:	Rev. Dato:	Rev. Description:

Builder:	ST1
Project:	SLK
Subject:	Hyginasation line 1 step 1
Rev. 2	


Int.:MDC	QC:CM	APP.:	Date: 26-06-2025
----------	-------	-------	------------------


LUNDSBY RENEWABLE SOLUTIONS	Lundsby Renewable Solutions A/S, Hjarbækvej 65, 8831 Lægstrup Tlf.: +45 96 49 43 00 info@lundsby.dk This Drawing is subject to copyright and may not be reproduced without permission from Lundsby Renewable Solutions A/S	Project nr...1768 Drawing nr... 9621
---------------------------------------	--	---

FORMAT: **A1**

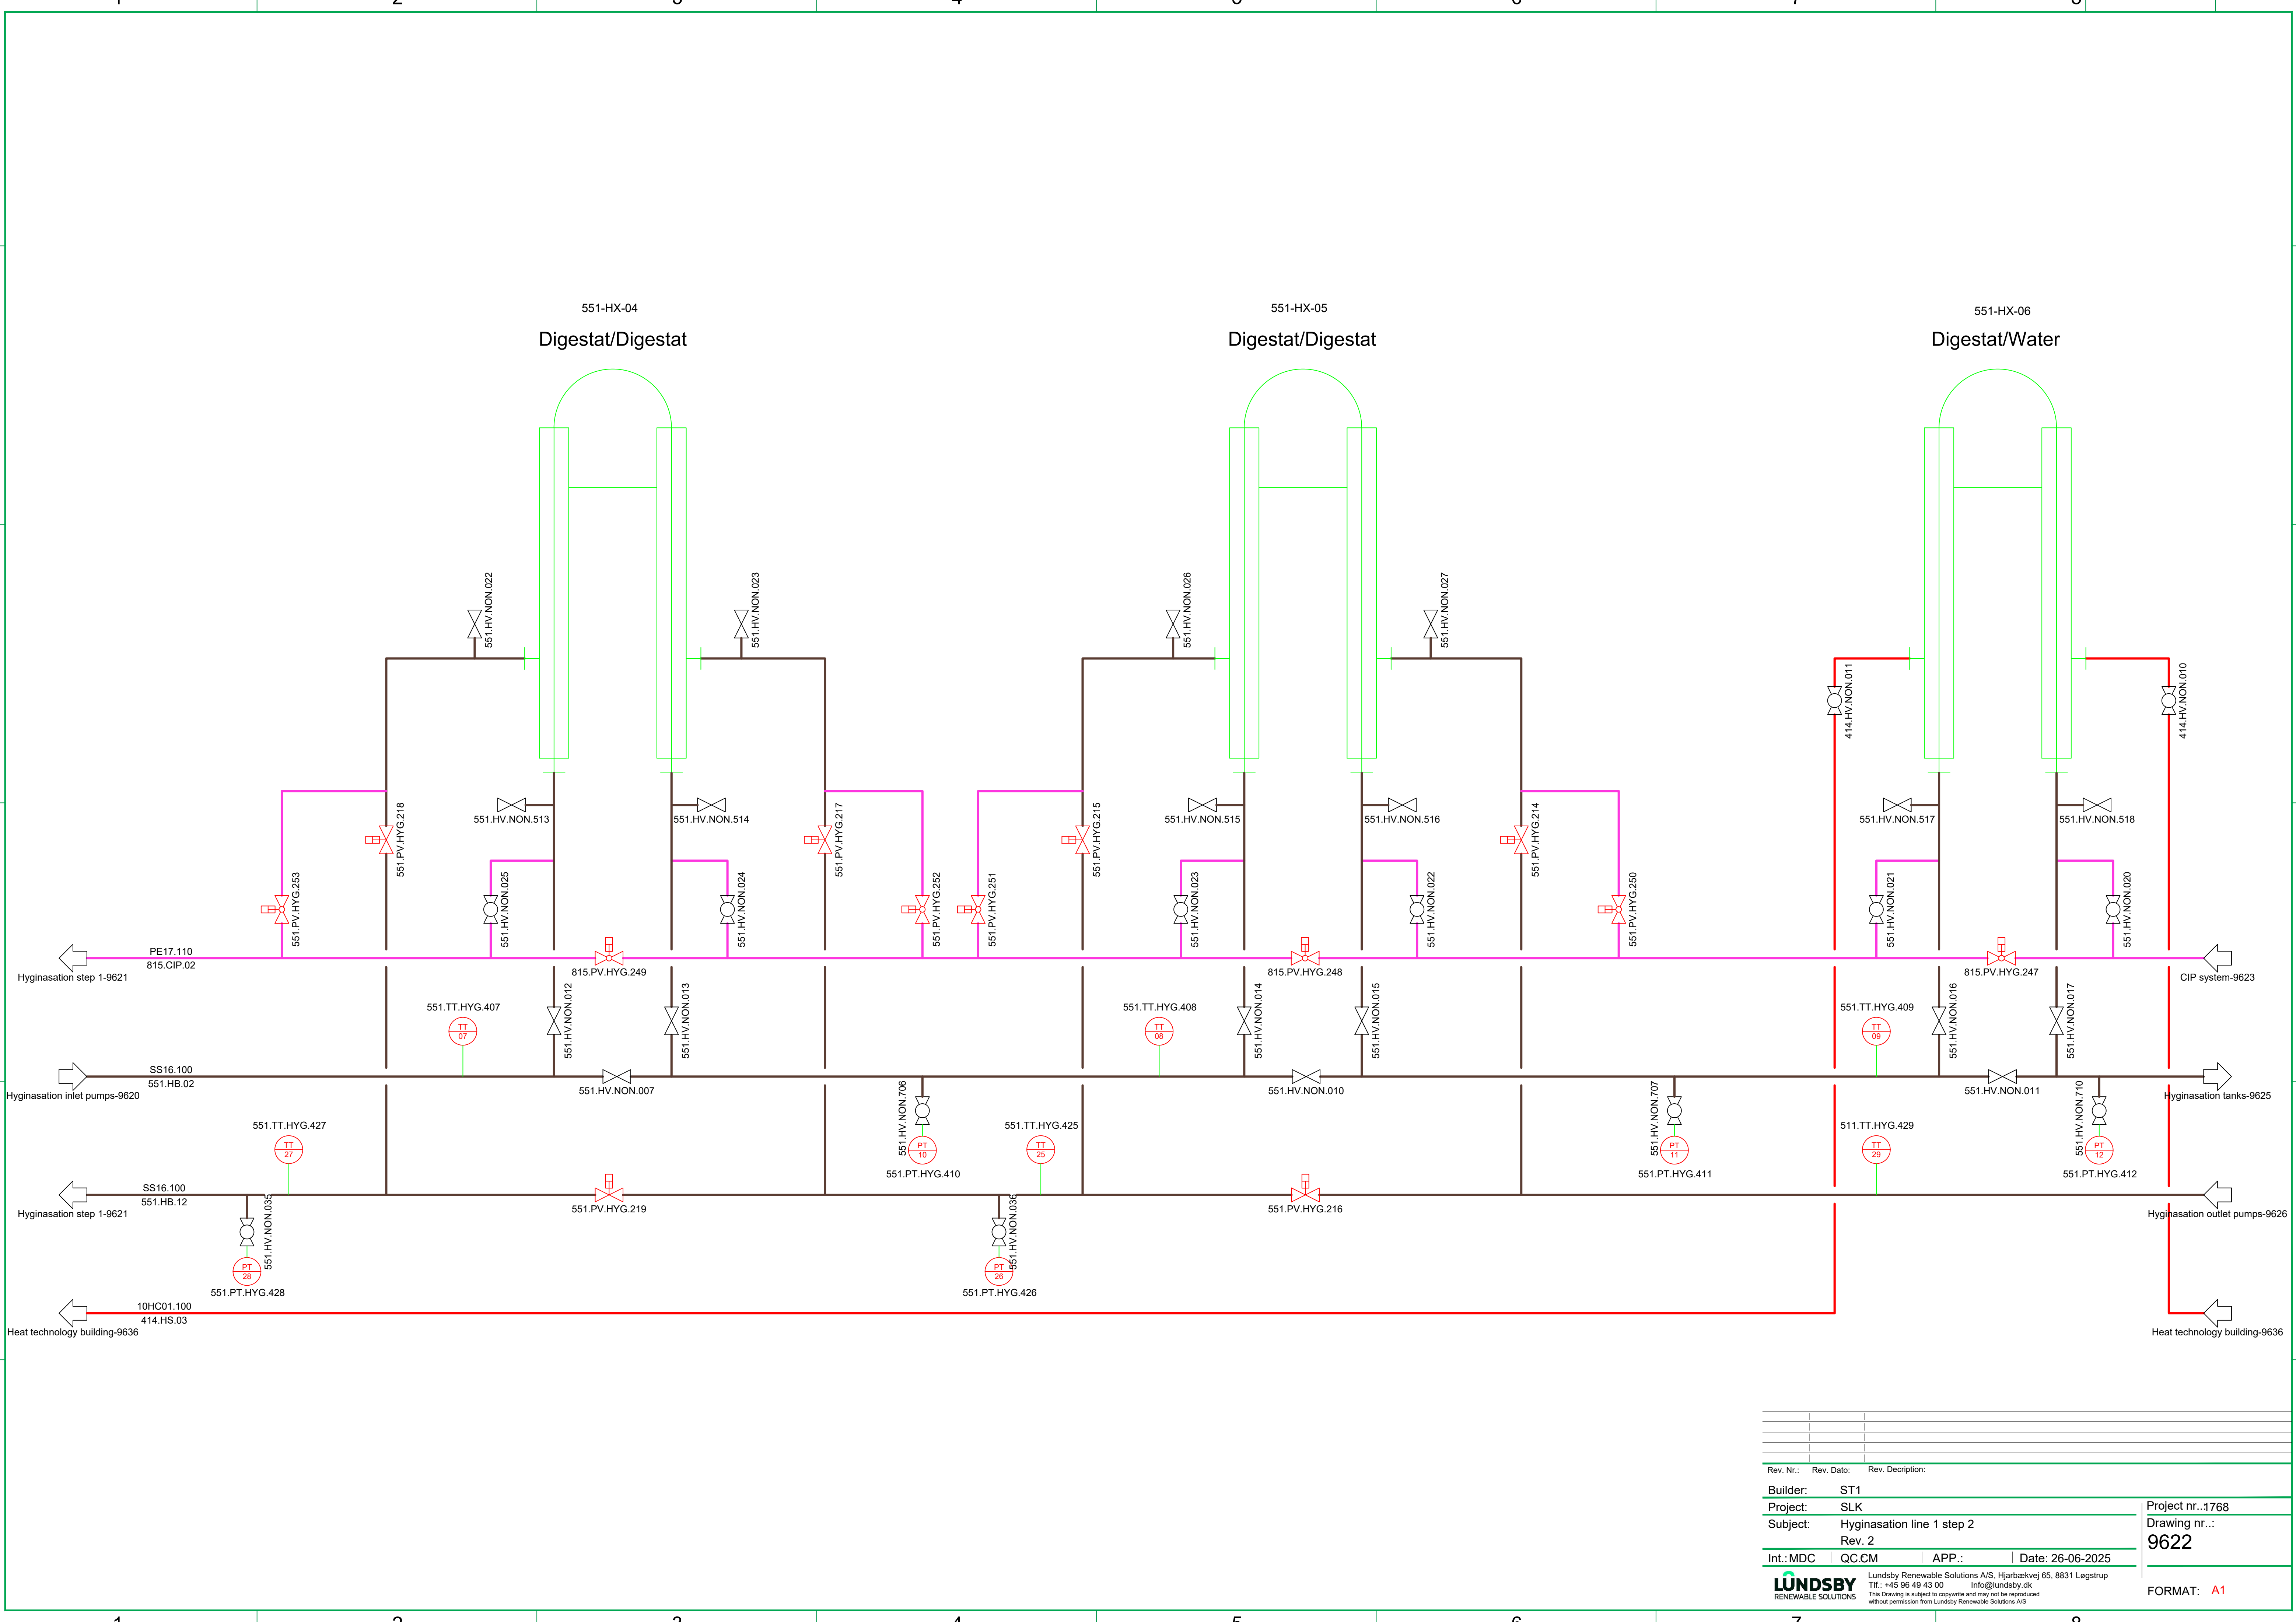


Rev. Nr.: Rev. Dato: Rev. Description:			
Builder: ST1			
Project: SLK			
Subject: Hyginasation line 1 step 2			
Rev. 2			
Int.: MDC	QC: CM	APP.:	Date: 26-06-2025
LUNDSBY RENEWABLE SOLUTIONS			Lundsby Renewable Solutions A/S, Hjarbækvej 65, 8831 Løgstrup Tlf.: +45 96 49 43 00 Info@lundsby.dk This Drawing is subject to copyright and may not be reproduced without permission from Lundsby Renewable Solutions A/S
Project nr.: 1768 Drawing nr.: 9622			FORMAT: A1

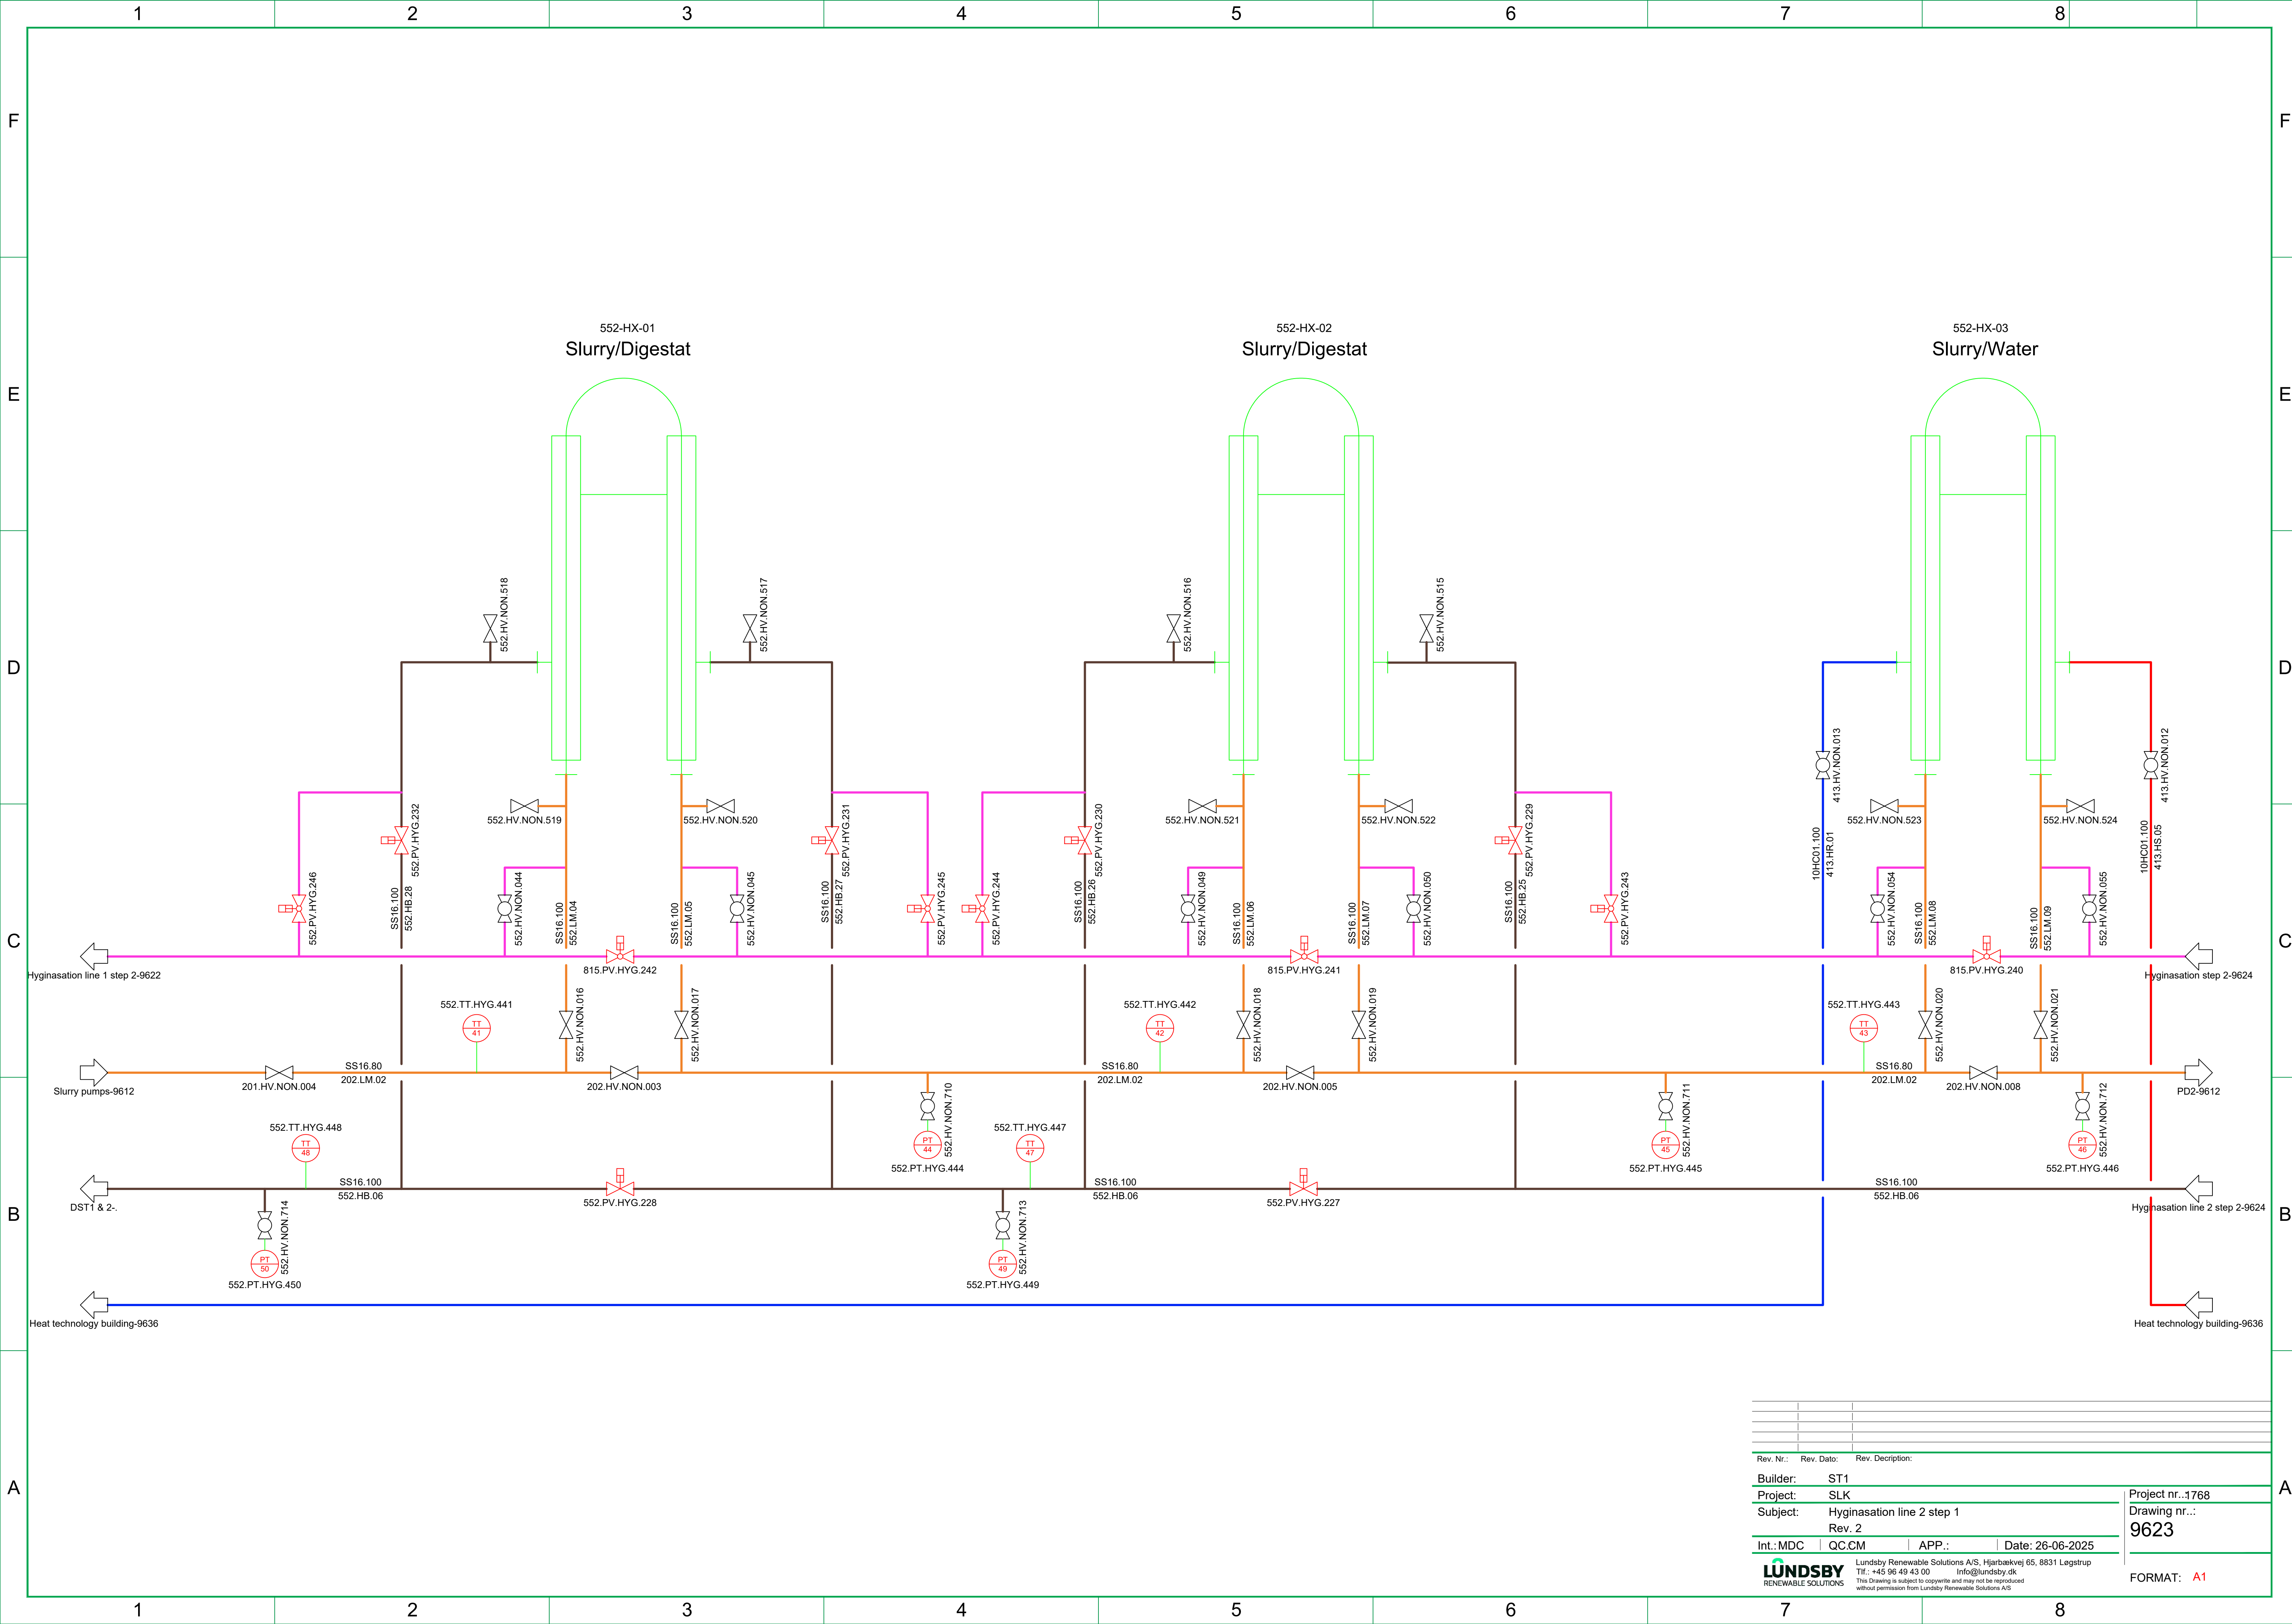

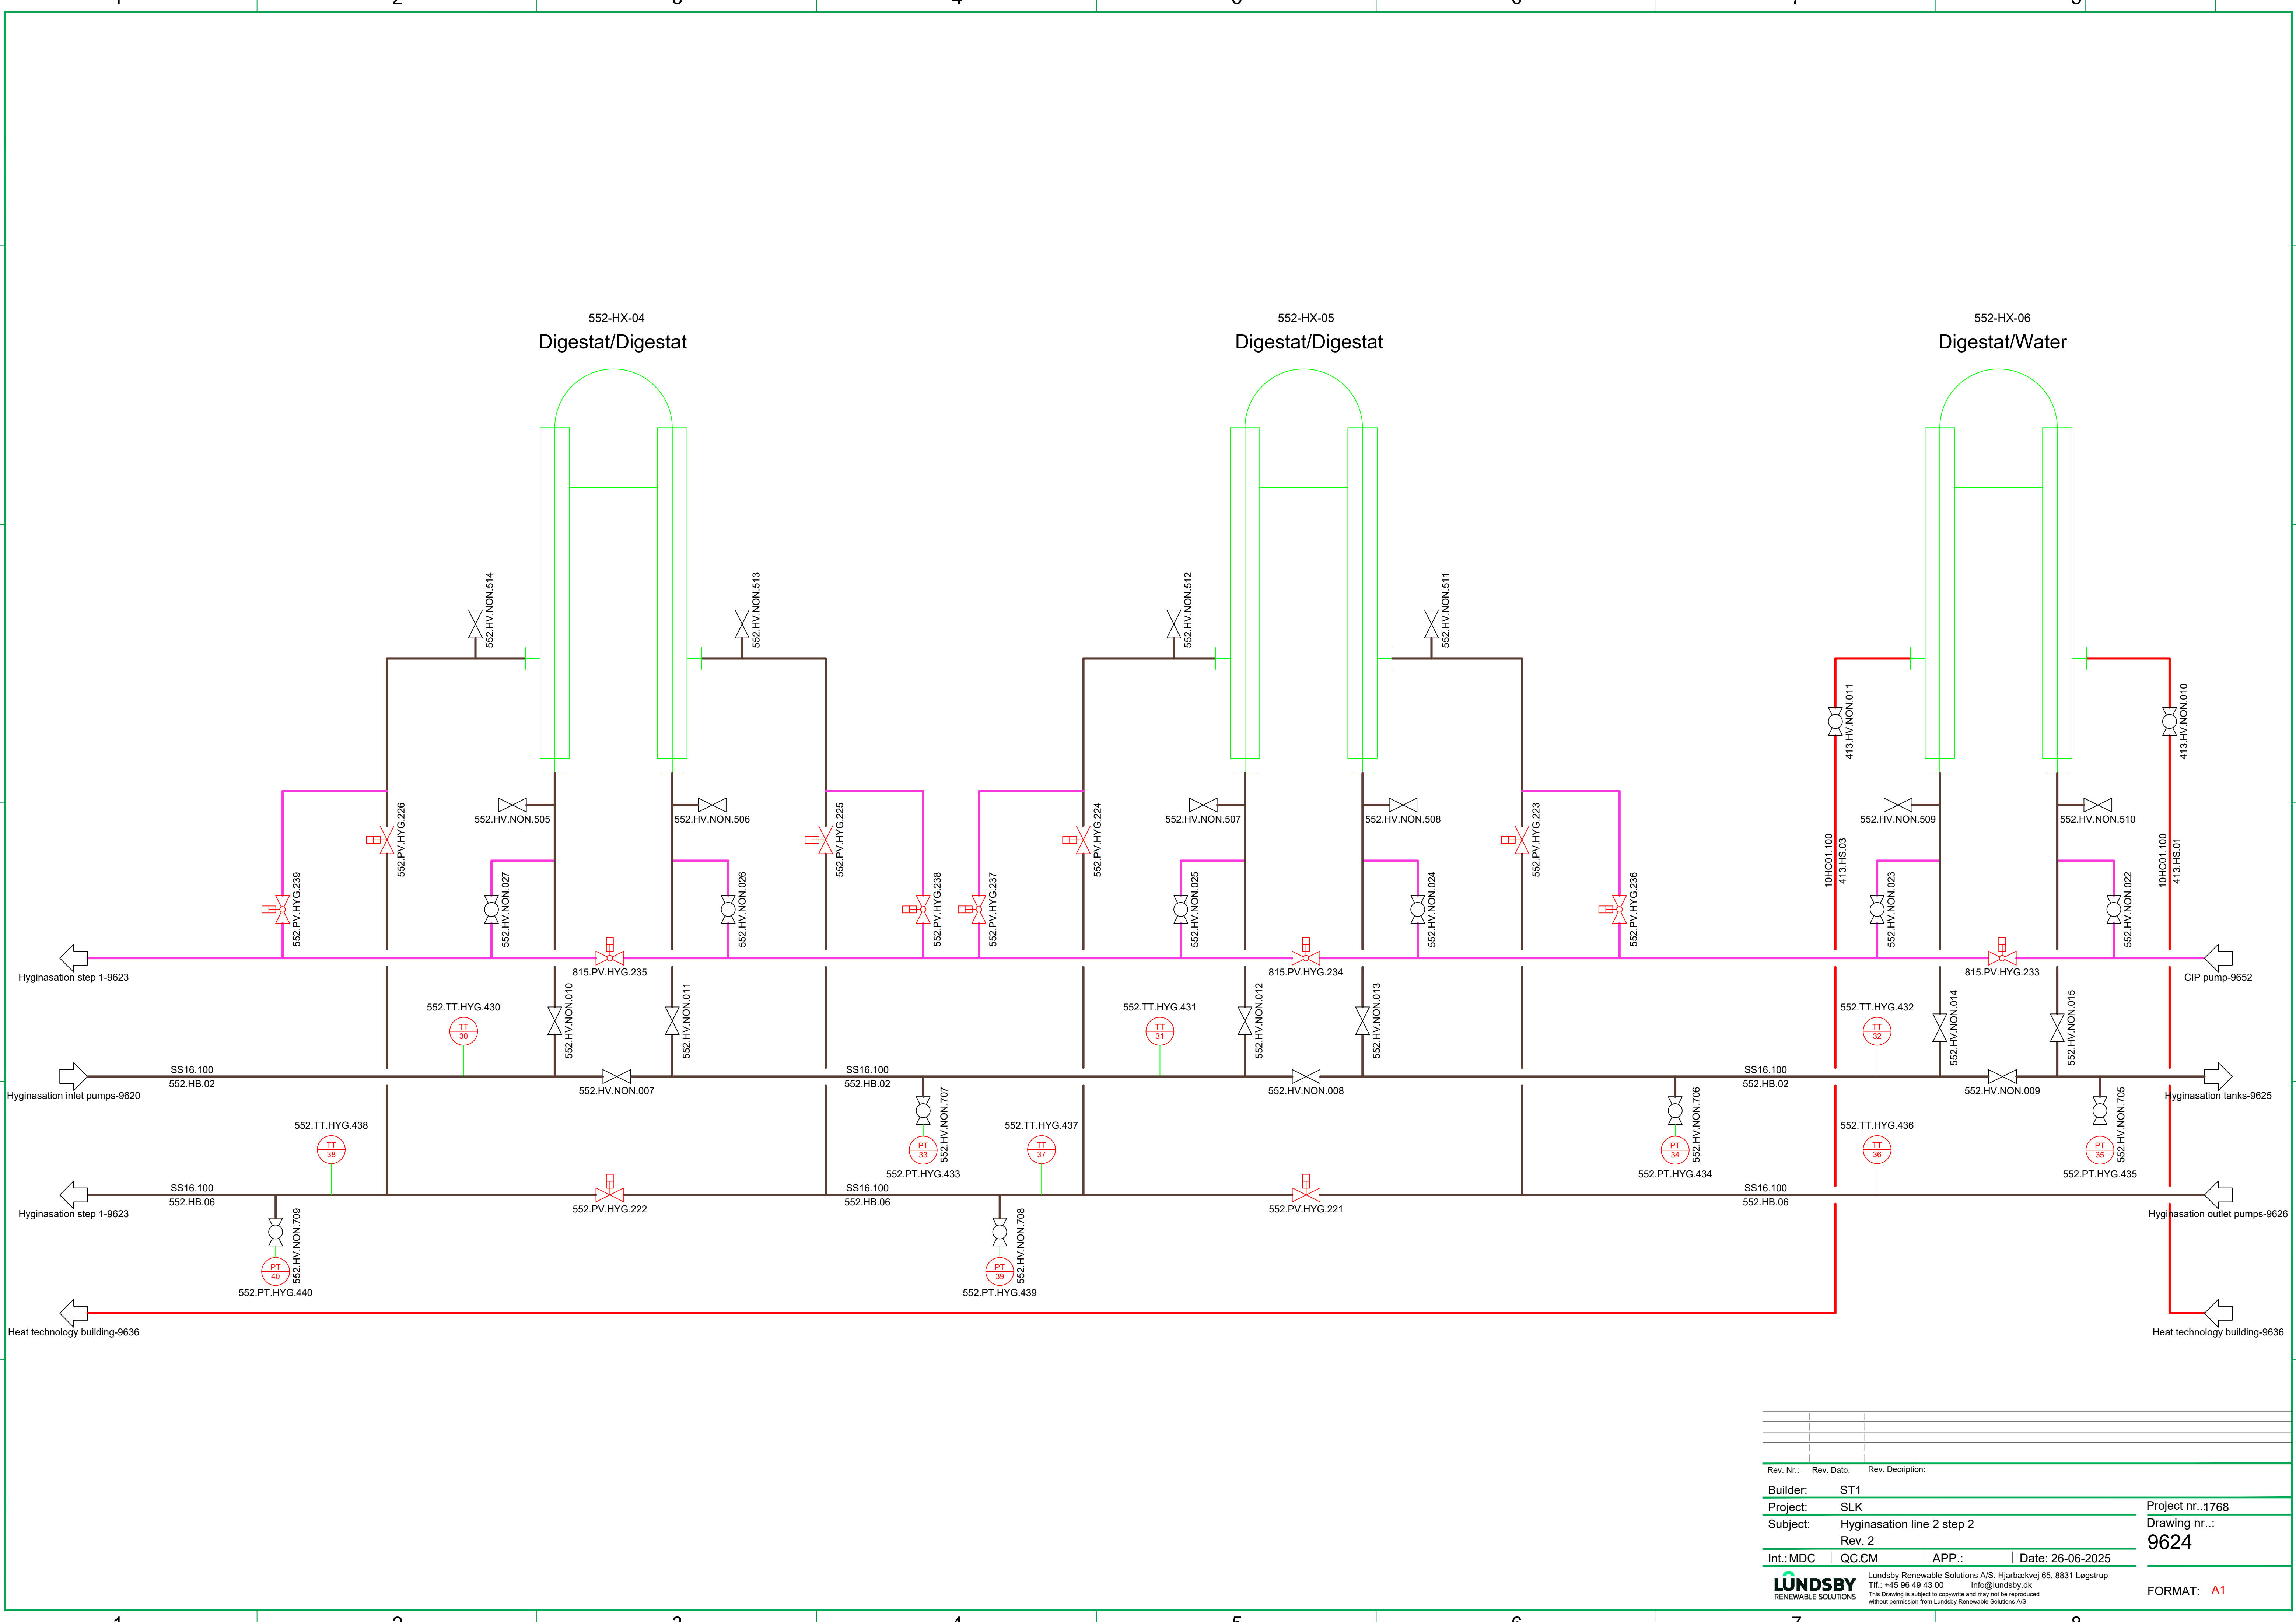


Rev. Nr.:	Rev. Dato:	Rev. Description:
Builder:	ST1	
Project:	SLK	
Subject:	Hyginasation line 2 step 2	
Rev. 2		
Int.:MDC	QC:CM	APP.:Date: 26-06-2025
LUNDSBY RENEWABLE SOLUTIONS		
Lundsby Renewable Solutions A/S, Hjarbrækvej 65, 8831 Lægstrup Tlf.: +45 96 49 43 00 Info@lundsby.dk This Drawing is subject to copyright and may not be reproduced without permission from Lundsby Renewable Solutions A/S		
Project nr...1768 Drawing nr... 9624		FORMAT: A1

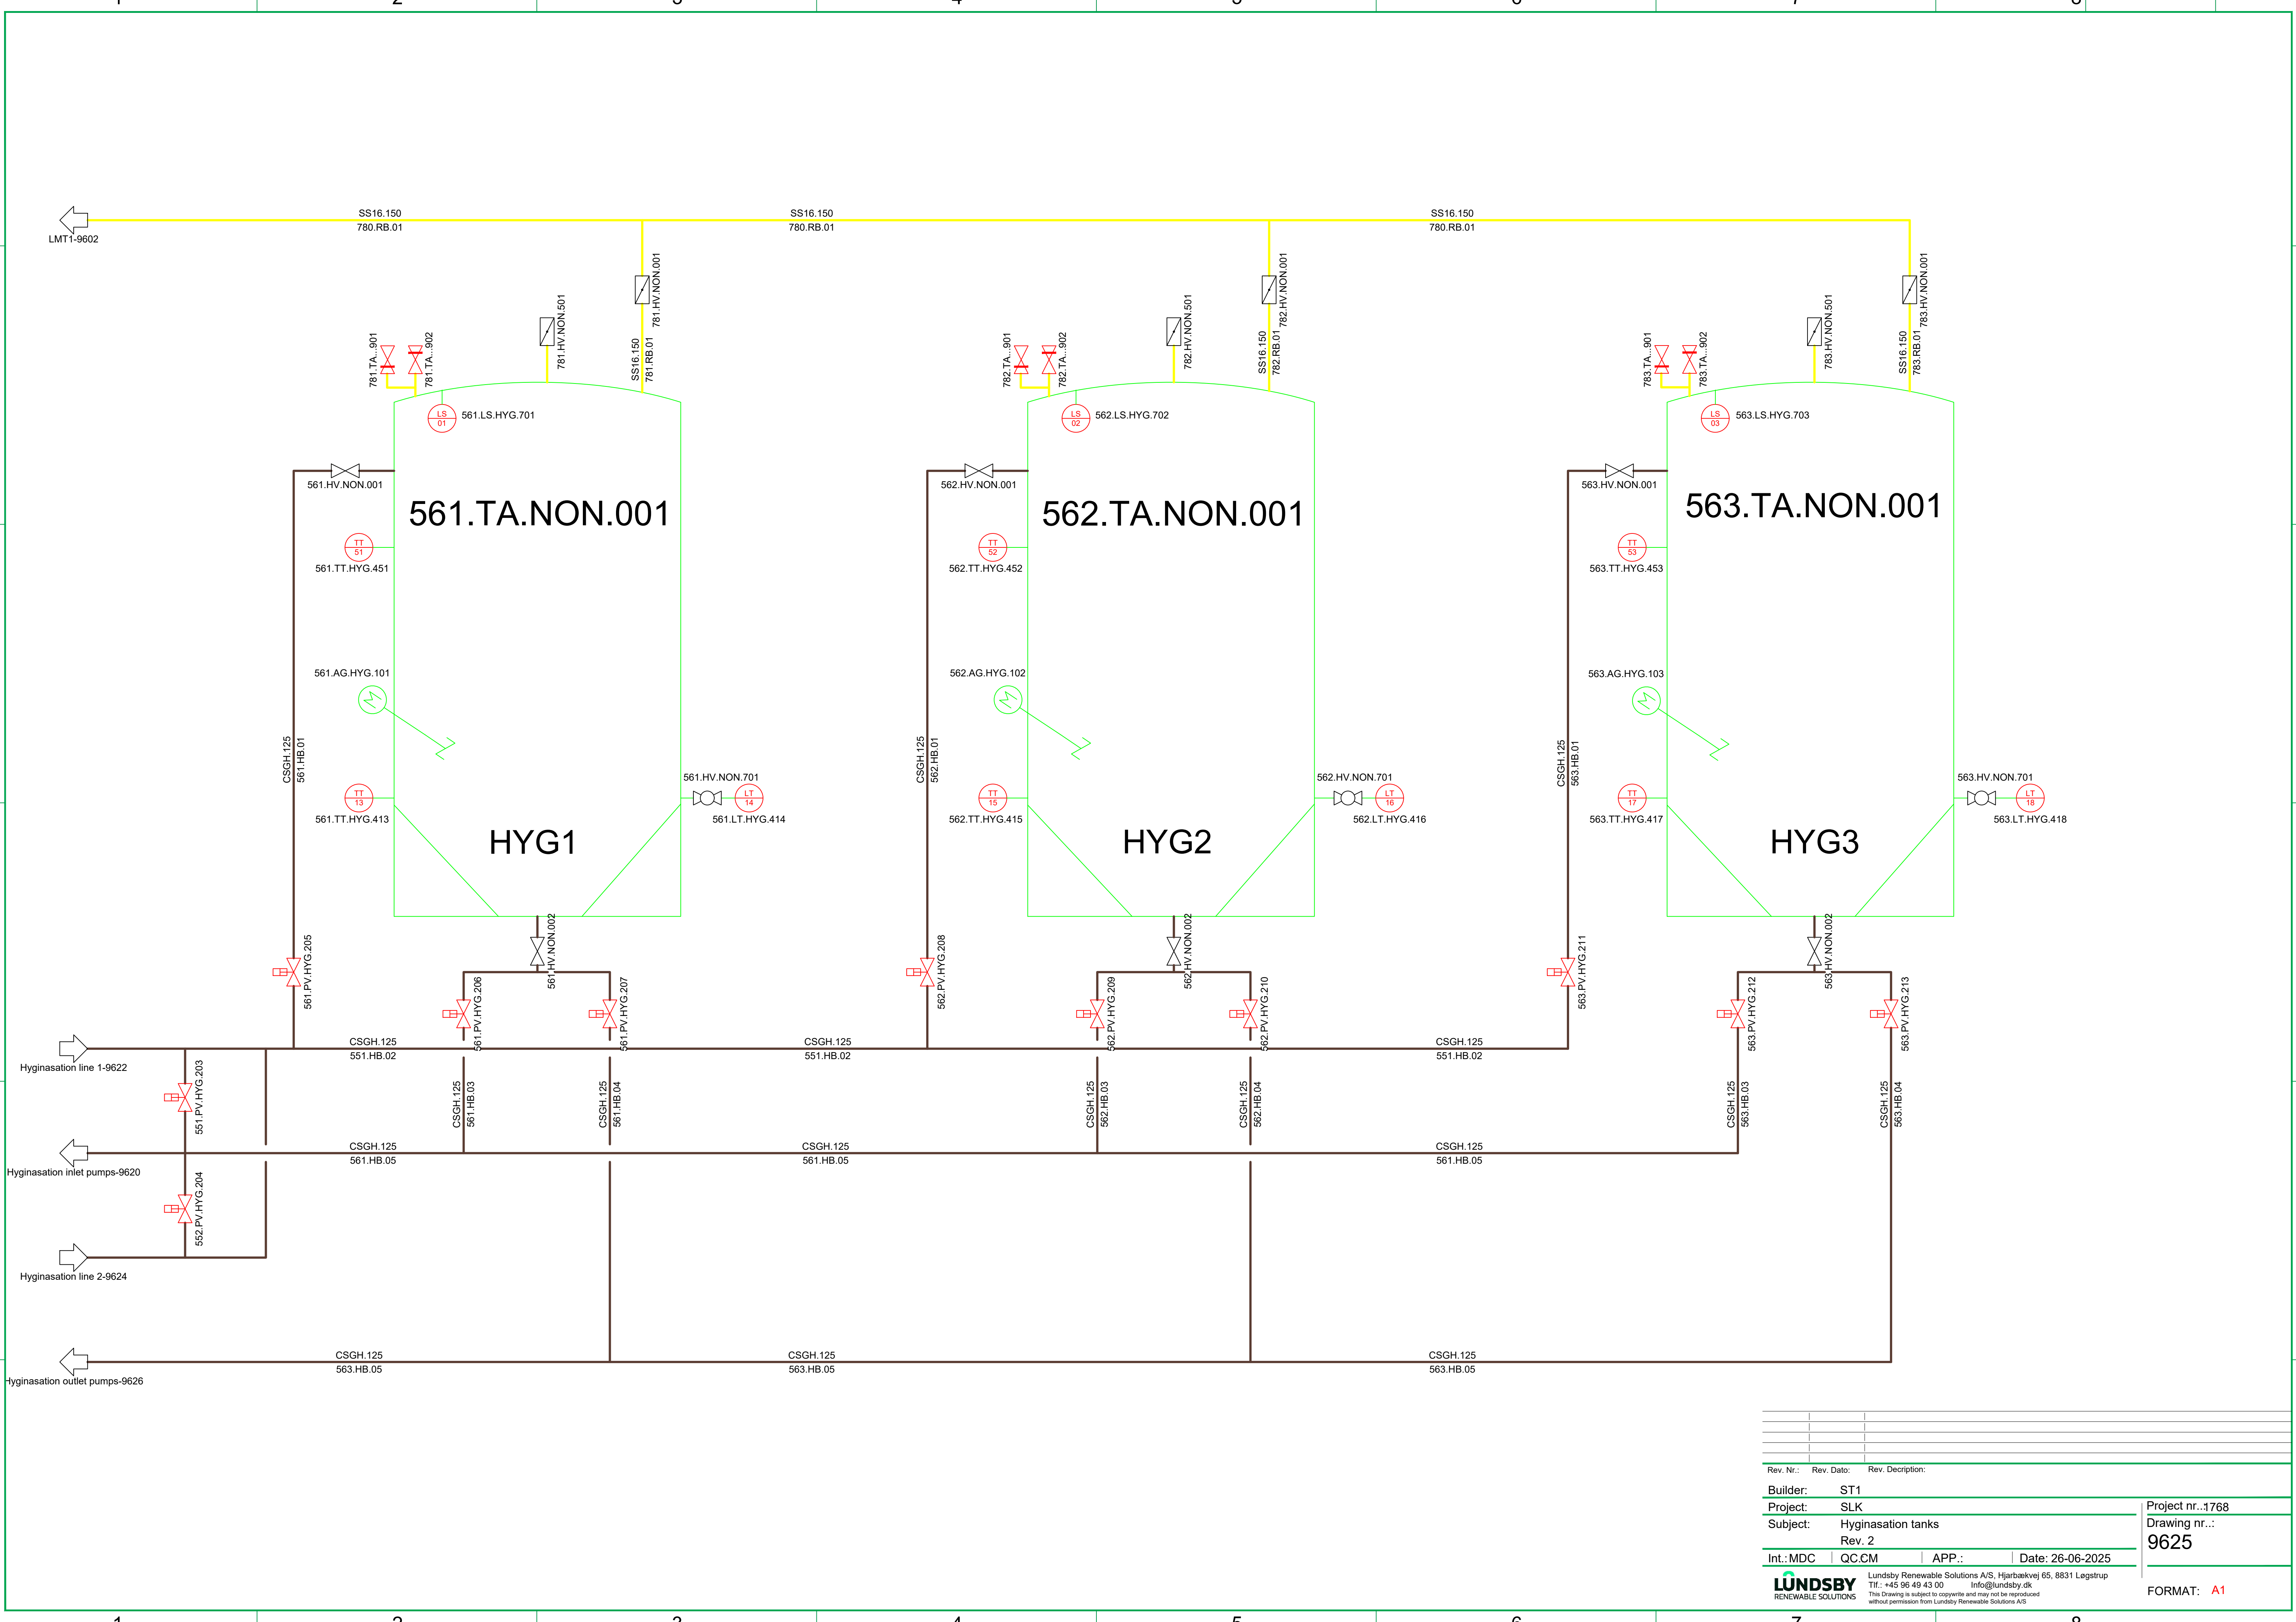


Rev. Nr.:	Rev. Dato:	Rev. Description:	
Builder:	ST1		
Project:	SLK		
Subject:	Hyginasation tanks		
	Rev. 2		
Int.:MDC	QC.CM	APP.:	Date: 26-06-2025
LUNDSBY RENEWABLE SOLUTIONS			Lundsby Renewable Solutions A/S, Hjarbækvej 65, 8831 Løgstrup Tlf.: +45 96 49 43 00 info@lundsby.dk This Drawing is subject to copyright and may not be reproduced without permission from Lundsby Renewable Solutions A/S
			Project nr.:1768 Drawing nr.: 9625
			FORMAT: A1

Tech Building


Outlet pumps

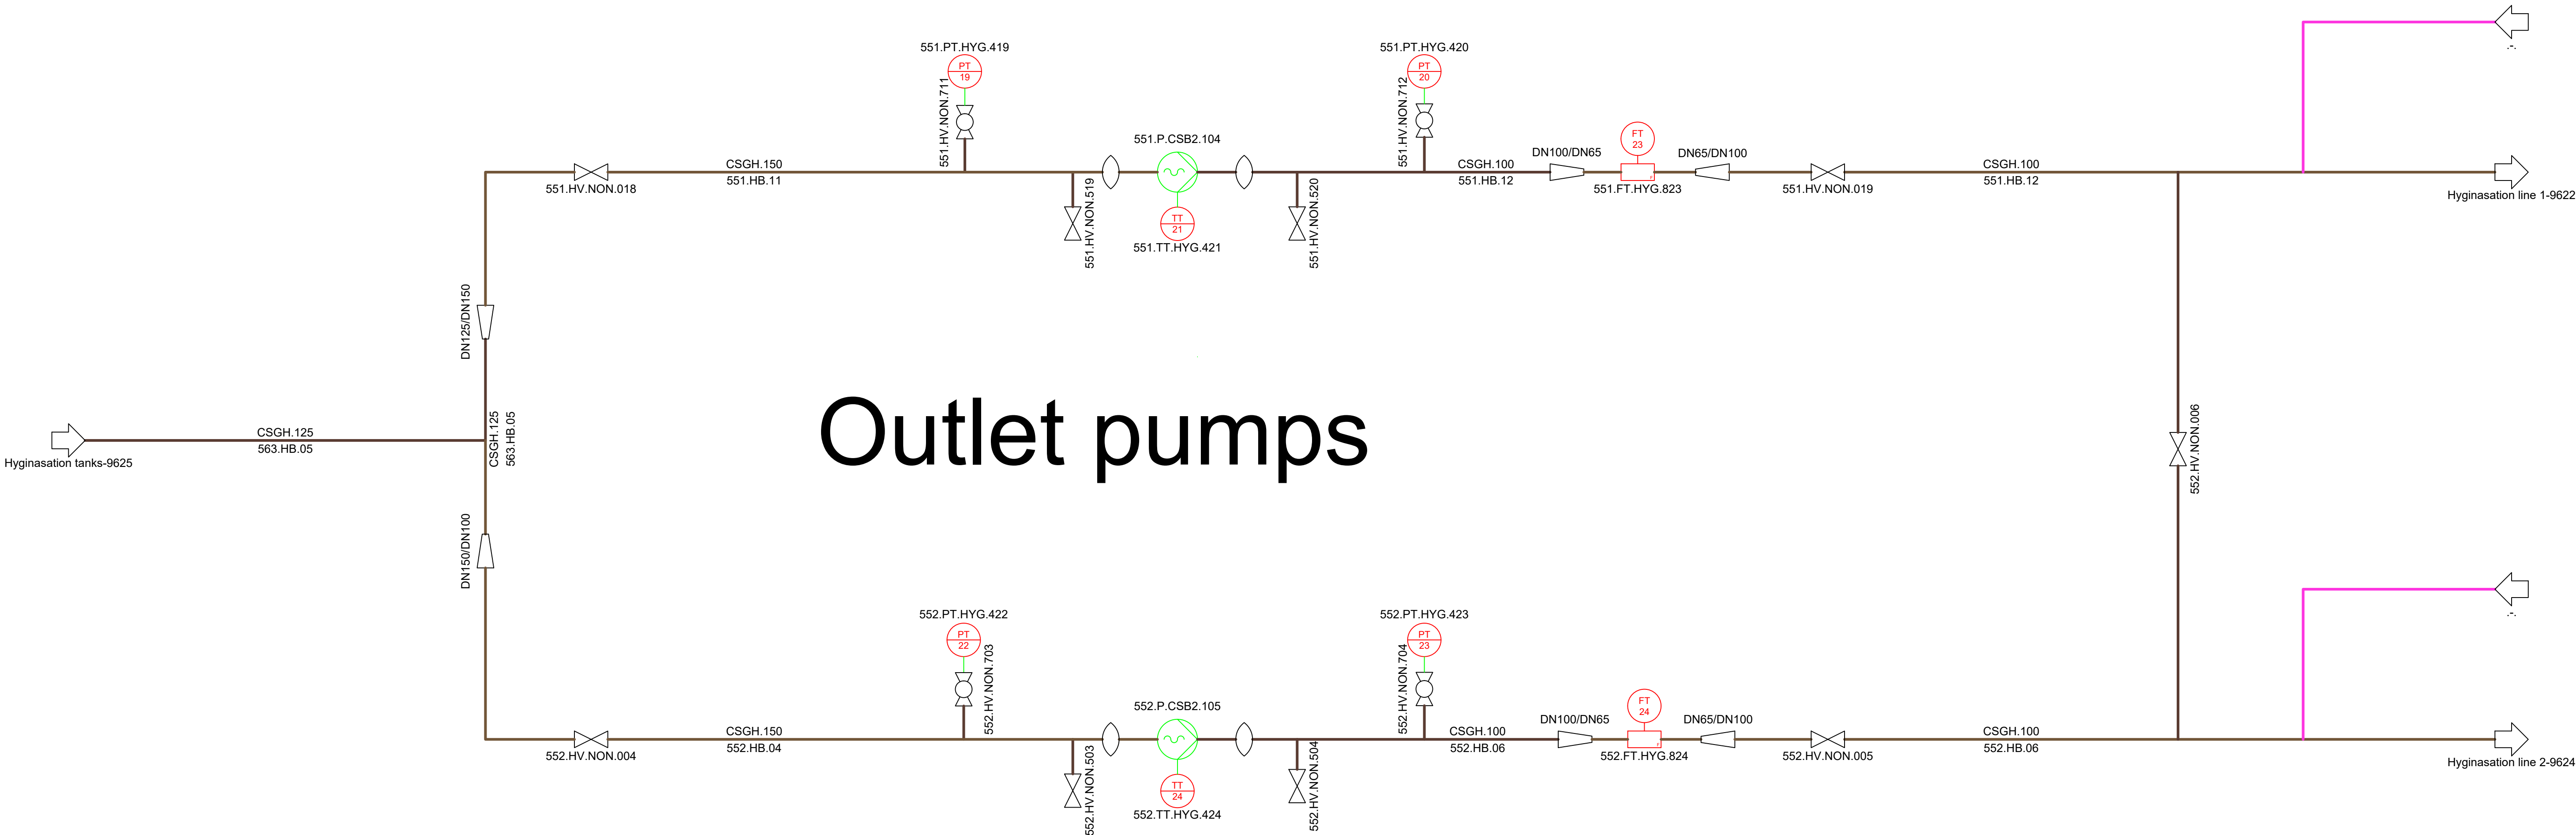


Rev. Nr.:	Rev. Dato:	Rev. Description:	
Builder:	ST1		
Project:	SLK		
Subject:	Hyginasation outlet pumps		
Rev. 2			
Int.:MDC	QC:CM	APP.:	Date: 26-06-2025
LUNDSBY RENEWABLE SOLUTIONS			Lundsby Renewable Solutions A/S, Hjarbækvej 65, 8831 Løgstrup Tlf.: +45 96 49 43 00 Info@lundsby.dk This Drawing is subject to copyright and may not be reproduced without permission from Lundsby Renewable Solutions A/S
Project nr.:1768 Drawing nr.: 9626			FORMAT: A1

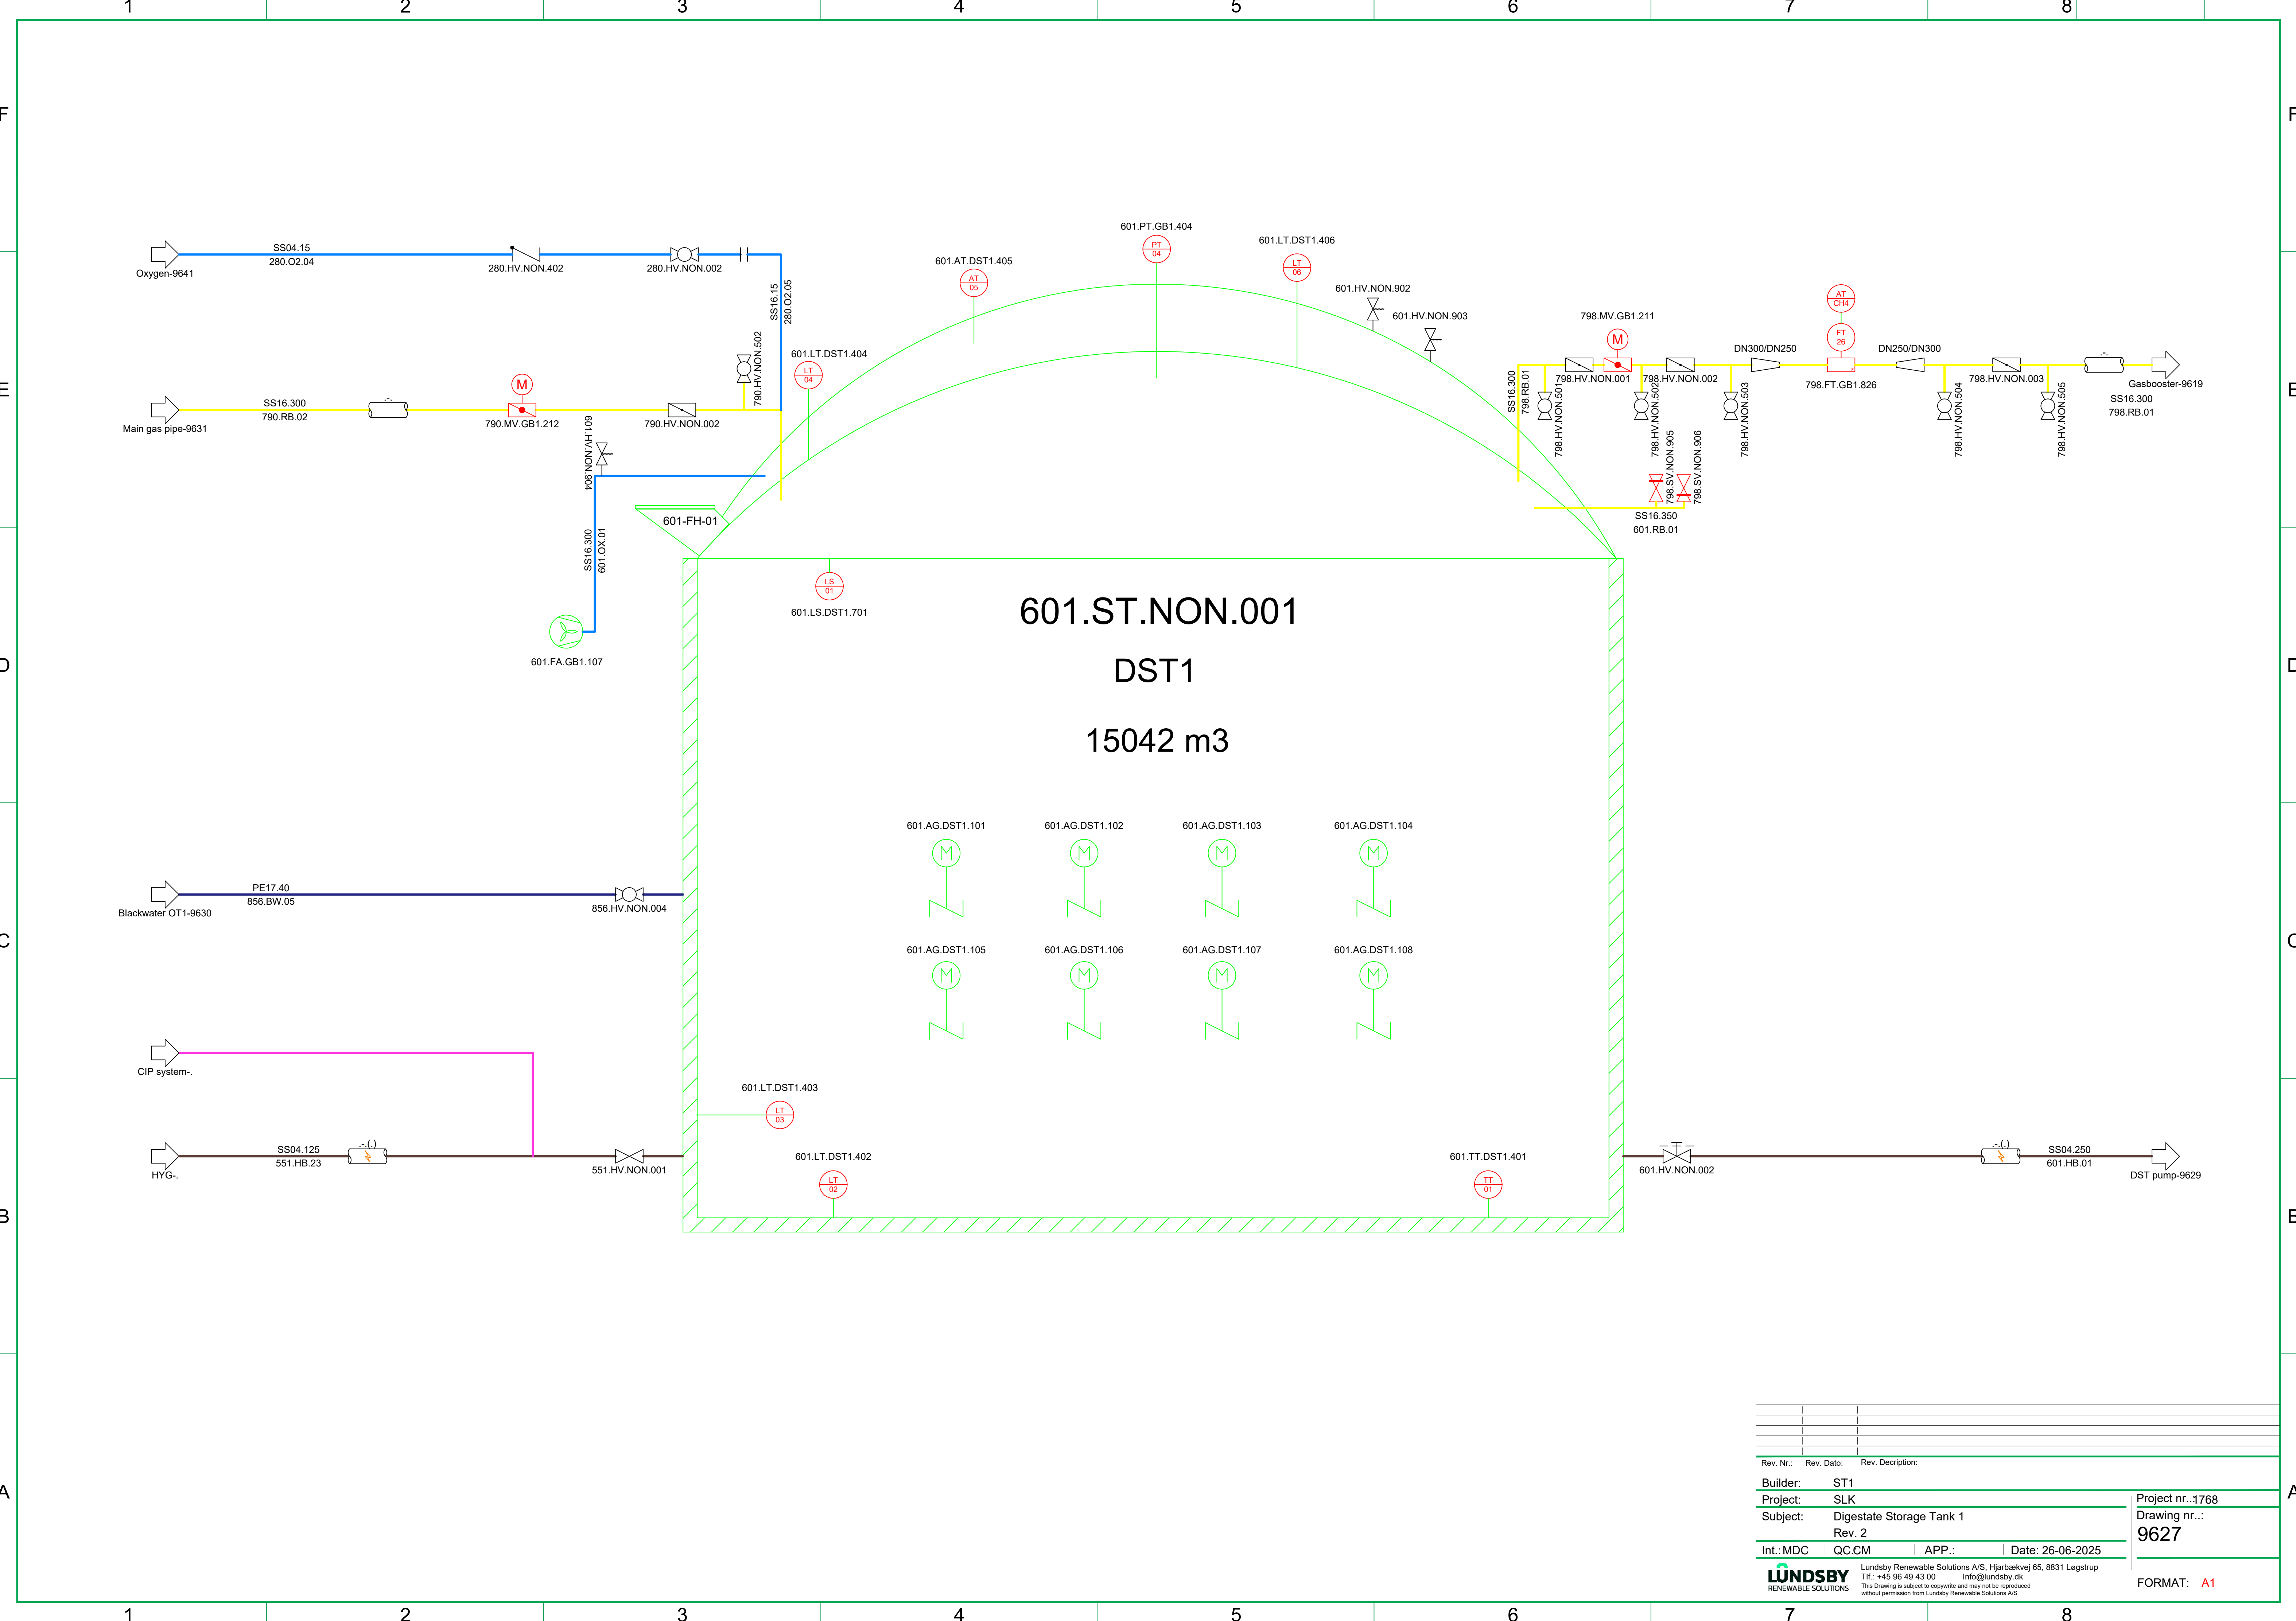


Rev. Nr.:	Rev. Dato:	Rev. Description:	
Builder:	ST1		
Project:	SLK		
Subject:	Digestate Storage Tank 1		
Rev. 2			
Int.:MDC	QC:CM	APP.:	Date: 26-06-2025
LUNDSBY RENEWABLE SOLUTIONS			Lundsby Renewable Solutions A/S, Hjarbækvej 65, 8831 Løgstrup Tlf.: +45 96 49 43 00 Info@lundsby.dk This Drawing is subject to copyright and may not be reproduced without permission from Lundsby Renewable Solutions A/S
Project nr.:1768 Drawing nr.: 9627			FORMAT: A1

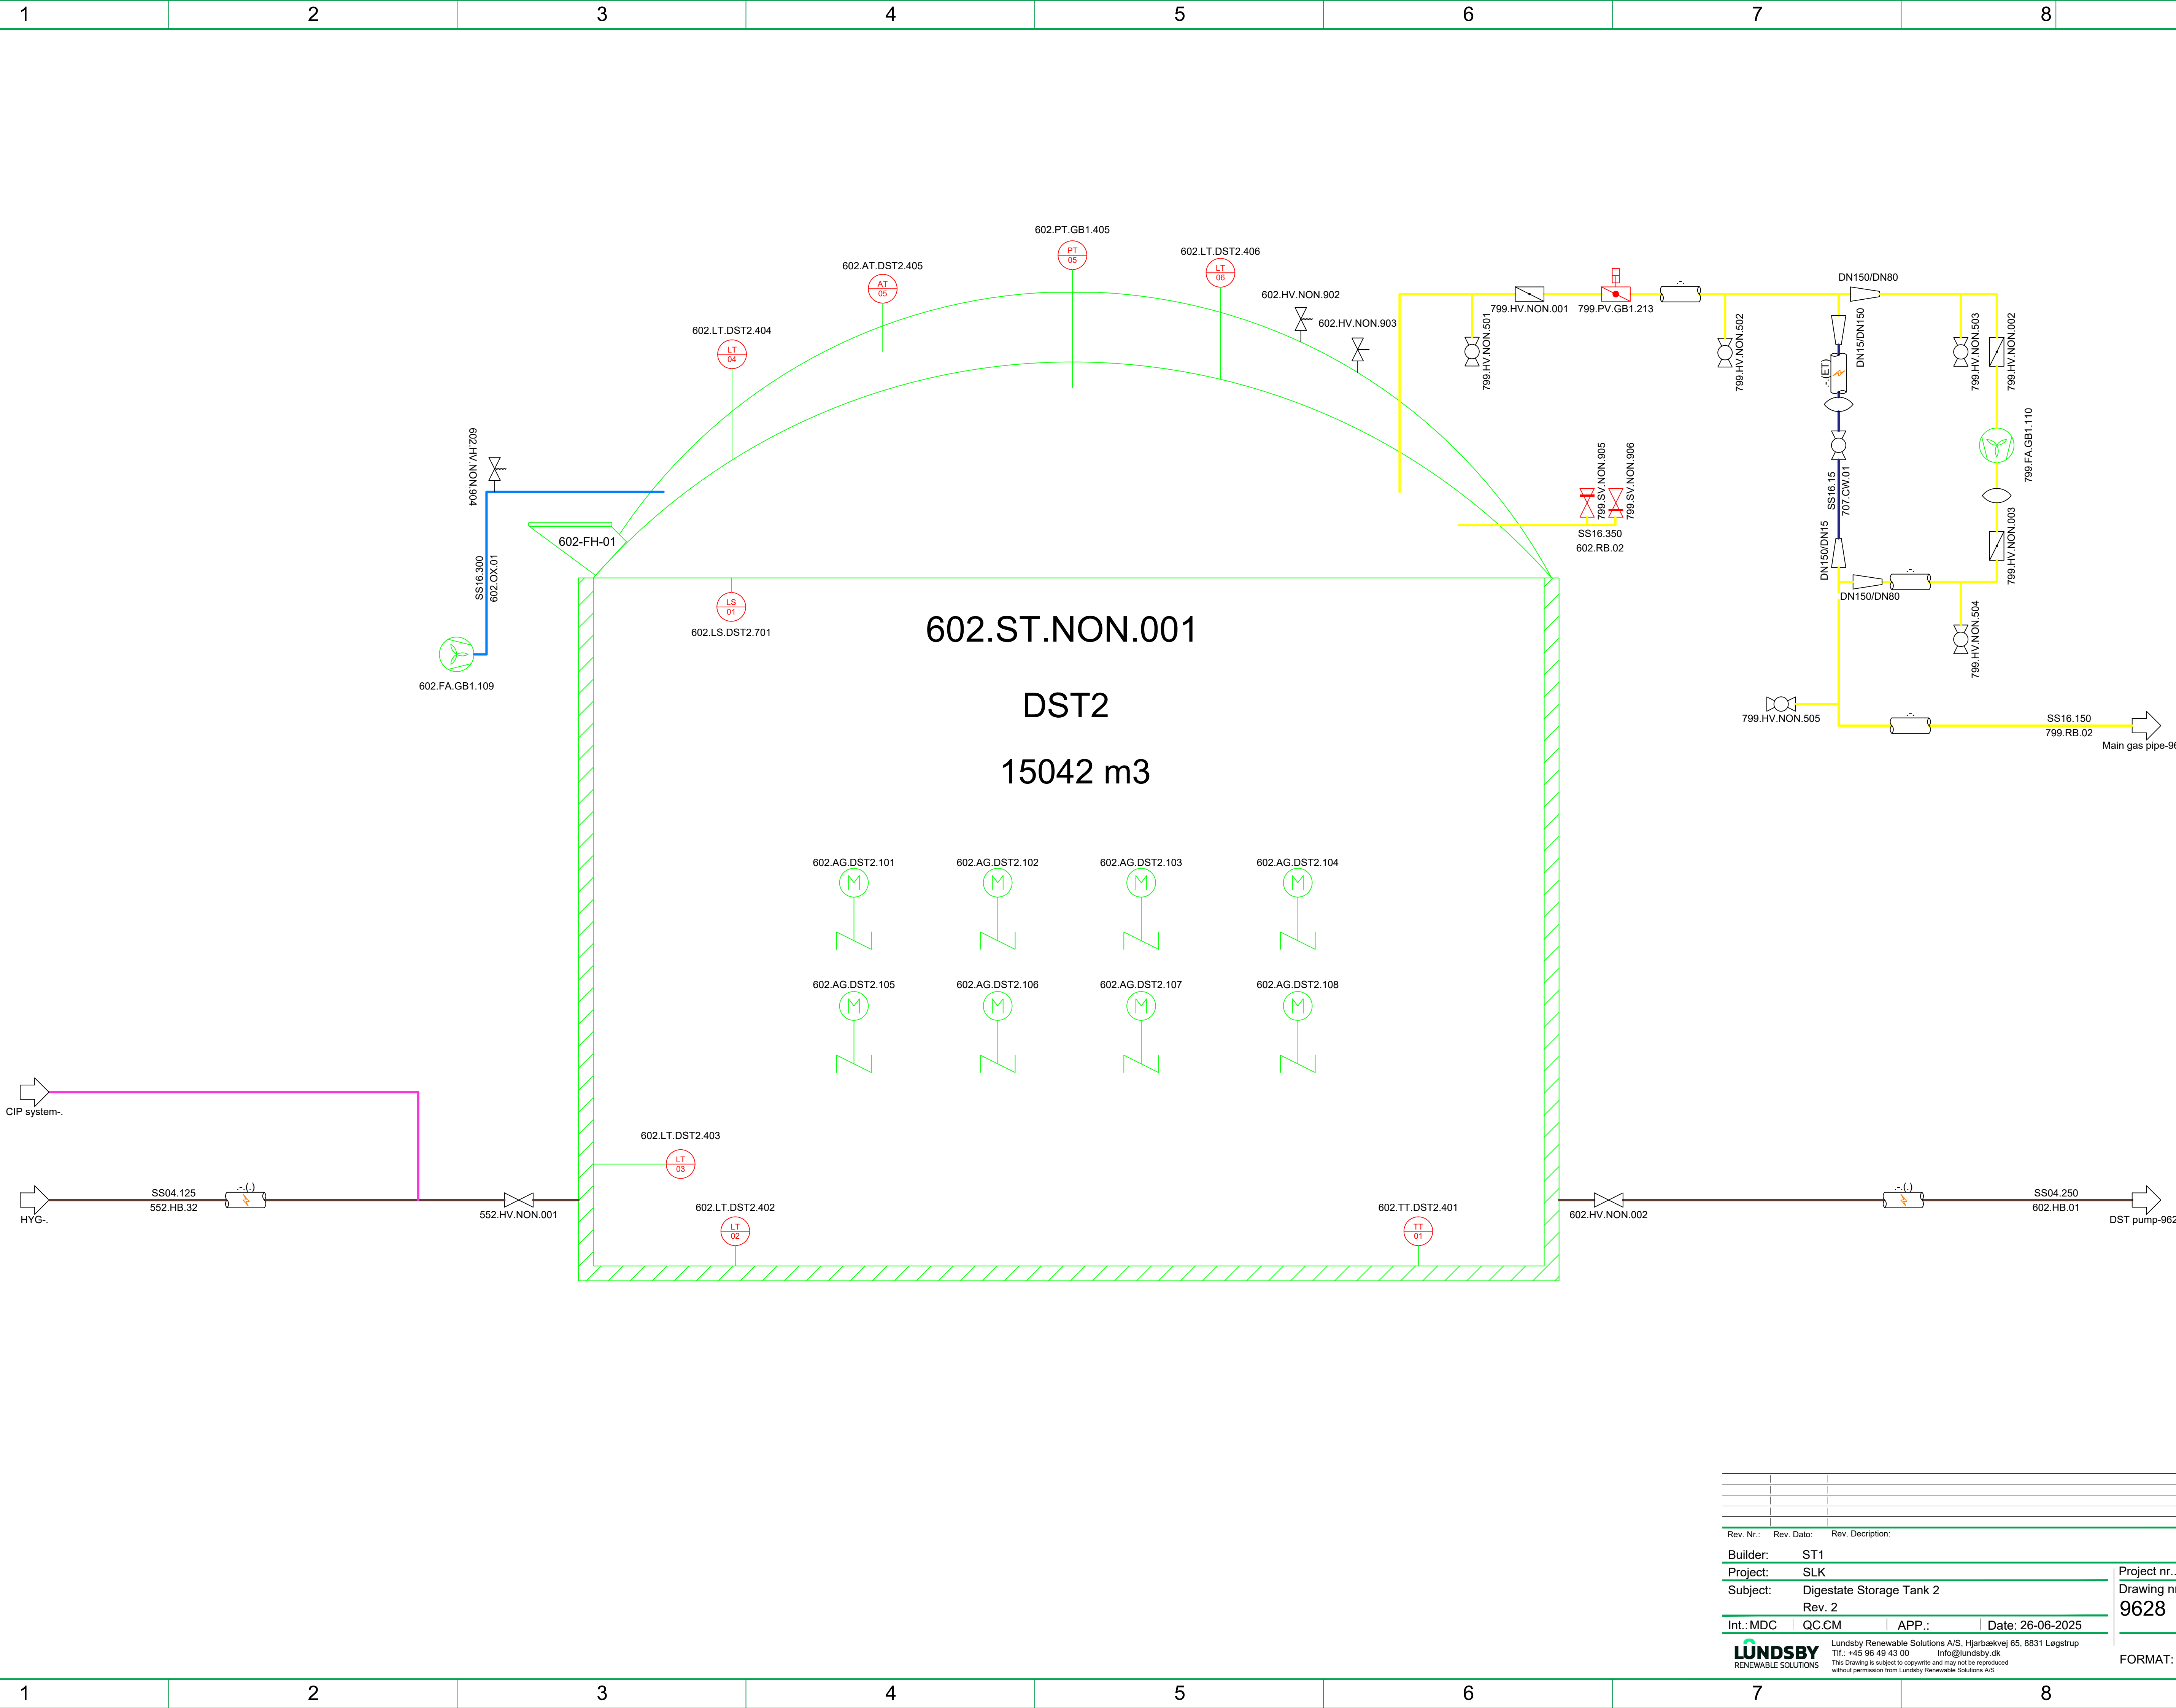


Rev. Nr.:	Rev. Dato:	Rev. Description:	
Builder:	ST1		
Project:	SLK		
Subject:	Digestate Storage Tank 2		
Rev. 2			
Int.: MDC	QC.CM	APP.:	Date: 26-06-2025
LUNDSBY RENEWABLE SOLUTIONS			Lundsby Renewable Solutions A/S, Hjarbækvej 65, 8831 Løgstrup Tlf.: +45 96 49 43 00 Info@lundsby.dk This Drawing is subject to copyright and may not be reproduced without permission from Lundsby Renewable Solutions A/S
Project nr.: 1768 Drawing nr.: 9628			FORMAT: A1

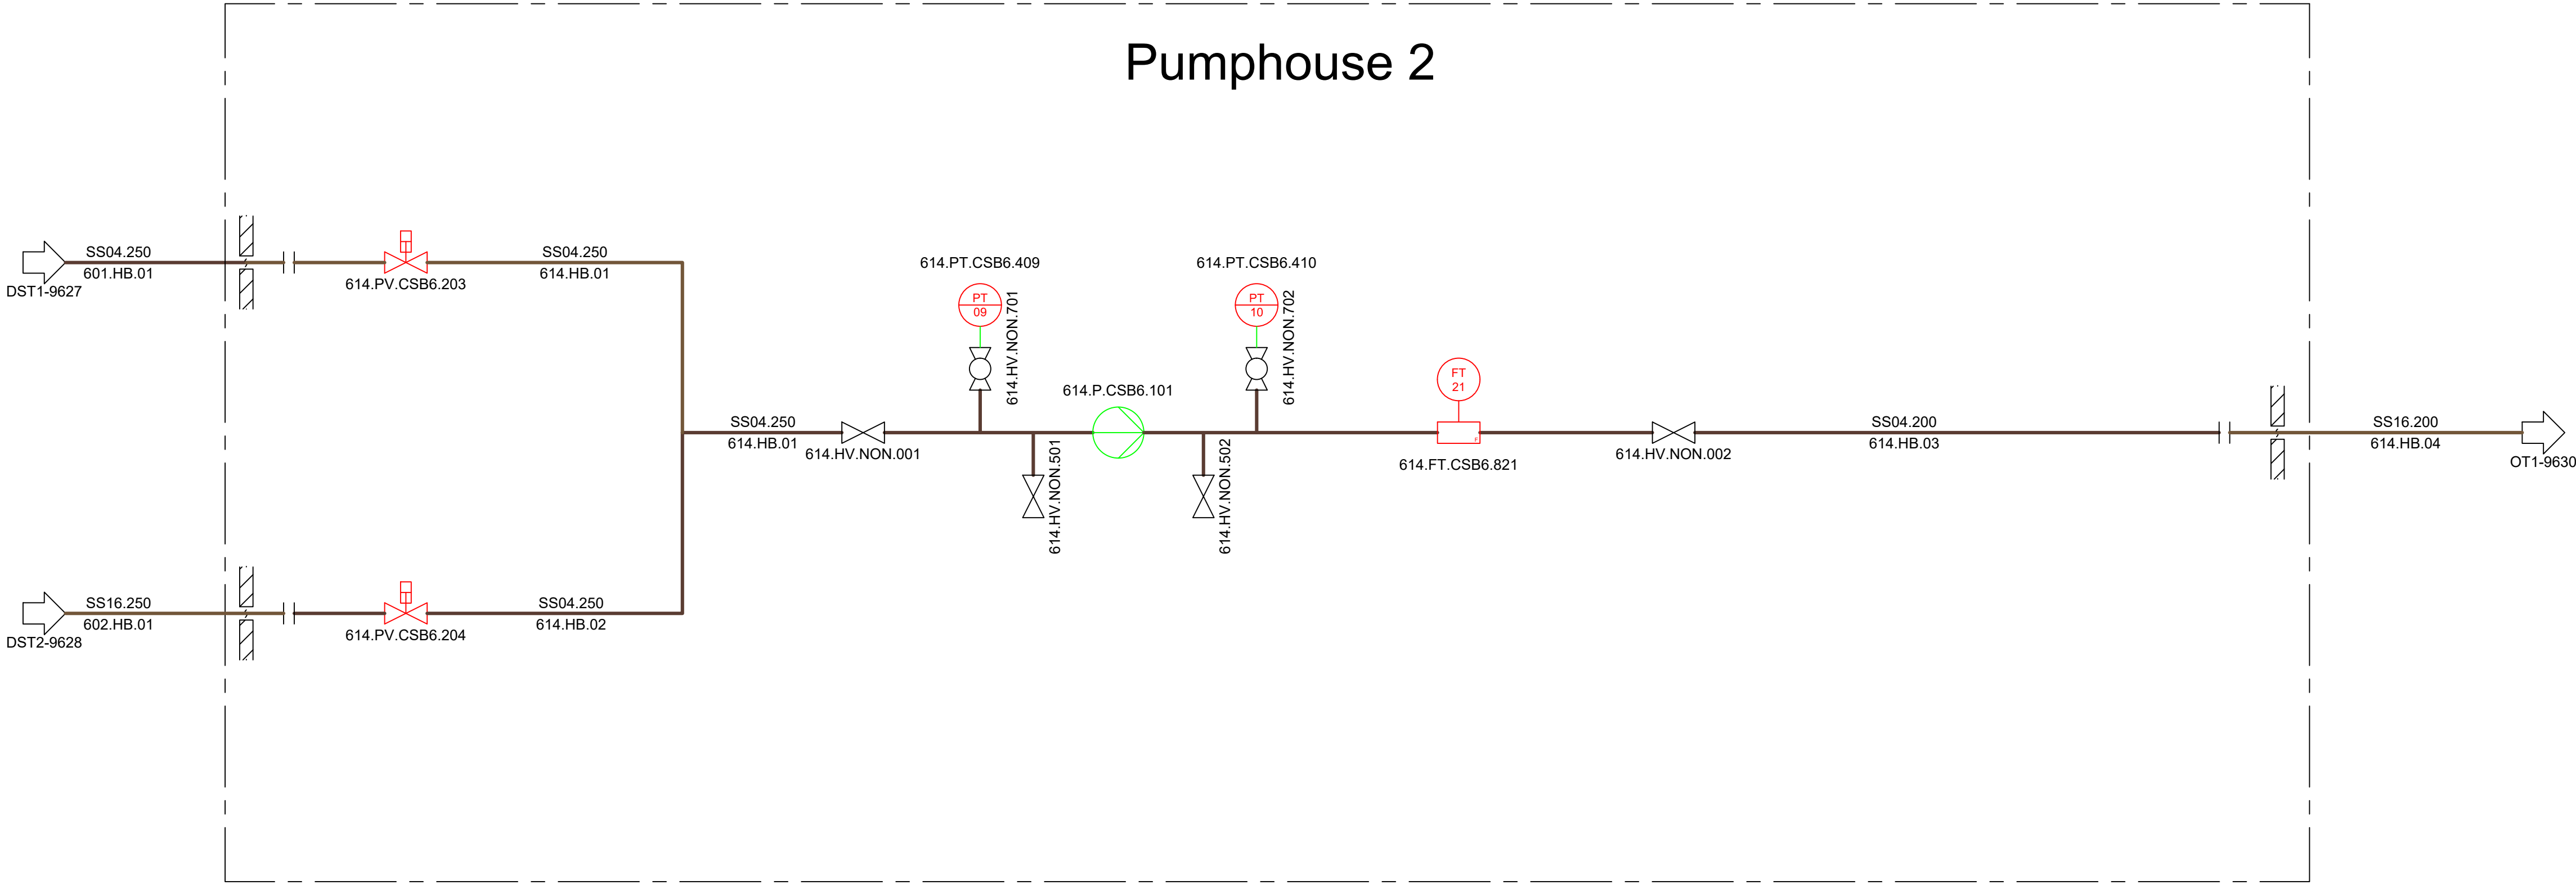


Rev. Nr.:	Rev. Dato:	Rev. Description:
Builder:	ST1	
Project:	SLK	
Subject:	DST pump	
	Rev. 2	
Int.:MDC	QC:CM	APP.: Date: 26-06-2025
LUNDSBY RENEWABLE SOLUTIONS		
Lundsby Renewable Solutions A/S, Hjarbækvej 65, 8831 Løgstrup Tlf.: +45 96 49 43 00 Info@lundsby.dk This Drawing is subject to copyright and may not be reproduced without permission from Lundsby Renewable Solutions A/S		
Project nr.:1768 Drawing nr.: 9629		FORMAT: A1

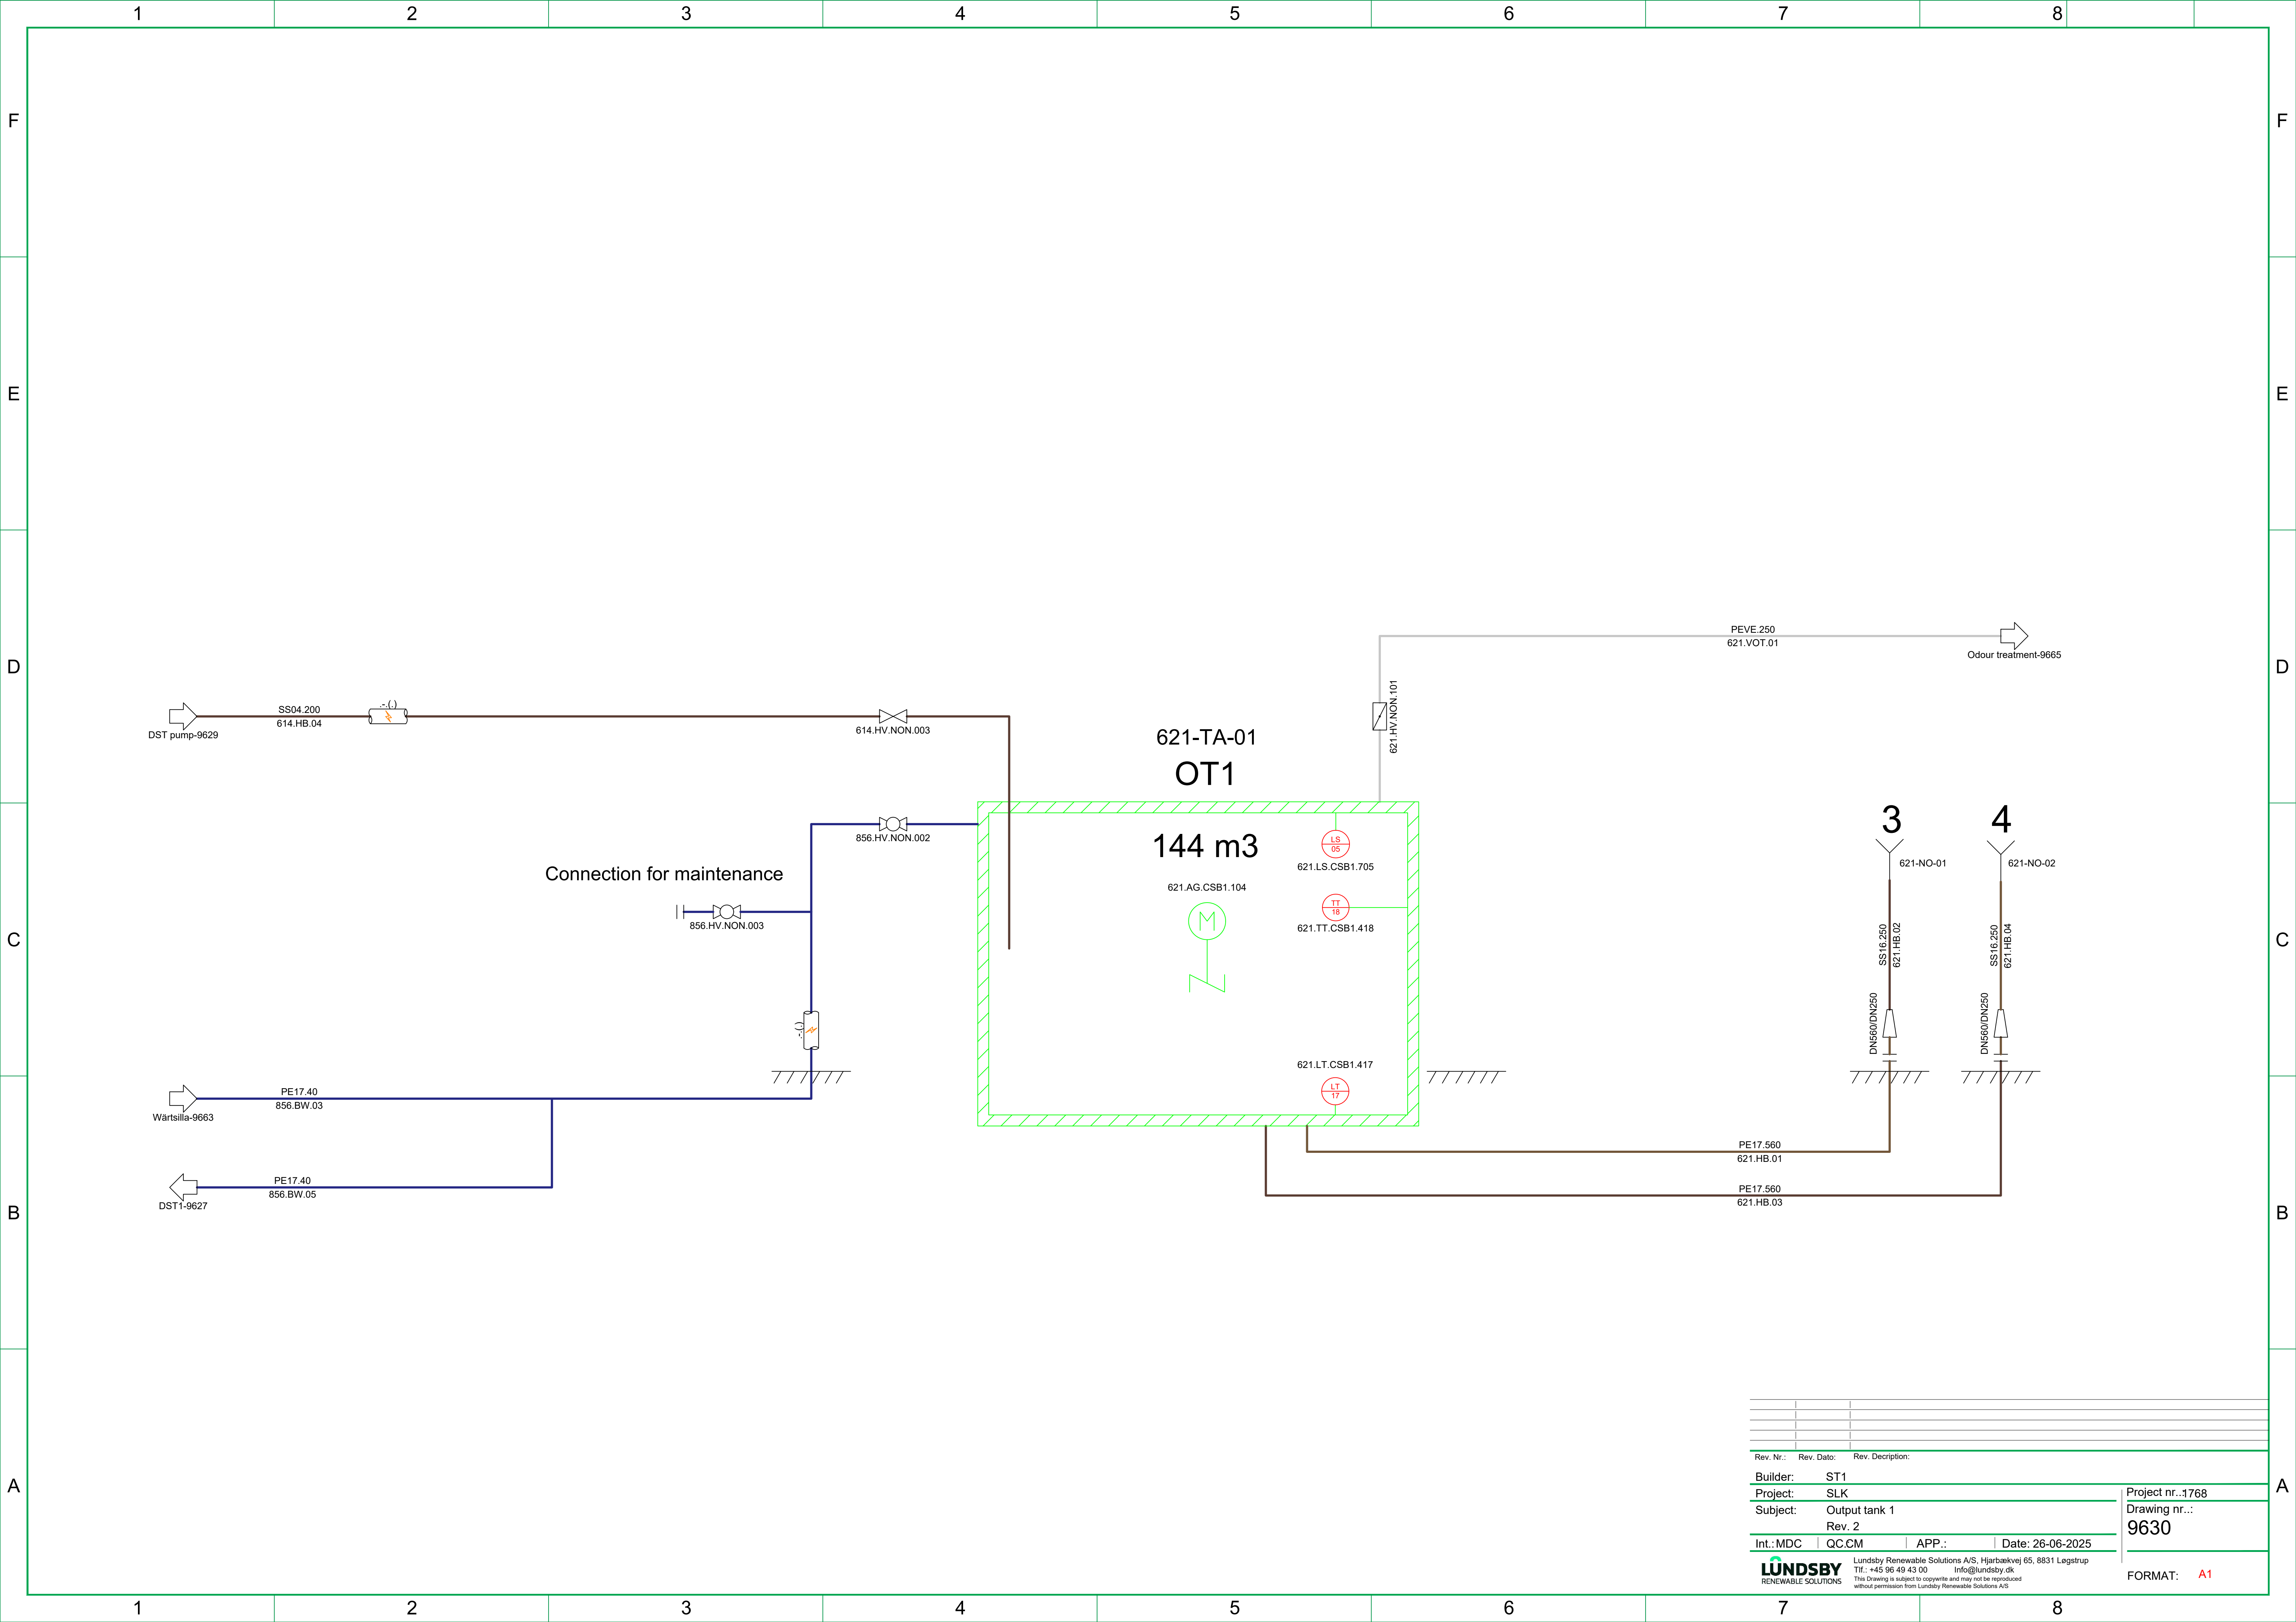

Rev. Nr.:	Rev. Date:	Rev. Description:	Project nr...1768
Builder:	ST1		Drawing nr...: 9630
Project:	SLK		
Subject:	Output tank 1		
	Rev. 2		
Int.:MDC	QC:CM	APP.:	Date: 26-06-2025
LUNDSBYRENEWABLE SOLUTIONS Lundsgby Renewable Solutions A/S, Hjarbrækvej 65, 8831 Lægstrup Tlf.: +45 96 49 43 00 Info@lundsgby.dk This Drawing is subject to copyright and may not be reproduced without permission from Lundsgby Renewable Solutions A/S			
FORMAT:			A1

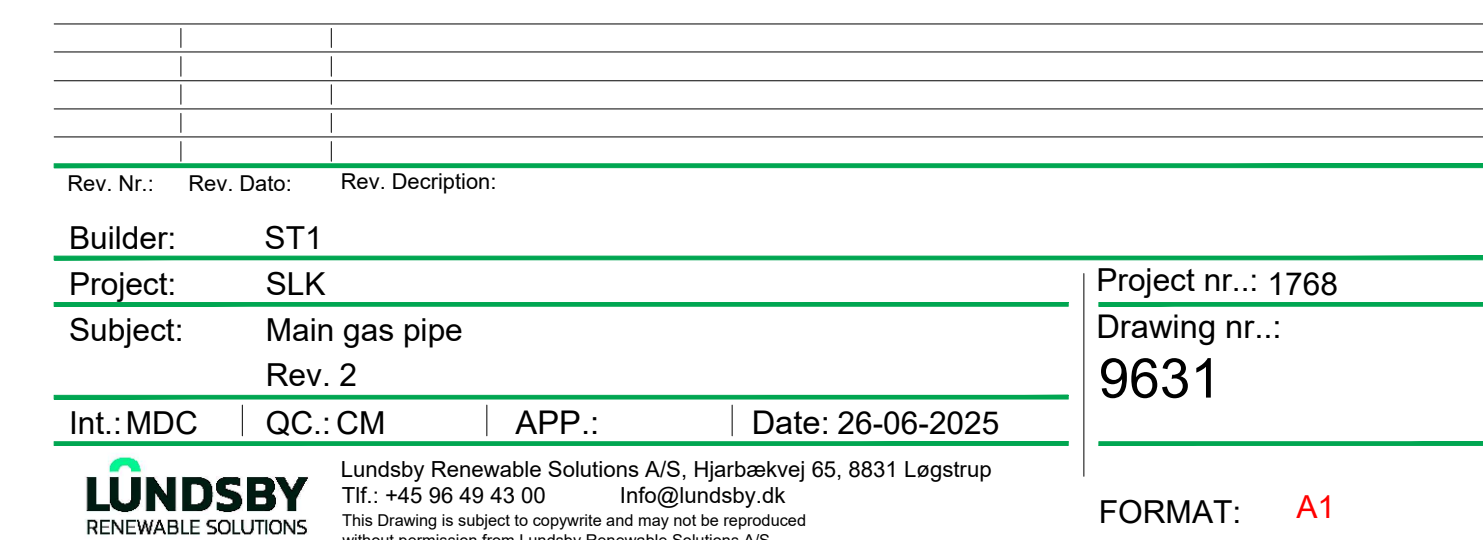

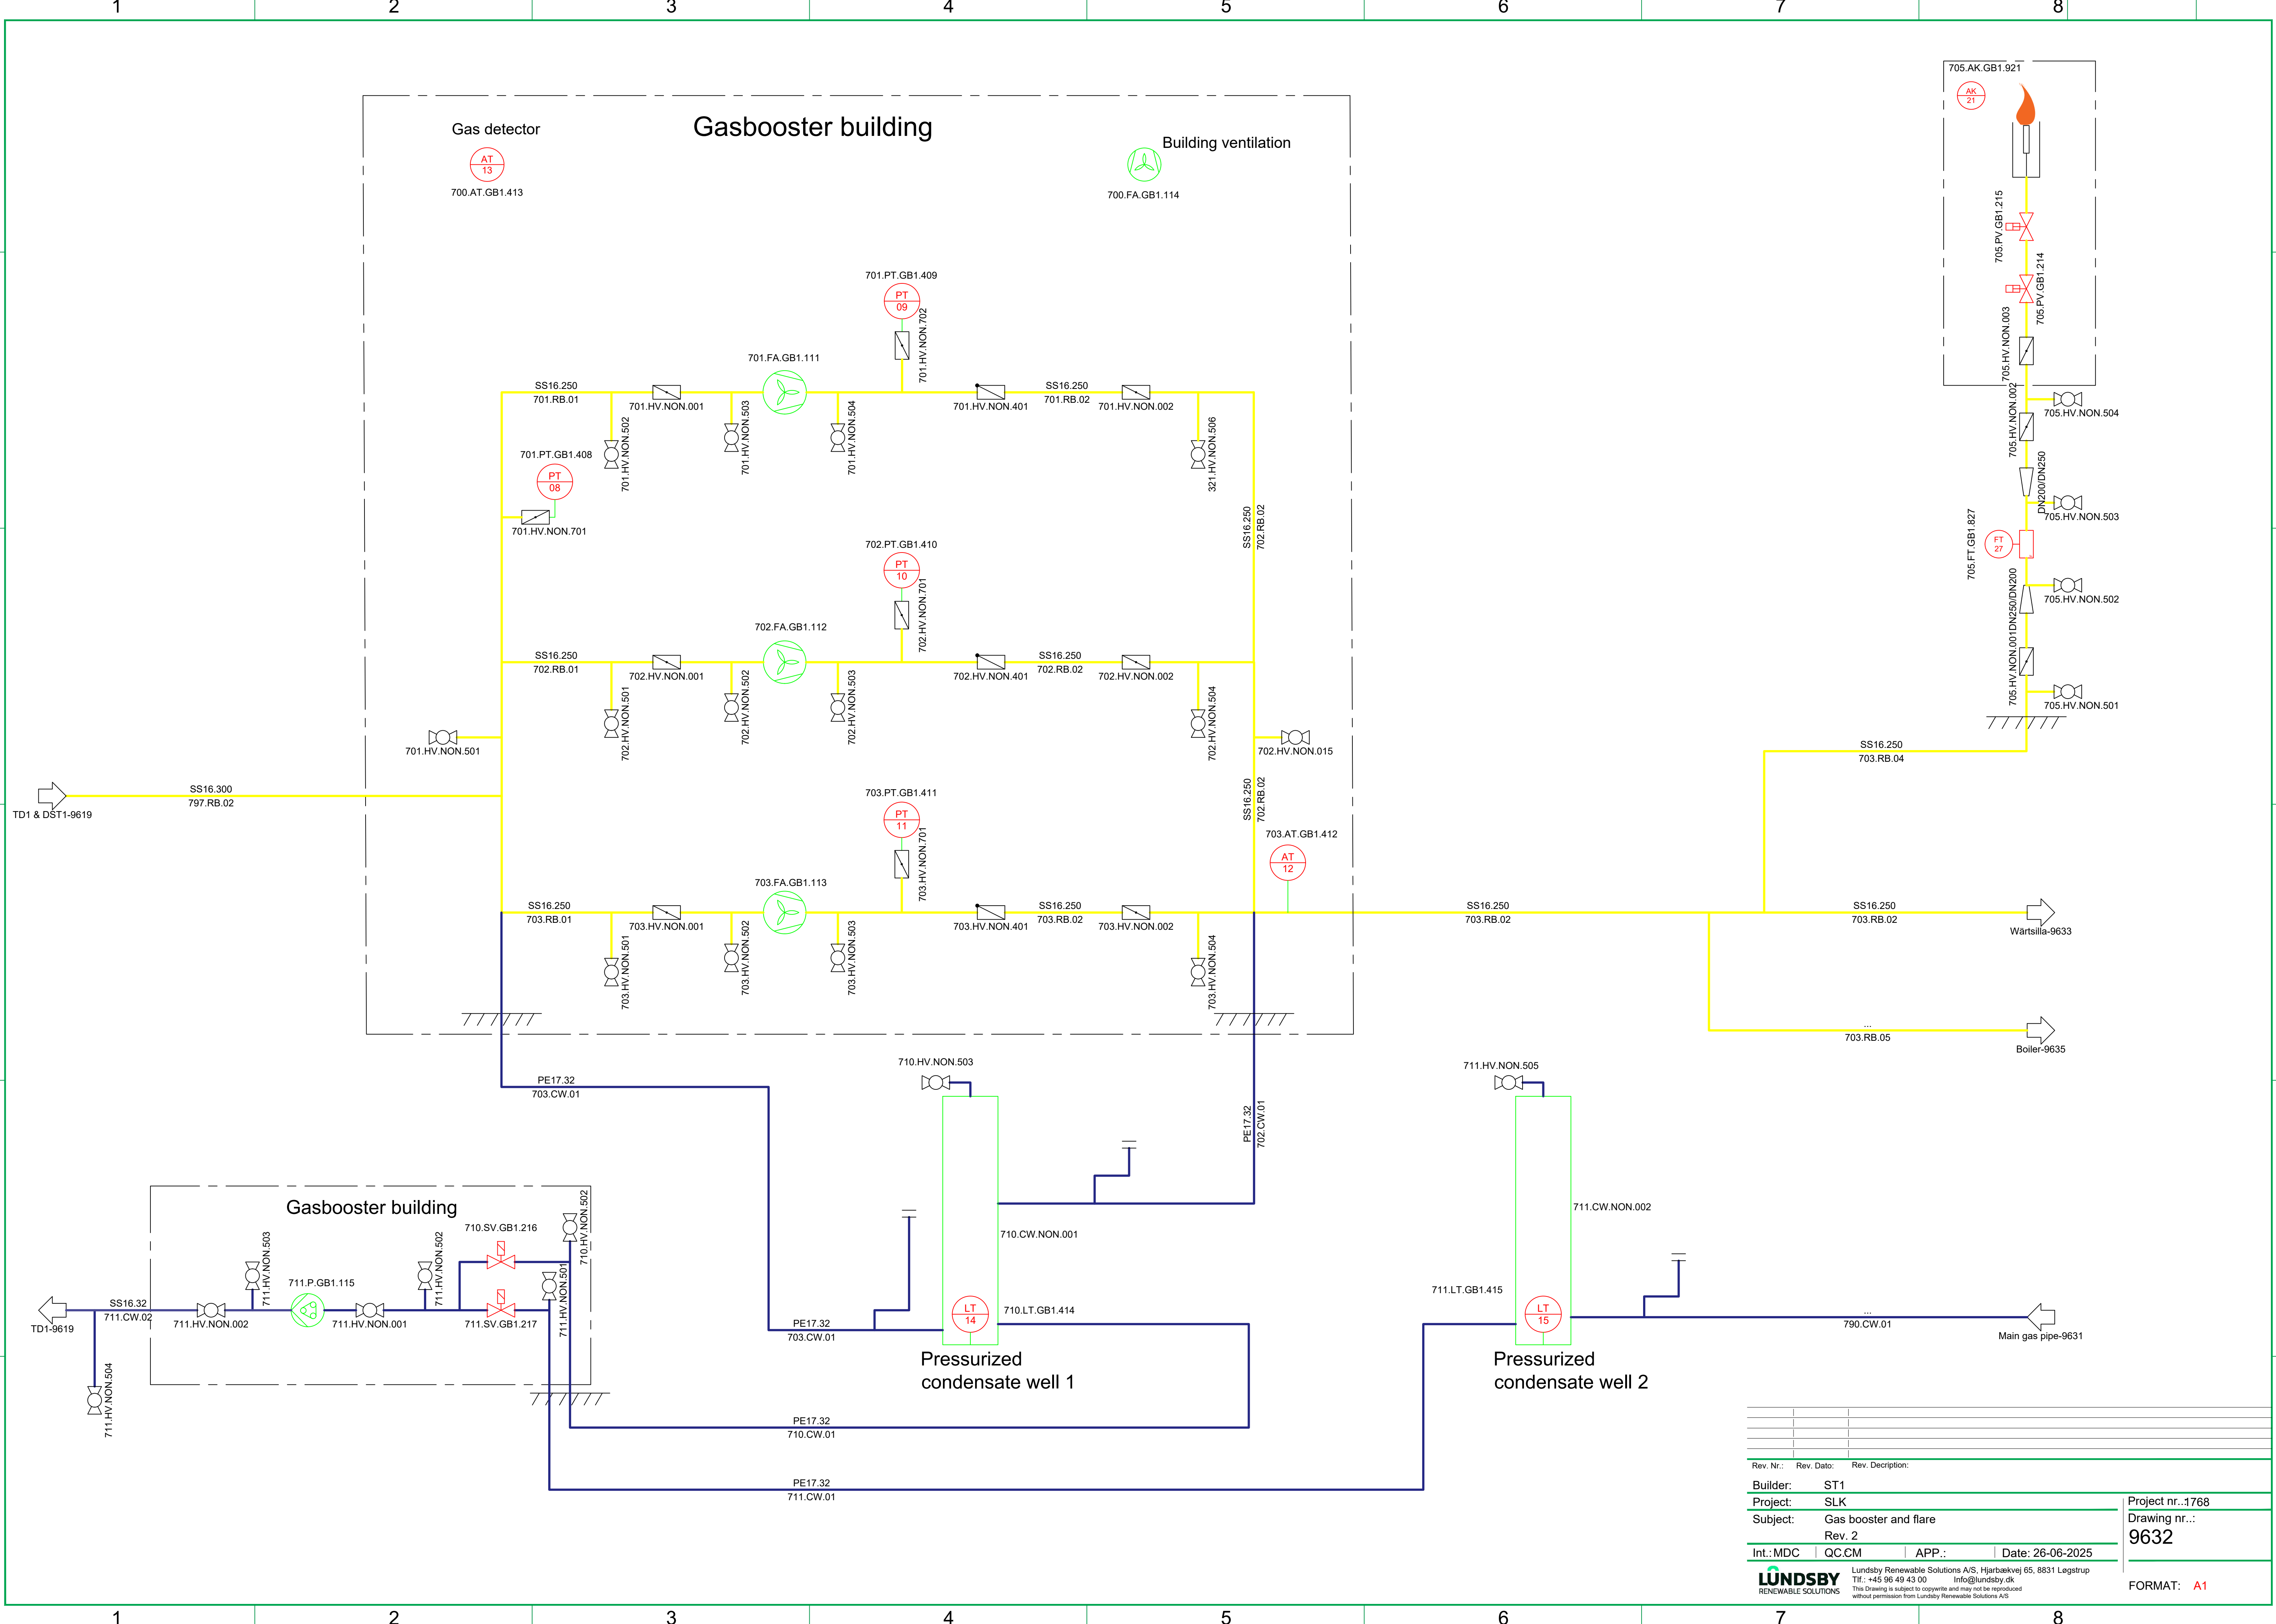


Rev. Nr.:	Rev. Dato:	Rev. Description:
Builder:	ST1	
Project:	SLK	
Subject:	Gas booster and flare	
Rev. 2		
Int.:MDC	QC.CM	APP.:
Date:	26-06-2025	
LUNDSBY RENEWABLE SOLUTIONS		
Lundsby Renewable Solutions A/S, Hjarbækvej 65, 8831 Lægstrup Tlf.: +45 96 49 43 00 info@lundsby.dk This drawing is subject to copyright and may not be reproduced without permission from Lundsby Renewable Solutions A/S		
Project nr.:1768 Drawing nr.: 9632		FORMAT: A1

Wärtsillä

730-UPG-01

730-LBG-01

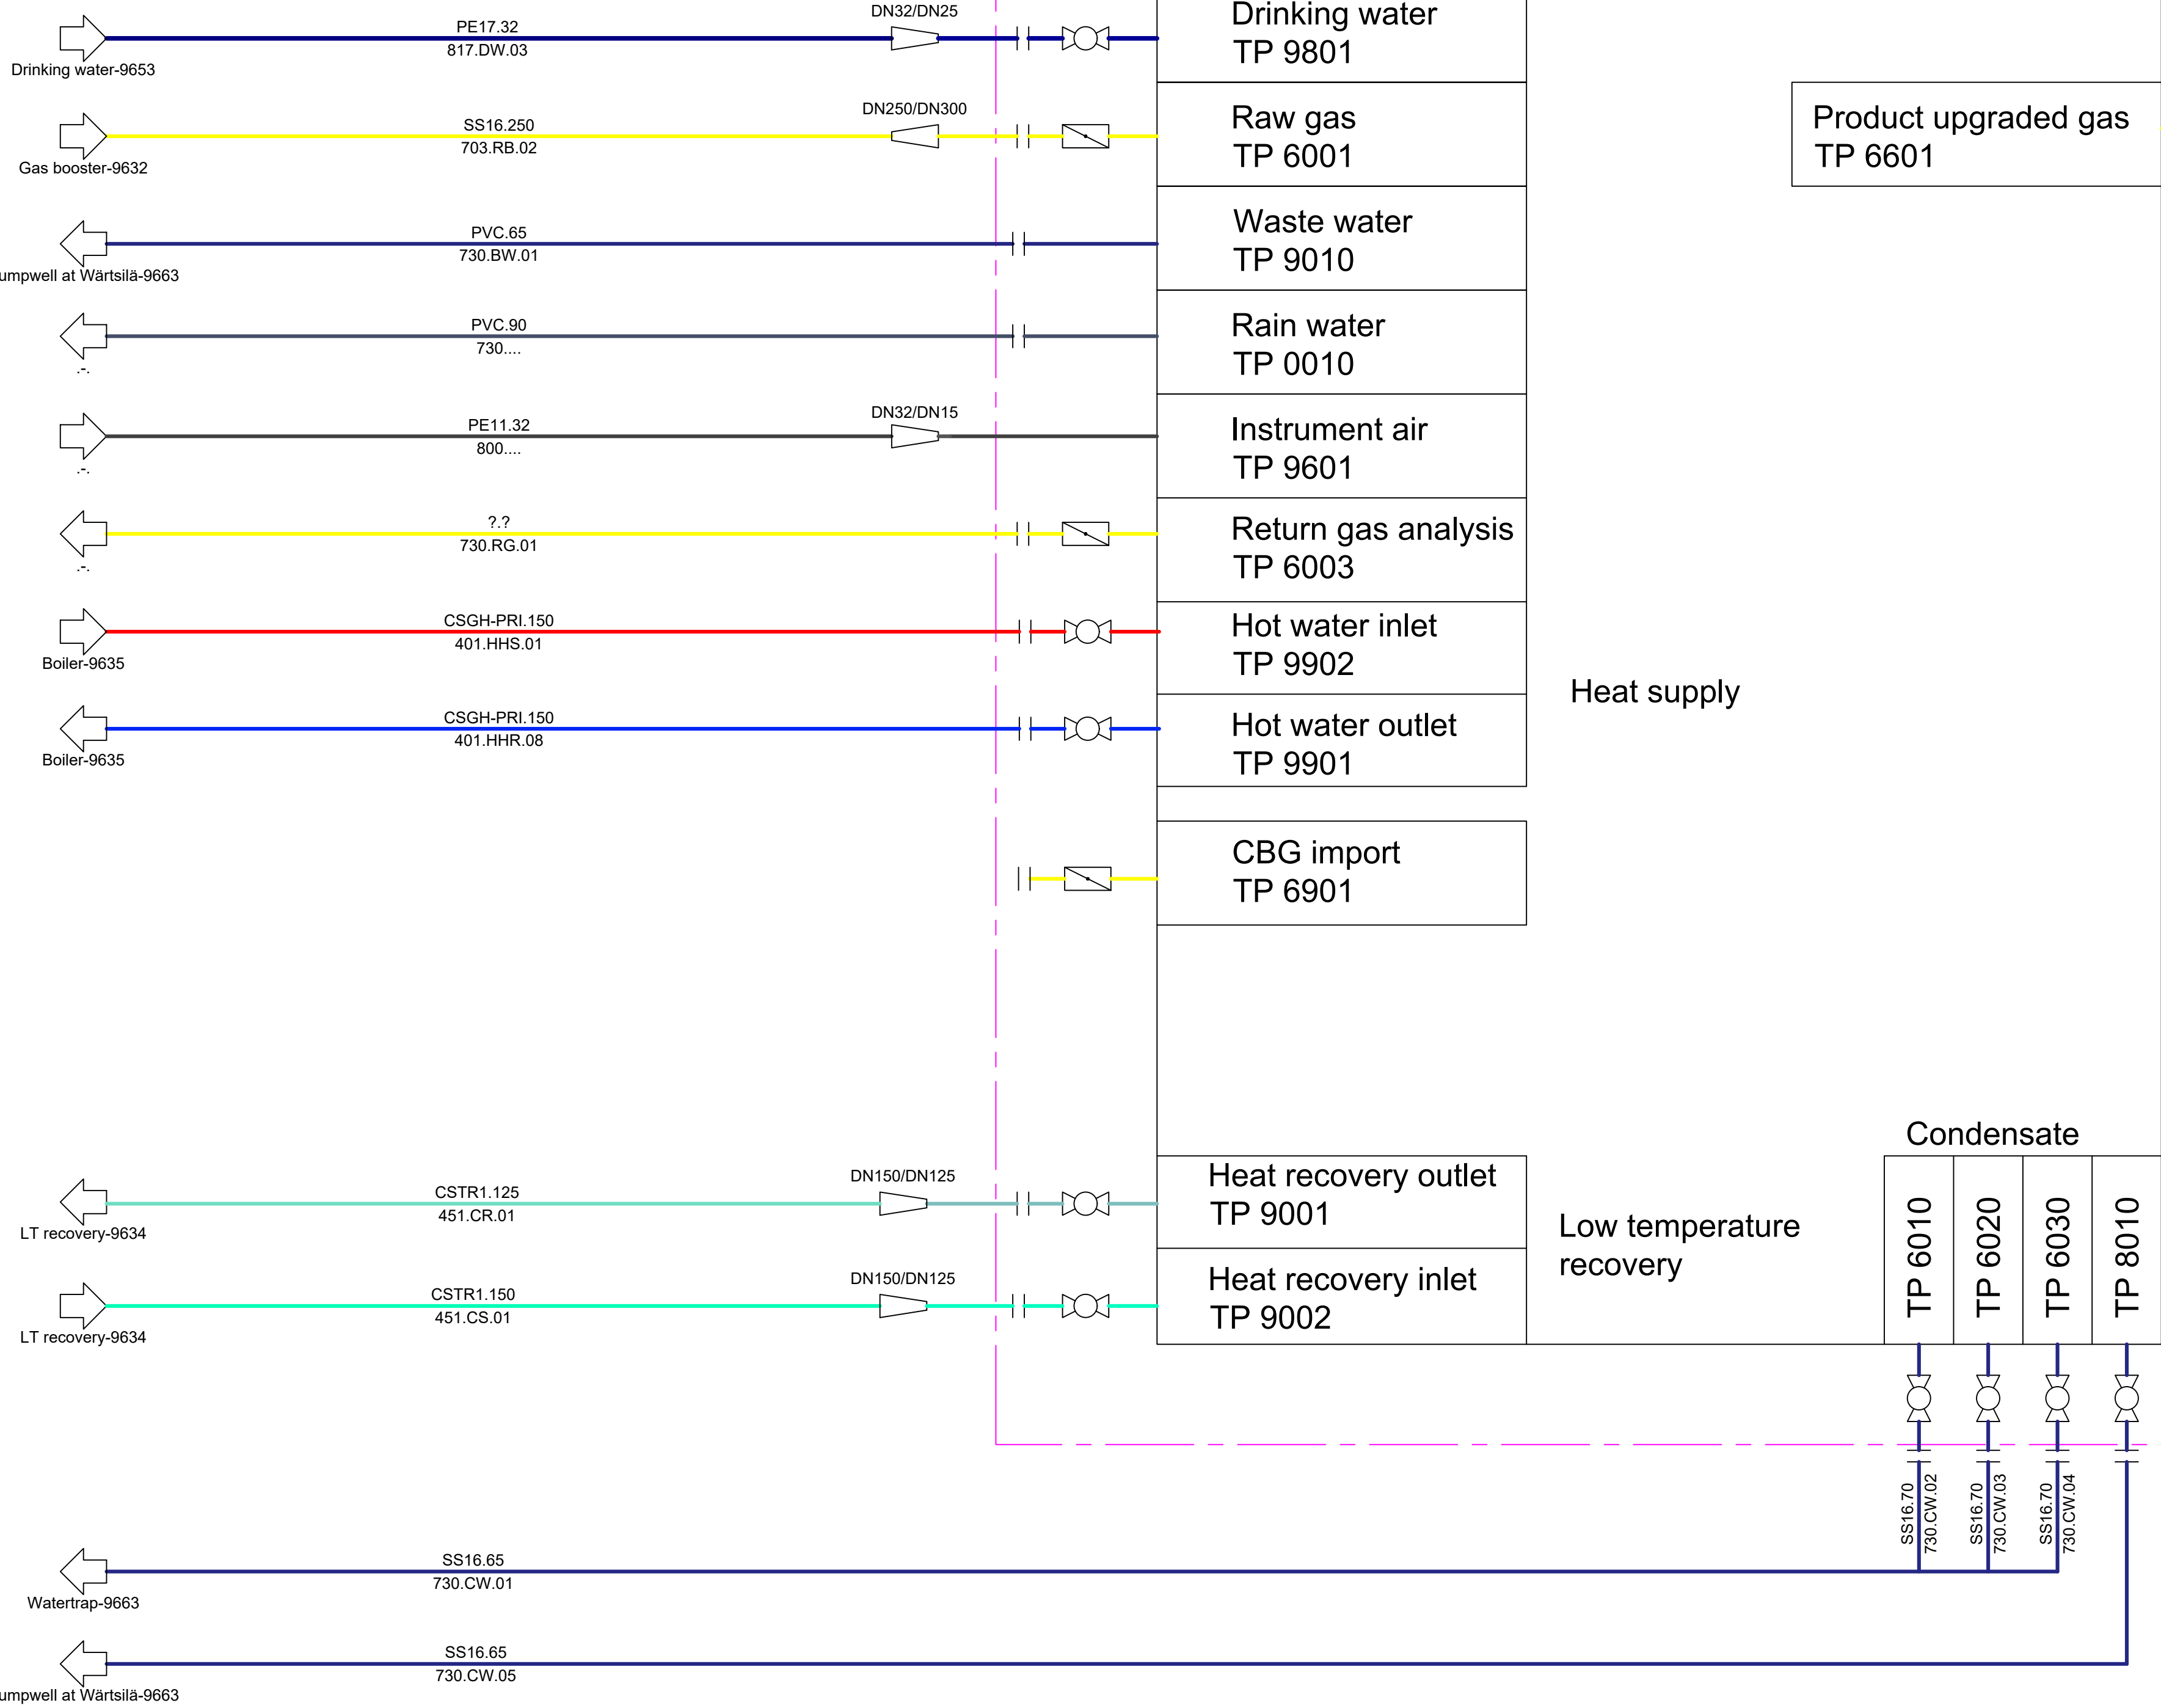

Product upgraded gas
TP 6601

BOG send-out
N7

AK
23

730.AK.LBG.923

Product upgraded gas
N1

Inlet

Liquefied gas
N2

Outlet

Inlet

Liquefied gas
N11

LBG send-out to truck
33S1800

Vapour return from
truck 33S1801

Nitrogen
N5

Heat supply

Low temperature
recovery

Condensate

TP 6010

TP 6020

TP 6030

TP 8010

Rev. Nr.: Rev. Dato: Rev. Description:

Builder: ST1

Project: SLK

Subject: Upgrade

Rev. 2


Int.:MDC QC.CM APP.: Date: 26-06-2025

LUNDSBY
RENEWABLE SOLUTIONS

Lundsby Renewable Solutions A/S, Hjarbækvej 65, 8831 Løgstrup
Tlf.: +45 96 49 43 00 Info@lundsby.dk
This Drawing is subject to copyright and may not be reproduced
without permission from Lundsby Renewable Solutions A/S

Project nr...:1768
Drawing nr...:
9633

FORMAT: A1

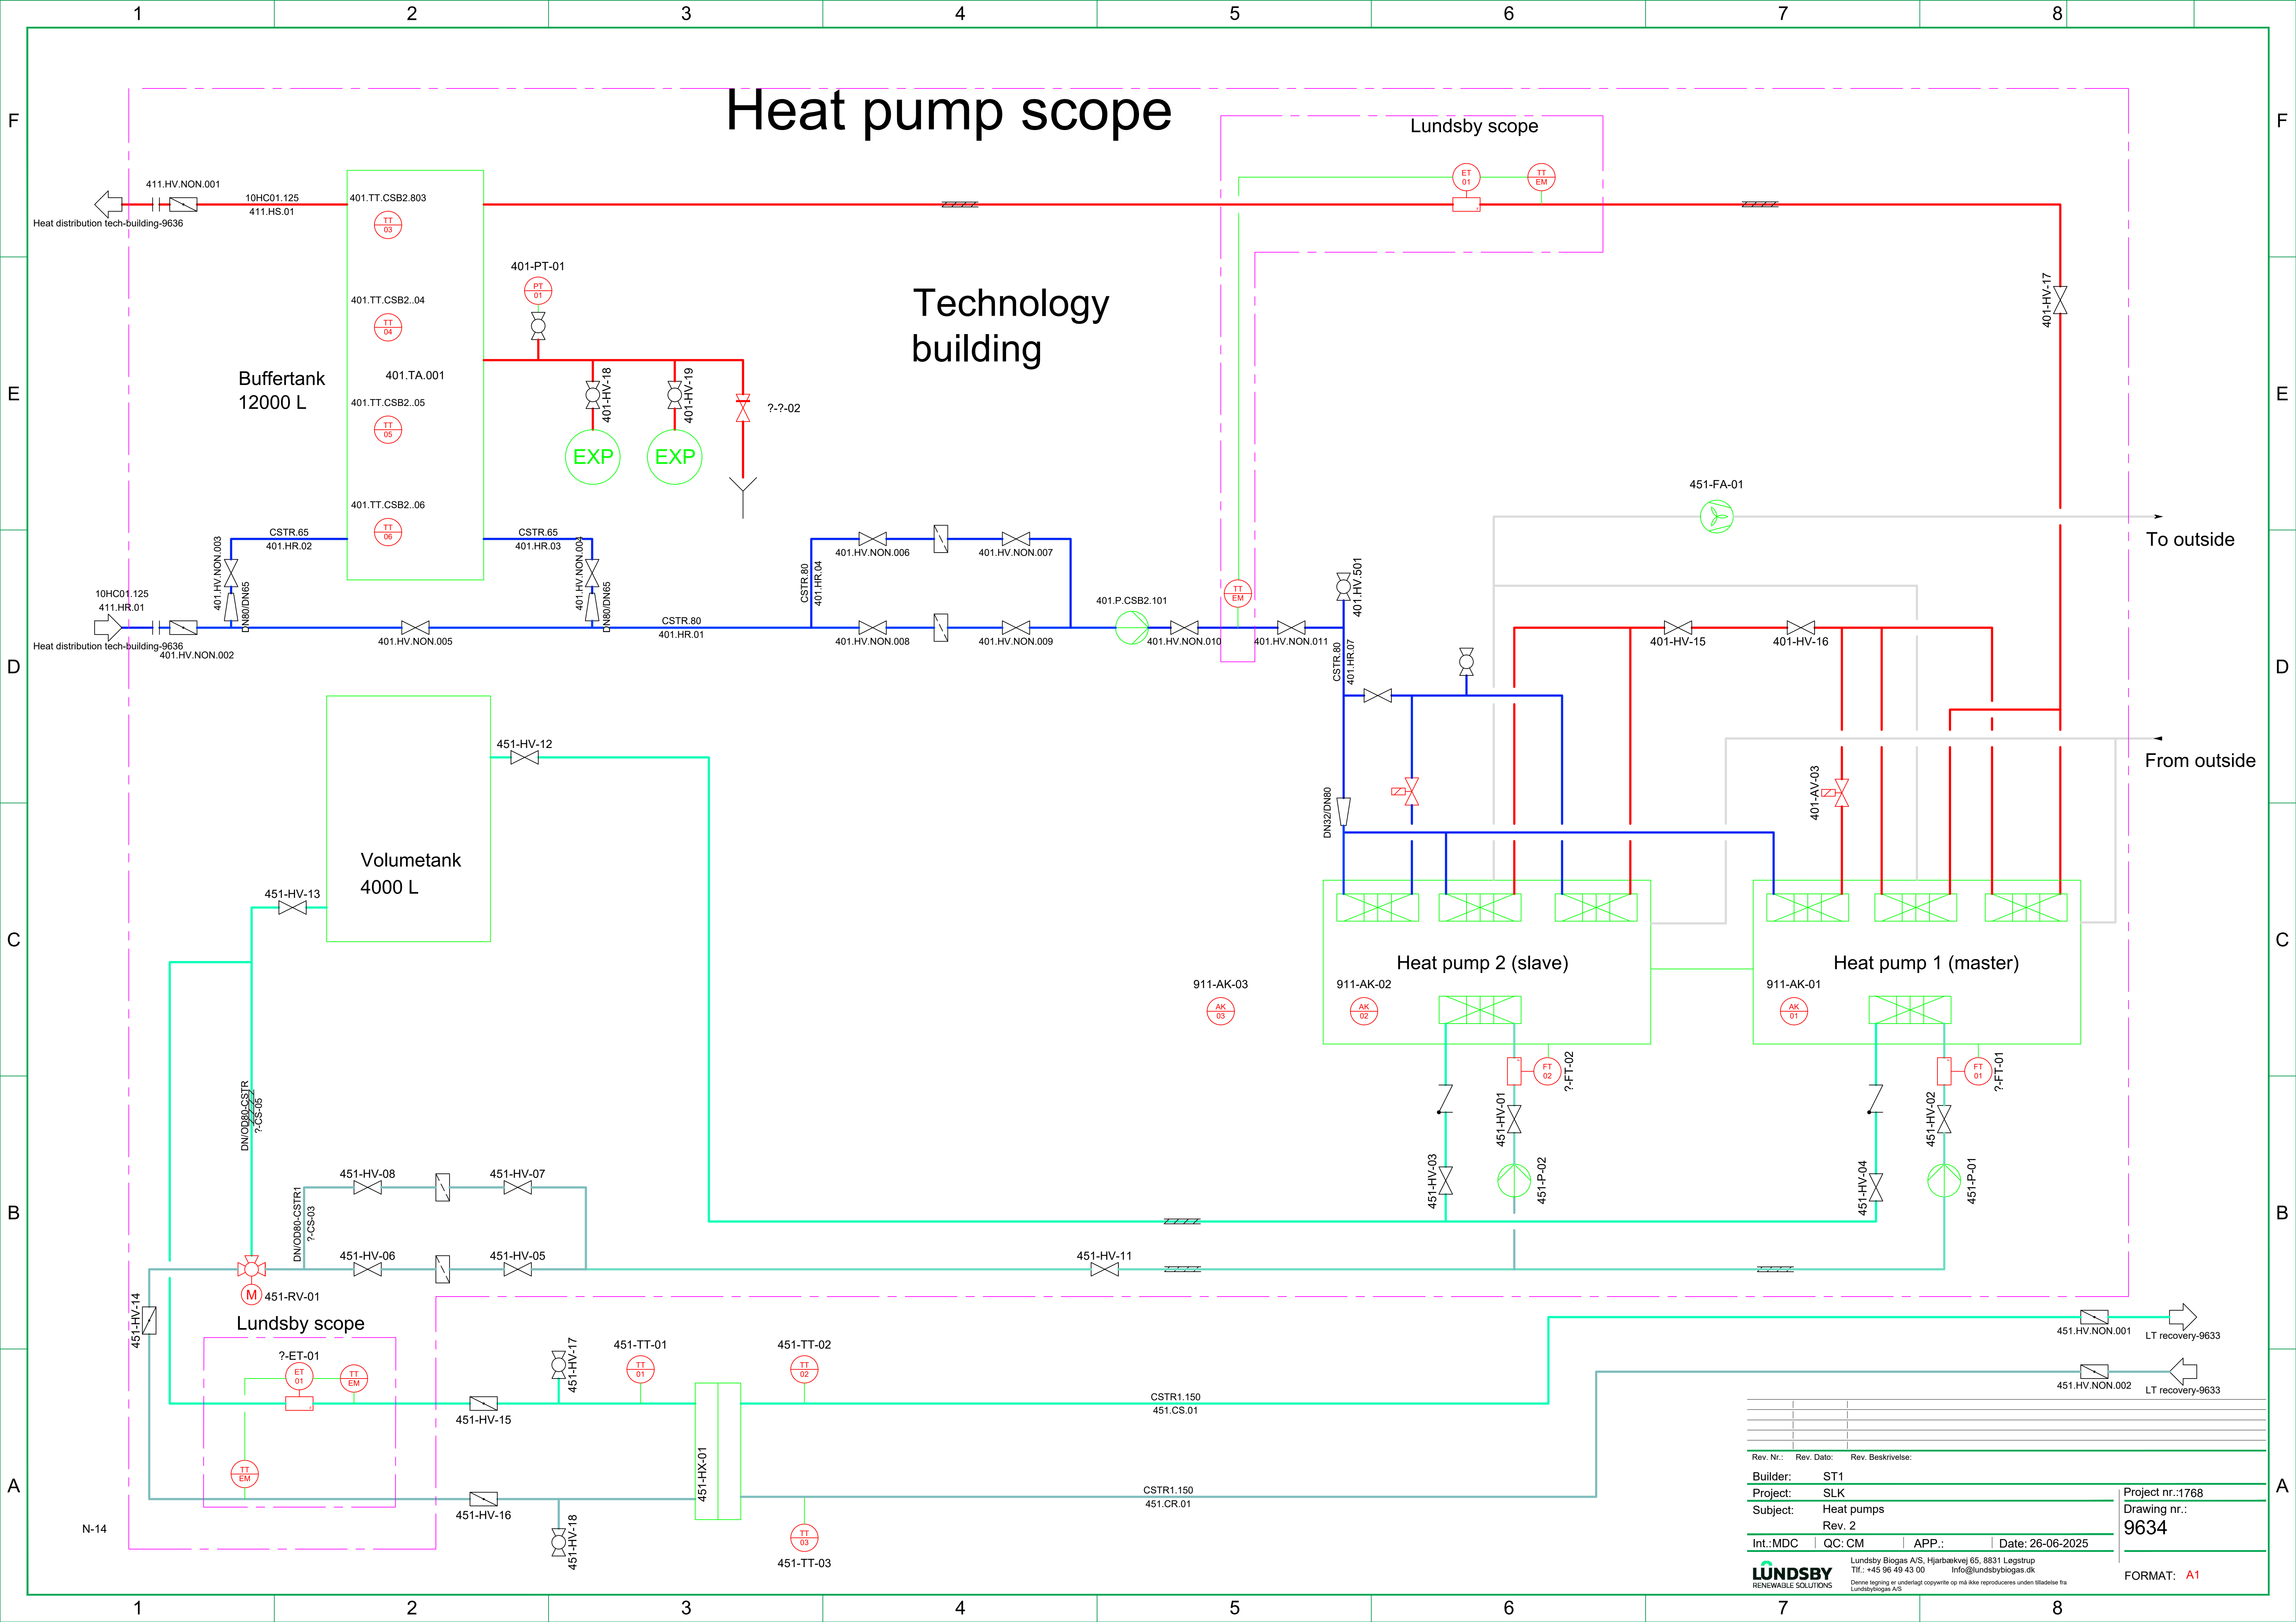

Heat pump scope

Technology building

Lundsby scope

Buffertank
12000 L

Volumetank
4000 L

Heat pump 2 (slave)


Heat pump 1 (master)

To outside

From outside

Lundsby scope

Rev. Nr.:	Rev. Dato:	Rev. Beskrivelse:
Builder:	ST1	
Project:	SLK	
Subject:	Heat pumps	
Rev. 2		
Int.:MDC	QC: CM	APP.: Date: 26-06-2025
LUNDSBY RENEWABLE SOLUTIONS		
Lundsby Biogas A/S, Hjarbækvej 65, 8831 Løgstrup Tlf.: +45 96 49 43 00 info@lundsbybiogas.dk Denne tegning er underlagt copywrite op må ikke reproducere uden tilladelse fra Lundsbybiogas A/S		
Project nr.:1768 Drawing nr.: 9634		FORMAT: A1

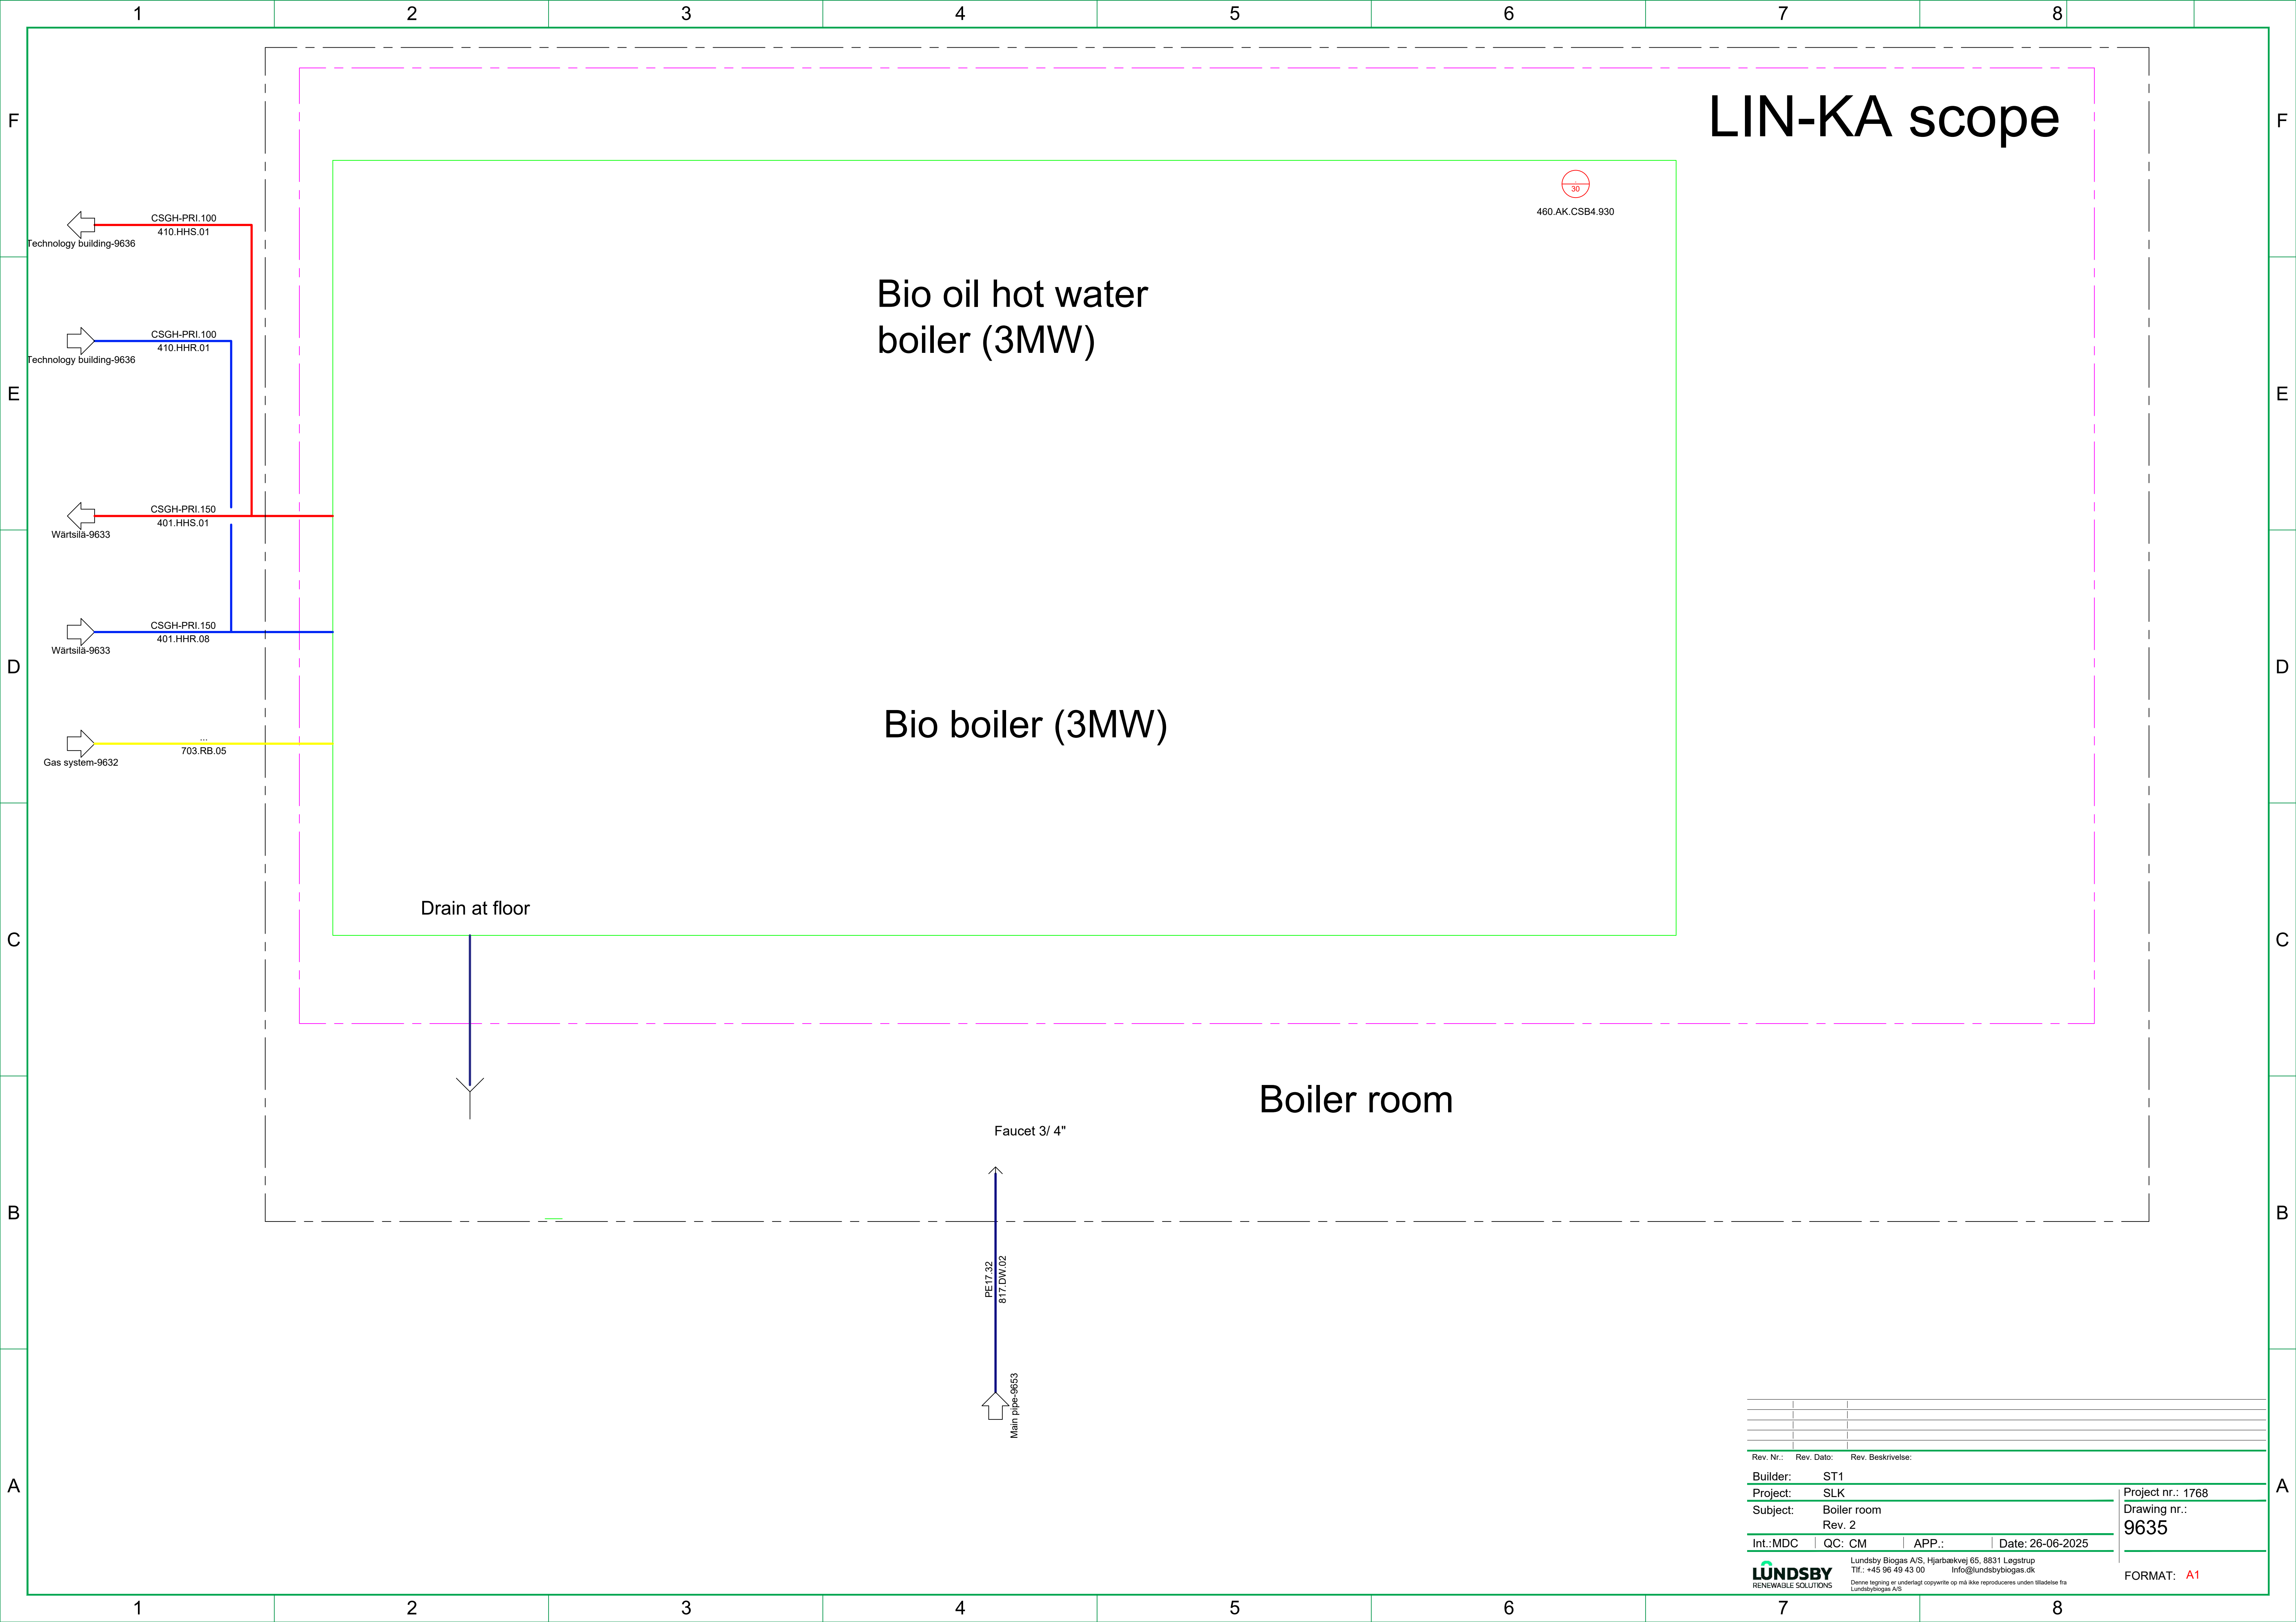

LIN-KA scope

Bio oil hot water
boiler (3MW)

Bio boiler (3MW)

Drain at floor


Boiler room

Faucet 3/ 4"


PE17.32
817/DW.02
Main pipe-9653

Rev. Nr.:	Rev. Dato:	Rev. Beskrivelse:	
Builder:	ST1		
Project:	SLK		
Subject:	Boiler room		
Int.:MDC	QC: CM	APP.:	Date: 26-06-2025
LUNDSBY RENEWABLE SOLUTIONS			Lundsby Biogas A/S, Hjarbækvej 65, 8831 Løgstrup Tlf.: +45 96 49 43 00 Info@lundsbybiogas.dk Denne tegning er underlagt copywrite op må ikke reproducere uden tilladelse fra Lundsbybiogas A/S
			Project nr.: 1768 Drawing nr.: 9635 FORMAT: A1

Heat technology building

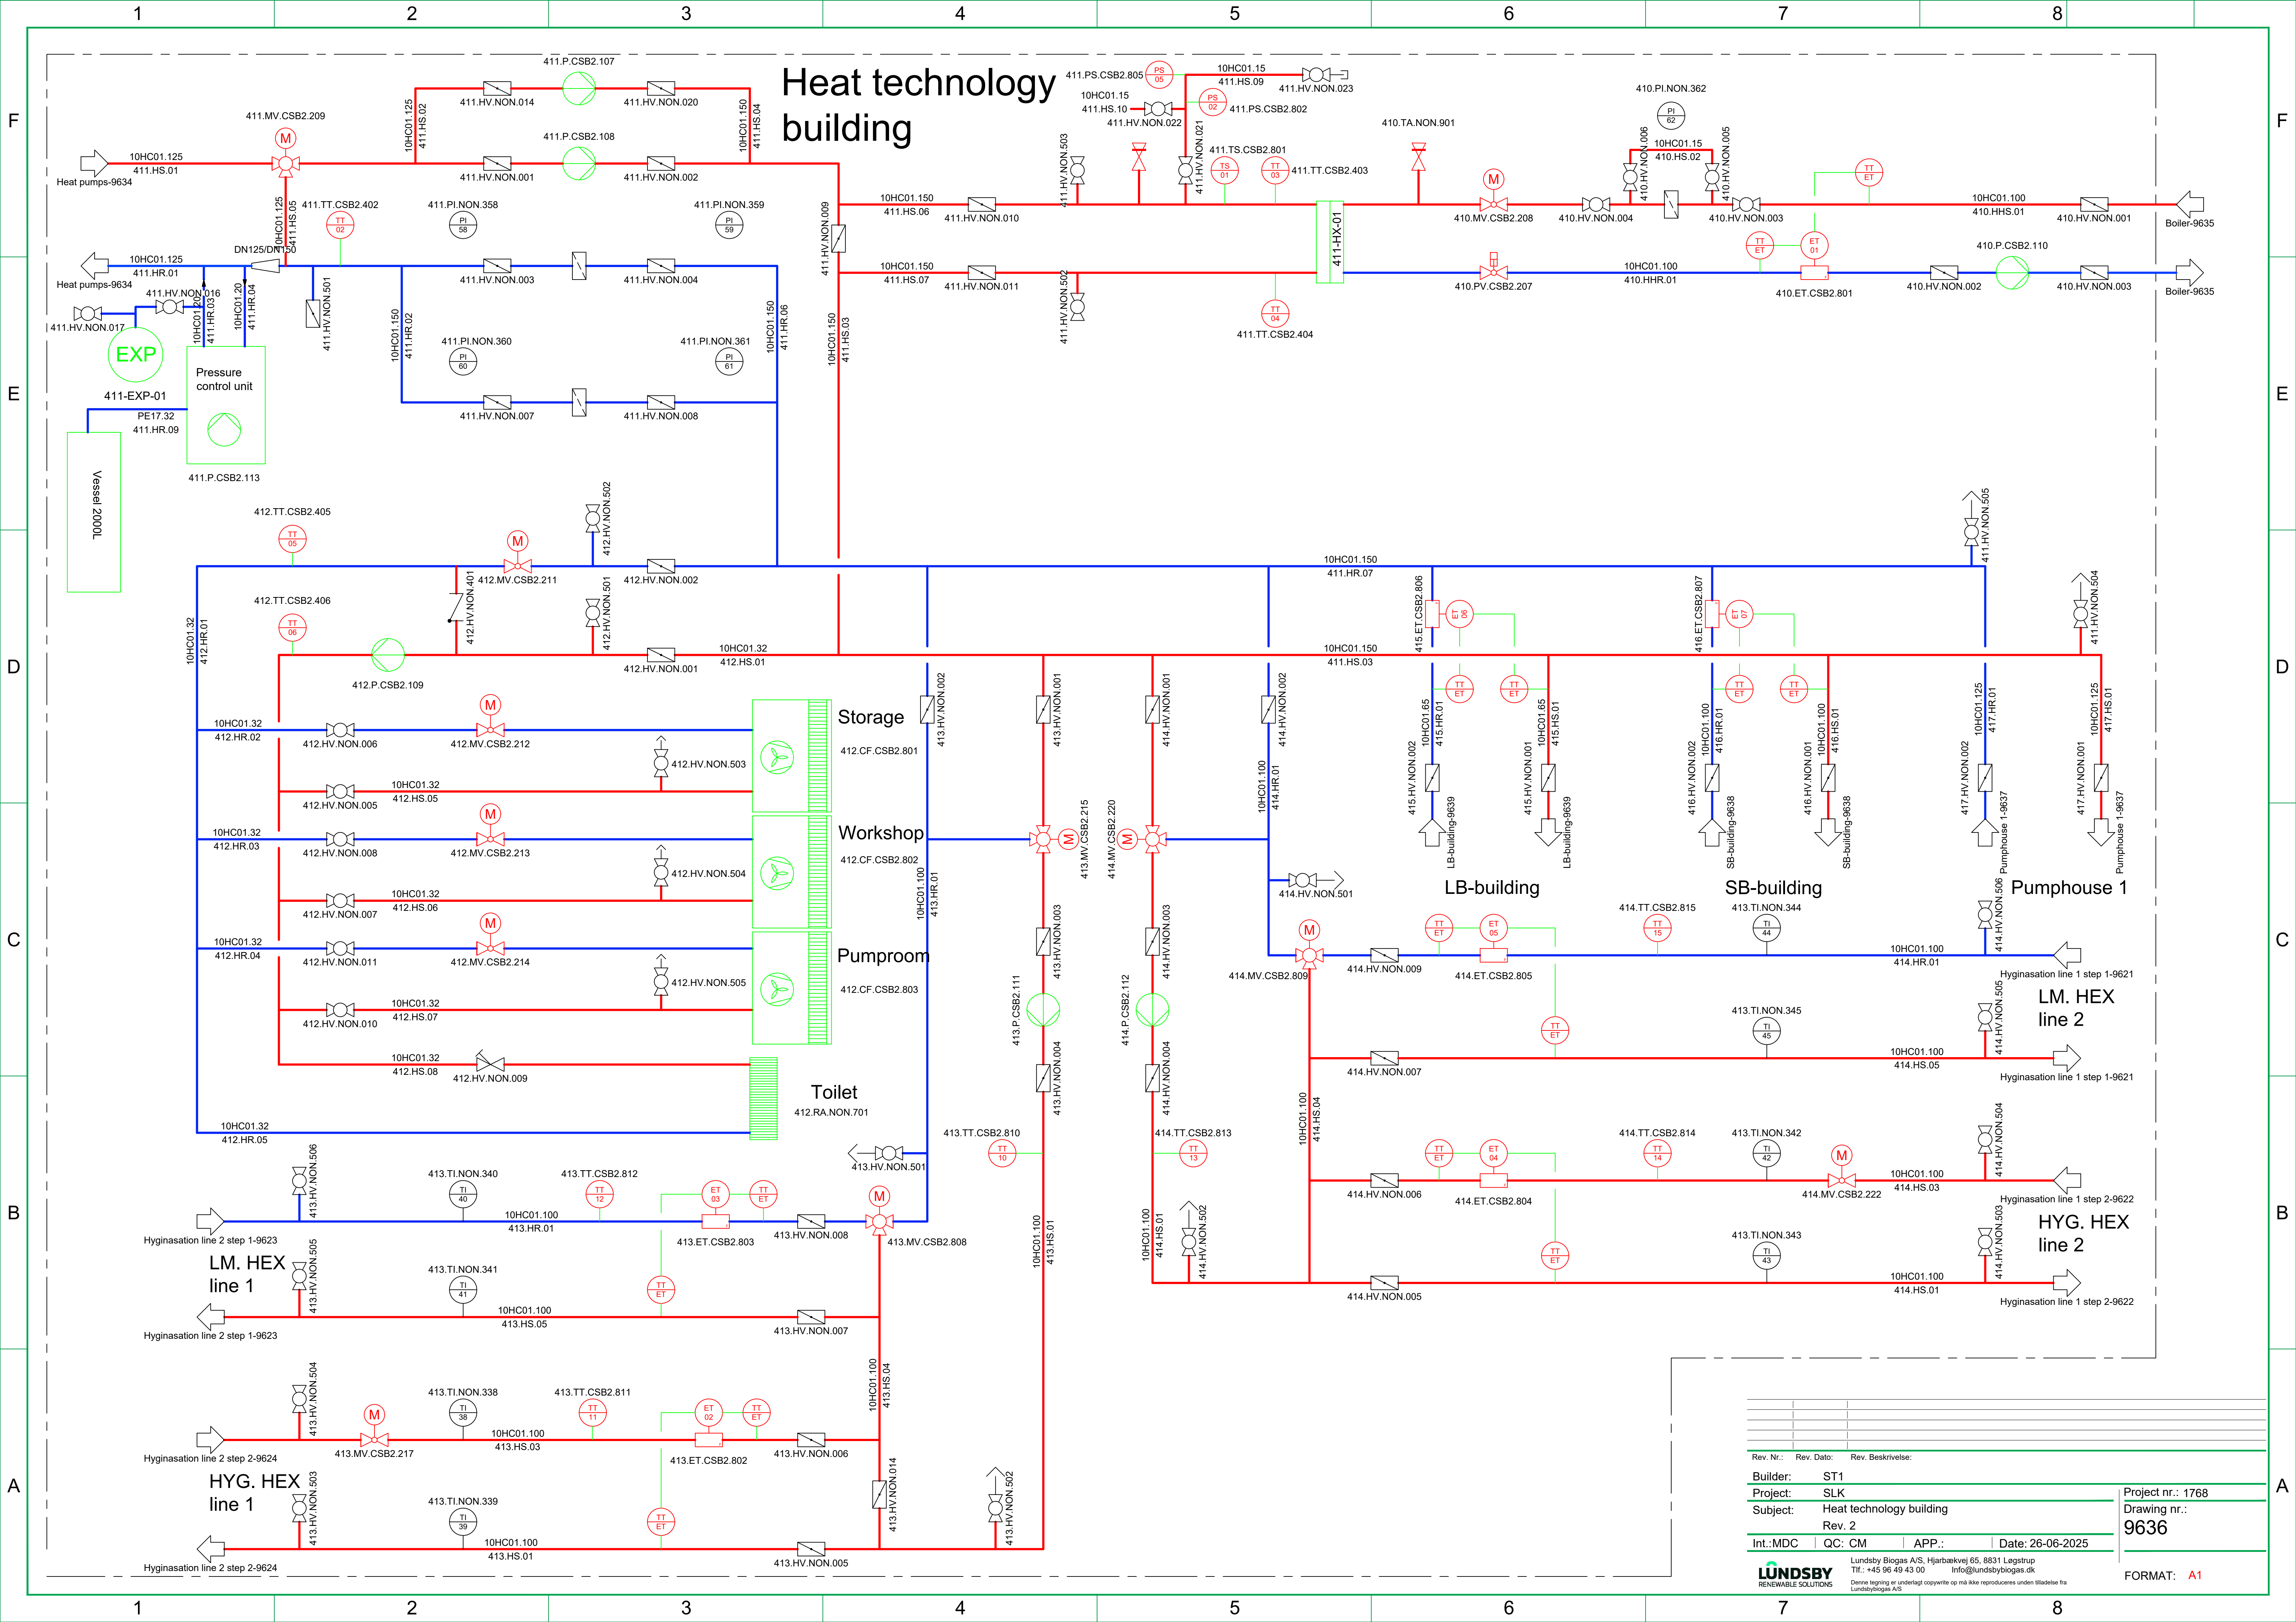

Rev. Nr.:	Rev. Dato:	Rev. Beskrivelse:
Builder:	ST1	
Project:	SLK	
Subject:	Heat technology building	
Rev. 2		
Int.:MDC	QC: CM	APP.: Date: 26-06-2025
LUNDSBY RENEWABLE SOLUTIONS		
Lundsby Biogas A/S, Hjarbækvej 65, 8831 Løgstrup Tlf.: +45 96 49 43 00 info@lundsbybiogas.dk Denne tegning er underlagt copyright og må ikke reproducere uden tilladelse fra Lundsbybiogas A/S		
Project nr.: 1768 Drawing nr.: 9636		FORMAT: A1

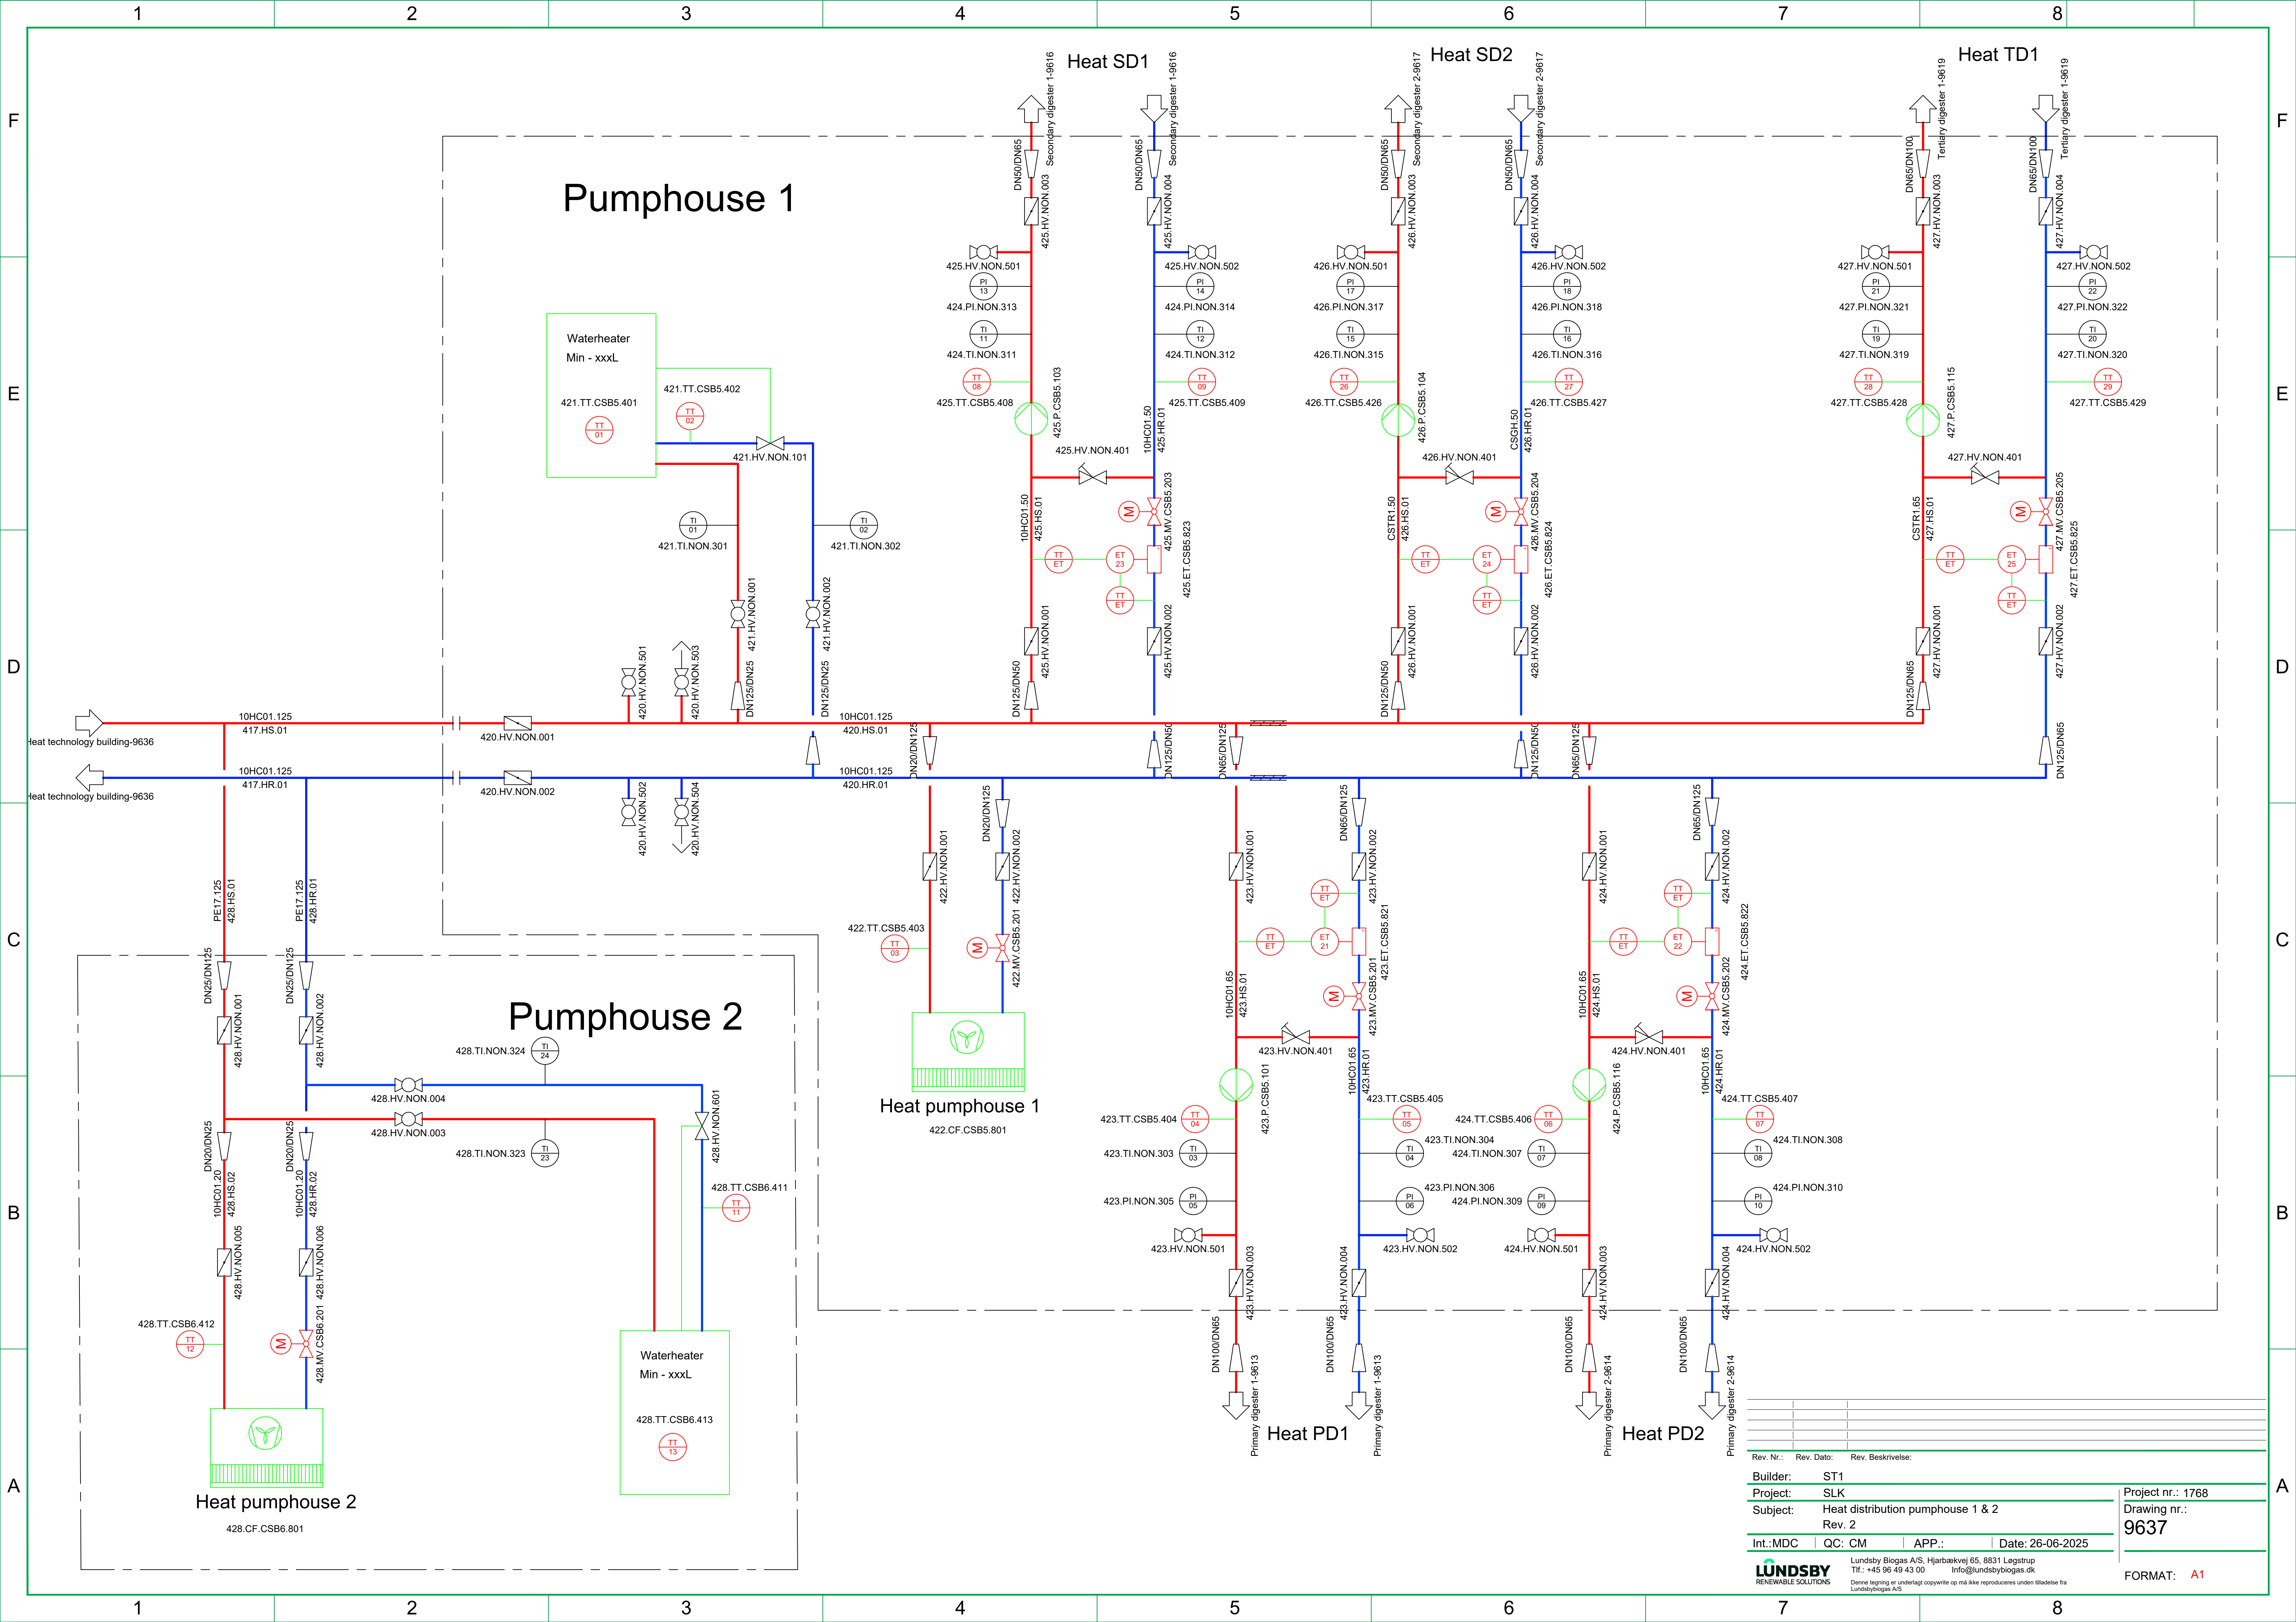

Rev. Nr.:	Rev. Dato:	Rev. Beskrivelse:
Builder:	ST1	
Project:	SLK	
Subject:	Heat distribution pumphouse 1 & 2	
Rev. 2		
Int.:MDC	QC: CM	APP.: Date: 26-06-2025


LUNDSBY
RENEWABLE SOLUTIONS
Lundsby Biogas A/S, Hjarbækvej 65, 8831 Løgstrup
Tlf.: +45 96 49 43 00
info@lundsbybiogas.dk
Denne tegning er underlagt copyright op på ikke reproduceres uden tilladelse fra
Lundsbybiogas A/S

Project nr.: 1768
Drawing nr.:
9637

FORMAT: A1


SB-Building

Adminstration

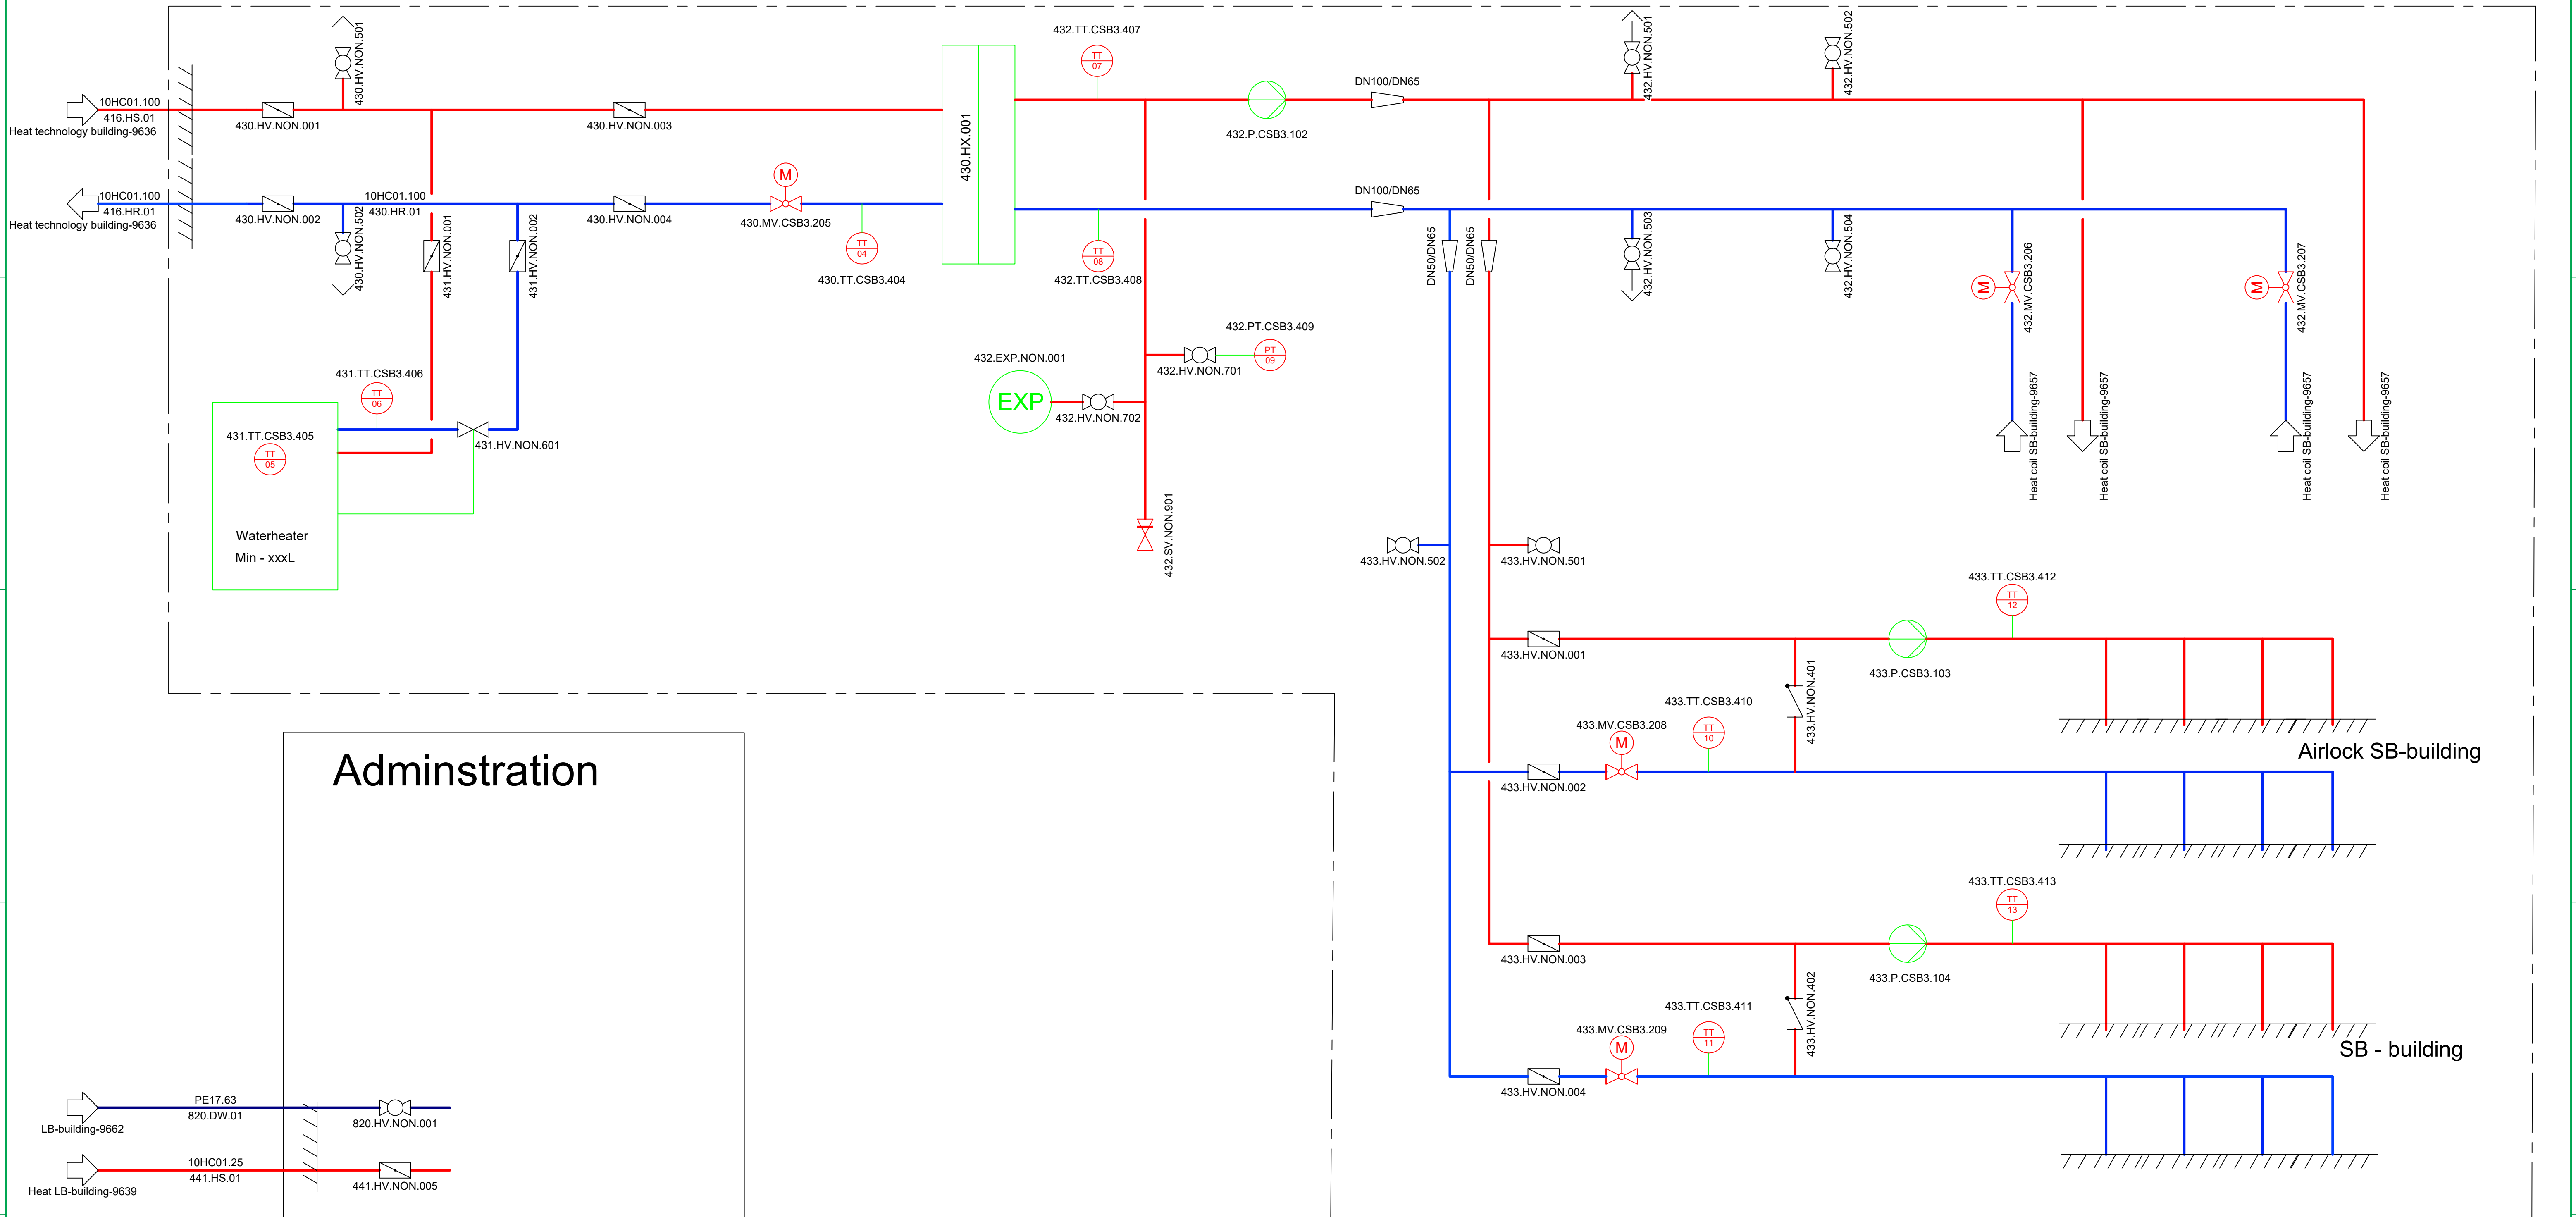


Rev. Nr.:	Rev. Dato:	Rev. Beskrivelse:	
Builder:	ST1		
Project:	SLK		
Subject:	Heat distribution SB-building		
Rev. 2			
Int.:MDC	QC: CM	APP.:	Date: 26-06-2025
LUNDSBY RENEWABLE SOLUTIONS			Lundsby Biogas A/S, Hjarbækvej 65, 8831 Løgstrup Tlf.: +45 96 49 43 00 info@lundsbybiogas.dk Denne tegning er underlagt copywrite op må ikke reproduceres uden tilladelse fra Lundsbybiogas A/S
Project nr.: 1768 Drawing nr.: 9638			FORMAT: A1

LB-Building

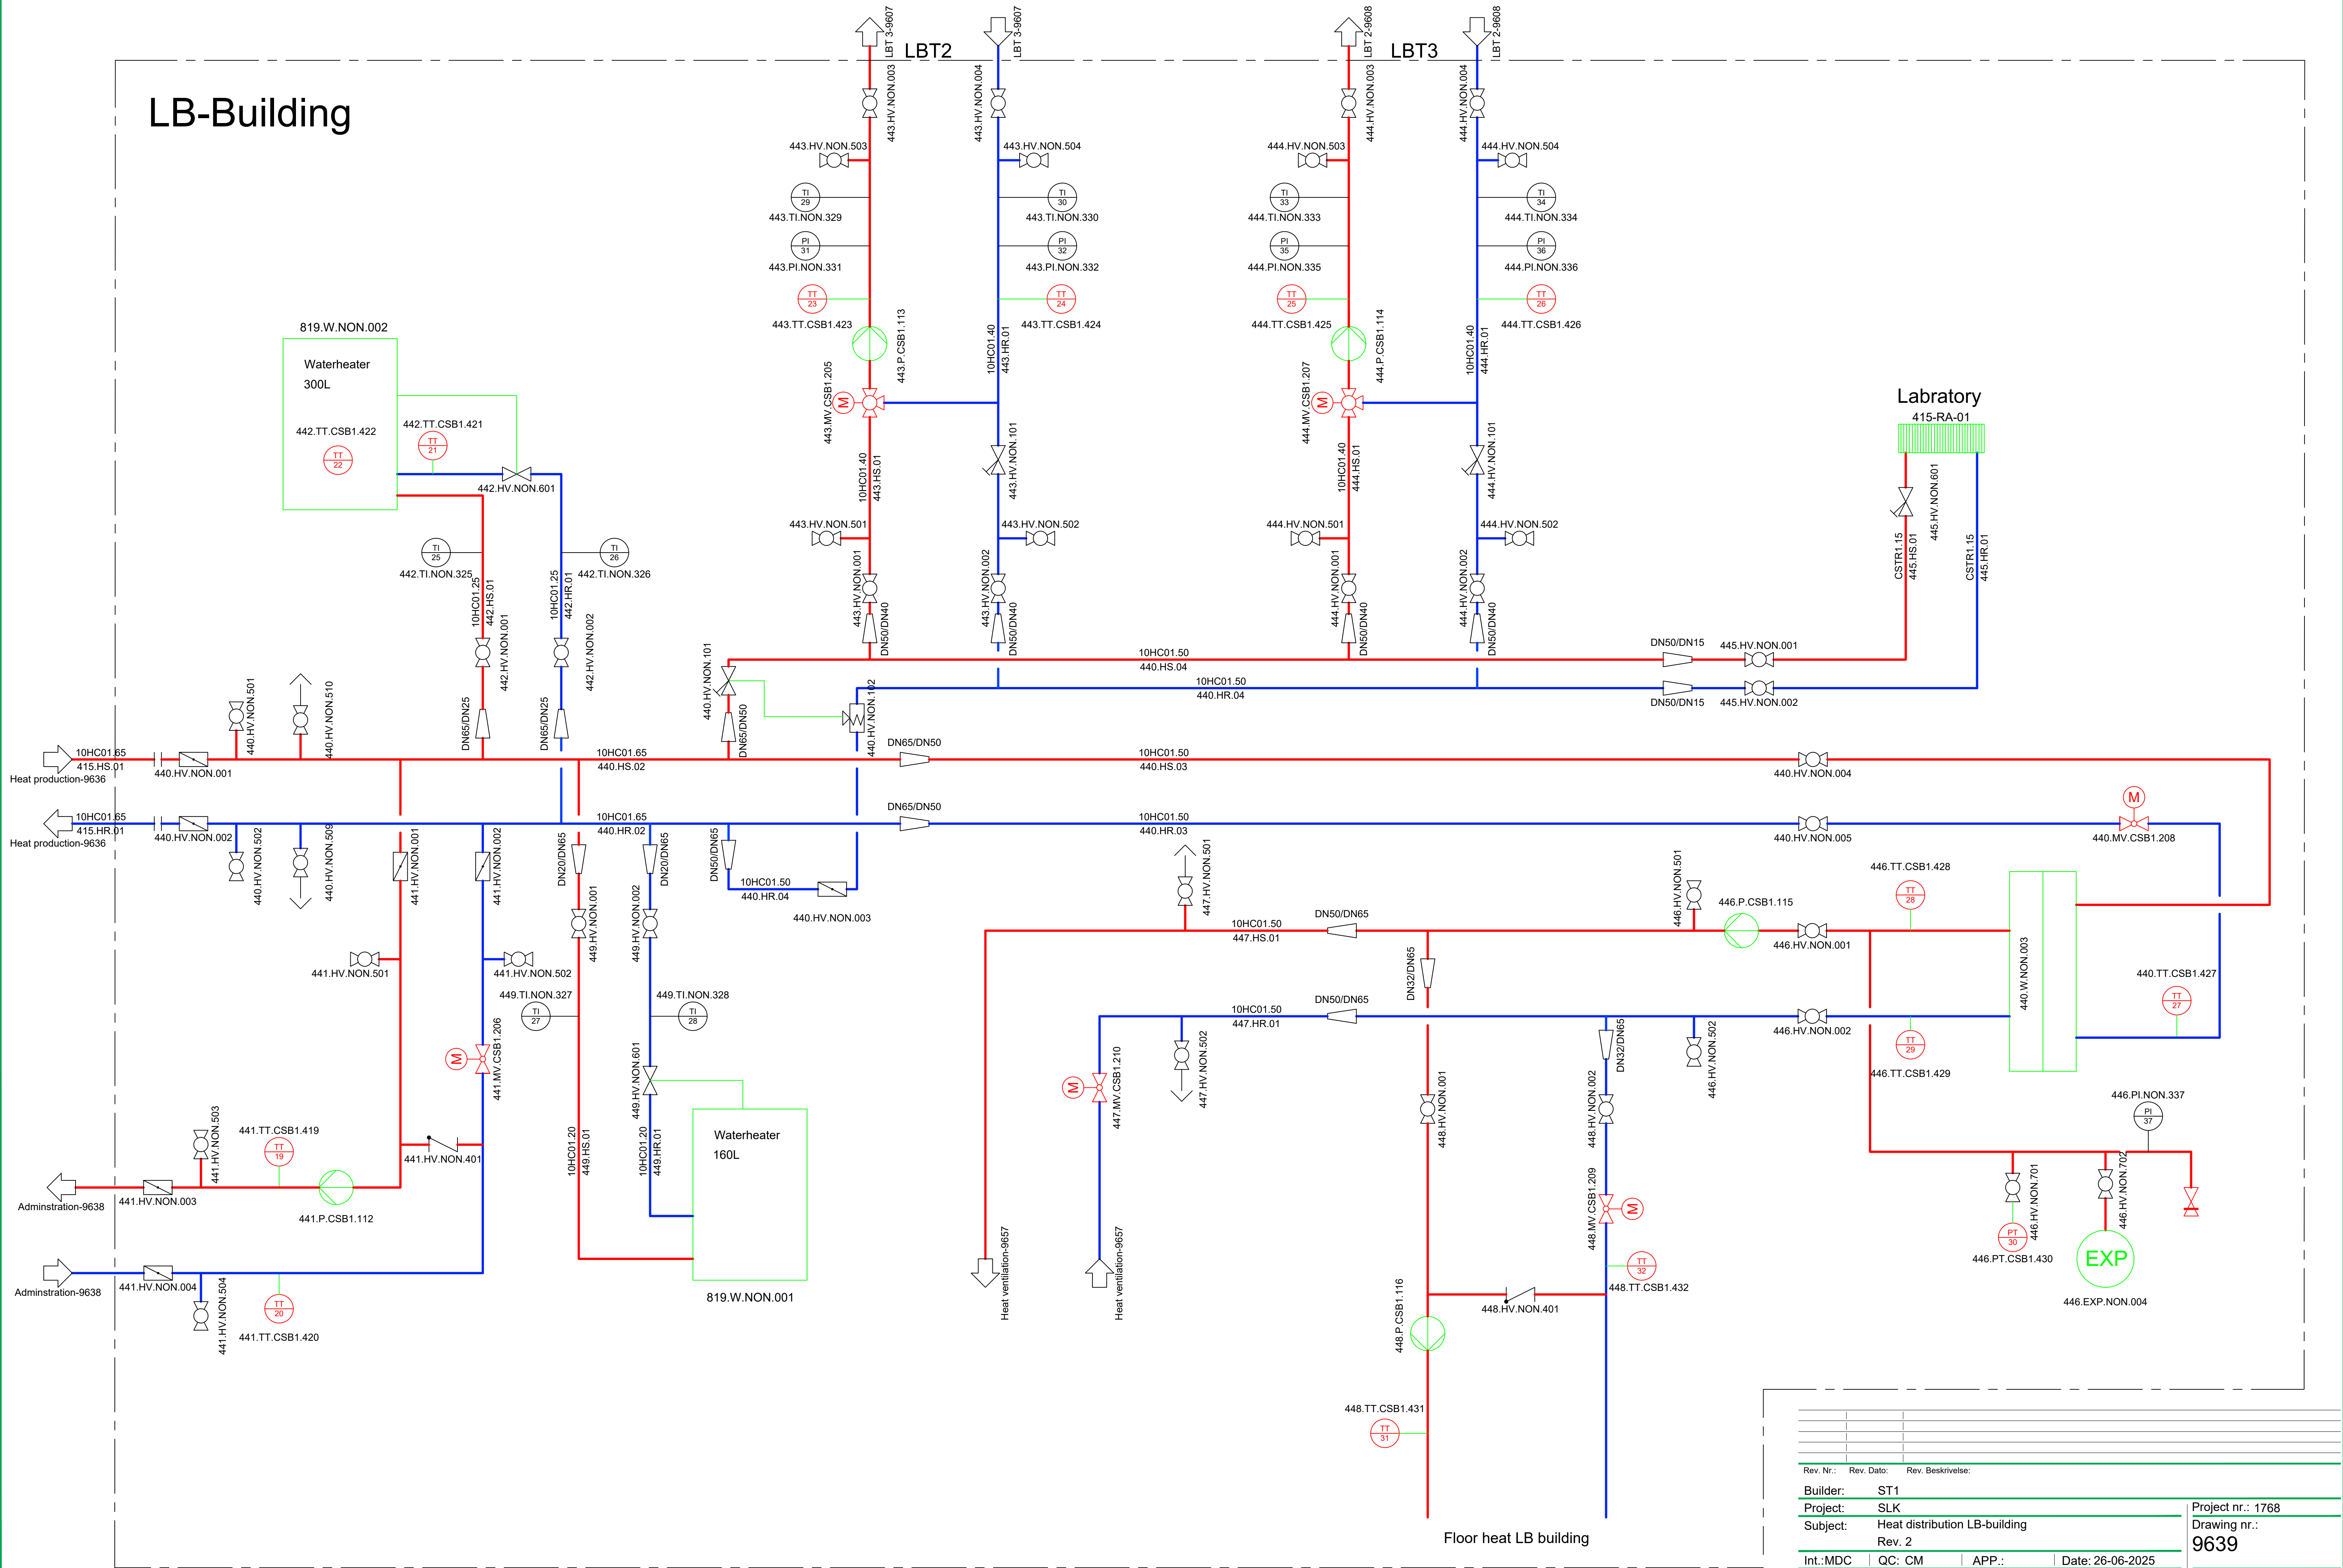


Rev. Nr.:	Rev. Dato:	Rev. Beskrivelse:
Builder:	ST1	
Project:	SLK	
Subject:	Heat distribution LB-building	
Rev. 2		
Int.:MDC	QC: CM	APP.: Date: 26-06-2025
LUNDSBY RENEWABLE SOLUTIONS		
Lundsby Biogas A/S, Hjarbækvej 65, 8831 Løgstrup Tlf.: +45 96 49 43 00 info@lundsbybiogas.dk		
Denne tegning er underlagt copyright og må ikke reproduceres uden tilladelse fra Lundsbybiogas A/S		
Project nr.: 1768		
Drawing nr.: 9639		
FORMAT: A1		


851-TA-01
Pumpwell at LB-building

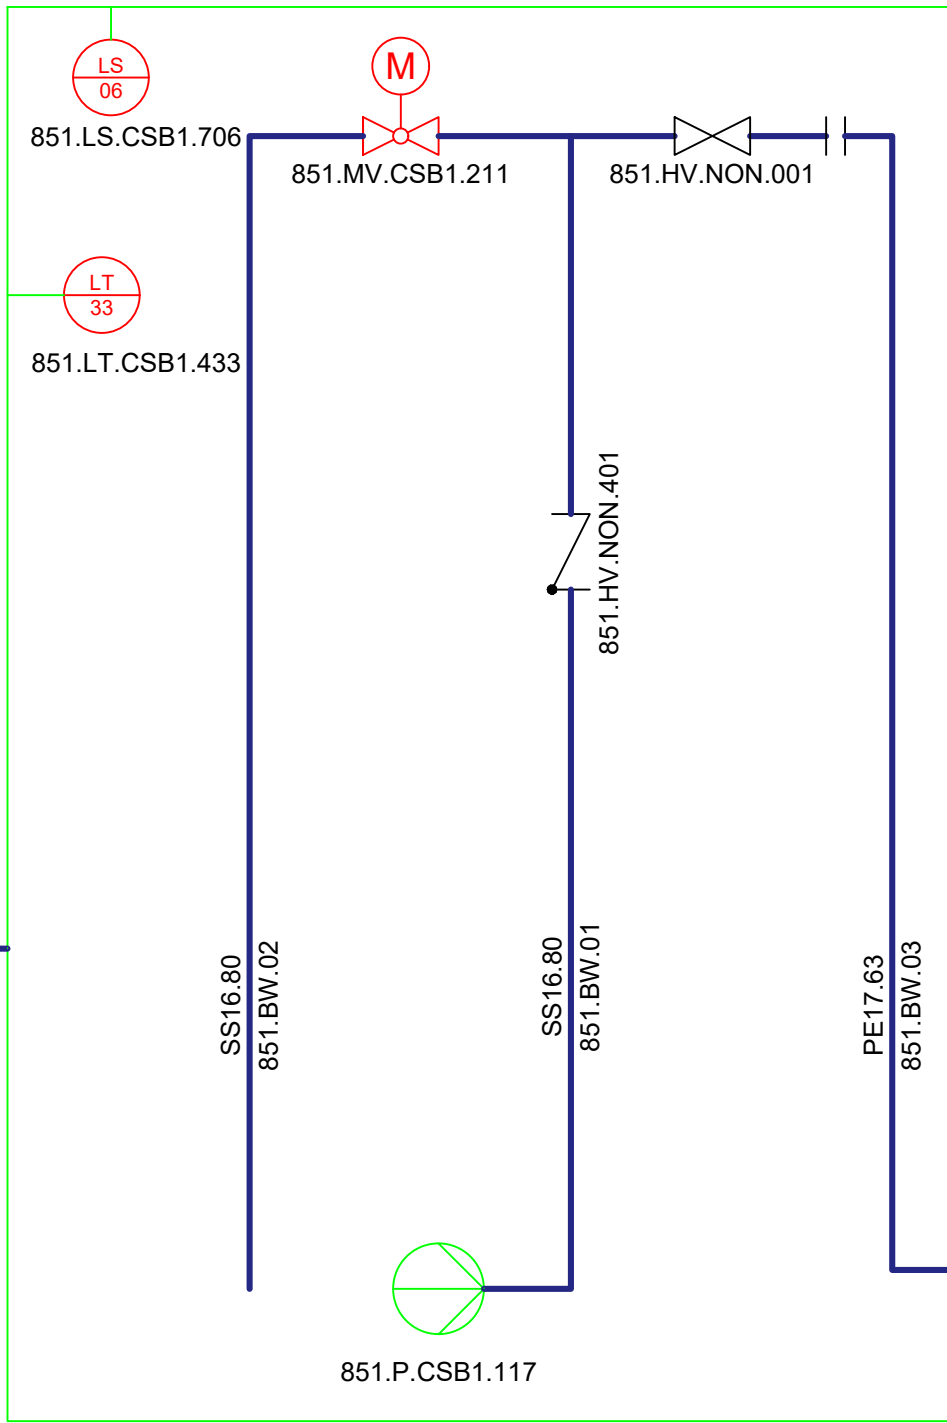


852-TA-01
Pumpwell at Pumphouse 1

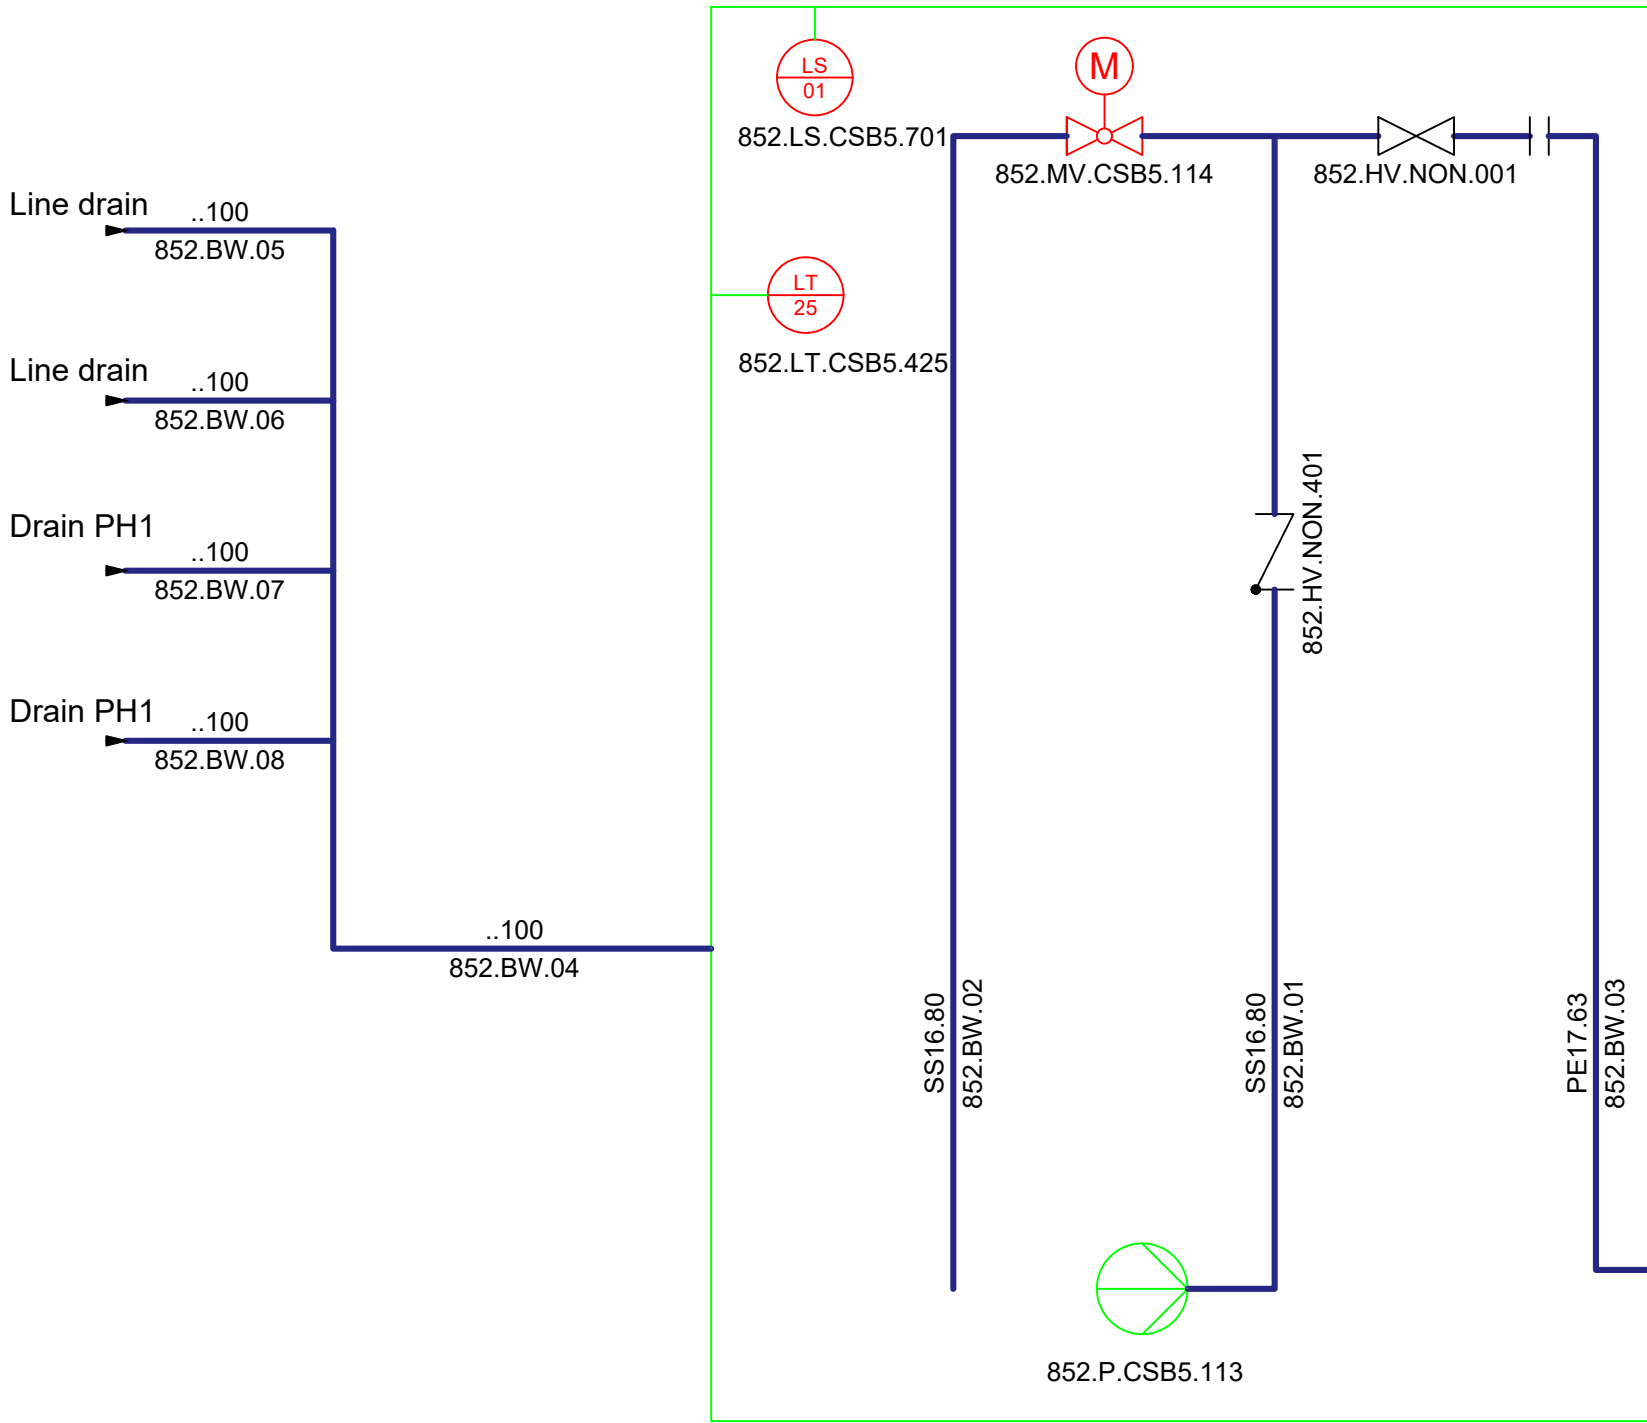

853-TA-01
Pumpwell at Tech. building

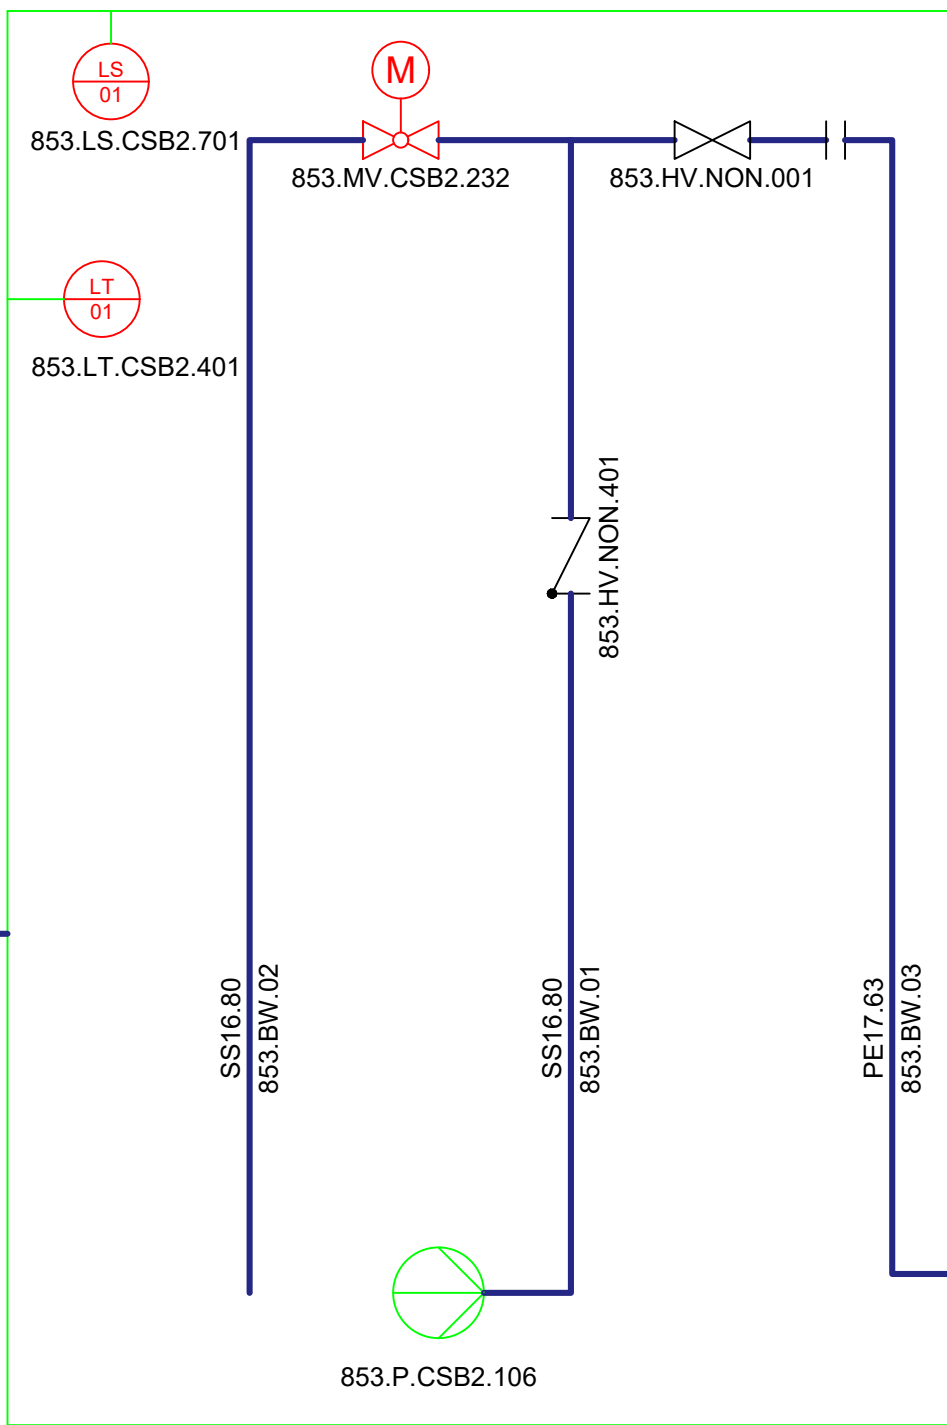


854-TA-01
Pumpwell at Pumphouse 2

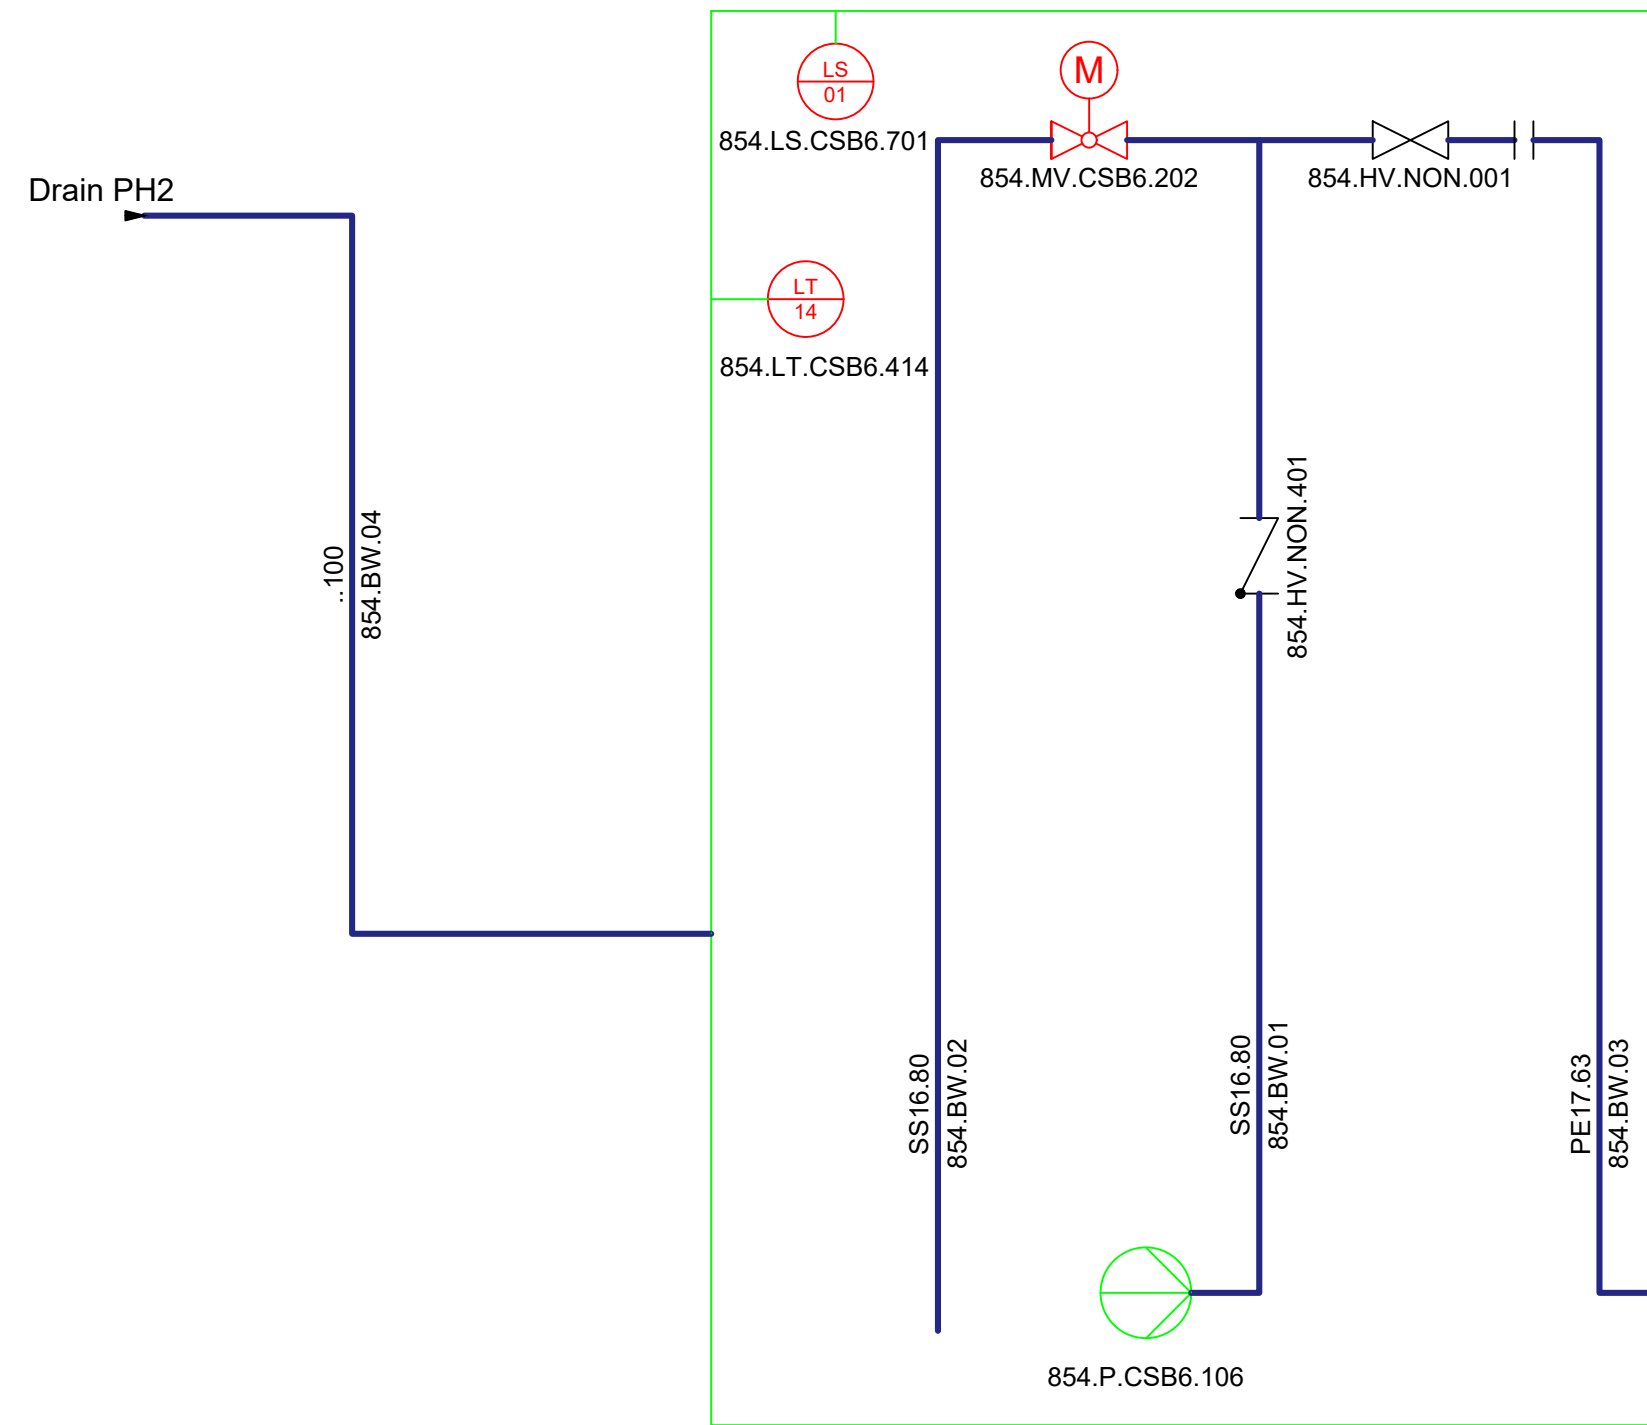


Rev. Nr.:	Rev. Dato:	Rev. Description:	
Builder:	ST1		
Project:	SLK		
Subject:	Blackwater wells		
Rev. 2			
Int.:MDC	QC:CM	APP.:	Date: 26-06-2025
LUNDSBY RENEWABLE SOLUTIONS			Lundsby Renewable Solutions A/S, Hjarbrækvej 65, 8831 Lægstrup Tlf.: +45 96 49 43 00 Info@lundsby.dk This Drawing is subject to copyright and may not be reproduced without permission from Lundsby Renewable Solutions A/S
			Project nr.:1768 Drawing nr.: 9640 FORMAT: A1

Pumphouse 1


JA Trykluft scope

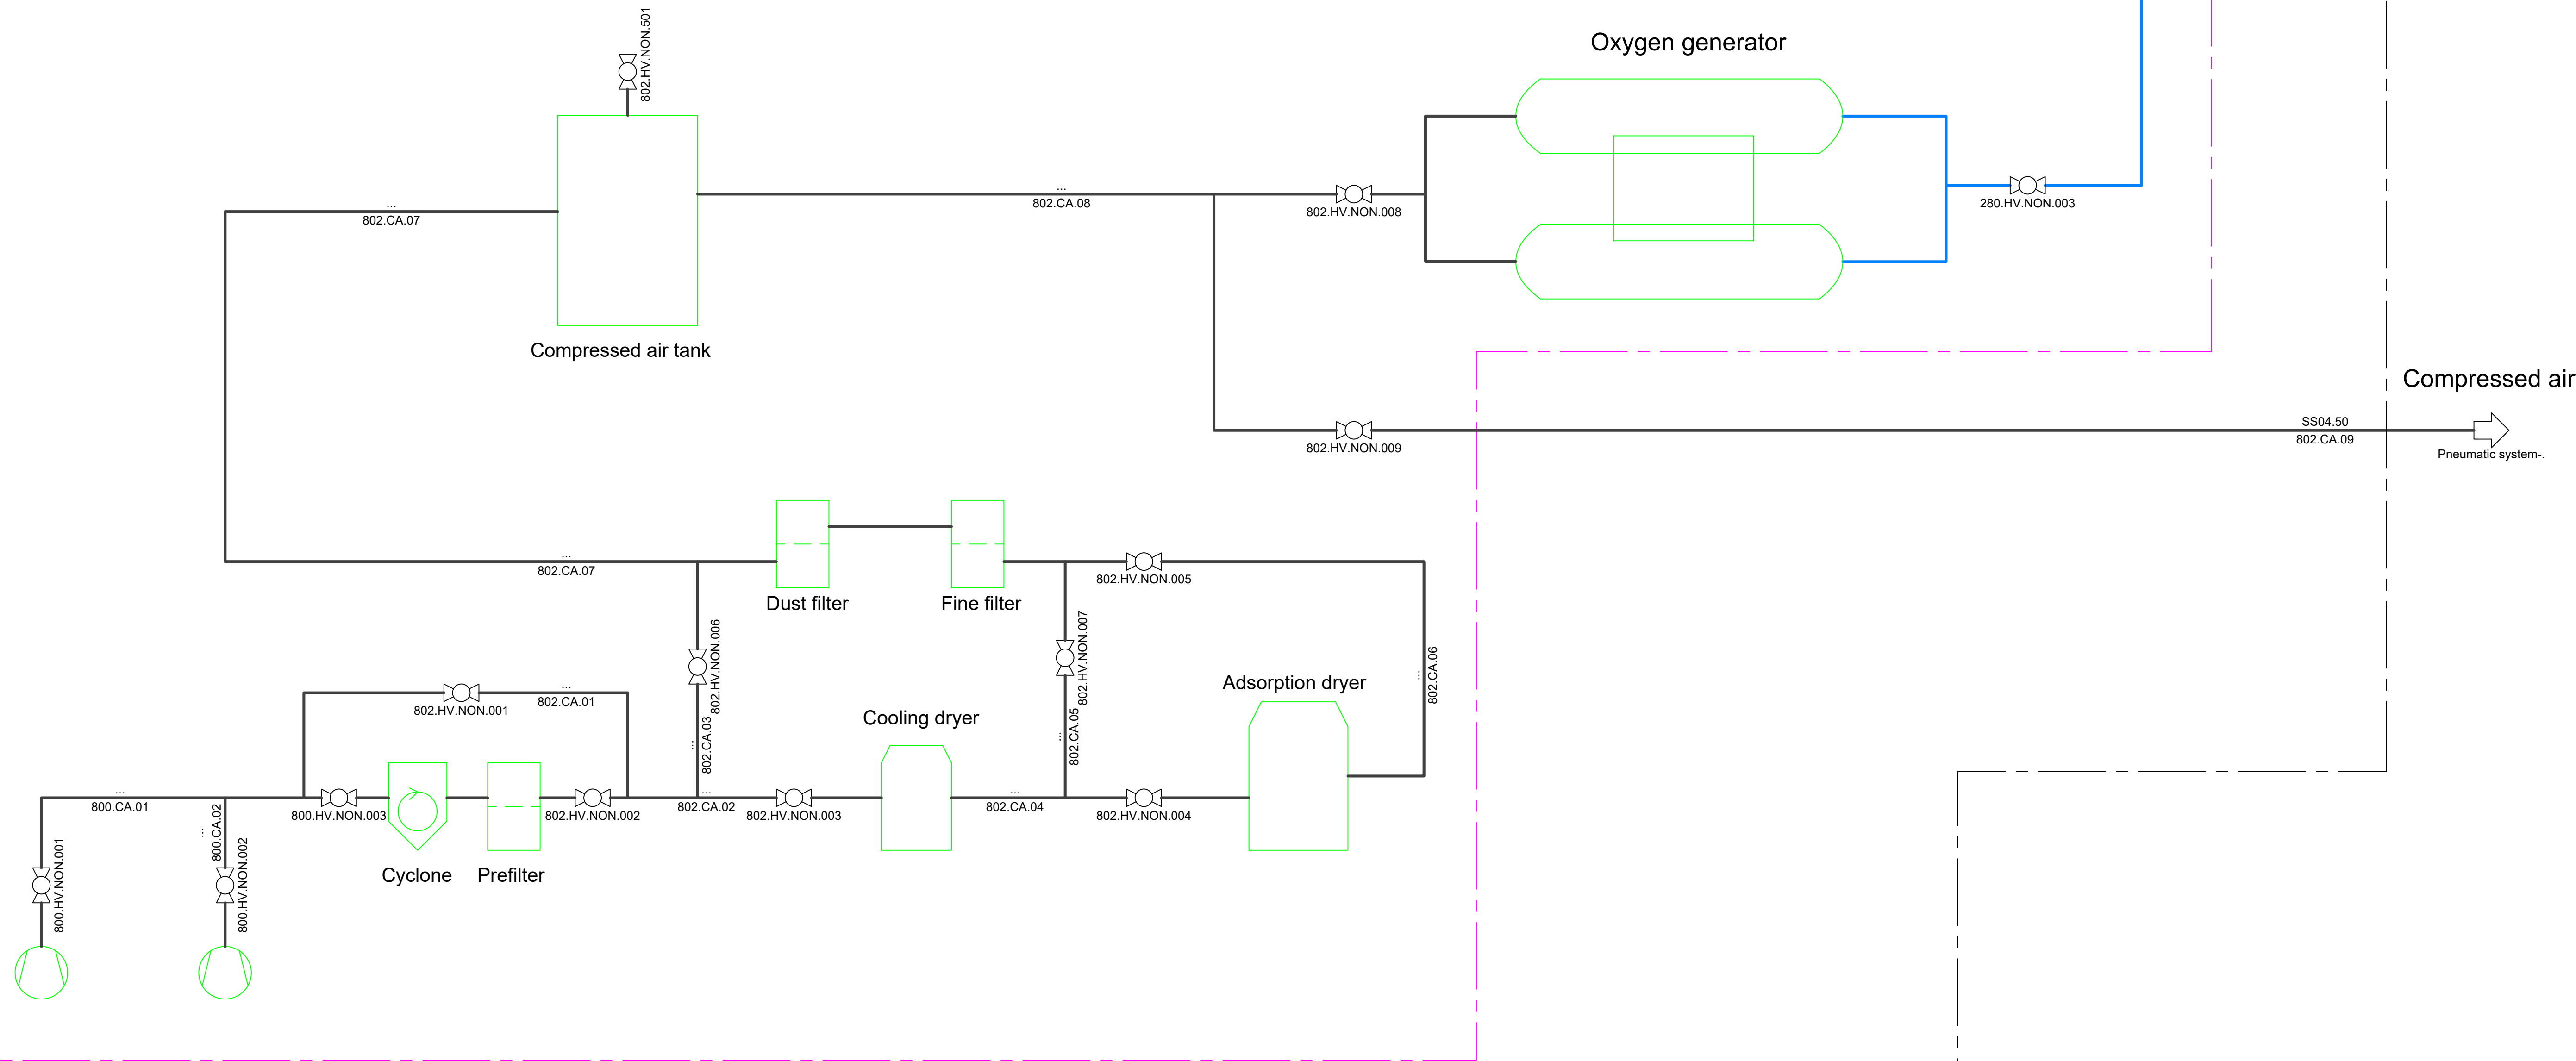

Rev. Nr.:	Rev. Dato:	Rev. Description:	
Builder:	ST1		
Project:	SLK		
Subject:	Compressed air & Oxygen		
Rev. 2			
Int.:MDC	QC:CM	APP.:	Date: 26-06-2025
LUNDSBY RENEWABLE SOLUTIONS			Lundby Renewable Solutions A/S, Hjarbrækvej 65, 8831 Lægstrup Tlf.: +45 96 49 43 00 Info@lundby.dk This Drawing is subject to copyright and may not be reproduced without permission from Lundby Renewable Solutions A/S
Project nr.:1768 Drawing nr.: 9641			FORMAT: A1

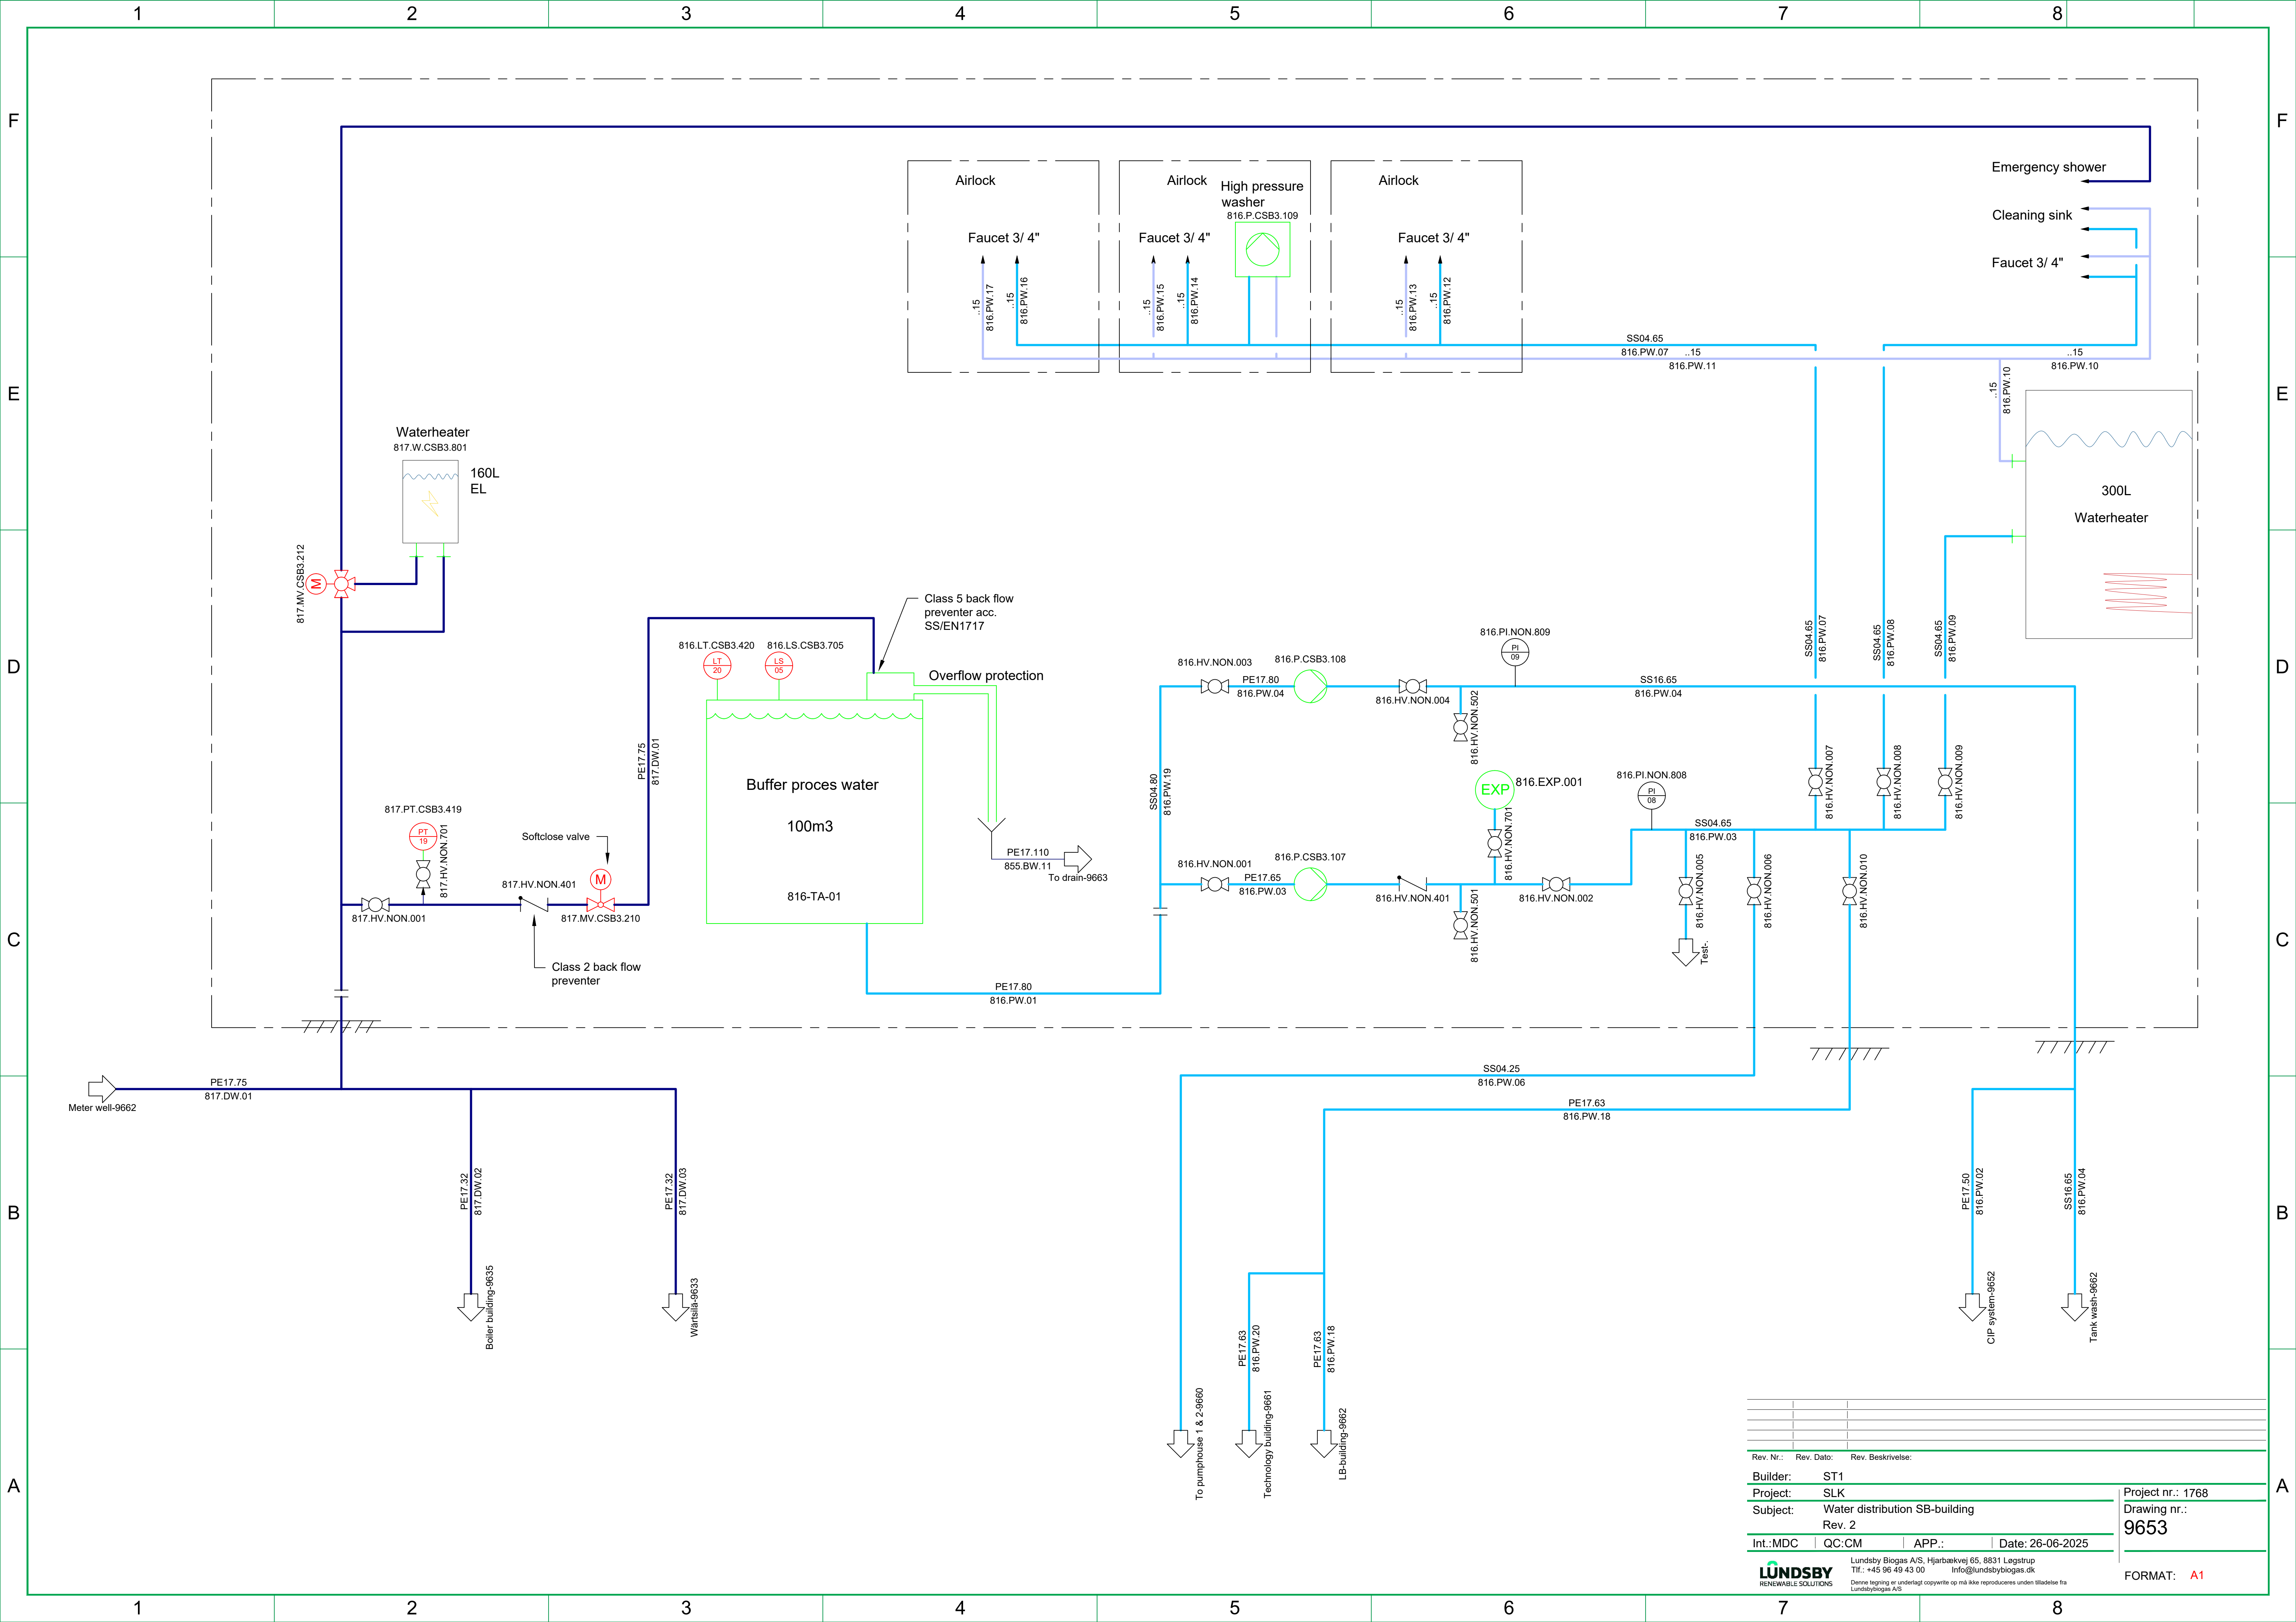


Rev. Nr.:	Rev. Dato:	Rev. Beskrivelse:
Builder:	ST1	
Project:	SLK	
Subject:	Water distribution SB-building	
Rev. 2		
Int.:MDC	QC:CM	APP.:
Date:	26-06-2025	
LUNDSBY RENEWABLE SOLUTIONS		
Lundsgby Biogas A/S, Hjarbækvej 65, 8831 Løgstrop Tlf.: +45 96 49 43 00 info@lundsgbybiogas.dk		
Denne tegning er underlagt copyright og må ikke reproduceres uden tilladelse fra Lundsgbybiogas A/S		
Project nr.: 1768		
Drawing nr.: 9653		
FORMAT: A1		

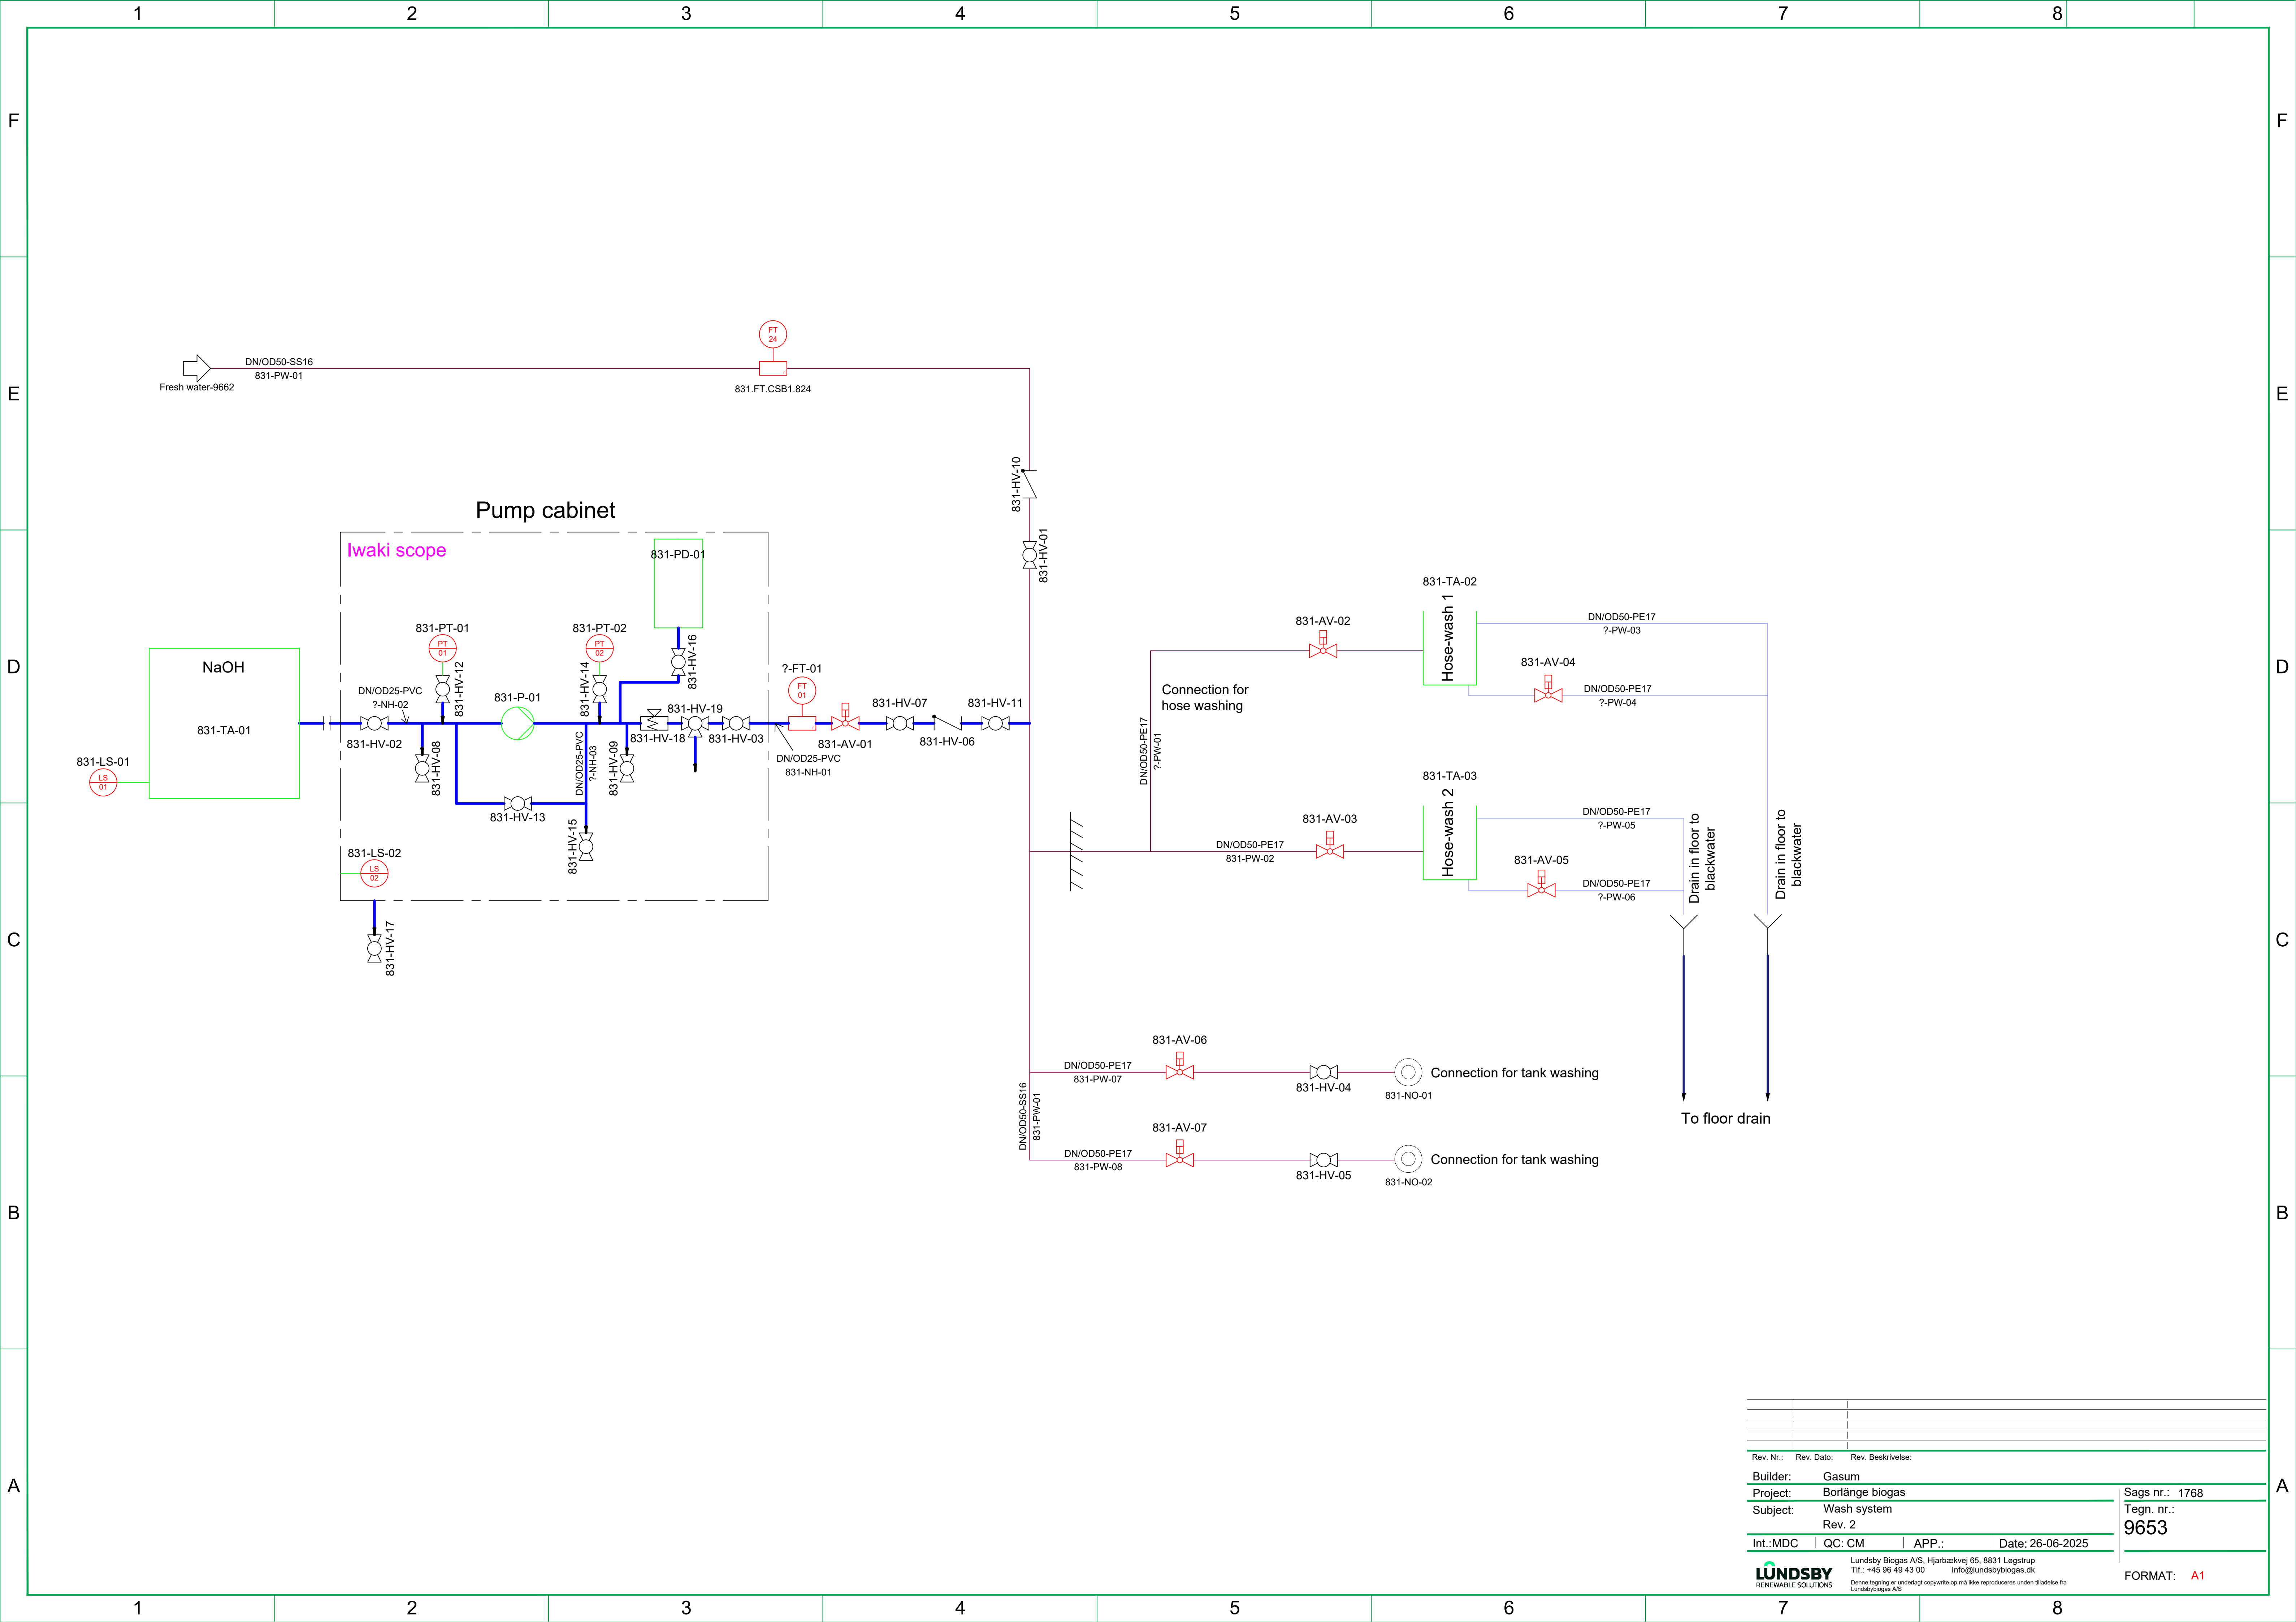


Rev. Nr.:	Rev. Dato:	Rev. Beskrivelse:	
Builder:	Gasum		
Project:	Borlänge biogas		
Subject:	Wash system		
Rev. 2			
Int.:MDC	QC: CM	APP.:	Date: 26-06-2025
LUNDSBY RENEWABLE SOLUTIONS			Lundsby Biogas A/S, Hjarbækvej 65, 8831 Løgstrup Tlf.: +45 96 49 43 00 Info@lundsbybiogas.dk Denne tegning er underlagt copyright og må ikke reproduceres uden tilladelse fra Lundsbybiogas A/S
Sags nr.: 1768			Tegn. nr.: 9653
FORMAT: A1			

LB-building

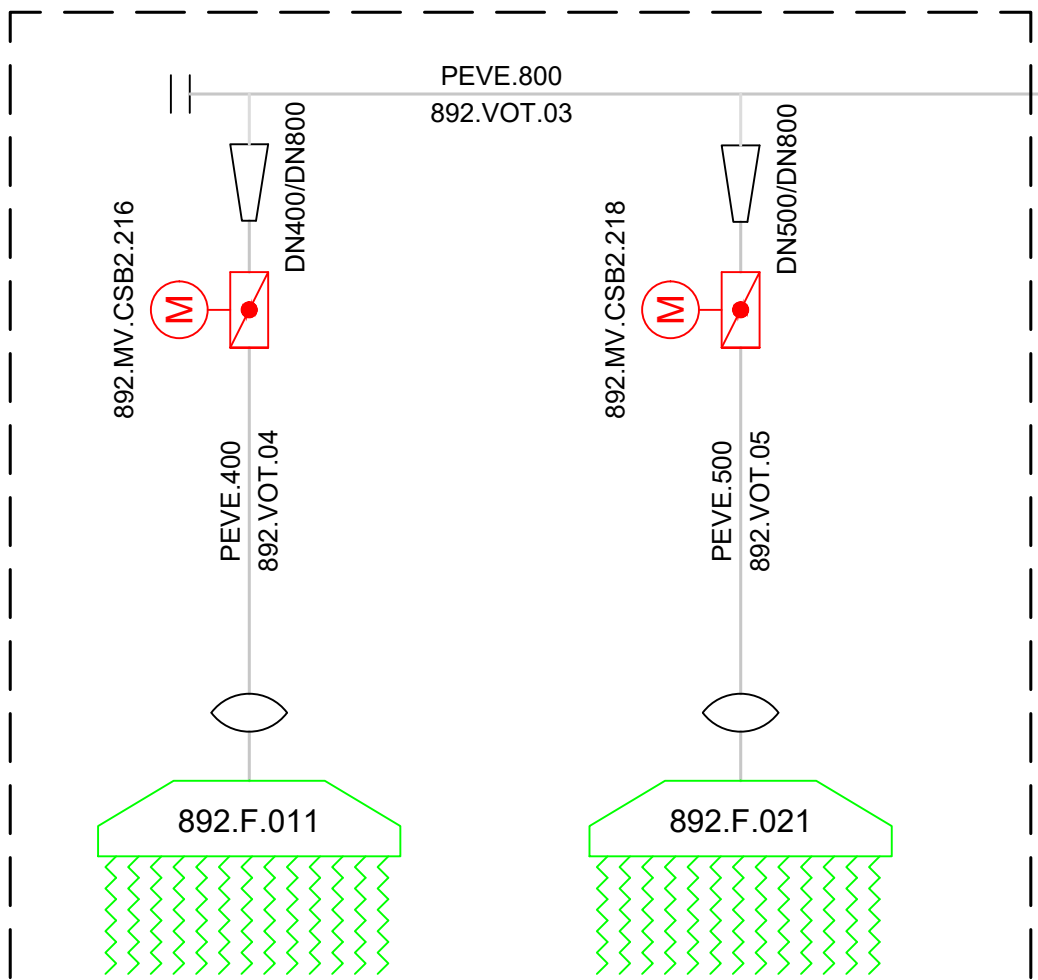

LB-building overhead
suction for trucks

890.PT.AK509.402

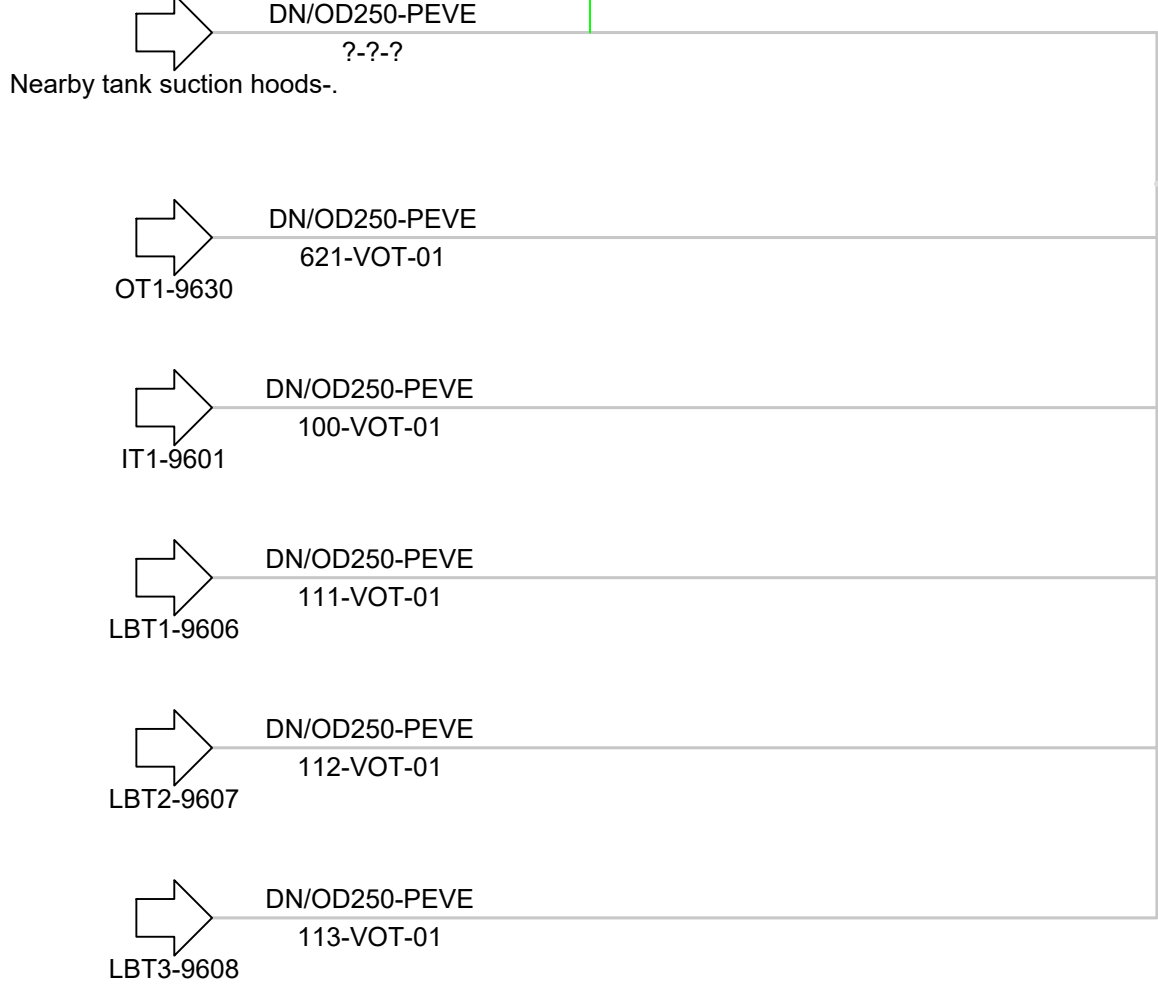


PEVE.250
730.VOT.01

892.MV.CSB2.219

890.PT.AK509.403

944.AK.CSB2.509

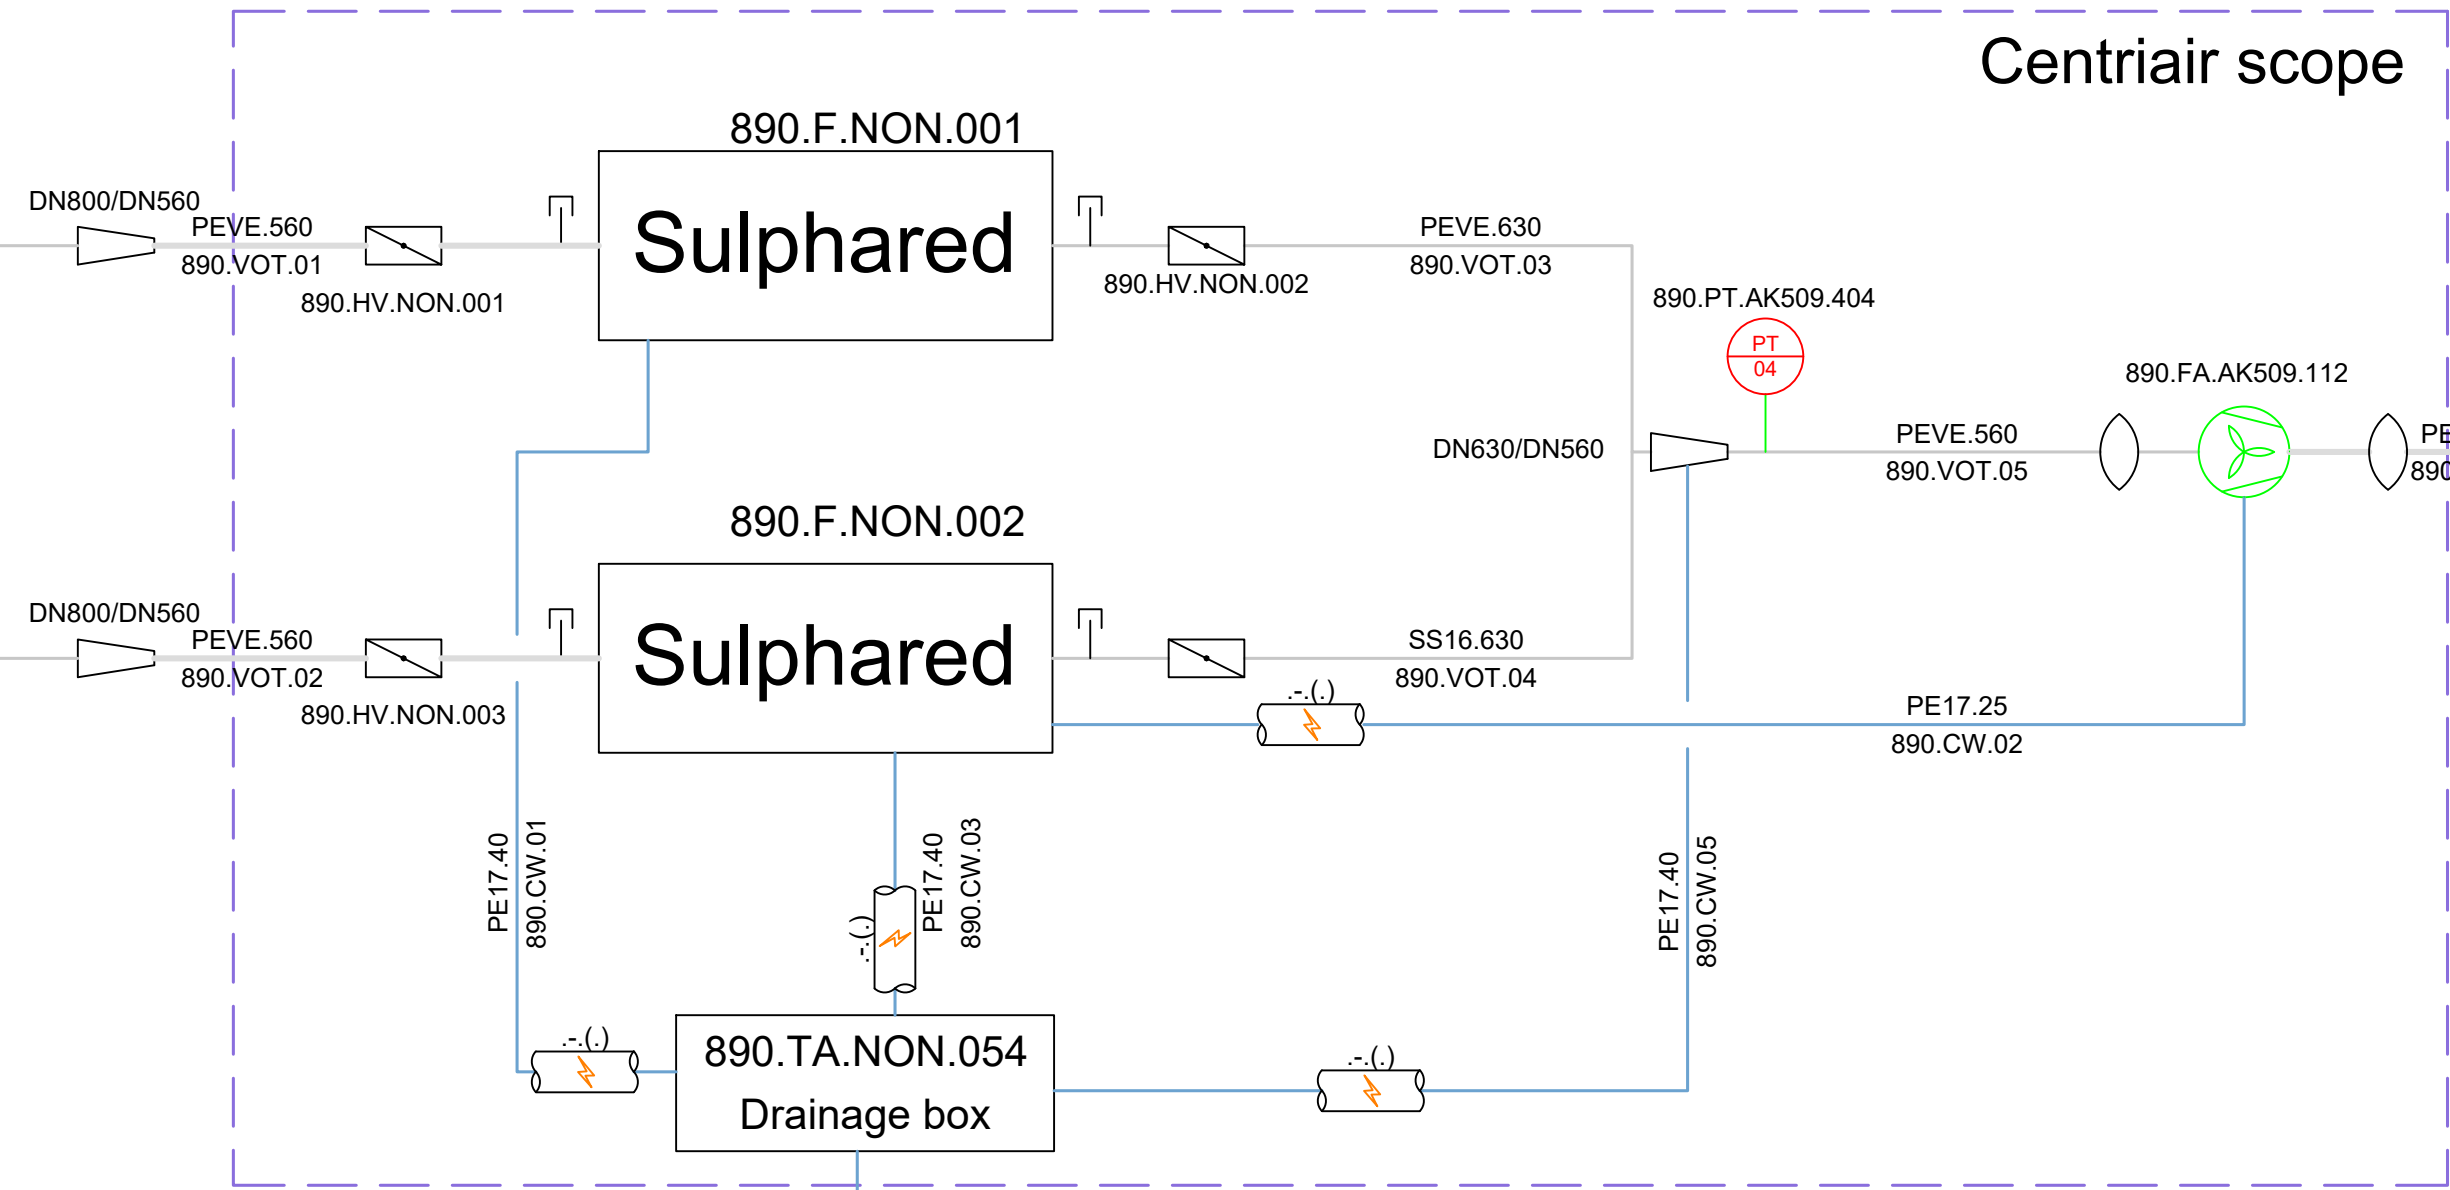


Centriair scope

Sulphared

Sulphared


890.TA.NON.054
Drainage box

Centriair UV reaktor-9666

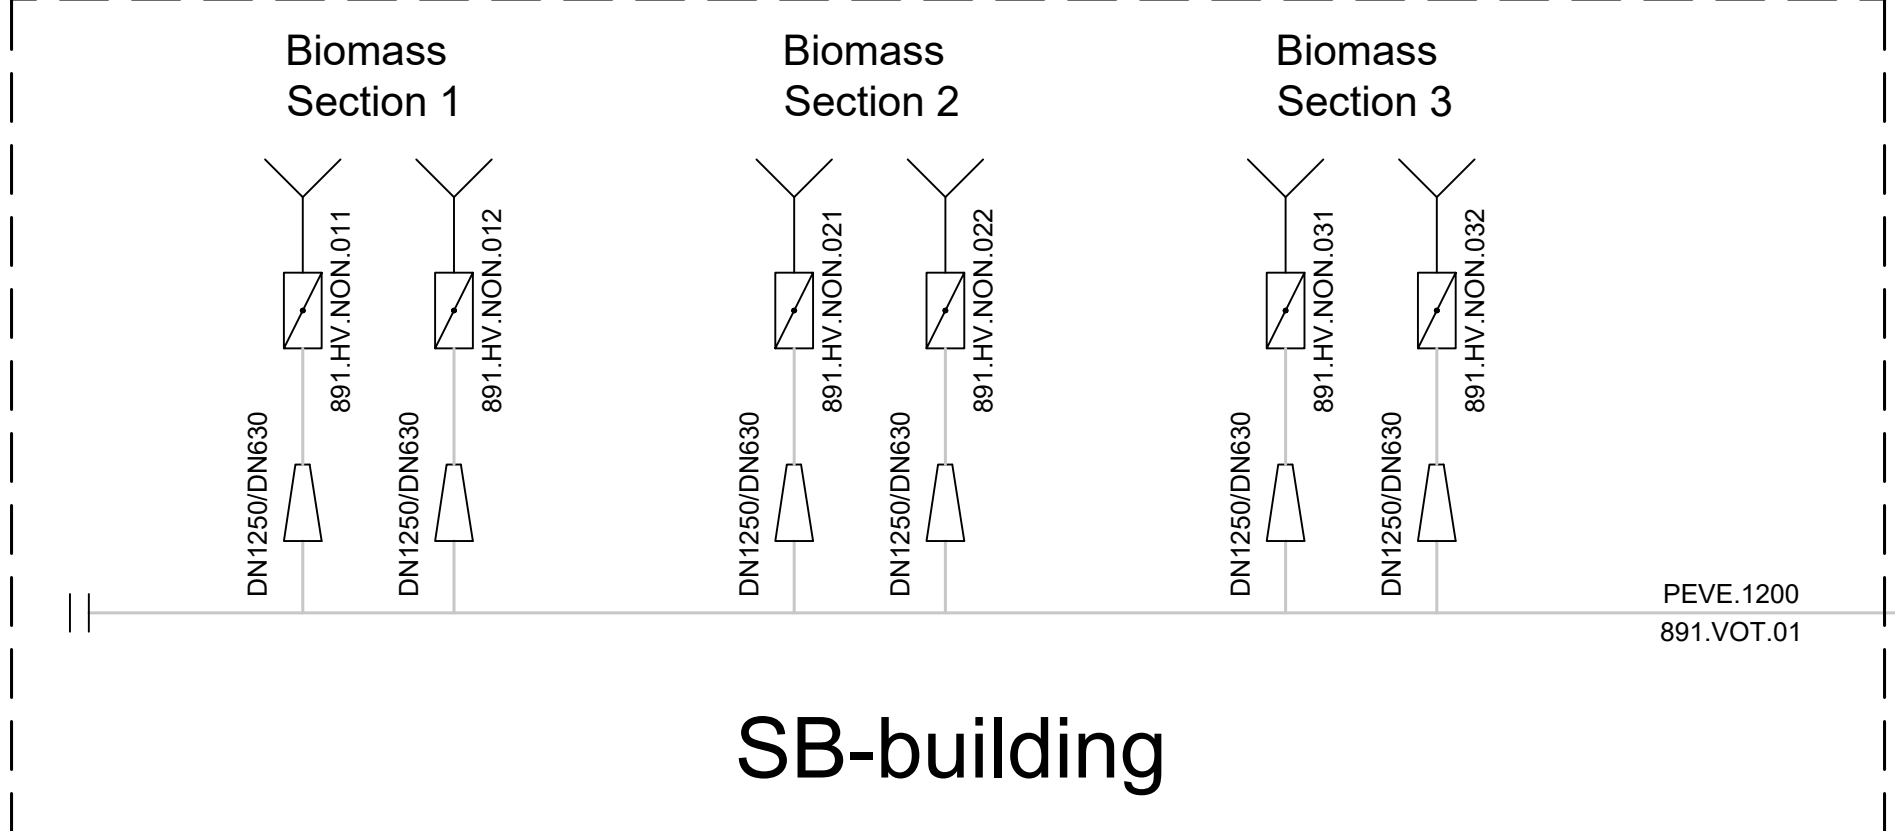


SB-building

Centriair scope

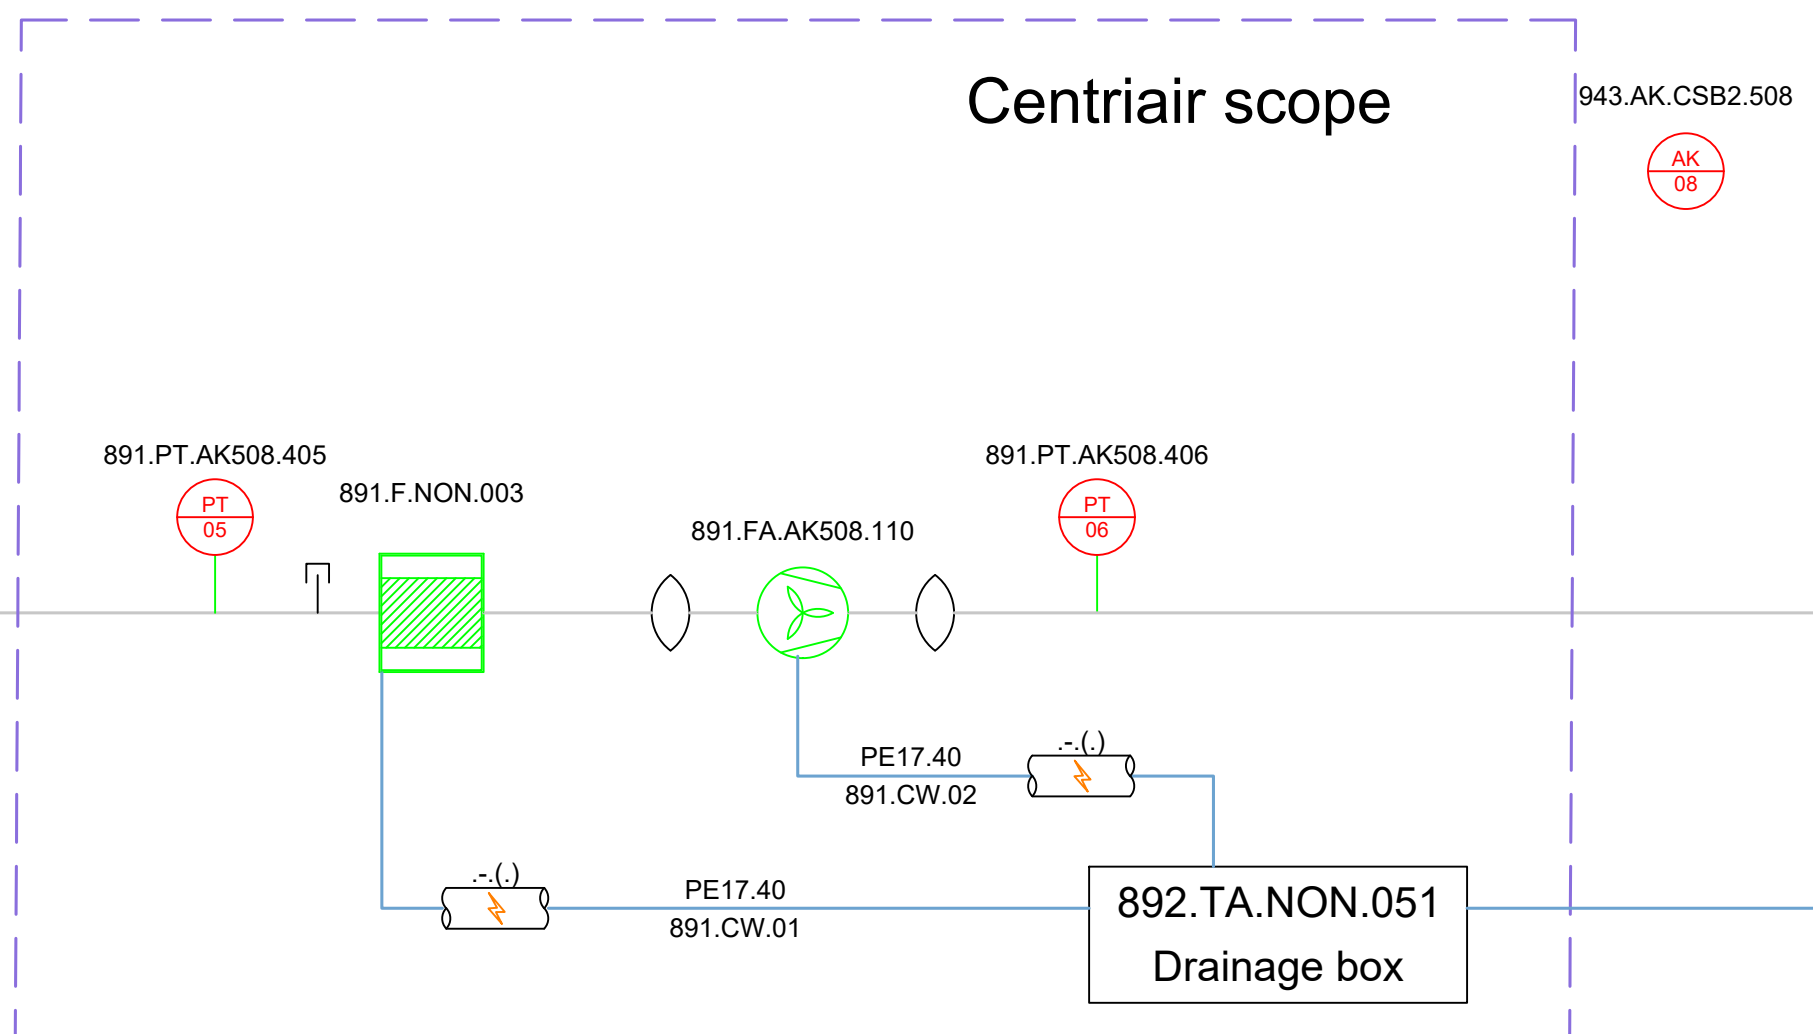



892.TA.NON.051
Drainage box



Rev. Nr.:	Rev. Dato:	Rev. Description:
Builder:	ST1	
Project:	SLK	
Subject:	Centriair SB-building & LB-building	
Rev. 2		
Int.:MDC	QC:CM	APP.:
Date:	26-06-2025	
LUNDSBY RENEWABLE SOLUTIONS		
Lundsby Renewable Solutions A/S, Hjarbækvej 65, 8831 Lægstrup Tlf.: +45 96 49 43 00 Info@lundsby.dk This Drawing is subject to copyright and may not be reproduced without permission from Lundsby Renewable Solutions A/S		
Project nr.:1768		Drawing nr.: 9656
FORMAT: A1		

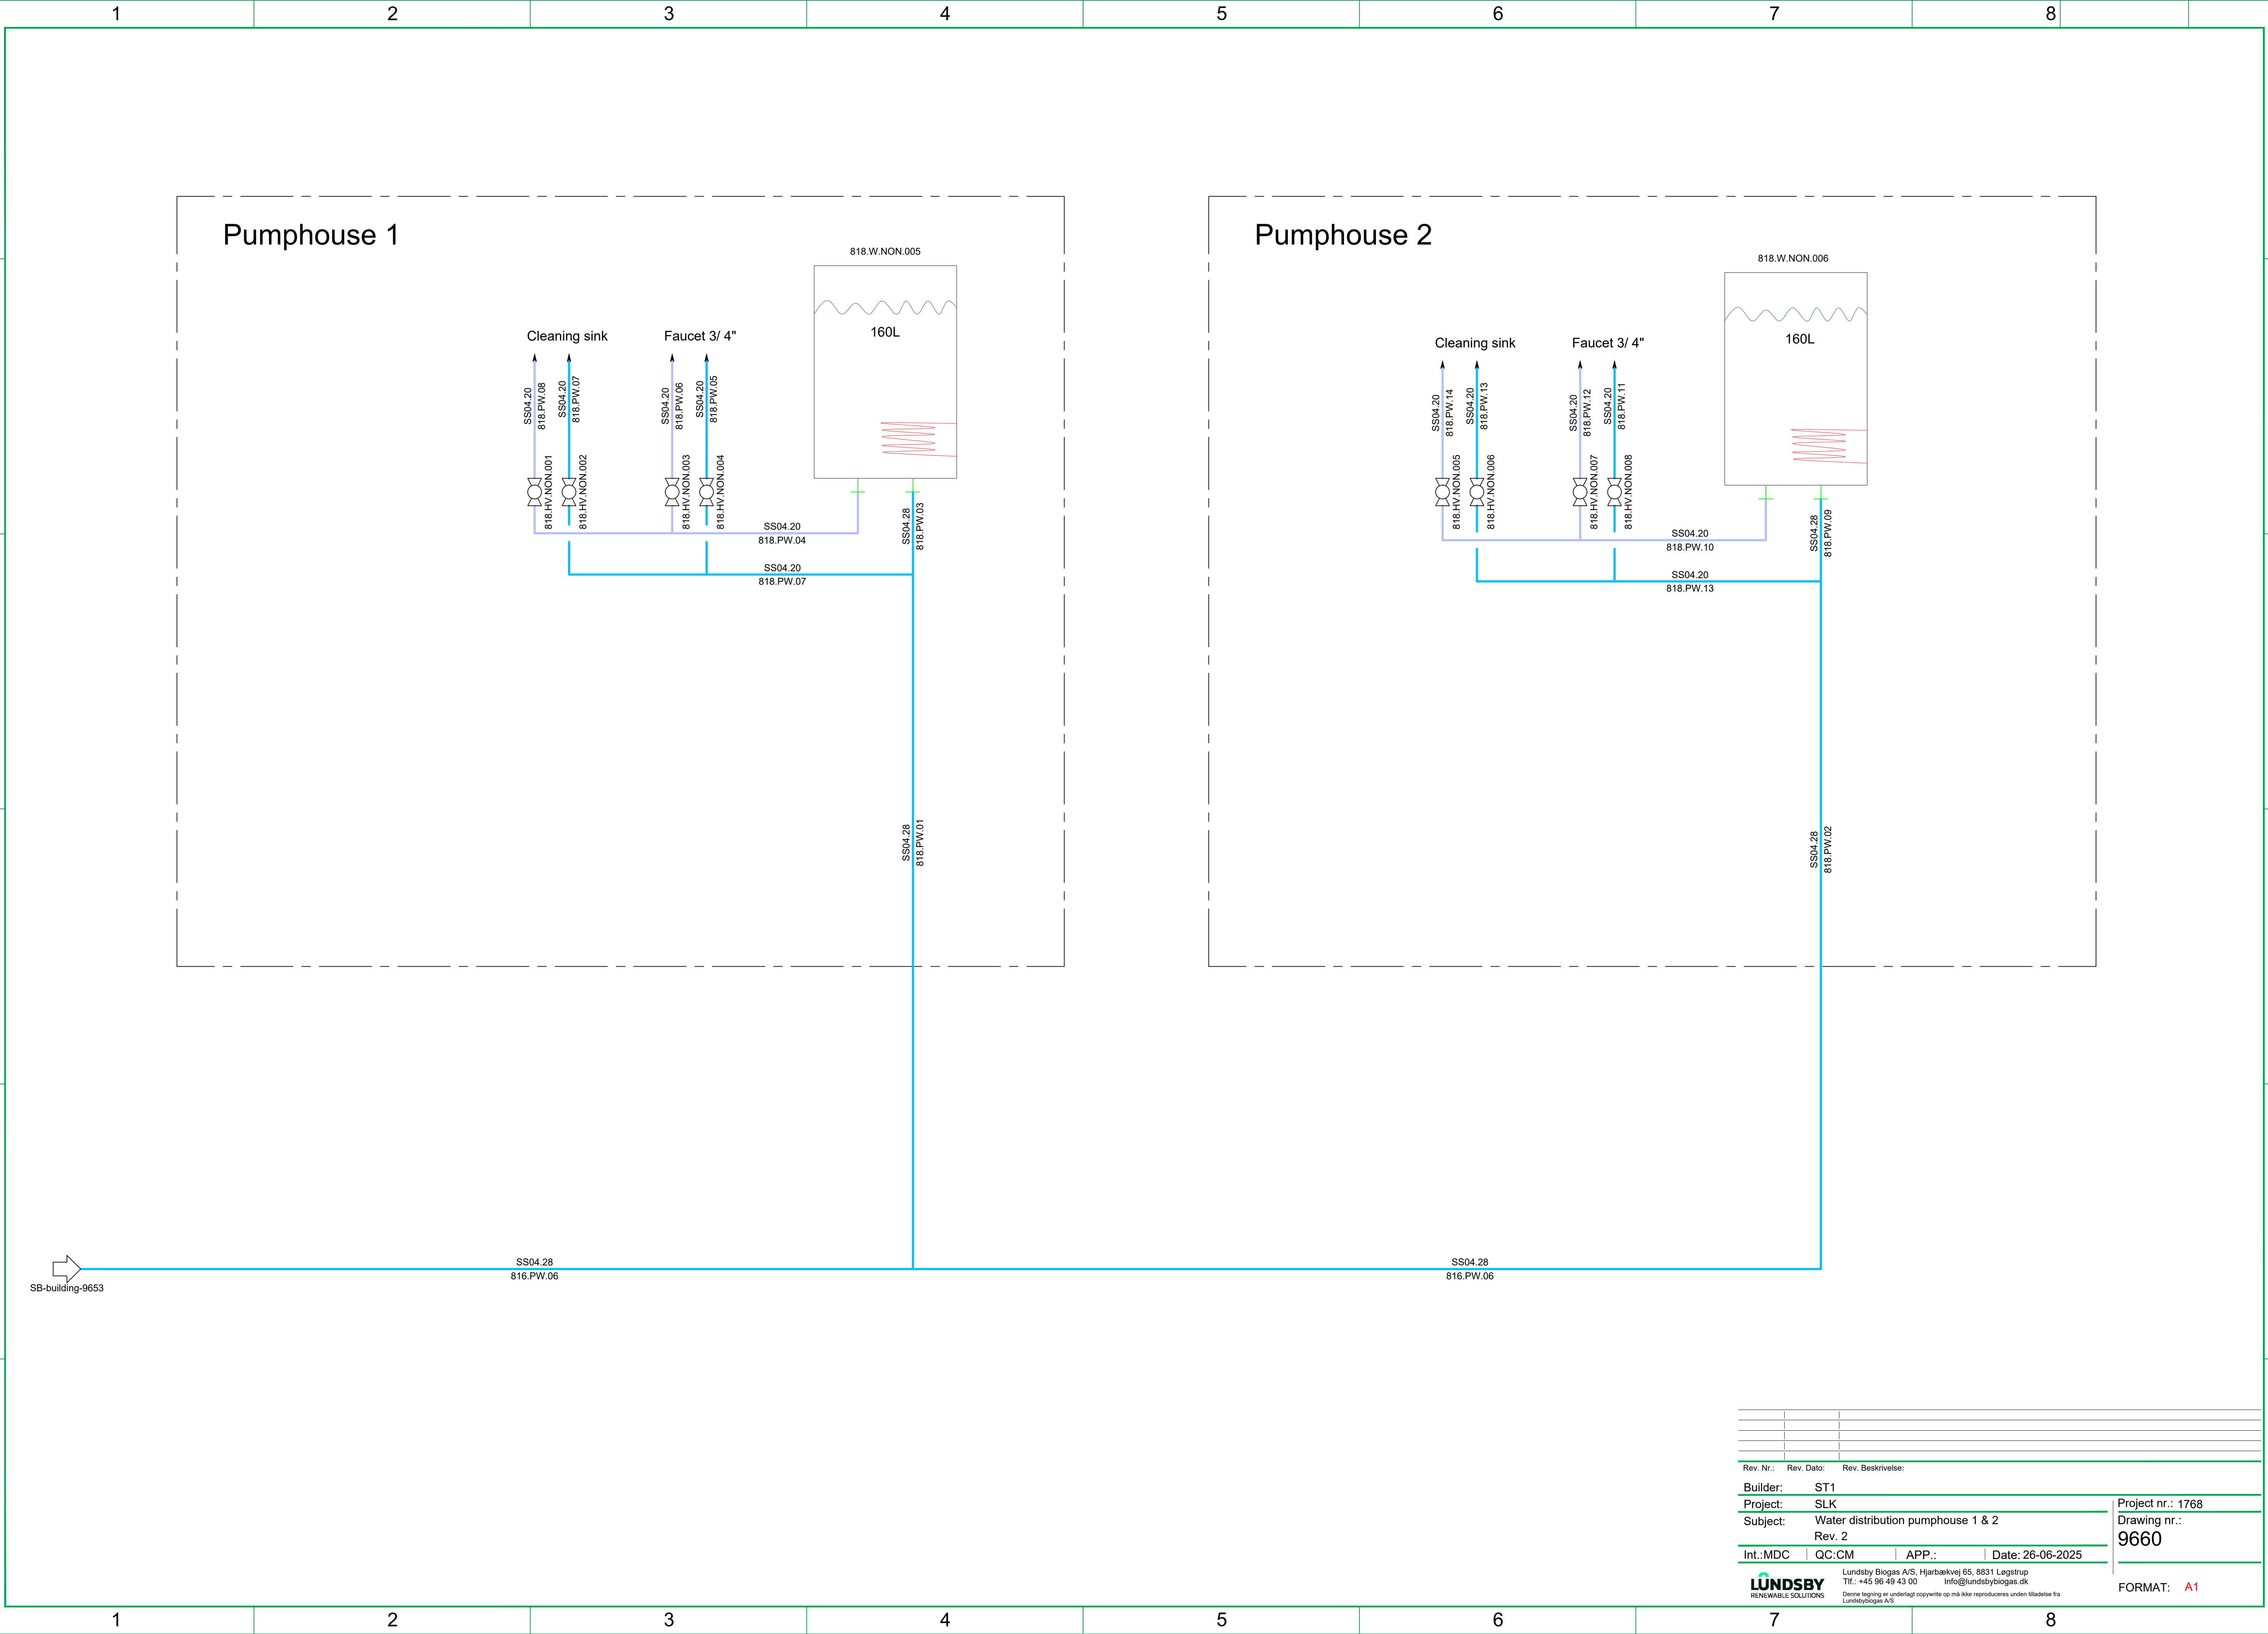

Technology building

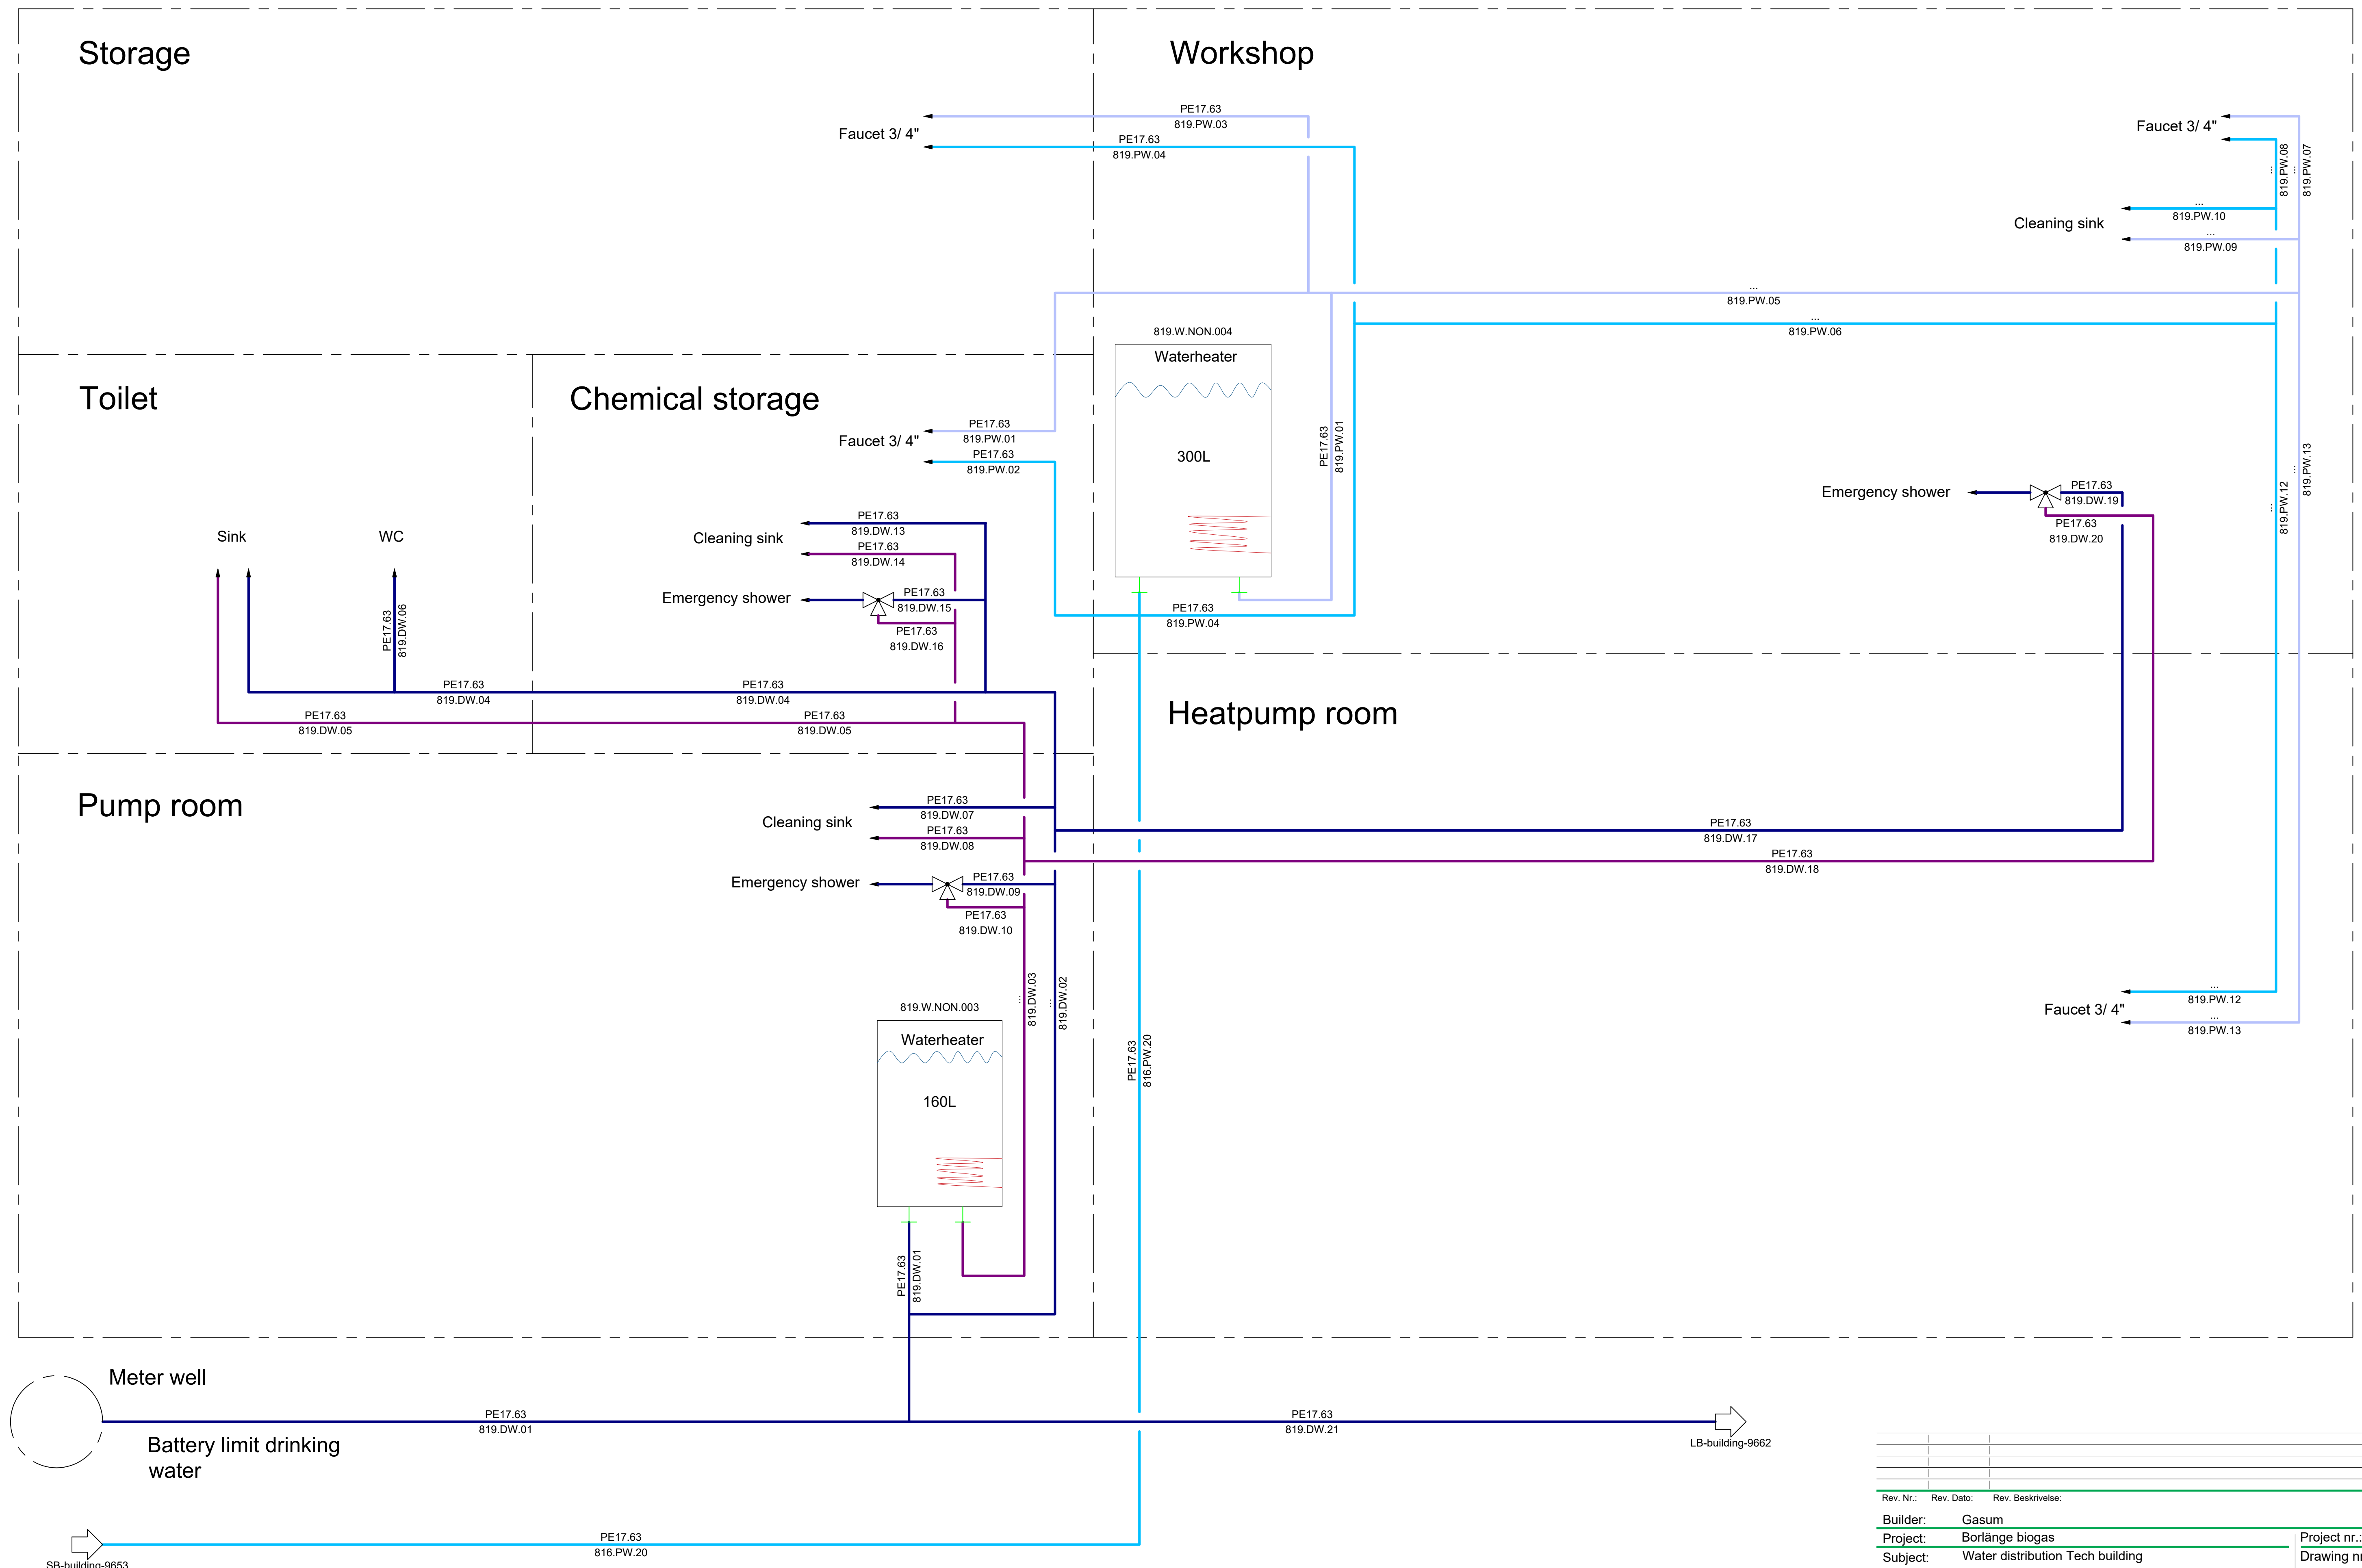[illegible]

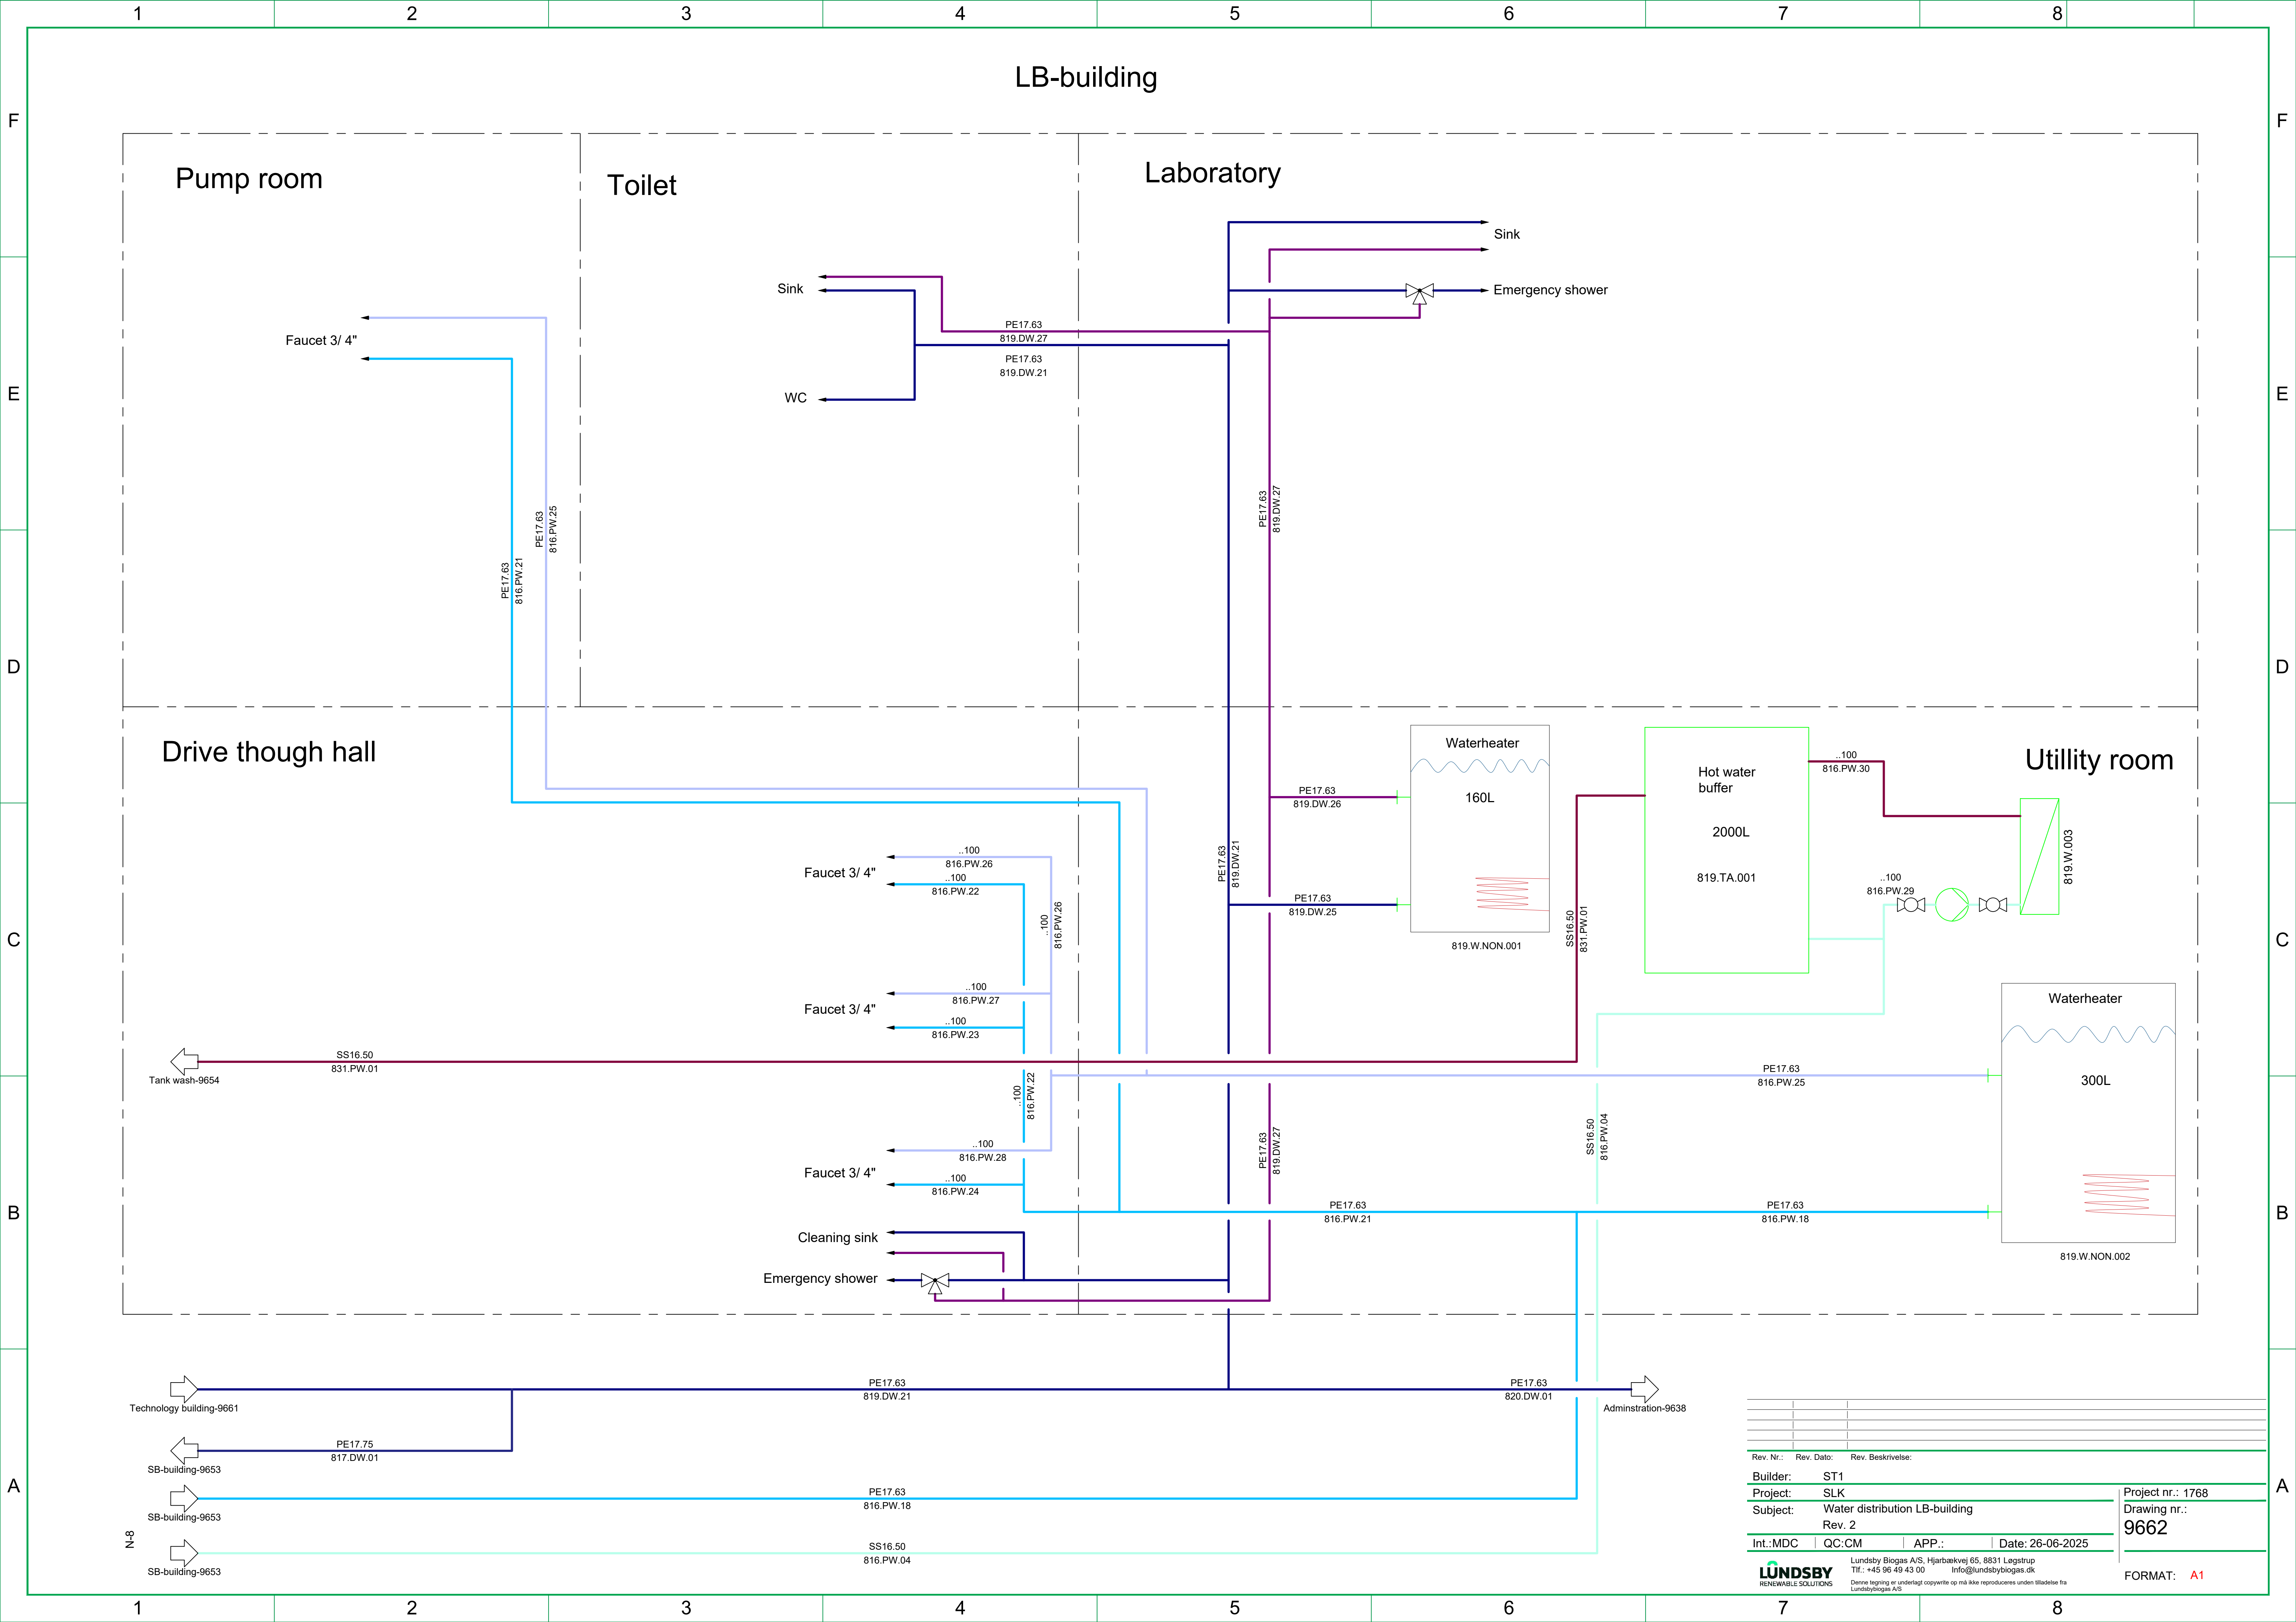

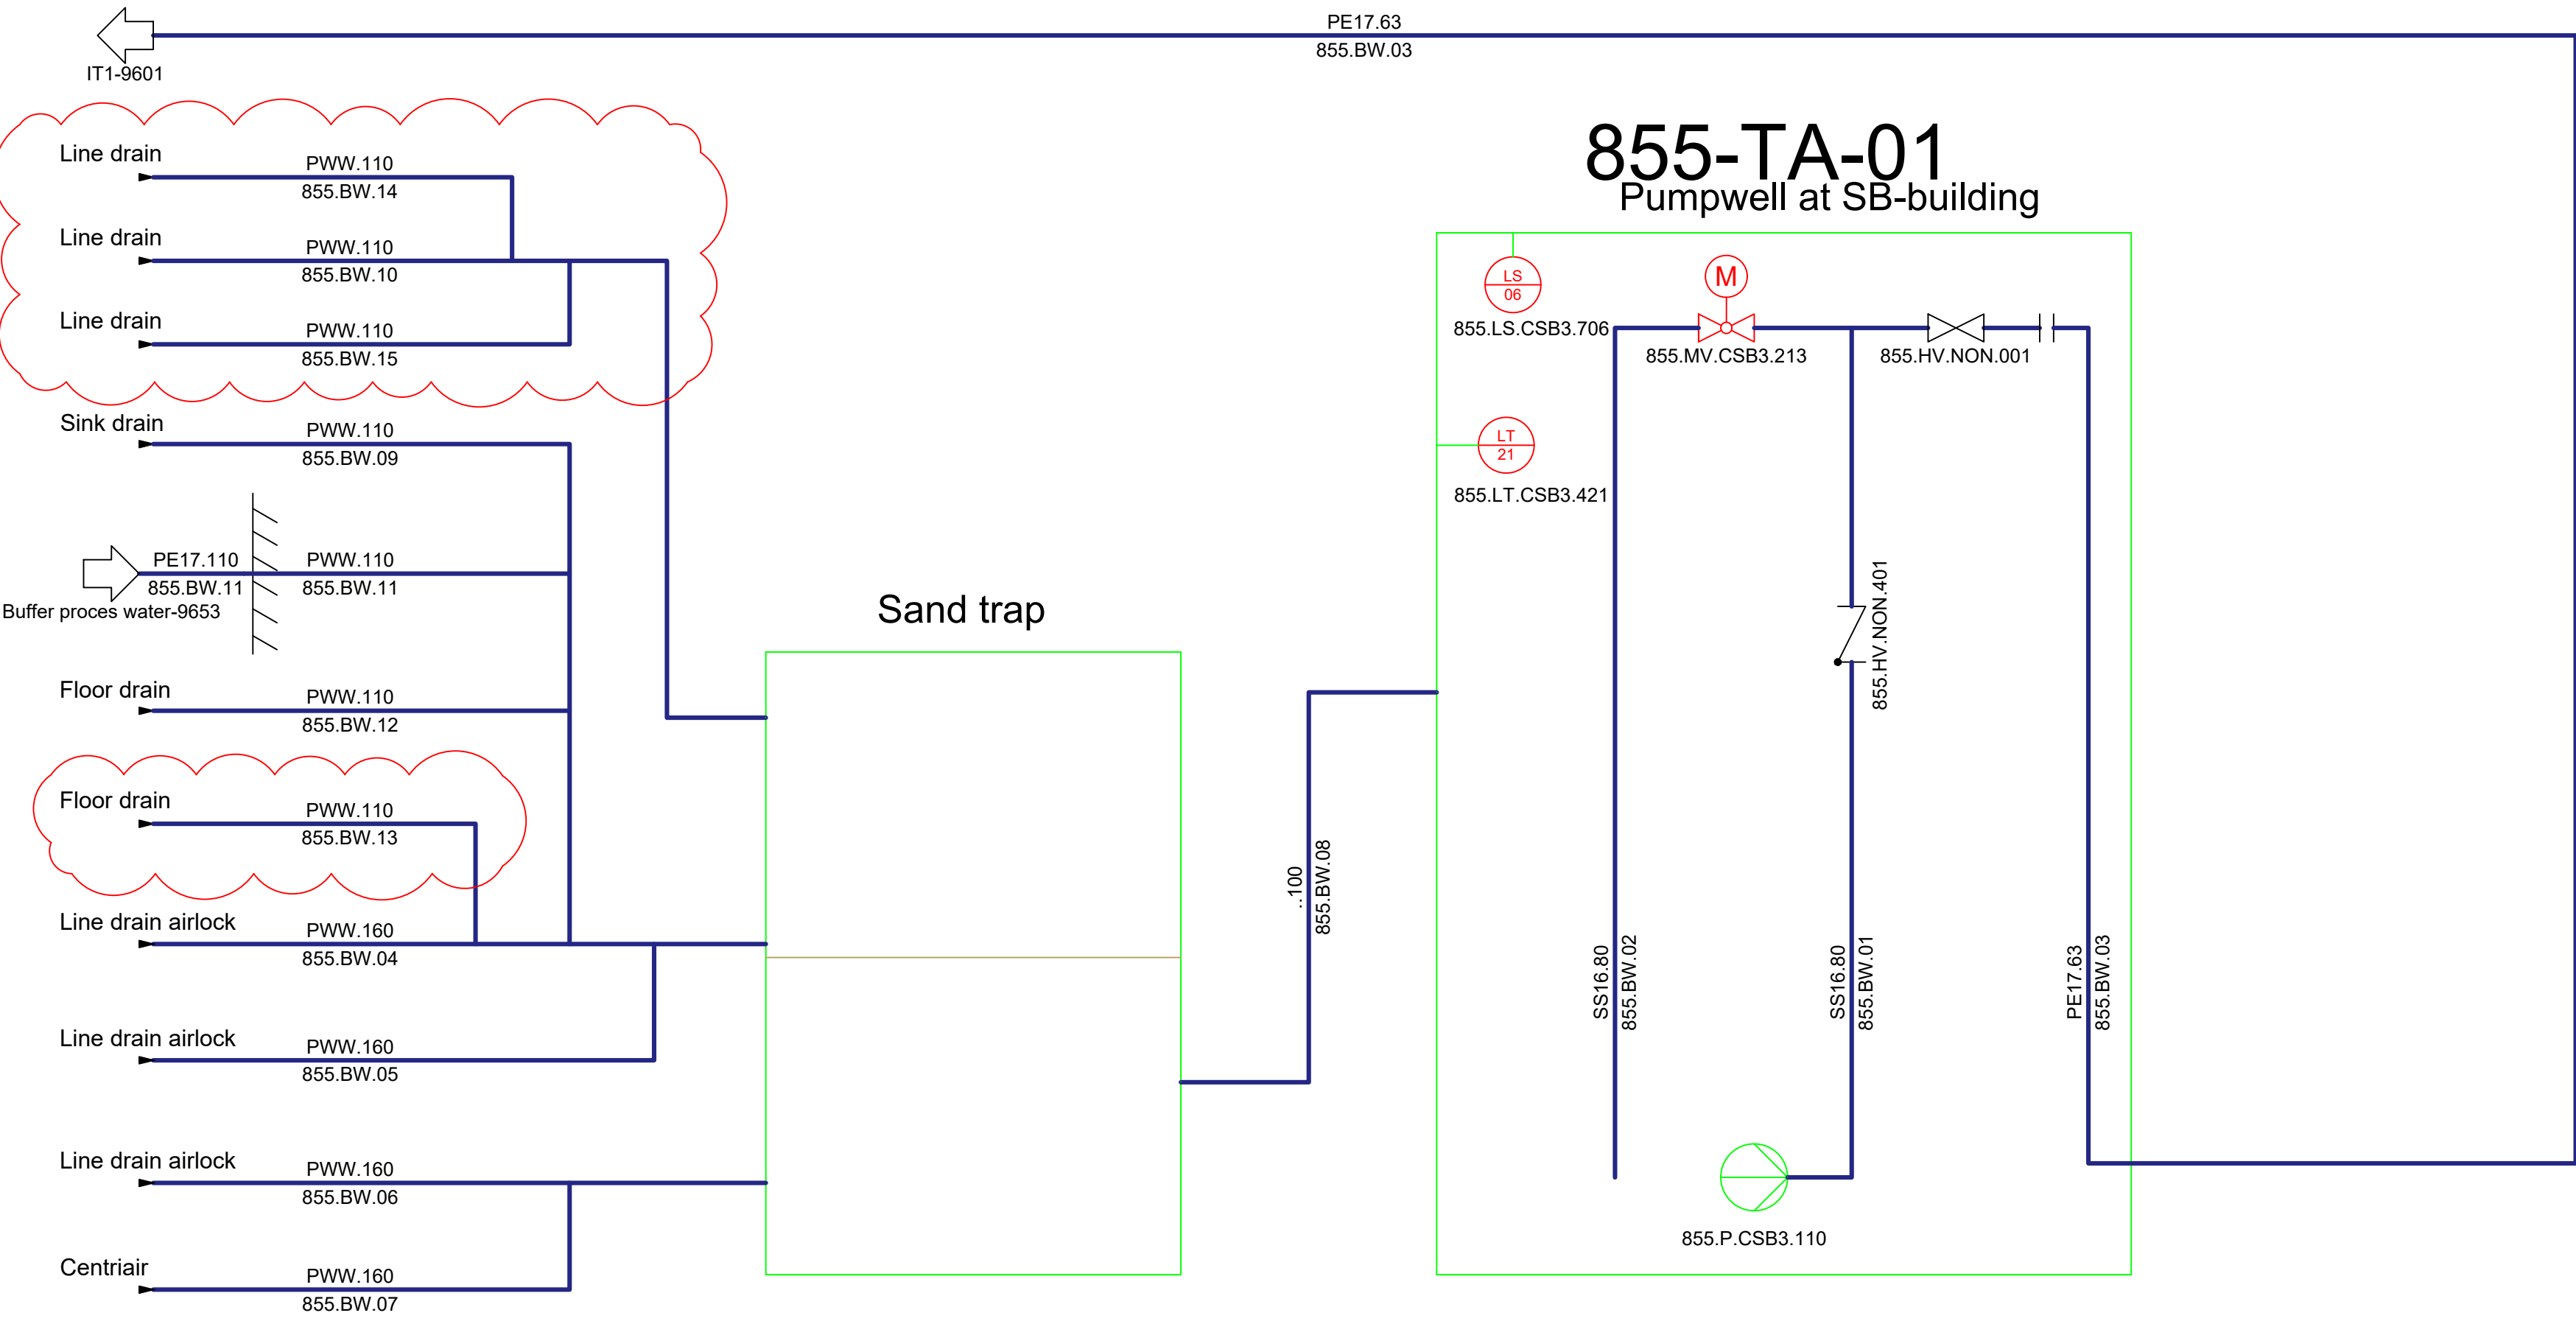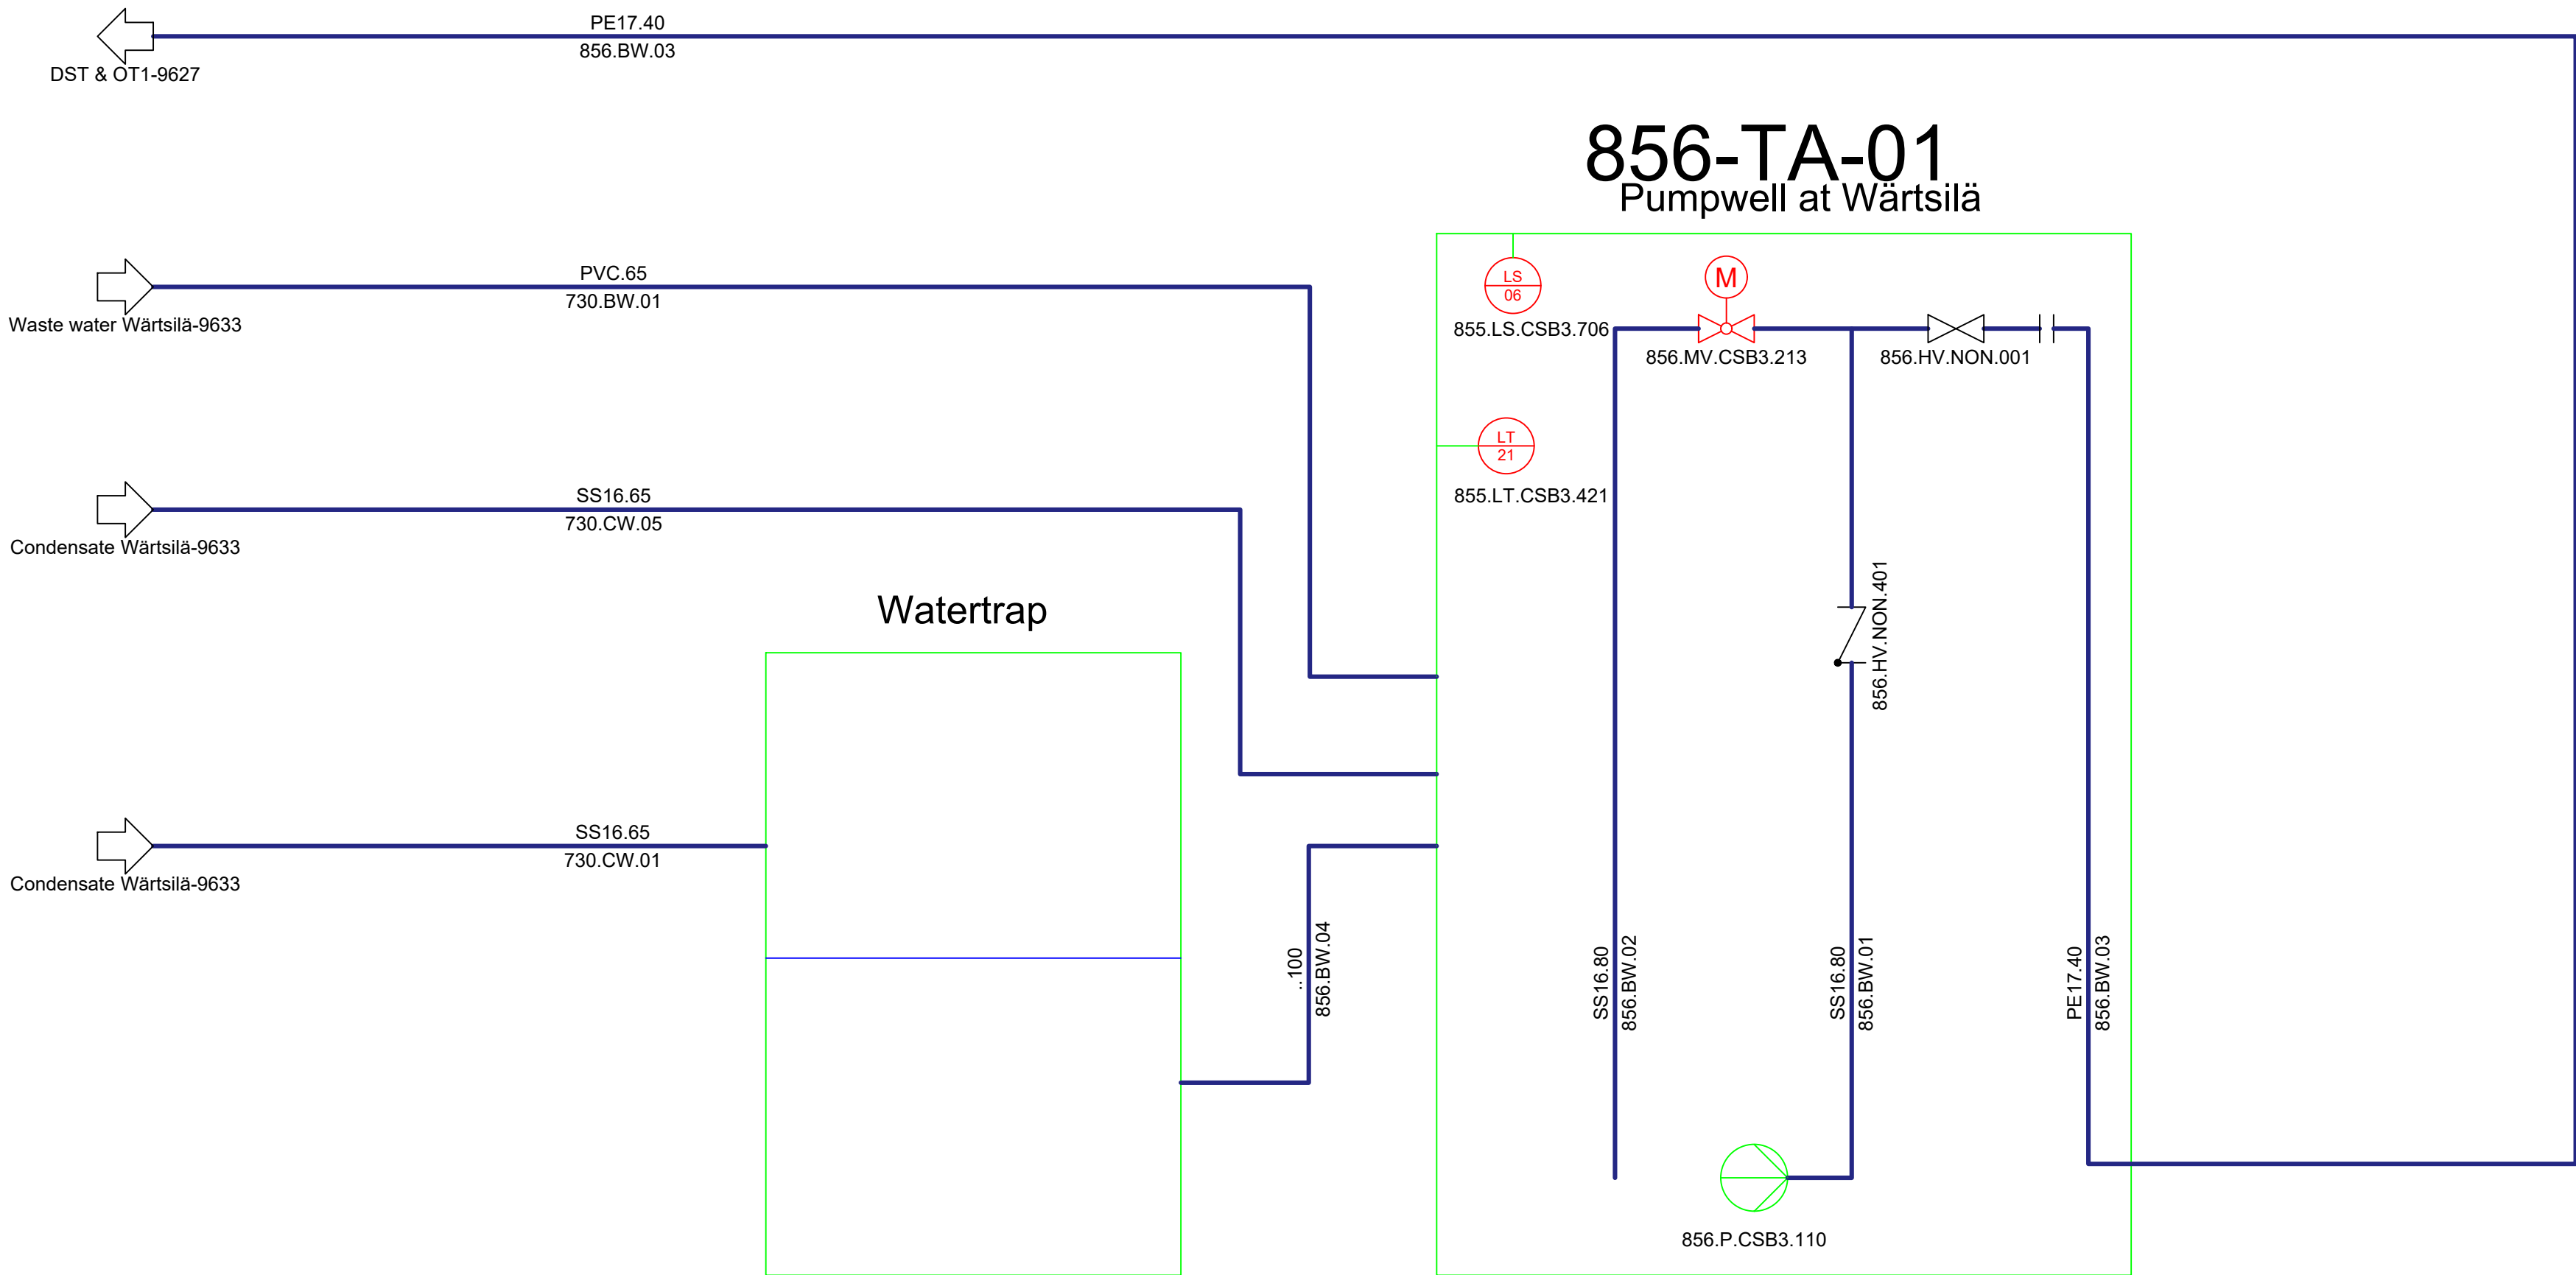

Rev. Nr.:	Rev. Dato:	Rev. Description:	
Builder:	ST1		
Project:	SLK		
Subject:	Blackwater well SB-building & Wärtsilä		
	Rev. 2		
Int.:MDC	QC.CM	APP.:	Date: 26-06-2025
LUNDSBY RENEWABLE SOLUTIONS			Lundsby Renewable Solutions A/S, Hjarbækvej 65, 8831 Løgstrup Tlf.: +45 96 49 43 00 Info@lundsby.dk This Drawing is subject to copyright and may not be reproduced without permission from Lundsby Renewable Solutions A/S
Project nr...1768 Drawing nr... 9640			FORMAT: A1

